

| QUANTITY : | CONCRETE VOLUME : | CONCRETE WEIGHT : | CONCRETE TYPE : |
|---|---|---|---|
| 47 EA. | 3.234 CU.M/EA | 7.762 T./EA | Cast in place |

REBAR BENDING SCHEDULE


| Pos | Diameter | Number | Grade | Length | Kg/p | Weight | Bending shape |
|---|---|---|---|---|---|---|---|
| 4 | 12 | 160 | SD40 | 790 | 0.70 | 112.24 | 111, 600, 45° |
| 309 | 25 | 24 | SD40 | 7300 | 28.13 | 675.22 | 6400, 203, 7°, 700 |
| 5 | 12 | 40 | SD40 | 2540 | 2.26 | 90.22 | 111, 600, 600 |
| | | | | Total: | | 877.68 | |

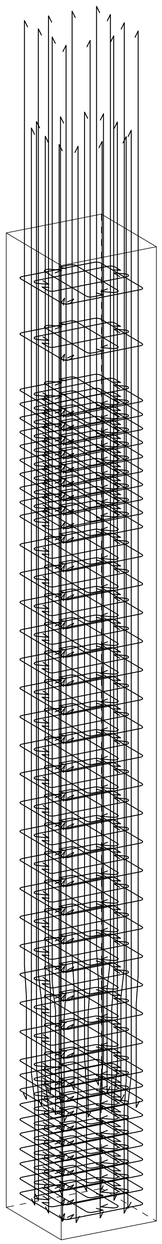


3D VIEW
SCALE : 1:20

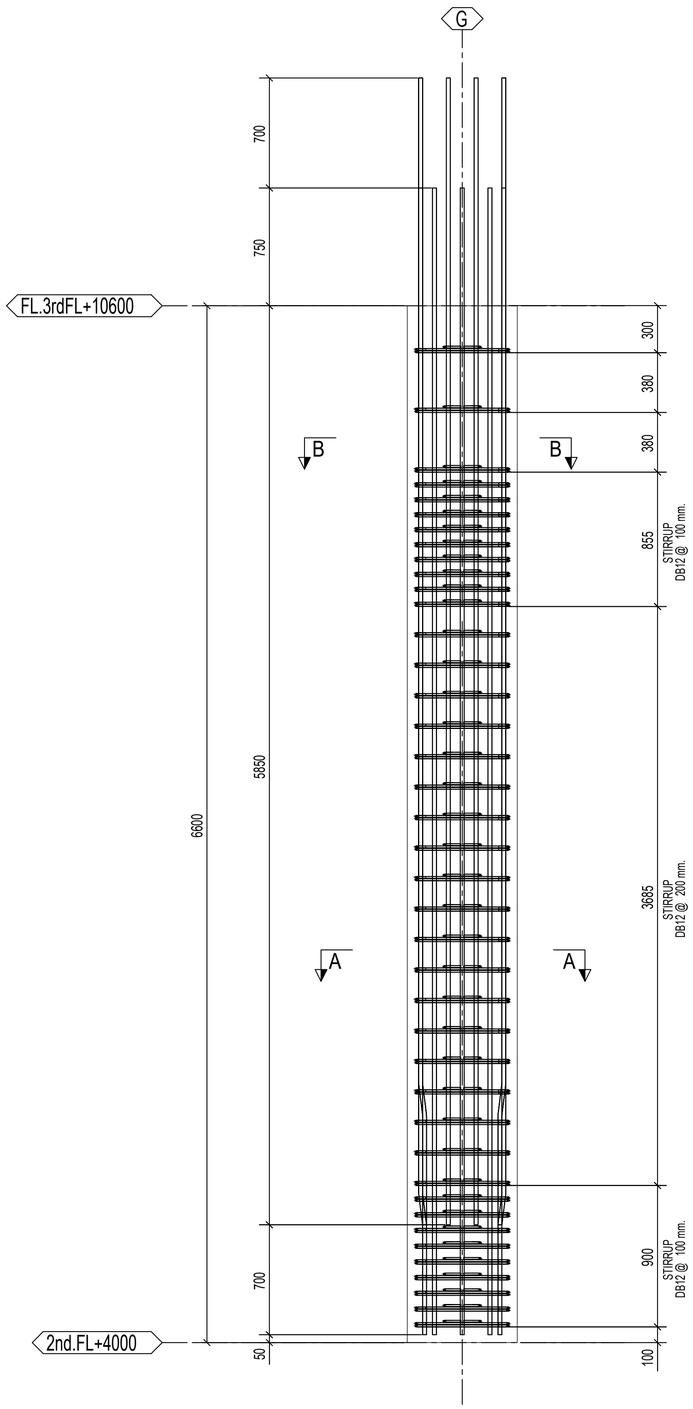


ELEVATION VIEW
SCALE : 1:20

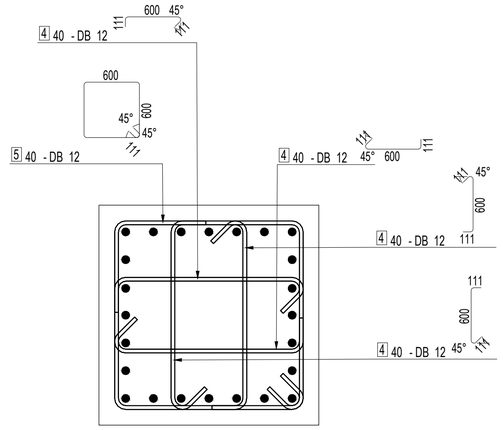


SECTION B - B
SCALE : 1:10

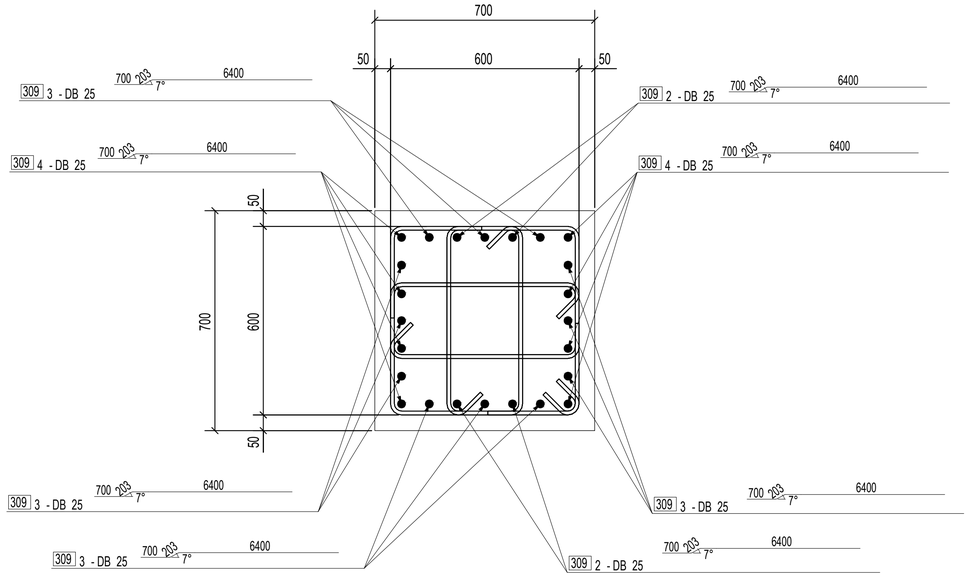


SECTION A - A
SCALE : 1:10

| REV. | DESCRIPTION | AUTHOR | CHK. | APPR. | DATE |
|---|---|---|---|---|---|
| 0A | ISSUED FOR CONSTRUCTION | WNS. | SP./TK. | TNP. | 15 AUG 2026 |

CLIENT NAME : GULF MTP LNG TERMINAL COMPANY LIMITED

CONTRACTOR : POSCO E&C / CAZ CONSORTIUM

GENERATED BY : P PROFESSIONAL ENGINEERING CO.,LTD

DRAWING TITLE :
GULF MTP LNG RECEIVING TERMINAL PROJECT
INSTRUMENT & SUBSTATION BUILDING
COLUMN No. 2C1-101

| DWG NO : | SHEET | REV NO : | SCALE : | SIZE : |
|---|---|---|---|---|
| GULF-ISB-CU-FL10600-2C1-101 | 1/1 | 0A | 1:10,1:20 | A1 |