

QUANTITY :	CONCRETE VOLUME :	CONCRETE WEIGHT :	CONCRETE TYPE :
1 EA.	3.234 CU.M/EA	7.762 T./EA	Cast in place

REBAR BENDING SCHEDULE


Pos	Diameter	Number	Grade	Length	Kg/p	Weight	Bending shape
4	12	148	SD40	790	0.70	103.82	600, 45°, 111, 111
309	25	24	SD40	7300	28.13	675.22	6400, 203, 7°, 700
5	12	37	SD40	2540	2.26	83.45	111, 600, 600
				Total:		862.50	

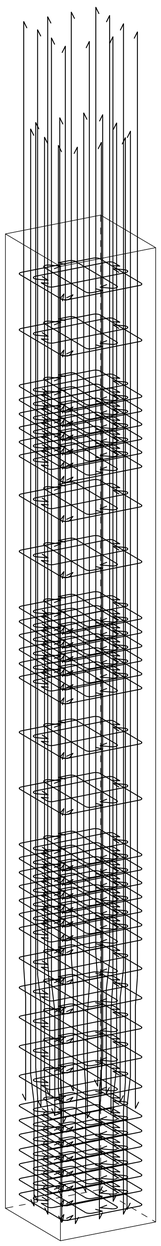


3D VIEW
SCALE : 1:20

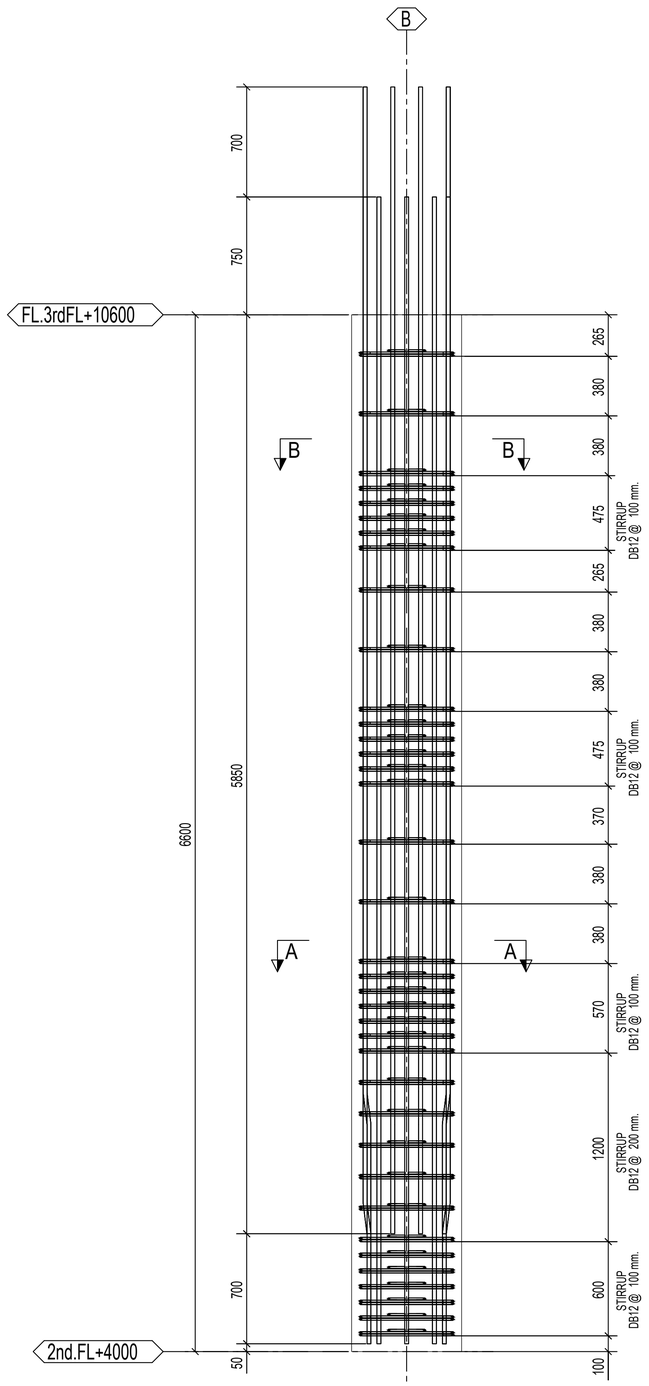

ELEVATION VIEW
SCALE : 1:20

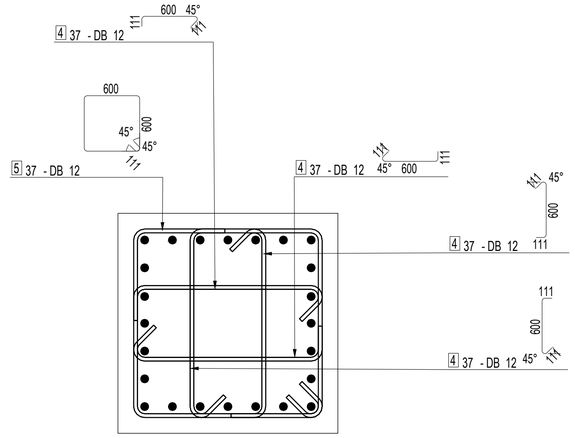

SECTION B - B
SCALE : 1:10

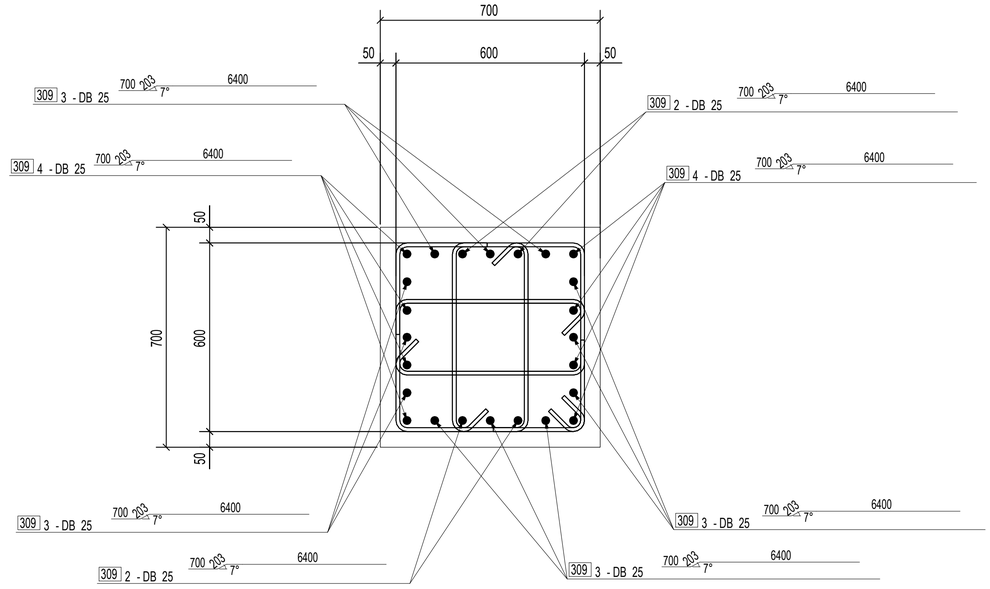

SECTION A - A
SCALE : 1:10

REV.	DESCRIPTION	AUTHOR	CHK.	APPR.	DATE
0A	ISSUED FOR CONSTRUCTION	WNS.	SP./TK.	TNP.	15 AUG 2026

CLIENT NAME : GULF MTP LNG TERMINAL COMPANY LIMITED

CONTRACTOR : POSCO E&C / CAZ CONSORTIUM

GENERATED BY : P PROFESSIONAL ENGINEERING CO.,LTD

DRAWING TITLE :
GULF MTP LNG RECEIVING TERMINAL PROJECT
INSTRUMENT & SUBSTATION BUILDING
COLUMN No. 2C1-103

DWG NO :	SHEET	REV NO :	SCALE :	SIZE :
GULF-ISB-CU-FL10600-2C1-103	1/1	0A	1:10, 1:20	A1