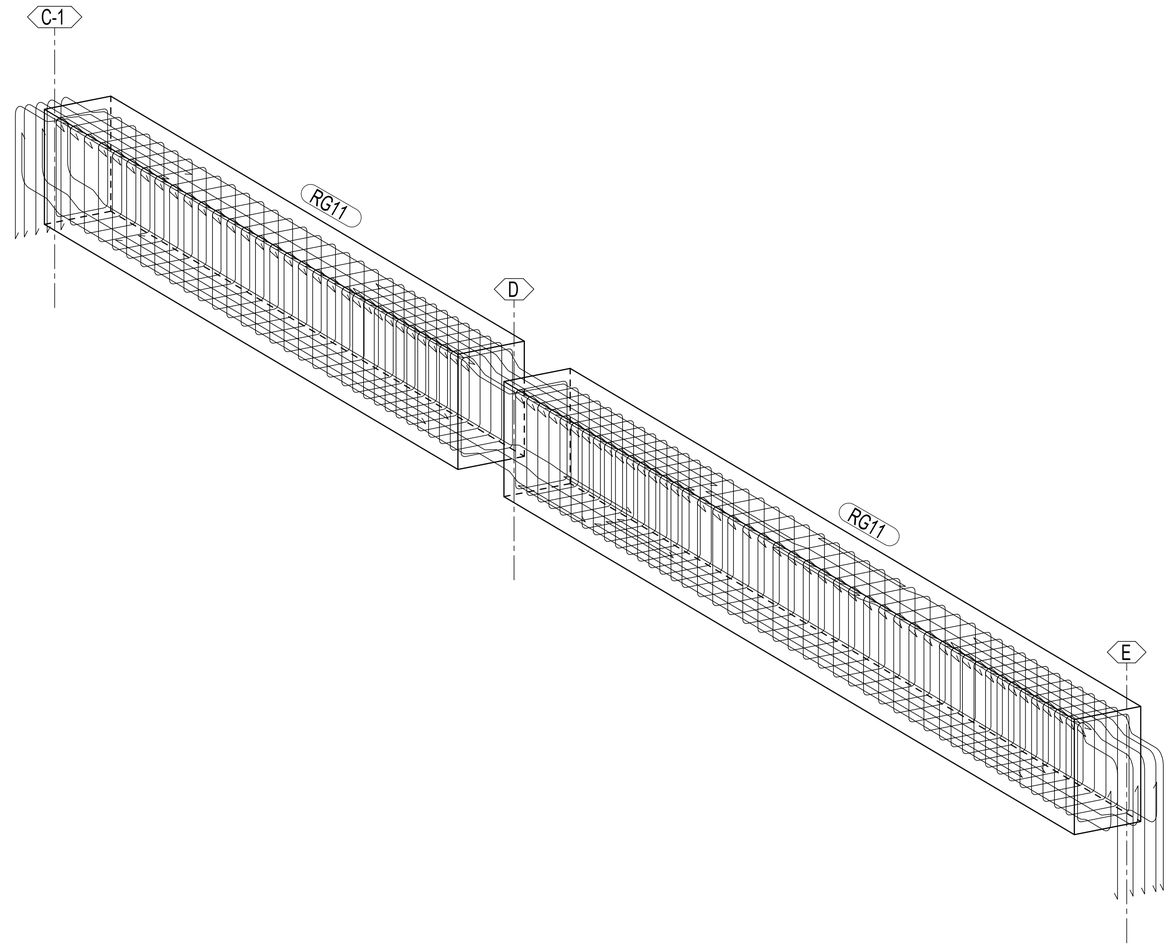


3D VIEW
SCALE : 1:20

REBAR BENDING SCHEDULE

Pos	Diameter	Q'ty	Grade	Length	Kg/p	Weight	Bending shape
363	25	2	SD40	4050	15.61	31.22	4050
364	25	2	SD40	5590	21.54	43.09	5590
376	25	2	SD40	4470	17.23	34.45	1572 166 22° 166 404 22° 2187
513	25	2	SD40	2800	10.79	21.58	957 429 20° 20° 16A 1327
515	25	2	SD40	3310	12.76	25.51	1817 164 20° 429 972
516	25	2	SD40	8100	31.22	62.43	7352 26° 173 344 312
517	25	1	SD40	7220	27.83	27.83	6472 20° 164 343 312
518	25	1	SD40	11960	46.09	46.09	957 16A 429 20° 5304 167 23° 157 404 4467 23°
519	25	1	SD40	11960	46.09	46.09	957 16A 429 20° 5304 166 22° 165 404 3327 22°
520	25	1	SD40	10820	41.70	41.70	957 16A 429 20° 5304 166 22° 165 404 3327 22°
521	25	1	SD40	6660	25.67	25.67	7° 1140 203 3828 20° 164 429 972
522	25	2	SD40	5530	21.31	42.63	7° 1140 203 2688 26° 173 430 972
523	25	1	SD40	7690	29.64	29.64	357 343 164 20° 5304 20° 163 403 12° 156 881
524	25	1	SD40	7690	29.64	29.64	357 343 164 20° 5304 20° 163 403 12° 156 881
525	25	1	SD40	8570	33.03	33.03	357 343 164 20° 5304 18° 153 403 9° 154 1761
28	12	77	SD40	2340	2.08	160.00	111 700 400
					Total:	700.60	

REV.	DESCRIPTION	AUTHOR	CHK.	APPR.	DATE
0A	ISSUED FOR CONSTRUCTION	TKW.	SP./WS.	TNP.	07 AUG 2026


CLIENT NAME : GULF MTP LNG TERMINAL COMPANY LIMITED

CONTRACTOR : POSCO E&C / CAZ CONSORTIUM


GENERATED BY : P PROFESSIONAL ENGINEERING CO.,LTD

DRAWING TITLE :
GULF MTP LNG RECEIVING TERMINAL PROJECT
INSTRUMENT & SUBSTATION BUILDING
2nd BEAM GL.2


DWG NO :	SHEET	REV NO :	SCALE :	SIZE :
GULF-ISB-CU-FL4000-B-101	1/4	0A	1:20	A1

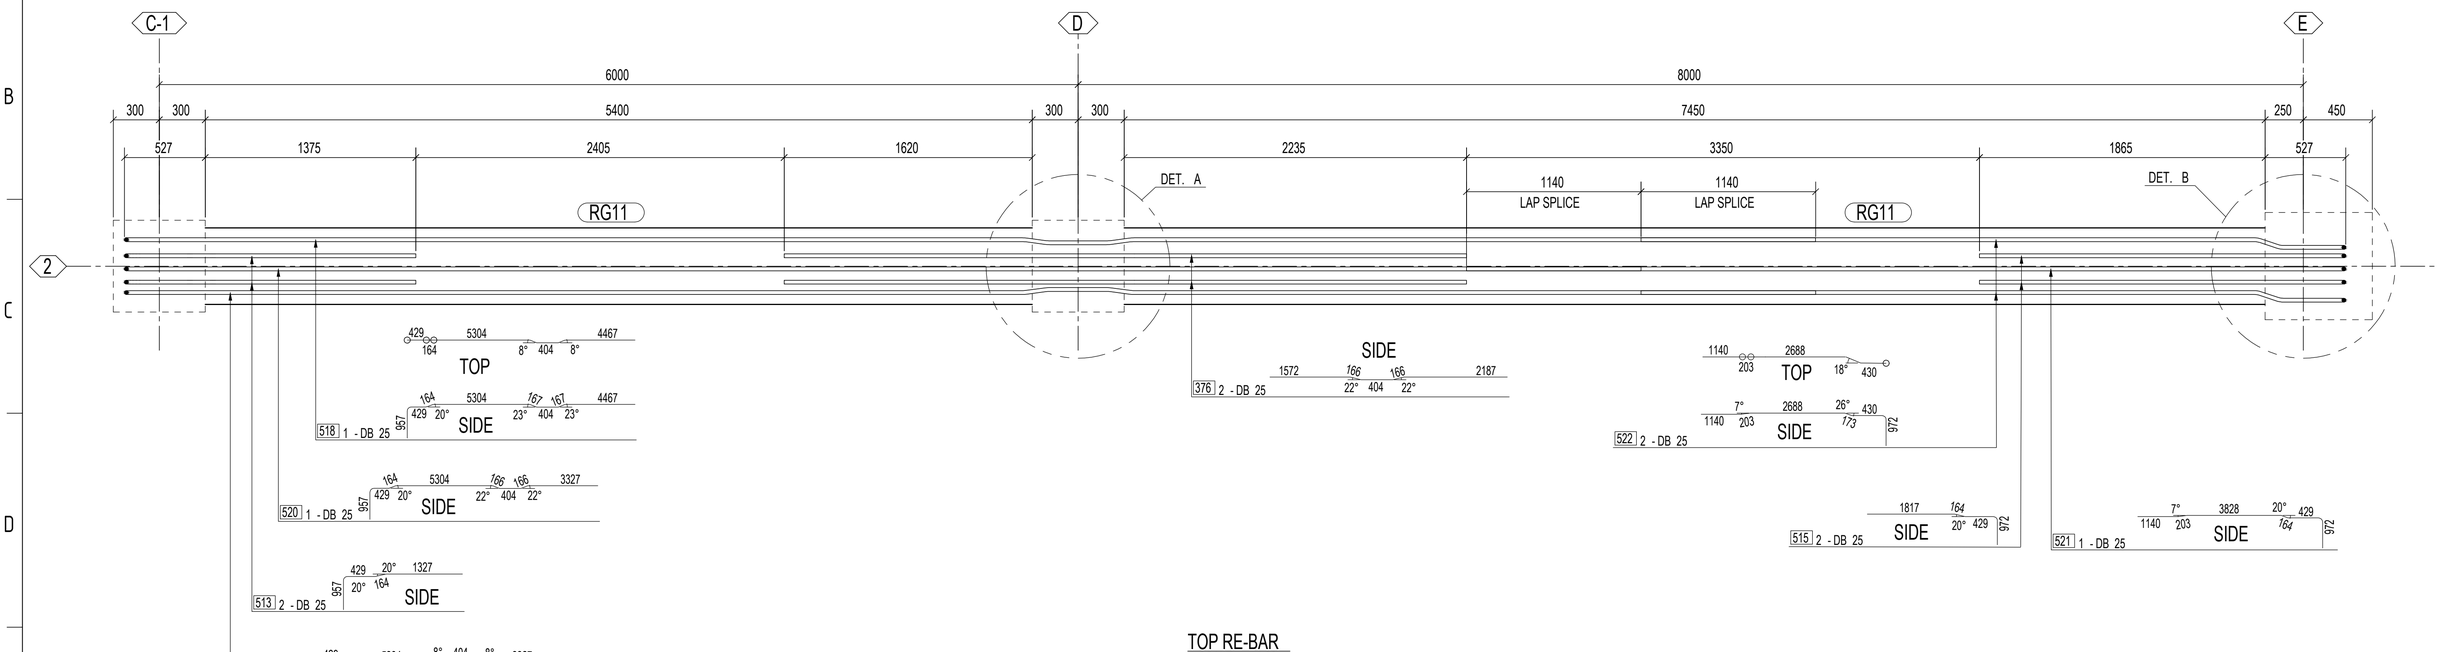

TOP RE-BAR
SCALE : 1:20

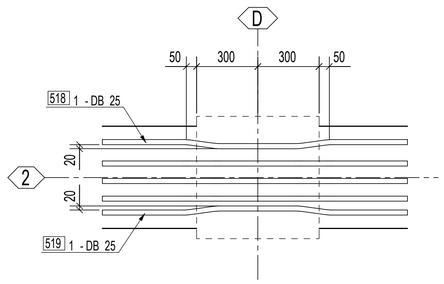

DETAIL A
SCALE : 1:15

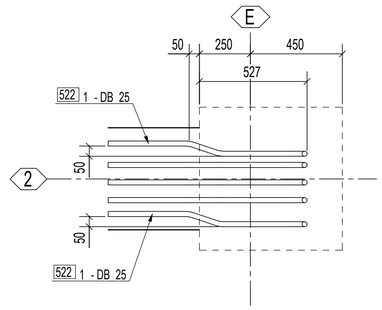

DETAIL B
SCALE : 1:15

REV.	DESCRIPTION	AUTHOR	CHK.	APPR.	DATE
0A	ISSUED FOR CONSTRUCTION	TKW.	SP./WS.	TNP.	07 AUG 2026


CLIENT NAME : GULF MTP LNG TERMINAL COMPANY LIMITED

CONTRACTOR : POSCO E&C / CAZ CONSORTIUM


GENERATED BY : P PROFESSIONAL ENGINEERING CO.,LTD

DRAWING TITLE :
GULF MTP LNG RECEIVING TERMINAL PROJECT
INSTRUMENT & SUBSTATION BUILDING
2nd BEAM GL.2


DWG NO :	SHEET	REV NO :	SCALE :	SIZE :
GULF-ISB-CU-FL4000-B-101	2/4	0A	1:15, 1:20	A1

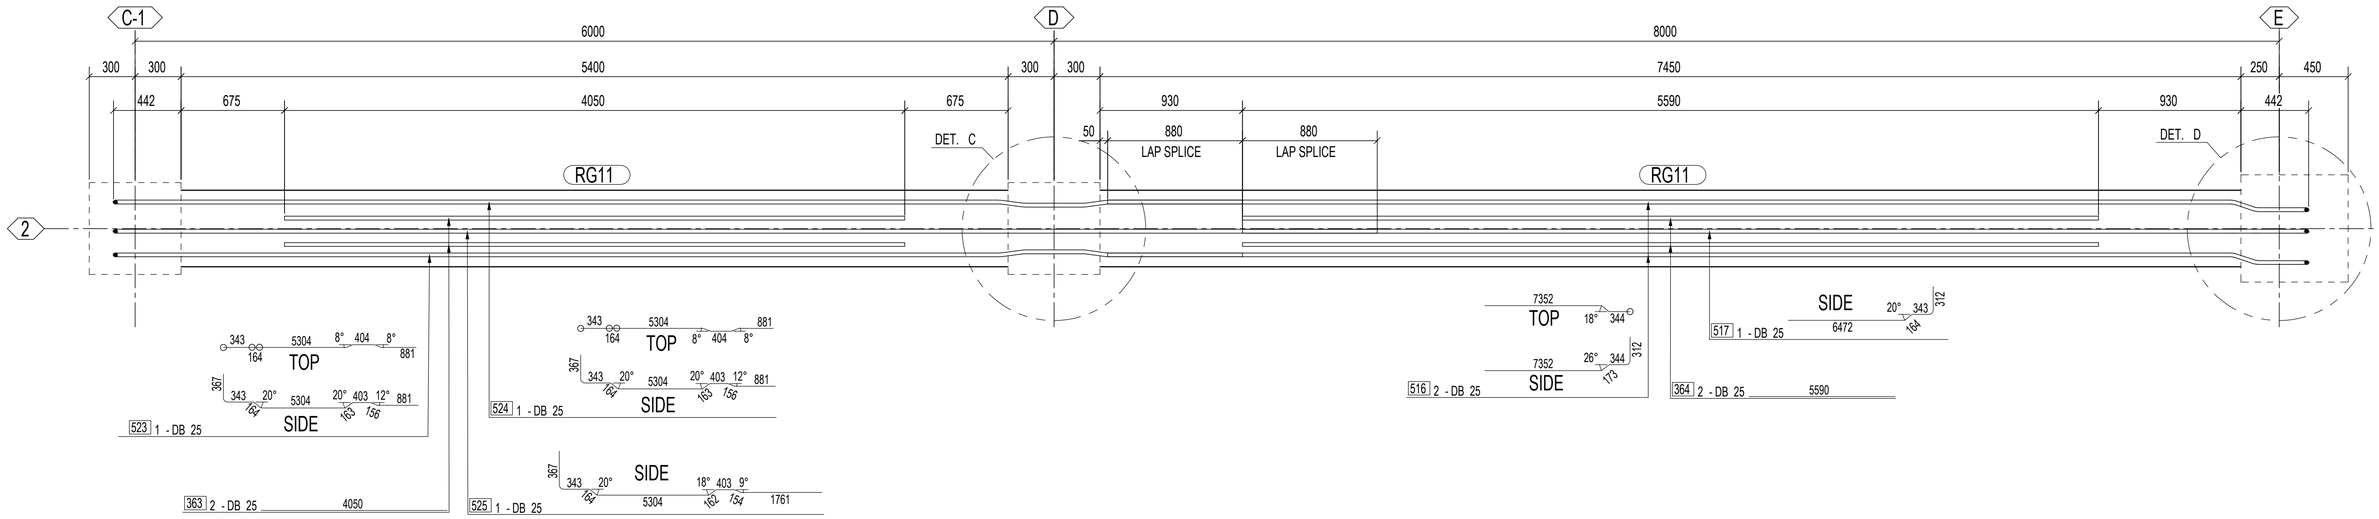

BOTTOM RE-BAR
SCALE : 1:20

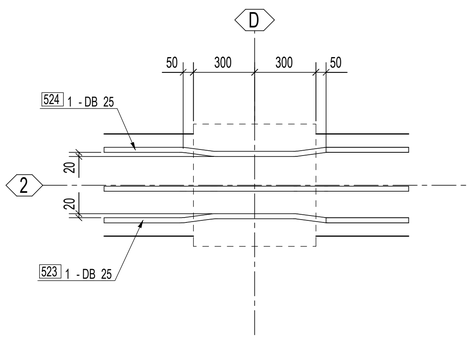

DETAIL C
SCALE : 1:15

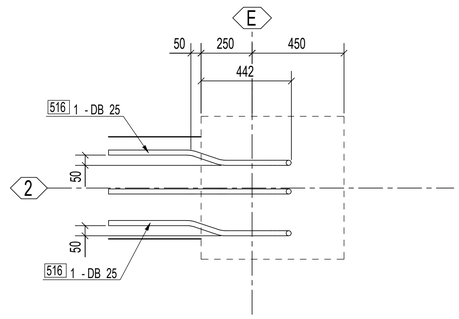

DETAIL D
SCALE : 1:15

REV.	DESCRIPTION	AUTHOR	CHK.	APPR.	DATE
0A	ISSUED FOR CONSTRUCTION	TKW.	SP./WS.	TNP.	07 AUG 2026


CLIENT NAME : GULF MTP LNG TERMINAL COMPANY LIMITED

CONTRACTOR : POSCO E&C / CAZ CONSORTIUM


GENERATED BY : P PROFESSIONAL ENGINEERING CO.,LTD

DRAWING TITLE :
GULF MTP LNG RECEIVING TERMINAL PROJECT
INSTRUMENT & SUBSTATION BUILDING
2nd BEAM GL.2


DWG NO :	SHEET	REV NO :	SCALE :	SIZE :
GULF-ISB-CU-FL4000-B-101	3/4	0A	1:15, 1:20	A1

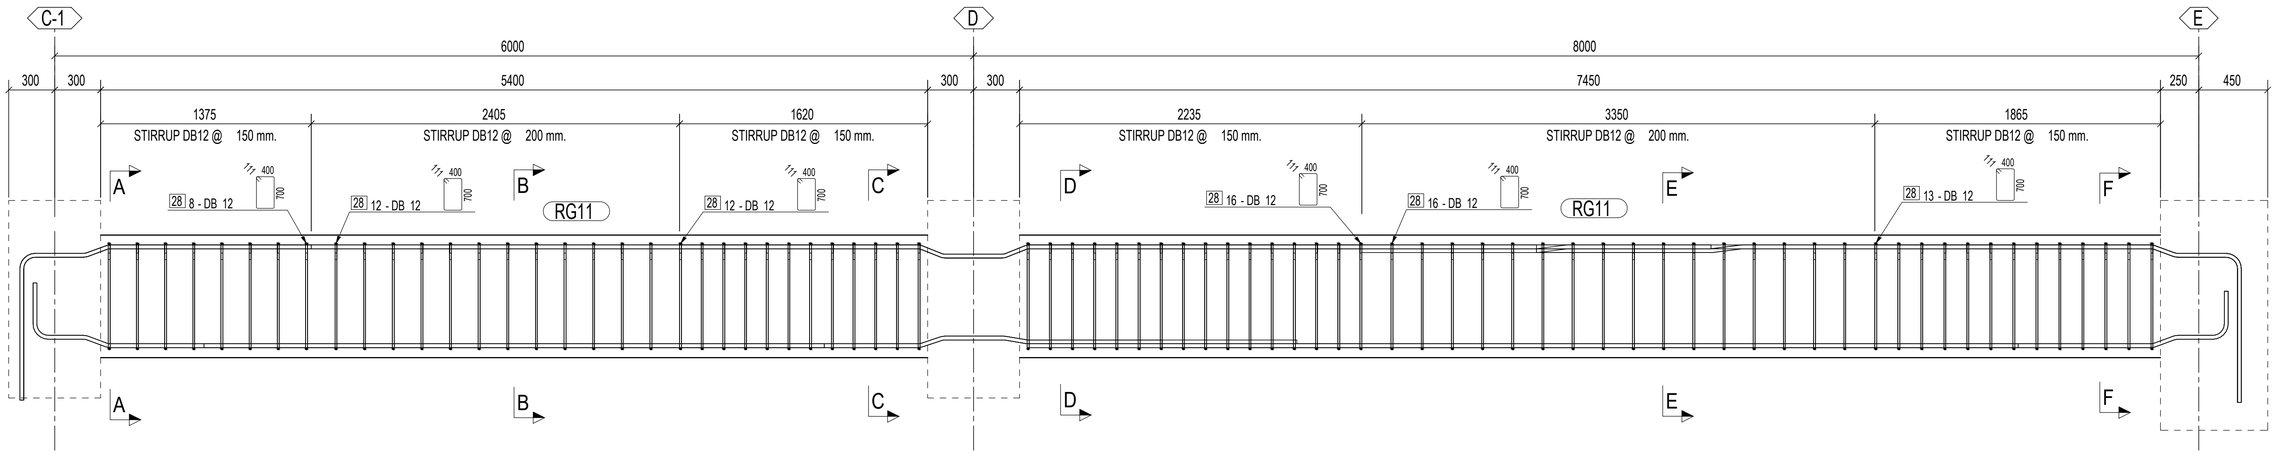


ELEVATION VIEW
SCALE : 1:20

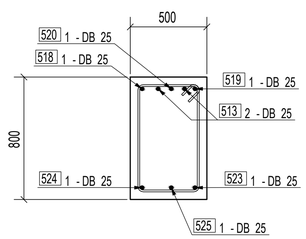


SECTION A - A
SCALE : 1:20

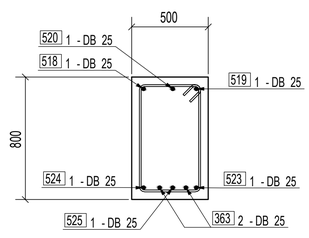


SECTION B - B
SCALE : 1:20

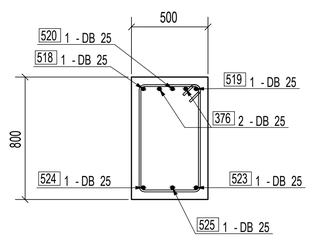


SECTION C - C
SCALE : 1:20

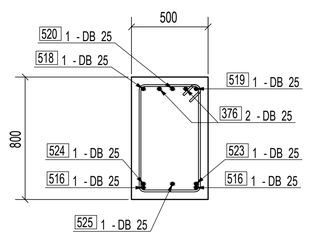

SECTION D - D
SCALE : 1:20

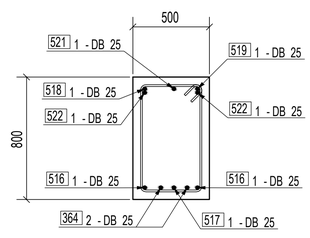

SECTION E - E
SCALE : 1:20

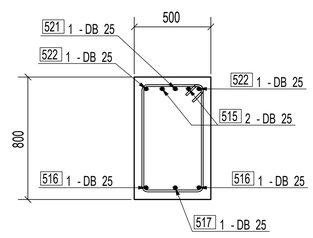

SECTION F - F
SCALE : 1:20

REV.	DESCRIPTION	AUTHOR	CHK.	APPR.	DATE
0A	ISSUED FOR CONSTRUCTION	TKW.	SP./WS.	TNP.	07 AUG 2026

CLIENT NAME : GULF MTP LNG TERMINAL COMPANY LIMITED

CONTRACTOR : POSCO E&C / CAZ CONSORTIUM

GENERATED BY : P PROFESSIONAL ENGINEERING CO.,LTD

DRAWING TITLE :
GULF MTP LNG RECEIVING TERMINAL PROJECT
INSTRUMENT & SUBSTATION BUILDING
2nd BEAM GL.2

DWG NO :	SHEET	REV NO :	SCALE :	SIZE :
GULF-ISB-CU-FL4000-B-101	4/4	0A	1:20	A1