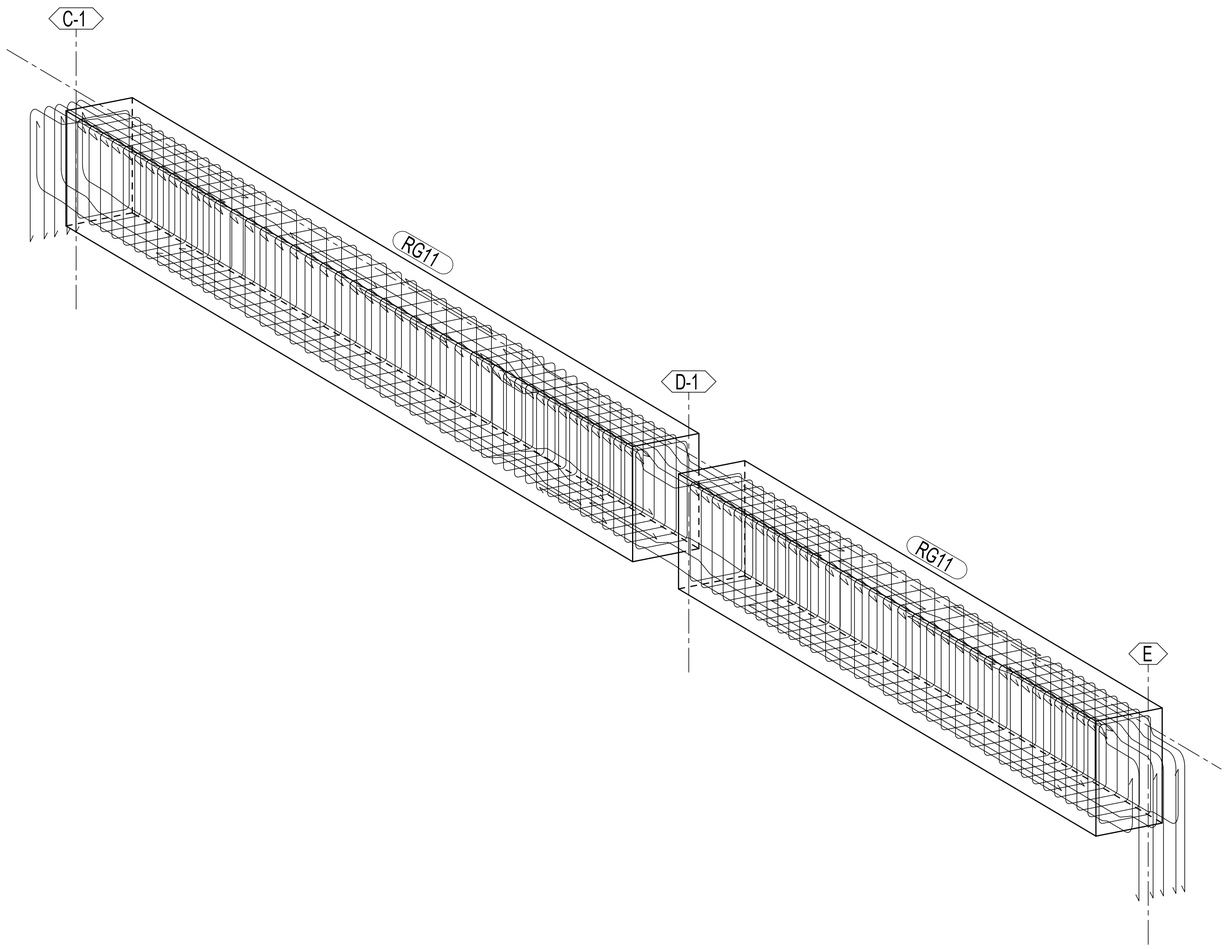


3D VIEW
SCALE : 1:20

REBAR BENDING SCHEDULE

Pos	Diameter	Q'ty	Grade	Length	Kg/p	Weight	Bending shape
474	25	2	SD40	4090	15.76	31.53	4090
276	25	2	SD40	3280	12.64	25.28	1802 164 20° 429 957
279	25	2	SD40	5560	21.43	42.86	477 18° 304 18° 4477 162 162
434	25	1	SD40	8210	31.64	31.64	1351 9° 303 18° 5354 164 343 467 154 162 20°
436	25	2	SD40	6270	24.16	48.33	7° 3453 172 1140 203 26° 430 957
437	25	1	SD40	5170	19.93	19.93	164 2343 7° 972 429 20° 203 1140
438	25	2	SD40	4040	15.57	31.14	173 1203 7° 972 430 26° 203 1140
476	25	2	SD40	8230	31.72	63.44	412 344 26° 5355 25° 405 25° 1302 172 171 171
477	25	1	SD40	7790	30.02	30.02	412 343 20° 18° 404 18° 882 164 5354 162 162
478	25	2	SD40	8350	32.18	64.36	3953 173 175 1355 186 186 1702 28° 406 28° 22° 304 22°
479	25	2	SD40	7800	30.06	60.12	931 9° 303 18° 5354 173 344 467 154 162 26°
512	25	2	SD40	4490	17.30	34.61	1587 186 186 1354 186 186 222 22° 404 22° 22° 304 22°
514	25	2	SD40	2810	10.83	21.66	164 1317 972 429 20°
1234	25	1	SD40	5130	19.77	19.77	7° 2313 164 1140 203 20° 429 957
1235	25	1	SD40	8340	32.14	32.14	2812 186 186 1354 186 186 2842 22° 404 22° 22° 304 22°
28	12	79	SD40	2340	2.08	164.16	111 400 700
					Total:	720.98	

REV.	DESCRIPTION	AUTHOR	CHK.	APPR.	DATE
0A	ISSUED FOR CONSTRUCTION	TKW.	SP./WS.	TNP.	07 AUG 2026


CLIENT NAME : GULF MTP LNG TERMINAL COMPANY LIMITED

CONTRACTOR : POSCO E&C / CAZ CONSORTIUM


GENERATED BY : P PROFESSIONAL ENGINEERING CO.,LTD

DRAWING TITLE :
GULF MTP LNG RECEIVING TERMINAL PROJECT
INSTRUMENT & SUBSTATION BUILDING
2nd BEAM GL.2-1


DWG NO :	SHEET	REV NO :	SCALE :	SIZE :
GULF-ISB-CU-FL4000-B-102	1/4	0A	1:20	A1

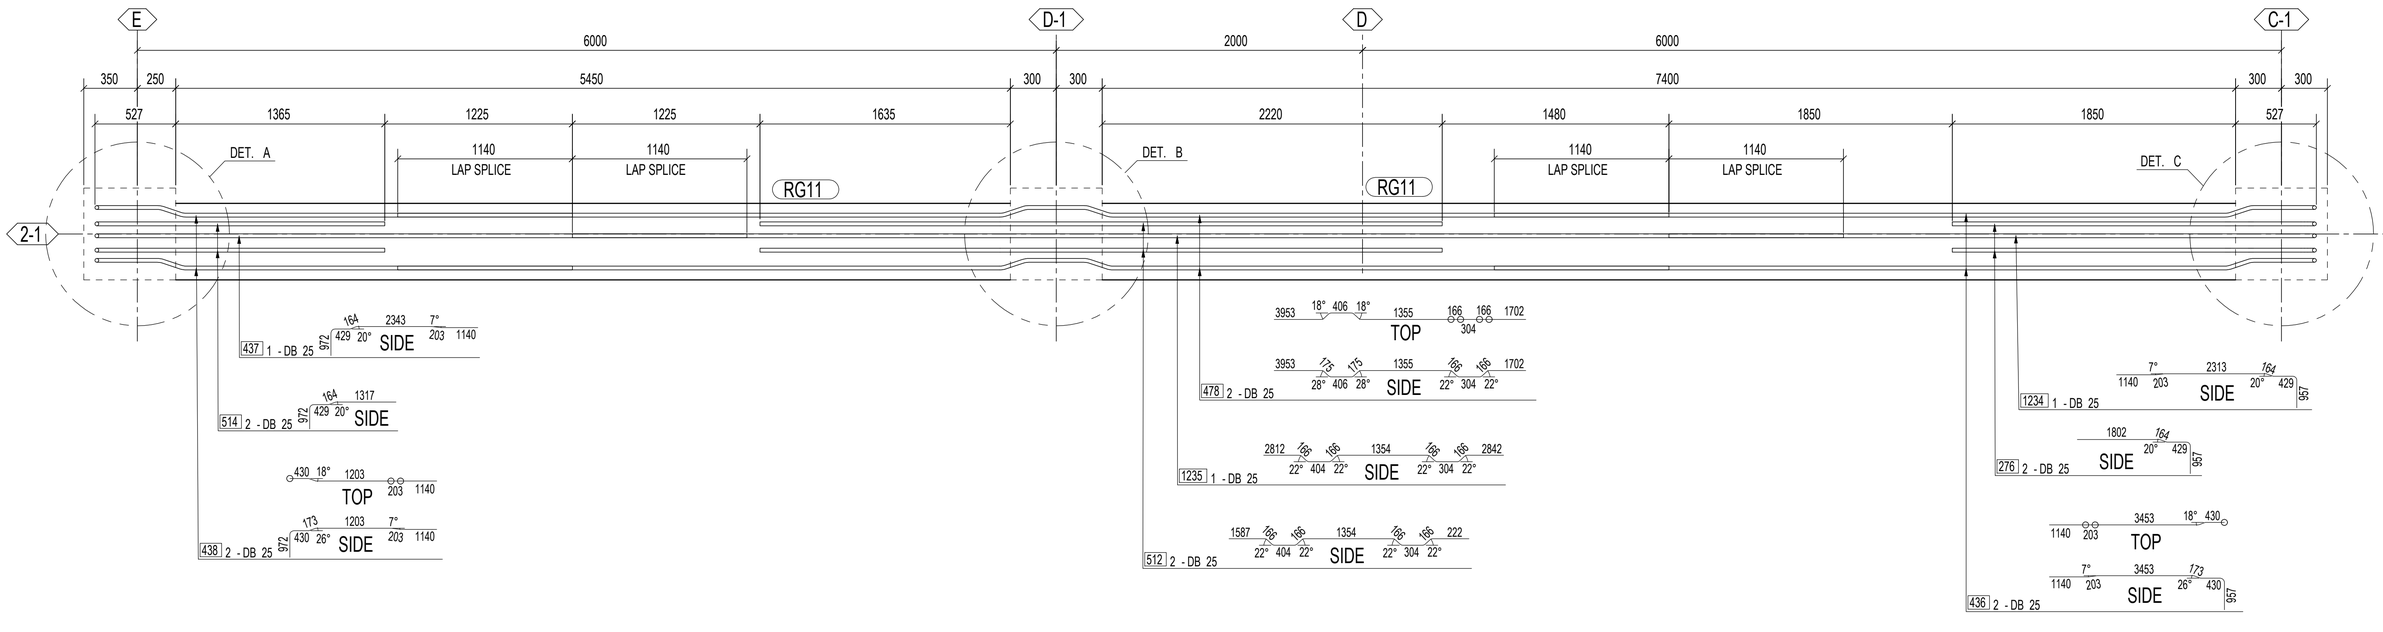


TOP RE-BAR
SCALE : 1:20

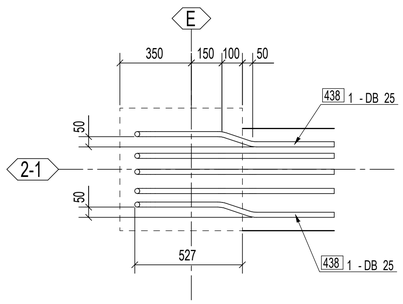

DETAIL A
SCALE : 1:15

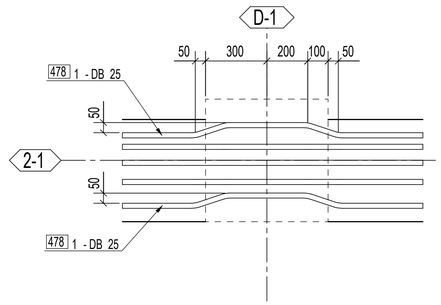

DETAIL B
SCALE : 1:15

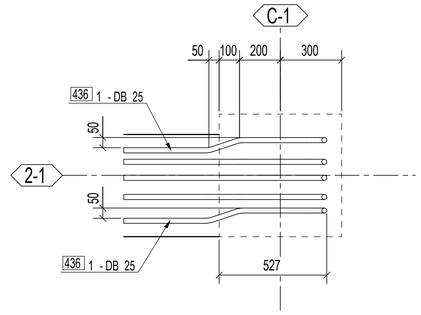

DETAIL C
SCALE : 1:15

REV.	DESCRIPTION	AUTHOR	CHK.	APPR.	DATE
0A	ISSUED FOR CONSTRUCTION	TKW.	SP./WS.	TNP.	07 AUG 2026


CLIENT NAME : GULF MTP LNG TERMINAL COMPANY LIMITED

CONTRACTOR : POSCO E&C / CAZ CONSORTIUM


GENERATED BY : P PROFESSIONAL ENGINEERING CO.,LTD

DRAWING TITLE :
GULF MTP LNG RECEIVING TERMINAL PROJECT
INSTRUMENT & SUBSTATION BUILDING
2nd BEAM GL.2-1


DWG NO :	SHEET	REV NO :	SCALE :	SIZE :
GULF-ISB-CU-FL4000-B-102	2/4	0A	1:15, 1:20	A1

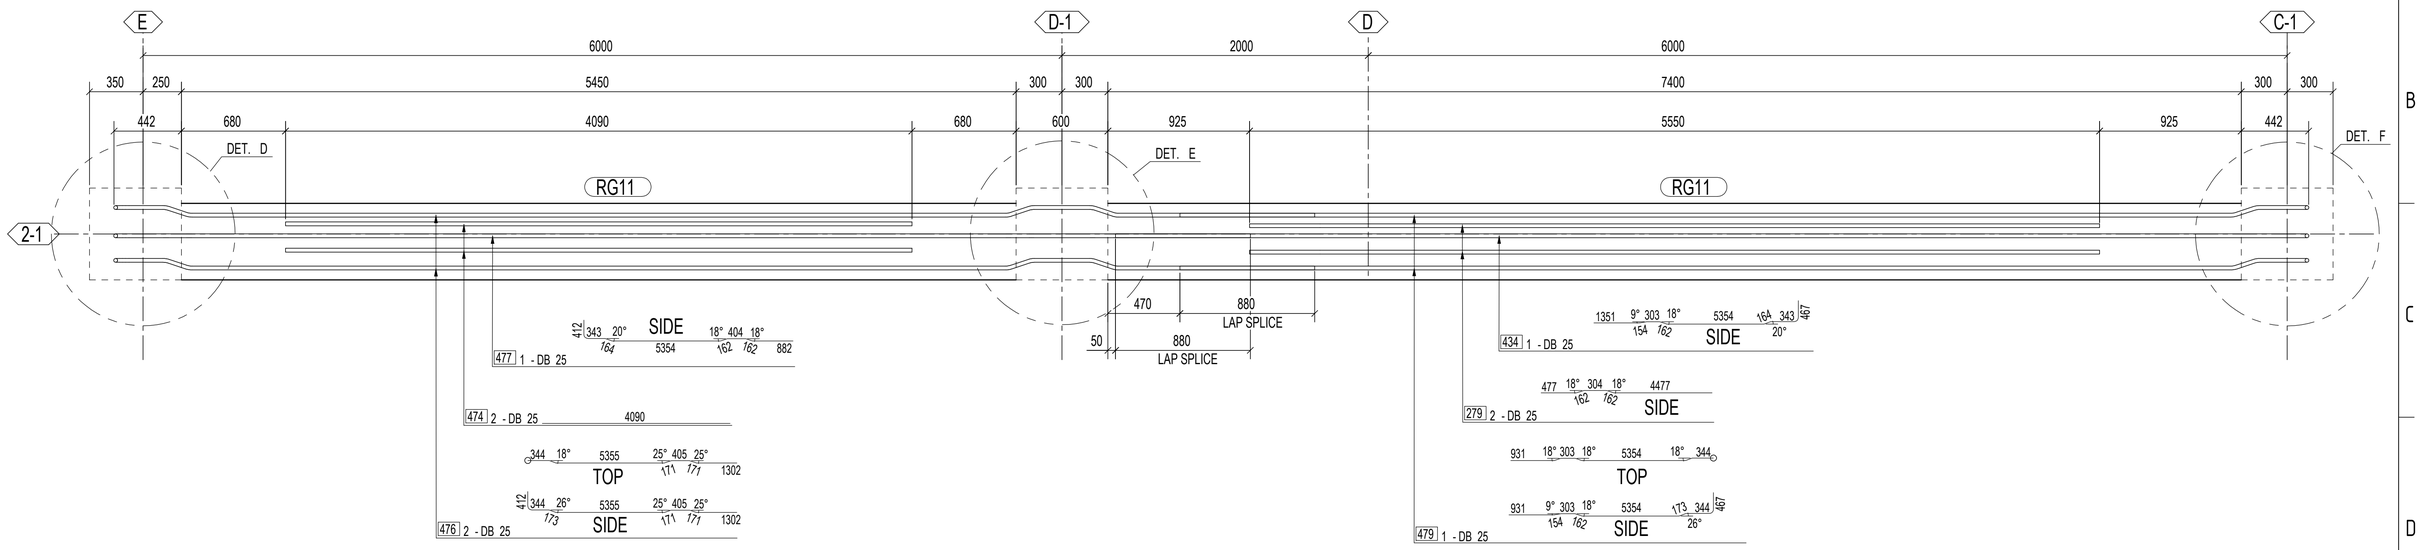


BOTTOM RE-BAR
SCALE : 1:20

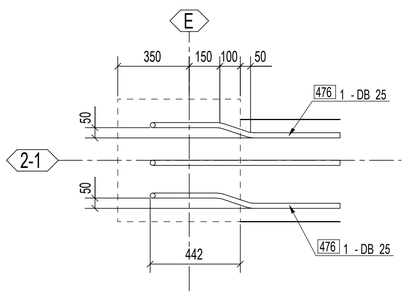

DETAIL D
SCALE : 1:15

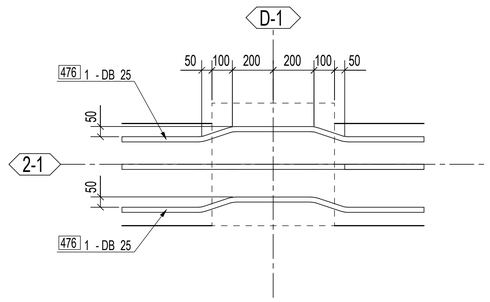

DETAIL E
SCALE : 1:15

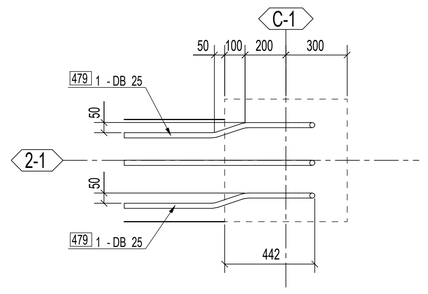

DETAIL F
SCALE : 1:15

REV.	DESCRIPTION	AUTHOR	CHK.	APPR.	DATE
0A	ISSUED FOR CONSTRUCTION	TKW.	SP./WS.	TNP.	07 AUG 2026


CLIENT NAME : GULF MTP LNG TERMINAL COMPANY LIMITED

CONTRACTOR : POSCO E&C / CAZ CONSORTIUM


GENERATED BY : P PROFESSIONAL ENGINEERING CO.,LTD

DRAWING TITLE :
GULF MTP LNG RECEIVING TERMINAL PROJECT
INSTRUMENT & SUBSTATION BUILDING
2nd BEAM GL.2-1


DWG NO :	SHEET	REV NO :	SCALE :	SIZE :
GULF-ISB-CU-FL4000-B-102	3/4	0A	1:15, 1:20	A1

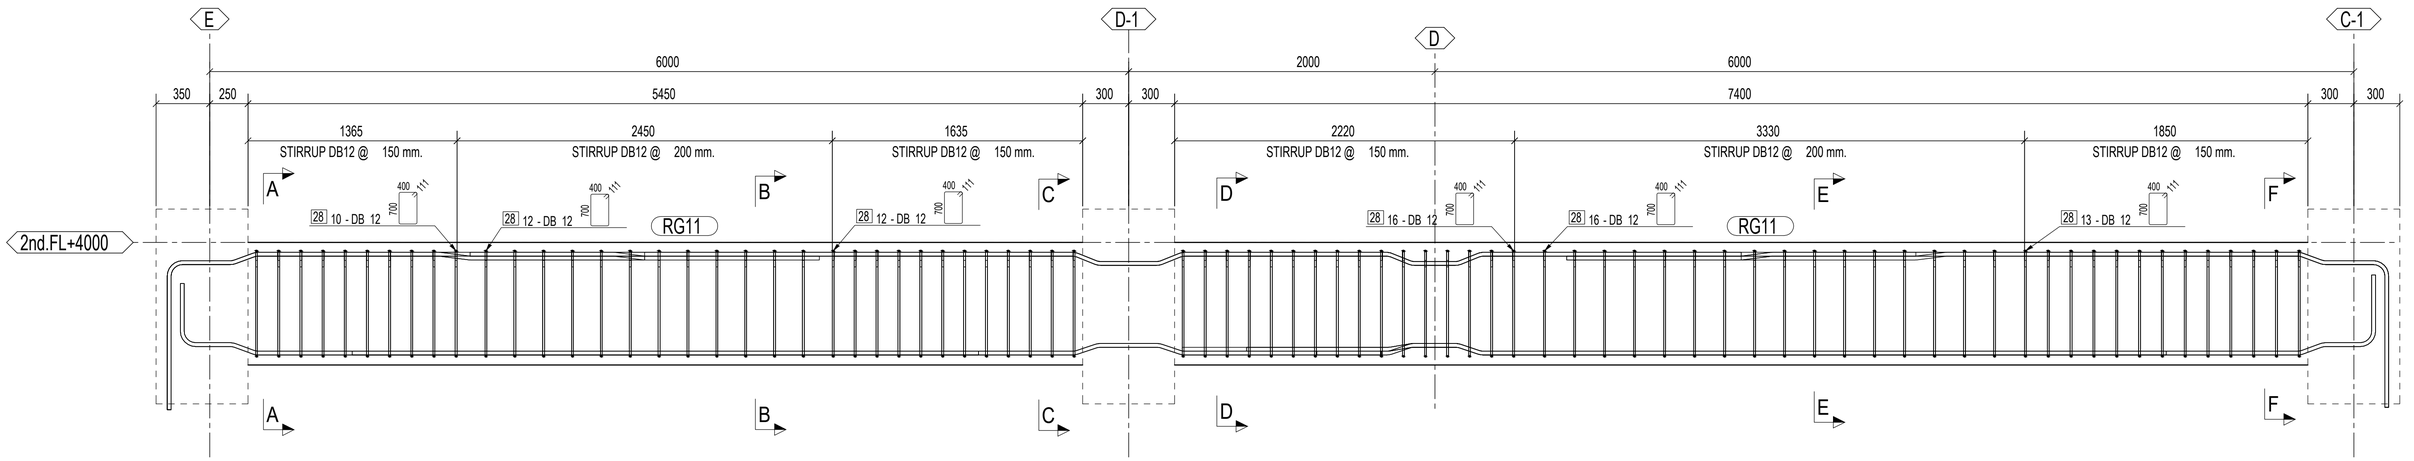


ELEVATION VIEW
SCALE : 1:20

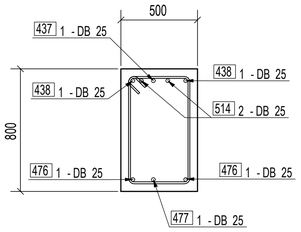


SECTION A - A
SCALE : 1:20

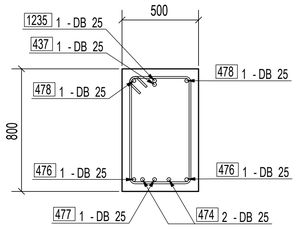


SECTION B - B
SCALE : 1:20

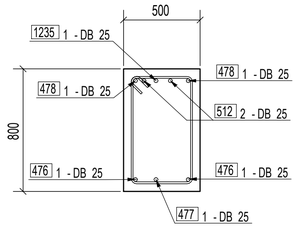


SECTION C - C
SCALE : 1:20

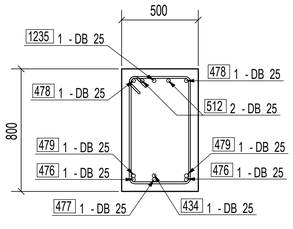

SECTION D - D
SCALE : 1:20

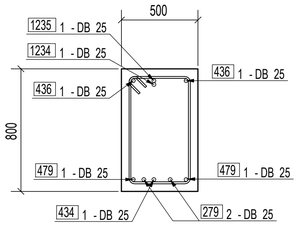

SECTION E - E
SCALE : 1:20

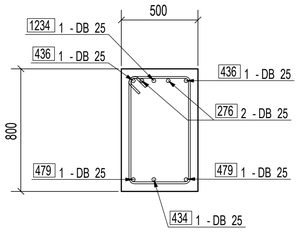

SECTION F - F
SCALE : 1:20

REV.	DESCRIPTION	AUTHOR	CHK.	APPR.	DATE
0A	ISSUED FOR CONSTRUCTION	TKW.	SP./WS.	TNP.	07 AUG 2026

CLIENT NAME : GULF MTP LNG TERMINAL COMPANY LIMITED

CONTRACTOR : POSCO E&C / CAZ CONSORTIUM

GENERATED BY : P PROFESSIONAL ENGINEERING CO.,LTD

DRAWING TITLE :
GULF MTP LNG RECEIVING TERMINAL PROJECT
INSTRUMENT & SUBSTATION BUILDING
2nd BEAM GL.2-1

DWG NO :	SHEET	REV NO :	SCALE :	SIZE :
GULF-ISB-CU-FL4000-B-102	4/4	0A	1:20	A1