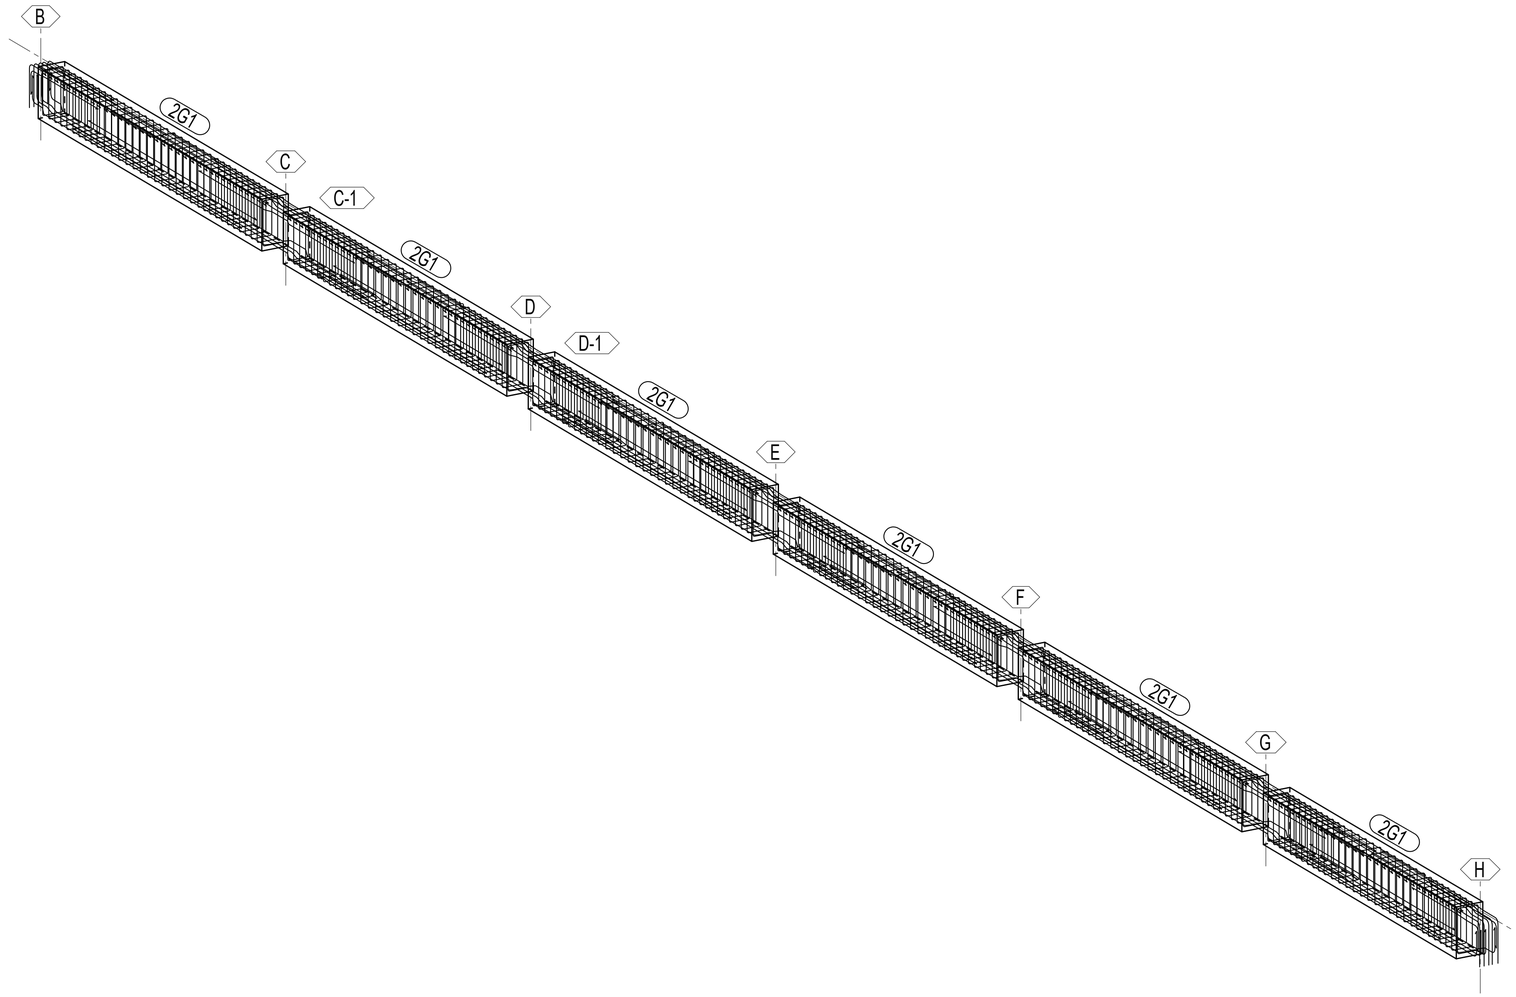


3D VIEW
SCALE : 1:50

REV.	DESCRIPTION	AUTHOR	CHK.	APPR.	DATE
0A	ISSUED FOR CONSTRUCTION	WNS.	SP./TK.	TNP.	31 JUL 2026

CLIENT NAME :
GULF
GULF MTP LNG TERMINAL COMPANY LIMITED

CONTRACTOR :
posco E&C / CAZ CONSORTIUM

GENERATED BY :
P PROFESSIONAL ENGINEERING CO.,LTD

DRAWING TITLE :
GULF MTP LNG RECEIVING TERMINAL PROJECT
INSTRUMENT & SUBSTATION BUILDING
2nd BEAM GL.4,5,6,7,8,9,10,11,12

DWG NO :	SHEET	REV NO :	SCALE :	SIZE :
GULF-ISB-CU-FL4000-B-104	1/19	0A	1:50	A1

REBAR BENDING SCHEDULE

Pos	Diameter	Number	Grade	Length	Kg/p	Weight	Bending shape
56	25	15	SD40	5480	21.12	316.80	5480
153	25	3	SD40	4730	18.23	54.69	4730
44	25	12	SD40	5100	19.66	235.86	2142, 166, 166, 2142, 22° 504 22°
125	25	3	SD40	4800	18.50	55.50	2142, 166, 166, 1842, 22° 504 22°
234	25	1	SD40	11120	42.86	42.86	467, 340, 28°, 7206, 28°, 506, 28°, 177, 177, 177, 2183
235	25	1	SD40	7100	27.36	27.36	1090, 203, 7°, 4913, 20°, 339, 467, 164
236	25	1	SD40	6020	23.20	23.20	1090, 203, 7°, 3823, 28°, 340, 467, 177
237	25	1	SD40	7110	27.40	27.40	1090, 203, 7°, 4913, 28°, 340, 467, 177
238	25	4	SD40	9100	35.07	140.29	1090, 203, 7°, 5912, 18°, 504, 18°, 162, 162, 1092
239	25	4	SD40	9120	35.15	140.59	1090, 203, 7°, 4823, 28°, 506, 28°, 177, 177, 2183
240	25	4	SD40	9120	35.15	140.59	1090, 203, 7°, 5913, 28°, 506, 28°, 177, 177, 1093
241	25	4	SD40	9100	35.07	140.29	1090, 203, 7°, 4822, 18°, 504, 18°, 162, 162, 2182
242	25	1	SD40	3250	12.53	12.53	164, 1777, 947, 439, 20°
243	25	2	SD40	2700	10.41	20.81	177, 1778, 437, 390, 28°
246	25	2	SD40	2450	9.44	18.88	1528, 177, 28°, 390, 437
248	25	1	SD40	5080	19.58	19.58	164, 1983, 7°, 7°, 947, 439, 20°, 203, 1420
249	25	1	SD40	5090	19.62	19.62	177, 1983, 203, 1420, 947, 440, 28°, 7°
250	25	1	SD40	6510	25.09	25.09	177, 3403, 203, 1420, 947, 440, 28°, 7°
251	25	2	SD40	9440	36.38	72.76	5022, 166, 166, 3602, 22° 504 22°
253	25	4	SD40	9460	36.46	145.84	3603, 178, 178, 5023, 29° 506 29°

Pos	Diameter	Number	Grade	Length	Kg/p	Weight	Bending shape
254	25	2	SD40	9440	36.38	72.76	1420, 203, 7°, 3403, 22°, 504, 22°, 166, 166, 1983, 7°, 203, 1420
255	25	1	SD40	8940	34.45	34.45	5022, 166, 166, 3102, 22° 504 22°
257	25	2	SD40	9460	36.46	72.92	1420, 203, 7°, 3404, 29°, 506, 29°, 178, 178, 1984, 7°, 203, 1420
259	25	1	SD40	8960	34.53	34.53	5023, 178, 178, 3103, 29° 506 29°
261	25	1	SD40	4590	17.69	17.69	1420, 203, 7°, 1483, 177, 28°, 440, 947
262	25	1	SD40	6010	23.16	23.16	1420, 203, 7°, 2903, 177, 28°, 440, 947
270	25	2	SD40	9440	36.38	72.76	3602, 166, 166, 5022, 22° 504 22°
274	25	2	SD40	9440	36.38	72.76	1420, 203, 7°, 1983, 22°, 504, 22°, 166, 166, 3403, 7°, 203, 1420
275	25	1	SD40	8940	34.45	34.45	3602, 166, 166, 4522, 22° 504 22°
277	25	1	SD40	6010	23.16	23.16	1090, 203, 7°, 3823, 20°, 339, 467, 164
278	25	1	SD40	4580	17.65	17.65	1420, 203, 7°, 1483, 20°, 439, 164, 947
281	25	1	SD40	11090	42.74	42.74	467, 339, 20°, 7204, 18°, 504, 18°, 164, 162, 162, 2182
282	25	1	SD40	6500	25.05	25.05	164, 20°, 3403, 7°, 7°, 947, 439, 20°, 203, 1420
283	25	1	SD40	10000	38.54	38.54	467, 339, 20°, 7204, 18°, 504, 18°, 164, 162, 162, 1092
284	25	1	SD40	10030	38.66	38.66	467, 340, 28°, 7206, 28°, 506, 28°, 177, 177, 177, 1093
323	25	2	SD40	9460	36.46	72.92	1420, 203, 7°, 1984, 29°, 506, 29°, 178, 178, 3404, 7°, 203, 1420
325	25	1	SD40	8960	34.53	34.53	3603, 178, 178, 4523, 29° 506 29°
331	25	1	SD40	3000	11.56	11.56	1527, 20°, 439, 164, 947
334	25	1	SD40	6000	23.12	23.12	1420, 203, 7°, 2903, 20°, 439, 164, 947
27	12	206	SD40	2540	2.26	464.64	111, 400, 800
					Total:	2908.61	

REV.	DESCRIPTION	AUTHOR	CHK.	APPR.	DATE
0A	ISSUED FOR CONSTRUCTION	WNS.	SP./TK.	TNP.	31 JUL 2026

CLIENT NAME : GULF MTP LNG TERMINAL COMPANY LIMITED


CONTRACTOR : POSCO E&C / CAZ CONSORTIUM


GENERATED BY : P PROFESSIONAL ENGINEERING CO.,LTD

DRAWING TITLE :


GULF MTP LNG RECEIVING TERMINAL PROJECT
INSTRUMENT & SUBSTATION BUILDING
2nd BEAM GL.4,5,6,7,8,9,10,11,12

DWG NO :	SHEET	REV NO :	SCALE :	SIZE :
GULF-ISB-CU-FL4000-B-104	2/19	0A	1:NTS	A1

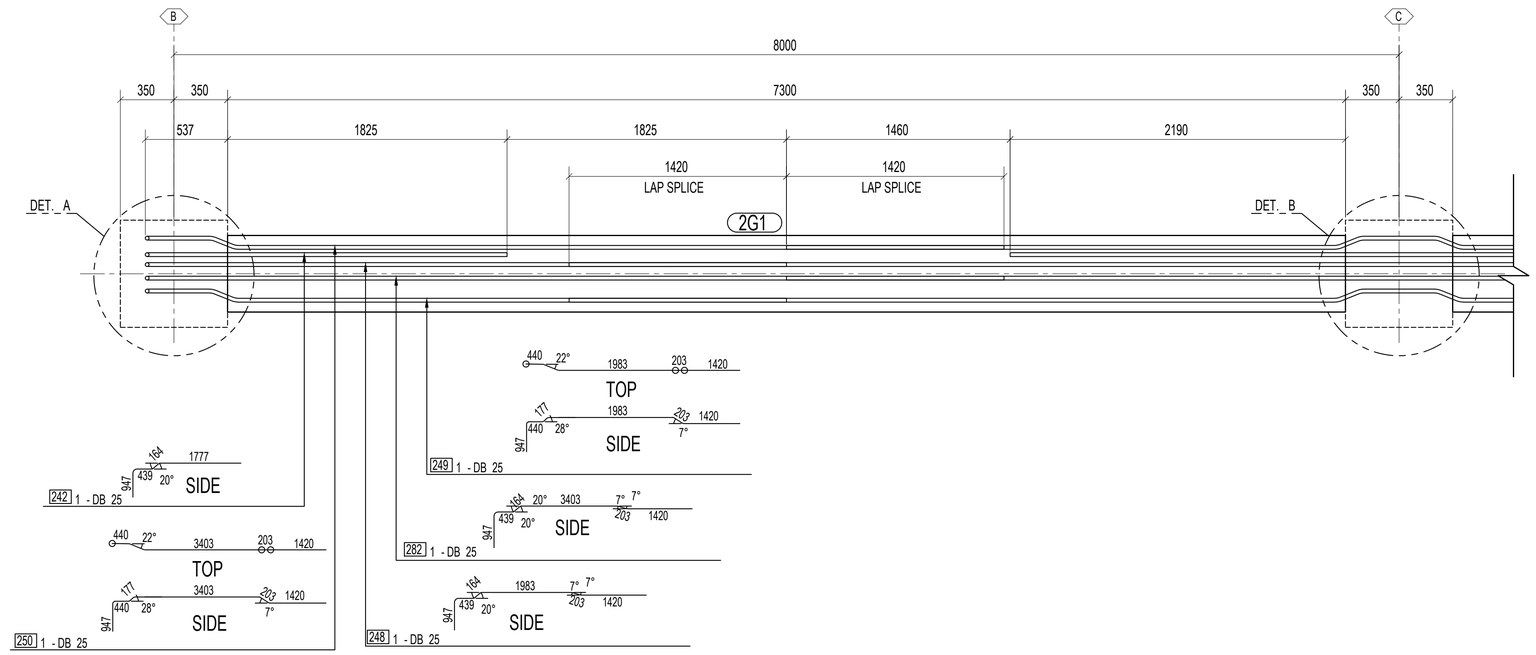


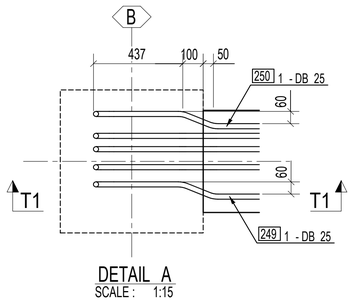


DETAIL A
SCALE : 1:15

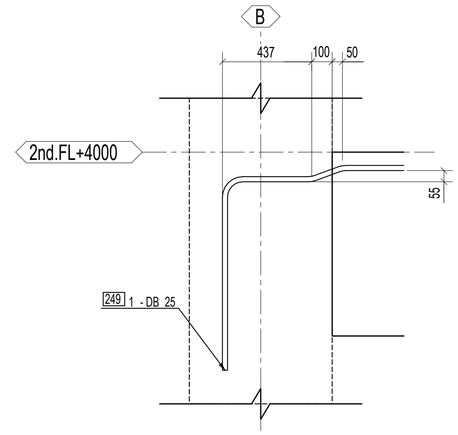


SECTION T1 - T1
SCALE : 1:15

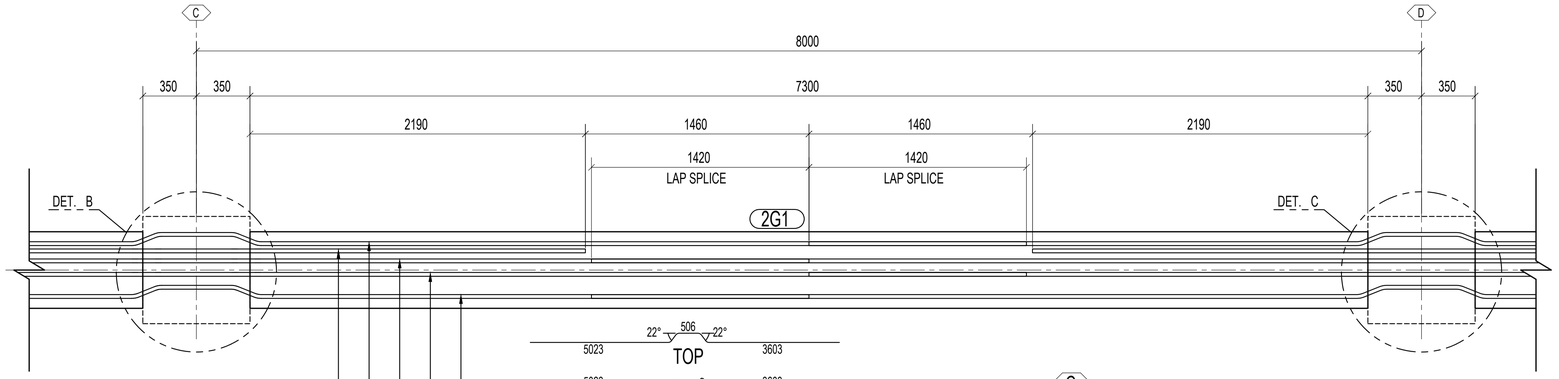

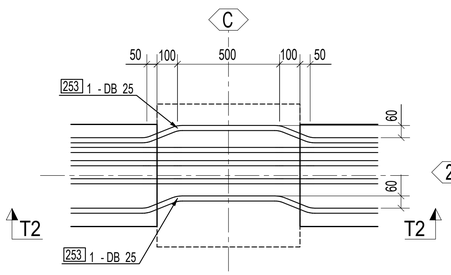

DETAIL B
SCALE : 1:15

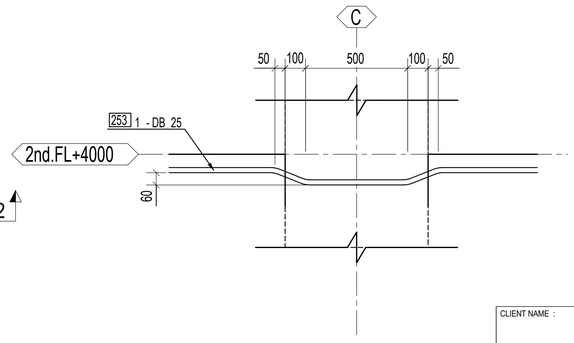

SECTION T2 - T2
SCALE : 1:15

TOP RE-BAR
SCALE : 1:20

REV.	DESCRIPTION	AUTHOR	CHK.	APPR.	DATE
0A	ISSUED FOR CONSTRUCTION	WNS.	SP./TK.	TNP.	31 JUL 2026


CLIENT NAME :
GULF MTP LNG TERMINAL COMPANY LIMITED


CONTRACTOR :
POSCO E&C / CAZ CONSORTIUM

GENERATED BY :
P PROFESSIONAL ENGINEERING CO.,LTD


DRAWING TITLE :
GULF MTP LNG RECEIVING TERMINAL PROJECT
INSTRUMENT & SUBSTATION BUILDING
2nd BEAM GL.4,5,6,7,8,9,10,11,12

DWG NO :	SHEET	REV NO :	SCALE :	SIZE :
GULF-ISB-CU-FL4000-B-104	3/19	0A	1:20,1:50	A1

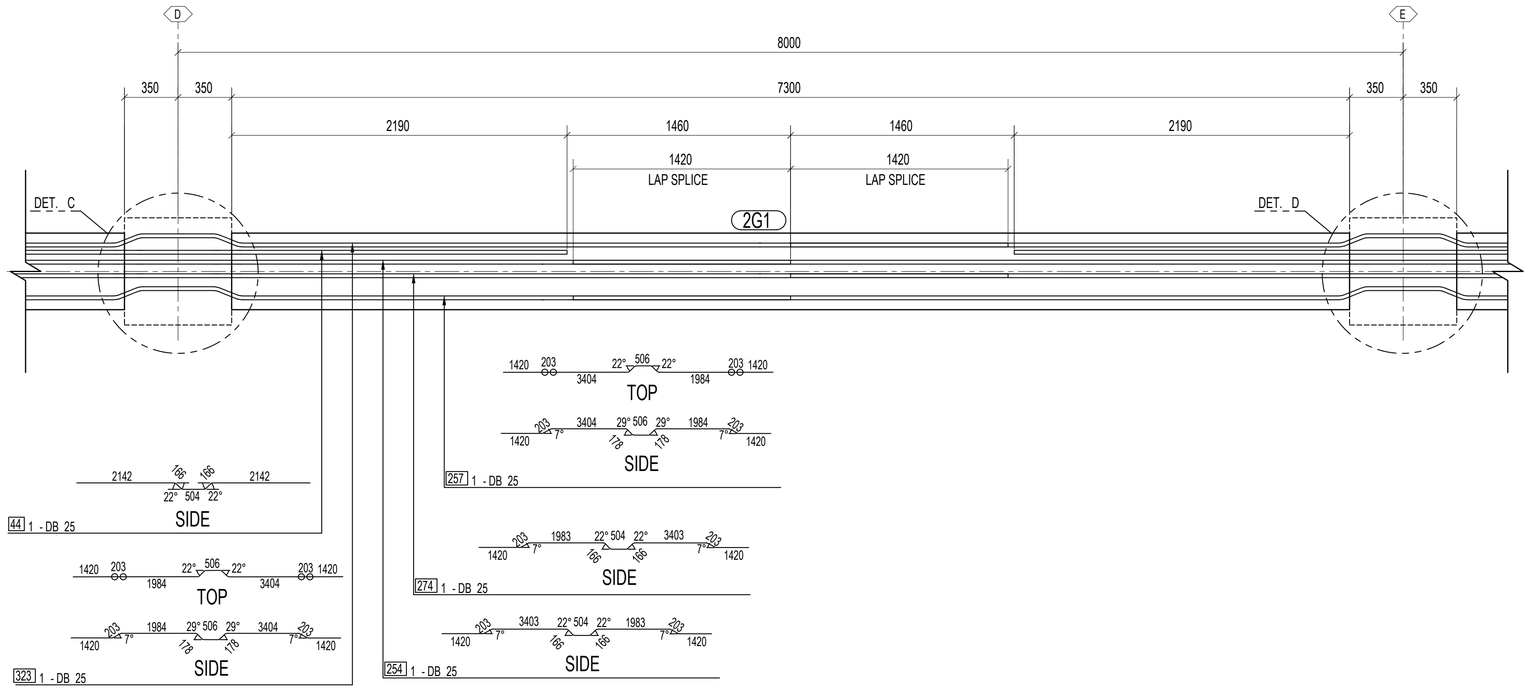


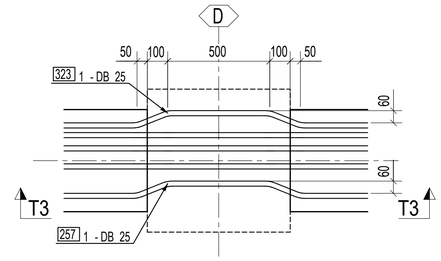


DETAIL C
SCALE : 1:15

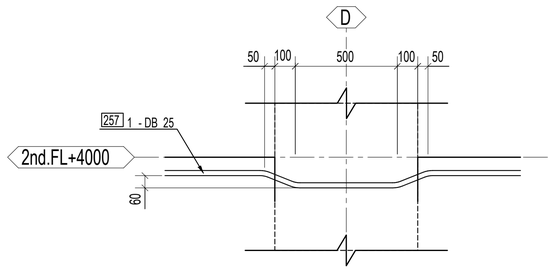


SECTION T3 - T3
SCALE : 1:15

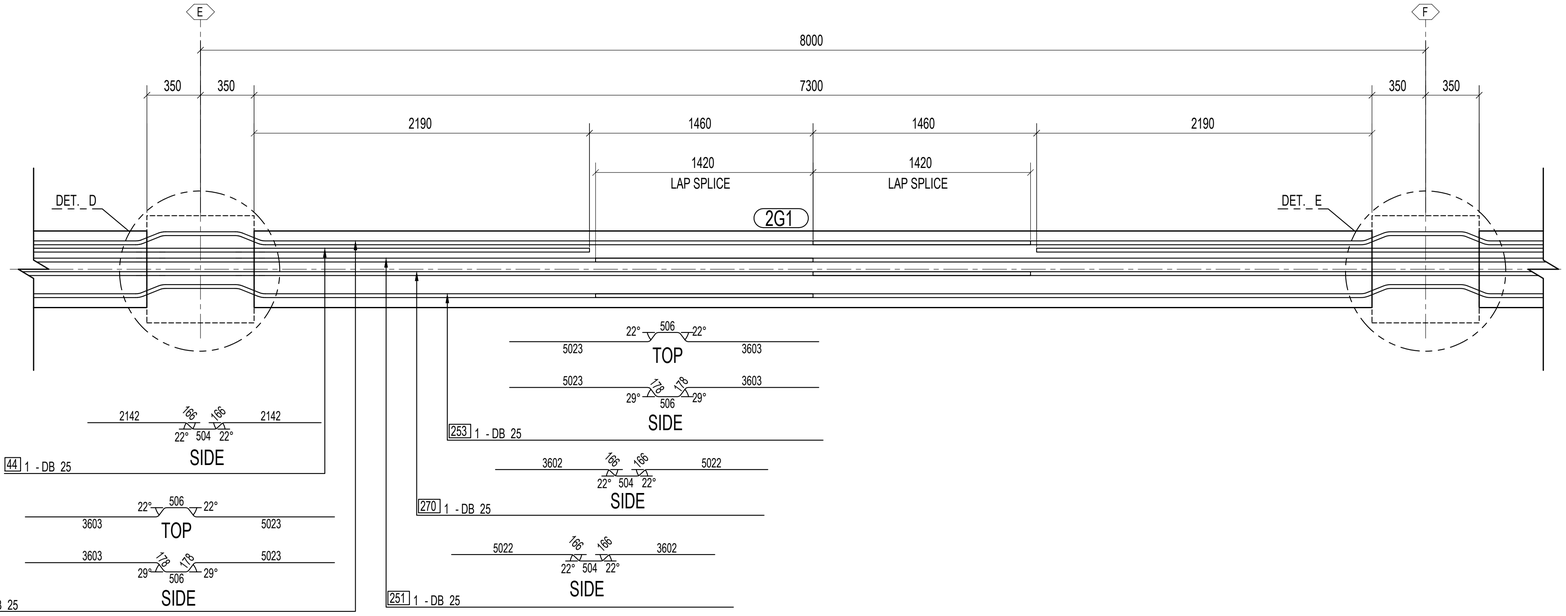

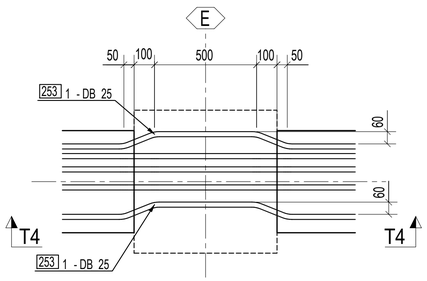

DETAIL D
SCALE : 1:15

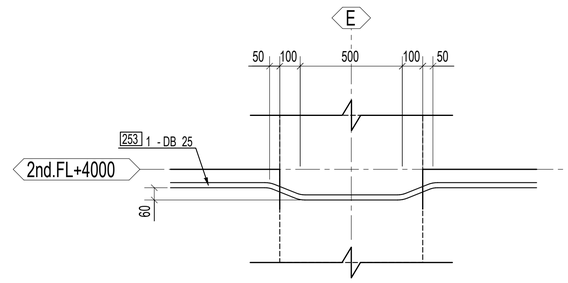

SECTION T4 - T4
SCALE : 1:15

TOP RE-BAR
SCALE : 1:20

REV.	DESCRIPTION	AUTHOR	CHK.	APPR.	DATE
0A	ISSUED FOR CONSTRUCTION	WNS.	SP./TK.	TNP.	31 JUL 2026


CLIENT NAME : GULF MTP LNG TERMINAL COMPANY LIMITED


CONTRACTOR : POSCO E&C / CAZ CONSORTIUM

GENERATED BY : P PROFESSIONAL ENGINEERING CO.,LTD


DRAWING TITLE :
GULF MTP LNG RECEIVING TERMINAL PROJECT
INSTRUMENT & SUBSTATION BUILDING
2nd BEAM GL.4,5,6,7,8,9,10,11,12

DWG NO :	SHEET	REV NO :	SCALE :	SIZE :
GULF-ISB-CU-FL4000-B-104	4/19	0A	1:20,1:50	A1

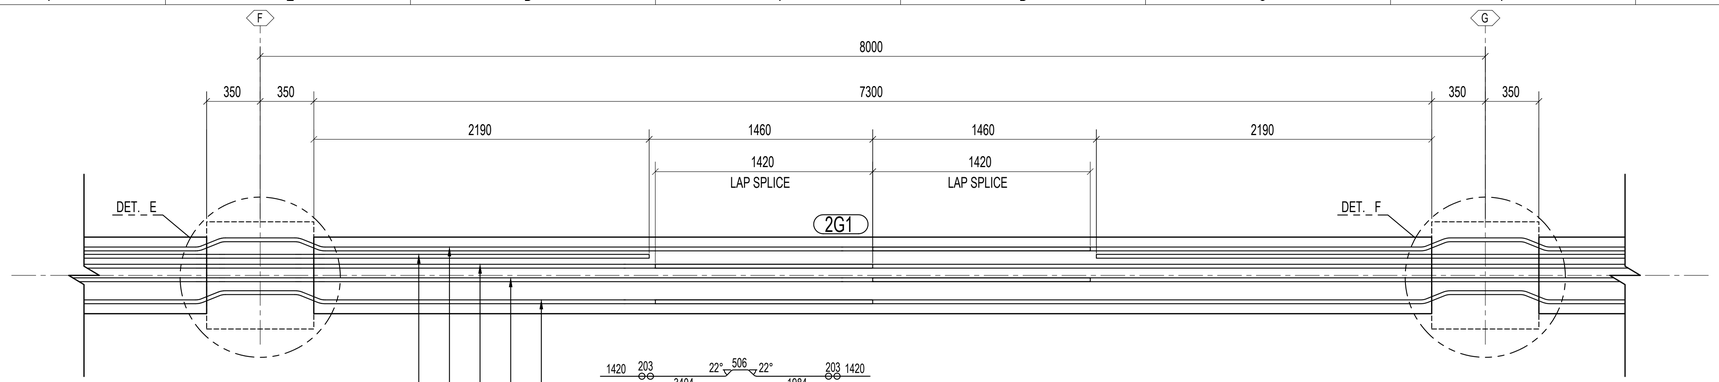


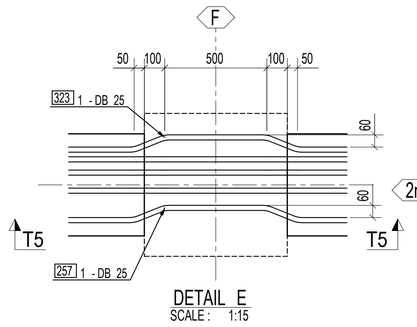


DETAIL E
SCALE : 1:15

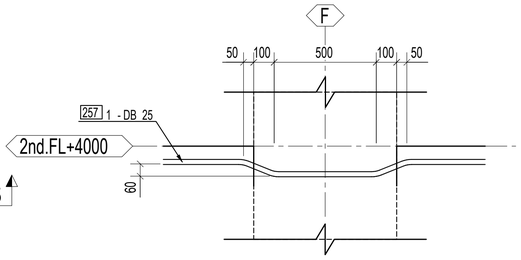


SECTION T5 - T5
SCALE : 1:15

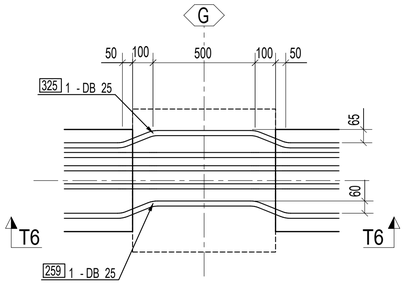


DETAIL F
SCALE : 1:15

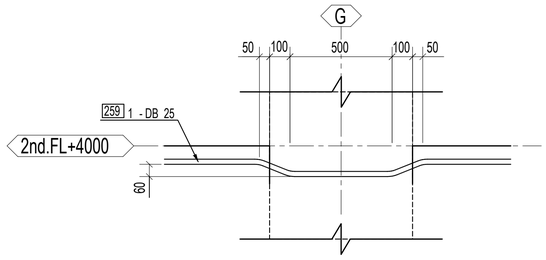


SECTION T6 - T6
SCALE : 1:15

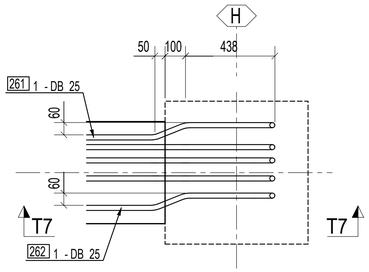

DETAIL G
SCALE : 1:15

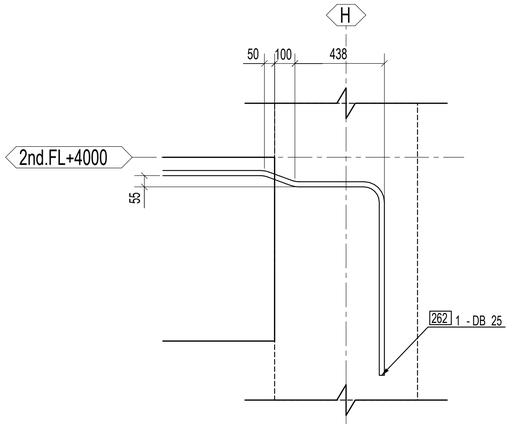

SECTION T7 - T7
SCALE : 1:15

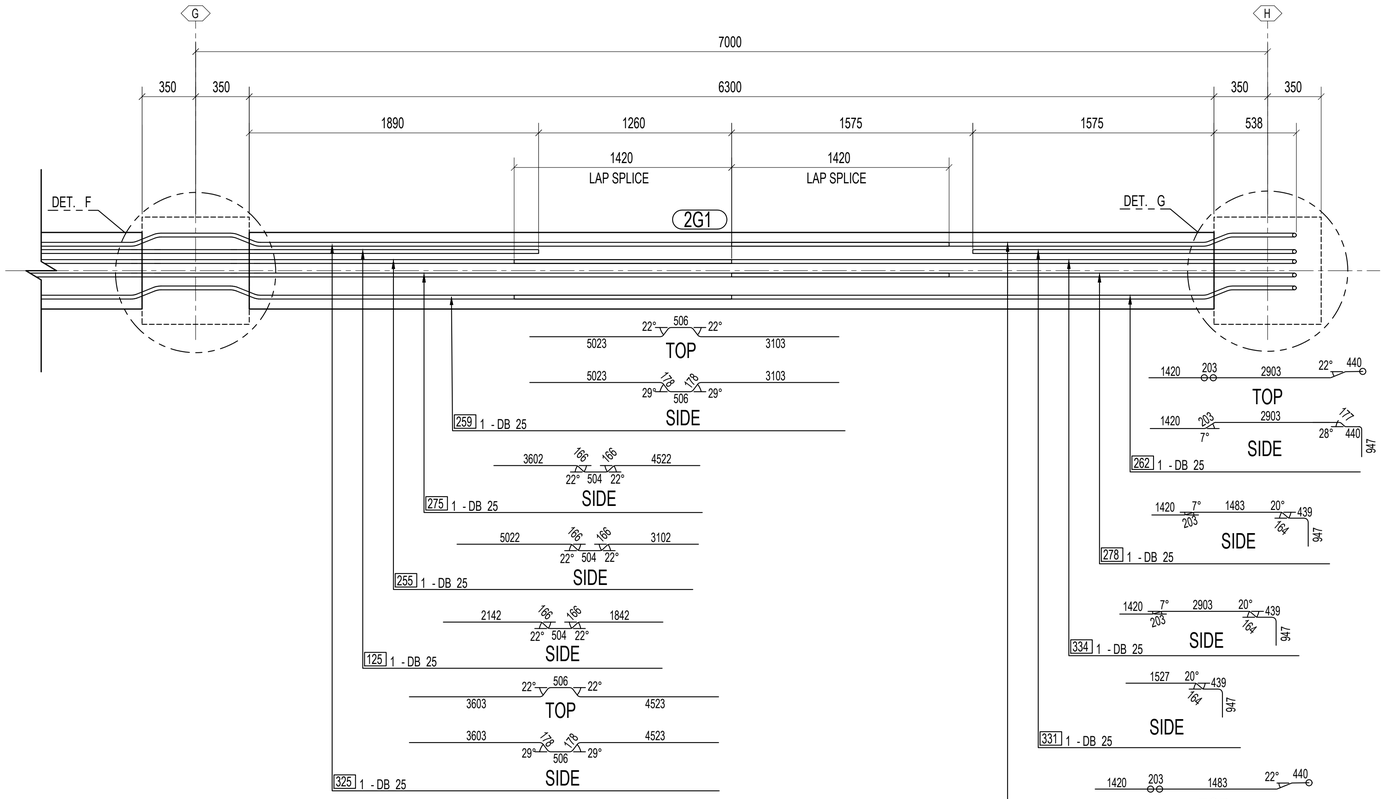

TOP RE-BAR
SCALE : 1:20

REV.	DESCRIPTION	AUTHOR	CHK.	APPR.	DATE
0A	ISSUED FOR CONSTRUCTION	WNS.	SP./TK.	TNP.	31 JUL 2026


CLIENT NAME : GULF MTP LNG TERMINAL COMPANY LIMITED


CONTRACTOR : POSCO E&C / CAZ CONSORTIUM

GENERATED BY : P PROFESSIONAL ENGINEERING CO.,LTD


DRAWING TITLE :
GULF MTP LNG RECEIVING TERMINAL PROJECT
INSTRUMENT & SUBSTATION BUILDING
2nd BEAM GL.4,5,6,7,8,9,10,11,12

DWG NO :	SHEET	REV NO :	SCALE :	SIZE :
GULF-ISB-CU-FL4000-B-104	5/19	0A	1:20,1:50	A1

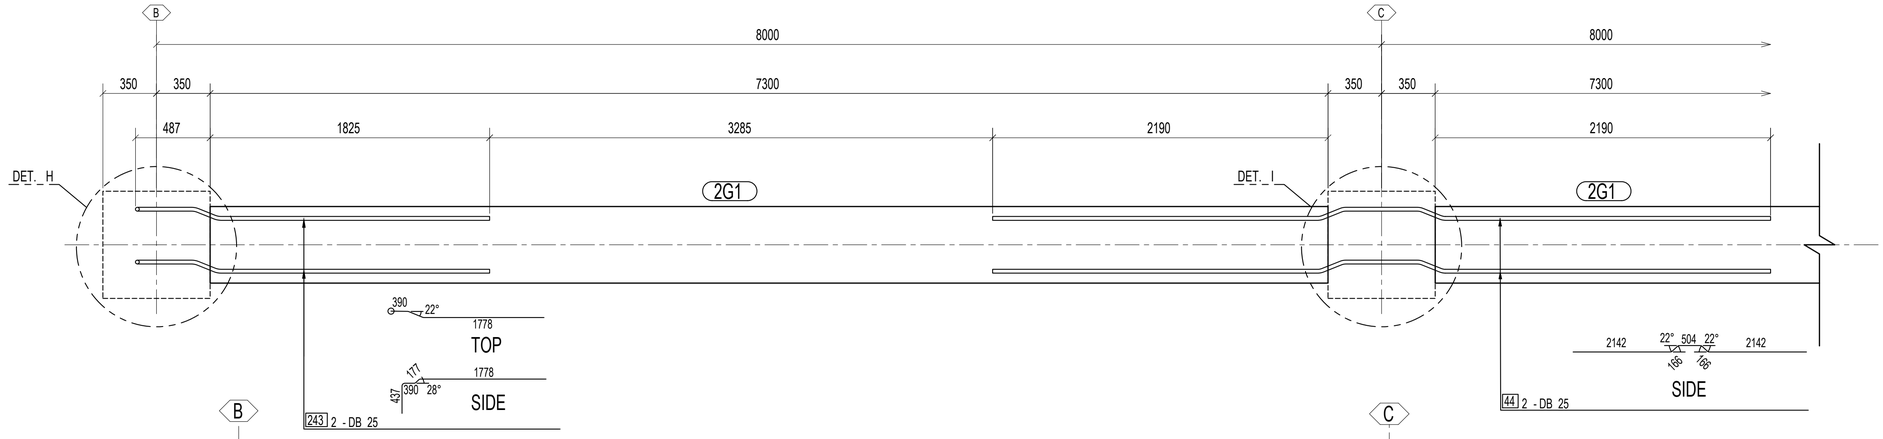


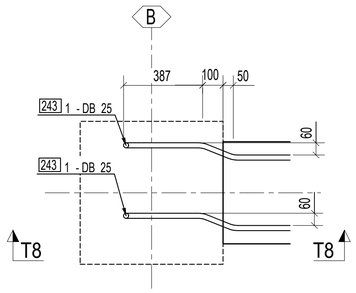


DETAIL H
SCALE : 1:15

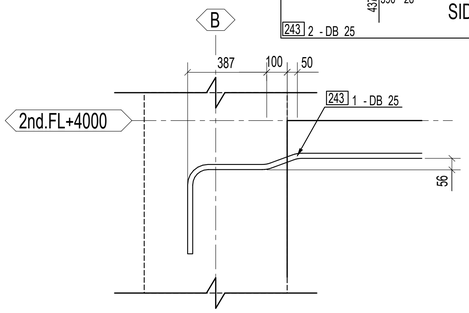


SECTION T8 - T8
SCALE : 1:15

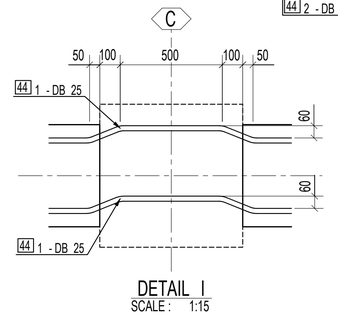


DETAIL I
SCALE : 1:15

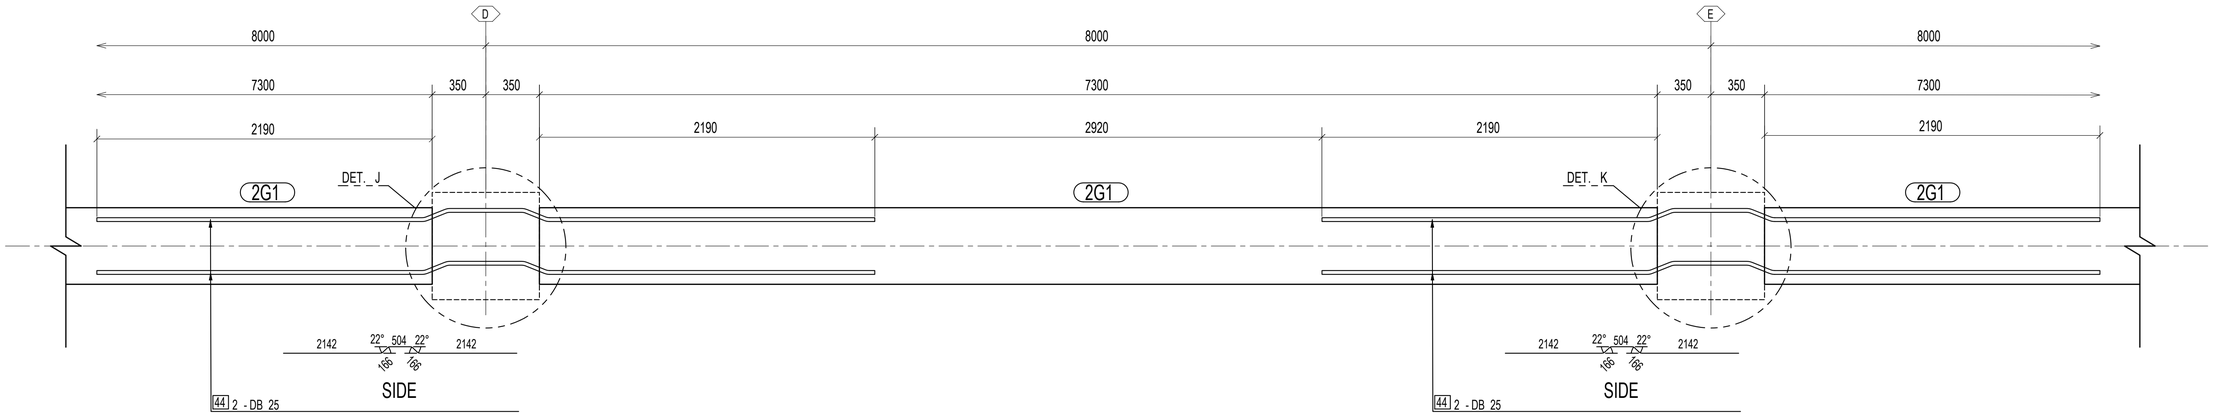

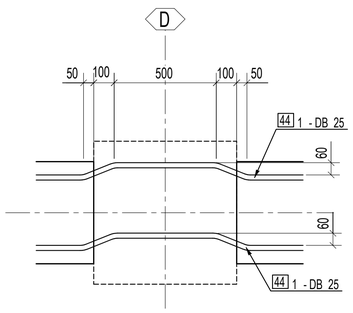

DETAIL J
SCALE : 1:15

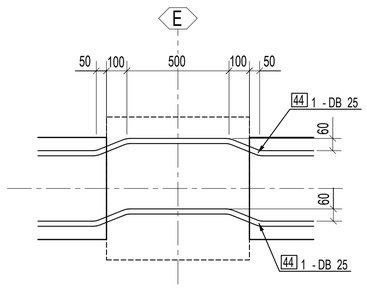

DETAIL K
SCALE : 1:15

TOP EXTRA RE-BAR
SCALE : 1:20

REV.	DESCRIPTION	AUTHOR	CHK.	APPR.	DATE
0A	ISSUED FOR CONSTRUCTION	WNS.	SP./TK.	TNP.	31 JUL 2026


CLIENT NAME : GULF MTP LNG TERMINAL COMPANY LIMITED


CONTRACTOR : POSCO E&C / CAZ CONSORTIUM

GENERATED BY : P PROFESSIONAL ENGINEERING CO.,LTD


DRAWING TITLE :
GULF MTP LNG RECEIVING TERMINAL PROJECT
INSTRUMENT & SUBSTATION BUILDING
2nd BEAM GL.4,5,6,7,8,9,10,11,12

DWG NO :	SHEET	REV NO :	SCALE :	SIZE :
GULF-ISB-CU-FL4000-B-104	6/19	0A	1:20,1:50	A1

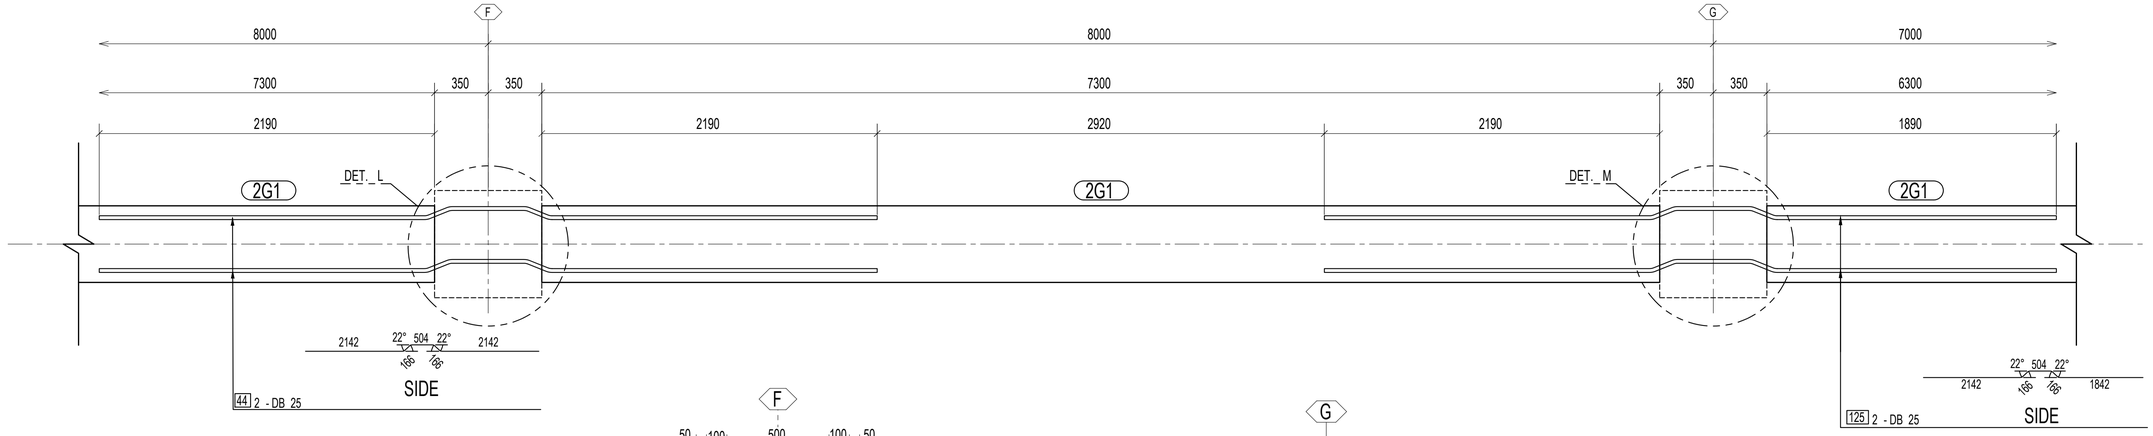


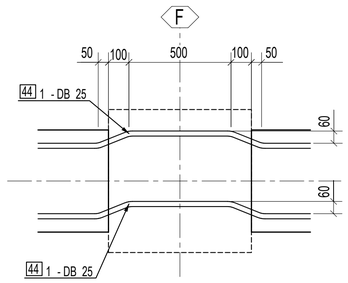


DETAIL L
SCALE : 1:15

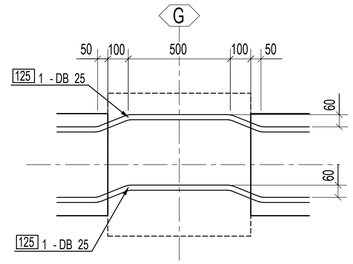


DETAIL M
SCALE : 1:15

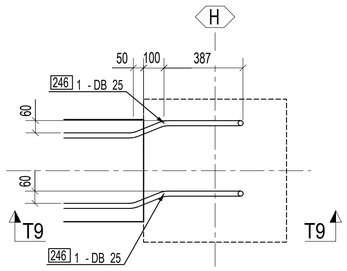

DETAIL N
SCALE : 1:15

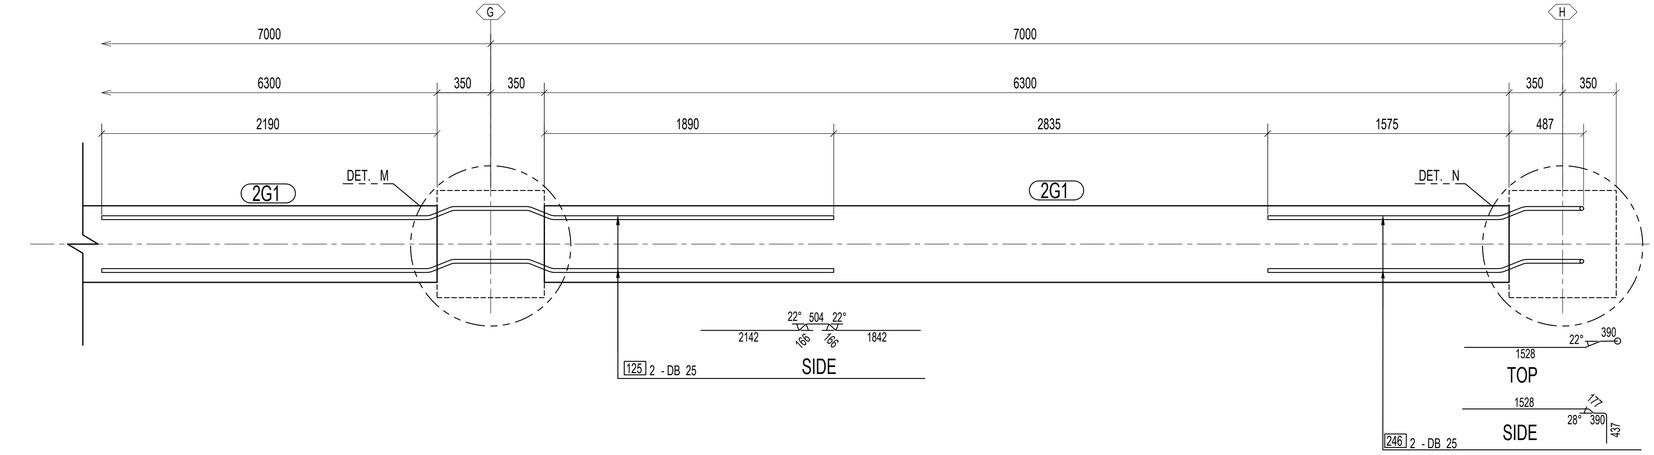

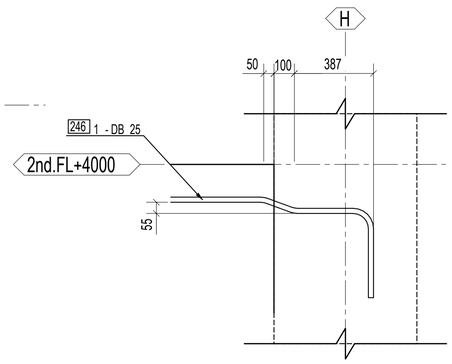

SECTION T9 - T9
SCALE : 1:15

TOP EXTRA RE-BAR
SCALE : 1:20

REV.	DESCRIPTION	AUTHOR	CHK.	APPR.	DATE
0A	ISSUED FOR CONSTRUCTION	WNS.	SP./TK.	TNP.	31 JUL 2026


CLIENT NAME : GULF MTP LNG TERMINAL COMPANY LIMITED

CONTRACTOR : POSCO E&C / CAZ CONSORTIUM


GENERATED BY : P PROFESSIONAL ENGINEERING CO.,LTD

DRAWING TITLE :
GULF MTP LNG RECEIVING TERMINAL PROJECT
INSTRUMENT & SUBSTATION BUILDING
2nd BEAM GL.4,5,6,7,8,9,10,11,12


DWG NO :	SHEET	REV NO :	SCALE :	SIZE :
GULF-ISB-CU-FL4000-B-104	7/19	0A	1:20,1:50	A1

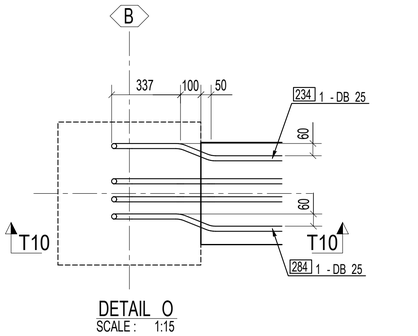


DETAIL O
SCALE : 1:15

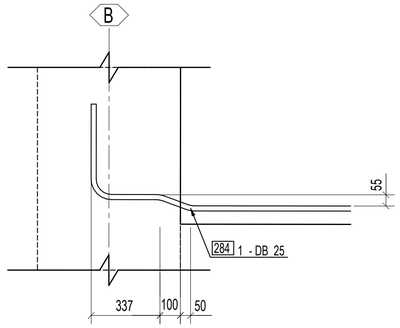


SECTION T10-T10
SCALE : 1:15

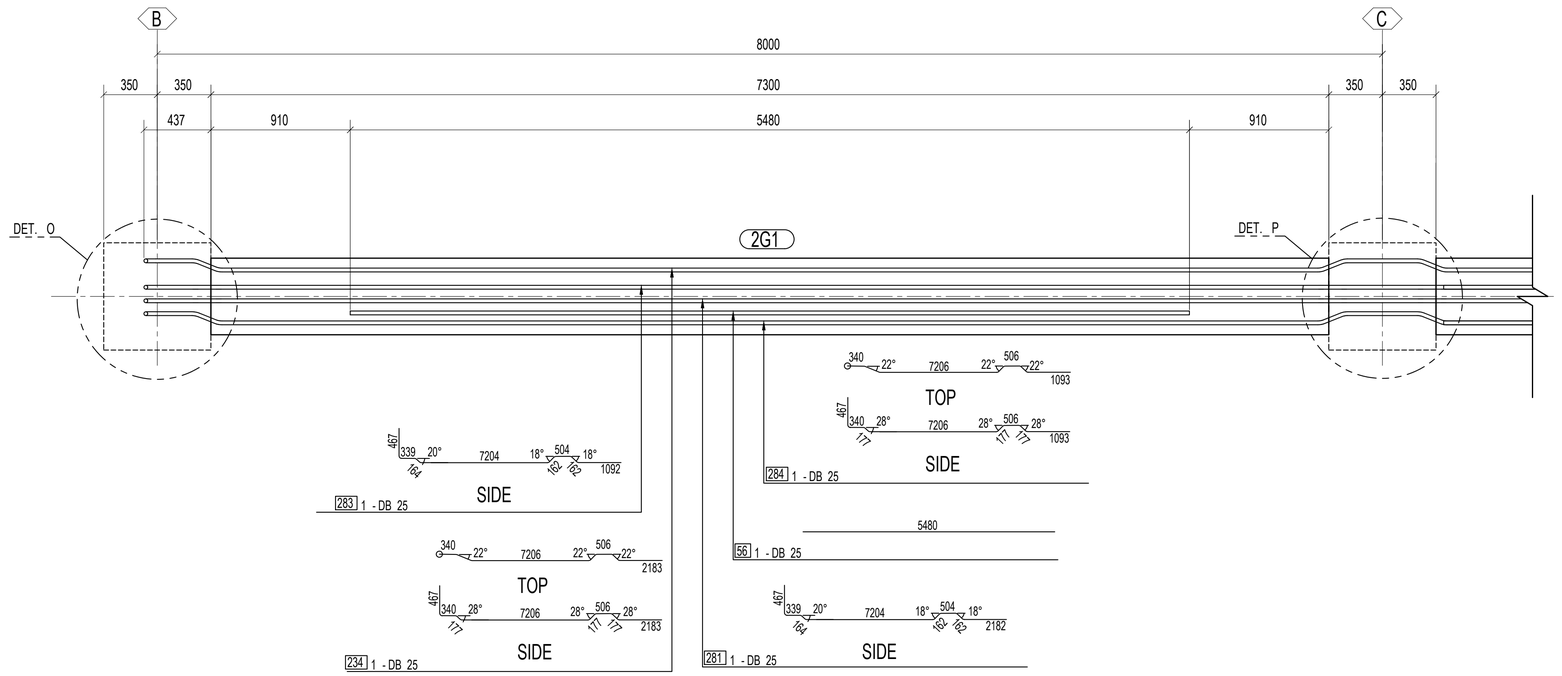


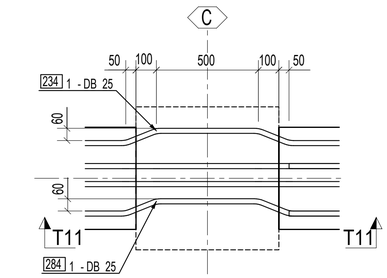

DETAIL P
SCALE : 1:15

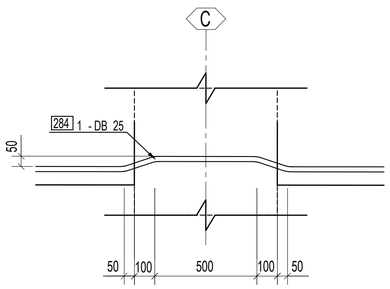

SECTION T11-T11
SCALE : 1:15

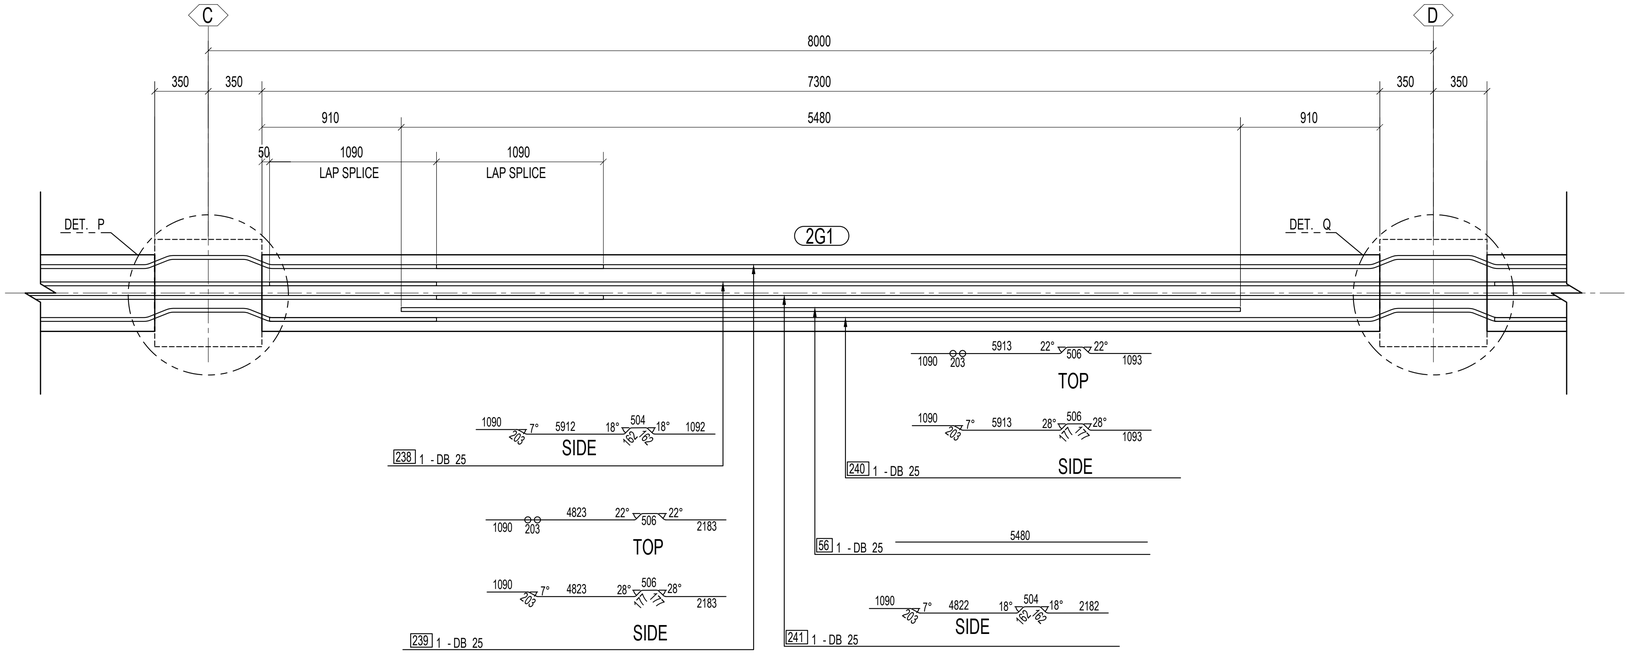

BOTTOM RE-BAR
SCALE : 1:20

REV.	DESCRIPTION	AUTHOR	CHK.	APPR.	DATE
0A	ISSUED FOR CONSTRUCTION	WNS.	SP./TK.	TNP.	31 JUL 2026


CLIENT NAME : GULF MTP LNG TERMINAL COMPANY LIMITED

CONTRACTOR : POSCO E&C / CAZ CONSORTIUM


GENERATED BY : P PROFESSIONAL ENGINEERING CO.,LTD

DRAWING TITLE : GULF MTP LNG RECEIVING TERMINAL PROJECT
INSTRUMENT & SUBSTATION BUILDING
2nd BEAM GL.4,5,6,7,8,9,10,11,12


DWG NO :	SHEET	REV NO :	SCALE :	SIZE :
GULF-ISB-CU-FL4000-B-104	8/19	0A	1:20,1:50	A1

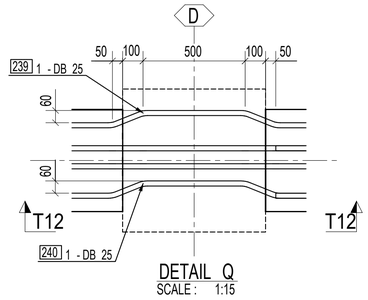


DETAIL Q
SCALE : 1:15

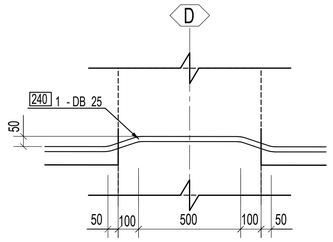


SECTION T12-T12
SCALE : 1:15

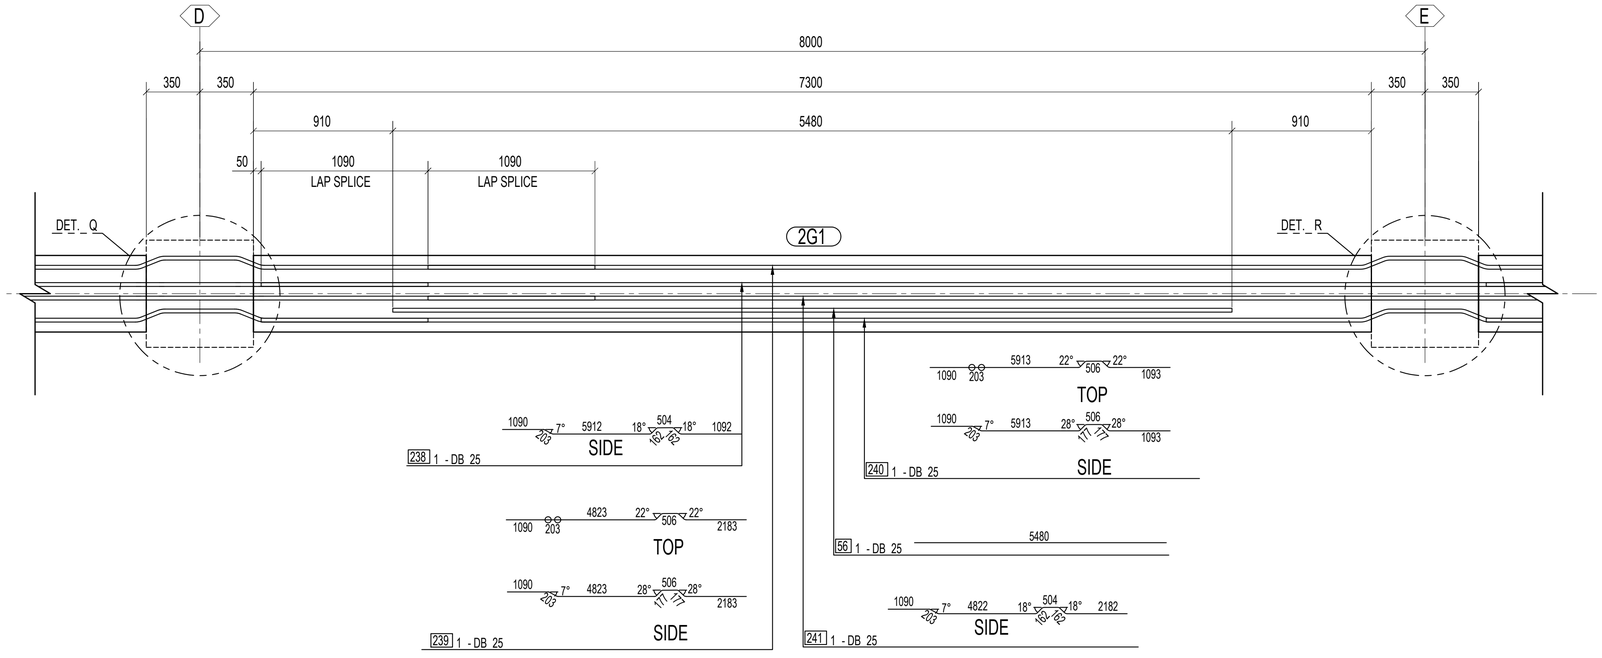


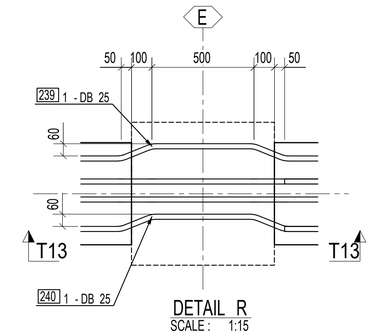

DETAIL R
SCALE : 1:15

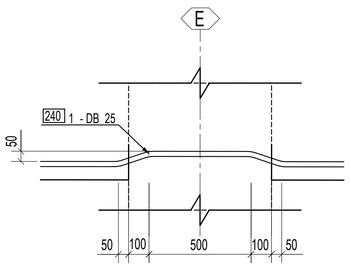

SECTION T13-T13
SCALE : 1:15

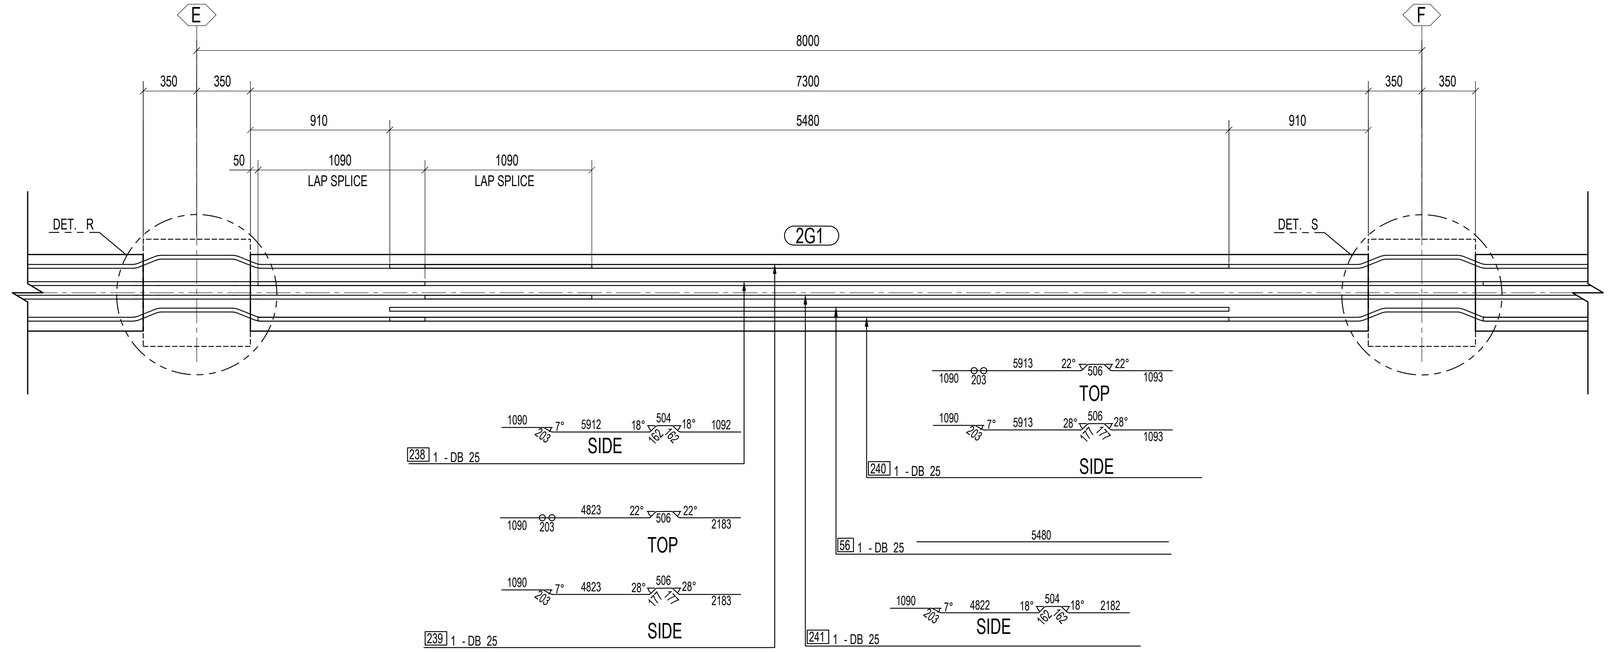

BOTTOM RE-BAR
SCALE : 1:20

REV.	DESCRIPTION	AUTHOR	CHK.	APPR.	DATE
0A	ISSUED FOR CONSTRUCTION	WNS.	SP./TK.	TNP.	31 JUL 2026


CLIENT NAME : GULF MTP LNG TERMINAL COMPANY LIMITED

CONTRACTOR : POSCO E&C / CAZ CONSORTIUM


GENERATED BY : P PROFESSIONAL ENGINEERING CO.,LTD

DRAWING TITLE :
GULF MTP LNG RECEIVING TERMINAL PROJECT
INSTRUMENT & SUBSTATION BUILDING
2nd BEAM GL.4,5,6,7,8,9,10,11,12


DWG NO :	SHEET	REV NO :	SCALE :	SIZE :
GULF-ISB-CU-FL4000-B-104	9/19	0A	1:20,1:50	A1

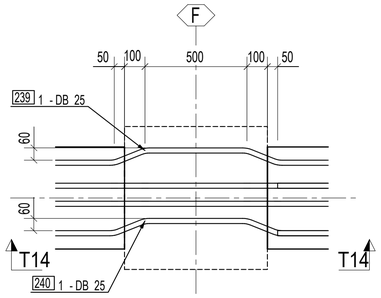


DETAIL S
SCALE : 1:15

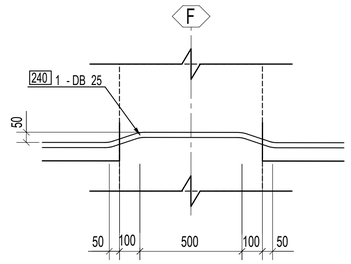


SECTION T14-T14
SCALE : 1:15

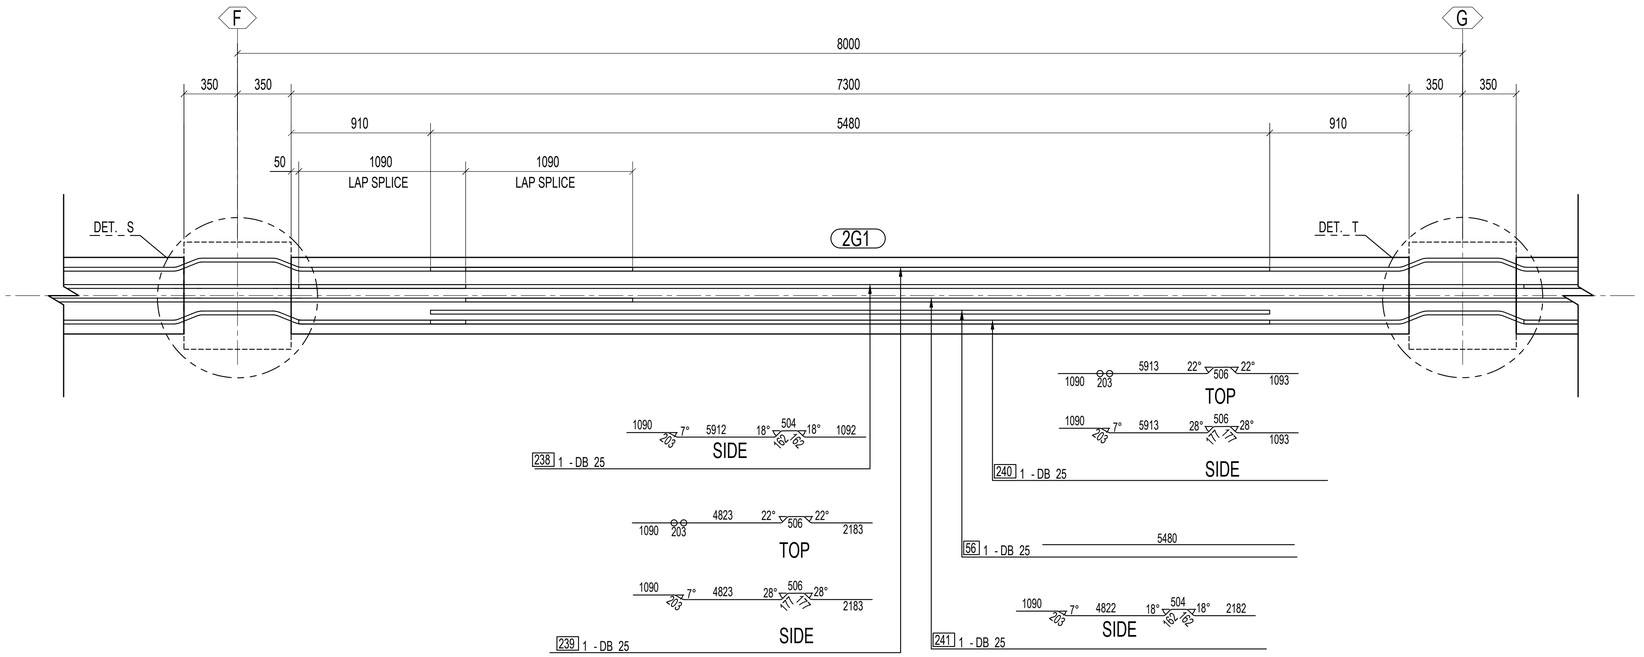


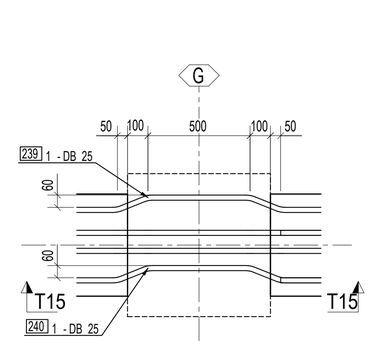


DETAIL T
SCALE : 1:15

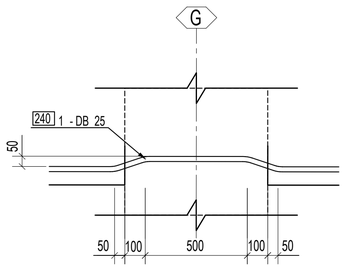


SECTION T15-T15
SCALE : 1:15

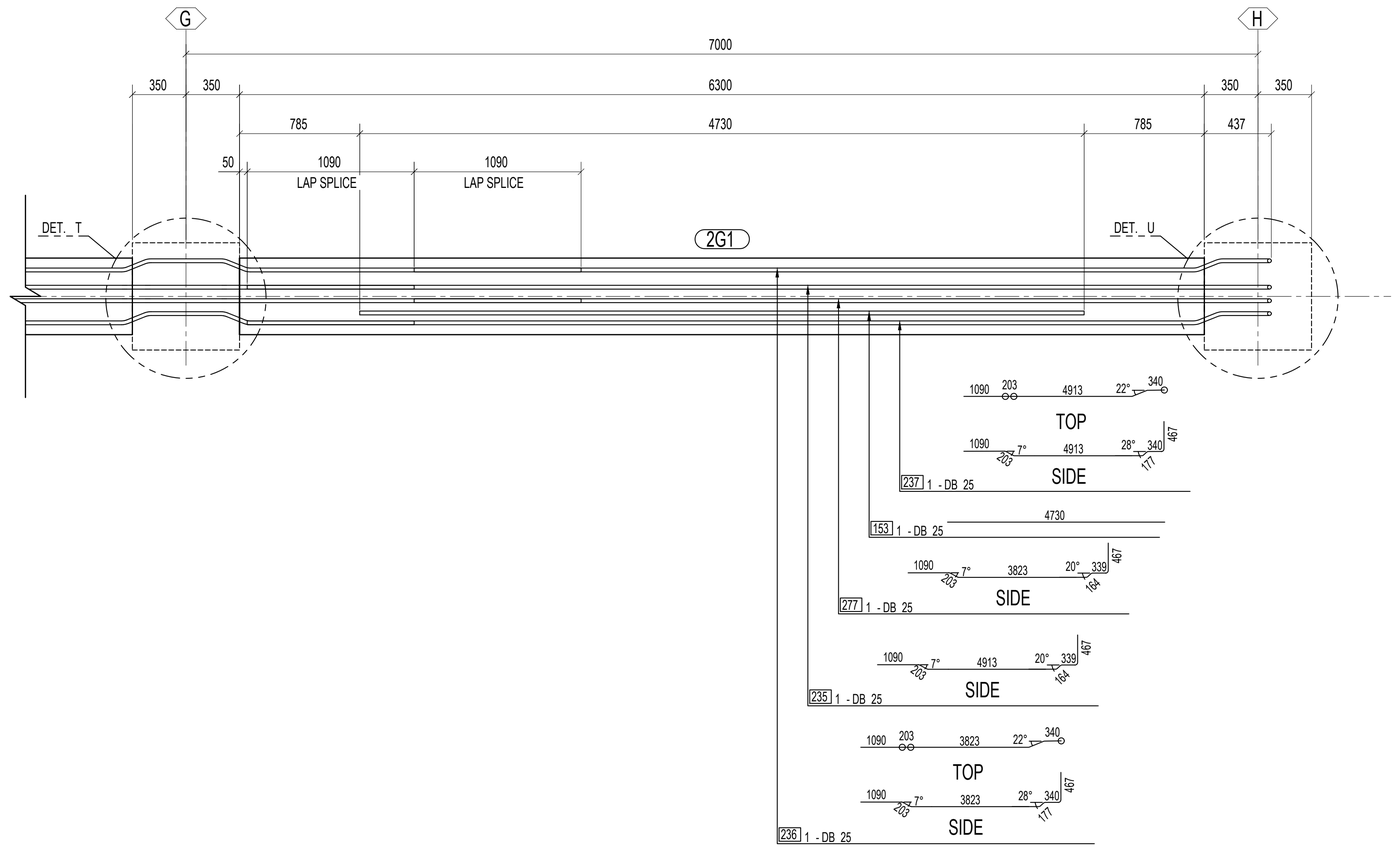

BOTTOM RE-BAR
SCALE : 1:20

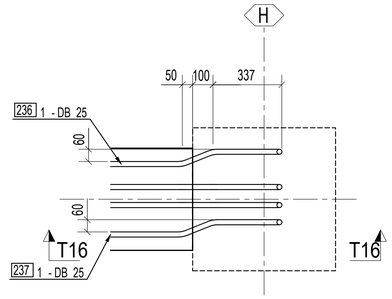

DETAIL U
SCALE : 1:15

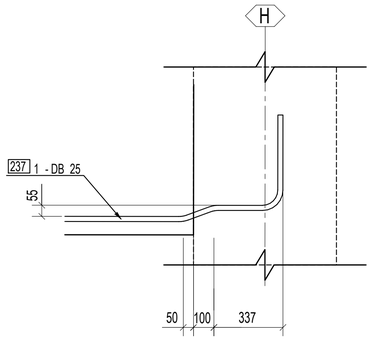

SECTION T16-T16
SCALE : 1:15

REV.	DESCRIPTION	AUTHOR	CHK.	APPR.	DATE
0A	ISSUED FOR CONSTRUCTION	WNS.	SP./TK.	TNP.	31 JUL 2026


CLIENT NAME : GULF MTP LNG TERMINAL COMPANY LIMITED


CONTRACTOR : POSCO E&C / CAZ CONSORTIUM


GENERATED BY : P PROFESSIONAL ENGINEERING CO.,LTD

DRAWING TITLE :
GULF MTP LNG RECEIVING TERMINAL PROJECT
INSTRUMENT & SUBSTATION BUILDING
2nd BEAM GL.4,5,6,7,8,9,10,11,12

DWG NO :	SHEET	REV NO :	SCALE :	SIZE :
GULF-ISB-CU-FL4000-B-104	10/19	0A	1:20,1:50	A1

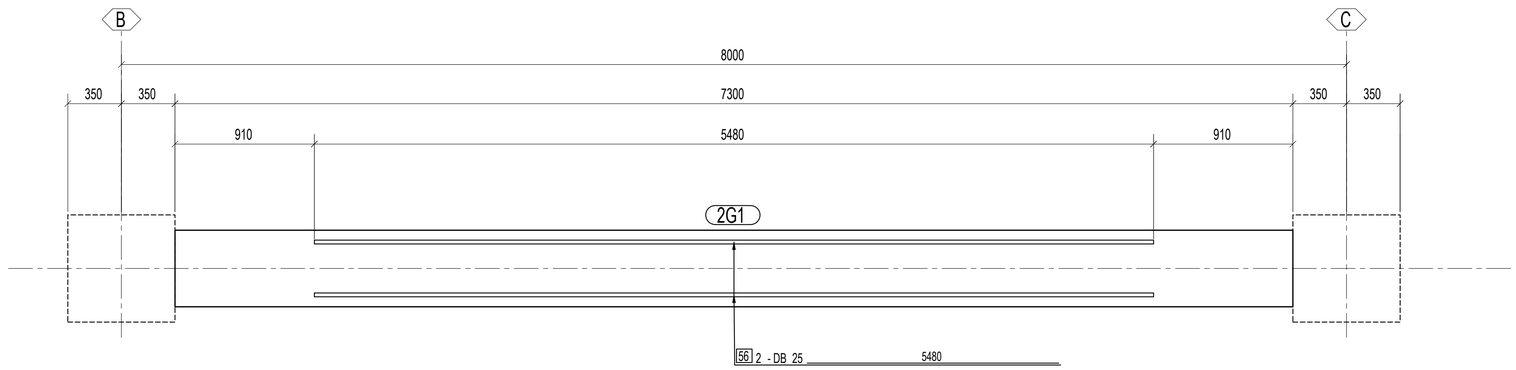

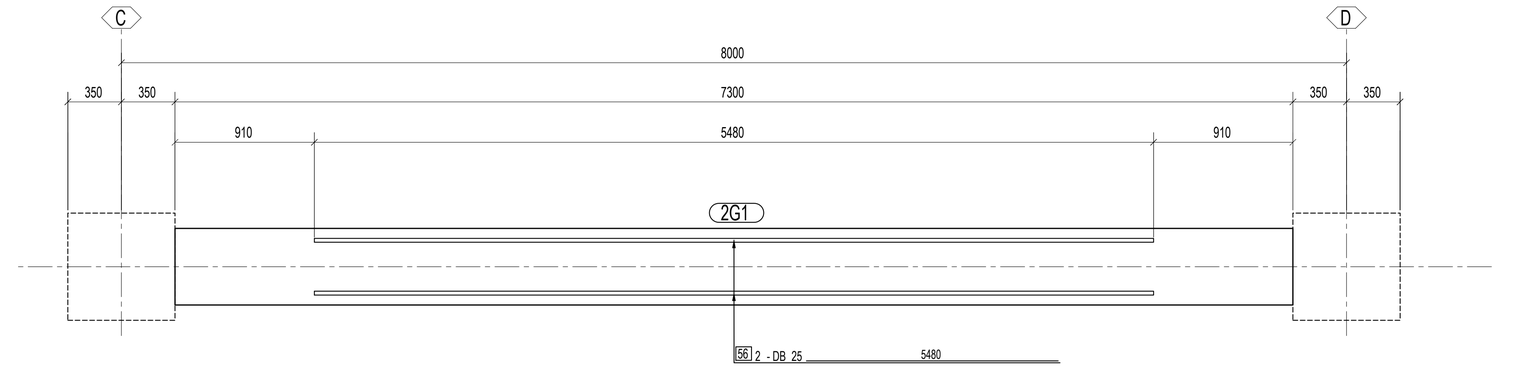

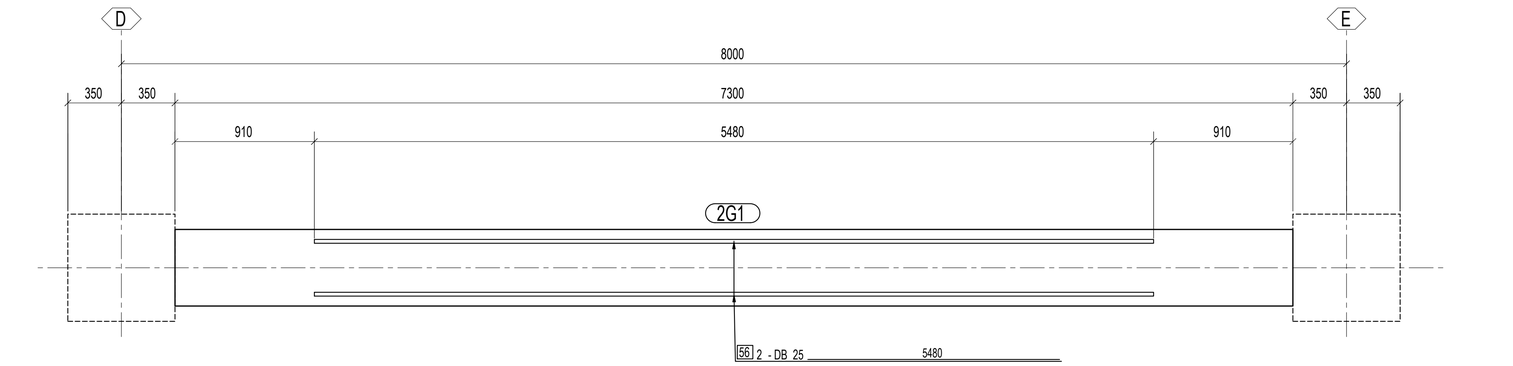

BOTTOM EXTRA RE-BAR
SCALE : 1:20

REV.	DESCRIPTION	AUTHOR	CHK.	APPR.	DATE
0A	ISSUED FOR CONSTRUCTION	WNS.	SP./TK.	TNP.	31 JUL 2026


CLIENT NAME : GULF MTP LNG TERMINAL COMPANY LIMITED

CONTRACTOR : POSCO E&C / CAZ CONSORTIUM

GENERATED BY : P PROFESSIONAL ENGINEERING CO.,LTD

DRAWING TITLE :
GULF MTP LNG RECEIVING TERMINAL PROJECT
INSTRUMENT & SUBSTATION BUILDING
2nd BEAM GL.4,5,6,7,8,9,10,11,12

DWG NO :	SHEET	REV NO :	SCALE :	SIZE :
GULF-ISB-CU-FL4000-B-104	11/19	0A	1:20	A1

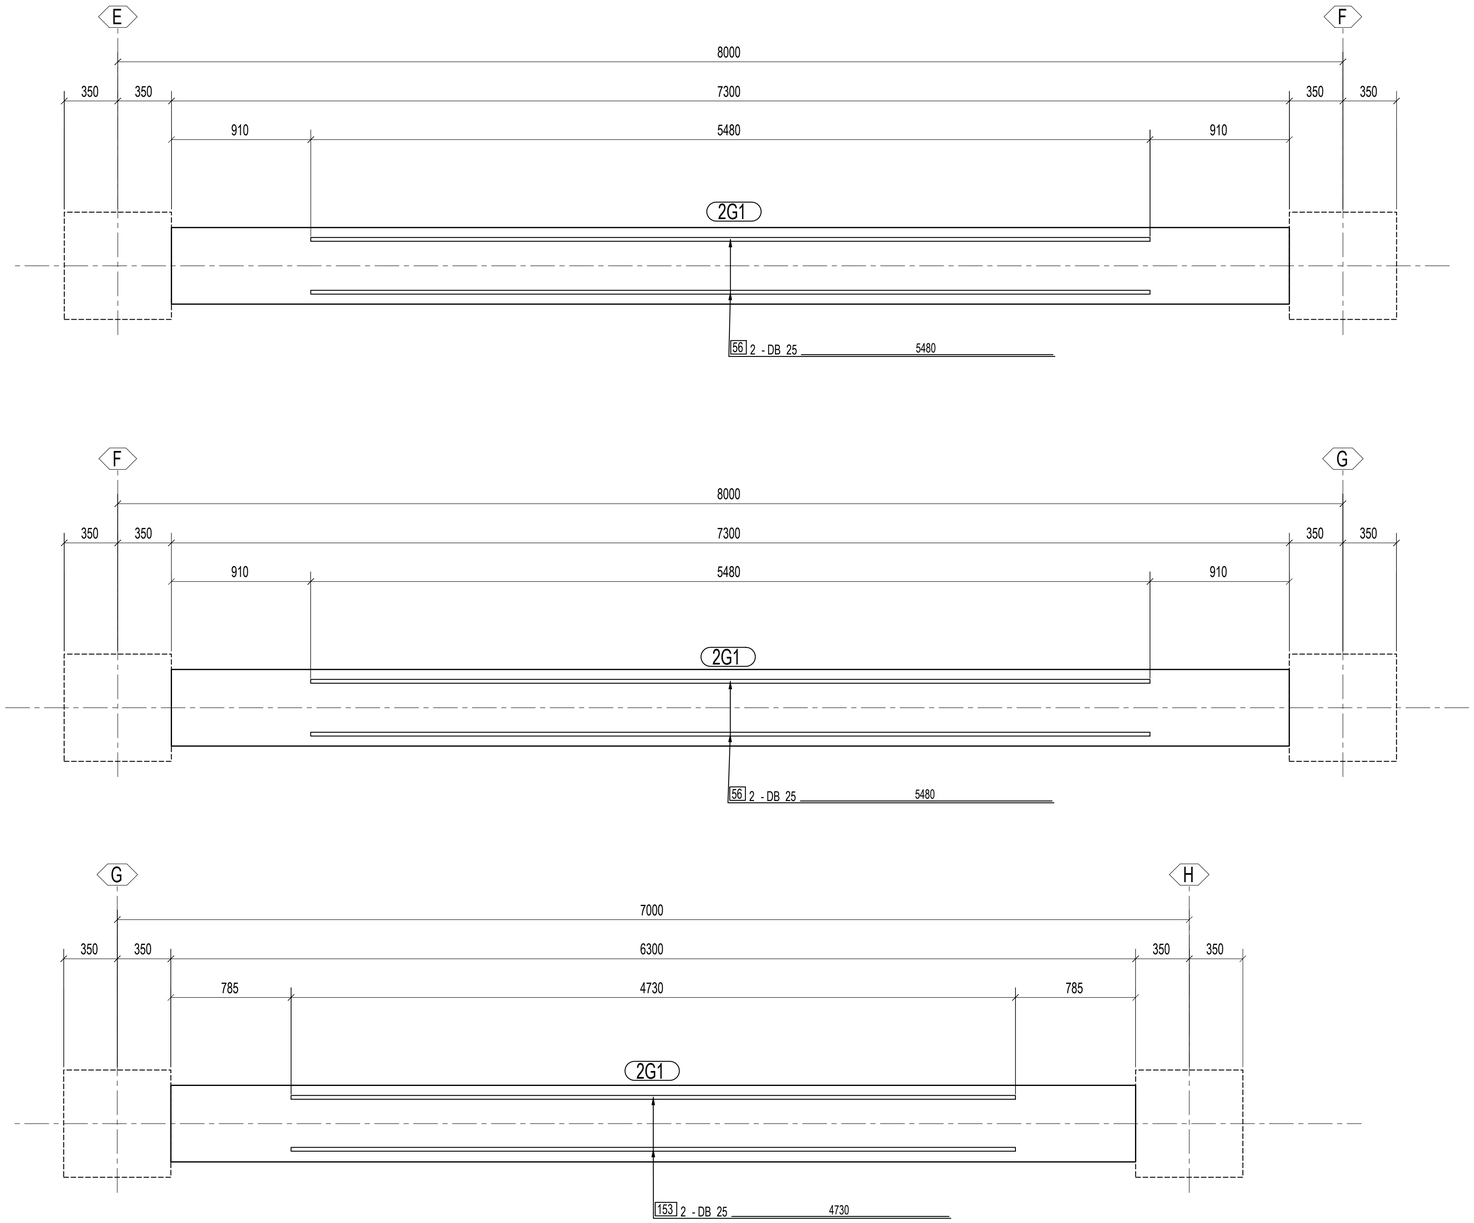

BOTTOM EXTRA RE-BAR
SCALE : 1:20

REV.	DESCRIPTION	AUTHOR	CHK.	APPR.	DATE
0A	ISSUED FOR CONSTRUCTION	WNS.	SP./TK.	TNP.	31 JUL 2026


CLIENT NAME : GULF MTP LNG TERMINAL COMPANY LIMITED


CONTRACTOR : POSCO E&C / CAZ CONSORTIUM

GENERATED BY : P PROFESSIONAL ENGINEERING CO.,LTD

DRAWING TITLE :
GULF MTP LNG RECEIVING TERMINAL PROJECT
INSTRUMENT & SUBSTATION BUILDING
2nd BEAM GL.4,5,6,7,8,9,10,11,12

DWG NO :	SHEET	REV NO :	SCALE :	SIZE :
GULF-ISB-CU-FL4000-B-104	12/19	0A	1:20	A1

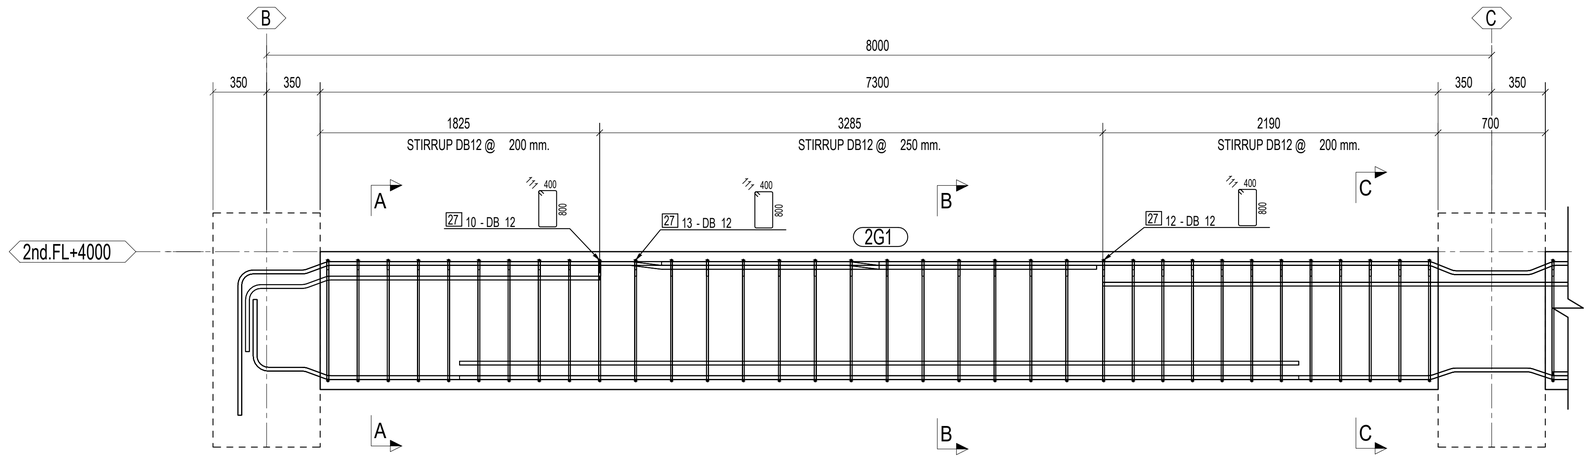

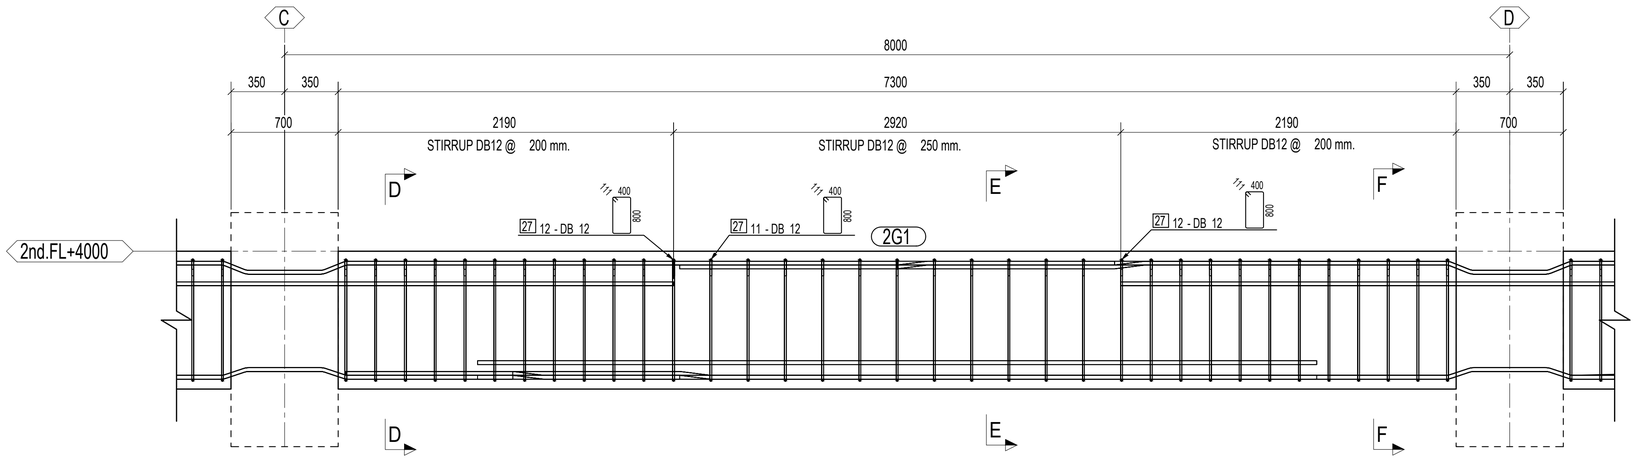

ELEVATION VIEW
SCALE : 1:20

REV.	DESCRIPTION	AUTHOR	CHK.	APPR.	DATE
0A	ISSUED FOR CONSTRUCTION	WNS.	SP./TK.	TNP.	31 JUL 2026


CLIENT NAME : GULF MTP LNG TERMINAL COMPANY LIMITED


CONTRACTOR : POSCO E&C / CAZ CONSORTIUM

GENERATED BY : P PROFESSIONAL ENGINEERING CO.,LTD

DRAWING TITLE :
GULF MTP LNG RECEIVING TERMINAL PROJECT
INSTRUMENT & SUBSTATION BUILDING
2nd BEAM GL.4,5,6,7,8,9,10,11,12

DWG NO :	SHEET	REV NO :	SCALE :	SIZE :
GULF-ISB-CU-FL4000-B-104	13/19	0A	1:20	A1

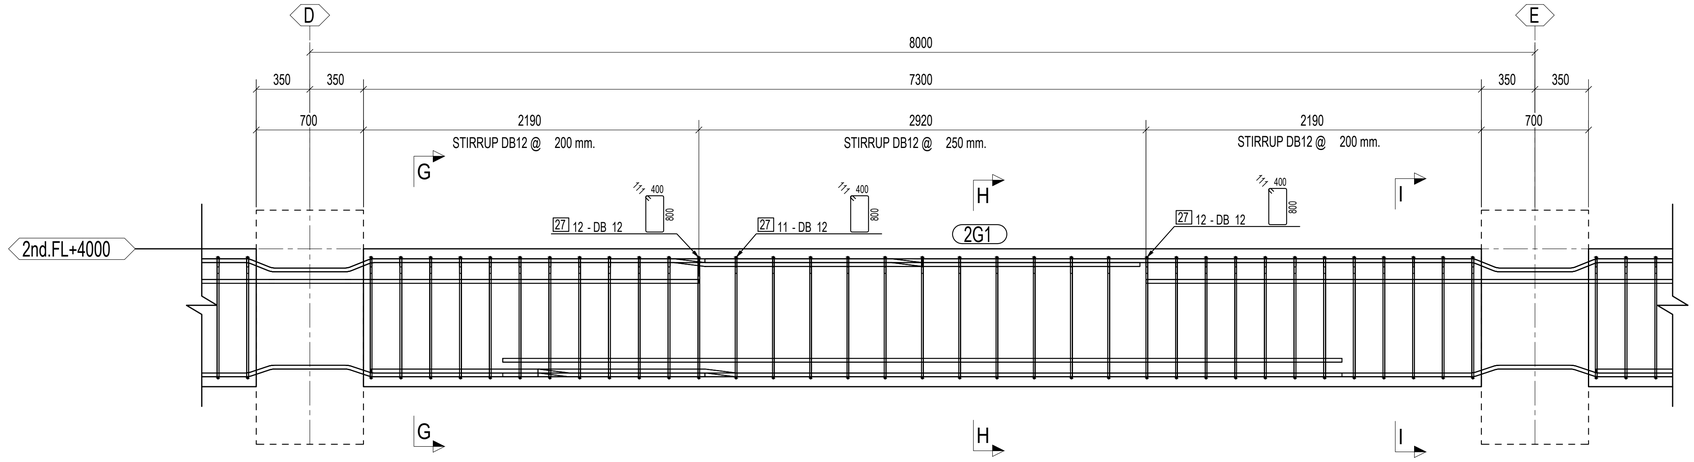

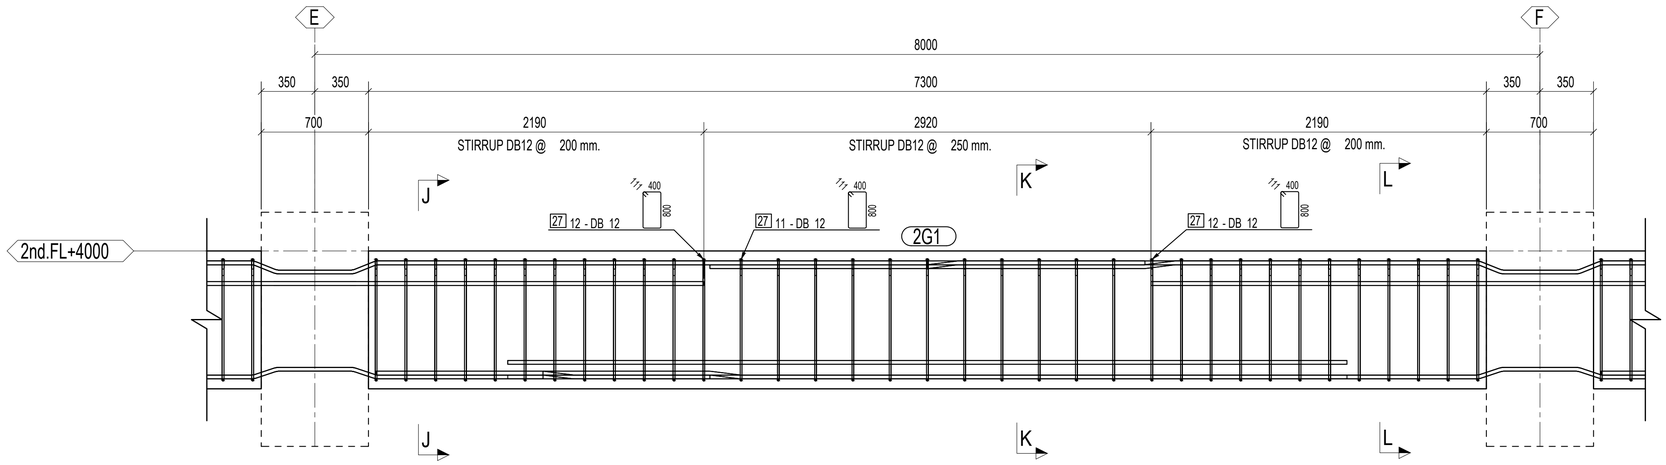

ELEVATION VIEW
SCALE : 1:20

REV.	DESCRIPTION	AUTHOR	CHK.	APPR.	DATE
0A	ISSUED FOR CONSTRUCTION	WNS.	SP./TK.	TNP.	31 JUL 2026


CLIENT NAME : GULF MTP LNG TERMINAL COMPANY LIMITED


CONTRACTOR : POSCO E&C / CAZ CONSORTIUM

GENERATED BY : P PROFESSIONAL ENGINEERING CO.,LTD

DRAWING TITLE :
GULF MTP LNG RECEIVING TERMINAL PROJECT
INSTRUMENT & SUBSTATION BUILDING
2nd BEAM GL.4,5,6,7,8,9,10,11,12

DWG NO :	SHEET	REV NO :	SCALE :	SIZE :
GULF-ISB-CU-FL4000-B-104	14/19	0A	1:20	A1

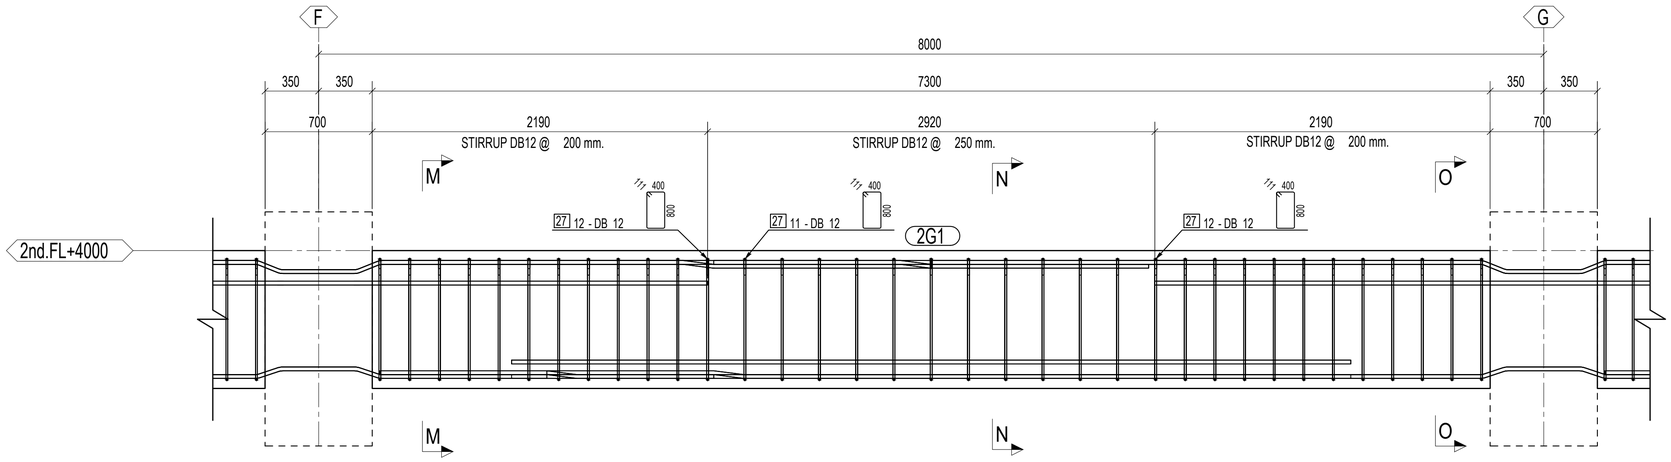

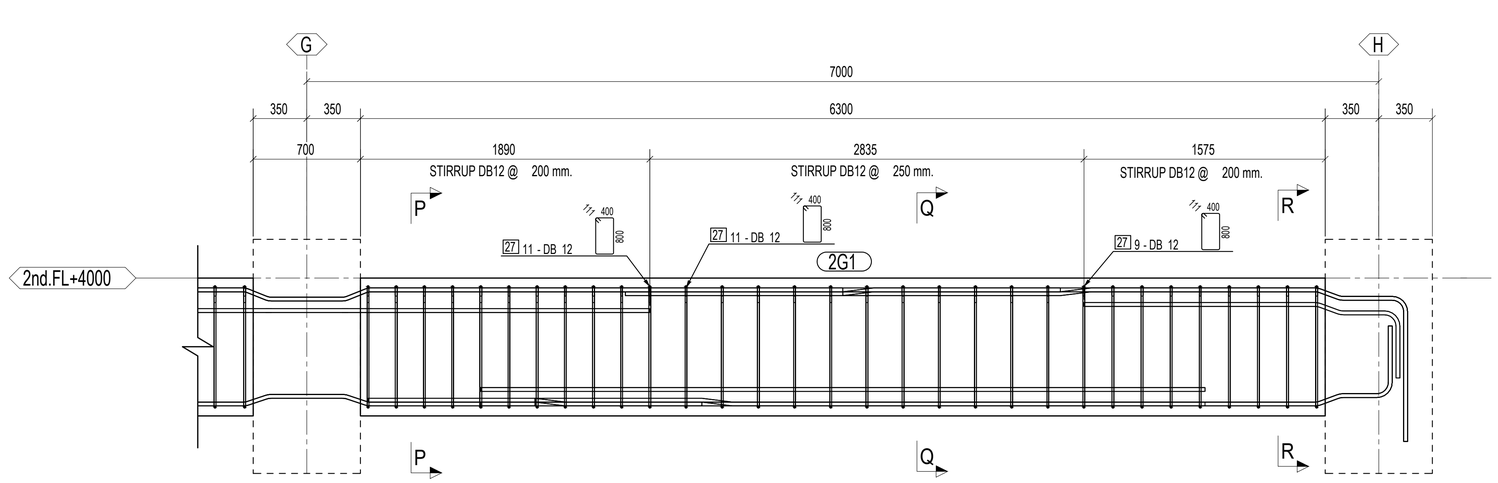

ELEVATION VIEW
SCALE : 1:20

REV.	DESCRIPTION	AUTHOR	CHK.	APPR.	DATE
0A	ISSUED FOR CONSTRUCTION	WNS.	SP./TK.	TNP.	31 JUL 2026


CLIENT NAME : GULF MTP LNG TERMINAL COMPANY LIMITED

CONTRACTOR : POSCO E&C / CAZ CONSORTIUM


GENERATED BY : P PROFESSIONAL ENGINEERING CO.,LTD

DRAWING TITLE :
GULF MTP LNG RECEIVING TERMINAL PROJECT
INSTRUMENT & SUBSTATION BUILDING
2nd BEAM GL.4,5,6,7,8,9,10,11,12


DWG NO :	SHEET	REV NO :	SCALE :	SIZE :
GULF-ISB-CU-FL4000-B-104	15/19	0A	1:20	A1

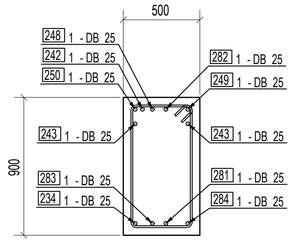


SECTION A - A
SCALE : 1:20

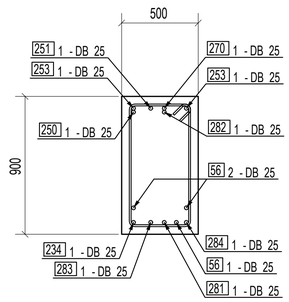


SECTION B - B
SCALE : 1:20

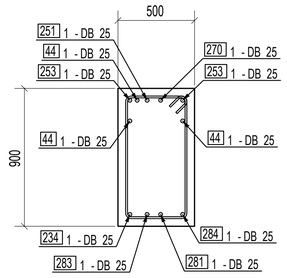


SECTION C - C
SCALE : 1:20

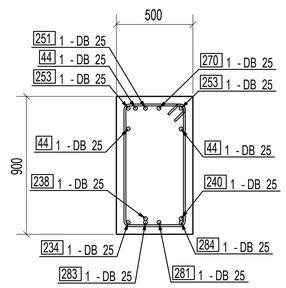


SECTION D - D
SCALE : 1:20

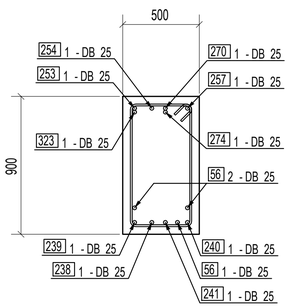


SECTION E - E
SCALE : 1:20

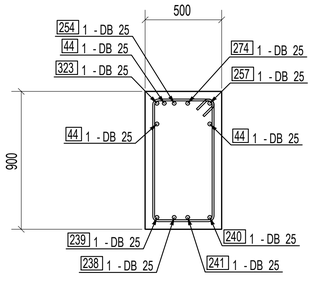


SECTION F - F
SCALE : 1:20

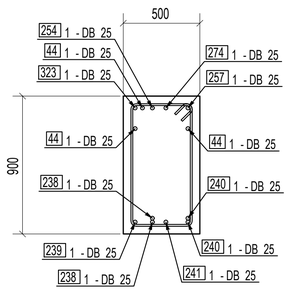


SECTION G - G
SCALE : 1:20

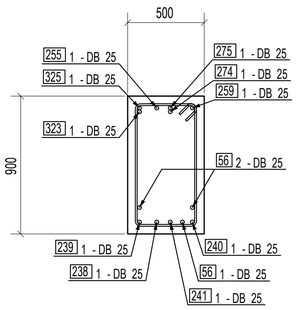


SECTION H - H
SCALE : 1:20

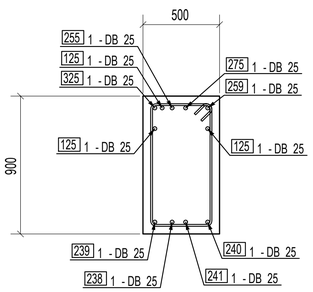


SECTION I - I
SCALE : 1:20

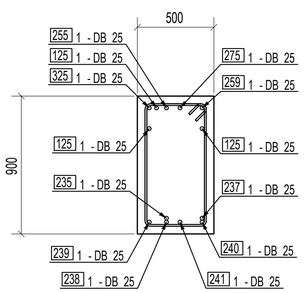

SECTION J - J
SCALE : 1:20

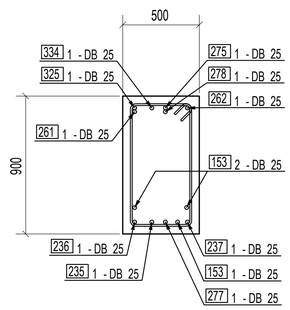

SECTION K - K
SCALE : 1:20

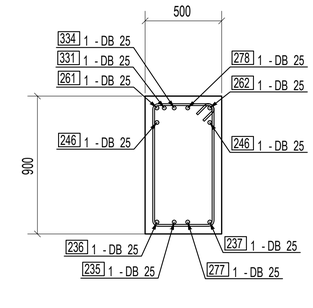

SECTION L - L
SCALE : 1:20

SECTION M - M
SCALE : 1:20

SECTION N - N
SCALE : 1:20

SECTION O - O
SCALE : 1:20

SECTION P - P
SCALE : 1:20

SECTION Q - Q
SCALE : 1:20

SECTION R - R
SCALE : 1:20

REV.	DESCRIPTION	AUTHOR	CHK.	APPR.	DATE
0A	ISSUED FOR CONSTRUCTION	WNS.	SP./TK.	TNP.	31 JUL 2026


CLIENT NAME :
GULF MTP LNG TERMINAL COMPANY LIMITED

CONTRACTOR :
POSCO E&C / CAZ CONSORTIUM

GENERATED BY :
P PROFESSIONAL ENGINEERING CO.,LTD

DRAWING TITLE :
GULF MTP LNG RECEIVING TERMINAL PROJECT
INSTRUMENT & SUBSTATION BUILDING
2nd BEAM GL.4,5,6,7,8,9,10,11,12

DWG NO :	SHEET	REV NO :	SCALE :	SIZE :
GULF-ISB-CU-FL4000-B-104	16/19	0A	1:20	A1

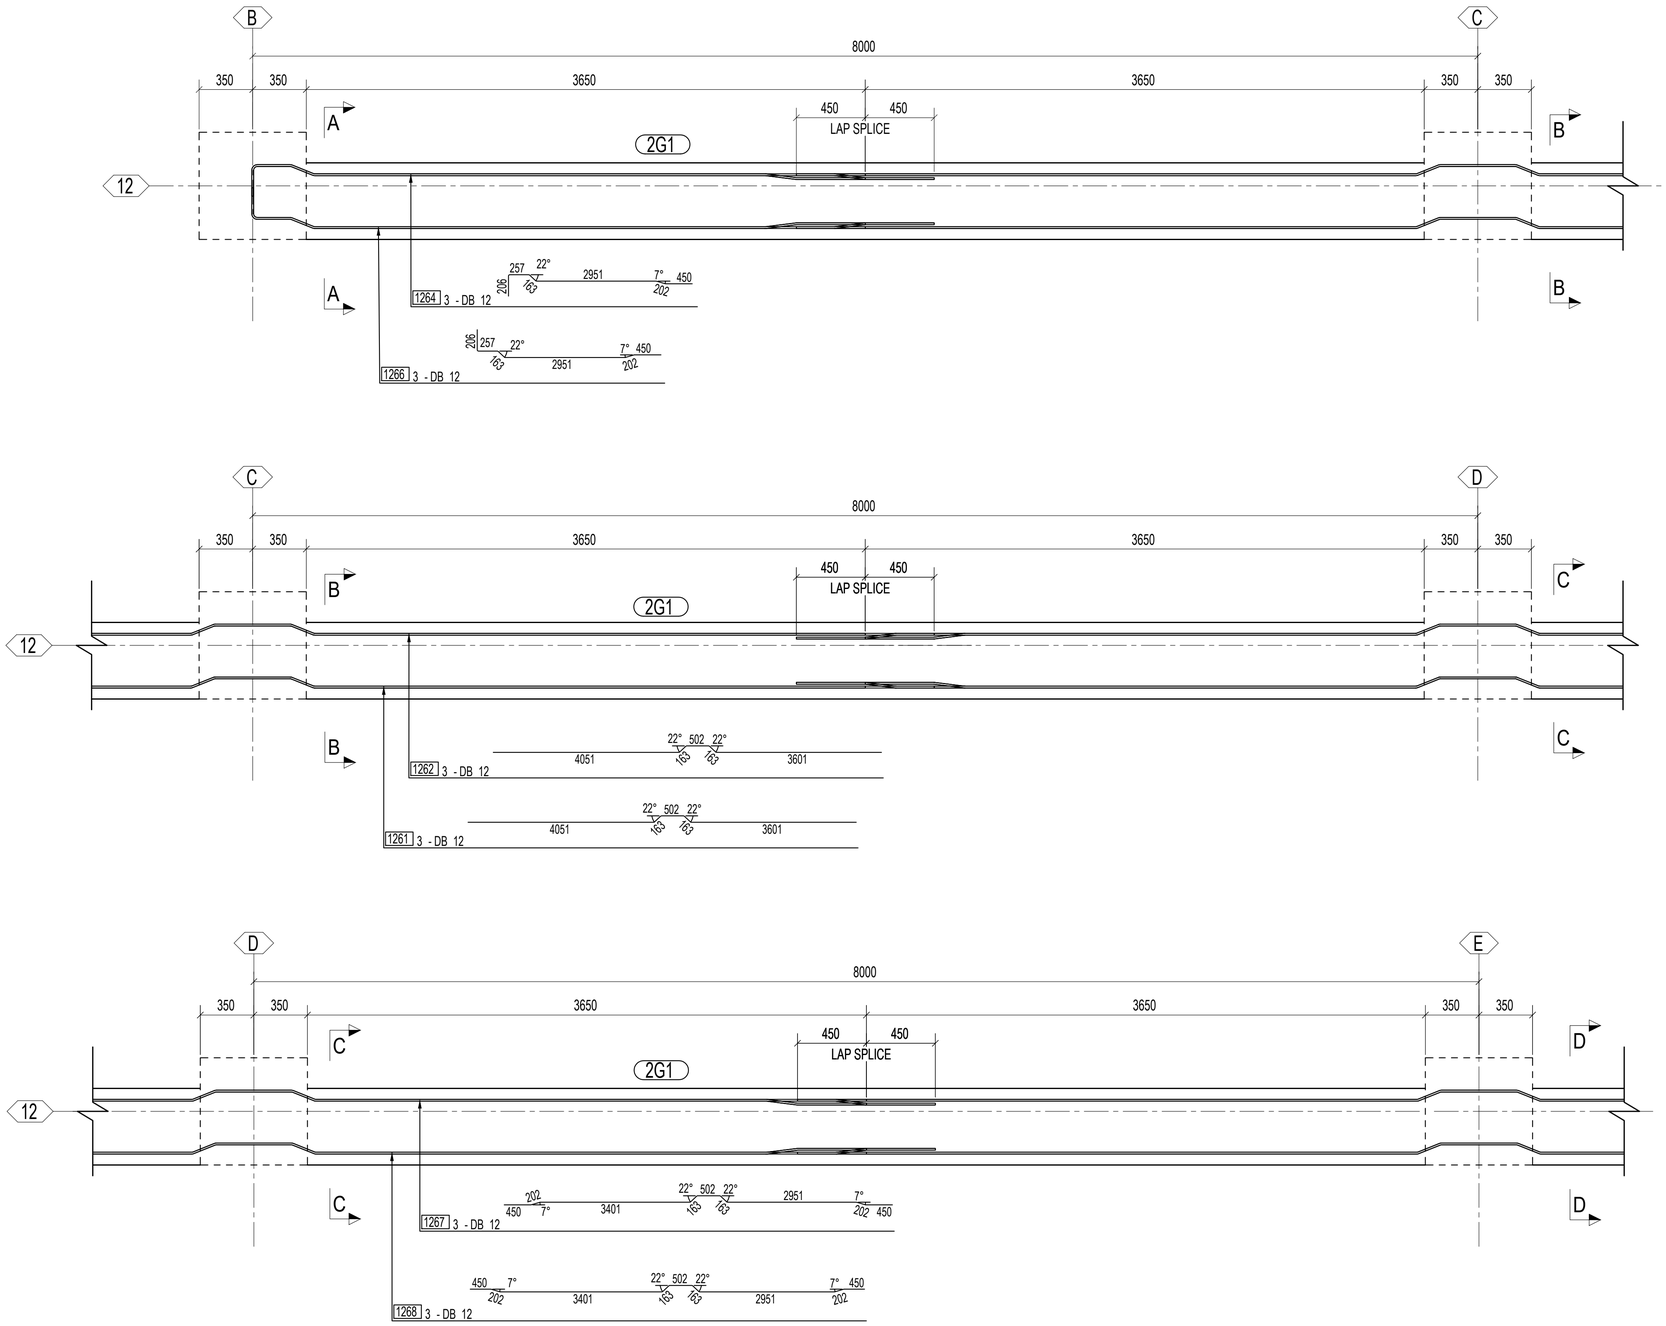

TOP VIEW
SKIN RE-BAR
SCALE : 1:20

REV.	DESCRIPTION	AUTHOR	CHK.	APPR.	DATE
0A	ISSUED FOR CONSTRUCTION	TKW.	SP./WS.	TNP.	31 JUL 2026


CLIENT NAME : GULF MTP LNG TERMINAL COMPANY LIMITED

CONTRACTOR : POSCO E&C / CAZ CONSORTIUM

GENERATED BY : P PROFESSIONAL ENGINEERING CO.,LTD

DRAWING TITLE :
GULF MTP LNG RECEIVING TERMINAL PROJECT
INSTRUMENT & SUBSTATION BUILDING
2nd BEAM GL.4,5,6,7,8,9,10,11,12

DWG NO :	SHEET	REV NO :	SCALE :	SIZE :
GULF-ISB-CU-FL4000-B-104	17/19	0A	1:20	A1

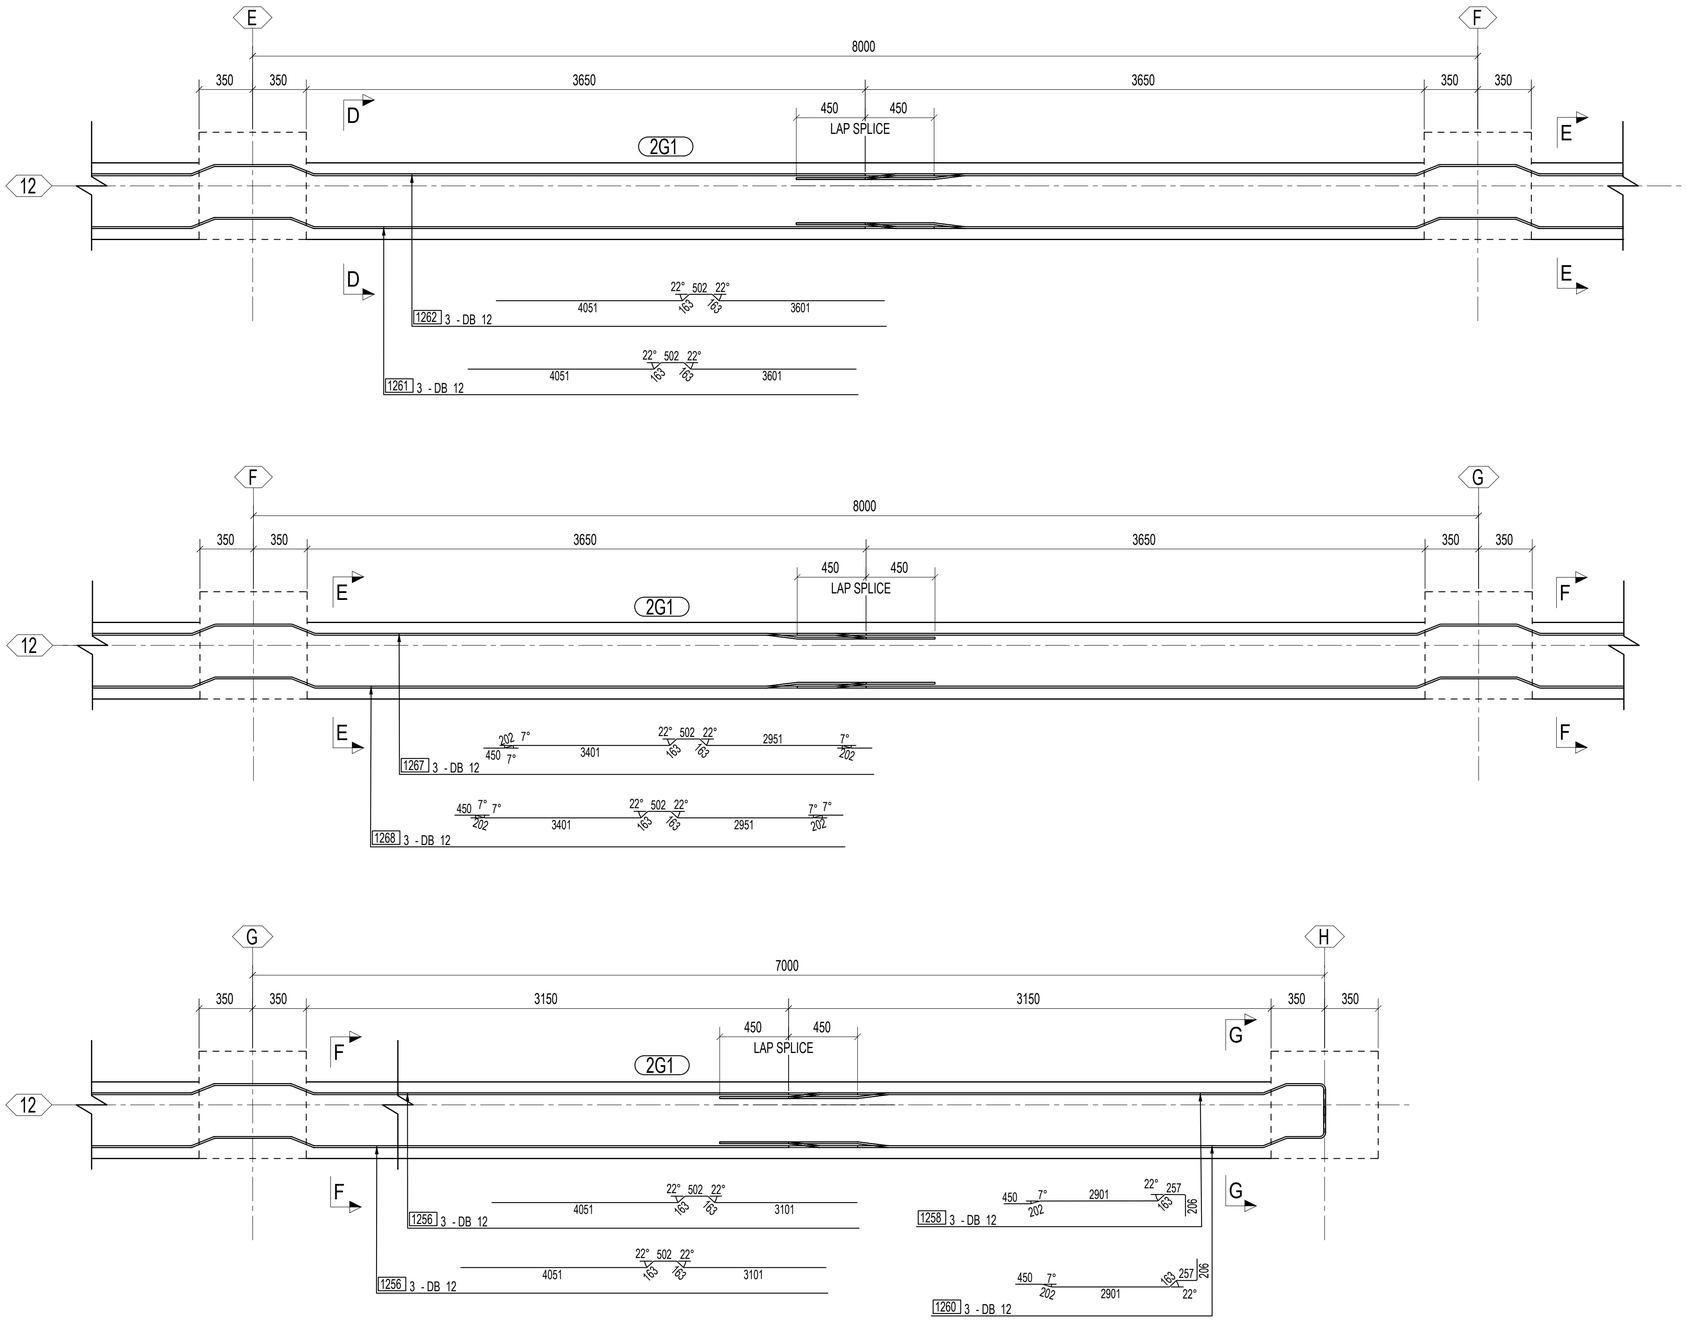

TOP VIEW
SKIN RE-BAR
SCALE : 1:20

REV.	DESCRIPTION	AUTHOR	CHK.	APPR.	DATE
0A	ISSUED FOR CONSTRUCTION	TKW.	SP./WS.	TNP.	31 JUL 2026


CLIENT NAME : GULF MTP LNG TERMINAL COMPANY LIMITED

CONTRACTOR : POSCO E&C / CAZ CONSORTIUM


GENERATED BY : P PROFESSIONAL ENGINEERING CO.,LTD

DRAWING TITLE :
GULF MTP LNG RECEIVING TERMINAL PROJECT
INSTRUMENT & SUBSTATION BUILDING
2nd BEAM GL.4,5,6,7,8,9,10,11,12


DWG NO :	SHEET	REV NO :	SCALE :	SIZE :
GULF-ISB-CU-FL4000-B-104	18/19	0A	1:20	A1

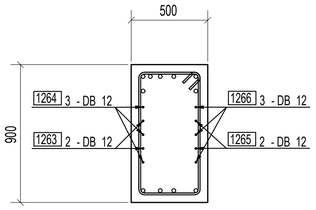


SECTION A - A
SCALE : 1:20

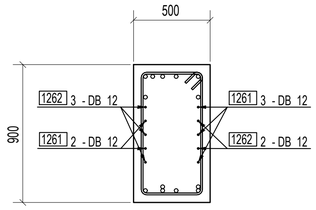


SECTION B - B
SCALE : 1:20

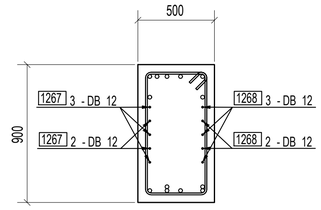


SECTION C - C
SCALE : 1:20

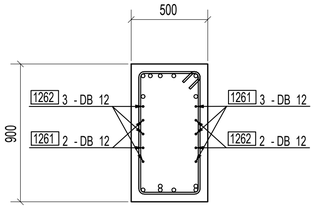


SECTION D - D
SCALE : 1:20

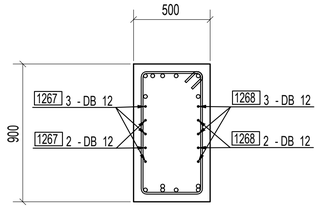

SECTION E - E
SCALE : 1:20













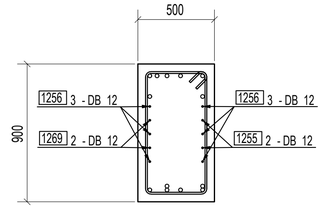


SECTION F - F
SCALE : 1:20

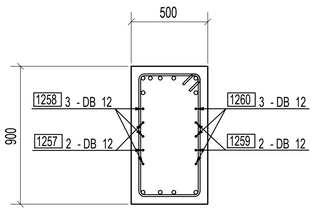

SECTION G - G
SCALE : 1:20

REBAR BENDING SCHEDULE

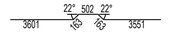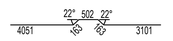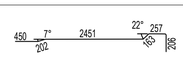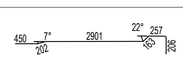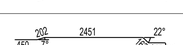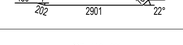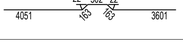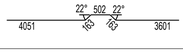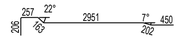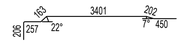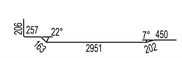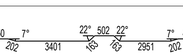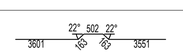Pos	Diameter	Number	Grade	Length	Kg/p	Weight	Bending shape
1255	12	4	SD40	7970	7.08	28.31	
1256	12	12	SD40	7970	7.08	84.93	
1257	12	4	SD40	3700	3.29	13.14	
1258	12	6	SD40	4150	3.69	22.11	
1259	12	4	SD40	3700	3.29	13.14	
1260	12	6	SD40	4150	3.69	22.11	
1261	12	20	SD40	8470	7.52	150.43	
1262	12	20	SD40	8470	7.52	150.43	
1263	12	4	SD40	4650	4.13	16.52	
1264	12	6	SD40	4200	3.73	22.38	
1265	12	4	SD40	4650	4.13	16.52	
1266	12	6	SD40	4200	3.73	22.38	
1267	12	20	SD40	8470	7.52	150.43	
1268	12	20	SD40	8470	7.52	150.43	
1269	12	4	SD40	7970	7.08	28.31	
					Total:	891.57	

REV.	DESCRIPTION	AUTHOR	CHK.	APPR.	DATE
0A	ISSUED FOR CONSTRUCTION	TKW.	SP./WS.	TNP.	31 JUL 2026

CLIENT NAME : GULF MTP LNG TERMINAL COMPANY LIMITED

CONTRACTOR : POSCO E&C / CAZ CONSORTIUM

GENERATED BY : P PROFESSIONAL ENGINEERING CO.,LTD

DRAWING TITLE :
GULF MTP LNG RECEIVING TERMINAL PROJECT
INSTRUMENT & SUBSTATION BUILDING
2nd BEAM GL.4,5,6,7,8,9,10,11,12

DWG NO :	SHEET	REV NO :	SCALE :	SIZE :
GULF-ISB-CU-FL4000-B-104	19/19	0A	1:20	A1