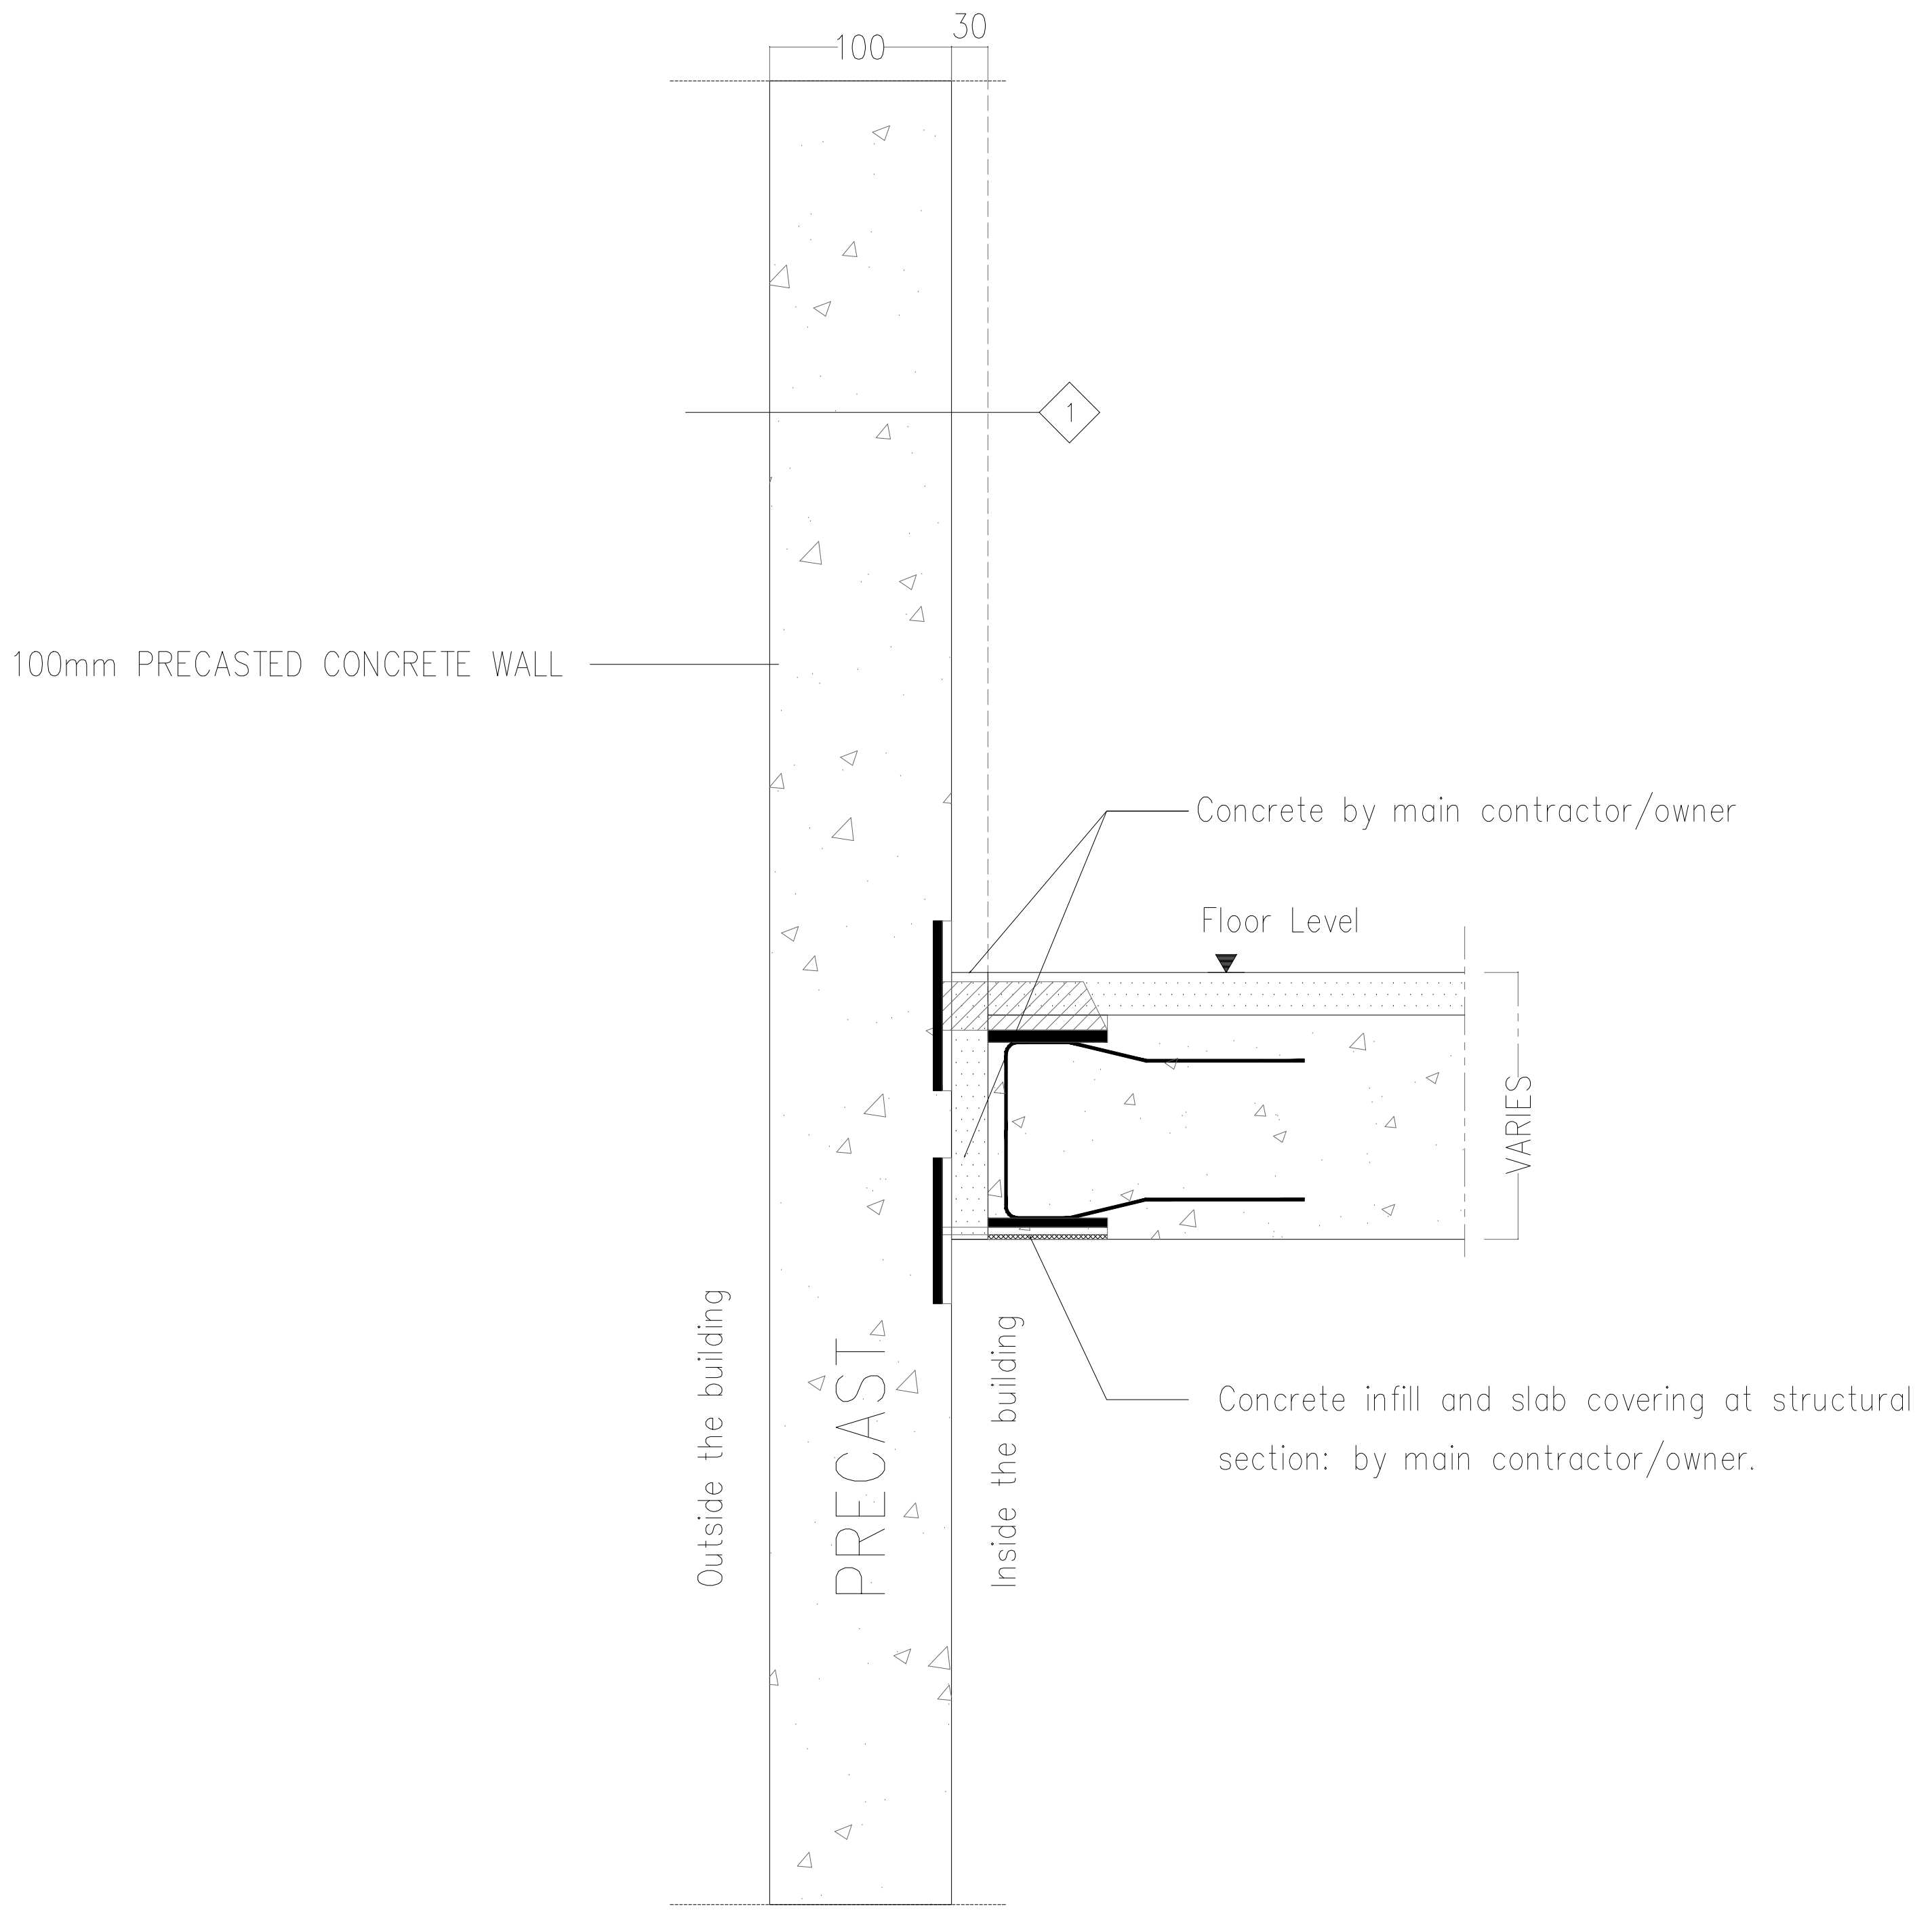
100
30
1
100mm PRECASTED CONCRETE WALL
Concrete by main contractor/owner
Floor Level
VARIES
Outside the building
PRECAST
Inside the building
Concrete infill and slab covering at structural section: by main contractor/owner.

WALL TYPE 1 PRECASTED CONCRETE/ See Engineering Drawing

1 100mm PRECASTED CONCRETE WALL

- Exterioir Wall

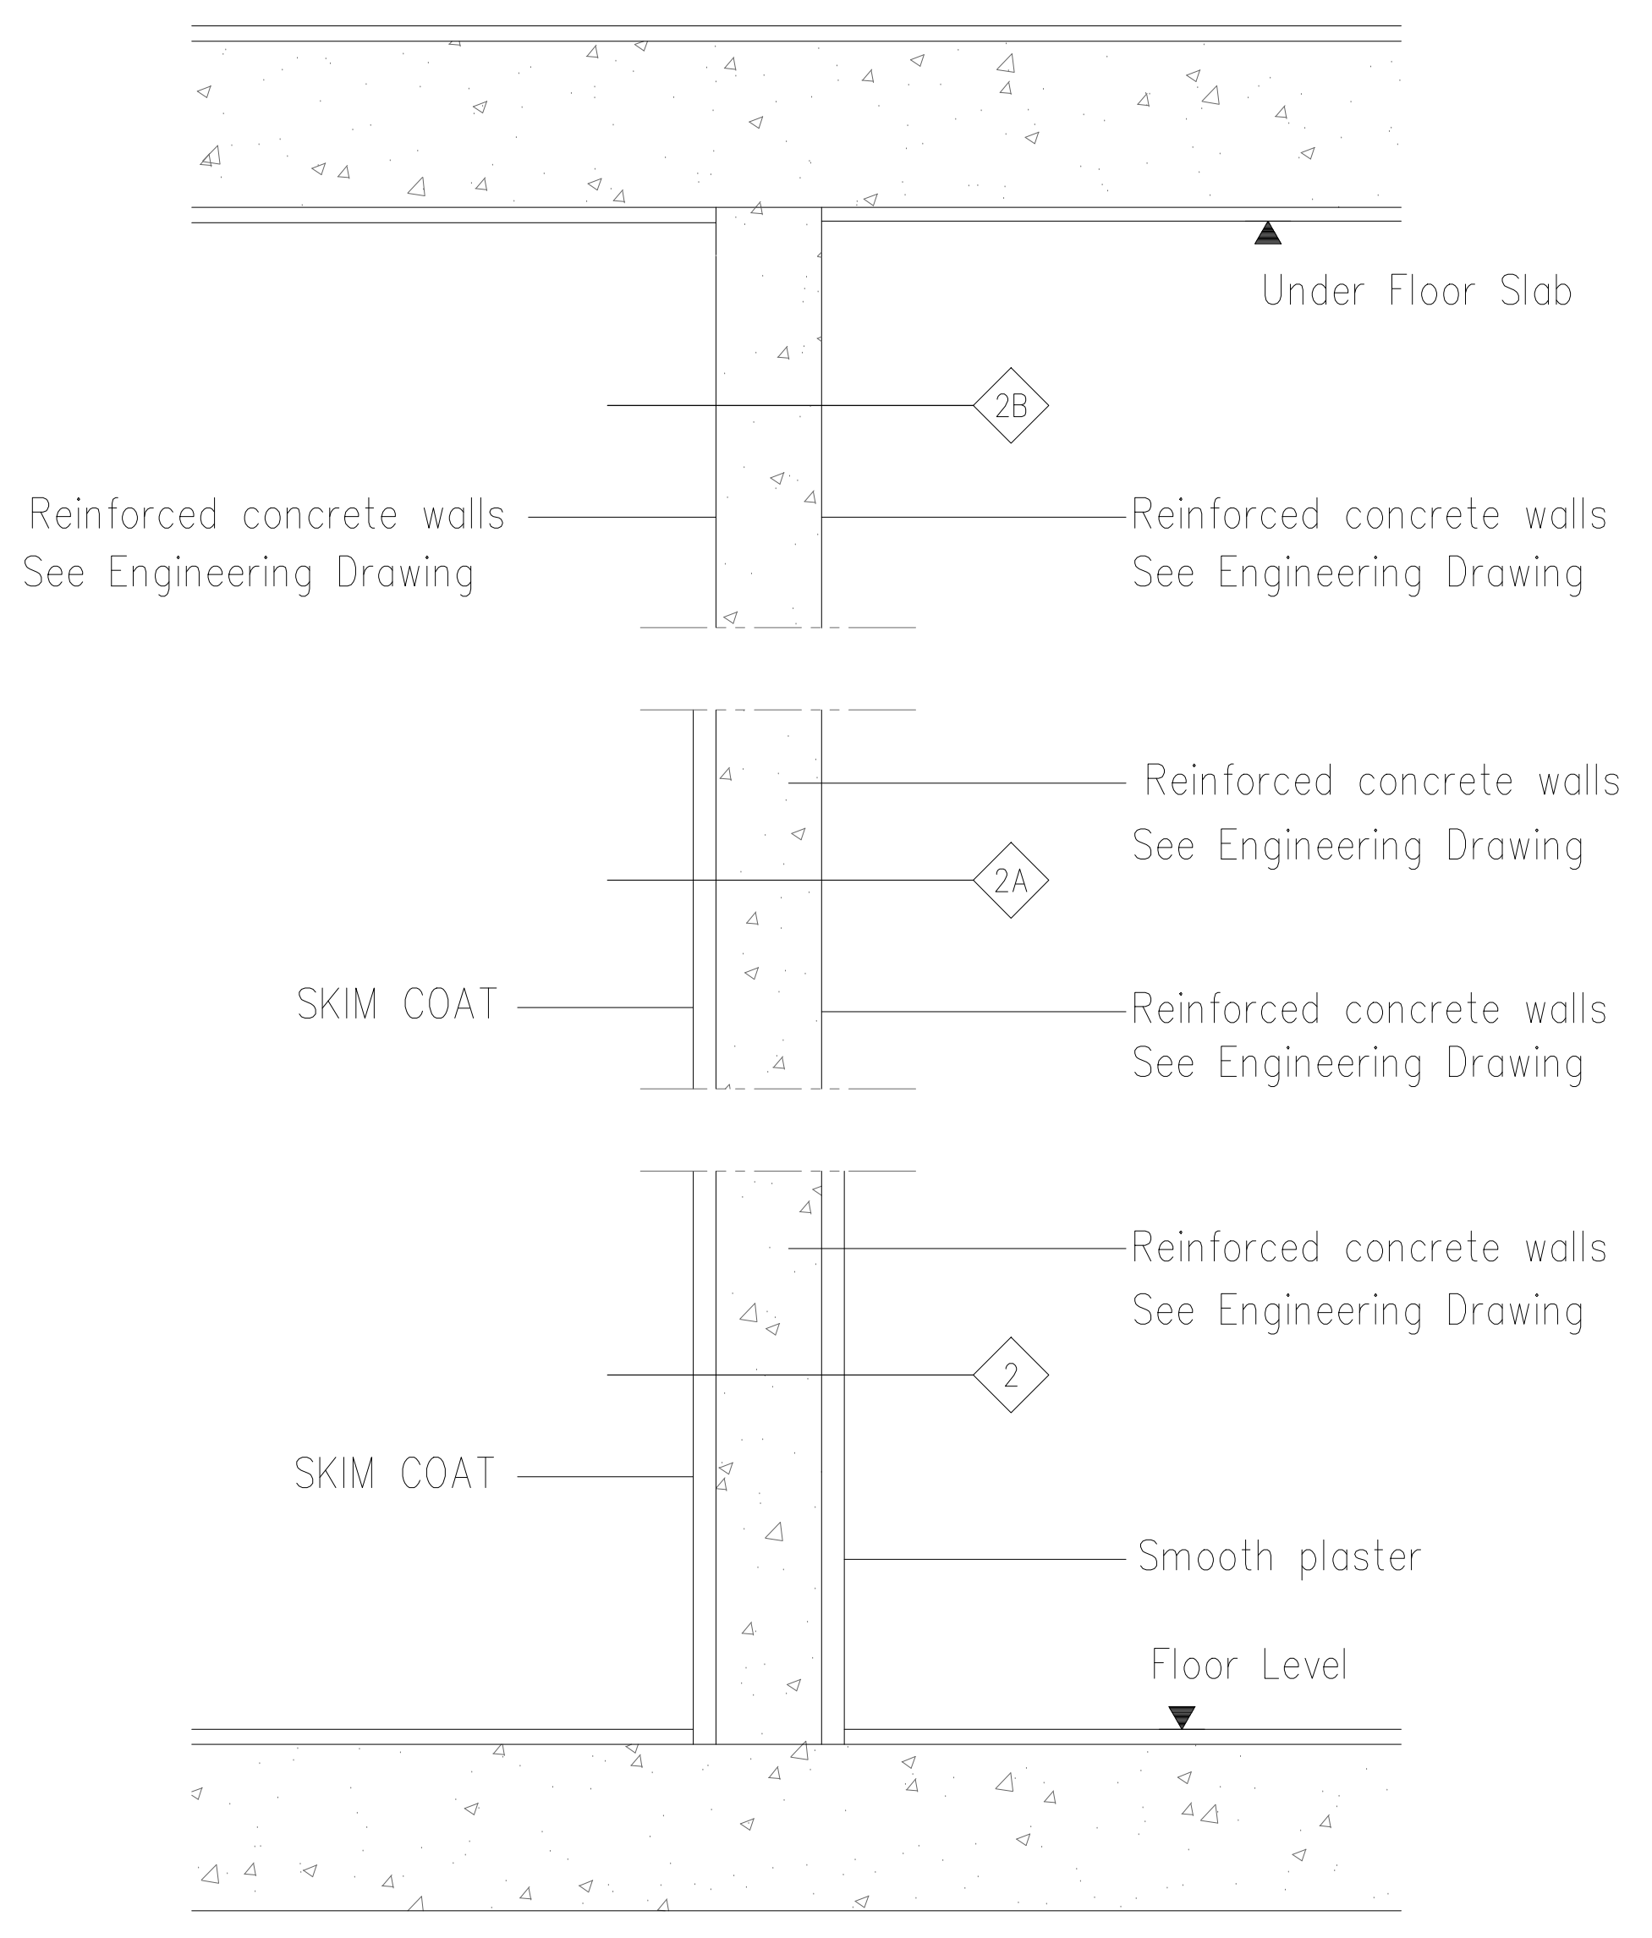

WALL TYPE 2 Reinforced concrete walls / See Engineering Drawing

2 Reinforced concrete walls with 2 sides Smooth plaster

2A Reinforced concrete walls with 1 sides Smooth plaster

2B Reinforced concrete walls

- For MEP room , Fire Stair Case , Lift

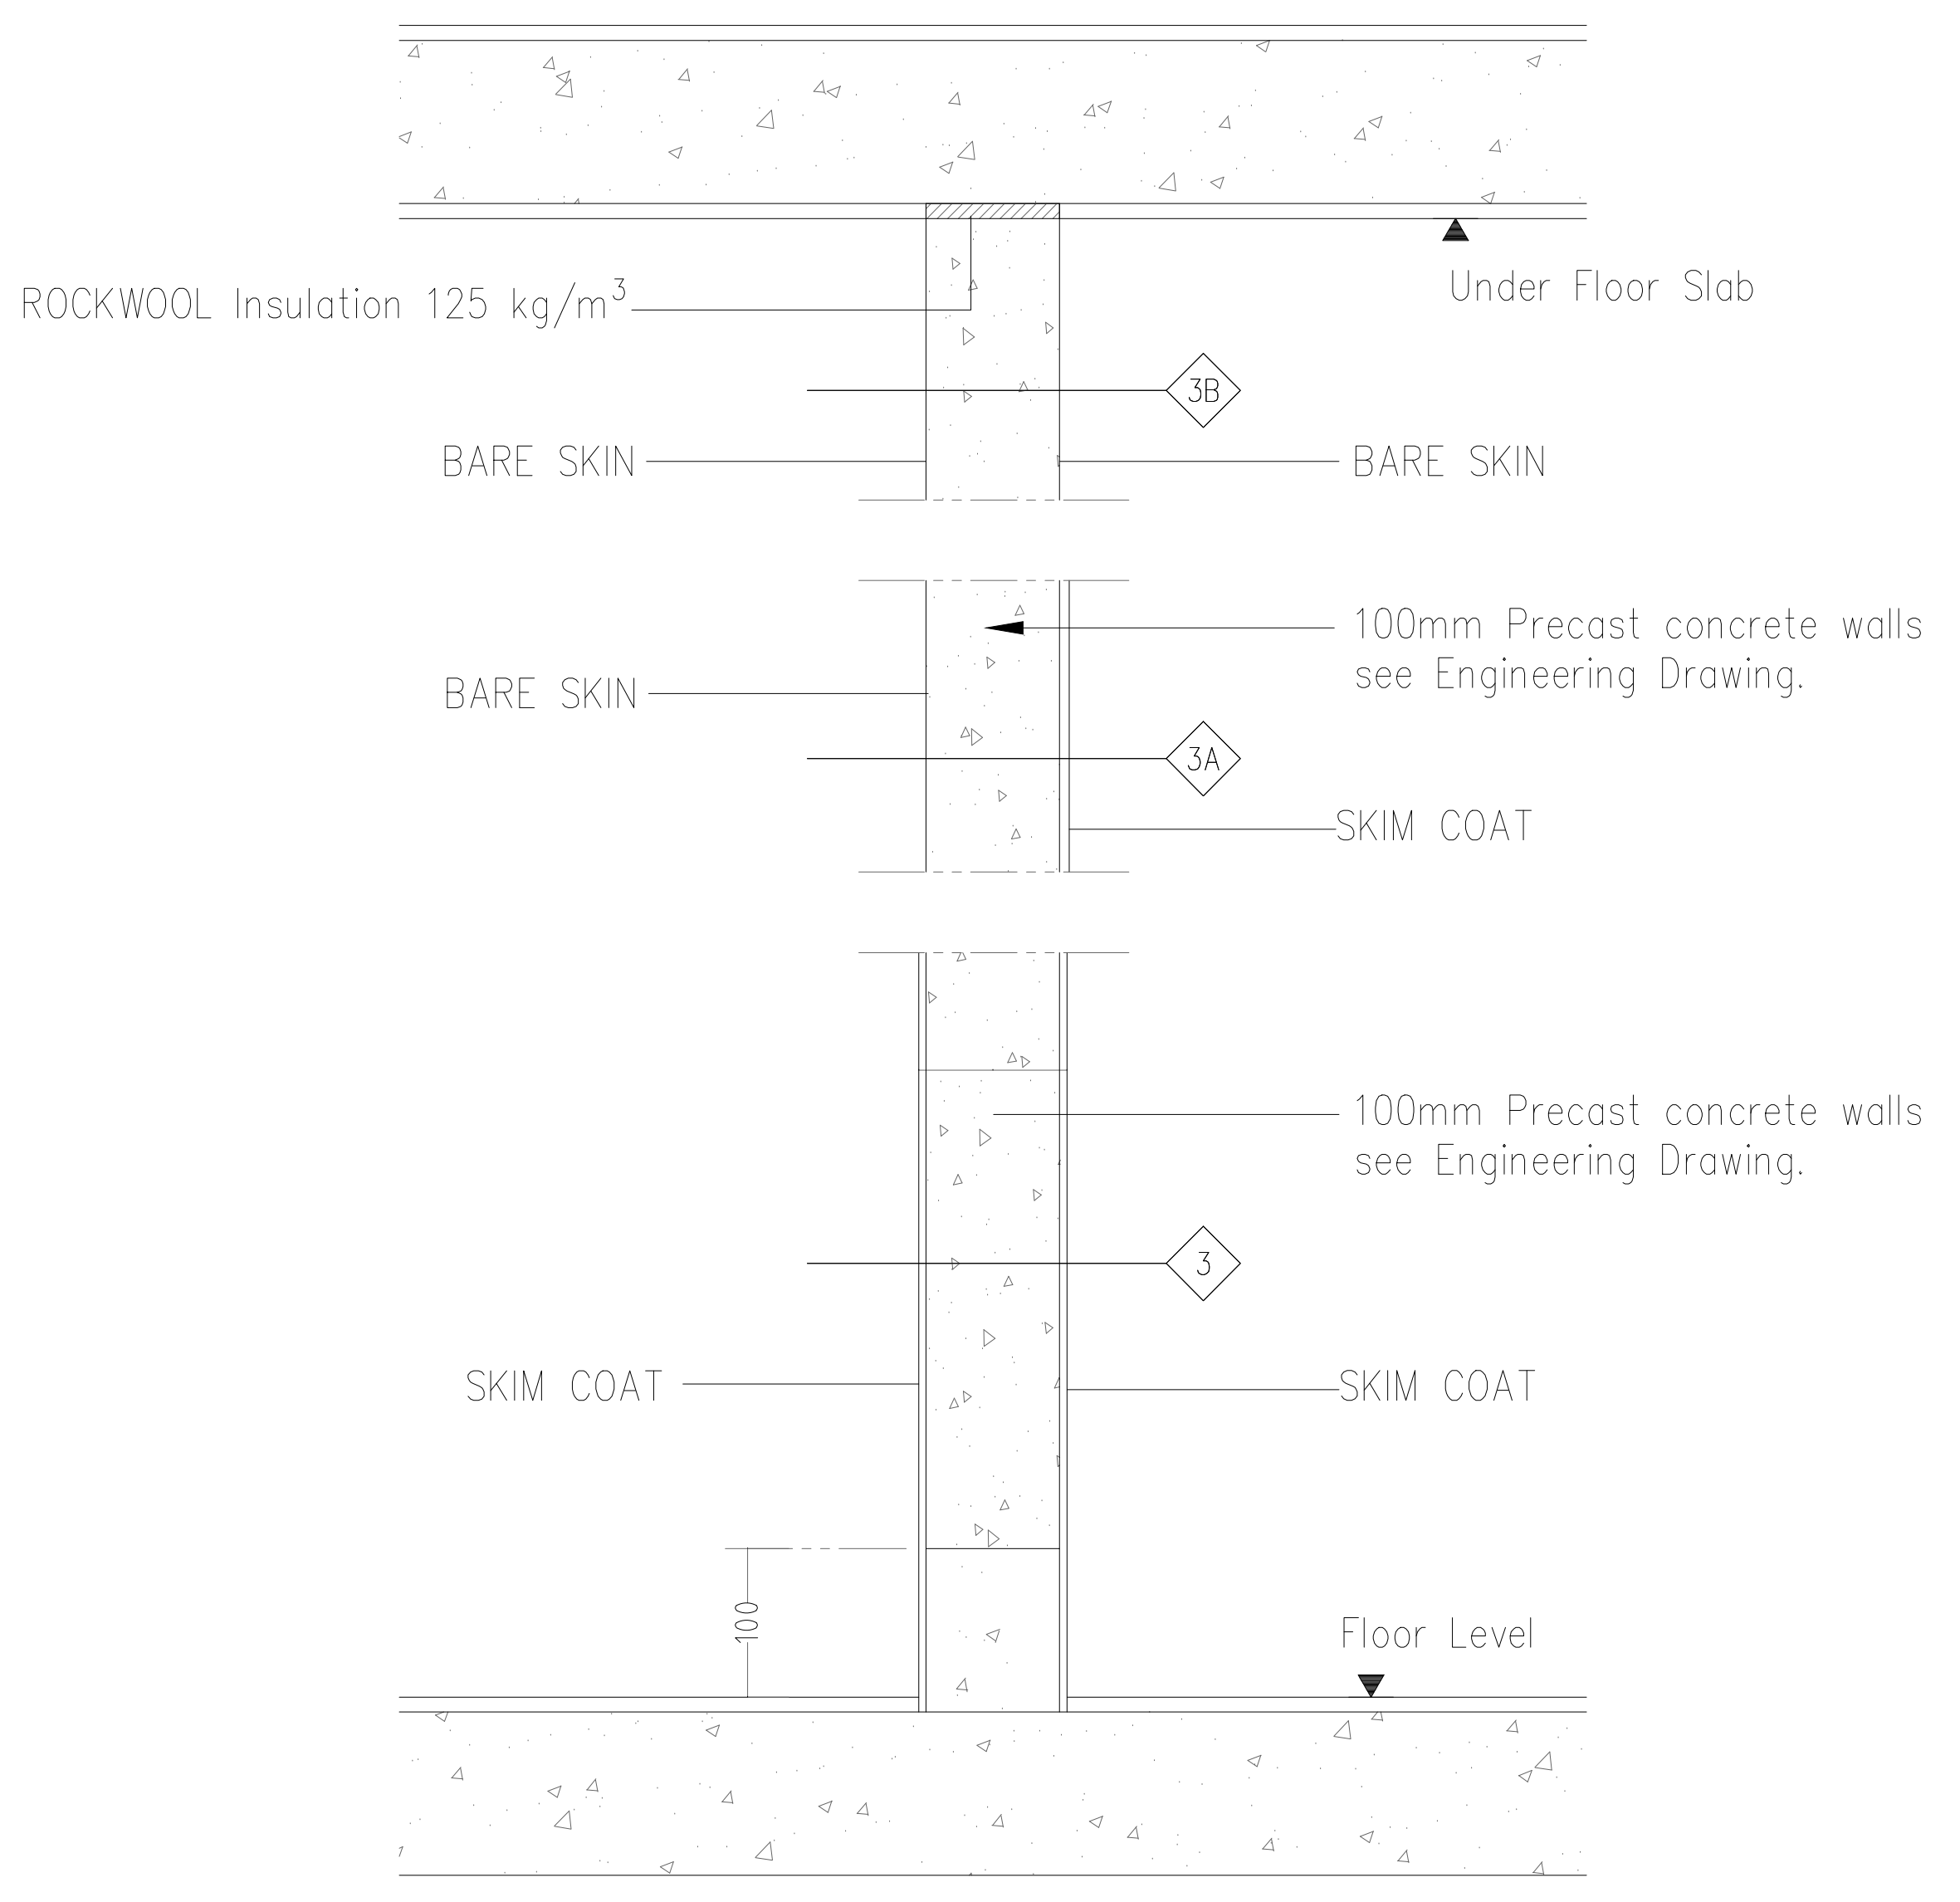

WALL TYPE 3 : Precast concrete walls / See Engineering Drawing

3 Precast concrete walls 100 mm. Thk 2 sides SKIM COAT

3A Precast concrete walls 100 mm. Thk 1 side SKIM COAT

3B Precast concrete walls 100 mm. Thk no SKIM COAT

NEED Fire Resistant Certificate 2 hrs.

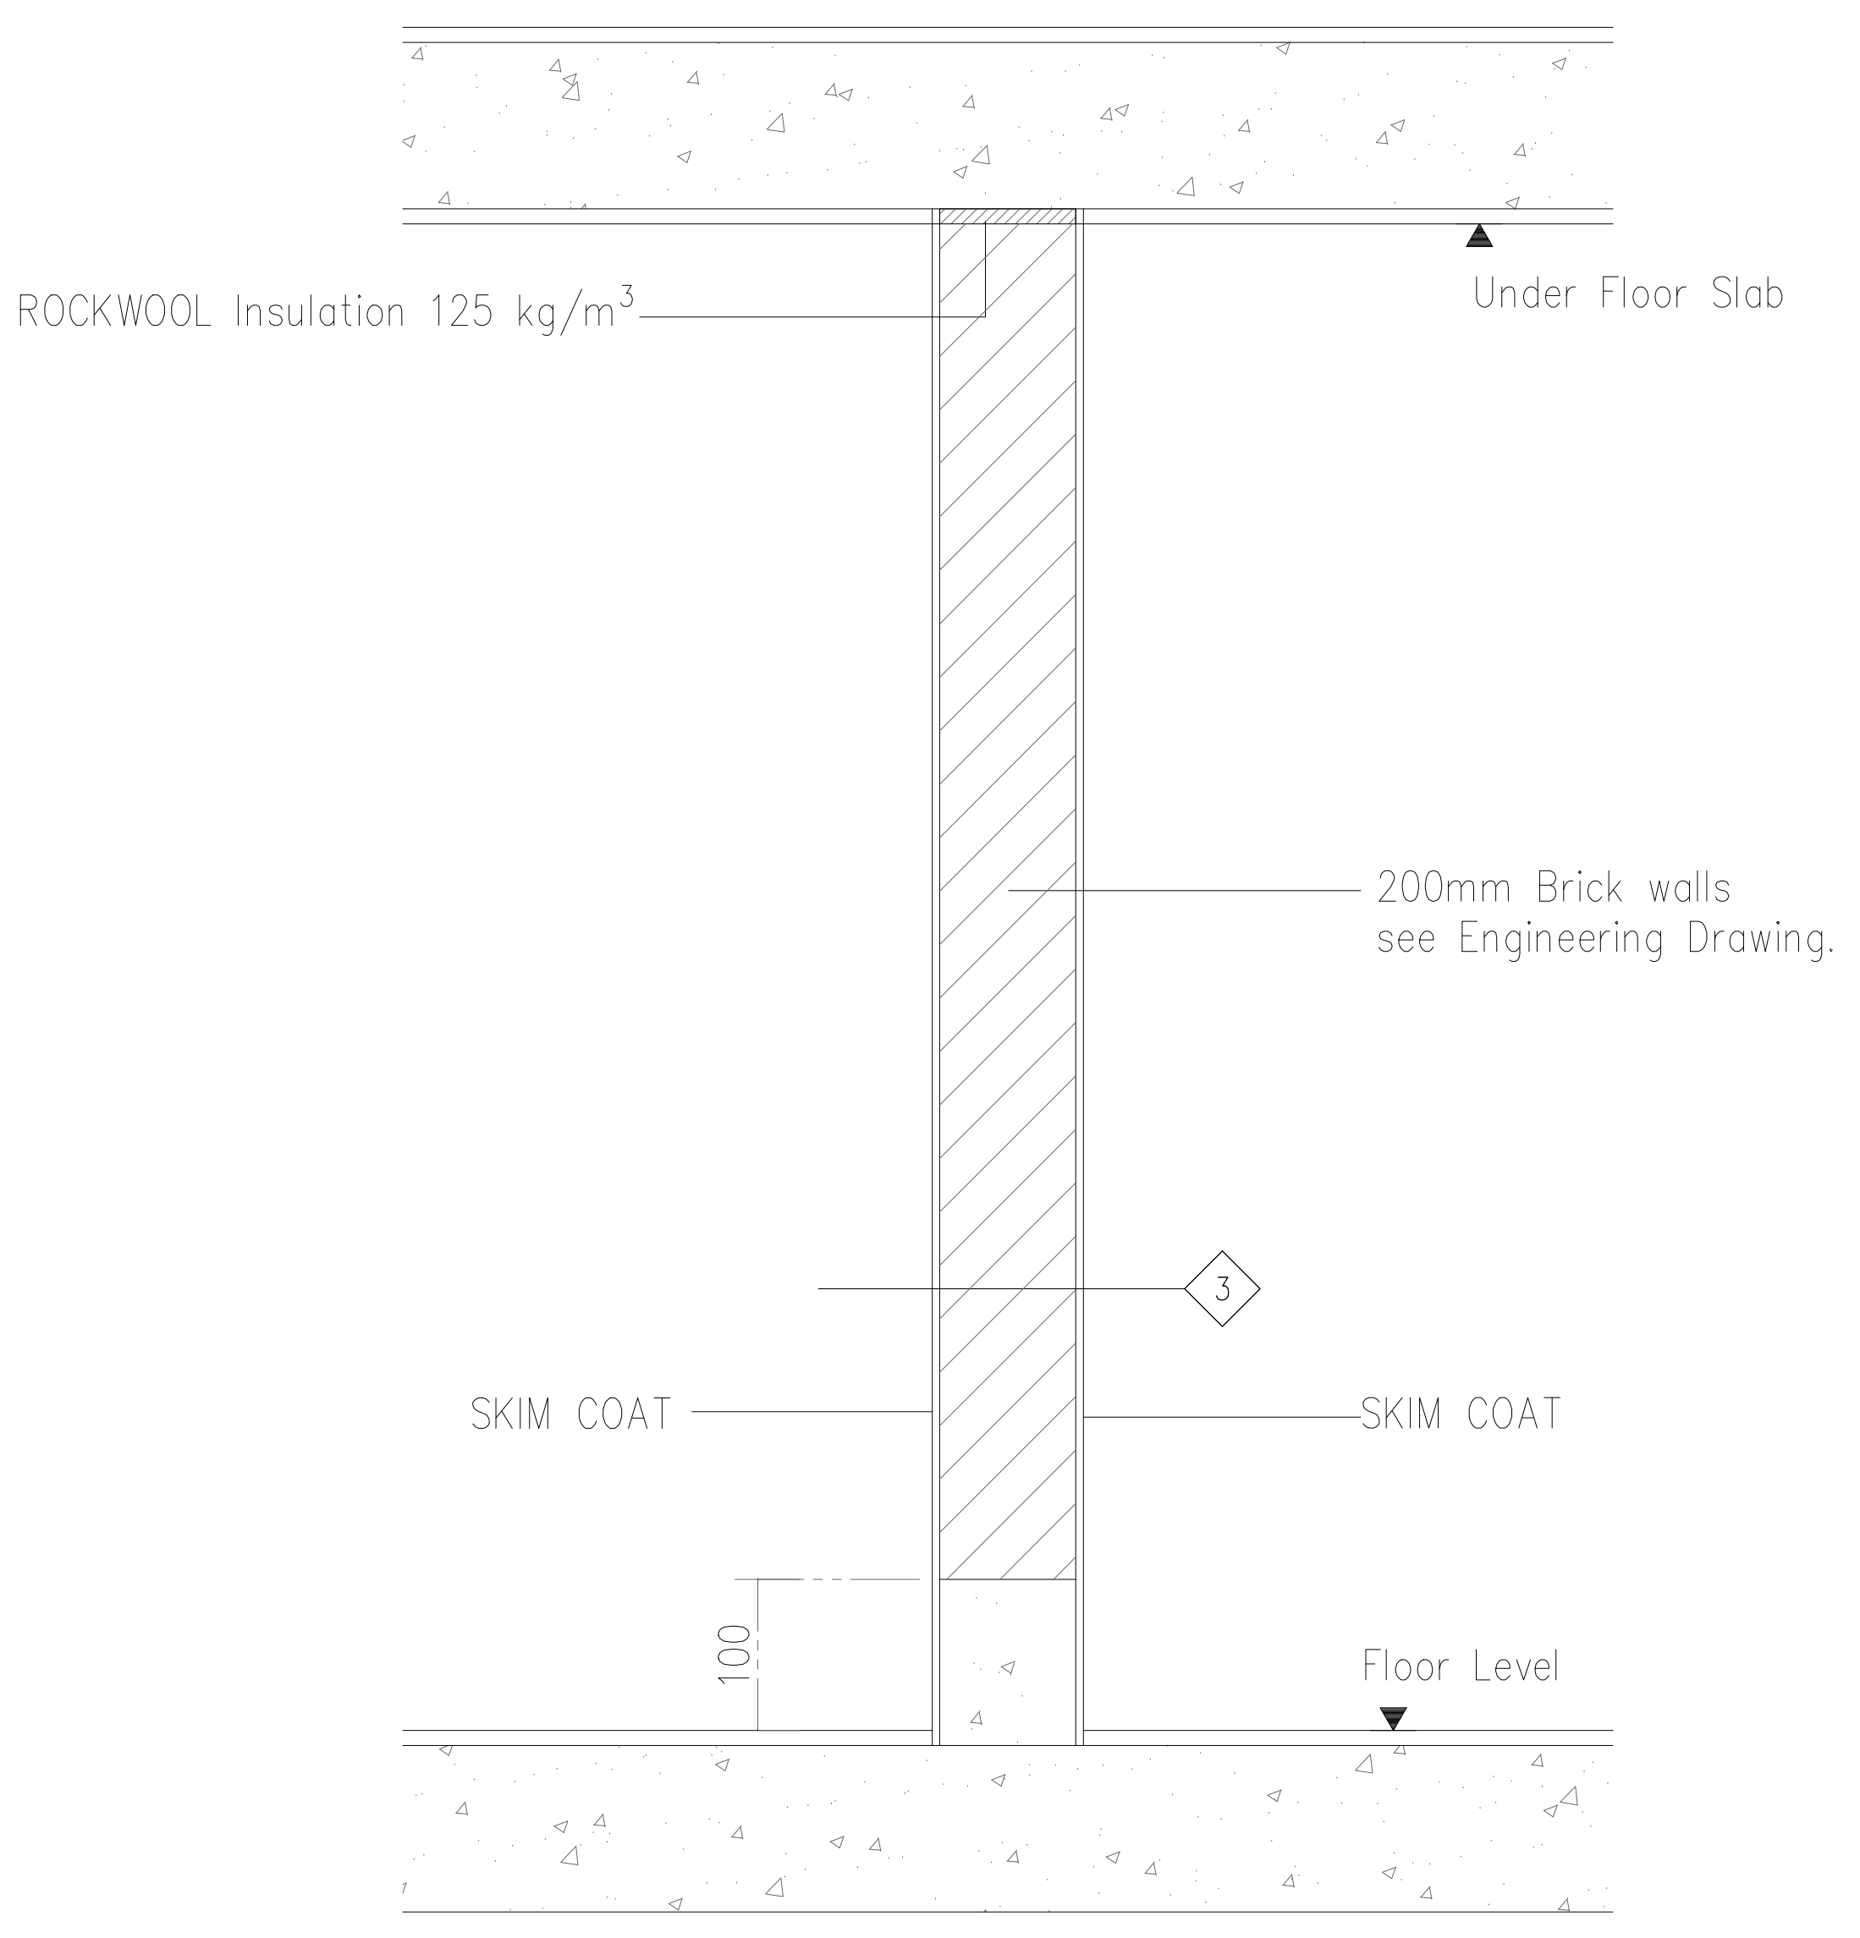

WALL TYPE 4 : Brick walls 200 mm

3 Brick walls 200 mm. Thk 2 sides SKIM COAT

NEED Fire Resistant Certificate 2 hrs.

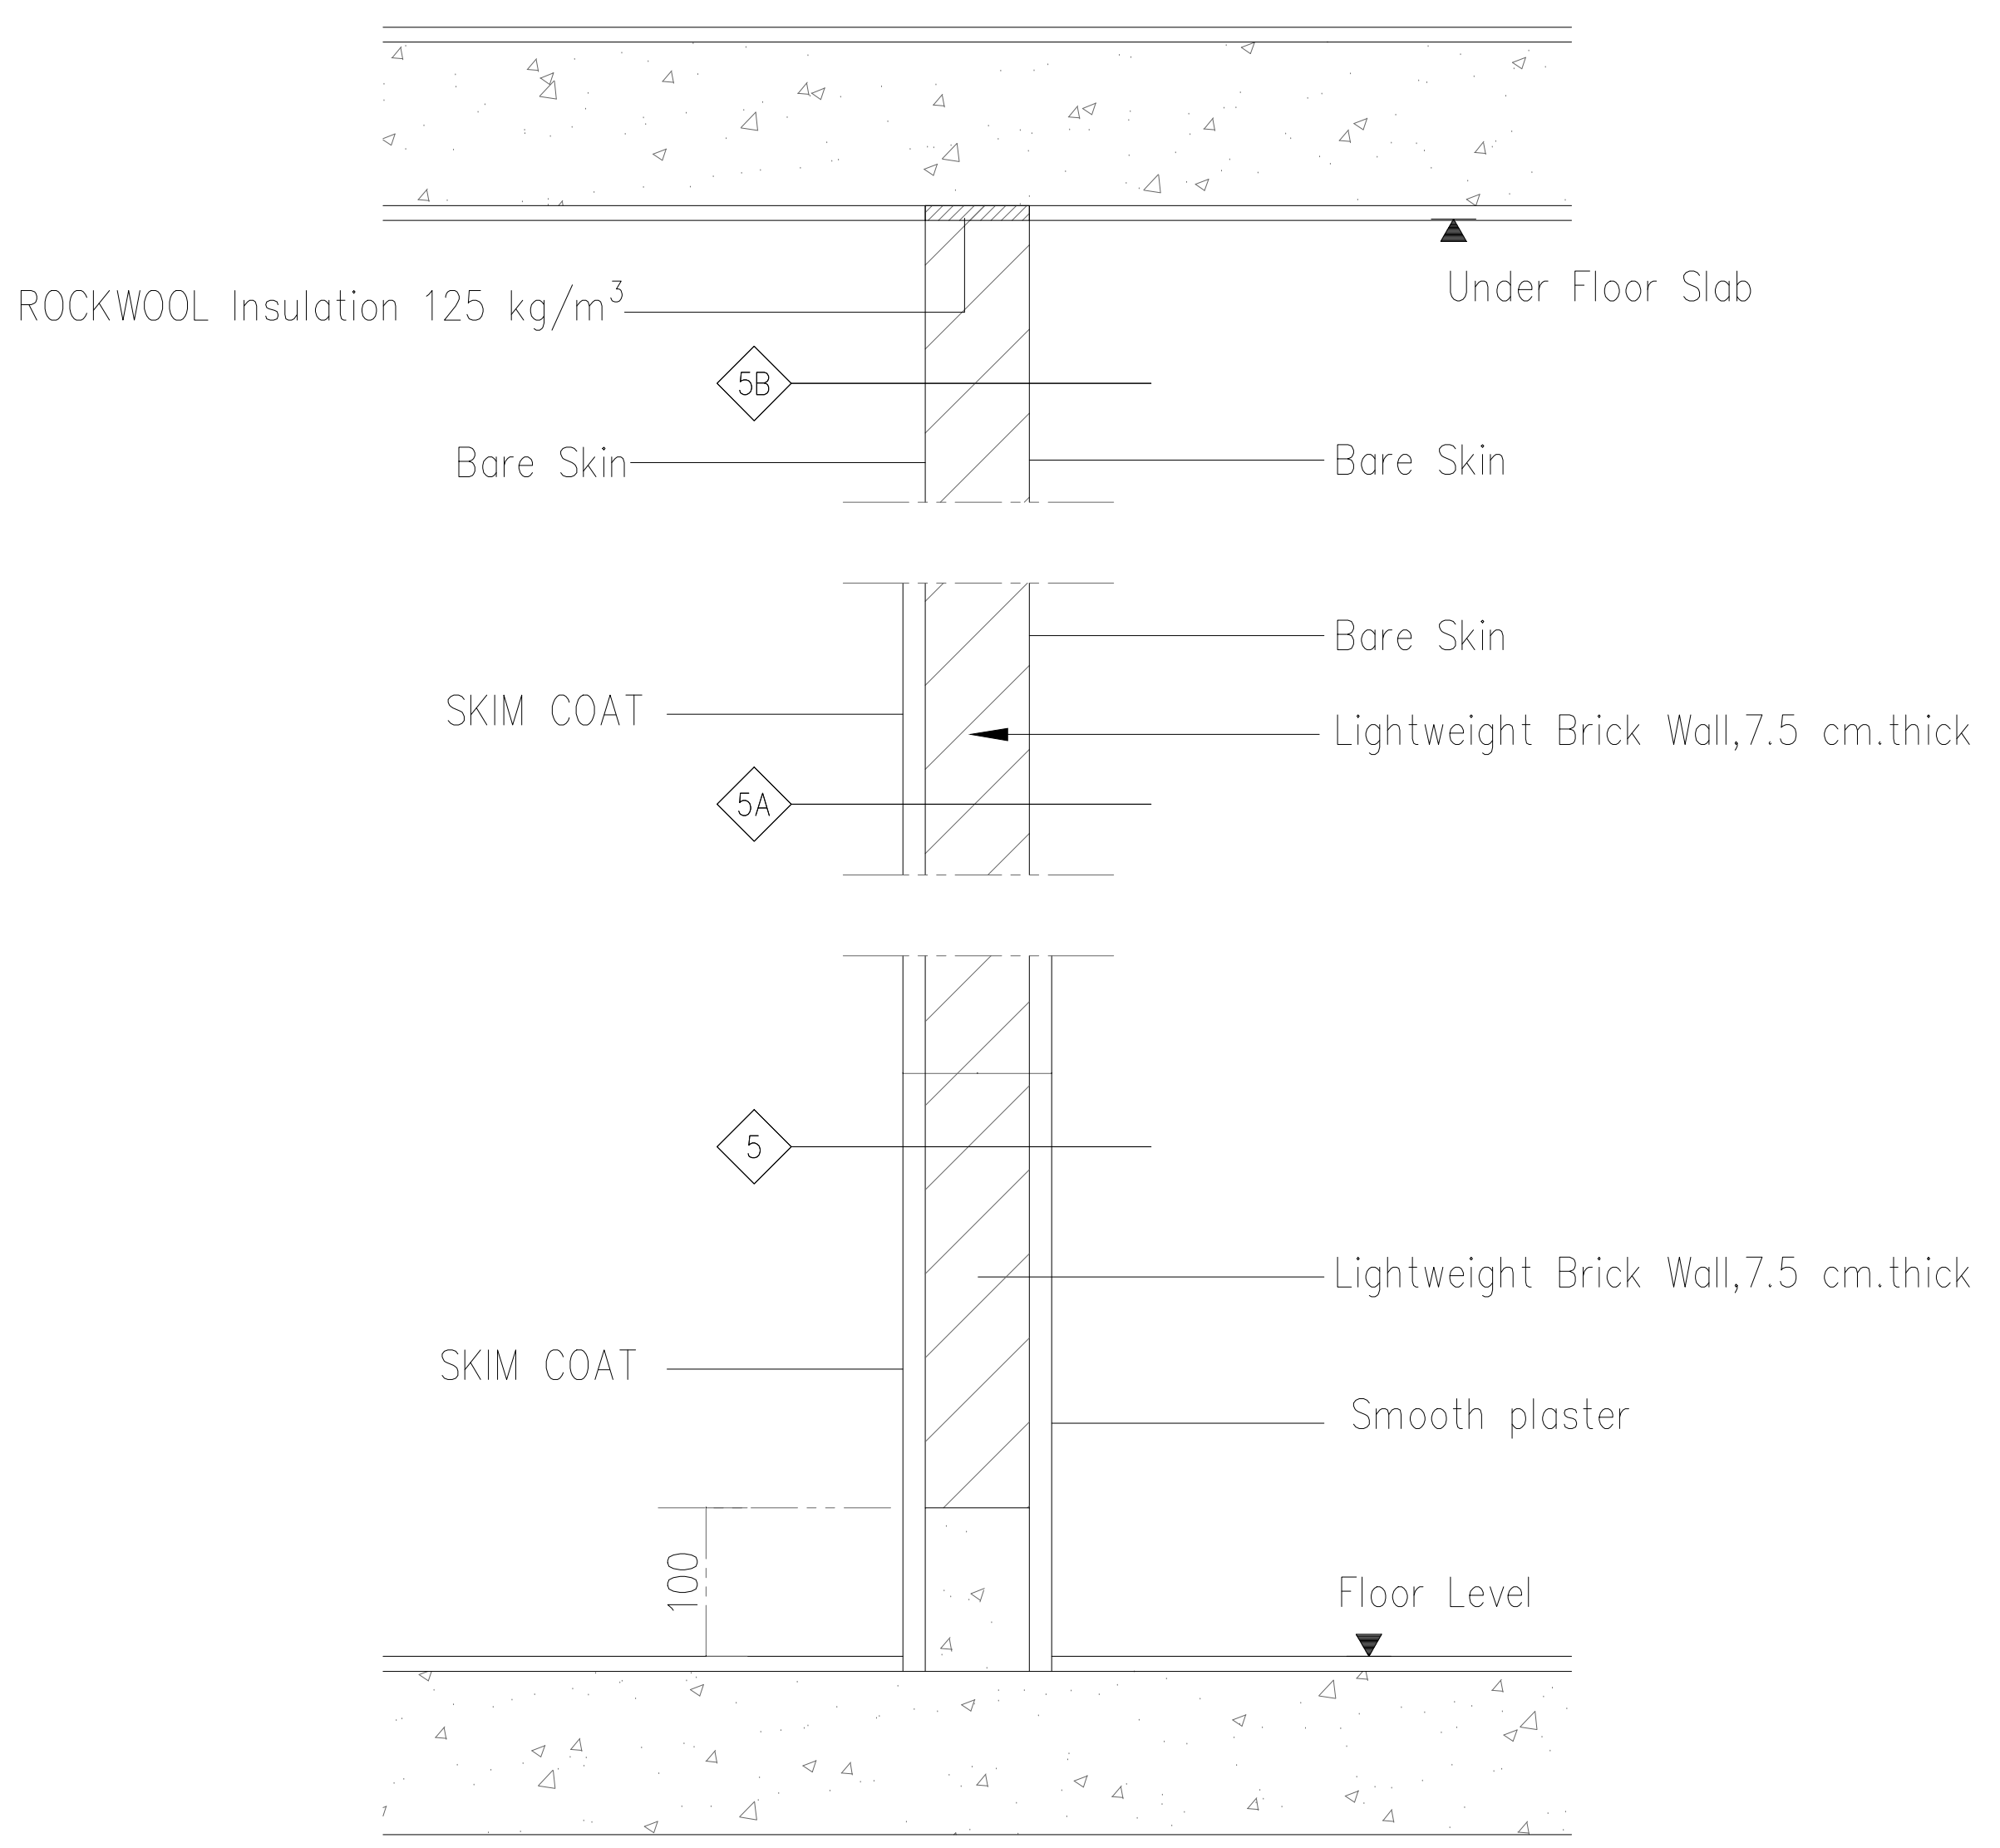
ROCKWOOL Insulation 125 kg/m3
Under Floor Slab
5B
Bare Skin
Bare Skin
Bare Skin
SKIM COAT
Lightweight Brick Wall,7.5 cm.thick
5A
5
Lightweight Brick Wall,7.5 cm.thick
SKIM COAT
Smooth plaster
100
Floor Level

WALL TYPE 5 Lightweight brick AAC (Autoclaved Aerated Concrete) wall 7.5 cm. thick

5 Lightweight Brick Wall,7.5 cm.thick with 2 side smooth plaster

5A Lightweight Brick Wall,7.5 cm.thick with 1 side smooth plaster

5B Lightweight Brick Wall,7.5 cm.thick

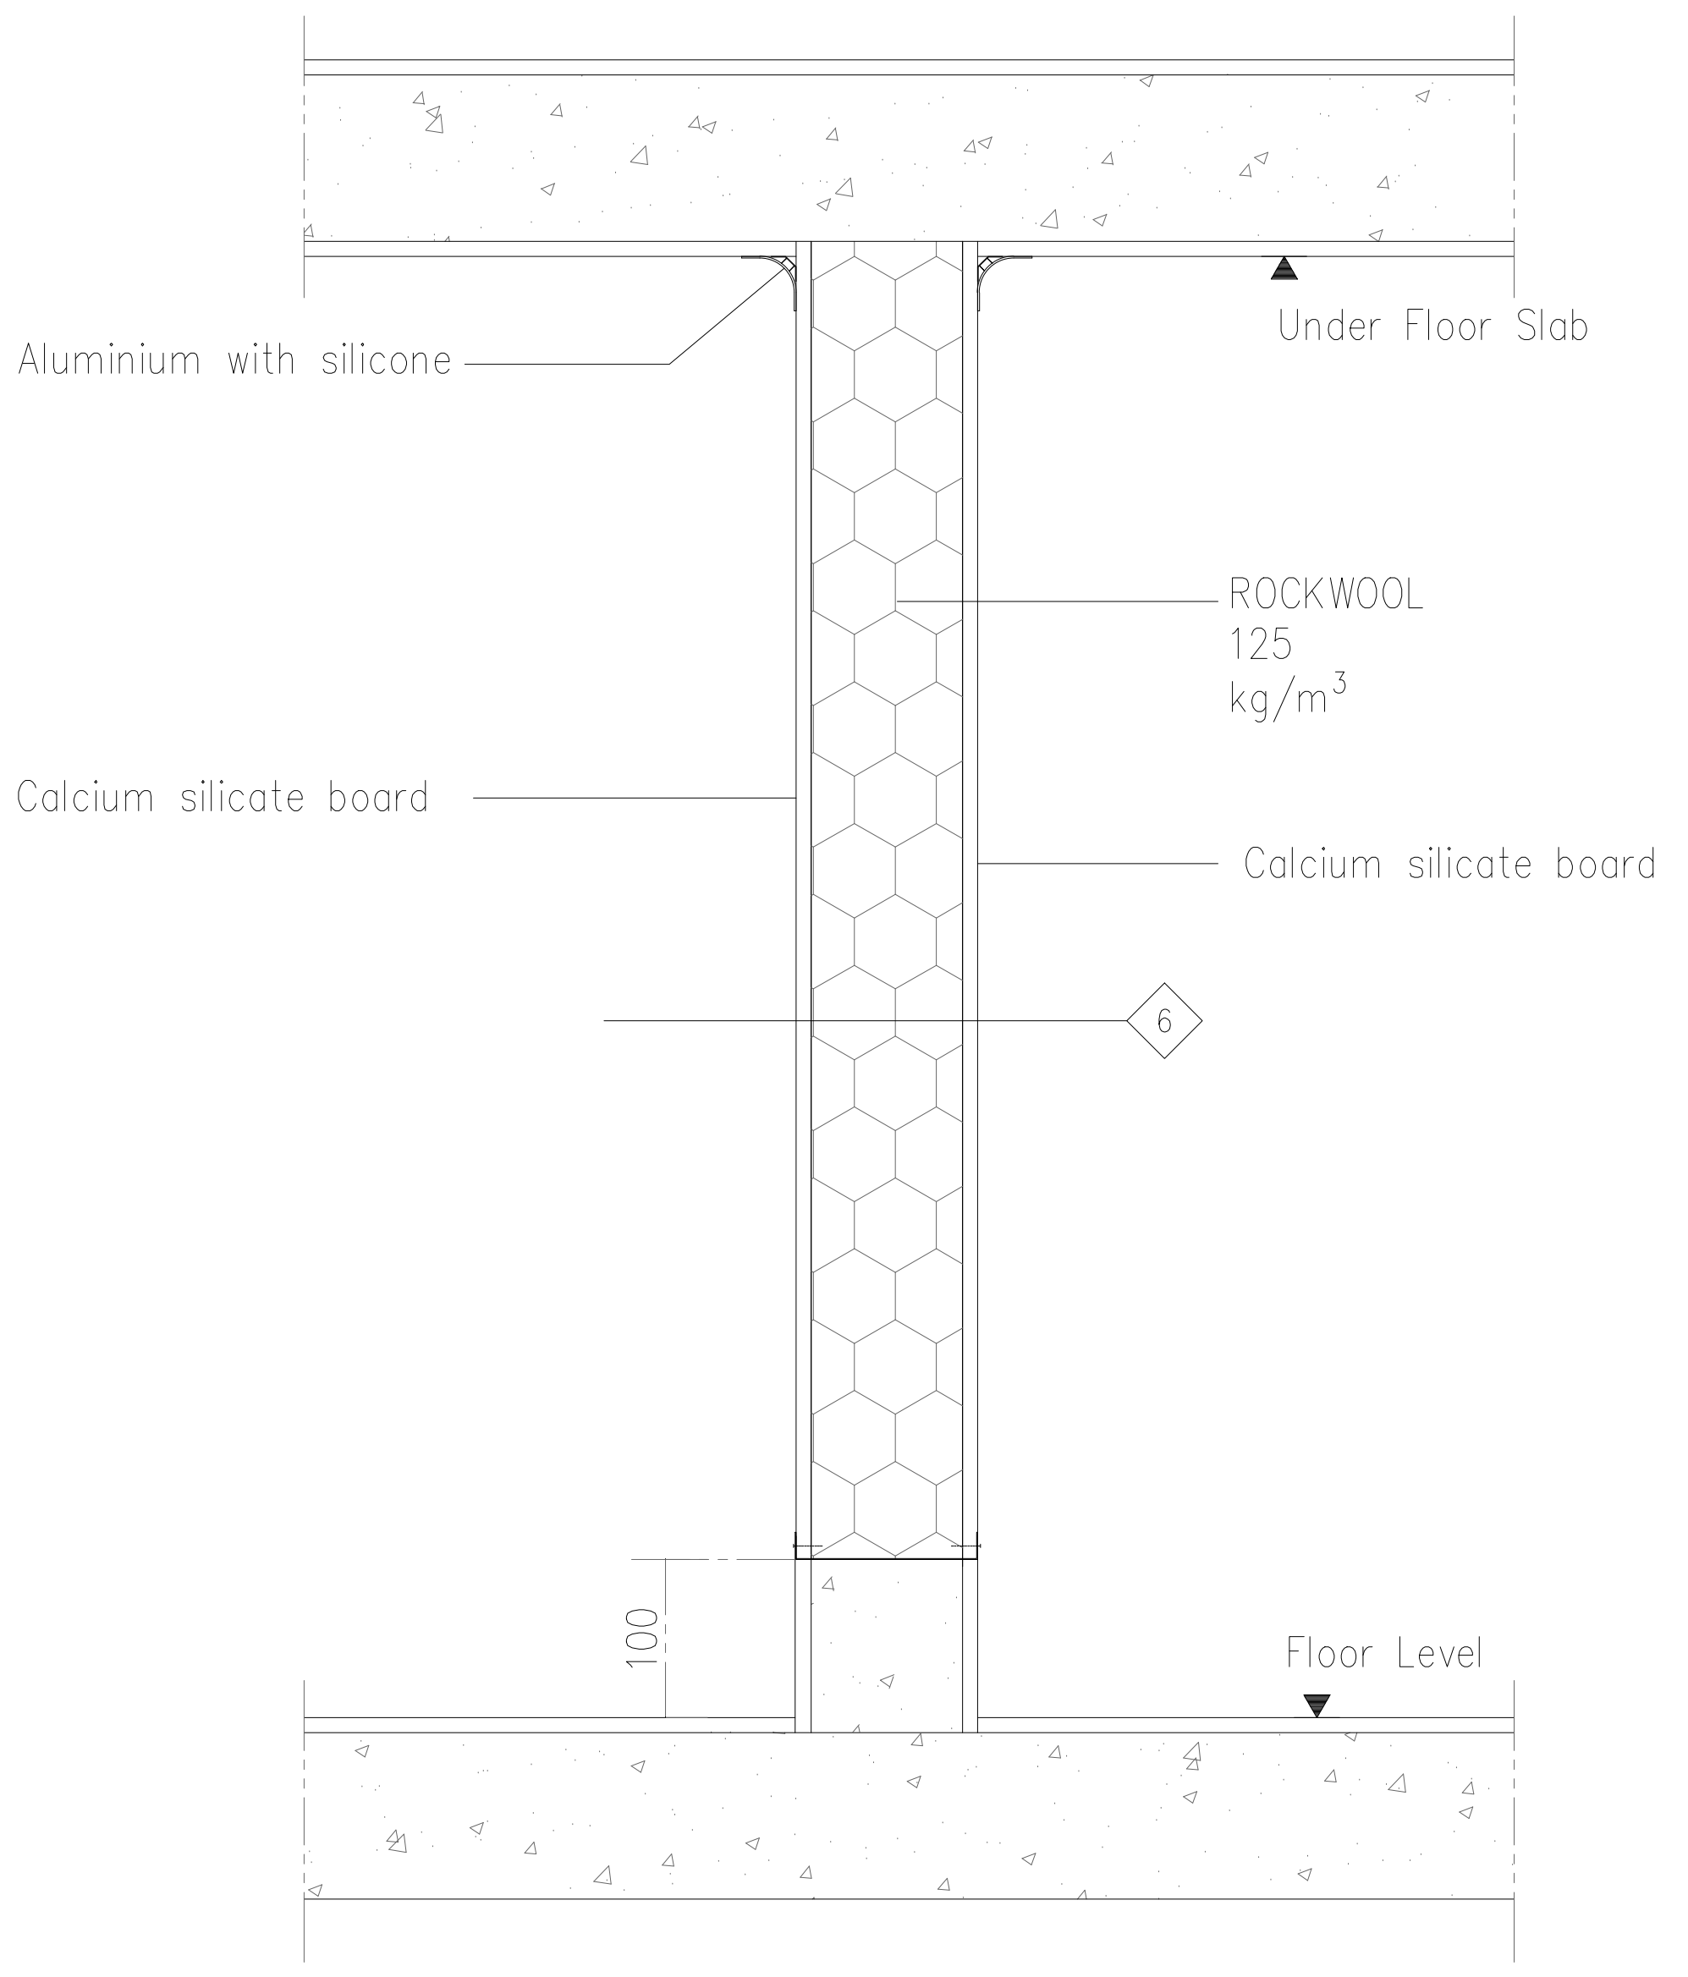

WALL TYPE 6 Calcium silicate board

6 Calcium silicate board 100mm.Thick

NEED Fire Resistant Certificate 2 hrs.

- For Data Hall room

NOTE : THIS PRINT IS OF A CONFIDENTIAL NATURE, IT SHALL NOT BE TRACED,PHOTOGRAPHED,PHOTOSTATED OR REPRODUCED IN ANY MANER,NOR USED FOR ANY PURPOSE WHATSOEVER EXCEPT BY WRITTEN PERMISSION.

CLIENT :

GULF EDGE DC 01

87 Wireless Road, M Thai Tower 11th. Floor, All Seasons Place, Lumpini,
Pathumwan, Bangkok 10330, Thailand

CONTRACTOR :

华西发展(泰国)有限公司
บริษัท หัวซีอ ดีเวลลอปเม้นต์ (ประเทศไทย) จำกัด
HUASHI DEVELOPMENT CO.,LTD
No. 202, Room No. 1403, 14/F, Le Concorde Building,
Ratchadapisek Road, Huaykhwang Sub-District,
Huaykhwang District, Bangkok Metropolitan 10310.

CONSULTANT :

ARbay
บริษัท เอ อาร์ เบย์ จำกัด
ARbay Company Limited
31 st Floor Bangkok Insurance Building
25 South Sathorn road Thungmahamek
Sathorn Bangkok 10120 THAILAND
T +66 (0) 2286 8199
F +66 (0) 2286 2863
info@arbay.co.th

CONSULTANT :

Qbic Engineers & Architects Co.,Ltd.
8 Soi KALONG 4 SANAMBINNAM ROAD,
THASAI SUB-DISTRICT, MUANG NONTHABURI DISTRICT
, NONTHABURI.
Tel 662-950-4374
Fax 662-580-3231
E-Mail : qbic@qbic.co.th, www.qbic.co.th
QBIC ENGINEERS AND ARCHITECTS CO.,LTD.

CONSULTANT :

MITR
MITR TECHNICAL CONSULTANT CO.,LTD.
1168/8 12th FLOOR, LUMPINI TOWER BUILDING,
RAMA IV RD., THUNGMAHAMEK, SATHORN, BANGKOK 10120, THAILAND
TEL : 0-2679-9079-84
FAX : 0-2679-9085 E-mail: mitr_dd@mitr.com

Architect : SIGNATURE
ประกิต พนานุรัตน์ วสถ. 580
ที่อยู่
251/1 ถ.จารุเมือง แขวงรองเมือง เขตปทุมวัน
กรุงเทพมหานคร โทรศัพท์ 02-286-8199

Structural Engineer : SIGNATURE
วิศวกรผู้ออกแบบโครงสร้าง
ณัฐสม สงวนวงษ์ วย 1423
ที่อยู่
2/1 ซ.รามคำแหง 150 ถ.รามคำแหง
แขวง สะพานสูง เขต สะพานสูง กทม. 10240

Structural Inspector : SIGNATURE
วิศวกรผู้ตรวจสอบโครงสร้าง
โกมล จุฑาภัทร วย 964
ที่อยู่
24/18 ซ.นวมินทร์ 129 ถ. นวมินทร์
แขวง นวลจันทร์ เขต บึงกุ่ม กทม. 10230

Electrical Engineer : SIGNATURE
วิศวกรผู้ออกแบบระบบไฟฟ้ากำลัง
นายสุภัทร บูรณวิทย์ วฟก.1265
ที่อยู่
21 ซอยทานสัมฤทธิ์ 13
ตำบลท่าทราย อ.เมืองนนทบุรี จ.นนทบุรี 11000

Mechanical Engineer : SIGNATURE
วิศวกรผู้ออกแบบระบบเครื่องกลและปรับอากาศ
นายประสิทธิ์ เกียวสุนทร วก.1221
ที่อยู่
44/372 ซอยบางกระดี่ 35/1 แขวงแสมดำ
เขตบางขุนเทียน กทม. 10150
ประสิทธิ์

Sanitary Engineer : SIGNATURE
วิศวกรผู้ออกแบบระบบสุขาภิบาล และดับเพลิง
นายทศวรรษ สนั่นฤทธิ์ วส. 215
ที่อยู่
บ้านเลขที่ 99/107 หมู่ที่ 3 ต.ศีรษะจรเข้น้อย
อ.บางเสาธง จ.สมุทรปราการ 10540
ทศวรรษ

ISSUE/REVISION

REV.	DESCRIPTION	DATE
A	90% DEVELOPED	09/05/2026

PROJECT NAME :
GEDC 01
LOCATION:
Nikhom Phattana district, Rayong ,industrial estate,CPGC

BUILDING :
SITE PLAN

90% DEVELOPED

TITLE :
MATERIAL DETAILS

JOB NO.	SCALE 1:100
DRAWN HJC	REF.
CHECKED LJC	DWG.NO. MPK00-90-A-GN-004
APPROVED LXD	
DATE 2026.05.09	