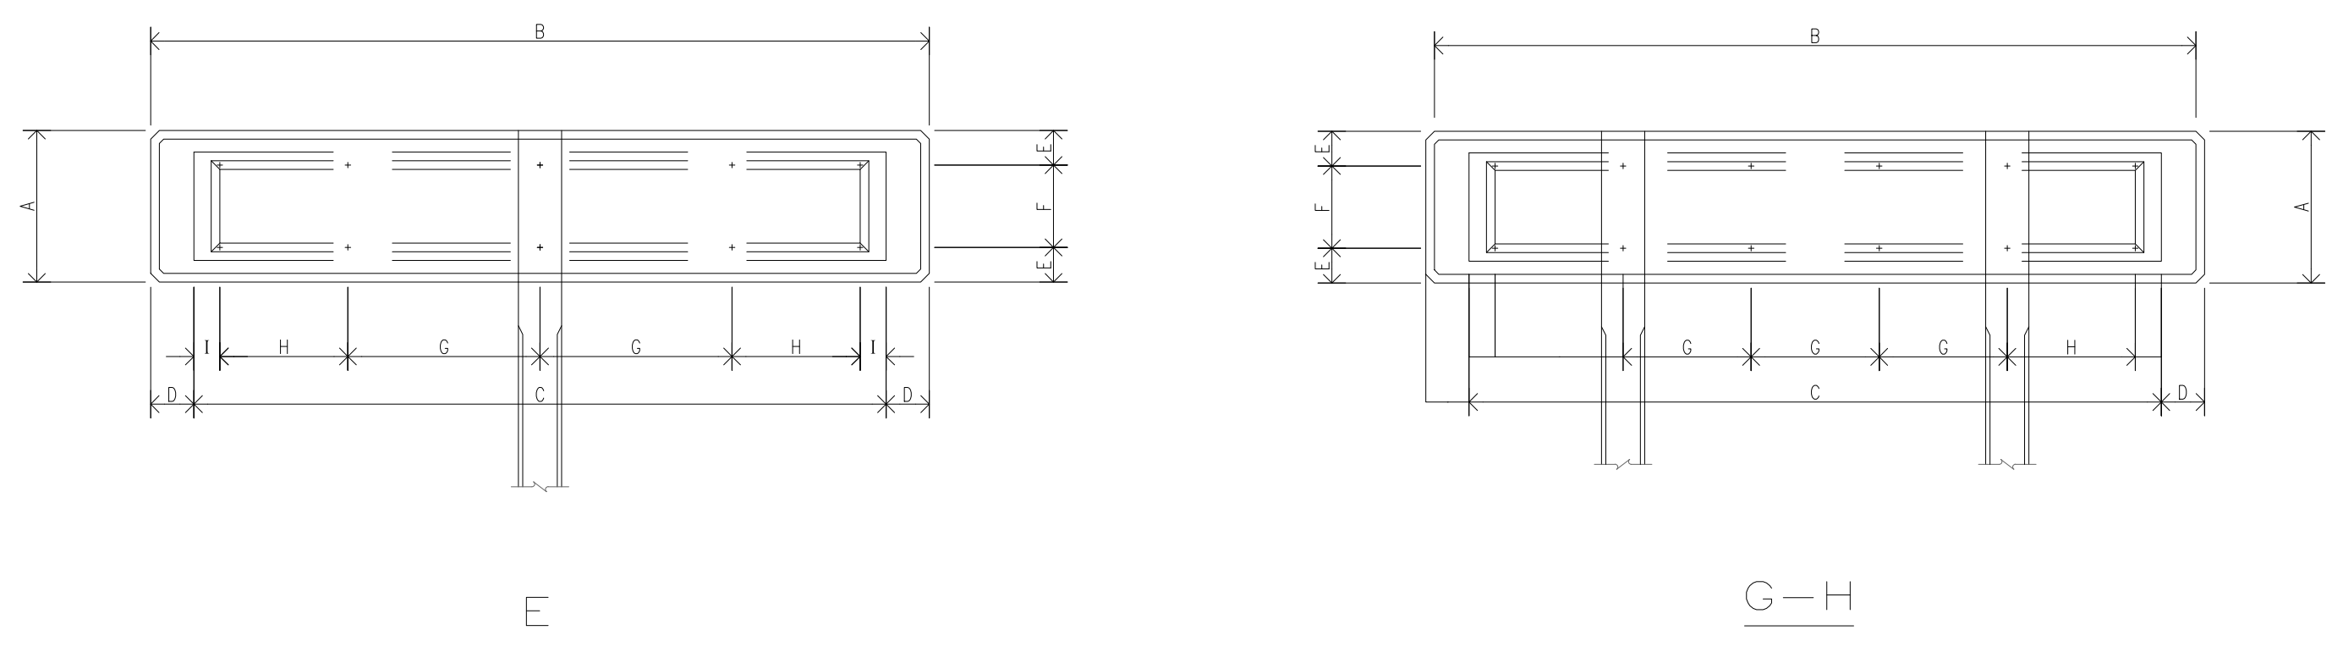

E

G–H

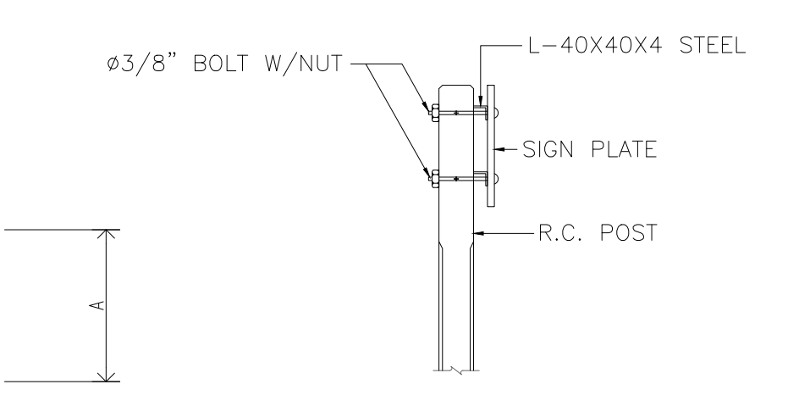
ø3/8" BOLT W/NUT
L–40X40X4 STEEL
SIGN PLATE
R.C. POST

TYPICAL FIXING OF MINOR SIGN
N.T.S.

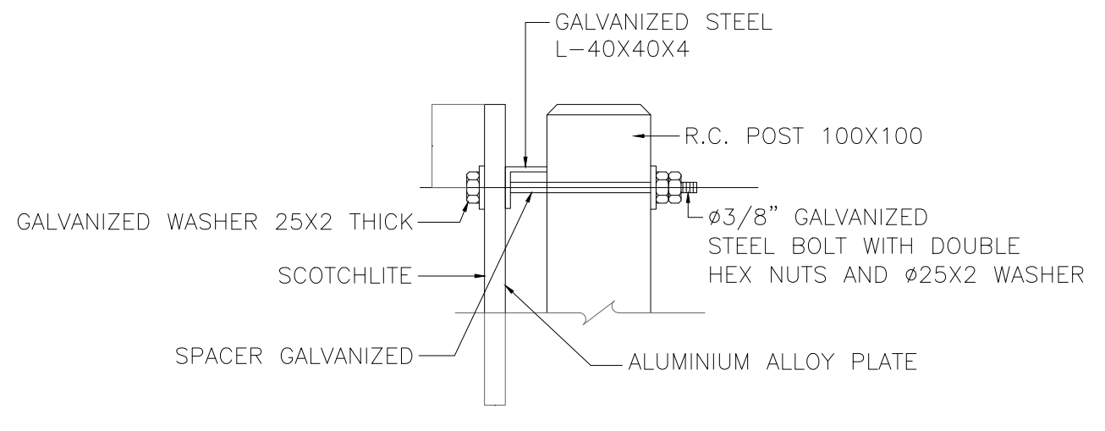
GALVANIZED STEEL L–40X40X4
R.C. POST 100X100
GALVANIZED WASHER 25X2 THICK
ø3/8" GALVANIZED STEEL BOLT WITH DOUBLE HEX NUTS AND ø25X2 WASHER
SCOTCHLITE
SPACER GALVANIZED
ALUMINIUM ALLOY PLATE

TYPICAL FIXING OF SIGN BOARD
N.T.S.

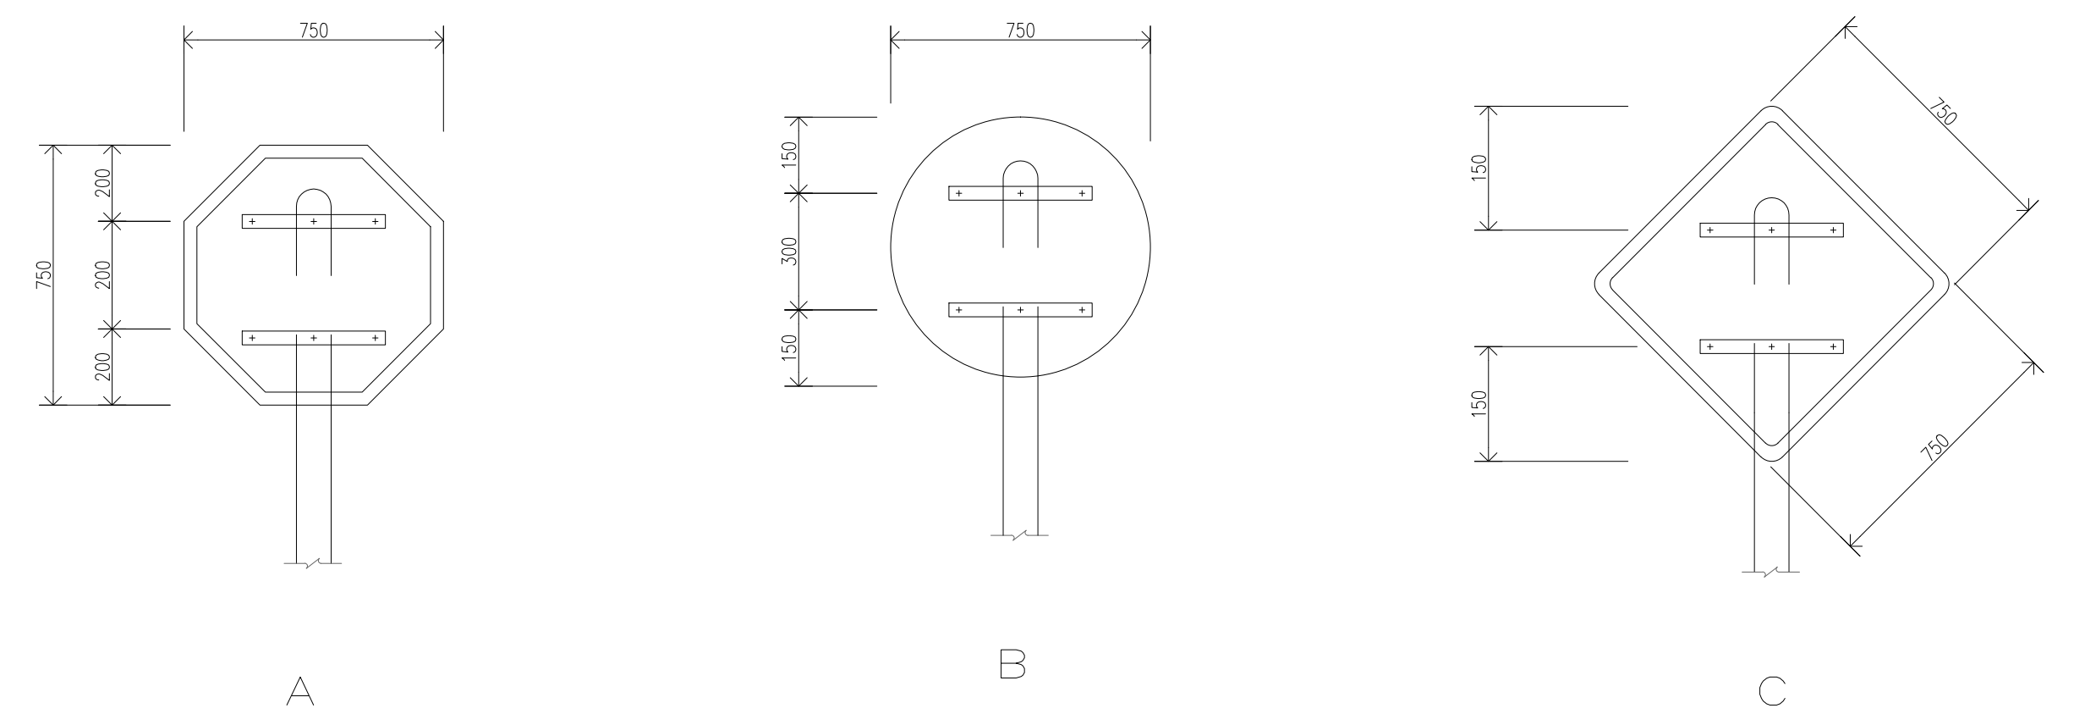
750
150
300
A
B
C

DETAIL OF BOLT HOLE LOCATION
N.T.S

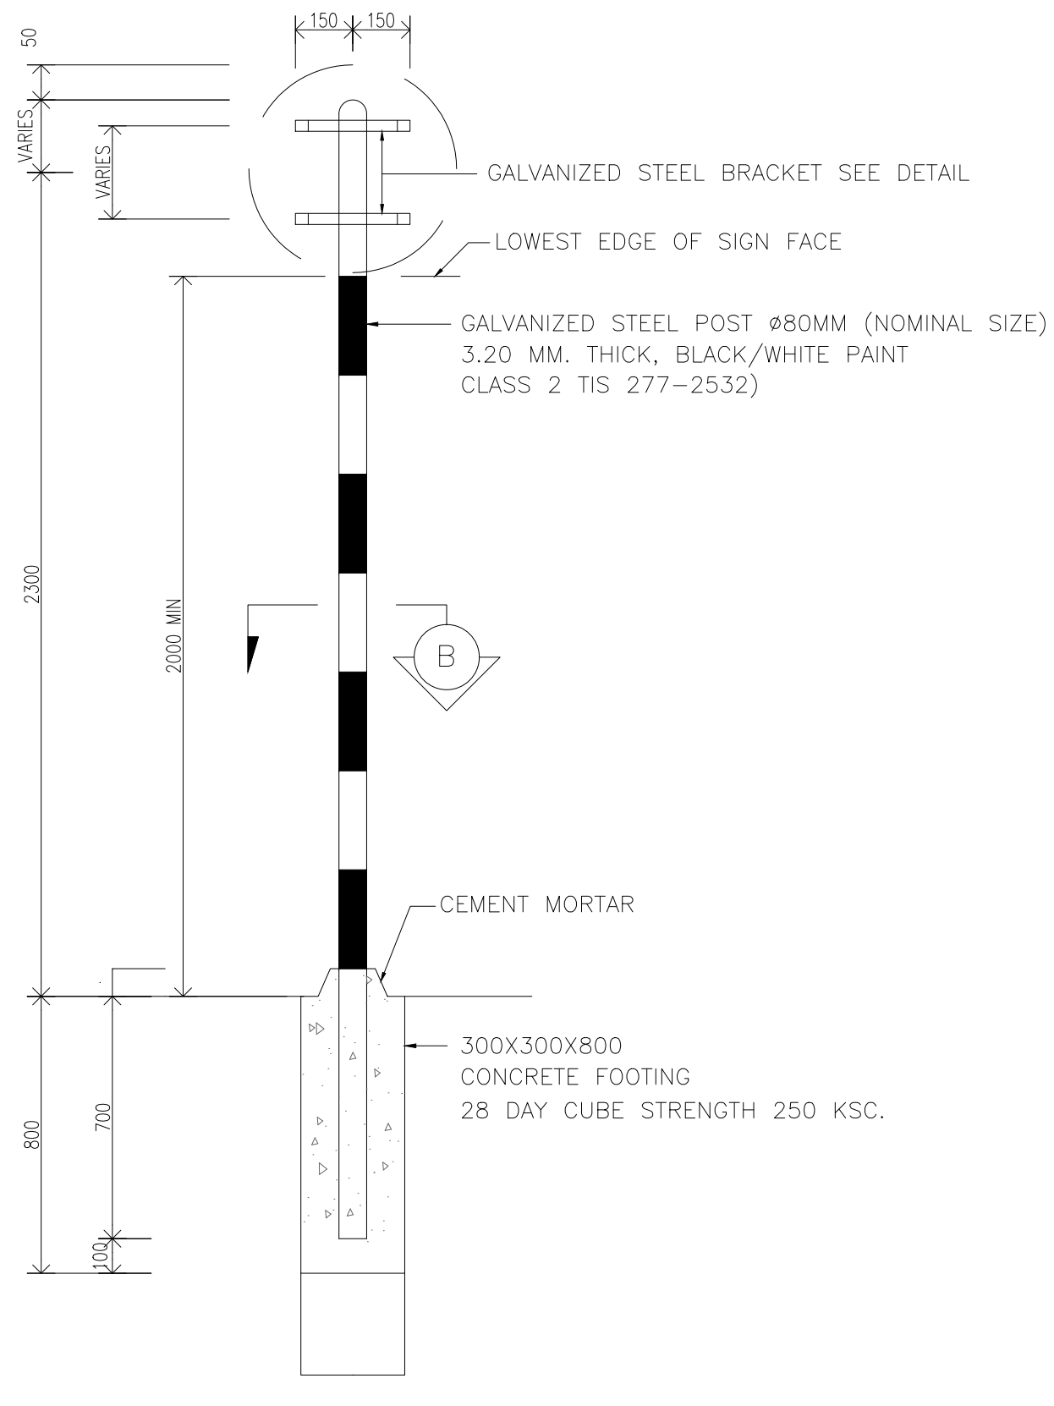
150
50
VARIES
2300
2000 MIN
800
700
100
B
GALVANIZED STEEL BRACKET SEE DETAIL
LOWEST EDGE OF SIGN FACE
GALVANIZED STEEL POST ø80MM (NOMINAL SIZE) 3.20 MM. THICK, BLACK/WHITE PAINT CLASS 2 TIS 277–2532)
CEMENT MORTAR
300X300X800 CONCRETE FOOTING 28 DAY CUBE STRENGTH 250 KSC.

ELEVATION
N.T.S

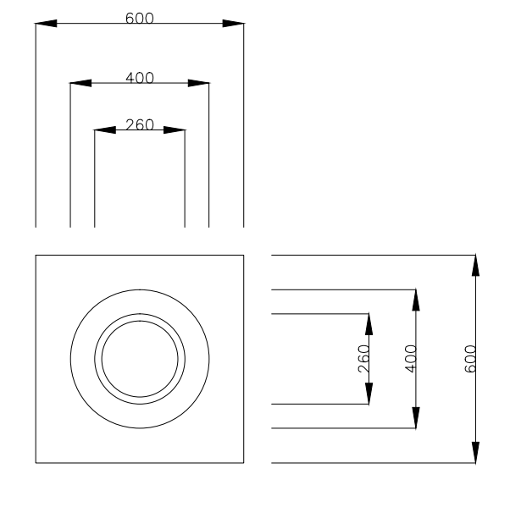

SECTION B
N.T.S

MOUNTING FOR GALVANIZED STEEL POST
N.T.S.

DETAIL		SIZE(CM)		DIMENSION (CM.)								REMARKS
		WITH A	LENGTH B(MIN)	C(MIN)	D	E	F	G	H	I	J	
E	1	35	180	160	10	5	25	37	37	6	2	DISTANCE SIGNS FOR SECONDARY AND PROVINCIAL HIGHWAY
	2	45	180	160	10	10	25	37	37	6	2	
	3	60	180	160	10	5	50	37	37	6	2	
G	1	45	200	200	–	10	25	50	19	6	2	DISTANCE SIGNS FOR PRIMARY HIGHWAY
	2	60	200	200	–	5	50	50	19	6	2	
	3	70	200	200	–	10	50	50	19	6	2	
H	1	35	240	230	5	5	25	50	34	6	2	DESTINATION SIGNS FOR PRIMARY, SECONDARY AND PROVINCIAL HIGHWAY
	2	45	240	230	5	10	25	50	34	6	2	
	3	60	240	230	5	5	50	50	34	6	2	

NOTES :

1. ALL DIMENSIONS ARE IN MILLIMETERS.
1. TYPES OF SIGNS TO BE INSTALLATED SHALL BE AS GIVEN IN THE DRAWINGS OR AS DIRECTED BY THE ENGINEER.
3. TRAFFIC SIGN INSTALLATIONS SHALL BE IN ACCORDANCE WITH THE MANUAL OF TRAFFIC CONTROL DEVICES AS PUBLISHED BY DOH.
4. PAINT FOR THE FINISH COAT SHALL CONFORM TO SPECIFICATIONS.
5. FRAME AND GUIDE SIGNS SHALL BE GALVANIZED STRUCTURAL STEEL 40X40X4 MMS. FASTENED TO SIGN PLATE AND POST BY ø3/8" NUT.
6. THE FOLLOWING TABLE GIVES BOLT HOLE DETAILS FOR DESTINATION SIGN AND DISTANCE SIGNS.

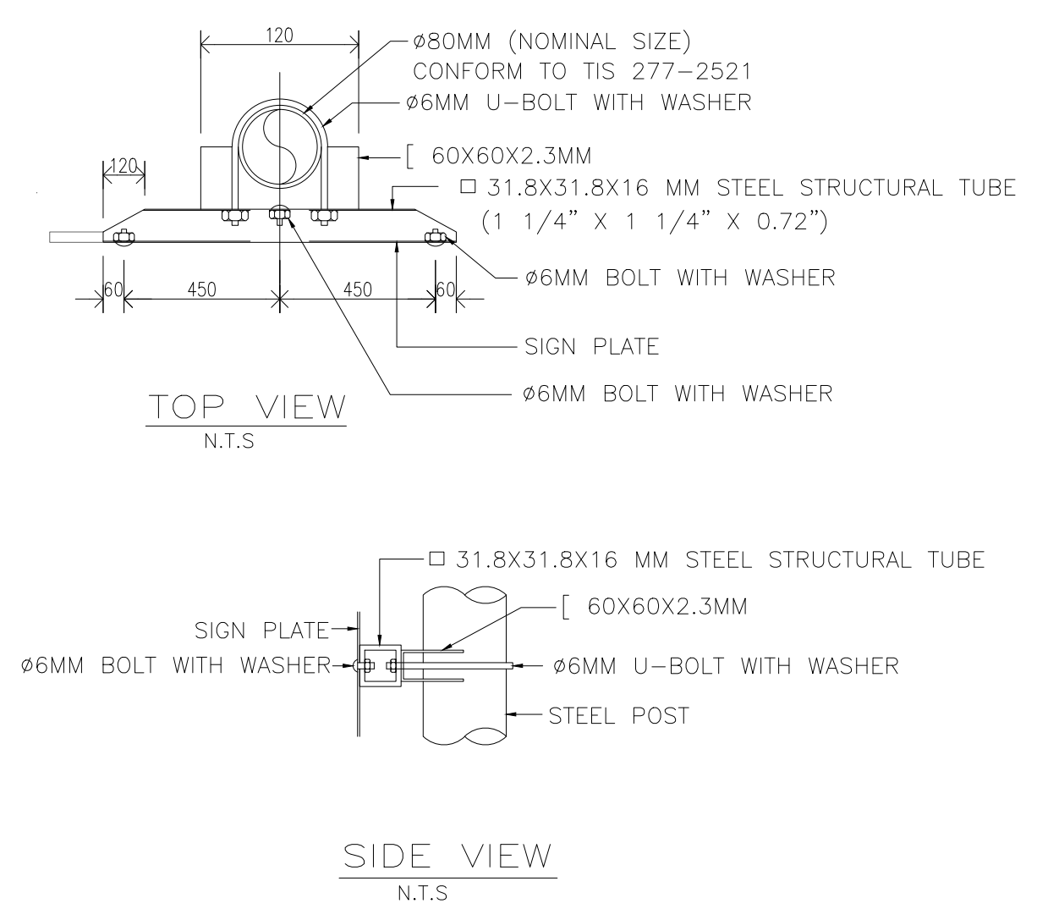
120
ø80MM (NOMINAL SIZE) CONFORM TO TIS 277–2521
ø6MM U–BOLT WITH WASHER
[60X60X2.3MM
□ 31.8X31.8X16 MM STEEL STRUCTURAL TUBE (1 1/4" X 1 1/4" X 0.72")
60
450
ø6MM BOLT WITH WASHER
SIGN PLATE
ø6MM BOLT WITH WASHER

TOP VIEW
N.T.S

□ 31.8X31.8X16 MM STEEL STRUCTURAL TUBE
[60X60X2.3MM
SIGN PLATE
ø6MM BOLT WITH WASHER
ø6MM U–BOLT WITH WASHER
STEEL POST

SIDE VIEW
N.T.S

GALVANIZED STEEL BRACKET DETAIL
N.T.S.

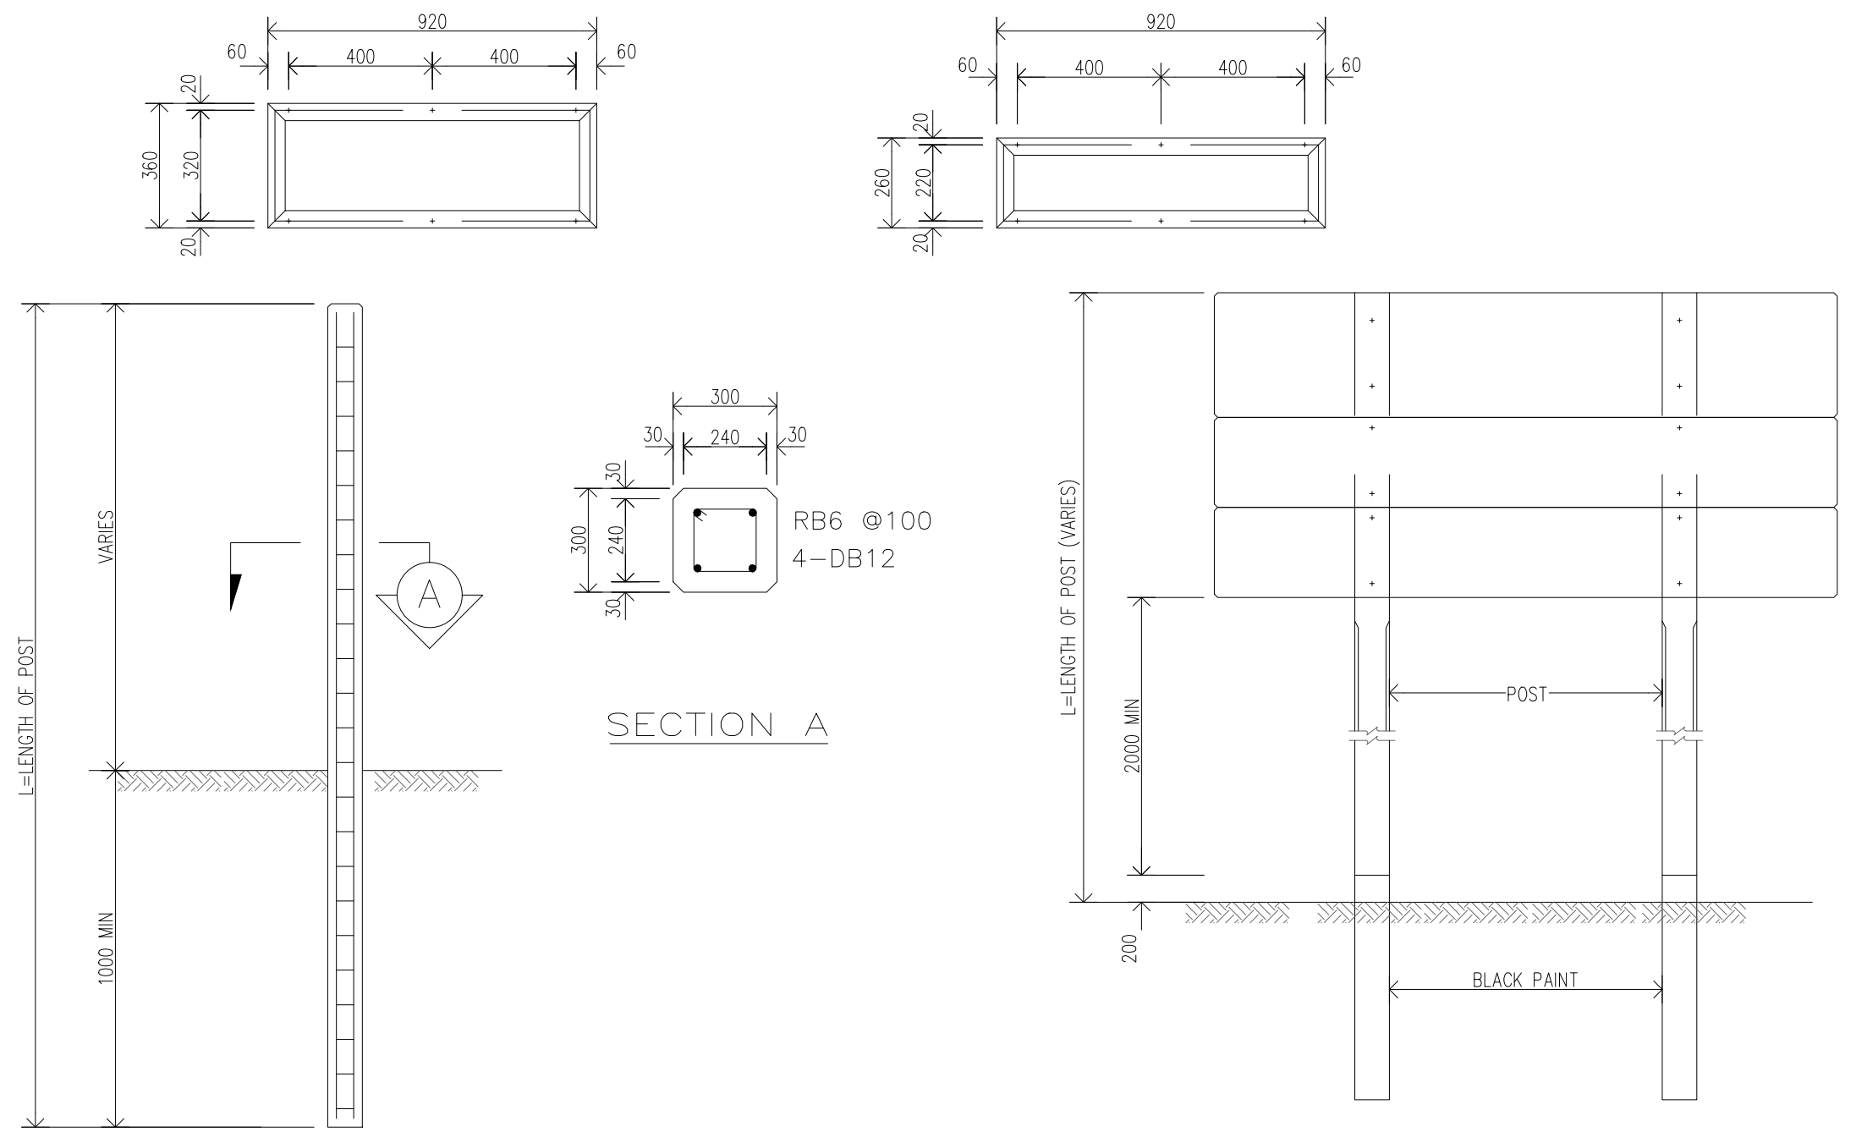
920
60
400
20
360
320
260
220
VARIES
L=LENGTH OF POST
1000 MIN
100
A
300
30
240
RB6 @100
4–DB12
L=LENGTH OF POST (VARIES)
2000 MIN
200
POST
BLACK PAINT

SECTION A

REINFROCED CONCRETE POST FOR SIGN BOARD
N.T.S.

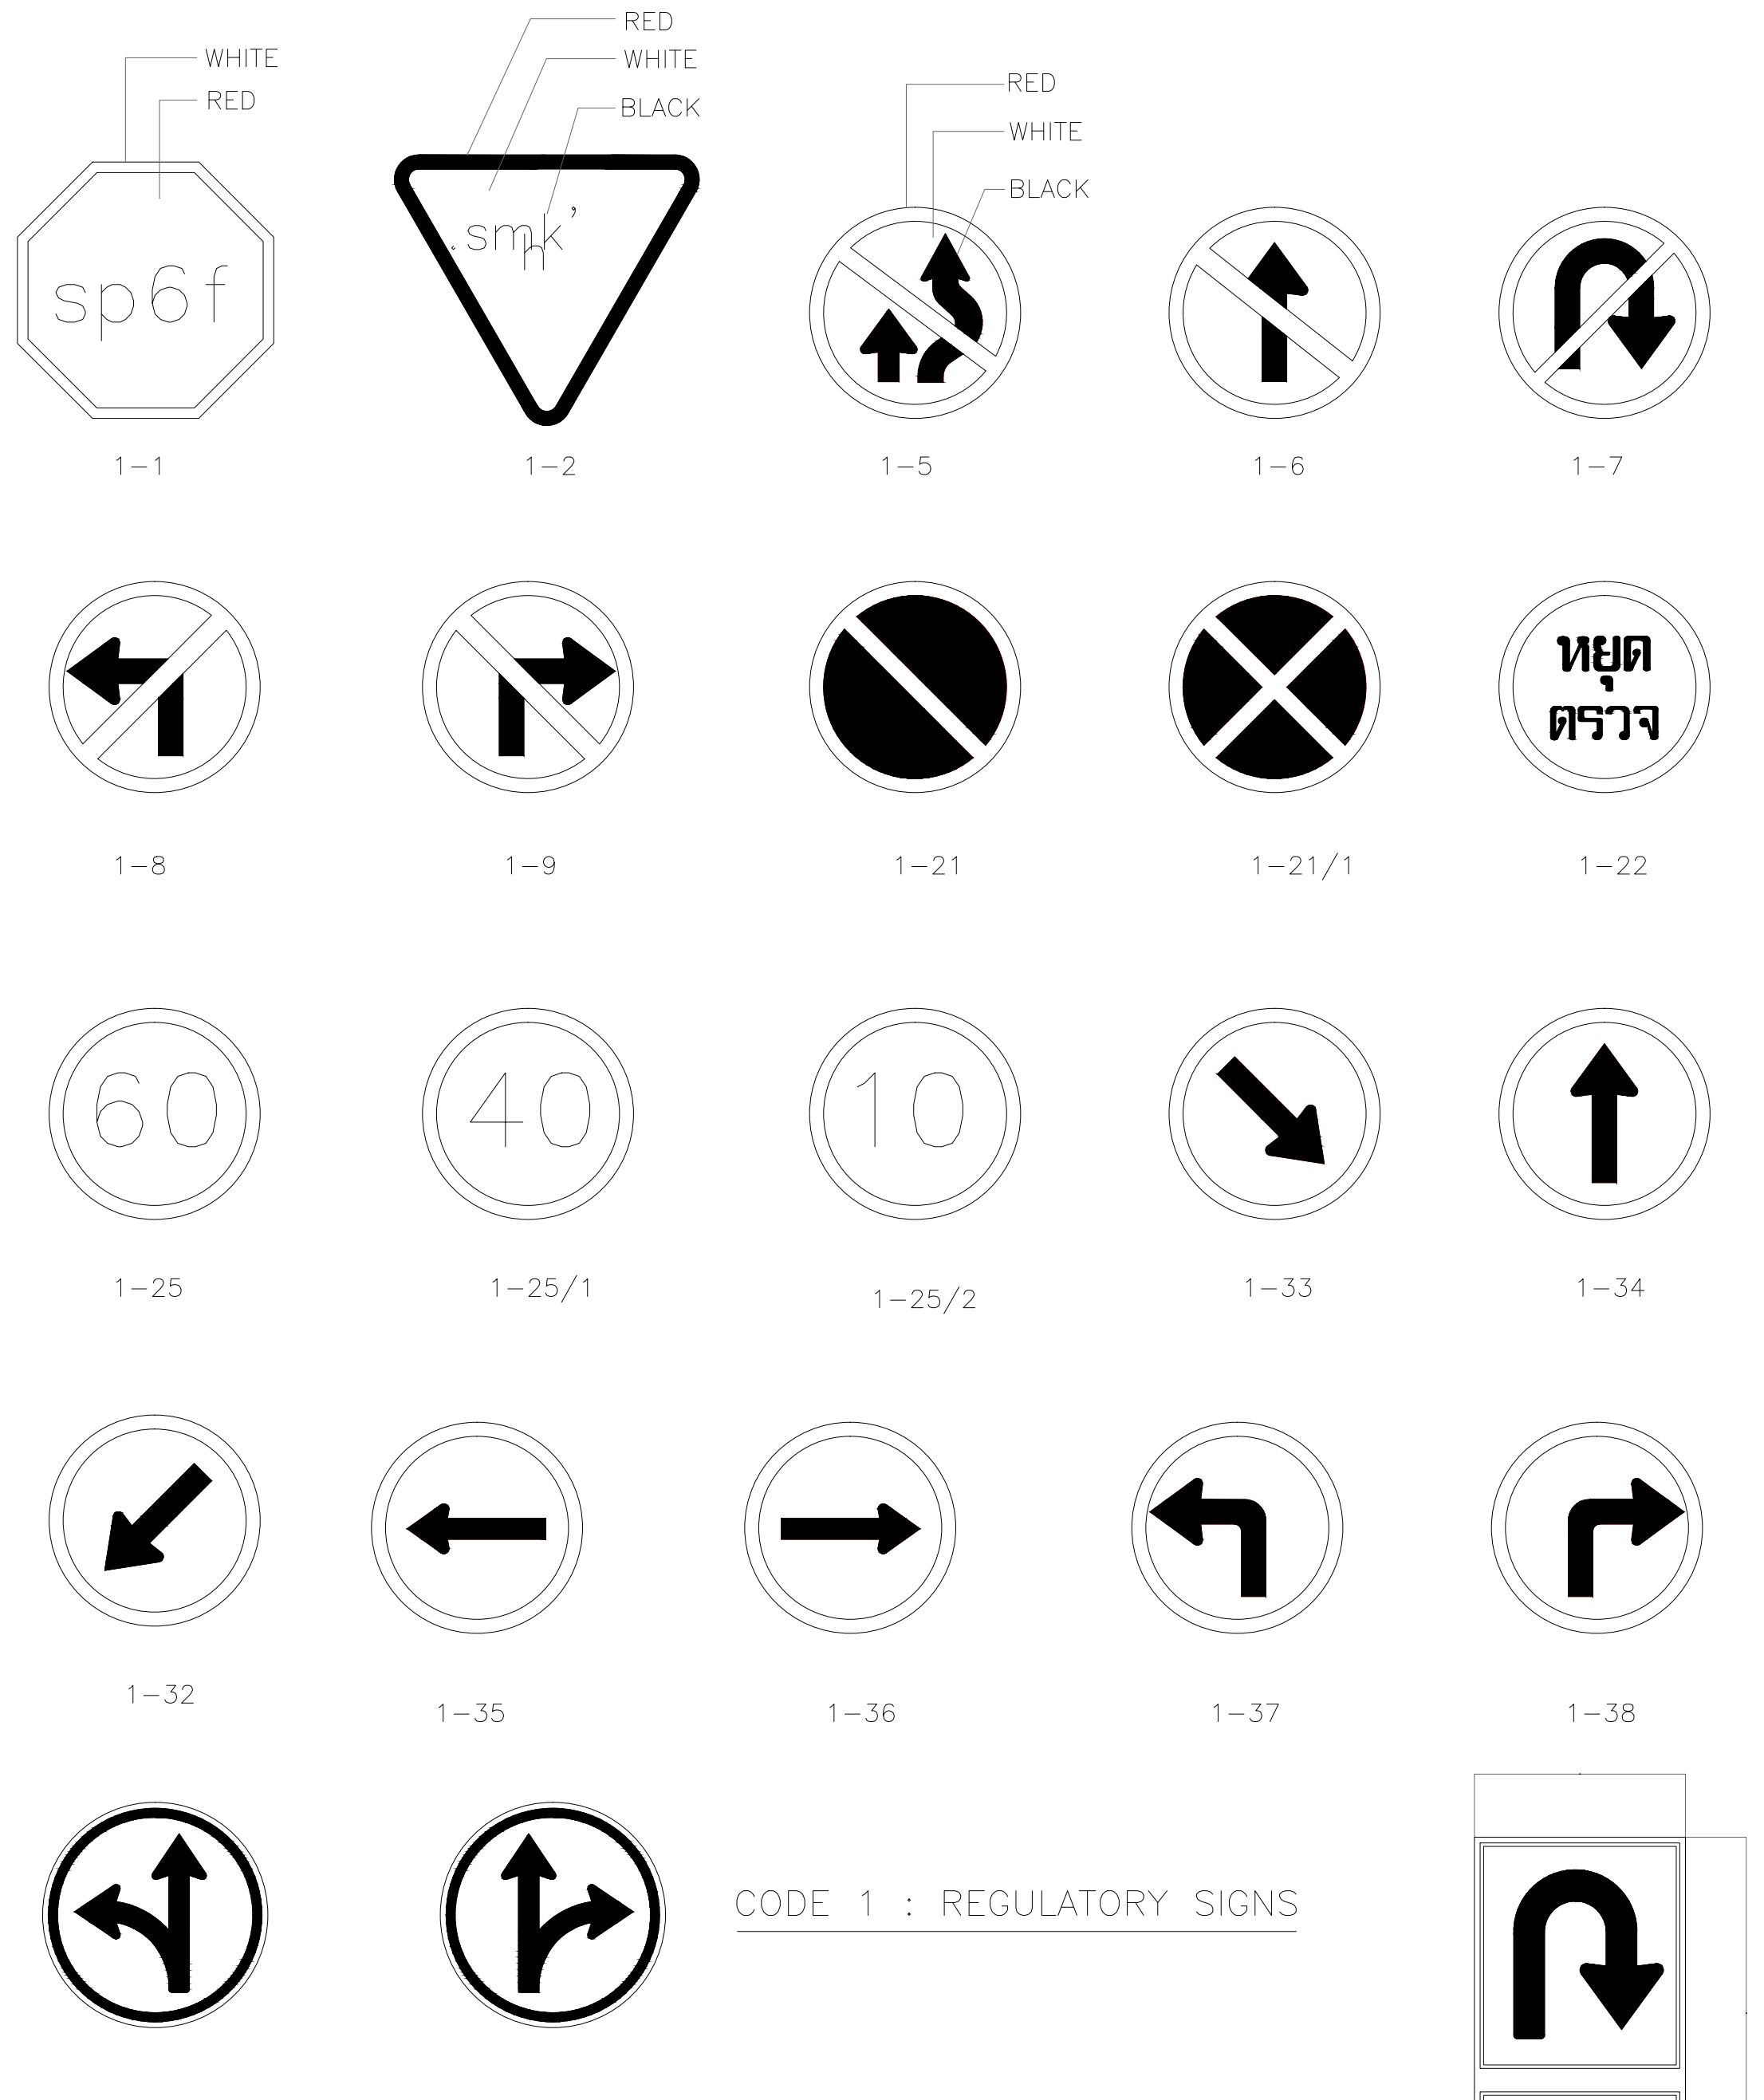
WHITE
RED
RED
WHITE
BLACK
RED
WHITE
BLACK
sp6f
smk
หยุด
ตรวจ
60
40
10
1–1
1–2
1–5
1–6
1–7
1–8
1–9
1–21
1–21/1
1–22
1–25
1–25/1
1–25/2
1–33
1–34
1–32
1–35
1–36
1–37
1–38

CODE 1 : REGULATORY SIGNS

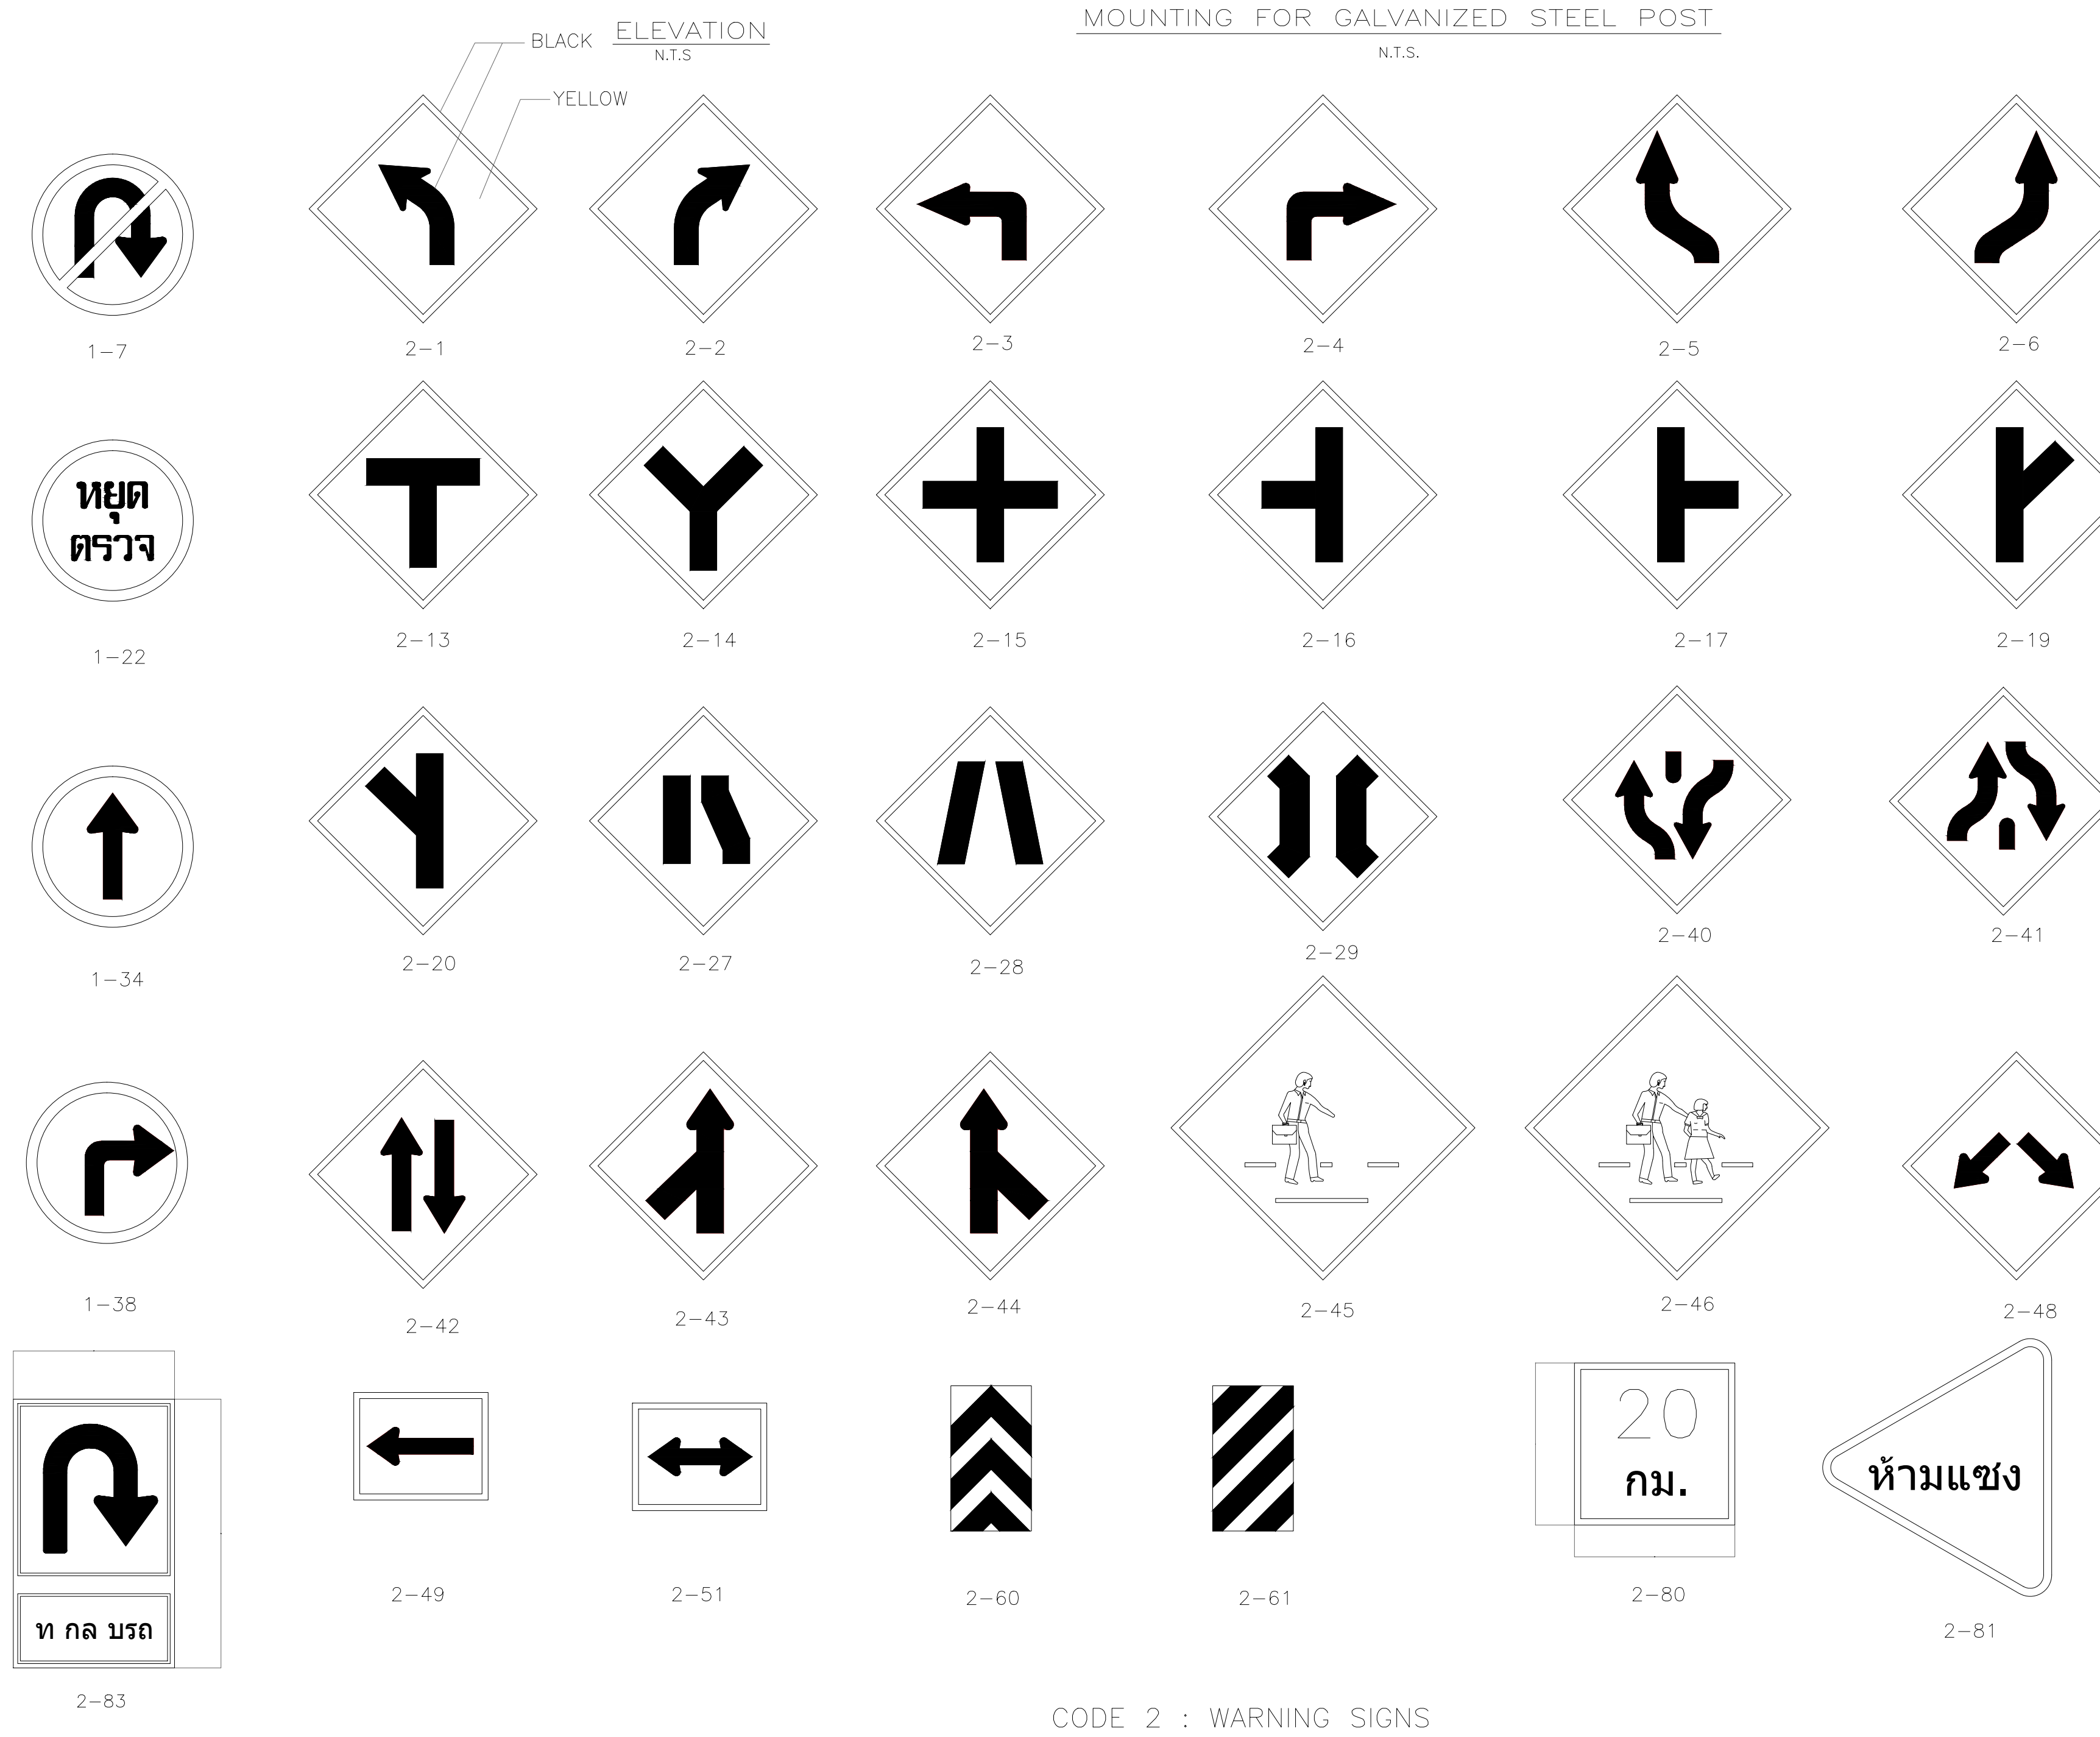
BLACK
YELLOW
2–1
2–2
2–3
2–4
2–5
2–6
2–13
2–14
2–15
2–16
2–17
2–19
2–20
2–27
2–28
2–29
2–40
2–41
2–42
2–43
2–44
2–45
2–46
2–48
ท กล บรถ
2–83
2–49
2–51
2–60
2–61
20
กม.
2–80
ห้ามแซง
2–81

CODE 2 : WARNING SIGNS

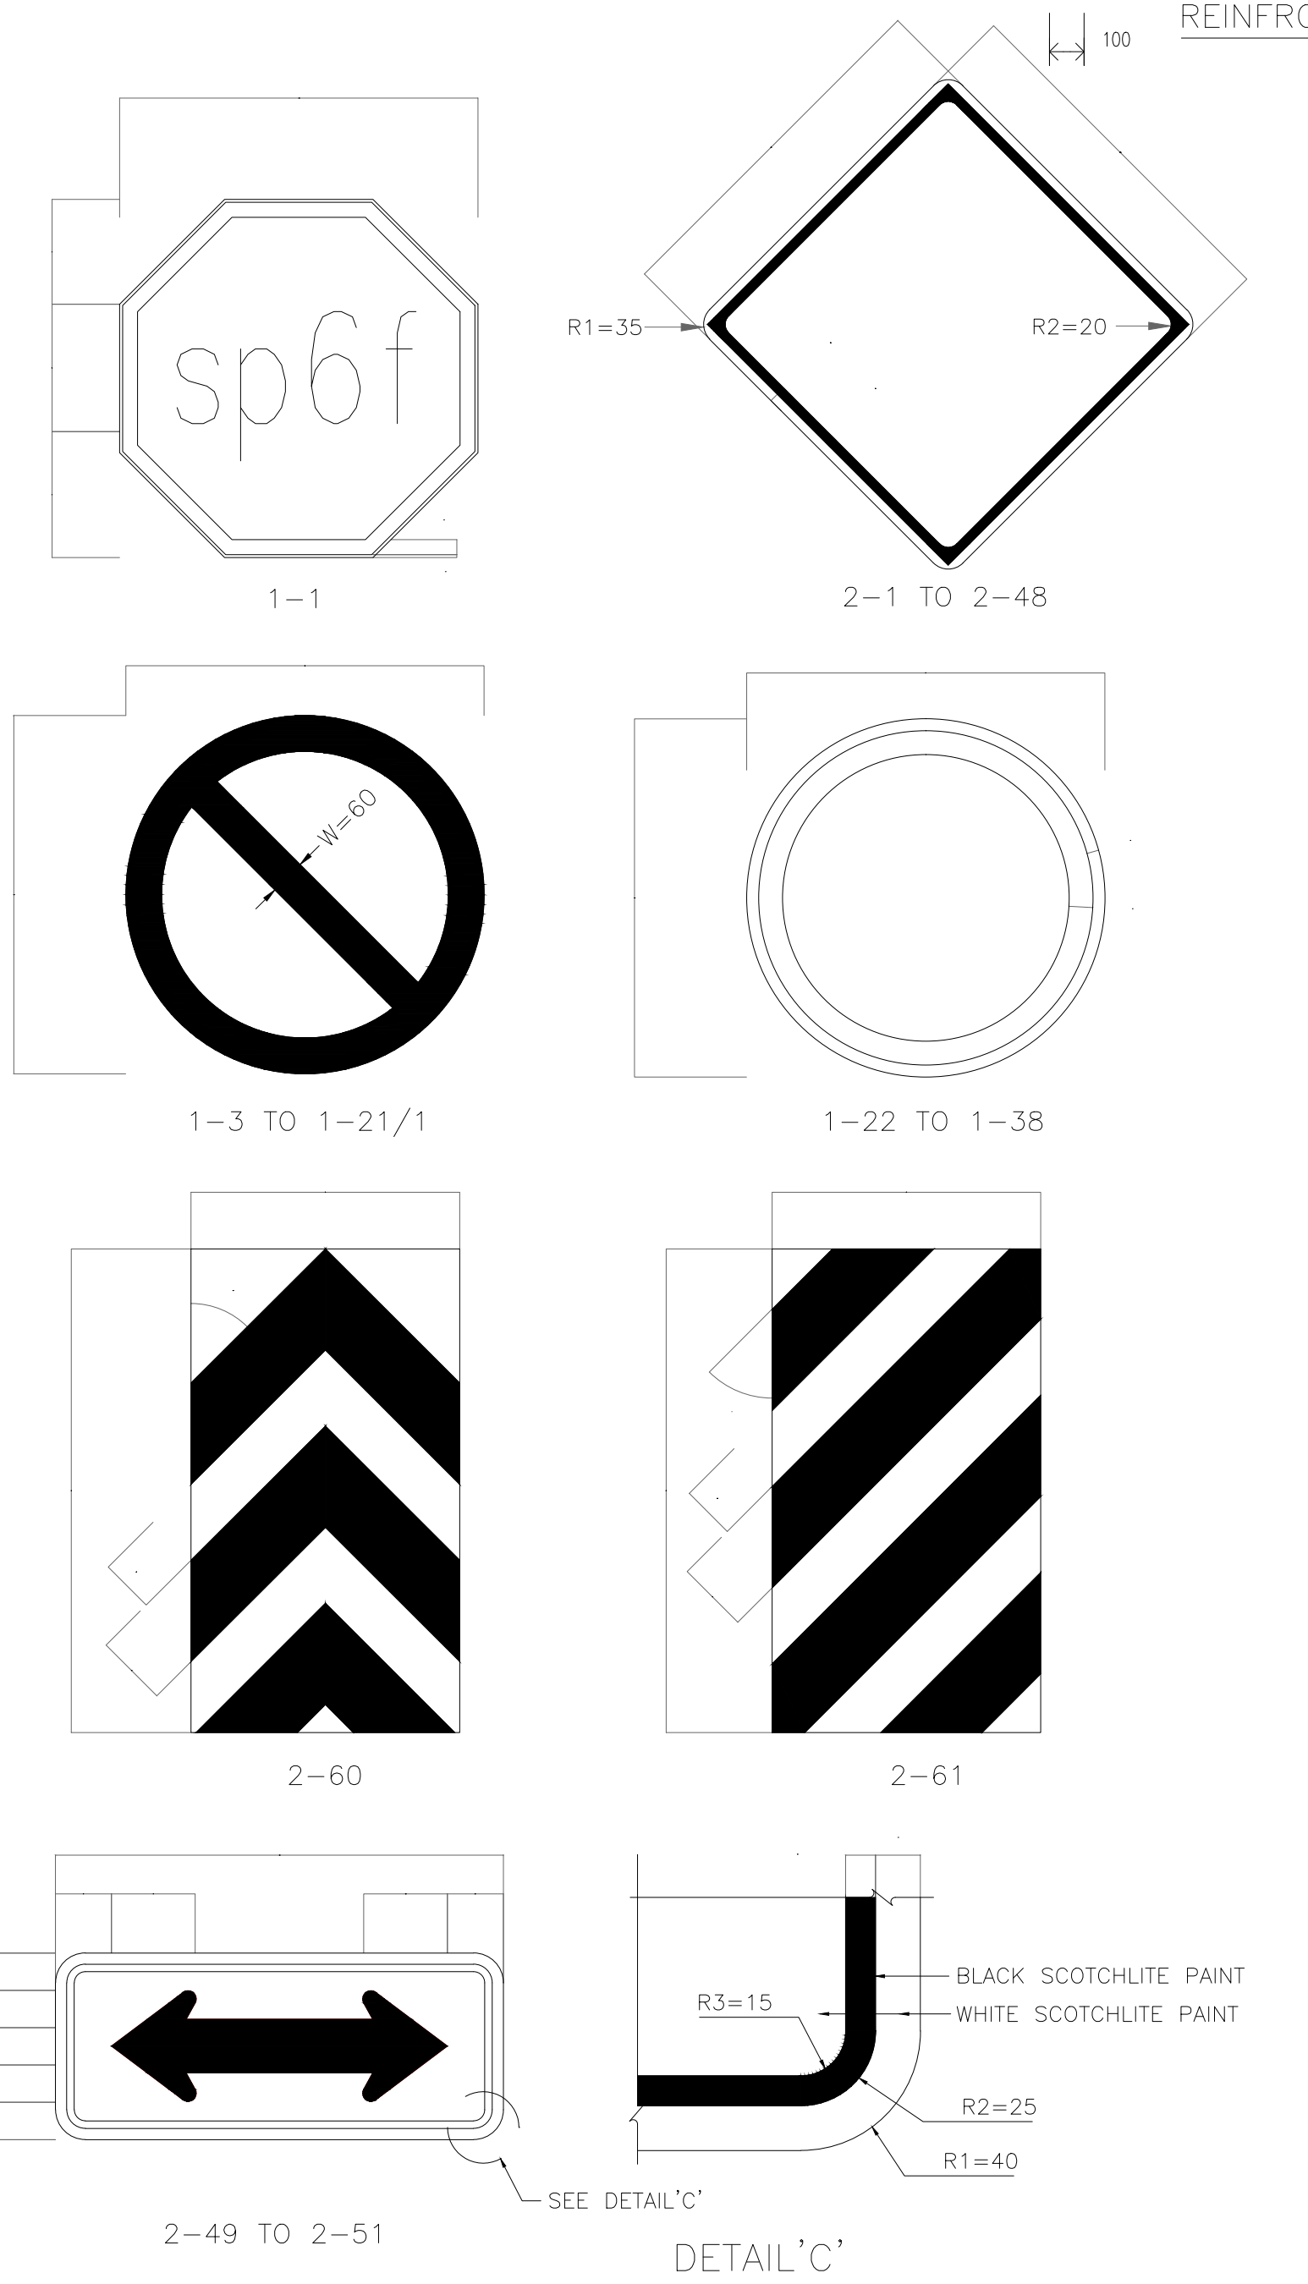
sp6f
1–1
R1=35
R2=20
2–1 TO 2–48
W=60
1–3 TO 1–21/1
1–22 TO 1–38
2–60
2–61
2–49 TO 2–51
SEE DETAIL'C'
R3=15
BLACK SCOTCHLITE PAINT
WHITE SCOTCHLITE PAINT
R2=25
R1=40

DETAIL'C'

SIGN DETAILS

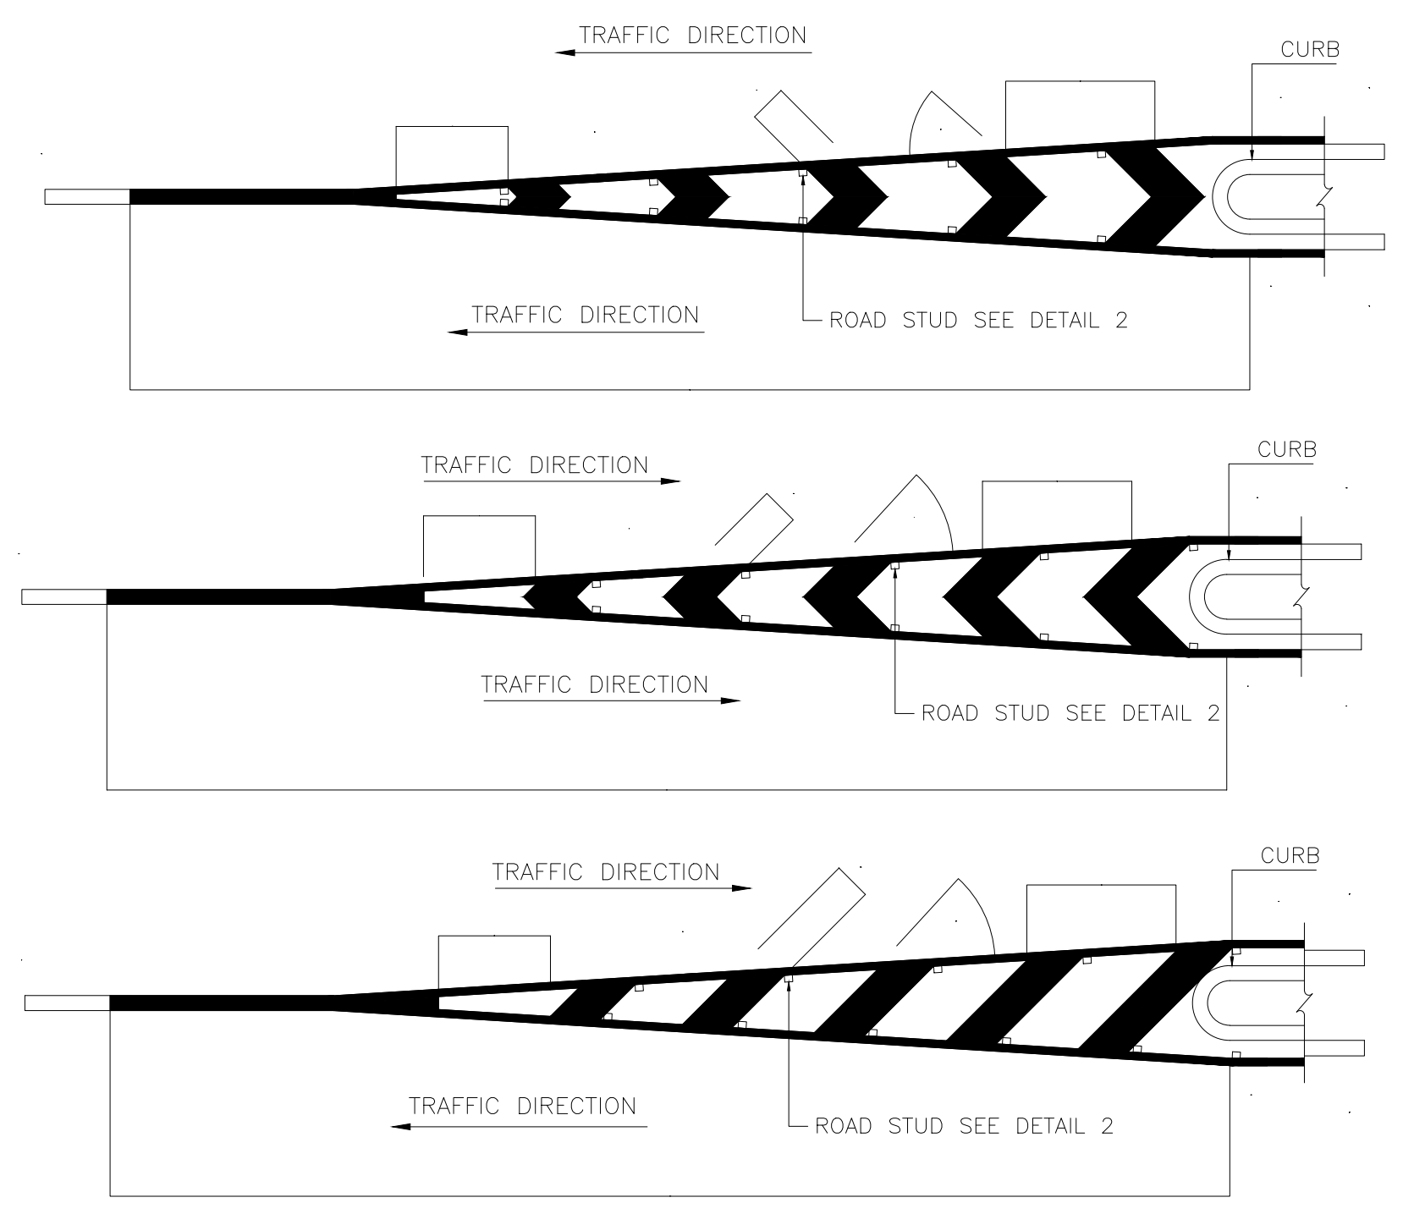
TRAFFIC DIRECTION
CURB
ROAD STUD SEE DETAIL 2

CHEVRON MARKING AT ISLAND APPROACH
NOT TO SCALE

BUS PARK CURB MARKING	ALTERNATE YELLOW AND WHITE STRIPES
NO PARK CURB MARKING	ALTERNATE RED AND WHITE STRIPES
CURB MARKING AROUND ISLAND	ALTERNATE BLACK AND WHITE STRIPES

COLOUR FOR CURB MARKING

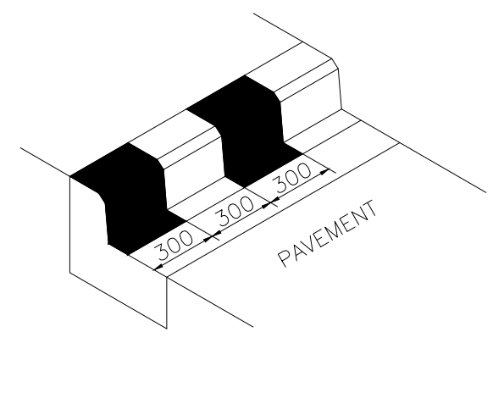
300
PAVEMENT

DETAIL 1 CURB MARKINGS
NOT TO SCALE

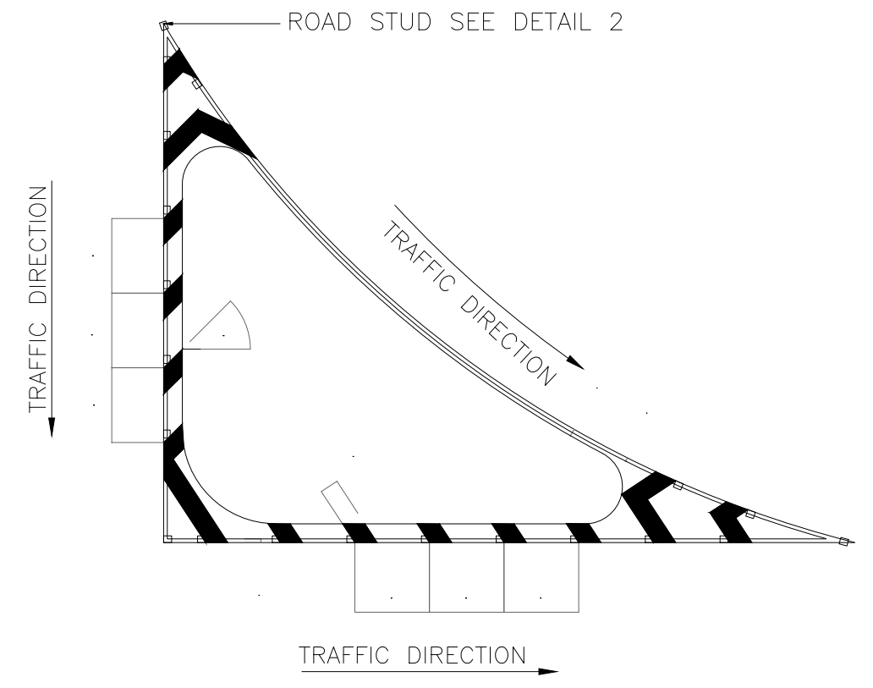
ROAD STUD SEE DETAIL 2
TRAFFIC DIRECTION
TRAFFIC DIRECTION
TRAFFIC DIRECTION

TYPICAL ISLAND MARKINGS
SCALE 1:200

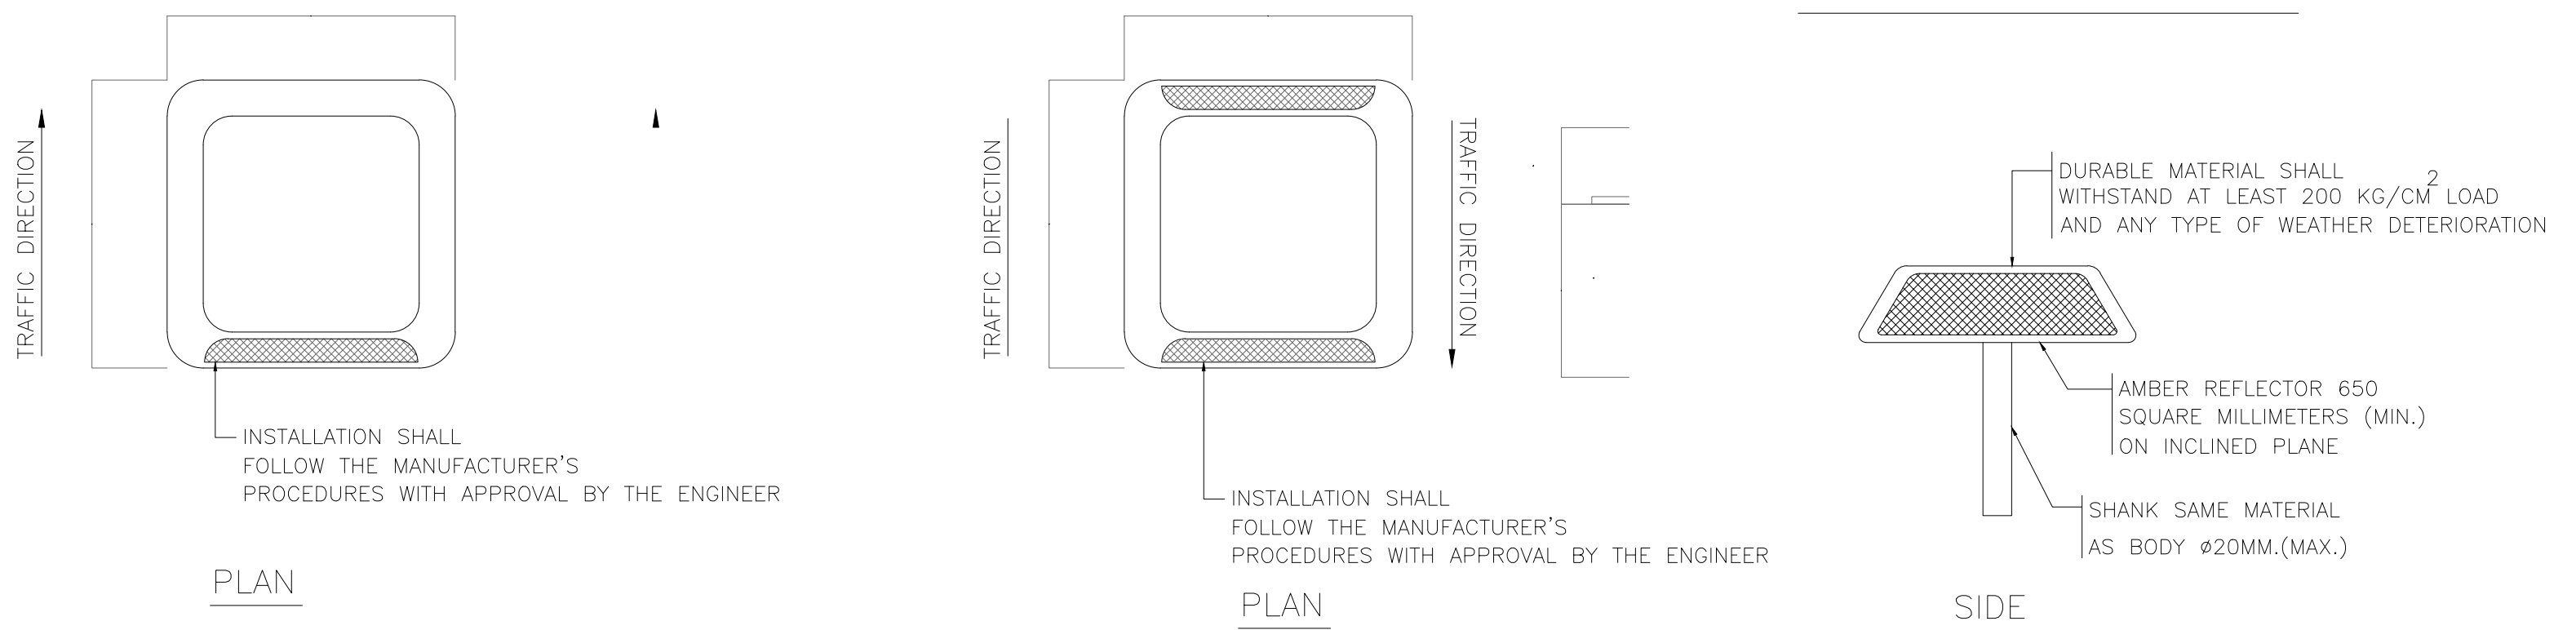
TRAFFIC DIRECTION
INSTALLATION SHALL FOLLOW THE MANUFACTURER'S PROCEDURES WITH APPROVAL BY THE ENGINEER
TRAFFIC DIRECTION
TRAFFIC DIRECTION
INSTALLATION SHALL FOLLOW THE MANUFACTURER'S PROCEDURES WITH APPROVAL BY THE ENGINEER
DURABLE MATERIAL SHALL WITHSTAND AT LEAST 200 KG/CM² LOAD AND ANY TYPE OF WEATHER DETERIORATION
AMBER REFLECTOR 650 SQUARE MILLIMETERS (MIN.) ON INCLINED PLANE
SHANK SAME MATERIAL AS BODY ø20MM.(MAX.)

PLAN
UNI–DIRECTIONAL TYPE

PLAN
BI–DIRECTIONAL TYPE

SIDE

DETAIL 2 ROAD STUD
NOT TO SCALE

NOTES:

1. ALL DIMENSIONS ARE IN MILLIMETERS UNLESS OTHERWISE NOTED.
2. ALL ARROWS AND PAVEMENT MARKING SHALL BE WHITE OR YELLOW REFLECTORIZED TERMOPLASTIC MATERIAL.
3. CURB MARKING SHALL BE ALTERNATE WHITE REFLECTORIZED ROAD PAINT AND OTHER NON REFLECTORIZED ROAD PAINT.
4. ALL TRAFFIC SIGNS SHALL BE IN ACCORDANCE WITH THE MANUAL OF TRAFFIC CONTROL DEVICES AS PUBLISHED BY THE DEPARTMENT OF HIGHWAYS, THE SPECIFICATION, AND THE DRAWINGS.
5. GUIDE SIGNS SHOWN ON THIS DRAWING ARE REPRESENTATIVE SAMPLES ONLY, ADDITIONAL TYPES MAY BE REQUIRED AS NECESSARY.

CLIENT :
GULF EDGE DC 01
87 Wireless Road, M Thai Tower 11th. Floor, All Seasons Place, Lumpini,
Pathumwan, Bangkok 10330, Thailand

CONTRACTOR :
华西发展(泰国)有限公司
บริษัท หัวซือ ดีเวลลอปเม้นต์ (ประเทศไทย) จำกัด
HUASHI DEVELOPMENT CO.,LTD
No. 202, Room No. 1403, 14/F, Le Concorde Building,
Ratchadapisek Road, Huaykhwang Sub–District,
Huaykhwang District, Bangkok Metropolitan 10310.

CONSULTANT :
ARbay
บริษัท เอ อาร์ เบย์ จำกัด
ARbay Company Limited
31 st Floor Bangkok Insurance Building
25 South Sathorn road Thungmahamek
Sathorn Bangkok 10120 THAILAND
T +66 (0) 2286 8199
F +66 (0) 2286 2863
info@arbay.co.th

CONSULTANT :
Qbic Engineers & Architects Co.,Ltd.
8 Soi KALONG 4 SANAMBINNAM ROAD,
THASAI SUB–DISTRICT, MUANG NONTHABURI DISTRICT
, NONTHABURI.
Tel 662–950–4374
Fax 662–580–3231
E–Mail : qbic@qbic.co.th, www.qbic.co.th
QBIC ENGINEERS AND ARCHITECTS CO.,LTD.

CONSULTANT :
MITR
MITR TECHNICAL CONSULTANT CO.,LTD.
1168/8 12th FLOOR, LUMPINI TOWER BUILDING,
RAMA IV RD., THUNGMAHAMEK, SATHORN, BANGKOK 10120, THAILAND
TEL : 0–2679–9079–84
FAX : 0–2679–9085 E–mail: mitr_dd@mitr.com

Architect : SIGNATURE
ประกิต พนานุรัตน์ วสถ. 580
ที่อยู่
251/1 ถ.จารุเมือง แขวงรองเมือง เขตปทุมวัน
กรุงเทพมหานคร โทรศัพท์ 02-286-8199

Structural Engineer : SIGNATURE
วิศวกรผู้ออกแบบโครงสร้าง
ณัฐสม สงวนวงษ์ วย 1423
ที่อยู่
2/1 ซ.รามคำแหง 150 ถ.รามคำแหง
แขวง สะพานสูง เขต สะพานสูง กทม. 10240

Structural Inspector : SIGNATURE
วิศวกรผู้ตรวจสอบโครงสร้าง
โกมล จุฑาภัทร วย 964
ที่อยู่
24/18 ซ.นวมินทร์ 129 ถ. นวมินทร์
แขวง นวลจันทร์ เขต บึงกุ่ม กทม. 10230

Electrical Engineer : SIGNATURE
วิศวกรผู้ออกแบบระบบไฟฟ้ากำลัง
นายสุภัทร บูรณวิทย์ วฟก.1265
ที่อยู่
21 ซอยทานสัมฤทธิ์ 13
ตำบลท่าทราย อ.เมืองนนทบุรี จ.นนทบุรี 11000

Mechanical Engineer : SIGNATURE
วิศวกรผู้ออกแบบระบบเครื่องกลและปรับอากาศ
นายประสิทธิ์ เกียวสุนทร วก.1221
ที่อยู่
44/372 ซอยบางกระดี่ 35/1 แขวงแสมดำ
เขตบางขุนเทียน กทม. 10150

Sanitary Engineer : SIGNATURE
วิศวกรผู้ออกแบบระบบสุขาภิบาล และดับเพลิง
นายทศวรรษ สันนฤทธิ์ วส. 215
ที่อยู่
บ้านเลขที่ 99/107 หมู่ที่ 3 ต.ศีรษะจรเข้น้อย
อ.บางเสาธง จ.สมุทรปราการ 10540

ISSUE/REVISION

REV.	DESCRIPTION	DATE
A	90% DEVELOPED	09/05/2026

PROJECT NAME :
GEDC 01
LOCATION:
Nikhom Phattana district, Rayong ,industrial estate,CPGC

BUILDING :
SITE PLAN

90% DEVELOPED

TITLE :
SITE PLAN SIGN DETAILS A

JOB NO.
SCALE 1:NTS
DRAWN HJC
REF.
CHECKED LJC
DWG.NO. MPK00–90–A–SD–001
APPROVED LXD
DATE 2026.05.09

NOTE : THIS PRINT IS OF A CONFIDENTIAL NATURE, IT SHALL NOT BE TRACED,PHOTOGRAPHED,PHOTOSTATED OR REPRODUCED IN ANY MANER,NOR USED FOR ANY PURPOSE WHATSOEVER EXCEPT BY WRITTEN PERMISSION