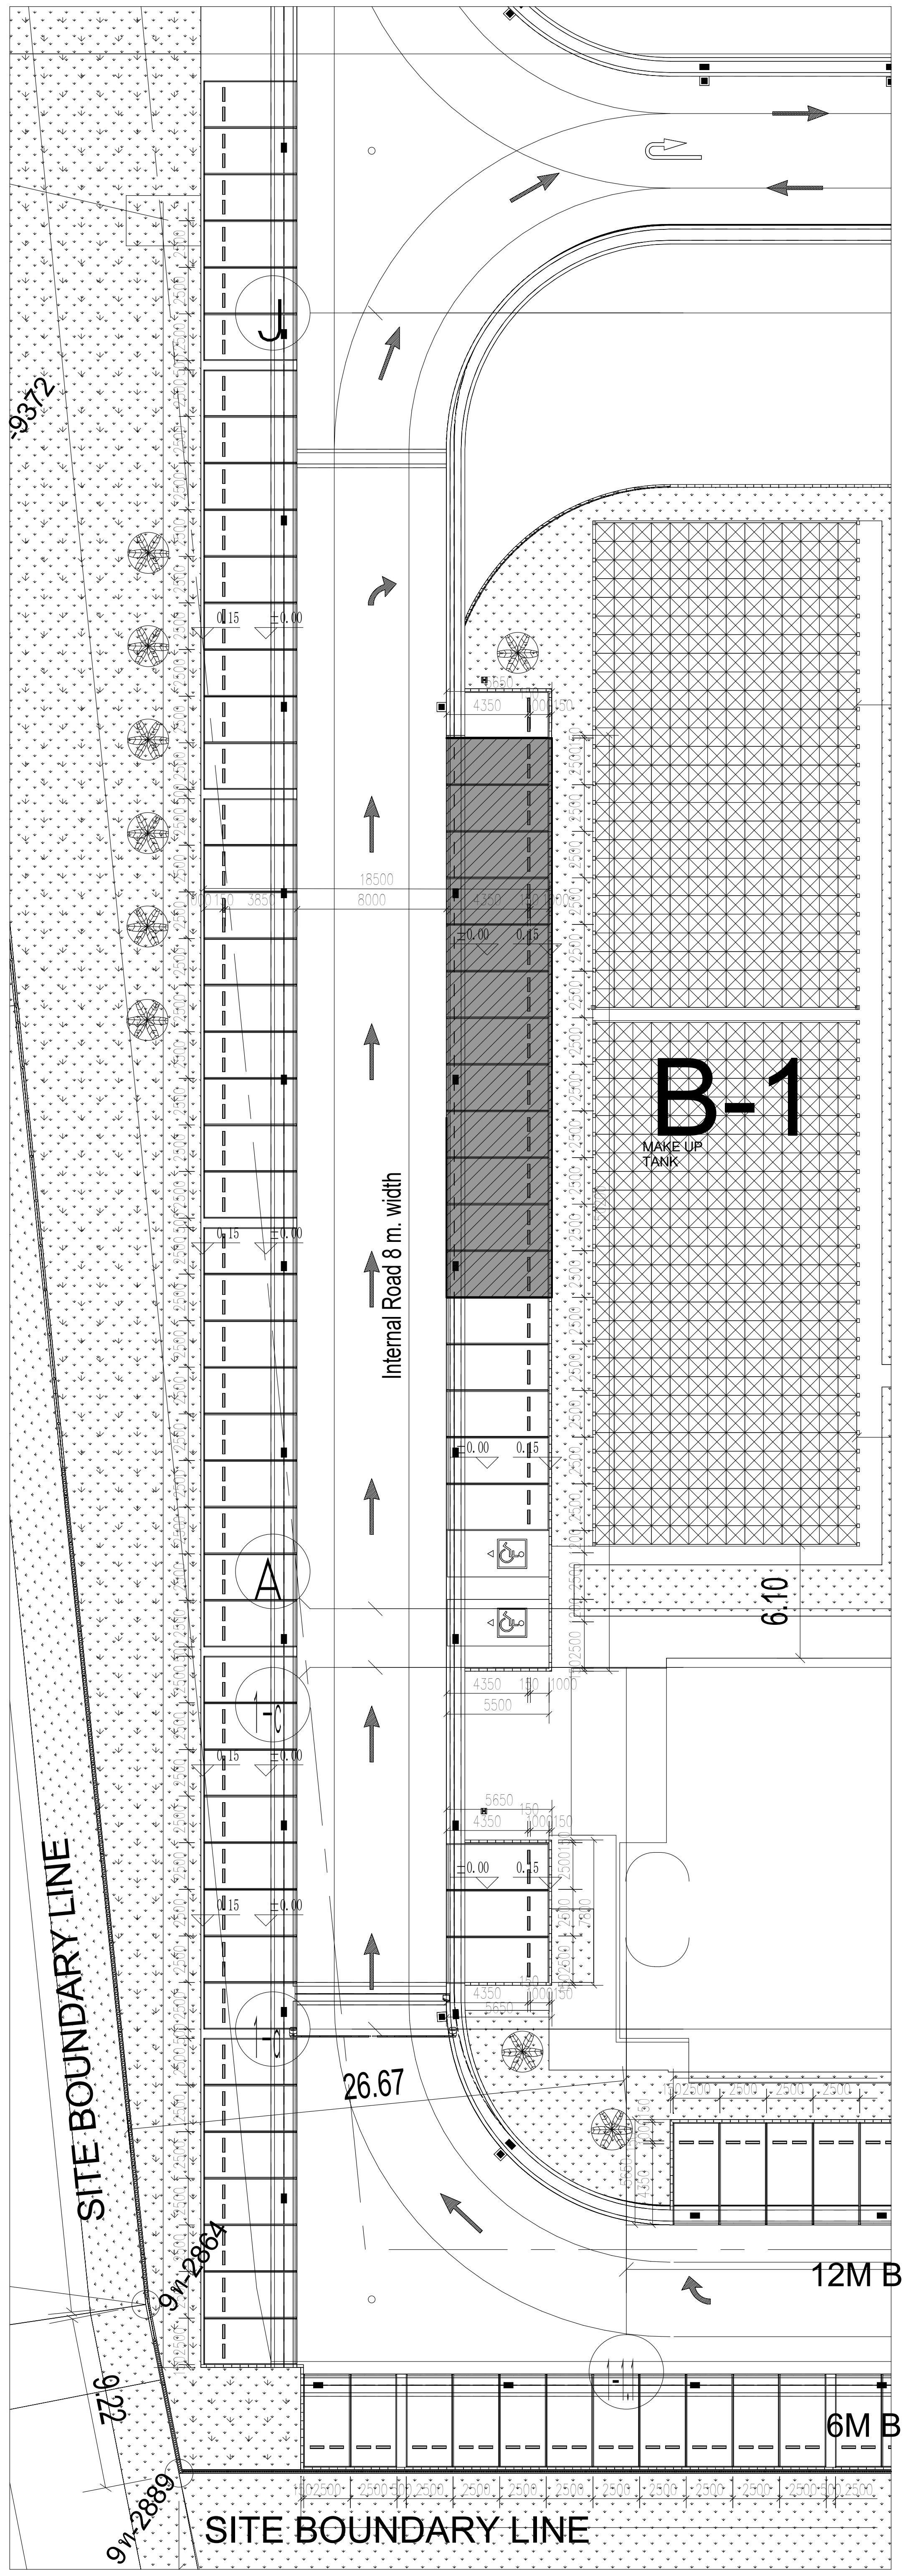
J
A
B-1
MAKE UP TANK
Internal Road 8 m. width
SITE BOUNDARY LINE
26.67
6.10
12M BUILDING SETBACK FROM SITE BOUNDARY LINE(AHJ requirement)
6M BUILDING SETBACK FROM SITE BOUNDARY LINE(AHJ requirement)
9ท-2864
9ท-2889
9ท-9372
9.22

CAR PARKING PLAN BLOW UP (A)

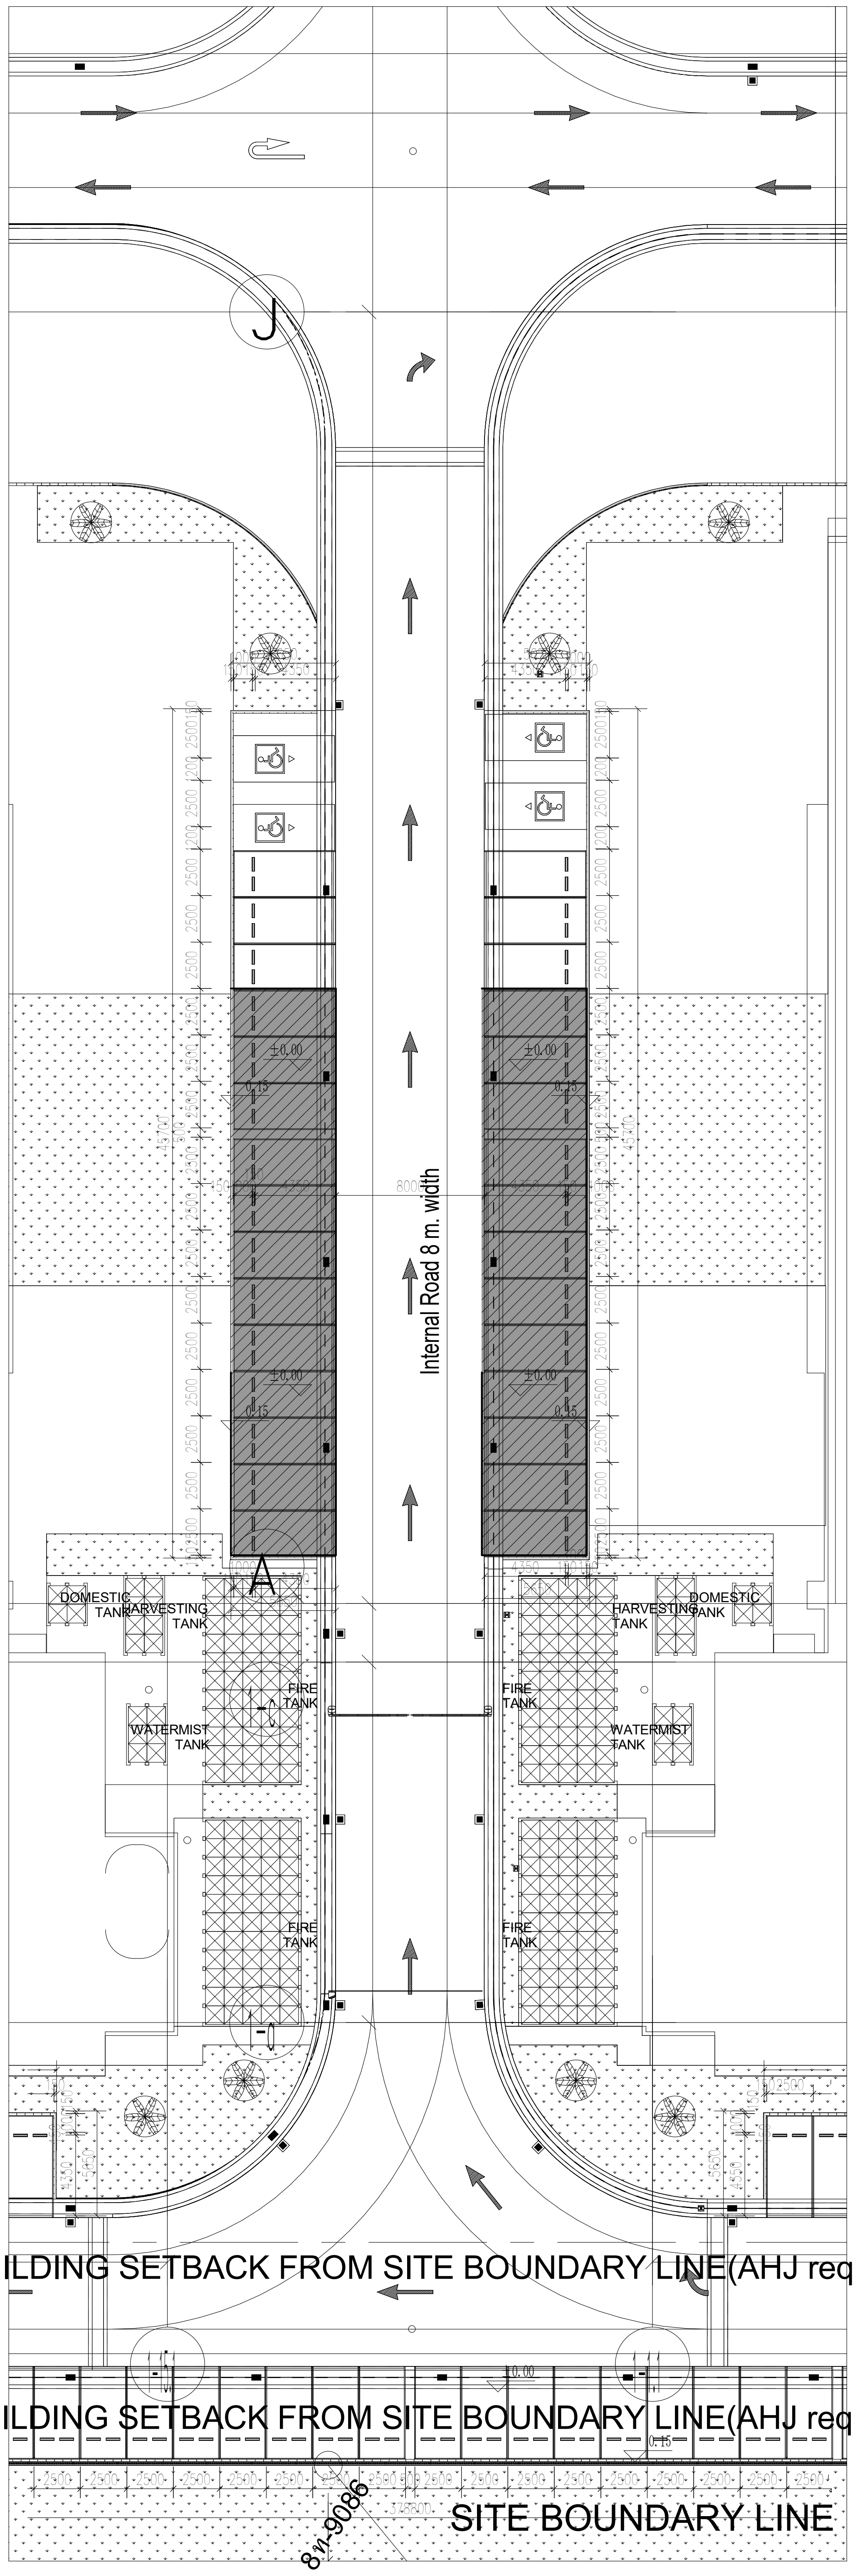

CAR PARKING PLAN BLOW UP (B)

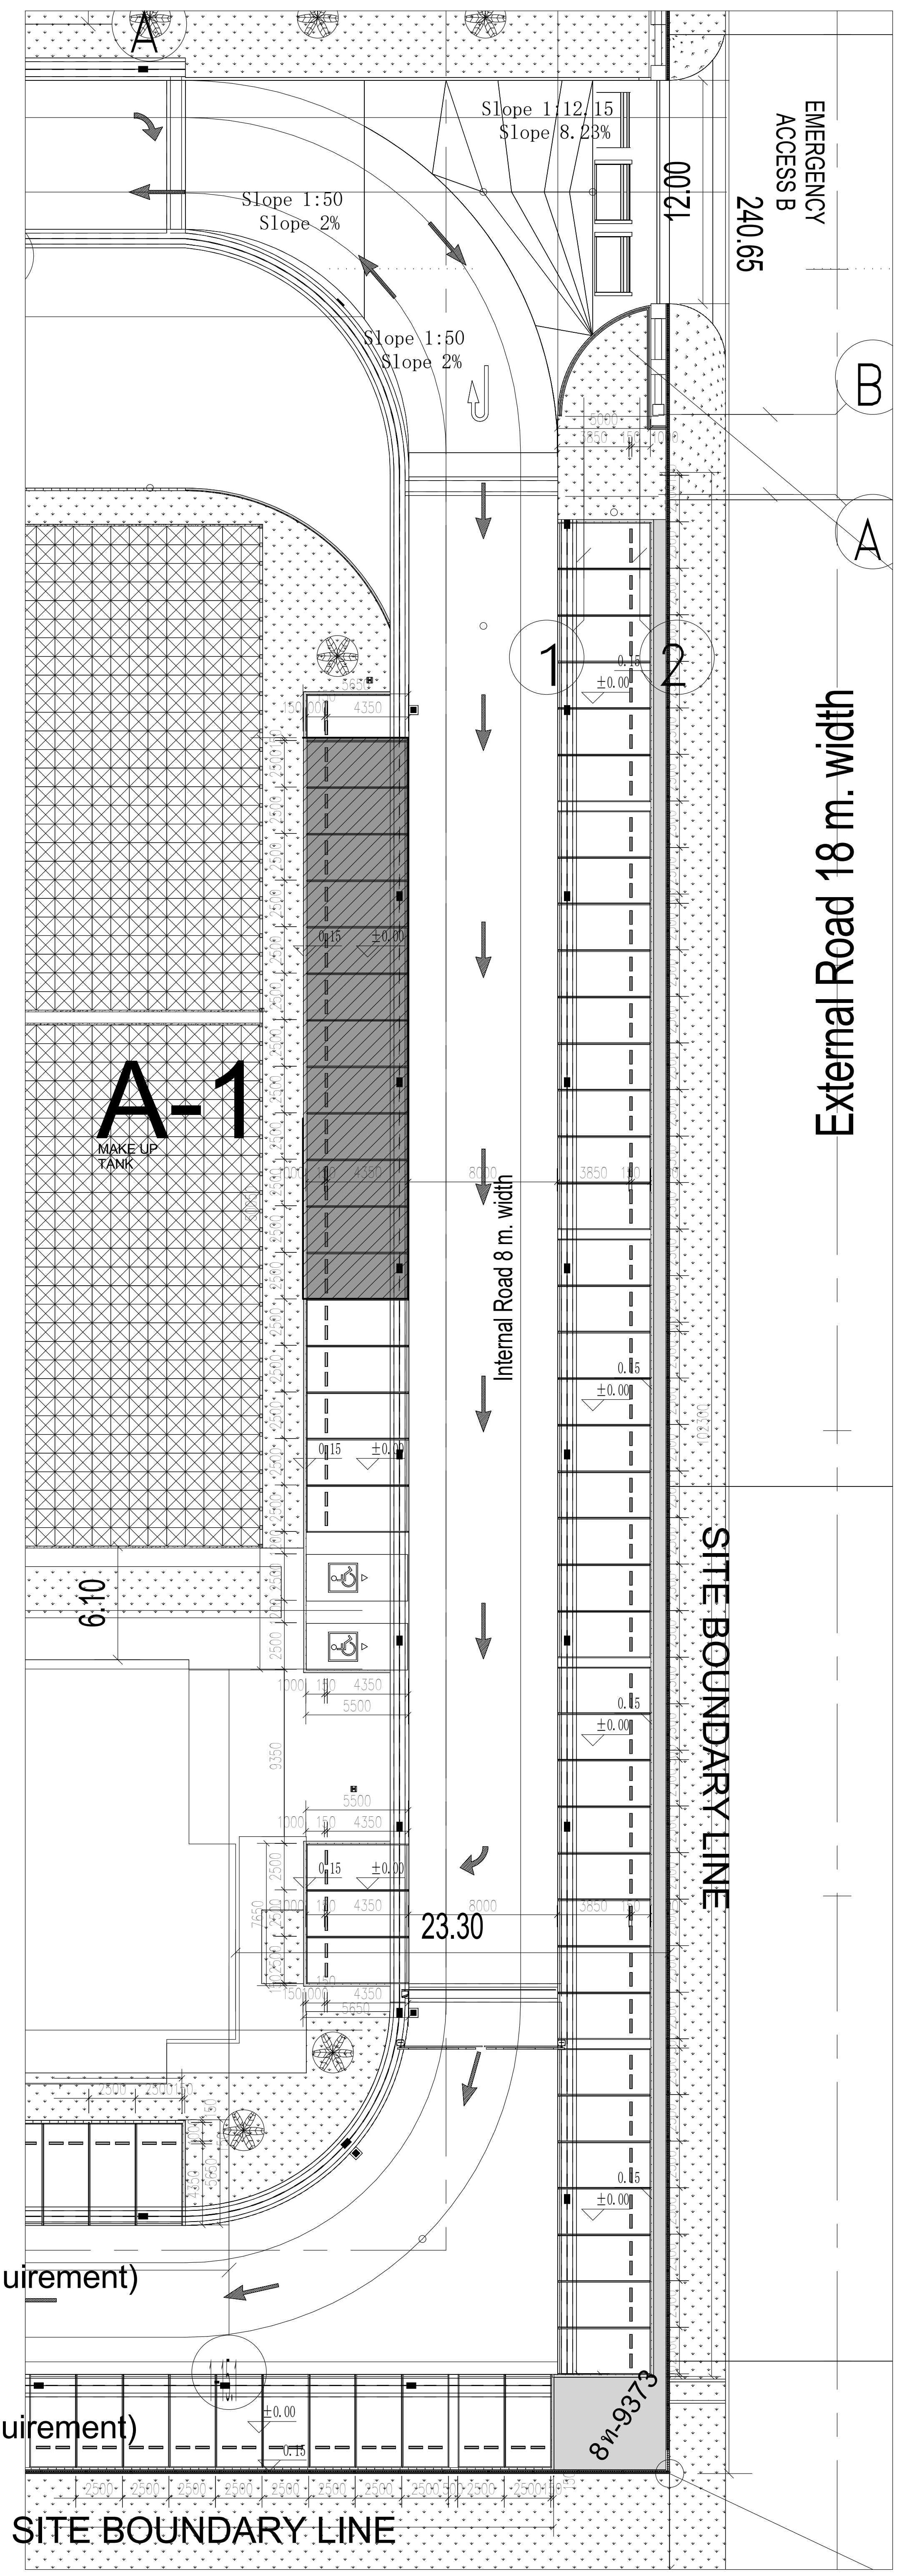

CAR PARKING PLAN BLOW UP (C)

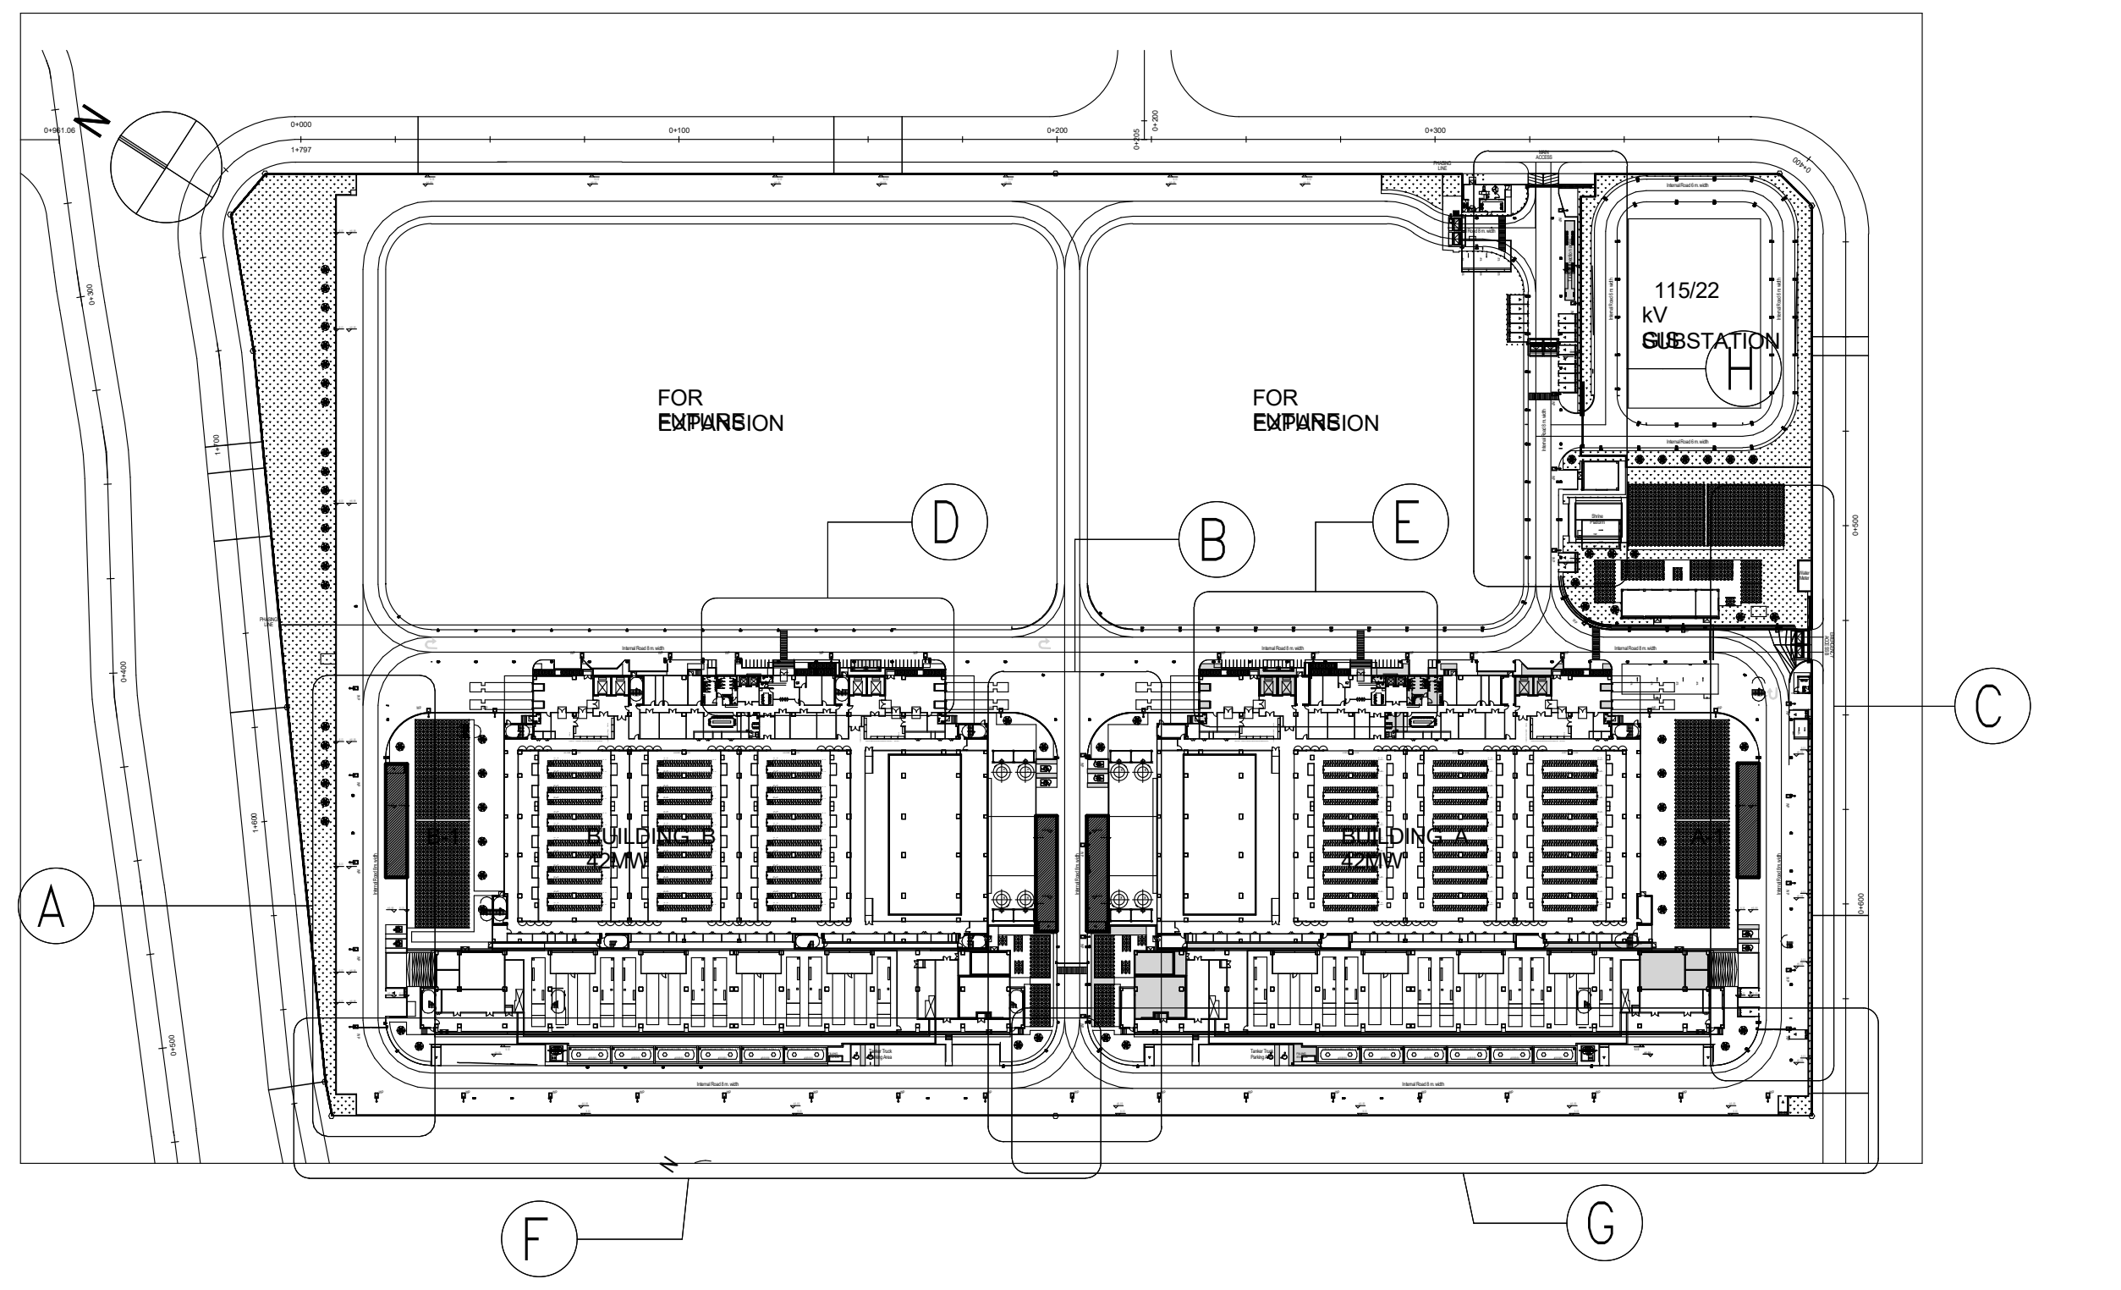

PARKING LOT INDEX PLAN
SCALE 1:2000

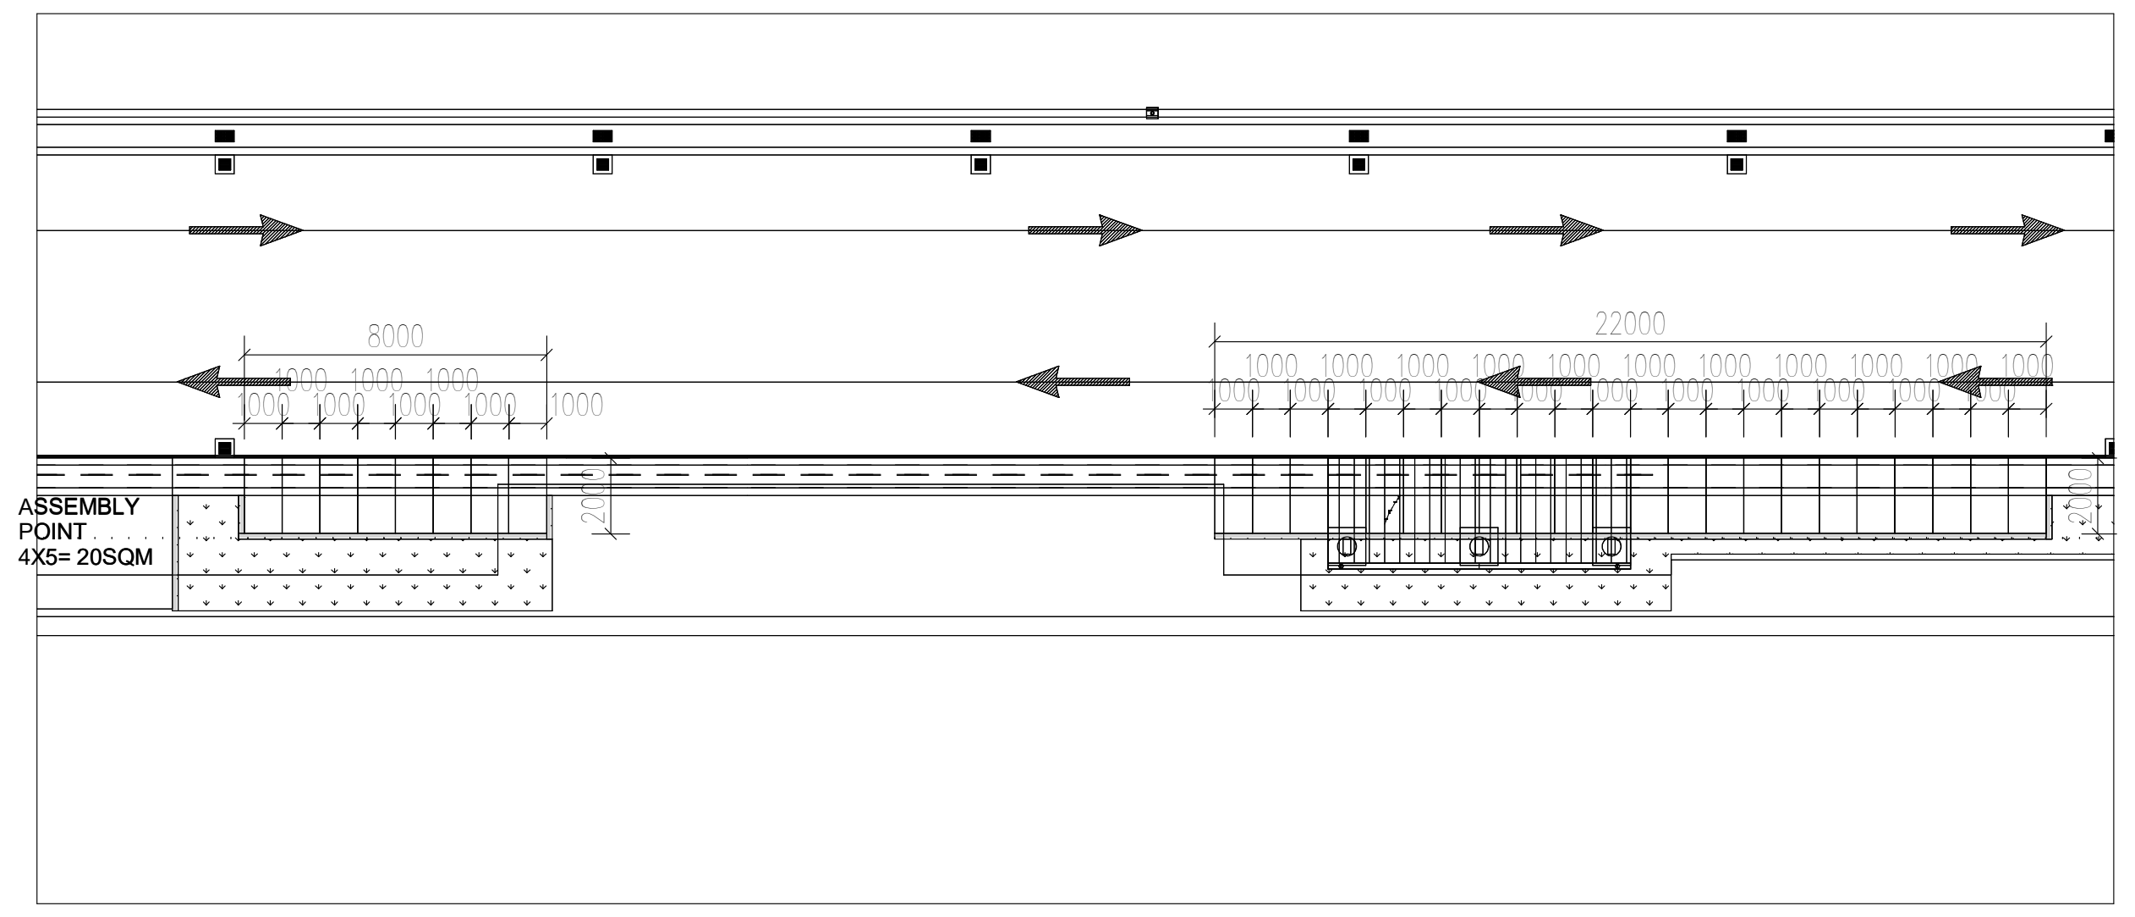

CAR PARKING PLAN BLOW UP (D)

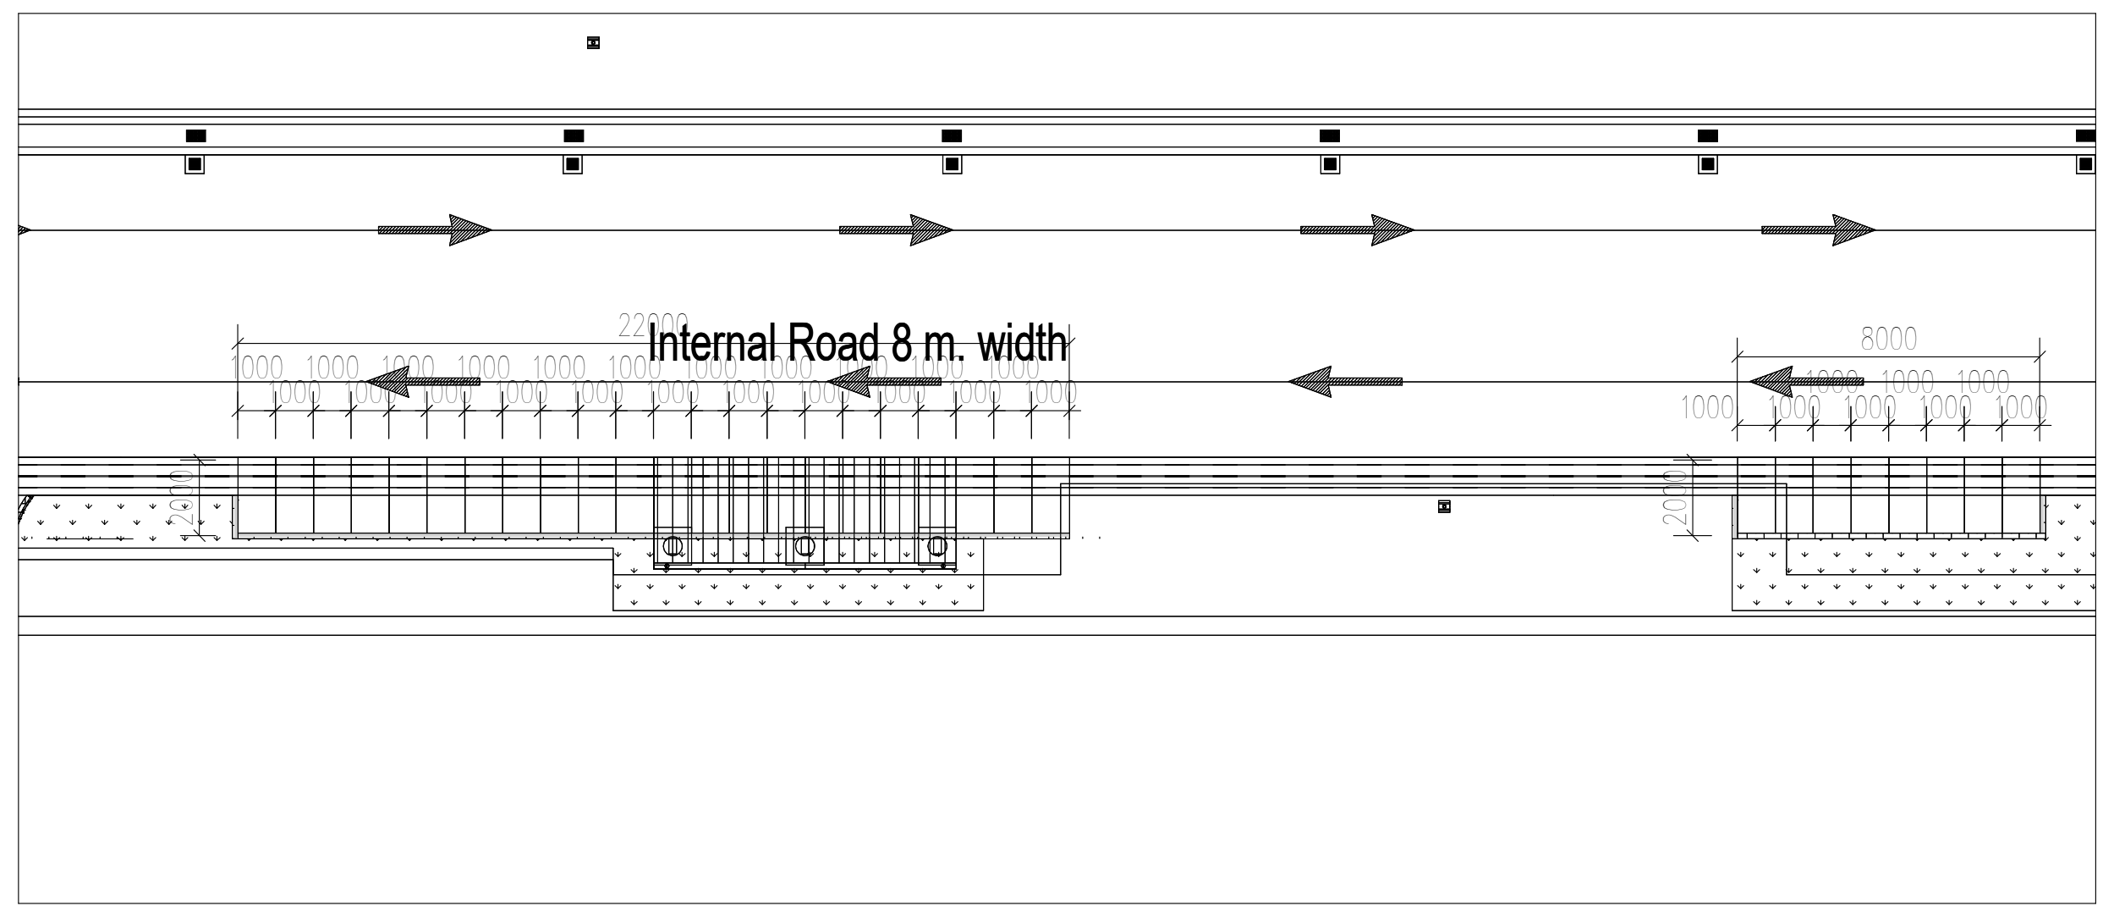

CAR PARKING PLAN BLOW UP (E)

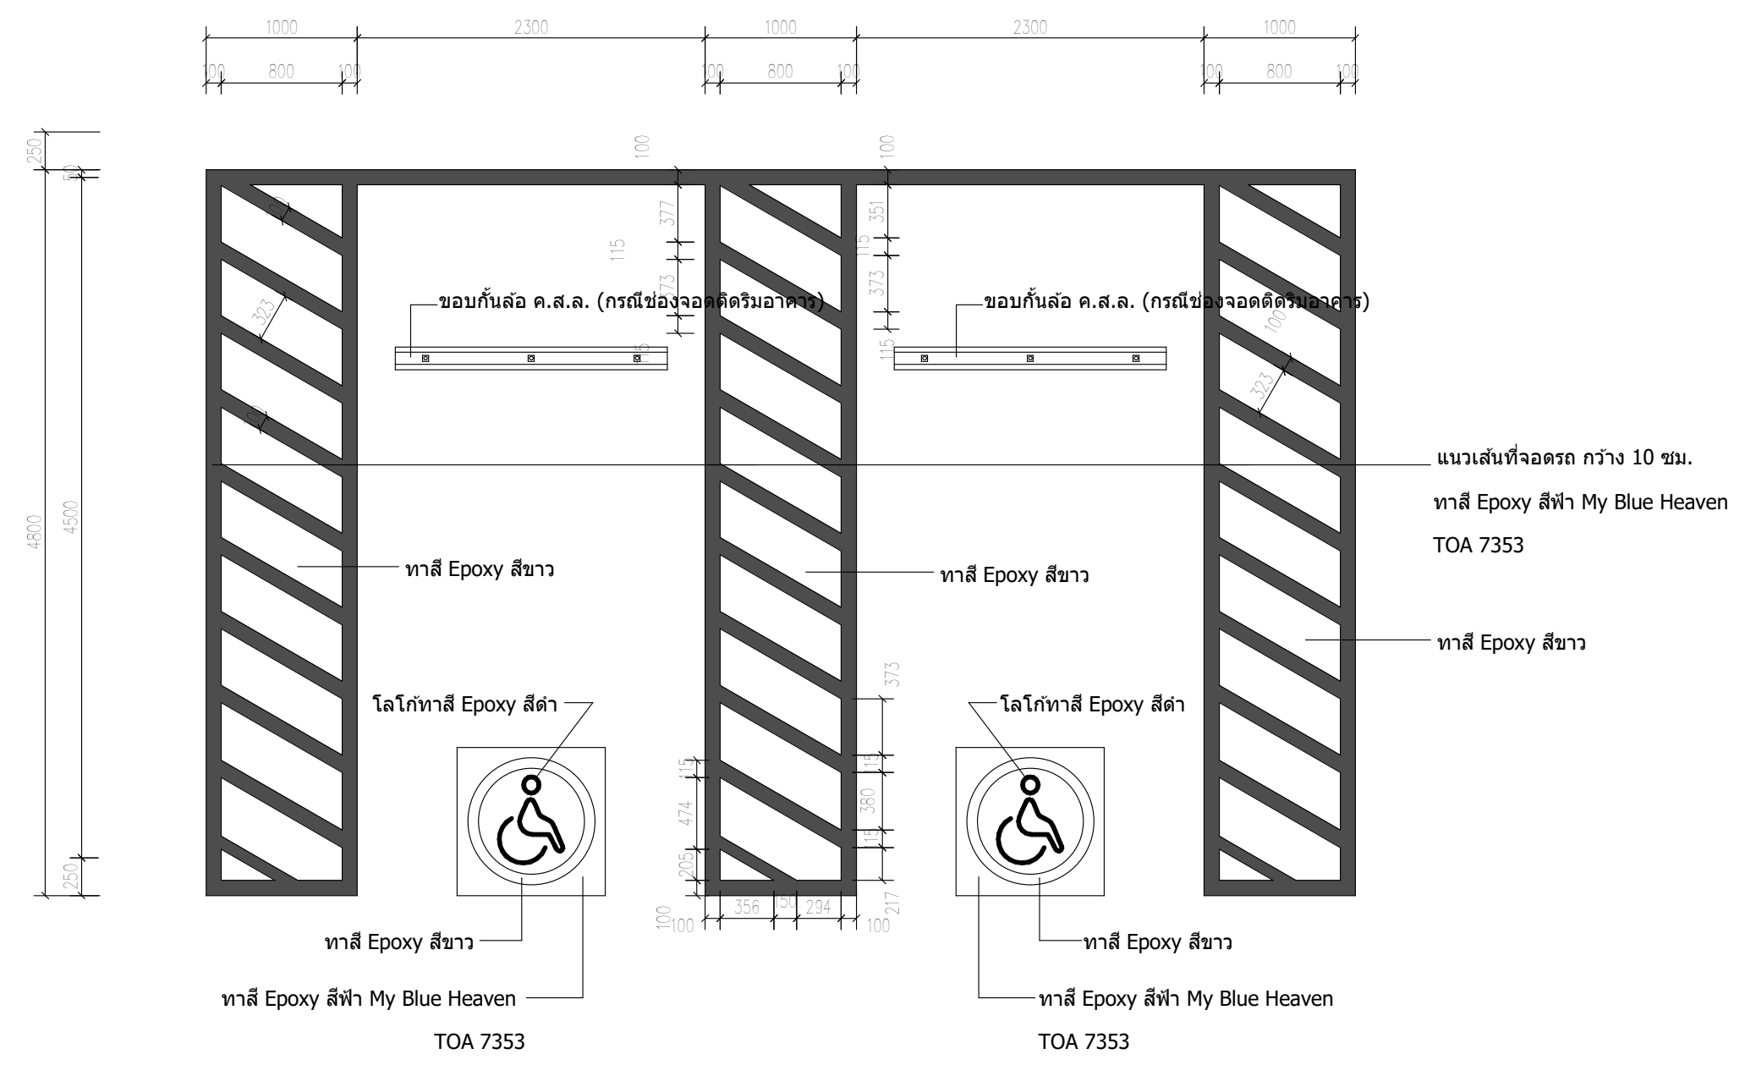
1000
2300
800
ขอบกั้นล้อ ค.ส.ล. (กรณีช่องจอดติดริมอาคาร)
ขอบกั้นล้อ ค.ส.ล. (กรณีช่องจอดติดริมอาคาร)
แนวเส้นที่จอดรถ กว้าง 10 ซม.
ทาสี Epoxy สีฟ้า My Blue Heaven
TOA 7353
ทาสี Epoxy สีขาว
ทาสี Epoxy สีขาว
ทาสี Epoxy สีขาว
โลโก้ทาสี Epoxy สีดำ
โลโก้ทาสี Epoxy สีดำ
ทาสี Epoxy สีขาว
ทาสี Epoxy สีขาว
ทาสี Epoxy สีฟ้า My Blue Heaven
TOA 7353
ทาสี Epoxy สีฟ้า My Blue Heaven
TOA 7353

ACCESSIBLE PARKING
SCALE 1:50

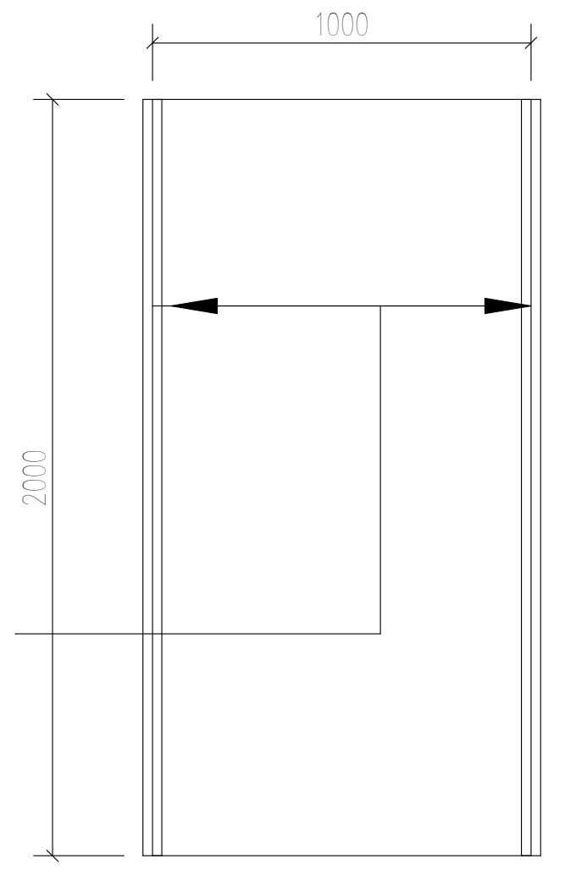

Parking stall line marking, road surface paint
Non-Reflective Thermoplastic
Width 1,800 x 50 mm

MOTORCYCLE PARKING
SCALE 1:20

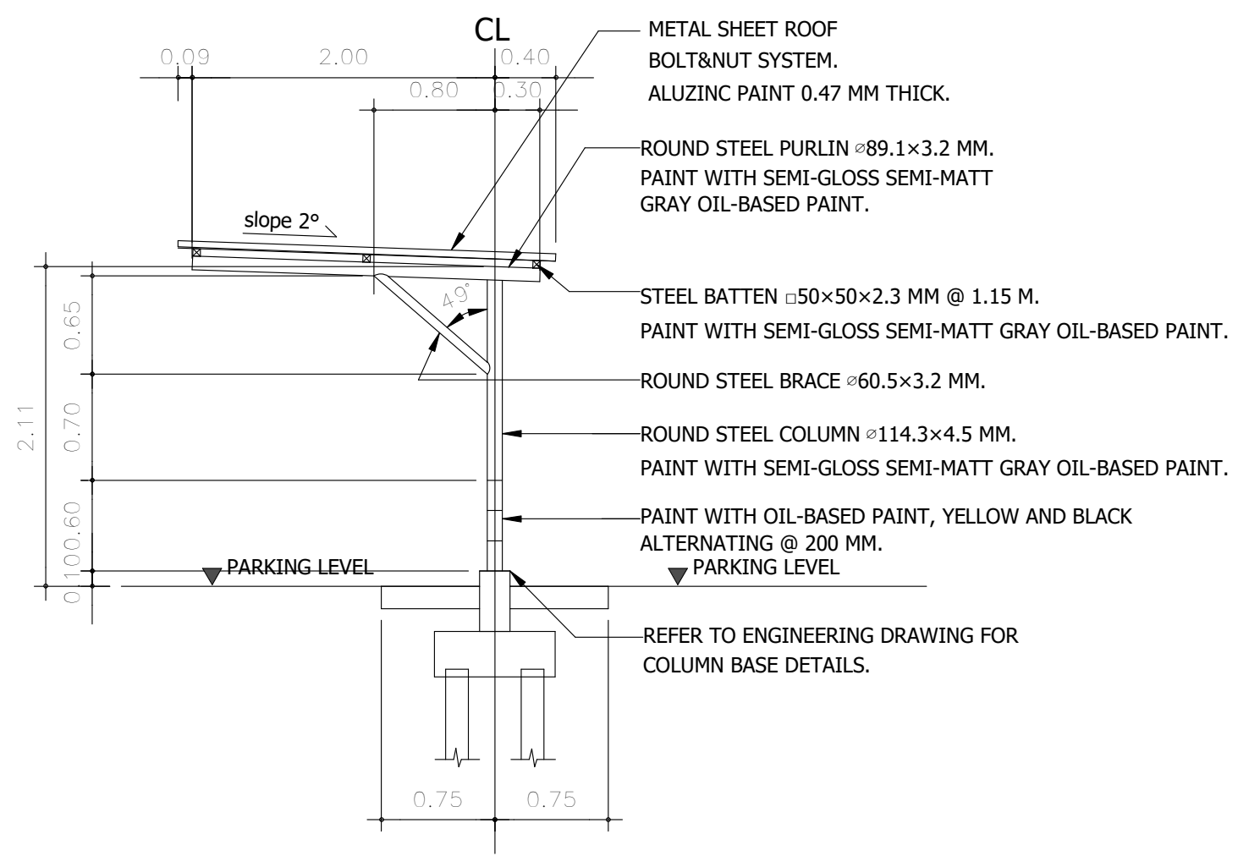
CL
0.09
2.00
0.40
0.80
0.30
slope 2°
49°
2.11
0.65
0.70
0.60
0.10
0.75
0.75
METAL SHEET ROOF
BOLT&NUT SYSTEM.
ALUZINC PAINT 0.47 MM THICK.
ROUND STEEL PURLIN ⌀89.1×3.2 MM.
PAINT WITH SEMI-GLOSS SEMI-MATT GRAY OIL-BASED PAINT.
STEEL BATTEN □50×50×2.3 MM @ 1.15 M.
PAINT WITH SEMI-GLOSS SEMI-MATT GRAY OIL-BASED PAINT.
ROUND STEEL BRACE ⌀60.5×3.2 MM.
ROUND STEEL COLUMN ⌀114.3×4.5 MM.
PAINT WITH SEMI-GLOSS SEMI-MATT GRAY OIL-BASED PAINT.
PAINT WITH OIL-BASED PAINT, YELLOW AND BLACK ALTERNATING @ 200 MM.
PARKING LEVEL
PARKING LEVEL
REFER TO ENGINEERING DRAWING FOR COLUMN BASE DETAILS.

BICYCLE SHELTER
SCALE 1:20

▨ Customer Dedicated Parking

NOTE :THIS PRINT IS OF A CONFIDENTIAL NATURE, IT SHALL NOT BE TRACED,PHOTOGRAPHED,PHOTOSTATED OR REPRODUCED IN ANY MANER,NOR USED FOR ANY PURPOSE WHATSOEVER EXCEPT BY WRITTEN PERMISSION

CLIENT :

GULF EDGE DC 01

87 Wireless Road, M Thai Tower 11th. Floor, All Seasons Place, Lumpini, Pathumwan, Bangkok 10330, Thailand

CONTRACTOR :

华西发展(泰国)有限公司
บริษัท หัวซือ ดีเวลลอปเม้นต์ (ประเทศไทย) จำกัด
HUASHI DEVELOPMENT CO.,LTD
No. 202, Room No. 1403, 14/F, Le Concorde Building,
Ratchadapisek Road, Huaykhwang Sub-District,
Huaykhwang District, Bangkok Metropolitan 10310.

CONSULTANT :

ARbay
บริษัท เอ อาร์ เบย์ จำกัด
ARbay Company Limited
31 st Floor Bangkok Insurance Building
25 South Sathorn road Thungmahamek
Sathorn Bangkok 10120 THAILAND
T +66 (0) 2286 8199
F +66 (0) 2286 2863
info@arbay.co.th

CONSULTANT :

Qbic Engineers & Architects Co.,Ltd.
8 Soi KALONG 4 SANAMBINNAM ROAD,
THASAI SUB-DISTRICT, MUANG NONTHABURI DISTRICT
, NONTHABURI.
Tel 662-950-4374
Fax 662-580-3231
E-Mail : qbic@qbic.co.th, www.qbic.co.th
QBIC ENGINEERS AND ARCHITECTS CO.,LTD.

CONSULTANT :

MITR
MITR TECHNICAL CONSULTANT CO.,LTD.
1168/8 12th FLOOR, LUMPINI TOWER BUILDING,
RAMA IV RD., THUNGMAHAMEK, SATHORN, BANGKOK 10120, THAILAND
TEL : 0-2679-9079-84
FAX : 0-2679-9085 E-mail: mitr_dd@mitr.com

Architect : SIGNATURE
ประกิต พนานุรัตน์ วสถ. 580
ที่อยู่
251/1 ถ.จารุเมือง แขวงรองเมือง เขตปทุมวัน
กรุงเทพมหานคร โทรศัพท์ 02-286-8199

Structural Engineer : SIGNATURE
วิศวกรผู้ออกแบบโครงสร้าง
ณัฐสม สงวนวงษ์ วย 1423
ที่อยู่
2/1 ซ.รามคำแหง 150 ถ.รามคำแหง
แขวง สะพานสูง เขต สะพานสูง กทม. 10240

Structural Inspector : SIGNATURE
วิศวกรผู้ตรวจสอบโครงสร้าง
โกมล จุฑาภัทร วย 964
ที่อยู่
24/18 ซ.นวมินทร์ 129 ถ. นวมินทร์
แขวง นวลจันทร์ เขต บึงกุ่ม กทม. 10230

Electrical Engineer : SIGNATURE
วิศวกรผู้ออกแบบระบบไฟฟ้ากำลัง
นายสุภัทร บูรณวิทย์ วฟก.1265
ที่อยู่
21 ซอยทานสัมฤทธิ์ 13
ตำบลท่าทราย อ.เมืองนนทบุรี จ.นนทบุรี 11000

Mechanical Engineer : SIGNATURE
วิศวกรผู้ออกแบบระบบเครื่องกลและปรับอากาศ
นายประสิทธิ์ เกี้ยวสุนทร วก.1221
ที่อยู่
44/372 ซอยบางกระดี่ 35/1 แขวงแสมดำ
เขตบางขุนเทียน กทม. 10150
ประสิทธิ์

Sanitary Engineer : SIGNATURE
วิศวกรผู้ออกแบบระบบสุขาภิบาล และดับเพลิง
นายทศวรรษ สนั่นฤทธิ์ วส. 215
ที่อยู่
บ้านเลขที่ 99/107 หมู่ที่ 3 ต.ศีรษะจรเข้น้อย
อ.บางเสาธง จ.สมุทรปราการ 10540
ทศวรรษ

ISSUE/REVISION

REV.	DESCRIPTION	DATE
A	90% DEVELOPED	09/05/2026

PROJECT NAME :

GEDC 01

LOCATION:
Nikhom Phattana district, Rayong ,industrial estate,CPGC

BUILDING :

90% DEVELOPED

TITLE :

CAR PARKING PLAN BLOW UP A

JOB NO.		SCALE	1 : 200
DRAWN	LTY	REF.	
CHECKED	LJC	DWG. NO.	MPK00-90-A-CP-001
APPROVED	LXD		
DATE	2026.05.09		