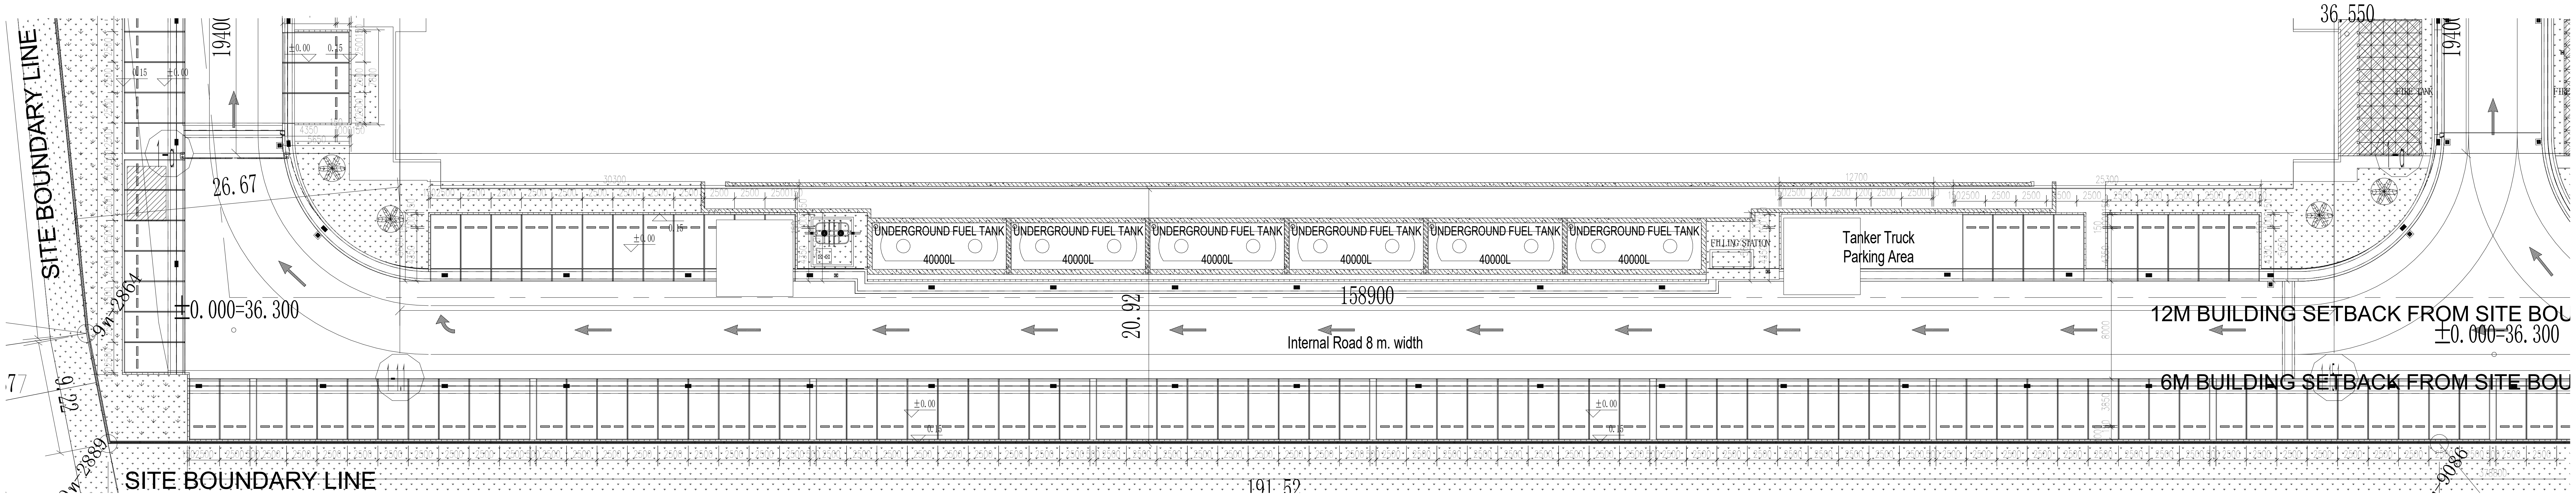

CAR PARKING PLAN BLOW UP (F)

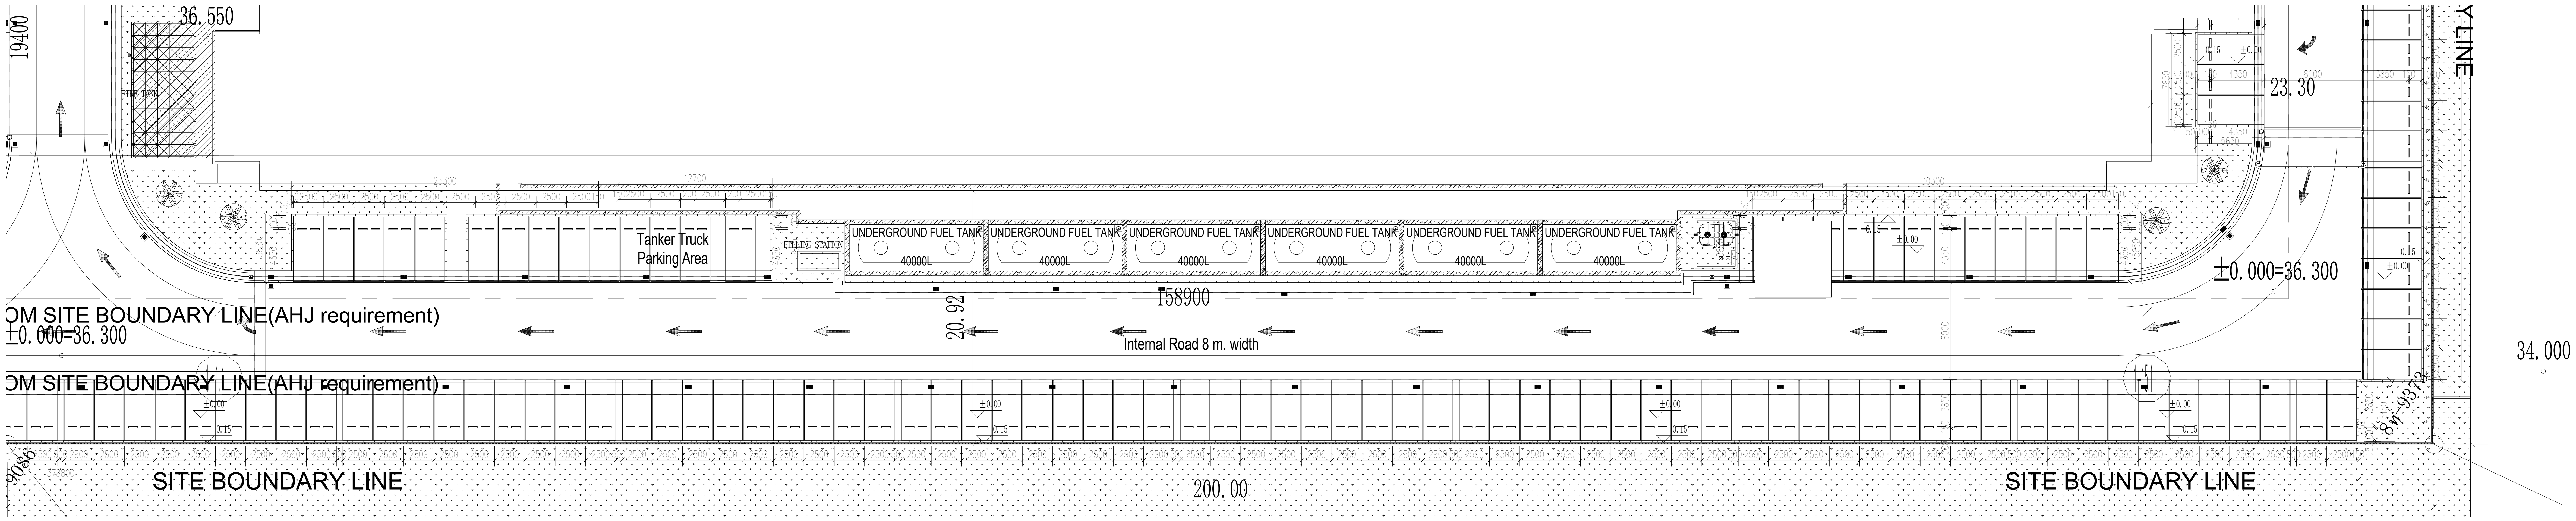

CAR PARKING PLAN BLOW UP (G)

▨ Customer Dedicated Parking

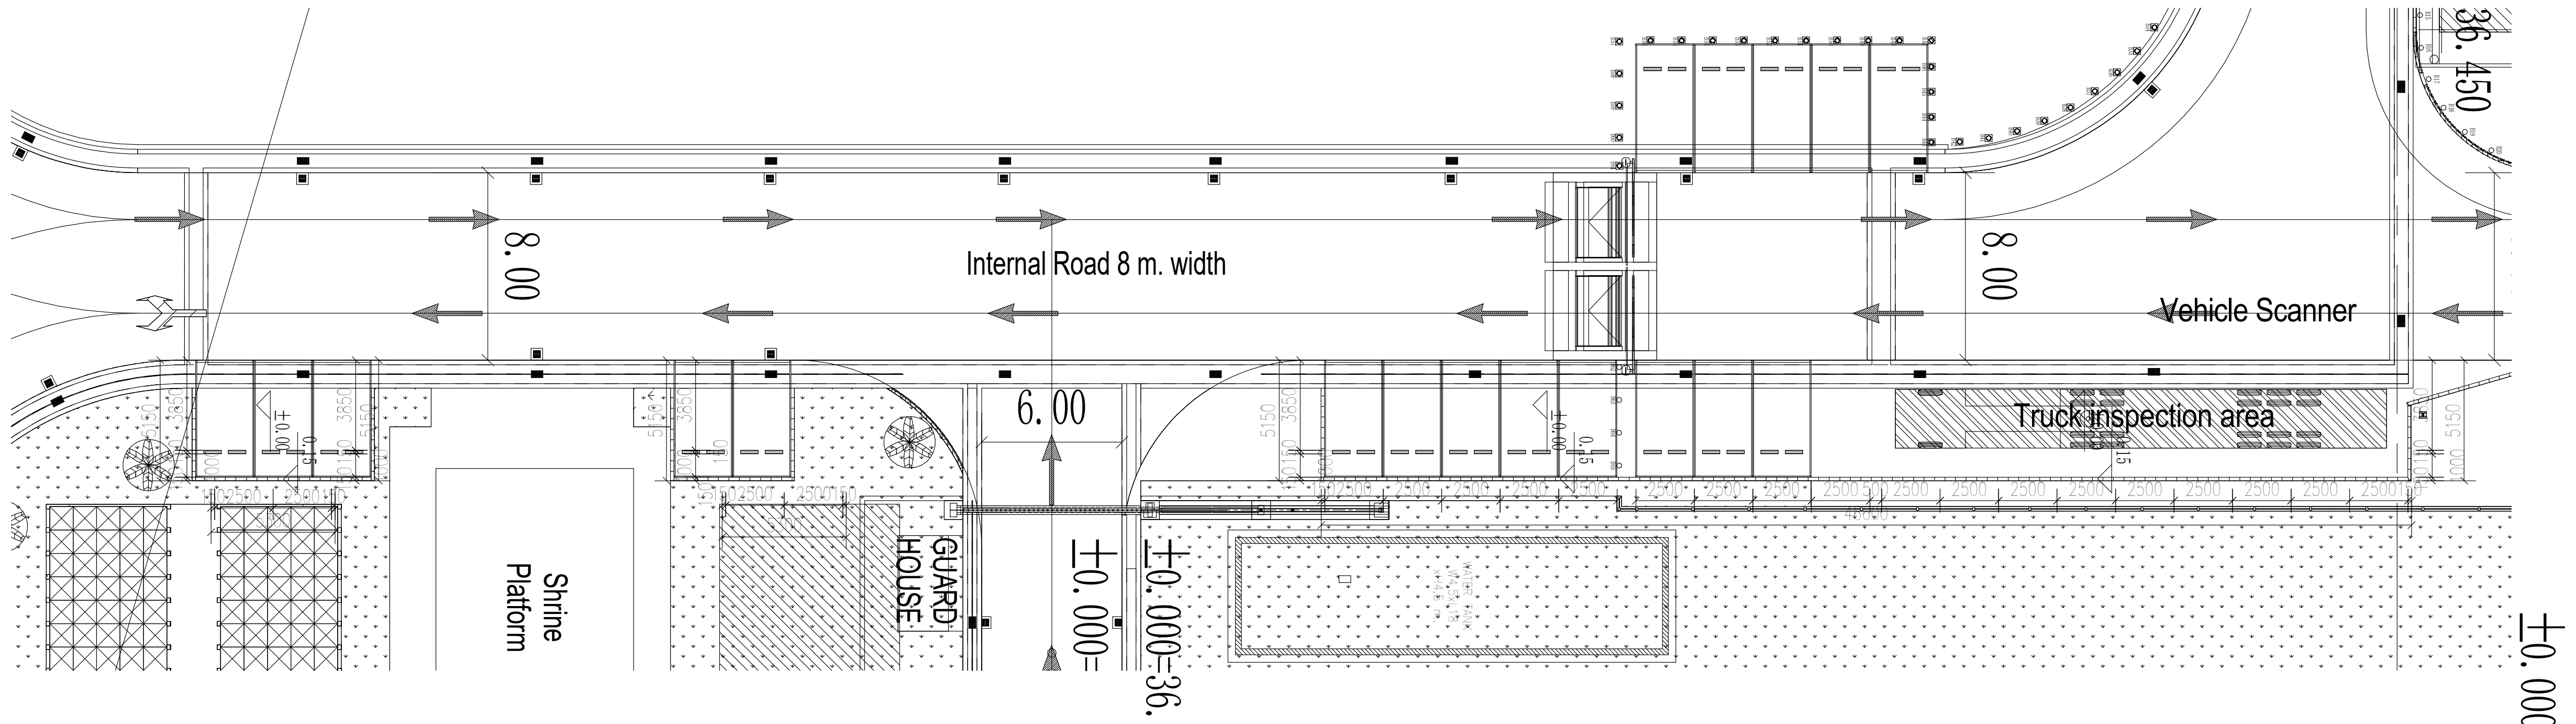

CAR PARKING PLAN BLOW UP (E)
SCALE 1:200

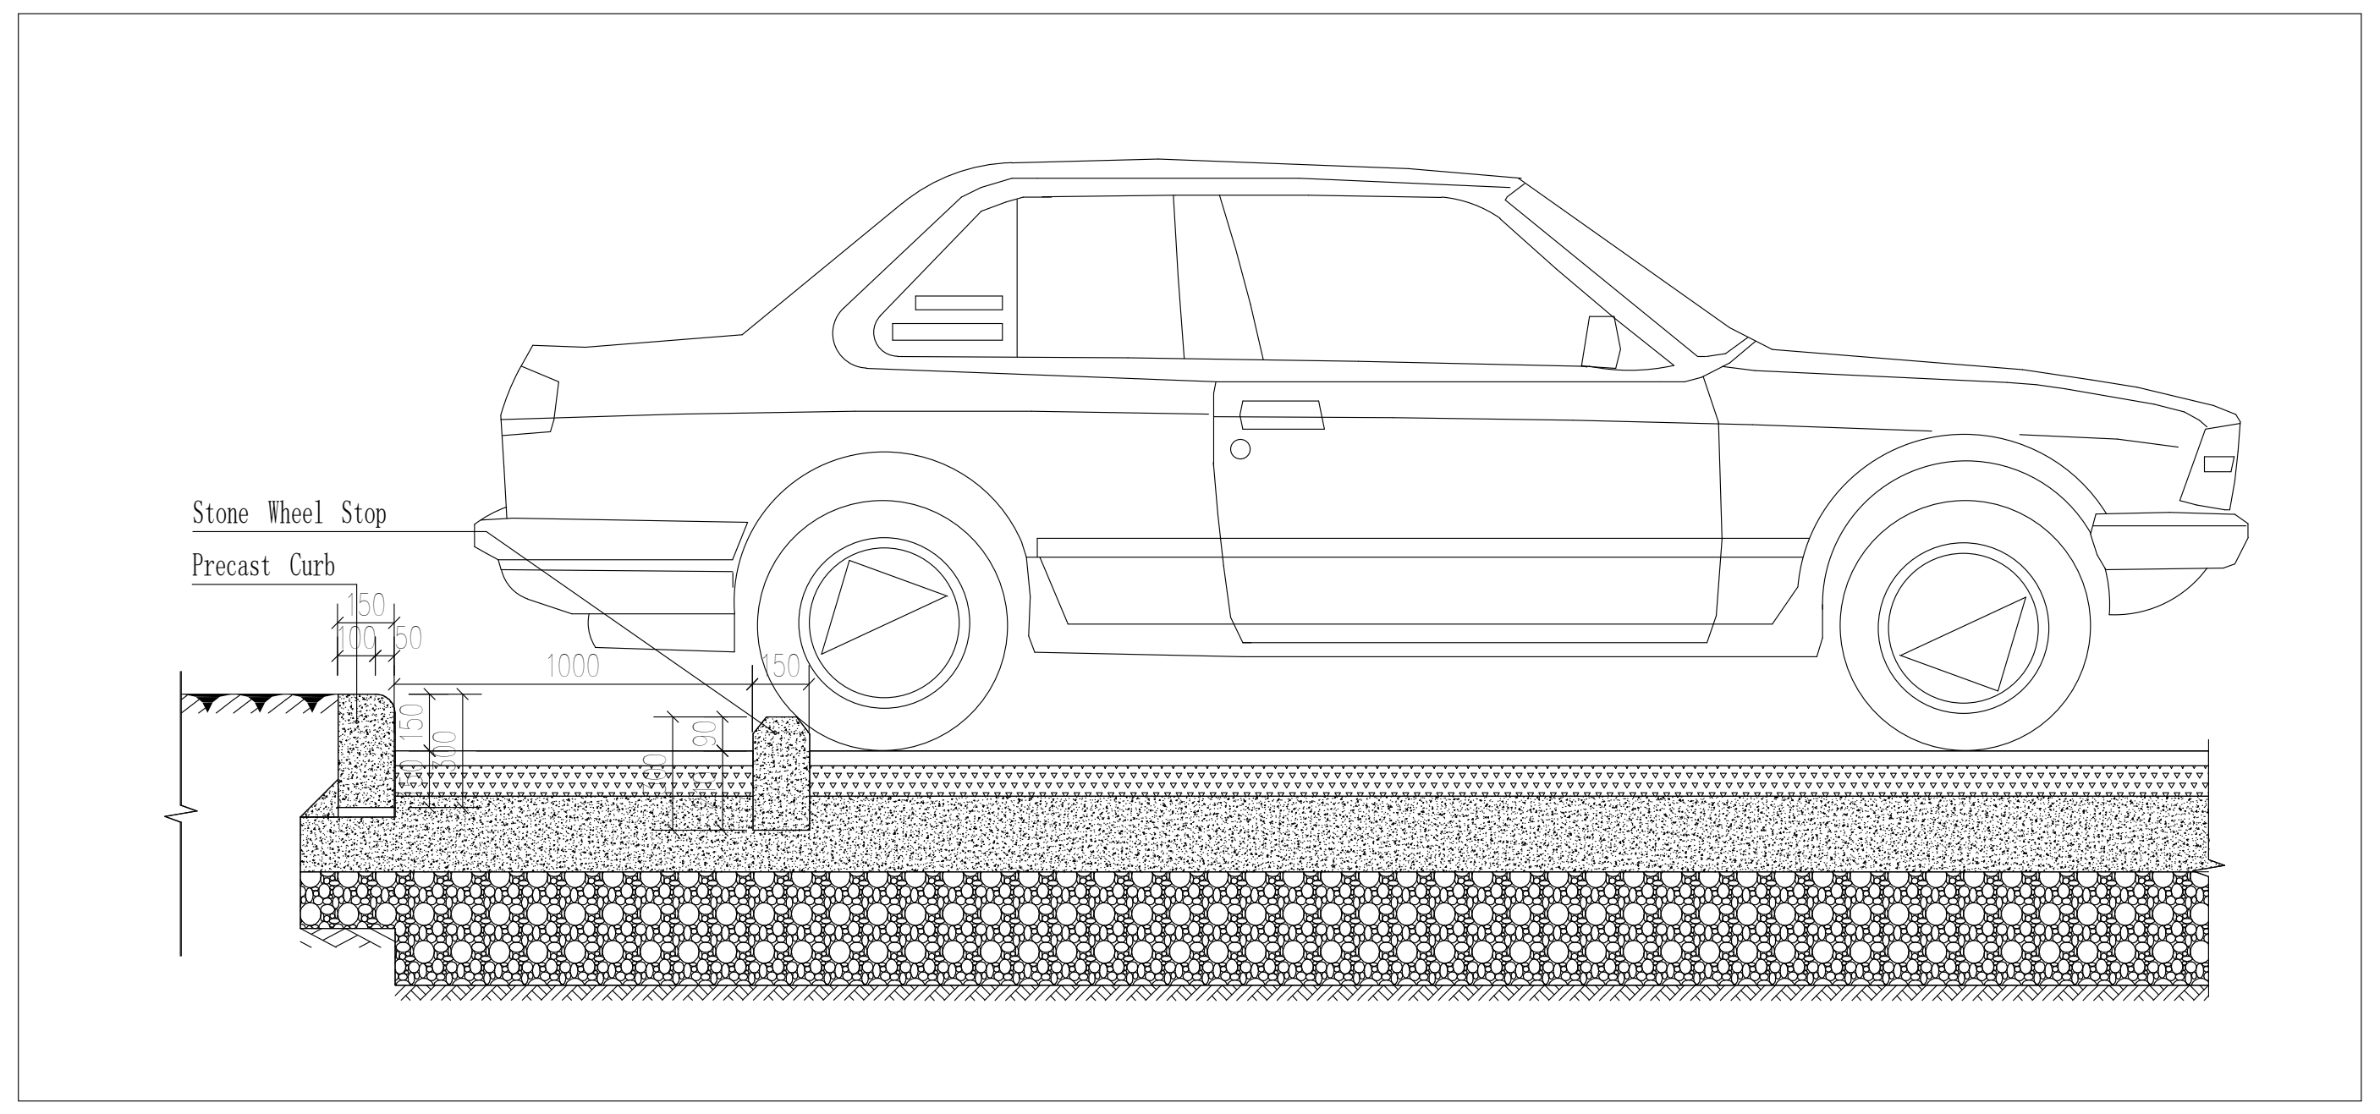

PARKING LOT CONSTRUCTION DETAIL DRAWING
SCALE 1:20

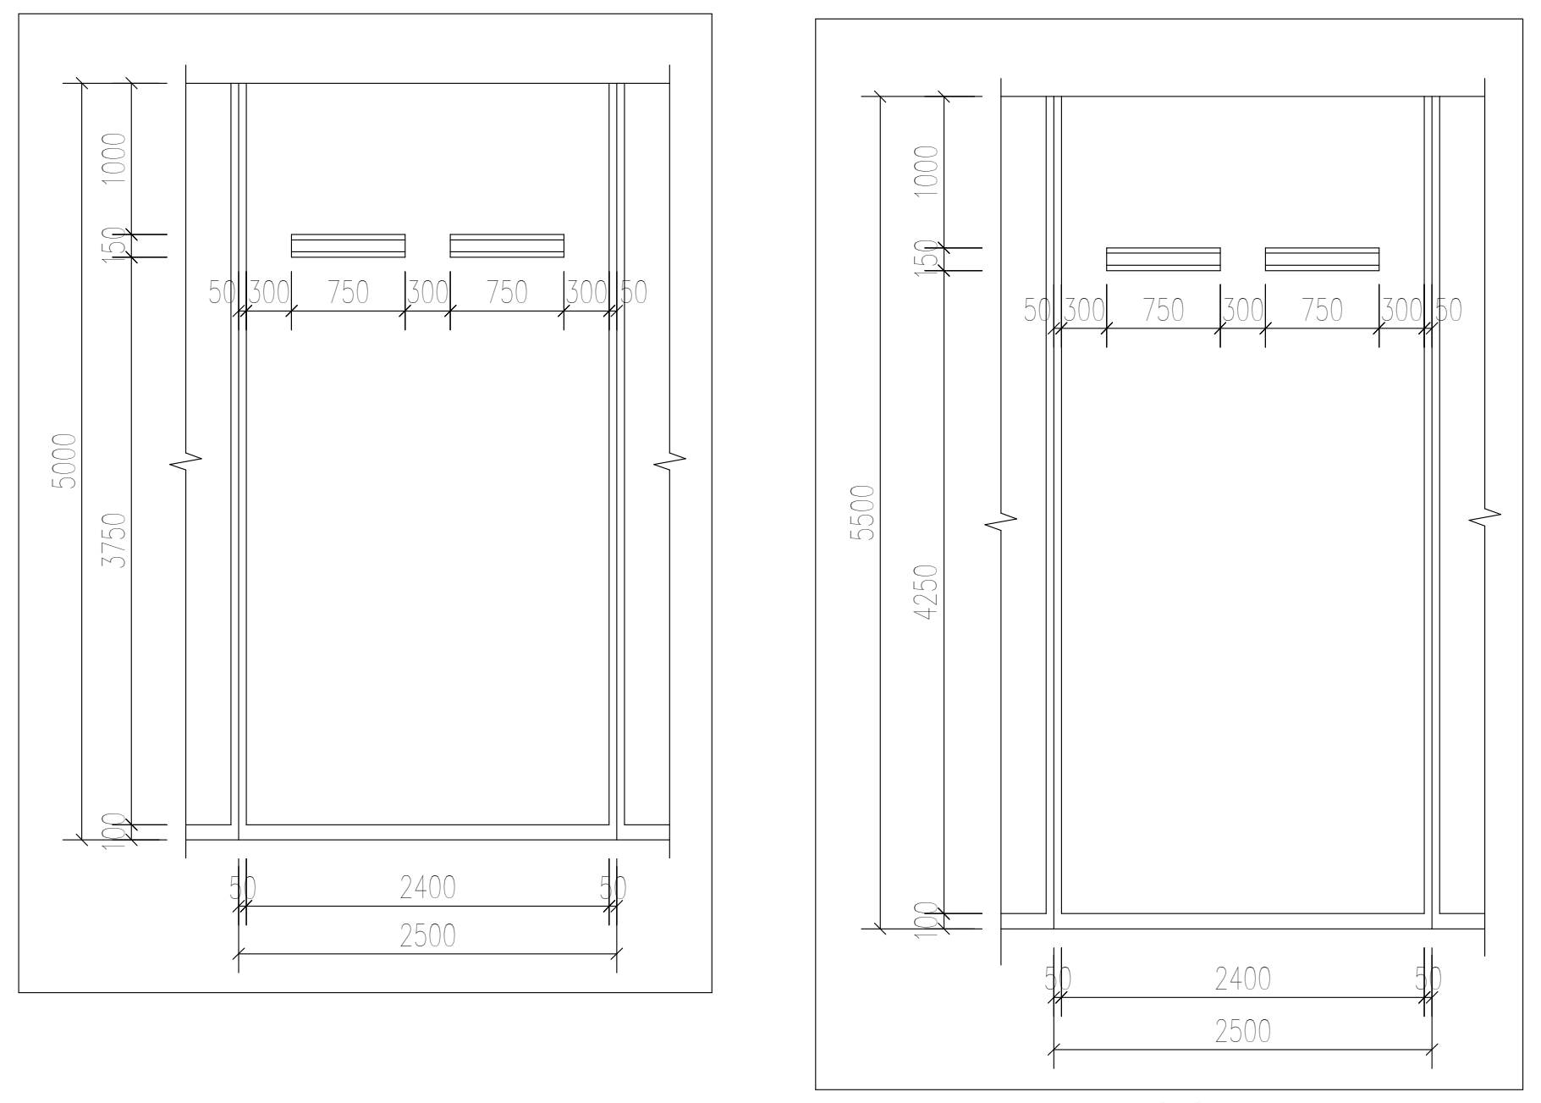

ENLARGED PLAN OF PARKING SPACE(s)
SCALE 1:20

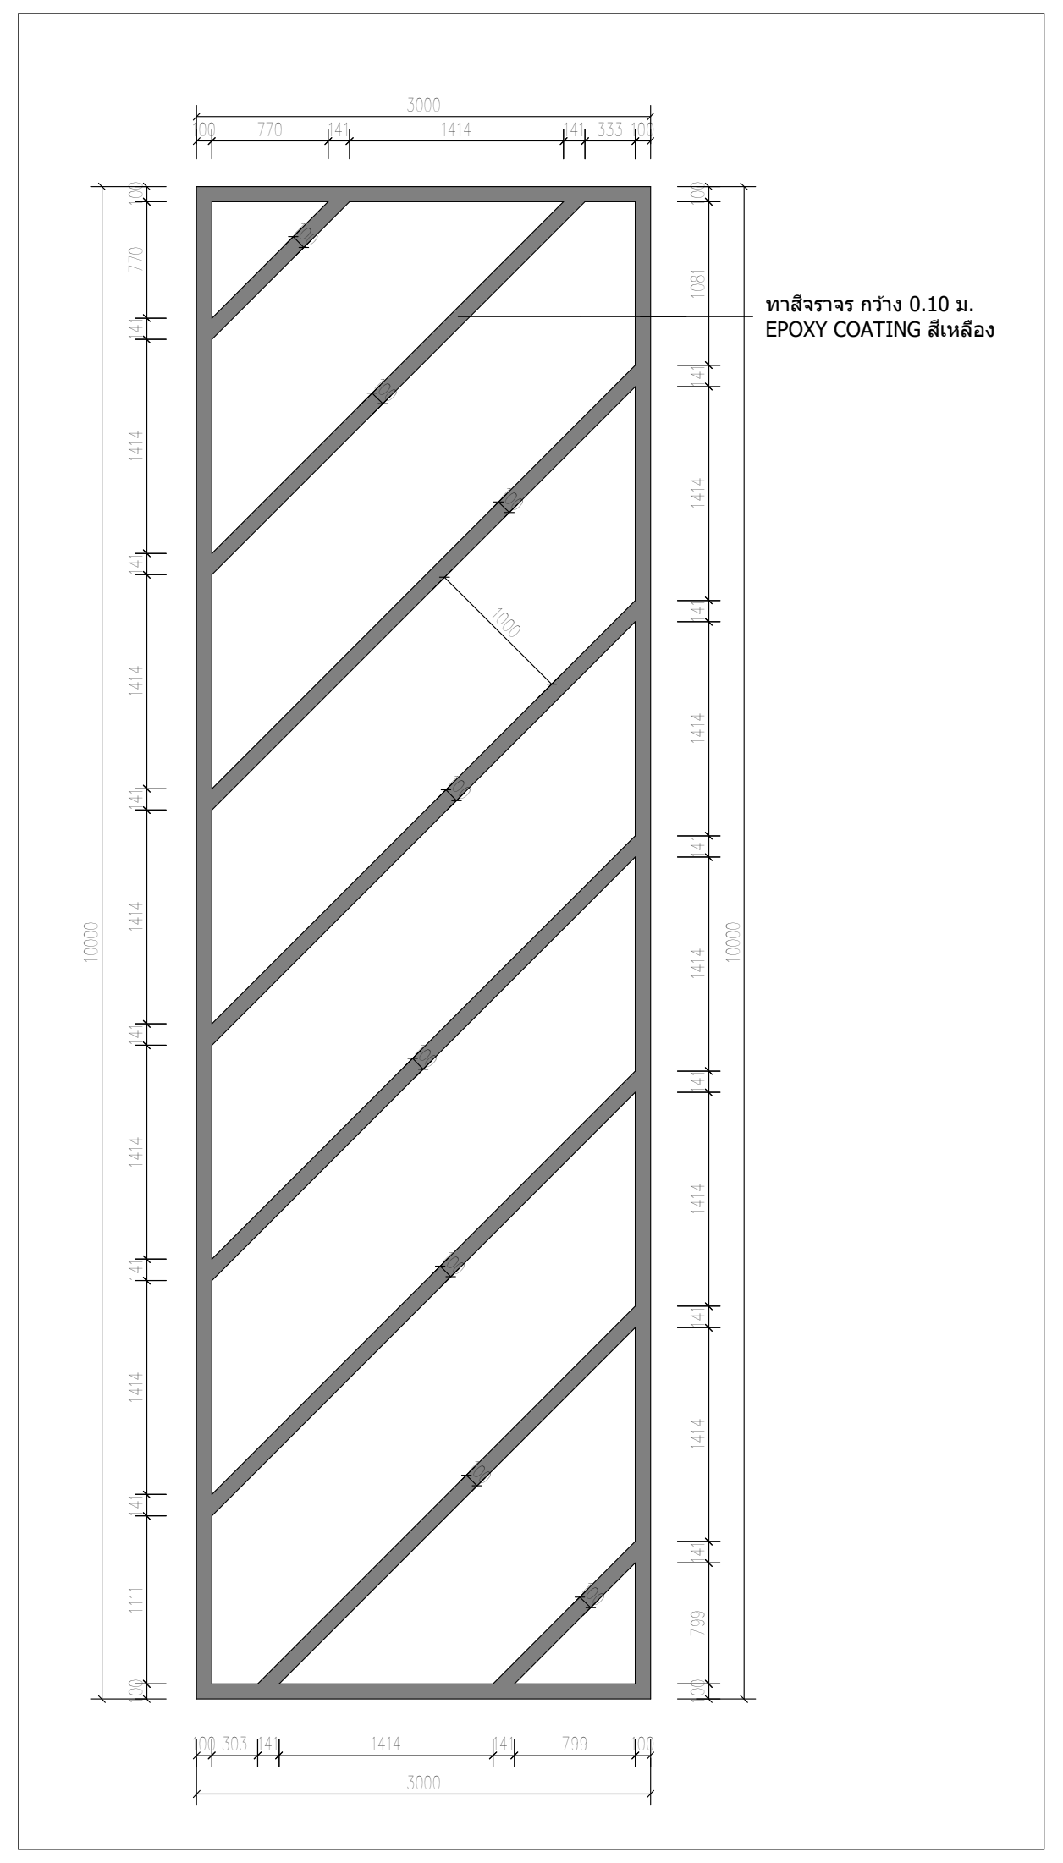

ทาสีจราจร กว้าง 0.10 ม.
EPOXY COATING สีเหลือง

FIRE TRUCK PARKING
SCALE 1:50

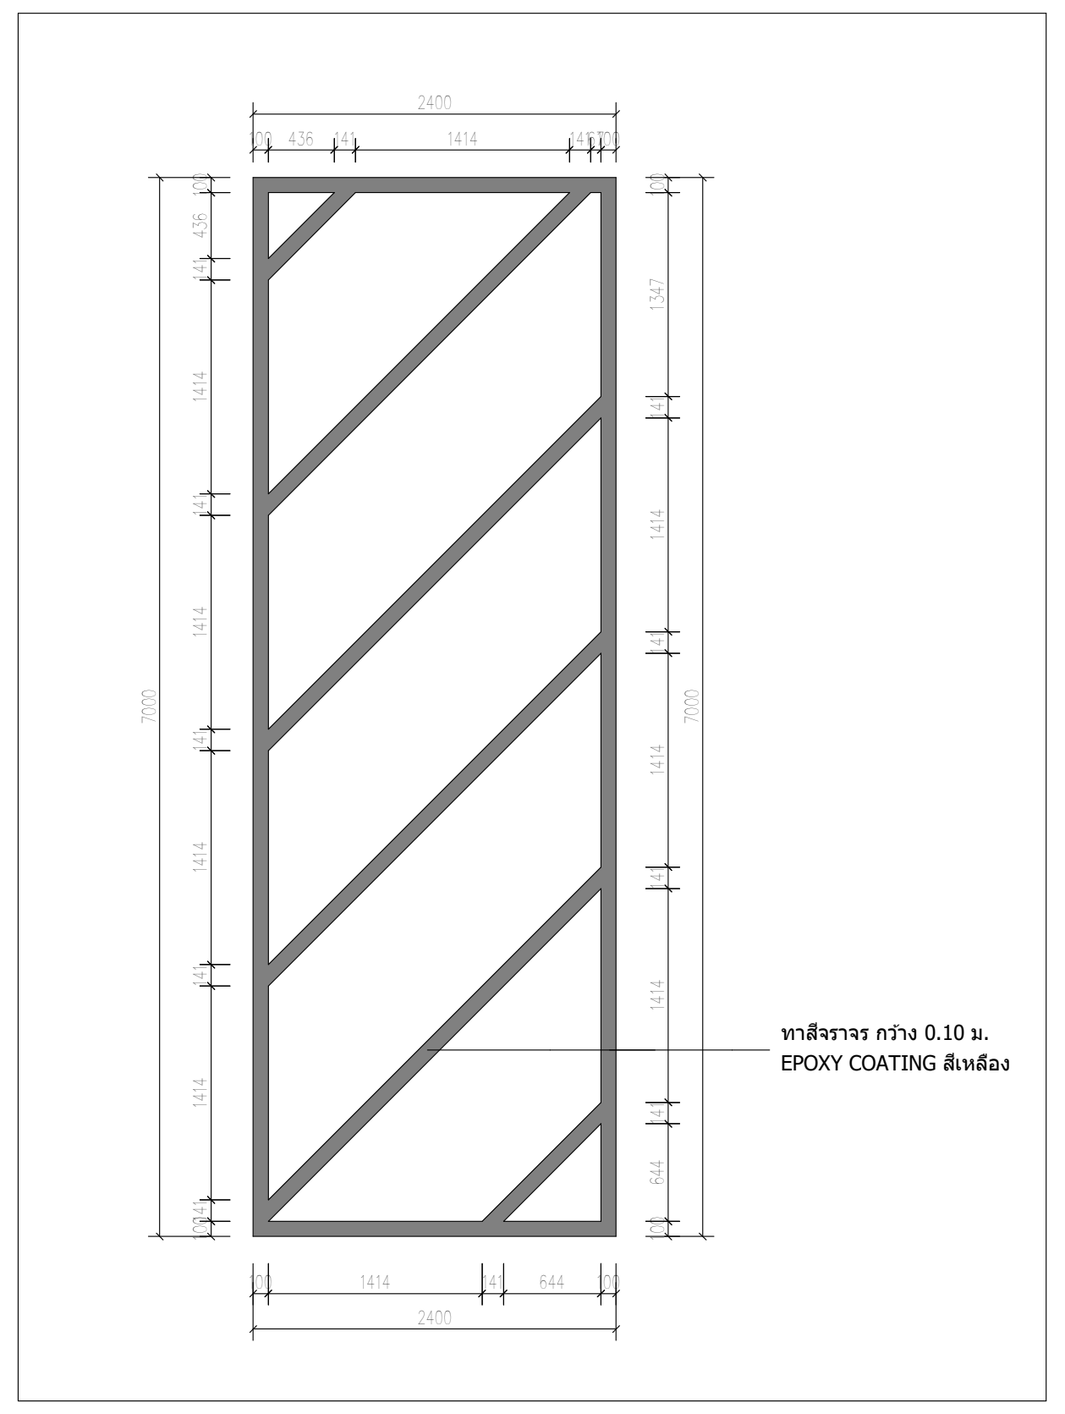

ทาสีจราจร กว้าง 0.10 ม.
EPOXY COATING สีเหลือง

AMBULANCE PARKING
SCALE 1:50

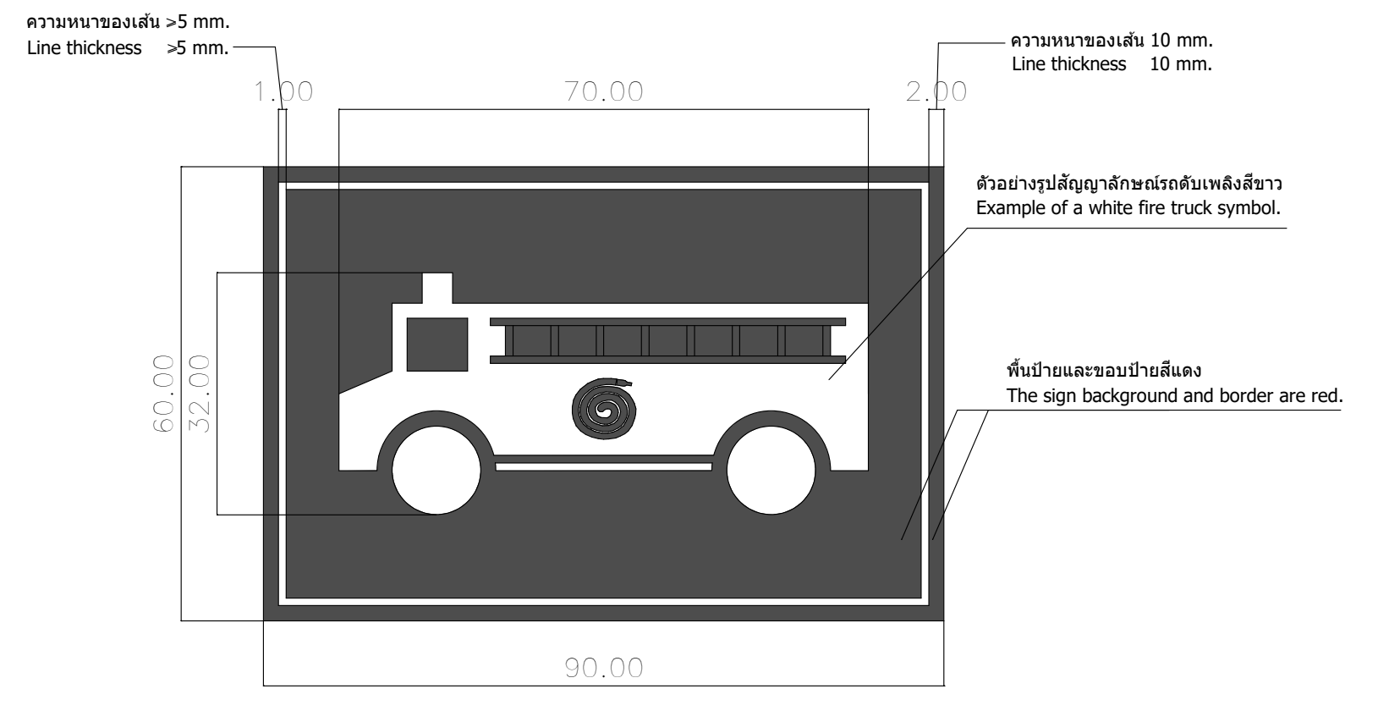

ความหนาของเส้น >5 mm.
Line thickness >5 mm.

ความหนาของเส้น 10 mm.
Line thickness 10 mm.

ตัวอย่างรูปสัญญาลักษณ์รถดับเพลิงสีขาว
Example of a white fire truck symbol.

พื้นป้ายและขอบป้ายสีแดง
The sign background and border are red.

รูปที่ 1 ขนาด ระยะ รูปแบบป้ายแสดงตำแหน่งพื้นที่สำหรับรถดับเพลิง
Figure 1. Size, distance, and design of signs indicating the location of fire trucks.

รูปแบบ สัญลักษณ์ และรายละเอียดเกี่ยวกับพื้นที่สำหรับยานพาหนะ
Design, symbols, and details regarding vehicle areas.

1. ป้ายแสดงตำแหน่งพื้นที่สำหรับรถดับเพลิง
   Sign indicating the location of the fire truck area.
   - 1.1 ป้ายมีลักษณะสี่เหลี่ยมผืนผ้า พื้นสีแดงสะท้อนแสง ขนาดความกว้าง 300 มิลลิเมตร สูง 450 มิลลิเมตร เป็นอย่างน้อย
     The sign is rectangular in shape with a reflective red background and measures at least 300 mm. in width and 450 mm. in height.
   - 1.2 แสดงสัญลักษณ์รูปรถดับเพลิงสีขาว ขนาดความสูงประมาณ 160 มิลลิเมตร ความยาว ประมาณ 350 มิลลิเมตร
     Display a white fire truck symbol, approximately 160 mm. in height and 350 mm. in length.
   - 1.3 กรณีที่ป้ายมีขนาดใหญ่กว่าที่กำหนด ให้ขยายขนาดสัญลักษณ์รูปรถดับเพลิง เพิ่มเป็นสัดส่วนโดยตรง
     If the sign is larger than specified, the size of the fire truck symbol should be increased proportionally.
   - 1.4 สีสะท้อนแสงมีความเข้มปานกลาง
     The fluorescent color is of medium intensity

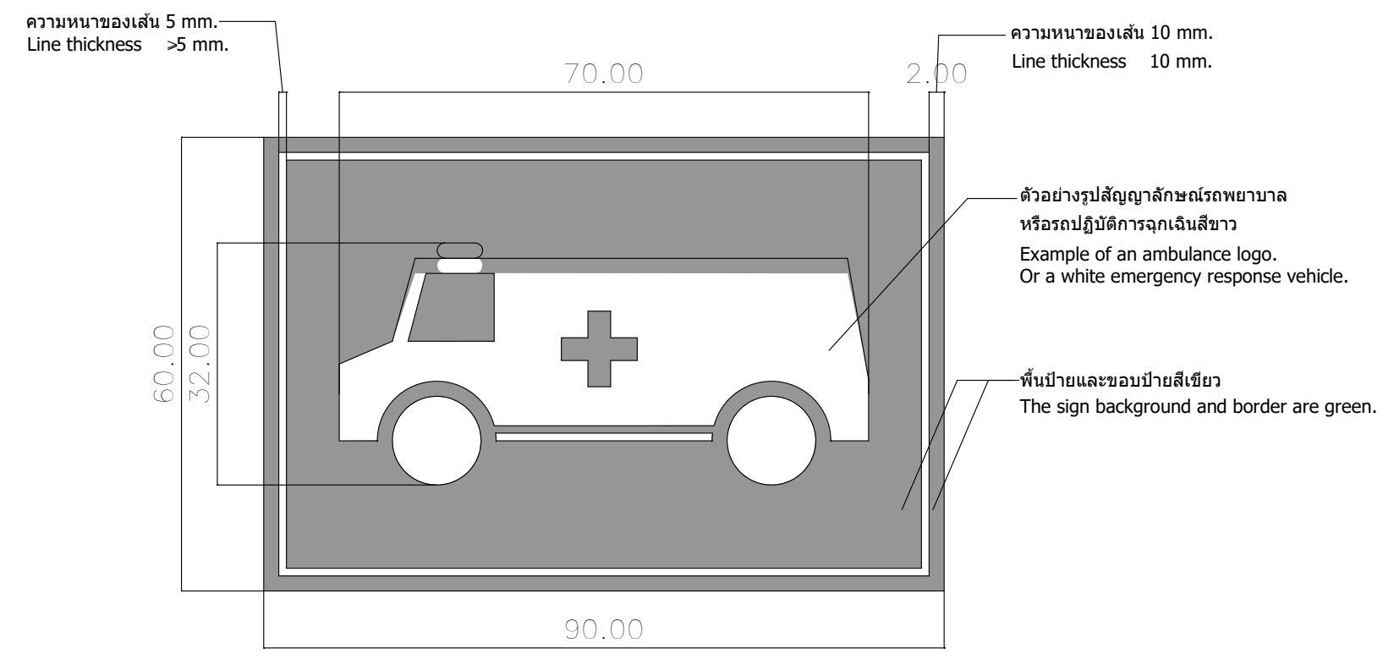

ความหนาของเส้น 5 mm.
Line thickness >5 mm.

ความหนาของเส้น 10 mm.
Line thickness 10 mm.

ตัวอย่างรูปสัญญาลักษณ์รถพยาบาล
หรือรถปฏิบัติการฉุกเฉินสีขาว
Example of an ambulance logo.
Or a white emergency response vehicle.

พื้นป้ายและขอบป้ายสีเขียว
The sign background and border are green.

รูปที่ 2 ขนาด ระยะ รูปแบบป้ายแสดงตำแหน่งพื้นที่สำหรับรถพยาบาลหรือรถปฏิบัติการฉุกเฉิน
Figure 2 shows the size, distance, and format of signs indicating the location of ambulances or emergency vehicles.

2. ป้ายแสดงตำแหน่งพื้นที่สำหรับรถพยาบาลหรือรถปฏิบัติการฉุกเฉิน
   Signs indicating the location of areas for ambulances or emergency vehicles.
   - 2.1 ป้ายมีลักษณะสี่เหลี่ยมผืนผ้า พื้นสีเขียวสะท้อนแสง ขนาดความกว้าง 300 มิลลิเมตร สูง 450 มิลลิเมตร เป็นอย่างน้อย
     The sign is rectangular in shape with a reflective green background and a width of 300 millimeters. At least 450 millimeters high.
   - 1.2 แสดงสัญลักษณ์รูปรถดับเพลิงสีขาว ขนาดความสูงประมาณ 160 มิลลิเมตร ความยาว ประมาณ 350 มิลลิเมตร
     Display a white fire truck symbol, approximately 160 millimeters in height and 350 millimeters in length.
   - 1.3 กรณีที่ป้ายมีขนาดใหญ่กว่าที่กำหนด ให้ขยายขนาดสัญลักษณ์รูปรถดับเพลิง เพิ่มเป็นสัดส่วนโดยตรง
     If the sign is larger than specified, the size of the fire truck symbol should be increased proportionally.
   - 1.4 สีสะท้อนแสงมีความเข้มปานกลาง
     The fluorescent color is of medium intensity

NOTE :THIS PRINT IS OF A CONFIDENTIAL NATURE, IT SHALL NOT BE TRACED,PHOTOGRAPHED,PHOTOSTATED OR REPRODUCED IN ANY MANER,NOR USED FOR ANY PURPOSE WHATSOEVER EXCEPT BY WRITTEN PERMISSION

CLIENT :

GULF EDGE DC 01

87 Wireless Road, M Thai Tower 11th. Floor, All Seasons Place, Lumpini,
Pathumwan, Bangkok 10330, Thailand

CONTRACTOR :

华西发展(泰国)有限公司
บริษัท หัวซือ ดีเวลลอปเม้นต์ (ประเทศไทย) จำกัด
HUASHI DEVELOPMENT CO.,LTD
No. 202, Room No. 1403, 14/F, Le Concorde Building,
Ratchadapisek Road, Huaykhwang Sub-District,
Huaykhwang District, Bangkok Metropolitan 10310.

CONSULTANT :

ARbay
บริษัท เอ อาร์ เบย์ จำกัด
ARbay Company Limited
31 st Floor Bangkok Insurance Building
25 South Sathorn road Thungmahamek
Sathorn Bangkok 10120 THAILAND
T +66 (0) 2286 8199
F +66 (0) 2286 2863
info@arbay.co.th

CONSULTANT :

Qbic Engineers & Architects Co.,Ltd.
8 Soi KALONG 4 SANAMBINNAM ROAD,
THASAI SUB-DISTRICT, MUANG NONTHABURI DISTRICT
, NONTHABURI.
Tel 662-950-4374
Fax 662-580-3231
E-Mail : qbic@qbic.co.th, www.qbic.co.th
QBIC ENGINEERS AND ARCHITECTS CO.,LTD.

CONSULTANT :

MITR
MITR TECHNICAL CONSULTANT CO.,LTD.
1168/8 12th FLOOR, LUMPINI TOWER BUILDING,
RAMA IV RD., THUNGMAHAMEK, SATHORN, BANGKOK 10120, THAILAND
TEL : 0-2679-9079-84
FAX : 0-2679-9085 E-mail: mitr_dd@mitr.com

Architect :	SIGNATURE
ประกิต พนานุรัตน์ วสถ. 580 ที่อยู่ 251/1 ถ.จารุเมือง แขวงรองเมือง เขตปทุมวัน กรุงเทพมหานคร โทรศัพท์ 02-286-8199	
Structural Engineer :	SIGNATURE
วิศวกรผู้ออกแบบโครงสร้าง	
ณัฐสม สงวนวงษ์ วย 1423 ที่อยู่ 2/1 ซ.รามคำแหง 150 ถ.รามคำแหง แขวง สะพานสูง เขต สะพานสูง กทม. 10240	ณัฐสม สงวนวงษ์
Structural Inspector :	SIGNATURE
วิศวกรผู้ตรวจสอบโครงสร้าง	
โกมล จุฑาภัทร วย 964 ที่อยู่ 24/18 ซ.นวมินทร์ 129 ถ. นวมินทร์ แขวง นวลจันทร์ เขต บึงกุ่ม กทม. 10230	
Electrical Engineer :	SIGNATURE
วิศวกรผู้ออกแบบระบบไฟฟ้ากำลัง	
นายสุภัทร บูรณวิทย์ วฟก.1265 ที่อยู่ 21 ซอยทานสัมฤทธิ์ 13 ตำบลท่าทราย อ.เมืองนนทบุรี จ.นนทบุรี 11000	
Mechanical Engineer :	SIGNATURE
วิศวกรผู้ออกแบบระบบเครื่องกลและปรับอากาศ	
นายประสิทธิ์ เกี้ยวสุนทร วก.1221 ที่อยู่ 44/372 ซอยบางกระดี่ 35/1 แขวงแสมดำ เขตบางขุนเทียน กทม. 10150	ประสิทธิ์
Sanitary Engineer :	SIGNATURE
วิศวกรผู้ออกแบบระบบสุขาภิบาล และดับเพลิง	
นายทศวรรษ สนั่นฤทธิ์ วส. 215 ที่อยู่ บ้านเลขที่ 99/107 หมู่ที่ 3 ต.ศีรษะจรเข้น้อย อ.บางเสาธง จ.สมุทรปราการ 10540	ทศวรรษ

ISSUE/REVISION

REV.	DESCRIPTION	DATE
A	90% DEVELOPED	09/05/2026

PROJECT NAME :

GEDC 01

LOCATION:
Nikhom Phattana district, Rayong ,industrial estate,CPGC

BUILDING :

90% DEVELOPED

TITLE :

CAR PARKING PLAN BLOW UP A

JOB NO.	SCALE 1:200
DRAWN LTY	REF.
CHECKED LJC	DWG. NO. MPK00-90-A-CP-002
APPROVED LXD	
DATE 2026.05.09	