FENCING LEGEND :		FENCING LEGEND :	
- - - -	Type A Security K4 Anti-Climb Fence mounted on top of retaining wall at Elevation 37.050 m	- - - -	Type J Security K4 Anti-Climb Fence mounted on top of retaining wall at Elevation 37.737 m
- - - -	Type B Security K4 Anti-Climb Fence mounted on top of retaining wall at Elevation 37.450 m	- - - -	Type K Security K4 Anti-Climb Fence mounted on top of retaining wall at Elevation 37.299 m
- - - -	Type C Security K4 Anti-Climb Fence mounted on top of retaining wall at Elevation 37.850 m	- - - -	Type L Security K4 Anti-Climb Fence mounted on top of retaining wall at Elevation 36.862 m
- - - -	Type D Security K4 Anti-Climb Fence mounted on top of retaining wall at Elevation 38.250 m	- - - -	Type M Security K4 Anti-Climb Fence mounted on top of retaining wall at Elevation 36.550 m
- - - -	Type E Security K4 Anti-Climb Fence mounted on top of retaining wall at Elevation 38.650 m	- - - -	Type N Security K4 Anti-Climb Fence mounted on top of retaining wall at Elevation 36.550 m
- - - -	Type F Security K4 Anti-Climb Fence mounted on top of retaining wall at Elevation 39.050 m	- - - -	Type P Security K4 Anti-Climb Fence mounted on top of retaining wall at Elevation 36.550 m
- - - -	Type G Security K4 Anti-Climb Fence mounted on top of retaining wall at Elevation 38.612 m	- - - -	Type Q Security NON-K4 Anti-Climb Fence mounted on top of retaining wall at Elevation 36.450 m
- - - -	Type H Security K4 Anti-Climb Fence mounted on top of retaining wall at Elevation 38.175 m	- - - -	Type R Security K4 Anti-Climb Fence mounted on top of retaining wall at Elevation 37.350 m
—·—·—	Temporary Fence	- - - -	Type S Security K4 Anti-Climb Fence mounted on top of retaining wall at Elevation 39.150 m

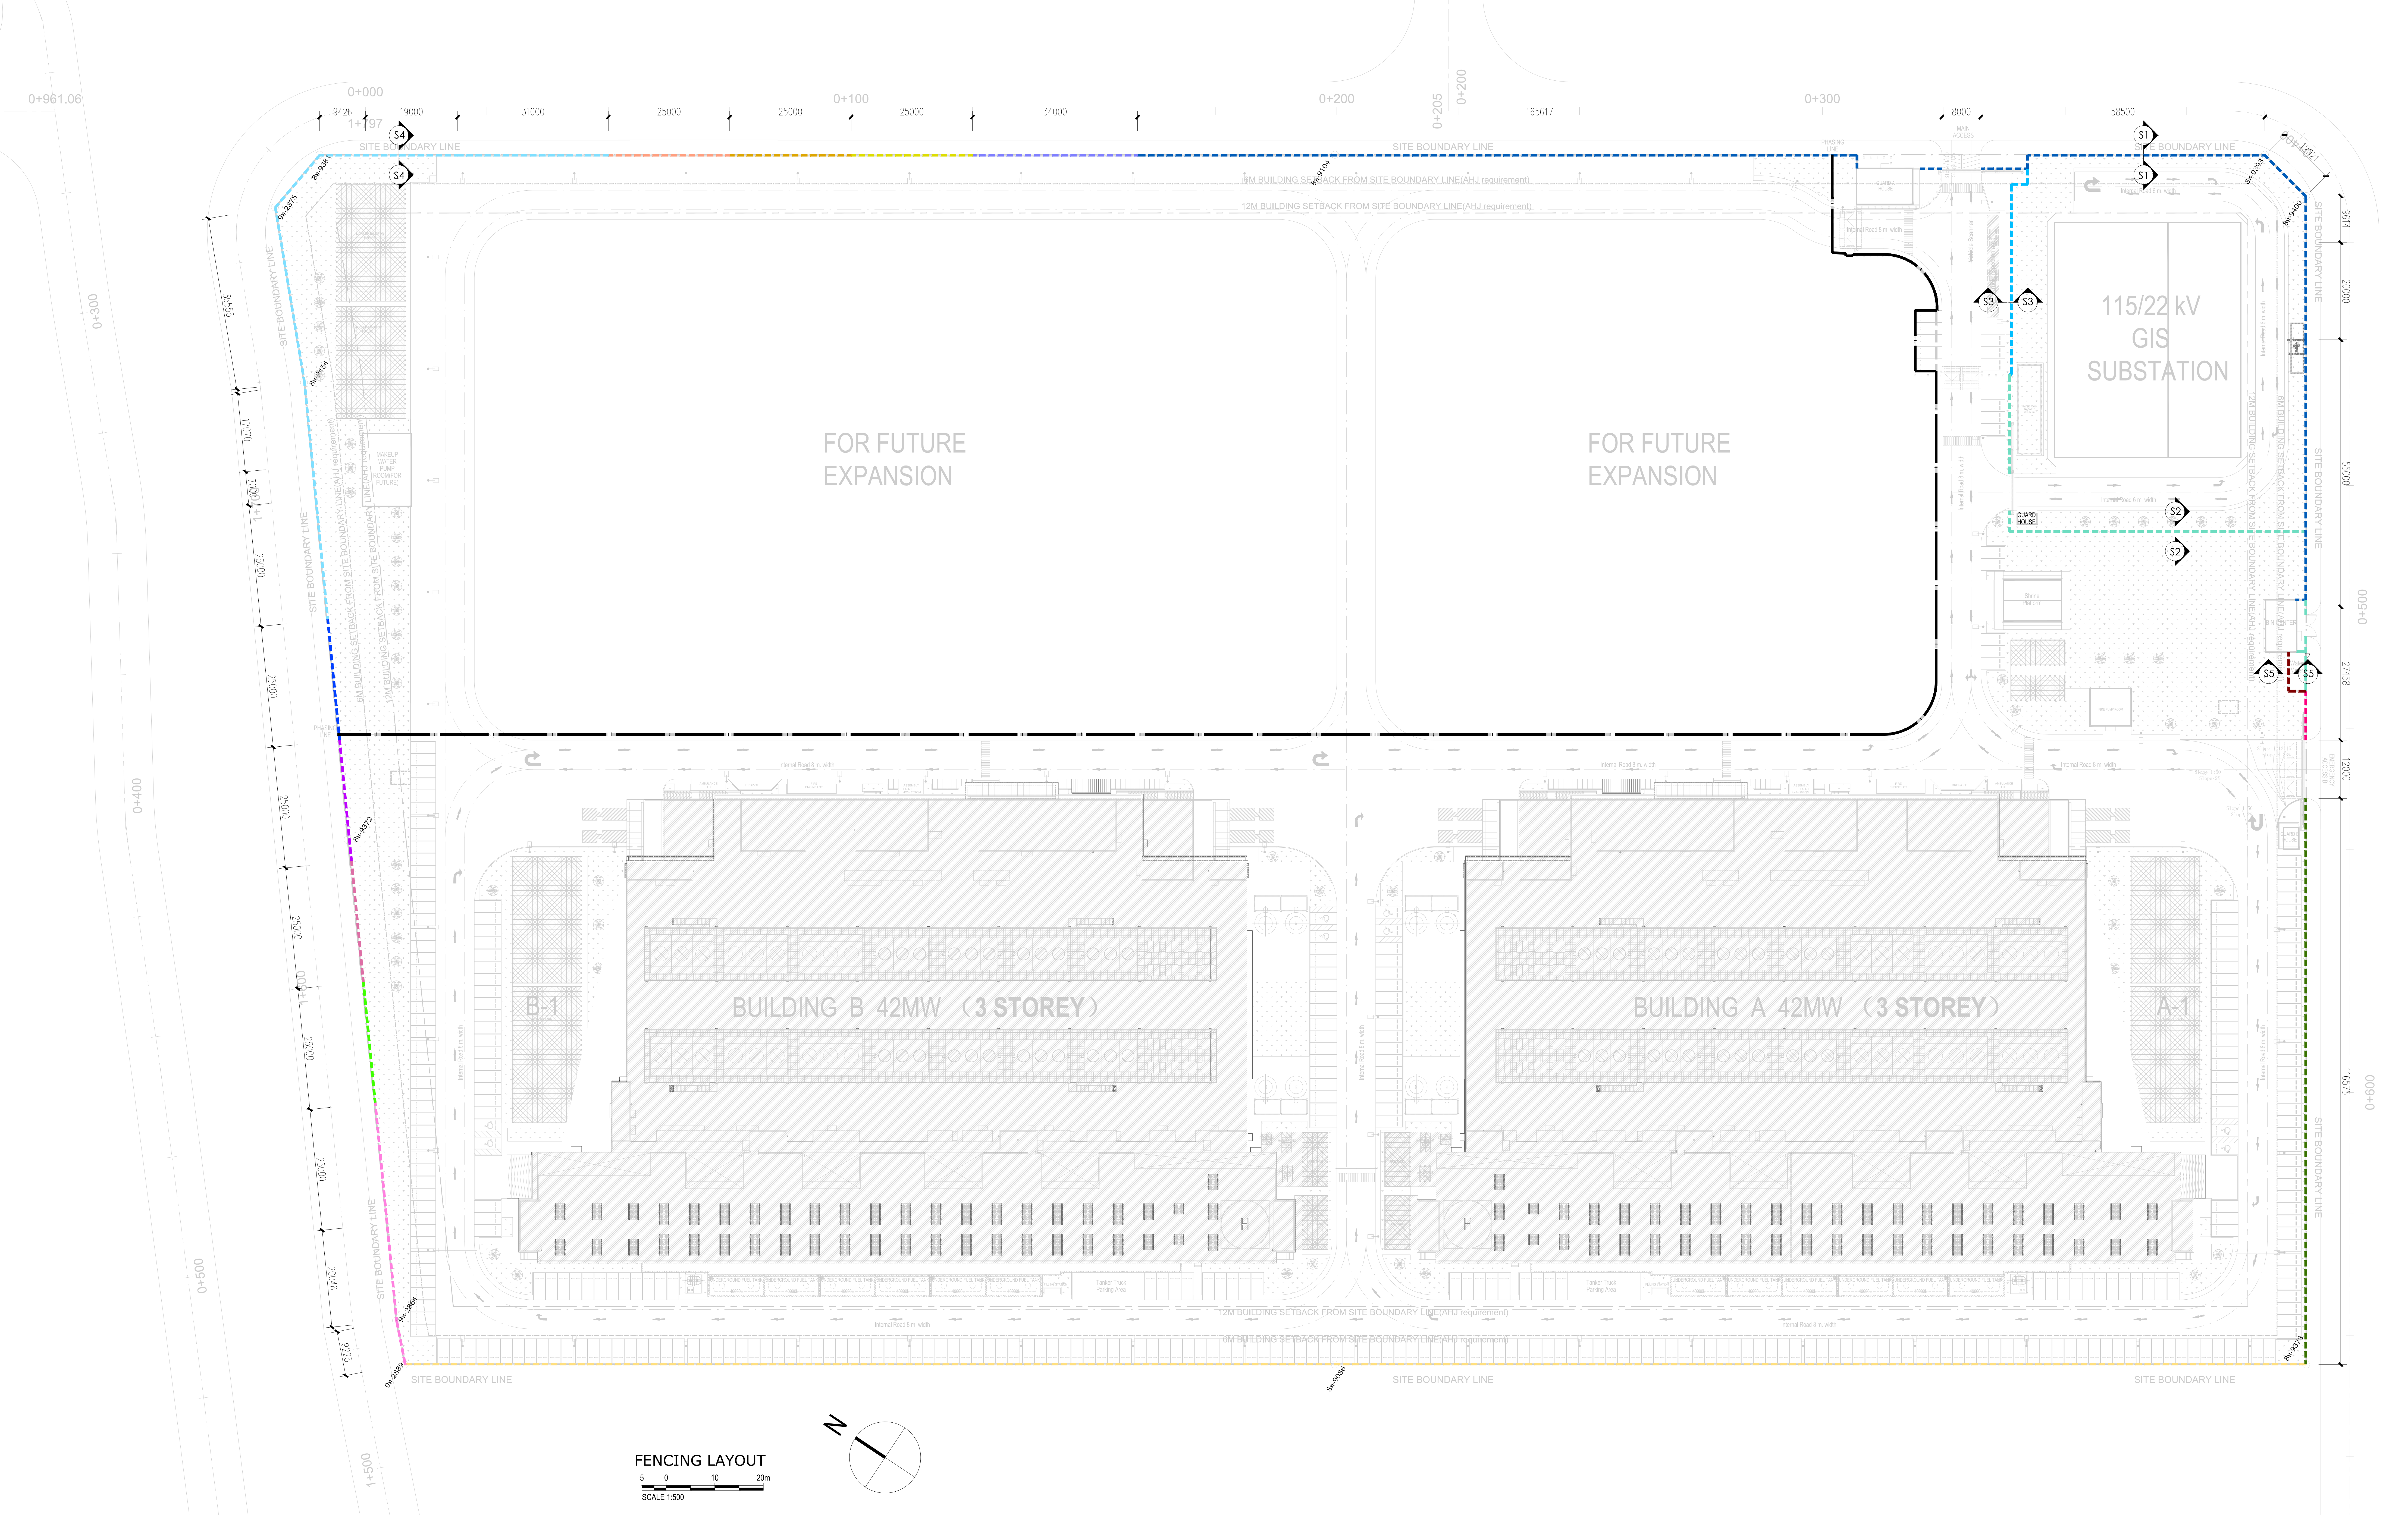

FENCING LAYOUT

5 0 10 20m

SCALE 1:500

NOTE : THIS PRINT IS OF A CONFIDENTIAL NATURE, IT SHALL NOT BE TRACED,PHOTOGRAPHED,PHOTOSTATED OR REPRODUCED IN ANY MANER,NOR USED FOR ANY PURPOSE WHATSOEVER EXCEPT BY WRITTEN PERMISSION

CLIENT :

GULF EDGE DC 01

87 Wireless Road, M Thai Tower 11th. Floor, All Seasons Place, Lumpini,
Pathumwan, Bangkok 10330, Thailand

CONTRACTOR :

华西发展(泰国)有限公司
บริษัท หัวซือ ดีเวลลอปเม้นต์ (ประเทศไทย) จำกัด
HUASHI DEVELOPMENT CO.,LTD
No. 202, Room No. 1403, 14/F, Le Concorde Building,
Ratchadapisek Road, Huaykhwang Sub-District,
Huaykhwang District, Bangkok Metropolitan 10310.

CONSULTANT :

ARbay
บริษัท เอ อาร์ เบย์ จำกัด
ARbay Company Limited
31 st Floor Bangkok Insurance Building
25 South Sathorn road Thungmahamek
Sathorn Bangkok 10120 THAILAND
T +66 (0) 2286 8199
F +66 (0) 2286 2863
info@arbay.co.th

CONSULTANT :

Qbic Engineers & Architects Co.,Ltd.
8 Soi KALONG 4 SANAMBINNAM ROAD,
THASAI SUB-DISTRICT, MUANG NONTHABURI DISTRICT
, NONTHABURI.
Tel 662-950-4374
Fax 662-580-3231
E-Mail : qbic@qbic.co.th, www.qbic.co.th
QBIC ENGINEERS AND ARCHITECTS CO.,LTD.

CONSULTANT :

MITR
MITR TECHNICAL CONSULTANT CO.,LTD.
1168/8 12th FLOOR, LUMPINI TOWER BUILDING,
RAMA IV RD., THUNGMAHAMEK, SATHORN, BANGKOK 10120, THAILAND
TEL : 0-2679-9079-84
FAX : 0-2679-9085 E-mail: mitr_dd@mitr.com

Architect :	SIGNATURE
ประกิต พนานุรัตน์ วสถ. 580 ที่อยู่ 251/1 ถ.จารุเมือง แขวงรองเมือง เขตปทุมวัน กรุงเทพมหานคร โทรศัพท์ 02-286-8199	

Structural Engineer :	SIGNATURE
วิศวกรผู้ออกแบบโครงสร้าง	
ณัฐสม สงวนวงษ์ วย 1423 ที่อยู่ 2/1 ซ.รามคำแหง 150 ถ.รามคำแหง แขวง สะพานสูง เขต สะพานสูง กทม. 10240	

Structural Inspector :	SIGNATURE
วิศวกรผู้ตรวจสอบโครงสร้าง	
โกมล จุฑาภัทร วย 964 ที่อยู่ 24/18 ซ.นวมินทร์ 129 ถ. นวมินทร์ แขวง นวลจันทร์ เขต บึงกุ่ม กทม. 10230	

Electrical Engineer :	SIGNATURE
วิศวกรผู้ออกแบบระบบไฟฟ้ากำลัง	
นายสุภัทร บูรณวิทย์ วฟก.1265 ที่อยู่ 21 ซอยทานสัมฤทธิ์ 13 ตำบลท่าทราย อ.เมืองนนทบุรี จ.นนทบุรี 11000	

Mechanical Engineer :	SIGNATURE
วิศวกรผู้ออกแบบระบบเครื่องกลและปรับอากาศ	
นายประสิทธิ์ โกียวสุนทร วก.1221 ที่อยู่ 44/372 ซอยบางกระดี่ 35/1 แขวงแสมดำ เขตบางขุนเทียน กทม. 10150	ประสิทธิ์

Sanitary Engineer :	SIGNATURE
วิศวกรผู้ออกแบบระบบสุขาภิบาล และดับเพลิง	
นายทศวรรษ สันนฤทธิ์ วส. 215 ที่อยู่ บ้านเลขที่ 99/107 หมู่ที่ 3 ต.ศีรษะจรเข้น้อย อ.บางเสาธง จ.สมุทรปราการ 10540	ทศวรรษ

ISSUE/REVISION

REV.	DESCRIPTION	DATE
A	90% DEVELOPED	09/05/2026

PROJECT NAME :

GEDC 01

LOCATION:
Nikhom Phattana district, Rayong ,industrial estate,CPGC

BUILDING :

SITE PLAN

90% DEVELOPED

TITLE :

FENCING LAYOUT

JOB NO.	SCALE 1:500
DRAWN HJC	REF.
CHECKED LJC	DWG.NO. MPK00-90-A-FL-001
APPROVED LXD	
DATE 2026.05.09	