KEY PLAN

SCALE: NTS

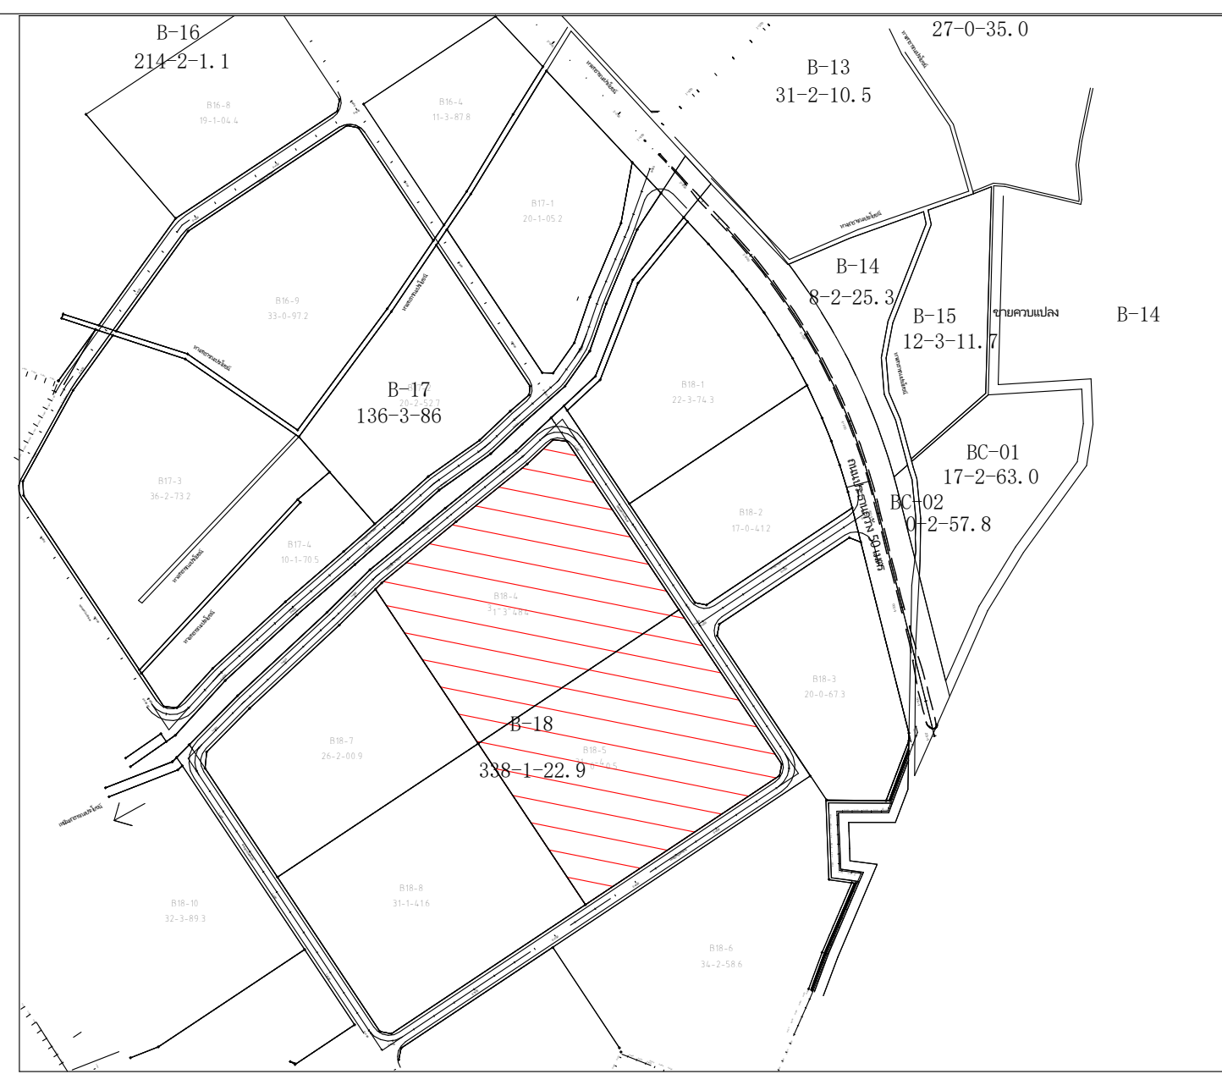

LOCATION PLAN

SCALE: NTS

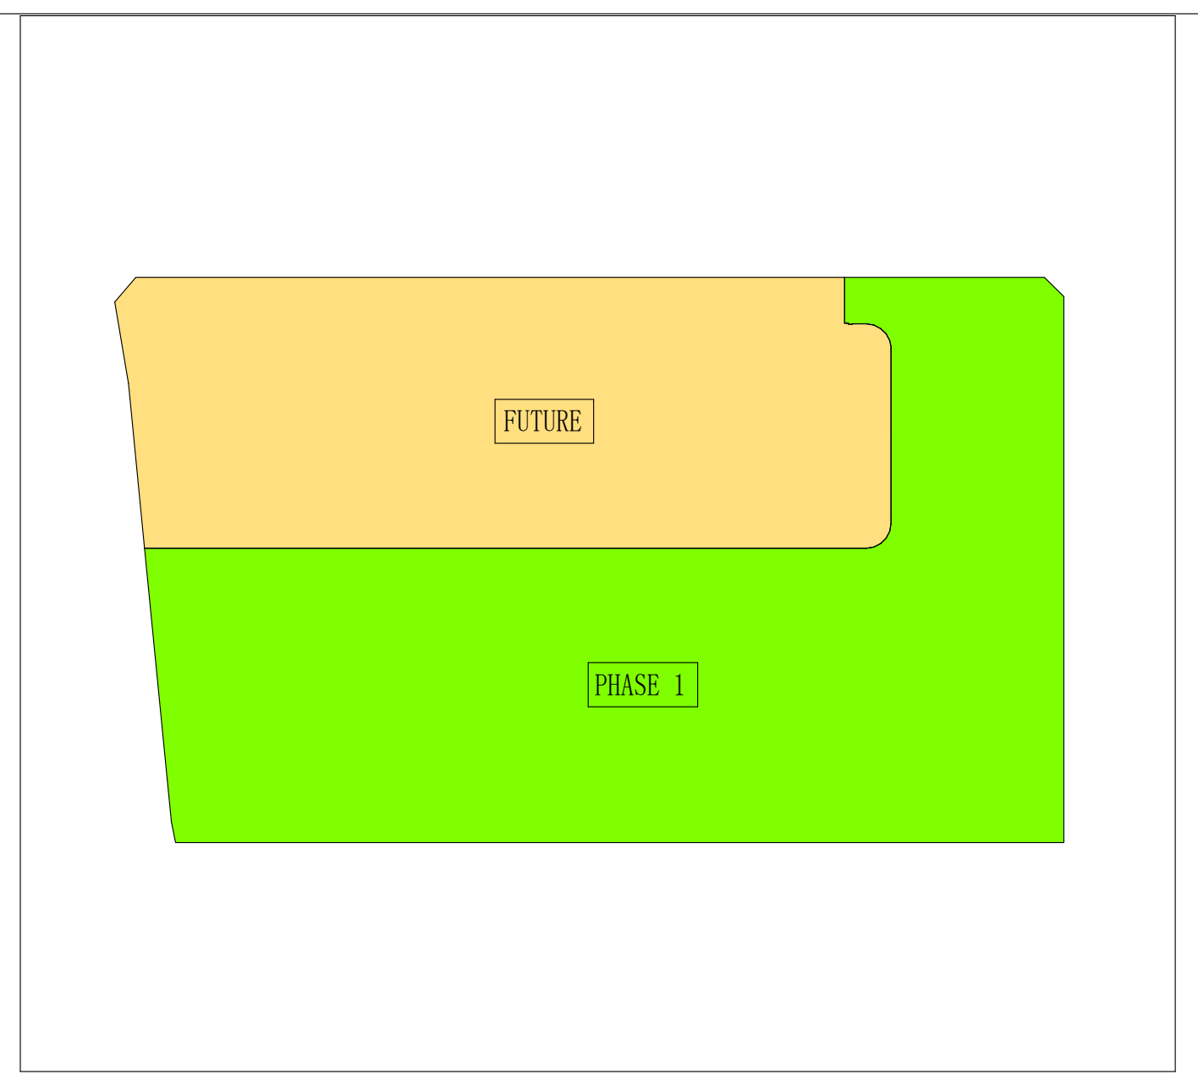

PHASING

SCALE: NTS

GENERAL LAYOUT INDICATORS

GENERAL LAYOUT INDICATORS			
PLOT AREA		100818.60 ㎡	BY LAW
OVERALL GROSS FLOOR AREA (GFA PHAS 01)		83499.29 ㎡	
SUB-ITEM	BUILDING A 42MW	41666.80 ㎡	
	BUILDING A-1 WATER TANK	756.00 ㎡	
	BUILDING B 42MW	41666.80 ㎡	
	BUILDING B-1 WATER TANK	756.00 ㎡	
	GUARD HOUSE	100.24 ㎡	
	FIRE PUMP HOUSE	65.45 ㎡	
	SUBSTATION	2991.12 ㎡	
	BIN CENTER	69.12 ㎡	
BUILDING COVERAGE AREA		46102.92 ㎡	＜70%
OPEN SPACE AREA		49504.18 ㎡	＞30%
PROPOSED PLOT RATIO(GFA/PLOT AREA)		1.51	
GREEN COVERAGE RATIO		10.33%	
TREE		63	1 tree / ral
TOTAL PARKING CAPACITY		468 lot	
CAR PARKING		388 lot	348 lot
HANDICAP PARKING		12 lot	12 lot
MOTORCYCLE PARKING		48 lot	48 lot
BICYCLE PARKING		16 lot	16 lot
AMBULANCE PARKING		2 lot	2 lot
FIRE TRUCK PARKING		2 lot	2 lot

LEGEND

🟥	SITE BOUNDARY
—	6M BUILDING SETBACK FROM SITE BOUNDARY LINE(AHJ requirement)
—	12M BUILDING SETBACK FROM SITE BOUNDARY LINE(AHJ requirement)
═	TYPE1: Security K4 Anti-Climb Fence
═	TYPE2: 2400MM Normal Security Anti-Climb Fence (Without Retaining Wall)
🟥	PHASING LINE
❋	A PERENNIAL PALM PLANT, UP TO 15 METERS TAL.THE TRUNK IS ERECT, NARROWED NEAR THE BASE.THE CENTER OF THE TRUNK IS A DARK GREEN VENT,ABOUT 1 METER LONG. THE TRUNK IS GREY, WITH CLEARLY VISIBLE NODES.THE TRUNK DIAMETER IS ABOUT 50 CENTIMETERS.
▥	PEDESTRIAN CROSSING
▨	LANDSCAPE

BICYCLE PARKING ONLY: 16 SPACES WITH SHELTER; NO CAR SHADE FOR ALL PARKING LOTS

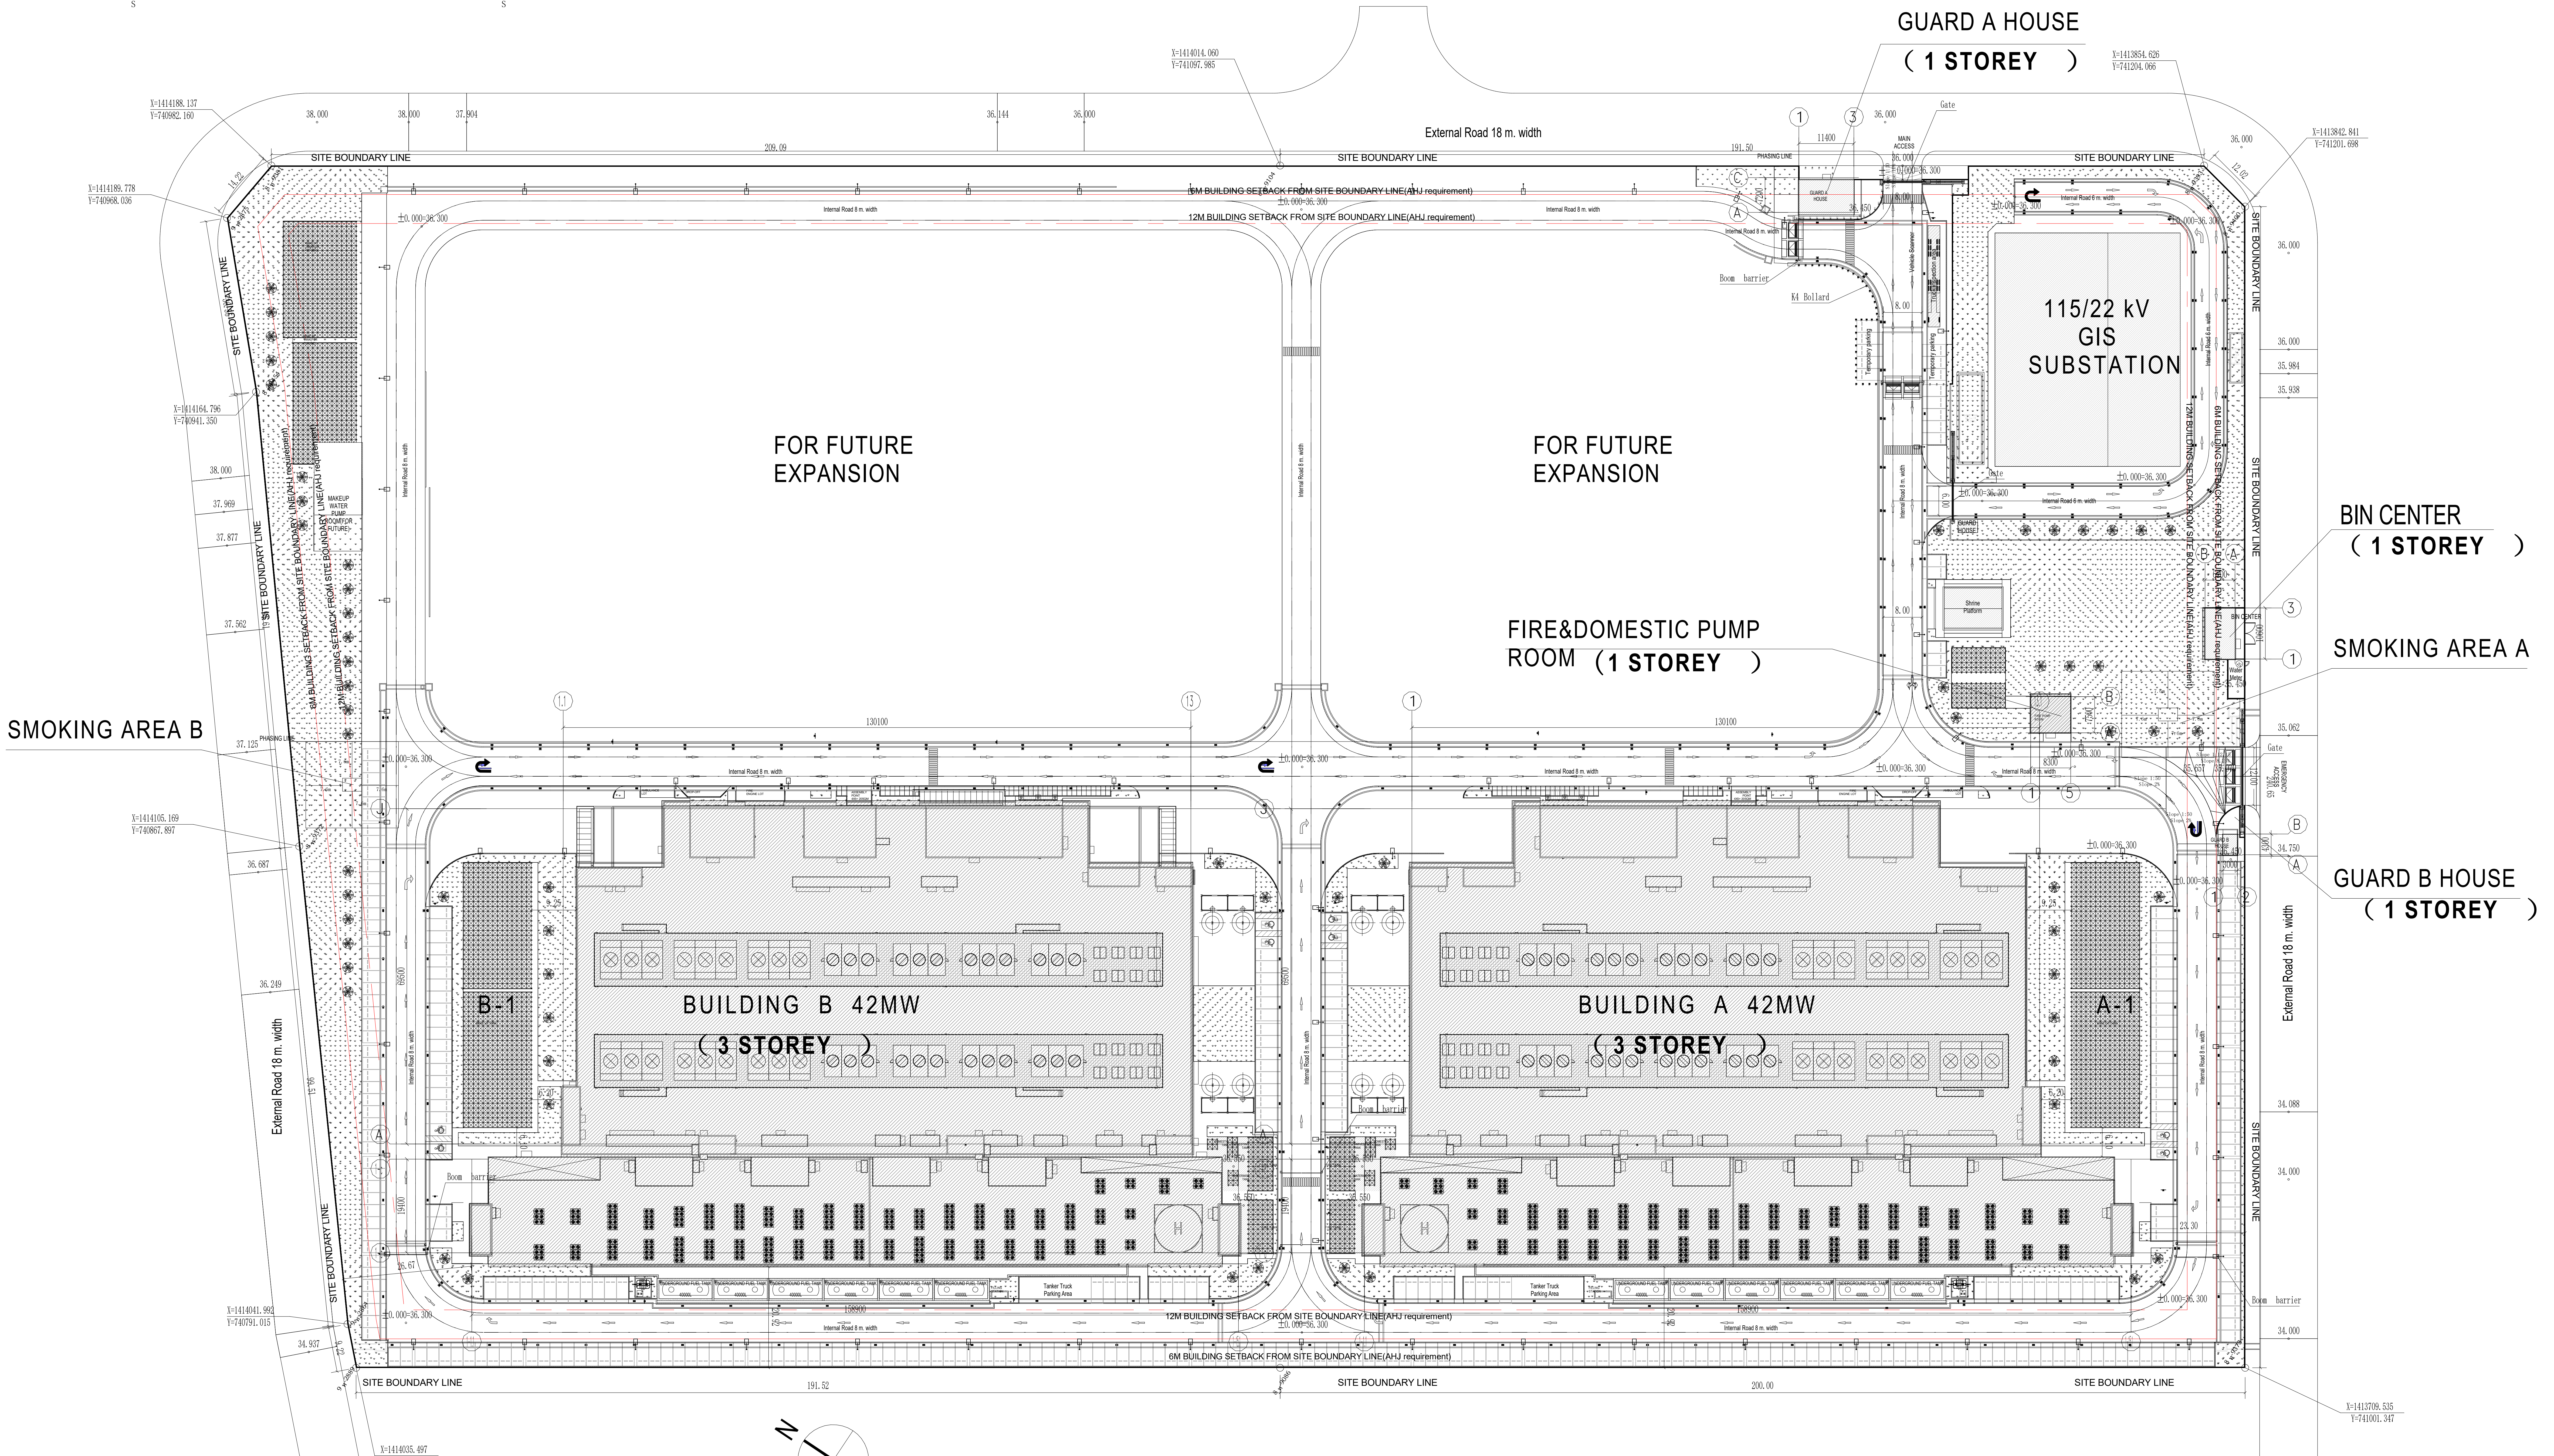

SITE PLAN

5 0 10 20m

SCALE 1:500

NOTE :THIS PRINT IS OF A CONFIDENTIAL NATURE, IT SHALL NOT BE TRACED,PHOTOGRAPHED,PHOTOSTATED OR REPRODUCED IN ANY MANER,NOR USED FOR ANY PURPOSE WHATSOEVER EXCEPT BY WRITTEN PERMISSION

CLIENT :

GULF EDGE DC 01

87 Wireless Road, M Thai Tower 11th. Floor, All Seasons Place, Lumpini,
Pathumwan, Bangkok 10330, Thailand

CONTRACTOR :

华西发展(泰国)有限公司
บริษัท หัวซือ ดีเวลลอปเม้นต์ (ประเทศไทย) จำกัด
HUASHI DEVELOPMENT CO.,LTD
No. 202, Room No. 1403, 14/F, Le Concorde Building,
Ratchadapisek Road, Huaykhwang Sub-District,
Huaykhwang District, Bangkok Metropolitan 10310.

CONSULTANT :

ARbay
บริษัท เอ อาร์ เบย์ จำกัด
ARbay Company Limited
31 st Floor Bangkok Insurance Building
25 South Sathorn road Thungmahamek
Sathorn Bangkok 10120 THAILAND
T +66 (0) 2286 8199
F +66 (0) 2286 2863
info@arbay.co.th

CONSULTANT :

Qbic Engineers & Architects Co.,Ltd.
8 Soi KALONG 4 SANAMBINNAM ROAD,
THASAI SUB-DISTRICT, MUANG NONTHABURI DISTRICT
, NONTHABURI.
Tel 662-950-4374
Fax 662-580-3231
E-Mail : qbic@qbic.co.th, www.qbic.co.th
QBIC ENGINEERS AND ARCHITECTS CO.,LTD.

CONSULTANT :

MITR
MITR TECHNICAL CONSULTANT CO.,LTD.
1168/8 12th FLOOR, LUMPINI TOWER BUILDING,
RAMA IV RD., THUNGMAHAMEK, SATHORN, BANGKOK 10120, THAILAND
TEL : 0-2679-9079-84
FAX : 0-2679-9085 E-mail: mitr_dd@mitr.com

Architect :	SIGNATURE
ประกิต พนานุรัตน์ วสถ. 580 ที่อยู่ 251/1 ถ.จารุเมือง แขวงรองเมือง เขตปทุมวัน กรุงเทพมหานคร โทรศัพท์ 02-286-8199	
Structural Engineer :	SIGNATURE
วิศวกรผู้ออกแบบโครงสร้าง	
ณัฐสม สงวนวงษ์ วย 1423 ที่อยู่ 2/1 ซ.รามคำแหง 150 ถ.รามคำแหง แขวง สะพานสูง เขต สะพานสูง กทม. 10240	ณัฐสม สงวนวงษ์
Structural Inspector :	SIGNATURE
วิศวกรผู้ตรวจสอบโครงสร้าง	
โกมล จุฑาภัทร วย 964 ที่อยู่ 24/18 ซ.นวมินทร์ 129 ถ. นวมินทร์ แขวง นวลจันทร์ เขต บึงกุ่ม กทม. 10230	
Electrical Engineer :	SIGNATURE
วิศวกรผู้ออกแบบระบบไฟฟ้ากำลัง	
นายสุภัทร บูรณวิทย์ วฟก.1265 ที่อยู่ 21 ซอยทานสัมฤทธิ์ 13 ตำบลท่าทราย อ.เมืองนนทบุรี จ.นนทบุรี 11000	สุภัทร
Mechanical Engineer :	SIGNATURE
วิศวกรผู้ออกแบบระบบเครื่องกลและปรับอากาศ	
นายประสิทธิ์ เกี้ยวสุนทร วก.1221 ที่อยู่ 44/372 ซอยบางกระดี่ 35/1 แขวงแสมดำ เขตบางขุนเทียน กทม. 10150	ประสิทธิ์
Sanitary Engineer :	SIGNATURE
วิศวกรผู้ออกแบบระบบสุขาภิบาล และดับเพลิง	
นายทศวรรษ สนั่นฤทธิ์ วส. 215 ที่อยู่ บ้านเลขที่ 99/107 หมู่ที่ 3 ต.ศีรษะจรเข้น้อย อ.บางเสาธง จ.สมุทรปราการ 10540	ทศวรรษ

ISSUE/REVISION

REV.	DESCRIPTION	DATE
A	90% DEVELOPED	09/05/2026

PROJECT NAME :

GEDC 01

LOCATION:
Nikhom Phattana district, Rayong ,industrial estate,CPGC

BUILDING :

90% DEVELOPED

TITLE :

SITE PLAN

JOB NO.	SCALE 1 : 500
DRAWN HJC	REF.
CHECKED LJC	DWG. NO. MPK00-90-A-SP-001
APPROVED LXD	
DATE 2026.05.09	