| | |
|---|---|
| ▨ | Fire Lane |
| ▲ | Fire Engine Access Entrance/Exit |
| - - - | Fire-truck circulation route |
| ■ | Assembly point |
| - - - | Pedestrian evacuation route |

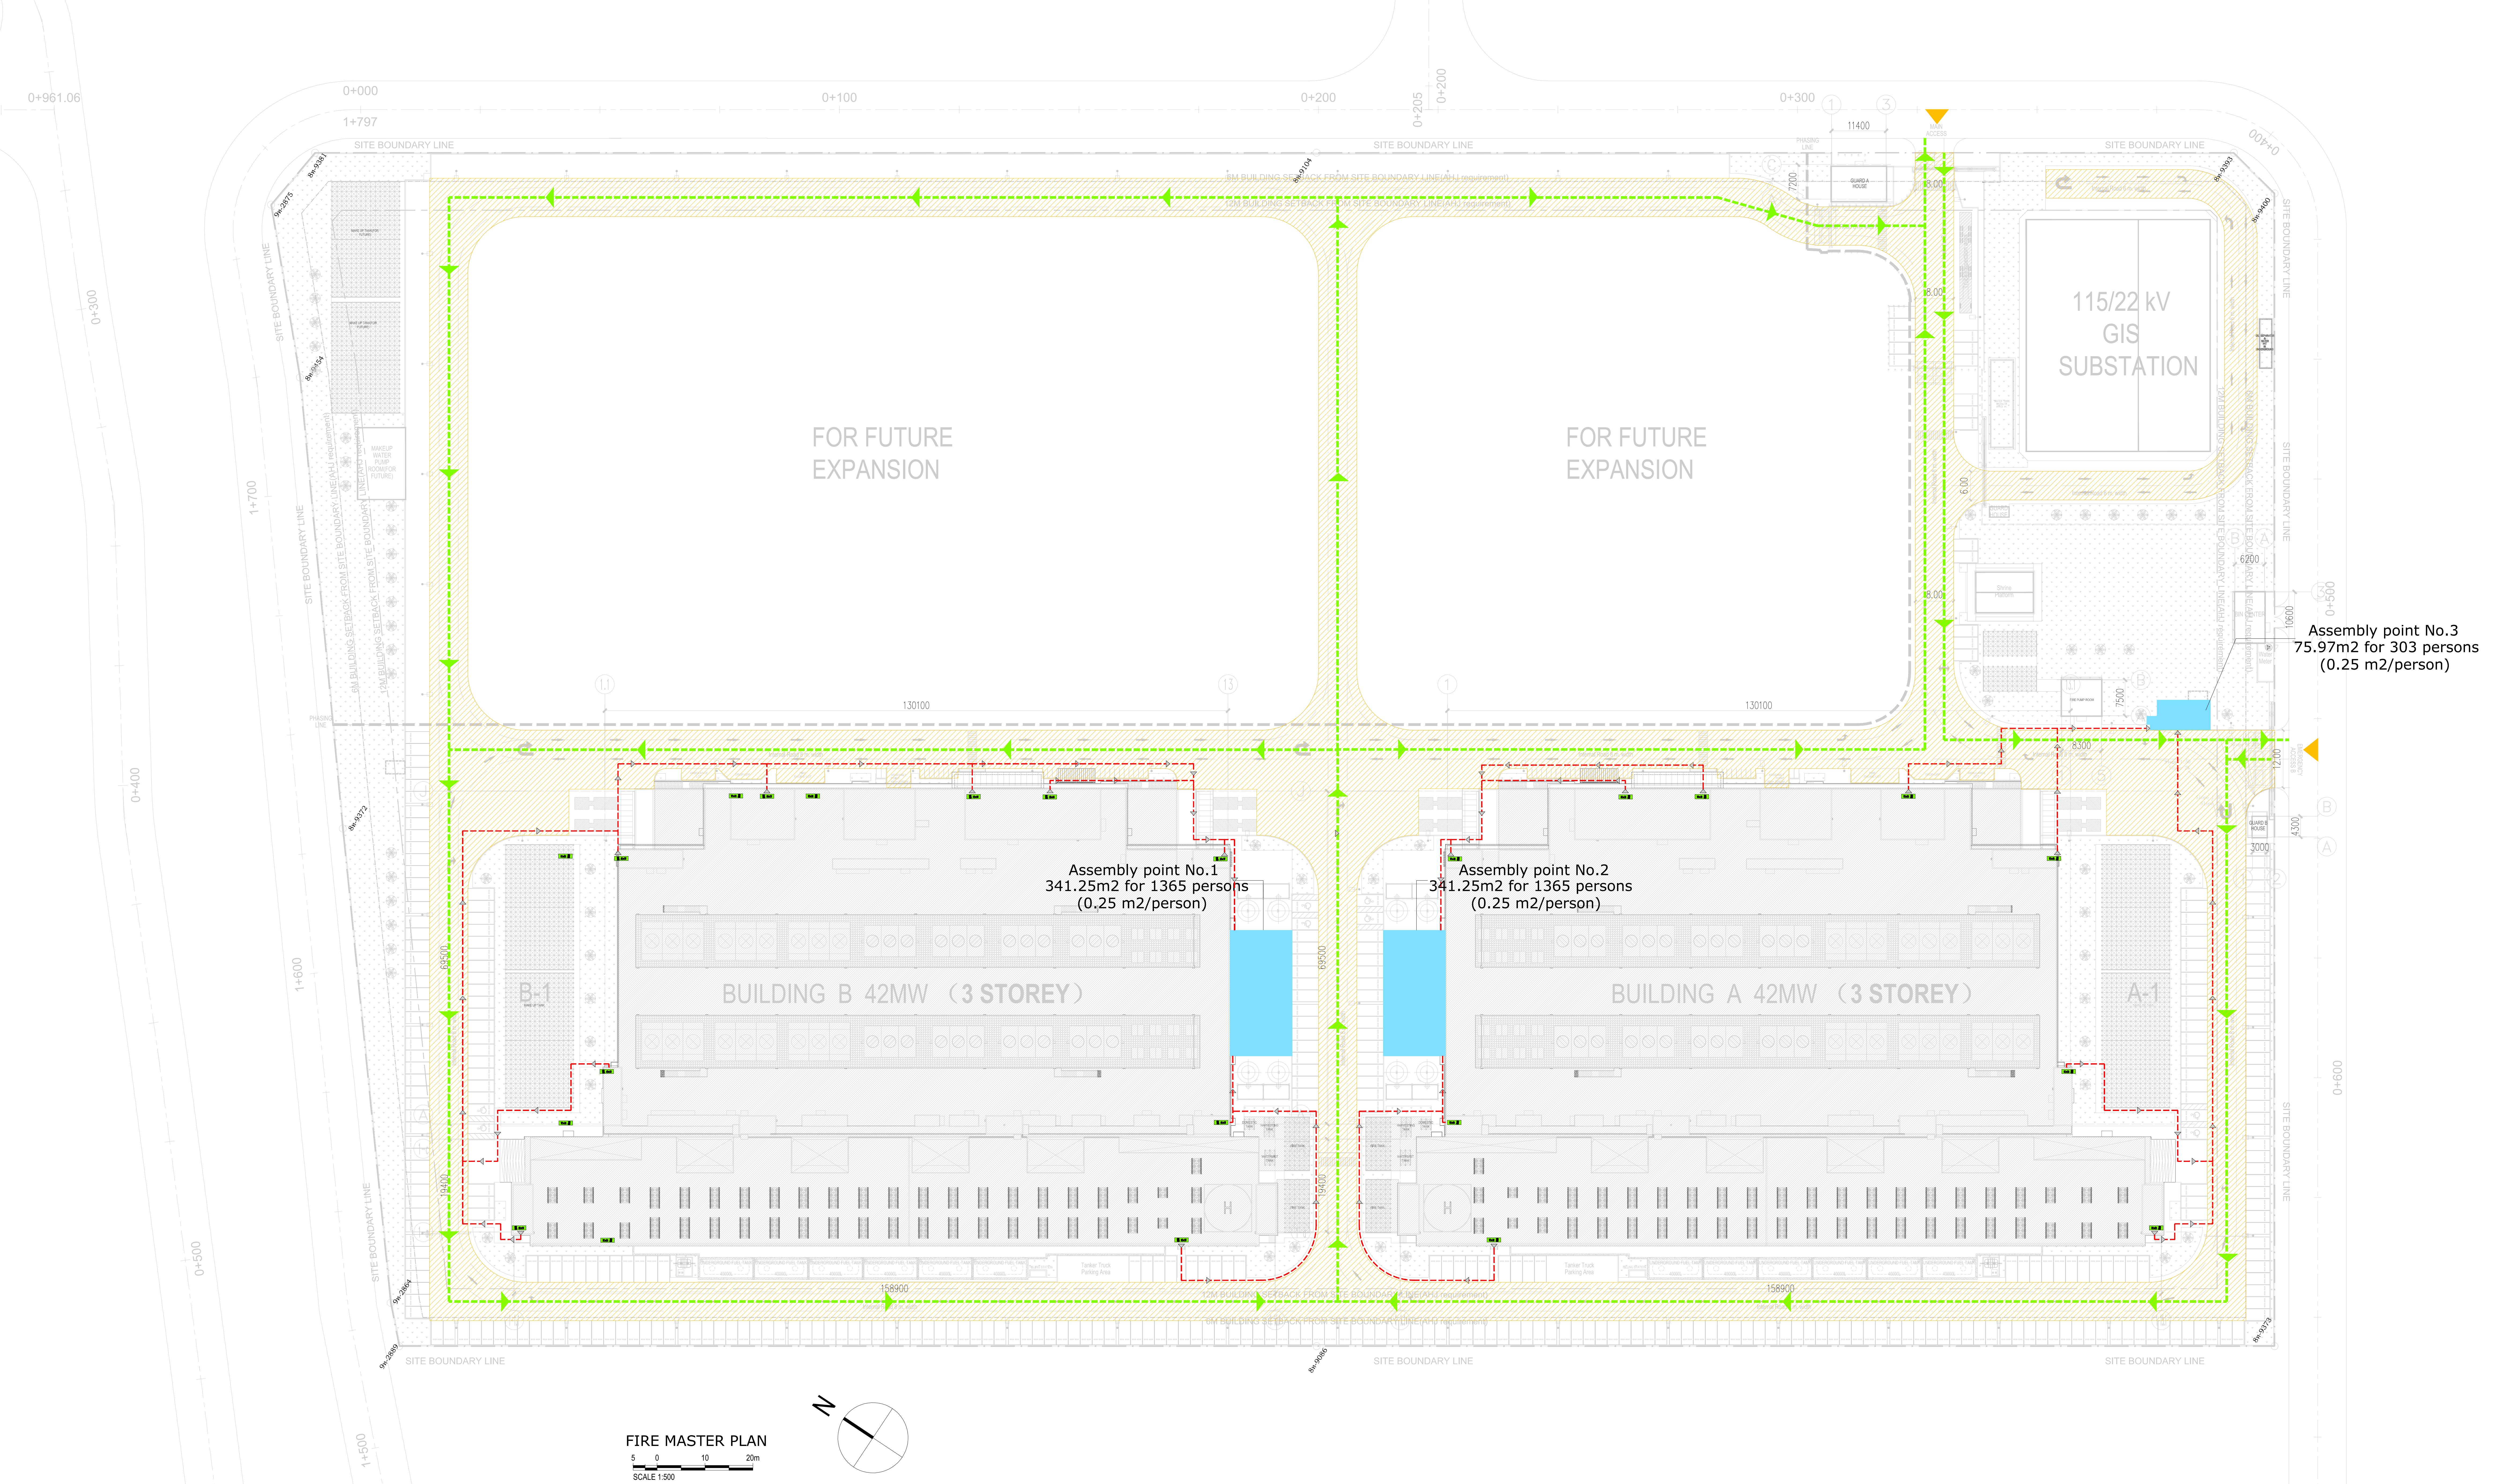

FIRE MASTER PLAN

5 0 10 20m

SCALE 1:500

NOTE : THIS PRINT IS OF A CONFIDENTIAL NATURE, IT SHALL NOT BE TRACED,PHOTOGRAPHED,PHOTOSTATED OR REPRODUCED IN ANY MANER,NOR USED FOR ANY PURPOSE WHATSOEVER EXCEPT BY WRITTEN PERMISSION

CLIENT :

GULF EDGE DC 01

87 Wireless Road, M Thai Tower 11th. Floor, All Seasons Place, Lumpini,
Pathumwan, Bangkok 10330, Thailand

CONTRACTOR :

华西发展(泰国)有限公司
บริษัท หัวซือ ดีเวลลอปเม้นต์ (ประเทศไทย) จำกัด
HUASHI DEVELOPMENT CO.,LTD
No. 202, Room No. 1403, 14/F, Le Concorde Building,
Ratchadapisek Road, Huaykhwang Sub-District,
Huaykhwang District, Bangkok Metropolitan 10310.

CONSULTANT :

ARbay
บริษัท เอ อาร์ เบย์ จำกัด
ARbay Company Limited
31 st Floor Bangkok Insurance Building
25 South Sathorn road Thungmahamek
Sathorn Bangkok 10120 THAILAND
T +66 (0) 2286 8199
F +66 (0) 2286 2863
info@arbay.co.th

CONSULTANT :

Qbic Engineers & Architects Co.,Ltd.
8 Soi KALONG 4 SANAMBINNAM ROAD,
THASAI SUB-DISTRICT, MUANG NONTHABURI DISTRICT
, NONTHABURI.
Tel 662-950-4374
Fax 662-580-3231
E-Mail : qbic@qbic.co.th, www.qbic.co.th
QBIC ENGINEERS AND ARCHITECTS CO.,LTD.

CONSULTANT :

MITR
MITR TECHNICAL CONSULTANT CO.,LTD.
1168/8 12th FLOOR, LUMPINI TOWER BUILDING,
RAMA IV RD., THUNGMAHAMEK, SATHORN, BANGKOK 10120, THAILAND
TEL : 0-2679-9079-84
FAX : 0-2679-9085 E-mail: mitr_dd@mitr.com

| Architect : | SIGNATURE |
|---|---|
| ประกิต พนานุรัตน์ วสถ. 580<br>ที่อยู่<br>251/1 ถ.จารุเมือง แขวงรองเมือง เขตปทุมวัน<br>กรุงเทพมหานคร โทรศัพท์ 02-286-8199 | |
| **Structural Engineer :** | **SIGNATURE** |
| วิศวกรผู้ออกแบบโครงสร้าง | |
| ณัฐสม สงวนวงษ์ วย 1423<br>ที่อยู่<br>2/1 ซ.รามคำแหง 150 ถ.รามคำแหง<br>แขวง สะพานสูง เขต สะพานสูง กทม. 10240 | ณัฐสม สงวนวงษ์ |
| **Structural Inspector :** | **SIGNATURE** |
| วิศวกรผู้ตรวจสอบโครงสร้าง | |
| โกมล จุฑาภัทร วย 964<br>ที่อยู่<br>24/18 ซ.นวมินทร์ 129 ถ. นวมินทร์<br>แขวง นวลจันทร์ เขต บึงกุ่ม กทม. 10230 | |
| **Electrical Engineer :** | **SIGNATURE** |
| วิศวกรผู้ออกแบบระบบไฟฟ้ากำลัง | |
| นายสุภัทร บูรณวิทย์ วฟก.1265<br>ที่อยู่<br>21 ซอยทานสัมฤทธิ์ 13<br>ตำบลท่าทราย อ.เมืองนนทบุรี จ.นนทบุรี 11000 | สุภัทร บูรณวิทย์ |
| **Mechanical Engineer :** | **SIGNATURE** |
| วิศวกรผู้ออกแบบระบบเครื่องกลและปรับอากาศ | |
| นายประสิทธิ์ เกียวสุนทร วก.1221<br>ที่อยู่<br>44/372 ซอยบางกระดี่ 35/1 แขวงแสมดำ<br>เขตบางขุนเทียน กทม. 10150 | ประสิทธิ์ |
| **Sanitary Engineer :** | **SIGNATURE** |
| วิศวกรผู้ออกแบบระบบสุขาภิบาล และดับเพลิง | |
| นายทศวรรษ สนั่นฤทธิ์ วส. 215<br>ที่อยู่<br>บ้านเลขที่ 99/107 หมู่ที่ 3 ต.ศีรษะจรเข้น้อย<br>อ.บางเสาธง จ.สมุทรปราการ 10540 | ทศวรรษ |

ISSUE/REVISION

| REV. | DESCRIPTION | DATE |
|---|---|---|
| A | 90% DEVELOPED | 09/05/2026 |
| | | |
| | | |
| | | |
| | | |
| | | |
| | | |
| | | |
| | | |

PROJECT NAME :

GEDC 01

LOCATION:
Nikhom Phattana district, Rayong ,industrial estate,CPGC

BUILDING :

SITE PLAN

90% DEVELOPED

TITLE :

FIRE MASTER PLAN

| | |
|---|---|
| JOB NO. | SCALE 1:500 |
| DRAWN HJC | REF. |
| CHECKED LJC | DWG.NO. MPK00-90-A-SP-003 |
| APPROVED LXD | |
| DATE 2026.05.09 | |