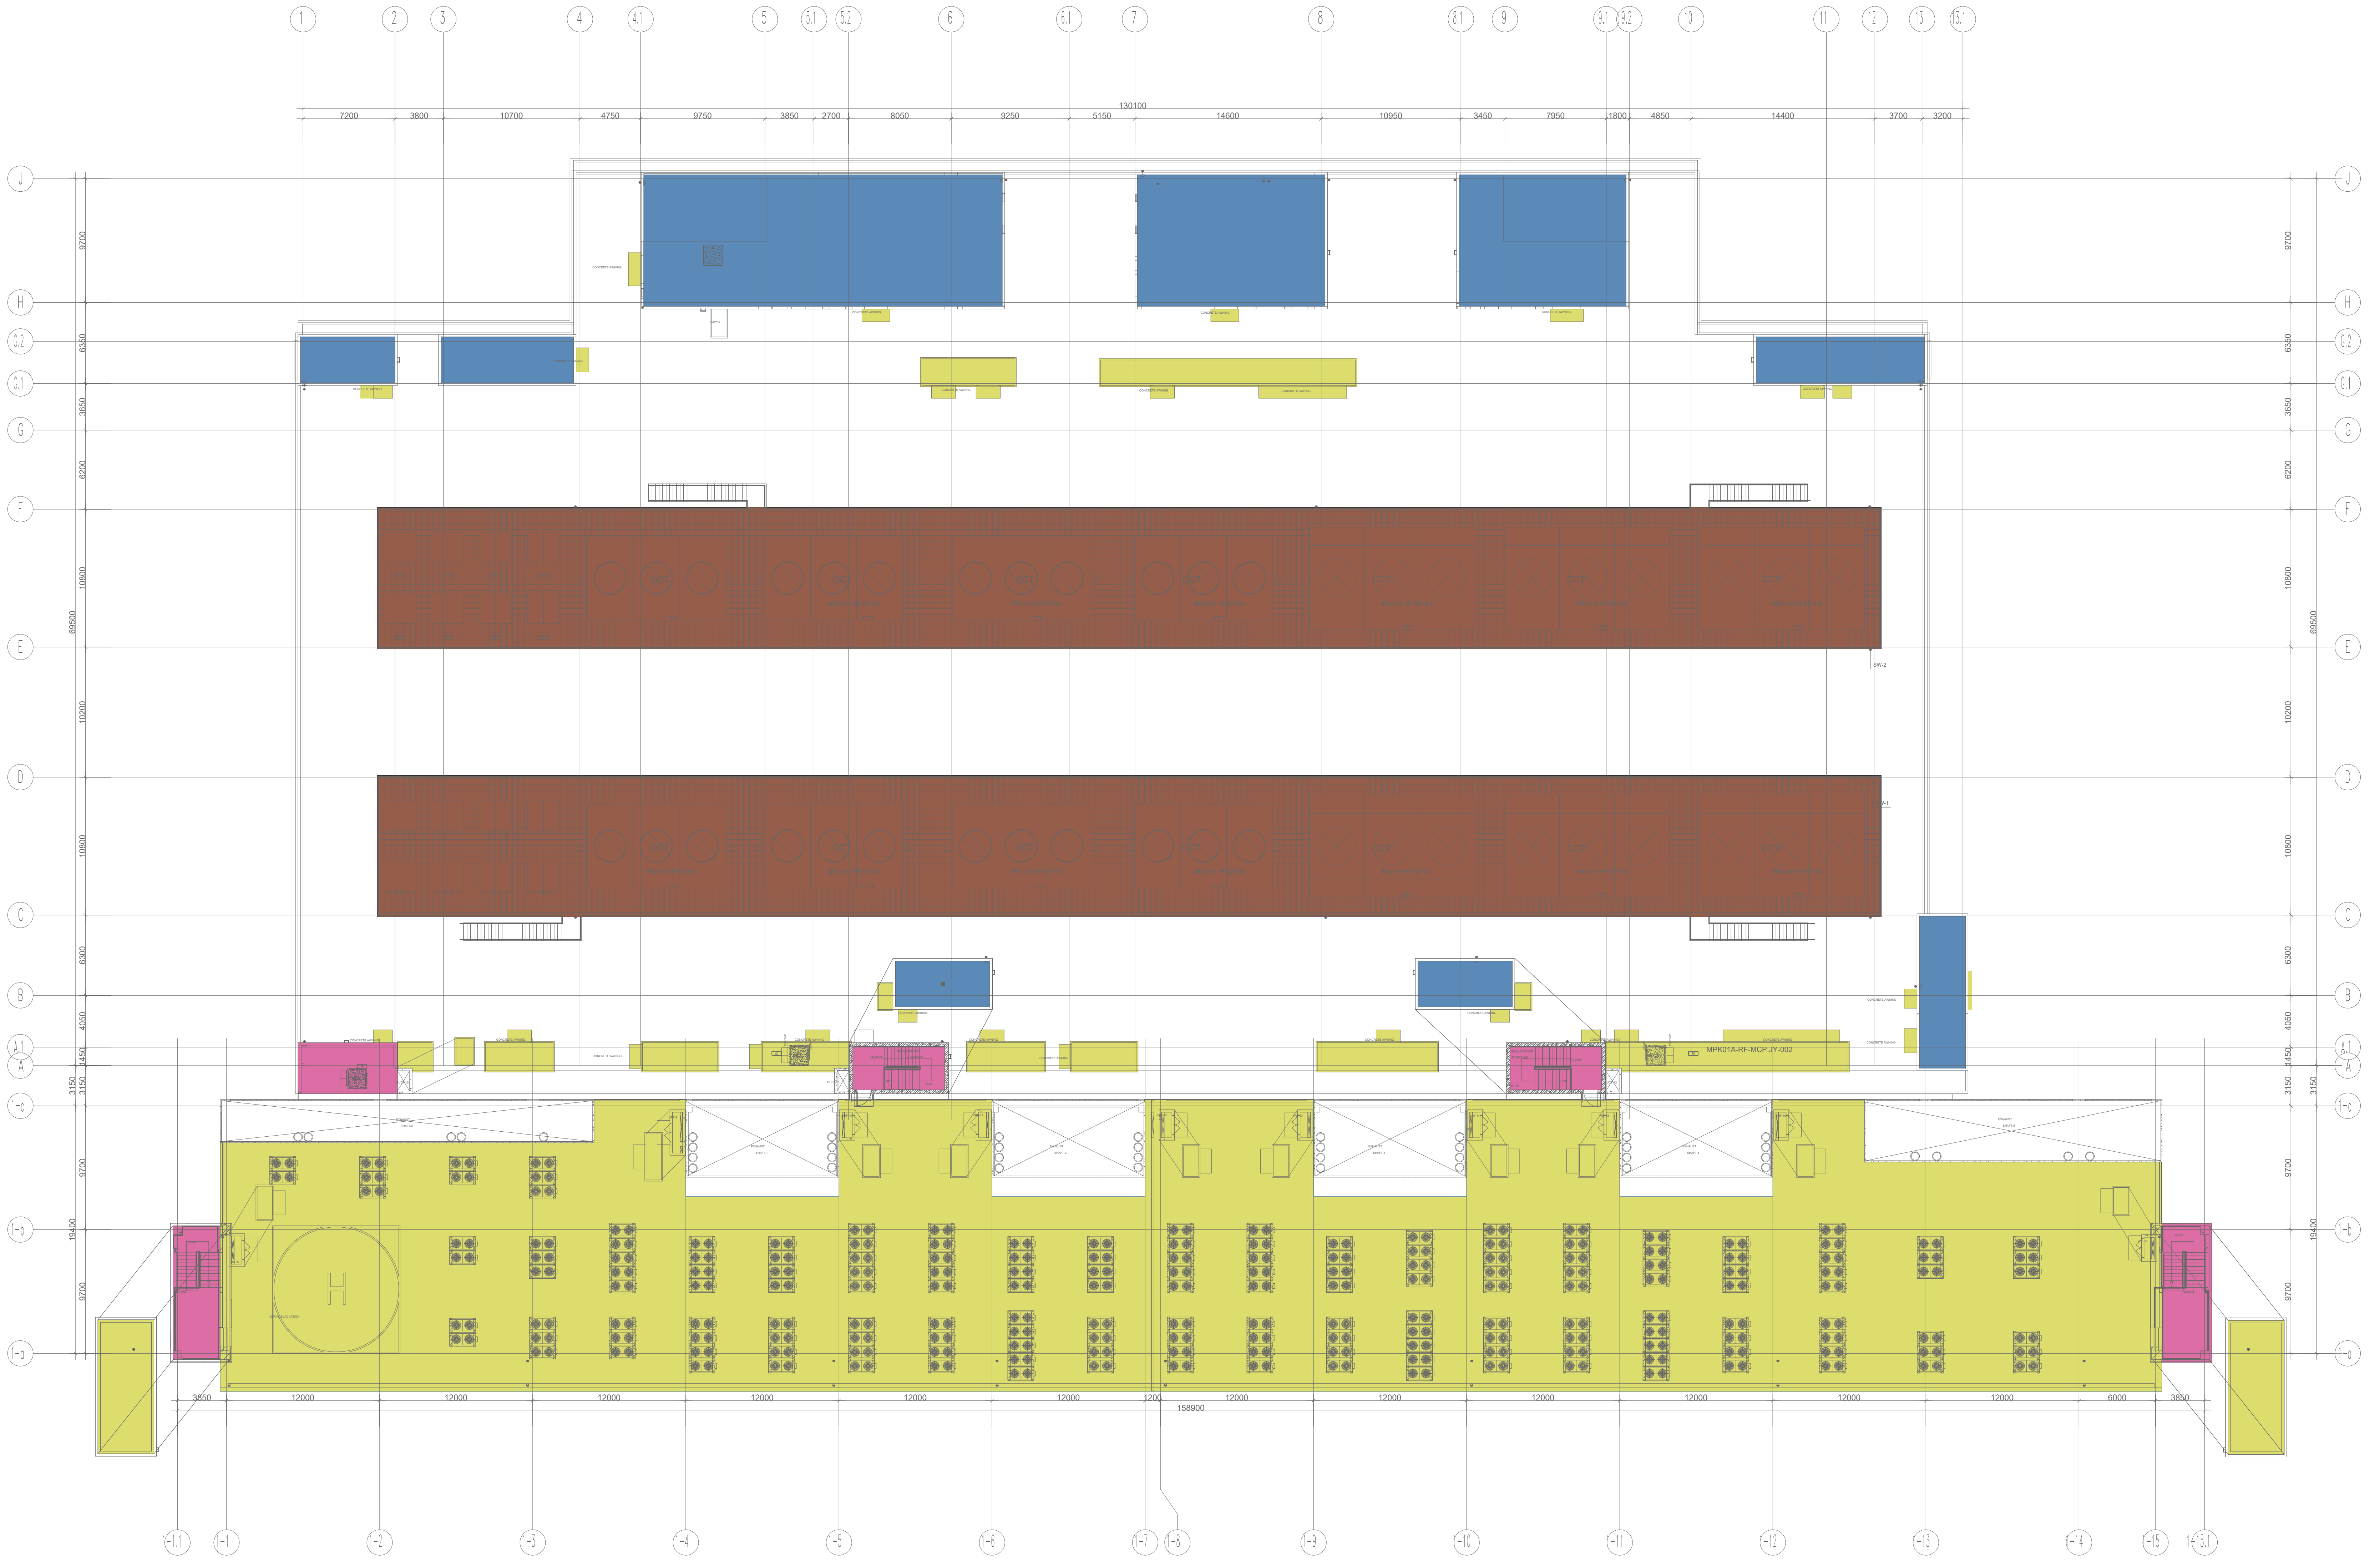

UPPER ROOF FLOOR PLAN(DC BUILDING A)

SCALE
1:250
FLOOR AREA:12238.10 sqm
OVERALL GROSS FLOOR AREA:40900.20 sqm

NOTE:
Before pouring the concrete for the structural floor slab on the ground level, a 0.2mm thick PE damp-proof membrane shall be laid in an additional layer to meet the moisture-proof requirements for the ground floor.

CODE NO.		DESCRIPTION	FLOOR FINISHES SPECIFICATION	VENDER
🟦	F-1	STRUCTURE SLAB	NO FLOOR FINISHING	LOCAL
🟨	F-2	CONCRETE WEAR-RESISTANT FLOOR FINISH	CURING AGENT_CARBORUNDUM	LOCAL
🟧	F-3	CONCRETE STEEL TROWEL FINISH	CONCRETE SCREED + CURING AGENT	LOCAL
🟧	F-4	CONCRETE SCREED + EPOXY FLOORING	CONCRETE STEEL TROWEL FINISH, TOP PAINT WITH LOW VOC,EPOXY COATING; LOW VOC CONTENT & EMISSION PRIMER FOR EPOXY COATING	LOCAL
🟥	F-5	CONCRETE STEEL TROWEL FINISH	CONCRETE SCREED + CURING AGENT+ 1.2mm THKCEMENTITIOUS WATERPROOF COATING	LOCAL
🟦	F-6	CONCRETE SCREED + EPOXY FLOORING	EPOXY+ 1.2mm THKCEMENTITIOUS WATERPROOF COATING	LOCAL
🟦	F-7	CERAMIC TILE	600X600 CERAMIC TILE ON CONCRETE STEEL TROWEL FINISH; LOW VOC CONTENT & EMISSION ADHESIVE	LOCAL
🟪	F-8	PORCELAIN TILE	600X600 12MM THK NON-SLIP HOMOGENOUS TILE (R10) ON 1.2mm THKCEMENTITIOUS WATERPROOF COATING,LOW VOC TILE ADHESIVE AND GROUT	LOCAL
🟪	F-9	CERAMIC TILE	300X300 12MM THK CERAMIC TILE,LOW VOC TILE ADHESIVE AND GROUT	LOCAL
🟩	F-10	OIL-RESISTANT FLOOR	CONCRETE SCREED + CURING AGENT + OILPROOFING	LOCAL
🟪	F-11	ANTI-STATIC EPOXY FLOORING	ANTI-STATIC + ESD FLOOR ON CONCRETE SCREED + EPOXY+ 1.2mm THKCEMENTITIOUS WATERPROOF COATING	LOCAL
🟩	F-12	ANTI-STATIC RAISED FLOOR	ANTI-STATIC + ESD CALCIUM SULFATE RAISED FLOOR SYSTEM WITH HPL FINISH ON CONCRETE SCREED + EPOXY(800MM HIGH) + WATER PROOFING	LOCAL
🟥	F-13	RAISED FLOOR	ESD CALCIUM SULFATE RAISED FLOOR SYSTEM WITH HPL FINISH ON CONCRETE SCREED + EPOXY(800MM HIGH) + 1.2mm THKCEMENTITIOUS WATERPROOF COATING	LOCAL
🟫	F-14	METAL MESH CATWALK	METAL MESH CATWALK ON STRUCTURE FRAME	LOCAL
🟦	F-15	WATERPROOFING ROOF	SELF-ADHESIVE POLYMER-MODIFIED BITUMEN WATERPROOFING MEMBRANE(3+3mmTHK.)+NON-CURING RUBBER ASPHALT WATERPROOF COATING(2mmTHK.)+XPS INSULATION BOARD(75mmTHK R-12(12 BTU/(h·°F·ft2)(2.12(K·m2)/W))Or Better)（XPS insulation board density ≥ 30 kg/m³, compressive strength ≥ 250 kPa）+REINFORCED CONCRETE COVER(50mm THK For Roof Slab Top Coat With TOA Heatshield Paint SRI≥82）	LOCAL
🟨	F-16	CONCRETE ROOF+WATERPROOFING	CONCRETE ROOF + CURING AGENT+ 1.2mm THKCEMENTITIOUS WATERPROOF COATING	LOCAL

NOTE : THIS PRINT IS OF A CONFIDENTIAL NATURE, IT SHALL NOT BE TRACED,PHOTOGRAPHED,PHOTOSTATED OR REPRODUCED IN ANY MANER,NOR USED FOR ANY PURPOSE WHATSOEVER EXCEPT BY WRITTEN PERMISSION

CLIENT :
GULF EDGE DC 01
87 Wireless Road, M Thai Tower 11th. Floor, All Seasons Place, Lumpini, Pathumwan, Bangkok 10330, Thailand

CONTRACTOR :
华西发展(泰国)有限公司
บริษัท หัวซือ ดีเวลลอปเม้นต์ (ประเทศไทย) จำกัด
HUASHI DEVELOPMENT CO.,LTD
No. 202, Room No. 1403, 14/F, Le Concorde Building,
Ratchadapisek Road, Huaykhwang Sub-District,
Huaykhwang District, Bangkok Metropolitan 10310.

CONSULTANT :
ARbay
บริษัท เอ อาร์ เบย์ จำกัด
ARbay Company Limited
31 st Floor Bangkok Insurance Building
25 South Sathorn road Thungmahamek
Sathorn Bangkok 10120 THAILAND
T +66 (0) 2286 8199
F +66 (0) 2286 2863
info@arbay.co.th

CONSULTANT :
Qbic Engineers & Architects Co.,Ltd.
8 Soi KALONG 4 SANAMBINNAM ROAD,
THASAI SUB-DISTRICT, MUANG NONTHABURI DISTRICT
, NONTHABURI.
Tel 662-950-4374
Fax 662-580-3231
E-Mail : qbic@qbic.co.th, www.qbic.co.th
QBIC ENGINEERS AND ARCHITECTS CO.,LTD.

CONSULTANT :
MITR
MITR TECHNICAL CONSULTANT CO.,LTD.
1168/8 12th FLOOR, LUMPINI TOWER BUILDING,
RAMA IV RD., THUNGMAHAMEK, SATHORN, BANGKOK 10120, THAILAND
TEL : 0-2679-9079-84
FAX : 0-2679-9085 E-mail: mitr_dd@mitr.com

Architect :	SIGNATURE
ประกิต พนานุรัตน์ วสถ. 580 ที่อยู่ 251/1 ถ.จารุเมือง แขวงรองเมือง เขตปทุมวัน กรุงเทพมหานคร โทรศัพท์ 02-286-8199	
Structural Engineer :	SIGNATURE
วิศวกรผู้ออกแบบโครงสร้าง	
ณัฐสม สงวนวงษ์ วย 1423 ที่อยู่ 2/1 ซ.รามคำแหง 150 ถ.รามคำแหง แขวง สะพานสูง เขต สะพานสูง กทม. 10240	ณัฐสม สงวนวงษ์
Structural Inspector :	SIGNATURE
วิศวกรผู้ตรวจสอบโครงสร้าง	
โกมล จุฑาภัทร วย 964 ที่อยู่ 24/18 ซ.นวมินทร์ 129 ถ. นวมินทร์ แขวง นวลจันทร์ เขต บึงกุ่ม กทม. 10230	
Electrical Engineer :	SIGNATURE
วิศวกรผู้ออกแบบระบบไฟฟ้ากำลัง	
นายสุภัทร บูรณวิทย์ วฟก.1265 ที่อยู่ 21 ซอยทานสัมฤทธิ์ 13 ตำบลท่าทราย อ.เมืองนนทบุรี จ.นนทบุรี 11000	
Mechanical Engineer :	SIGNATURE
วิศวกรผู้ออกแบบระบบเครื่องกลและปรับอากาศ	
นายประสิทธิ์ เกียวสุนทร วก.1221 ที่อยู่ 44/372 ซอยบางกระดี่ 35/1 แขวงแสมดำ เขตบางขุนเทียน กทม. 10150	ประสิทธิ์
Sanitary Engineer :	SIGNATURE
วิศวกรผู้ออกแบบระบบสุขาภิบาล และดับเพลิง	
นายทศวรรษ สันนฤทธิ์ วส. 215 ที่อยู่ บ้านเลขที่ 99/107 หมู่ที่ 3 ต.ศีรษะจรเข้น้อย อ.บางเสาธง จ.สมุทรปราการ 10540	ทศวรรษ

ISSUE/REVISION

REV.	DESCRIPTION	DATE
A	90% DEVELOPED	09/05/2026

PROJECT NAME :
GEDC 01
LOCATION:
Nikhom Phattana district, Rayong ,industrial estate,CPGC

BUILDING :
MAIN BUILDING

90% DEVELOPED

TITLE :
FLOOR FINISHES LAYOUT - URF

JOB NO.	SCALE 1:250
DRAWN WHY	REF.
CHECKED LJC	DWG.NO. MPK01A-60-A-FF-501
APPROVED LXD	
DATE 2026.05.09	