LEGEND		
	DESCRIPTION	SPECIFICATION
╌╌	CAST-IN-PLACE CONCRETE PANEL WALL	2 HOUR FIRE RATED CAST-IN-PLACE CONCRETE PANEL WALL(DETAILED STRUCTURAL CONSTRUCTION DRAWINGS)
╌╌	PRE-CAST CONCRETE PANEL WALL	2 HOUR FIRE RATED 100MM PRE-CAST CONCRETE PANEL WALL(INCLUDES 30MM RESERVED INSTALLATION DISTANCE)(U-value < 0.5 W/(m²·K)(ATTACHED EXTERIOR WALL)
╌╌	PRE-CAST CONCRETE PANEL WALL	2 HOUR FIRE RATED 100MM PRE-CAST CONCRETE PANEL WALL(INCLUDES 30MM RESERVED INSTALLATION DISTANCE)(U-value < 0.5 W/(m²·K)(INTERFLOOR WALL)
╌╌	LIGHT STEEL CALCIUM SILICATE BOARD	2 HOUR FIRE RATED 100MM LIGHT GAUGE STEEL FRAMING WITH FIBER CEMENT CALCIUM SILICATE COMPOSITE BOARD PARTITION
╌╌	PRECAST ACC CONCRETE WALL PANELS	2 HOUR FIRE RATED 100MM PRECAST ACC CONCRETE WALL PANELS(U-value < 0.5 W/(m²·K)
╌╌	PRECAST ACC CONCRETE WALL PANELS	2 HOUR FIRE RATED 200MM PRECAST ACC CONCRETE WALL PANELS
╌╌	CONCRETE BLOCK WALL	2 HOUR FIRE RATED 200MM CONCRETE BLOCK WALL
╌╌	LIGHT STEEL CALCIUM SILICATE BOARD	（NO FIRESTOP REQUIRED）2 HOUR FIRE RATED 100 MM LIGHT GAUGE STEEL FRAMING WITH FIBER CEMENT CALCIUM SILICATE COMPOSITE BOARD PARTITION

▨ FIRE COMPARTMENT

"Note:

All adhesives, sealants, paints, primers, and coatings shall be low-VOC content and low-VOC emissionsmaterials.

All ceiling boards shall be low-VOC emissions materials.

Used at least 20 EPD products from 5 manufacturers.

All materials shall comply with LEED TOR."

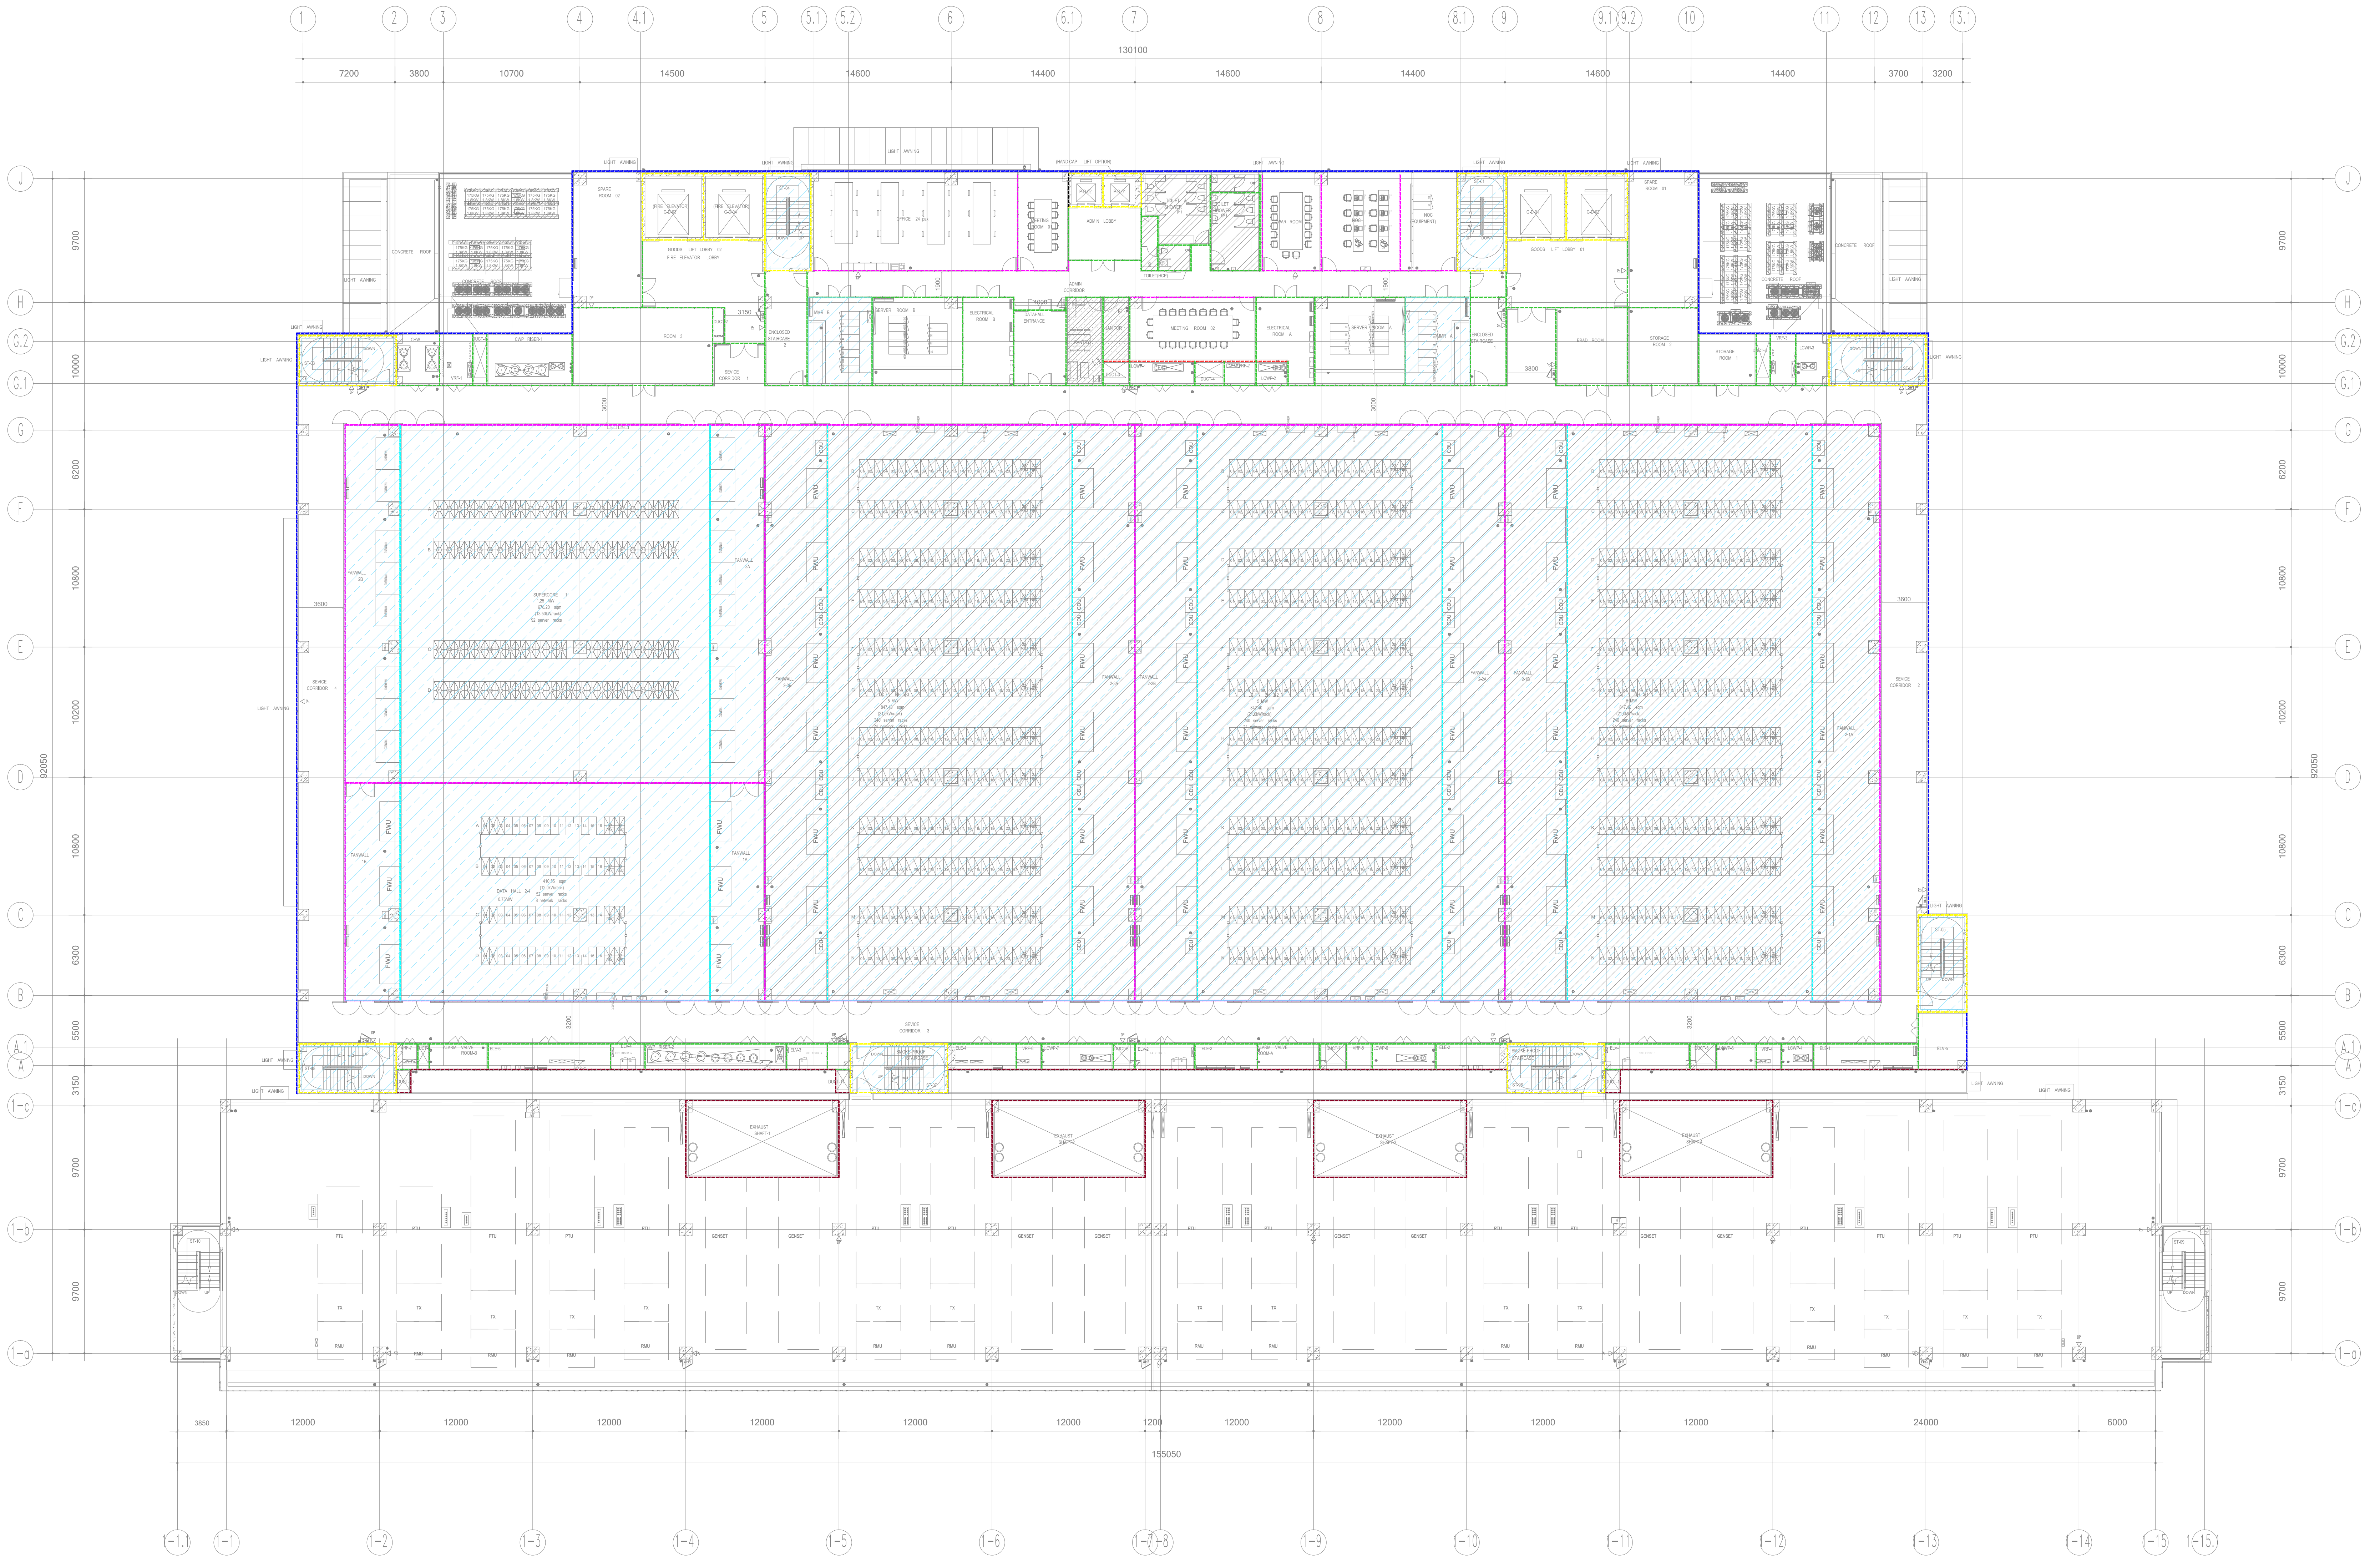

2ND FLOOR PLAN(DC BUILDING A)

SCALE 1:250

FLOOR AREA:12238.10 sqm
OVERALL GROSS FLOOR AREA:40900.20 sqm

NOTE : THIS PRINT IS OF A CONFIDENTIAL NATURE, IT SHALL NOT BE TRACED,PHOTOGRAPHED,PHOTOSTATED OR REPRODUCED IN ANY MANER,NOR USED FOR ANY PURPOSE WHATSOEVER EXCEPT BY WRITTEN PERMISSION

CLIENT :

GULF EDGE DC 01

87 Wireless Road, M Thai Tower 11th. Floor, All Seasons Place, Lumpini,
Pathumwan, Bangkok 10330, Thailand

CONTRACTOR :

华西发展(泰国)有限公司
บริษัท หัวซือ ดีเวลลอปเม้นต์ (ประเทศไทย) จำกัด
HUASHI DEVELOPMENT CO.,LTD
No. 202, Room No. 1403, 14/F, Le Concorde Building,
Ratchadapisek Road, Huaykhwang Sub-District,
Huaykhwang District, Bangkok Metropolitan 10310.

CONSULTANT :

ARbay
บริษัท เอ อาร์ เบย์ จำกัด
ARbay Company Limited
31 st Floor Bangkok Insurance Building
25 South Sathorn road Thungmahamek
Sathorn Bangkok 10120 THAILAND
T +66 (0) 2286 8199
F +66 (0) 2286 2863
info@arbay.co.th

CONSULTANT :

Qbic Engineers & Architects Co.,Ltd.
8 Soi KALONG 4 SANAMBINNAM ROAD,
THASAI SUB-DISTRICT, MUANG NONTHABURI DISTRICT
, NONTHABURI.
Tel 662-950-4374
Fax 662-580-3231
E-Mail : qbic@qbic.co.th, www.qbic.co.th
QBIC ENGINEERS AND ARCHITECTS CO.,LTD.

CONSULTANT :

MITR
MITR TECHNICAL CONSULTANT CO.,LTD.
1168/8 12th FLOOR, LUMPINI TOWER BUILDING,
RAMA IV RD., THUNGMAHAMEK, SATHORN, BANGKOK 10120, THAILAND
TEL : 0-2679-9079-84
FAX : 0-2679-9085 E-mail: mitr_dd@mitr.com

Architect :	SIGNATURE
ประกิต พนานุรัตน์ วสถ. 580 ที่อยู่ 251/1 ถ.จารุเมือง แขวงรองเมือง เขตปทุมวัน กรุงเทพมหานคร โทรศัพท์ 02-286-8199	
Structural Engineer :	SIGNATURE
วิศวกรผู้ออกแบบโครงสร้าง	
ณัฐสม สงวนวงษ์ วย 1423 ที่อยู่ 2/1 ซ.รามคำแหง 150 ถ.รามคำแหง แขวง สะพานสูง เขต สะพานสูง กทม. 10240	ณัฐสม สงวนวงษ์
Structural Inspector :	SIGNATURE
วิศวกรผู้ตรวจสอบโครงสร้าง	
โกมล จุฑาภัทร วย 964 ที่อยู่ 24/18 ซ.นวมินทร์ 129 ถ. นวมินทร์ แขวง นวลจันทร์ เขต บึงกุ่ม กทม. 10230	
Electrical Engineer :	SIGNATURE
วิศวกรผู้ออกแบบระบบไฟฟ้ากำลัง	
นายสุภัทร บูรณวิทย์ วฟก.1265 ที่อยู่ 21 ซอยทานสัมฤทธิ์ 13 ตำบลท่าทราย อ.เมืองนนทบุรี จ.นนทบุรี 11000	
Mechanical Engineer :	SIGNATURE
วิศวกรผู้ออกแบบระบบเครื่องกลและปรับอากาศ	
นายประสิทธิ์ เกียวสุนทร วก.1221 ที่อยู่ 44/372 ซอยบางกระดี่ 35/1 แขวงแสมดำ เขตบางขุนเทียน กทม. 10150	ประสิทธิ์
Sanitary Engineer :	SIGNATURE
วิศวกรผู้ออกแบบระบบสุขาภิบาล และดับเพลิง	
นายทศวรรษ สนั่นฤทธิ์ วส. 215 ที่อยู่ บ้านเลขที่ 99/107 หมู่ที่ 3 ต.ศีรษะจรเข้น้อย อ.บางเสาธง จ.สมุทรปราการ 10540	ทศวรรษ

ISSUE/REVISION

REV.	DESCRIPTION	DATE
A	90% DEVELOPED	09/05/2026

PROJECT NAME :

GEDC 01

LOCATION:
Nikhom Phattana district, Rayong ,industrial estate,CPGC

BUILDING :

90% DEVELOPED

TITLE :

WALL COMPARTMENTATION
LAYOUT-2F

JOB NO.	SCALE 1:250
DRAWN LW	REF.
CHECKED LJC	DWG.NO. MPK01A-90-A-WC-201
APPROVED LXD	
DATE 2026.05.09	