LEGEND		
	DESCRIPTION	SPECIFICATION
🟨	CAST-IN-PLACE CONCRETE PANEL WALL	2 HOUR FIRE RATED CAST-IN-PLACE CONCRETE PANEL WALL(DETAILED STRUCTURAL CONSTRUCTION DRAWINGS)
🟦	PRE-CAST CONCRETE PANEL WALL	2 HOUR FIRE RATED 100MM PRE-CAST CONCRETE PANEL WALL(INCLUDES 30MM RESERVED INSTALLATION DISTANCE)(U-value < 0.5 W/(m²·K)(ATTACHED EXTERIOR WALL)
🟫	PRE-CAST CONCRETE PANEL WALL	2 HOUR FIRE RATED 100MM PRE-CAST CONCRETE PANEL WALL(INCLUDES 30MM RESERVED INSTALLATION DISTANCE)(U-value < 0.5 W/(m²·K)(INTERFLOOR WALL)
🟪	LIGHT STEEL CALCIUM SILICATE BOARD	2 HOUR FIRE RATED 100MM LIGHT GAUGE STEEL FRAMING WITH FIBER CEMENT CALCIUM SILICATE COMPOSITE BOARD PARTITION
🟩	PRECAST ACC CONCRETE WALL PANELS	2 HOUR FIRE RATED 100MM PRECAST ACC CONCRETE WALL PANELS(U-value < 0.5 W/(m²·K)
🟥	PRECAST ACC CONCRETE WALL PANELS	2 HOUR FIRE RATED 200MM PRECAST ACC CONCRETE WALL PANELS
🟧	CONCRETE BLOCK WALL	2 HOUR FIRE RATED 200MM CONCRETE BLOCK WALL
🟦	LIGHT STEEL CALCIUM SILICATE BOARD	（NO FIRESTOP REQUIRED）2 HOUR FIRE RATED 100 MM LIGHT GAUGE STEEL FRAMING WITH FIBER CEMENT CALCIUM SILICATE COMPOSITE BOARD PARTITION

▨ FIRE COMPARTMENT

"Note:
All adhesives, sealants, paints, primers, and coatings shall be low-VOC content and low-VOC emissionsmaterials.
All ceiling boards shall be low-VOC emissions materials.
Used at least 20 EPD products from 5 manufacturers.
All materials shall comply with LEED TOR."

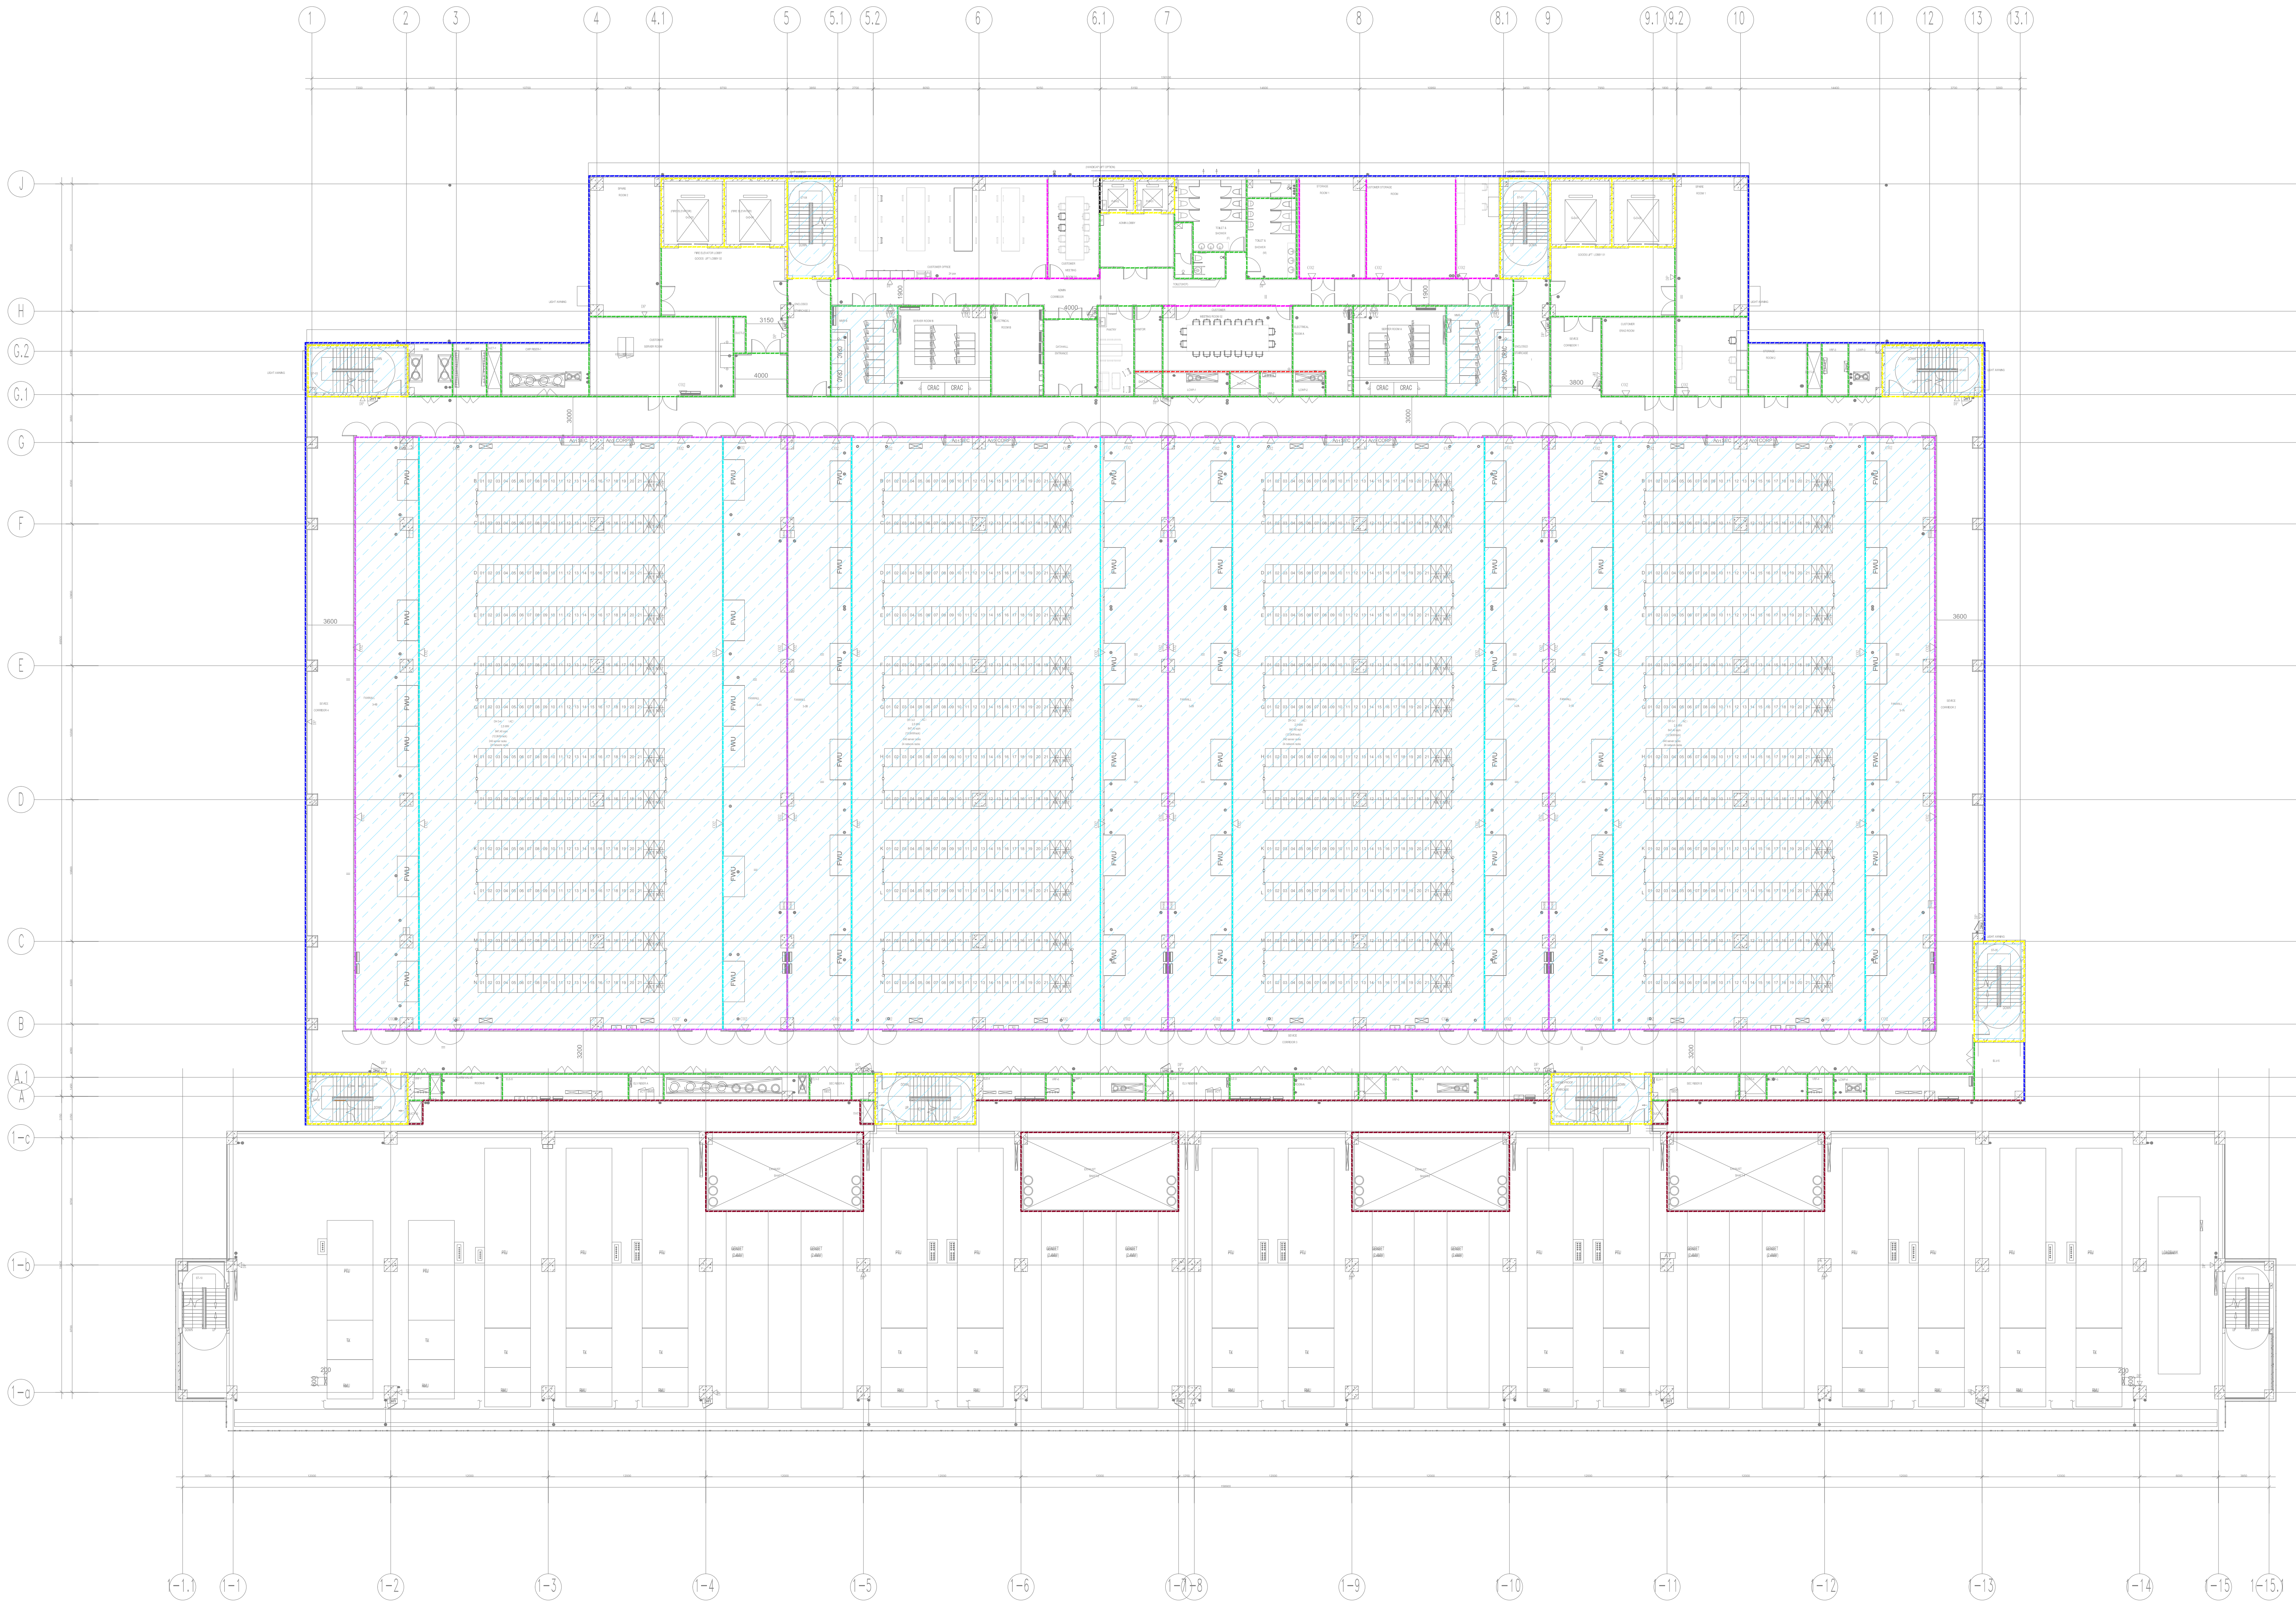

3RD FLOOR PLAN(BUILDING A)

SCALE 1:250

FLOOR AREA:12238.10 sqm
OVERALL GROSS FLOOR AREA:40900.20 sqm

CLIENT :

GULF EDGE DC 01

87 Wireless Road, M Thai Tower 11th. Floor, All Seasons Place, Lumpini,
Pathumwan, Bangkok 10330, Thailand

CONTRACTOR :

华西发展(泰国)有限公司
บริษัท หัวซือ ดีเวลลอปเม้นต์ (ประเทศไทย) จำกัด
HUASHI DEVELOPMENT CO.,LTD
No. 202, Room No. 1403, 14/F, Le Concorde Building,
Ratchadapisek Road, Huaykhwang Sub-District,
Huaykhwang District, Bangkok Metropolitan 10310.

CONSULTANT :

ARbay
บริษัท เอ อาร์ เบย์ จำกัด
ARbay Company Limited
31 st Floor Bangkok Insurance Building
25 South Sathorn road Thungmahamek
Sathorn Bangkok 10120 THAILAND
T +66 (0) 2286 8199
F +66 (0) 2286 2863
info@arbay.co.th

CONSULTANT :

Qbic Engineers & Architects Co.,Ltd.
8 Soi KALONG 4 SANAMBINNAM ROAD,
THASAI SUB-DISTRICT, MUANG NONTHABURI DISTRICT
, NONTHABURI.
Tel 662-950-4374
Fax 662-580-3231
E-Mail : qbic@qbic.co.th, www.qbic.co.th
QBIC ENGINEERS AND ARCHITECTS CO.,LTD.

CONSULTANT :

MITR
MITR TECHNICAL CONSULTANT CO.,LTD.
1168/8 12th FLOOR, LUMPINI TOWER BUILDING,
RAMA IV RD., THUNGMAHAMEK, SATHORN, BANGKOK 10120, THAILAND
TEL : 0-2679-9079-84
FAX : 0-2679-9085 E-mail: mitr_dd@mitr.com

Architect : SIGNATURE
ประกิต พนานุรัตน์ วสถ. 580
ที่อยู่
251/1 ถ.จารุเมือง แขวงรองเมือง เขตปทุมวัน
กรุงเทพมหานคร โทรศัพท์ 02-286-8199

Structural Engineer : SIGNATURE
วิศวกรผู้ออกแบบโครงสร้าง
ณัฐสม สงวนวงษ์ วย 1423
ที่อยู่
2/1 ซ.รามคำแหง 150 ถ.รามคำแหง
แขวง สะพานสูง เขต สะพานสูง กทม. 10240

Structural Inspector : SIGNATURE
วิศวกรผู้ตรวจสอบโครงสร้าง
โกมล จุฑาภัทร วย 964
ที่อยู่
24/18 ซ.นวมินทร์ 129 ถ. นวมินทร์
แขวง นวลจันทร์ เขต บึงกุ่ม กทม. 10230

Electrical Engineer : SIGNATURE
วิศวกรผู้ออกแบบระบบไฟฟ้ากำลัง
นายสุภัทร บูรณวิทย์ วฟก.1265
ที่อยู่
21 ซอยทานสัมฤทธิ์ 13
ตำบลท่าทราย อ.เมืองนนทบุรี จ.นนทบุรี 11000

Mechanical Engineer : SIGNATURE
วิศวกรผู้ออกแบบระบบเครื่องกลและปรับอากาศ
นายประสิทธิ์ เกียวสุนทร วก.1221
ที่อยู่
44/372 ซอยบางกระดี่ 35/1 แขวงแสมดำ
เขตบางขุนเทียน กทม. 10150
ประสิทธิ์

Sanitary Engineer : SIGNATURE
วิศวกรผู้ออกแบบระบบสุขาภิบาล และดับเพลิง
นายทศวรรษ สนันฤทธิ์ วส. 215
ที่อยู่
บ้านเลขที่ 99/107 หมู่ที่ 3 ต.ศีรษะจรเข้น้อย
อ.บางเสาธง จ.สมุทรปราการ 10540
ทศวรรษ

ISSUE/REVISION

REV.	DESCRIPTION	DATE
A	90% DEVELOPED	09/05/2026

PROJECT NAME :
GEDC 01

LOCATION:
Nikhom Phattana district, Rayong ,industrial estate,CPGC

BUILDING :

90% DEVELOPED

TITLE :
WALL COMPARTMENTATION
LAYOUT-3F

JOB NO.	SCALE 1:250
DRAWN LW	REF.
CHECKED LJC	DWG.NO. MPK01A-90-A-WC-301
APPROVED LXD	
DATE 2026.05.09	

NOTE : THIS PRINT IS OF A CONFIDENTIAL NATURE, IT SHALL NOT BE TRACED,PHOTOGRAPHED,PHOTOSTATED OR REPRODUCED IN ANY MANER,NOR USED FOR ANY PURPOSE WHATSOEVER EXCEPT BY WRITTEN PERMISSION