FIRE DETECTION AND ALARM

⊗ E	LED EMERGENCY LIGHT 5W (SELF CONTAINED TYPE) ,SURFACE OR SUSPENDED MOUNTED ,WITH 2-HOURS BACK UP TIME,BUILT-IN ADDRESSABLE MODULE
⊗ EWP	WEATHERPROOF TYPE LED EMERGENCY LIGHT 5W (SELF CONTAINED TYPE) ,SURFACE OR SUSPENDED MOUNTED ,WITH 2-HOURS BACK UP TIME,BUILT-IN ADDRESSABLE MODULE
⊠	LED EMERGENCY LIGHT 2x9W(SELF CONTAINED TYPE) , WALL MOUNTED, WITH 2-HOURS BACK UP TIME,BUILT-IN ADDRESSABLE MODULE
⊠ wp	WEATHERPROOF TYPE LED EMERGENCY LIGHT 2x9W(SELF CONTAINED TYPE) , WALL MOUNTED, WITH 2-HOURS BACK UP TIME,BUILT-IN ADDRESSABLE MODULE
E	LED EXIT SIGN LUMINAIRE (SELF CONTAINED TYPE) , WALL OR SUSPENDED MOUNTED, WITH 2-HOURS BACK UP TIME,BUILT-IN ADDRESSABLE MODULE
E wp	WEATHERPROOF TYPE LED EXIT SIGN LUMINAIRE (SELF CONTAINED TYPE) , WALL OR SUSPENDED MOUNTED, WITH 2-HOURS BACK UP TIME,BUILT-IN ADDRESSABLE MODULE
→ ←	LED DIRECTIONAL SIGN LUMINAIRE (SELF CONTAINED TYPE) , SUSPENDED MOUNTED (SINGLE SIDE),WITH 2-HOURS BACK UP TIME BUILT-IN ADDRESSABLE MODULE
→ wp ← wp	WEATHERPROOF TYPE LED DIRECTIONAL SIGN LUMINAIRE (SELF CONTAINED TYPE) , SUSPENDED MOUNTED (SINGLE SIDE),WITH 2-HOURS BACK UP TIME BUILT-IN ADDRESSABLE MODULE
⇄	LED DIRECTIONAL SIGN LUMINAIRE (SELF CONTAINED TYPE) , SUSPENDED MOUNTED (DOUBLE SIDE) ,WITH 2-HOURS BACK UP TIME,BUILT-IN ADDRESSABLE MODULE
⇄ wp	WEATHERPROOF TYPE LED DIRECTIONAL SIGN LUMINAIRE (SELF CONTAINED TYPE) , SUSPENDED MOUNTED (DOUBLE SIDE) ,WITH 2-HOURS BACK UP TIME,BUILT-IN ADDRESSABLE MODULE
FW↑	LED DIRECTIONAL SIGN LUMINAIRE (SELF CONTAINED TYPE) ,SURFACE OR SUSPENDED MOUNTED(SINGLE SIDE),WITH 2-HOURS BACK UP TIME BUILT-IN ADDRESSABLE MODULE
FW↑ wp	WEATHERPROOF TYPE LED DIRECTIONAL SIGN LUMINAIRE (SELF CONTAINED TYPE) ,SURFACE OR SUSPENDED MOUNTED(SINGLE SIDE),WITH 2-HOURS BACK UP TIME BUILT-IN ADDRESSABLE MODULE

SYMBOLS

FCP	FIRE ALARM CONTROL PANEL
ANN	GRAPHIC ANNUNCIATOR BOARD
RANN	REMOTE GRAPHIC ANNUNCIATOR BOARD
FATB	FIRE ALARM TERMINAL BOX
ASD	ASPIRATED SMOKE DETECTION CONTROL PANEL
Ⓗ	SURFACE MOUNTED HEAT DETECTOR,COMBINATION TYPE
Ⓗ 135°F	SURFACE MOUNTED HEAT DETECTOR FIXED TEMPERATURE AT 135°F
SD	SURFACE MOUNTED SMOKE DETECTOR, PHOTOELECTRIC TYPE
SD V	SMOKE DETECTOR INSIDE COLD CONTENTMENT
DS	DUCT SMOKE DETECTOR
M	MANUAL CALL POINT / BREAK GLASS ALARM WITH KEY SWITCH ZONE
AD	ADDRESSABLE TYPE
U	UNDERNEATH RAISE FLOOR
C	ABOVE CEILING
V	LASER SMOKE DETECTOR TYPE
Ⓑ	FIRE ALARM BELL 6"
⊗	FLASHSTROBE LIGHT 110 Cd
	ASD SAMPLING POINT
F	FIRE MAN TELEPHONE OUTLET
MM	MONITOR MODULE
CM	CONTROL MODULE
IM	FAULT ISOLATOR MODULE
F	FIRE ALARM SPEAKER WALL MOUNTED
F	FIRE ALARM SPEAKER W/STORBE LIGHT, WALL MOUNTED
FS	FLOW SWITCH (BY OTHER)
SV	SUPERVISORY SWITCH (BY OTHER)
T	PHOTO ELECTRIC BEAM SMOKE DETECTOR, TRANSMITTER
R	PHOTO ELECTRIC BEAM SMOKE DETECTOR, RECEIVER
E——×	ASPIRATED SMOKE DETECTION AND END CAP
EOL	END OF LINE
L	FIRE CONDITION ACTIVATED LIFT HOMING.
PA	FIRE CONDITION ACTIVATED BACKGROUND MUSIC SYSTEM SHUT-OFF
A/C	FIRE CONDITION ACTIVATED AIR-CONDITIONING SHUT-OFF.
NOV	FIRE CONDITION MONITORED NOVEC
FP	FIRE CONDITION MONITORED FIRE PUMP
P	PULL BOX
■	MAN HOLE
FSS	FIRE SUPPRESSION SYSTEM
K	KEY SWITCH

FIRE EVACUATION ROUTE

🟩	56.25M
🟪	79.21M
🟫	46.70M
🟦	53.40M
🟩	36.50M
🟨	70.26M
🟥	51.60M
🟦	59.71M
🟨	INTERNAL WALL, TWO-HOUR FIRE RESISTANCE RATING
🟩	EXTERIOR WALL, TWO-HOUR FIRE RESISTANCE RATING

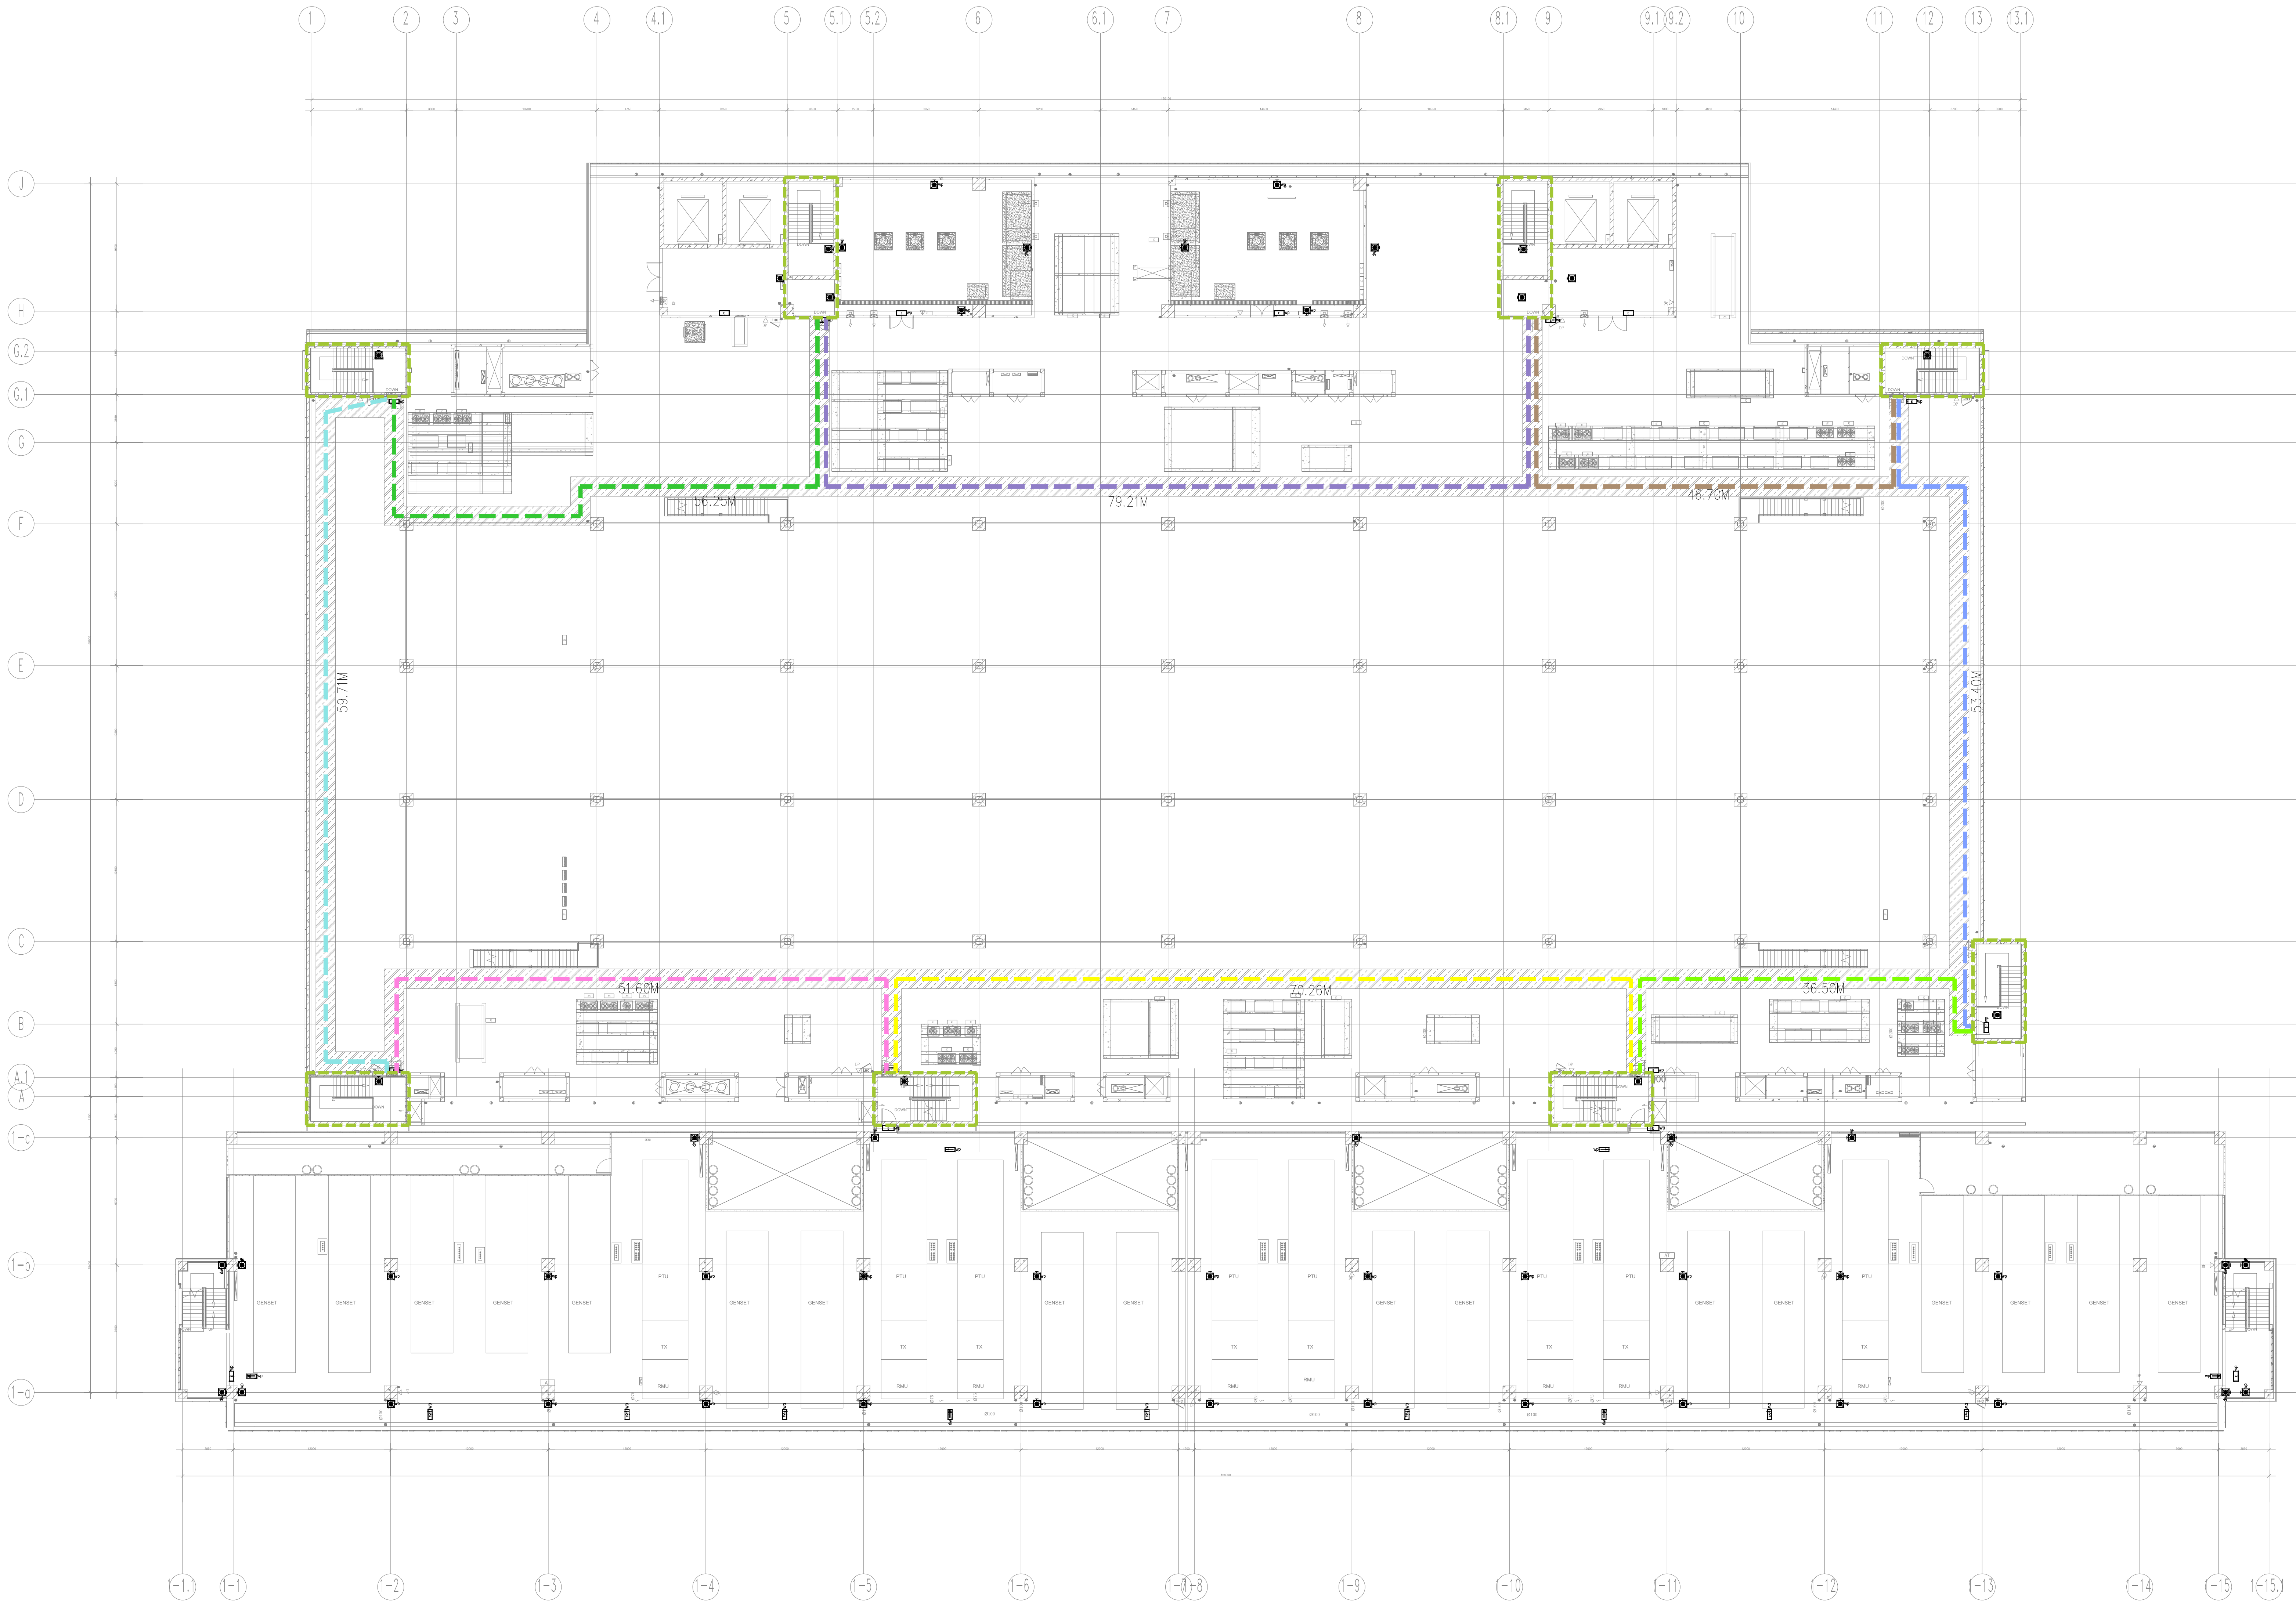

ROOF FLOOR PLAN(DC BUILDING A)

SCALE 1:250
FLOOR AREA:12238.10 sqm
OVERALL GROSS FLOOR AREA:40900.20 sqm

COMPARTMENT AND EVACUATION ANALYSIS – RF

NOTE : THIS PRINT IS OF A CONFIDENTIAL NATURE, IT SHALL NOT BE TRACED,PHOTOGRAPHED,PHOTOSTATED OR REPRODUCED IN ANY MANER,NOR USED FOR ANY PURPOSE WHATSOEVER EXCEPT BY WRITTEN PERMISSION

CLIENT :

GULF EDGE DC 01

87 Wireless Road, M Thai Tower 11th. Floor, All Seasons Place, Lumpini,
Pathumwan, Bangkok 10330, Thailand

CONTRACTOR :

华西发展(泰国)有限公司
บริษัท หัวซือ ดีเวลลอปเม้นต์ (ประเทศไทย) จำกัด
HUASHI DEVELOPMENT CO.,LTD
No. 202, Room No. 1403, 14/F, Le Concorde Building,
Ratchadapisek Road, Huaykhwang Sub-District,
Huaykhwang District, Bangkok Metropolitan 10310.

CONSULTANT :

ARbay
บริษัท เอ อาร์ เบย์ จำกัด
ARbay Company Limited
31 st Floor Bangkok Insurance Building
25 South Sathorn road Thungmahamek
Sathorn Bangkok 10120 THAILAND
T +66 (0) 2286 8199
F +66 (0) 2286 2863
info@arbay.co.th

CONSULTANT :

Qbic Engineers & Architects Co.,Ltd.
8 Soi KALONG 4 SANAMBINNAM ROAD,
THASAI SUB-DISTRICT, MUANG NONTHABURI DISTRICT
, NONTHABURI.
Tel 662-950-4374
Fax 662-580-3231
E-Mail : qbic@qbic.co.th, www.qbic.co.th
QBIC ENGINEERS AND ARCHITECTS CO.,LTD.

CONSULTANT :

MITR
MITR TECHNICAL CONSULTANT CO.,LTD.
1168/8 12th FLOOR, LUMPINI TOWER BUILDING,
RAMA IV RD., THUNGMAHAMEK, SATHORN, BANGKOK 10120, THAILAND
TEL : 0-2679-9079-84
FAX : 0-2679-9085 E-mail: mitr_dd@mitr.com

Architect : SIGNATURE
ประกิต พนานุรัตน์ วสถ. 580
ที่อยู่
251/1 ถ.จารุเมือง แขวงรองเมือง เขตปทุมวัน
กรุงเทพมหานคร โทรศัพท์ 02-286-8199

Structural Engineer : SIGNATURE
วิศวกรผู้ออกแบบโครงสร้าง
ณัฐสม สงวนวงษ์ วย 1423
ที่อยู่
2/1 ซ.รามคำแหง 150 ถ.รามคำแหง
แขวง สะพานสูง เขต สะพานสูง กทม. 10240

Structural Inspector : SIGNATURE
วิศวกรผู้ตรวจสอบโครงสร้าง
โกมล จุฑาภัทร วย 964
ที่อยู่
24/18 ซ.นวมินทร์ 129 ถ. นวมินทร์
แขวง นวลจันทร์ เขต บึงกุ่ม กทม. 10230

Electrical Engineer : SIGNATURE
วิศวกรผู้ออกแบบระบบไฟฟ้ากำลัง
นายสุภัทร บูรณวิทย์ วฟก.1265
ที่อยู่
21 ซอยทานสัมฤทธิ์ 13
ตำบลท่าทราย อ.เมืองนนทบุรี จ.นนทบุรี 11000

Mechanical Engineer : SIGNATURE
วิศวกรผู้ออกแบบระบบเครื่องกลและปรับอากาศ
นายประสิทธิ์ เกียวสุนทร วก.1221
ที่อยู่
44/372 ซอยบางกระดี่ 35/1 แขวงแสมดำ
เขตบางขุนเทียน กทม. 10150
ประสิทธิ์

Sanitary Engineer : SIGNATURE
วิศวกรผู้ออกแบบระบบสุขาภิบาล และดับเพลิง
นายทศวรรษ สนั่นฤทธิ์ วส. 215
ที่อยู่
บ้านเลขที่ 99/107 หมู่ที่ 3 ต.ศีรษะจรเข้น้อย
อ.บางเสาธง จ.สมุทรปราการ 10540
ทศวรรษ

ISSUE/REVISION

REV.	DESCRIPTION	DATE
A	90% DEVELOPED	09/05/2026

PROJECT NAME :
GEDC 01

LOCATION:
Nikhom Phattana district, Rayong ,industrial estate,CPGC

BUILDING :

90% DEVELOPED

TITLE :
COMPARTMENT AND EVACUATION
ANALYSIS-RF

JOB NO.	SCALE 1:250
DRAWN LW	REF.
CHECKED LJC	DWG.NO. MPK01A-90-A-CACE-401
APPROVED LXD	
DATE 2026.05.09	