SIGNAGE DETAIL LAYOUT

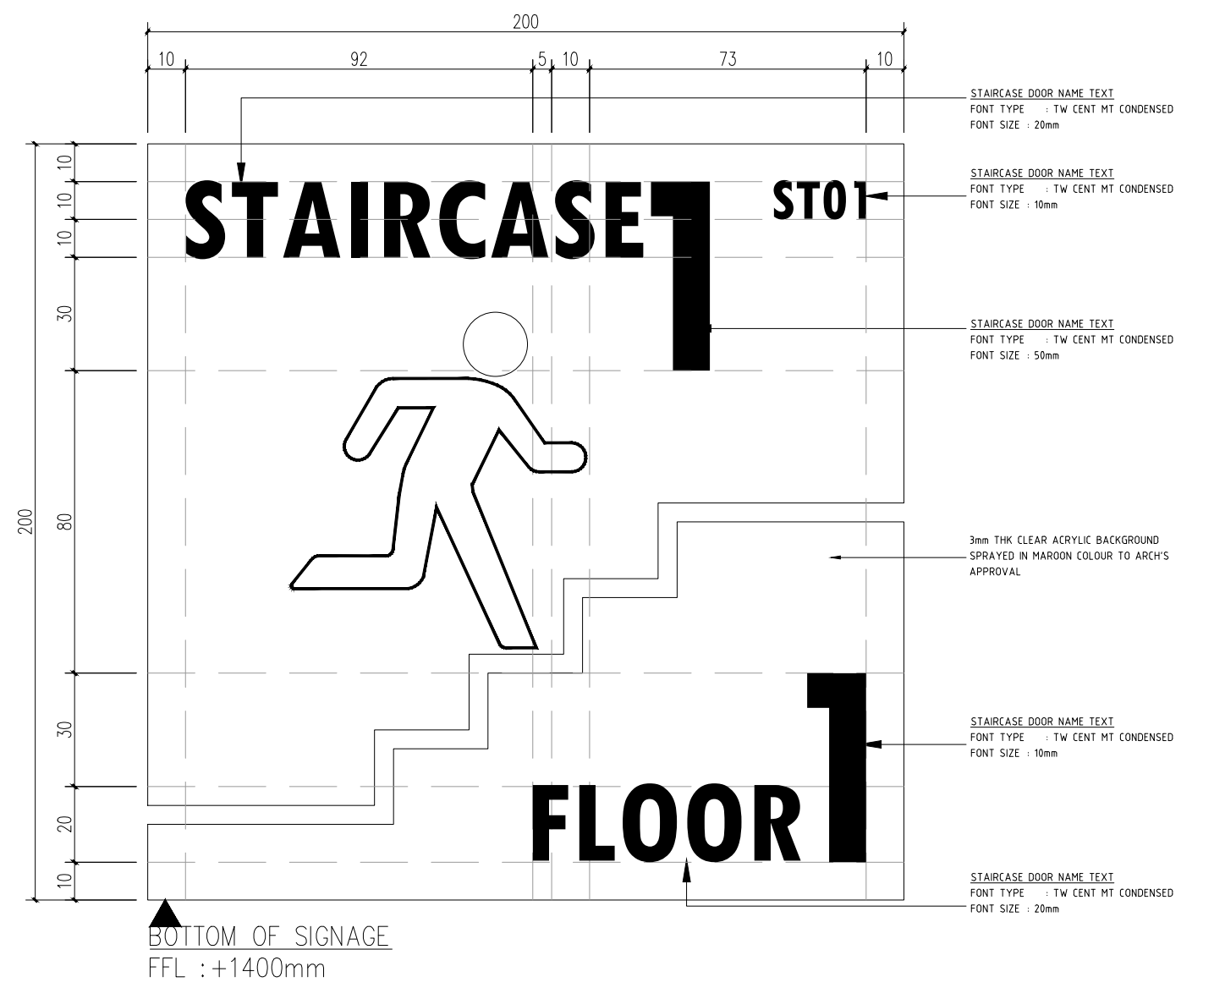
200
10
92
5
10
73
10
STAIRCASE 1
ST01
FLOOR 1
STAIRCASE DOOR NAME TEXT
FONT TYPE : TW CENT MT CONDENSED
FONT SIZE : 20mm
STAIRCASE DOOR NAME TEXT
FONT TYPE : TW CENT MT CONDENSED
FONT SIZE : 10mm
STAIRCASE DOOR NAME TEXT
FONT TYPE : TW CENT MT CONDENSED
FONT SIZE : 50mm
3mm THK CLEAR ACRYLIC BACKGROUND SPRAYED IN MAROON COLOUR TO ARCH'S APPROVAL
STAIRCASE DOOR NAME TEXT
FONT TYPE : TW CENT MT CONDENSED
FONT SIZE : 10mm
STAIRCASE DOOR NAME TEXT
FONT TYPE : TW CENT MT CONDENSED
FONT SIZE : 20mm
30
80
20

BOTTOM OF SIGNAGE
FFL :+1400mm

STAIRCASE / FLOOR	SIGN	QUANTITY	MATERIAL
ST1 / FIRST FLOOR	STAIRCASE 1 FLOOR 1	1	3mm TRANSPARENT ACRYLIC 140mm X 240mm with HIGH RES UV PRINT STICKER TO MATCH PANTONE NAVY BLUE
ST2 / FIRST FLOOR	STAIRCASE 2 FLOOR 1	1	
ST3 / FIRST FLOOR	STAIRCASE 3 FLOOR 1	1	
ST4 / FIRST FLOOR	STAIRCASE 4 FLOOR 1	1	
ST5 / FIRST FLOOR	STAIRCASE 5 FLOOR 1	1	

STAIRCASE / FLOOR	SIGN	QUANTITY	MATERIAL
ST6 / FIRST FLOOR	STAIRCASE 6 FLOOR 1	1	3mm TRANSPARENT ACRYLIC 140mm X 240mm with HIGH RES UV PRINT STICKER TO MATCH PANTONE NAVY BLUE
ST7 / FIRST FLOOR	STAIRCASE 7 FLOOR 1	1	
ST8 / FIRST FLOOR	STAIRCASE 8 FLOOR 1	1	
ST9 / FIRST FLOOR	STAIRCASE 9 FLOOR 1	1	
ST10 / FIRST FLOOR	STAIRCASE 10 FLOOR 1	1	

SIGNAGE DETAIL LAYOUT

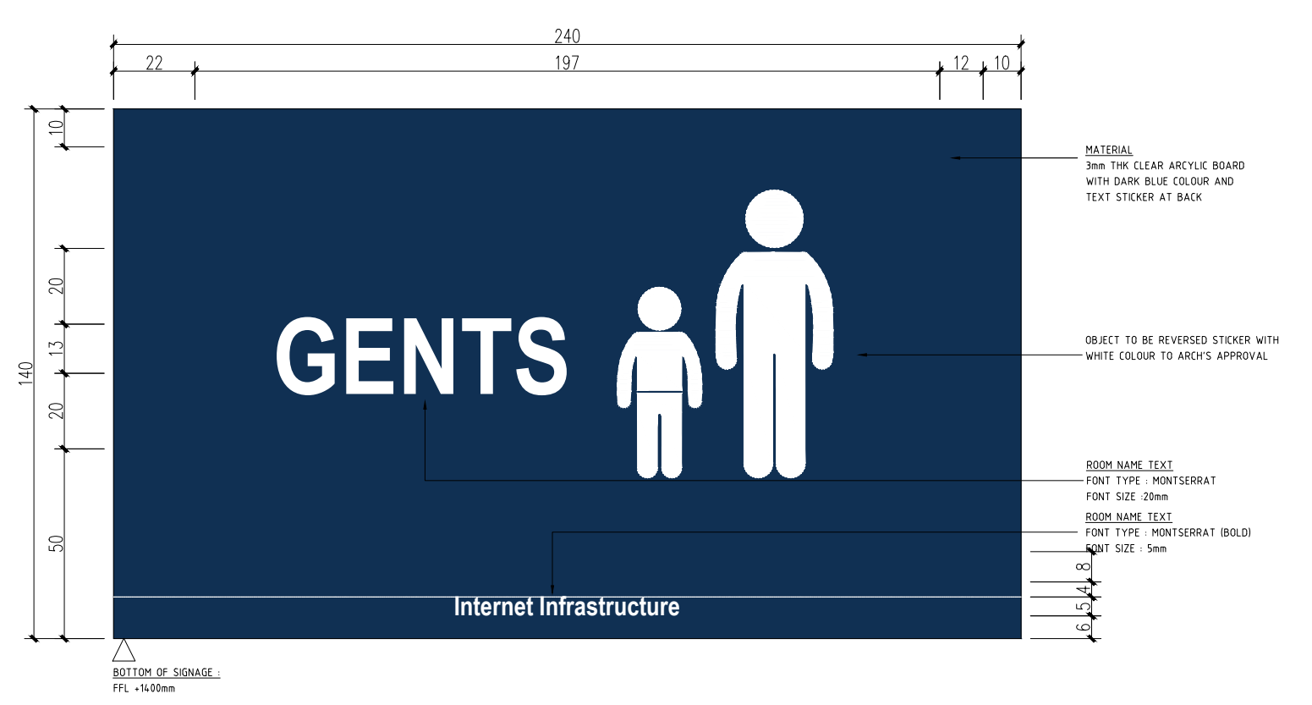
240
197
GENTS
Internet Infrastructure
140
50

BOTTOM OF SIGNAGE :
FFL +1400mm

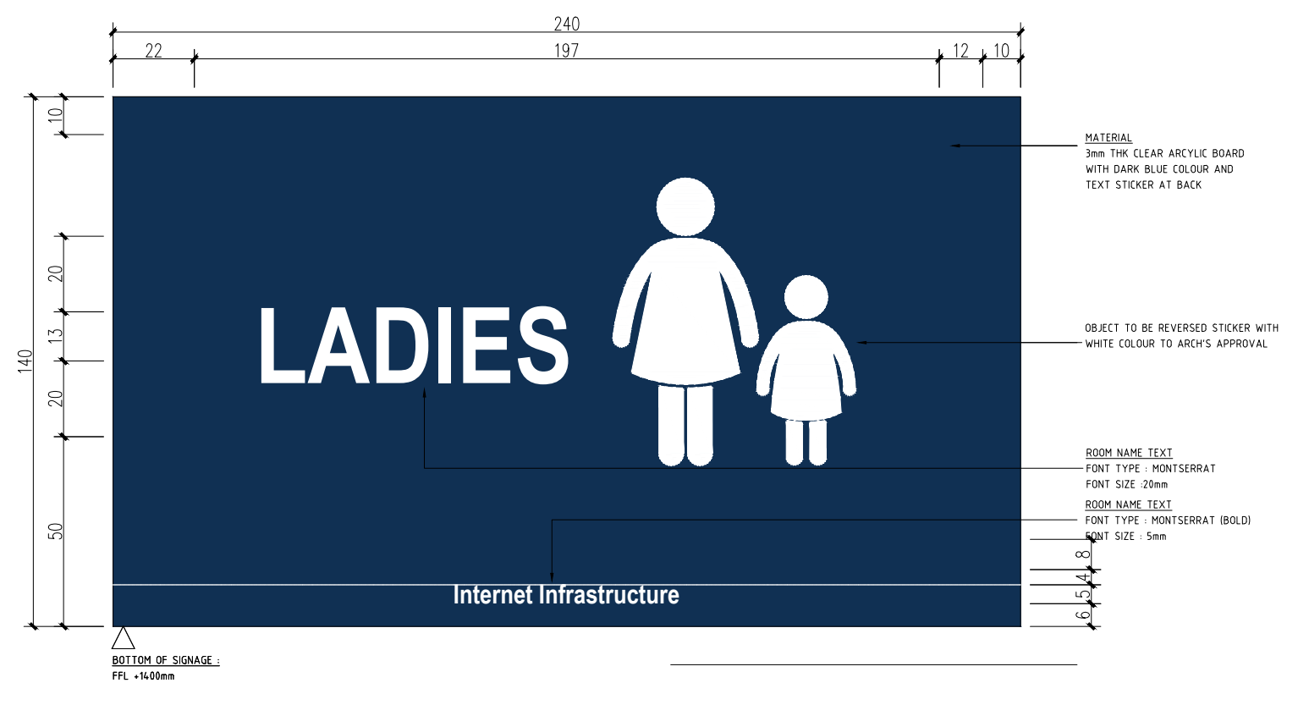
240
197
LADIES
Internet Infrastructure

LOCATION	SIGNAGE		QUANTITY	MATERIAL
	ENGLISH	THAI		
	LOBBY TOILET(F)	-	1	
	LOBBY TOILET(M)	-	1	
	TOILET(HCP)	-	1	
	TOILET&SHOWER(F)	-	1	
	TOILET&SHOWER(M)	-	1	
	TOILET 02	-	1	
	TOILET 01	-	1	
	SUB TOTAL		7	

SIGNAGE DETAIL LAYOUT

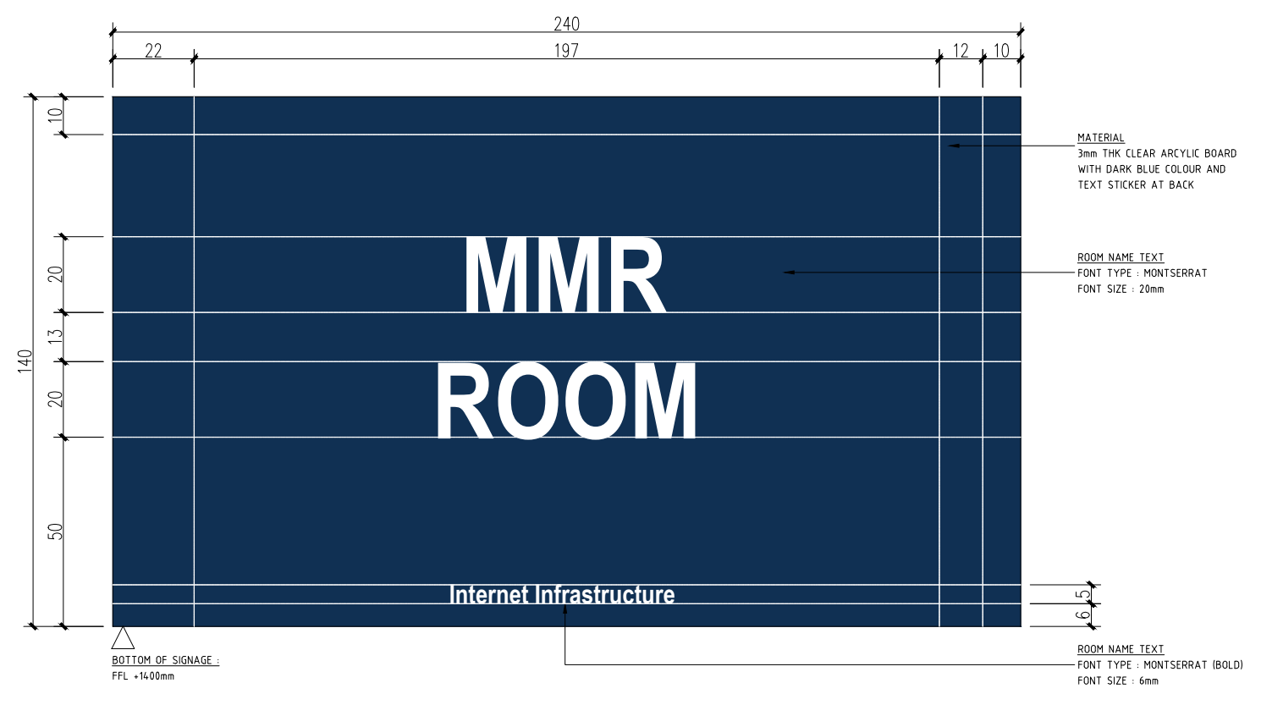
240
197
MMR
ROOM
Internet Infrastructure
6.5
6
ROOM NAME TEXT
FONT SIZE : 6mm

BOTTOM OF SIGNAGE :
FFL +1400mm

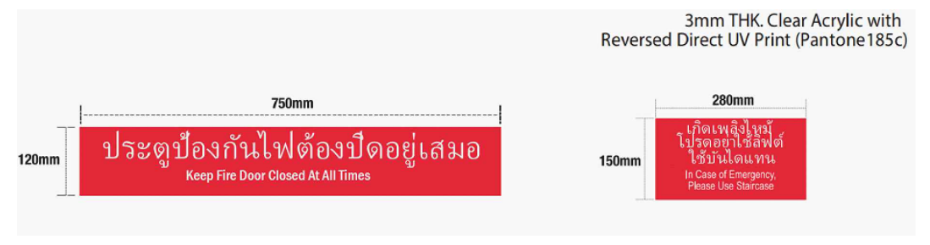
3mm THK. Clear Acrylic with Reversed Direct UV Print (Pantone185c)
750mm
120mm
ประตูป้องกันไฟต้องปิดอยู่เสมอ
Keep Fire Door Closed At All Times
280mm
150mm
เกิดเพลิงไหม้ โปรดอย่าใช้ลิฟต์ ใช้บันไดแทน
In Case of Emergency, Please Use Staircase

ESCAPE DOOR SIGNAGE
*The height of signage 1100mm from floor level
*Type A - Single leaf door required 2 signage (1-front & 1-rear)
*Type B - Double leaf door required 4 signage (2-front & 2-rear)

FIRE LIFT SIGNAGE

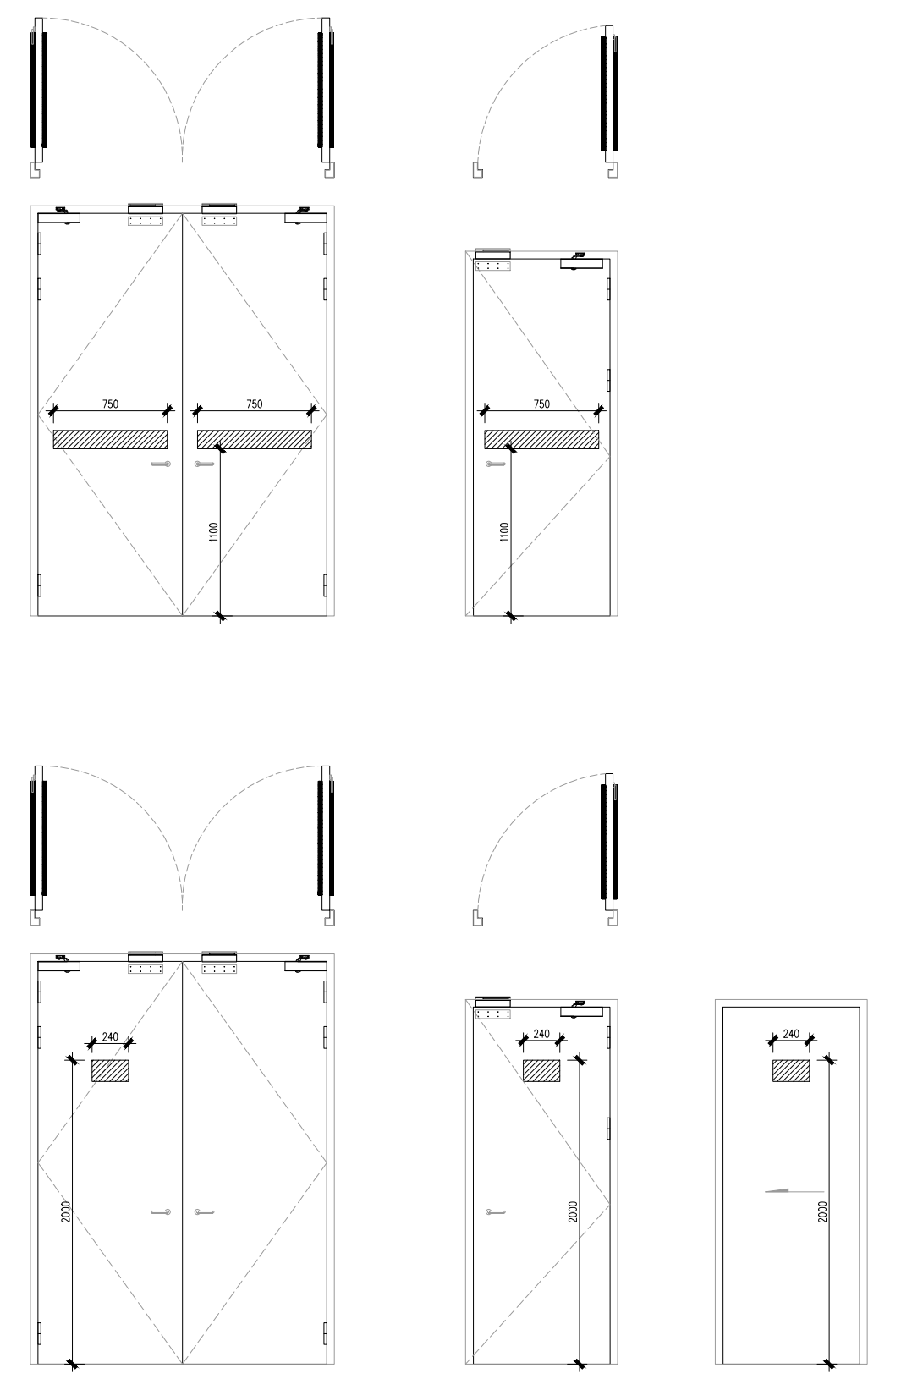

LOCATION	SIGNAGE		QUANTITY	MATERIAL
	ENGLISH	THAI		
	LOBBY	-	1	3mm TRANSPARENT ACRYLC 140mm X240mm with HIGH RES UV PRINT STICKER TO MATCH PANTONE NAVY BLUE
	VISITOR MEETING ROOM	-	1	
	SECURITY 01	-	1	
	SECURITY OFFICE	-	1	
	PASSENGER LIFT 01/02	-	1	
	ADMIN LOBBY	-	1	
	DUCT-1	-	1	
	FCC	-	2	
	SOC	-	1	
	MDF-01	-	1	
	STAIR-01	-	3	
	GOODS LIFT 01/02	-	1	
	GOODS LIFT LOBBY 01	-	1	
	UNLOADING 01	-	4	
	STAIR-02	-	2	
	SECURITY 02	-	1	
	LCWP-1	-	1	
	VRF-1	-	1	
	DUCT-2	-	1	
	UNPACKING 01	-	1	
	STAGING 01	-	1	
	MMR A	-	1	
	SERVER ROOM A	-	1	
	ELECTRICAL ROOM A	-	1	
	MEETING ROOM	-	1	
	LCWP-2	-	1	
	VRF-2	-	1	
	DUCT-3	-	1	
	LCWP-3	-	1	
	DUCT-4	-	1	
	JANITOR	-	1	
	PANTRY	-	1	
	DATA HALL ENTRANCE	-	2	
	ADMIN CORRIDOR	-	1	
	ELECTRIAL ROOM B	-	1	
	SEVER ROOM B	-	1	
	MMR B	-	1	
	STAGING 02	-	1	
	CWP RISER-1	-	1	
	DUCT-5	-	1	
	VRF-3	-	1	
	CHW	-	1	
	STAIR-03	-	2	
	SECURITY 03	-	1	
	UNPACKING 02	-	1	
	UNLOADING 02	-	4	
	GOODS LIFT LOBBY 02	-	1	
	GOODS LIFT 03/04	-	1	
	STAIR-04	-	3	
	MDF-02	-	1	
	SEVICE CORRIDOR	-	1	
	DATA HALL 1-1	-	4	
	FAN WALL 1-1A	-	2	
	FAN WALL 1-1B	-	2	
	DATA HALL 1-2	-	4	
	FAN WALL 1-2A	-	2	
	FAN WALL 1-2B	-	2	
	DATA HALL 1-3	-	4	
	FAN WALL 1-3A	-	2	
	FAN WALL 1-3B	-	2	
	CHILER ROOM -1	-	1	
	CHILER ROOM -2	-	1	
	CHILER ROOM -3	-	1	
	STAIR-05	-	2	
	MDF-03	-	1	
	ELE-1	-	1	
	LCWP-4	-	1	
	VRF-4	-	1	
	LCWP-5	-	1	
	DUCT-6	-	1	
	ELV-1	-	1	
	DUCT-7	-	1	
	STAIR-06	-	2	
	ELE-2	-	1	
	LCWP-6	-	1	
	VRF-5	-	1	
	DUCT-8	-	1	
	ALARM VALVE ROOM A	-	1	
	ELV-2	-	1	
	ELE-3	-	1	
	DUCT-9	-	1	
	LCWP-7	-	1	
	VRF-6	-	1	
	ELE-4	-	1	
	STAIR-07	-	2	
	DUCT-10	-	1	
	ELV-3	-	1	
	CWP RISER-2	-	2	
	ELV-4	-	1	
	ELE-5	-	1	
	STORAGE	-	1	
	ALARM VALVE ROOM B	-	1	
	DUCT-11	-	1	
	VRF-7	-	1	
	STAIR-08	-	3	
	MDF-04	-	1	
	STAIR-09	-	1	
	WET GARBAGE ROOM	-	1	
	GARBAGE ROOM	-	1	
	PUMP ROOM	-	1	
	MV-A	-	2	
	FUEL PUMP ROOM A	-	1	
	EXHAUST SHAFT-1	-	1	
	EXHAUST SHAFT-2	-	1	
	EXHAUST SHAFT-3	-	1	
	EXHAUST SHAFT-4	-	1	
	FUEL PUMP ROOM B	-	1	
	MV-B	-	2	
	ALARM VALVE ROOM C	-	1	
	DOMESTIC WATER PUMP ROOM	-	1	
	FIRE PUMP ROOM	-	1	
	STAIR-10	-	1	
	ELECTRICAL GANTRY	-	1	
	SUB TOTAL		150	

MAIN DRAWING

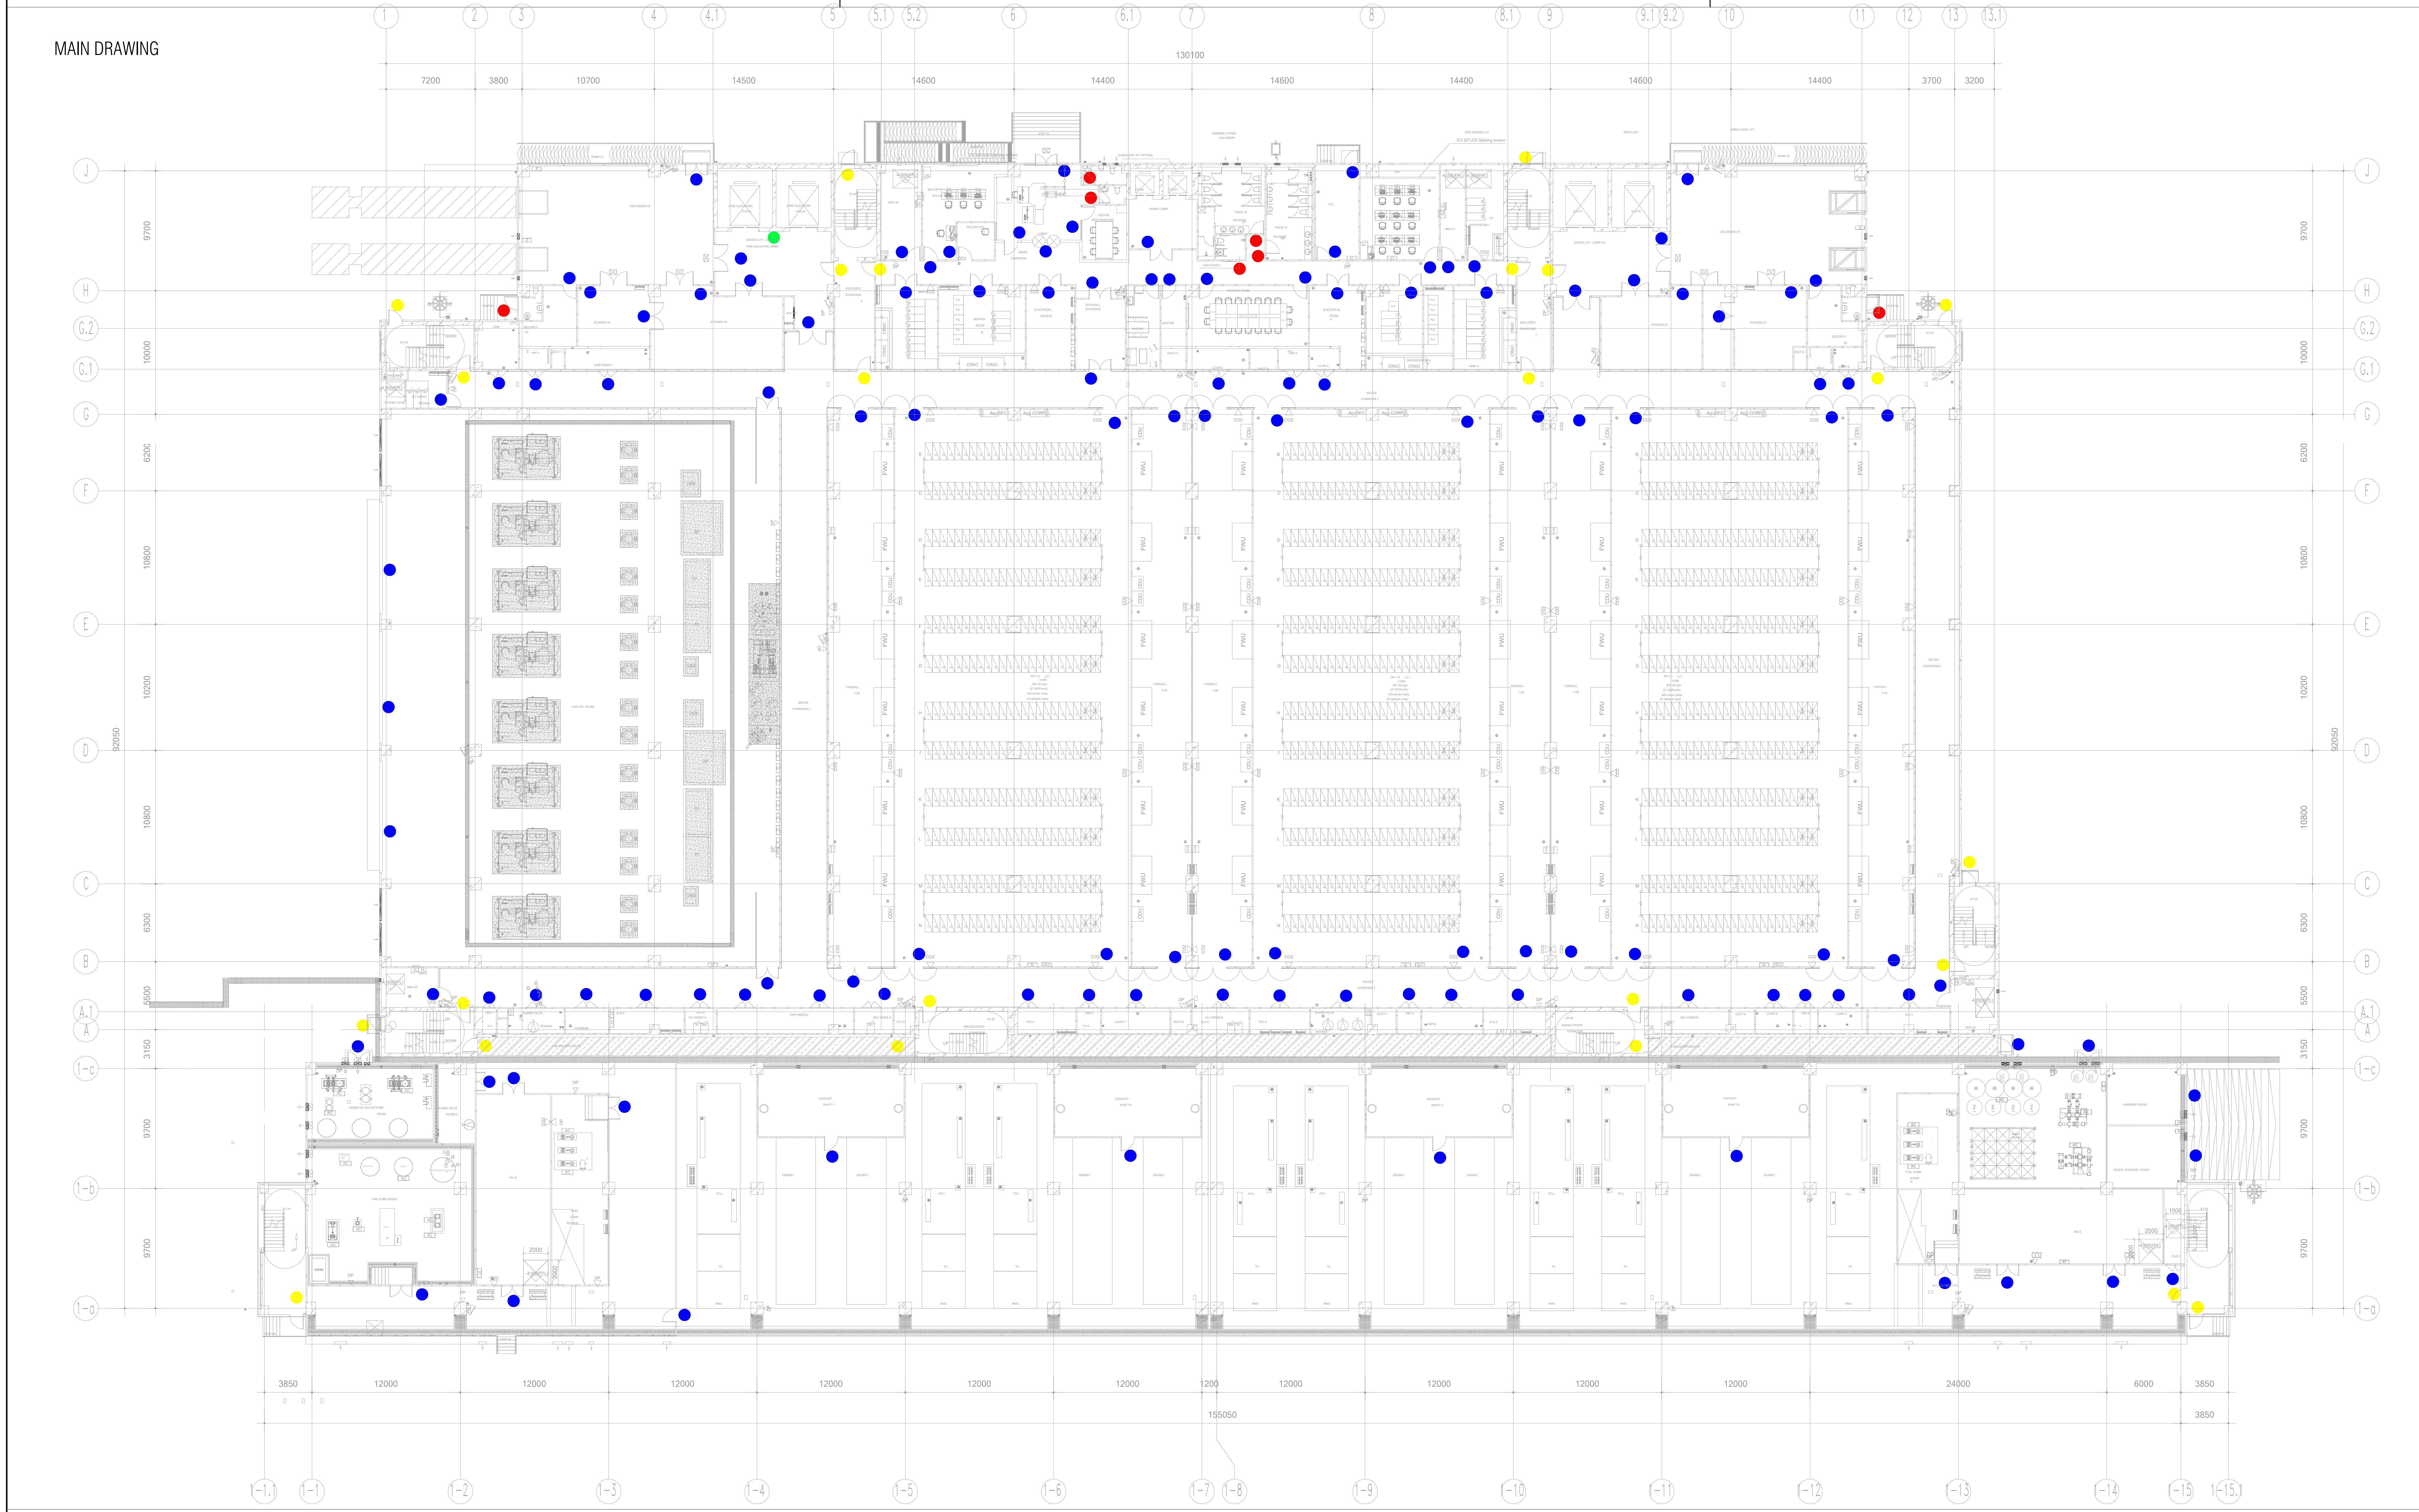
1
2
3
4
4.1
5
5.1
5.2
6
6.1
7
8
8.1
9
9.1
9.2
10
11
12
13
13.1
130100
7200
3800
10700
14500
14600
14400
14600
14400
14600
14400
3700
3200
J
H
G.2
G.1
G
F
E
D
C
B
A.1
A
1-c
1-b
1-a
9700
10000
6200
10800
10200
10800
6300
5500
3150
9700
9700
92050
3850
12000
12000
12000
12000
12000
12000
1200
12000
12000
12000
24000
6000
3850
155050
3850
1-1
1-2
1-3
1-4
1-5
1-6
1-7
1-8
1-9
1-10
1-11
1-12
1-13
1-14
1-15
1-15.1

SIGNAGE LAGEND	
🔴	TOILET & DISABLED DOOR SIGNAGE
🟡	STAIRCASE DOOR SIGNAGE
🔵	ROOM FACILITY SIGNAGE
🟢	FIRE LIFT SIGNAGE

SIGNAGE LAYOUT-1F

NOTE : THIS PRINT IS OF A CONFIDENTIAL NATURE, IT SHALL NOT BE TRACED,PHOTOGRAPHED,PHOTOSTATED OR REPRODUCED IN ANY MANER,NOR USED FOR ANY PURPOSE WHATSOEVER EXCEPT BY WRITTEN PERMISSION

CLIENT :

GULF EDGE DC 01

87 Wireless Road, M Thai Tower 11th. Floor, All Seasons Place, Lumpini, Pathumwan, Bangkok 10330, Thailand

CONTRACTOR :

华西发展(泰国)有限公司
บริษัท หัวซือ ดีเวลลอปเม้นต์ (ประเทศไทย) จำกัด
HUASHI DEVELOPMENT CO.,LTD
No. 202, Room No. 1403, 14/F, Le Concorde Building,
Ratchadapisek Road, Huaykhwang Sub-District,
Huaykhwang District, Bangkok Metropolitan 10310.

CONSULTANT :

ARbay
บริษัท เอ อาร์ เบย์ จำกัด
ARbay Company Limited
31 st Floor Bangkok Insurance Building
25 South Sathorn road Thungmahamek
Sathorn Bangkok 10120 THAILAND
T +66 (0) 2286 8199
F +66 (0) 2286 2863
info@arbay.co.th

CONSULTANT :

Qbic Engineers & Architects Co.,Ltd.
8 Soi KALONG 4 SANAMBINNAM ROAD,
THASAI SUB-DISTRICT, MUANG NONTHABURI DISTRICT
, NONTHABURI.
Tel 662-950-4374
Fax 662-580-3231
E-Mail : qbic@qbic.co.th, www.qbic.co.th
QBIC ENGINEERS AND ARCHITECTS CO.,LTD.

CONSULTANT :

MITR
MITR TECHNICAL CONSULTANT CO.,LTD.
1168/8 12th FLOOR, LUMPINI TOWER BUILDING,
RAMA IV RD., THUNGMAHAMEK, SATHORN, BANGKOK 10120, THAILAND
TEL : 0-2679-9079-84
FAX : 0-2679-9085 E-mail: mitr_dd@mitr.com

Architect : SIGNATURE
ประกิต พนานุรัตน์ วสถ. 580
ที่อยู่
251/1 ถ.จารุเมือง แขวงรองเมือง เขตปทุมวัน
กรุงเทพมหานคร โทรศัพท์ 02-286-8199

Structural Engineer : SIGNATURE
วิศวกรผู้ออกแบบโครงสร้าง
ณัฐสม สงวนวงษ์ วย 1423
ที่อยู่
2/1 ซ.รามคำแหง 150 ถ.รามคำแหง
แขวง สะพานสูง เขต สะพานสูง กทม. 10240

Structural Inspector : SIGNATURE
วิศวกรผู้ตรวจสอบโครงสร้าง
โกมล จุฑาภัทร วย 964
ที่อยู่
24/18 ซ.นวมินทร์ 129 ถ. นวมินทร์
แขวง นวลจันทร์ เขต บึงกุ่ม กทม. 10230

Electrical Engineer : SIGNATURE
วิศวกรผู้ออกแบบระบบไฟฟ้ากำลัง
นายสุภัทร บูรณวิทย์ วฟก.1265
ที่อยู่
21 ซอยทานสัมฤทธิ 13
ตำบลท่าทราย อ.เมืองนนทบุรี จ.นนทบุรี 11000

Mechanical Engineer : SIGNATURE
วิศวกรผู้ออกแบบระบบเครื่องกลและปรับอากาศ
นายประสิทธิ์ เกียวสุนทร วก.1221
ที่อยู่
44/372 ซอยบางกระดี 35/1 แขวงแสมดำ
เขตบางขุนเทียน กทม. 10150
ประสิทธิ์

Sanitary Engineer : SIGNATURE
วิศวกรผู้ออกแบบระบบสุขาภิบาล และดับเพลิง
นายทศวรรษ สนันฤทธิ วส. 215
ที่อยู่
บ้านเลขที 99/107 หมู่ที 3 ต.ศีรษะจรเข้น้อย
อ.บางเสาธง จ.สมุทรปราการ 10540
ทศวรรษ

ISSUE/REVISION

REV.	DESCRIPTION	DATE
A	90% DEVELOPED	09/05/2026

PROJECT NAME :
GEDC 01
LOCATION:
Nikhom Phattana district, Rayong ,industrial estate,CPGC

BUILDING :

90% DEVELOPED

TITLE :
SIGNAGE LAYOUT-1F

JOB NO.	SCALE 1:200
DRAWN LXP	REF.
CHECKED LJC	DWG.NO. MPK01A-90-A-SN-101
APPROVED LXD	
DATE 2026.05.09	

SIGNAGE DETAIL LAYOUT

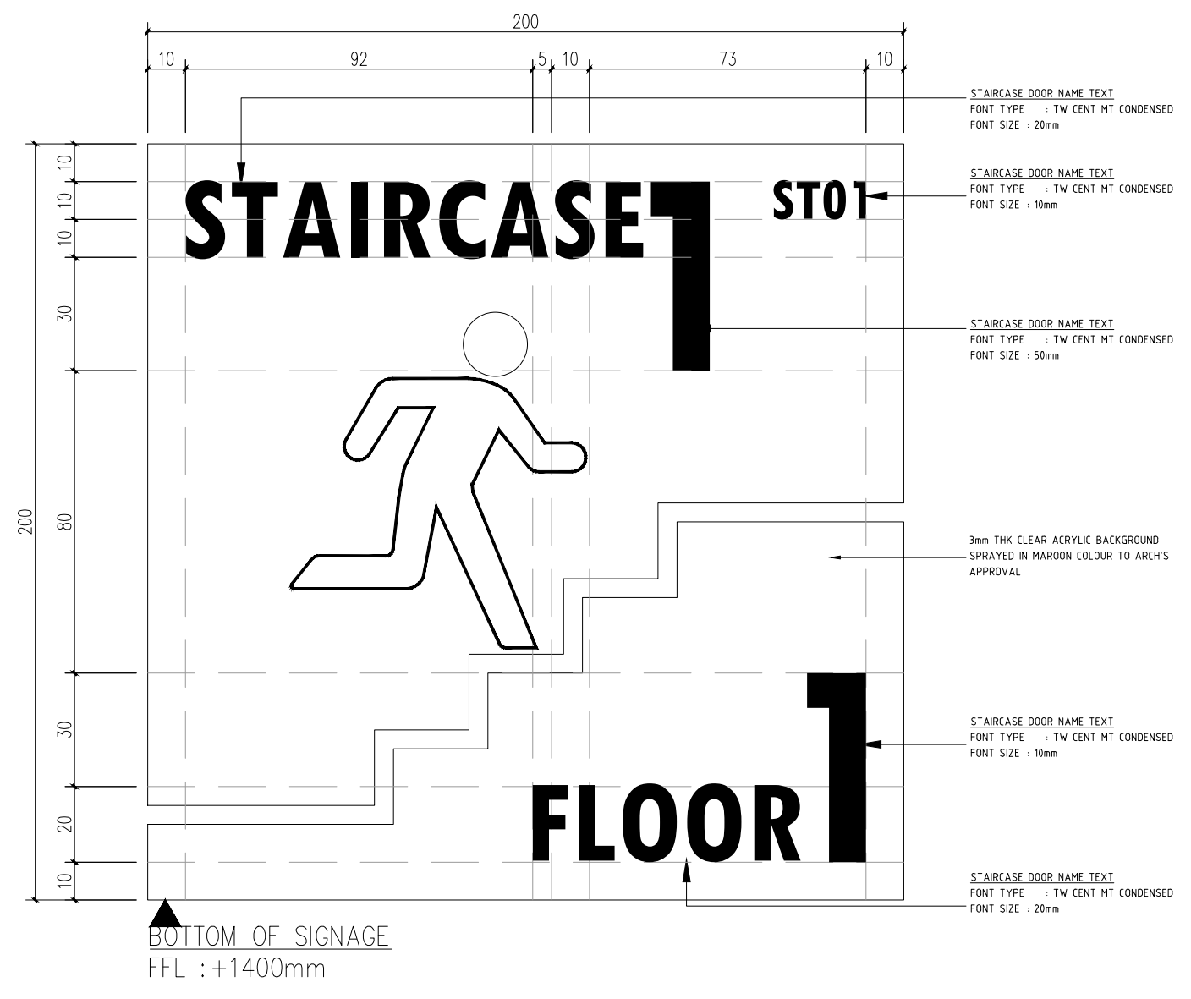
200
10
92
5
10
73
10
STAIRCASE 1
ST01
FLOOR 1
10
10
10
30
80
30
20
10
200
STAIRCASE DOOR NAME TEXT
FONT TYPE : TW CENT MT CONDENSED
FONT SIZE : 20mm
STAIRCASE DOOR NAME TEXT
FONT TYPE : TW CENT MT CONDENSED
FONT SIZE : 10mm
STAIRCASE DOOR NAME TEXT
FONT TYPE : TW CENT MT CONDENSED
FONT SIZE : 50mm
3mm THK CLEAR ACRYLIC BACKGROUND SPRAYED IN MAROON COLOUR TO ARCH'S APPROVAL
STAIRCASE DOOR NAME TEXT
FONT TYPE : TW CENT MT CONDENSED
FONT SIZE : 10mm
STAIRCASE DOOR NAME TEXT
FONT TYPE : TW CENT MT CONDENSED
FONT SIZE : 20mm

BOTTOM OF SIGNAGE
FFL : +1400mm

STAIRCASE / FLOOR	SIGN	QUANTITY	MATERIAL
ST1 / SECOND FLOOR	STAIRCASE 1 FLOOR 2	1	3mm TRANSPARENT ACRYLIC 140mm X 240mm with HIGH RES UV PRINT STICKER TO MATCH PANTONE NAVY BLUE
ST2 / SECOND FLOOR	STAIRCASE 2 FLOOR 2	1	
ST3 / SECOND FLOOR	STAIRCASE 3 FLOOR 2	1	
ST4 / SECOND FLOOR	STAIRCASE 4 FLOOR 2	1	
ST5 / SECOND FLOOR	STAIRCASE 5 FLOOR 2	1	

STAIRCASE / FLOOR	SIGN	QUANTITY	MATERIAL
ST6 / SECOND FLOOR	STAIRCASE 6 FLOOR 2	1	3mm TRANSPARENT ACRYLIC 140mm X 240mm with HIGH RES UV PRINT STICKER TO MATCH PANTONE NAVY BLUE
ST7 / SECOND FLOOR	STAIRCASE 7 FLOOR 2	1	
ST8 / SECOND FLOOR	STAIRCASE 8 FLOOR 2	1	
ST9 / SECOND FLOOR	STAIRCASE 9 FLOOR 2	1	
ST10 / SECOND FLOOR	STAIRCASE 10 FLOOR 2	1	

SIGNAGE DETAIL LAYOUT

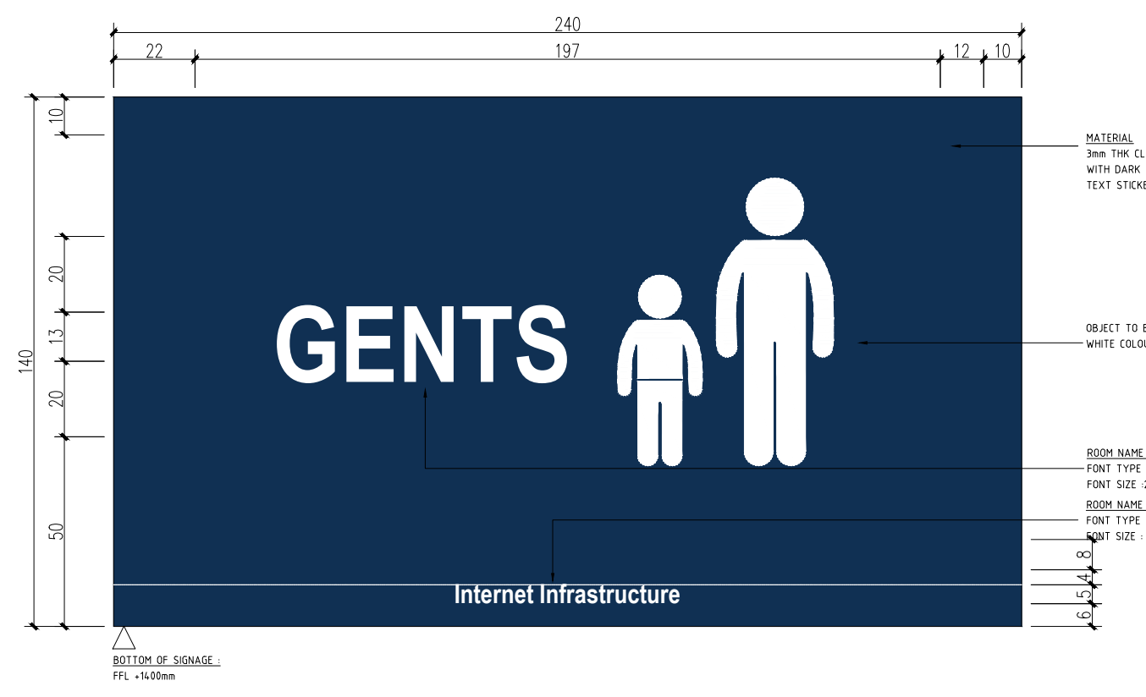
240
22
197
12
10
10
20
13
20
50
140
GENTS
Internet Infrastructure
MATERIAL
3mm THK CLEAR ARCYLIC BOARD WITH DARK BLUE COLOUR AND TEXT STICKER AT BACK
OBJECT TO BE REVERSED STICKER WITH WHITE COLOUR TO ARCH'S APPROVAL
ROOM NAME TEXT
FONT TYPE : MONTSERRAT
FONT SIZE :20mm
ROOM NAME TEXT
FONT TYPE : MONTSERRAT (BOLD)
FONT SIZE : 5mm
8
4
5
6
BOTTOM OF SIGNAGE :
FFL +1400mm

LOCATION	SIGNAGE		QUANTITY	MATERIAL
	ENGLISH	THAI		
	TOILET(HCP)	-	1	
	TOILET&SHOWER(F)	-	1	
	TOILET&SHOWER(M)	-	1	
	SUB TOTAL		3	

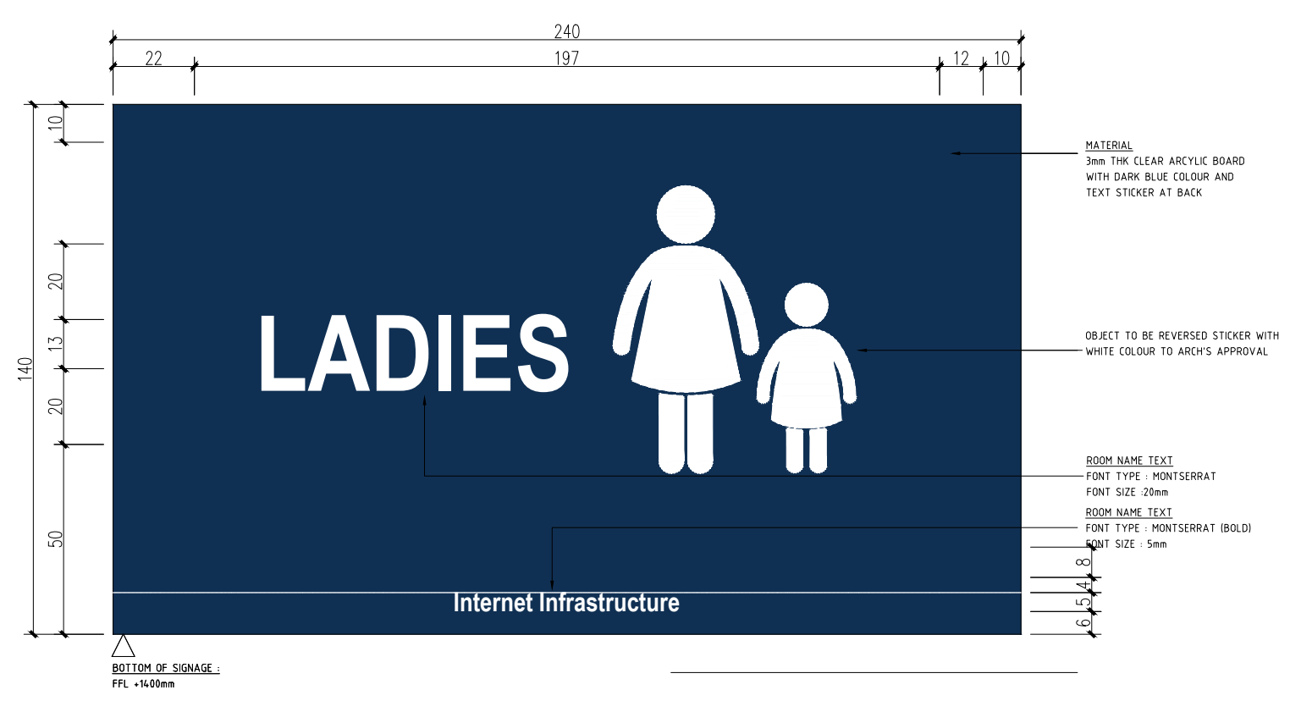
240
22
197
12
10
10
20
13
20
50
140
LADIES
Internet Infrastructure
MATERIAL
3mm THK CLEAR ARCYLIC BOARD WITH DARK BLUE COLOUR AND TEXT STICKER AT BACK
OBJECT TO BE REVERSED STICKER WITH WHITE COLOUR TO ARCH'S APPROVAL
ROOM NAME TEXT
FONT TYPE : MONTSERRAT
FONT SIZE :20mm
ROOM NAME TEXT
FONT TYPE : MONTSERRAT (BOLD)
FONT SIZE : 5mm
8
4
5
6
BOTTOM OF SIGNAGE :
FFL +1400mm

SIGNAGE DETAIL LAYOUT

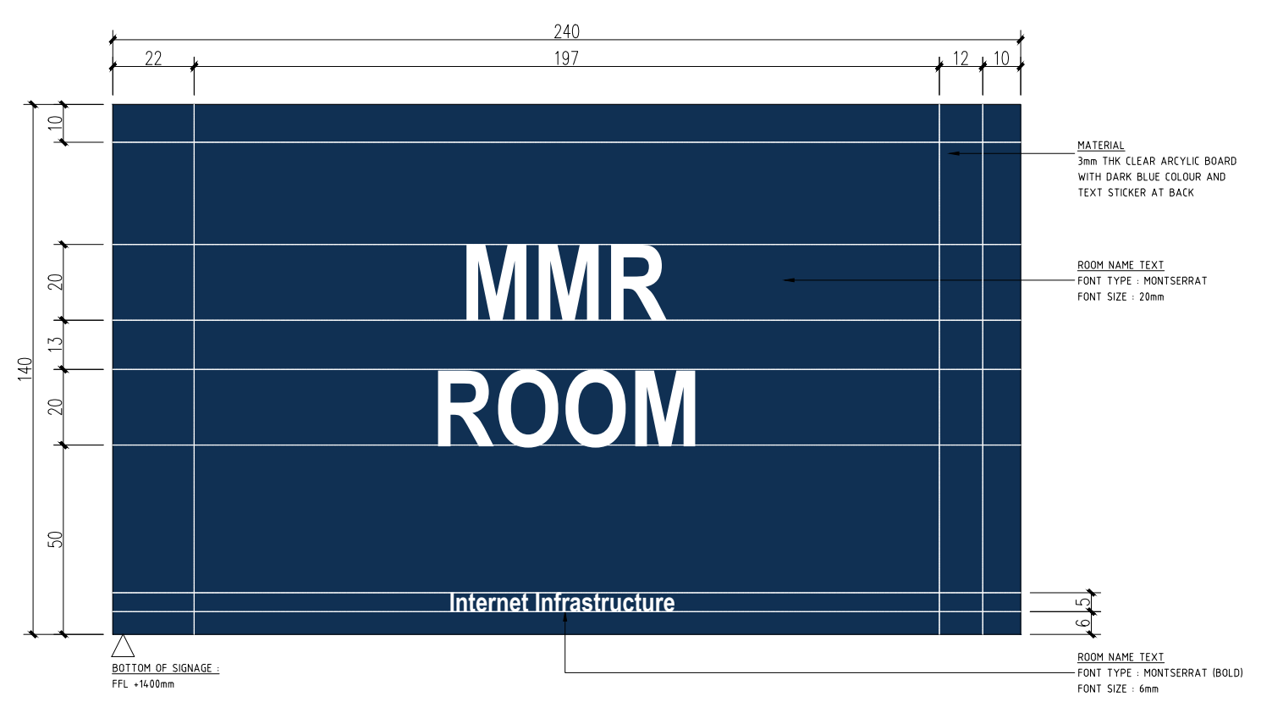
240
22
197
12
10
10
20
13
20
50
140
MMR
ROOM
Internet Infrastructure
MATERIAL
3mm THK CLEAR ARCYLIC BOARD WITH DARK BLUE COLOUR AND TEXT STICKER AT BACK
ROOM NAME TEXT
FONT TYPE : MONTSERRAT
FONT SIZE : 20mm
5
6
ROOM NAME TEXT
FONT TYPE : MONTSERRAT (BOLD)
FONT SIZE : 6mm
BOTTOM OF SIGNAGE :
FFL +1400mm

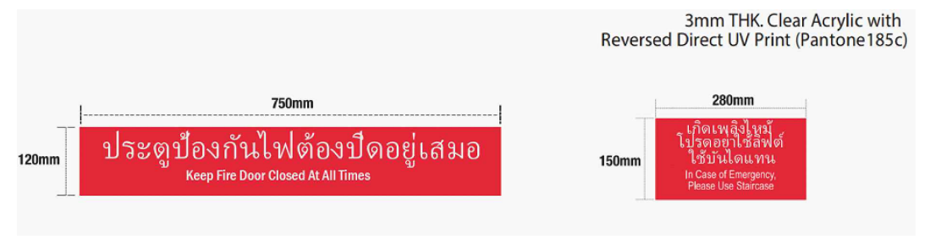
3mm THK. Clear Acrylic with
Reversed Direct UV Print (Pantone185c)
750mm
120mm
ประตูป้องกันไฟต้องปิดอยู่เสมอ
Keep Fire Door Closed At All Times
280mm
150mm
เกิดเพลิงไหม้ โปรดอย่าใช้ลิฟต์ ใช้บันไดแทน
In Case of Emergency, Please Use Staircase

ESCAPE DOOR SIGNAGE
*The height of signage 1100mm from floor level
*Type A - Single leaf door required 2 signage (1-front & 1-rear)
*Type B - Double leaf door required 4 signage (2-front & 2-rear)

LIFT SIGNAGE

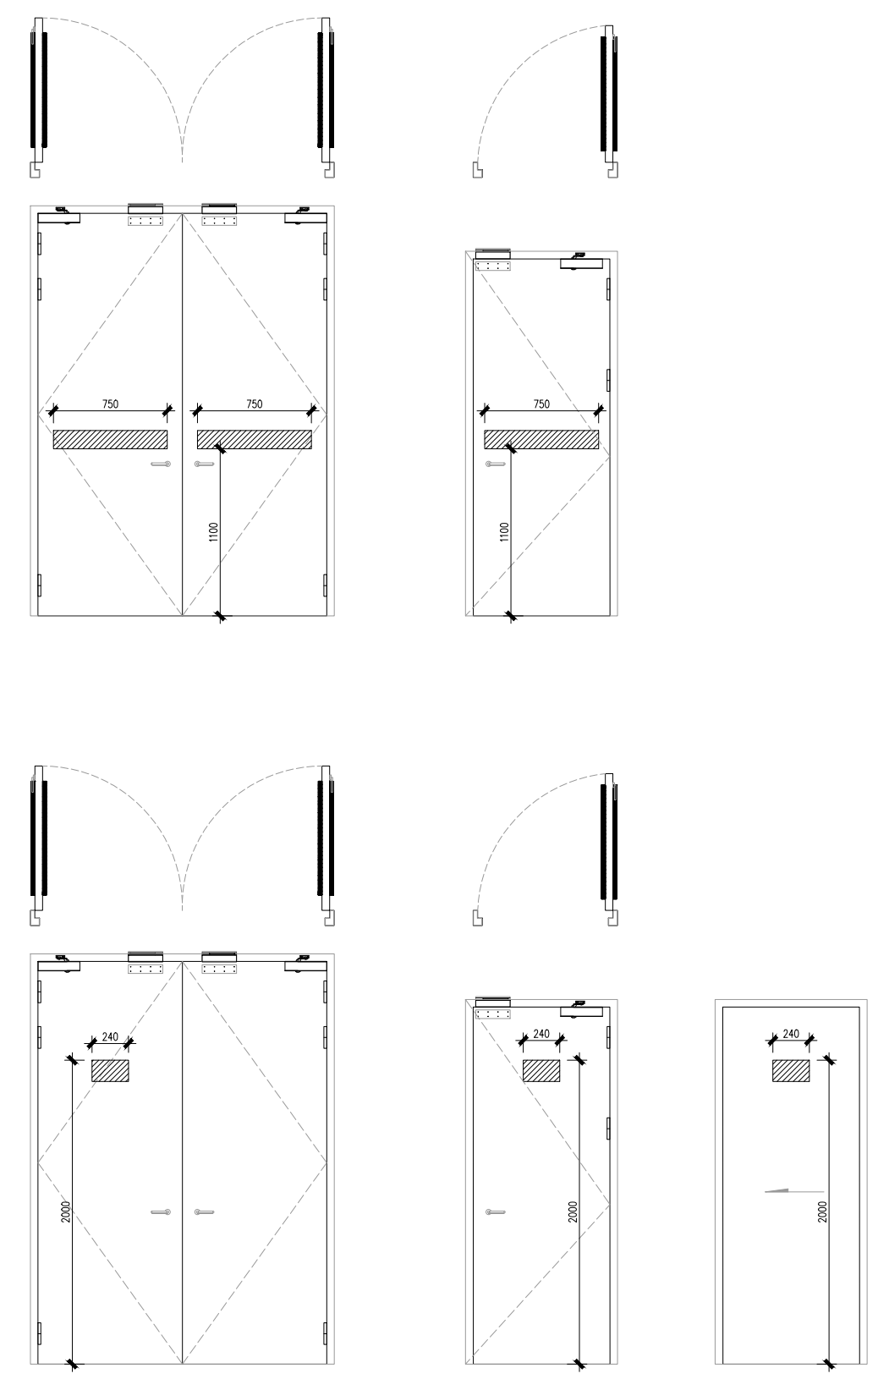
750
750
750
1100
1100
240
240
240
2000
2000
2000

LOCATION	SIGNAGE		QUANTITY	MATERIAL
	ENGLISH	THAI		
	OFFICE	-	2	3mm TRANSPARENT ACRYLC 140mm X240mm with HIGH RES UV PRINT STICKER TO MATCH PANTONE NAVY BLUE
	MEETING ROOM 01	-	1	
	PASSENGER LIFT 01/02	-	1	
	ADMIN LOBBY	-	1	
	DUCT-1	-	1	
	NOC(EQUIPMENT)	-	1	
	NOC	-	1	
	WAR ROOM	-	1	
	STAIR-01	-	1	
	GOODS LIFT 01/02	-	1	
	GOODS LIFT LOBBY 01	-	1	
	SPARE ROOM 01	-	1	
	STAIR-02	-	1	
	LCWP-1	-	1	
	VRF-1	-	1	
	DUCT-2	-	1	
	STORAGE ROOM 1	-	1	
	STORAGE ROOM 2	-	1	
	ERAD ROOM	-	1	
	MMR A	-	1	
	SERVER ROOM A	-	1	
	ELECTRICAL ROOM A	-	1	
	MEETING ROOM 2	-	2	
	LCWP-2	-	1	
	VRF-2	-	1	
	DUCT-3	-	1	
	LCWP-3	-	1	
	DUCT-4	-	1	
	JANITOR	-	1	
	PANTRY	-	1	
	DATA HALL ENTRANCE	-	1	
	ADMIN CORRIDOR	-	1	
	ELECTRICAL ROOM B	-	1	
	SERVER ROOM B	-	1	
	MMR B	-	1	
	STORAGE ROOM 3	-	1	
	CWP RISER-1	-	1	
	DUCT-5	-	1	
	VRF-3	-	1	
	CHW	-	1	
	STAIR-03	-	1	
	SPARE ROOM 02	-	1	
	GOODS LIFT LOBBY 02	-	1	
	GOODS LIFT 03/04	-	1	
	STAIR-04	-	1	
	SEVICE CORRIDOR	-	1	
	DATA HALL 2-1	-	4	
	FAN WALL 2-1A	-	2	
	FAN WALL 2-1B	-	2	
	DATA HALL 2-2	-	4	
	FAN WALL 2-2A	-	2	
	FAN WALL 2-2B	-	2	
	DATA HALL 2-3	-	4	
	FAN WALL 2-3A	-	2	
	FAN WALL 2-3B	-	2	
	DATA HALL 2-4	-	4	
	FAN WALL 1A	-	1	
	FAN WALL 1B	-	2	
	SUPER CORE 1	-	1	
	FAN WALL 2A	-	1	
	FAN WALL 2B	-	1	
	STAIR-05	-	1	
	ELV-1	-	1	
	ELE-1	-	1	
	LCWP-4	-	1	
	VRF-4	-	1	
	LCWP-5	-	1	
	DUCT-6	-	1	
	ELV-2	-	1	
	DUCT-7	-	1	
	STAIR-06	-	2	
	ELE-2	-	1	
	LCWP-6	-	1	
	VRF-5	-	1	
	DUCT-8	-	1	
	ALARM VALVE ROOM A	-	1	
	ELV-3	-	1	
	ELE-3	-	1	
	DUCT-9	-	1	
	LCWP-7	-	1	
	VRF-6	-	1	
	ELE-4	-	1	
	STAIR-07	-	2	
	DUCT-10	-	1	
	ELV-4	-	1	
	CWP RISER-2	-	2	
	ELV-5	-	1	
	ELE-5	-	1	
	ALARM VALVE ROOM B	-	1	
	DUCT-11	-	1	
	VRF-7	-	1	
	STAIR-08	-	1	
	DUCT-12	-	1	
	STAIR-09	-	1	
	EXHAUST SHAFT-1	-	1	
	EXHAUST SHAFT-2	-	1	
	EXHAUST SHAFT-3	-	1	
	EXHAUST SHAFT-4	-	1	
	STAIR-10	-	1	
	ELECTRICAL GANTRY	-	1	
	SUB TOTAL		124	

MAIN DRAWING

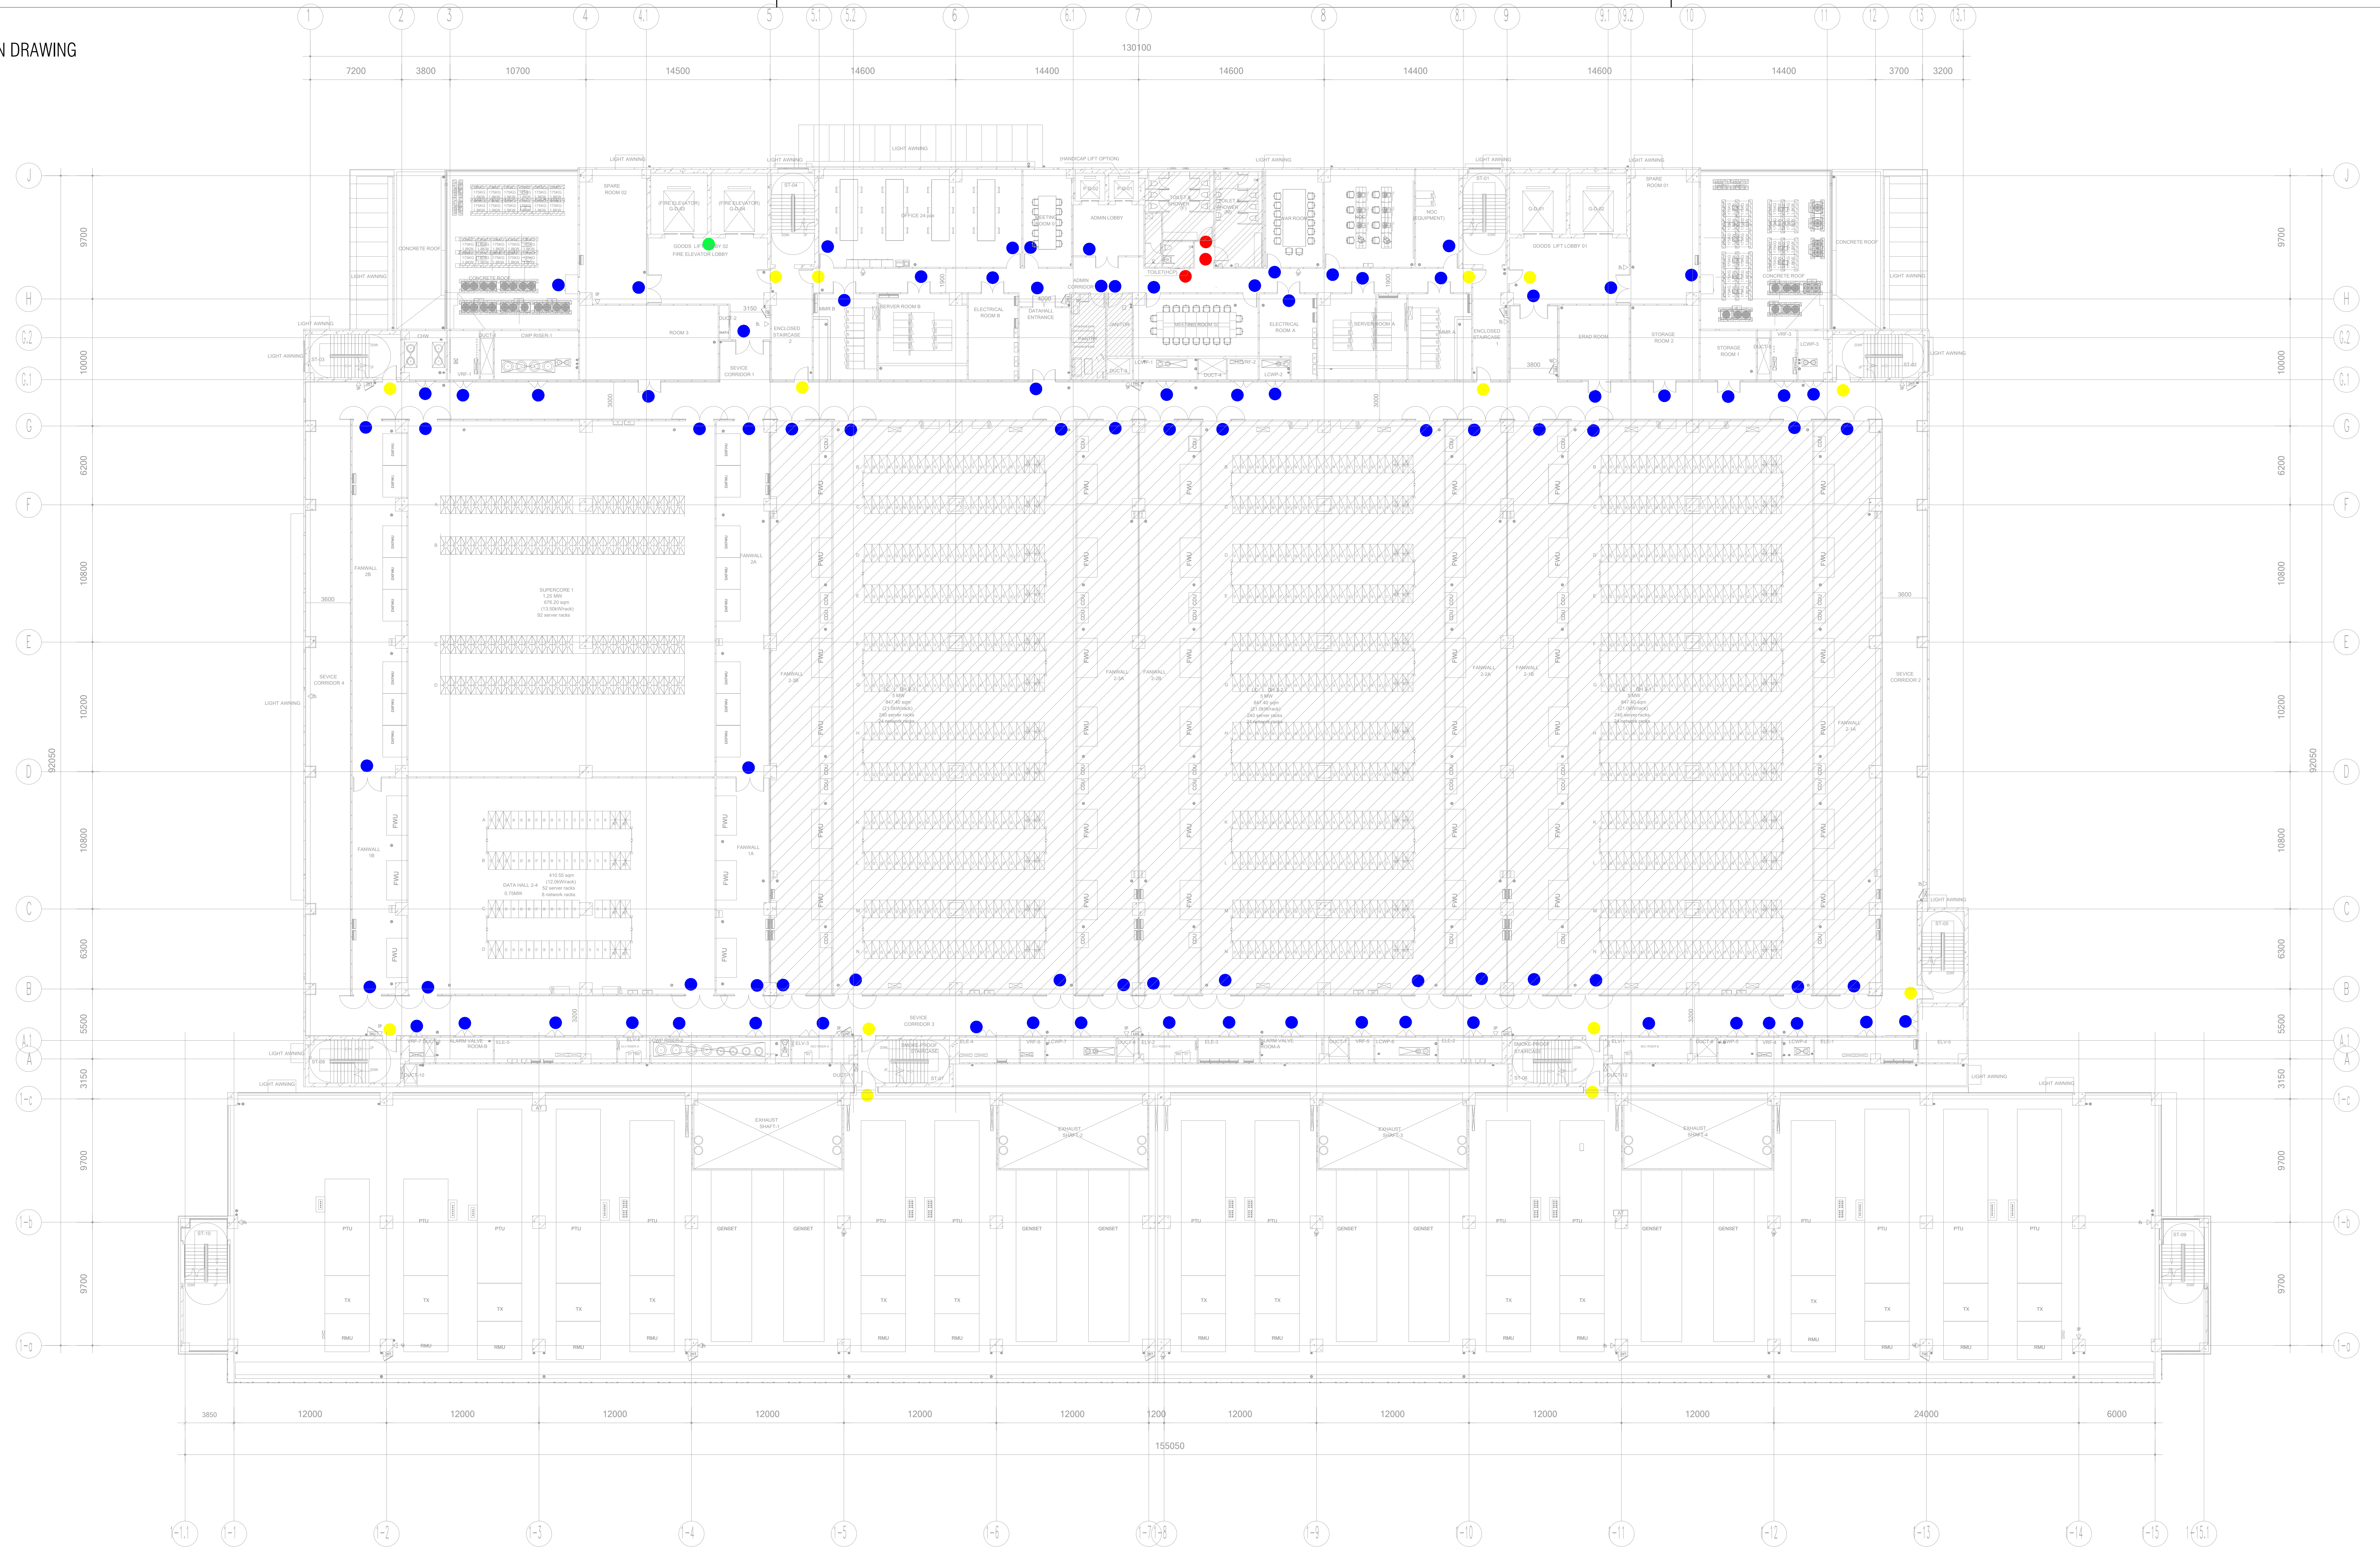
1
2
3
4
4.1
5
5.1
5.2
6
6.1
7
8
8.1
9
9.1
9.2
10
11
12
13
13.1
130100
7200
3800
10700
14500
14600
14400
14600
14400
14600
14400
14600
14400
3700
3200
J
H
G.2
G.1
G
F
E
D
C
B
A.1
A
9700
10000
6200
10800
10200
10800
6300
5500
3150
9700
9700
92050
3800
12000
12000
12000
12000
12000
12000
1200
12000
12000
12000
12000
24000
6000
155050

SIGNAGE LAYOUT-2F

SIGNAGE LAGEND	
🔴	TOILET & DISABLED DOOR SIGNAGE
🟡	STAIRCASE DOOR SIGNAGE
🔵	ROOM FACILITY SIGNAGE
🟢	FIRE LIFT SIGNAGE

CLIENT :

GULF EDGE DC 01

87 Wireless Road, M Thai Tower 11th. Floor, All Seasons Place, Lumpini,
Pathumwan, Bangkok 10330, Thailand

CONTRACTOR :

华西发展(泰国)有限公司
บริษัท หัวซือ ดีเวลลอปเม้นต์ (ประเทศไทย) จำกัด
HUASHI DEVELOPMENT CO.,LTD
No. 202, Room No. 1403, 14/F, Le Concorde Building,
Ratchadapisek Road, Huaykhwang Sub-District,
Huaykhwang District, Bangkok Metropolitan 10310.

CONSULTANT :

ARbay
บริษัท เอ อาร์ เบย์ จำกัด
ARbay Company Limited
31 st Floor Bangkok Insurance Building
25 South Sathorn road Thungmahamek
Sathorn Bangkok 10120 THAILAND
T +66 (0) 2286 8199
F +66 (0) 2286 2863
info@arbay.co.th

CONSULTANT :

Qbic Engineers & Architects Co.,Ltd.
8 Soi KALONG 4 SANAMBINNAM ROAD,
THASAI SUB-DISTRICT, MUANG NONTHABURI DISTRICT
, NONTHABURI.
Tel 662-950-4374
Fax 662-580-3231
E-Mail : qbic@qbic.co.th, www.qbic.co.th
QBIC ENGINEERS AND ARCHITECTS CO.,LTD.

CONSULTANT :

MITR
MITR TECHNICAL CONSULTANT CO.,LTD.
1168/8 12th FLOOR, LUMPINI TOWER BUILDING,
RAMA IV RD., THUNGMAHAMEK, SATHORN, BANGKOK 10120, THAILAND
TEL : 0-2679-9079-84
FAX : 0-2679-9085 E-mail: mitr_dd@mitr.com

Architect :	SIGNATURE
ประกิต พนานุรัตน์ วสถ. 580 ที่อยู่ 251/1 ถ.จารุเมือง แขวงรองเมือง เขตปทุมวัน กรุงเทพมหานคร โทรศัพท์ 02-286-8199	

Structural Engineer :	SIGNATURE
วิศวกรผู้ออกแบบโครงสร้าง	
ณัฐสม สงวนวงษ์ วย 1423 ที่อยู่ 2/1 ซ.รามคำแหง 150 ถ.รามคำแหง แขวง สะพานสูง เขต สะพานสูง กทม. 10240	

Structural Inspector :	SIGNATURE
วิศวกรผู้ตรวจสอบโครงสร้าง	
โกมล จุฑาภัทร วย 964 ที่อยู่ 24/18 ซ.นวมินทร์ 129 ถ. นวมินทร์ แขวง นวลจันทร์ เขต บึงกุ่ม กทม. 10230	

Electrical Engineer :	SIGNATURE
วิศวกรผู้ออกแบบระบบไฟฟ้ากำลัง	
นายสุภัทร บูรณวิทย์ วฟก.1265 ที่อยู่ 21 ซอยทานสัมฤทธิ 13 ตำบลท่าทราย อ.เมืองนนทบุรี จ.นนทบุรี 11000	

Mechanical Engineer :	SIGNATURE
วิศวกรผู้ออกแบบระบบเครื่องกลและปรับอากาศ	
นายประสิทธิ์ เกียวสุนทร วก.1221 ที่อยู่ 44/372 ซอยบางกระดี 35/1 แขวงแสมดำ เขตบางขุนเทียน กทม. 10150	ประสิทธิ์

Sanitary Engineer :	SIGNATURE
วิศวกรผู้ออกแบบระบบสุขาภิบาล และดับเพลิง	
นายทศวรรษ สนันฤทธิ์ วส. 215 ที่อยู่ บ้านเลขที่ 99/107 หมู่ที่ 3 ต.ศีรษะจรเข้น้อย อ.บางเสาธง จ.สมุทรปราการ 10540	ทศวรรษ

ISSUE/REVISION

REV.	DESCRIPTION	DATE
A	90% DEVELOPED	09/05/2026

PROJECT NAME :

GEDC 01

LOCATION:
Nikhom Phattana district, Rayong ,industrial estate,CPGC

BUILDING :

90% DEVELOPED

TITLE :

SIGNAGE LAYOUT-2F

JOB NO.	SCALE 1:200
DRAWN LXP	REF.
CHECKED LJC	DWG.NO. MPK01A-90-A-SN-201
APPROVED LXD	
DATE 2026.05.09	

SIGNAGE DETAIL LAYOUT

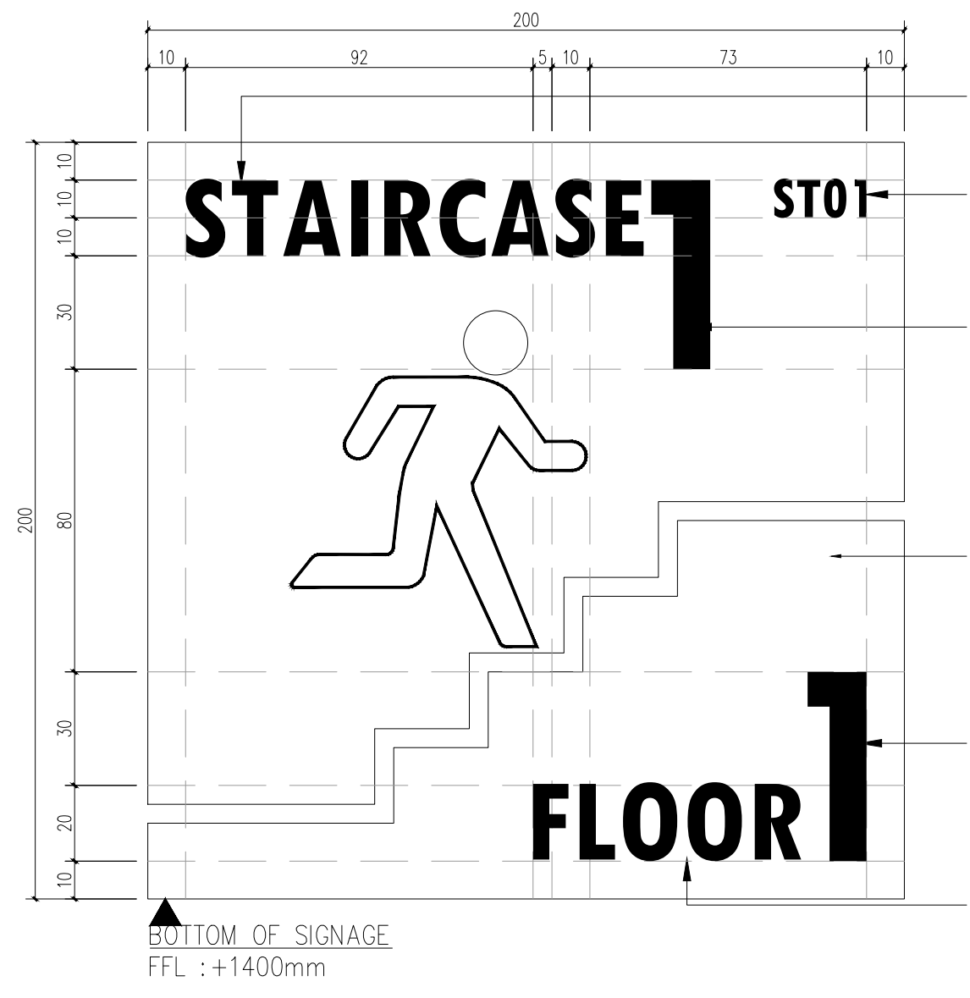

STAIRCASE DOOR NAME TEXT
FONT TYPE : TW CENT MT CONDENSED
FONT SIZE : 20mm

STAIRCASE DOOR NAME TEXT
FONT TYPE : TW CENT MT CONDENSED
FONT SIZE : 10mm

STAIRCASE DOOR NAME TEXT
FONT TYPE : TW CENT MT CONDENSED
FONT SIZE : 50mm

3mm THK CLEAR ACRYLIC BACKGROUND SPRAYED IN MAROON COLOUR TO ARCH'S APPROVAL

STAIRCASE DOOR NAME TEXT
FONT TYPE : TW CENT MT CONDENSED
FONT SIZE : 10mm

STAIRCASE DOOR NAME TEXT
FONT TYPE : TW CENT MT CONDENSED
FONT SIZE : 20mm

BOTTOM OF SIGNAGE
FFL : +1400mm

STAIRCASE / FLOOR	SIGN	QUANTITY	MATERIAL
ST1 / THIRD FLOOR	STAIRCASE 1 FLOOR 3	1	3mm TRANSPARENT ACRYLIC 140mm X 240mm with HIGH RES UV PRINT STICKER TO MATCH PANTONE NAVY BLUE
ST2 / THIRD FLOOR	STAIRCASE 2 FLOOR 3	1	
ST3 / THIRD FLOOR	STAIRCASE 3 FLOOR 3	1	
ST4 / THIRD FLOOR	STAIRCASE 4 FLOOR 3	1	
ST5 / THIRD FLOOR	STAIRCASE 5 FLOOR 3	1	

STAIRCASE / FLOOR	SIGN	QUANTITY	MATERIAL
ST6 / FIRST FLOOR	STAIRCASE 6 FLOOR 3	1	3mm TRANSPARENT ACRYLIC 140mm X 240mm with HIGH RES UV PRINT STICKER TO MATCH PANTONE NAVY BLUE
ST7 / FIRST FLOOR	STAIRCASE 7 FLOOR 3	1	
ST8 / FIRST FLOOR	STAIRCASE 8 FLOOR 3	1	
ST9 / FIRST FLOOR	STAIRCASE 9 FLOOR 3	1	
ST10 / THIRD FLOOR	STAIRCASE 10 FLOOR 3	1	

SIGNAGE DETAIL LAYOUT

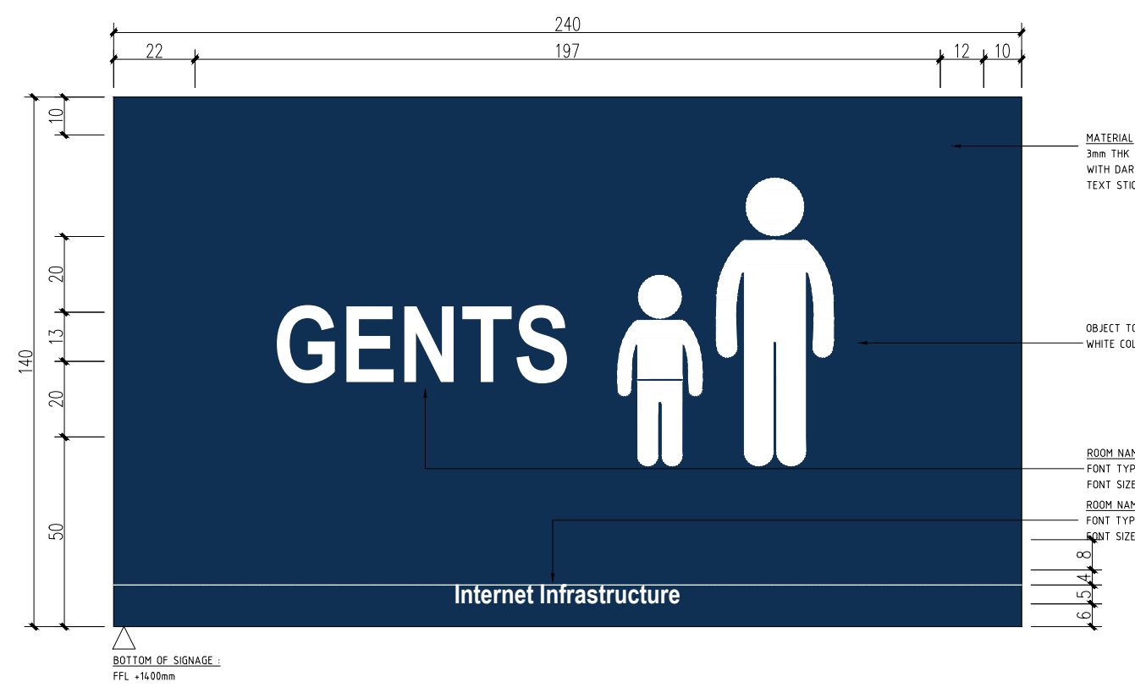

MATERIAL
3mm THK CLEAR ARCYLIC BOARD WITH DARK BLUE COLOUR AND TEXT STICKER AT BACK

OBJECT TO BE REVERSED STICKER WITH WHITE COLOUR TO ARCH'S APPROVAL

ROOM NAME TEXT
FONT TYPE : MONTSERRAT
FONT SIZE :20mm

ROOM NAME TEXT
FONT TYPE : MONTSERRAT (BOLD)
FONT SIZE : 5mm

BOTTOM OF SIGNAGE :
FFL +1400mm

<table>
<tr><th rowspan="2">LOCATION</th><th colspan="2">SIGNAGE</th><th rowspan="2">QUANTITY</th><th rowspan="2">MATERIAL</th></tr>
<tr><th>ENGLISH</th><th>THAI</th></tr>
<tr><td></td><td>TOILET(HCP)</td><td>-</td><td>1</td><td></td></tr>
<tr><td></td><td>TOILET&SHOWER(F)</td><td>-</td><td>1</td><td></td></tr>
<tr><td></td><td>TOILET&SHOWER(M)</td><td>-</td><td>1</td><td></td></tr>
<tr><td></td><td>SUB TOTAL</td><td></td><td>3</td><td></td></tr>
</table>

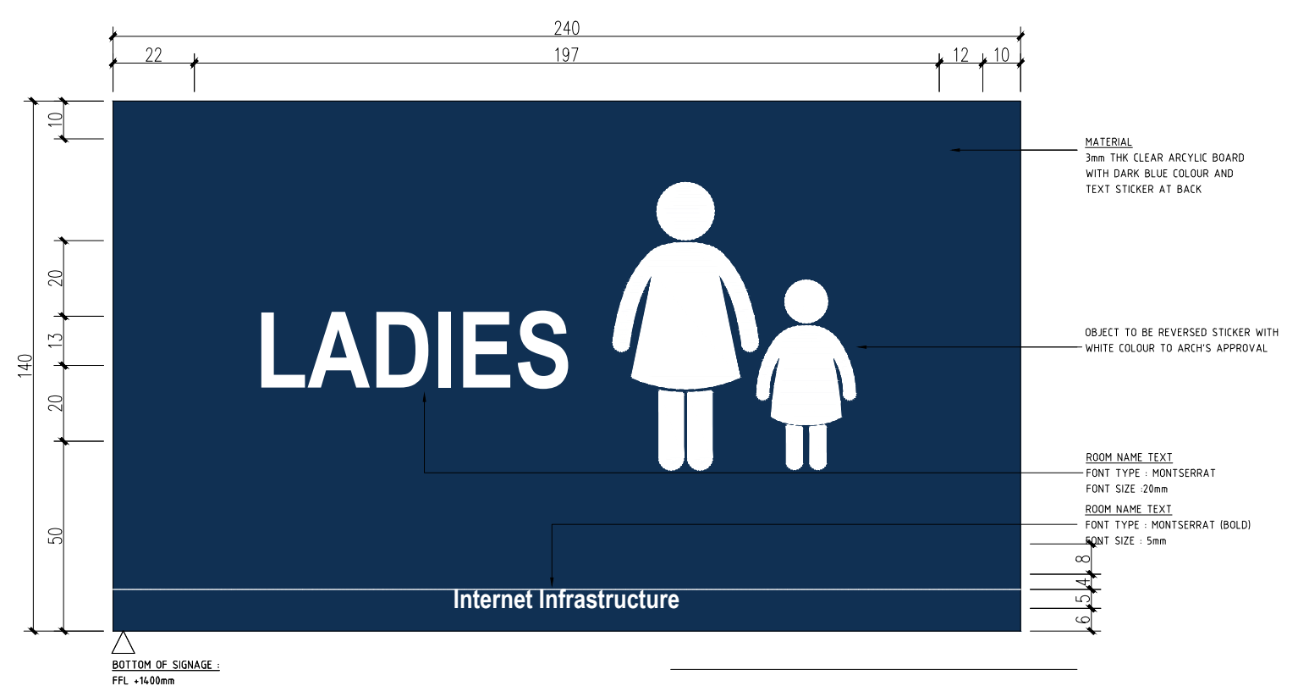

MATERIAL
3mm THK CLEAR ARCYLIC BOARD WITH DARK BLUE COLOUR AND TEXT STICKER AT BACK

OBJECT TO BE REVERSED STICKER WITH WHITE COLOUR TO ARCH'S APPROVAL

ROOM NAME TEXT
FONT TYPE : MONTSERRAT
FONT SIZE :20mm

ROOM NAME TEXT
FONT TYPE : MONTSERRAT (BOLD)
FONT SIZE : 5mm

BOTTOM OF SIGNAGE :
FFL +1400mm

SIGNAGE DETAIL LAYOUT

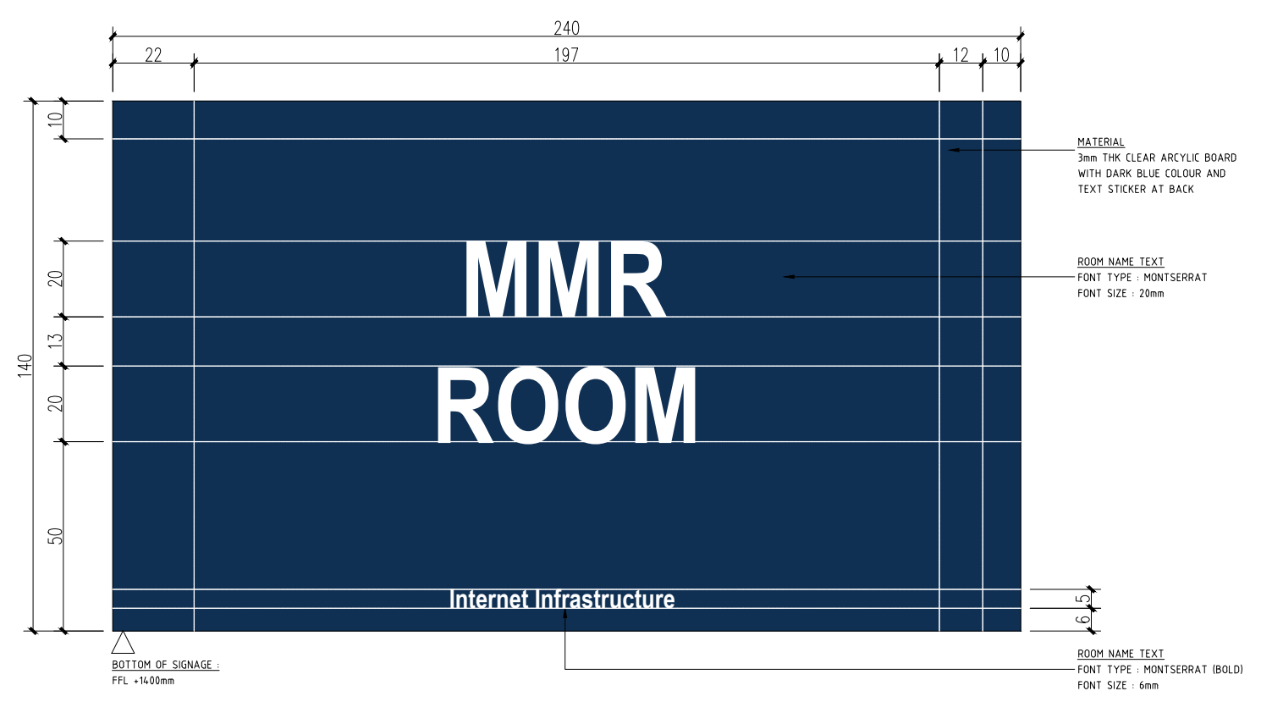

MATERIAL
3mm THK CLEAR ARCYLIC BOARD WITH DARK BLUE COLOUR AND TEXT STICKER AT BACK

ROOM NAME TEXT
FONT TYPE : MONTSERRAT
FONT SIZE : 20mm

BOTTOM OF SIGNAGE :
FFL +1400mm

ROOM NAME TEXT
FONT TYPE : MONTSERRAT (BOLD)
FONT SIZE : 6mm

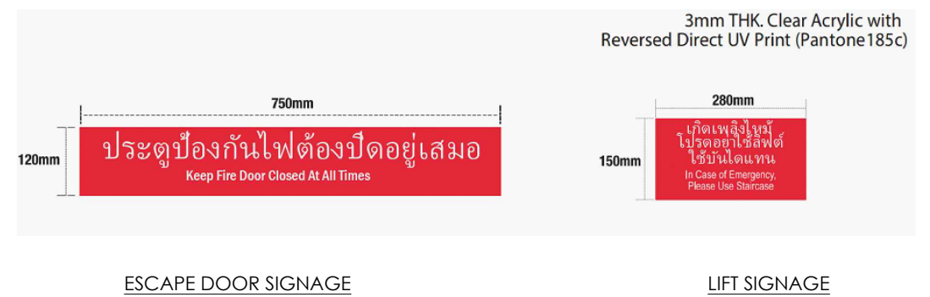
3mm THK. Clear Acrylic with
Reversed Direct UV Print (Pantone185c)

ESCAPE DOOR SIGNAGE
*The height of signage 1100mm from floor level
*Type A - Single leaf door required 2 signage (1-front & 1-rear)
*Type B - Double leaf door required 4 signage (2-front & 2-rear)

LIFT SIGNAGE

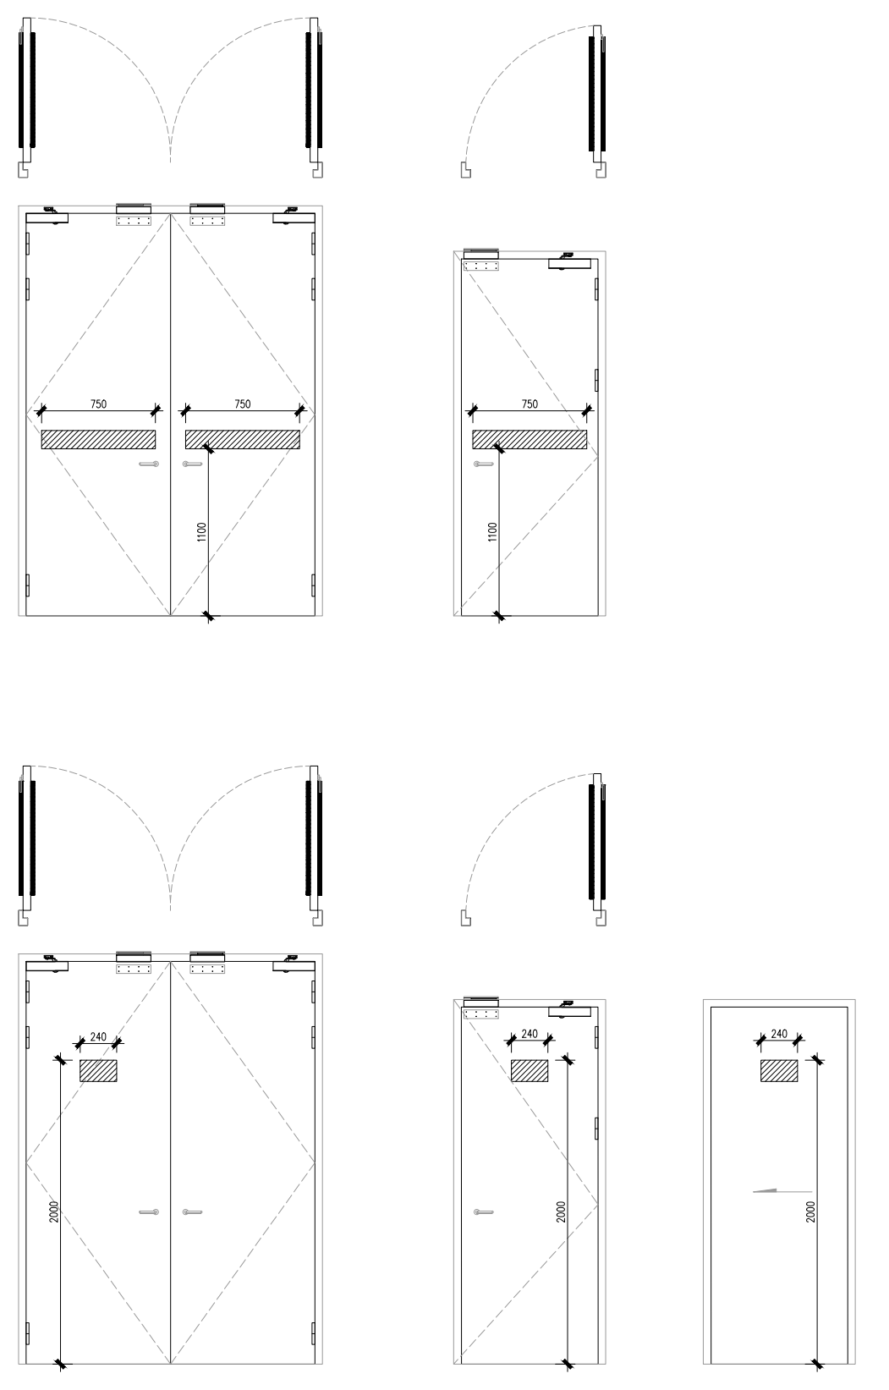

<table>
<tr><th rowspan="2">LOCATION</th><th colspan="2">SIGNAGE</th><th rowspan="2">QUANTITY</th><th rowspan="2">MATERIAL</th></tr>
<tr><th>ENGLISH</th><th>THAI</th></tr>
<tr><td></td><td>OFFICE</td><td>-</td><td>2</td><td>3mm TRANSPARENT ACRYLC 140mm X240mm with HIGH RES UV PRINT STICKER TO MATCH PANTONE NAVY BLUE</td></tr>
<tr><td></td><td>MEETING ROOM 01</td><td>-</td><td>1</td><td></td></tr>
<tr><td></td><td>PASSENGER LIFT 01/02</td><td>-</td><td>1</td><td></td></tr>
<tr><td></td><td>ADMIN LOBBY</td><td>-</td><td>1</td><td></td></tr>
<tr><td></td><td>DUCT-1</td><td>-</td><td>1</td><td></td></tr>
<tr><td></td><td>STORAGE ROOM 1</td><td>-</td><td>1</td><td></td></tr>
<tr><td></td><td>CUSTOMER STORAGE ROOM</td><td>-</td><td>1</td><td></td></tr>
<tr><td></td><td>CUSTOMER SOC</td><td>-</td><td>1</td><td></td></tr>
<tr><td></td><td>STAIR-01</td><td>-</td><td>1</td><td></td></tr>
<tr><td></td><td>GOODS LIFT 01/02</td><td>-</td><td>1</td><td></td></tr>
<tr><td></td><td>GOODS LIFT LOBBY 01</td><td>-</td><td>1</td><td></td></tr>
<tr><td></td><td>SPARE ROOM-1</td><td>-</td><td>1</td><td></td></tr>
<tr><td></td><td>STAIR-02</td><td>-</td><td>1</td><td></td></tr>
<tr><td></td><td>LCWP-1</td><td>-</td><td>1</td><td></td></tr>
<tr><td></td><td>VRF-1</td><td>-</td><td>1</td><td></td></tr>
<tr><td></td><td>DUCT-2</td><td>-</td><td>1</td><td></td></tr>
<tr><td></td><td>STORAGE ROOM 2</td><td>-</td><td>1</td><td></td></tr>
<tr><td></td><td>CUSTOMER SECURITY STORAGE ROOM</td><td>-</td><td>1</td><td></td></tr>
<tr><td></td><td>CUSTOMER ERAD ROOM</td><td>-</td><td>1</td><td></td></tr>
<tr><td></td><td>MMR A</td><td>-</td><td>1</td><td></td></tr>
<tr><td></td><td>SERVER ROOM A</td><td>-</td><td>1</td><td></td></tr>
<tr><td></td><td>ELECTRICAL ROOM A</td><td>-</td><td>1</td><td></td></tr>
<tr><td></td><td>MEETING ROOM 02</td><td>-</td><td>2</td><td></td></tr>
<tr><td></td><td>LCWP-2</td><td>-</td><td>1</td><td></td></tr>
<tr><td></td><td>VRF-2</td><td>-</td><td>1</td><td></td></tr>
<tr><td></td><td>DUCT-3</td><td>-</td><td>1</td><td></td></tr>
<tr><td></td><td>LCWP-3</td><td>-</td><td>1</td><td></td></tr>
<tr><td></td><td>DUCT-4</td><td>-</td><td>1</td><td></td></tr>
<tr><td></td><td>JANITOR</td><td>-</td><td>1</td><td></td></tr>
<tr><td></td><td>PANTRY</td><td>-</td><td>1</td><td></td></tr>
<tr><td></td><td>DATA HALL ENTRANCE</td><td>-</td><td>1</td><td></td></tr>
<tr><td></td><td>ADMIN CORRIDOR</td><td>-</td><td>1</td><td></td></tr>
<tr><td></td><td>ELECTRIAL ROOM B</td><td>-</td><td>1</td><td></td></tr>
<tr><td></td><td>SEVER ROOM B</td><td>-</td><td>1</td><td></td></tr>
<tr><td></td><td>MMR B</td><td>-</td><td>1</td><td></td></tr>
<tr><td></td><td>CUSTOMER SEVER ROOM</td><td>-</td><td>1</td><td></td></tr>
<tr><td></td><td>CWP RISER-1</td><td>-</td><td>1</td><td></td></tr>
<tr><td></td><td>DUCT-5</td><td>-</td><td>1</td><td></td></tr>
<tr><td></td><td>VRF-3</td><td>-</td><td>1</td><td></td></tr>
<tr><td></td><td>CHW</td><td>-</td><td>1</td><td></td></tr>
<tr><td></td><td>STAIR-03</td><td>-</td><td>1</td><td></td></tr>
<tr><td></td><td>SPARE ROOM-2</td><td>-</td><td>1</td><td></td></tr>
<tr><td></td><td>GOODS LIFT LOBBY 02</td><td>-</td><td>1</td><td></td></tr>
<tr><td></td><td>GOODS LIFT 03/04</td><td>-</td><td>1</td><td></td></tr>
<tr><td></td><td>STAIR-04</td><td>-</td><td>1</td><td></td></tr>
<tr><td></td><td>SEVICE CORRIDOR</td><td>-</td><td>1</td><td></td></tr>
<tr><td></td><td>DATA HALL 3-1</td><td>-</td><td>4</td><td></td></tr>
<tr><td></td><td>FAN WALL 3-1A</td><td>-</td><td>2</td><td></td></tr>
<tr><td></td><td>FAN WALL 3-1B</td><td>-</td><td>2</td><td></td></tr>
<tr><td></td><td>DATA HALL 3-2</td><td>-</td><td>4</td><td></td></tr>
<tr><td></td><td>FAN WALL 3-2A</td><td>-</td><td>2</td><td></td></tr>
<tr><td></td><td>FAN WALL 3-2B</td><td>-</td><td>2</td><td></td></tr>
<tr><td></td><td>DATA HALL 3-3</td><td>-</td><td>4</td><td></td></tr>
<tr><td></td><td>FAN WALL 3-3A</td><td>-</td><td>2</td><td></td></tr>
<tr><td></td><td>FAN WALL 3-3B</td><td>-</td><td>2</td><td></td></tr>
<tr><td></td><td>DATA HALL 3-4</td><td>-</td><td>4</td><td></td></tr>
<tr><td></td><td>FAN WALL 3-4A</td><td>-</td><td>2</td><td></td></tr>
<tr><td></td><td>FAN WALL 3-4B</td><td>-</td><td>2</td><td></td></tr>
<tr><td></td><td>STAIR-05</td><td>-</td><td>1</td><td></td></tr>
<tr><td></td><td>ELV-1</td><td>-</td><td>1</td><td></td></tr>
<tr><td></td><td>ELE-1</td><td>-</td><td>1</td><td></td></tr>
<tr><td></td><td>LCWP-4</td><td>-</td><td>1</td><td></td></tr>
<tr><td></td><td>VRF-4</td><td>-</td><td>1</td><td></td></tr>
<tr><td></td><td>LCWP-5</td><td>-</td><td>1</td><td></td></tr>
<tr><td></td><td>DUCT-6</td><td>-</td><td>1</td><td></td></tr>
<tr><td></td><td>ELV-2</td><td>-</td><td>1</td><td></td></tr>
<tr><td></td><td>DUCT-7</td><td>-</td><td>1</td><td></td></tr>
<tr><td></td><td>STAIR-06</td><td>-</td><td>2</td><td></td></tr>
<tr><td></td><td>ELE-2</td><td>-</td><td>1</td><td></td></tr>
<tr><td></td><td>LCWP-6</td><td>-</td><td>1</td><td></td></tr>
<tr><td></td><td>VRF-5</td><td>-</td><td>1</td><td></td></tr>
<tr><td></td><td>DUCT-8</td><td>-</td><td>1</td><td></td></tr>
<tr><td></td><td>ALARM VALVE ROOM A</td><td>-</td><td>1</td><td></td></tr>
<tr><td></td><td>ELV-3</td><td>-</td><td>1</td><td></td></tr>
<tr><td></td><td>ELE-3</td><td>-</td><td>1</td><td></td></tr>
<tr><td></td><td>DUCT-9</td><td>-</td><td>1</td><td></td></tr>
<tr><td></td><td>LCWP-7</td><td>-</td><td>1</td><td></td></tr>
<tr><td></td><td>VRF-6</td><td>-</td><td>1</td><td></td></tr>
<tr><td></td><td>ELE-4</td><td>-</td><td>1</td><td></td></tr>
<tr><td></td><td>STAIR-07</td><td>-</td><td>2</td><td></td></tr>
<tr><td></td><td>DUCT-10</td><td>-</td><td>1</td><td></td></tr>
<tr><td></td><td>ELV-4</td><td>-</td><td>1</td><td></td></tr>
<tr><td></td><td>CWP RISER-2</td><td>-</td><td>2</td><td></td></tr>
<tr><td></td><td>ELV-5</td><td>-</td><td>1</td><td></td></tr>
<tr><td></td><td>ELE-5</td><td>-</td><td>1</td><td></td></tr>
<tr><td></td><td>ALARM VALVE ROOM B</td><td>-</td><td>1</td><td></td></tr>
<tr><td></td><td>DUCT-11</td><td>-</td><td>1</td><td></td></tr>
<tr><td></td><td>VRF-7</td><td>-</td><td>1</td><td></td></tr>
<tr><td></td><td>STAIR-08</td><td>-</td><td>1</td><td></td></tr>
<tr><td></td><td>DUCT-12</td><td>-</td><td>1</td><td></td></tr>
<tr><td></td><td>STAIR-09</td><td>-</td><td>1</td><td></td></tr>
<tr><td></td><td>EXHAUST SHAFT-1</td><td>-</td><td>1</td><td></td></tr>
<tr><td></td><td>EXHAUST SHAFT-2</td><td>-</td><td>1</td><td></td></tr>
<tr><td></td><td>EXHAUST SHAFT-3</td><td>-</td><td>1</td><td></td></tr>
<tr><td></td><td>EXHAUST SHAFT-4</td><td>-</td><td>1</td><td></td></tr>
<tr><td></td><td>STAIR-10</td><td>-</td><td>1</td><td></td></tr>
<tr><td></td><td>ELECTRICAL GANTRY</td><td>-</td><td>1</td><td></td></tr>
<tr><td></td><td>SUB TOTAL</td><td></td><td>122</td><td></td></tr>
</table>

MAIN DRAWING

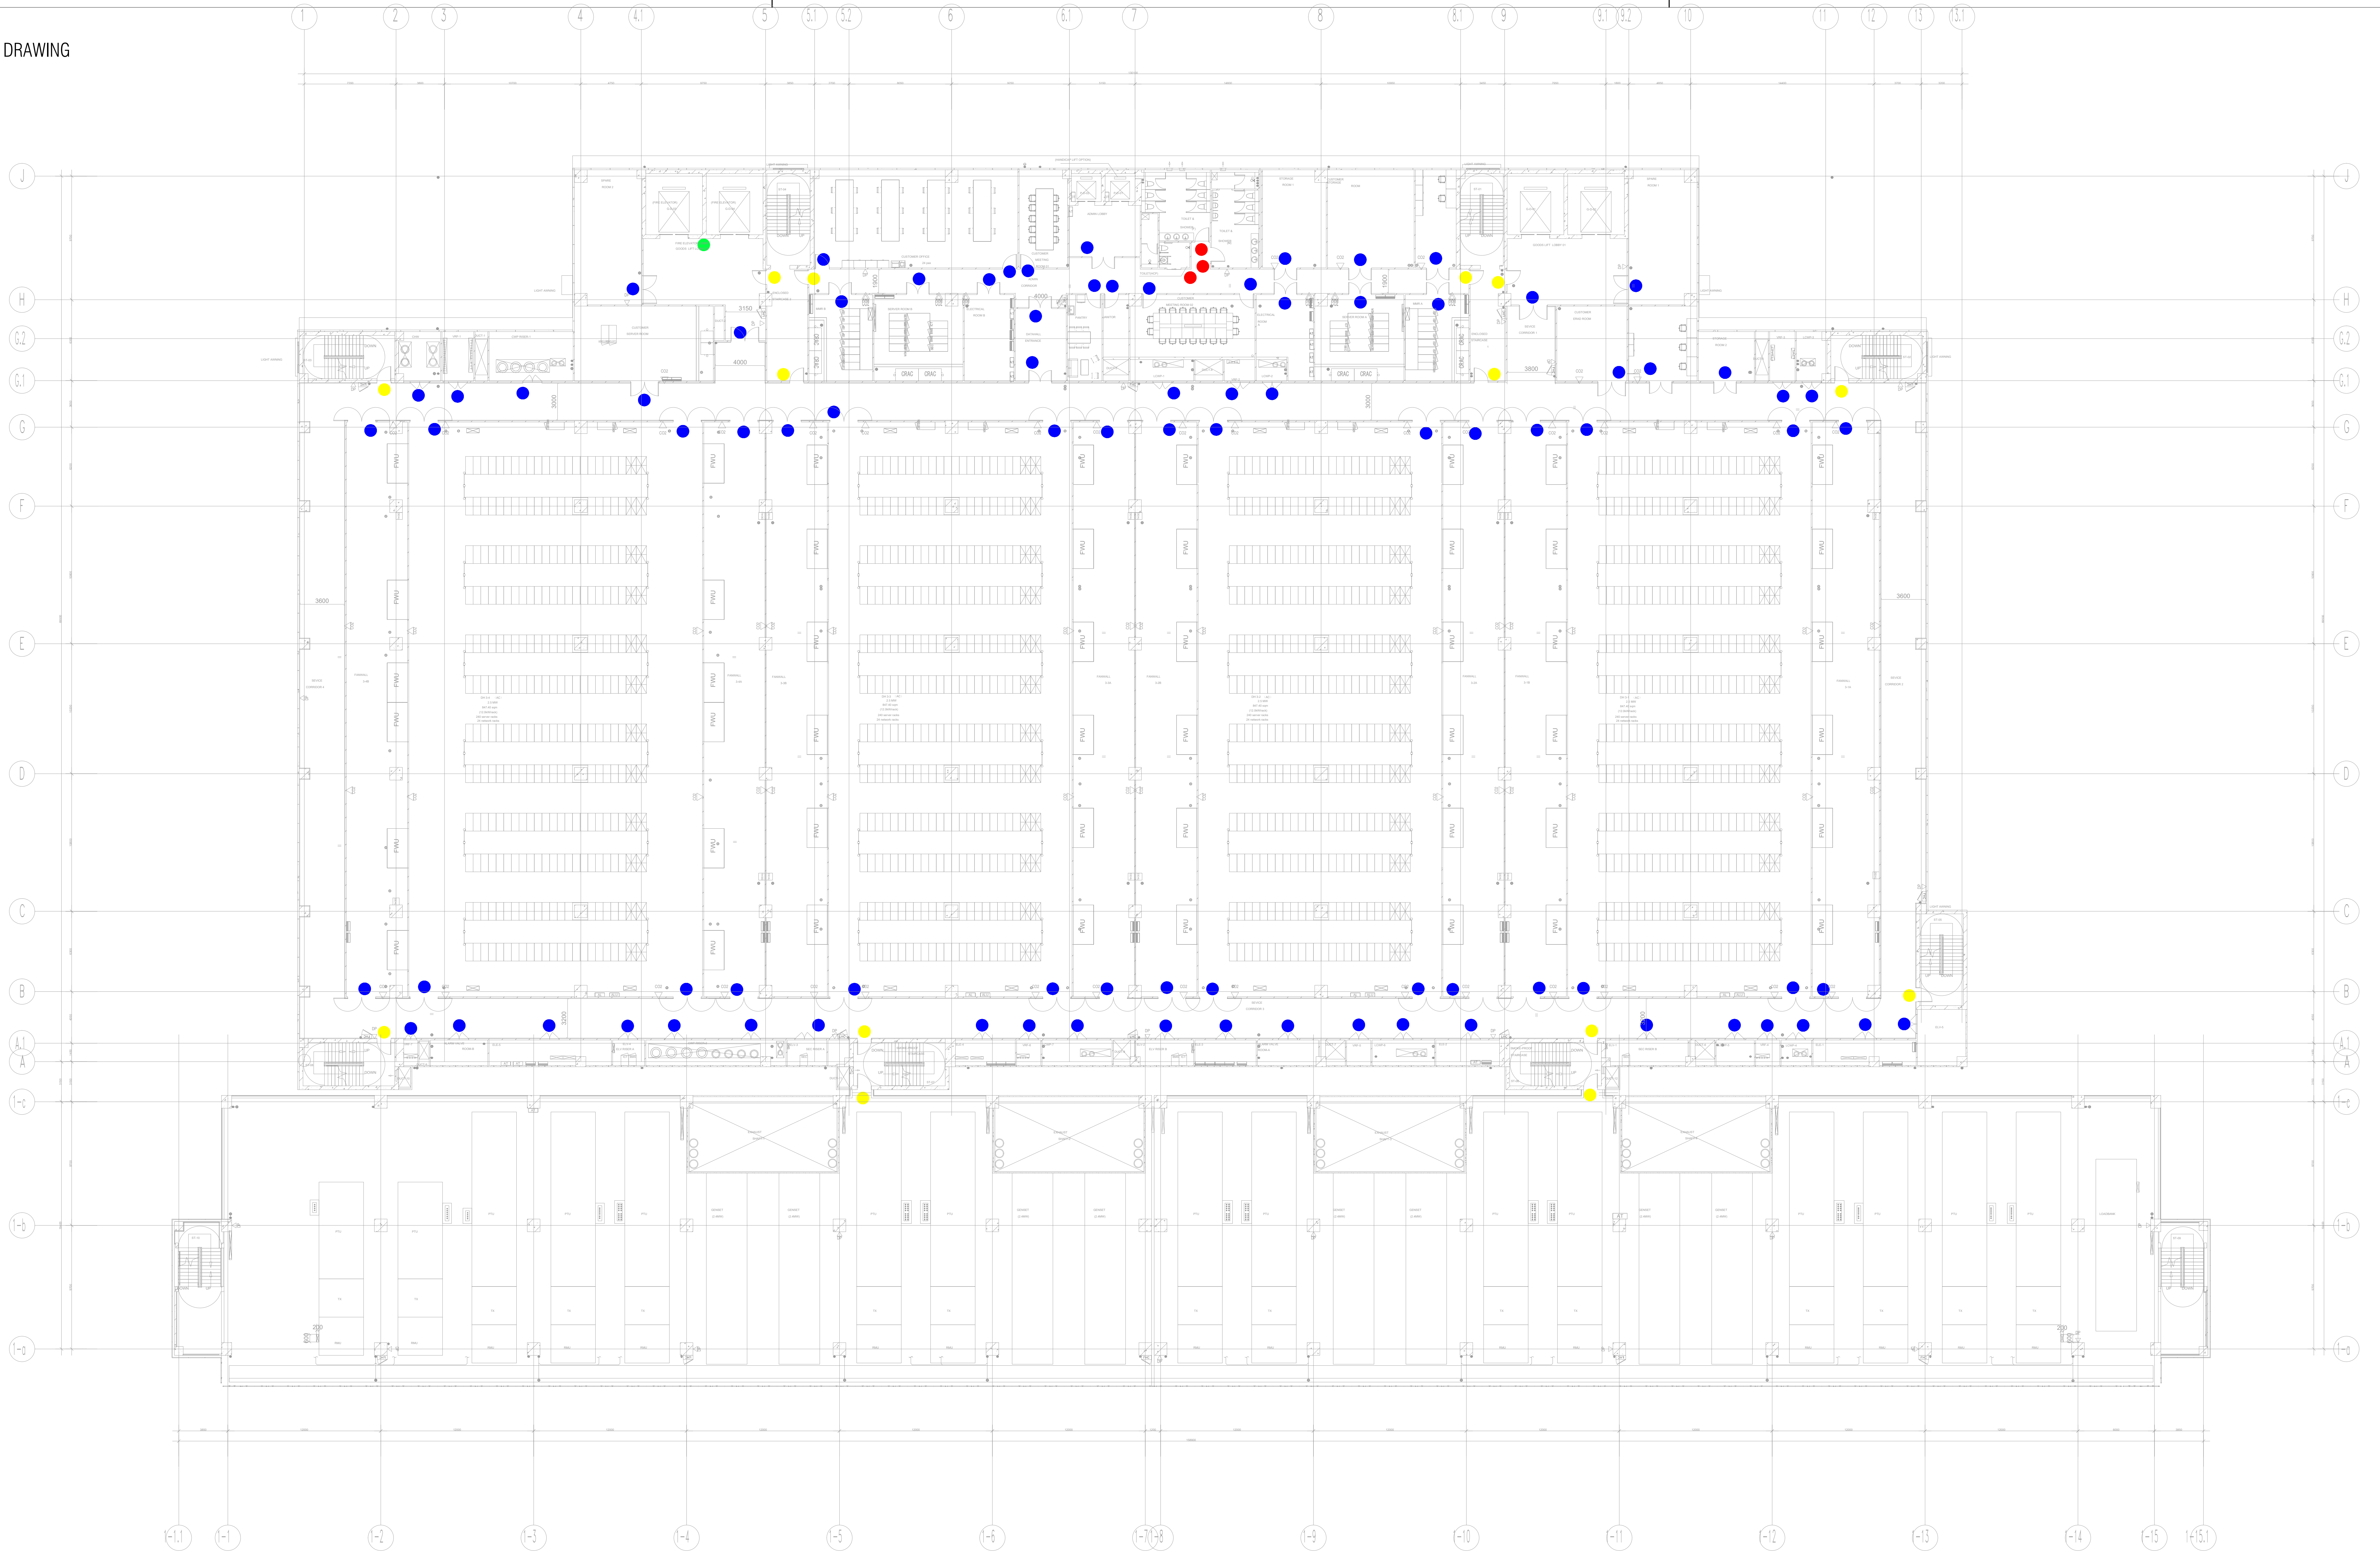

SIGNAGE LAGEND	
🔴	TOILET & DISABLED DOOR SIGNAGE
🟡	STAIRCASE DOOR SIGNAGE
🔵	ROOM FACILITY SIGNAGE
🟢	FIRE LIFT SIGNAGE

SIGNAGE LAYOUT-3F

CLIENT :

GULF EDGE DC 01

87 Wireless Road, M Thai Tower 11th. Floor, All Seasons Place, Lumpini,
Pathumwan, Bangkok 10330, Thailand

CONTRACTOR :

华西发展(泰国)有限公司
บริษัท หัวซือ ดีเวลลอปเม้นต์ (ประเทศไทย) จำกัด
HUASHI DEVELOPMENT CO.,LTD
No. 202, Room No. 1403, 14/F, Le Concorde Building,
Ratchadapisek Road, Huaykhwang Sub-District,
Huaykhwang District, Bangkok Metropolitan 10310.

CONSULTANT :

ARbay
บริษัท เอ อาร์ เบย์ จำกัด
ARbay Company Limited
31 st Floor Bangkok Insurance Building
25 South Sathorn road Thungmahamek
Sathorn Bangkok 10120 THAILAND
T +66 (0) 2286 8199
F +66 (0) 2286 2863
info@arbay.co.th

CONSULTANT :

Qbic Engineers & Architects Co.,Ltd.
8 Soi KALONG 4 SANAMBINNAM ROAD,
THASAI SUB-DISTRICT, MUANG NONTHABURI DISTRICT
, NONTHABURI.
Tel 662-950-4374
Fax 662-580-3231
E-Mail : qbic@qbic.co.th, www.qbic.co.th
QBIC ENGINEERS AND ARCHITECTS CO.,LTD.

CONSULTANT :

MITR
MITR TECHNICAL CONSULTANT CO.,LTD.
1168/8 12th FLOOR, LUMPINI TOWER BUILDING,
RAMA IV RD., THUNGMAHAMEK, SATHORN, BANGKOK 10120, THAILAND
TEL : 0-2679-9079-84
FAX : 0-2679-9085 E-mail: mitr_dd@mitr.com

Architect :	SIGNATURE
ประกิต พนานุรัตน์ วสถ. 580 ที่อยู่ 251/1 ถ.จารุเมือง แขวงรองเมือง เขตปทุมวัน กรุงเทพมหานคร โทรศัพท์ 02-286-8199	
Structural Engineer :	SIGNATURE
วิศวกรผู้ออกแบบโครงสร้าง	
ณัฐสม สงวนวงษ์ วย 1423 ที่อยู่ 2/1 ซ.รามคำแหง 150 ถ.รามคำแหง แขวง สะพานสูง เขต สะพานสูง กทม. 10240	ณัฐสม สงวนวงษ์
Structural Inspector :	SIGNATURE
วิศวกรผู้ตรวจสอบโครงสร้าง	
โกมล จุฑาภัทร วย 964 ที่อยู่ 24/18 ซ.นวมินทร์ 129 ถ. นวมินทร์ แขวง นวลจันทร์ เขต บึงกุ่ม กทม. 10230	
Electrical Engineer :	SIGNATURE
วิศวกรผู้ออกแบบระบบไฟฟ้ากำลัง	
นายสุภัทร บูรณวิทย์ วฟก.1265 ที่อยู่ 21 ซอยทานสัมฤทธิ 13 ตำบลท่าทราย อ.เมืองนนทบุรี จ.นนทบุรี 11000	
Mechanical Engineer :	SIGNATURE
วิศวกรผู้ออกแบบระบบเครื่องกลและปรับอากาศ	
นายประสิทธิ์ เกียวสุนทร วก.1221 ที่อยู่ 44/372 ซอยบางกระดี 35/1 แขวงแสมดำ เขตบางขุนเทียน กทม. 10150	ประสิทธิ์
Sanitary Engineer :	SIGNATURE
วิศวกรผู้ออกแบบระบบสุขาภิบาล และดับเพลิง	
นายทศวรรษ สนันฤทธิ์ วส. 215 ที่อยู่ บ้านเลขที่ 99/107 หมู่ที่ 3 ต.ศีรษะจรเข้น้อย อ.บางเสาธง จ.สมุทรปราการ 10540	ทศวรรษ

ISSUE/REVISION

REV.	DESCRIPTION	DATE
A	90% DEVELOPED	09/05/2026

PROJECT NAME :

GEDC 01

LOCATION:
Nikhom Phattana district, Rayong ,industrial estate,CPGC

BUILDING :

90% DEVELOPED

TITLE :

SIGNAGE LAYOUT-3F

JOB NO.	SCALE 1:200
DRAWN LXP	REF.
CHECKED LJC	DWG.NO. MPK01A-90-A-SN-301
APPROVED LXD	
DATE 2026.05.09	

SIGNAGE DETAIL LAYOUT

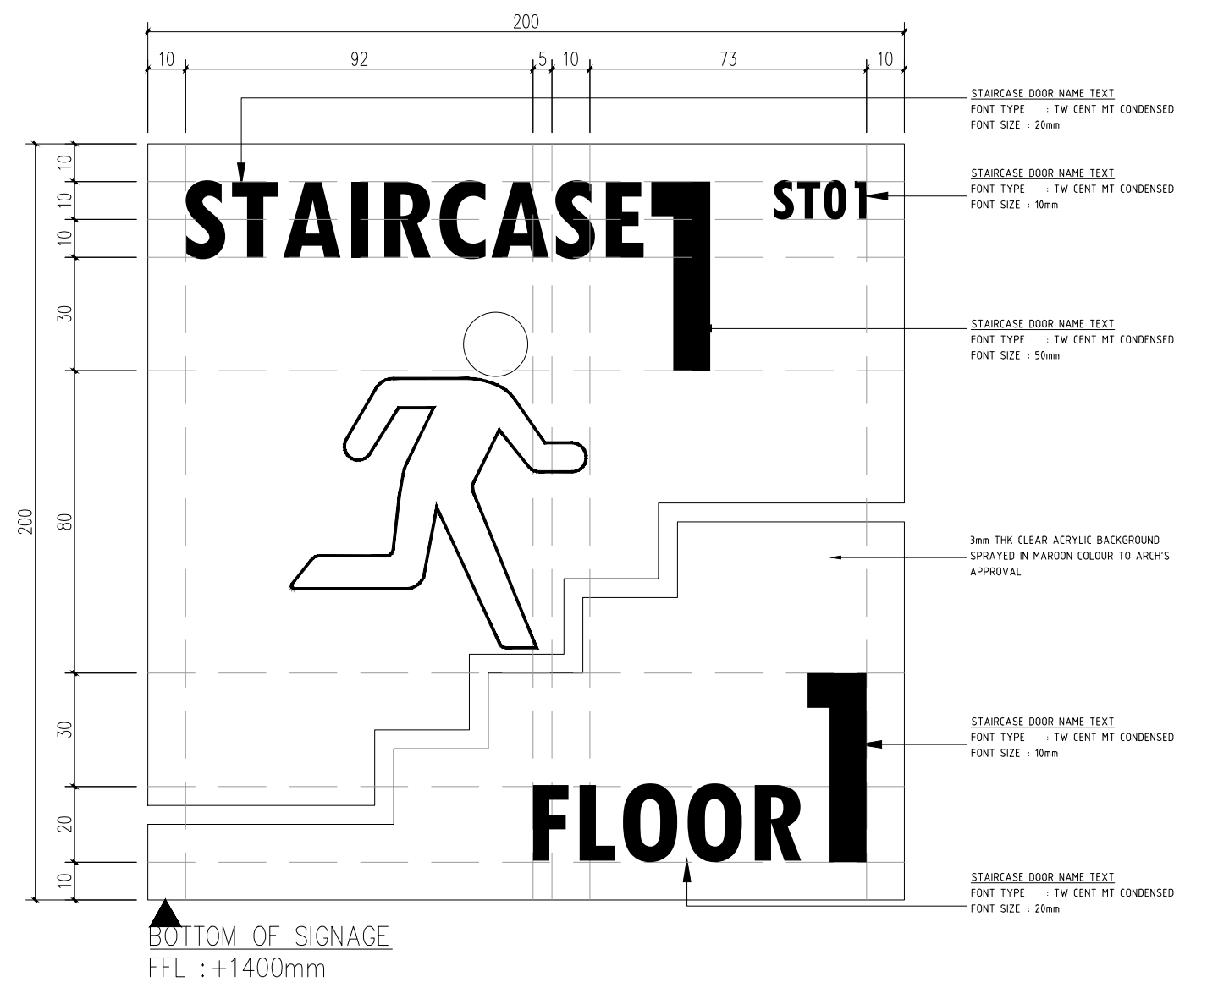
200
10
92
5
10
73
10
STAIRCASE 1
ST01
FLOOR 1
10
10
10
30
80
30
20
10
200

STAIRCASE DOOR NAME TEXT
FONT TYPE : TW CENT MT CONDENSED
FONT SIZE : 20mm

STAIRCASE DOOR NAME TEXT
FONT TYPE : TW CENT MT CONDENSED
FONT SIZE : 10mm

STAIRCASE DOOR NAME TEXT
FONT TYPE : TW CENT MT CONDENSED
FONT SIZE : 50mm

3mm THK CLEAR ACRYLIC BACKGROUND SPRAYED IN MAROON COLOUR TO ARCH'S APPROVAL

STAIRCASE DOOR NAME TEXT
FONT TYPE : TW CENT MT CONDENSED
FONT SIZE : 10mm

STAIRCASE DOOR NAME TEXT
FONT TYPE : TW CENT MT CONDENSED
FONT SIZE : 20mm

BOTTOM OF SIGNAGE
FFL :+1400mm

STAIRCASE / FLOOR	SIGN	QUANTITY	MATERIAL
ST1 / ROOF FLOOR	STAIRCASE 1 FLOOR 4	1	3mm TRANSPARENT ACRYLIC 140mm X 240mm with HIGH RES UV PRINT STICKER TO MATCH PANTONE NAVY BLUE
ST2 / ROOF FLOOR	STAIRCASE 2 FLOOR 4	1	
ST3 / ROOF FLOOR	STAIRCASE 3 FLOOR 4	1	
ST4 / ROOF FLOOR	STAIRCASE 4 FLOOR 4	1	
ST5 / ROOF FLOOR	STAIRCASE 5 FLOOR 4	1	

STAIRCASE / FLOOR	SIGN	QUANTITY	MATERIAL
ST6 / ROOF FLOOR	STAIRCASE 6 FLOOR 4	1	3mm TRANSPARENT ACRYLIC 140mm X 240mm with HIGH RES UV PRINT STICKER TO MATCH PANTONE NAVY BLUE
ST7 / ROOF FLOOR	STAIRCASE 7 FLOOR 4	1	
ST8 / ROOF FLOOR	STAIRCASE 8 FLOOR 4	1	
ST9 / ROOF FLOOR	STAIRCASE 9 FLOOR 4	1	
ST10 / ROOF FLOOR	STAIRCASE 10 FLOOR 4	1	

SIGNAGE DETAIL LAYOUT

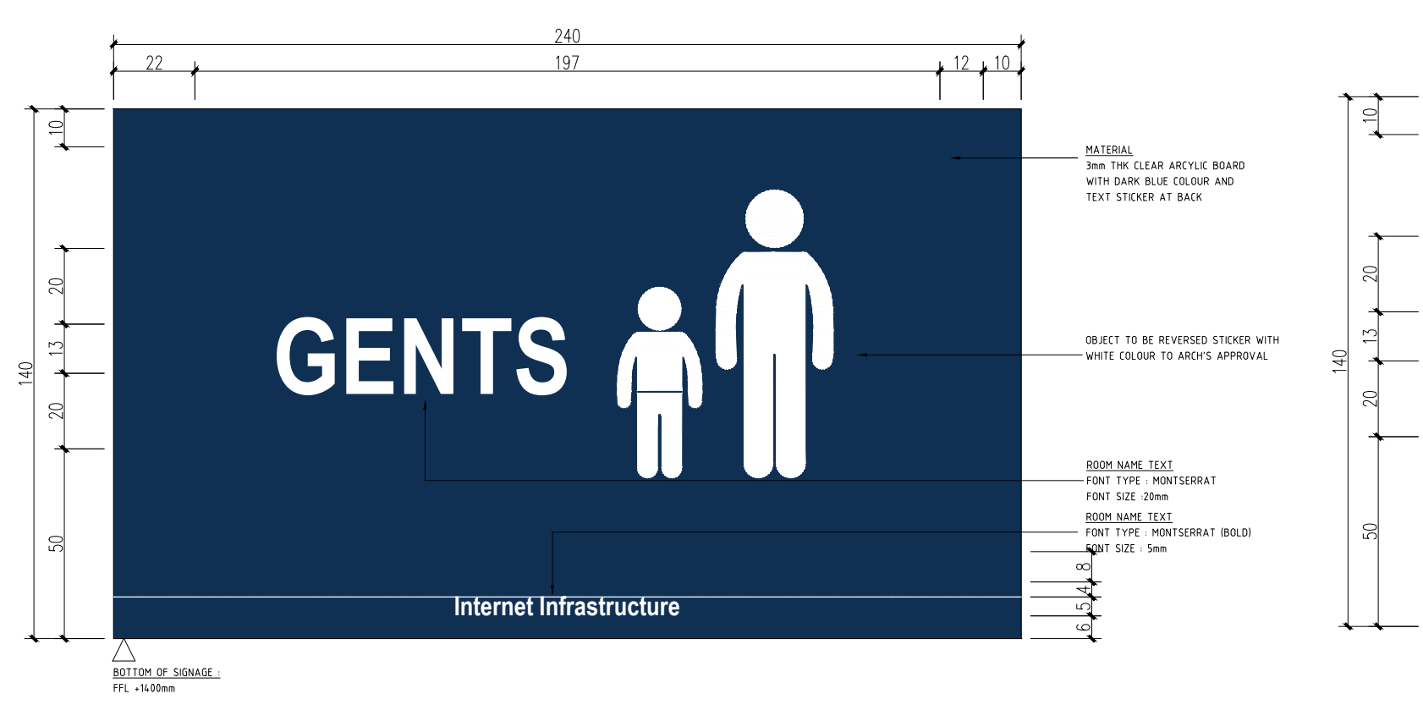
240
197
12
10
GENTS
Internet Infrastructure
140
10
20
13
20
50
8
4
5
6

MATERIAL
3mm THK CLEAR ARCYLIC BOARD WITH DARK BLUE COLOUR AND TEXT STICKER AT BACK

OBJECT TO BE REVERSED STICKER WITH WHITE COLOUR TO ARCH'S APPROVAL

ROOM NAME TEXT
FONT TYPE : MONTSERRAT
FONT SIZE :20mm

ROOM NAME TEXT
FONT TYPE : MONTSERRAT (BOLD)
FONT SIZE : 5mm

BOTTOM OF SIGNAGE :
FFL +1400mm

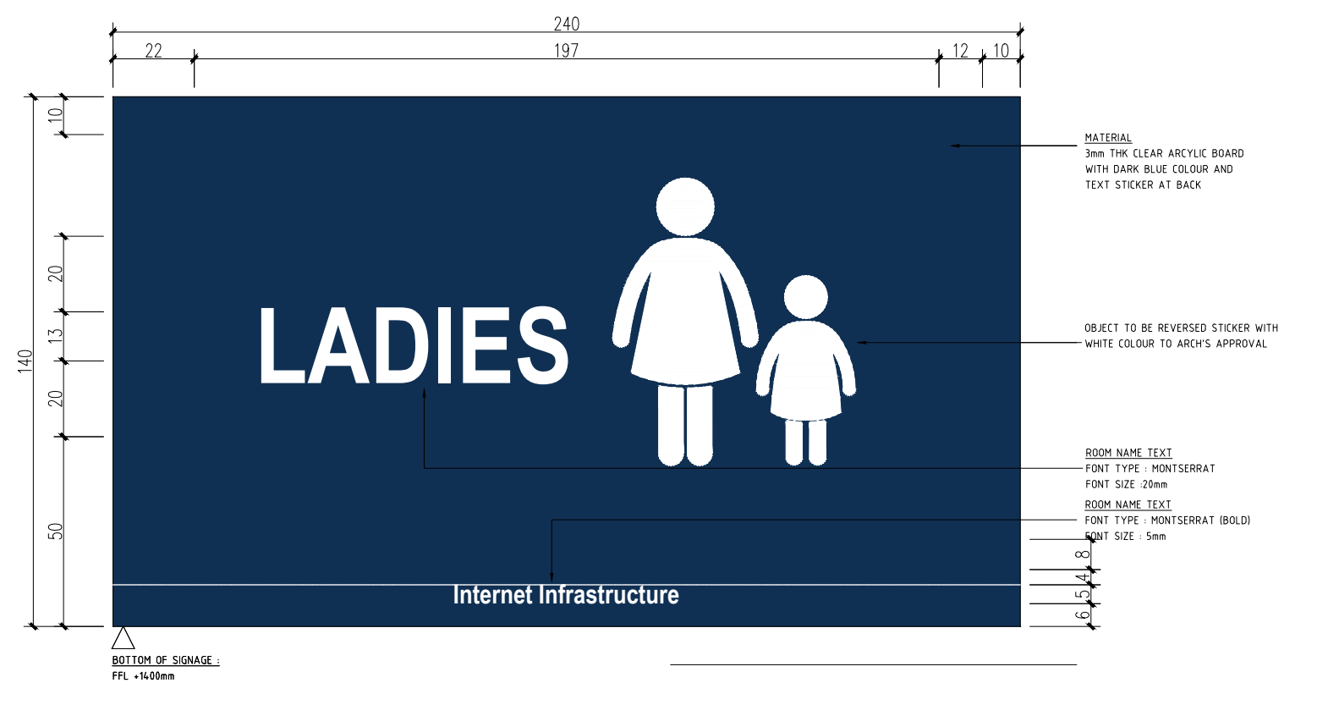
240
197
22
12
10
LADIES
Internet Infrastructure
140
10
20
13
20
50

BOTTOM OF SIGNAGE :
FFL +1400mm

SIGNAGE DETAIL LAYOUT

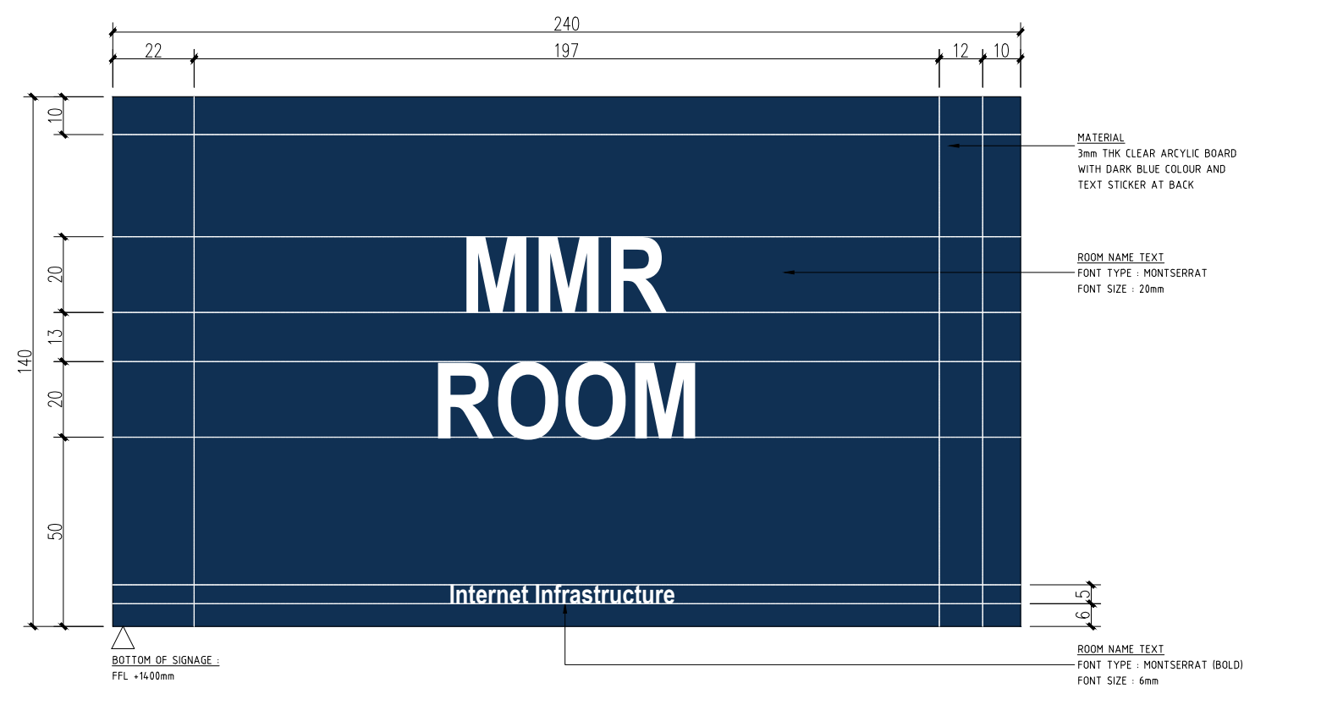
240
197
22
12
10
MMR ROOM
Internet Infrastructure
140
10
20
13
20
50
5
6

MATERIAL
3mm THK CLEAR ARCYLIC BOARD WITH DARK BLUE COLOUR AND TEXT STICKER AT BACK

ROOM NAME TEXT
FONT TYPE : MONTSERRAT
FONT SIZE : 20mm

ROOM NAME TEXT
FONT TYPE : MONTSERRAT (BOLD)
FONT SIZE : 6mm

BOTTOM OF SIGNAGE :
FFL +1400mm

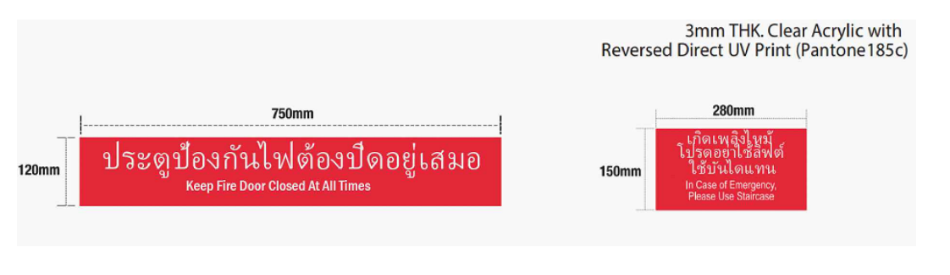
3mm THK. Clear Acrylic with
Reversed Direct UV Print (Pantone185c)
750mm
120mm
ประตูป้องกันไฟต้องปิดอยู่เสมอ
Keep Fire Door Closed At All Times
280mm
150mm
เกิดเพลิงไหม้ โปรดอย่าใช้ลิฟต์ ใช้บันไดแทน
In Case of Emergency, Please Use Staircase

ESCAPE DOOR SIGNAGE
*The height of signage 1100mm from floor level
*Type A - Single leaf door required 2 signage (1-front & 1-rear)
*Type B - Double leaf door required 4 signage (2-front & 2-rear)

LIFT SIGNAGE

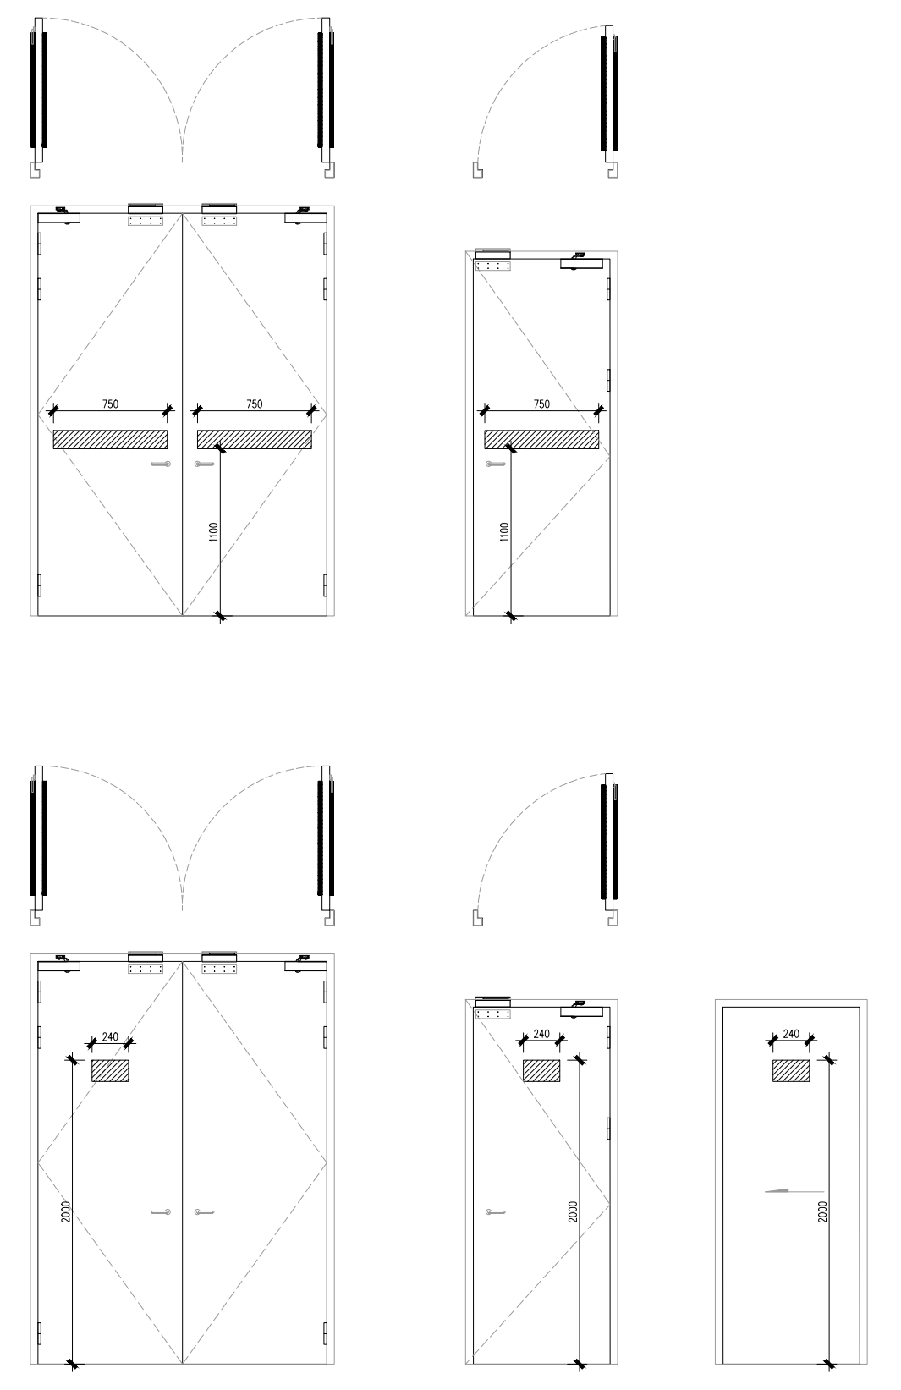
750
240
2000

LOCATION	SIGNAGE		QUANTITY	MATERIAL
	ENGLISH	THAI		
	LIQUID WATER PUMP ROOM 1	-	1	3mm TRANSPARENT ACRYLC 140mm X240mm with HIGH RES UV PRINT STICKER TO MATCH PANTONE NAVY BLUE
	LIQUID WATER PUMP ROOM 2	-	1	
	STAIR-01	-	1	
	GOODS LIFT 01/02	-	1	
	GOODS LIFT LOBBY 01	-	1	
	STAIR-02	-	1	
	LCWP-1	-	1	
	ELV-1	-	1	
	ELE-1	-	1	
	LCWP-2	-	1	
	LCWP-3	-	1	
	ELE-2	-	1	
	ELV-2	-	1	
	CWP RISER-1	-	1	
	STAIR-03	-	1	
	GOODS LIFT LOBBY 02	-	1	
	GOODS LIFT 03/04	-	1	
	STAIR-04	-	1	
	STAIR-05	-	1	
	ELV-3	-	1	
	ELE-3	-	1	
	LCWP-4	-	1	
	LCWP-5	-	1	
	ELV-4	-	1	
	STAIR-06	-	2	
	LCWP-6	-	1	
	LCWP-7	-	1	
	ELE-4	-	1	
	STAIR-07	-	2	
	ELV-5	-	1	
	CWP RISER-2	-	1	
	ELE-5	-	1	
	STAIR-08	-	1	
	EXHAUST SHAFT-5	-	1	
	EXHAUST SHAFT-6	-	1	
	ELECTRICAL GANTRY	-	1	
	SUB TOTAL		40	

MAIN DRAWING

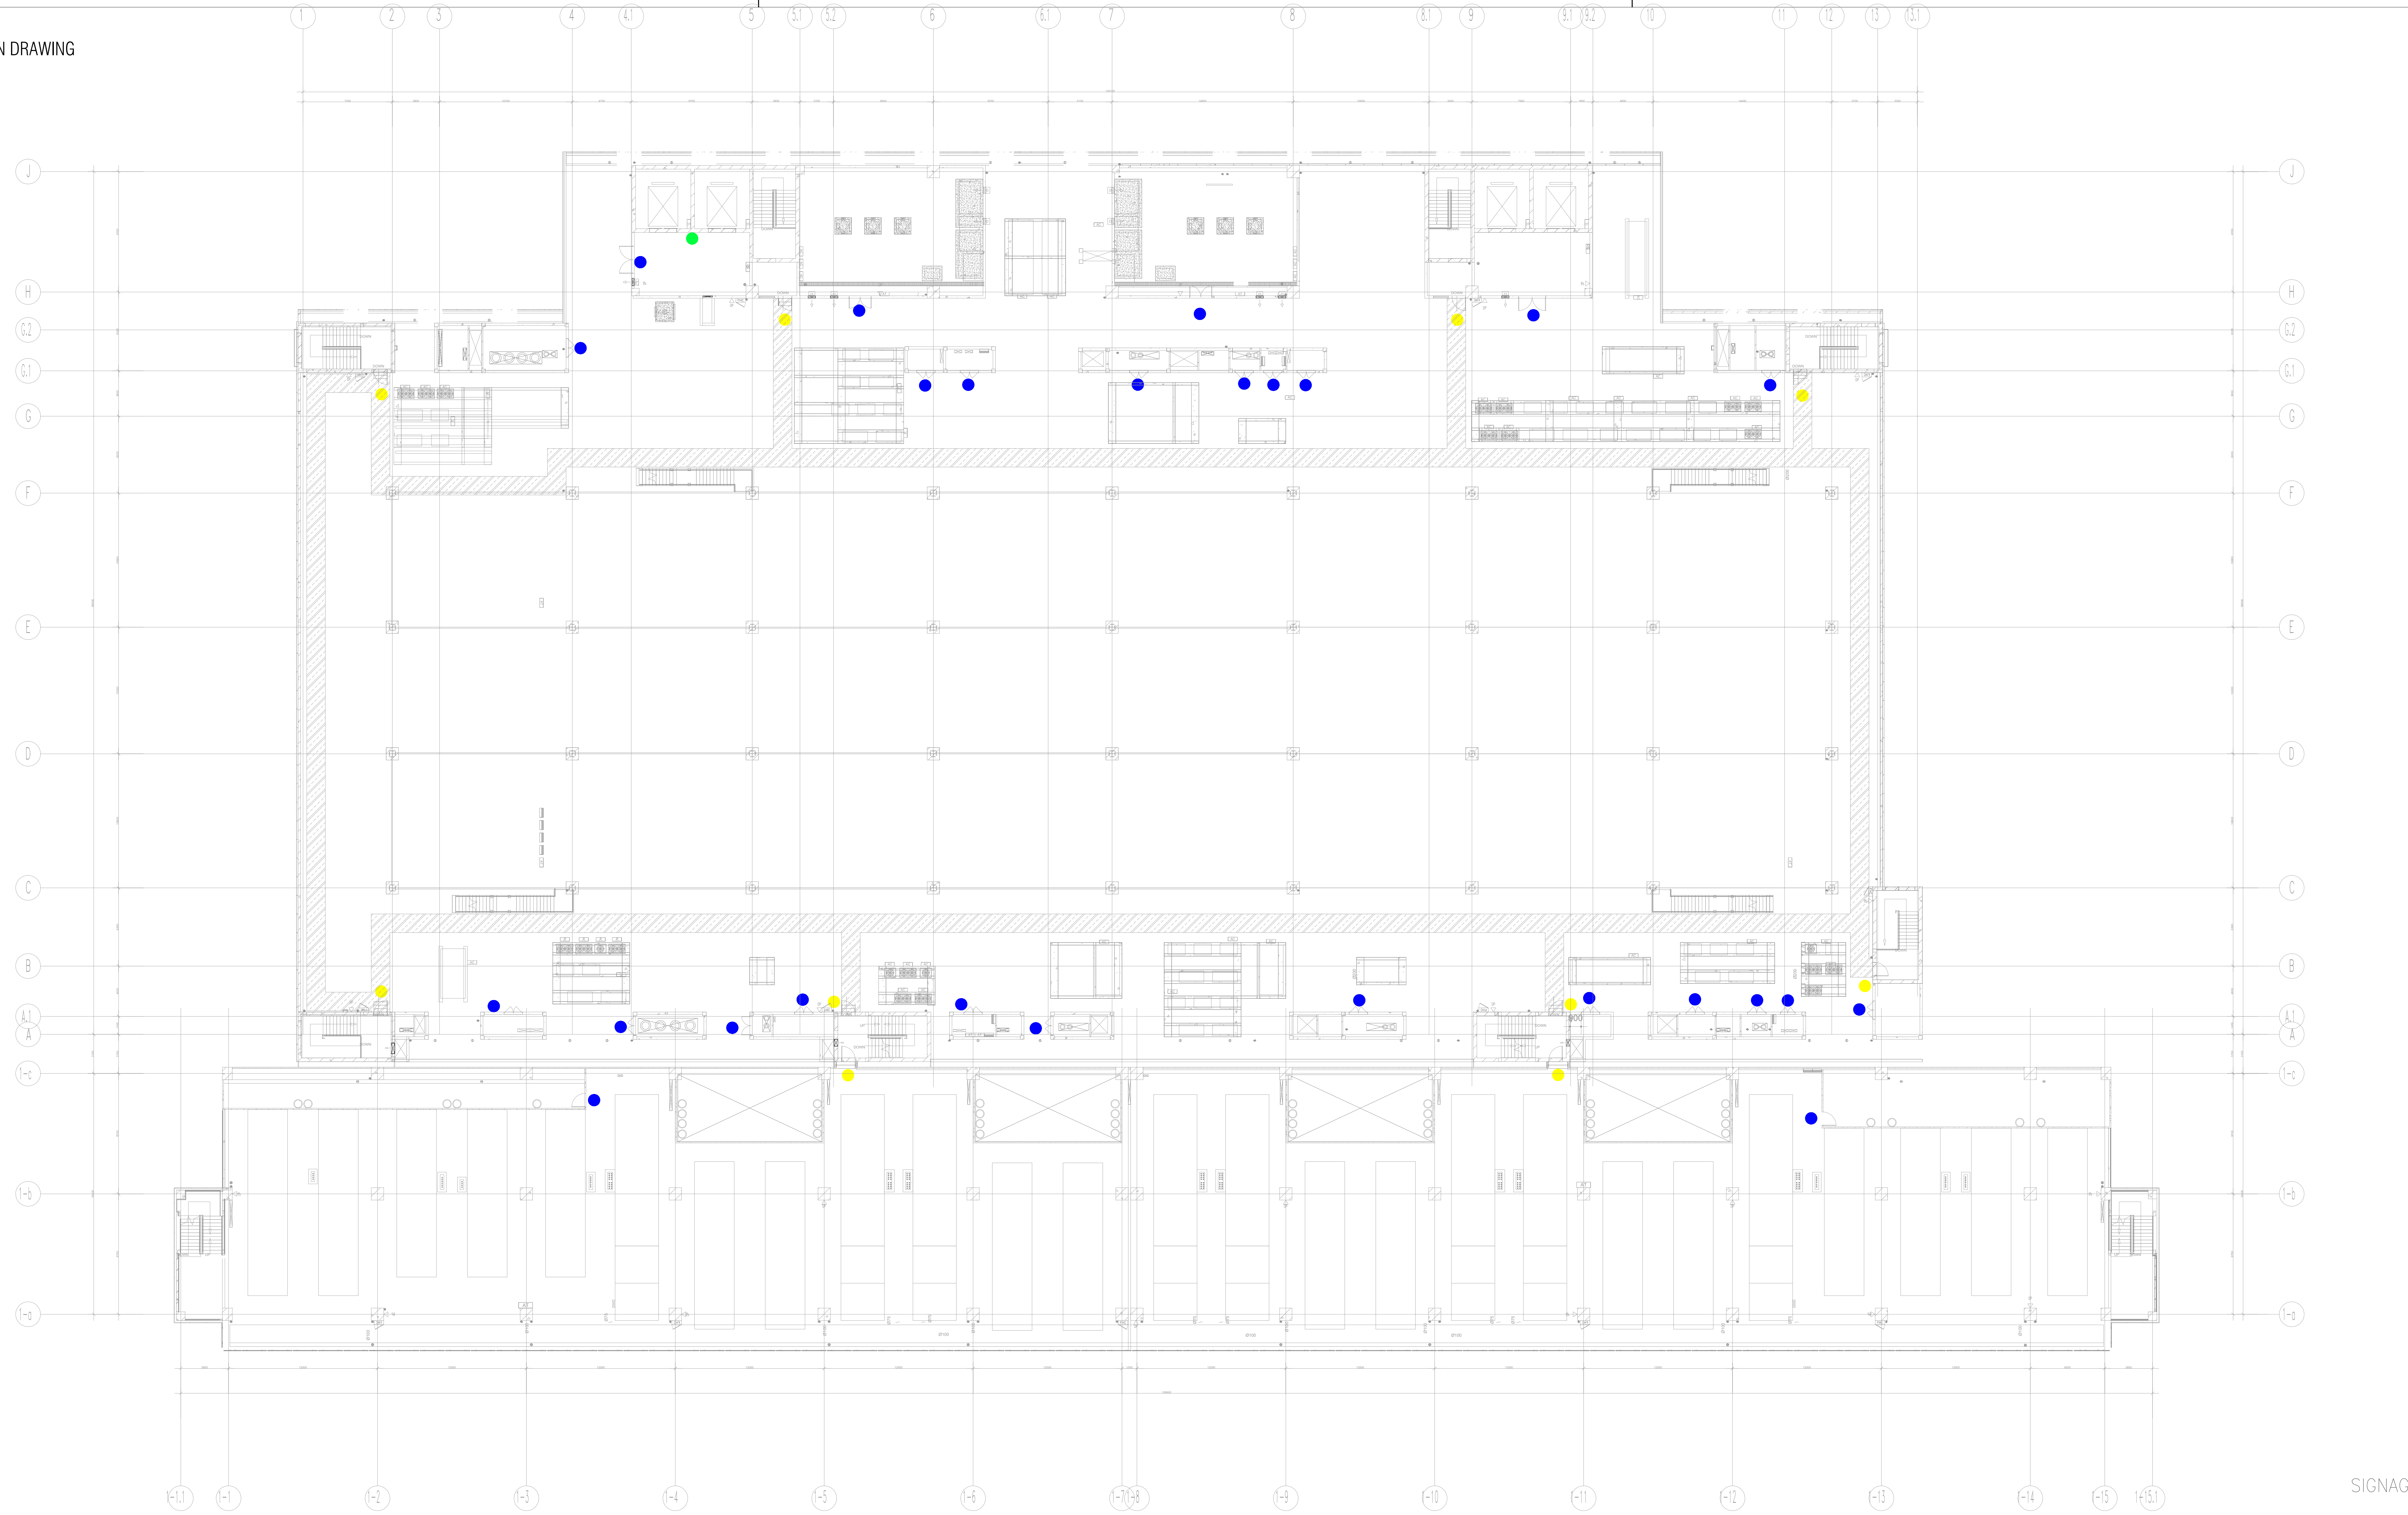
1
2
3
4
4.1
5
5.1
5.2
6
6.1
7
8
8.1
9
9.1
9.2
10
11
12
13
13.1
J
H
G.2
G.1
G
F
E
D
C
B
A.1
A
1-c
1-b
1-a
1-1
1-2
1-3
1-4
1-5
1-6
1-7
1-8
1-9
1-10
1-11
1-12
1-13
1-14
1-15

SIGNAGE LAGEND	
🔴	TOILET & DISABLED DOOR SIGNAGE
🟡	STAIRCASE DOOR SIGNAGE
🔵	ROOM FACILITY SIGNAGE
🟢	FIRE LIFT SIGNAGE

SIGNAGE LAYOUT-RF

CLIENT :

GULF EDGE DC 01

87 Wireless Road, M Thai Tower 11th. Floor, All Seasons Place, Lumpini,
Pathumwan, Bangkok 10330, Thailand

CONTRACTOR :

华西发展(泰国)有限公司
บริษัท หัวซือ ดีเวลลอปเม้นต์ (ประเทศไทย) จำกัด
HUASHI DEVELOPMENT CO.,LTD
No. 202, Room No. 1403, 14/F, Le Concorde Building,
Ratchadapisek Road, Huaykhwang Sub-District,
Huaykhwang District, Bangkok Metropolitan 10310.

CONSULTANT :

ARbay
บริษัท เอ อาร์ เบย์ จำกัด
ARbay Company Limited
31 st Floor Bangkok Insurance Building
25 South Sathorn road Thungmahamek
Sathorn Bangkok 10120 THAILAND
T +66 (0) 2286 8199
F +66 (0) 2286 2863
info@arbay.co.th

CONSULTANT :

Qbic Engineers & Architects Co.,Ltd.
8 Soi KALONG 4 SANAMBINNAM ROAD,
THASAI SUB-DISTRICT, MUANG NONTHABURI DISTRICT
, NONTHABURI.
Tel 662-950-4374
Fax 662-580-3231
E-Mail : qbic@qbic.co.th, www.qbic.co.th
QBIC ENGINEERS AND ARCHITECTS CO.,LTD.

CONSULTANT :

MITR
MITR TECHNICAL CONSULTANT CO.,LTD.
1168/8 12th FLOOR, LUMPINI TOWER BUILDING,
RAMA IV RD., THUNGMAHAMEK, SATHORN, BANGKOK 10120, THAILAND
TEL : 0-2679-9079-84
FAX : 0-2679-9085 E-mail: mitr_dd@mitr.com

Architect :	SIGNATURE
ประกิต พนานุรัตน์ วสถ. 580 ที่อยู่ 251/1 ถ.จารุเมือง แขวงรองเมือง เขตปทุมวัน กรุงเทพมหานคร โทรศัพท์ 02-286-8199	

Structural Engineer :	SIGNATURE
วิศวกรผู้ออกแบบโครงสร้าง	
ณัฐสม สงวนวงษ์ วย 1423 ที่อยู่ 2/1 ซ.รามคำแหง 150 ถ.รามคำแหง แขวง สะพานสูง เขต สะพานสูง กทม. 10240	

Structural Inspector :	SIGNATURE
วิศวกรผู้ตรวจสอบโครงสร้าง	
โกมล จุฑาภัทร วย 964 ที่อยู่ 24/18 ซ.นวมินทร์ 129 ถ. นวมินทร์ แขวง นวลจันทร์ เขต บึงกุ่ม กทม. 10230	

Electrical Engineer :	SIGNATURE
วิศวกรผู้ออกแบบระบบไฟฟ้ากำลัง	
นายสุภัทร บูรณวิทย์ วฟก.1265 ที่อยู่ 21 ซอยทานสัมฤทธิ 13 ตำบลท่าทราย อ.เมืองนนทบุรี จ.นนทบุรี 11000	

Mechanical Engineer :	SIGNATURE
วิศวกรผู้ออกแบบระบบเครื่องกลและปรับอากาศ	
นายประสิทธิ์ เกียวสุนทร วก.1221 ที่อยู่ 44/372 ซอยบางกระดี 35/1 แขวงแสมดำ เขตบางขุนเทียน กทม. 10150	ประสิทธิ์

Sanitary Engineer :	SIGNATURE
วิศวกรผู้ออกแบบระบบสุขาภิบาล และดับเพลิง	
นายทศวรรษ สนันฤทธิ์ วส. 215 ที่อยู่ บ้านเลขที 99/107 หมู่ที 3 ต.ศีรษะจรเข้น้อย อ.บางเสาธง จ.สมุทรปราการ 10540	ทศวรรษ

ISSUE/REVISION

REV.	DESCRIPTION	DATE
A	90% DEVELOPED	09/05/2026

PROJECT NAME :
GEDC 01

LOCATION:
Nikhom Phattana district, Rayong ,industrial estate,CPGC

BUILDING :

90% DEVELOPED

TITLE :
SIGNAGE LAYOUT-RF

JOB NO.	SCALE 1:200
DRAWN LXP	REF.
CHECKED LJC	DWG.NO. MPK01A-90-A-SN-401
APPROVED LXD	
DATE 2026.05.09	

SIGNAGE DETAIL LAYOUT

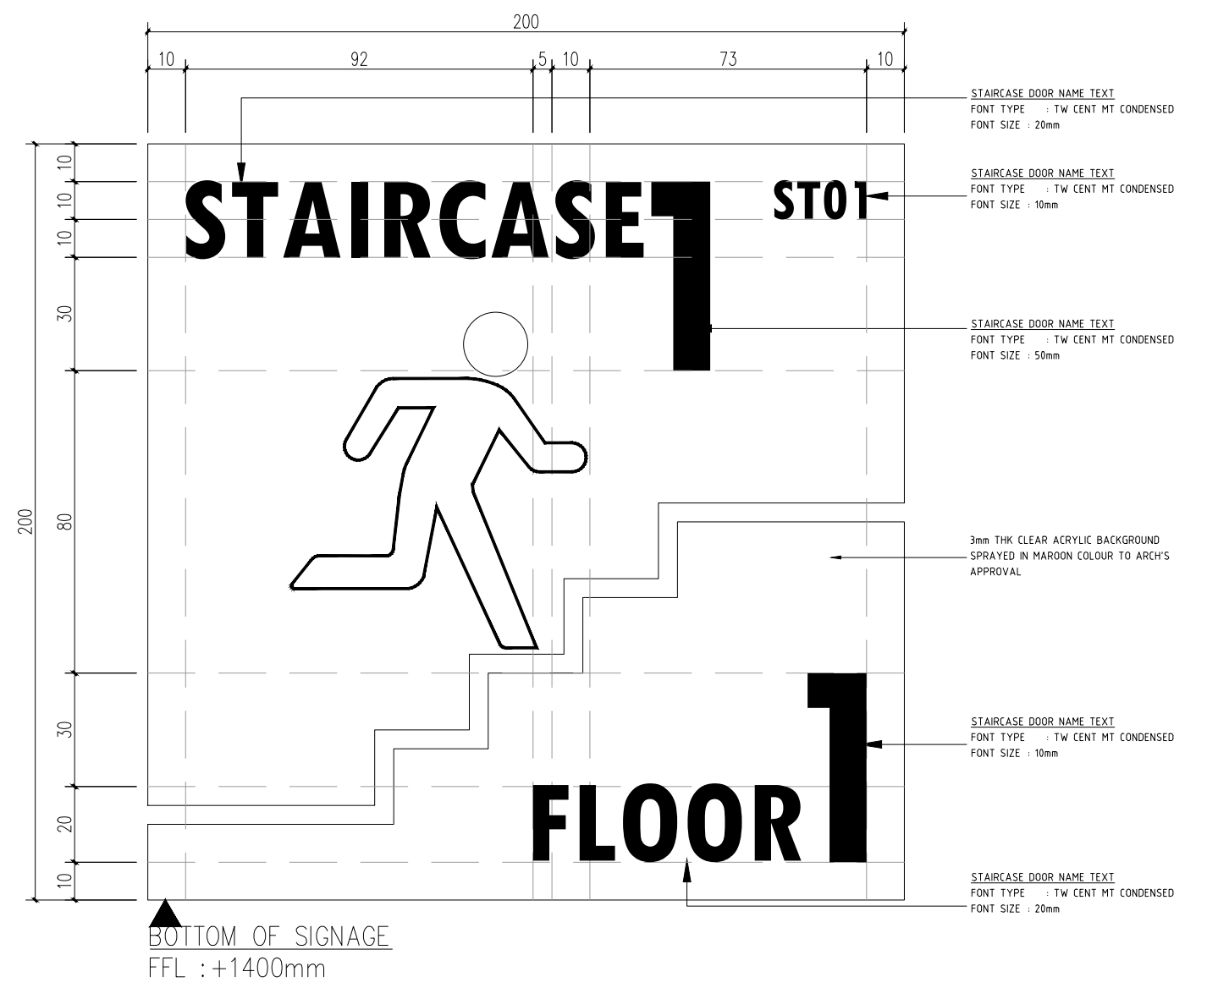
200
10
92
5
10
73
10
STAIRCASE 1
ST01
FLOOR 1
STAIRCASE DOOR NAME TEXT
FONT TYPE : TW CENT MT CONDENSED
FONT SIZE : 20mm
STAIRCASE DOOR NAME TEXT
FONT TYPE : TW CENT MT CONDENSED
FONT SIZE : 10mm
STAIRCASE DOOR NAME TEXT
FONT TYPE : TW CENT MT CONDENSED
FONT SIZE : 50mm
3mm THK CLEAR ACRYLIC BACKGROUND SPRAYED IN MAROON COLOUR TO ARCH'S APPROVAL
STAIRCASE DOOR NAME TEXT
FONT TYPE : TW CENT MT CONDENSED
FONT SIZE : 10mm
STAIRCASE DOOR NAME TEXT
FONT TYPE : TW CENT MT CONDENSED
FONT SIZE : 20mm
200
80
30
30
20
10
BOTTOM OF SIGNAGE
FFL : +1400mm

STAIRCASE / FLOOR	SIGN	QUANTITY	MATERIAL
ST1 / UPPER ROOF FLOOR	STAIRCASE 1 FLOOR 5	1	3mm TRANSPARENT ACRYLIC 140mm X 240mm with HIGH RES UV PRINT STICKER TO MATCH PANTONE NAVY BLUE
ST2 / UPPER ROOF FLOOR	STAIRCASE 2 FLOOR 5	1	
ST3 / UPPER ROOF FLOOR	STAIRCASE 3 FLOOR 5	1	
ST4 / UPPER ROOF FLOOR	STAIRCASE 4 FLOOR 5	1	
ST5 / UPPER ROOF FLOOR	STAIRCASE 5 FLOOR 5	1	

STAIRCASE / FLOOR	SIGN	QUANTITY	MATERIAL
ST6 / UPPER ROOF FLOOR	STAIRCASE 6 FLOOR 5	1	3mm TRANSPARENT ACRYLIC 140mm X 240mm with HIGH RES UV PRINT STICKER TO MATCH PANTONE NAVY BLUE
ST7 / UPPER ROOF FLOOR	STAIRCASE 7 FLOOR 5	1	
ST8 / UPPER ROOF FLOOR	STAIRCASE 8 FLOOR 5	1	
ST9 / UPPER ROOF FLOOR	STAIRCASE 9 FLOOR 5	1	
ST10 / UPPER ROOF FLOOR	STAIRCASE 10 FLOOR 5	1	

SIGNAGE DETAIL LAYOUT

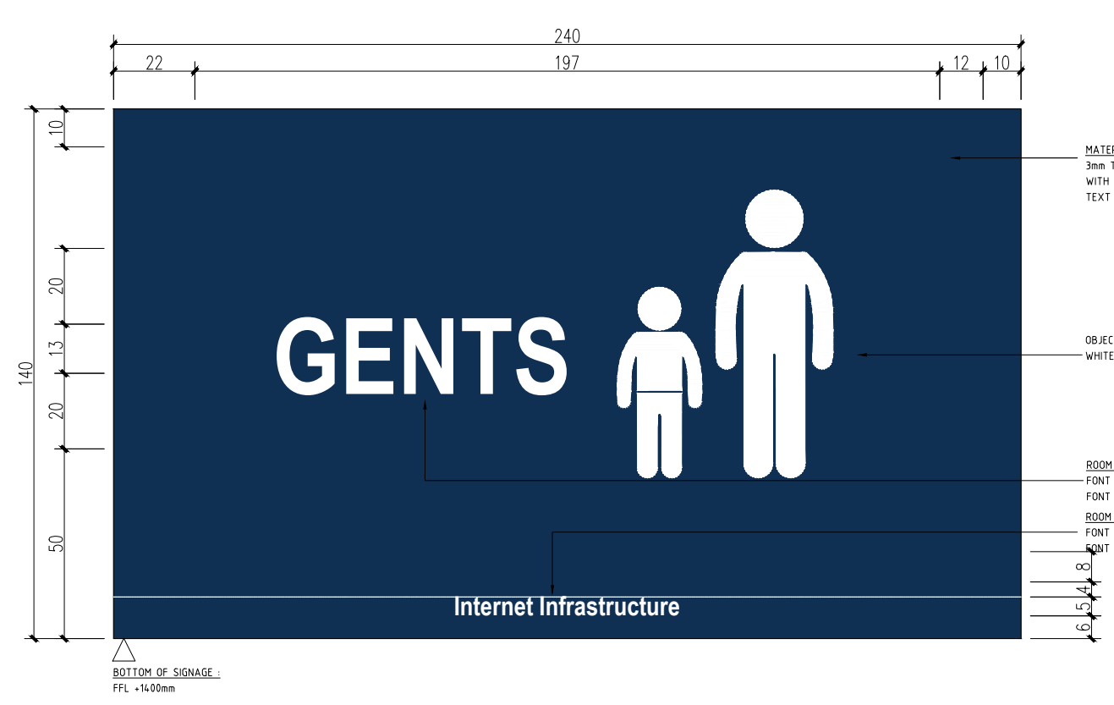
240
22
197
12
10
GENTS
Internet Infrastructure
MATERIAL
3mm THK CLEAR ARCYLIC BOARD WITH DARK BLUE COLOUR AND TEXT STICKER AT BACK
OBJECT TO BE REVERSED STICKER WITH WHITE COLOUR TO ARCH'S APPROVAL
ROOM NAME TEXT
FONT TYPE : MONTSERRAT
FONT SIZE :20mm
ROOM NAME TEXT
FONT TYPE : MONTSERRAT (BOLD)
FONT SIZE : 5mm
140
10
20
13
20
50
8
4
5
6
BOTTOM OF SIGNAGE :
FFL +1400mm

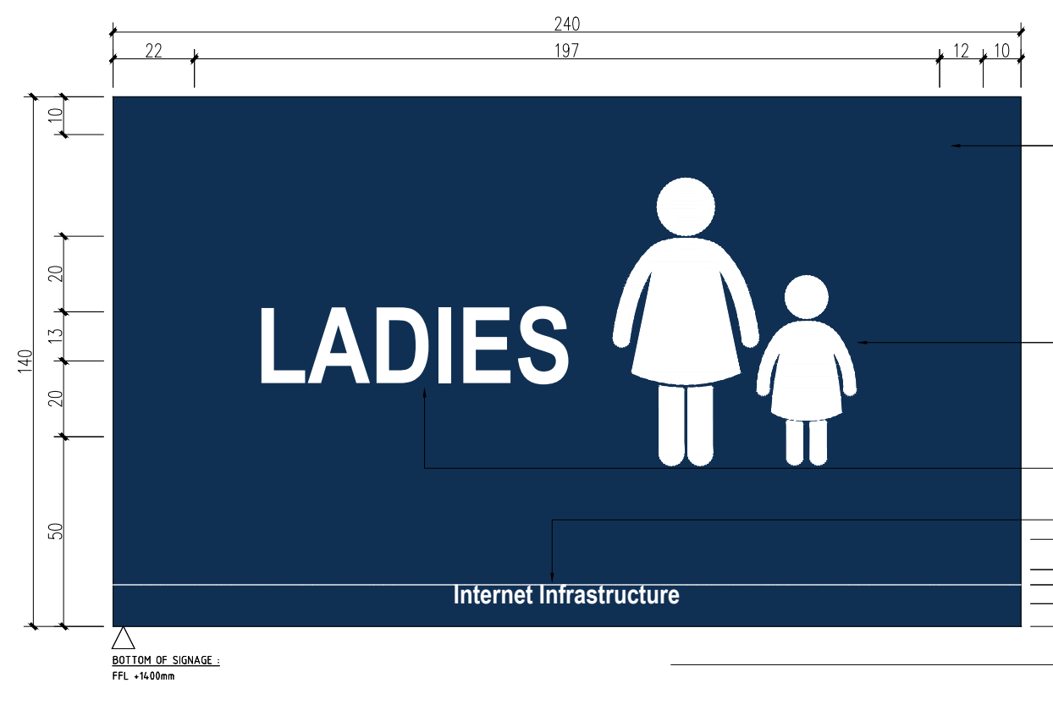
240
22
197
12
10
LADIES
Internet Infrastructure
MATERIAL
3mm THK CLEAR ARCYLIC BOARD WITH DARK BLUE COLOUR AND TEXT STICKER AT BACK
OBJECT TO BE REVERSED STICKER WITH WHITE COLOUR TO ARCH'S APPROVAL
ROOM NAME TEXT
FONT TYPE : MONTSERRAT
FONT SIZE :20mm
ROOM NAME TEXT
FONT TYPE : MONTSERRAT (BOLD)
FONT SIZE : 5mm
140
10
20
13
20
50
8
4
5
6
BOTTOM OF SIGNAGE :
FFL +1400mm

SIGNAGE DETAIL LAYOUT

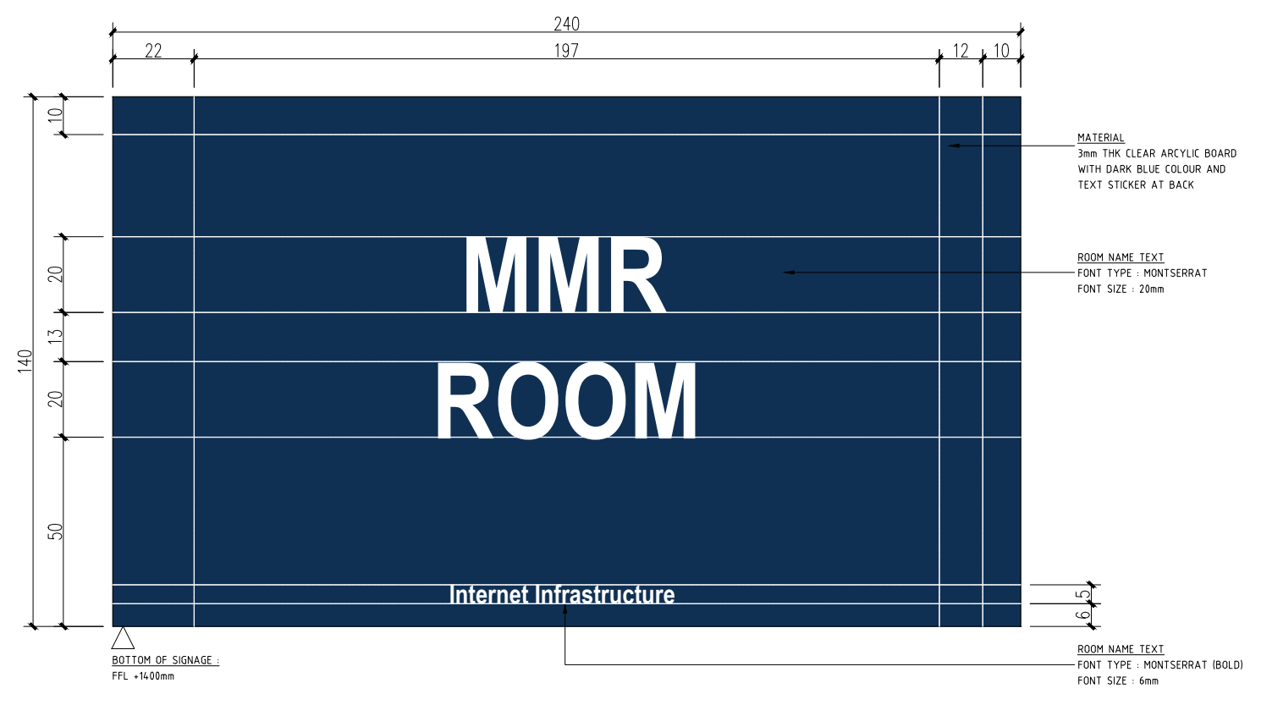
240
22
197
12
10
MMR
ROOM
Internet Infrastructure
MATERIAL
3mm THK CLEAR ARCYLIC BOARD WITH DARK BLUE COLOUR AND TEXT STICKER AT BACK
ROOM NAME TEXT
FONT TYPE : MONTSERRAT
FONT SIZE : 20mm
ROOM NAME TEXT
FONT TYPE : MONTSERRAT (BOLD)
FONT SIZE : 6mm
140
10
20
13
20
50
5
6
BOTTOM OF SIGNAGE :
FFL +1400mm

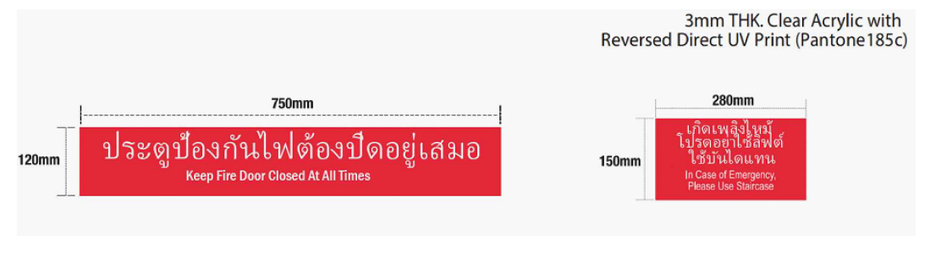
3mm THK. Clear Acrylic with Reversed Direct UV Print (Pantone185c)
750mm
120mm
ประตูป้องกันไฟต้องปิดอยู่เสมอ
Keep Fire Door Closed At All Times
280mm
150mm
เกิดเพลิงไหม้ โปรดอย่าใช้ลิฟต์ ใช้บันไดแทน
In Case of Emergency, Please Use Staircase

ESCAPE DOOR SIGNAGE
*The height of signage 1100mm from floor level
*Type A - Single leaf door required 2 signage (1-front & 1-rear)
*Type B - Double leaf door required 4 signage (2-front & 2-rear)

LIFT SIGNAGE

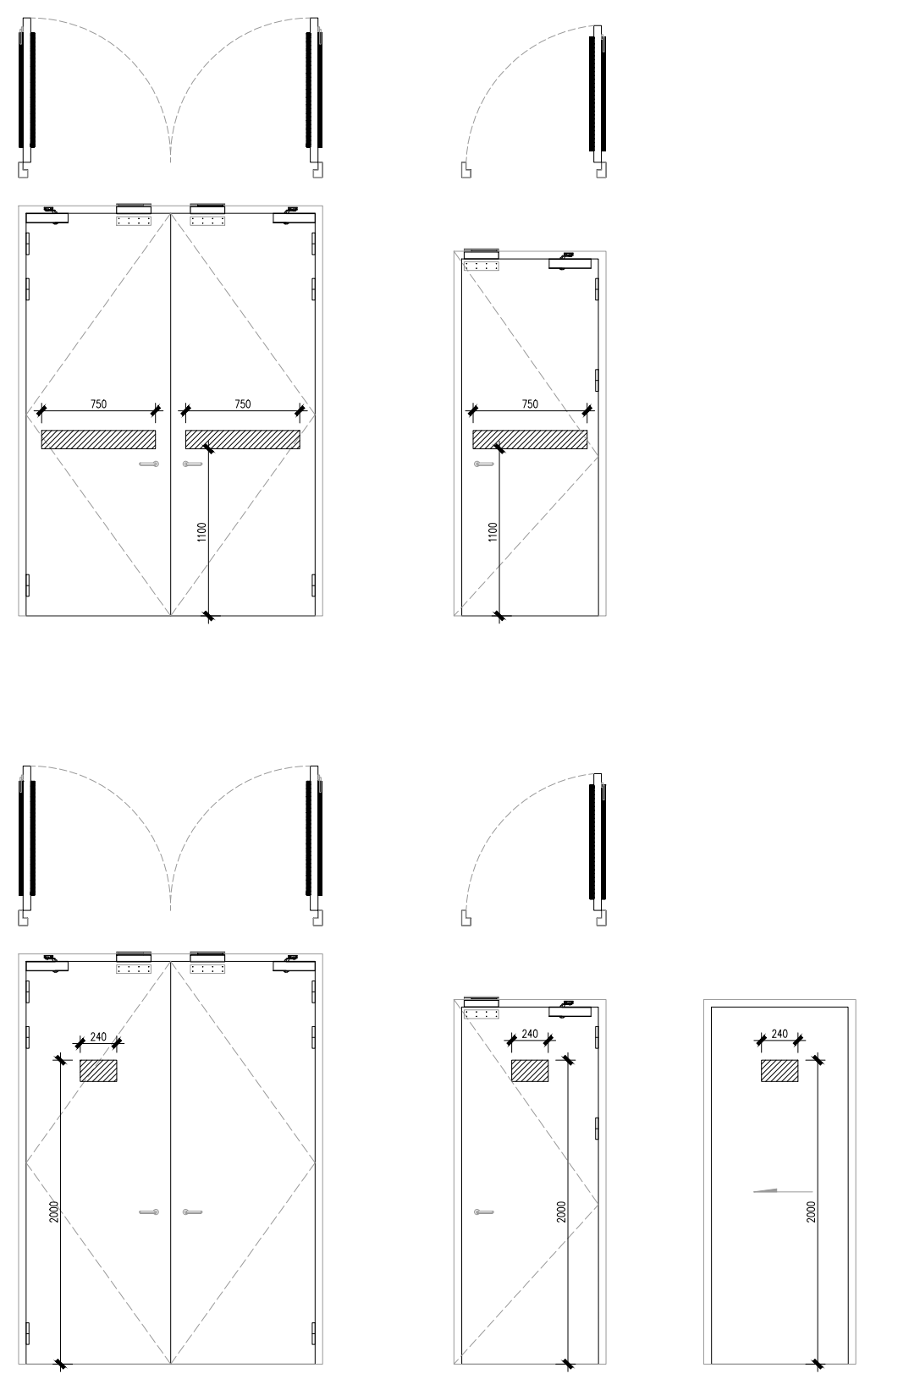
750
240
2000

LOCATION	SIGNAGE		QUANTITY	MATERIAL
	ENGLISH	THAI		
	STAIR-06	-	1	3mm TRANSPARENT ACRYLC 140mm X240mm with HIGH RES UV PRINT STICKER TO MATCH PANTONE NAVY BLUE
	STAIR-07	-	1	
	SUB TOTAL		2	

MAIN DRAWING

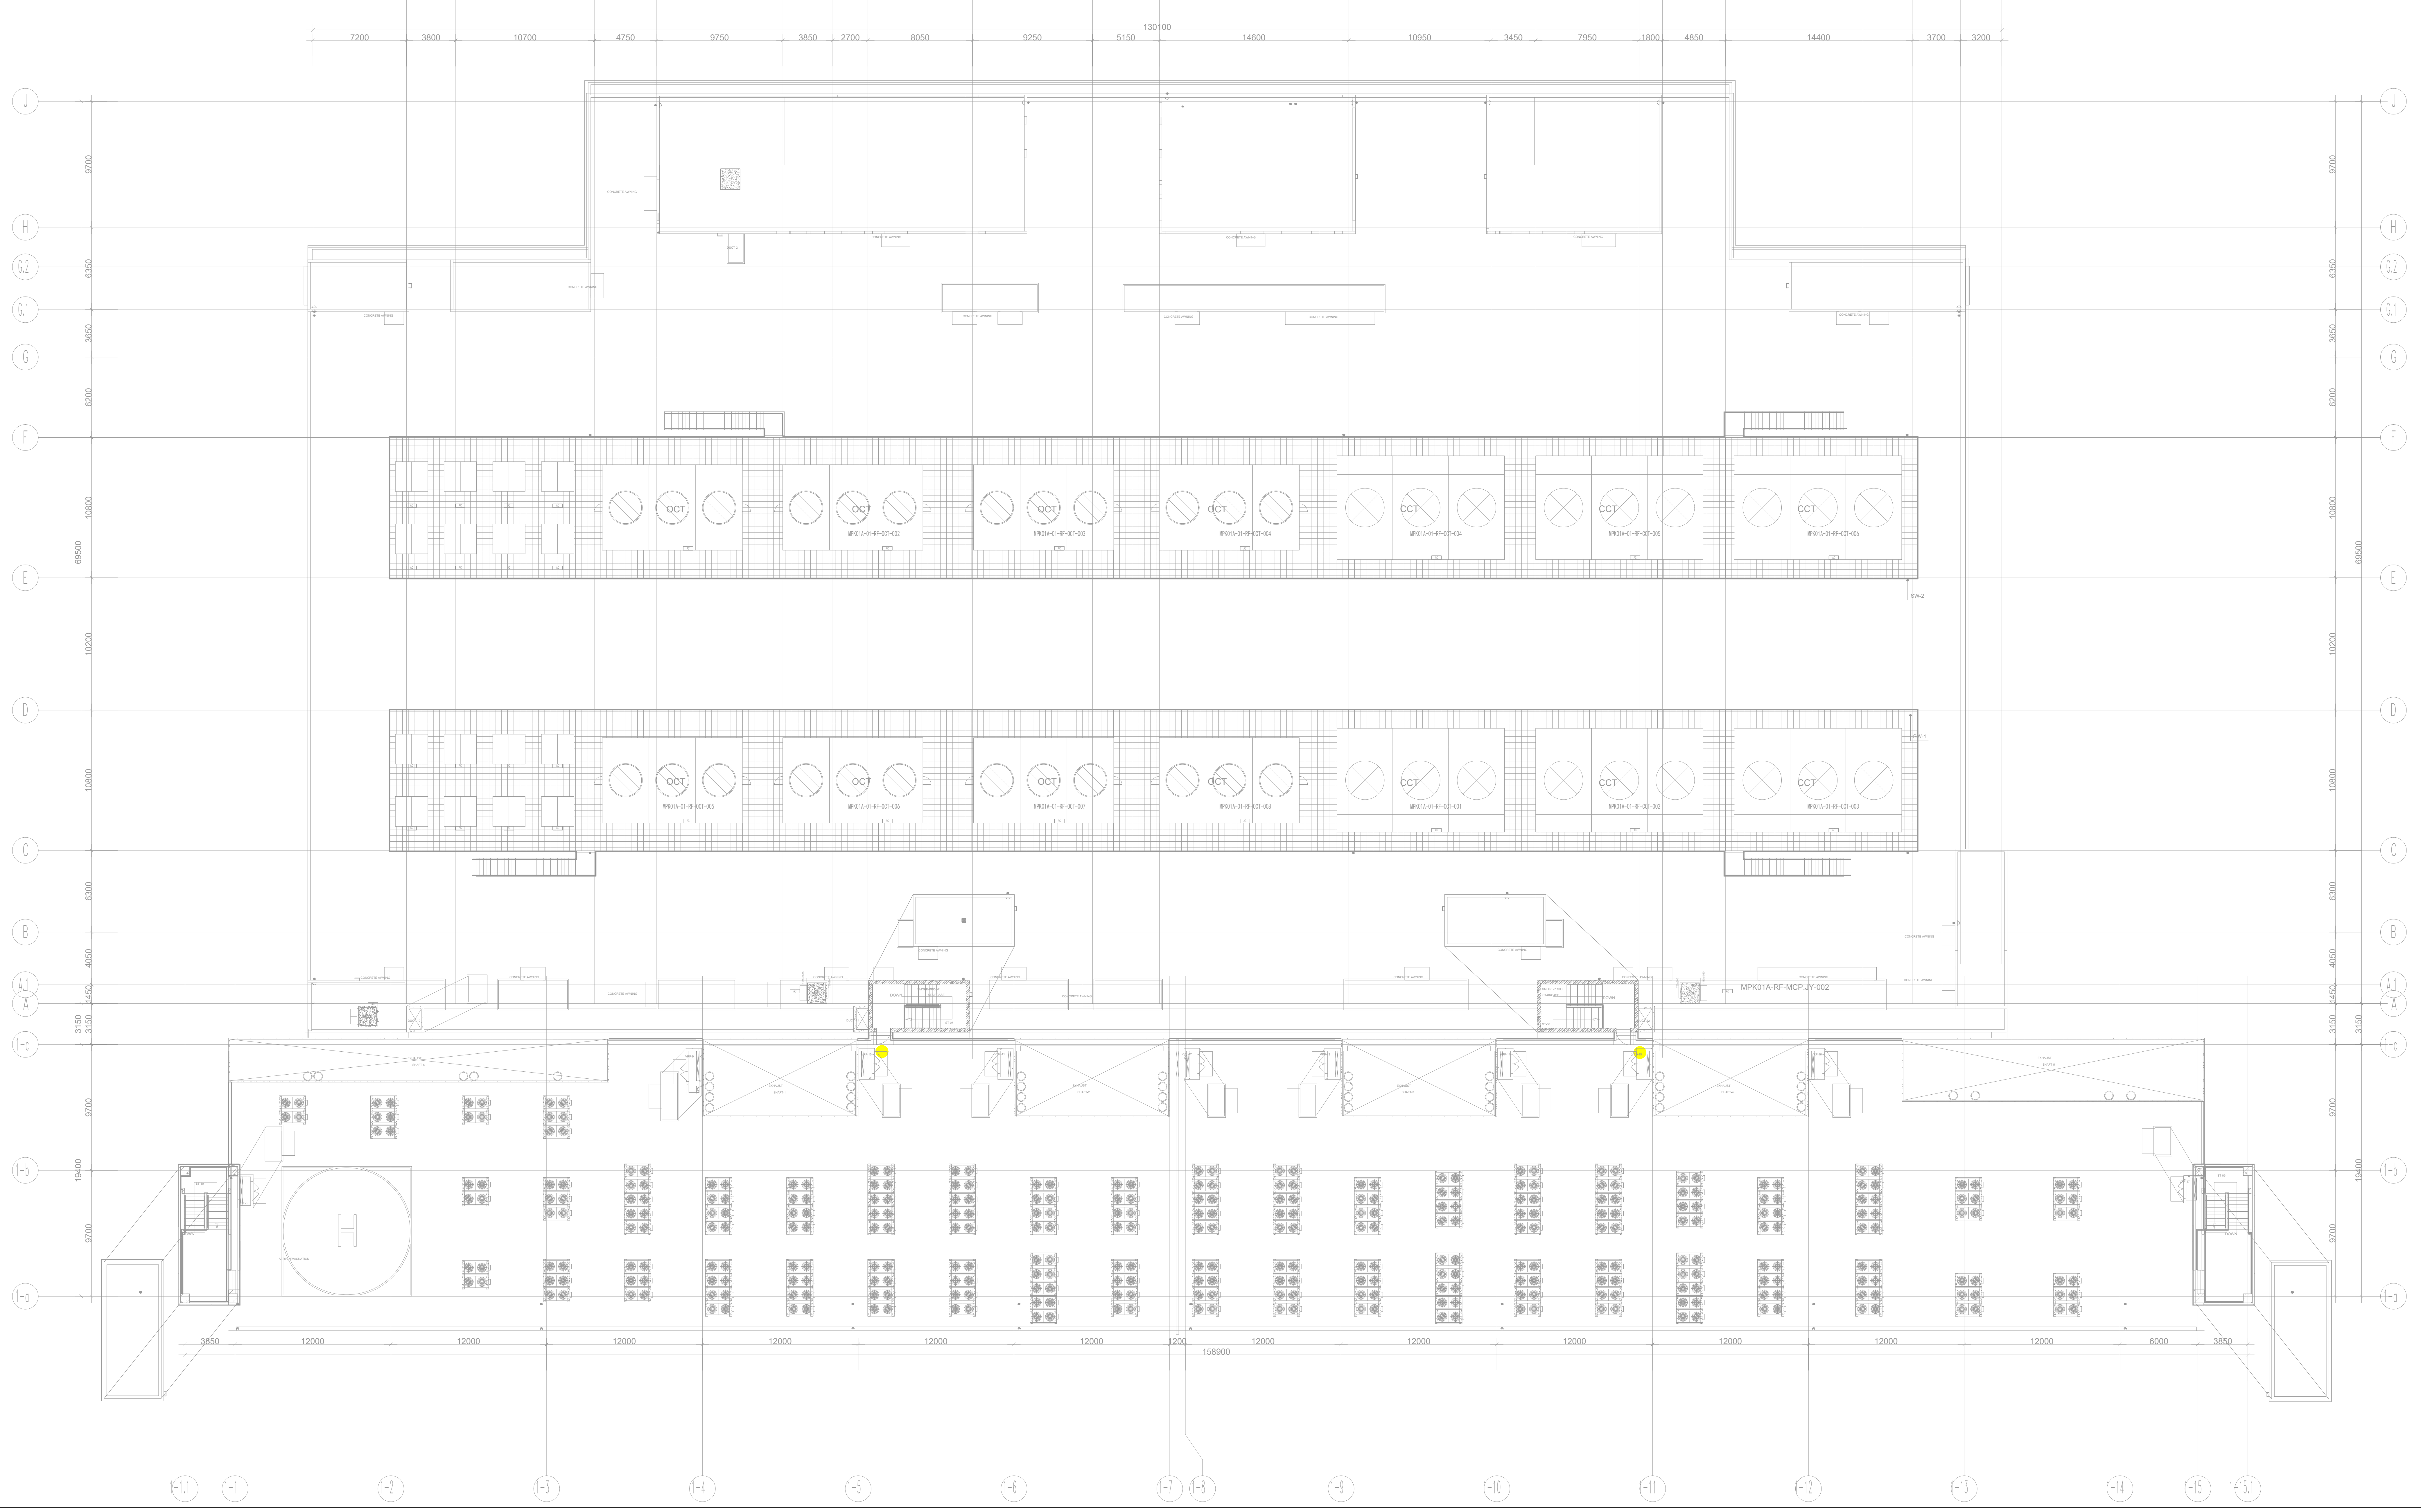
130100
7200
3800
10700
4750
9750
3650
2700
8050
9250
5150
14600
10950
3450
7950
1800
4850
14400
3700
3200
J
H
G.2
G.1
G
F
E
D
C
B
A.1
A
I-c
I-b
I-a
9700
6350
3650
6200
10800
69900
10200
6300
4050
3450
3150
19400
CCT
MPK01A-RF-MCP-JY-002
12000
8000
3650
158900

SIGNAGE LAGEND	
🔴	TOILET & DISABLED DOOR SIGNAGE
🟡	STAIRCASE DOOR SIGNAGE
🔵	ROOM FACILITY SIGNAGE
🟢	FIRE LIFT SIGNAGE

SIGNAGE LAYOUT-UPPER RF

CLIENT :

GULF EDGE DC 01
87 Wireless Road, M Thai Tower 11th. Floor, All Seasons Place, Lumpini,
Pathumwan, Bangkok 10330, Thailand

CONTRACTOR :

华西发展(泰国)有限公司
บริษัท หัวซือ ดีเวลลอปเม้นต์ (ประเทศไทย) จำกัด
HUASHI DEVELOPMENT CO.,LTD
No. 202, Room No. 1403, 14/F, Le Concorde Building,
Ratchadapisek Road, Huaykhwang Sub-District,
Huaykhwang District, Bangkok Metropolitan 10310.

CONSULTANT :

ARbay
บริษัท เอ อาร์ เบย์ จำกัด
ARbay Company Limited
31 st Floor Bangkok Insurance Building
25 South Sathorn road Thungmahamek
Sathorn Bangkok 10120 THAILAND
T +66 (0) 2286 8199
F +66 (0) 2286 2863
info@arbay.co.th

CONSULTANT :

Qbic Engineers & Architects Co.,Ltd.
8 Soi KALONG 4 SANAMBINNAM ROAD,
THASAI SUB-DISTRICT, MUANG NONTHABURI DISTRICT
, NONTHABURI.
Tel 662-950-4374
Fax 662-580-3231
E-Mail : qbic@qbic.co.th, www.qbic.co.th
QBIC ENGINEERS AND ARCHITECTS CO.,LTD.

CONSULTANT :

MITR
MITR TECHNICAL CONSULTANT CO.,LTD.
1168/8 12th FLOOR, LUMPINI TOWER BUILDING,
RAMA IV RD., THUNGMAHAMEK, SATHORN, BANGKOK 10120, THAILAND
TEL : 0-2679-9079-84
FAX : 0-2679-9085 E-mail: mitr_dd@mitr.com

Architect :	SIGNATURE
ประกิต พนานุรัตน์ วสถ. 580 ที่อยู่ 251/1 ถ.จารุเมือง แขวงรองเมือง เขตปทุมวัน กรุงเทพมหานคร โทรศัพท์ 02-286-8199	
Structural Engineer :	SIGNATURE
วิศวกรผู้ออกแบบโครงสร้าง	
ณัฐสม สงวนวงษ์ วย 1423 ที่อยู่ 2/1 ซ.รามคำแหง 150 ถ.รามคำแหง แขวง สะพานสูง เขต สะพานสูง กทม. 10240	ณัฐสม สงวนวงษ์
Structural Inspector :	SIGNATURE
วิศวกรผู้ตรวจสอบโครงสร้าง	
โกมล จุฑาภัทร วย 964 ที่อยู่ 24/18 ซ.นวมินทร์ 129 ถ. นวมินทร์ แขวง นวลจันทร์ เขต บึงกุ่ม กทม. 10230	
Electrical Engineer :	SIGNATURE
วิศวกรผู้ออกแบบระบบไฟฟ้ากำลัง	
นายสุภัทร บูรณวิทย์ วฟก.1265 ที่อยู่ 21 ซอยทานสัมฤทธิ 13 ตำบลท่าทราย อ.เมืองนนทบุรี จ.นนทบุรี 11000	สุภัทร บูรณวิทย์
Mechanical Engineer :	SIGNATURE
วิศวกรผู้ออกแบบระบบเครืองกลและปรับอากาศ	
นายประสิทธิ เกียวสุนทร วก.1221 ที่อยู่ 44/372 ซอยบางกระดี 35/1 แขวงแสมดำ เขตบางขุนเทียน กทม. 10150	ประสิทธิ์
Sanitary Engineer :	SIGNATURE
วิศวกรผู้ออกแบบระบบสุขาภิบาล และดับเพลิง	
นายทศวรรษ สนันฤทธิ วส. 215 ที่อยู่ บ้านเลขที 99/107 หมู่ที 3 ต.ศีรษะจรเข้น้อย อ.บางเสาธง จ.สมุทรปราการ 10540	ทศวรรษ

ISSUE/REVISION

REV.	DESCRIPTION	DATE
A	90% DEVELOPED	09/05/2026

PROJECT NAME :

GEDC 01

LOCATION:
Nikhom Phattana district, Rayong ,industrial estate,CPGC

BUILDING :

90% DEVELOPED

TITLE :

SIGNAGE LAYOUT-UPPER RF

JOB NO.	SCALE 1:200
DRAWN LXP	REF.
CHECKED LJC	DWG.NO. MPK01A-90-A-SN-501
APPROVED LXD	
DATE 2026.05.09	