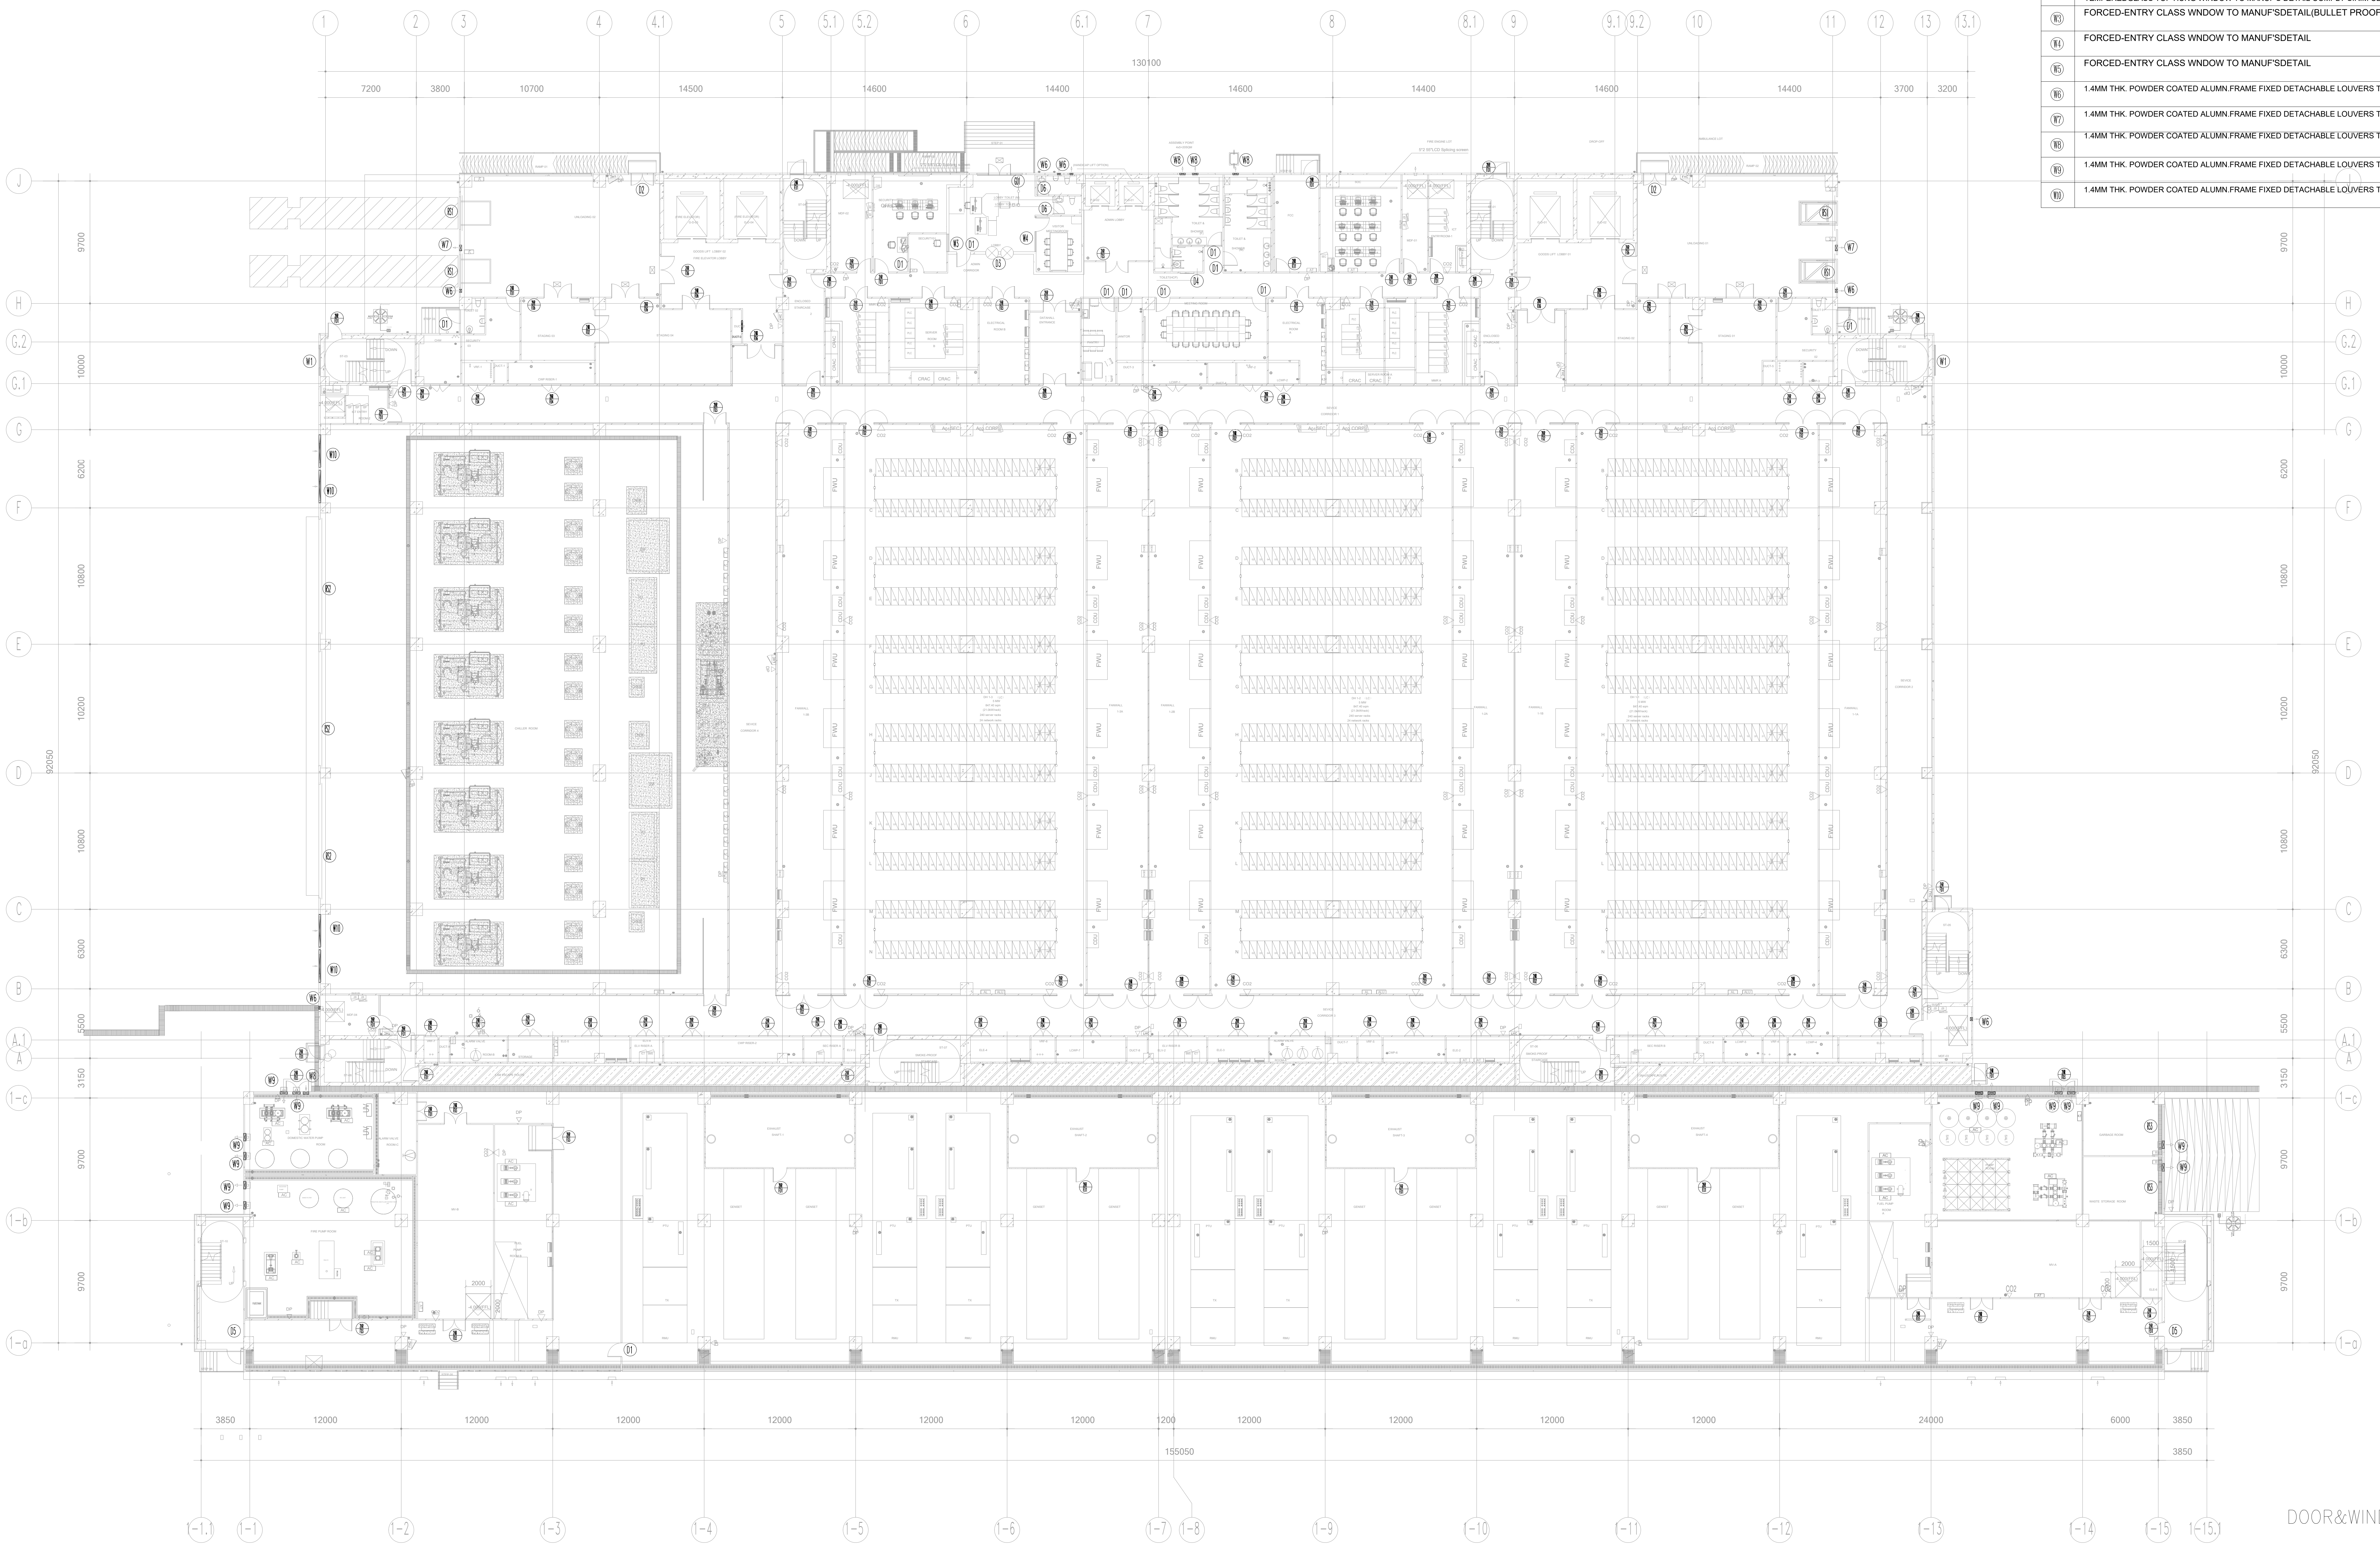

DOOR&WINDOW LAYOUT-1F

DOOR SCHEDULE		
	DESCRIPTION	SISE(MM) WIDTH X HEIGHT
2HR FD1	G.I METAL FRAME SINGLE LEAF2 HOUR FIRE RATED SOLID STEEL DOOR PANEL	1100 X 2400
2HR FD2	G.I METAL FRAME DOUBLE LEAF 2 HOUR FIRE RATED SOLID STEEL DOOR PANEL (THE DOOR OPENS 180 DEGREES)	2200 X3100
2HR FD3	G.I METAL FRAME DOUBLE LEAF 2 HOUR FIRE RATED SOLID STEEL DOOR PANEL	1800 X 2400
2HR FD4	G.I METAL FRAME DOUBLE LEAF 2 HOUR FIRE RATED SOLID STEEL DOOR PANEL	1500 X 2200
2HR FD5	G.I METAL FRAME DOUBLE LEAF 2 HOUR FIRE RATED SOLID STEEL DOOR PANEL	900 X 2200
2HR FD6	G.I METAL FRAME DOUBLE LEAF 2 HOUR FIRE RATED SOLID STEEL DOOR PANEL (THE DOOR OPENS 90 DEGREES)	2200 X3100
2HR FD7	G.I METAL FRAME DOUBLE LEAF 2 HOUR FIRE RATED SOLID STEEL DOOR PANEL	1500 X 1700
GD1	ALUMINUM-FRAMED CASEMENT DOOR WITH ALUMINUM FIXED GLASS PANEL, TO BE EXECUTED ACCORDING TO MANUFACTURER'S DETAILS	3600 X 4000
D1	WOODEN-FRAMED CASEMENT DOOR, TO BE EXECUTED ACCORDING TO MANUFACTURER'S DETAILS	1100 X 2400
D2	G.I METAL FRAME SINGLE LEAF SOLID STEEL DOOR PANEL	1800 X 2400
D3	S/S FRAME WITH S/S REVOLVING DOOR AND CASEMENT DOOR TO MANUF'S DETAIL AND ARCH'S APPROVAL	2200 X 3500
D4	WOODEN-FRAMED CASEMENT DOOR, TO BE EXECUTED ACCORDING TO MANUFACTURER'S DETAILS	1100 X 2400
D5	PERFORATED ALUMINUM PANEL	1100 X 2400
D6	WOODEN-FRAMED CASEMENT DOOR, TO BE EXECUTED ACCORDING TO MANUFACTURER'S DETAILS	900 X 2400
RS1	ALUMINIUM ROLLER SHUTTER TO MANUF'S DETAIL	2600 X 3600
RS2	ALUMINIUM ROLLER SHUTTER TO MANUF'S DETAIL	9000 X 4000
RS3	ALUMINIUM ROLLER SHUTTER TO MANUF'S DETAIL	3600 X 4000
W1	1.4MIM THK. POWDER COATED ALUMN. FRAME WITH 6MIM THK. DARK GREY TINTED TEMPEREDGLASS TOP HUNG WINDOW TO MANUF'S DETAIL COMPLY SIRIM CERTIFICATE	2400 X 800
W2	1.4MIM THK. POWDER COATED ALUMN. FRAME WITH 6MIM THK. DARK GREY TINTED TEMPEREDGLASS TOP HUNG WINDOW TO MANUF'S DETAIL COMPLY SIRIM CERTIFICATE	1200 X 800
W3	FORCED-ENTRY CLASS WNDOW TO MANUF'SDETAIL(BULLET PROOF GLASS)	3300 X 2100
W4	FORCED-ENTRY CLASS WNDOW TO MANUF'SDETAIL	2800 X 2400
W5	FORCED-ENTRY CLASS WNDOW TO MANUF'SDETAIL	3700 X 1500
W6	1.4MM THK. POWDER COATED ALUMN.FRAME FIXED DETACHABLE LOUVERS TO MANUF'S DETAIL	φ250
W7	1.4MM THK. POWDER COATED ALUMN.FRAME FIXED DETACHABLE LOUVERS TO MANUF'S DETAIL	450 X 300
W8	1.4MM THK. POWDER COATED ALUMN.FRAME FIXED DETACHABLE LOUVERS TO MANUF'S DETAIL	450 X 250
W9	1.4MM THK. POWDER COATED ALUMN.FRAME FIXED DETACHABLE LOUVERS TO MANUF'S DETAIL	600 X 600
W10	1.4MM THK. POWDER COATED ALUMN.FRAME FIXED DETACHABLE LOUVERS TO MANUF'S DETAIL	2600 X 1600

CLIENT :

GULF EDGE DC 01

87 Wireless Road, M Thai Tower 11th. Floor, All Seasons Place, Lumpini,
Pathumwan, Bangkok 10330, Thailand

CONTRACTOR :

华西发展(泰国)有限公司
บริษัท หัวซือ ดีเวลลอปเม้นต์ (ประเทศไทย) จำกัด
HUASHI DEVELOPMENT CO.,LTD
No. 202, Room No. 1403, 14/F, Le Concorde Building,
Ratchadapisek Road, Huaykhwang Sub-District,
Huaykhwang District, Bangkok Metropolitan 10310.

CONSULTANT :

ARbay
บริษัท เอ อาร์ เบย์ จำกัด
ARbay Company Limited
31 st Floor Bangkok Insurance Building
25 South Sathorn road Thungmahamek
Sathorn Bangkok 10120 THAILAND
T +66 (0) 2286 8199
F +66 (0) 2286 2863
info@arbay.co.th

CONSULTANT :

Qbic Engineers & Architects Co.,Ltd.
8 Soi KALONG 4 SANAMBINNAM ROAD,
THASAI SUB-DISTRICT, MUANG NONTHABURI DISTRICT
, NONTHABURI.
Tel 662-950-4374
Fax 662-580-3231
E-Mail : qbic@qbic.co.th, www.qbic.co.th
QBIC ENGINEERS AND ARCHITECTS CO.,LTD.

CONSULTANT :

MITR
MITR TECHNICAL CONSULTANT CO.,LTD.
1168/8 12th FLOOR, LUMPINI TOWER BUILDING,
RAMA IV RD., THUNGMAHAMEK, SATHORN, BANGKOK 10120, THAILAND
TEL : 0-2679-9079-84
FAX : 0-2679-9085 E-mail: mitr_dd@mitr.com

Architect :	SIGNATURE
ประกิต พนานุรัตน์ วสถ. 580 ทีอยู่ 251/1 ถ.จารุเมือง แขวงรองเมือง เขตปทุมวัน กรุงเทพมหานคร โทรศัพท์ 02-286-8199	
Structural Engineer :	SIGNATURE
วิศวกรผู้ออกแบบโครงสร้าง	
ณัฐสม สงวนวงษ์ วย 1423 ทีอยู่ 2/1 ซ.รามคำแหง 150 ถ.รามคำแหง แขวง สะพานสูง เขต สะพานสูง กทม. 10240	
Structural Inspector :	SIGNATURE
วิศวกรผู้ตรวจสอบโครงสร้าง	
โกมล จุฑาภัทร วย 964 ทีอยู่ 24/18 ซ.นวมินทร์ 129 ถ. นวมินทร์ แขวง นวลจันทร์ เขต บึงกุ่ม กทม. 10230	
Electrical Engineer :	SIGNATURE
วิศวกรผู้ออกแบบระบบไฟฟ้ากำลัง	
นายสุภัทร บูรณวิทย์ วฟก.1265 ทีอยู่ 21 ซอยทานสัมฤทธิ 13 ตำบลท่าทราย อ.เมืองนนทบุรี จ.นนทบุรี 11000	
Mechanical Engineer :	SIGNATURE
วิศวกรผู้ออกแบบระบบเครื่องกลและปรับอากาศ	
นายประสิทธิ์ เกียวสุนทร วก.1221 ทีอยู่ 44/372 ซอยบางกระดี 35/1 แขวงแสมดำ เขตบางขุนเทียน กทม. 10150	ประสิทธิ์
Sanitary Engineer :	SIGNATURE
วิศวกรผู้ออกแบบระบบสุขาภิบาล และดับเพลิง	
นายทศวรรษ สนันฤทธิ วส. 215 ทีอยู่ บ้านเลขที 99/107 หมู่ที 3 ต.ศีรษะจรเข้น้อย อ.บางเสาธง จ.สมุทรปราการ 10540	ทศวรรษ

ISSUE/REVISION

REV.	DESCRIPTION	DATE
A	90% DEVELOPED	09/05/2026

PROJECT NAME :

GEDC 01

LOCATION:
Nikhom Phattana district, Rayong ,industrial estate,CPGC

BUILDING :

90% DEVELOPED

TITLE :

DOOR&WINDOW LAYOUT-1F

JOB NO.	SCALE 1:200
DRAWN LXP	REF.
CHECKED LJC	DWG.NO. MPK01A-90-A-DW-101
APPROVED LXD	
DATE 2026.05.09	

DOOR SCHEDULE

	DESCRIPTION	SISE(MM) WIDTH X HEIGHT
2HR FD1	G.I METAL FRAME SINGLE LEAF2 HOUR FIRE RATED SOLID STEEL DOOR PANEL	1100 X 2400
2HR FD2	G.I METAL FRAME DOUBLE LEAF 2 HOUR FIRE RATED SOLID STEEL DOOR PANEL (THE DOOR OPENS 180 DEGREES)	2200 X3100
2HR FD3	G.I METAL FRAME DOUBLE LEAF 2 HOUR FIRE RATED SOLID STEEL DOOR PANEL	1800 X 2400
2HR FD4	G.I METAL FRAME DOUBLE LEAF 2 HOUR FIRE RATED SOLID STEEL DOOR PANEL	1500 X 2200
2HR FD5	G.I METAL FRAME DOUBLE LEAF 2 HOUR FIRE RATED SOLID STEEL DOOR PANEL	900 X 2200
2HR FD6	G.I METAL FRAME DOUBLE LEAF 2 HOUR FIRE RATED SOLID STEEL DOOR PANEL (THE DOOR OPENS 90 DEGREES)	2200 X3100
2HR FD7	G.I METAL FRAME DOUBLE LEAF 2 HOUR FIRE RATED SOLID STEEL DOOR PANEL	1500 X 1700
GD1	ALUMINUM-FRAMED CASEMENT DOOR WITH ALUMINUM FIXED GLASS PANEL, TO BE EXECUTED ACCORDING TO MANUFACTURER'S DETAILS	3600 X 4000
D1	WOODEN-FRAMED CASEMENT DOOR, TO BE EXECUTED ACCORDING TO MANUFACTURER'S DETAILS	1100 X 2400
D2	G.I METAL FRAME SINGLE LEAF SOLID STEEL DOOR PANEL	1800 X 2400
D3	S/S FRAME WITH S/S REVOLVING DOOR AND CASEMENT DOOR TO MANUF'S DETAIL AND ARCH'S APPROVAL	2200 X 3500
D4	WOODEN-FRAMED CASEMENT DOOR, TO BE EXECUTED ACCORDING TO MANUFACTURER'S DETAILS	1100 X 2400
D5	PERFORATED ALUMINUM PANEL	1100 X 2400
D6	WOODEN-FRAMED CASEMENT DOOR, TO BE EXECUTED ACCORDING TO MANUFACTURER'S DETAILS	900 X 2400
RS1	ALUMINIUM ROLLER SHUTTER TO MANUF'S DETAIL	2600 X 3600
RS2	ALUMINIUM ROLLER SHUTTER TO MANUF'S DETAIL	9000 X 4000
RS3	ALUMINIUM ROLLER SHUTTER TO MANUF'S DETAIL	3600 X 4000
W1	1.4MIM THK. POWDER COATED ALUMN. FRAME WITH 6MIM THK. DARK GREY TINTED TEMPEREDGLASS TOP HUNG WINDOW TO MANUF'S DETAIL COMPLY SIRIM CERTIFICATE	2400 X 800
W2	1.4MIM THK. POWDER COATED ALUMN. FRAME WITH 6MIM THK. DARK GREY TINTED TEMPEREDGLASS TOP HUNG WINDOW TO MANUF'S DETAIL COMPLY SIRIM CERTIFICATE	1200 X 800
W3	FORCED-ENTRY CLASS WNDOW TO MANUF'SDETAIL(BULLET PROOF GLASS)	3300 X 2100
W4	FORCED-ENTRY CLASS WNDOW TO MANUF'SDETAIL	2800 X 2400
W5	FORCED-ENTRY CLASS WNDOW TO MANUF'SDETAIL	3700 X 1500
W6	1.4MM THK. POWDER COATED ALUMN.FRAME FIXED DETACHABLE LOUVERS TO MANUF'S DETAIL	φ250
W7	1.4MM THK. POWDER COATED ALUMN.FRAME FIXED DETACHABLE LOUVERS TO MANUF'S DETAIL	450 X 300
W8	1.4MM THK. POWDER COATED ALUMN.FRAME FIXED DETACHABLE LOUVERS TO MANUF'S DETAIL	450 X 250
W9	1.4MM THK. POWDER COATED ALUMN.FRAME FIXED DETACHABLE LOUVERS TO MANUF'S DETAIL	600 X 600
W10	1.4MM THK. POWDER COATED ALUMN.FRAME FIXED DETACHABLE LOUVERS TO MANUF'S DETAIL	2600 X 1600

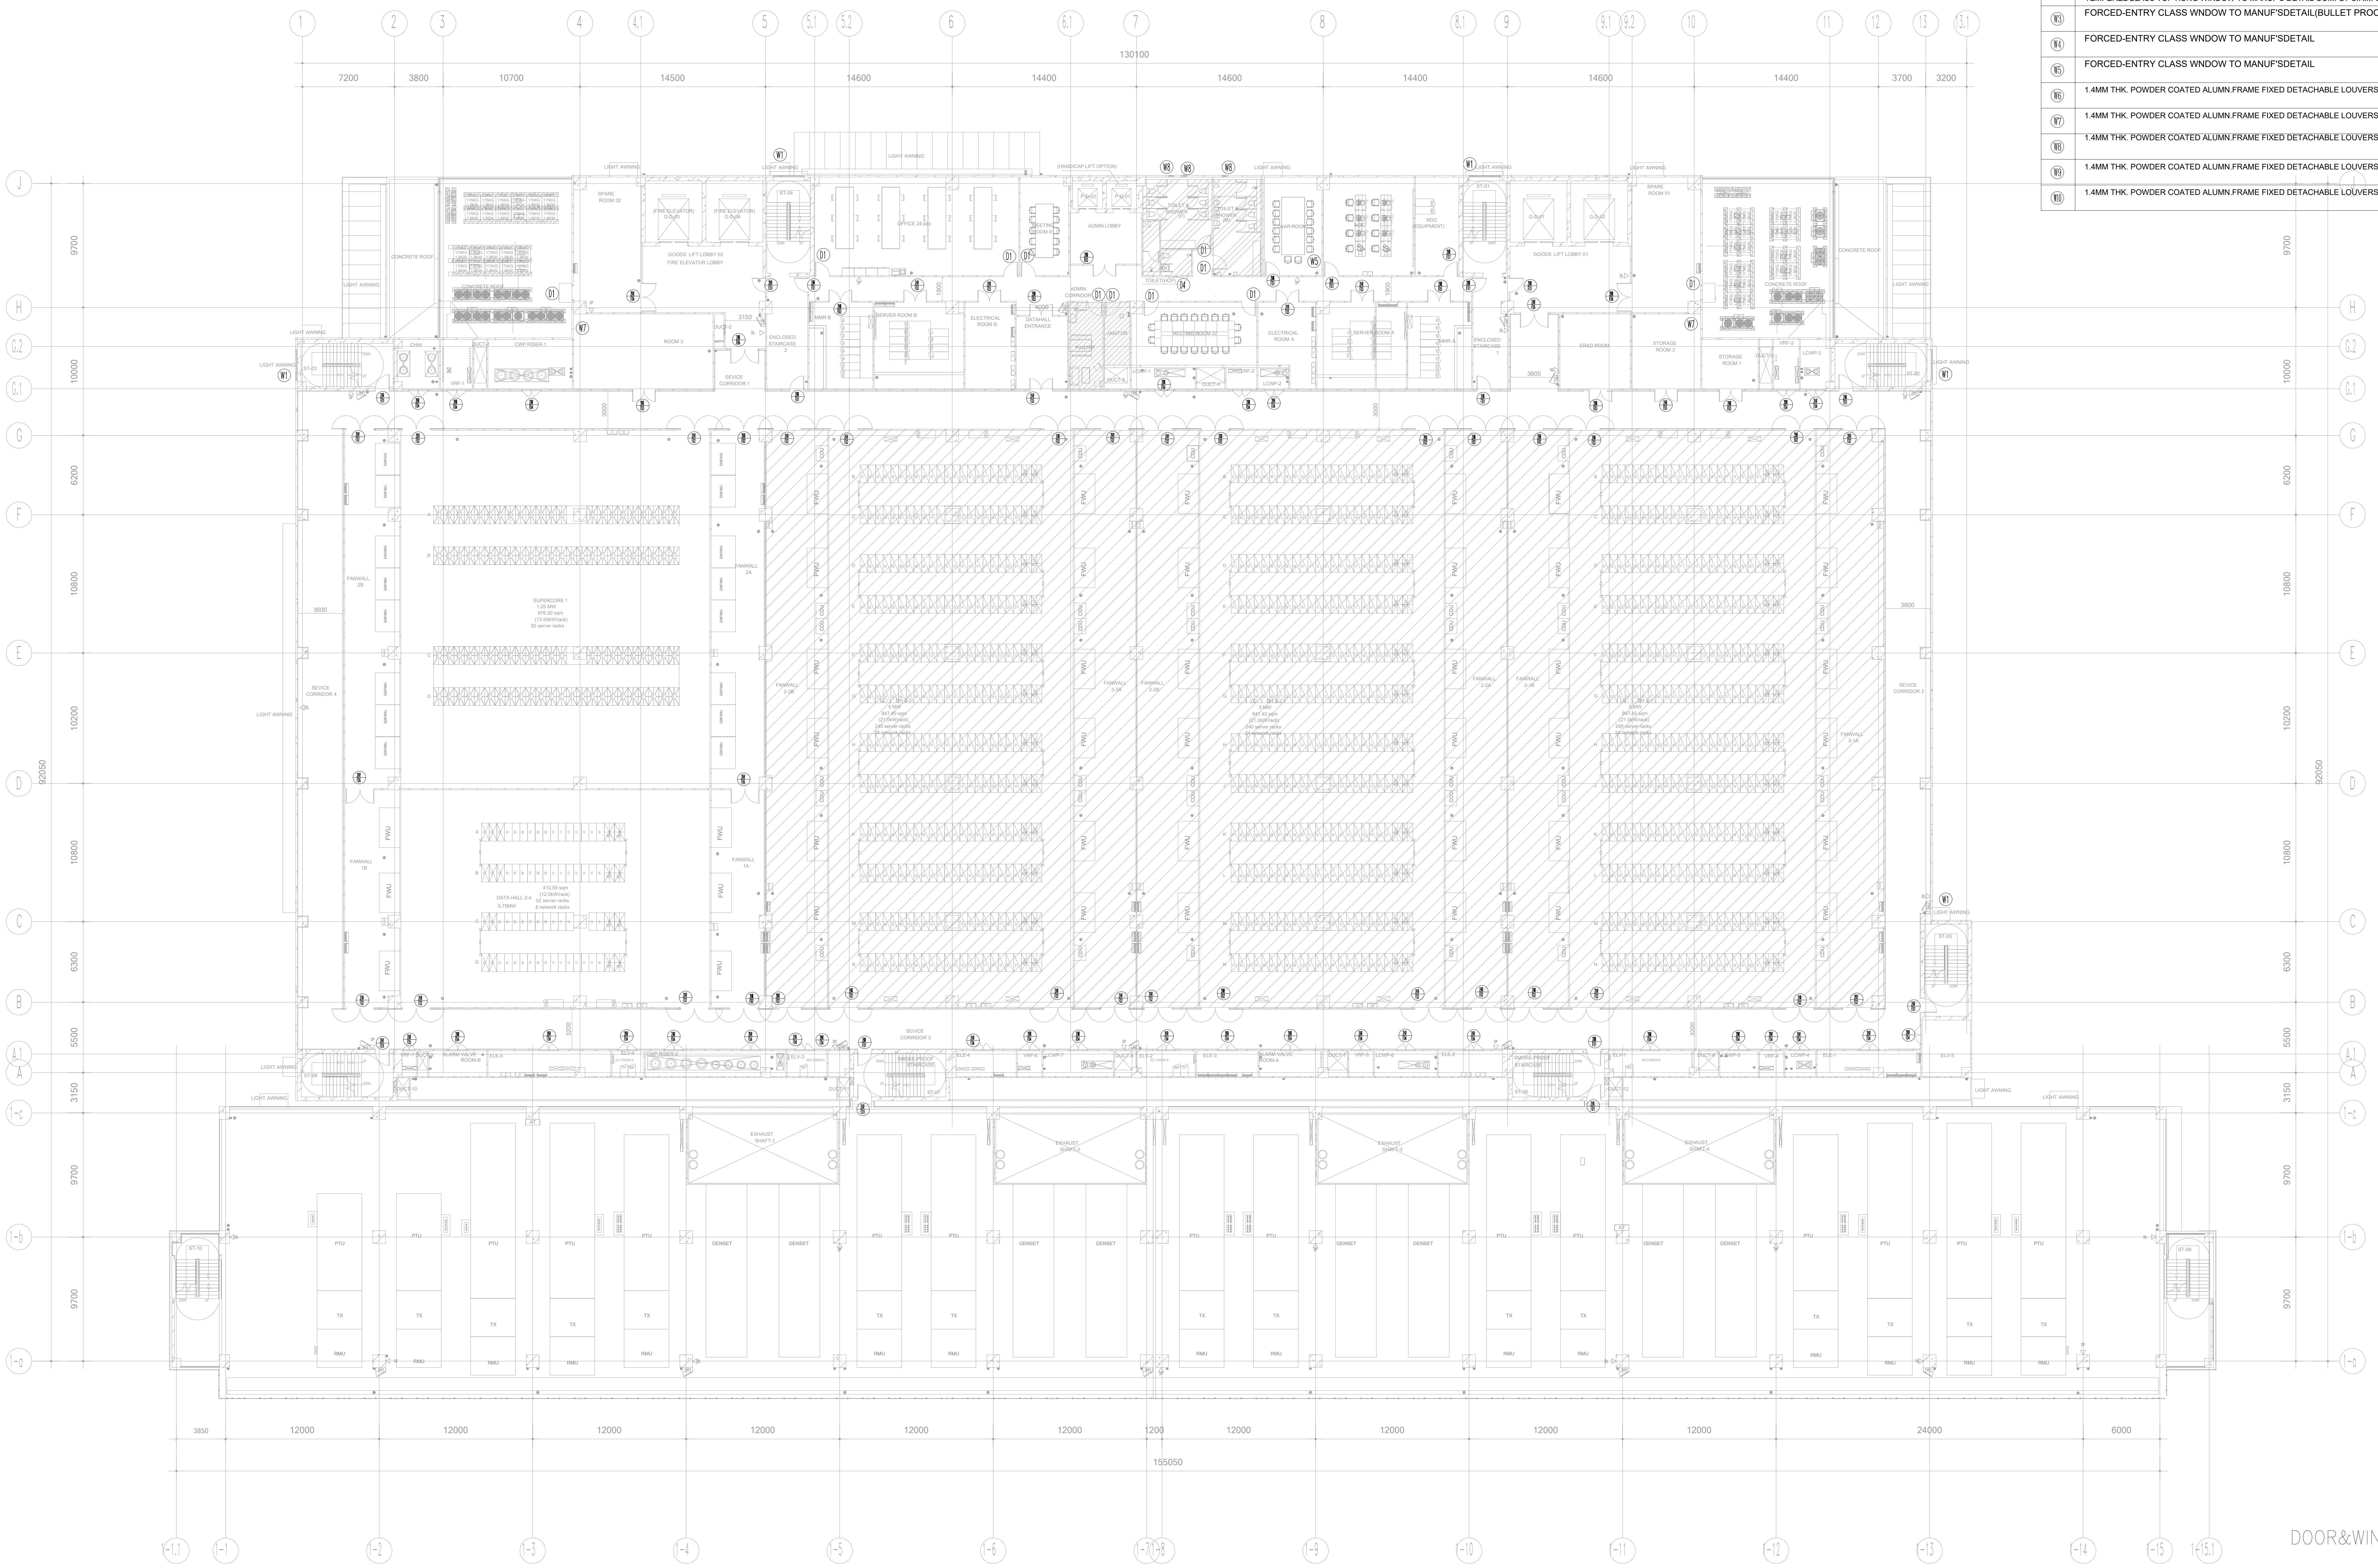

DOOR&WINDOW LAYOUT-2F

NOTE : THIS PRINT IS OF A CONFIDENTIAL NATURE, IT SHALL NOT BE TRACED,PHOTOGRAPHED,PHOTOSTATED OR REPRODUCED IN ANY MANER,NOR USED FOR ANY PURPOSE WHATSOEVER EXCEPT BY WRITTEN PERMISSION

CLIENT :

GULF EDGE DC 01

87 Wireless Road, M Thai Tower 11th. Floor, All Seasons Place, Lumpini,
Pathumwan, Bangkok 10330, Thailand

CONTRACTOR :

华西发展(泰国)有限公司
บริษัท หัวซือ ดีเวลลอปเม้นต์ (ประเทศไทย) จำกัด
HUASHI DEVELOPMENT CO.,LTD
No. 202, Room No. 1403, 14/F, Le Concorde Building,
Ratchadapisek Road, Huaykhwang Sub-District,
Huaykhwang District, Bangkok Metropolitan 10310.

CONSULTANT :

ARbay
บริษัท เอ อาร์ เบย์ จำกัด
ARbay Company Limited
31 st Floor Bangkok Insurance Building
25 South Sathorn road Thungmahamek
Sathorn Bangkok 10120 THAILAND
T +66 (0) 2286 8199
F +66 (0) 2286 2863
info@arbay.co.th

CONSULTANT :

Qbic Engineers & Architects Co.,Ltd.
8 Soi KALONG 4 SANAMBINNAM ROAD,
THASAI SUB-DISTRICT, MUANG NONTHABURI DISTRICT
, NONTHABURI.
Tel 662-950-4374
Fax 662-580-3231
E-Mail : qbic@qbic.co.th, www.qbic.co.th
QBIC ENGINEERS AND ARCHITECTS CO.,LTD.

CONSULTANT :

MITR
MITR TECHNICAL CONSULTANT CO.,LTD.
1168/8 12th FLOOR, LUMPINI TOWER BUILDING,
RAMA IV RD., THUNGMAHAMEK, SATHORN, BANGKOK 10120, THAILAND
TEL : 0-2679-9079-84
FAX : 0-2679-9085 E-mail: mitr_dd@mitr.com

Architect : SIGNATURE
ประกิต พนานุรัตน์ วสถ. 580
ทีอยู่
251/1 ถ.จารุเมือง แขวงรองเมือง เขตปทุมวัน
กรุงเทพมหานคร โทรศัพท์ 02-286-8199

Structural Engineer : SIGNATURE
วิศวกรผู้ออกแบบโครงสร้าง
ณัฐสม สงวนวงษ์ วย 1423
ทีอยู่
2/1 ซ.รามคำแหง 150 ถ.รามคำแหง
แขวง สะพานสูง เขต สะพานสูง กทม. 10240
ณัฐสม สงวนวงษ์

Structural Inspector : SIGNATURE
วิศวกรผู้ตรวจสอบโครงสร้าง
โกมล จุฑาภัทร วย 964
ทีอยู่
24/18 ซ.นวมินทร์ 129 ถ. นวมินทร์
แขวง นวลจันทร์ เขต บึงกุ่ม กทม. 10230

Electrical Engineer : SIGNATURE
วิศวกรผู้ออกแบบระบบไฟฟ้ากำลัง
นายสุภัทร บูรณวิทย์ วฟก.1265
ทีอยู่
21 ซอยทานสัมฤทธิ 13
ตำบลท่าทราย อ.เมืองนนทบุรี จ.นนทบุรี 11000
สุภัทร

Mechanical Engineer : SIGNATURE
วิศวกรผู้ออกแบบระบบเครื่องกลและปรับอากาศ
นายประสิทธิ์ เกียวสุนทร วก.1221
ทีอยู่
44/372 ซอยบางกระดี 35/1 แขวงแสมดำ
เขตบางขุนเทียน กทม. 10150
ประสิทธิ์

Sanitary Engineer : SIGNATURE
วิศวกรผู้ออกแบบระบบสุขาภิบาล และดับเพลิง
นายทศวรรษ สนันฤทธิ วส. 215
ทีอยู่
บ้านเลขที 99/107 หมู่ที 3 ต.ศีรษะจรเข้น้อย
อ.บางเสาธง จ.สมุทรปราการ 10540
ทศวรรษ

ISSUE/REVISION

REV.	DESCRIPTION	DATE
A	90% DEVELOPED	09/05/2026

PROJECT NAME :
GEDC 01
LOCATION:
Nikhom Phattana district, Rayong ,industrial estate,CPGC

BUILDING :

90% DEVELOPED

TITLE :
DOOR&WINDOW LAYOUT-2F

JOB NO.
SCALE 1:200
DRAWN LXP
REF.
CHECKED LJC
DWG.NO. MPK01A-90-A-DW-201
APPROVED LXD
DATE 2026.05.09

DOOR SCHEDULE

	DESCRIPTION	SISE(MM) WIDTH X HEIGHT
2HR FD1	G.I METAL FRAME SINGLE LEAF2 HOUR FIRE RATED SOLID STEEL DOOR PANEL	1100 X 2400
2HR FD2	G.I METAL FRAME DOUBLE LEAF 2 HOUR FIRE RATED SOLID STEEL DOOR PANEL (THE DOOR OPENS 180 DEGREES)	2200 X3100
2HR FD3	G.I METAL FRAME DOUBLE LEAF 2 HOUR FIRE RATED SOLID STEEL DOOR PANEL	1800 X 2400
2HR FD4	G.I METAL FRAME DOUBLE LEAF 2 HOUR FIRE RATED SOLID STEEL DOOR PANEL	1500 X 2200
2HR FD5	G.I METAL FRAME DOUBLE LEAF 2 HOUR FIRE RATED SOLID STEEL DOOR PANEL	900 X 2200
2HR FD6	G.I METAL FRAME DOUBLE LEAF 2 HOUR FIRE RATED SOLID STEEL DOOR PANEL (THE DOOR OPENS 90 DEGREES)	2200 X3100
2HR FD7	G.I METAL FRAME DOUBLE LEAF 2 HOUR FIRE RATED SOLID STEEL DOOR PANEL	1500 X 1700
GD1	ALUMINUM-FRAMED CASEMENT DOOR WITH ALUMINUM FIXED GLASS PANEL, TO BE EXECUTED ACCORDING TO MANUFACTURER'S DETAILS	3600 X 4000
D1	WOODEN-FRAMED CASEMENT DOOR, TO BE EXECUTED ACCORDING TO MANUFACTURER'S DETAILS	1100 X 2400
D2	G.I METAL FRAME SINGLE LEAF SOLID STEEL DOOR PANEL	1800 X 2400
D3	S/S FRAME WITH S/S REVOLVING DOOR AND CASEMENT DOOR TO MANUF'S DETAIL AND ARCH'S APPROVAL	2200 X 3500
D4	WOODEN-FRAMED CASEMENT DOOR, TO BE EXECUTED ACCORDING TO MANUFACTURER'S DETAILS	1100 X 2400
D5	PERFORATED ALUMINUM PANEL	1100 X 2400
D6	WOODEN-FRAMED CASEMENT DOOR, TO BE EXECUTED ACCORDING TO MANUFACTURER'S DETAILS	900 X 2400
RS1	ALUMINIUM ROLLER SHUTTER TO MANUF'S DETAIL	2600 X 3600
RS2	ALUMINIUM ROLLER SHUTTER TO MANUF'S DETAIL	9000 X 4000
RS3	ALUMINIUM ROLLER SHUTTER TO MANUF'S DETAIL	3600 X 4000
W1	1.4MIM THK. POWDER COATED ALUMN. FRAME WITH 6MIM THK. DARK GREY TINTED TEMPEREDGLASS TOP HUNG WINDOW TO MANUF'S DETAIL COMPLY SIRIM CERTIFICATE	2400 X 800
W2	1.4MIM THK. POWDER COATED ALUMN. FRAME WITH 6MIM THK. DARK GREY TINTED TEMPEREDGLASS TOP HUNG WINDOW TO MANUF'S DETAIL COMPLY SIRIM CERTIFICATE	1200 X 800
W3	FORCED-ENTRY CLASS WNDOW TO MANUF'SDETAIL(BULLET PROOF GLASS)	3300 X 2100
W4	FORCED-ENTRY CLASS WNDOW TO MANUF'SDETAIL	2800 X 2400
W5	FORCED-ENTRY CLASS WNDOW TO MANUF'SDETAIL	3700 X 1500
W6	1.4MM THK. POWDER COATED ALUMN.FRAME FIXED DETACHABLE LOUVERS TO MANUF'S DETAIL	φ250
W7	1.4MM THK. POWDER COATED ALUMN.FRAME FIXED DETACHABLE LOUVERS TO MANUF'S DETAIL	450 X 300
W8	1.4MM THK. POWDER COATED ALUMN.FRAME FIXED DETACHABLE LOUVERS TO MANUF'S DETAIL	450 X 250
W9	1.4MM THK. POWDER COATED ALUMN.FRAME FIXED DETACHABLE LOUVERS TO MANUF'S DETAIL	600 X 600
W10	1.4MM THK. POWDER COATED ALUMN.FRAME FIXED DETACHABLE LOUVERS TO MANUF'S DETAIL	2600 X 1600

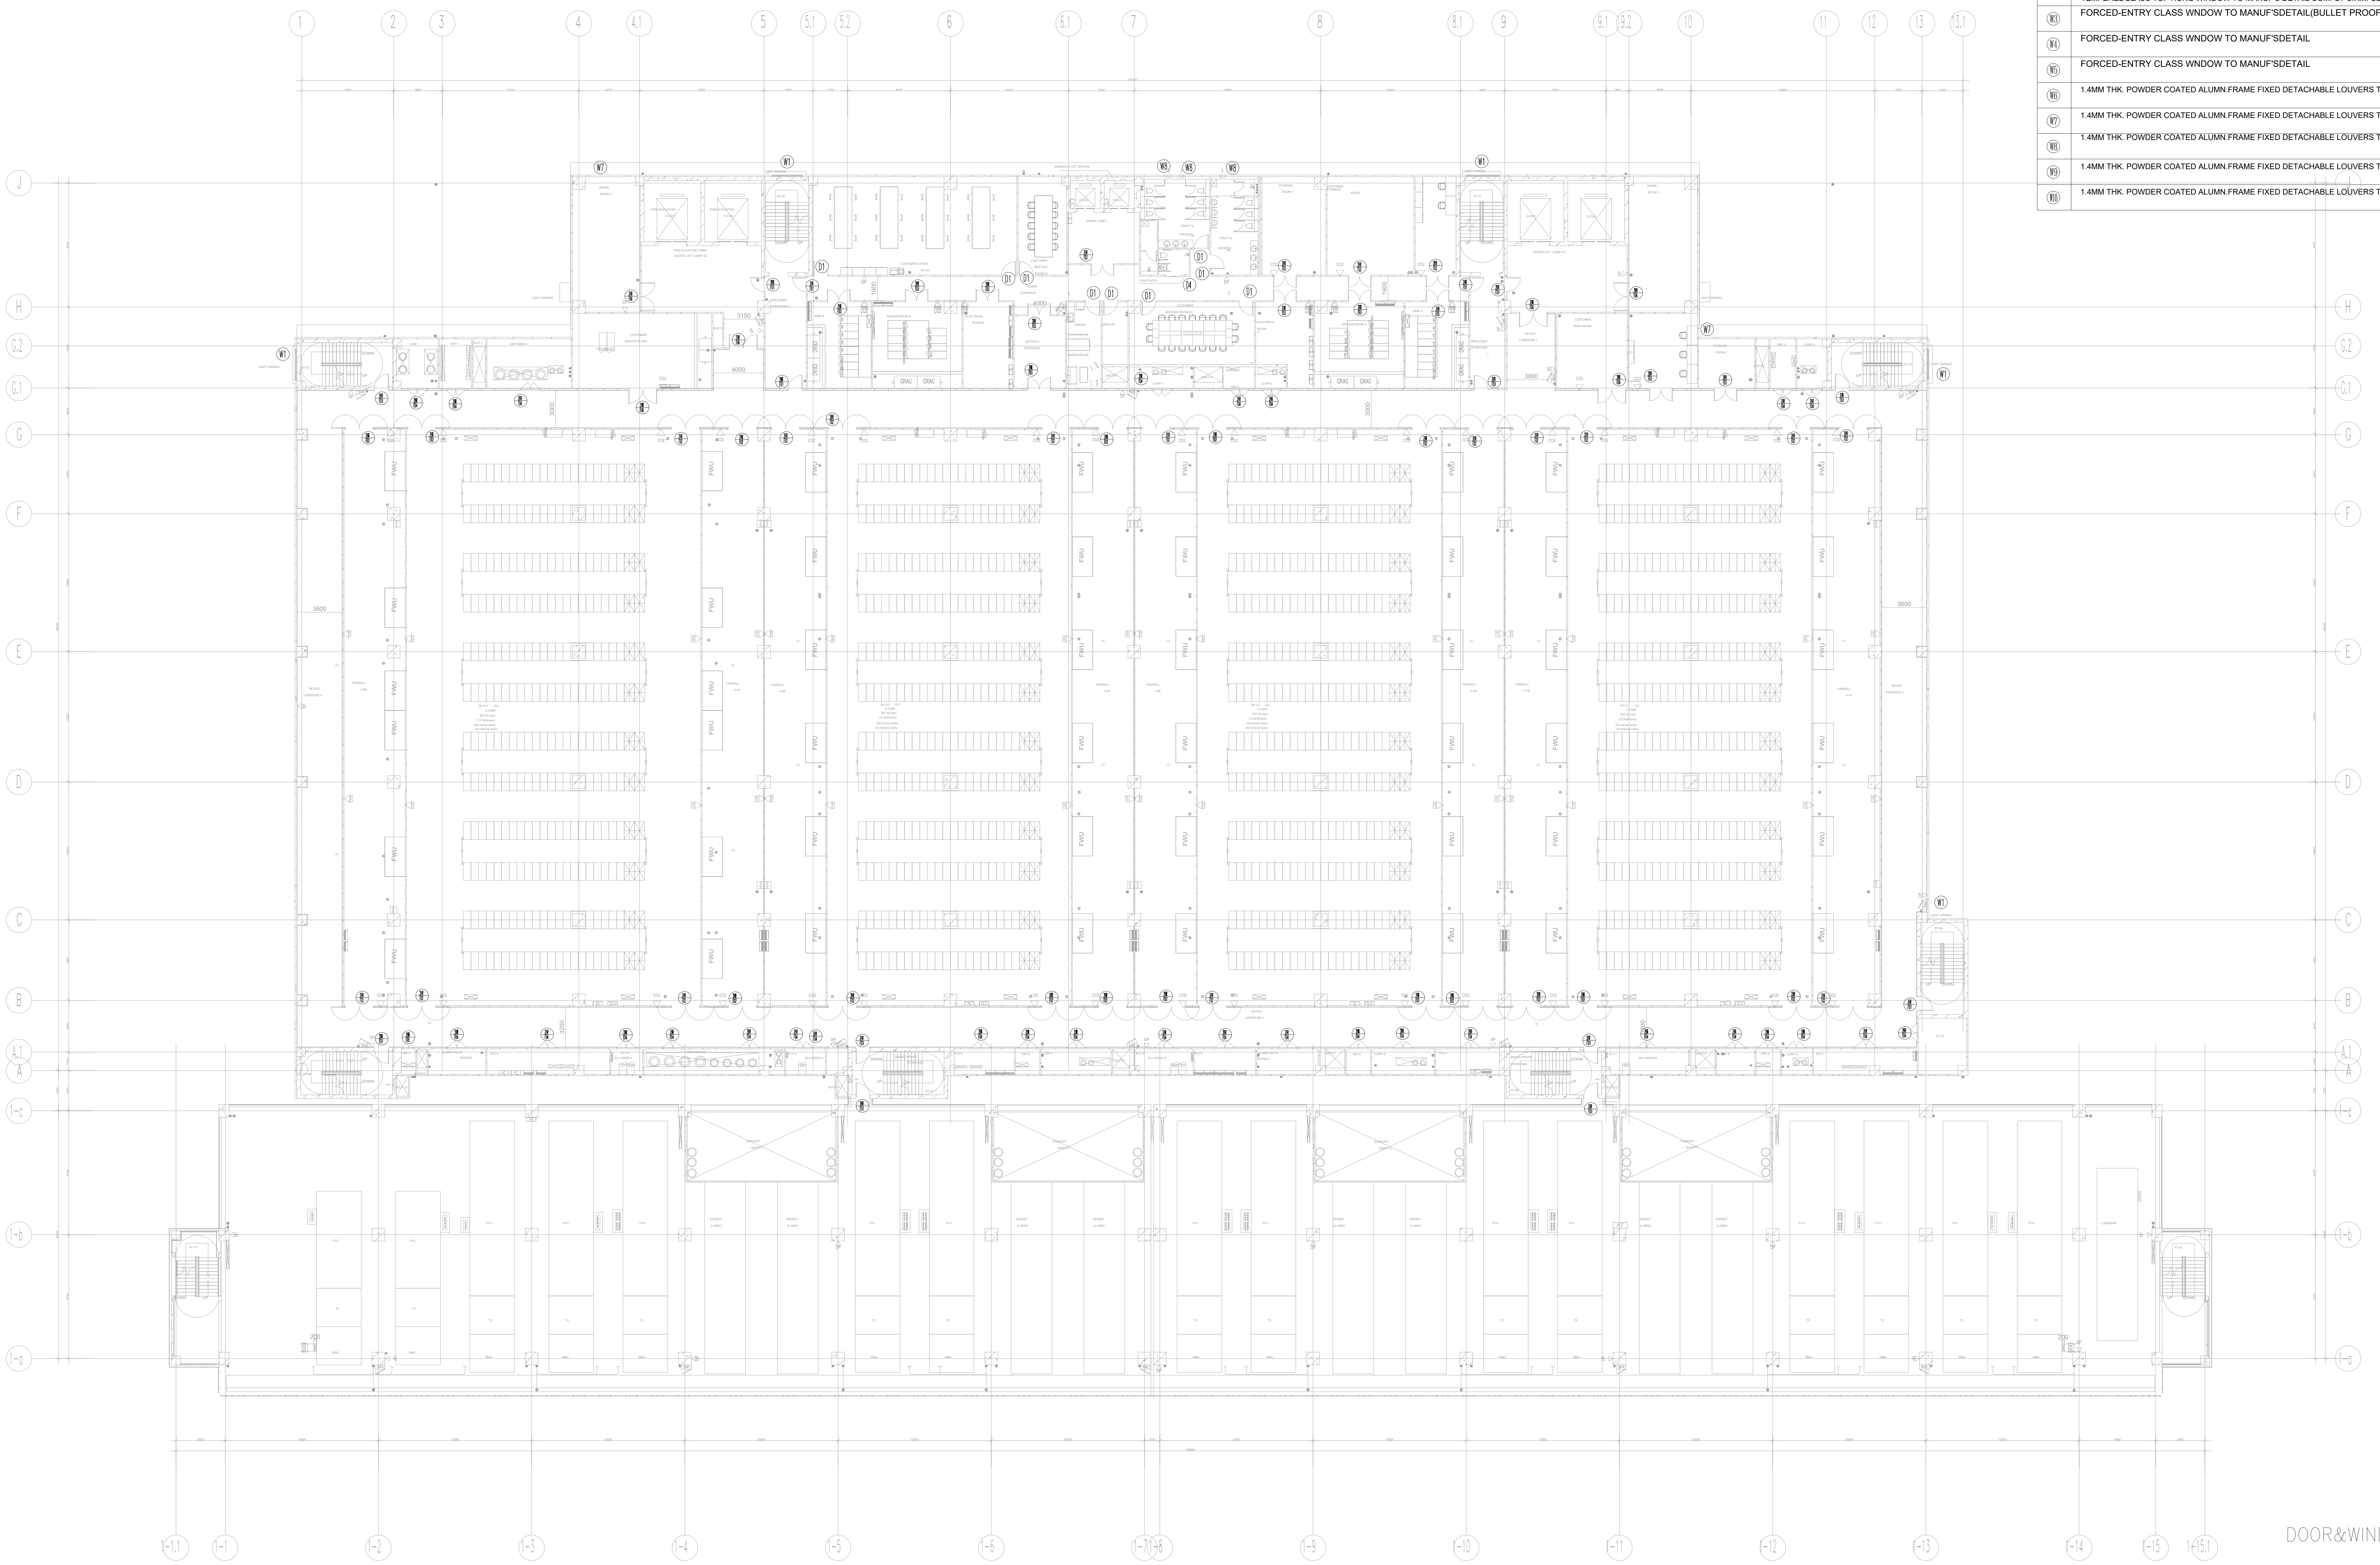

DOOR&WINDOW LAYOUT-3F

NOTE : THIS PRINT IS OF A CONFIDENTIAL NATURE, IT SHALL NOT BE TRACED,PHOTOGRAPHED,PHOTOSTATED OR REPRODUCED IN ANY MANER,NOR USED FOR ANY PURPOSE WHATSOEVER EXCEPT BY WRITTEN PERMISSION

CLIENT :

GULF EDGE DC 01

87 Wireless Road, M Thai Tower 11th. Floor, All Seasons Place, Lumpini,
Pathumwan, Bangkok 10330, Thailand

CONTRACTOR :

华西发展(泰国)有限公司
บริษัท หัวซือ ดีเวลลอปเม้นต์ (ประเทศไทย) จำกัด
HUASHI DEVELOPMENT CO.,LTD
No. 202, Room No. 1403, 14/F, Le Concorde Building,
Ratchadapisek Road, Huaykhwang Sub-District,
Huaykhwang District, Bangkok Metropolitan 10310.

CONSULTANT :

ARbay
บริษัท เอ อาร์ เบย์ จำกัด
ARbay Company Limited
31 st Floor Bangkok Insurance Building
25 South Sathorn road Thungmahamek
Sathorn Bangkok 10120 THAILAND
T +66 (0) 2286 8199
F +66 (0) 2286 2863
info@arbay.co.th

CONSULTANT :

Qbic Engineers & Architects Co.,Ltd.
8 Soi KALONG 4 SANAMBINNAM ROAD,
THASAI SUB-DISTRICT, MUANG NONTHABURI DISTRICT
, NONTHABURI.
Tel 662-950-4374
Fax 662-580-3231
E-Mail : qbic@qbic.co.th, www.qbic.co.th
QBIC ENGINEERS AND ARCHITECTS CO.,LTD.

CONSULTANT :

MITR
MITR TECHNICAL CONSULTANT CO.,LTD.
1168/8 12th FLOOR, LUMPINI TOWER BUILDING,
RAMA IV RD., THUNGMAHAMEK, SATHORN, BANGKOK 10120, THAILAND
TEL : 0-2679-9079-84
FAX : 0-2679-9085 E-mail: mitr_dd@mitr.com

Architect :	SIGNATURE
ประกิต พนานุรัตน์ วสถ. 580 ที่อยู่ 251/1 ถ.จารุเมือง แขวงรองเมือง เขตปทุมวัน กรุงเทพมหานคร โทรศัพท์ 02-286-8199	
Structural Engineer :	**SIGNATURE**
วิศวกรผู้ออกแบบโครงสร้าง	
ณัฐสม สงวนวงษ์ วย 1423 ที่อยู่ 2/1 ซ.รามคำแหง 150 ถ.รามคำแหง แขวง สะพานสูง เขต สะพานสูง กทม. 10240	ณัฐสม สงวนวงษ์
Structural Inspector :	**SIGNATURE**
วิศวกรผู้ตรวจสอบโครงสร้าง	
โกมล จุฑาภัทร วย 964 ที่อยู่ 24/18 ซ.นวมินทร์ 129 ถ. นวมินทร์ แขวง นวลจันทร์ เขต บึงกุ่ม กทม. 10230	
Electrical Engineer :	**SIGNATURE**
วิศวกรผู้ออกแบบระบบไฟฟ้ากำลัง	
นายสุภัทร บูรณวิทย์ วฟก.1265 ที่อยู่ 21 ซอยทานสัมฤทธิ 13 ตำบลท่าทราย อ.เมืองนนทบุรี จ.นนทบุรี 11000	สุภัทร บูรณวิทย์
Mechanical Engineer :	**SIGNATURE**
วิศวกรผู้ออกแบบระบบเครื่องกลและปรับอากาศ	
นายประสิทธิ์ เกียวสุนทร วก.1221 ที่อยู่ 44/372 ซอยบางกระดี 35/1 แขวงแสมดำ เขตบางขุนเทียน กทม. 10150	ประสิทธิ์
Sanitary Engineer :	**SIGNATURE**
วิศวกรผู้ออกแบบระบบสุขาภิบาล และดับเพลิง	
นายทศวรรษ สนั่นฤทธิ วส. 215 ที่อยู่ บ้านเลขที่ 99/107 หมู่ที่ 3 ต.ศีรษะจรเข้น้อย อ.บางเสาธง จ.สมุทรปราการ 10540	ทศวรรษ

ISSUE/REVISION

REV.	DESCRIPTION	DATE
A	90% DEVELOPED	09/05/2026

PROJECT NAME :

GEDC 01

LOCATION:
Nikhom Phattana district, Rayong ,industrial estate,CPGC

BUILDING :

90% DEVELOPED

TITLE :

DOOR&WINDOW LAYOUT-3F

JOB NO.	SCALE 1:200
DRAWN LXP	REF.
CHECKED LJC	DWG.NO. MPK01A-90-A-DW-301
APPROVED LXD	
DATE 2026.05.09	

DOOR SCHEDULE

	DESCRIPTION	SISE(MM) WIDTH X HEIGHT
2HR FD1	G.I METAL FRAME SINGLE LEAF2 HOUR FIRE RATED SOLID STEEL DOOR PANEL	1100 X 2400
2HR FD2	G.I METAL FRAME DOUBLE LEAF 2 HOUR FIRE RATED SOLID STEEL DOOR PANEL (THE DOOR OPENS 180 DEGREES)	2200 X3100
2HR FD3	G.I METAL FRAME DOUBLE LEAF 2 HOUR FIRE RATED SOLID STEEL DOOR PANEL	1800 X 2400
2HR FD4	G.I METAL FRAME DOUBLE LEAF 2 HOUR FIRE RATED SOLID STEEL DOOR PANEL	1500 X 2200
2HR FD5	G.I METAL FRAME DOUBLE LEAF 2 HOUR FIRE RATED SOLID STEEL DOOR PANEL	900 X 2200
2HR FD6	G.I METAL FRAME DOUBLE LEAF 2 HOUR FIRE RATED SOLID STEEL DOOR PANEL (THE DOOR OPENS 90 DEGREES)	2200 X3100
2HR FD7	G.I METAL FRAME DOUBLE LEAF 2 HOUR FIRE RATED SOLID STEEL DOOR PANEL	1500 X 1700
GD1	ALUMINUM-FRAMED CASEMENT DOOR WITH ALUMINUM FIXED GLASS PANEL, TO BE EXECUTED ACCORDING TO MANUFACTURER'S DETAILS	3600 X 4000
D1	WOODEN-FRAMED CASEMENT DOOR, TO BE EXECUTED ACCORDING TO MANUFACTURER'S DETAILS	1100 X 2400
D2	G.I METAL FRAME SINGLE LEAF SOLID STEEL DOOR PANEL	1800 X 2400
D3	S/S FRAME WITH S/S REVOLVING DOOR AND CASEMENT DOOR TO MANUF'S DETAIL AND ARCH'S APPROVAL	2200 X 3500
D4	WOODEN-FRAMED CASEMENT DOOR, TO BE EXECUTED ACCORDING TO MANUFACTURER'S DETAILS	1100 X 2400
D5	PERFORATED ALUMINUM PANEL	1100 X 2400
D6	WOODEN-FRAMED CASEMENT DOOR, TO BE EXECUTED ACCORDING TO MANUFACTURER'S DETAILS	900 X 2400
RS1	ALUMINIUM ROLLER SHUTTER TO MANUF'S DETAIL	2600 X 3600
RS2	ALUMINIUM ROLLER SHUTTER TO MANUF'S DETAIL	9000 X 4000
RS3	ALUMINIUM ROLLER SHUTTER TO MANUF'S DETAIL	3600 X 4000
W1	1.4MIM THK. POWDER COATED ALUMN. FRAME WITH 6MIM THK. DARK GREY TINTED TEMPEREDGLASS TOP HUNG WINDOW TO MANUF'S DETAIL COMPLY SIRIM CERTIFICATE	2400 X 800
W2	1.4MIM THK. POWDER COATED ALUMN. FRAME WITH 6MIM THK. DARK GREY TINTED TEMPEREDGLASS TOP HUNG WINDOW TO MANUF'S DETAIL COMPLY SIRIM CERTIFICATE	1200 X 800
W3	FORCED-ENTRY CLASS WNDOW TO MANUF'SDETAIL(BULLET PROOF GLASS)	3300 X 2100
W4	FORCED-ENTRY CLASS WNDOW TO MANUF'SDETAIL	2800 X 2400
W5	FORCED-ENTRY CLASS WNDOW TO MANUF'SDETAIL	3700 X 1500
W6	1.4MM THK. POWDER COATED ALUMN.FRAME FIXED DETACHABLE LOUVERS TO MANUF'S DETAIL	φ250
W7	1.4MM THK. POWDER COATED ALUMN.FRAME FIXED DETACHABLE LOUVERS TO MANUF'S DETAIL	450 X 300
W8	1.4MM THK. POWDER COATED ALUMN.FRAME FIXED DETACHABLE LOUVERS TO MANUF'S DETAIL	450 X 250
W9	1.4MM THK. POWDER COATED ALUMN.FRAME FIXED DETACHABLE LOUVERS TO MANUF'S DETAIL	600 X 600
W10	1.4MM THK. POWDER COATED ALUMN.FRAME FIXED DETACHABLE LOUVERS TO MANUF'S DETAIL	2600 X 1600

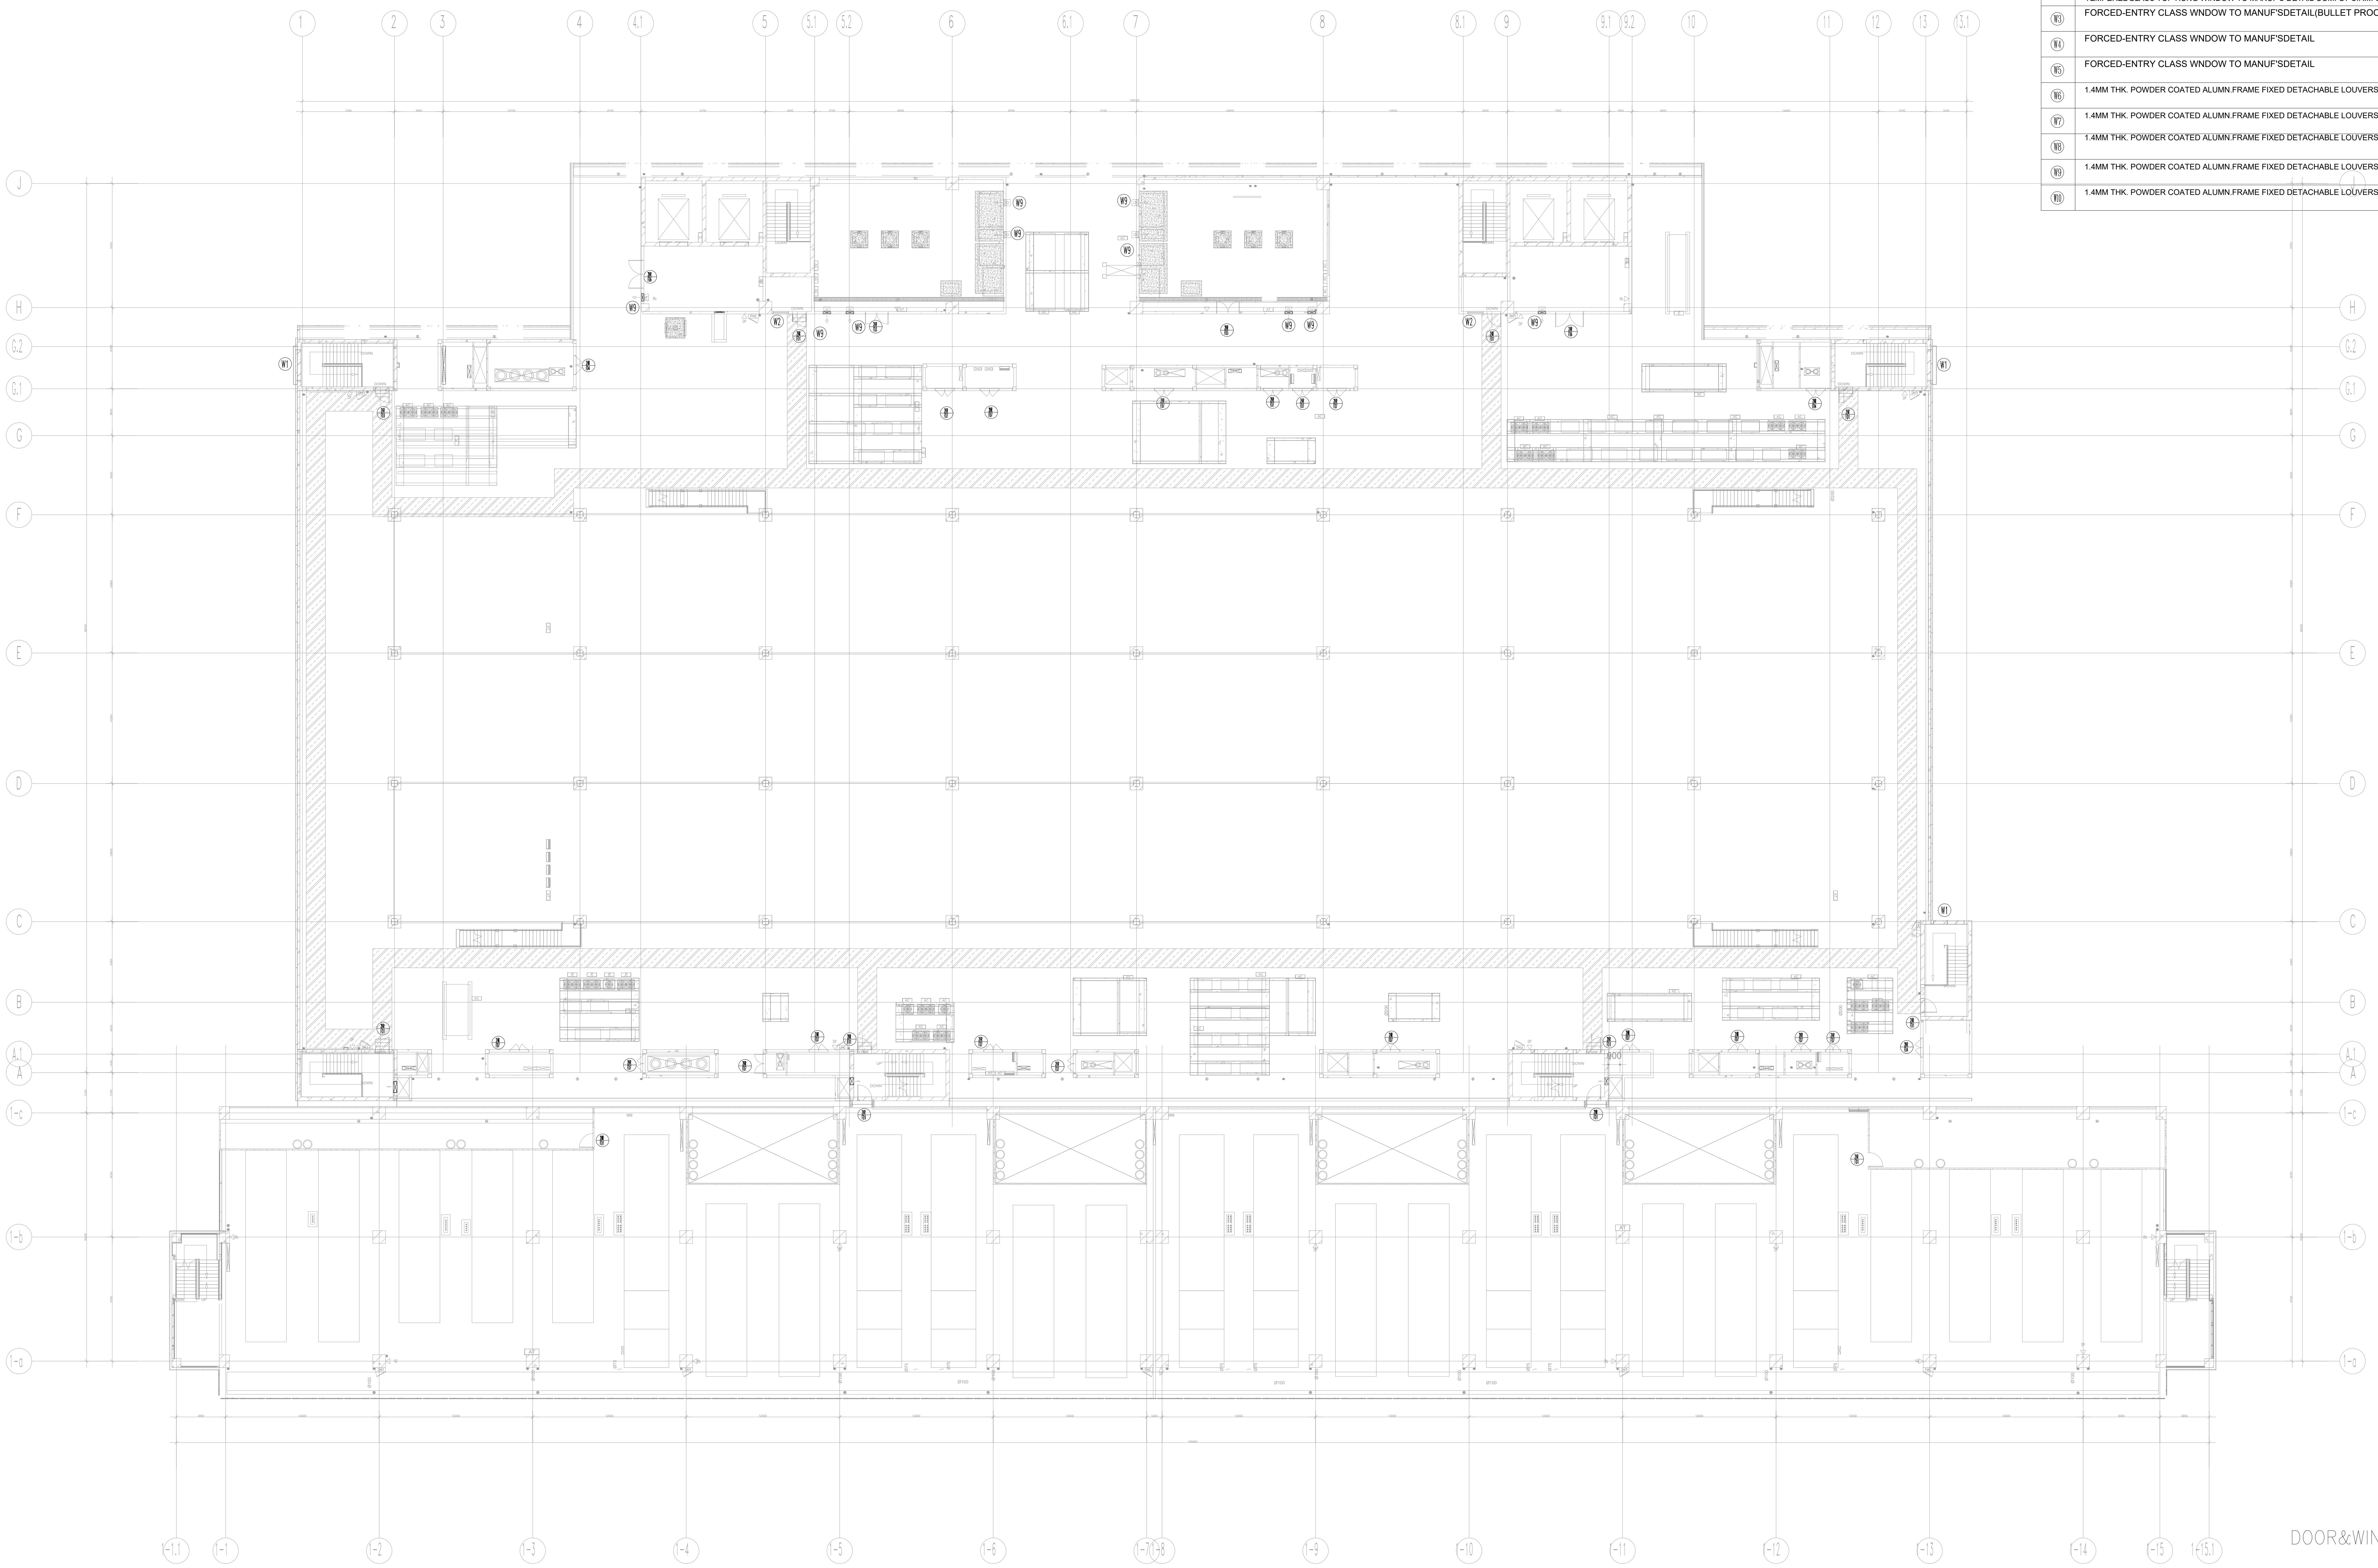

DOOR&WINDOW LAYOUT-RF

CLIENT :

GULF EDGE DC 01

87 Wireless Road, M Thai Tower 11th. Floor, All Seasons Place, Lumpini,
Pathumwan, Bangkok 10330, Thailand

CONTRACTOR :

华西发展(泰国)有限公司
บริษัท หัวซือ ดีเวลลอปเม้นต์ (ประเทศไทย) จำกัด
HUASHI DEVELOPMENT CO.,LTD
No. 202, Room No. 1403, 14/F, Le Concorde Building,
Ratchadapisek Road, Huaykhwang Sub-District,
Huaykhwang District, Bangkok Metropolitan 10310.

CONSULTANT :

ARbay
บริษัท เอ อาร์ เบย์ จำกัด
ARbay Company Limited
31 st Floor Bangkok Insurance Building
25 South Sathorn road Thungmahamek
Sathorn Bangkok 10120 THAILAND
T +66 (0) 2286 8199
F +66 (0) 2286 2863
info@arbay.co.th

CONSULTANT :

Qbic Engineers & Architects Co.,Ltd.
8 Soi KALONG 4 SANAMBINNAM ROAD,
THASAI SUB-DISTRICT, MUANG NONTHABURI DISTRICT
, NONTHABURI.
Tel 662-950-4374
Fax 662-580-3231
E-Mail : qbic@qbic.co.th, www.qbic.co.th
QBIC ENGINEERS AND ARCHITECTS CO.,LTD.

CONSULTANT :

MITR
MITR TECHNICAL CONSULTANT CO.,LTD.
1168/8 12th FLOOR, LUMPINI TOWER BUILDING,
RAMA IV RD., THUNGMAHAMEK, SATHORN, BANGKOK 10120, THAILAND
TEL : 0-2679-9079-84
FAX : 0-2679-9085 E-mail: mitr_dd@mitr.com

Architect :	SIGNATURE
ประกิต พนานุรัตน์ วสถ. 580 ทีอยู่ 251/1 ถ.จารุเมือง แขวงรองเมือง เขตปทุมวัน กรุงเทพมหานคร โทรศัพท์ 02-286-8199	
Structural Engineer :	SIGNATURE
วิศวกรผู้ออกแบบโครงสร้าง	
ณัฐสม สงวนวงษ์ วย 1423 ทีอยู่ 2/1 ซ.รามคำแหง 150 ถ.รามคำแหง แขวง สะพานสูง เขต สะพานสูง กทม. 10240	ณัฐสม สงวนวงษ์
Structural Inspector :	SIGNATURE
วิศวกรผู้ตรวจสอบโครงสร้าง	
โกมล จุฑาภัทร วย 964 ทีอยู่ 24/18 ซ.นวมินทร์ 129 ถ. นวมินทร์ แขวง นวลจันทร์ เขต บึงกุ่ม กทม. 10230	
Electrical Engineer :	SIGNATURE
วิศวกรผู้ออกแบบระบบไฟฟ้ากำลัง	
นายสุภัทร บูรณวิทย์ วฟก.1265 ทีอยู่ 21 ซอยทานสัมฤทธิ 13 ตำบลท่าทราย อ.เมืองนนทบุรี จ.นนทบุรี 11000	
Mechanical Engineer :	SIGNATURE
วิศวกรผู้ออกแบบระบบเครื่องกลและปรับอากาศ	
นายประสิทธิ เกียวสุนทร วก.1221 ทีอยู่ 44/372 ซอยบางกระดี 35/1 แขวงแสมดำ เขตบางขุนเทียน กทม. 10150	ประสิทธิ์
Sanitary Engineer :	SIGNATURE
วิศวกรผู้ออกแบบระบบสุขาภิบาล และดับเพลิง	
นายทศวรรษ สนันฤทธิ วส. 215 ทีอยู่ บ้านเลขที 99/107 หมู่ที 3 ต.ศีรษะจรเข้น้อย อ.บางเสาธง จ.สมุทรปราการ 10540	ทศวรรษ

ISSUE/REVISION

REV.	DESCRIPTION	DATE
A	90% DEVELOPED	09/05/2026

PROJECT NAME :
GEDC 01
LOCATION:
Nikhom Phattana district, Rayong ,industrial estate,CPGC

BUILDING :

90% DEVELOPED

TITLE :
DOOR&WINDOW LAYOUT-RF

JOB NO.	SCALE 1:200
DRAWN LXP	REF.
CHECKED LJC	DWG.NO. MPK01A-90-A-DW-401
APPROVED LXD	
DATE 2026.05.09	

DOOR SCHEDULE

	DESCRIPTION	SISE(MM) WIDTH X HEIGHT
2HR FD1	G.I METAL FRAME SINGLE LEAF2 HOUR FIRE RATED SOLID STEEL DOOR PANEL	1100 X 2400
2HR FD2	G.I METAL FRAME DOUBLE LEAF 2 HOUR FIRE RATED SOLID STEEL DOOR PANEL (THE DOOR OPENS 180 DEGREES)	2200 X3100
2HR FD3	G.I METAL FRAME DOUBLE LEAF 2 HOUR FIRE RATED SOLID STEEL DOOR PANEL	1800 X 2400
2HR FD4	G.I METAL FRAME DOUBLE LEAF 2 HOUR FIRE RATED SOLID STEEL DOOR PANEL	1500 X 2200
2HR FD5	G.I METAL FRAME DOUBLE LEAF 2 HOUR FIRE RATED SOLID STEEL DOOR PANEL	900 X 2200
2HR FD6	G.I METAL FRAME DOUBLE LEAF 2 HOUR FIRE RATED SOLID STEEL DOOR PANEL (THE DOOR OPENS 90 DEGREES)	2200 X3100
2HR FD7	G.I METAL FRAME DOUBLE LEAF 2 HOUR FIRE RATED SOLID STEEL DOOR PANEL	1500 X 1700
GD1	ALUMINUM-FRAMED CASEMENT DOOR WITH ALUMINUM FIXED GLASS PANEL, TO BE EXECUTED ACCORDING TO MANUFACTURER'S DETAILS	3600 X 4000
D1	WOODEN-FRAMED CASEMENT DOOR, TO BE EXECUTED ACCORDING TO MANUFACTURER'S DETAILS	1100 X 2400
D2	G.I METAL FRAME SINGLE LEAF SOLID STEEL DOOR PANEL	1800 X 2400
D3	S/S FRAME WITH S/S REVOLVING DOOR AND CASEMENT DOOR TO MANUF'S DETAIL AND ARCH'S APPROVAL	2200 X 3500
D4	WOODEN-FRAMED CASEMENT DOOR, TO BE EXECUTED ACCORDING TO MANUFACTURER'S DETAILS	1100 X 2400
D5	PERFORATED ALUMINUM PANEL	1100 X 2400
D6	WOODEN-FRAMED CASEMENT DOOR, TO BE EXECUTED ACCORDING TO MANUFACTURER'S DETAILS	900 X 2400
RS1	ALUMINIUM ROLLER SHUTTER TO MANUF'S DETAIL	2600 X 3600
RS2	ALUMINIUM ROLLER SHUTTER TO MANUF'S DETAIL	9000 X 4000
RS3	ALUMINIUM ROLLER SHUTTER TO MANUF'S DETAIL	3600 X 4000
W1	1.4MIM THK. POWDER COATED ALUMN. FRAME WITH 6MIM THK. DARK GREY TINTED TEMPEREDGLASS TOP HUNG WINDOW TO MANUF'S DETAIL COMPLY SIRIM CERTIFICATE	2400 X 800
W2	1.4MIM THK. POWDER COATED ALUMN. FRAME WITH 6MIM THK. DARK GREY TINTED TEMPEREDGLASS TOP HUNG WINDOW TO MANUF'S DETAIL COMPLY SIRIM CERTIFICATE	1200 X 800
W3	FORCED-ENTRY CLASS WNDOW TO MANUF'SDETAIL(BULLET PROOF GLASS)	3300 X 2100
W4	FORCED-ENTRY CLASS WNDOW TO MANUF'SDETAIL	2800 X 2400
W5	FORCED-ENTRY CLASS WNDOW TO MANUF'SDETAIL	3700 X 1500
W6	1.4MM THK. POWDER COATED ALUMN.FRAME FIXED DETACHABLE LOUVERS TO MANUF'S DETAIL	φ250
W7	1.4MM THK. POWDER COATED ALUMN.FRAME FIXED DETACHABLE LOUVERS TO MANUF'S DETAIL	450 X 300
W8	1.4MM THK. POWDER COATED ALUMN.FRAME FIXED DETACHABLE LOUVERS TO MANUF'S DETAIL	450 X 250
W9	1.4MM THK. POWDER COATED ALUMN.FRAME FIXED DETACHABLE LOUVERS TO MANUF'S DETAIL	600 X 600
W10	1.4MM THK. POWDER COATED ALUMN.FRAME FIXED DETACHABLE LOUVERS TO MANUF'S DETAIL	2600 X 1600

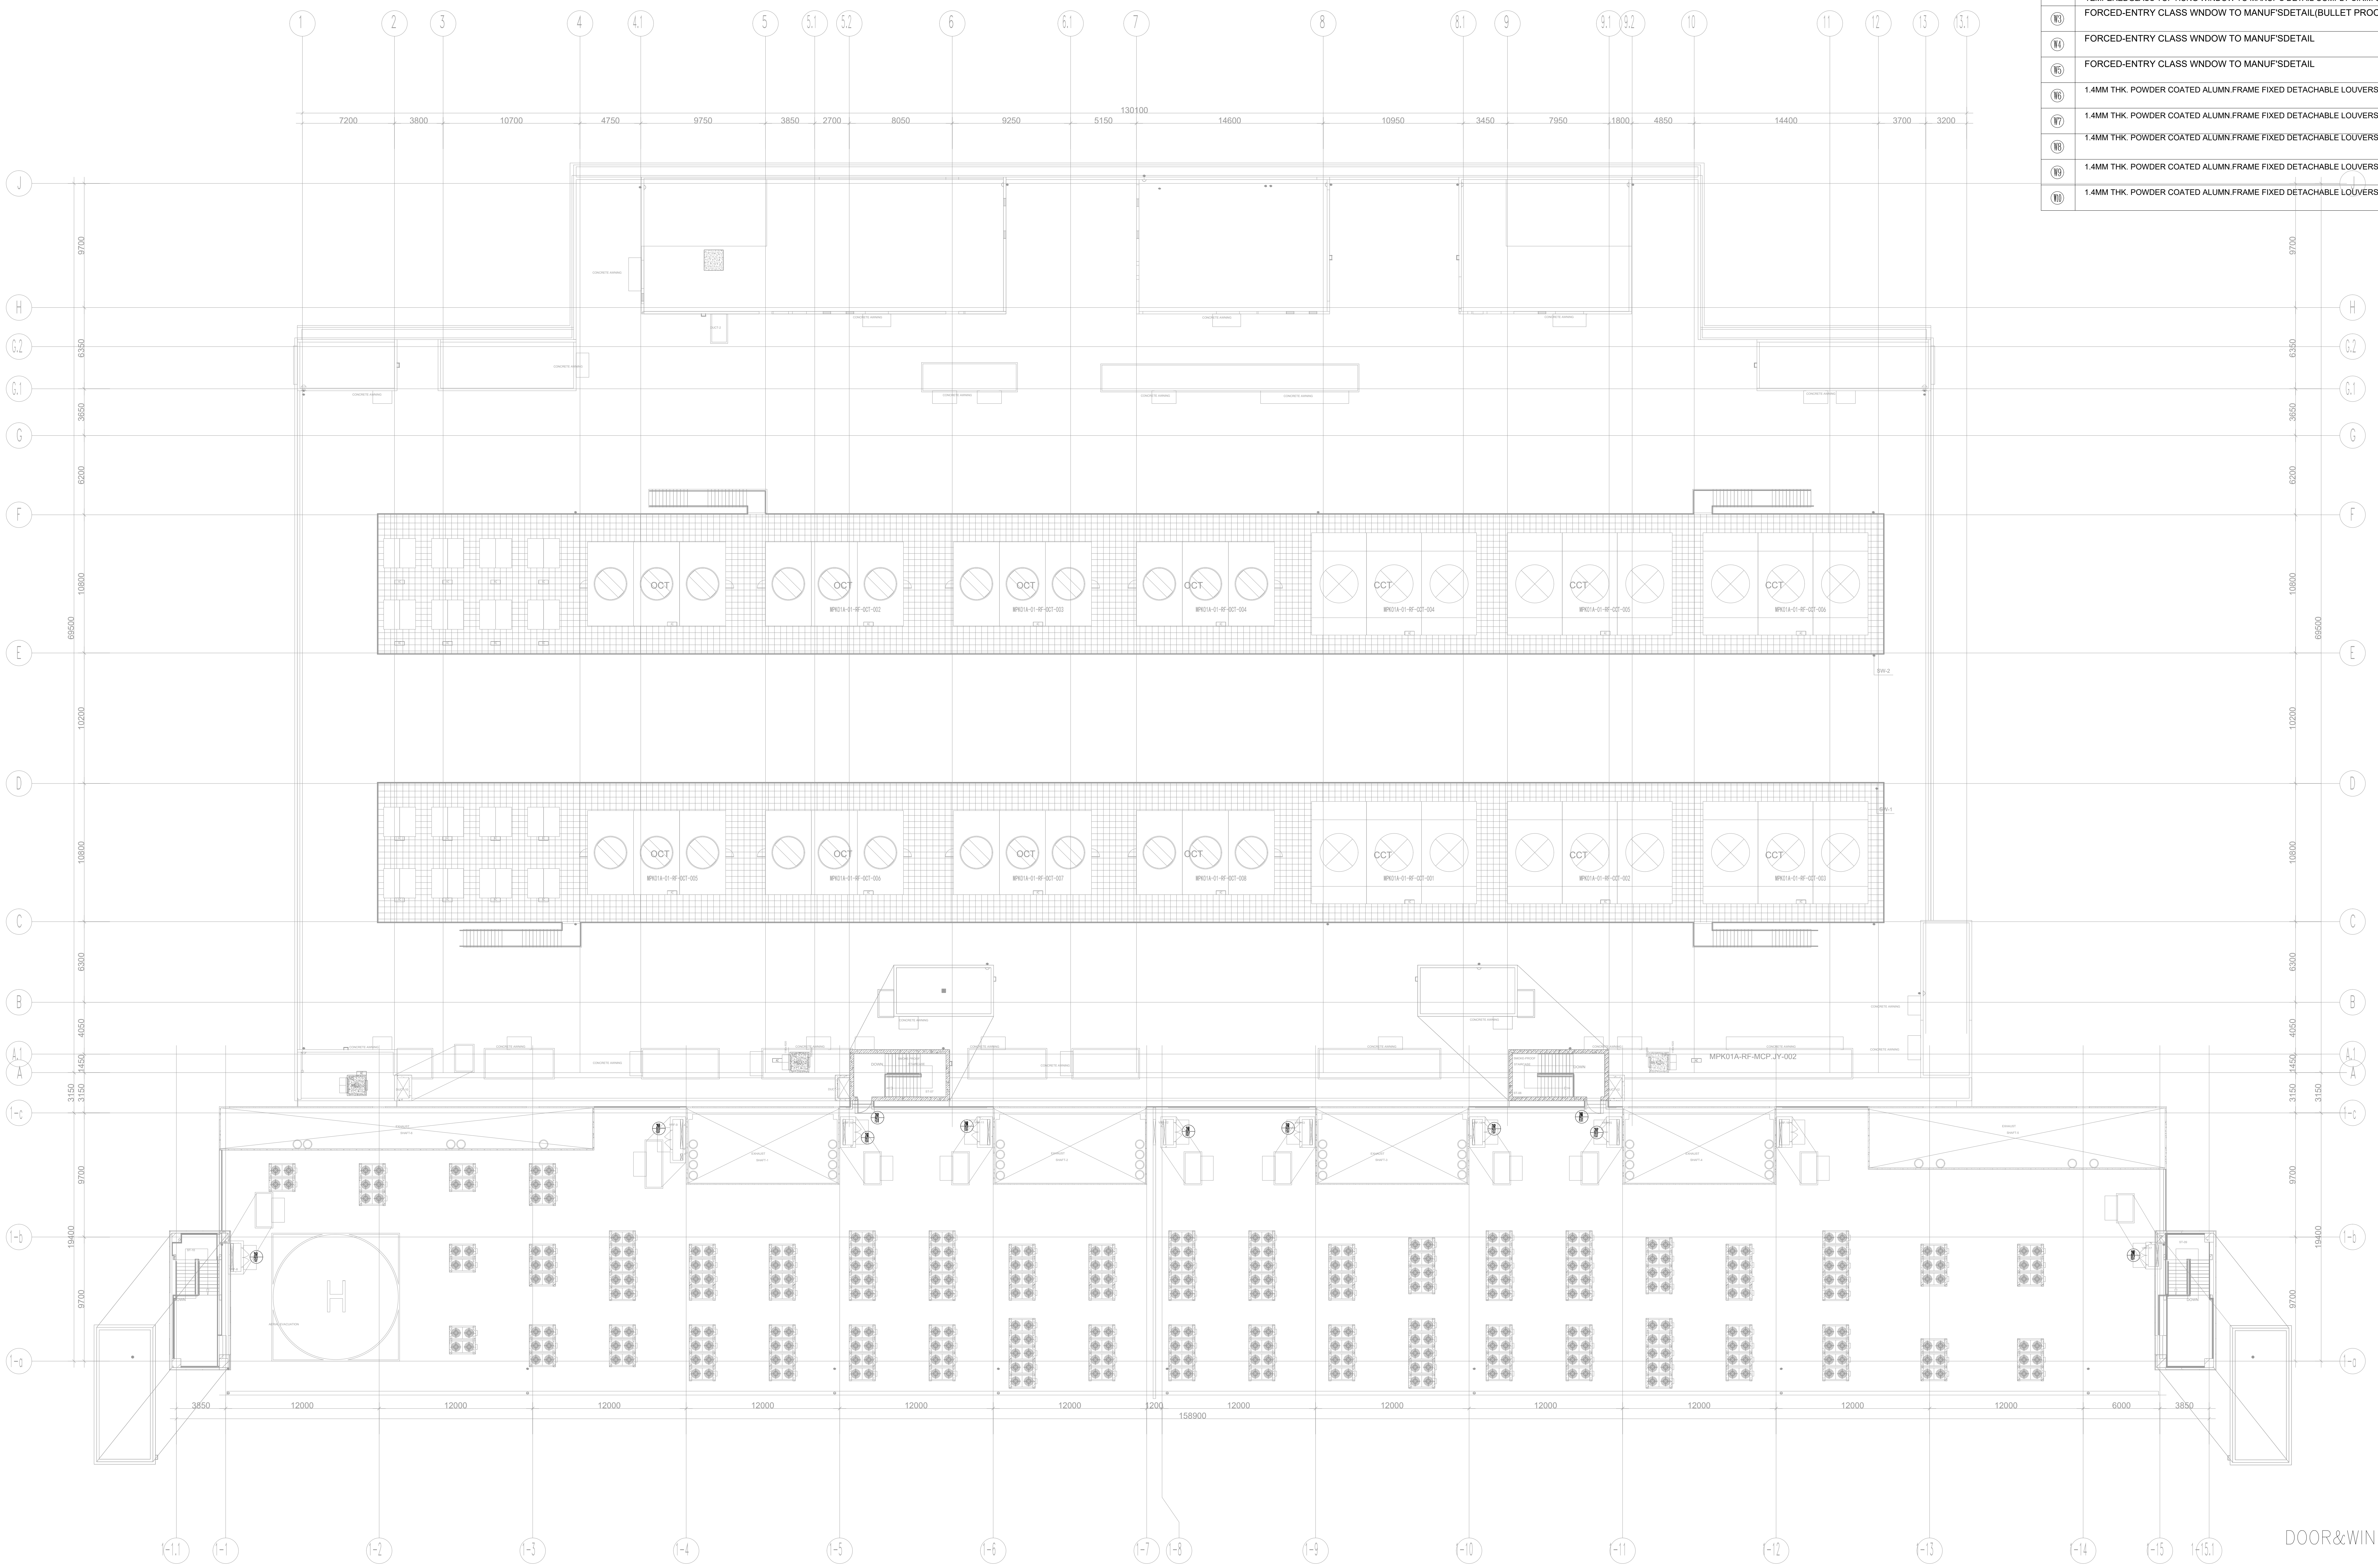

DOOR&WINDOW LAYOUT-UPPER RF

CLIENT :

GULF EDGE DC 01

87 Wireless Road, M Thai Tower 11th. Floor, All Seasons Place, Lumpini,
Pathumwan, Bangkok 10330, Thailand

CONTRACTOR :

华西发展(泰国)有限公司
บริษัท หัวซือ ดีเวลลอปเม้นต์ (ประเทศไทย) จำกัด
HUASHI DEVELOPMENT CO.,LTD
No. 202, Room No. 1403, 14/F, Le Concorde Building,
Ratchadapisek Road, Huaykhwang Sub-District,
Huaykhwang District, Bangkok Metropolitan 10310.

CONSULTANT :

ARbay
บริษัท เอ อาร์ เบย์ จำกัด
ARbay Company Limited
31 st Floor Bangkok Insurance Building
25 South Sathorn road Thungmahamek
Sathorn Bangkok 10120 THAILAND
T +66 (0) 2286 8199
F +66 (0) 2286 2863
info@arbay.co.th

CONSULTANT :

Qbic Engineers & Architects Co.,Ltd.
8 Soi KALONG 4 SANAMBINNAM ROAD,
THASAI SUB-DISTRICT, MUANG NONTHABURI DISTRICT
, NONTHABURI.
Tel 662-950-4374
Fax 662-580-3231
E-Mail : qbic@qbic.co.th, www.qbic.co.th
QBIC ENGINEERS AND ARCHITECTS CO.,LTD.

CONSULTANT :

MITR
MITR TECHNICAL CONSULTANT CO.,LTD.
1168/8 12th FLOOR, LUMPINI TOWER BUILDING,
RAMA IV RD., THUNGMAHAMEK, SATHORN, BANGKOK 10120, THAILAND
TEL : 0-2679-9079-84
FAX : 0-2679-9085 E-mail: mitr_dd@mitr.com

Architect : SIGNATURE
ประกิต พนานุรัตน์ วสถ. 580
ที่อยู่
251/1 ถ.จารุเมือง แขวงรองเมือง เขตปทุมวัน
กรุงเทพมหานคร โทรศัพท์ 02-286-8199

Structural Engineer : SIGNATURE
วิศวกรผู้ออกแบบโครงสร้าง
ณัฐสม สงวนวงษ์ วย 1423
ที่อยู่
2/1 ซ.รามคำแหง 150 ถ.รามคำแหง
แขวง สะพานสูง เขต สะพานสูง กทม. 10240

Structural Inspector : SIGNATURE
วิศวกรผู้ตรวจสอบโครงสร้าง
โกมล จุฑาภัทร วย 964
ที่อยู่
24/18 ซ.นวมินทร์ 129 ถ. นวมินทร์
แขวง นวลจันทร์ เขต บึงกุ่ม กทม. 10230

Electrical Engineer : SIGNATURE
วิศวกรผู้ออกแบบระบบไฟฟ้ากำลัง
นายสุภัทร บูรณวิทย์ วฟก.1265
ที่อยู่
21 ซอยทานสัมฤทธิ์ 13
ตำบลท่าทราย อ.เมืองนนทบุรี จ.นนทบุรี 11000

Mechanical Engineer : SIGNATURE
วิศวกรผู้ออกแบบระบบเครื่องกลและปรับอากาศ
นายประสิทธิ์ เกียวสุนทร วก.1221
ที่อยู่
44/372 ซอยบางกระดี 35/1 แขวงแสมดำ
เขตบางขุนเทียน กทม. 10150
ประสิทธิ์

Sanitary Engineer : SIGNATURE
วิศวกรผู้ออกแบบระบบสุขาภิบาล และดับเพลิง
นายทศวรรษ สนันฤทธิ์ วส. 215
ที่อยู่
บ้านเลขที่ 99/107 หมู่ที่ 3 ต.ศีรษะจรเข้น้อย
อ.บางเสาธง จ.สมุทรปราการ 10540
ทศวรรษ

ISSUE/REVISION

REV.	DESCRIPTION	DATE
A	90% DEVELOPED	09/05/2026

PROJECT NAME :
GEDC 01
LOCATION:
Nikhom Phattana district, Rayong ,industrial estate,CPGC

BUILDING :

90% DEVELOPED

TITLE :
DOOR&WINDOW LAYOUT-UPPER RF

JOB NO.	SCALE 1:200
DRAWN LXP	REF.
CHECKED LJC	DWG.NO.
APPROVED LXD	MPK01A-90-A-DW-501
DATE 2026.05.09	