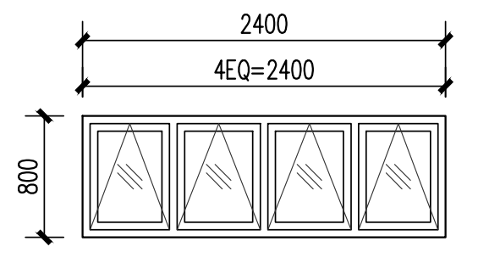

W1

LOCATION:	STAIRS
ACCESSORIES:	
OPERATION:	ALUMINUM ALLOY TOP-HUNG WINDOW
HINGE:	
HAND IN HAND:	
TRANSMISSION:	
LOCK POINT:	
BOLT:	
LOCK SEAT:	
LIMITER:	
WIND SUPPORT:	
ANTI-FALL ROPE:	
KEY:	
TOTAL:	18
GLASS:	6MM.ANNUALCLEARGLASS+0.38PVB+ 6MM.ANNULCLEAR GLASS

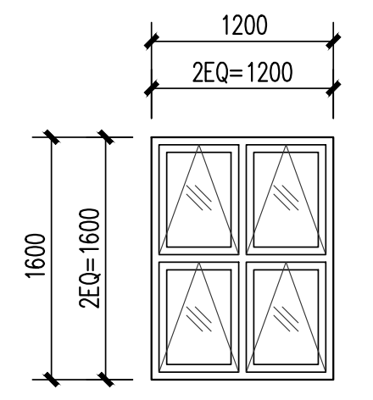

W2

LOCATION:	STAIRS
ACCESSORIES:	
OPERATION:	ALUMINUM ALLOY TOP-HUNG WINDOW
HINGE:	
HAND IN HAND:	
TRANSMISSION:	
LOCK POINT:	
BOLT:	
LOCK SEAT:	
LIMITER:	
WIND SUPPORT:	
ANTI-FALL ROPE:	
KEY:	
TOTAL:	2
GLASS:	6MM.ANNUALCLEARGLASS+0.38PVB+ 6MM.ANNULCLEAR GLASS

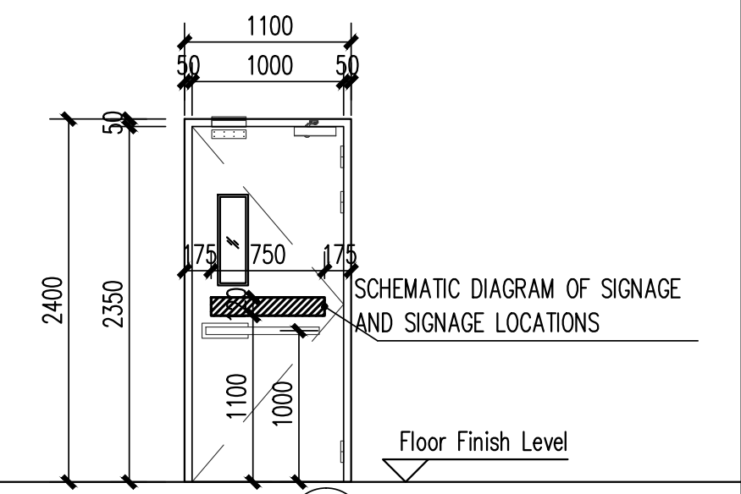

2HR FD1

LOCATION:	FIRE EXIT DOOR
ACCESSORIES:	
OPERATION:	STEEL SINGLE DOOR,2HRS FIRE RATED
DOOR PANEL:	45MM THICK STEEL DOOR PANEL, 2-HOUR FIRE RESISTANCE, COATED WITH SEMIGLOSS PAINT, COLOR AND SURFACE FINISH TO MATCH
DOOR FRAME:	STEEL DOORFRAME, SIZE 2"X4", COATED WITH SEMIGLOSS PAINT, COLOR AND FINISH TO MATCH THE WALL
HINGE:	STAINLESS STEEL HINGES FOR STEEL DOORS OR STAINLESS STEEL DOORS
HANDLE LOCKSET:	THE EQUIPMENT IS EQUIPPED WITH STAINLESS STEEL HANDLES TO MEET THE REQUIREMENTS OF HAFELE OR EQUIVALENT STANDARDS.
BOLT:	DOOR FRAME SIDE HINGE, HAFELE BRAND OR EQUIVALENT PRODUCT
DOOR STOPPER:	DOOR BLOCK, HAFELE BRAND OR EQUIVALENT
DOOR CLOSER:	DOOR SURFACE ANTI-COLLISION DEVICE, INSTALLED ACCORDING TO MANUFACTURER'S STANDARDS
KEY:	PANIC BAR DEVCE KEY(ELECTROMAGNETIC LOCK)
TOTAL:	87
GLASS:	1-HOUR FIRE-RESISTANT GLASS

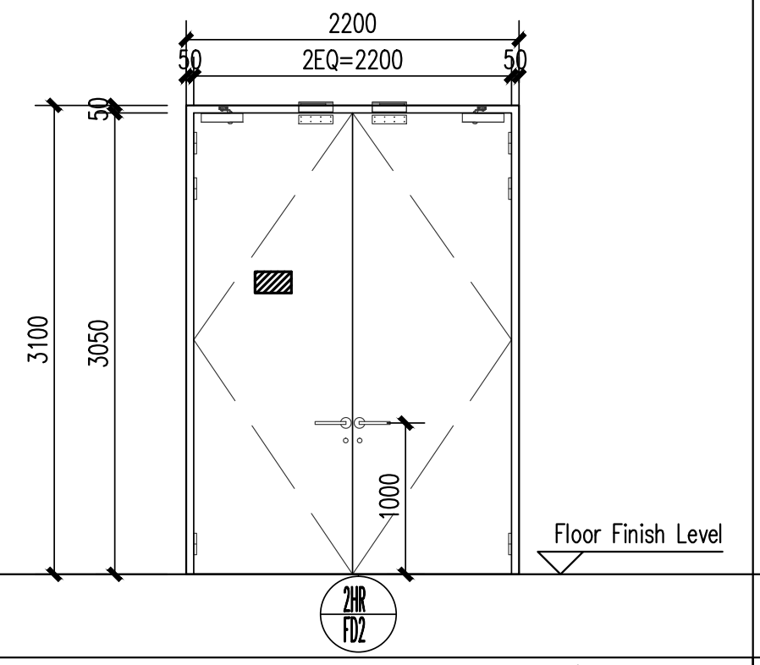

2HR FD2

LOCATION:	MATERIAL ENTRANCE,CAN BE OPENED 180°
ACCESSORIES:	
OPERATION:	STEEL DOUBLE LEAF DOOR 2HRS FIRE RATED DOUBLE LEAF OPENING
DOOR PANEL:	45MM THICK STEEL DOOR PANEL, 2-HOUR FIRE RESISTANCE, COATED WITH SEMIGLOSS PAINT, COLOR AND SURFACE FINISH TO MATCH
DOOR FRAME:	STEEL DOORFRAME, SIZE 2"X4", COATED WITH SEMIGLOSS PAINT, COLOR AND FINISH TO MATCH THE WALL
HINGE:	STAINLESS STEEL HINGES FOR STEEL DOORS OR STAINLESS STEEL DOORS
HANDLE LOCKSET:	THE EQUIPMENT IS EQUIPPED WITH STAINLESS STEEL HANDLES TO MEET THE REQUIREMENTS OF HAFELE OR EQUIVALENT STANDARDS.
BOLT:	DOOR FRAME SIDE HINGE, HAFELE BRAND OR EQUIVALENT PRODUCT
DOOR STOPPER:	DOOR BLOCK, HAFELE BRAND OR EQUIVALENT
DOOR CLOSER:	DOOR SURFACE ANTI-COLLISION DEVICE, INSTALLED ACCORDING TO MANUFACTURER'S STANDARDS
KEY:	KEY(ELECTROMAGNETIC LOCK)
TOTAL:	88
GLASS:	

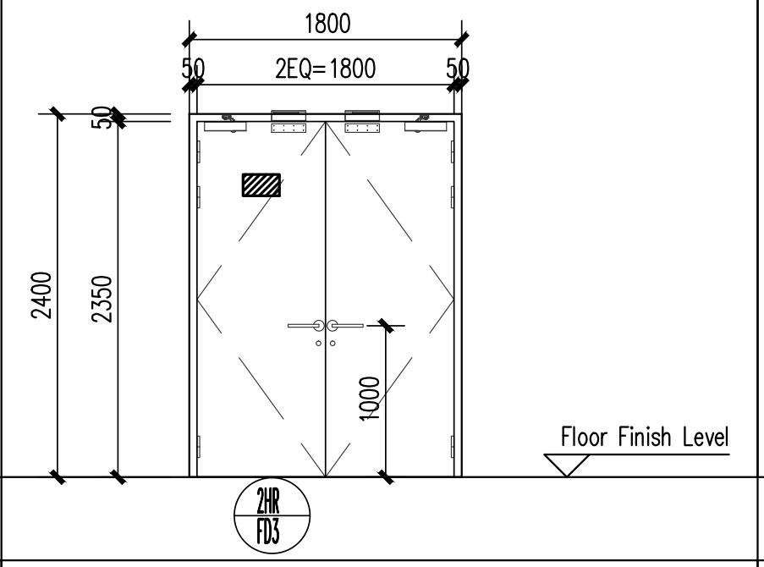

2HR FD3

LOCATION:	MATERIAL ENTRANCE
ACCESSORIES:	
OPERATION:	STEEL DOUBLE LEAF DOOR,2HRS FIRE RATED DOUBLE LEAF OPENING
DOOR PANEL:	45MM THICK STEEL DOOR PANEL, 2-HOUR FIRE RESISTANCE, COATED WITH SEMIGLOSS PAINT, COLOR AND SURFACE FINISH TO MATCH
DOOR FRAME:	STEEL DOORFRAME, SIZE 2"X4", COATED WITH SEMIGLOSS PAINT, COLOR AND FINISH TO MATCH THE WALL
HINGE:	STAINLESS STEEL HINGES FOR STEEL DOORS OR STAINLESS STEEL DOORS
HANDLE LOCKSET:	THE EQUIPMENT IS EQUIPPED WITH STAINLESS STEEL HANDLES TO MEET THE REQUIREMENTS OF HAFELE OR EQUIVALENT STANDARDS.
BOLT:	DOOR FRAME SIDE HINGE, HAFELE BRAND OR EQUIVALENT PRODUCT
DOOR STOPPER:	DOOR BLOCK, HAFELE BRAND OR EQUIVALENT
DOOR CLOSER:	DOOR SURFACE ANTI-COLLISION DEVICE, INSTALLED ACCORDING TO MANUFACTURER'S STANDARDS
KEY:	KEY(ELECTROMAGNETIC LOCK)
TOTAL:	50
GLASS:	

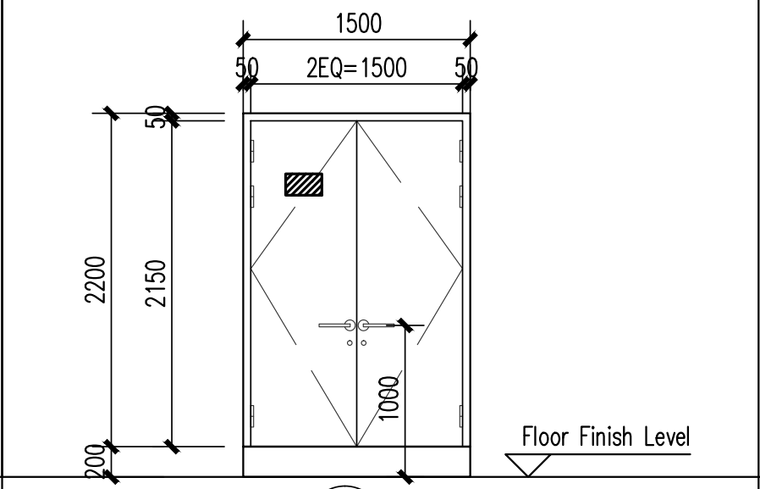

2HR FD4

LOCATION:	
ACCESSORIES:	
OPERATION:	STEEL DOUBLE LEAF DOOR,2HRS FIRE RATED
DOOR PANEL:	45MM THICK STEEL DOOR PANEL, 2-HOUR FIRE RESISTANCE, COATED WITH SEMIGLOSS PAINT, COLOR AND SURFACE FINISH TO MATCH
DOOR FRAME:	STEEL DOORFRAME, SIZE 2"X4", COATED WITH SEMIGLOSS PAINT, COLOR AND FINISH TO MATCH THE WALL
HINGE:	STAINLESS STEEL HINGES FOR STEEL DOORS OR STAINLESS STEEL DOORS
HANDLE LOCKSET:	THE EQUIPMENT IS EQUIPPED WITH STAINLESS STEEL HANDLES TO MEET THE REQUIREMENTS OF HAFELE OR EQUIVALENT STANDARDS.
BOLT:	DOOR FRAME SIDE HINGE, HAFELE BRAND OR EQUIVALENT PRODUCT
DOOR STOPPER:	DOOR BLOCK, HAFELE BRAND OR EQUIVALENT
DOOR CLOSER:	DOOR SURFACE ANTI-COLLISION DEVICE, INSTALLED ACCORDING TO MANUFACTURER'S STANDARDS
KEY:	KEY(MECHANICAL LOCK)
TOTAL:	91
GLASS:	

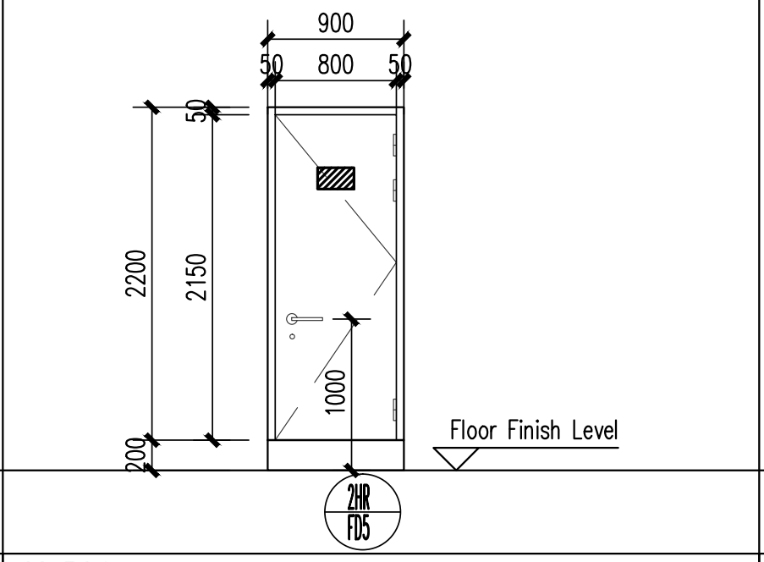

2HR FD5

LOCATION:	
ACCESSORIES:	
OPERATION:	STEEL SINGLE DOOR,2HRS FIRE RATED
DOOR PANEL:	45MM THICK STEEL DOOR PANEL, 2-HOUR FIRE RESISTANCE, COATED WITH SEMIGLOSS PAINT, COLOR AND SURFACE FINISH TO MATCH
DOOR FRAME:	STEEL DOORFRAME, SIZE 2"X4", COATED WITH SEMIGLOSS PAINT, COLOR AND FINISH TO MATCH THE WALL
HINGE:	STAINLESS STEEL HINGES FOR STEEL DOORS OR STAINLESS STEEL DOORS
HANDLE LOCKSET:	THE EQUIPMENT IS EQUIPPED WITH STAINLESS STEEL HANDLES TO MEET THE REQUIREMENTS OF HAFELE OR EQUIVALENT STANDARDS.
BOLT:	DOOR FRAME SIDE HINGE, HAFELE BRAND OR EQUIVALENT PRODUCT
DOOR STOPPER:	DOOR BLOCK, HAFELE BRAND OR EQUIVALENT
DOOR CLOSER:	DOOR SURFACE ANTI-COLLISION DEVICE, INSTALLED ACCORDING TO MANUFACTURER'S STANDARDS
KEY:	KEY(MECHANICAL LOCK)
TOTAL:	3
GLASS:	

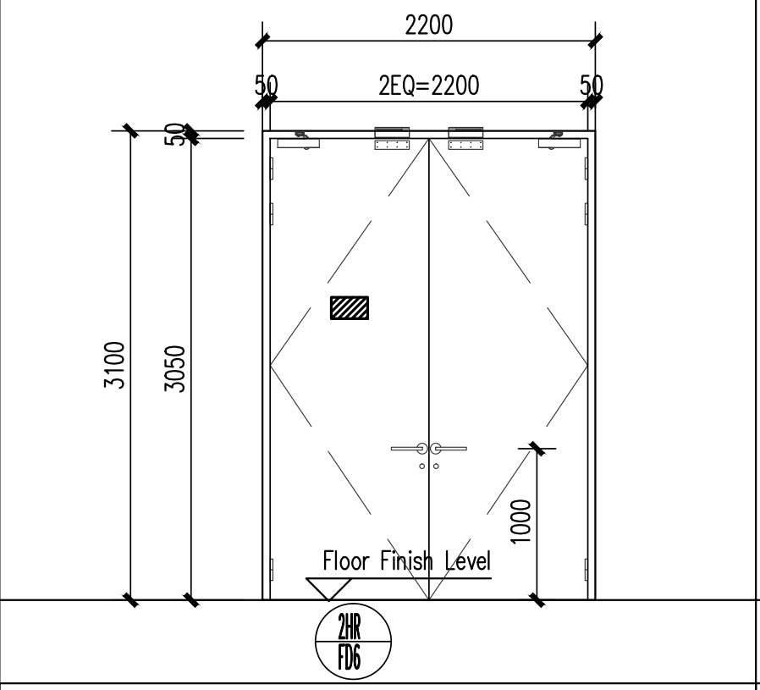

2HR FD6

LOCATION:	MATERIAL ENTRANCE,CAN BE OPENED 90°
ACCESSORIES:	
OPERATION:	STEEL DOUBLE LEAF DOOR,2HRS FIRE RATED DOUBLE LEAF OPENING
DOOR PANEL:	45MM THICK STEEL DOOR PANEL, 2-HOUR FIRE RESISTANCE, COATED WITH SEMIGLOSS PAINT, COLOR AND SURFACE FINISH TO MATCH
DOOR FRAME:	STEEL DOORFRAME, SIZE 2"X4", COATED WITH SEMIGLOSS PAINT, COLOR AND FINISH TO MATCH THE WALL
HINGE:	STAINLESS STEEL HINGES FOR STEEL DOORS OR STAINLESS STEEL DOORS
HANDLE LOCKSET:	THE EQUIPMENT IS EQUIPPED WITH STAINLESS STEEL HANDLES TO MEET THE REQUIREMENTS OF HAFELE OR EQUIVALENT STANDARDS.
BOLT:	DOOR FRAME SIDE HINGE, HAFELE BRAND OR EQUIVALENT PRODUCT
DOOR STOPPER:	DOOR BLOCK, HAFELE BRAND OR EQUIVALENT
DOOR CLOSER:	DOOR SURFACE ANTI-COLLISION DEVICE, INSTALLED ACCORDING TO MANUFACTURER'S STANDARDS
KEY:	KEY(ELECTROMAGNETIC LOCK)
TOTAL:	25
GLASS:	

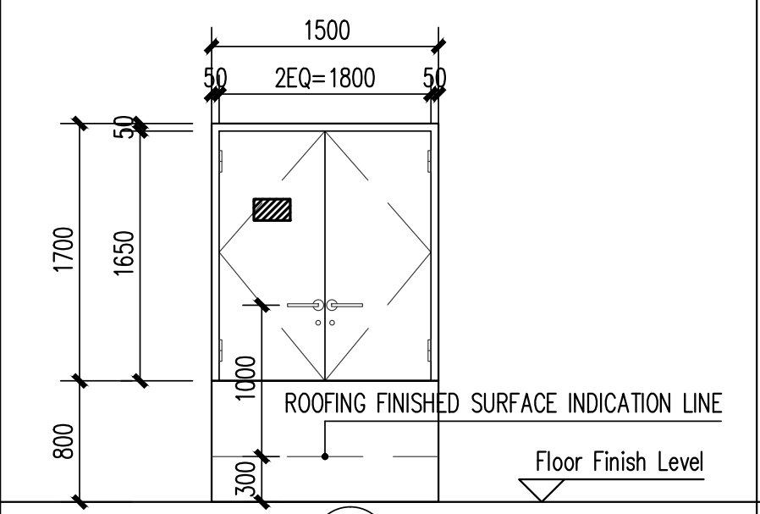

2HR FD7

LOCATION:	
ACCESSORIES:	
OPERATION:	STEEL DOUBLE LEAF DOOR,2HRS FIRE RATED DOUBLE LEAF OPENING
DOOR PANEL:	45MM THICK STEEL DOOR PANEL, 2-HOUR FIRE RESISTANCE, COATED WITH SEMIGLOSS PAINT, COLOR AND SURFACE FINISH TO MATCH
DOOR FRAME:	STEEL DOORFRAME, SIZE 2"X4", COATED WITH SEMIGLOSS PAINT, COLOR AND FINISH TO MATCH THE WALL
HINGE:	STAINLESS STEEL HINGES FOR STEEL DOORS OR STAINLESS STEEL DOORS
HANDLE LOCKSET:	THE EQUIPMENT IS EQUIPPED WITH STAINLESS STEEL HANDLES TO MEET THE REQUIREMENTS OF HAFELE OR EQUIVALENT STANDARDS.
BOLT:	DOOR FRAME SIDE HINGE, HAFELE BRAND OR EQUIVALENT PRODUCT
DOOR STOPPER:	DOOR BLOCK, HAFELE BRAND OR EQUIVALENT
DOOR CLOSER:	DOOR SURFACE ANTI-COLLISION DEVICE, INSTALLED ACCORDING TO MANUFACTURER'S STANDARDS
KEY:	KEY(ELECTROMAGNETIC LOCK)
TOTAL:	27
GLASS:	

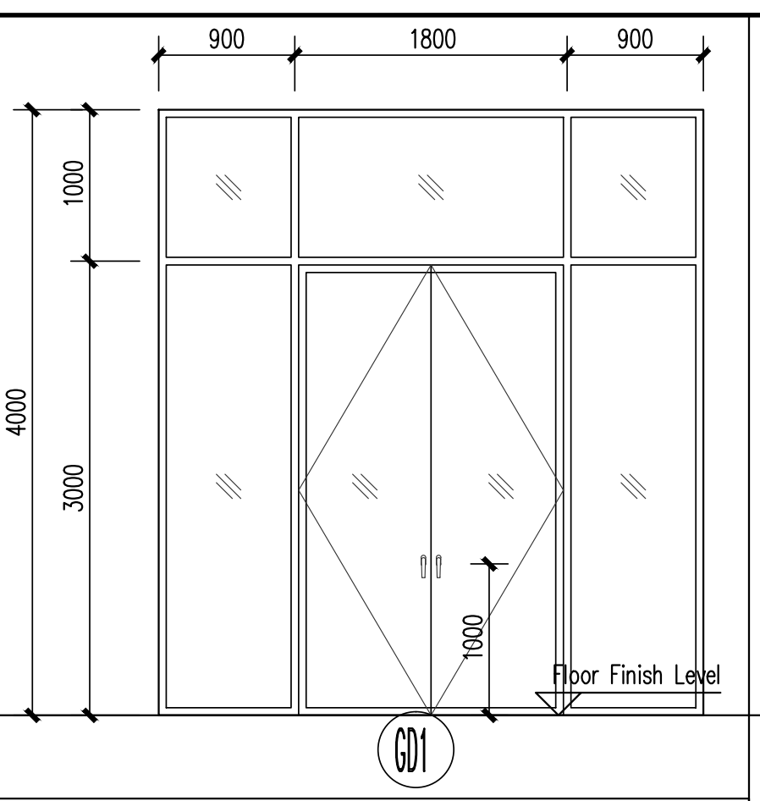

GD1

LOCATION:	LOBBY ENTRANCE
ACCESSORIES:	
OPERATION:	THE ALUMINUM ALLOY DOOR OPENS WITH TWO FANS
DOOR PANEL:	
DOOR FRAME:	
HINGE:	
HANDLE LOCKSET:	
BOLT:	
DOOR STOPPER:	
DOOR CLOSER:	
KEY:	KEY(ELECTROMAGNETIC LOCK)
TOTAL:	1
GLASS:	6MM.ANNUALCLEARGLASS+0.38PVB+6MM.ANNULCLEAR GLASS

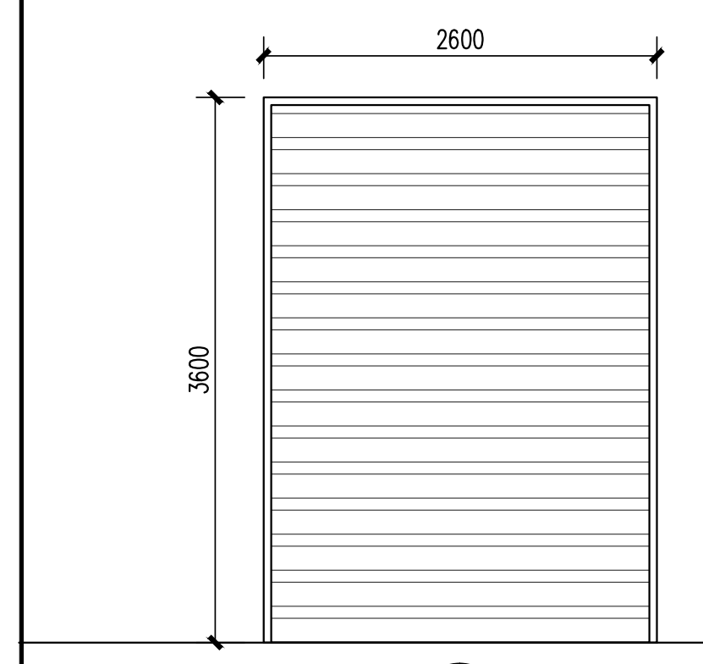

RS1

TYPE	ROLLER SHUTTER DOOR
FRAME	2HOURS FIRE RATED ROLLER SHUTTER : MIN 1.6MM THK. MOTORIZED ALUNMINIUM ROLLER SHUTTER CURTAIN C/W INSULATION POWDER COATED AS FINISHES; SIDE GUIDE TO BE MIN 1.6MM THK S/S STEEL C/W POWDER COATED FINISHES; BOTTOM BAR, SHUTTER HO
Total	4

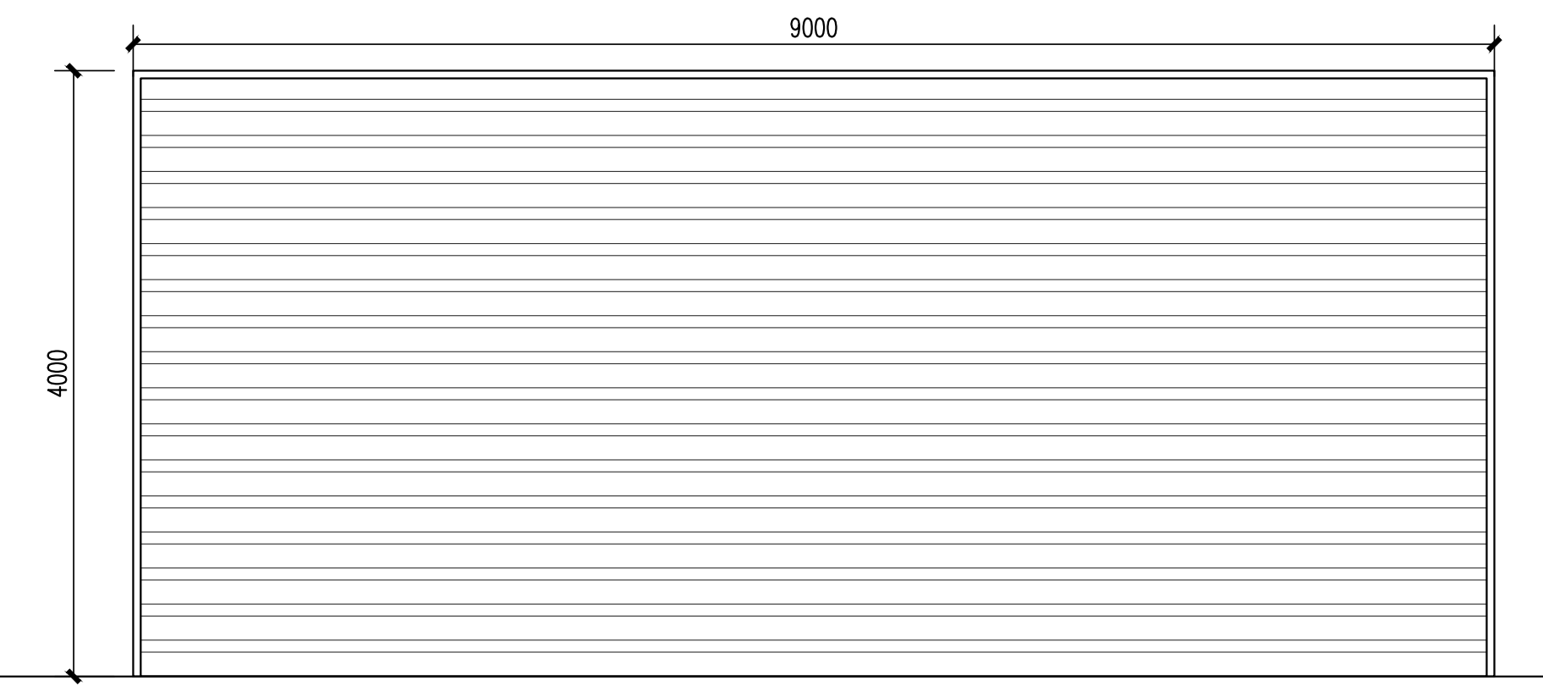

RS2

TYPE	ROLLER SHUTTER DOOR
FRAME	2HOURS FIRE RATED ROLLER SHUTTER : MIN 1.6MM THK. MOTORIZED ALUNMINIUM ROLLER SHUTTER CURTAIN C/W INSULATION POWDER COATED AS FINISHES; SIDE GUIDE TO BE MIN 1.6MM THK S/S STEEL C/W POWDER COATED FINISHES; BOTTOM BAR, SHUTTER HO
Total	3

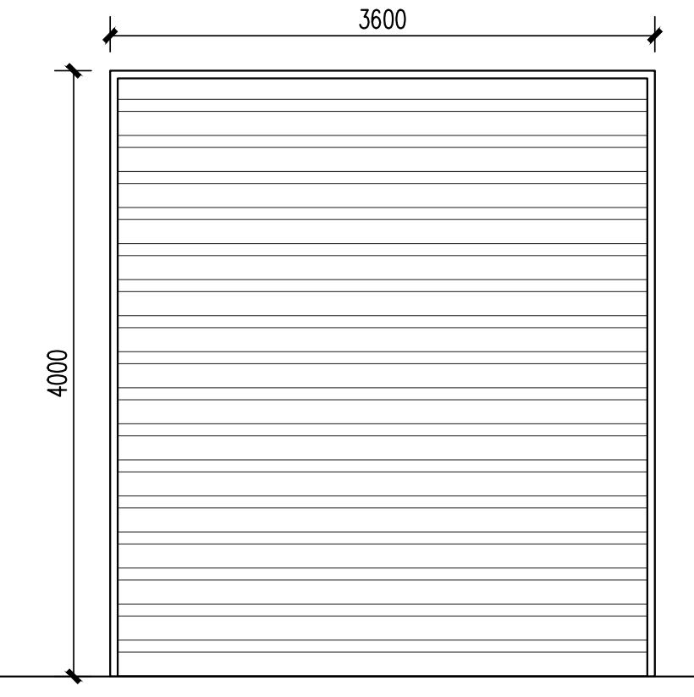

RS3

TYPE	ROLLER SHUTTER DOOR
FRAME	2HOURS FIRE RATED ROLLER SHUTTER : MIN 1.6MM THK. MOTORIZED ALUNMINIUM ROLLER SHUTTER CURTAIN C/W INSULATION POWDER COATED AS FINISHES; SIDE GUIDE TO BE MIN 1.6MM THK S/S STEEL C/W POWDER COATED FINISHES; BOTTOM BAR, SHUTTER HO
Total	2

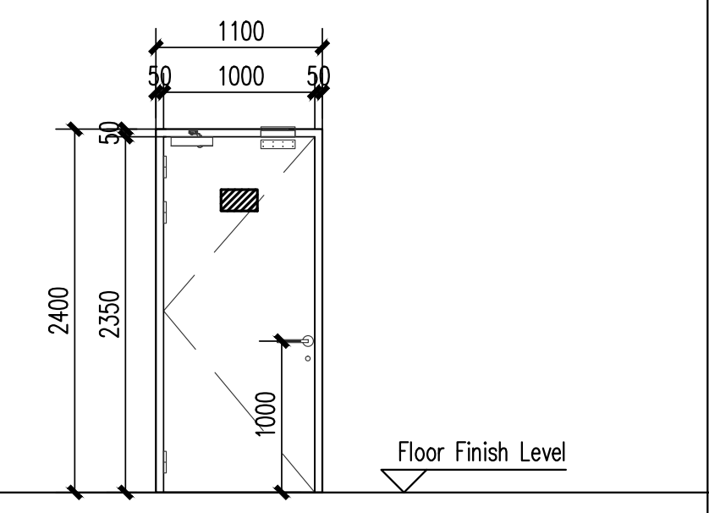

D1

LOCATION:	PERSONAL ENTRANCE
ACCESSORIES:	
OPERATION:	STEEL SINGLE DOOR SINGLE SWING
DOOR PANEL:	45MM THICK STEEL DOOR PANEL, 2-HOUR FIRE RESISTANCE, COATED WITH SEMIGLOSS PAINT, COLOR AND SURFACE FINISH TO MATCH
DOOR FRAME:	STEEL DOORFRAME, SIZE 2"X4", COATED WITH SEMIGLOSS PAINT, COLOR AND FINISH TO MATCH THE WALL
HINGE:	STAINLESS STEEL HINGES FOR STEEL DOORS OR STAINLESS STEEL DOORS
HANDLE LOCKSET:	THE EQUIPMENT IS EQUIPPED WITH STAINLESS STEEL HANDLES TO MEET THE REQUIREMENTS OF HAFELE OR EQUIVALENT STANDARDS.
BOLT:	DOOR FRAME SIDE HINGE, HAFELE BRAND OR EQUIVALENT PRODUCT
DOOR STOPPER:	DOOR BLOCK, HAFELE BRAND OR EQUIVALENT
DOOR CLOSER:	DOOR SURFACE ANTI-COLLISION DEVICE, INSTALLED ACCORDING TO MANUFACTURER'S STANDARDS
KEY:	KEY(ELECTROMAGNETIC LOCK)
TOTAL:	32
GLASS:	

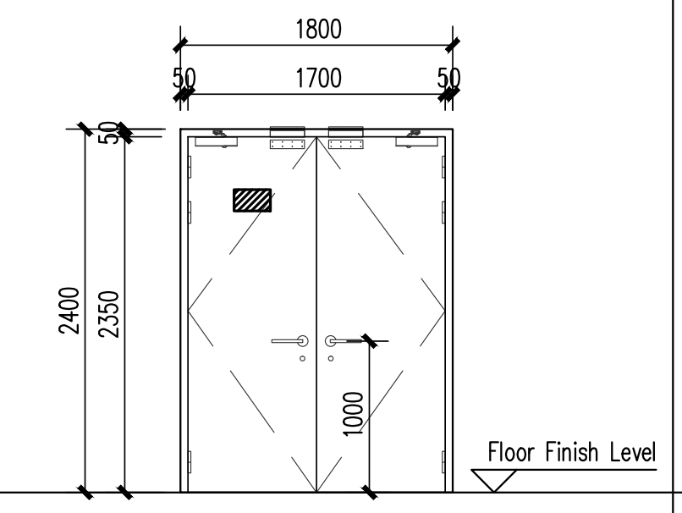

D2

LOCATION:	PERSONAL ENTRANCE
ACCESSORIES:	
OPERATION:	STEEL DOUBLE DOOR DOUBLE LEAF OPENING
DOOR PANEL:	45MM THICK STEEL DOOR PANEL, 2-HOUR FIRE RESISTANCE, COATED WITH SEMIGLOSS PAINT, COLOR AND SURFACE FINISH TO MATCH
DOOR FRAME:	STEEL DOORFRAME, SIZE 2"X4", COATED WITH SEMIGLOSS PAINT, COLOR AND FINISH TO MATCH THE WALL
HINGE:	STAINLESS STEEL HINGES FOR STEEL DOORS OR STAINLESS STEEL DOORS
HANDLE LOCKSET:	THE EQUIPMENT IS EQUIPPED WITH STAINLESS STEEL HANDLES TO MEET THE REQUIREMENTS OF HAFELE OR EQUIVALENT STANDARDS.
BOLT:	DOOR FRAME SIDE HINGE, HAFELE BRAND OR EQUIVALENT PRODUCT
DOOR STOPPER:	DOOR BLOCK, HAFELE BRAND OR EQUIVALENT
DOOR CLOSER:	DOOR SURFACE ANTI-COLLISION DEVICE, INSTALLED ACCORDING TO MANUFACTURER'S STANDARDS
KEY:	KEY(ELECTROMAGNETIC LOCK)
TOTAL:	2
GLASS:	

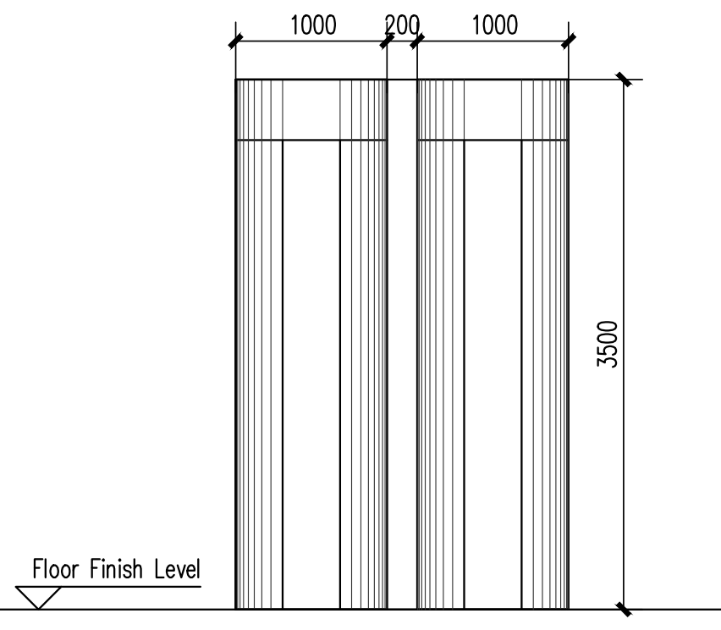

D3

LOCATION:	FULL HEIGHT AUTOMATIC CAPSULE TURNSTILE
ACCESSORIES:	
OPERATION:	ALUMINUM DOOR;REVOLVING DOOR WITH MANUFACTURER'S DETAILED DESIGN.
DOOR PANEL:	
DOOR FRAME:	
HINGE:	
HANDLE LOCKSET:	
BOLT:	
DOOR STOPPER:	
DOOR CLOSER:	
KEY:	KEY(ELECTROMAGNETIC LOCK)
TOTAL:	1
GLASS:	

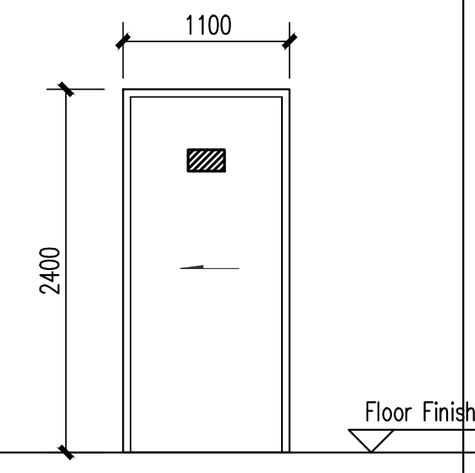

D4

LOCATION:	ACCESSIBLE TOILET
ACCESSORIES:	
OPERATION:	STEEL SLIDING DOOR SINGLE SWING
DOOR PANEL:	45MM THICK STEEL DOOR PANEL, 2-HOUR FIRE RESISTANCE, COATED WITH SEMIGLOSS PAINT, COLOR AND SURFACE FINISH TO MATCH
DOOR FRAME:	STEEL DOORFRAME, SIZE 2"X4", COATED WITH SEMIGLOSS PAINT, COLOR AND FINISH TO MATCH THE WALL
HINGE:	STAINLESS STEEL HINGES FOR STEEL DOORS OR STAINLESS STEEL DOORS
HANDLE LOCKSET:	THE EQUIPMENT IS EQUIPPED WITH STAINLESS STEEL HANDLES TO MEET THE REQUIREMENTS OF HAFELE OR EQUIVALENT STANDARDS.
BOLT:	DOOR FRAME SIDE HINGE, HAFELE BRAND OR EQUIVALENT PRODUCT
DOOR STOPPER:	DOOR BLOCK, HAFELE BRAND OR EQUIVALENT
DOOR CLOSER:	DOOR SURFACE ANTI-COLLISION DEVICE, INSTALLED ACCORDING TO MANUFACTURER'S STANDARDS
KEY:	KEY(ELECTROMAGNETIC LOCK)
TOTAL:	3
GLASS:	

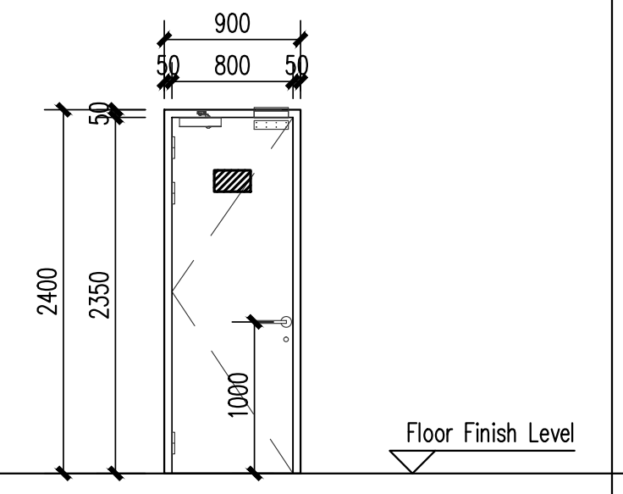

D6

LOCATION:	PERSONAL ENTRANCE
ACCESSORIES:	
OPERATION:	STEEL SINGLE DOOR SINGLE SWING
DOOR PANEL:	45MM THICK STEEL DOOR PANEL, 2-HOUR FIRE RESISTANCE, COATED WITH SEMIGLOSS PAINT, COLOR AND SURFACE FINISH TO MATCH
DOOR FRAME:	STEEL DOORFRAME, SIZE 2"X4", COATED WITH SEMIGLOSS PAINT, COLOR AND FINISH TO MATCH THE WALL
HINGE:	STAINLESS STEEL HINGES FOR STEEL DOORS OR STAINLESS STEEL DOORS
HANDLE LOCKSET:	THE EQUIPMENT IS EQUIPPED WITH STAINLESS STEEL HANDLES TO MEET THE REQUIREMENTS OF HAFELE OR EQUIVALENT STANDARDS.
BOLT:	DOOR FRAME SIDE HINGE, HAFELE BRAND OR EQUIVALENT PRODUCT
DOOR STOPPER:	DOOR BLOCK, HAFELE BRAND OR EQUIVALENT
DOOR CLOSER:	DOOR SURFACE ANTI-COLLISION DEVICE, INSTALLED ACCORDING TO MANUFACTURER'S STANDARDS
KEY:	KEY(ELECTROMAGNETIC LOCK)
TOTAL:	2
GLASS:	

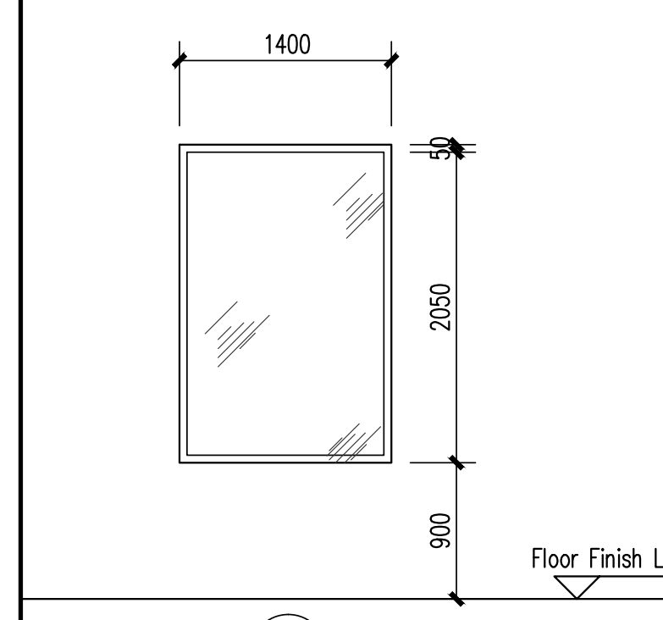

W3

LOCATION:	SECURITY01
ACCESSORIES:	
OPERATION:	GALVANIZED STEEL WINDOW (BULLET PROOF GLASS)
HINGE:	
HAND IN HAND:	
TRANSMISSION:	
LOCK POINT:	
BOLT:	
LOCK SEAT:	
LIMITER:	
WIND SUPPORT:	
ANTI-FALL ROPE:	
KEY:	
TOTAL:	1
GLASS:	

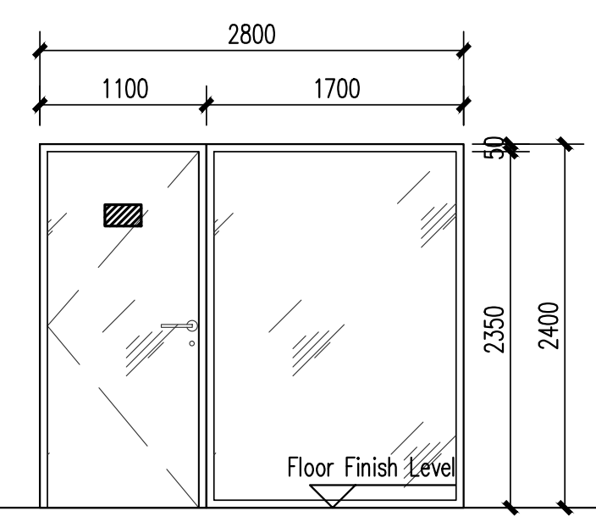

W4

LOCATION:	SECURITY01
ACCESSORIES:	
OPERATION:	ALUMINUM CASENENT WNDOW
HINGE:	
HAND IN HAND:	
TRANSMISSION:	
LOCK POINT:	
BOLT:	
LOCK SEAT:	
LIMITER:	
WIND SUPPORT:	
ANTI-FALL ROPE:	
KEY:	
TOTAL:	1
GLASS:	

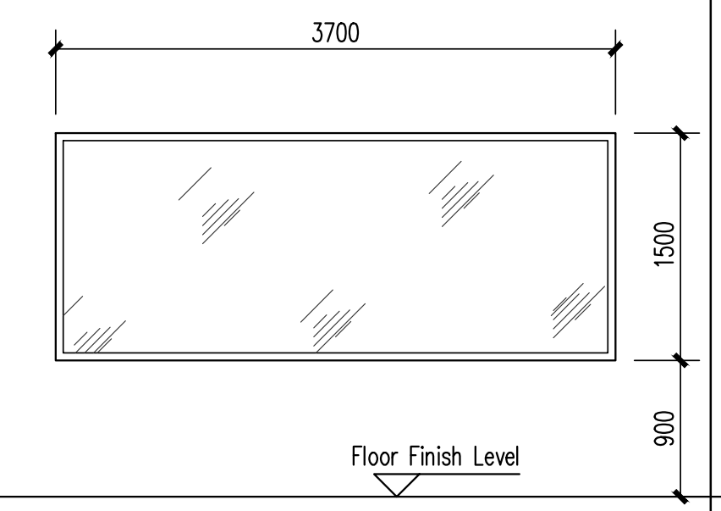

W5

LOCATION:	SECURITY01
ACCESSORIES:	
OPERATION:	ALUMINUM CASENENT WNDOW
HINGE:	
HAND IN HAND:	
TRANSMISSION:	
LOCK POINT:	
BOLT:	
LOCK SEAT:	
LIMITER:	
WIND SUPPORT:	
ANTI-FALL ROPE:	
KEY:	
TOTAL:	1
GLASS:	

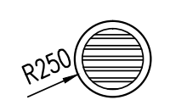

W6

LOCATION:	VENTILATE
OPERATION:	ALUMINUM CASENENT WNDOW
HARDWARE	1.4mm THK.POWDER COATED ALUMN. FRAME FIXED DETACHABLE LOUVERS TO MANUF'S DETAIL; FACADE LOUVRES SHALL HAVE POWDER-COATED FINISH TO MATCH SURROUNDING FACADE TREATMENTS. EXTERNAL LOUVRES SHALL BE DOUBLE BANK RAINPROOFED TO PREVENT WATER INGRESS.
Total	6

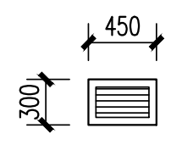

W7

LOCATION:	VENTILATE
OPERATION:	ALUMINUM CASENENT WNDOW
HARDWARE	1.4mm THK.POWDER COATED ALUMN. FRAME FIXED DETACHABLE LOUVERS TO MANUF'S DETAIL; FACADE LOUVRES SHALL HAVE POWDER-COATED FINISH TO MATCH SURROUNDING FACADE TREATMENTS. EXTERNAL LOUVRES SHALL BE DOUBLE BANK RAINPROOFED TO PREVENT WATER INGRESS.
Total	6

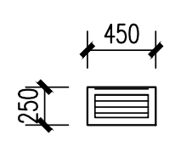

W8

LOCATION:	VENTILATE
OPERATION:	ALUMINUM CASENENT WNDOW
HARDWARE	1.4mm THK.POWDER COATED ALUMN. FRAME FIXED DETACHABLE LOUVERS TO MANUF'S DETAIL; FACADE LOUVRES SHALL HAVE POWDER-COATED FINISH TO MATCH SURROUNDING FACADE TREATMENTS. EXTERNAL LOUVRES SHALL BE DOUBLE BANK RAINPROOFED TO PREVENT WATER INGRESS.
Total	10

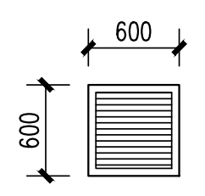

W9

LOCATION:	VENTILATE
OPERATION:	ALUMINUM CASENENT WNDOW
HARDWARE	1.4mm THK.POWDER COATED ALUMN. FRAME FIXED DETACHABLE LOUVERS TO MANUF'S DETAIL; FACADE LOUVRES SHALL HAVE POWDER-COATED FINISH TO MATCH SURROUNDING FACADE TREATMENTS. EXTERNAL LOUVRES SHALL BE DOUBLE BANK RAINPROOFED TO PREVENT WATER INGRESS.
Total	22

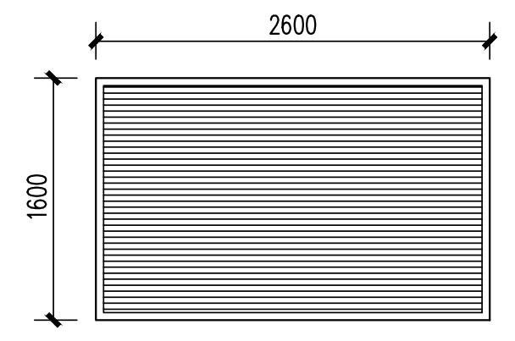

W10

LOCATION:	VENTILATE
OPERATION:	ALUMINUM CASENENT WNDOW
HARDWARE	1.4mm THK.POWDER COATED ALUMN. FRAME FIXED DETACHABLE LOUVERS TO MANUF'S DETAIL; FACADE LOUVRES SHALL HAVE POWDER-COATED FINISH TO MATCH SURROUNDING FACADE TREATMENTS. EXTERNAL LOUVRES SHALL BE DOUBLE BANK RAINPROOFED TO PREVENT WATER INGRESS.
Total	4

odified according to the review comments (ACM_GSA03_DesignReview_SD60_Rev B - Arch)

NOTES:
REQUIRE DOOR TAG FROM MANUFACTURER

▨	SCHEMATIC DIAGRAM OF SIGNAGE AND SIGNAGE LOCATIONS

LEED: REMARK FOR ALL DOOR & WINDOW GLAZING EXTERIOR GLAZING PERFORMANCE:
SHGC=0.3 OR BETTER
U-VALUE = 2.0 W/(M2K) OR BETTER'

NOTES:
THE SPECIFIC SPECIFICATIONS FOR DOORS, WINDOWS, AND HARDWARE WILL BE PROVIDED DURING THE IFC REVIEW STAGE.

NOTE : THIS PRINT IS OF A CONFIDENTIAL NATURE, IT SHALL NOT BE TRACED,PHOTOGRAPHED,PHOTOSTATED OR REPRODUCED IN ANY MANER,NOR USED FOR ANY PURPOSE WHATSOEVER EXCEPT BY WRITTEN PERMISSION

CLIENT :
GULF EDGE DC 01
87 Wireless Road, M Thai Tower 11th. Floor, All Seasons Place, Lumpini, Pathumwan, Bangkok 10330, Thailand

CONTRACTOR :
华西发展(泰国)有限公司
บริษัท หัวซือ ดีเวลลอปเม้นต์ (ประเทศไทย) จำกัด
HUASHI DEVELOPMENT CO.,LTD
No. 202, Room No. 1403, 14/F, Le Concorde Building, Ratchadapisek Road, Huaykhwang Sub-District, Huaykhwang District, Bangkok Metropolitan 10310.

CONSULTANT :
ARbay
บริษัท เอ อาร์ เบย์ จำกัด
ARbay Company Limited
31 st Floor Bangkok Insurance Building
25 South Sathorn road Thungmahamek
Sathorn Bangkok 10120 THAILAND
T +66 (0) 2286 8199
F +66 (0) 2286 2863
info@arbay.co.th

CONSULTANT :
Qbic Engineers & Architects Co.,Ltd.
8 Soi KALONG 4 SANAMBINNAM ROAD,
THASAI SUB-DISTRICT, MUANG NONTHABURI DISTRICT
, NONTHABURI.
Tel 662-950-4374
Fax 662-580-3231
E-Mail : qbic@qbic.co.th, www.qbic.co.th
QBIC ENGINEERS AND ARCHITECTS CO.,LTD.

CONSULTANT :
MITR
MITR TECHNICAL CONSULTANT CO.,LTD.
1168/8 12th FLOOR, LUMPINI TOWER BUILDING,
RAMA IV RD., THUNGMAHAMEK, SATHORN, BANGKOK 10120, THAILAND
TEL : 0-2679-9079-84
FAX : 0-2679-9085 E-mail: mitr_dd@mitr.com

	SIGNATURE
Architect :	SIGNATURE
ประกิต พนานุรัตน์ วสถ. 580 ที่อยู่ 251/1 ถ.จารุเมือง แขวงรองเมือง เขตปทุมวัน กรุงเทพมหานคร โทรศัพท์ 02-286-8199	
Structural Engineer :	SIGNATURE
วิศวกรผู้ออกแบบโครงสร้าง	
ณัฐสม สงวนวงษ์ วย 1423 ที่อยู่ 2/1 ซ.รามคำแหง 150 ถ.รามคำแหง แขวง สะพานสูง เขต สะพานสูง กทม. 10240	
Structural Inspector :	SIGNATURE
วิศวกรผู้ตรวจสอบโครงสร้าง	
โกมล จุฑาภัทร วย 964 ที่อยู่ 24/18 ซ.นวมินทร์ 129 ถ. นวมินทร์ แขวง นวลจันทร์ เขต บึงกุ่ม กทม. 10230	
Electrical Engineer :	SIGNATURE
วิศวกรผู้ออกแบบระบบไฟฟ้ากำลัง	
นายสุภัทร บูรณวิทย์ วฟก.1265 ที่อยู่ 21 ซอยทานสัมฤทธิ์ 13 ตำบลท่าทราย อ.เมืองนนทบุรี จ.นนทบุรี 11000	
Mechanical Engineer :	SIGNATURE
วิศวกรผู้ออกแบบระบบเครื่องกลและปรับอากาศ	
นายประสิทธิ์ เกียวสุนทร วก.1221 ที่อยู่ 44/372 ซอยบางกระดี่ 35/1 แขวงแสมดำ เขตบางขุนเทียน กทม. 10150	ประสิทธิ์
Sanitary Engineer :	SIGNATURE
วิศวกรผู้ออกแบบระบบสุขาภิบาล และดับเพลิง	
นายทศวรรษ สันนฤทธิ์ วส. 215 ที่อยู่ บ้านเลขที่ 99/107 หมู่ที่ 3 ต.ศีรษะจรเข้น้อย อ.บางเสาธง จ.สมุทรปราการ 10540	ทศวรรษ

ISSUE/REVISION

REV.	DESCRIPTION	DATE
A	90% DEVELOPED	09/05/2026

PROJECT NAME :
GEDC 01

LOCATION:
Nikhom Phattana district, Rayong ,industrial estate,CPGC

BUILDING :
MAIN BUILDING

90% DEVELOPED

TITLE :
SCHEDULE OF DOOR & WINDOW

JOB NO.	SCALE 1:50
DRAWN KHJ	REF.
CHECKED LJC	DWG.NO. MPK00-90-A-SC-002
APPROVED LXD	
DATE 2026.05.09	