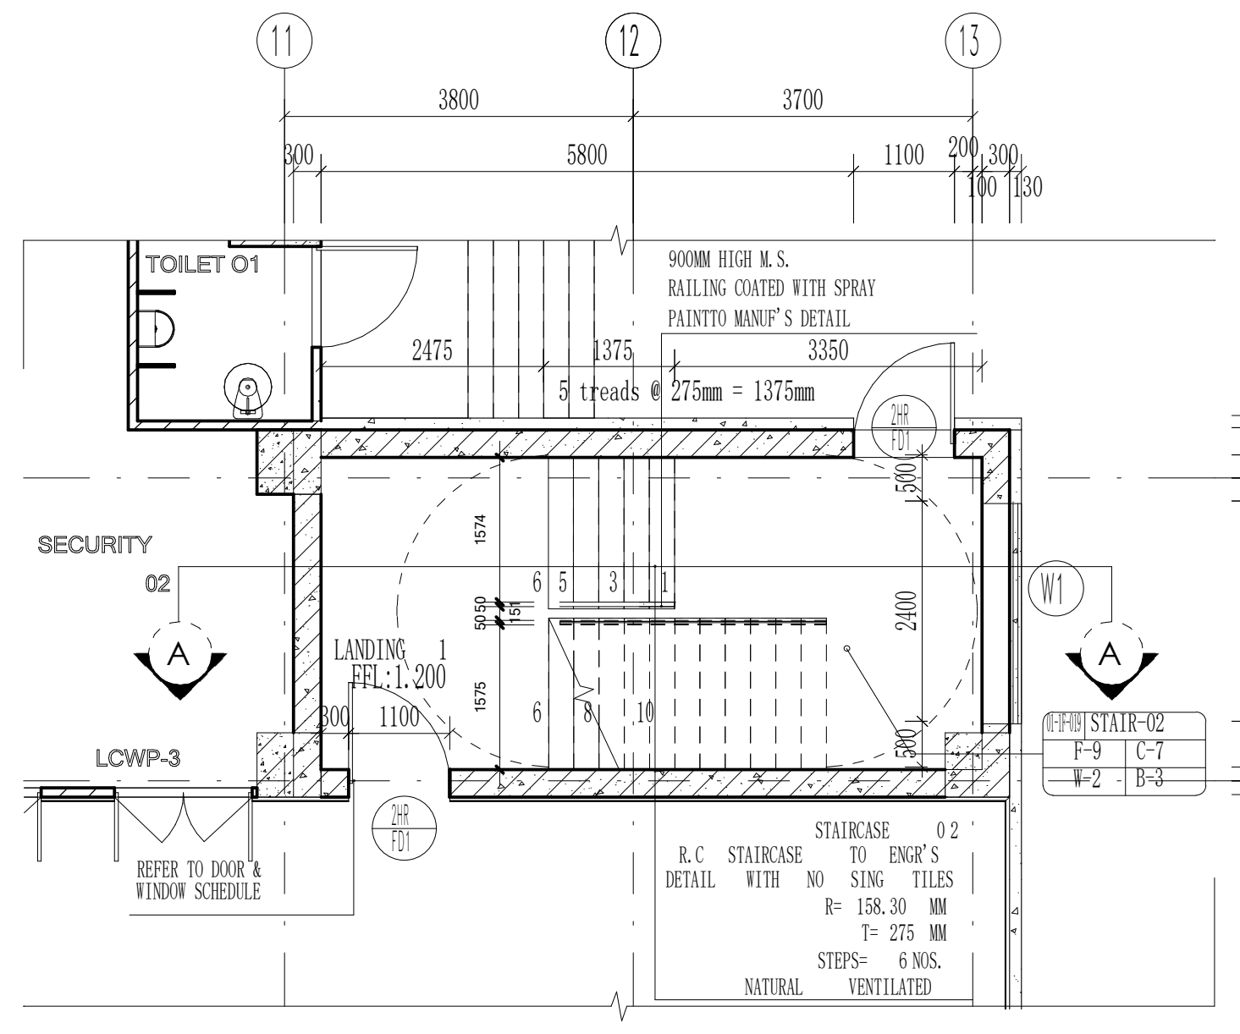
TOILET 01
SECURITY 02
LCWP-3
900MM HIGH M.S. RAILING COATED WITH SPRAY PAINTTO MANUF'S DETAIL
5 treads @ 275mm = 1375mm
LANDING 1 FFL:1.200
REFER TO DOOR & WINDOW SCHEDULE
STAIRCASE 02 R.C STAIRCASE TO ENGR'S DETAIL WITH NO SING TILES
R= 166.70 MM
T= 275 MM
STEPS= 48 NOS.
NATURAL VENTILATED
3800
3700
5800

STAIR-2 1ST FL
SCALE 1:75

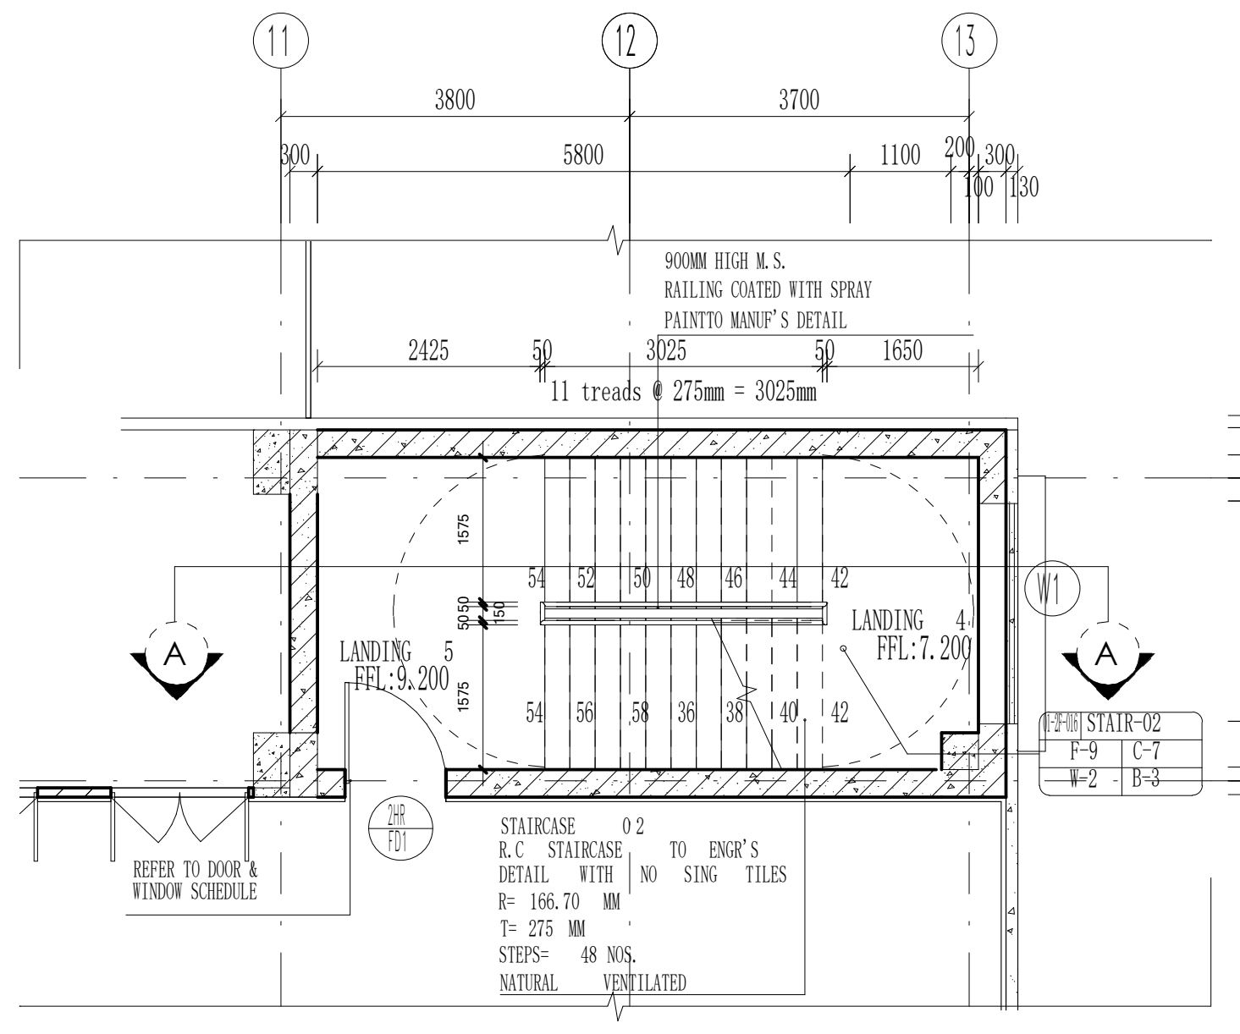
900MM HIGH M.S. RAILING COATED WITH SPRAY PAINTTO MANUF'S DETAIL
11 treads @ 275mm = 3025mm
LANDING 5 FFL:5.200
LANDING 4 FFL:7.200
STAIRCASE 02 R.C STAIRCASE TO ENGR'S DETAIL WITH NO SING TILES
R= 166.70 MM
T= 275 MM
STEPS= 48 NOS.
NATURAL VENTILATED

STAIR-2 2ND FL
SCALE 1:75

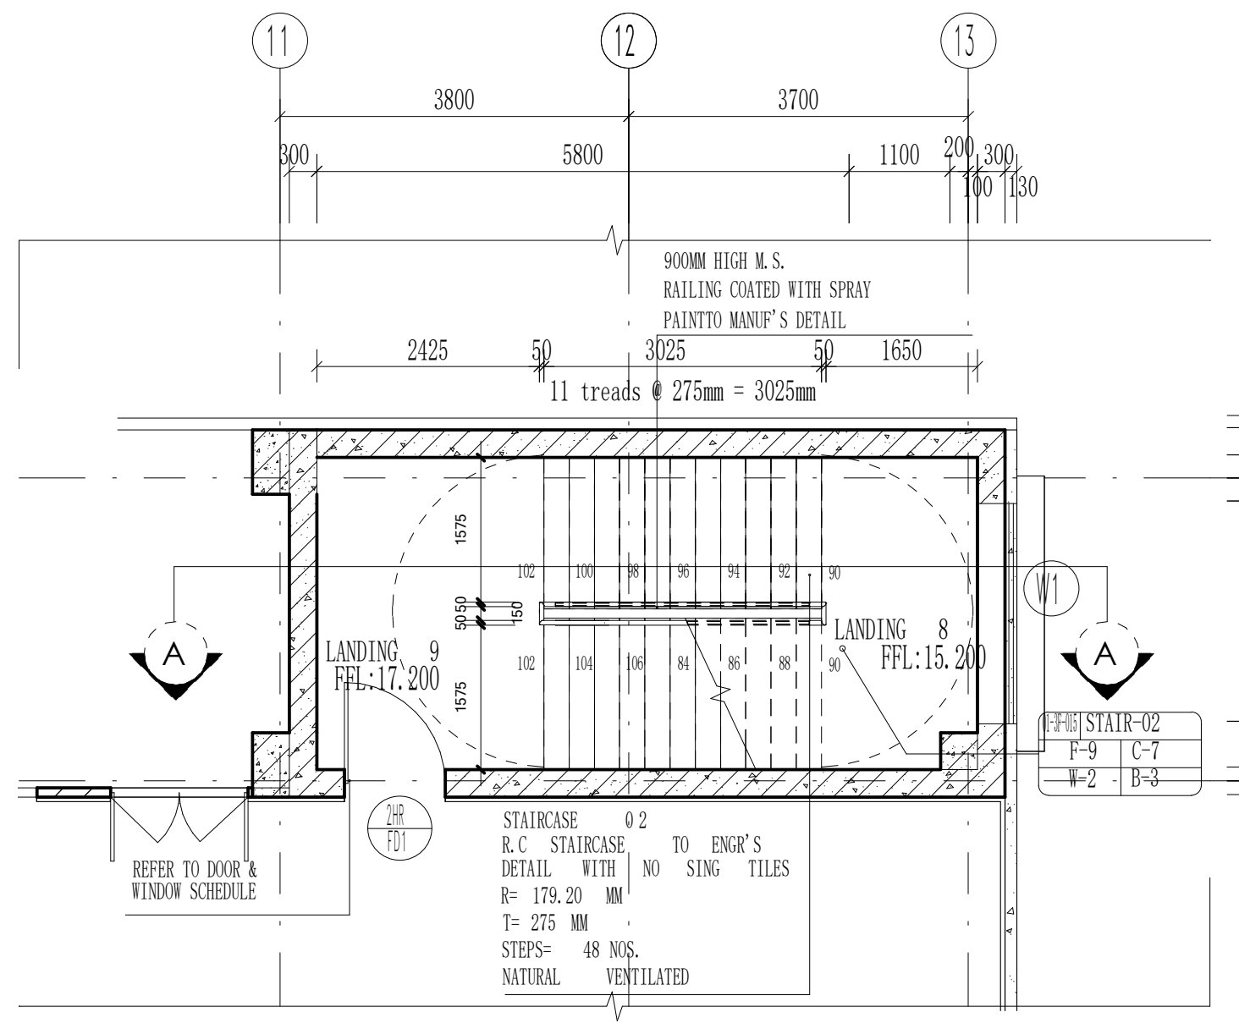
900MM HIGH M.S. RAILING COATED WITH SPRAY PAINTTO MANUF'S DETAIL
11 treads @ 275mm = 3025mm
LANDING 9 FFL:17.200
LANDING 8 FFL:15.200
STAIRCASE 02 R.C STAIRCASE TO ENGR'S DETAIL WITH NO SING TILES
R= 176.20 MM
T= 275 MM
STEPS= 48 NOS.
NATURAL VENTILATED

STAIR-2 3RD FL
SCALE 1:75

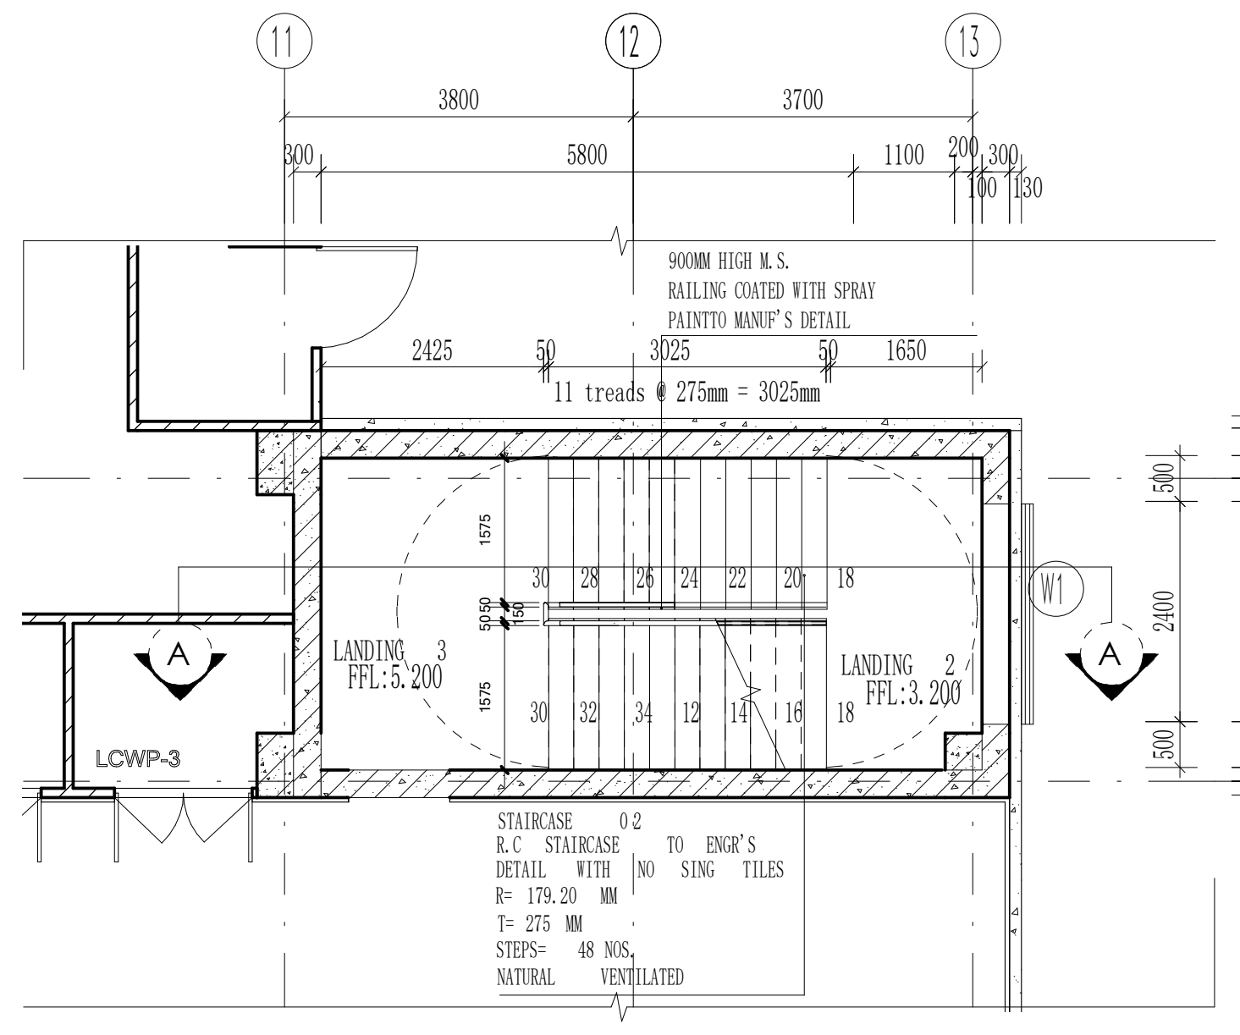
900MM HIGH M.S. RAILING COATED WITH SPRAY PAINTTO MANUF'S DETAIL
11 treads @ 275mm = 3025mm
LANDING 3 FFL:5.200
LANDING 2 FFL:3.200
LCWP-3
STAIRCASE 02 R.C STAIRCASE TO ENGR'S DETAIL WITH NO SING TILES
R= 176.20 MM
T= 275 MM
STEPS= 48 NOS.
NATURAL VENTILATED

STAIR-2 5.200 ELEVATION PLAN FL
SCALE 1:75

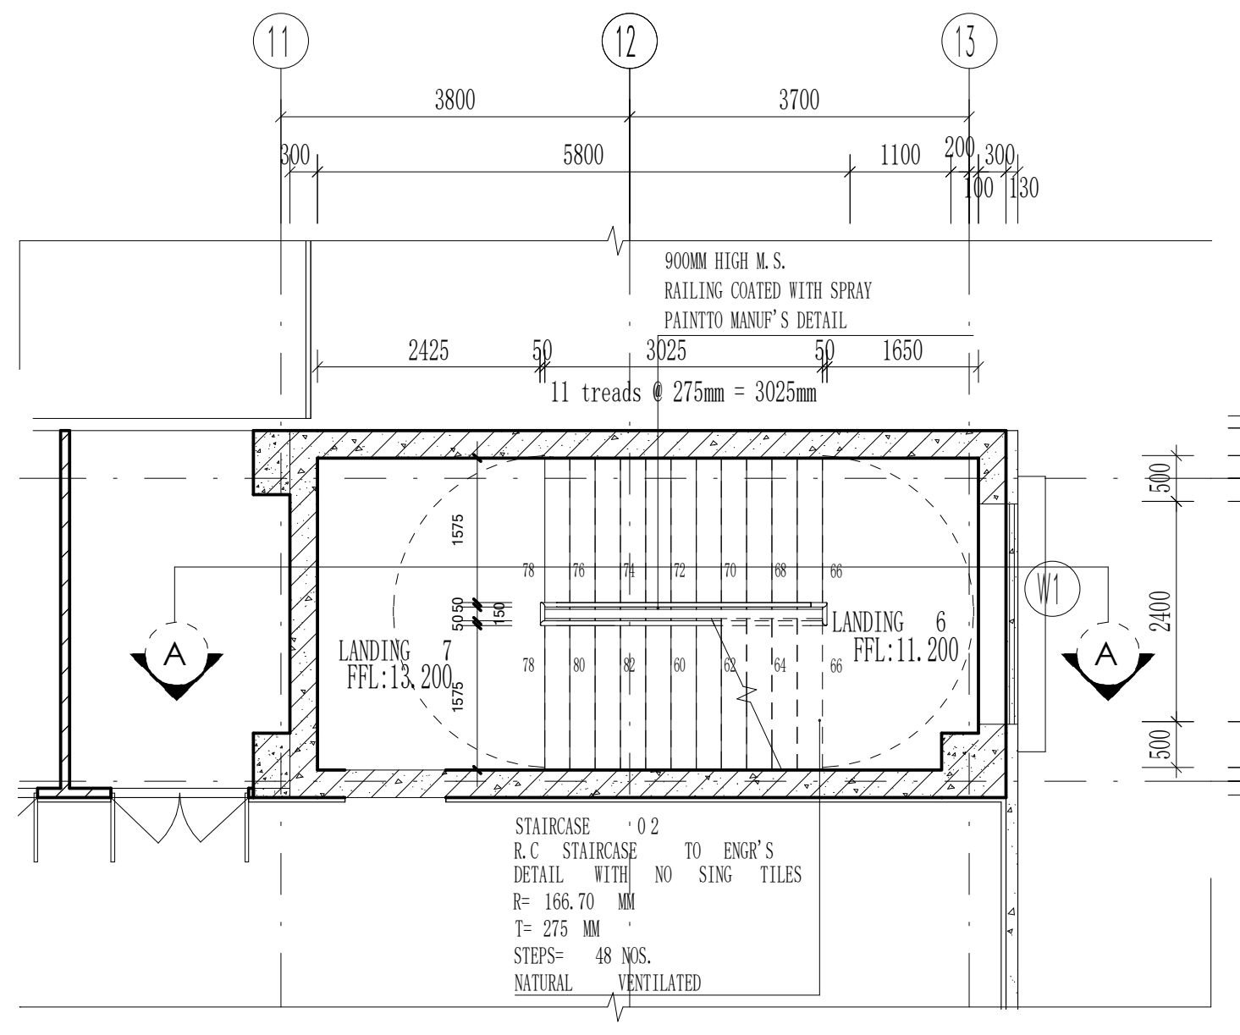
900MM HIGH M.S. RAILING COATED WITH SPRAY PAINTTO MANUF'S DETAIL
11 treads @ 275mm = 3025mm
LANDING 7 FFL:13.200
LANDING 6 FFL:11.200
STAIRCASE 02 R.C STAIRCASE TO ENGR'S DETAIL WITH NO SING TILES
R= 166.70 MM
T= 275 MM
STEPS= 48 NOS.
NATURAL VENTILATED

STAIR-2 13.200 ELEVATION PLAN FL
SCALE 1:75

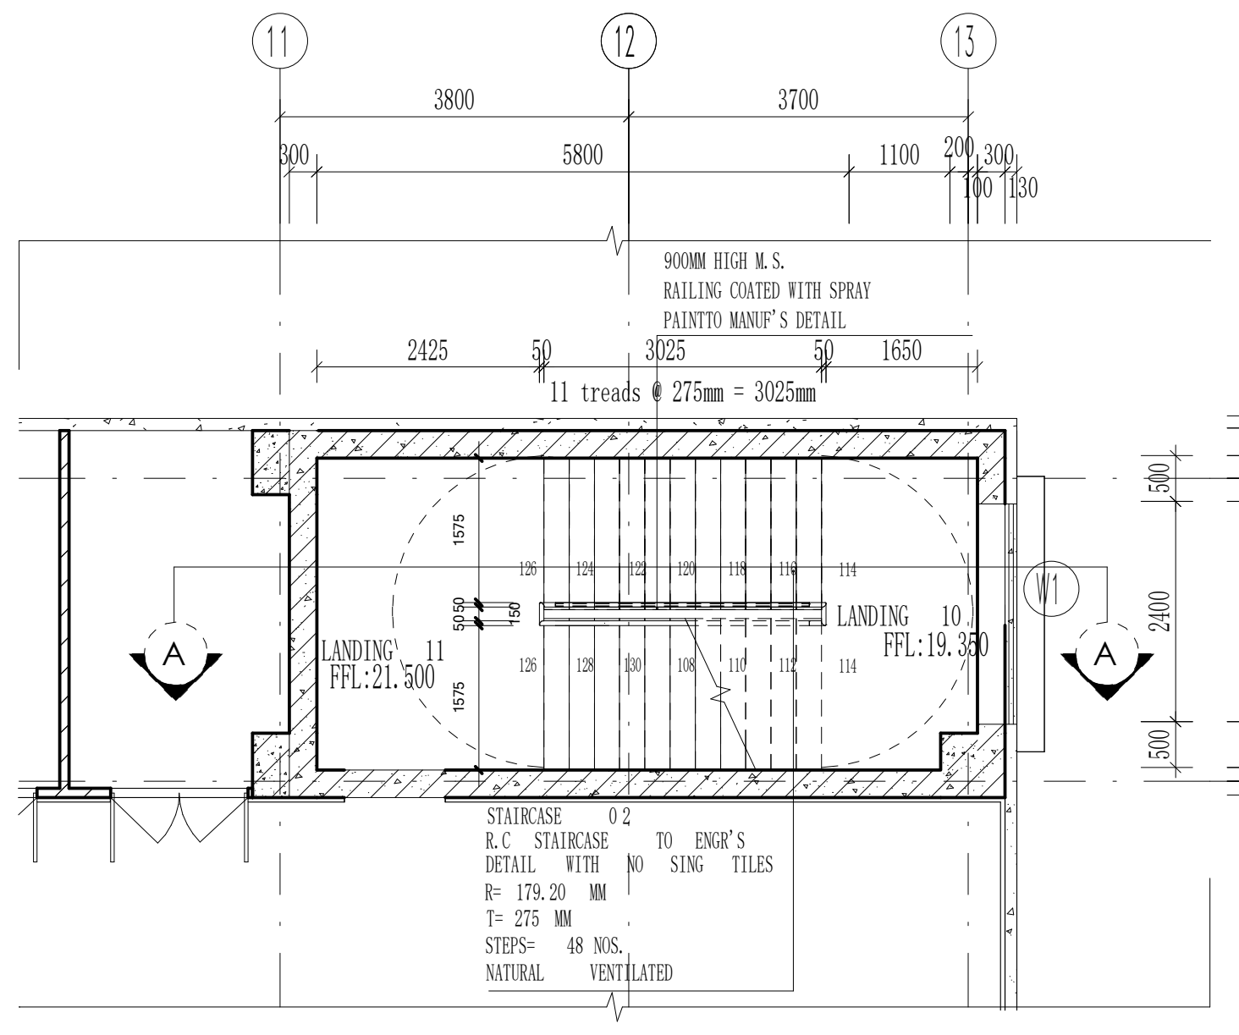
900MM HIGH M.S. RAILING COATED WITH SPRAY PAINTTO MANUF'S DETAIL
11 treads @ 275mm = 3025mm
LANDING 11 FFL:21.500
LANDING 10 FFL:19.350
STAIRCASE 02 R.C STAIRCASE TO ENGR'S DETAIL WITH NO SING TILES
R= 176.20 MM
T= 275 MM
STEPS= 48 NOS.
NATURAL VENTILATED

STAIR-2 21.500 ELEVATION PLAN FL
SCALE 1:75

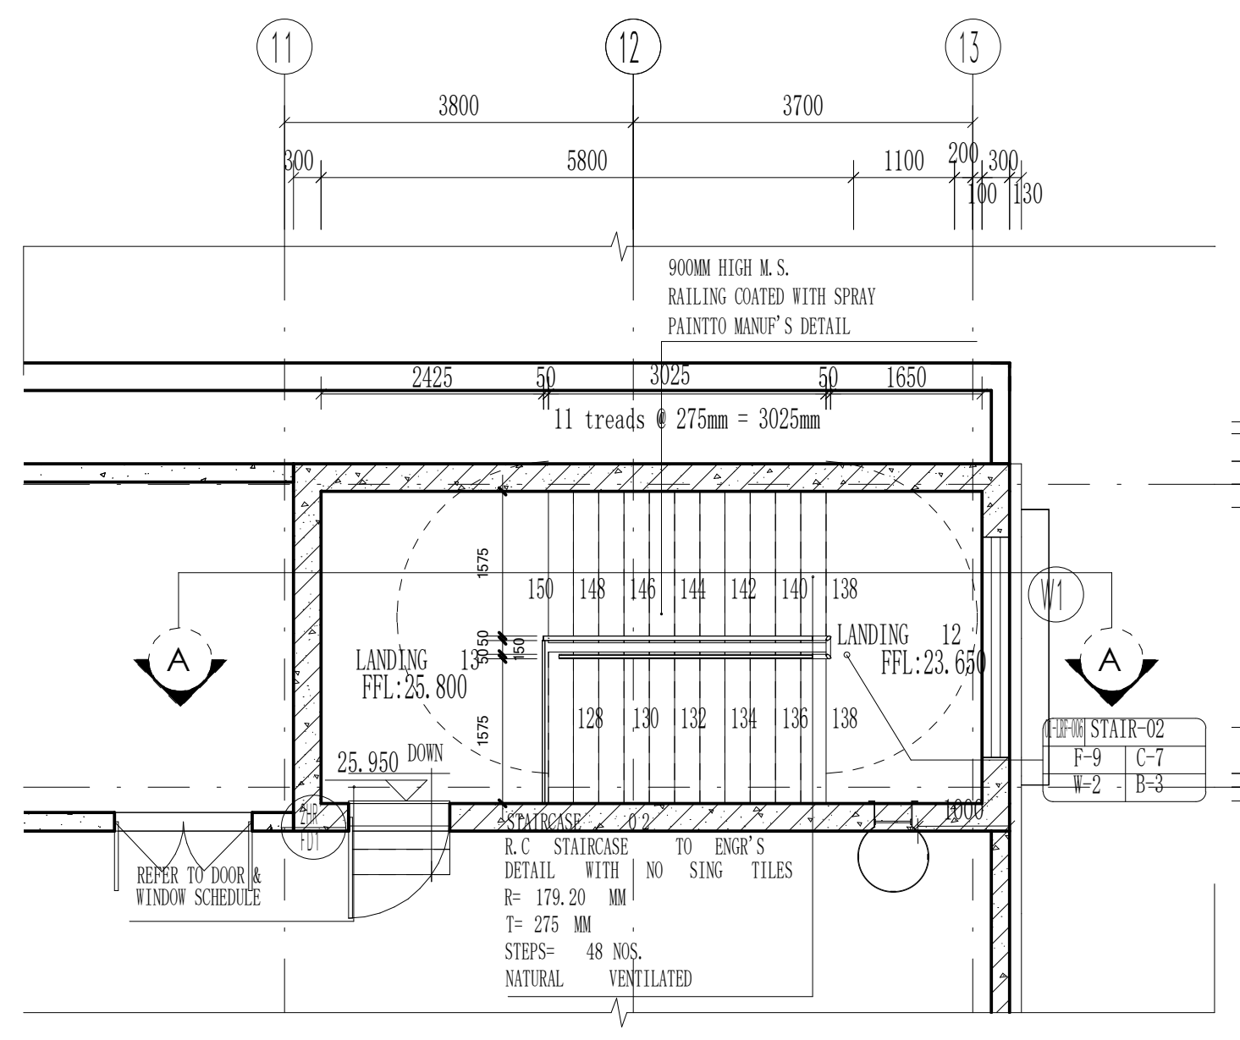
900MM HIGH M.S. RAILING COATED WITH SPRAY PAINTTO MANUF'S DETAIL
11 treads @ 275mm = 3025mm
LANDING 13 FFL:26.800
LANDING 12 FFL:23.650
25.950 DOWN
REFER TO DOOR & WINDOW SCHEDULE
STAIRCASE 02 R.C STAIRCASE TO ENGR'S DETAIL WITH NO SING TILES
R= 176.20 MM
T= 275 MM
STEPS= 48 NOS.
NATURAL VENTILATED

STAIR-2 RF FL
SCALE 1:75

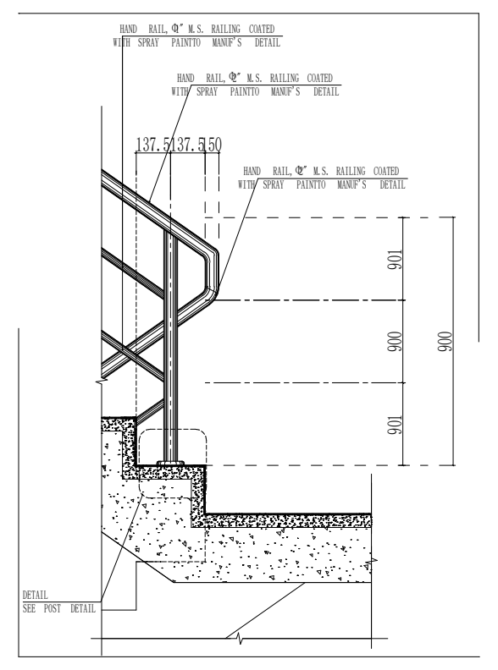

HANDRAIL DETAILS
SCALE 1:75

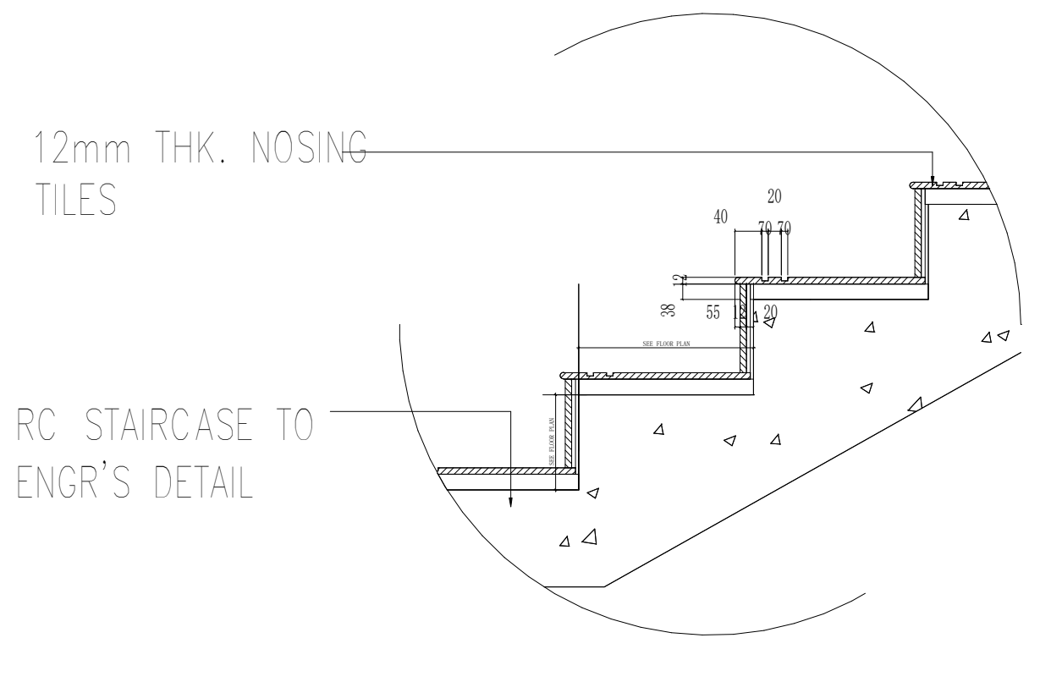
12mm THK. NOSING TILES
RC STAIRCASE TO ENGR'S DETAIL

STEP DETAILS
SCALE 1:75

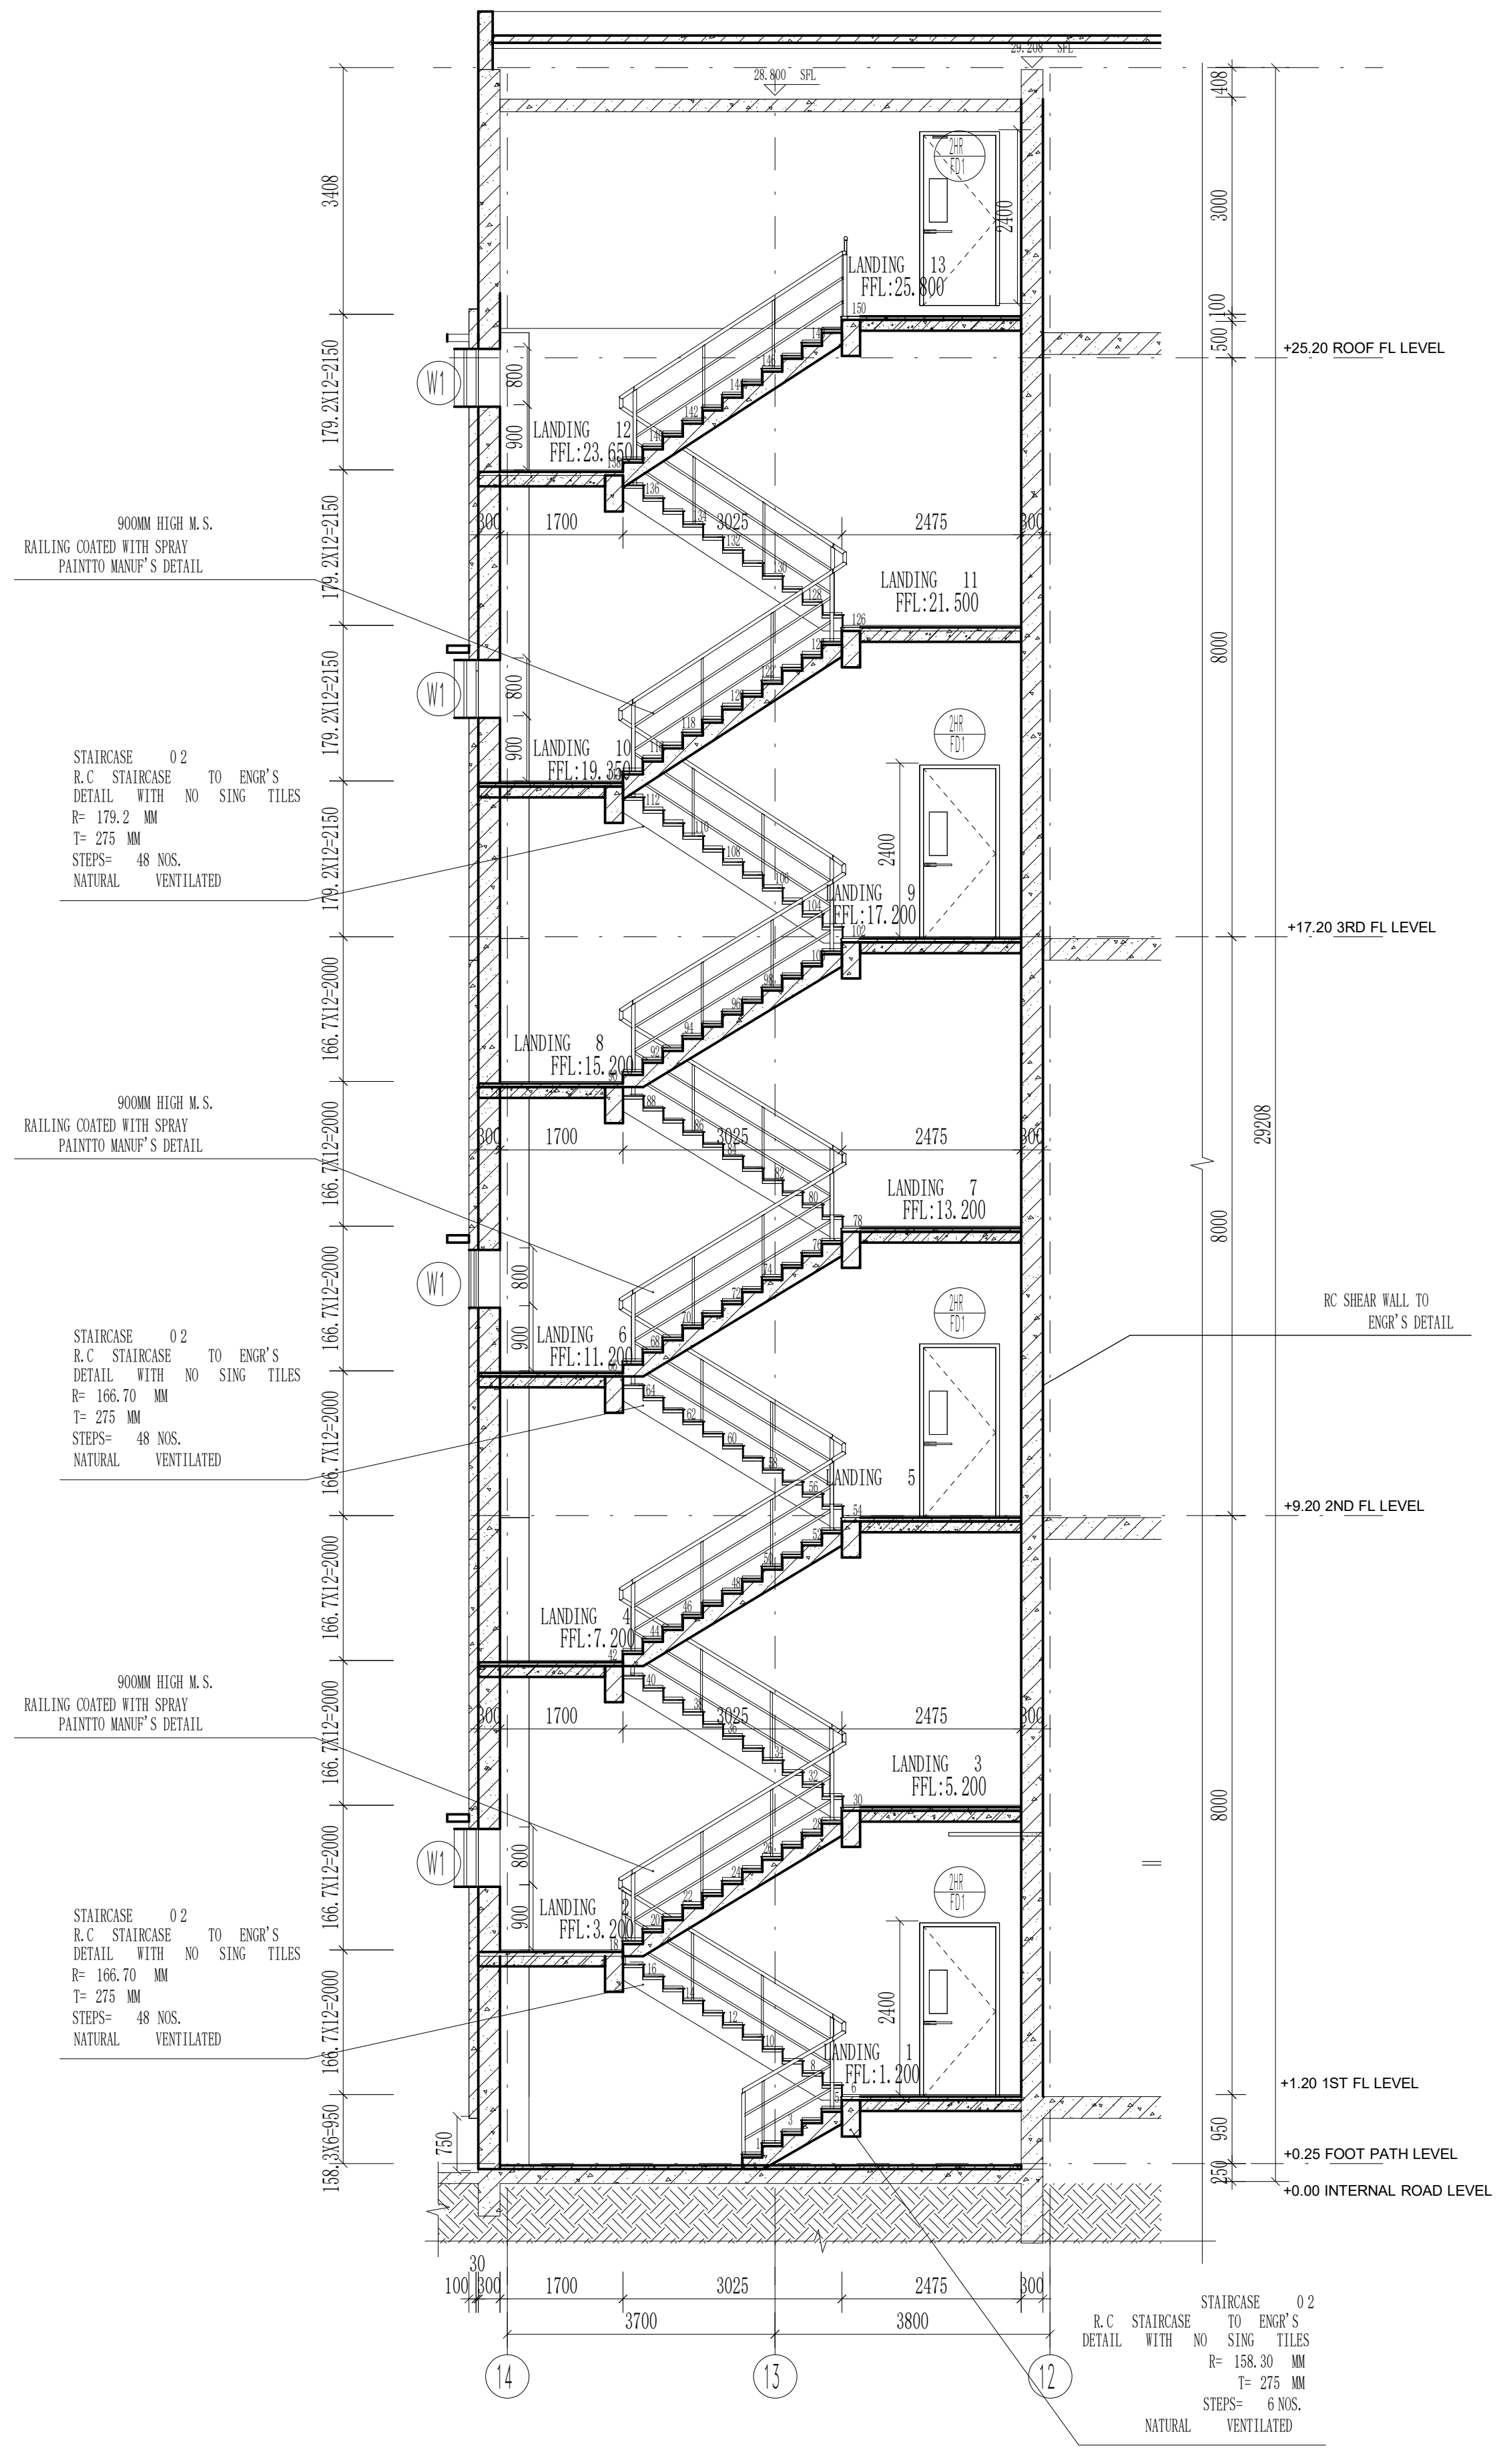
+25.20 ROOF FL LEVEL
+17.20 3RD FL LEVEL
+9.20 2ND FL LEVEL
+1.20 1ST FL LEVEL
+0.25 FOOT PATH LEVEL
±0.00 INTERNAL ROAD LEVEL
RC SHEAR WALL TO ENGR'S DETAIL
900MM HIGH M.S. RAILING COATED WITH SPRAY PAINTTO MANUF'S DETAIL
STAIRCASE 02 R.C STAIRCASE TO ENGR'S DETAIL WITH NO SING TILES
LANDING 13 FFL:25.800
LANDING 12 FFL:23.650
LANDING 11 FFL:21.500
LANDING 10 FFL:19.350
LANDING 9 FFL:17.200
LANDING 8 FFL:15.200
LANDING 7 FFL:13.200
LANDING 6 FFL:11.200
LANDING 5
LANDING 4 FFL:7.200
LANDING 3 FFL:5.200
LANDING 2 FFL:3.200
LANDING 1 FFL:1.200
1700
2475
3700
3025
3800
14
13
12

Section A
SCALE 1:75

CLIENT :

GULF EDGE DC 01

87 Wireless Road, M Thai Tower 11th. Floor, All Seasons Place, Lumpini,
Pathumwan, Bangkok 10330, Thailand

CONTRACTOR :

华西发展(泰国)有限公司
บริษัท หัวซือ ดีเวลลอปเม้นต์ (ประเทศไทย) จำกัด
HUASHI DEVELOPMENT CO.,LTD
No. 202, Room No. 1403, 14/F, Le Concorde Building,
Ratchadapisek Road, Huaykhwang Sub-District,
Huaykhwang District, Bangkok Metropolitan 10310.

CONSULTANT :

ARbay
บริษัท เอ อาร์ เบย์ จำกัด
ARbay Company Limited
31 st Floor Bangkok Insurance Building
25 South Sathorn road Thungmahamek
Sathorn Bangkok 10120 THAILAND
T +66 (0) 2286 8199
F +66 (0) 2286 2863
info@arbay.co.th

CONSULTANT :

Qbic Engineers & Architects Co.,Ltd.
8 Soi KALONG 4 SANAMBINNAM ROAD,
THASAI SUB-DISTRICT, MUANG NONTHABURI DISTRICT
, NONTHABURI.
Tel 662-950-4374
Fax 662-580-3231
E-Mail : qbic@qbic.co.th, www.qbic.co.th
QBIC ENGINEERS AND ARCHITECTS CO.,LTD.

CONSULTANT :

MITR
MITR TECHNICAL CONSULTANT CO.,LTD.
1168/8 12th FLOOR, LUMPINI TOWER BUILDING,
RAMA IV RD., THUNGMAHAMEK, SATHORN, BANGKOK 10120, THAILAND
TEL : 0-2679-9079-84
FAX : 0-2679-9085 E-mail: mitr_dd@mitr.com

Architect : SIGNATURE
ประกิต พนานุรัตน์ วสถ. 580
ที่อยู่
251/1 ถ.จารุเมือง แขวงรองเมือง เขตปทุมวัน
กรุงเทพมหานคร โทรศัพท์ 02-286-8199

Structural Engineer : SIGNATURE
วิศวกรผู้ออกแบบโครงสร้าง
ณัฐสม สงวนวงษ์ วย 1423
ที่อยู่
2/1 ซ.รามคำแหง 150 ถ.รามคำแหง
แขวง สะพานสูง เขต สะพานสูง กทม. 10240

Structural Inspector : SIGNATURE
วิศวกรผู้ตรวจสอบโครงสร้าง
โกมล จุฑาภัทร วย 964
ที่อยู่
24/18 ซ.นวมินทร์ 129 ถ. นวมินทร์
แขวง นวลจันทร์ เขต บึงกุ่ม กทม. 10230

Electrical Engineer : SIGNATURE
วิศวกรผู้ออกแบบระบบไฟฟ้ากำลัง
นายสุภัทร บูรณวิทย์ วฟก.1265
ที่อยู่
21 ซอยทานสัมฤทธิ์ 13
ตำบลท่าทราย อ.เมืองนนทบุรี จ.นนทบุรี 11000

Mechanical Engineer : SIGNATURE
วิศวกรผู้ออกแบบระบบเครื่องกลและปรับอากาศ
นายประสิทธิ์ เกี้ยวสุนทร วก.1221
ที่อยู่
44/372 ซอยบางกระดี่ 35/1 แขวงแสมดำ
เขตบางขุนเทียน กทม. 10150

ประสิทธิ์

Sanitary Engineer : SIGNATURE
วิศวกรผู้ออกแบบระบบสุขาภิบาล และดับเพลิง
นายทศวรรษ สนั่นฤทธิ์ วส. 215
ที่อยู่
บ้านเลขที่ 99/107 หมู่ที่ 3 ต.ศีรษะจรเข้น้อย
อ.บางเสาธง จ.สมุทรปราการ 10540

ทศวรรษ

ISSUE/REVISION

REV.	DESCRIPTION	DATE
A	90% DEVELOPED	09/05/2026

PROJECT NAME :

GEDC 01

LOCATION:
Nikhom Phattana district, Rayong ,industrial estate,CPGC

BUILDING :
MAIN BUILDING

90% DEVELOPED

TITLE :

STAIRCASE 02

JOB NO.
SCALE 1 : 75
DRAWN WYSH
REF.
CHECKED LJC
DWG. NO. MPK01A-90-A-ST-002
APPROVED LXD
DATE 2026.05.09

NOTE :THIS PRINT IS OF A CONFIDENTIAL NATURE, IT SHALL NOT BE TRACED,PHOTOGRAPHED,PHOTOSTATED OR REPRODUCED IN ANY MANER,NOR USED FOR ANY PURPOSE WHATSOEVER EXCEPT BY WRITTEN PERMISSION