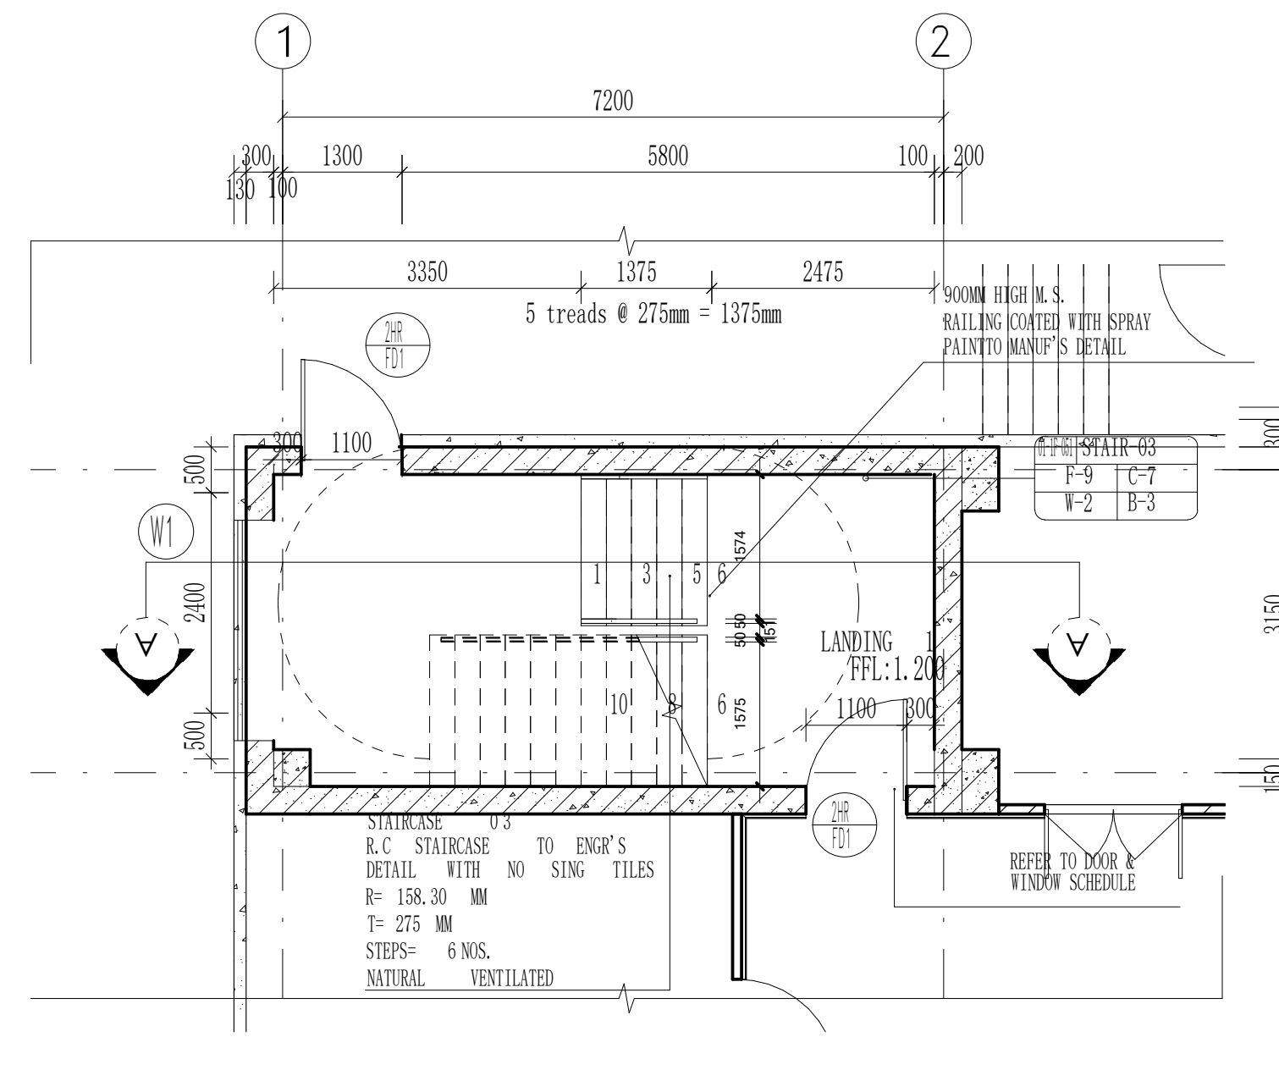
1
2
7200
300
1300
5800
100
200
130
100
3350
1375
2475
5 treads @ 275mm = 1375mm
900MM HIGH M.S. RAILING COATED WITH SPRAY PAINTTO MANUF'S DETAIL
2HR FD1
1100
STAIR-03
F-9
C-7
W-2
B-3
W1
A
LANDING 1
FFL:1.200
G.2
G.1
3150
3300
STAIRCASE 03
R.C STAIRCASE TO ENGR'S DETAIL WITH NO SING TILES
R= 158.30 MM
T= 275 MM
STEPS= 6 NOS.
NATURAL VENTILATED
REFER TO DOOR & WINDOW SCHEDULE

STAIR-3 1ST FL

SCALE 1:75

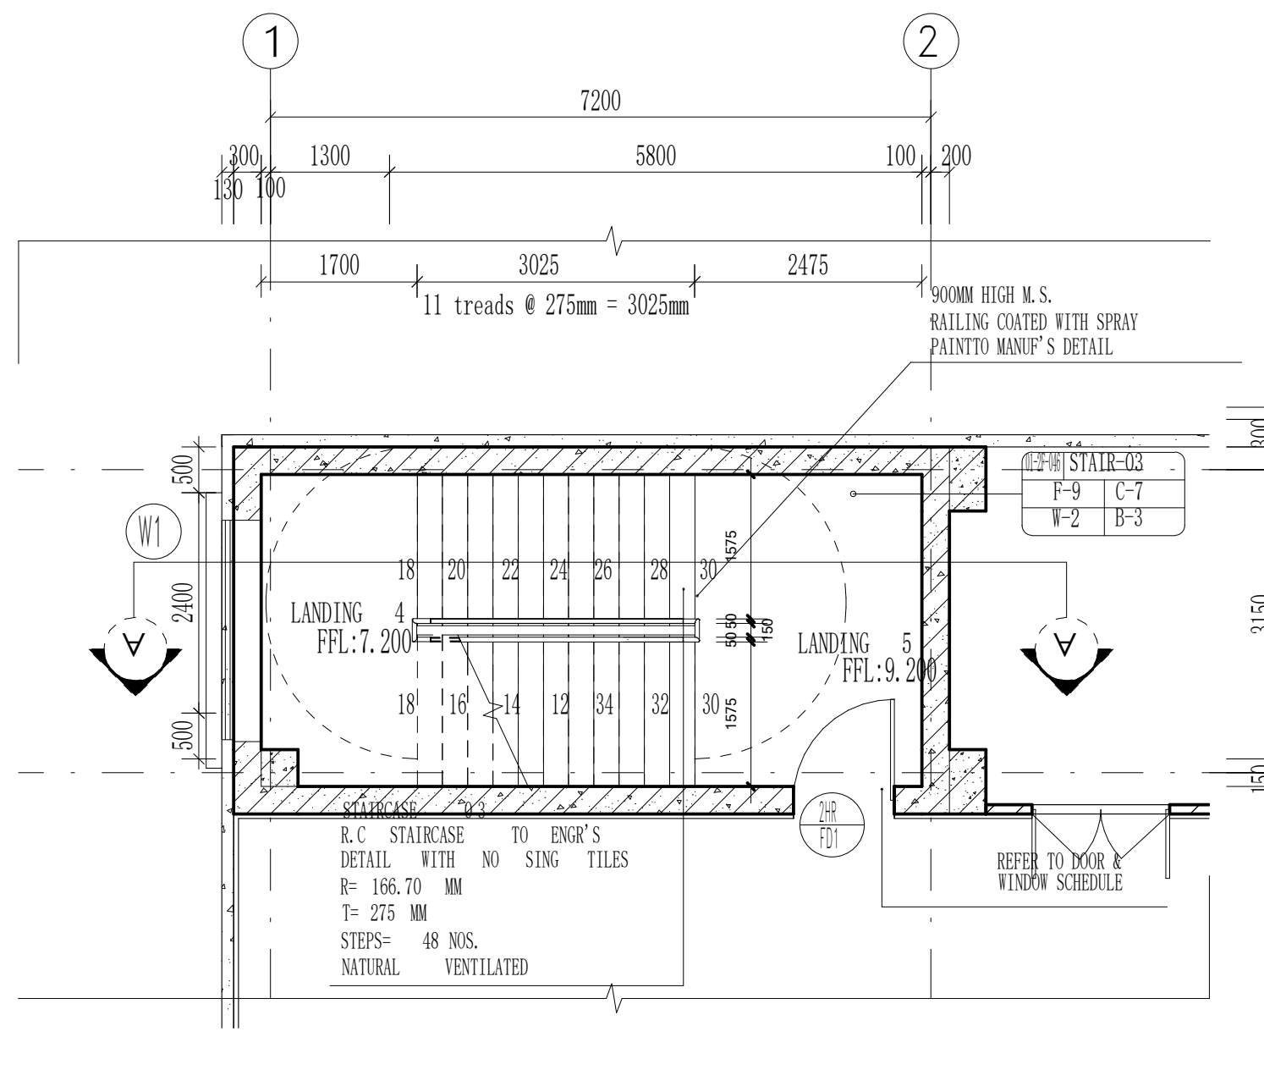
1
2
7200
1700
3025
2475
11 treads @ 275mm = 3025mm
900MM HIGH M.S. RAILING COATED WITH SPRAY PAINTTO MANUF'S DETAIL
LANDING 4
FFL:7.200
LANDING 5
FFL:9.200
STAIRCASE 03
R.C STAIRCASE TO ENGR'S DETAIL WITH NO SING TILES
R= 166.70 MM
T= 275 MM
STEPS= 48 NOS.
NATURAL VENTILATED
REFER TO DOOR & WINDOW SCHEDULE

STAIR-3 2ND FL

SCALE 1:75

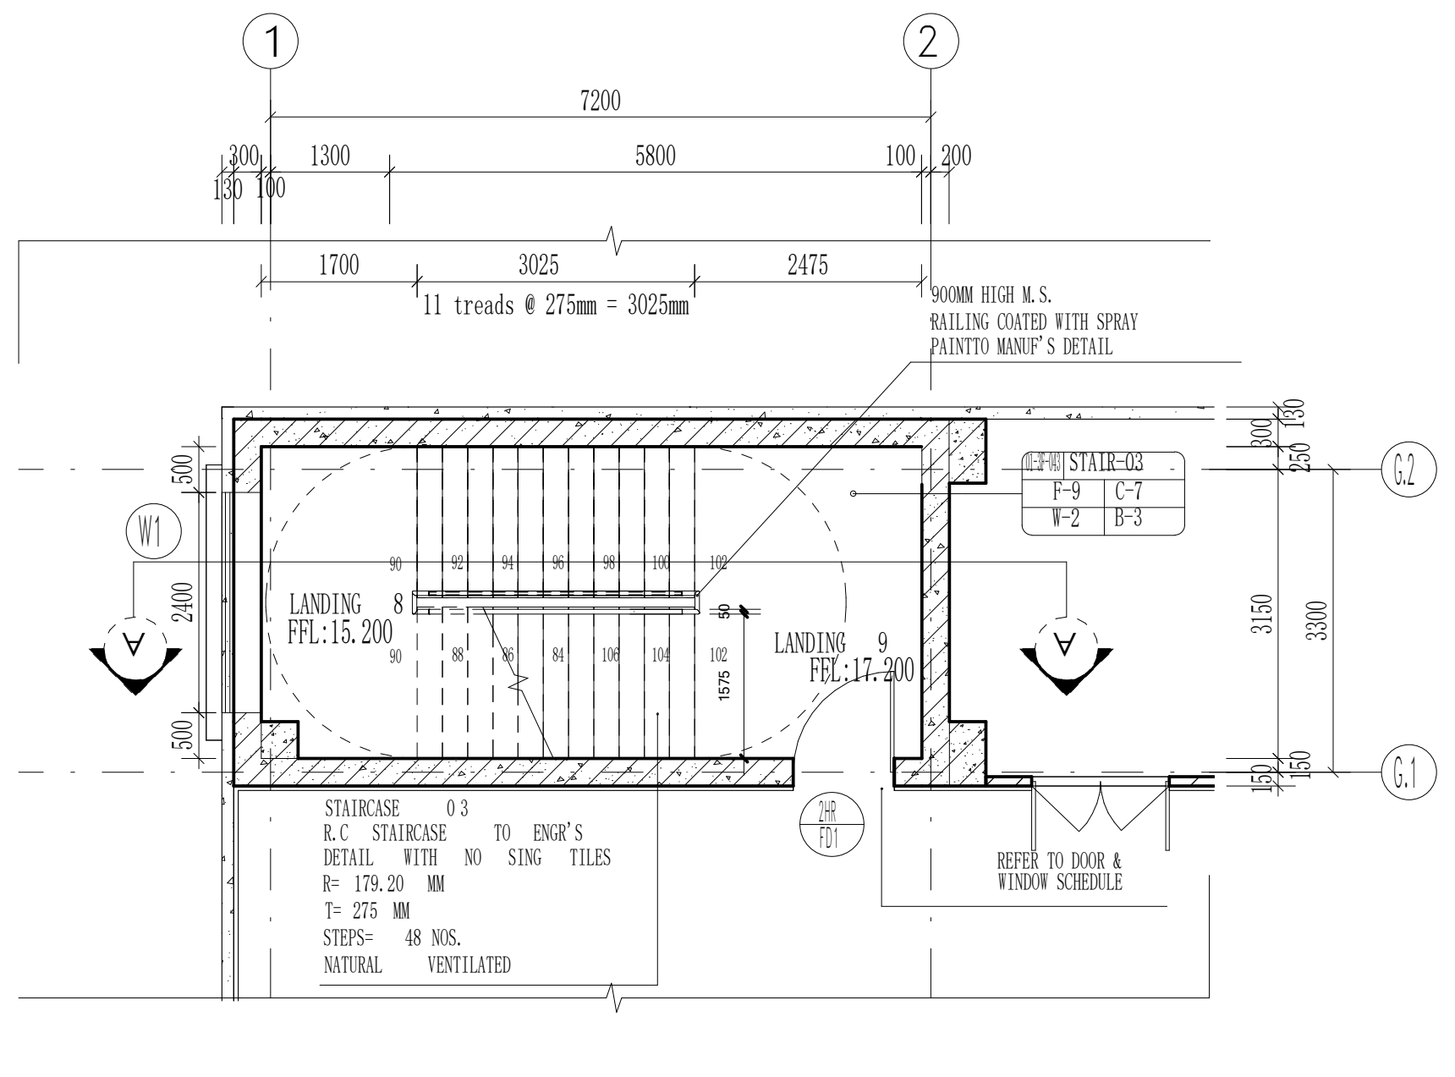
1
2
7200
1700
3025
2475
11 treads @ 275mm = 3025mm
900MM HIGH M.S. RAILING COATED WITH SPRAY PAINTTO MANUF'S DETAIL
LANDING 8
FFL:15.200
LANDING 9
FFL:17.200
STAIRCASE 03
R.C STAIRCASE TO ENGR'S DETAIL WITH NO SING TILES
R= 179.20 MM
T= 275 MM
STEPS= 48 NOS.
NATURAL VENTILATED
REFER TO DOOR & WINDOW SCHEDULE

STAIR-3 3RD FL

SCALE 1:75

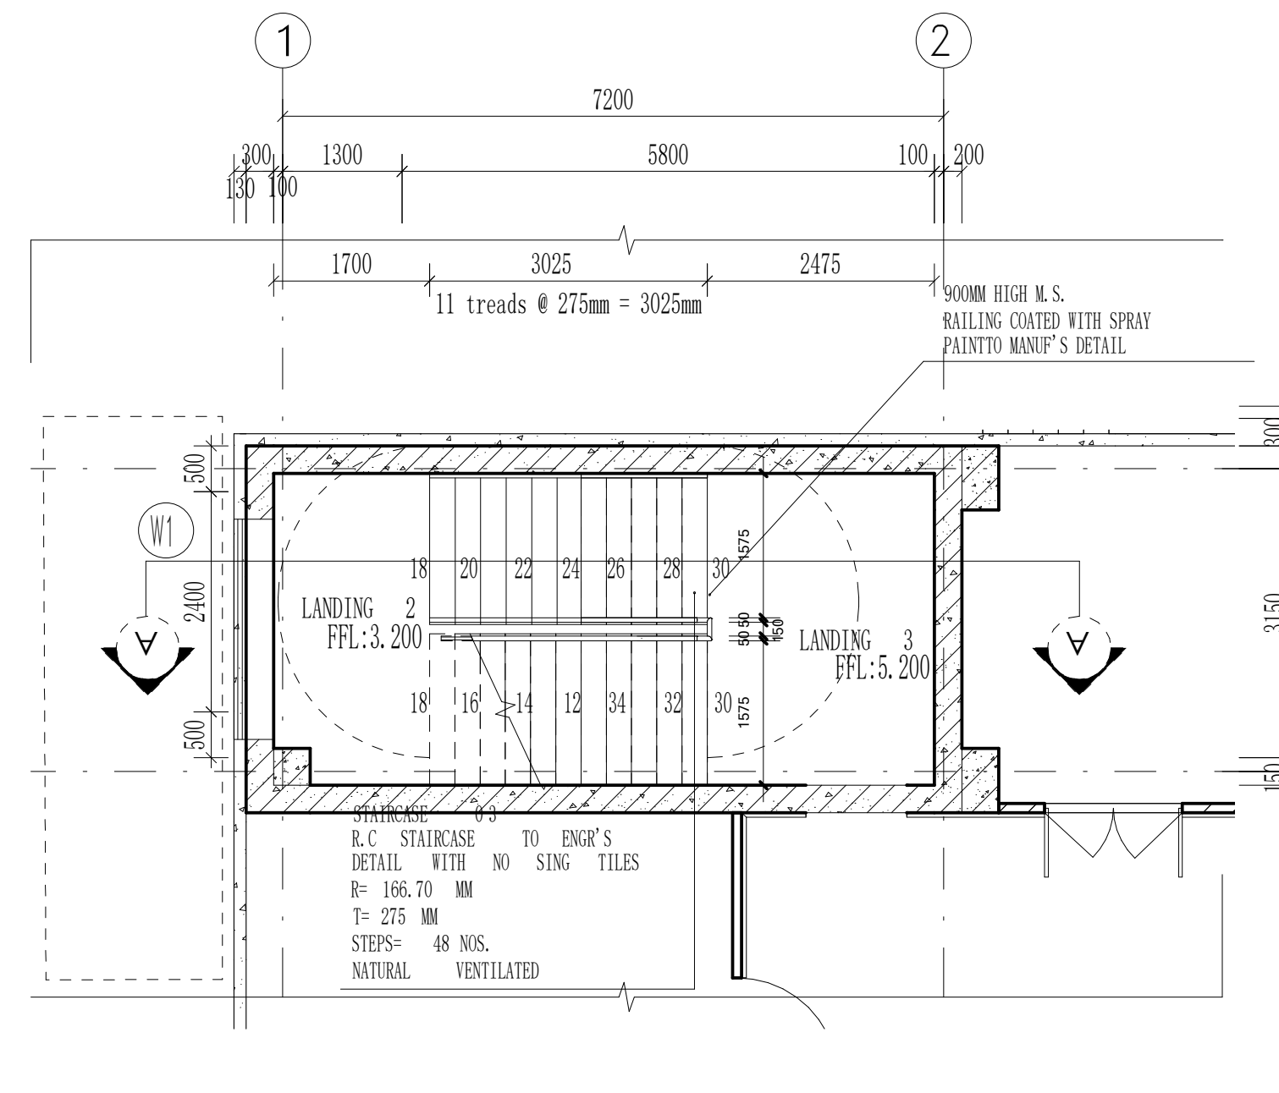
1
2
7200
1700
3025
2475
11 treads @ 275mm = 3025mm
900MM HIGH M.S. RAILING COATED WITH SPRAY PAINTTO MANUF'S DETAIL
LANDING 2
FFL:3.200
LANDING 3
FFL:5.200
STAIRCASE 03
R.C STAIRCASE TO ENGR'S DETAIL WITH NO SING TILES
R= 166.70 MM
T= 275 MM
STEPS= 48 NOS.
NATURAL VENTILATED

STAIR-3 5.200 ELEVATION PLAN FL

SCALE 1:75

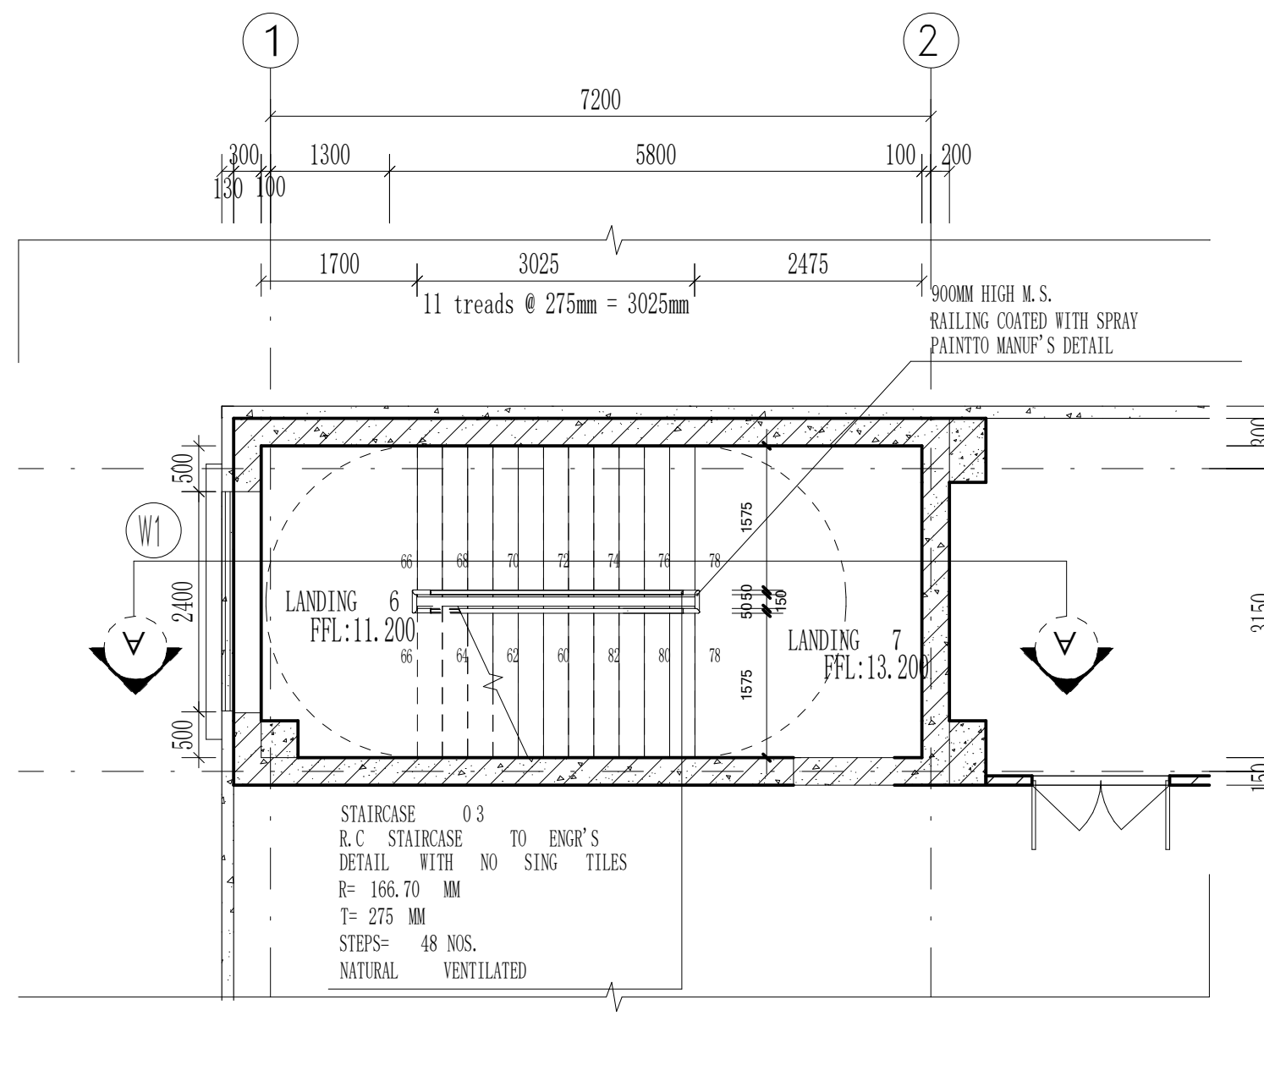
1
2
7200
1700
3025
2475
11 treads @ 275mm = 3025mm
900MM HIGH M.S. RAILING COATED WITH SPRAY PAINTTO MANUF'S DETAIL
LANDING 6
FFL:11.200
LANDING 7
FFL:13.200
STAIRCASE 03
R.C STAIRCASE TO ENGR'S DETAIL WITH NO SING TILES
R= 166.70 MM
T= 275 MM
STEPS= 48 NOS.
NATURAL VENTILATED

STAIR-3 13.200 ELEVATION PLAN FL

SCALE 1:75

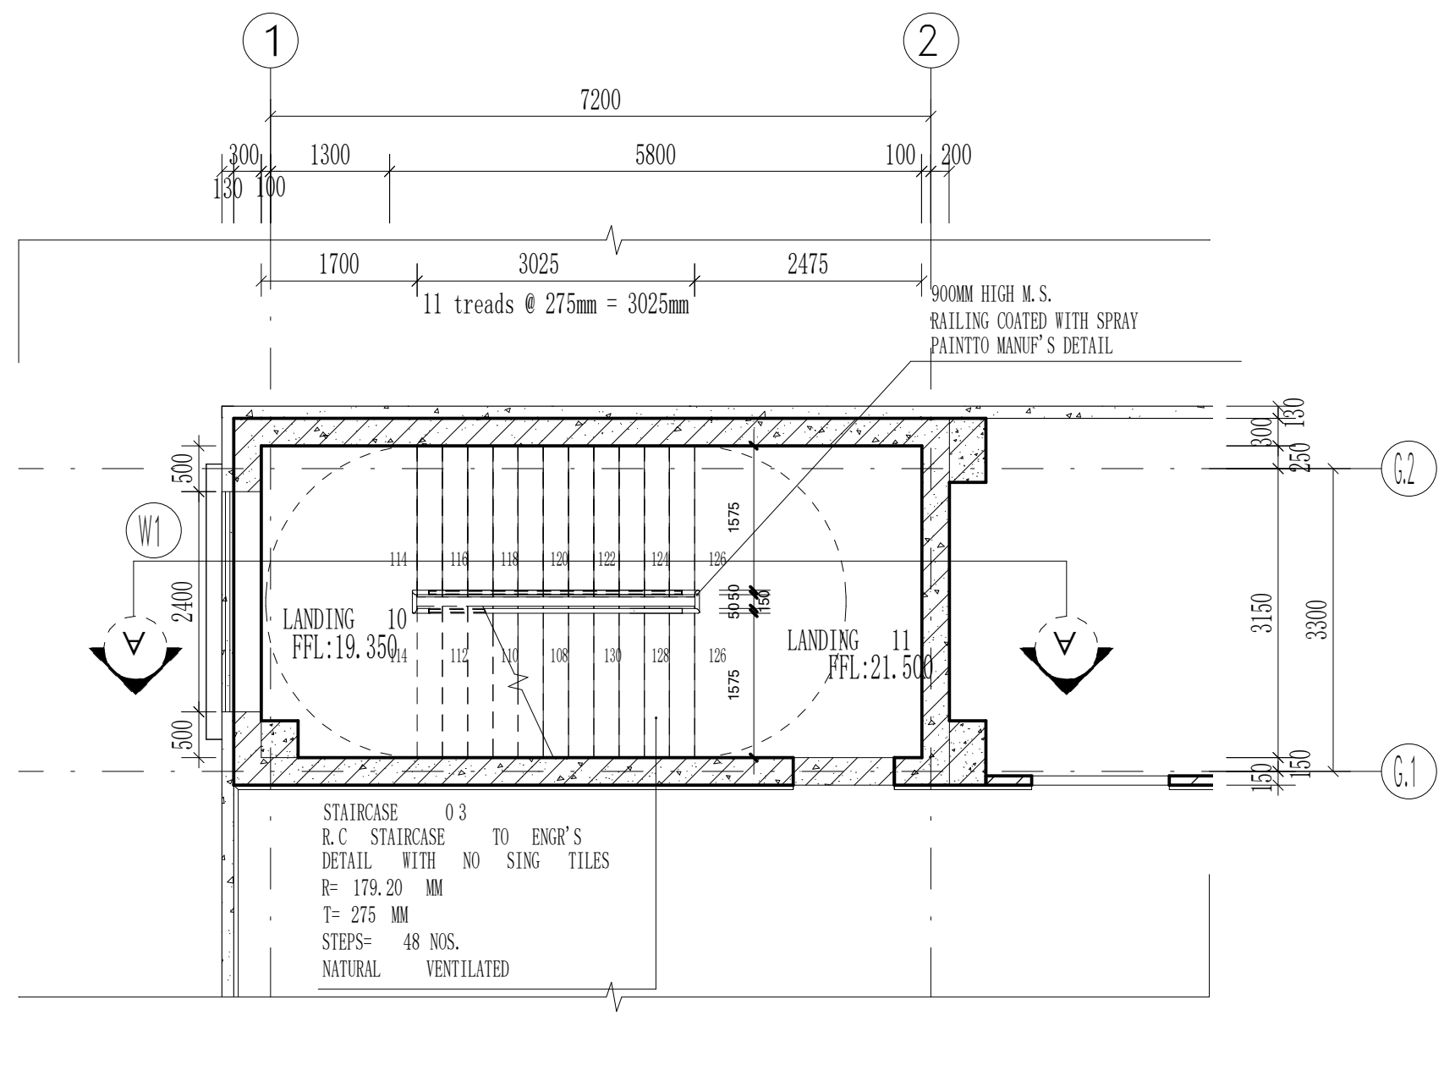
1
2
7200
1700
3025
2475
11 treads @ 275mm = 3025mm
900MM HIGH M.S. RAILING COATED WITH SPRAY PAINTTO MANUF'S DETAIL
LANDING 10
FFL:19.350
LANDING 11
FFL:21.500
STAIRCASE 03
R.C STAIRCASE TO ENGR'S DETAIL WITH NO SING TILES
R= 179.20 MM
T= 275 MM
STEPS= 48 NOS.
NATURAL VENTILATED

STAIR-3 21.500 ELEVATION PLAN FL

SCALE 1:75

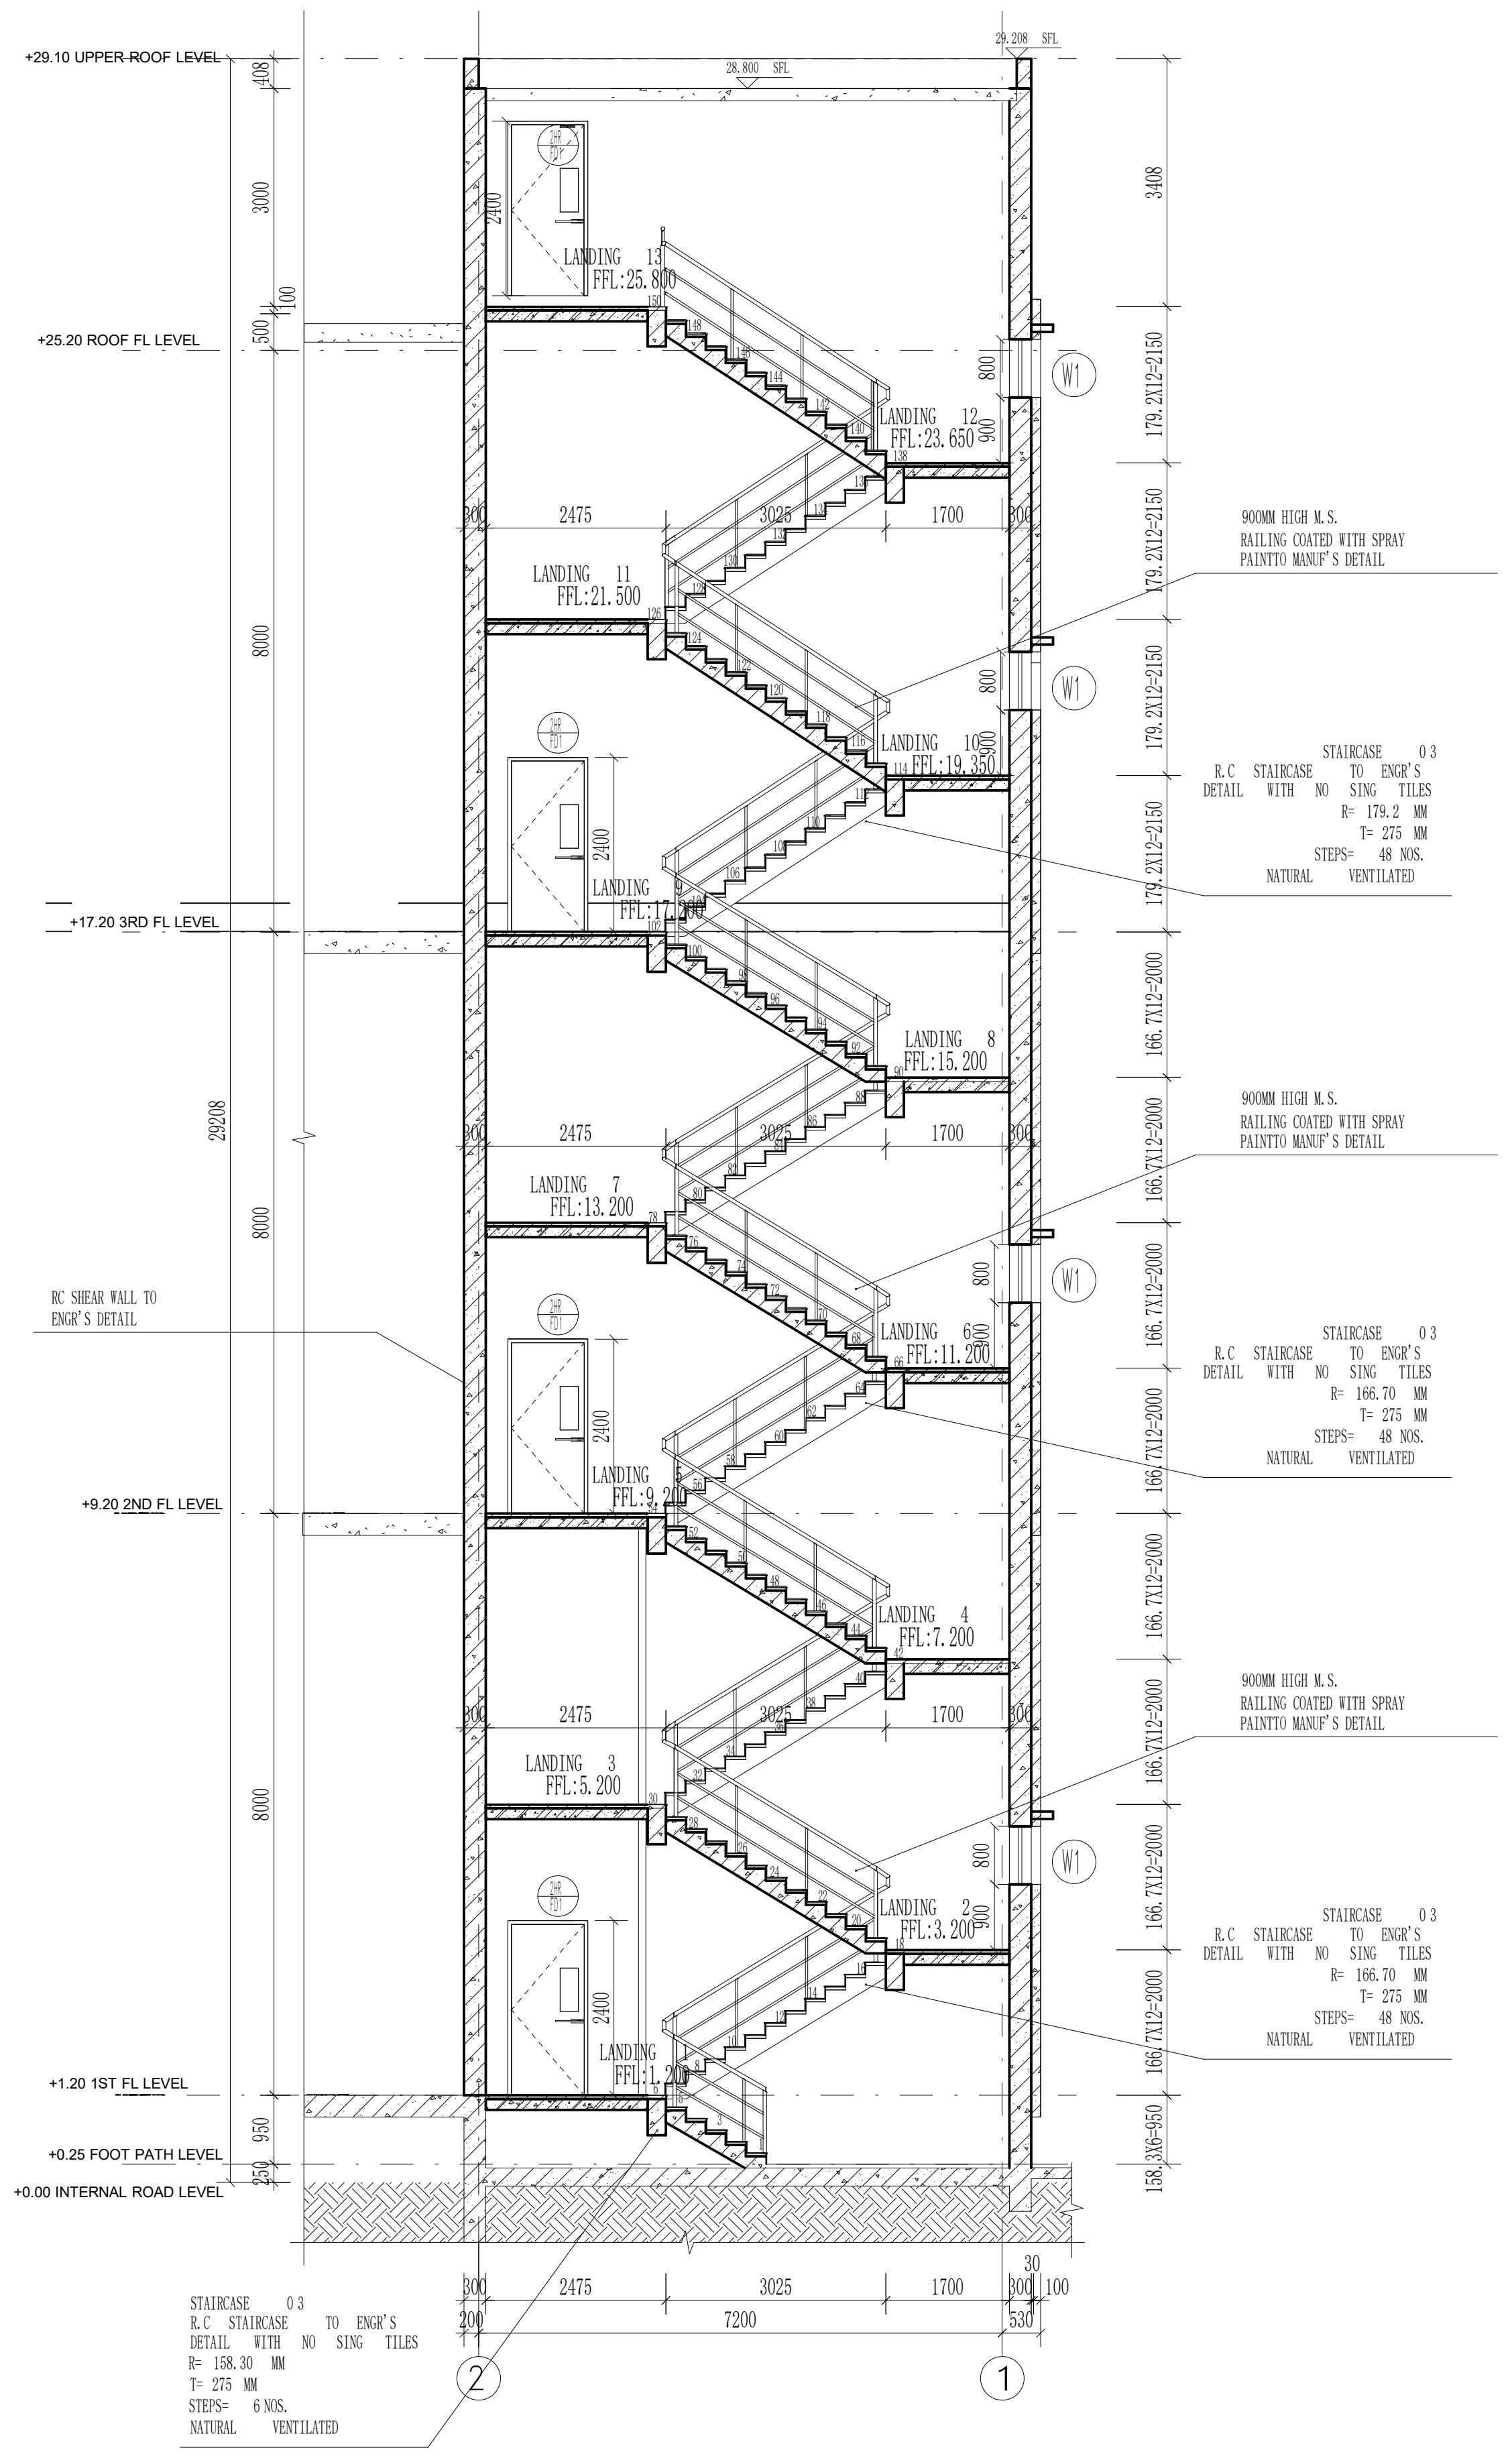
+29.10 UPPER ROOF LEVEL
+25.20 ROOF FL LEVEL
+17.20 3RD FL LEVEL
+9.20 2ND FL LEVEL
+1.20 1ST FL LEVEL
+0.25 FOOT PATH LEVEL
+0.00 INTERNAL ROAD LEVEL
29.208 SFL
28.800 SFL
29208
8000
3408
LANDING 13
FFL:25.800
LANDING 12
FFL:23.650
LANDING 11
FFL:21.500
LANDING 10
FFL:19.350
LANDING 9
FFL:17.200
LANDING 8
FFL:15.200
LANDING 7
FFL:13.200
LANDING 6
FFL:11.200
LANDING 5
FFL:9.200
LANDING 4
FFL:7.200
LANDING 3
FFL:5.200
LANDING 2
FFL:3.200
LANDING 1
FFL:1.200
179.2X12=2150
166.7X12=2000
158.3X6=950
W1
2HR FD1
900MM HIGH M.S. RAILING COATED WITH SPRAY PAINTTO MANUF'S DETAIL
RC SHEAR WALL TO ENGR'S DETAIL
STAIRCASE 03
R.C STAIRCASE TO ENGR'S DETAIL WITH NO SING TILES
R= 179.2 MM
T= 275 MM
STEPS= 48 NOS.
NATURAL VENTILATED
R= 166.70 MM
R= 158.30 MM
STEPS= 6 NOS.
300
2475
3025
1700
7200
530
2
1

Section A

SCALE 1:75

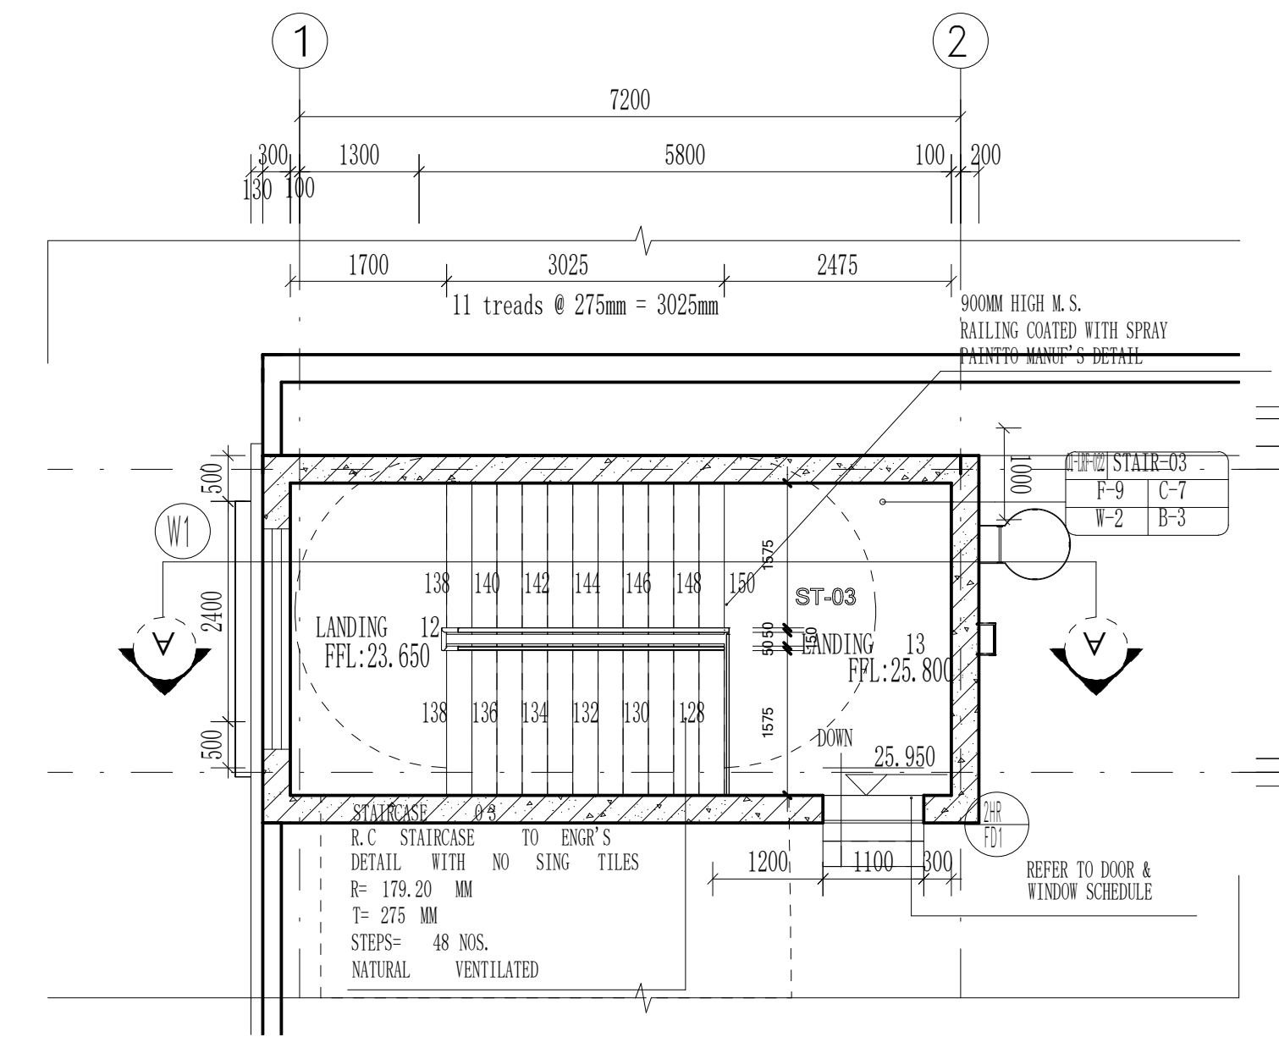
1
2
7200
1700
3025
2475
11 treads @ 275mm = 3025mm
900MM HIGH M.S. RAILING COATED WITH SPRAY PAINTTO MANUF'S DETAIL
STAIR-03
F-9
C-7
W-2
B-3
ST-03
LANDING 12
FFL:23.650
LANDING 13
FFL:25.800
25.950
STAIRCASE 03
R.C STAIRCASE TO ENGR'S DETAIL WITH NO SING TILES
R= 179.20 MM
T= 275 MM
STEPS= 48 NOS.
NATURAL VENTILATED
REFER TO DOOR & WINDOW SCHEDULE

STAIR-3 RF FL

SCALE 1:75

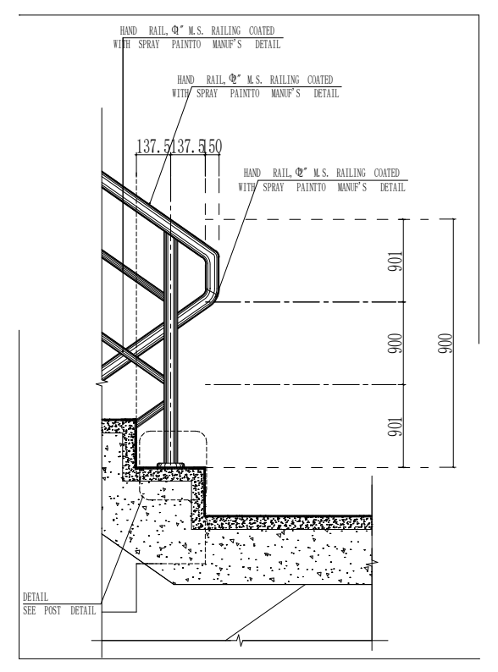
HAND RAIL, M.S. RAILING COATED WITH SPRAY PAINTTO MANUF'S DETAIL
137.5
50
901
900
DETAIL SEE POST DETAIL

HANDRAIL DETAILS

SCALE 1:75

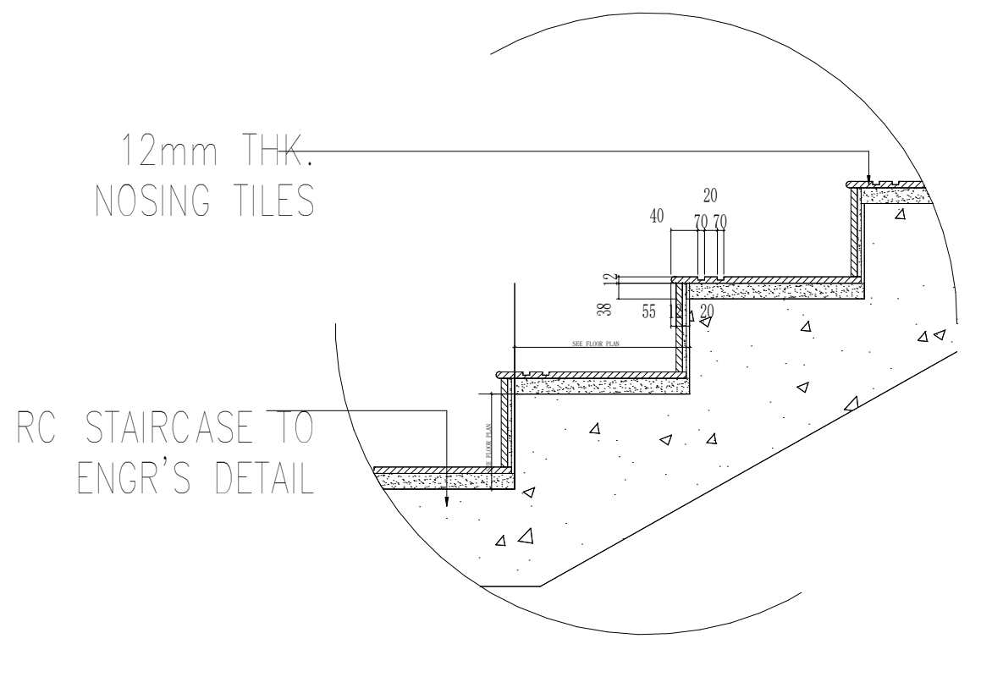
12mm THK. NOSING TILES
RC STAIRCASE TO ENGR'S DETAIL
20
40
70
70
12
38
55
SEE FLOOR PLAN

STEP DETAILS

SCALE 1:75

NOTE :THIS PRINT IS OF A CONFIDENTIAL NATURE, IT SHALL NOT BE TRACED,PHOTOGRAPHED,PHOTOSTATED OR REPRODUCED IN ANY MANER,NOR USED FOR ANY PURPOSE WHATSOEVER EXCEPT BY WRITTEN PERMISSION

CLIENT :

GULF EDGE DC 01

87 Wireless Road, M Thai Tower 11th. Floor, All Seasons Place, Lumpini,
Pathumwan, Bangkok 10330, Thailand

CONTRACTOR :

华西发展(泰国)有限公司
บริษัท หัวซือ ดีเวลลอปเม้นต์ (ประเทศไทย) จำกัด
HUASHI DEVELOPMENT CO.,LTD
No. 202, Room No. 1403, 14/F, Le Concorde Building,
Ratchadapisek Road, Huaykhwang Sub-District,
Huaykhwang District, Bangkok Metropolitan 10310.

CONSULTANT :

ARbay
บริษัท เอ อาร์ เบย์ จำกัด
ARbay Company Limited
31 st Floor Bangkok Insurance Building
25 South Sathorn road Thungmahamek
Sathorn Bangkok 10120 THAILAND
T +66 (0) 2286 8199
F +66 (0) 2286 2863
info@arbay.co.th

CONSULTANT :

Qbic Engineers & Architects Co.,Ltd.
8 Soi KALONG 4 SANAMBINNAM ROAD,
THASAI SUB-DISTRICT, MUANG NONTHABURI DISTRICT
, NONTHABURI.
Tel 662-950-4374
Fax 662-580-3231
E-Mail : qbic@qbic.co.th, www.qbic.co.th
QBIC ENGINEERS AND ARCHITECTS CO.,LTD.

CONSULTANT :

MITR
MITR TECHNICAL CONSULTANT CO.,LTD.
1168/8 12th FLOOR, LUMPINI TOWER BUILDING,
RAMA IV RD., THUNGMAHAMEK, SATHORN, BANGKOK 10120, THAILAND
TEL : 0-2679-9079-84
FAX : 0-2679-9085 E-mail: mitr_dd@mitr.com

Architect :	SIGNATURE
ประกิต พนานุรัตน์ วสถ. 580 ที่อยู่ 251/1 ถ.จารุเมือง แขวงรองเมือง เขตปทุมวัน กรุงเทพมหานคร โทรศัพท์ 02-286-8199	
Structural Engineer :	SIGNATURE
วิศวกรผู้ออกแบบโครงสร้าง	
ณัฐสม สงวนวงษ์ วย 1423 ที่อยู่ 2/1 ซ.รามคำแหง 150 ถ.รามคำแหง แขวง สะพานสูง เขต สะพานสูง กทม. 10240	ณัฐสม สงวนวงษ์
Structural Inspector :	SIGNATURE
วิศวกรผู้ตรวจสอบโครงสร้าง	
โกมล จุฑาภัทร วย 964 ที่อยู่ 24/18 ซ.นวมินทร์ 129 ถ. นวมินทร์ แขวง นวลจันทร์ เขต บึงกุ่ม กทม. 10230	
Electrical Engineer :	SIGNATURE
วิศวกรผู้ออกแบบระบบไฟฟ้ากำลัง	
นายสุภัทร บูรณวิทย์ วฟก.1265 ที่อยู่ 21 ซอยทานสัมฤทธิ์ 13 ตำบลท่าทราย อ.เมืองนนทบุรี จ.นนทบุรี 11000	สุภัทร
Mechanical Engineer :	SIGNATURE
วิศวกรผู้ออกแบบระบบเครื่องกลและปรับอากาศ	
นายประสิทธิ์ เกี้ยวสุนทร วก.1221 ที่อยู่ 44/372 ซอยบางกระดี่ 35/1 แขวงแสมดำ เขตบางขุนเทียน กทม. 10150	ประสิทธิ์
Sanitary Engineer :	SIGNATURE
วิศวกรผู้ออกแบบระบบสุขาภิบาล และดับเพลิง	
นายทศวรรษ สนั่นฤทธิ์ วส. 215 ที่อยู่ บ้านเลขที่ 99/107 หมู่ที่ 3 ต.ศีรษะจรเข้น้อย อ.บางเสาธง จ.สมุทรปราการ 10540	ทศวรรษ

ISSUE/REVISION

REV.	DESCRIPTION	DATE
A	90% DEVELOPED	09/05/2026

PROJECT NAME :

GEDC 01

LOCATION:
Nikhom Phattana district, Rayong ,industrial estate,CPGC

BUILDING :
MAIN BUILDING

90% DEVELOPED

TITLE :

STAIRCASE 03

JOB NO.		SCALE	1 : 75
DRAWN	WYSH	REF.	
CHECKED	LJC	DWG. NO.	MPK01A-90-A-ST-003
APPROVED	LXD		
DATE	2026.05.09		