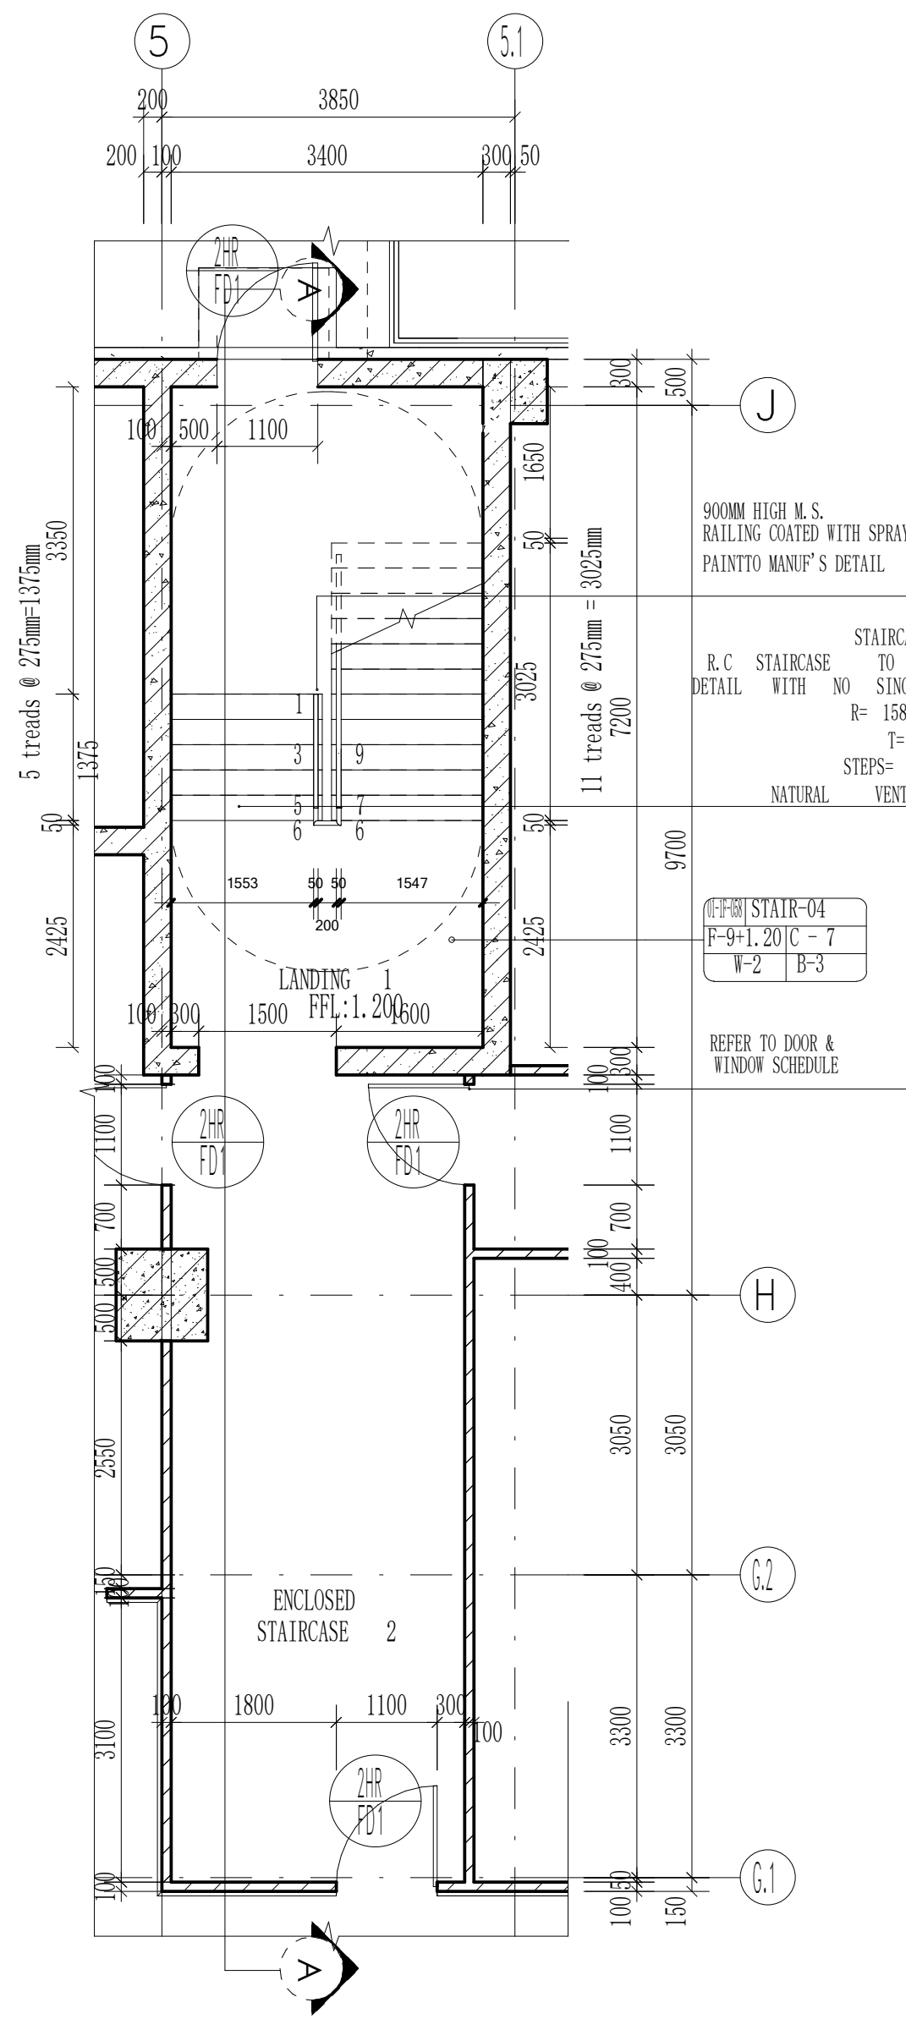
5
5.1
3850
3400
J
H
G.1
G.1
900MM HIGH M.S. RAILING COATED WITH SPRAY PAINTTO MANUF'S DETAIL
STAIRCASE 04 R.C STAIRCASE TO ENGR'S DETAIL WITH NO SING TILES R= 158.30 MM T= 275 MM STEPS= 6 NOS. NATURAL VENTILATED
5 treads @ 275mm=1375mm
11 treads @ 275mm = 3025mm
01-1F-058 STAIR-04 F-9+1.20 C - 7 W-2 B-3
LANDING 1 FFL:1.200
REFER TO DOOR & WINDOW SCHEDULE
2HR FD1
ENCLOSED STAIRCASE 2
A

STAIRCASE 04 GROUND FL
SCALE 1:75

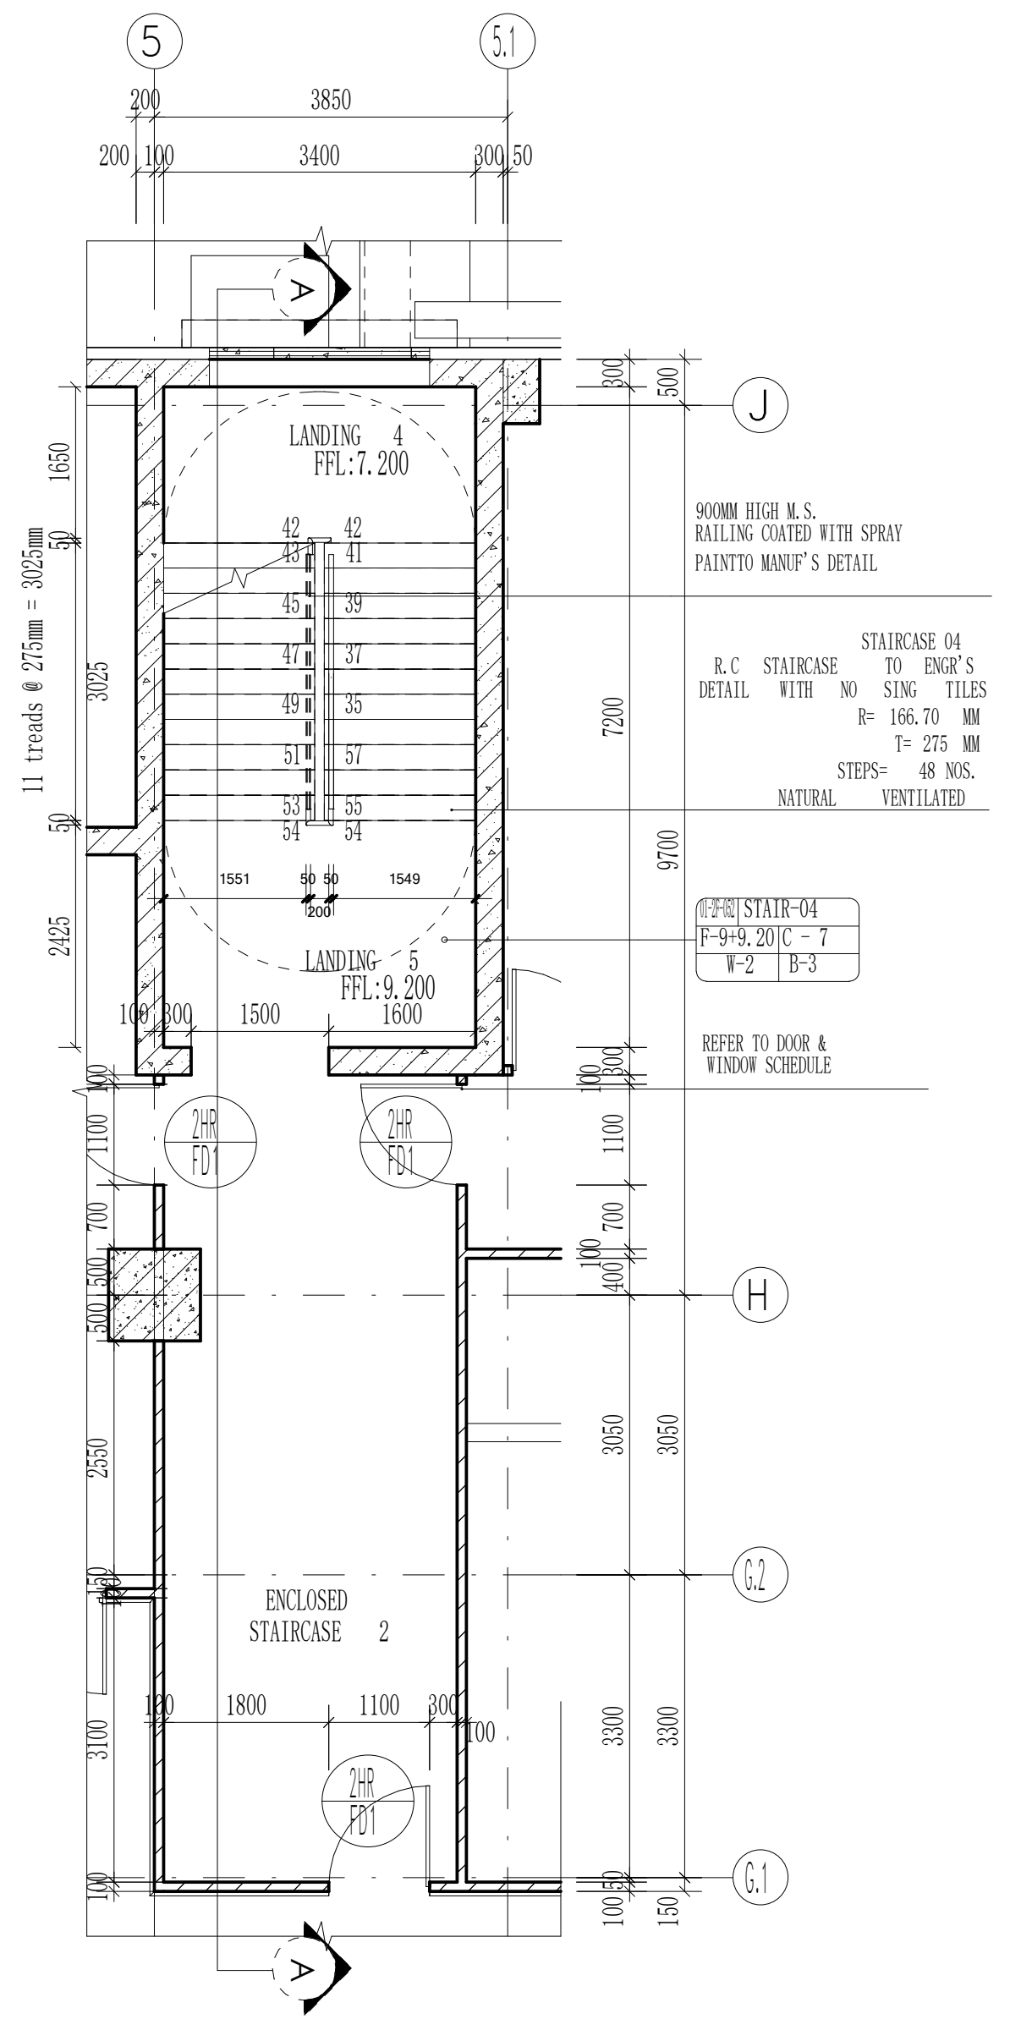
LANDING 4 FFL:7.200
LANDING 5 FFL:9.200
900MM HIGH M.S. RAILING COATED WITH SPRAY PAINTTO MANUF'S DETAIL
STAIRCASE 04 R.C STAIRCASE TO ENGR'S DETAIL WITH NO SING TILES R= 166.70 MM T= 275 MM STEPS= 48 NOS. NATURAL VENTILATED
REFER TO DOOR & WINDOW SCHEDULE
ENCLOSED STAIRCASE 2

STAIRCASE 04& 2ND FL
SCALE 1:75

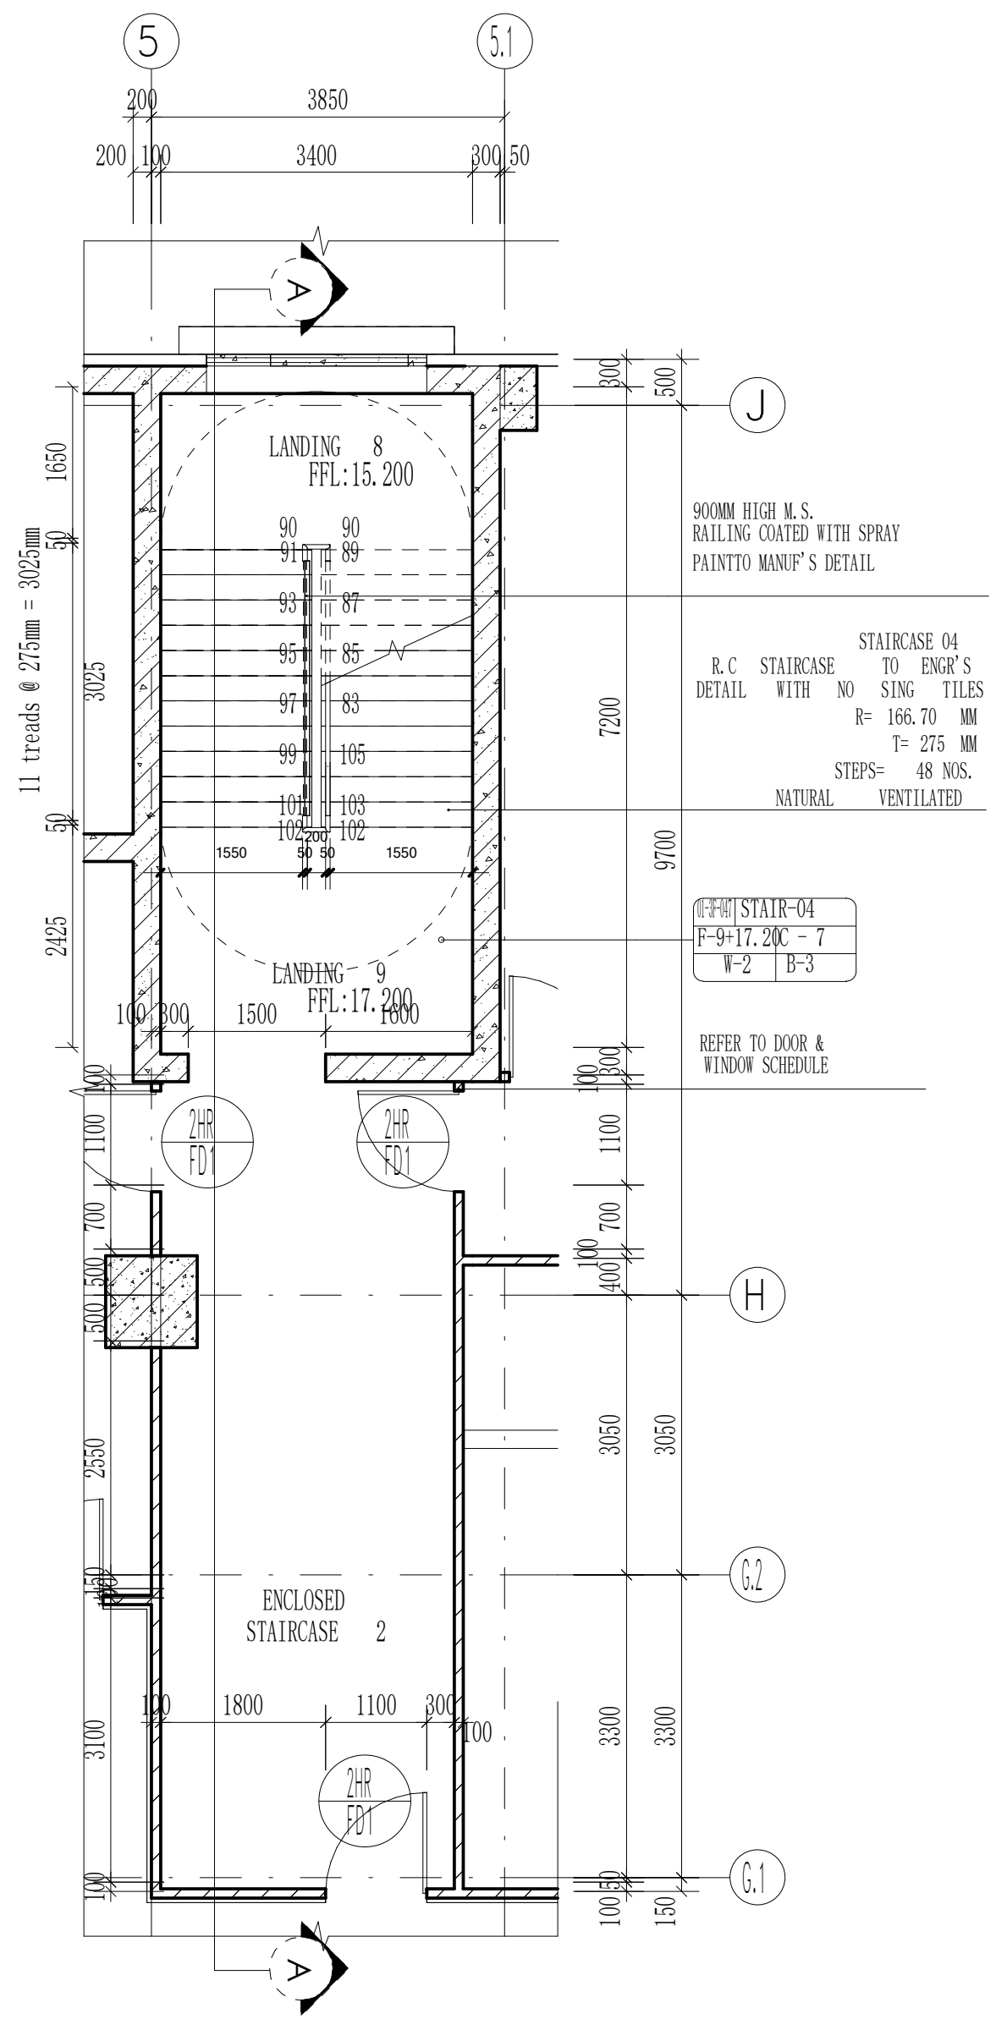
LANDING 8 FFL:15.200
LANDING 9 FFL:17.200
900MM HIGH M.S. RAILING COATED WITH SPRAY PAINTTO MANUF'S DETAIL
STAIRCASE 04 R.C STAIRCASE TO ENGR'S DETAIL WITH NO SING TILES R= 179.17 MM T= 275 MM STEPS= 48 NOS. NATURAL VENTILATED
REFER TO DOOR & WINDOW SCHEDULE
ENCLOSED STAIRCASE 2

STAIRCASE 04& 3RD FL
SCALE 1:75

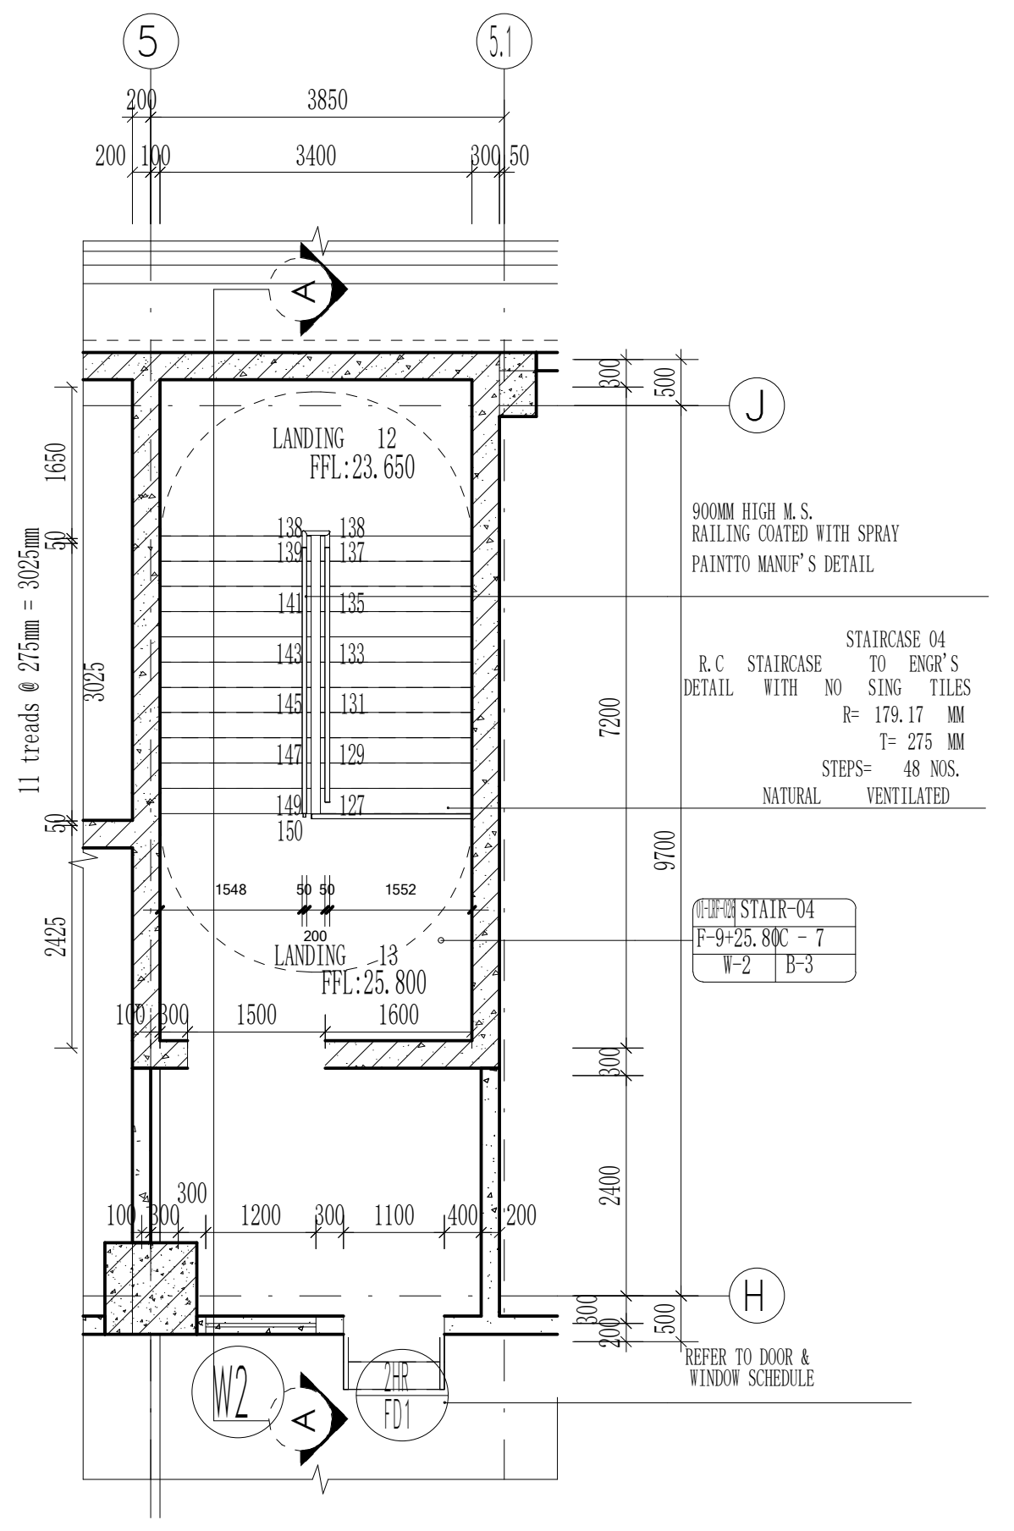
LANDING 12 FFL:23.650
LANDING 13 FFL:25.800
900MM HIGH M.S. RAILING COATED WITH SPRAY PAINTTO MANUF'S DETAIL
STAIRCASE 04 R.C STAIRCASE TO ENGR'S DETAIL WITH NO SING TILES R= 179.17 MM T= 275 MM STEPS= 48 NOS. NATURAL VENTILATED
REFER TO DOOR & WINDOW SCHEDULE
W2

STAIRCASE 04 ROOF FL
SCALE 1:75

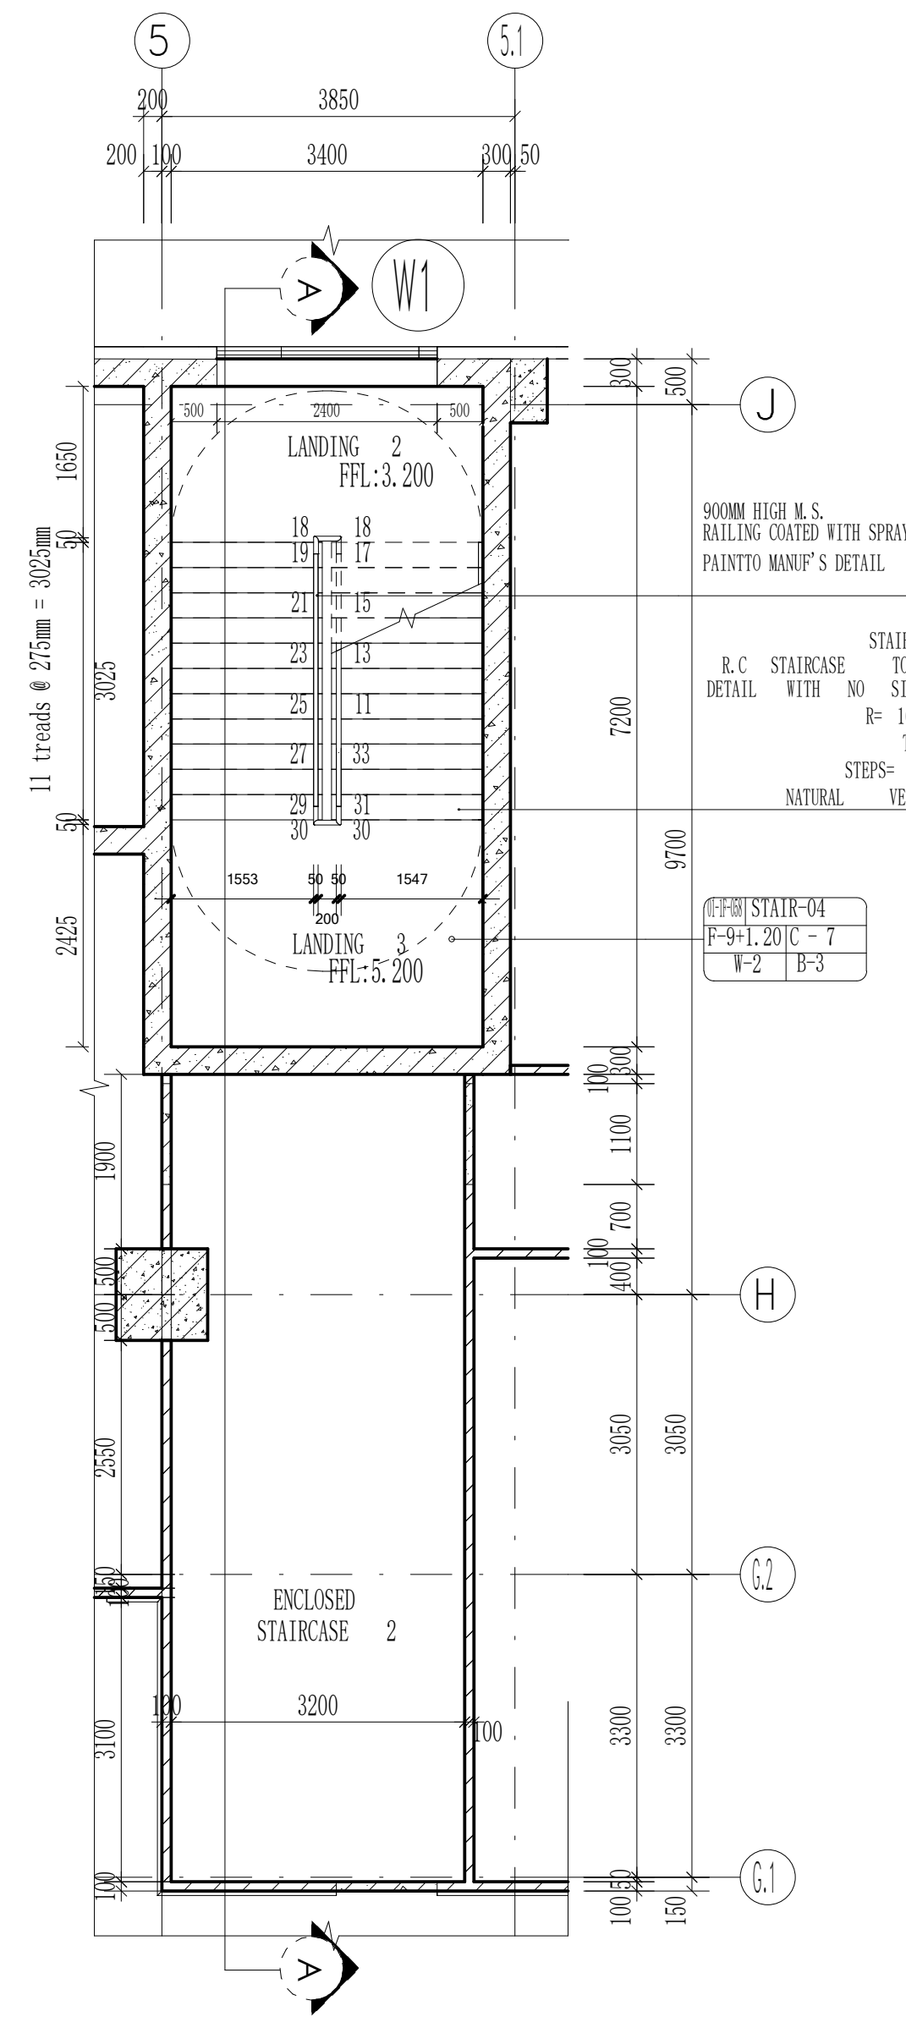
W1
LANDING 2 FFL:3.200
LANDING 3 FFL:5.200
900MM HIGH M.S. RAILING COATED WITH SPRAY PAINTTO MANUF'S DETAIL
STAIRCASE 04 R.C STAIRCASE TO ENGR'S DETAIL WITH NO SING TILES R= 166.70 MM T= 275 MM STEPS= 48 NOS. NATURAL VENTILATED
ENCLOSED STAIRCASE 2

STAIRCASE 04 5.200 ELEVATION PLAN FL
SCALE 1:75

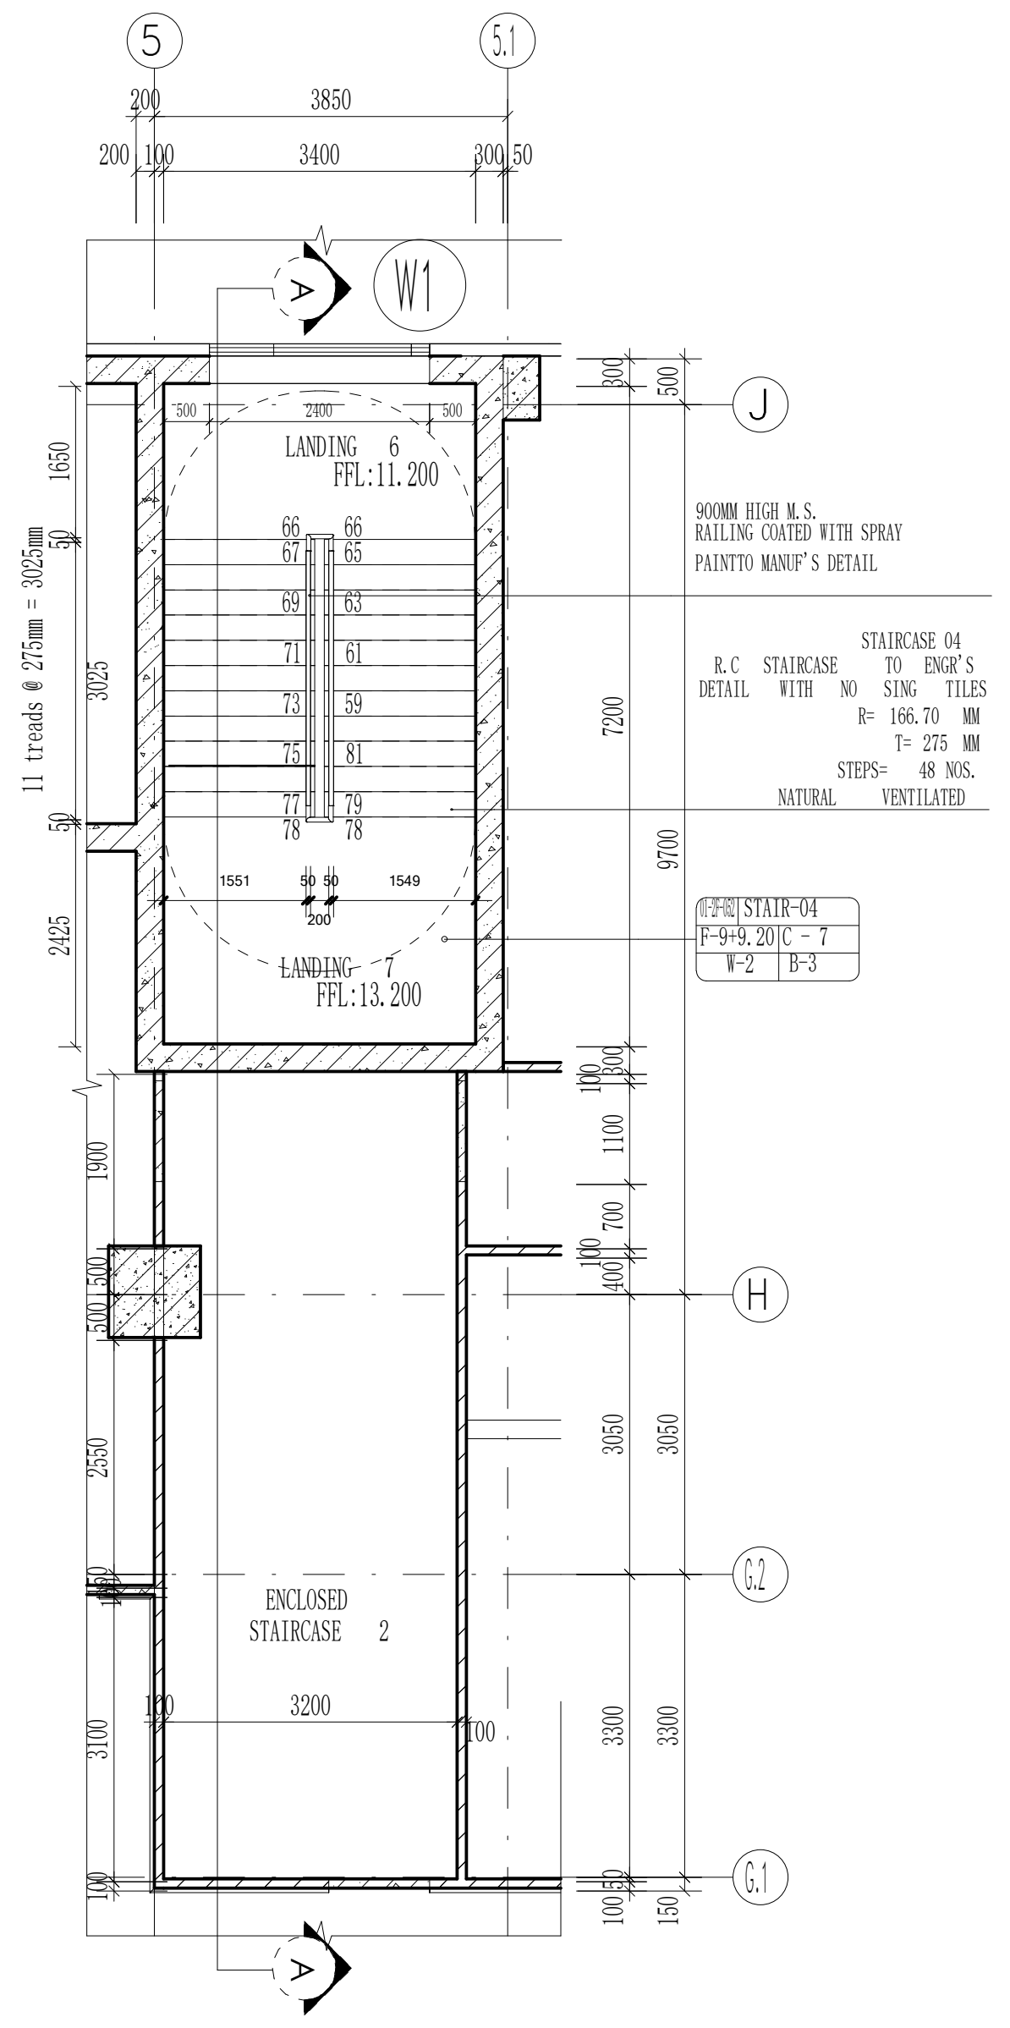
W1
LANDING 6 FFL:11.200
LANDING 7 FFL:13.200
900MM HIGH M.S. RAILING COATED WITH SPRAY PAINTTO MANUF'S DETAIL
STAIRCASE 04 R.C STAIRCASE TO ENGR'S DETAIL WITH NO SING TILES R= 166.70 MM T= 275 MM STEPS= 48 NOS. NATURAL VENTILATED
ENCLOSED STAIRCASE 2

STAIRCASE 04 13.200 ELEVATION PLAN FL
SCALE 1:75

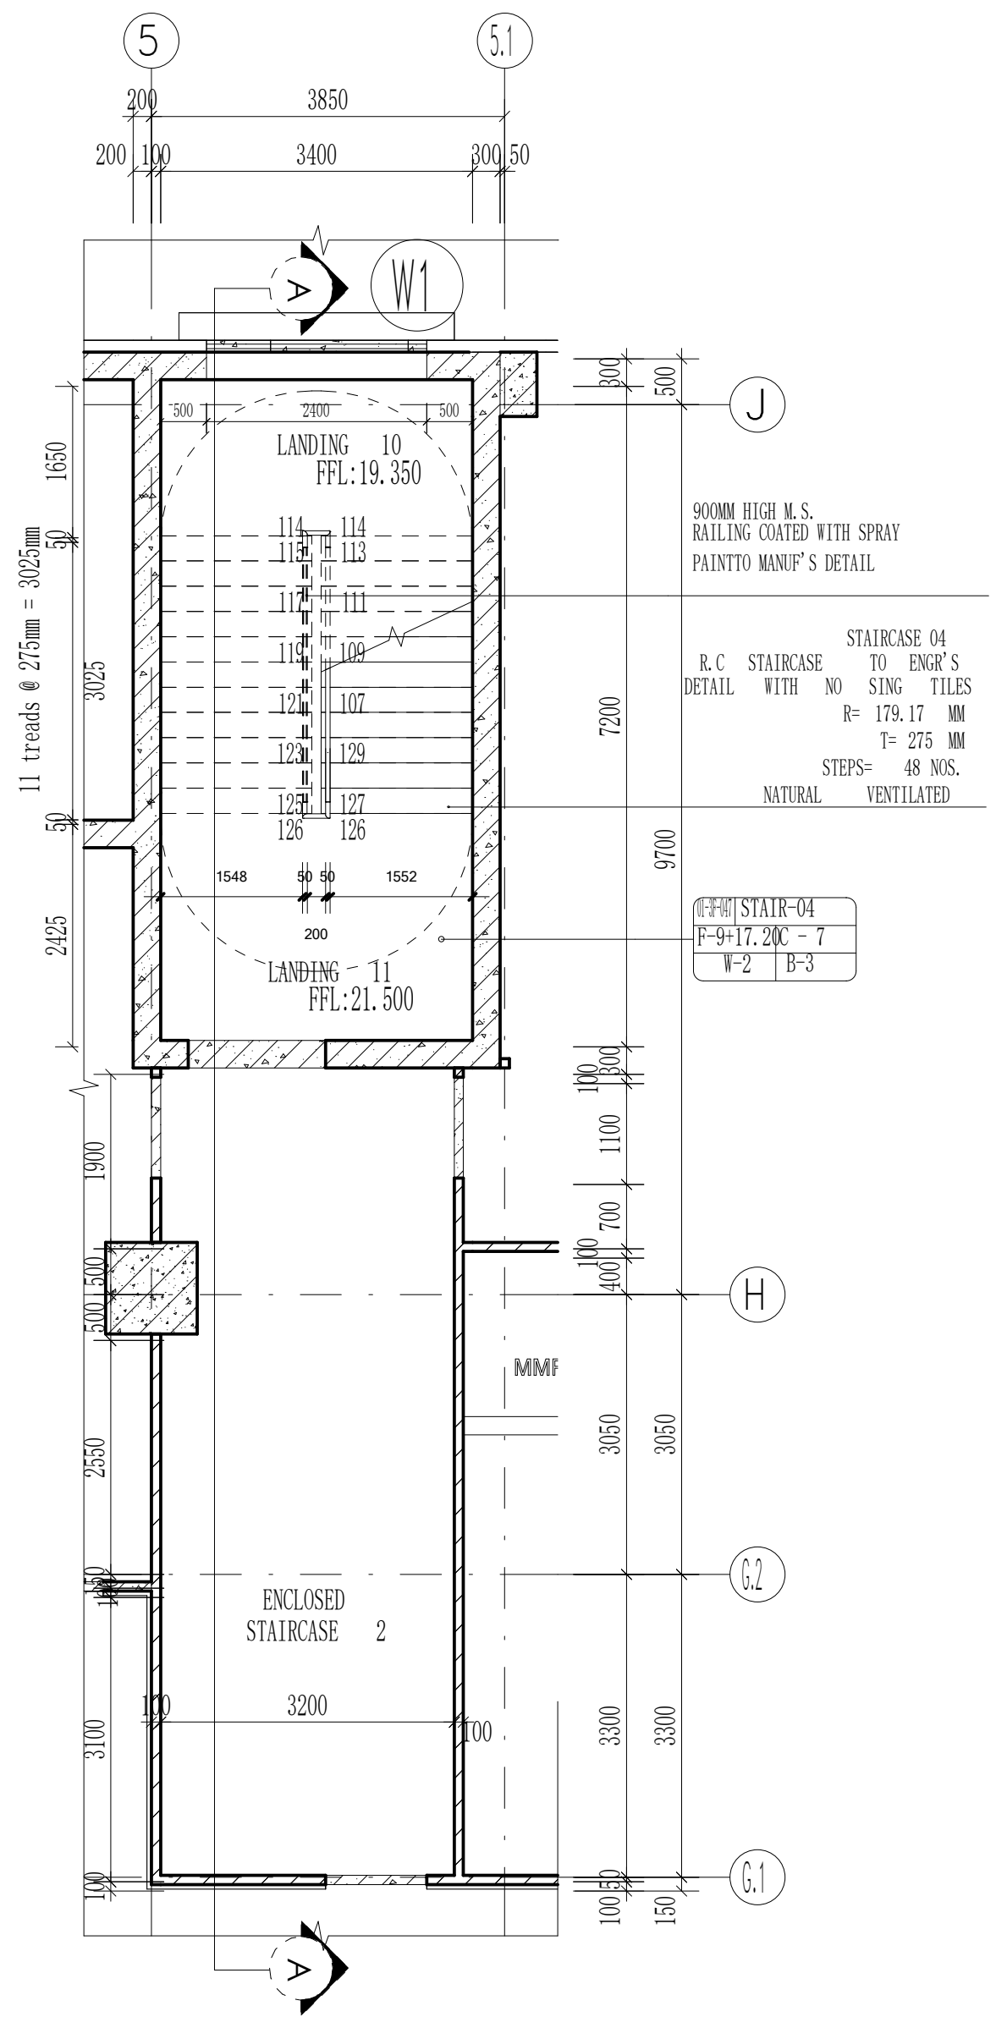
W1
LANDING 10 FFL:19.350
LANDING 11 FFL:21.500
900MM HIGH M.S. RAILING COATED WITH SPRAY PAINTTO MANUF'S DETAIL
STAIRCASE 04 R.C STAIRCASE TO ENGR'S DETAIL WITH NO SING TILES R= 179.17 MM T= 275 MM STEPS= 48 NOS. NATURAL VENTILATED
ENCLOSED STAIRCASE 2

STAIRCASE 04 21.500 ELEVATION PLAN FL
SCALE 1:75

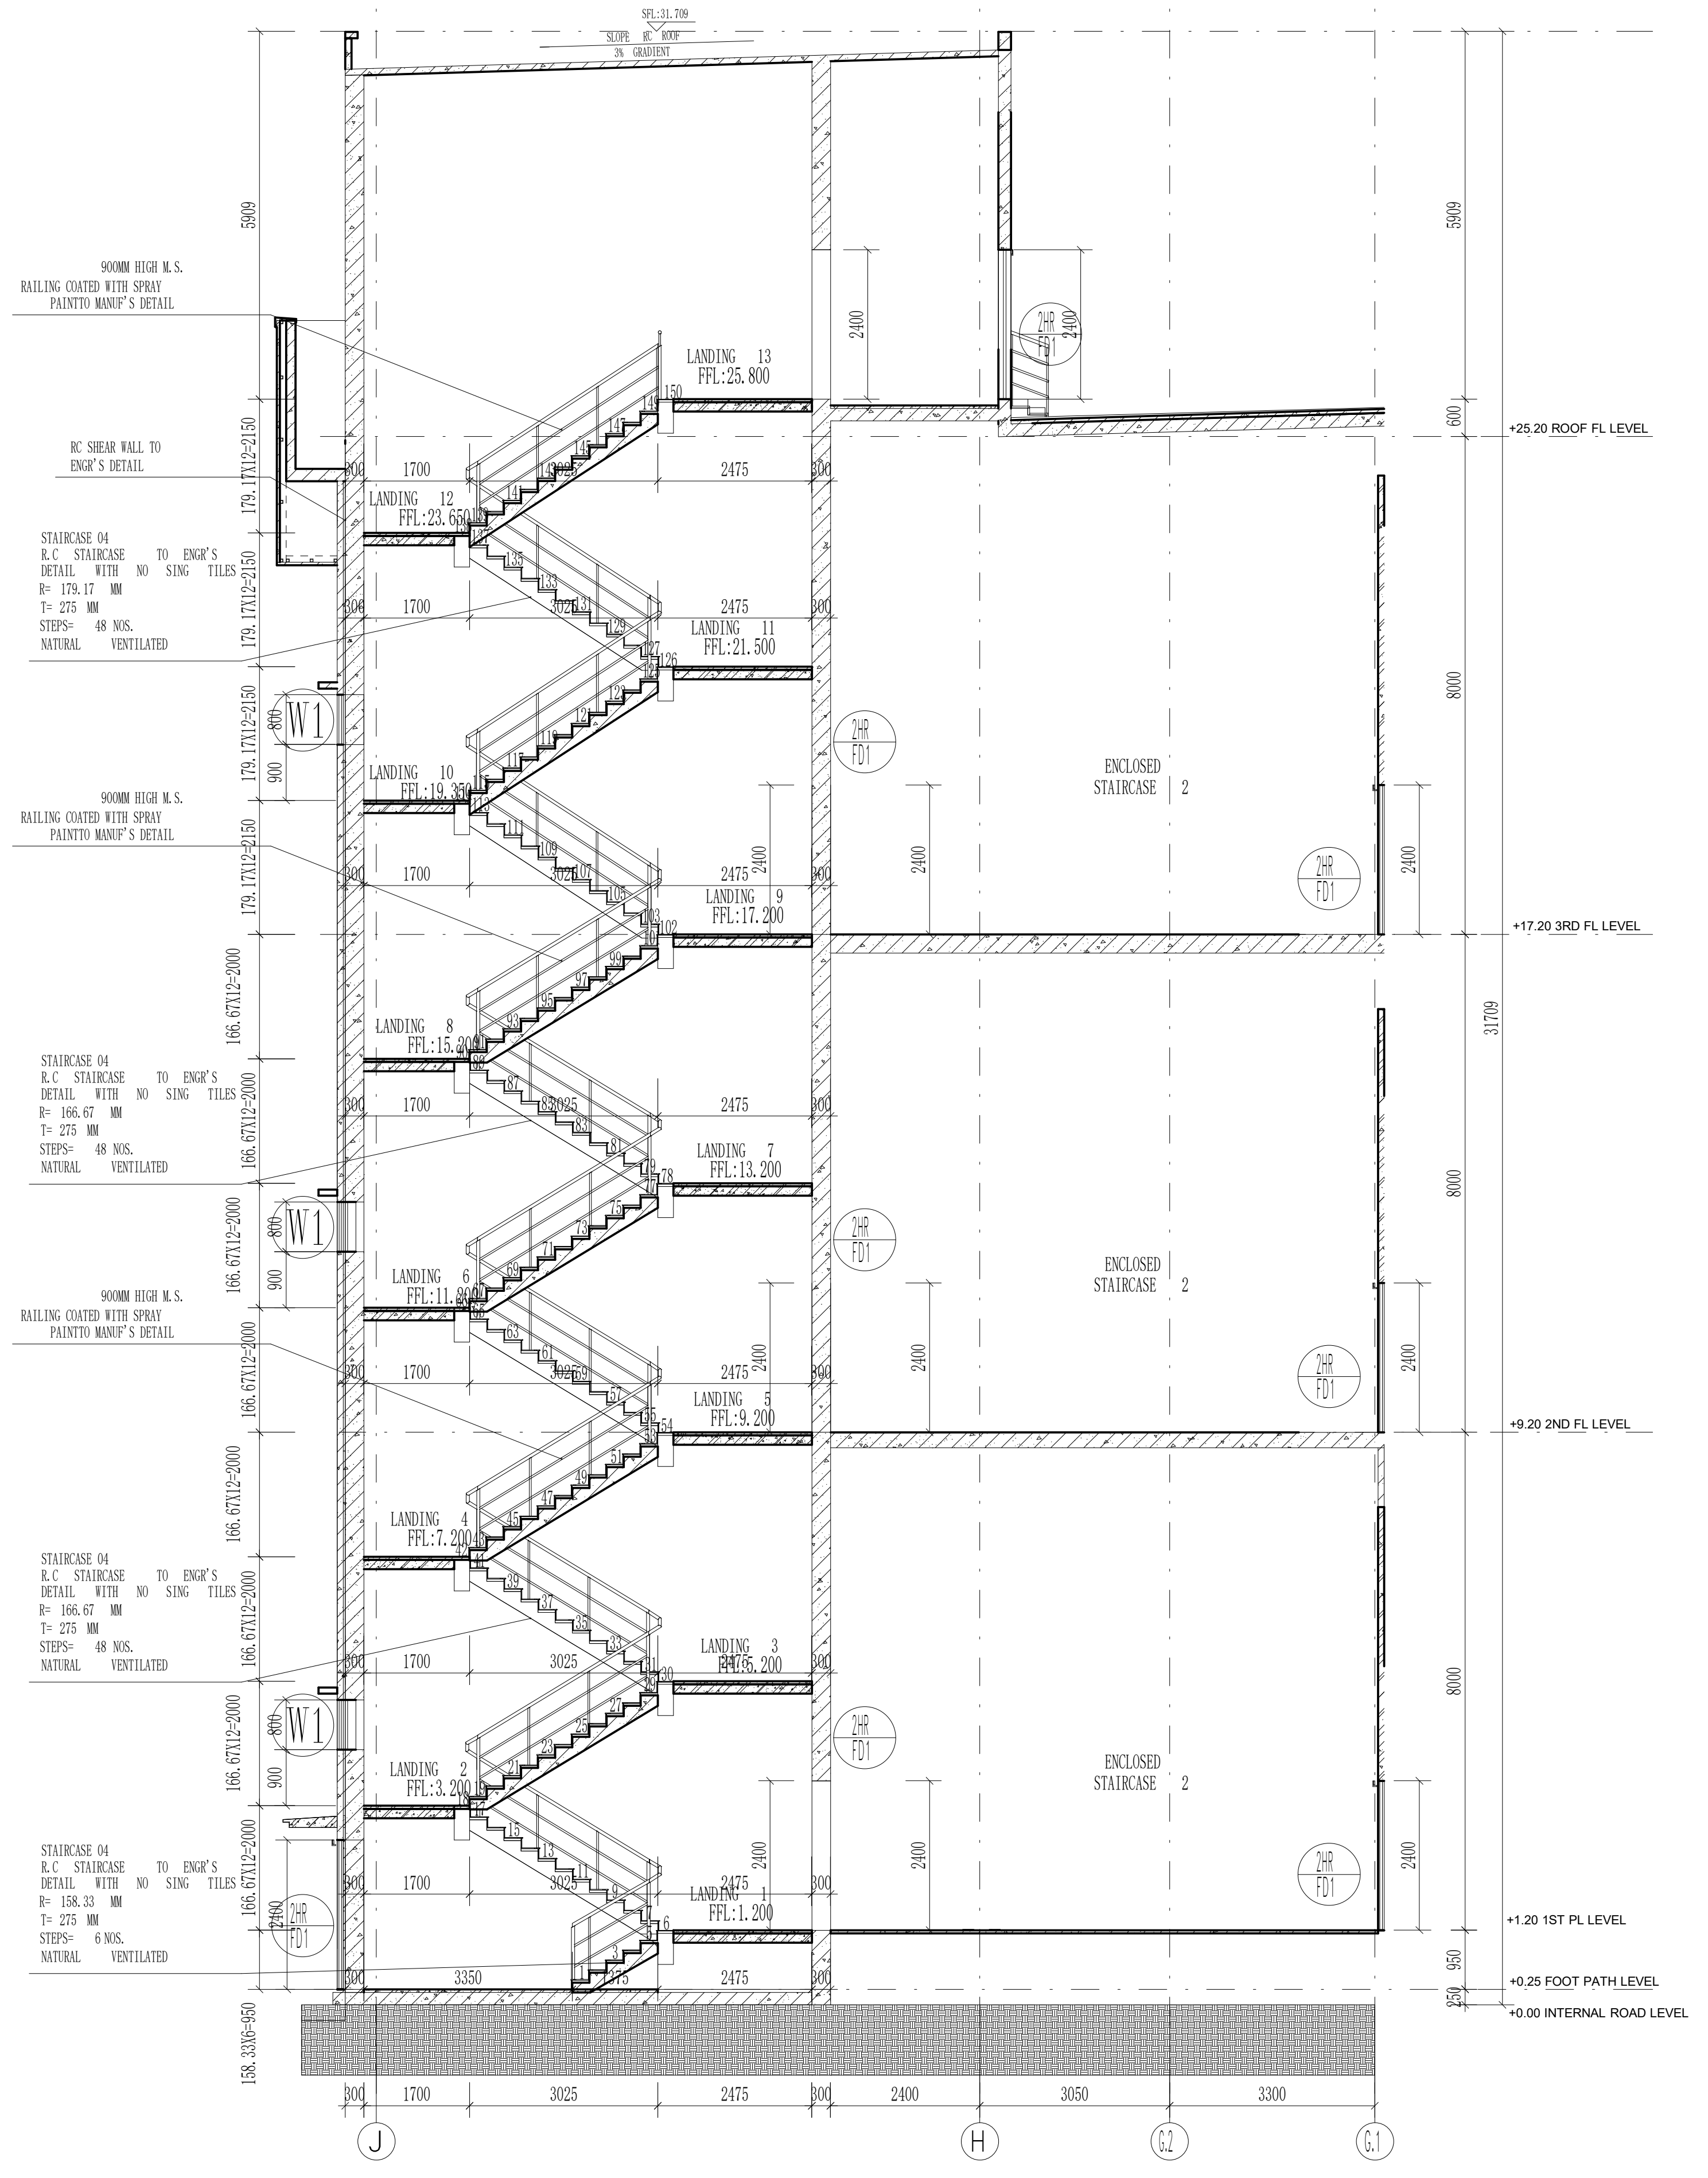
SFL:31.709
SLOPE RC ROOF 3% GRADIENT
900MM HIGH M.S. RAILING COATED WITH SPRAY PAINTTO MANUF'S DETAIL
RC SHEAR WALL TO ENGR'S DETAIL
STAIRCASE 04 R.C STAIRCASE TO ENGR'S DETAIL WITH NO SING TILES R= 179.17 MM T= 275 MM STEPS= 48 NOS. NATURAL VENTILATED
STAIRCASE 04 R.C STAIRCASE TO ENGR'S DETAIL WITH NO SING TILES R= 166.67 MM T= 275 MM STEPS= 48 NOS. NATURAL VENTILATED
STAIRCASE 04 R.C STAIRCASE TO ENGR'S DETAIL WITH NO SING TILES R= 158.33 MM T= 275 MM STEPS= 6 NOS. NATURAL VENTILATED
LANDING 13 FFL:25.800
LANDING 12 FFL:23.650
LANDING 11 FFL:21.500
LANDING 10 FFL:19.350
LANDING 9 FFL:17.200
LANDING 8 FFL:15.200
LANDING 7 FFL:13.200
LANDING 6 FFL:11.200
LANDING 5 FFL:9.200
LANDING 4 FFL:7.200
LANDING 3 FFL:5.200
LANDING 2 FFL:3.200
LANDING 1 FFL:1.200
ENCLOSED STAIRCASE 2
W1
2HR FD1
+25.20 ROOF FL LEVEL
+17.20 3RD FL LEVEL
+9.20 2ND FL LEVEL
+1.20 1ST FL LEVEL
+0.25 FOOT PATH LEVEL
+0.00 INTERNAL ROAD LEVEL
J
H
G.1
G.1

Section A
SCALE 1:75

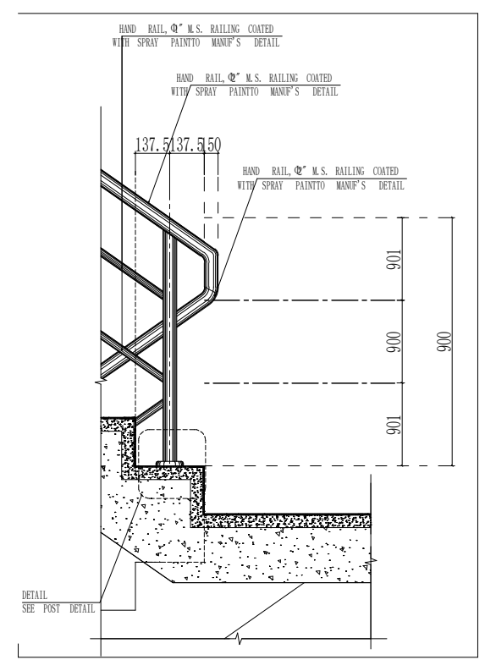

HANDRAIL DETAILS
SCALE 1:75

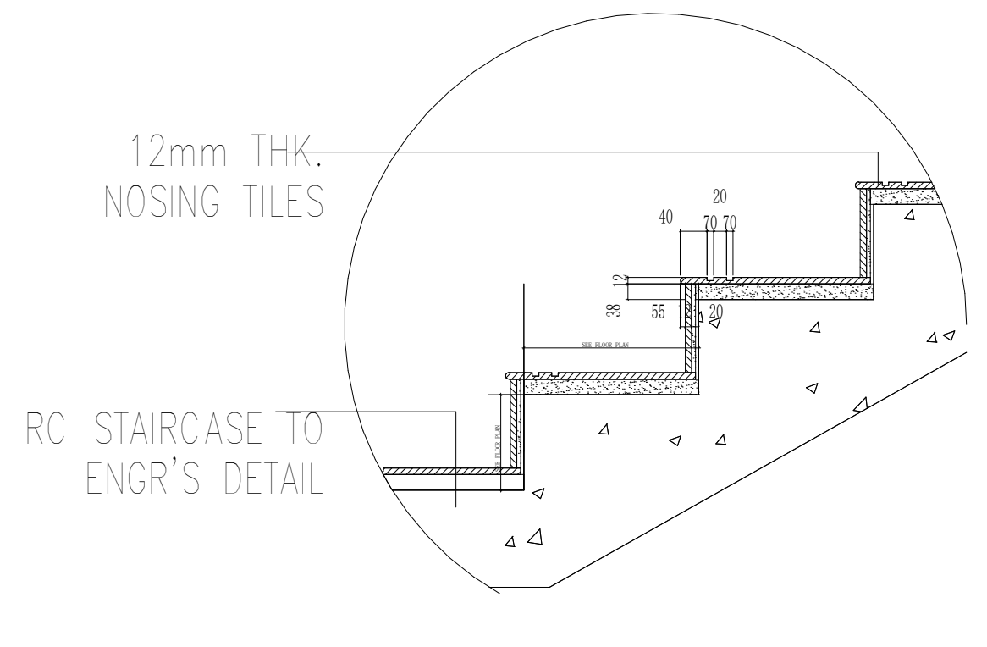
12mm THK. NOSING TILES
RC STAIRCASE TO ENGR'S DETAIL

STEP DETAILS
SCALE 1:75

NOTE :THIS PRINT IS OF A CONFIDENTIAL NATURE, IT SHALL NOT BE TRACED,PHOTOGRAPHED,PHOTOSTATED OR REPRODUCED IN ANY MANER,NOR USED FOR ANY PURPOSE WHATSOEVER EXCEPT BY WRITTEN PERMISSION

CLIENT :
GULF EDGE DC 01
87 Wireless Road, M Thai Tower 11th. Floor, All Seasons Place, Lumpini, Pathumwan, Bangkok 10330, Thailand

CONTRACTOR :
华西发展(泰国)有限公司
บริษัท หัวซือ ดีเวลลอปเม้นต์ (ประเทศไทย) จำกัด
HUASHI DEVELOPMENT CO.,LTD
No. 202, Room No. 1403, 14/F, Le Concorde Building,
Ratchadapisek Road, Huaykhwang Sub-District,
Huaykhwang District, Bangkok Metropolitan 10310.

CONSULTANT :
ARbay
บริษัท เอ อาร์ เบย์ จำกัด
ARbay Company Limited
31 st Floor Bangkok Insurance Building
25 South Sathorn road Thungmahamek
Sathorn Bangkok 10120 THAILAND
T +66 (0) 2286 8199
F +66 (0) 2286 2863
info@arbay.co.th

CONSULTANT :
Qbic Engineers & Architects Co.,Ltd.
8 Soi KALONG 4 SANAMBINNAM ROAD,
THASAI SUB-DISTRICT, MUANG NONTHABURI DISTRICT
, NONTHABURI.
Tel 662-950-4374
Fax 662-580-3231
E-Mail : qbic@qbic.co.th, www.qbic.co.th
QBIC ENGINEERS AND ARCHITECTS CO.,LTD.

CONSULTANT :
MITR
MITR TECHNICAL CONSULTANT CO.,LTD.
1168/8 12th FLOOR, LUMPINI TOWER BUILDING,
RAMA IV RD., THUNGMAHAMEK, SATHORN, BANGKOK 10120, THAILAND
TEL : 0-2679-9079-84
FAX : 0-2679-9085 E-mail: mitr_dd@mitr.com

Architect : SIGNATURE
ประกิต พนานุรัตน์ วสถ. 580
ที่อยู่
251/1 ถ.จารุเมือง แขวงรองเมือง เขตปทุมวัน
กรุงเทพมหานคร โทรศัพท์ 02-286-8199

Structural Engineer : SIGNATURE
วิศวกรผู้ออกแบบโครงสร้าง
ณัฐสม สงวนวงษ์ วย 1423
ที่อยู่
2/1 ซ.รามคำแหง 150 ถ.รามคำแหง
แขวง สะพานสูง เขต สะพานสูง กทม. 10240

Structural Inspector : SIGNATURE
วิศวกรผู้ตรวจสอบโครงสร้าง
โกมล จุฑาภัทร วย 964
ที่อยู่
24/18 ซ.นวมินทร์ 129 ถ. นวมินทร์
แขวง นวลจันทร์ เขต บึงกุ่ม กทม. 10230

Electrical Engineer : SIGNATURE
วิศวกรผู้ออกแบบระบบไฟฟ้ากำลัง
นายสุภัทร บูรณวิทย์ วฟก.1265
ที่อยู่
21 ซอยทานสัมฤทธิ์ 13
ตำบลท่าทราย อ.เมืองนนทบุรี จ.นนทบุรี 11000

Mechanical Engineer : SIGNATURE
วิศวกรผู้ออกแบบระบบเครื่องกลและปรับอากาศ
นายประสิทธิ์ เกี้ยวสุนทร วก.1221
ที่อยู่
44/372 ซอยบางกระดี่ 35/1 แขวงแสมดำ
เขตบางขุนเทียน กทม. 10150
ประสิทธิ์

Sanitary Engineer : SIGNATURE
วิศวกรผู้ออกแบบระบบสุขาภิบาล และดับเพลิง
นายทศวรรษ สนั่นฤทธิ์ วส. 215
ที่อยู่
บ้านเลขที่ 99/107 หมู่ที่ 3 ต.ศีรษะจรเข้น้อย
อ.บางเสาธง จ.สมุทรปราการ 10540
ทศวรรษ

ISSUE/REVISION

REV.	DESCRIPTION	DATE
A	90% DEVELOPED	09/05/2026

PROJECT NAME :
GEDC 01
LOCATION:
Nikhom Phattana district, Rayong ,industrial estate,CPGC

BUILDING :
MAIN BUILDING

90% DEVELOPED

TITLE :
STAIRCASE 04

JOB NO.	SCALE 1 : 75
DRAWN LW	REF.
CHECKED LJC	DWG. NO. MPK01A-90-A-ST-004
APPROVED LXD	
DATE 2026.05.09	