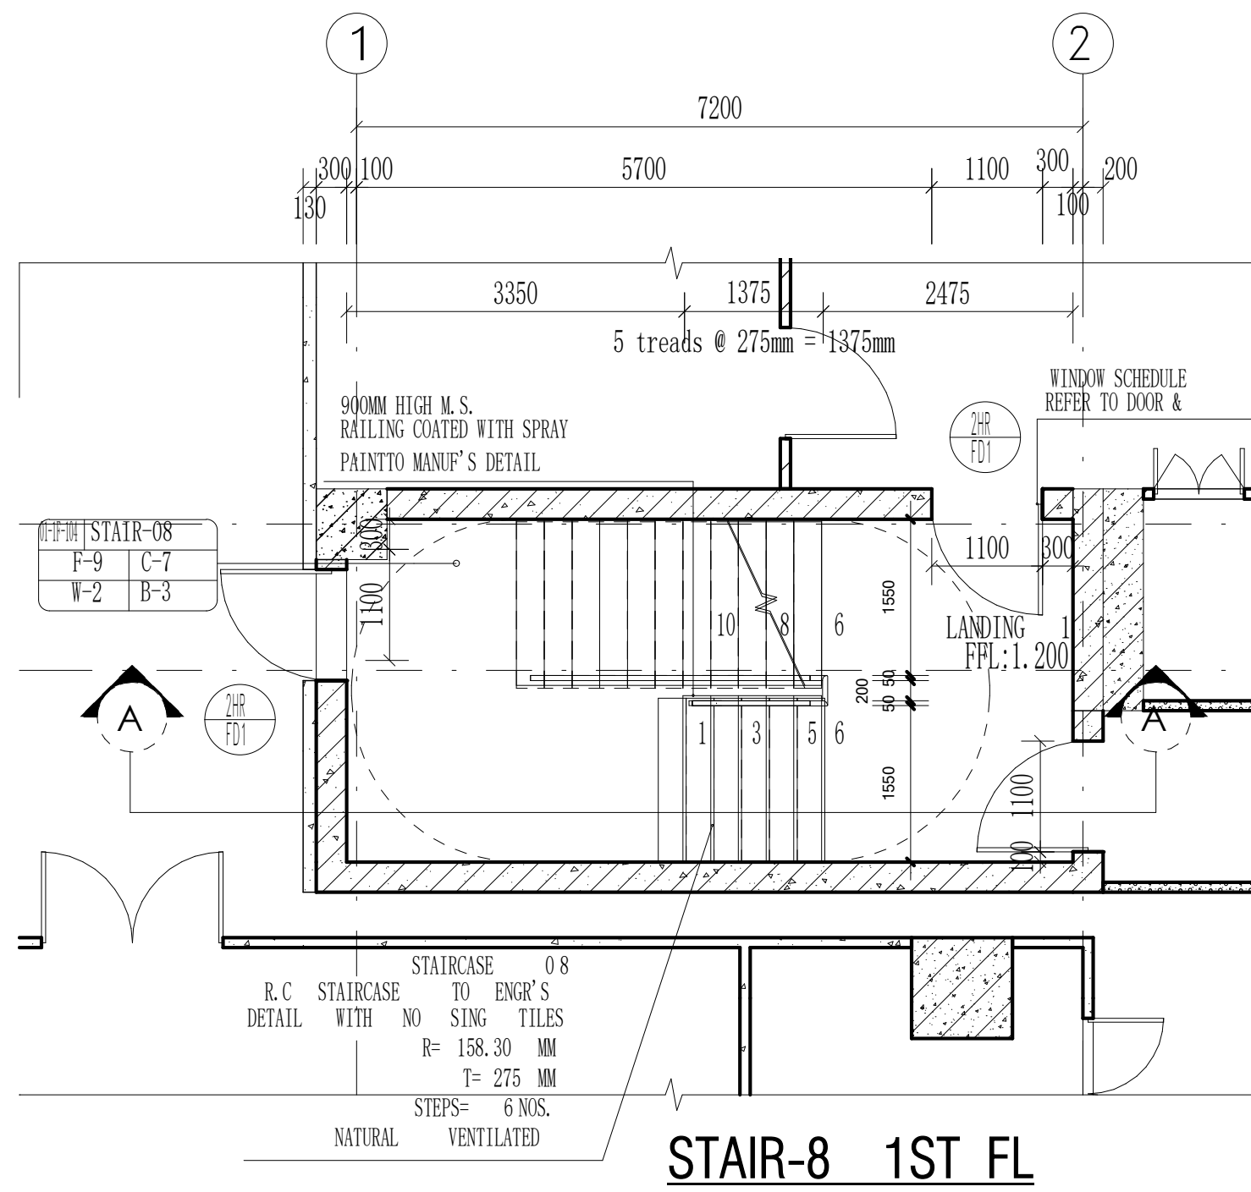
1
2
7200
300 100 5700 1100 300 200
130 100
3350 1375 2475
5 treads @ 275mm = 1375mm
900MM HIGH M.S.
RAILING COATED WITH SPRAY
PAINTTO MANUF'S DETAIL
WINDOW SCHEDULE
REFER TO DOOR &
STAIR-08
F-9 C-7
W-2 B-3
2HR FD1
LANDING 1
FFL:1.200
A.1
A
STAIRCASE 08
R.C STAIRCASE TO ENGR'S
DETAIL WITH NO SING TILES
R= 158.30 MM
T= 275 MM
STEPS= 6 NOS.
NATURAL VENTILATED

STAIR-8 1ST FL

SCALE 1:75

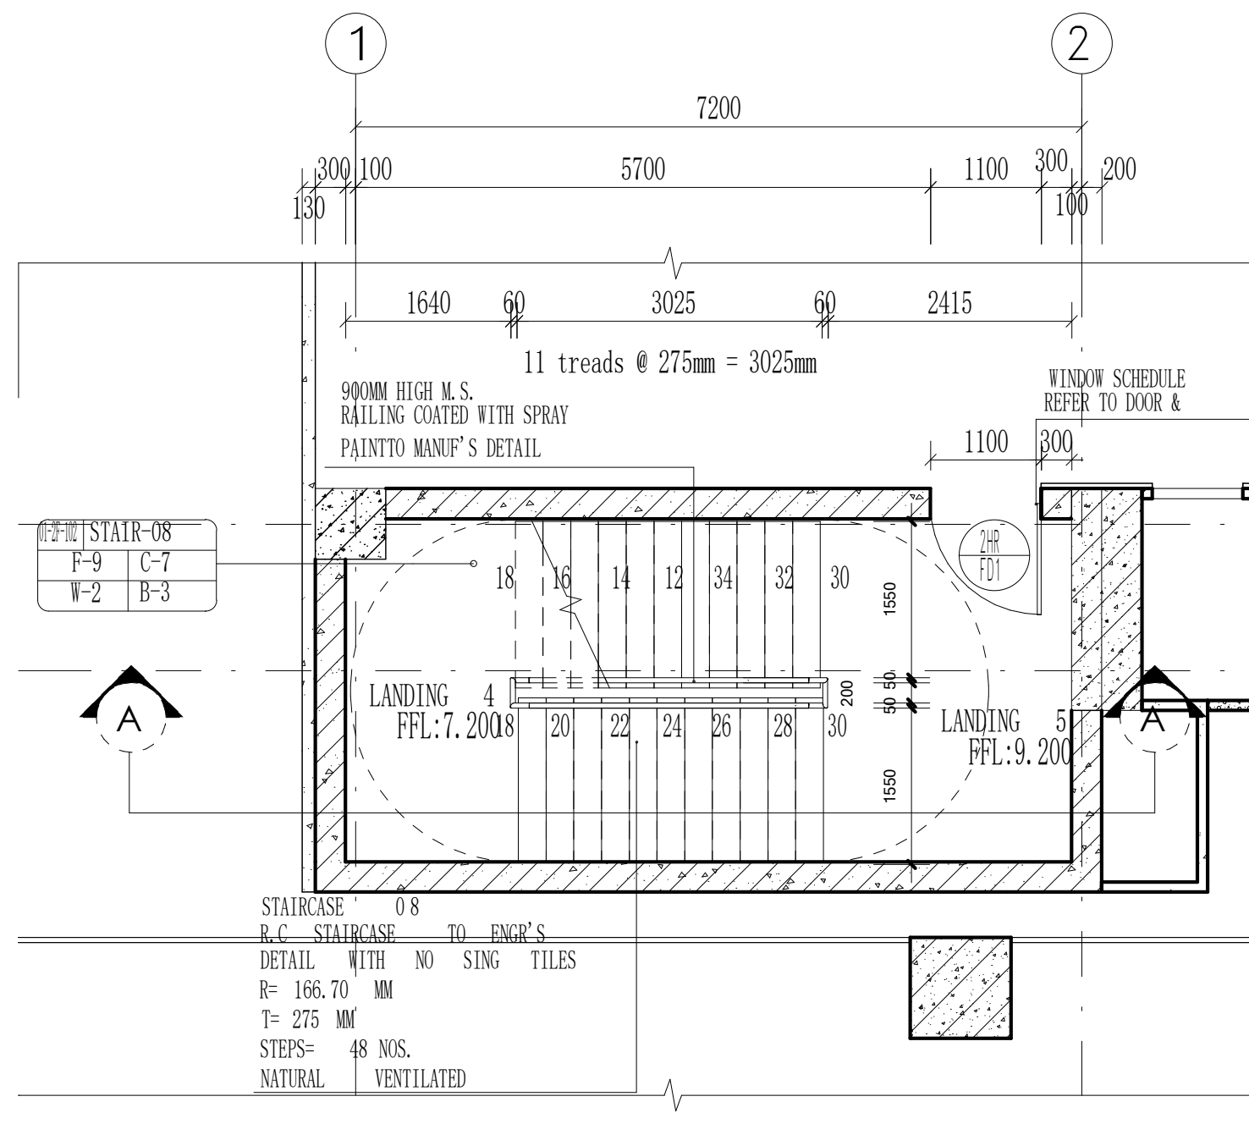
1
2
7200
300 100 5700 1100 300 200
1640 60 3025 60 2415
11 treads @ 275mm = 3025mm
900MM HIGH M.S.
RAILING COATED WITH SPRAY
PAINTTO MANUF'S DETAIL
WINDOW SCHEDULE
REFER TO DOOR &
LANDING 4
FFL:7.200
LANDING 5
FFL:9.200
STAIRCASE 08
R.C STAIRCASE TO ENGR'S
DETAIL WITH NO SING TILES
R= 166.70 MM
T= 275 MM
STEPS= 48 NOS.
NATURAL VENTILATED

STAIR-8 2ND FL

SCALE 1:75

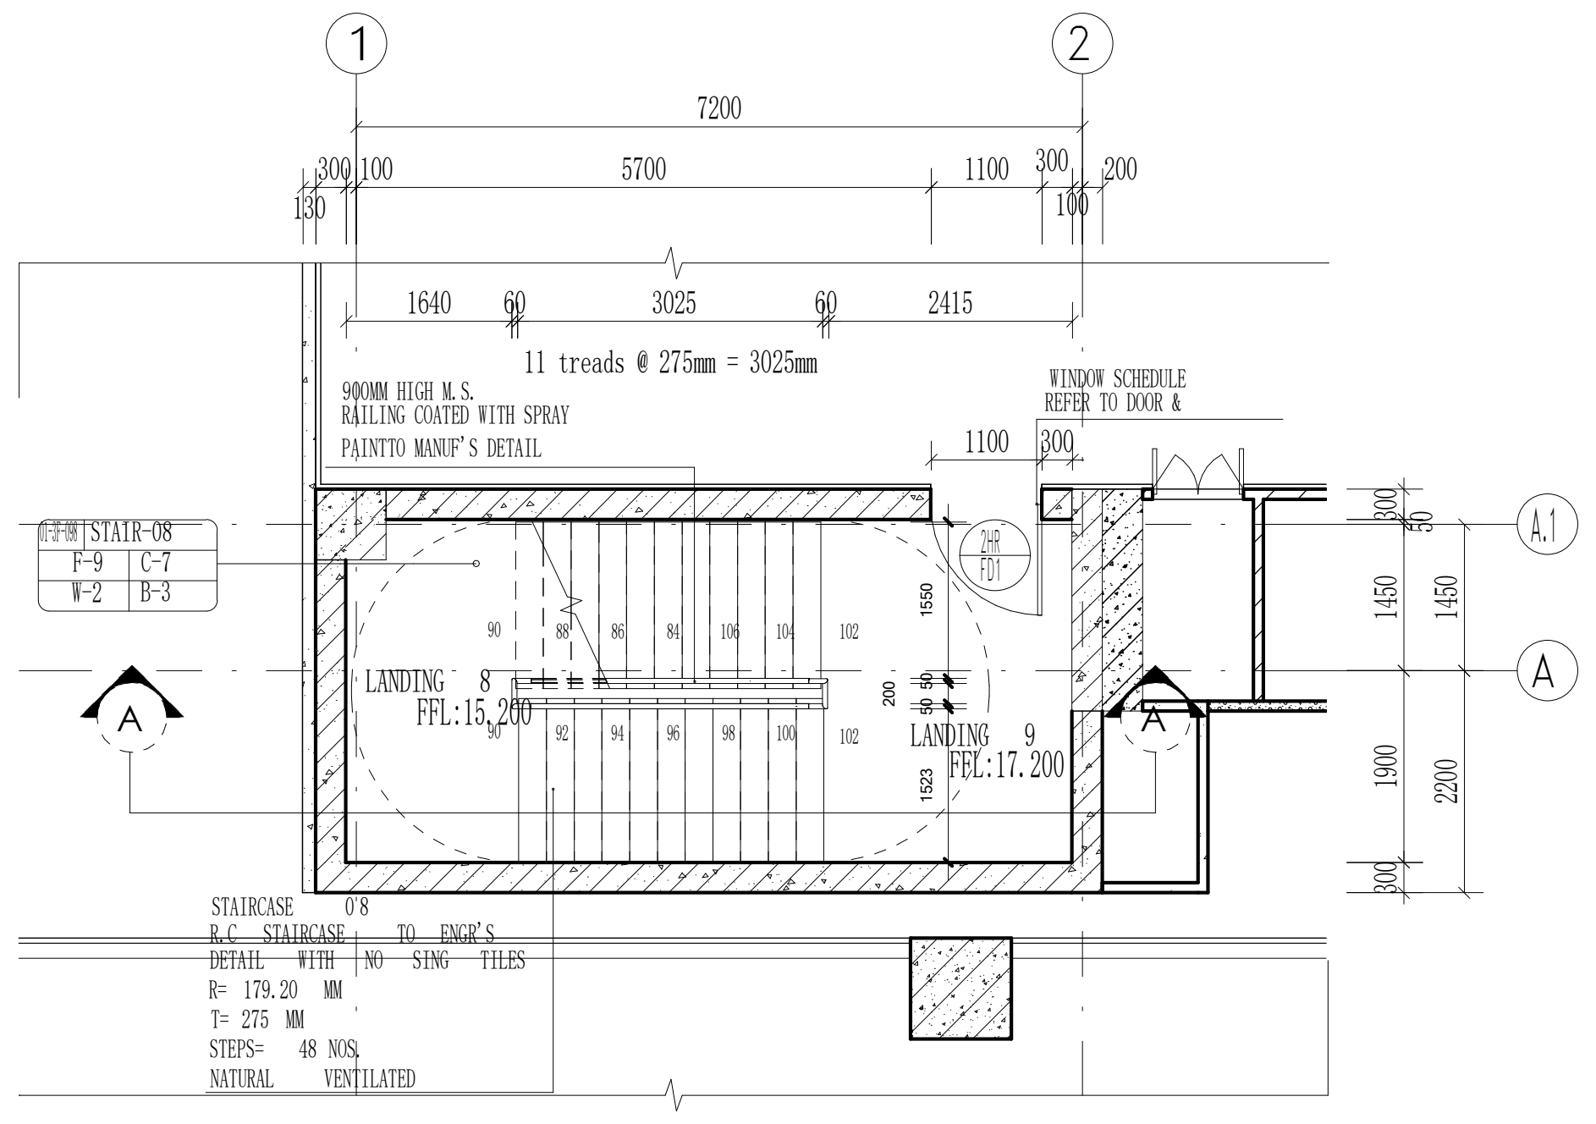
1
2
7200
300 100 5700 1100 300 200
1640 60 3025 60 2415
11 treads @ 275mm = 3025mm
900MM HIGH M.S.
RAILING COATED WITH SPRAY
PAINTTO MANUF'S DETAIL
WINDOW SCHEDULE
REFER TO DOOR &
LANDING 8
FFL:15.200
LANDING 9
FFL:17.200
STAIRCASE 08
R.C STAIRCASE TO ENGR'S
DETAIL WITH NO SING TILES
R= 179.20 MM
T= 275 MM
STEPS= 48 NOS.
NATURAL VENTILATED

STAIR-8 3RD FL

SCALE 1:75

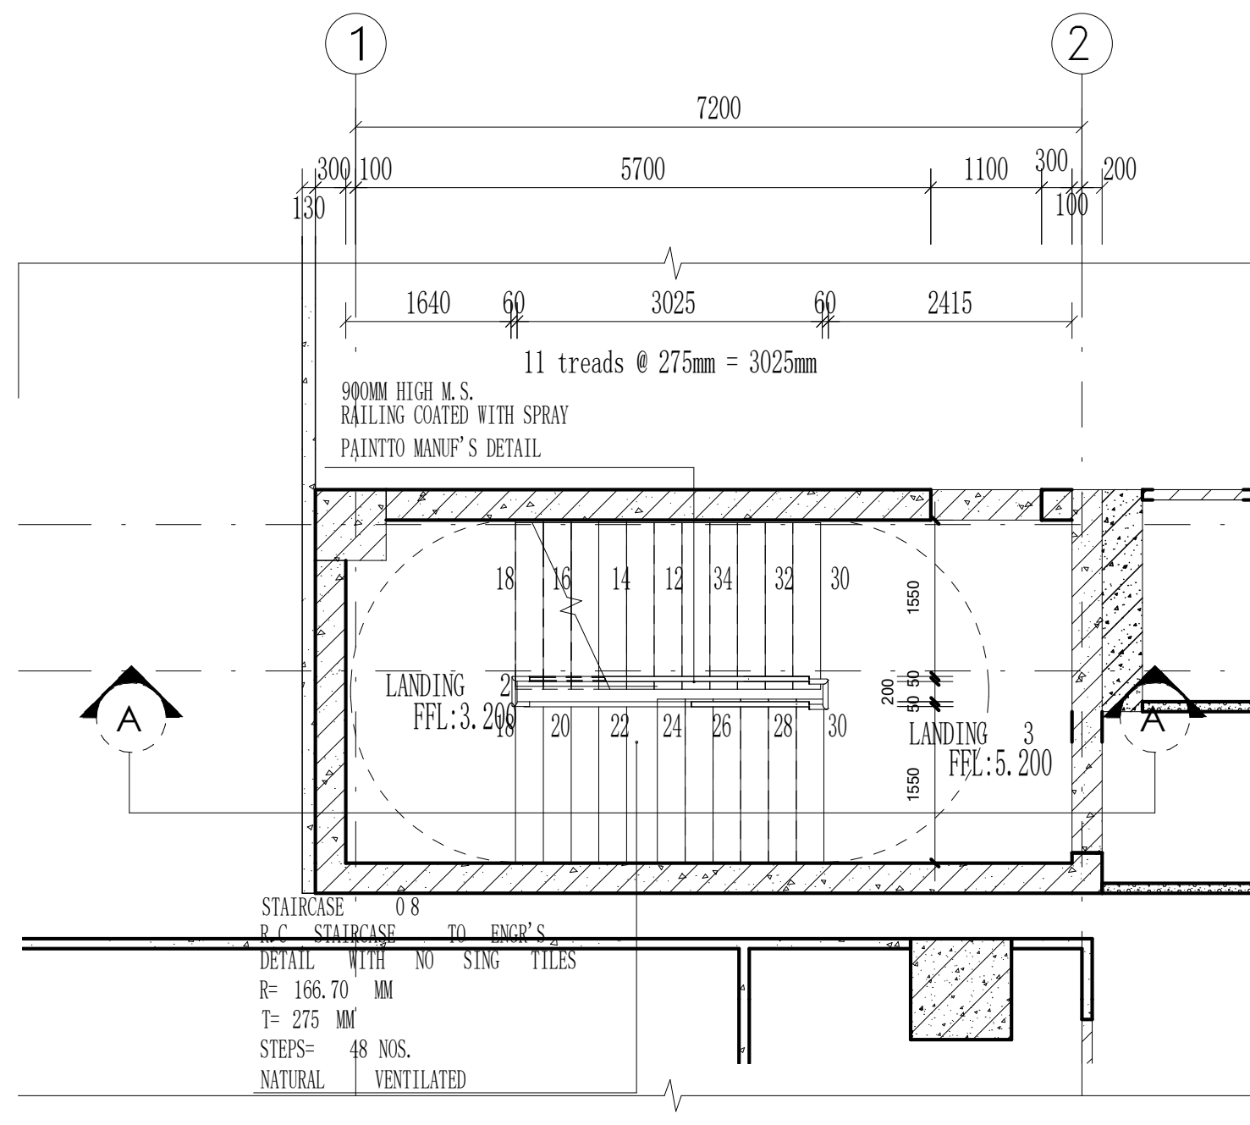
1
2
7200
1640 60 3025 60 2415
11 treads @ 275mm = 3025mm
900MM HIGH M.S.
RAILING COATED WITH SPRAY
PAINTTO MANUF'S DETAIL
LANDING 2
FFL:3.200
LANDING 3
FFL:5.200
STAIRCASE 08
R.C STAIRCASE TO ENGR'S
DETAIL WITH NO SING TILES
R= 166.70 MM
T= 275 MM
STEPS= 48 NOS.
NATURAL VENTILATED

STAIR-8 5.200 ELEVATION PLAN FL

SCALE 1:75

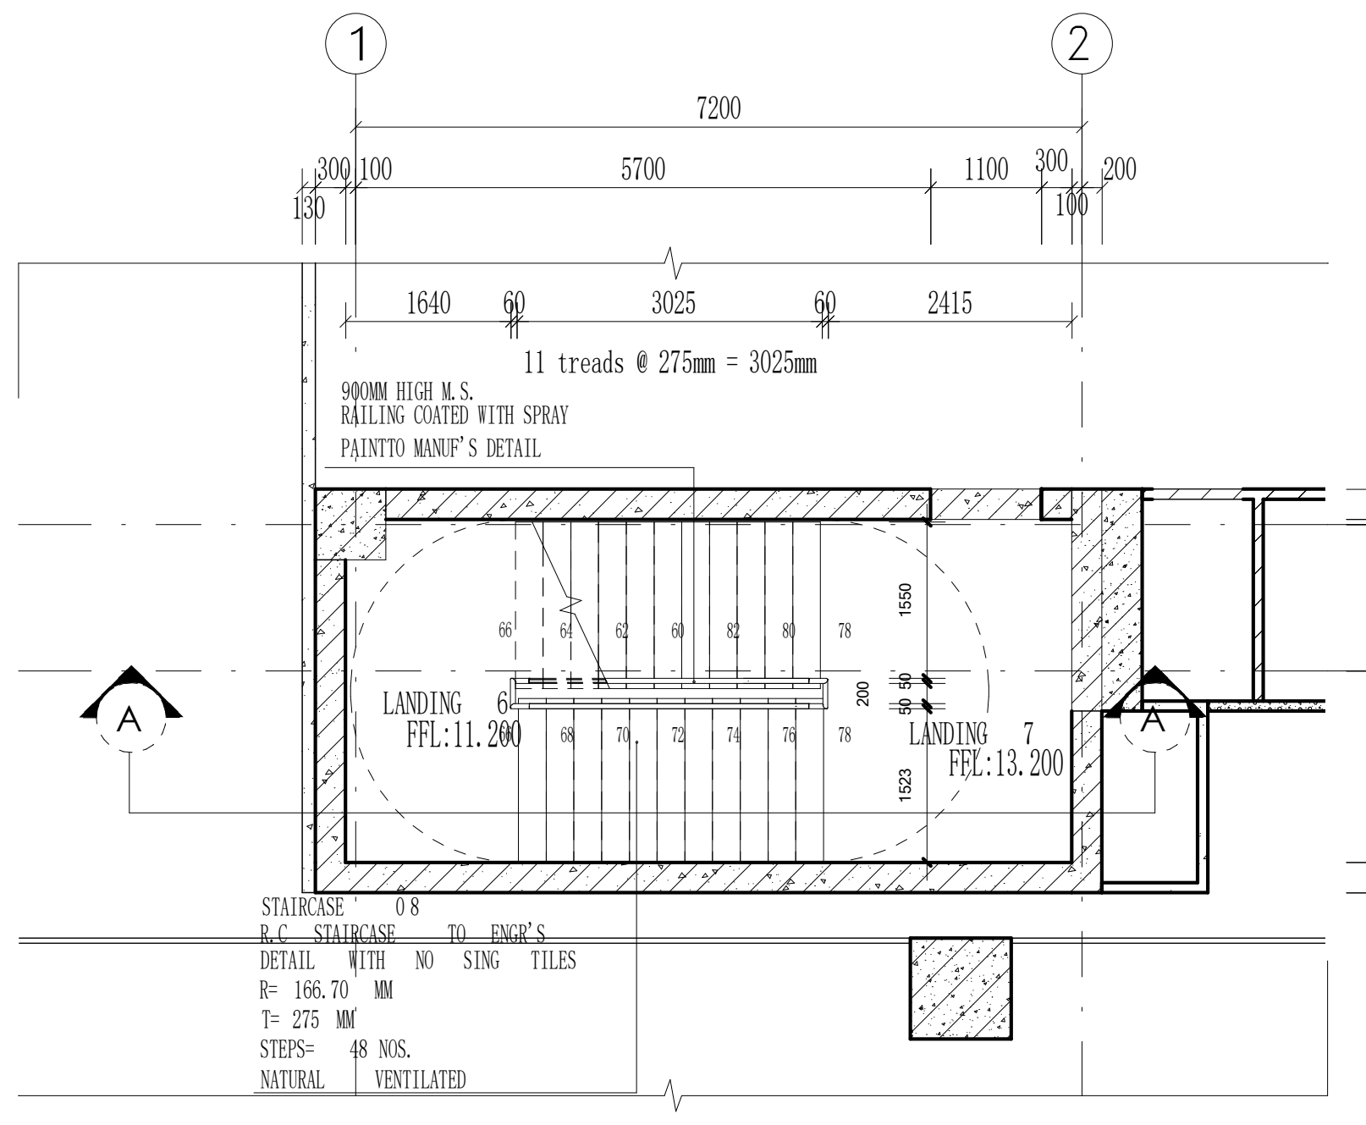
1
2
7200
1640 60 3025 60 2415
11 treads @ 275mm = 3025mm
900MM HIGH M.S.
RAILING COATED WITH SPRAY
PAINTTO MANUF'S DETAIL
LANDING 6
FFL:11.200
LANDING 7
FFL:13.200
STAIRCASE 08
R.C STAIRCASE TO ENGR'S
DETAIL WITH NO SING TILES
R= 166.70 MM
T= 275 MM
STEPS= 48 NOS.
NATURAL VENTILATED

STAIR-8 13.200 ELEVATION PLAN FL

SCALE 1:75

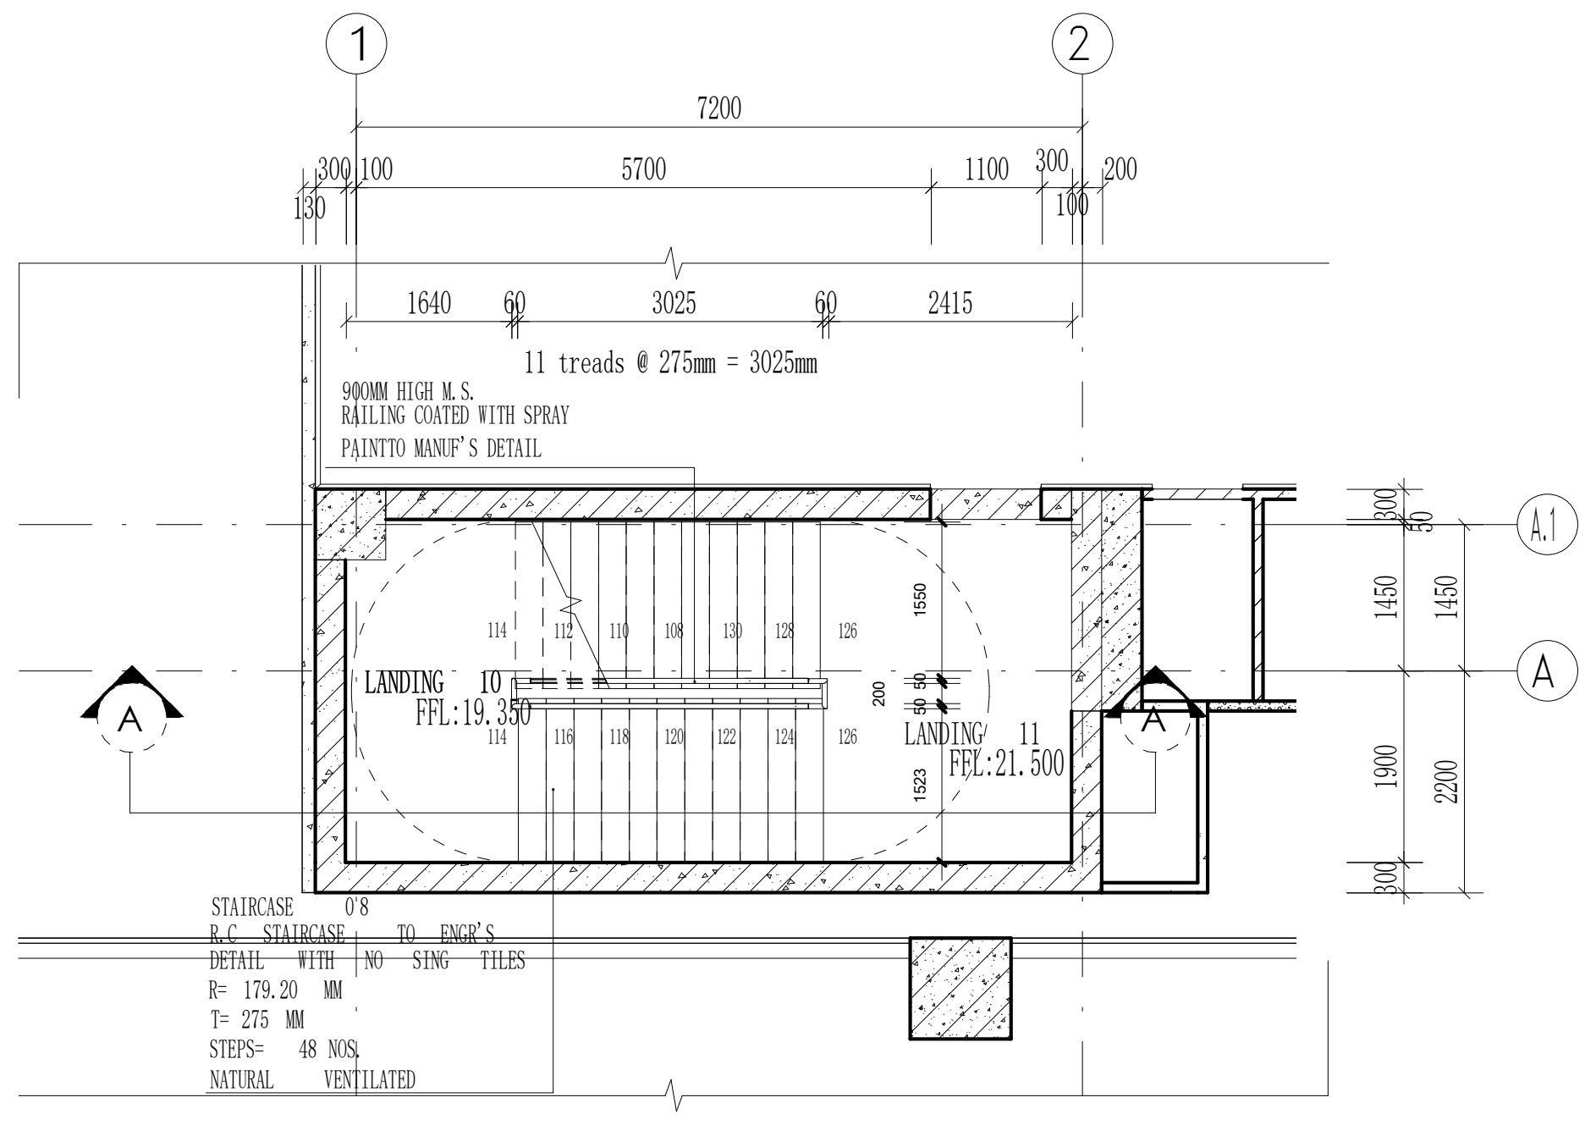
1
2
7200
1640 60 3025 60 2415
11 treads @ 275mm = 3025mm
900MM HIGH M.S.
RAILING COATED WITH SPRAY
PAINTTO MANUF'S DETAIL
LANDING 10
FFL:19.350
LANDING 11
FFL:21.500
STAIRCASE 08
R.C STAIRCASE TO ENGR'S
DETAIL WITH NO SING TILES
R= 166.70 MM
T= 275 MM
STEPS= 48 NOS.
NATURAL VENTILATED

STAIR-8 21.500 ELEVATION PLAN FL

SCALE 1:75

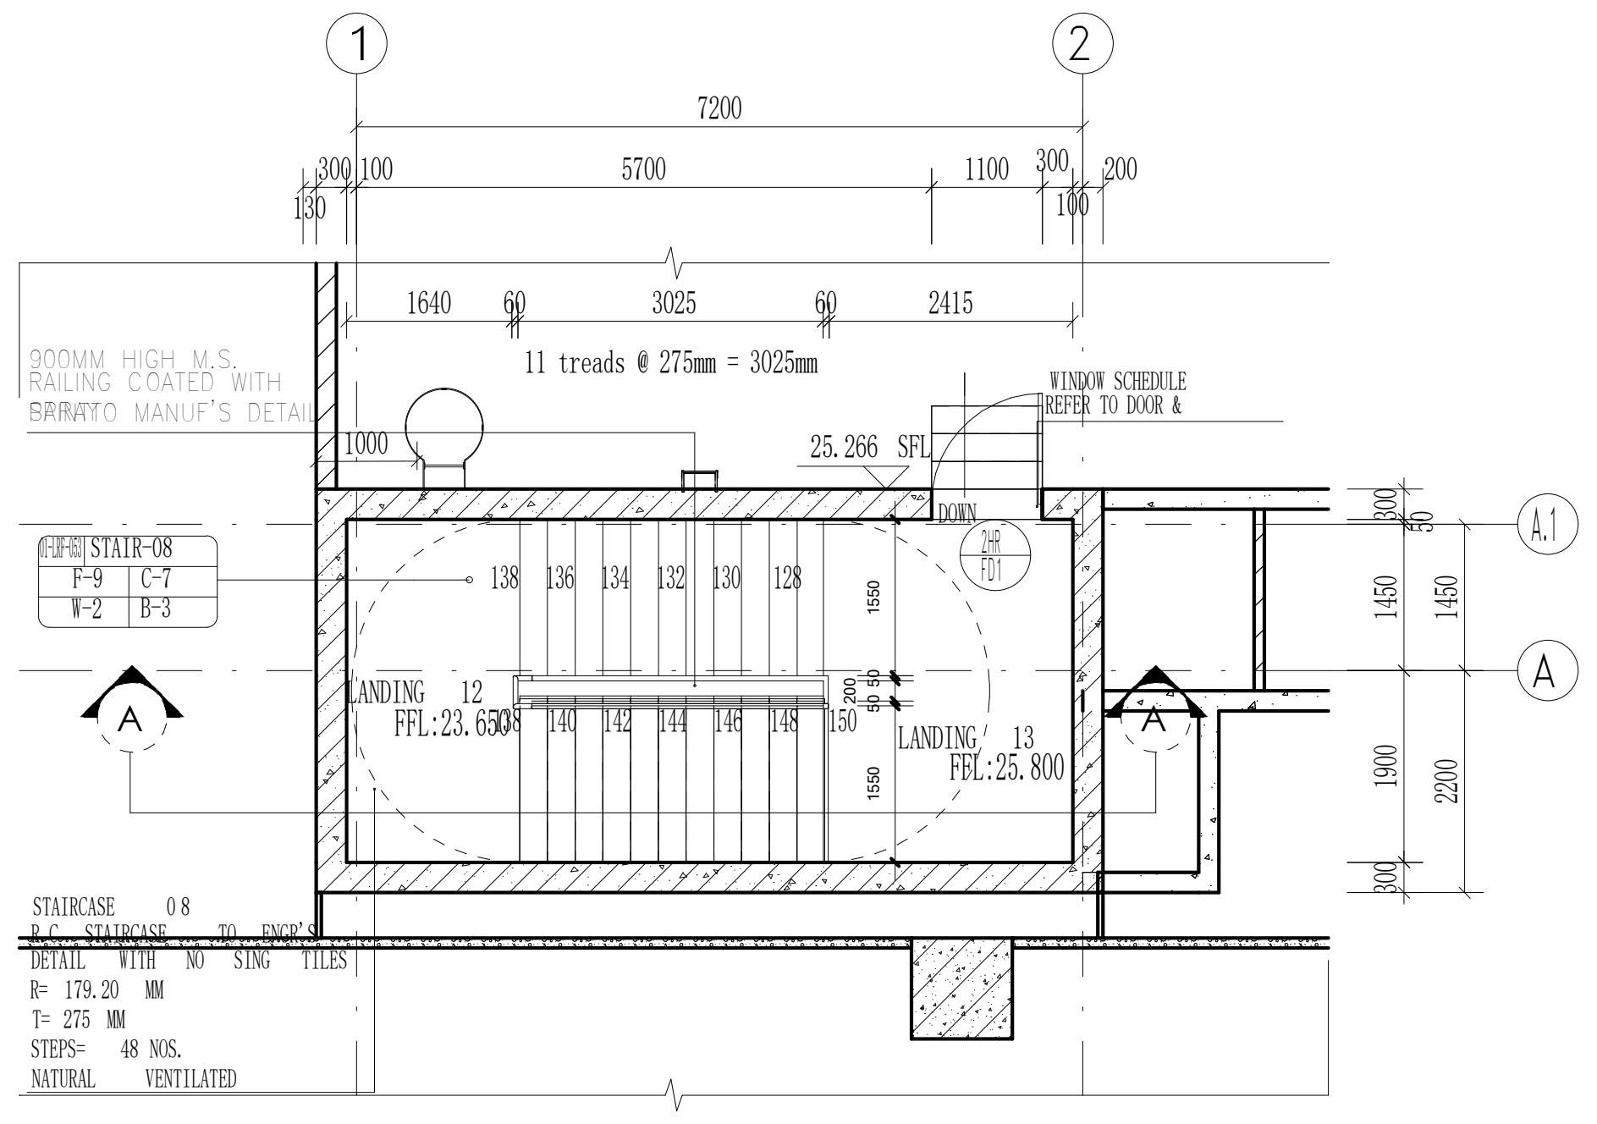
1
2
7200
1640 60 3025 60 2415
11 treads @ 275mm = 3025mm
900MM HIGH M.S.
RAILING COATED WITH
SPRAY MANUF'S DETAIL
WINDOW SCHEDULE
REFER TO DOOR &
25.266 SFL
STAIR-08
F-9 C-7
W-2 B-3
LANDING 12
FFL:23.650
LANDING 13
FFL:25.800
STAIRCASE 08
R.C STAIRCASE TO ENGR'S
DETAIL WITH NO SING TILES
R= 179.20 MM
T= 275 MM
STEPS= 48 NOS.
NATURAL VENTILATED

STAIR-8 RF FL

SCALE 1:75

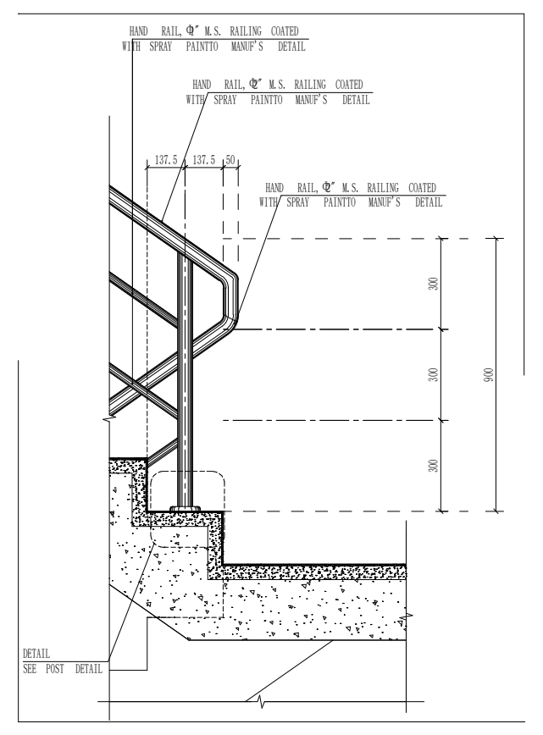

HANDRAIL DETAILS

SCALE 1:75

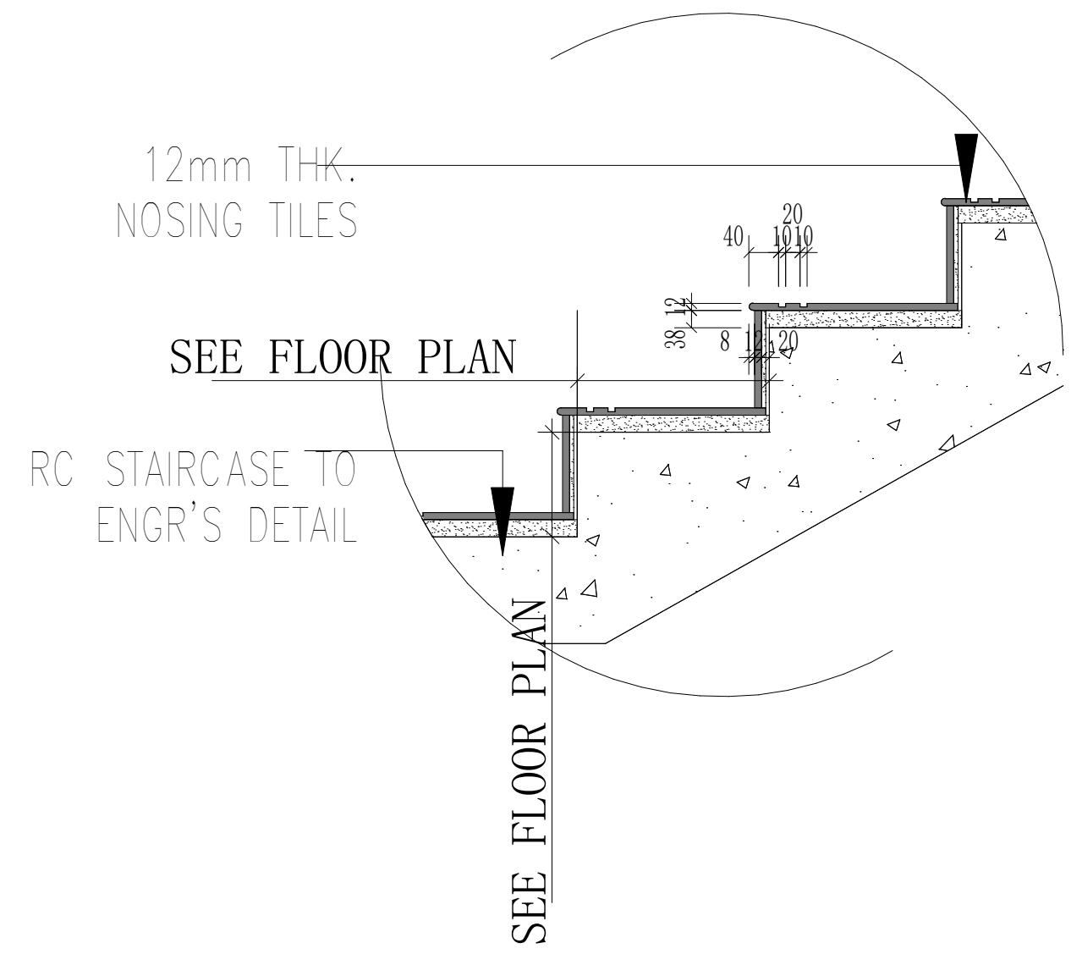
12mm THK.
NOSING TILES
SEE FLOOR PLAN
RC STAIRCASE TO
ENGR'S DETAIL
SEE FLOOR PLAN
40
20
10 10
12
38
8
12
20

STEP DETAILS

SCALE 1:75

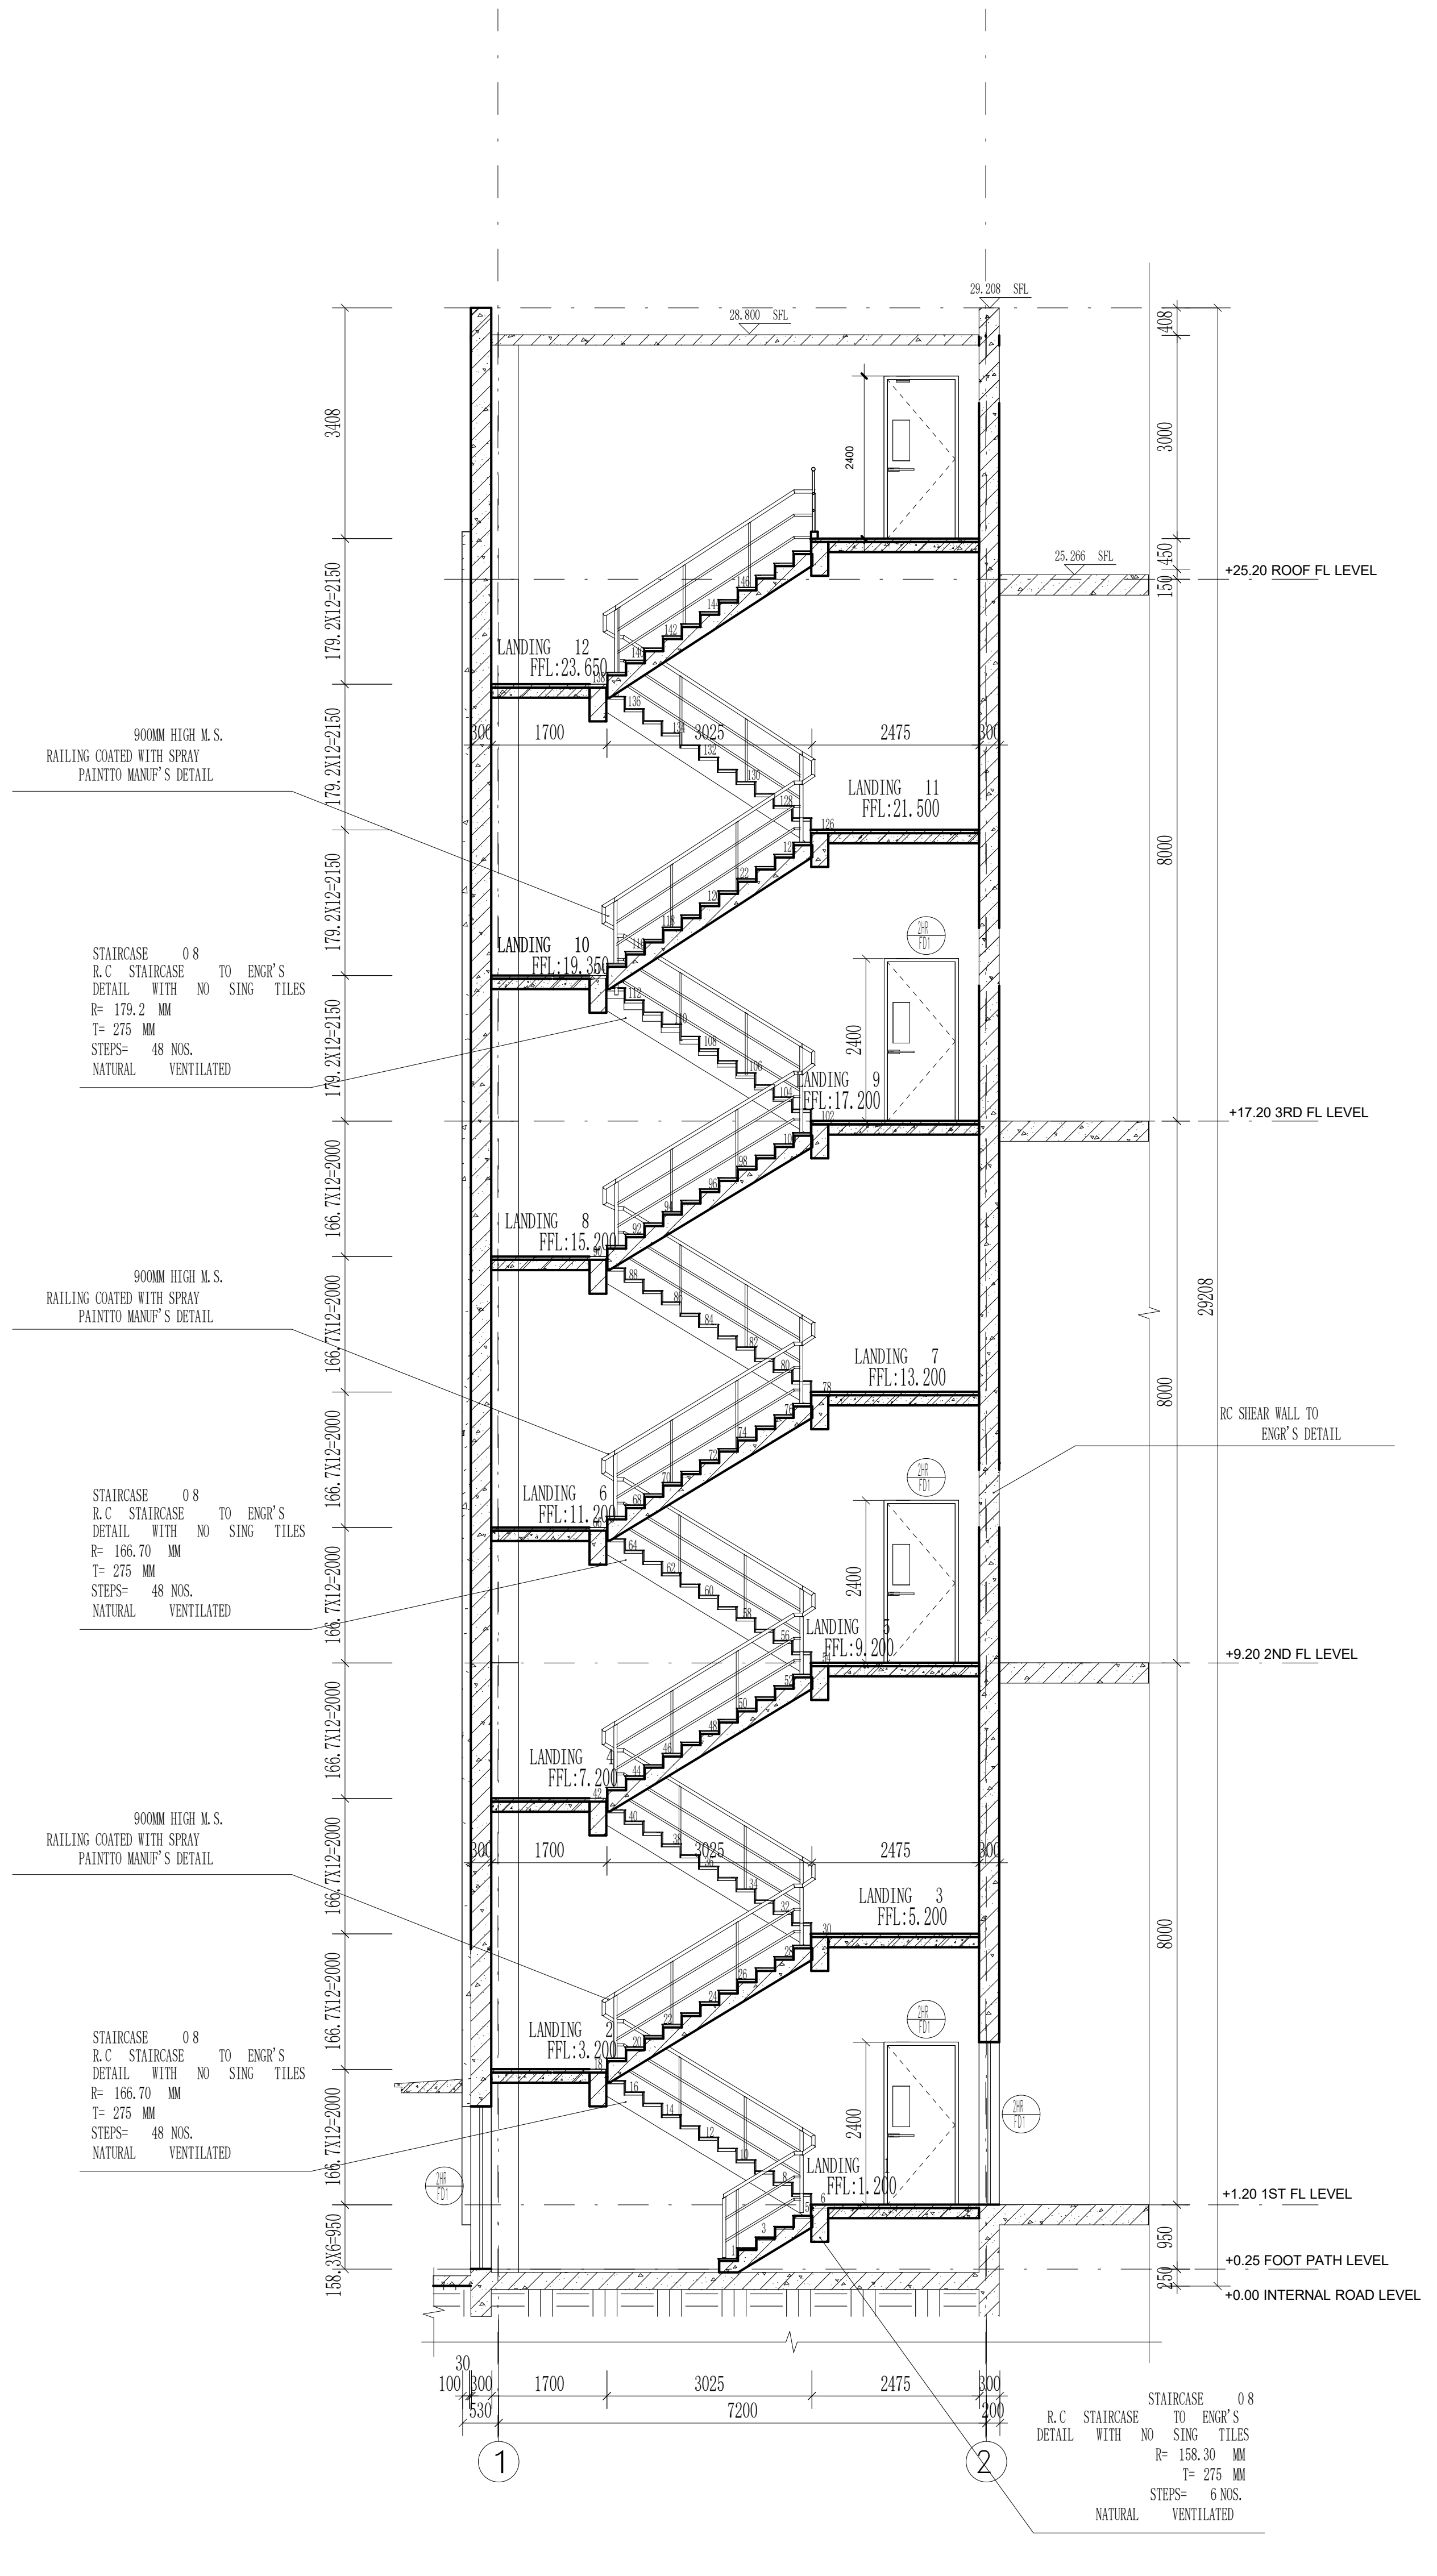
28.800 SFL
29.208 SFL
25.266 SFL
+25.20 ROOF FL LEVEL
+17.20 3RD FL LEVEL
+9.20 2ND FL LEVEL
+1.20 1ST FL LEVEL
+0.25 FOOT PATH LEVEL
+0.00 INTERNAL ROAD LEVEL
LANDING 1 FFL:1.200
LANDING 2 FFL:3.200
LANDING 3 FFL:5.200
LANDING 4 FFL:7.200
LANDING 5 FFL:9.200
LANDING 6 FFL:11.200
LANDING 7 FFL:13.200
LANDING 8 FFL:15.200
LANDING 9 FFL:17.200
LANDING 10 FFL:19.350
LANDING 11 FFL:21.500
LANDING 12 FFL:23.650
900MM HIGH M.S.
RAILING COATED WITH SPRAY
PAINTTO MANUF'S DETAIL
STAIRCASE 08
R.C STAIRCASE TO ENGR'S
DETAIL WITH NO SING TILES
R= 179.2 MM
R= 166.70 MM
R= 158.30 MM
T= 275 MM
STEPS= 48 NOS.
STEPS= 6 NOS.
NATURAL VENTILATED
RC SHEAR WALL TO
ENGR'S DETAIL
3408
179.2X12=2150
166.7X12=2000
158.3X6=950
408
3000
150 450
8000
29208
950
250
2400
30
100 300 1700 3025 2475 300
530 7200 200
1700
1
2

Section A

SCALE 1:75

NOTE :THIS PRINT IS OF A CONFIDENTIAL NATURE, IT SHALL NOT BE TRACED,PHOTOGRAPHED,PHOTOSTATED OR REPRODUCED IN ANY MANER,NOR USED FOR ANY PURPOSE WHATSOEVER EXCEPT BY WRITTEN PERMISSION

CLIENT :

GULF EDGE DC 01

87 Wireless Road, M Thai Tower 11th. Floor, All Seasons Place, Lumpini,
Pathumwan, Bangkok 10330, Thailand

CONTRACTOR :

华西发展(泰国)有限公司
บริษัท หัวซือ ดีเวลลอปเม้นต์ (ประเทศไทย) จำกัด
HUASHI DEVELOPMENT CO.,LTD
No. 202, Room No. 1403, 14/F, Le Concorde Building,
Ratchadapisek Road, Huaykhwang Sub-District,
Huaykhwang District, Bangkok Metropolitan 10310.

CONSULTANT :

ARbay
บริษัท เอ อาร์ เบย์ จำกัด
ARbay Company Limited
31 st Floor Bangkok Insurance Building
25 South Sathorn road Thungmahamek
Sathorn Bangkok 10120 THAILAND
T +66 (0) 2286 8199
F +66 (0) 2286 2863
info@arbay.co.th

CONSULTANT :

Qbic Engineers & Architects Co.,Ltd.
8 Soi KALONG 4 SANAMBINNAM ROAD,
THASAI SUB-DISTRICT, MUANG NONTHABURI DISTRICT
, NONTHABURI.
Tel 662-950-4374
Fax 662-580-3231
E-Mail : qbic@qbic.co.th, www.qbic.co.th
QBIC ENGINEERS AND ARCHITECTS CO.,LTD.

CONSULTANT :

MITR
MITR TECHNICAL CONSULTANT CO.,LTD.
1168/8 12th FLOOR, LUMPINI TOWER BUILDING,
RAMA IV RD., THUNGMAHAMEK, SATHORN, BANGKOK 10120, THAILAND
TEL : 0-2679-9079-84
FAX : 0-2679-9085 E-mail: mitr_dd@mitr.com

Architect :	SIGNATURE
ประกิต พนานุรัตน์ วสถ. 580 ที่อยู่ 251/1 ถ.จารุเมือง แขวงรองเมือง เขตปทุมวัน กรุงเทพมหานคร โทรศัพท์ 02-286-8199	
Structural Engineer :	SIGNATURE
วิศวกรผู้ออกแบบโครงสร้าง	
ณัฐสม สงวนวงษ์ วย 1423 ที่อยู่ 2/1 ซ.รามคำแหง 150 ถ.รามคำแหง แขวง สะพานสูง เขต สะพานสูง กทม. 10240	
Structural Inspector :	SIGNATURE
วิศวกรผู้ตรวจสอบโครงสร้าง	
โกมล จุฑาภัทร วย 964 ที่อยู่ 24/18 ซ.นวมินทร์ 129 ถ. นวมินทร์ แขวง นวลจันทร์ เขต บึงกุ่ม กทม. 10230	
Electrical Engineer :	SIGNATURE
วิศวกรผู้ออกแบบระบบไฟฟ้ากำลัง	
นายสุภัทร บูรณวิทย์ วฟก.1265 ที่อยู่ 21 ซอยทานสัมฤทธิ์ 13 ตำบลท่าทราย อ.เมืองนนทบุรี จ.นนทบุรี 11000	
Mechanical Engineer :	SIGNATURE
วิศวกรผู้ออกแบบระบบเครื่องกลและปรับอากาศ	
นายประสิทธิ์ เกี้ยวสุนทร วก.1221 ที่อยู่ 44/372 ซอยบางกระดี่ 35/1 แขวงแสมดำ เขตบางขุนเทียน กทม. 10150	ประสิทธิ์
Sanitary Engineer :	SIGNATURE
วิศวกรผู้ออกแบบระบบสุขาภิบาล และดับเพลิง	
นายทศวรรษ สนั่นฤทธิ์ วส. 215 ที่อยู่ บ้านเลขที่ 99/107 หมู่ที่ 3 ต.ศีรษะจรเข้น้อย อ.บางเสาธง จ.สมุทรปราการ 10540	ทศวรรษ

ISSUE/REVISION

REV.	DESCRIPTION	DATE
A	90% DEVELOPED	09/05/2026

PROJECT NAME :

GEDC 01

LOCATION:
Nikhom Phattana district, Rayong ,industrial estate,CPGC

BUILDING :
MAIN BUILDING

90% DEVELOPED

TITLE :

STAIRCASE 08

JOB NO.	SCALE 1 : 75
DRAWN WYSH	REF.
CHECKED LJC	DWG. NO. MPK01A-90-A-ST-008
APPROVED LXD	
DATE 2026.05.09	