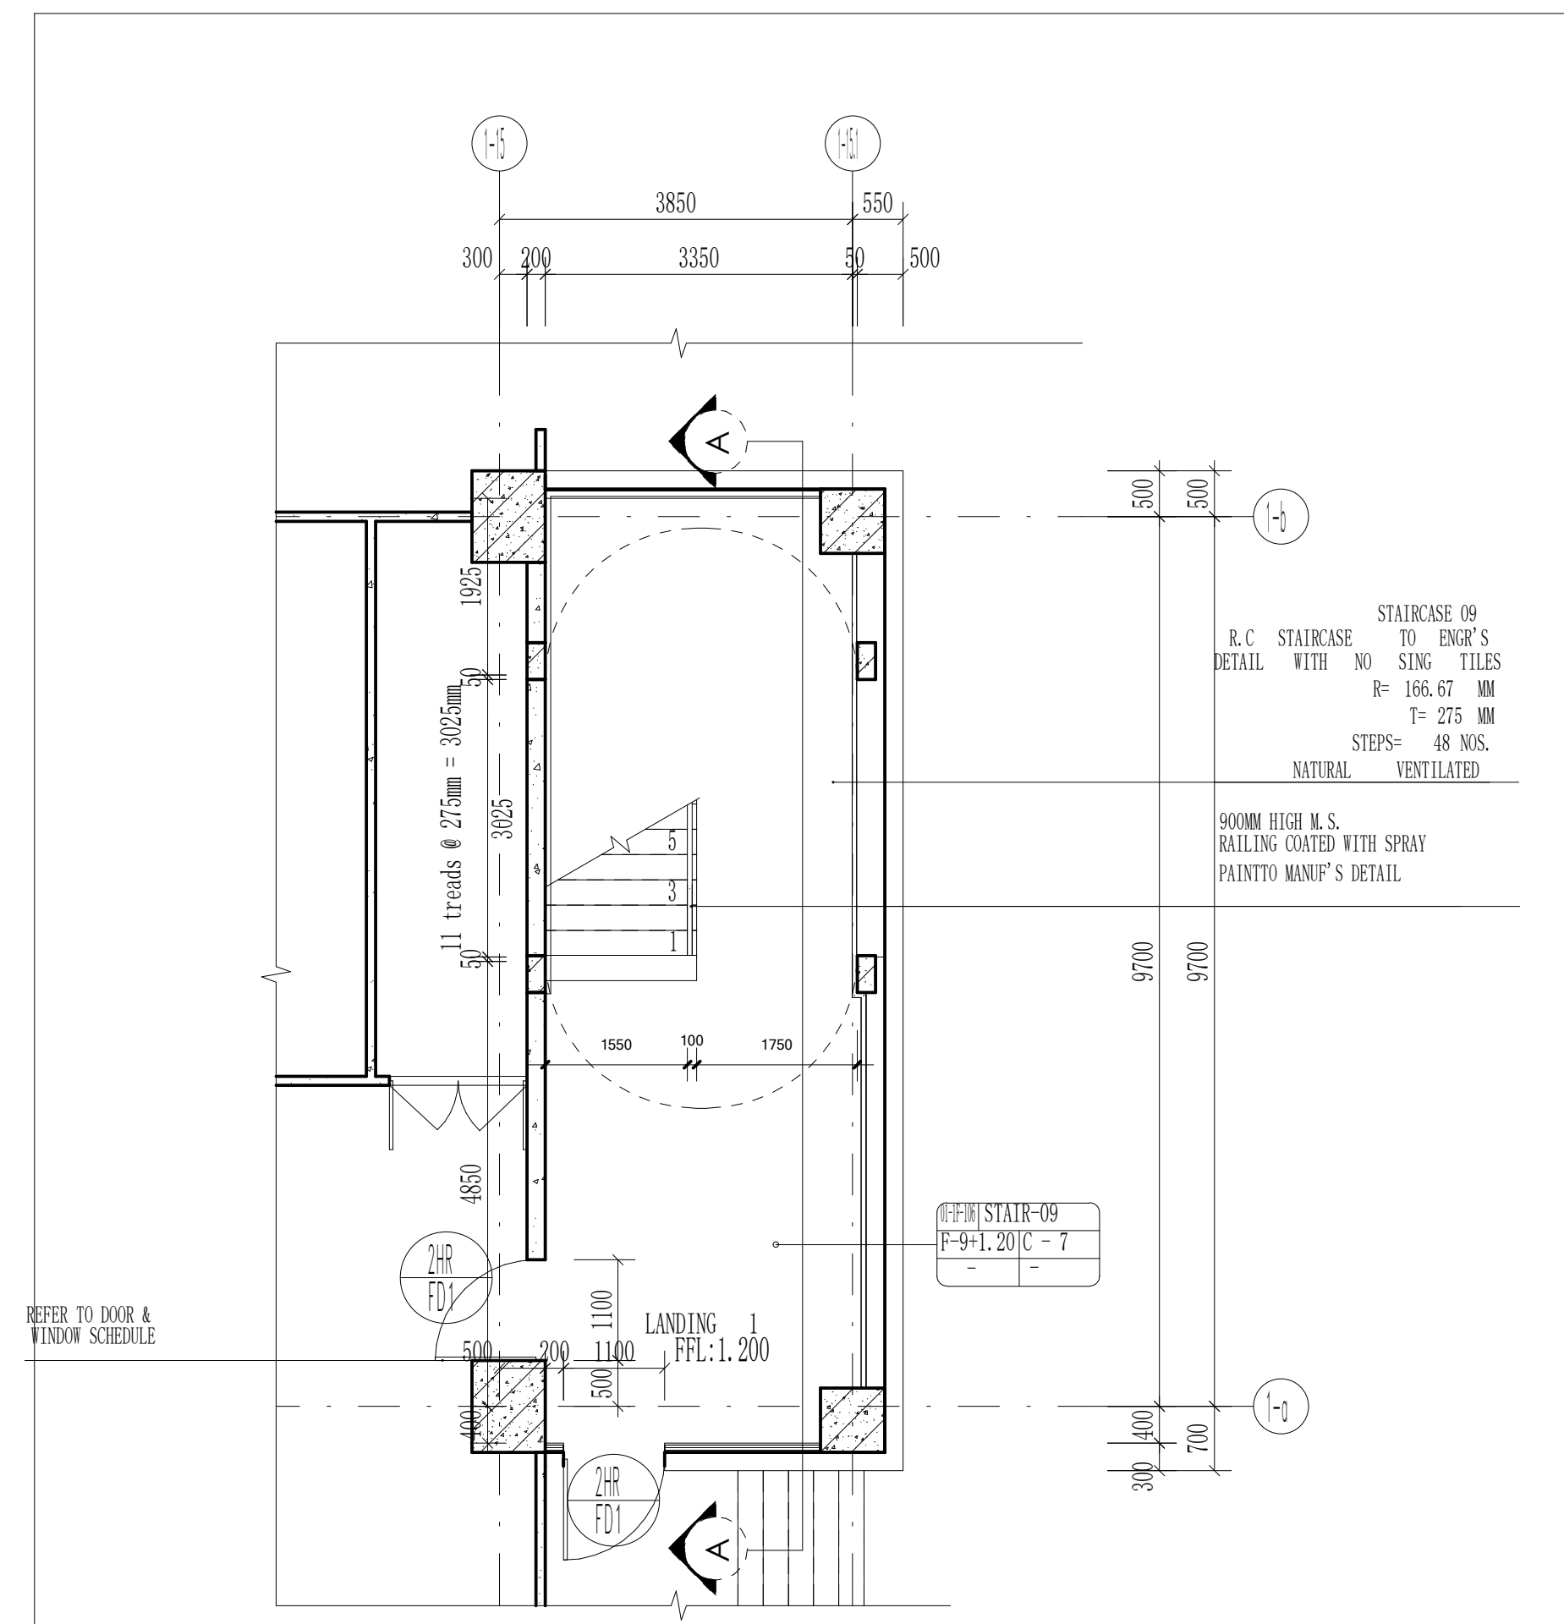

1-15
1-15.1
3850
550
300
200
3350
50
500
1-b
1-a
STAIRCASE 09
R.C STAIRCASE TO ENGR'S
DETAIL WITH NO SING TILES
R= 166.67 MM
T= 275 MM
STEPS= 48 NOS.
NATURAL VENTILATED
900MM HIGH M.S.
RAILING COATED WITH SPRAY
PAINTTO MANUF'S DETAIL
11 treads @ 275mm = 3025mm
1925
3025
4850
9700
1550
100
1750
2HR
FD1
REFER TO DOOR & WINDOW SCHEDULE
LANDING 1
FFL:1.200
STAIR-09
F-9+1.20
C - 7

STAIR-9 GROUND FL
SCALE 1:75

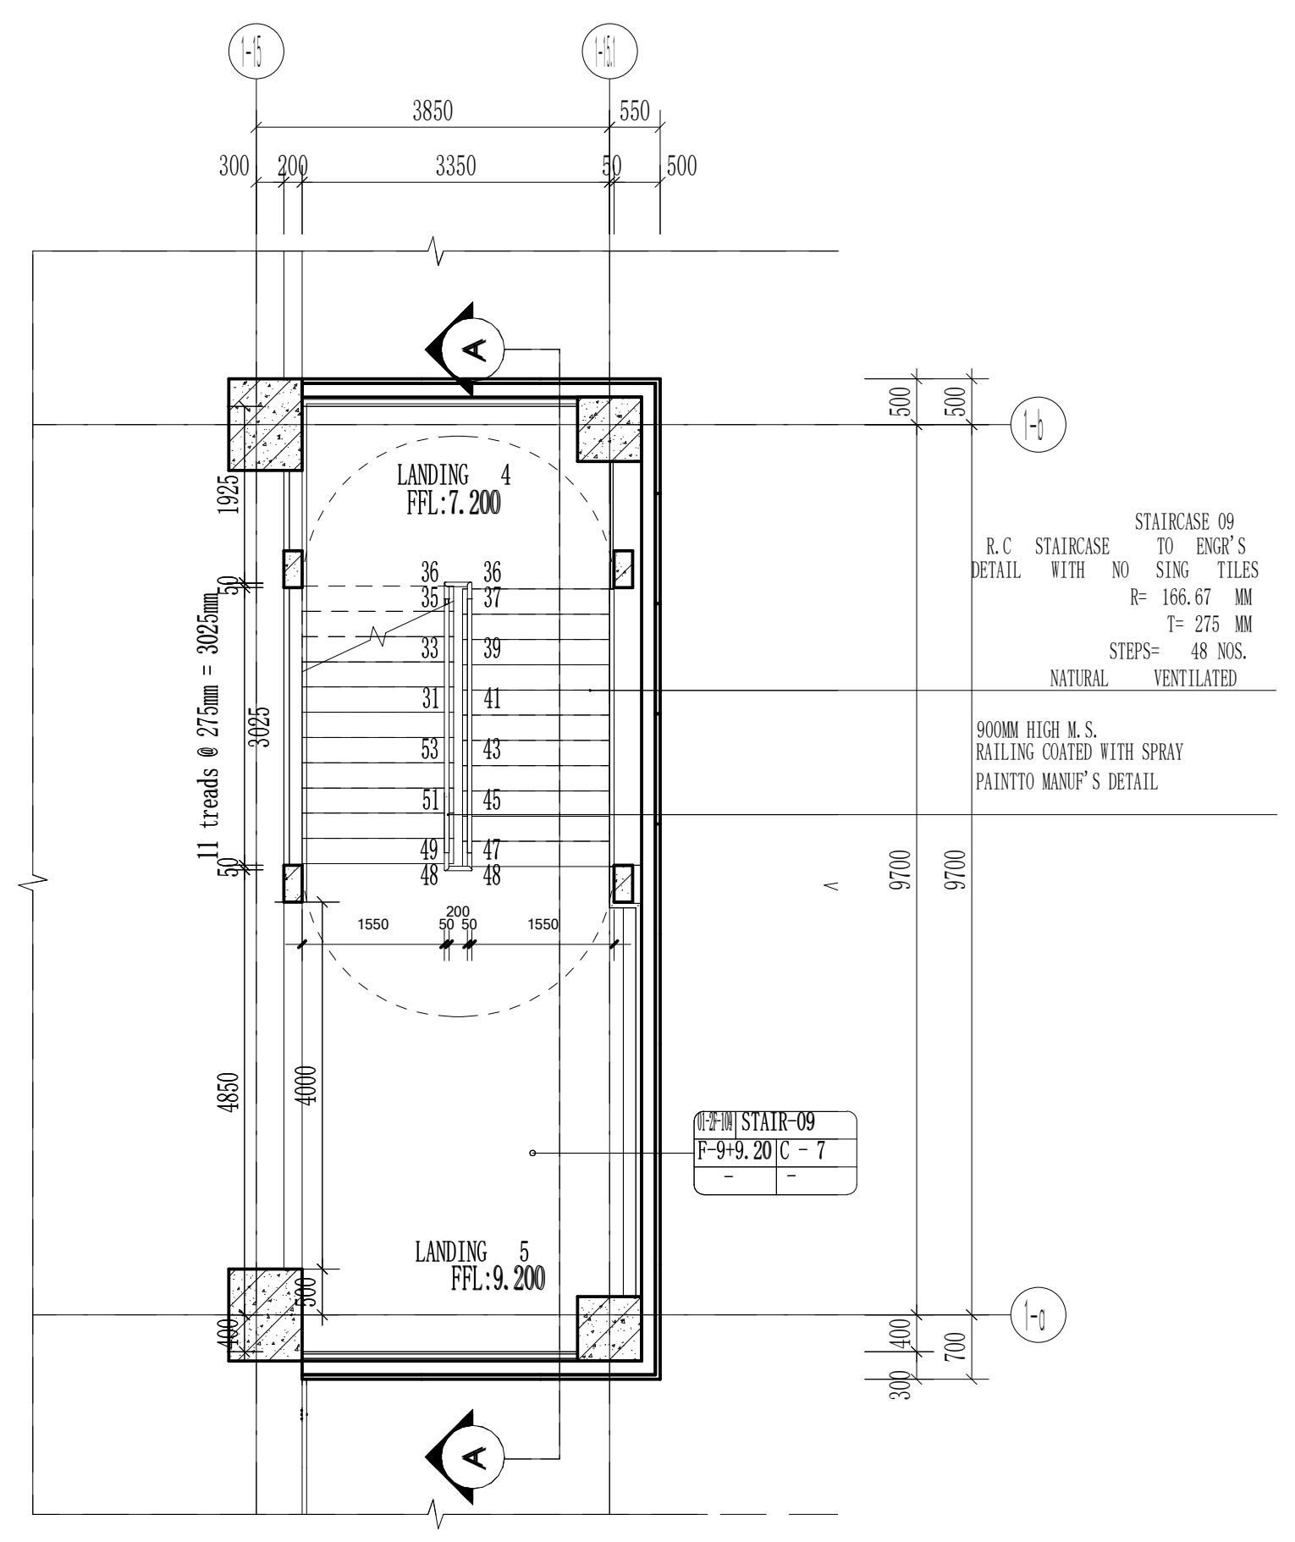

3850
3350
LANDING 4
FFL:7.200
LANDING 5
FFL:9.200
11 treads @ 275mm = 3025mm
STAIRCASE 09
R.C STAIRCASE TO ENGR'S
DETAIL WITH NO SING TILES
R= 166.67 MM
T= 275 MM
STEPS= 48 NOS.
NATURAL VENTILATED
900MM HIGH M.S.
RAILING COATED WITH SPRAY
PAINTTO MANUF'S DETAIL
9700

STAIR-9 2ND FL
SCALE 1:75

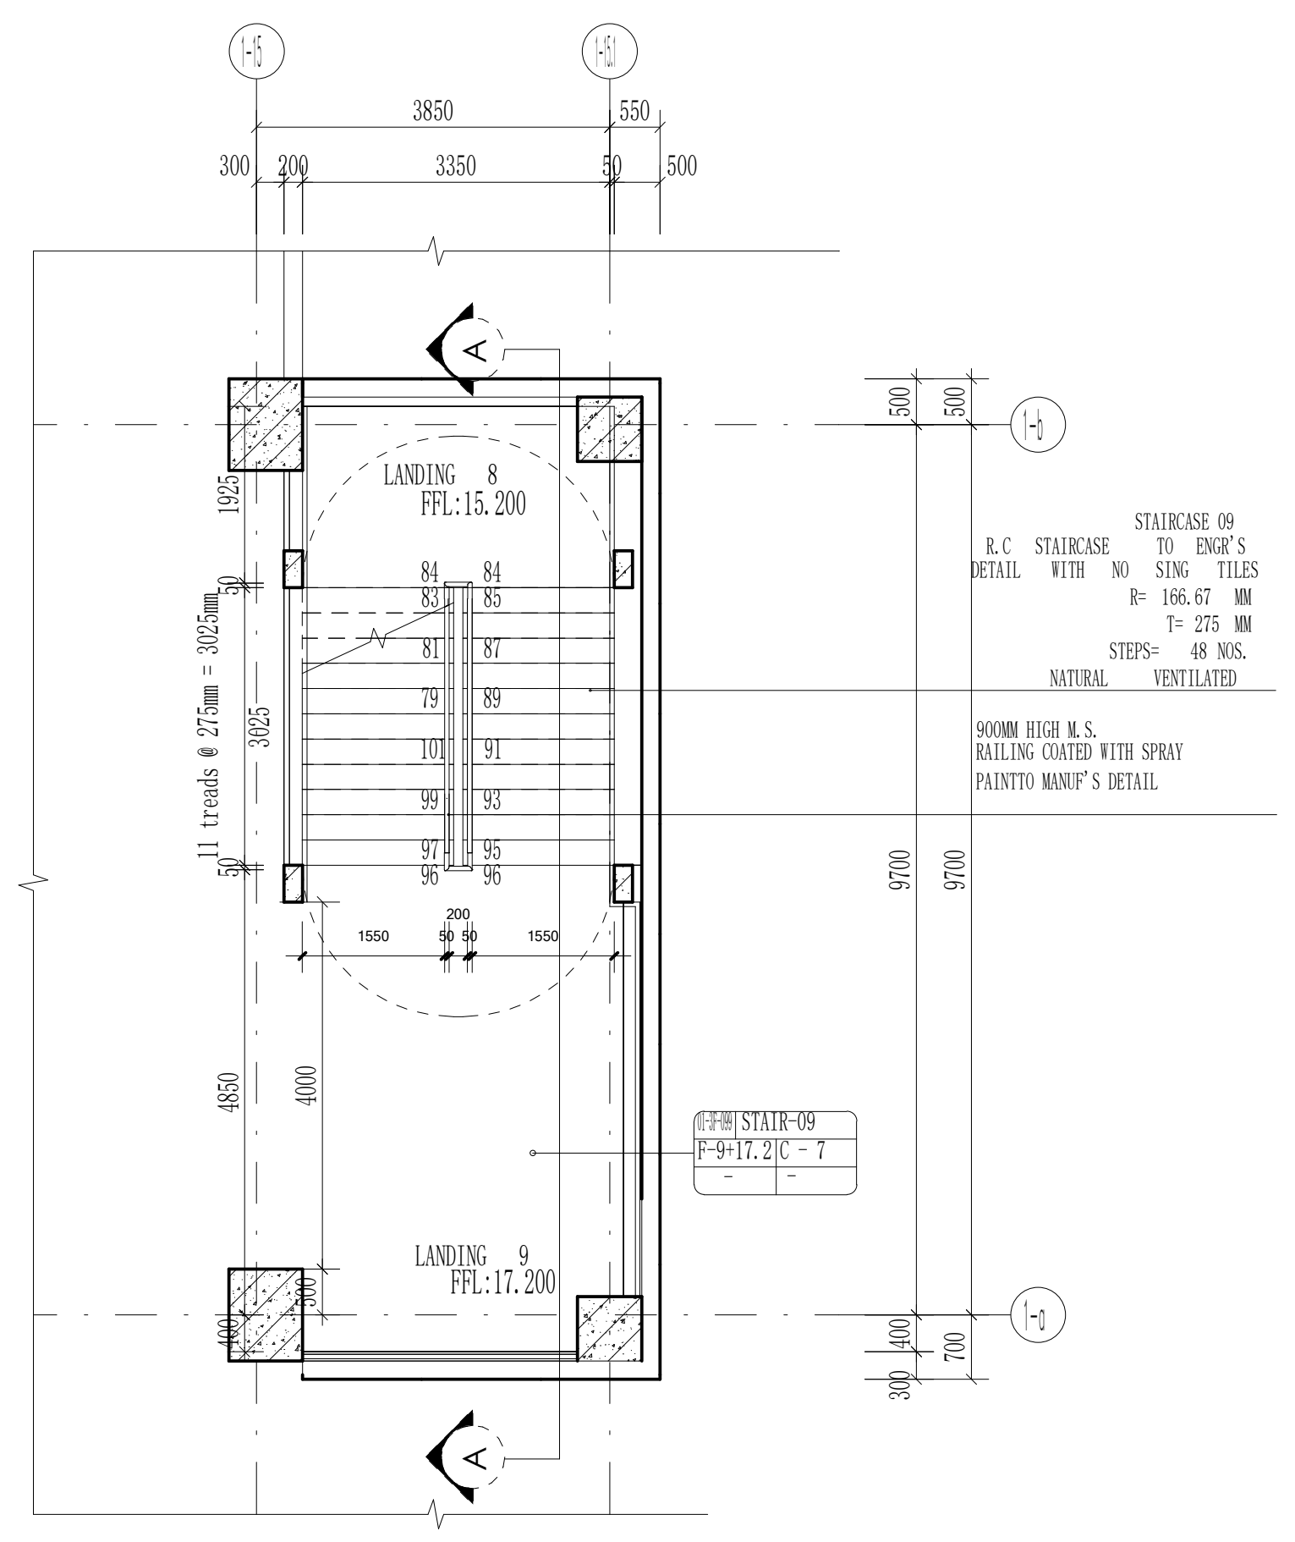

3850
3350
LANDING 8
FFL:15.200
LANDING 9
FFL:17.200
11 treads @ 275mm = 3025mm
STAIRCASE 09
R.C STAIRCASE TO ENGR'S
DETAIL WITH NO SING TILES
R= 166.67 MM
T= 275 MM
STEPS= 48 NOS.
NATURAL VENTILATED
900MM HIGH M.S.
RAILING COATED WITH SPRAY
PAINTTO MANUF'S DETAIL
9700

STAIR-9 3RD FL
SCALE 1:75

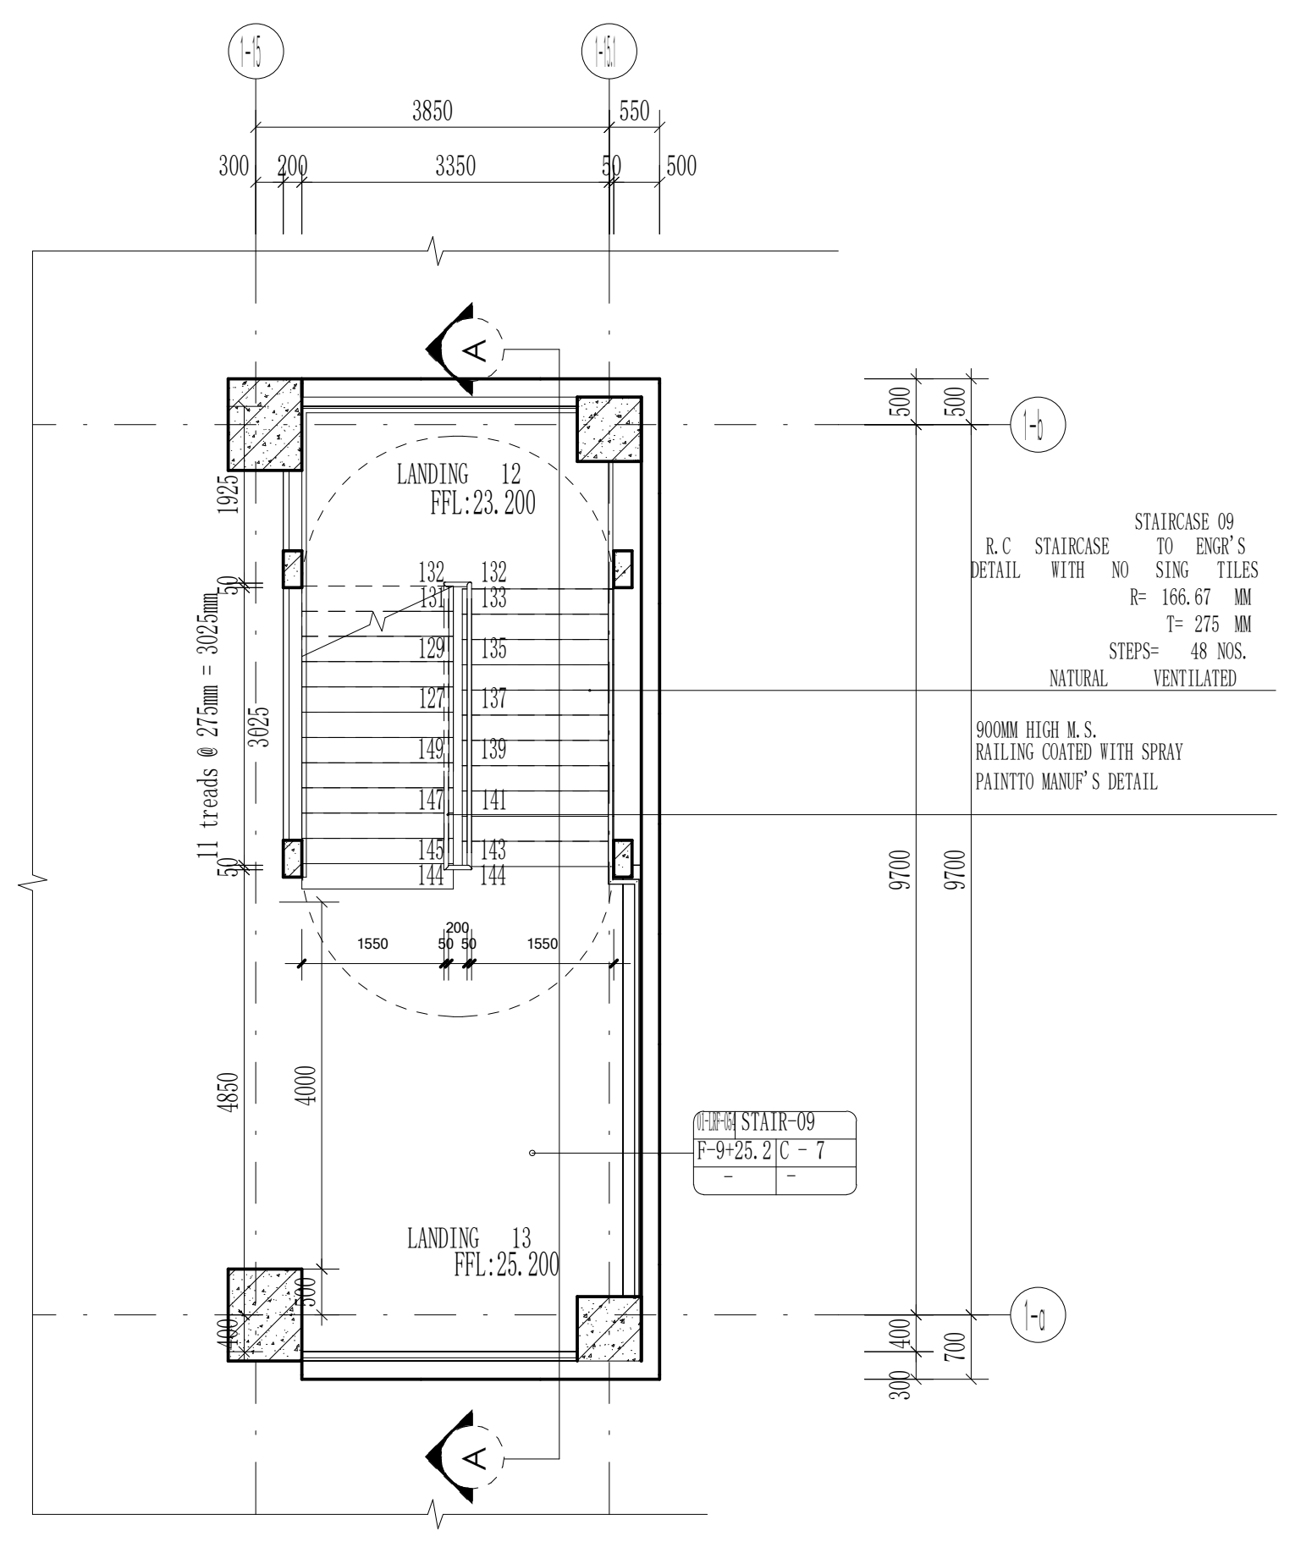

3850
3350
LANDING 12
FFL:23.200
LANDING 13
FFL:25.200
11 treads @ 275mm = 3025mm
STAIRCASE 09
R.C STAIRCASE TO ENGR'S
DETAIL WITH NO SING TILES
R= 170.45 MM
T= 275 MM
STEPS= 44 NOS.
NATURAL VENTILATED
900MM HIGH M.S.
RAILING COATED WITH SPRAY
PAINTTO MANUF'S DETAIL
9700

STAIR-9 ROOF FL
SCALE 1:75

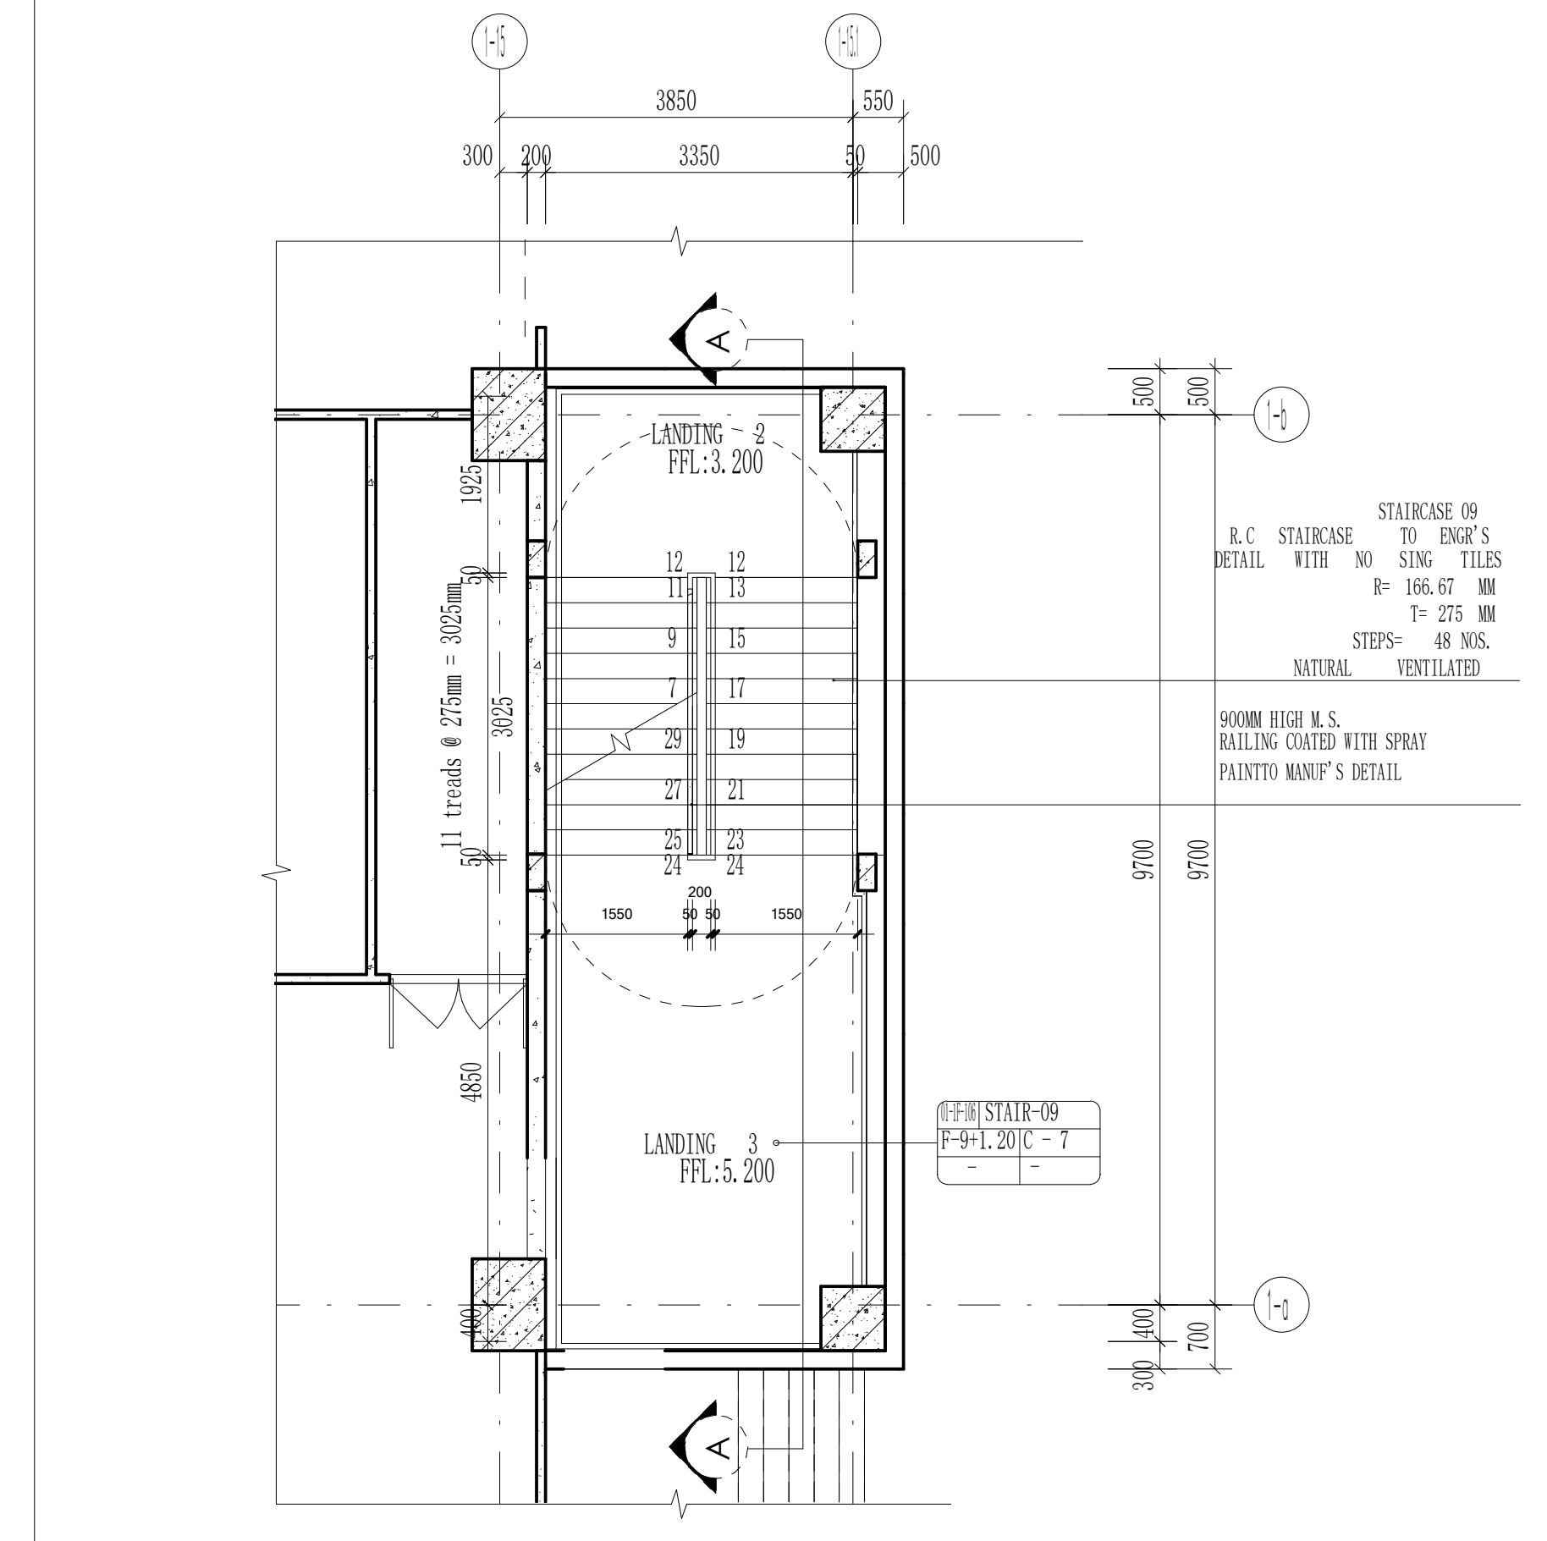

3850
3350
LANDING 2
FFL:3.200
LANDING 3
FFL:5.200
11 treads @ 275mm = 3025mm
STAIRCASE 09
R.C STAIRCASE TO ENGR'S
DETAIL WITH NO SING TILES
R= 166.67 MM
T= 275 MM
STEPS= 48 NOS.
NATURAL VENTILATED
900MM HIGH M.S.
RAILING COATED WITH SPRAY
PAINTTO MANUF'S DETAIL
9700

STAIR-9 5.200 ELEVATION PLAN FL
SCALE 1:75

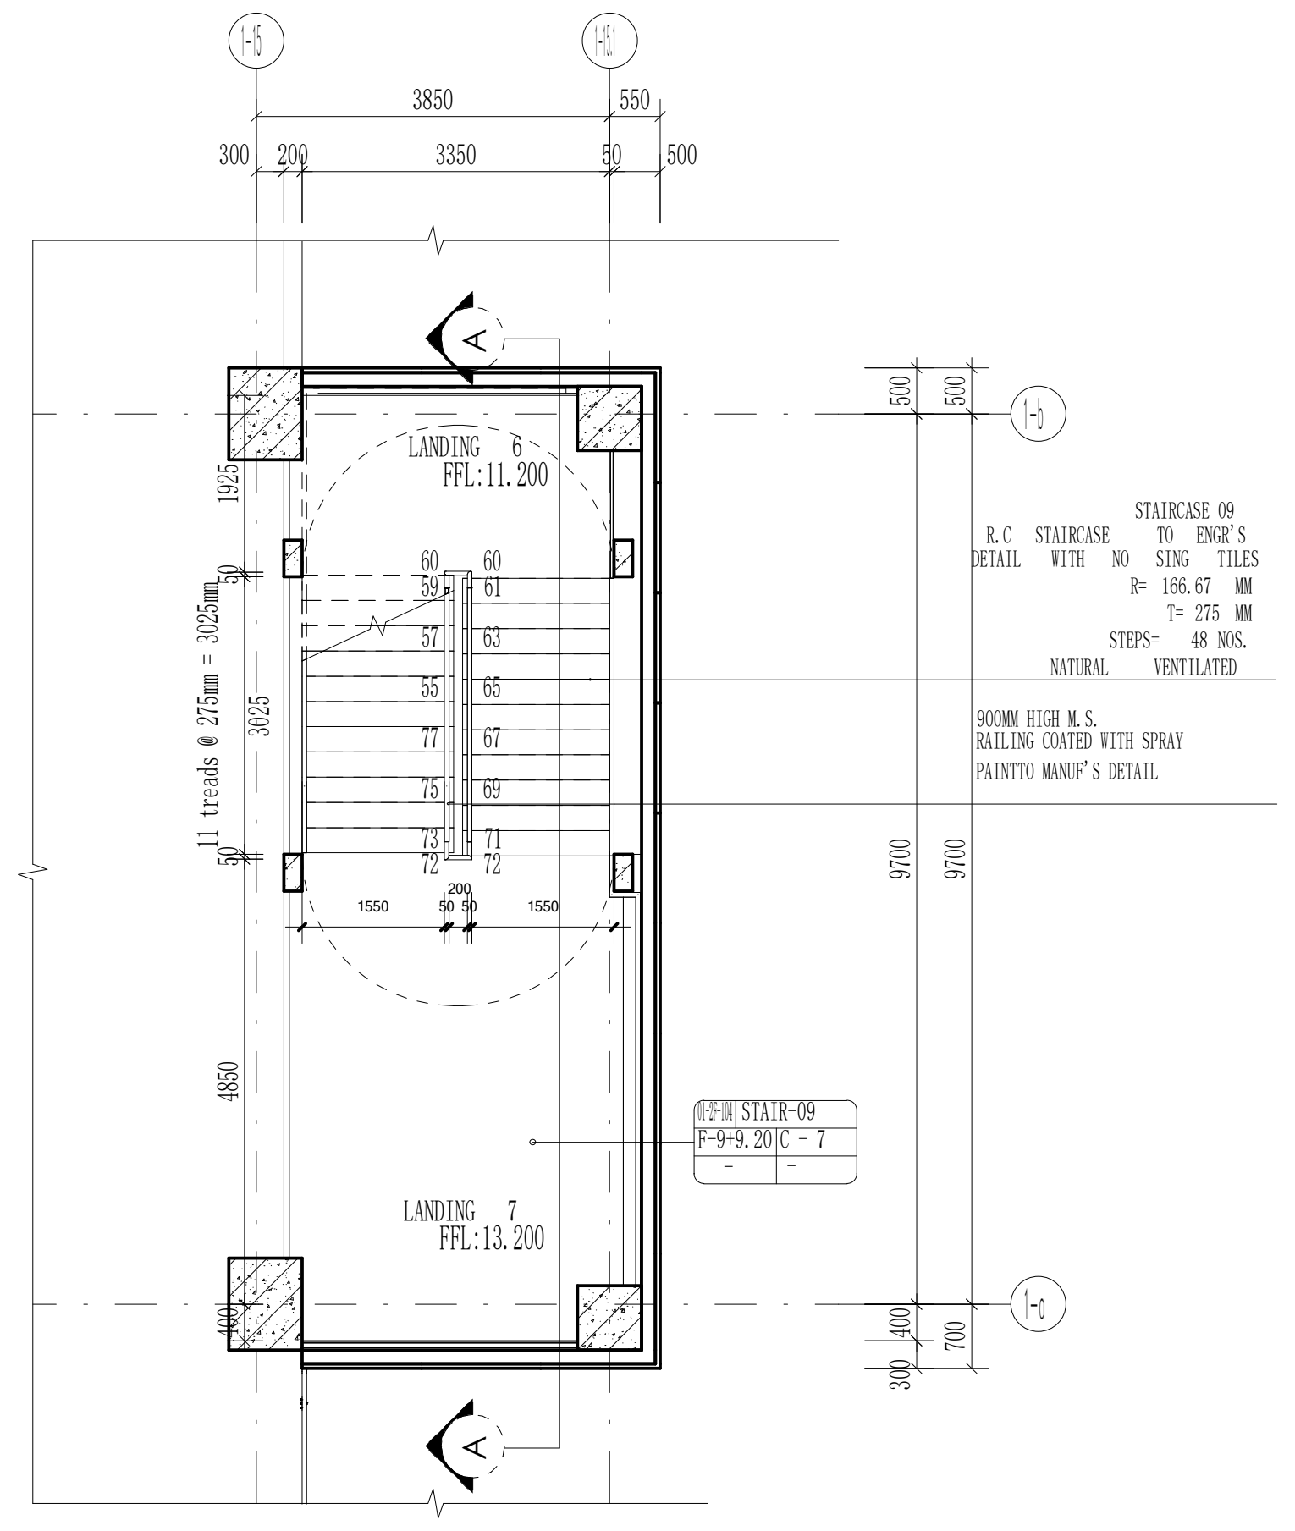

3850
3350
LANDING 6
FFL:11.200
LANDING 7
FFL:13.200
11 treads @ 275mm = 3025mm
STAIRCASE 09
R.C STAIRCASE TO ENGR'S
DETAIL WITH NO SING TILES
R= 166.67 MM
T= 275 MM
STEPS= 48 NOS.
NATURAL VENTILATED
900MM HIGH M.S.
RAILING COATED WITH SPRAY
PAINTTO MANUF'S DETAIL
9700

STAIR-9 13.200 ELEVATION PLAN FL
SCALE 1:75

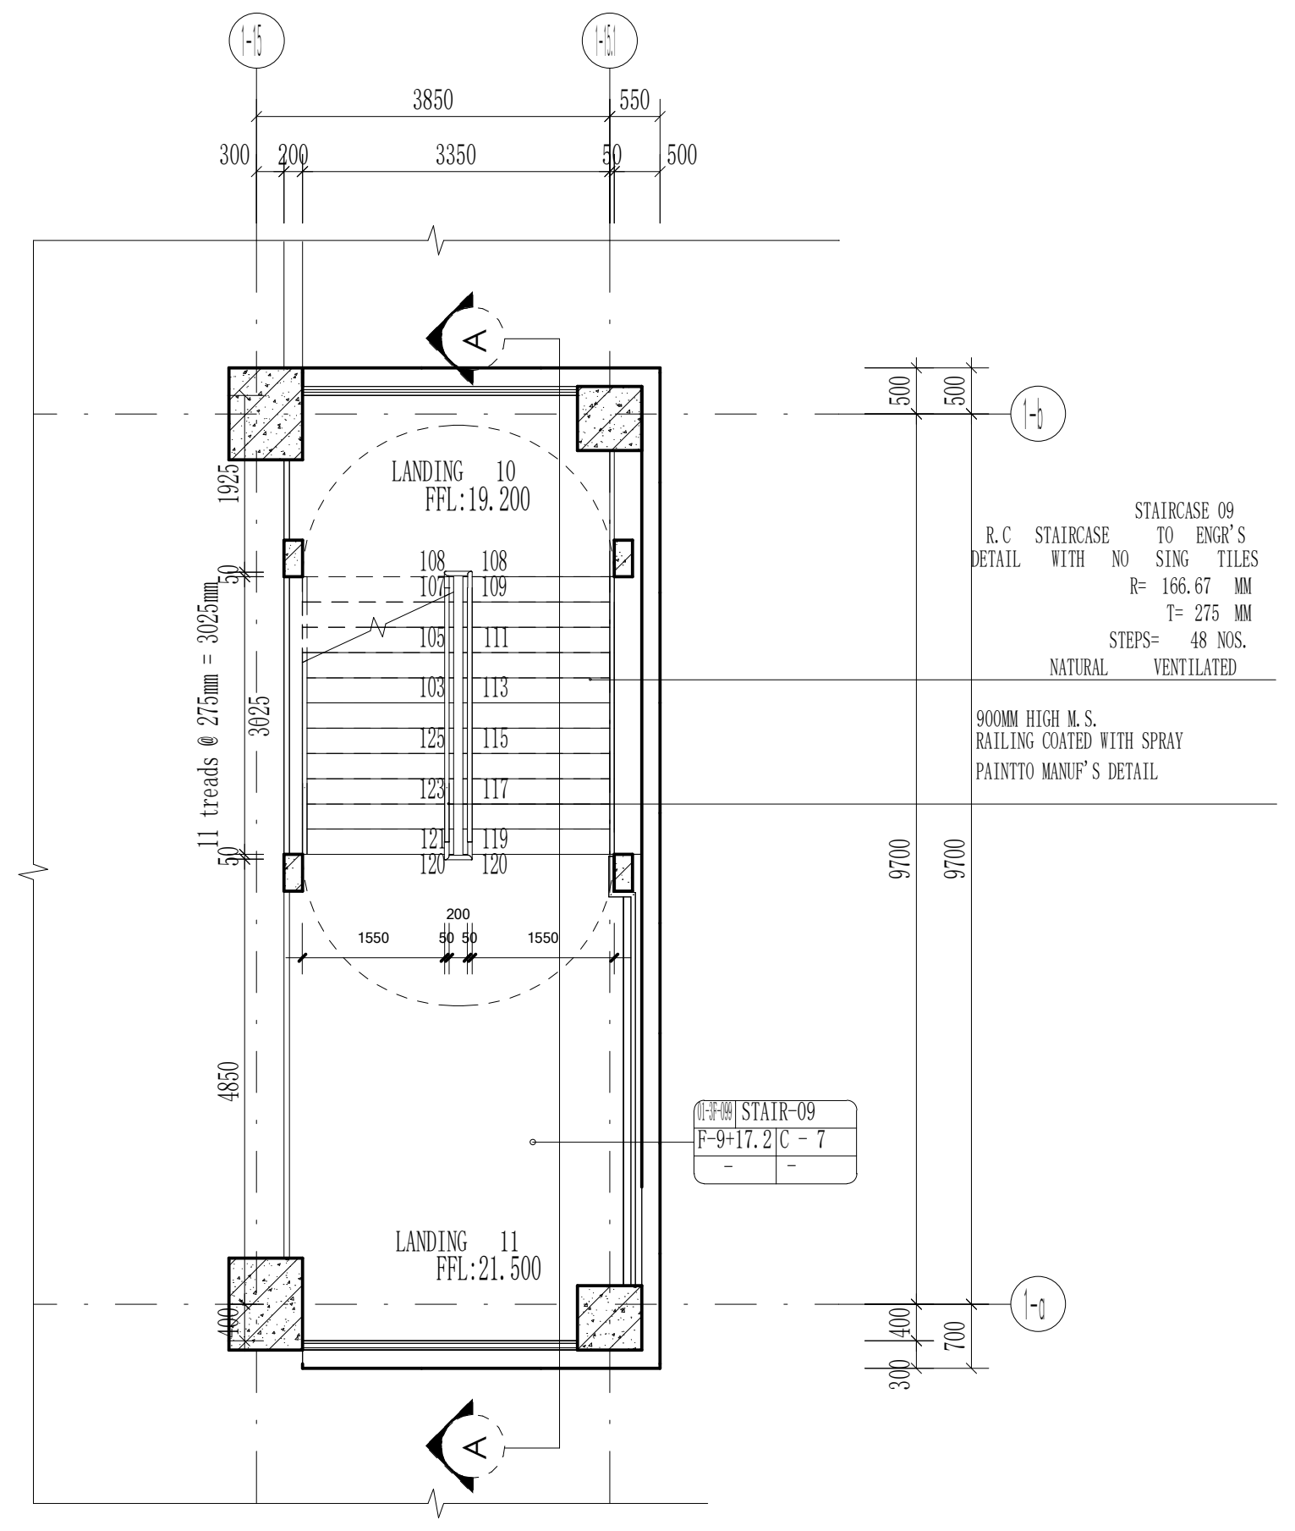

3850
3350
LANDING 10
FFL:19.200
LANDING 11
FFL:21.500
11 treads @ 275mm = 3025mm
STAIRCASE 09
R.C STAIRCASE TO ENGR'S
DETAIL WITH NO SING TILES
R= 166.67 MM
T= 275 MM
STEPS= 48 NOS.
NATURAL VENTILATED
900MM HIGH M.S.
RAILING COATED WITH SPRAY
PAINTTO MANUF'S DETAIL
9700

STAIR-9 21.500 ELEVATION PLAN FL
SCALE 1:75

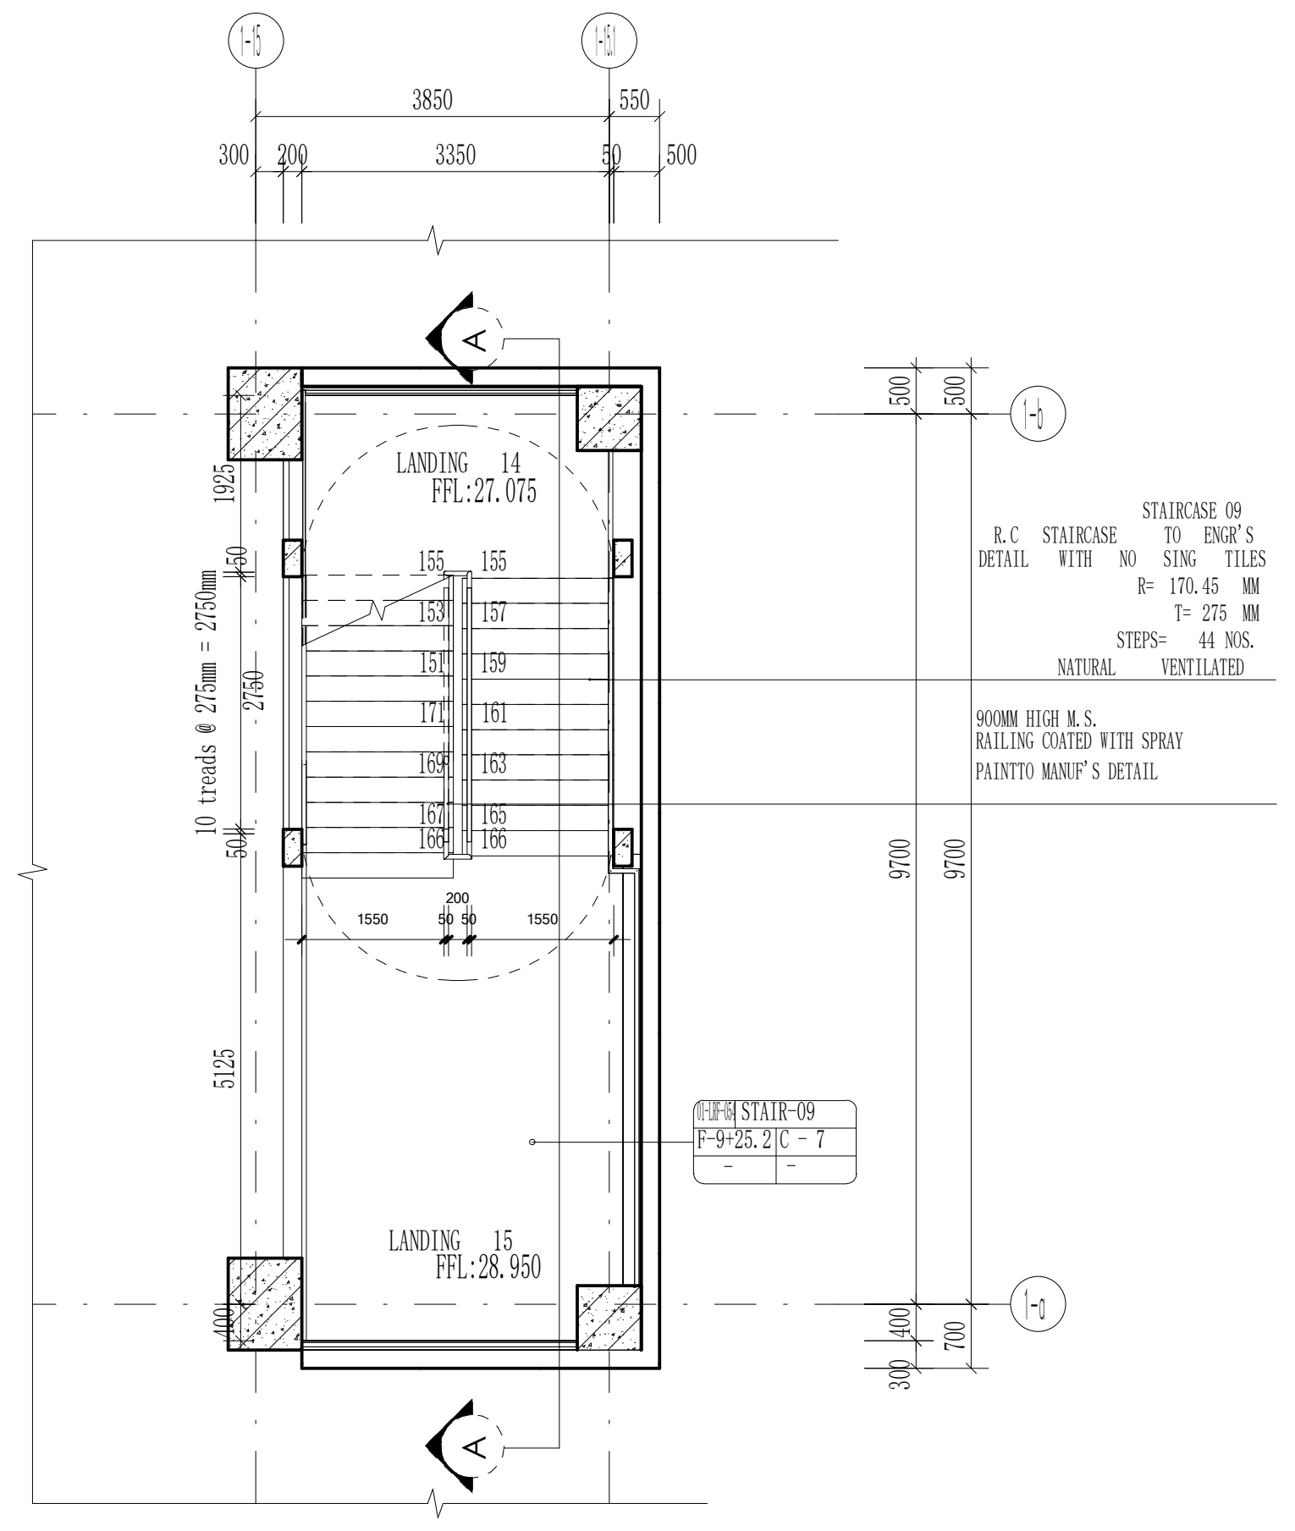

3850
3350
LANDING 14
FFL:27.075
LANDING 15
FFL:28.950
10 treads @ 275mm = 2750mm
STAIRCASE 09
R.C STAIRCASE TO ENGR'S
DETAIL WITH NO SING TILES
R= 170.45 MM
T= 275 MM
STEPS= 44 NOS.
NATURAL VENTILATED
900MM HIGH M.S.
RAILING COATED WITH SPRAY
PAINTTO MANUF'S DETAIL
9700

STAIR-9 28.950 ELEVATION PLANFL
SCALE 1:75

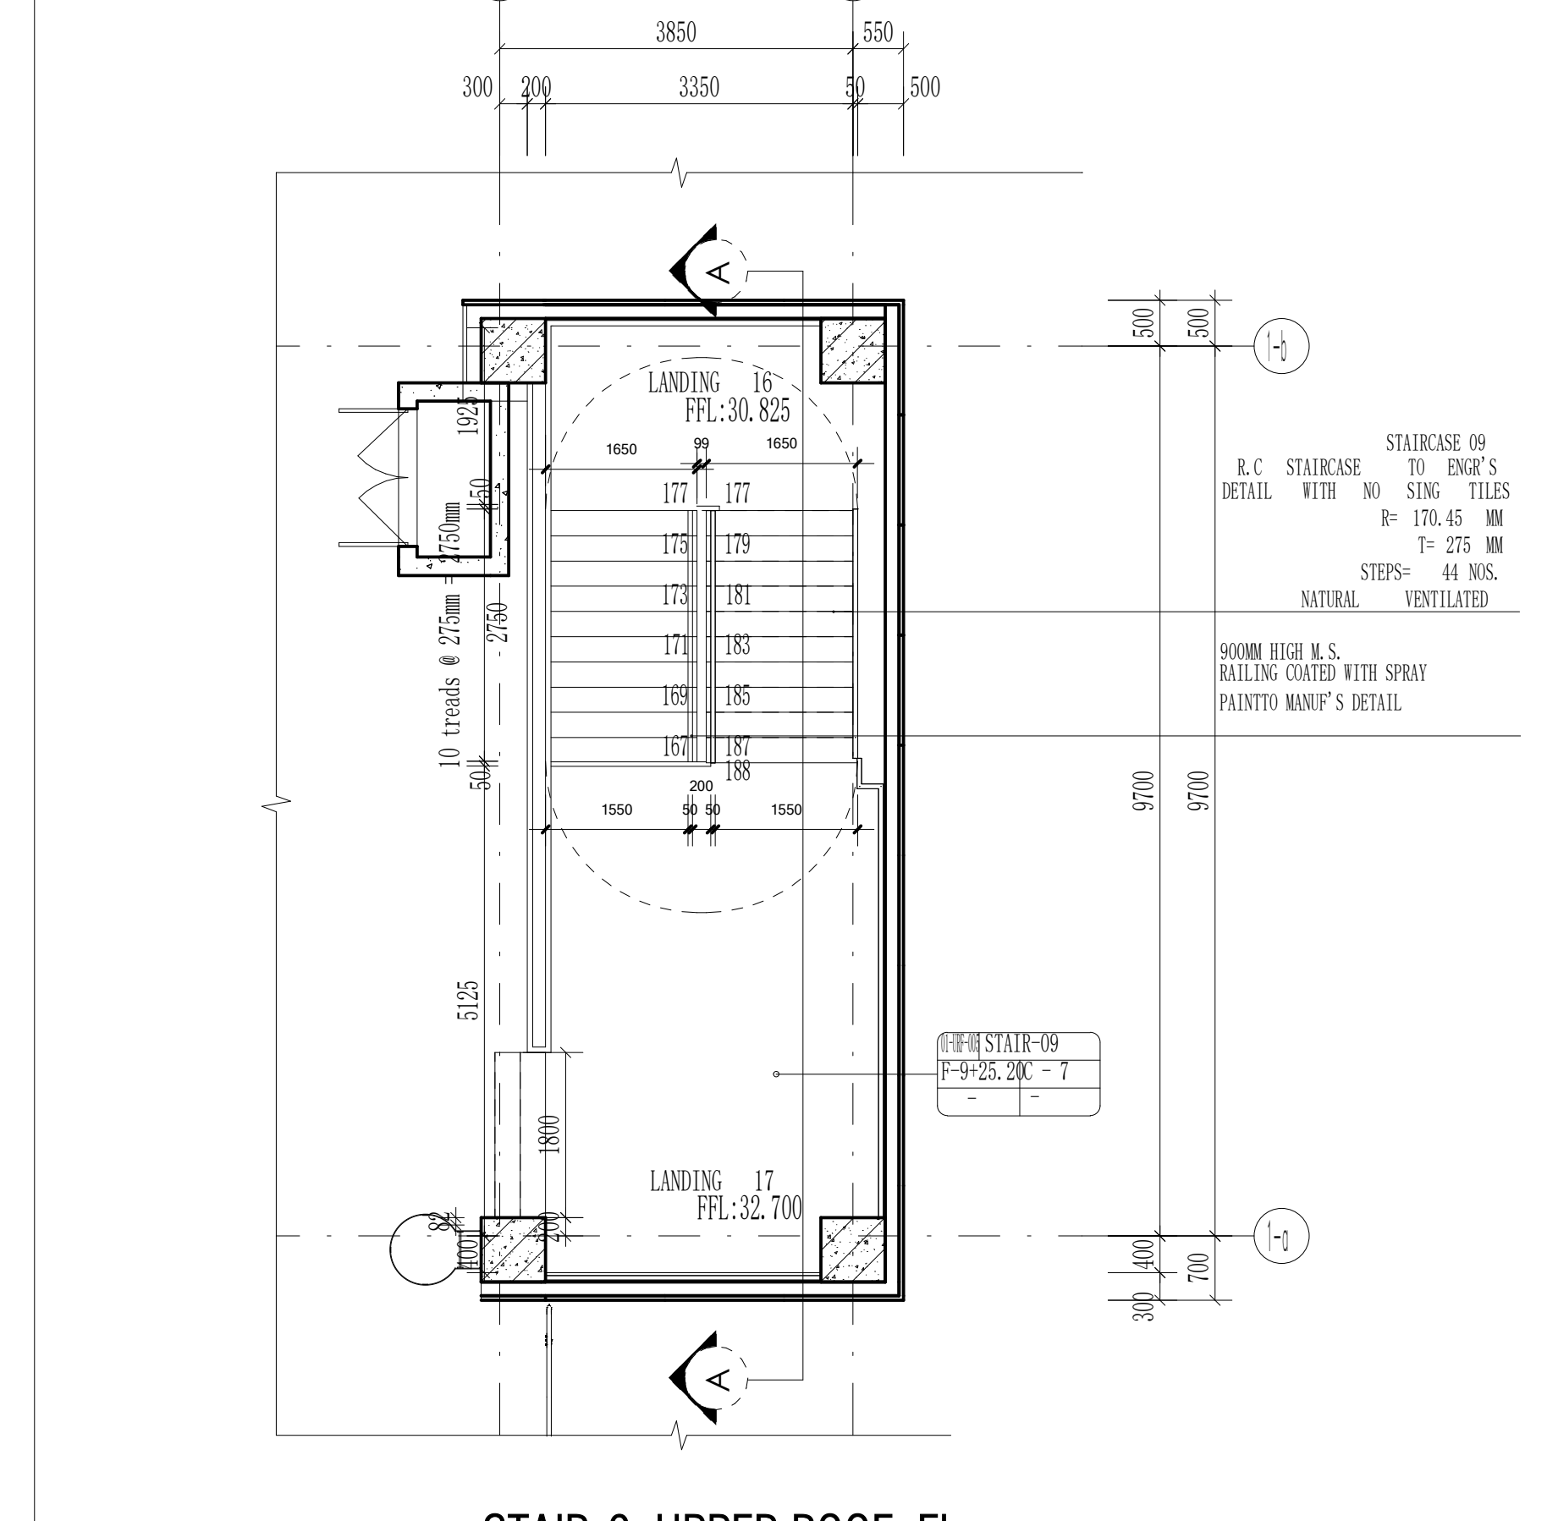

3850
3350
LANDING 16
FFL:30.825
LANDING 17
FFL:32.700
10 treads @ 275mm = 2750mm
STAIRCASE 09
R.C STAIRCASE TO ENGR'S
DETAIL WITH NO SING TILES
R= 170.45 MM
T= 275 MM
STEPS= 44 NOS.
NATURAL VENTILATED
900MM HIGH M.S.
RAILING COATED WITH SPRAY
PAINTTO MANUF'S DETAIL
9700

STAIR-9 UPPER ROOF FL
SCALE 1:75

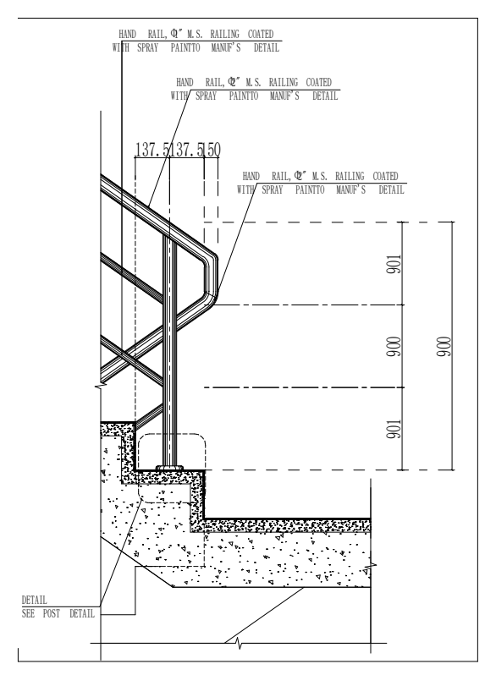

HAND RAIL, Φ1" M.S. RAILING COATED WITH SPRAY PAINTTO MANUF'S DETAIL
HAND RAIL, Φ2" M.S. RAILING COATED WITH SPRAY PAINTTO MANUF'S DETAIL
HAND RAIL, Φ2" M.S. RAILING COATED WITH SPRAY PAINTTO MANUF'S DETAIL
137.5
137.5
50
901
900
900
901
DETAIL
SEE POST DETAIL

HANDRAIL DETAILS
SCALE
1:75

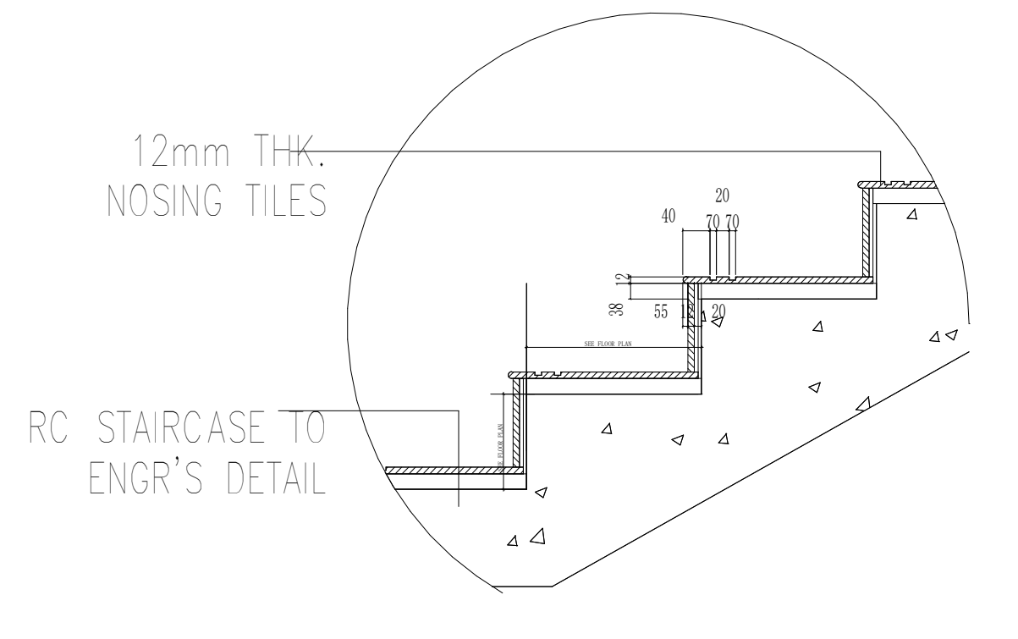

12mm THK.
NOSING TILES
RC STAIRCASE TO
ENGR'S DETAIL
20
40
70
70
12
38
55
20

STEP DETAILS
SCALE
1:75

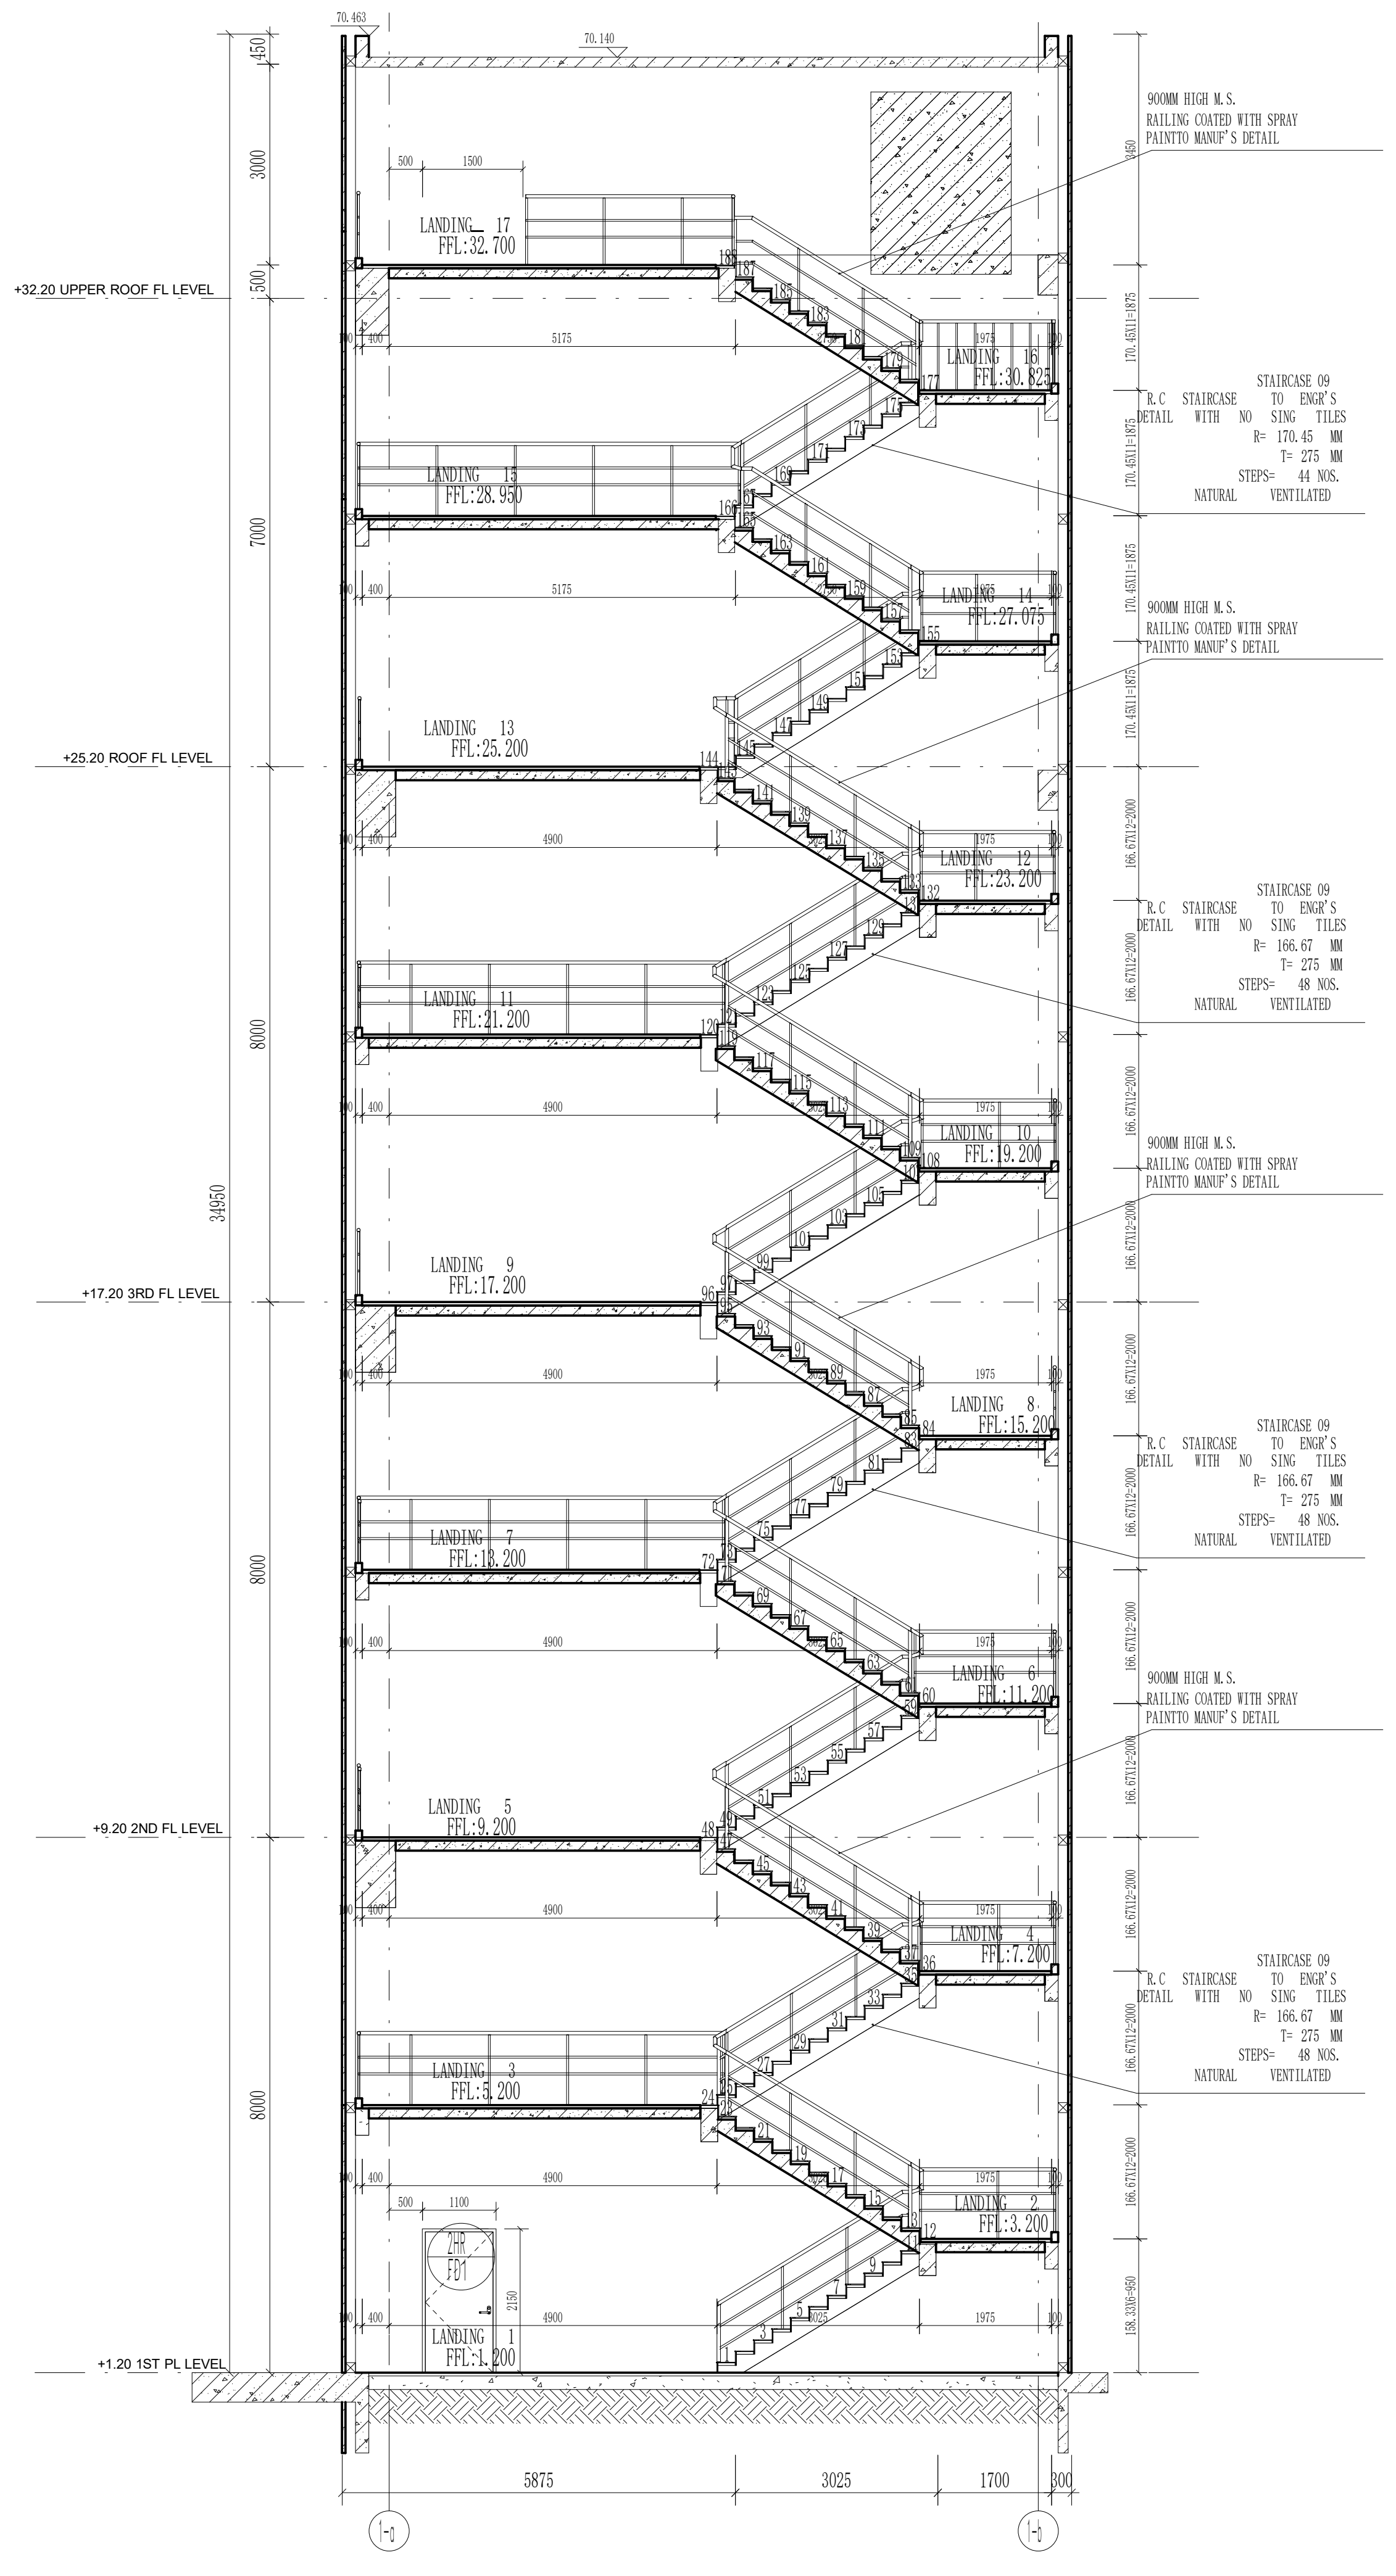

70.463
70.140
+32.20 UPPER ROOF FL LEVEL
+25.20 ROOF FL LEVEL
+17.20 3RD FL LEVEL
+9.20 2ND FL LEVEL
+1.20 1ST PL LEVEL
LANDING 17
FFL:32.700
LANDING 16
FFL:30.825
LANDING 15
FFL:28.950
LANDING 14
FFL:27.075
LANDING 13
FFL:25.200
LANDING 12
FFL:23.200
LANDING 11
FFL:21.200
LANDING 10
FFL:19.200
LANDING 9
FFL:17.200
LANDING 8
FFL:15.200
LANDING 7
FFL:13.200
LANDING 6
FFL:11.200
LANDING 5
FFL:9.200
LANDING 4
FFL:7.200
LANDING 3
FFL:5.200
LANDING 2
FFL:3.200
LANDING 1
FFL:1.200
2HR
FD1
900MM HIGH M.S.
RAILING COATED WITH SPRAY
PAINTTO MANUF'S DETAIL
STAIRCASE 09
R.C STAIRCASE TO ENGR'S
DETAIL WITH NO SING TILES
R= 170.45 MM
T= 275 MM
STEPS= 44 NOS.
NATURAL VENTILATED
STAIRCASE 09
R.C STAIRCASE TO ENGR'S
DETAIL WITH NO SING TILES
R= 166.67 MM
T= 275 MM
STEPS= 48 NOS.
NATURAL VENTILATED
450
3000
500
7000
8000
8000
34950
5175
4900
1975
170.45X11=1875
166.67X12=2000
158.33X6=950
5875
3025
1700
300
1-a
1-b

Section A
SCALE 1:75

NOTE :THIS PRINT IS OF A CONFIDENTIAL NATURE, IT SHALL NOT BE TRACED,PHOTOSTATED OR REPRODUCED IN ANY MANER,NOR USED FOR ANY PURPOSE WHATSOEVER EXCEPT BY WRITTEN PERMISSION

CLIENT :

GULF EDGE DC 01

87 Wireless Road, M Thai Tower 11th. Floor, All Seasons Place, Lumpini,
Pathumwan, Bangkok 10330, Thailand

CONTRACTOR :

华西发展(泰国)有限公司
บริษัท หัวซือ ดีเวลลอปเม้นต์ (ประเทศไทย) จำกัด
HUASHI DEVELOPMENT CO.,LTD
No. 202, Room No. 1403, 14/F, Le Concorde Building,
Ratchadapisek Road, Huaykhwang Sub-District,
Huaykhwang District, Bangkok Metropolitan 10310.

CONSULTANT :

ARbay
บริษัท เอ อาร์ เบย์ จำกัด
ARbay Company Limited
31 st Floor Bangkok Insurance Building
25 South Sathorn road Thungmahamek
Sathorn Bangkok 10120 THAILAND
T +66 (0) 2286 8199
F +66 (0) 2286 2863
info@arbay.co.th

CONSULTANT :

Qbic Engineers & Architects Co.,Ltd.
8 Soi KALONG 4 SANAMBINNAM ROAD,
THASAI SUB-DISTRICT, MUANG NONTHABURI DISTRICT
, NONTHABURI.
Tel 662-950-4374
Fax 662-580-3231
E-Mail : qbic@qbic.co.th, www.qbic.co.th
QBIC ENGINEERS AND ARCHITECTS CO.,LTD.

CONSULTANT :

MITR
MITR TECHNICAL CONSULTANT CO.,LTD.
1168/8 12th FLOOR, LUMPINI TOWER BUILDING,
RAMA IV RD., THUNGMAHAMEK, SATHORN, BANGKOK 10120, THAILAND
TEL : 0-2679-9079-84
FAX : 0-2679-9085 E-mail: mitr_dd@mitr.com

Architect :	SIGNATURE
ประกิต พนานุรัตน์ วสถ. 580 ที่อยู่ 251/1 ถ.จารุเมือง แขวงรองเมือง เขตปทุมวัน กรุงเทพมหานคร โทรศัพท์ 02-286-8199	
Structural Engineer :	SIGNATURE
วิศวกรผู้ออกแบบโครงสร้าง	
ณัฐสม สงวนวงษ์ วย 1423 ที่อยู่ 2/1 ซ.รามคำแหง 150 ถ.รามคำแหง แขวง สะพานสูง เขต สะพานสูง กทม. 10240	ณัฐสม สงวนวงษ์
Structural Inspector :	SIGNATURE
วิศวกรผู้ตรวจสอบโครงสร้าง	
โกมล จุฑาภัทร วย 964 ที่อยู่ 24/18 ซ.นวมินทร์ 129 ถ. นวมินทร์ แขวง นวลจันทร์ เขต บึงกุ่ม กทม. 10230	
Electrical Engineer :	SIGNATURE
วิศวกรผู้ออกแบบระบบไฟฟ้ากำลัง	
นายสุภัทร บูรณวิทย์ วฟก.1265 ที่อยู่ 21 ซอยทานสัมฤทธิ์ 13 ตำบลท่าทราย อ.เมืองนนทบุรี จ.นนทบุรี 11000	
Mechanical Engineer :	SIGNATURE
วิศวกรผู้ออกแบบระบบเครื่องกลและปรับอากาศ	
นายประสิทธิ์ เกี๋ยวสุนทร วก.1221 ที่อยู่ 44/372 ซอยบางกระดี่ 35/1 แขวงแสมดำ เขตบางขุนเทียน กทม. 10150	ประสิทธิ์
Sanitary Engineer :	SIGNATURE
วิศวกรผู้ออกแบบระบบสุขาภิบาล และดับเพลิง	
นายทศวรรษ สนั่นฤทธิ์ วส. 215 ที่อยู่ บ้านเลขที่ 99/107 หมู่ที่ 3 ต.ศีรษะจรเข้น้อย อ.บางเสาธง จ.สมุทรปราการ 10540	ทศวรรษ

ISSUE/REVISION

REV.	DESCRIPTION	DATE
A	90% DEVELOPED	09/05/2026

PROJECT NAME :

GEDC 01

LOCATION:
Nikhom Phattana district, Rayong ,industrial estate,CPGC

BUILDING :
MAIN BUILDING

90% DEVELOPED

TITLE :

STAIRCASE 09

JOB NO.	SCALE 1 : 75
DRAWN LW	REF.
CHECKED LJC	DWG. NO.
APPROVED LXD	MPK01A-90-A-ST-009
DATE 2026.05.09	