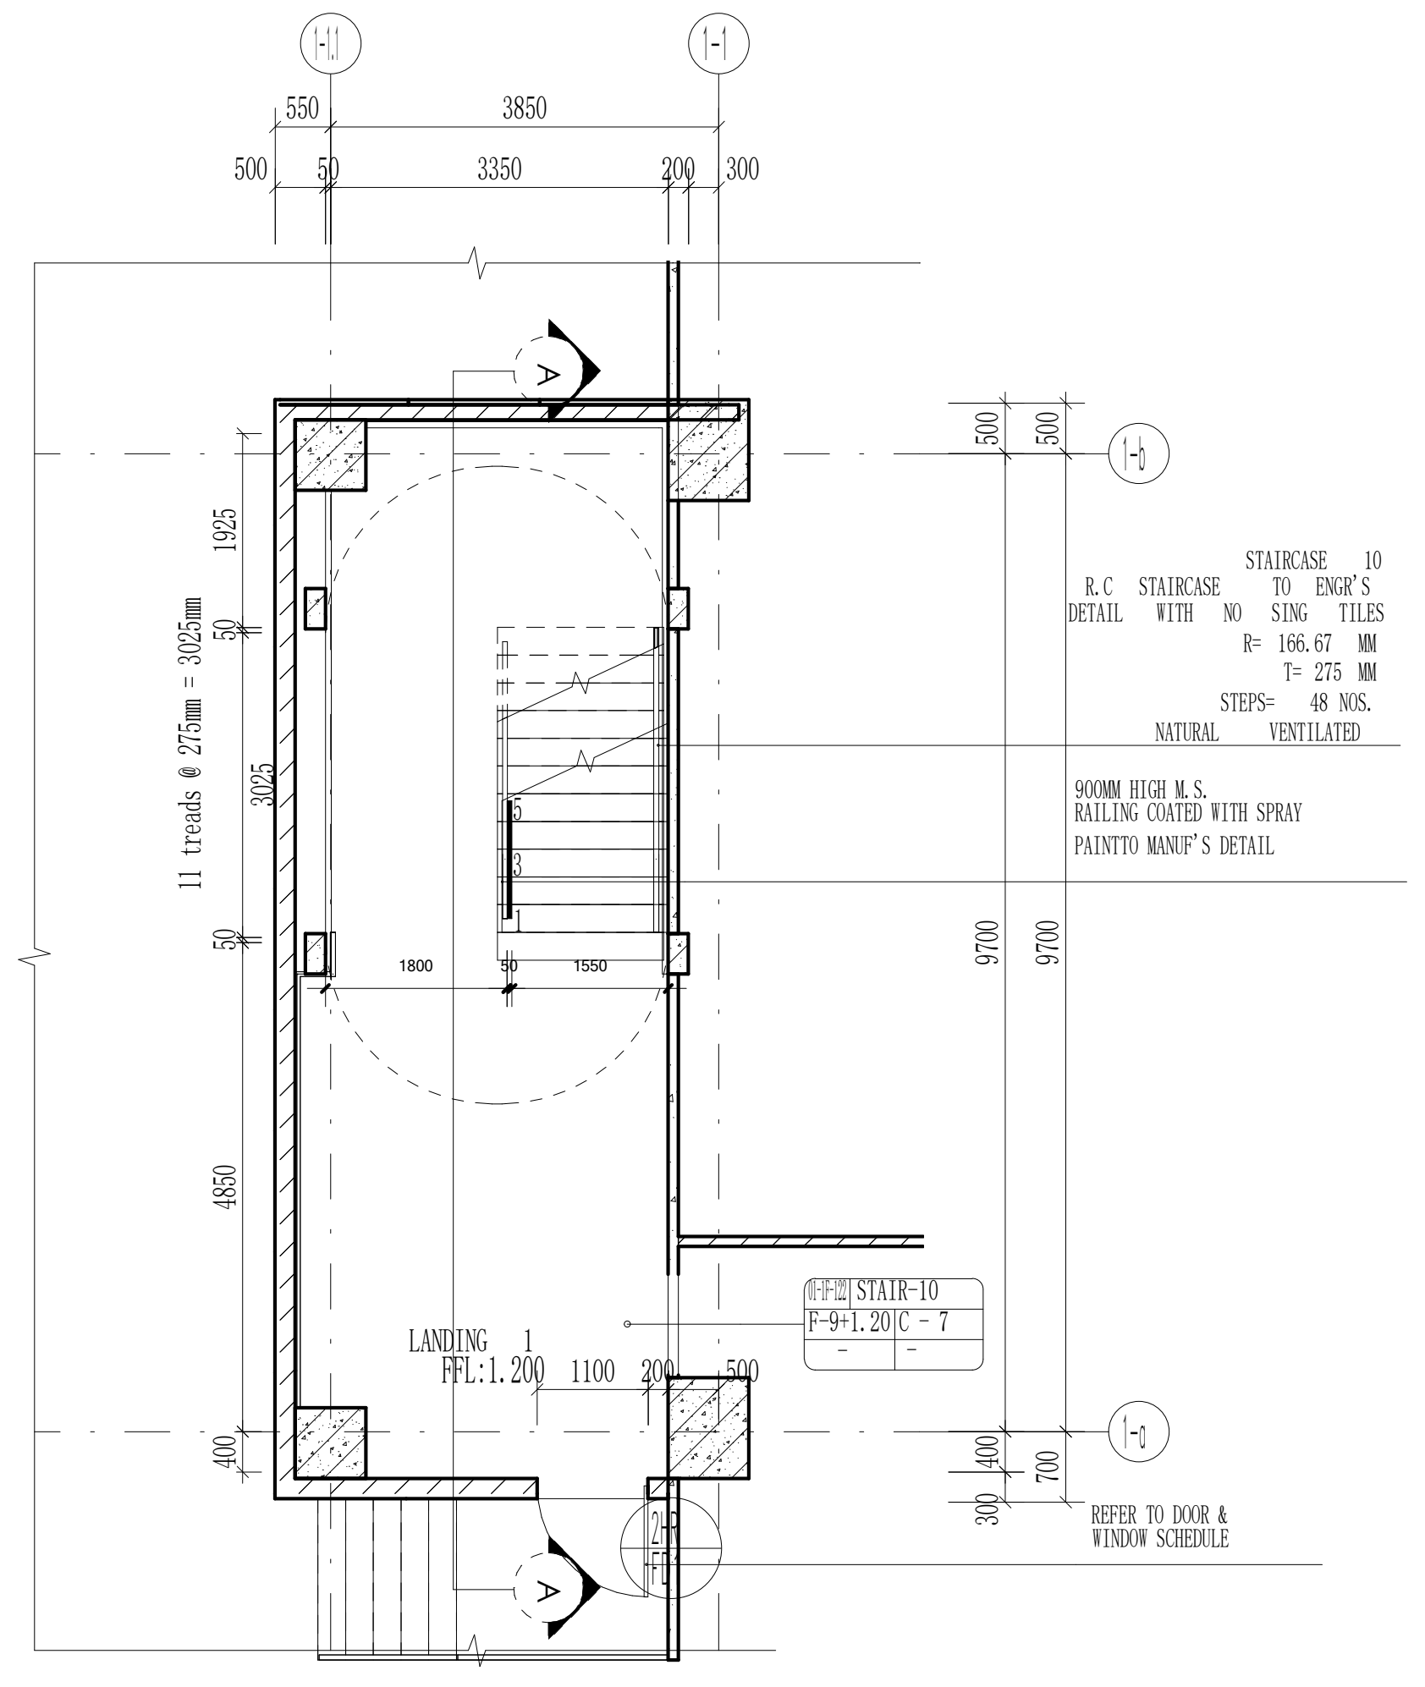

STAIR-10 GROUND FL
SCALE 1:75

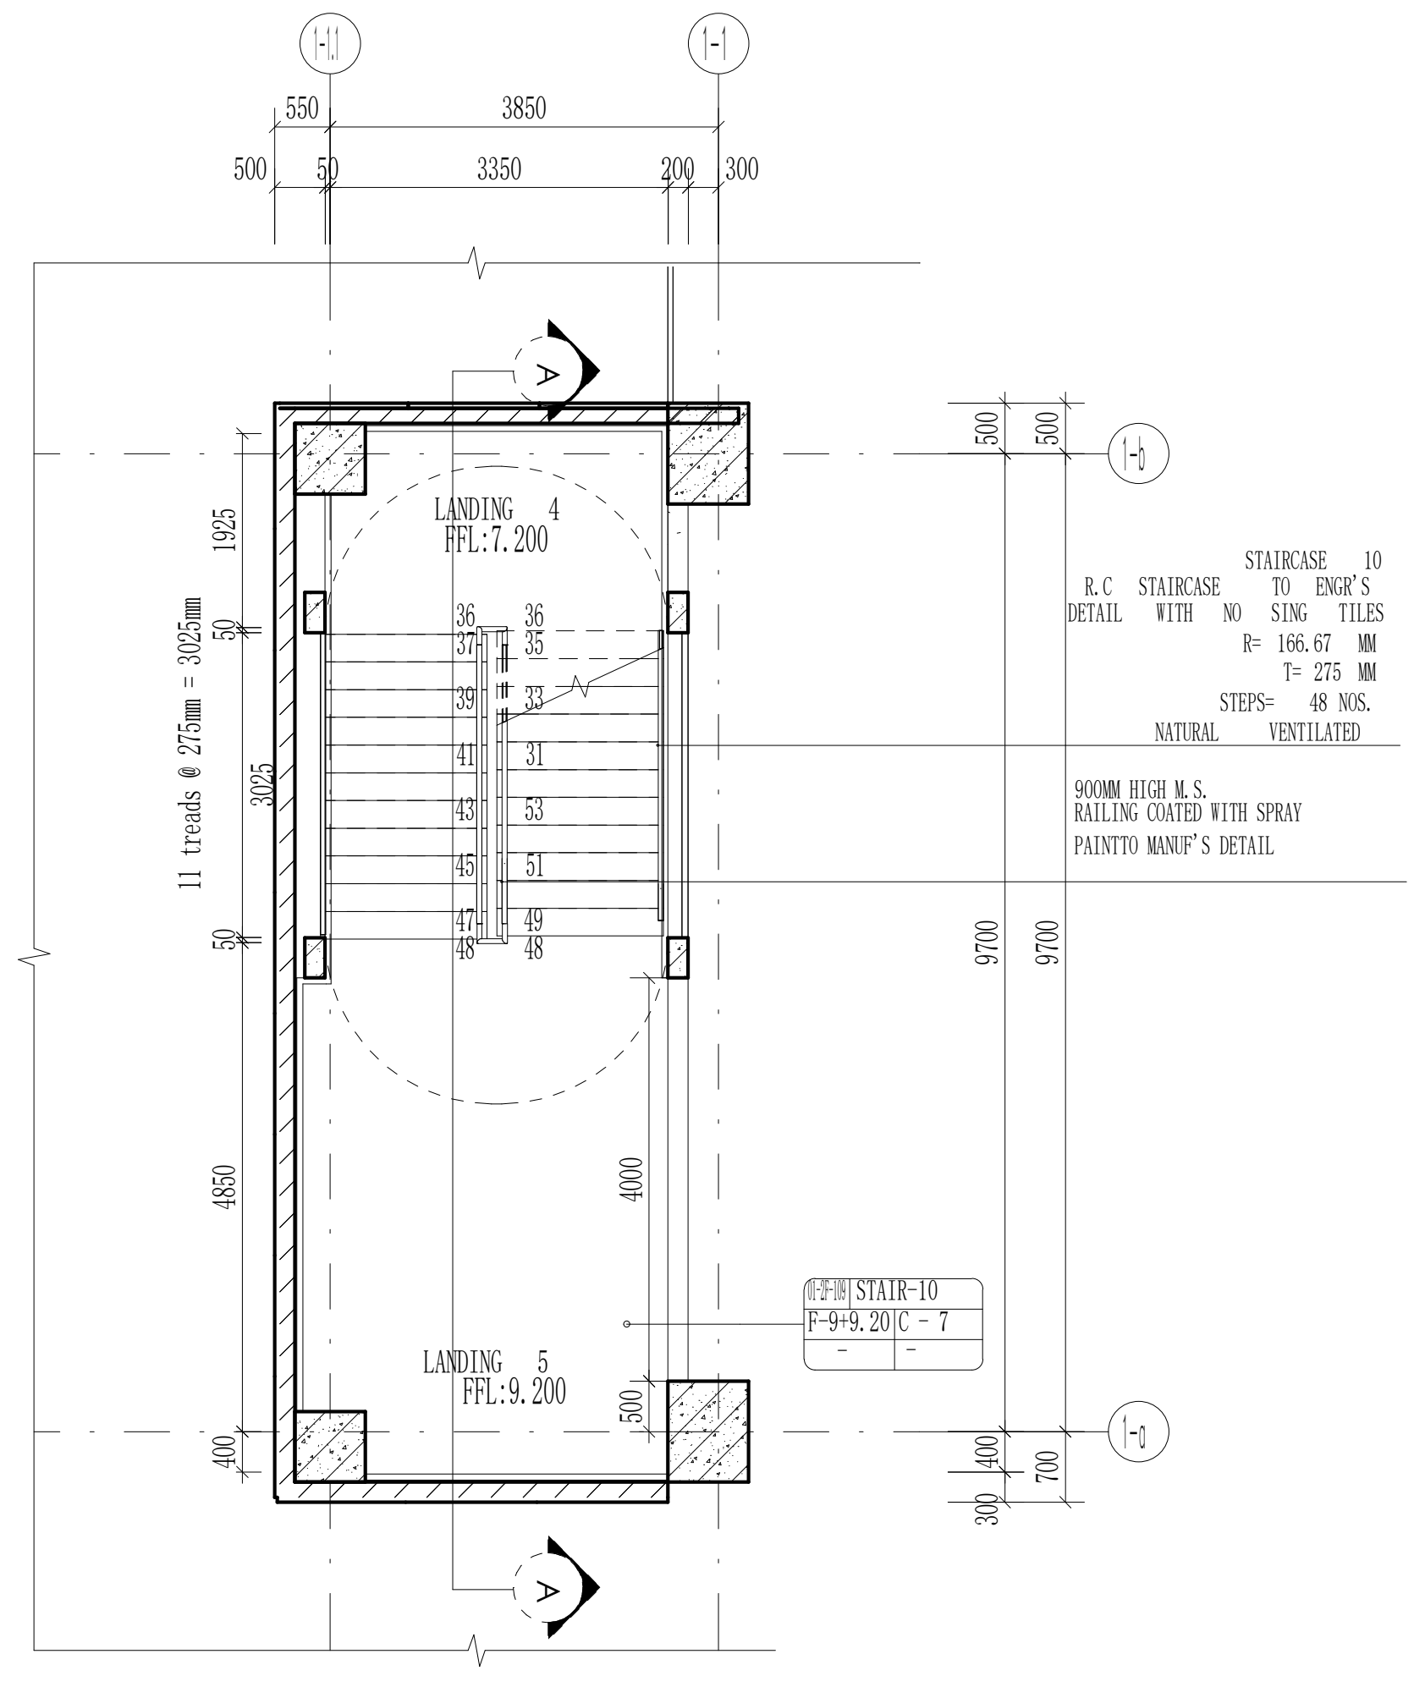

STAIR-10 2ND FL
SCALE 1:75

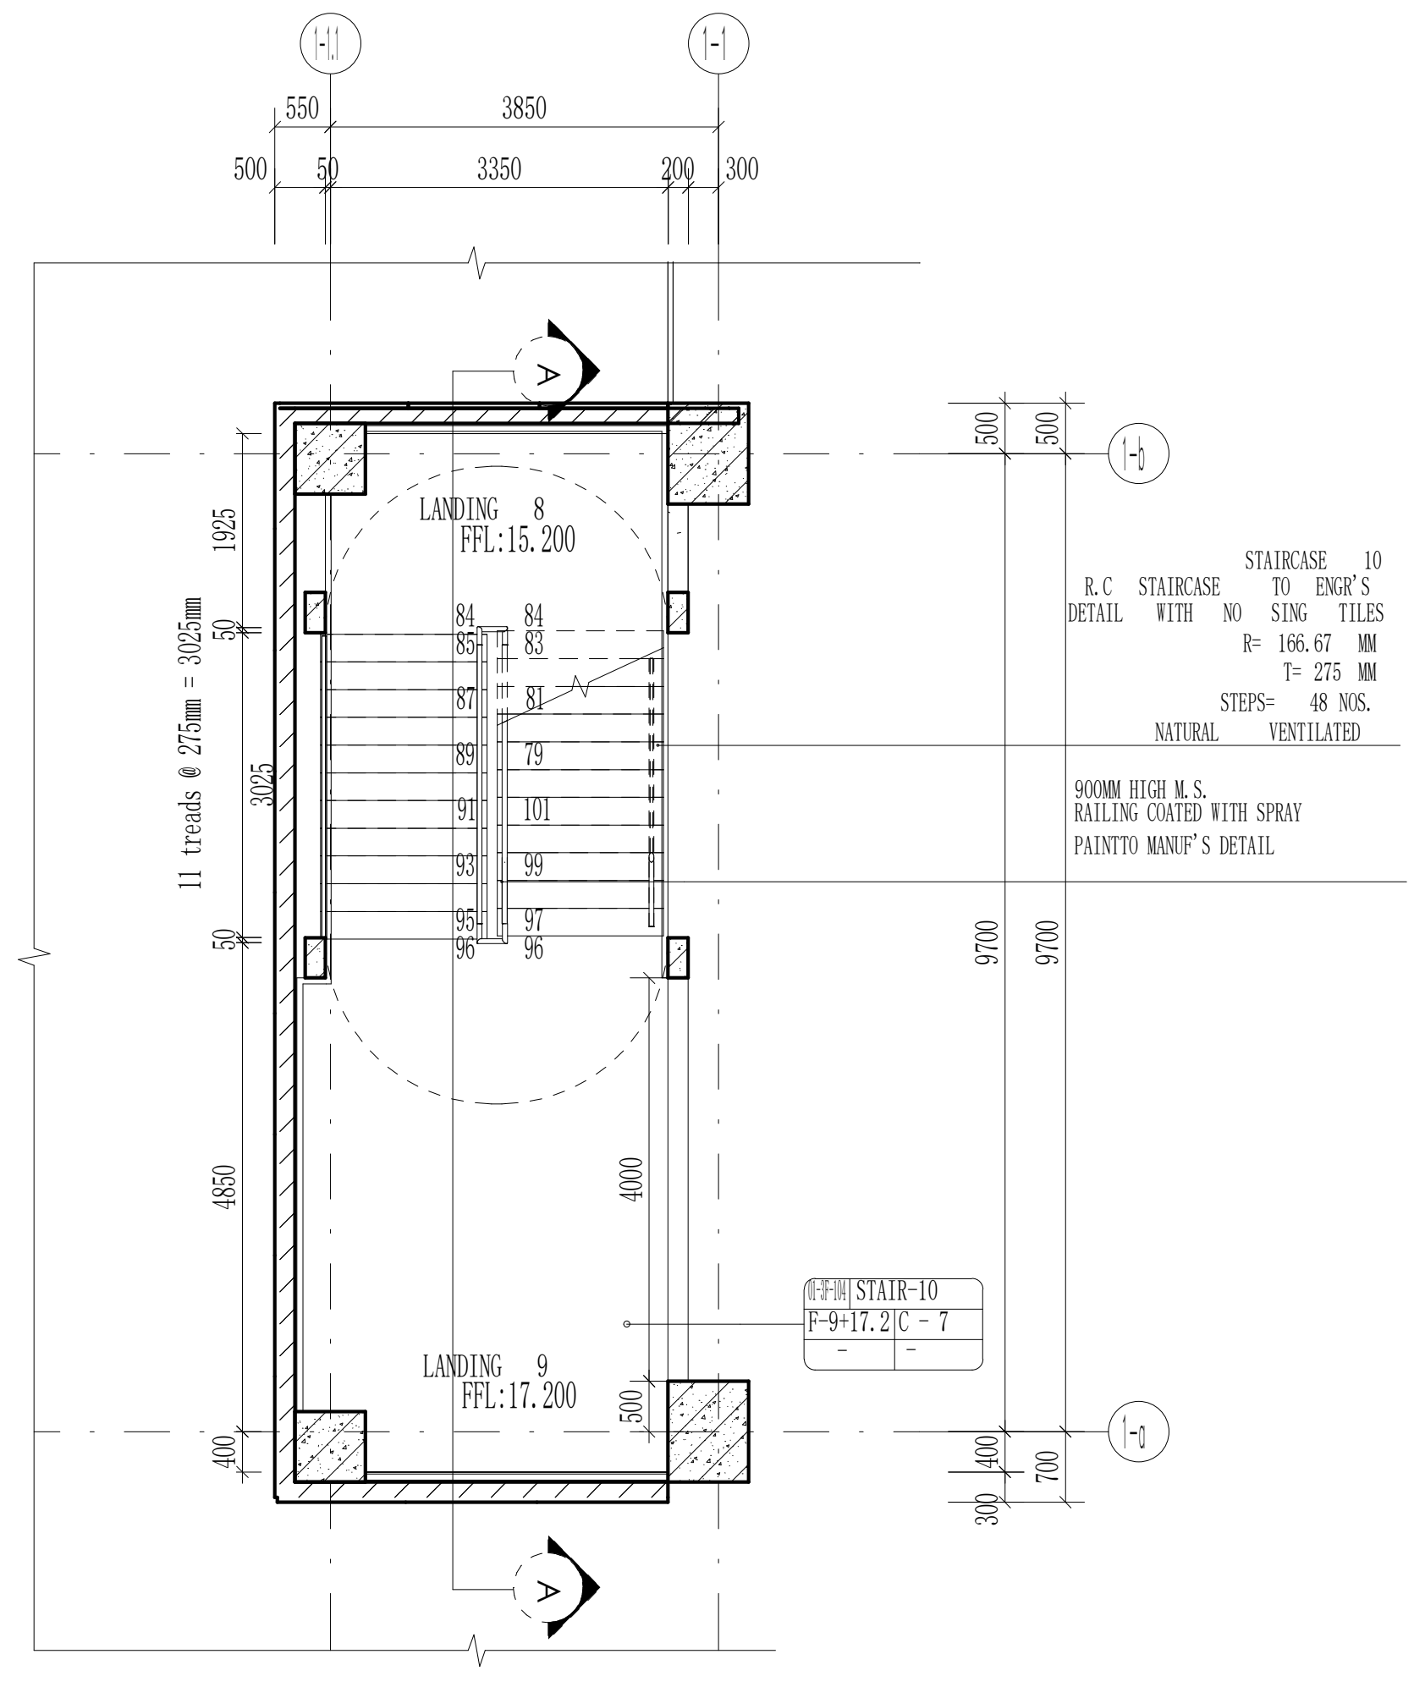

STAIR-10 3RD FL
SCALE 1:75

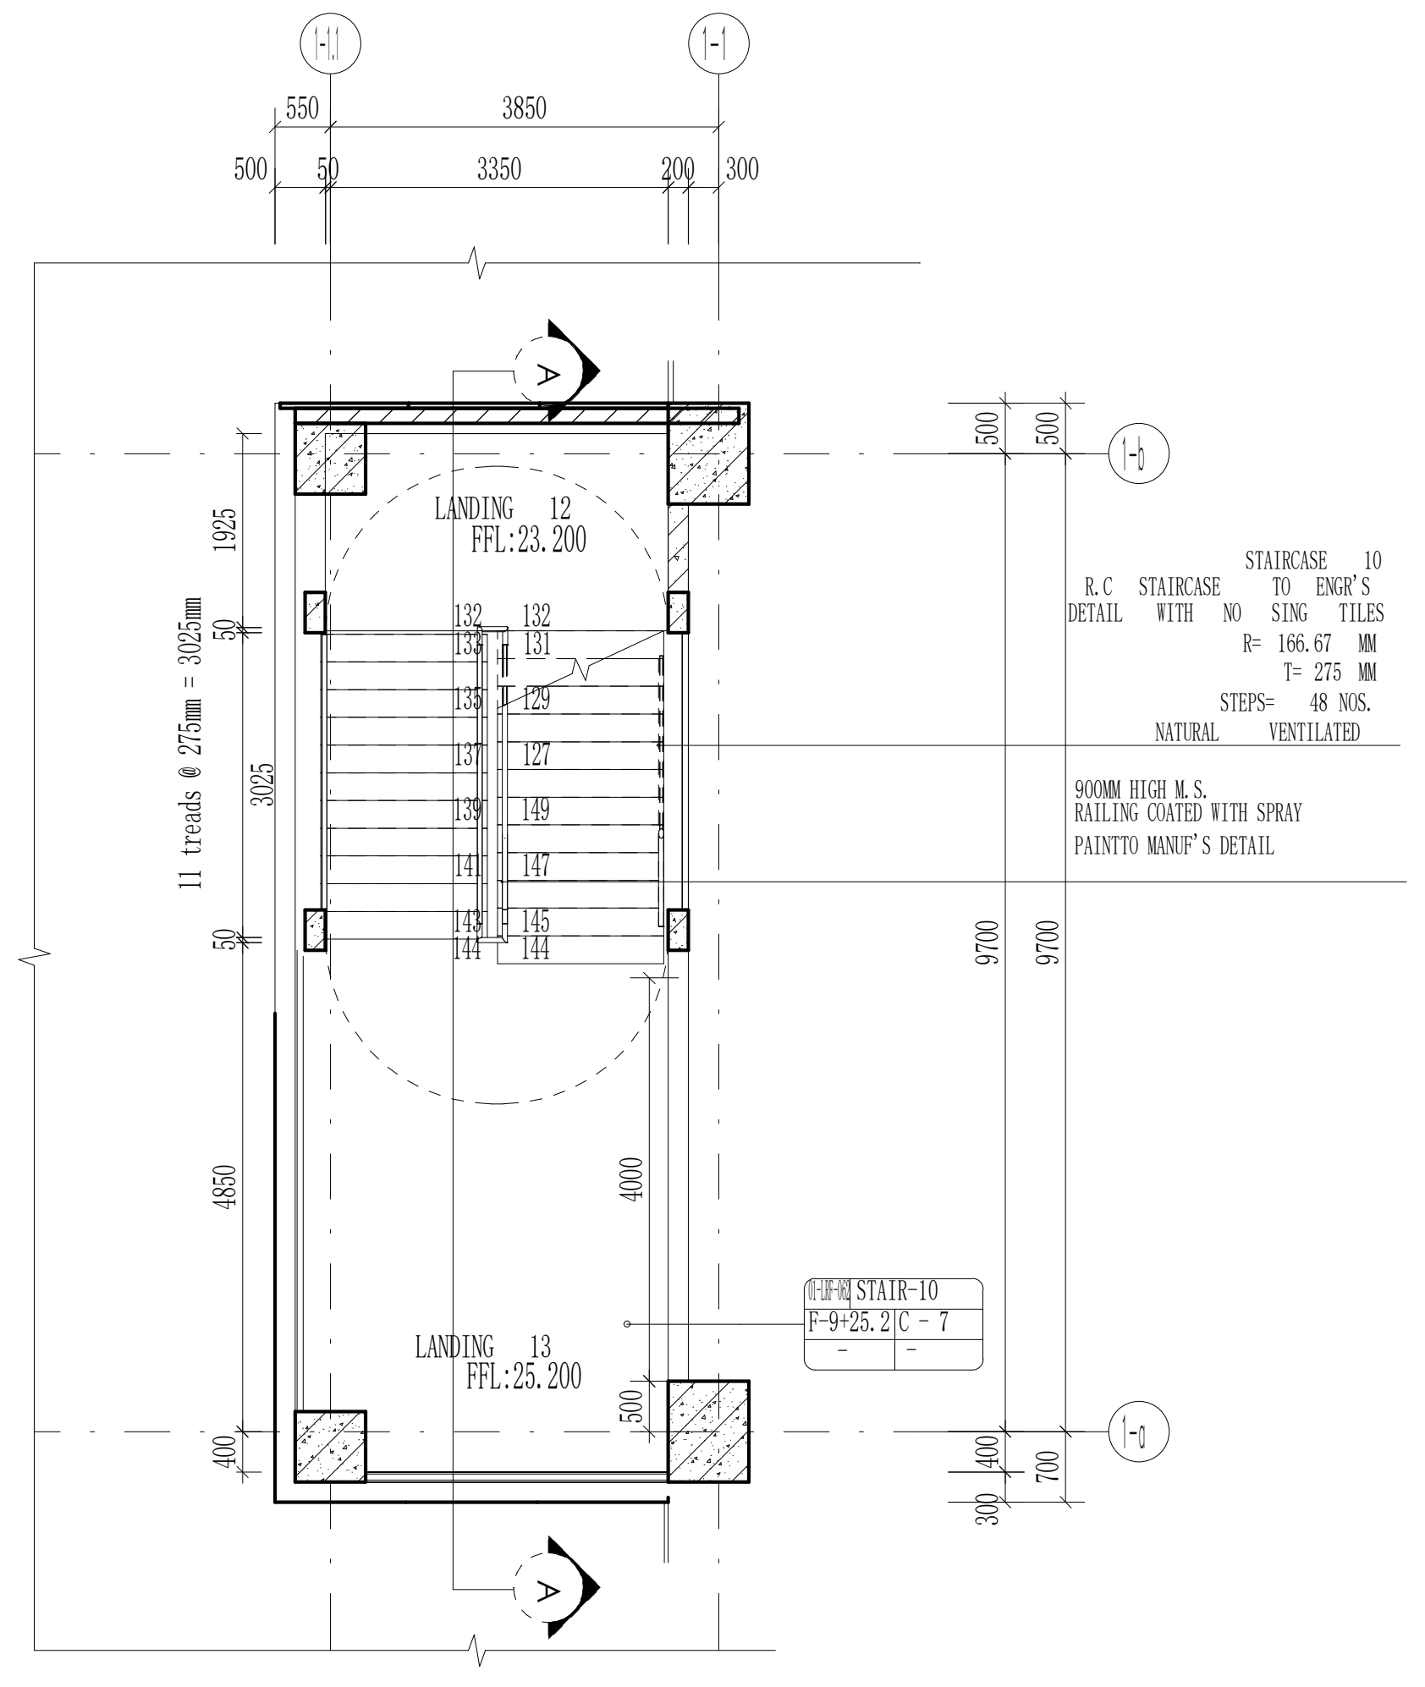
LANDING 12
FFL:23.200
LANDING 13
FFL:25.200
STAIRCASE 10
R.C STAIRCASE TO ENGR'S DETAIL WITH NO SING TILES
T= 275 MM
NATURAL VENTILATED
900MM HIGH M.S. RAILING COATED WITH SPRAY PAINTTO MANUF'S DETAIL
STAIR-10
F-9+25.20 C - 7
A

STAIR-10 ROOF FL
SCALE 1:75

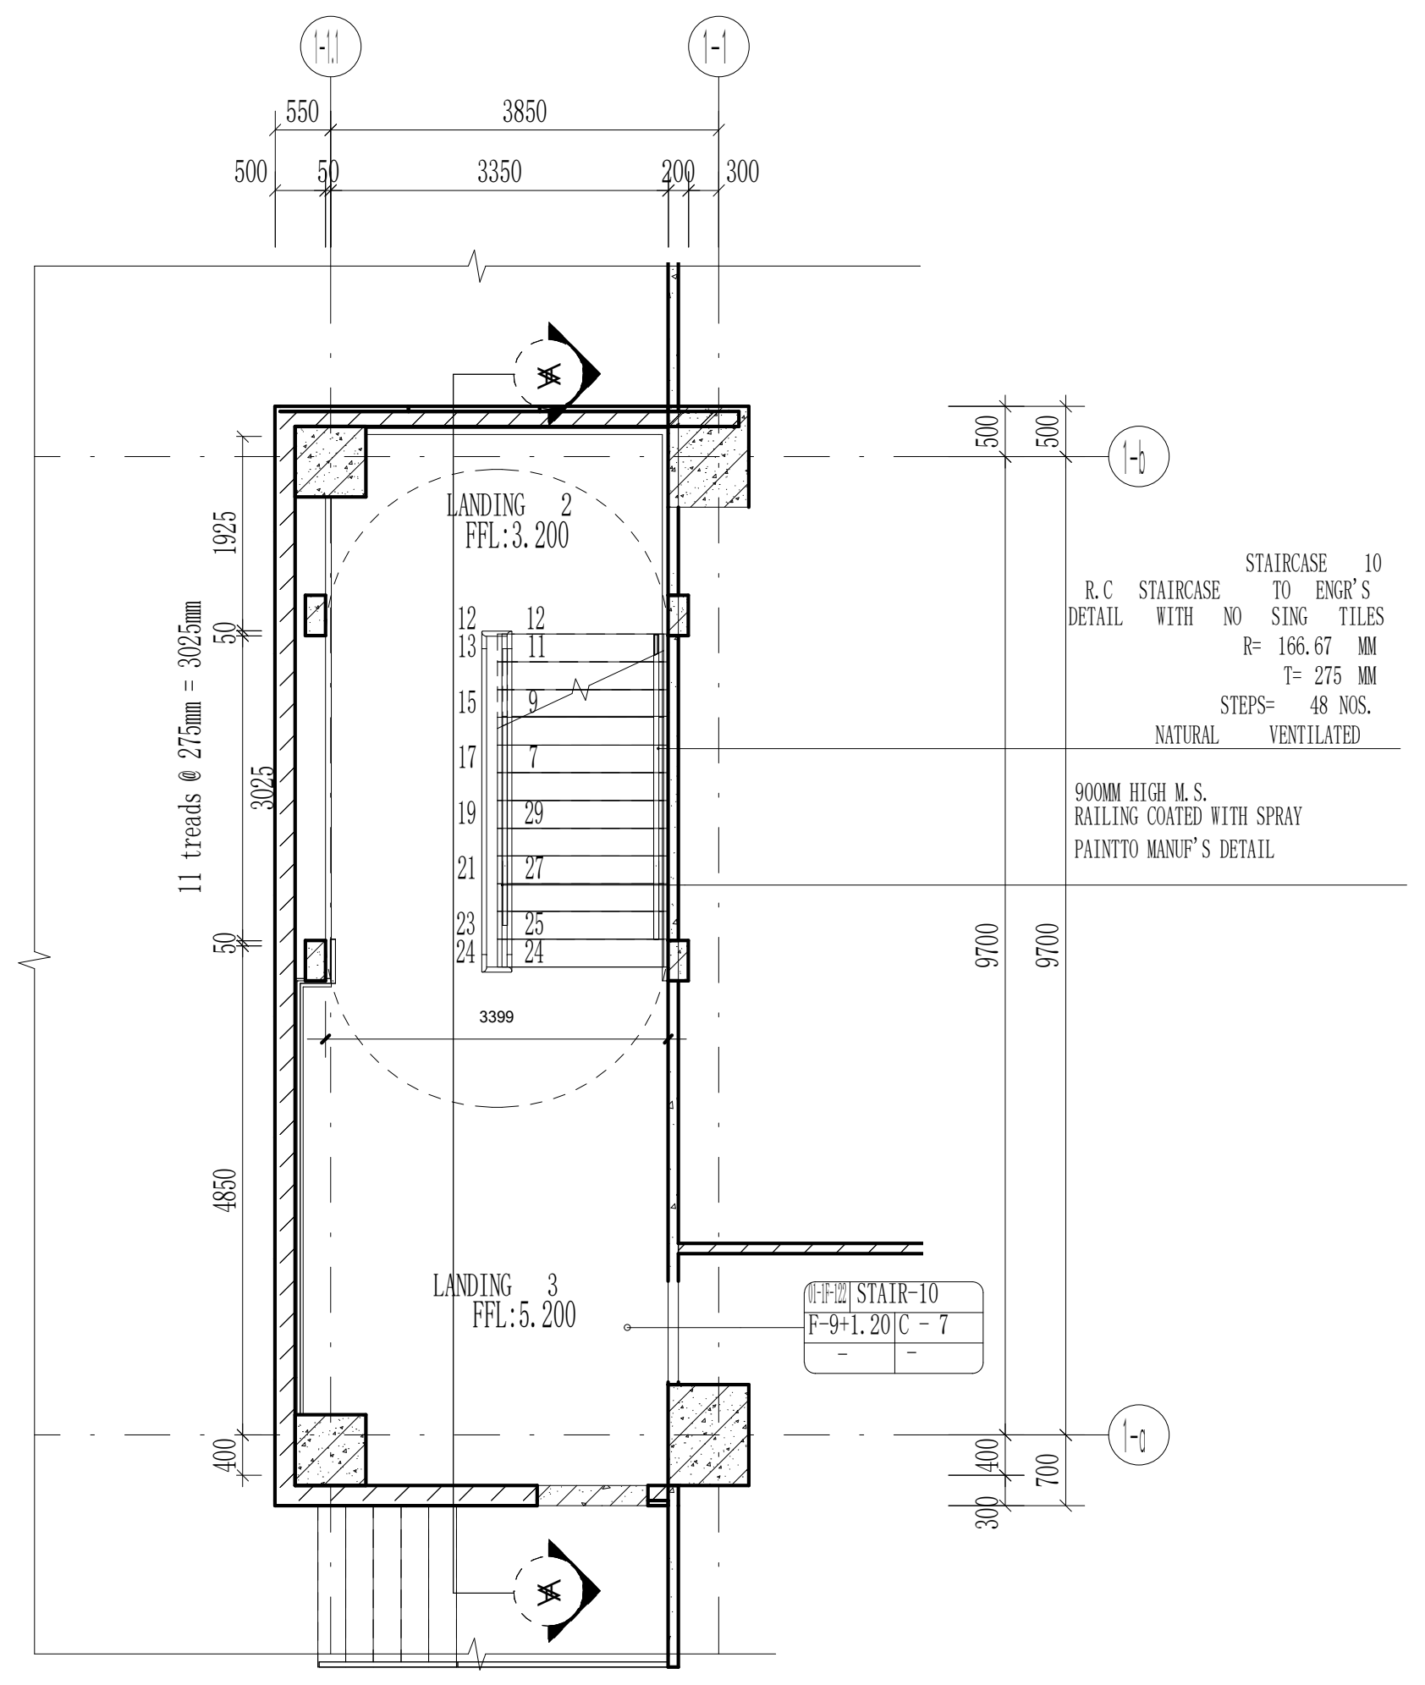
LANDING 2
FFL:3.200
LANDING 3
FFL:5.200
11 treads @ 275mm = 3025mm
STAIRCASE 10
R.C STAIRCASE TO ENGR'S DETAIL WITH NO SING TILES
R= 166.67 MM
T= 275 MM
STEPS= 48 NOS.
NATURAL VENTILATED
900MM HIGH M.S. RAILING COATED WITH SPRAY PAINTTO MANUF'S DETAIL
STAIR-10
F-9+1.20 C - 7
A

STAIR-10 5.200 ELEVATION PLAN FL
SCALE 1:75

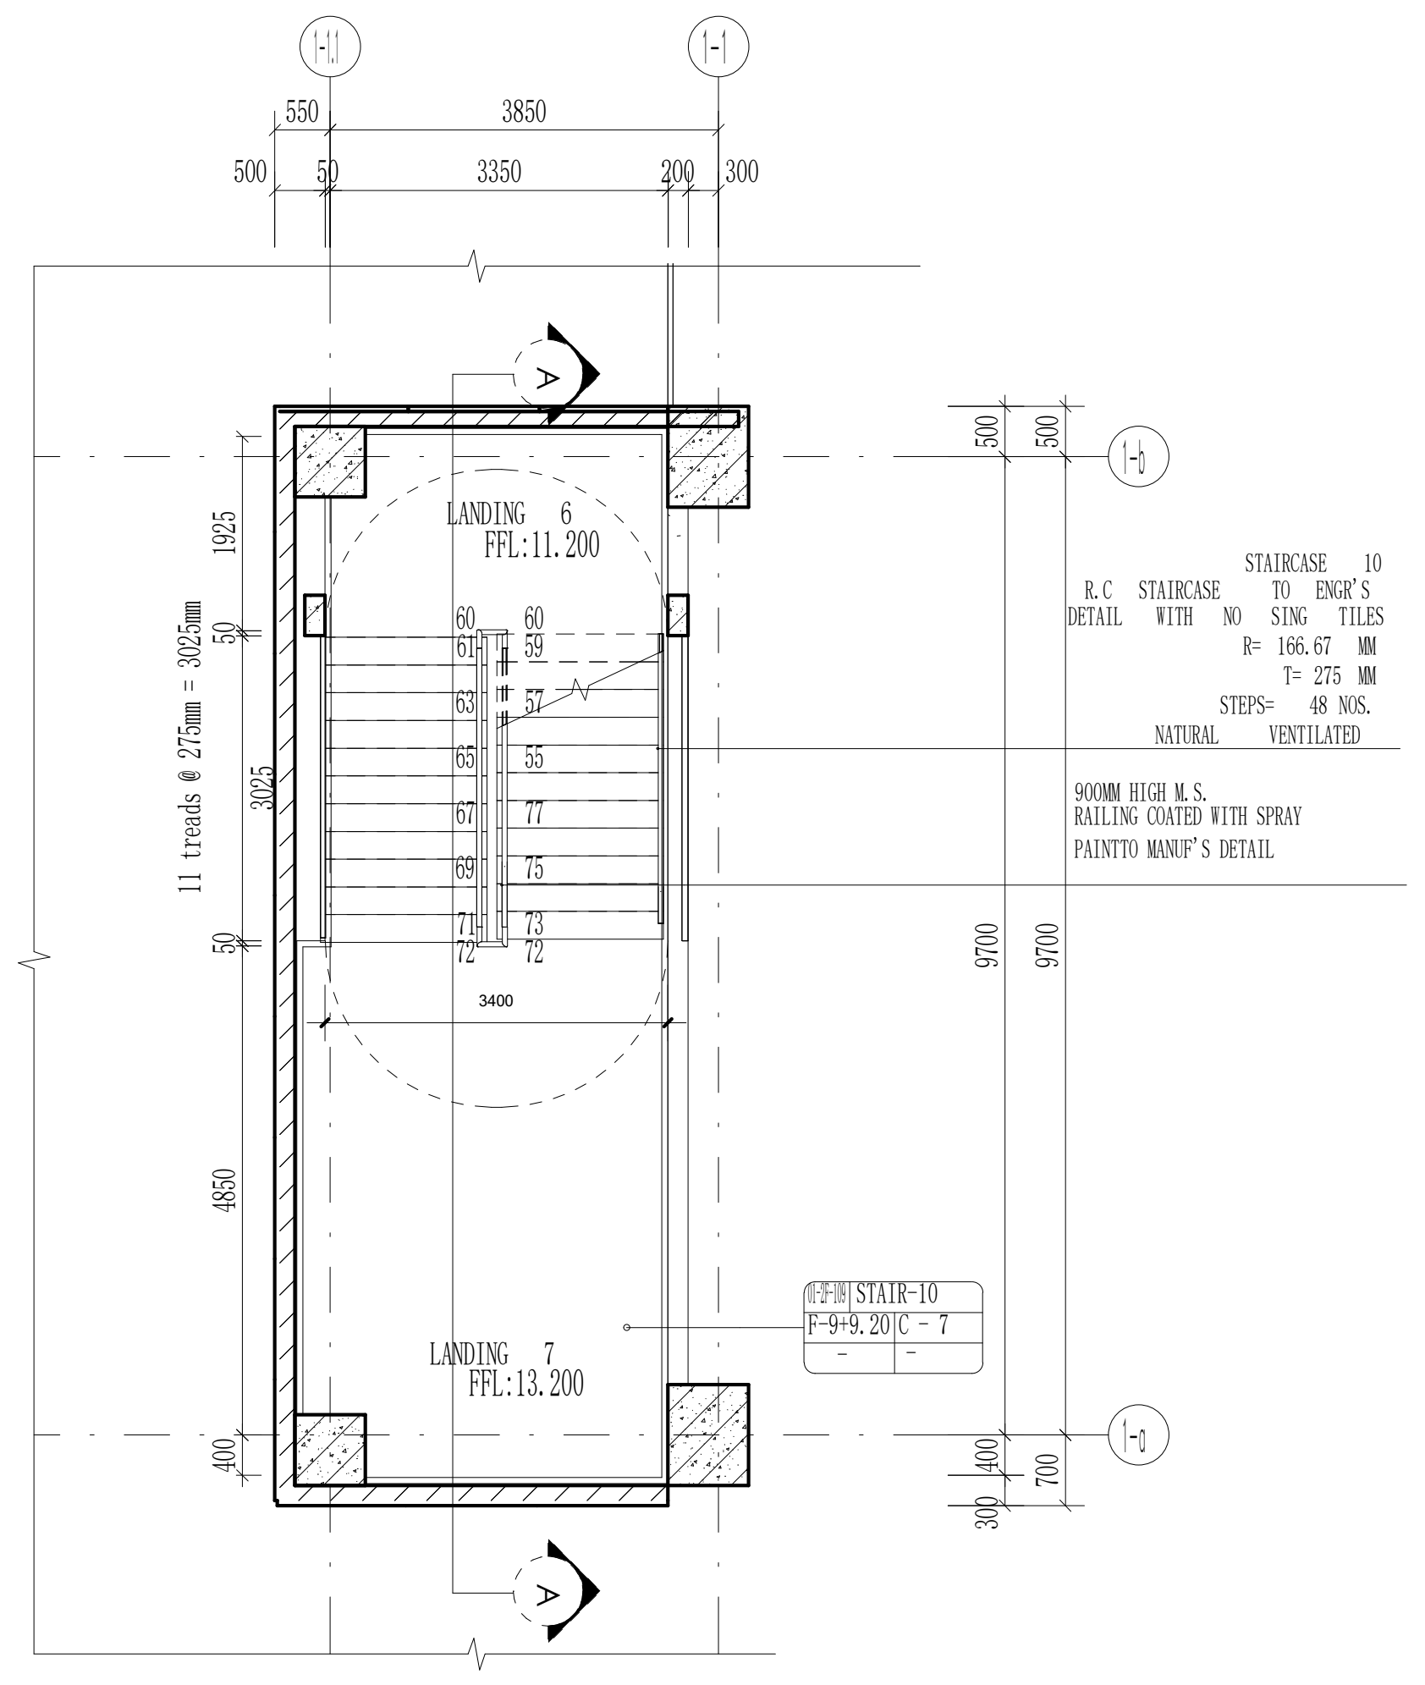
LANDING 6
FFL:11.200
LANDING 7
FFL:13.200
11 treads @ 275mm = 3025mm
STAIRCASE 10
R.C STAIRCASE TO ENGR'S DETAIL WITH NO SING TILES
R= 166.67 MM
T= 275 MM
STEPS= 48 NOS.
NATURAL VENTILATED
900MM HIGH M.S. RAILING COATED WITH SPRAY PAINTTO MANUF'S DETAIL
STAIR-10
F-9+9.20 C - 7
A

STAIR-10 13.200 ELEVATION PLAN FL
SCALE 1:75

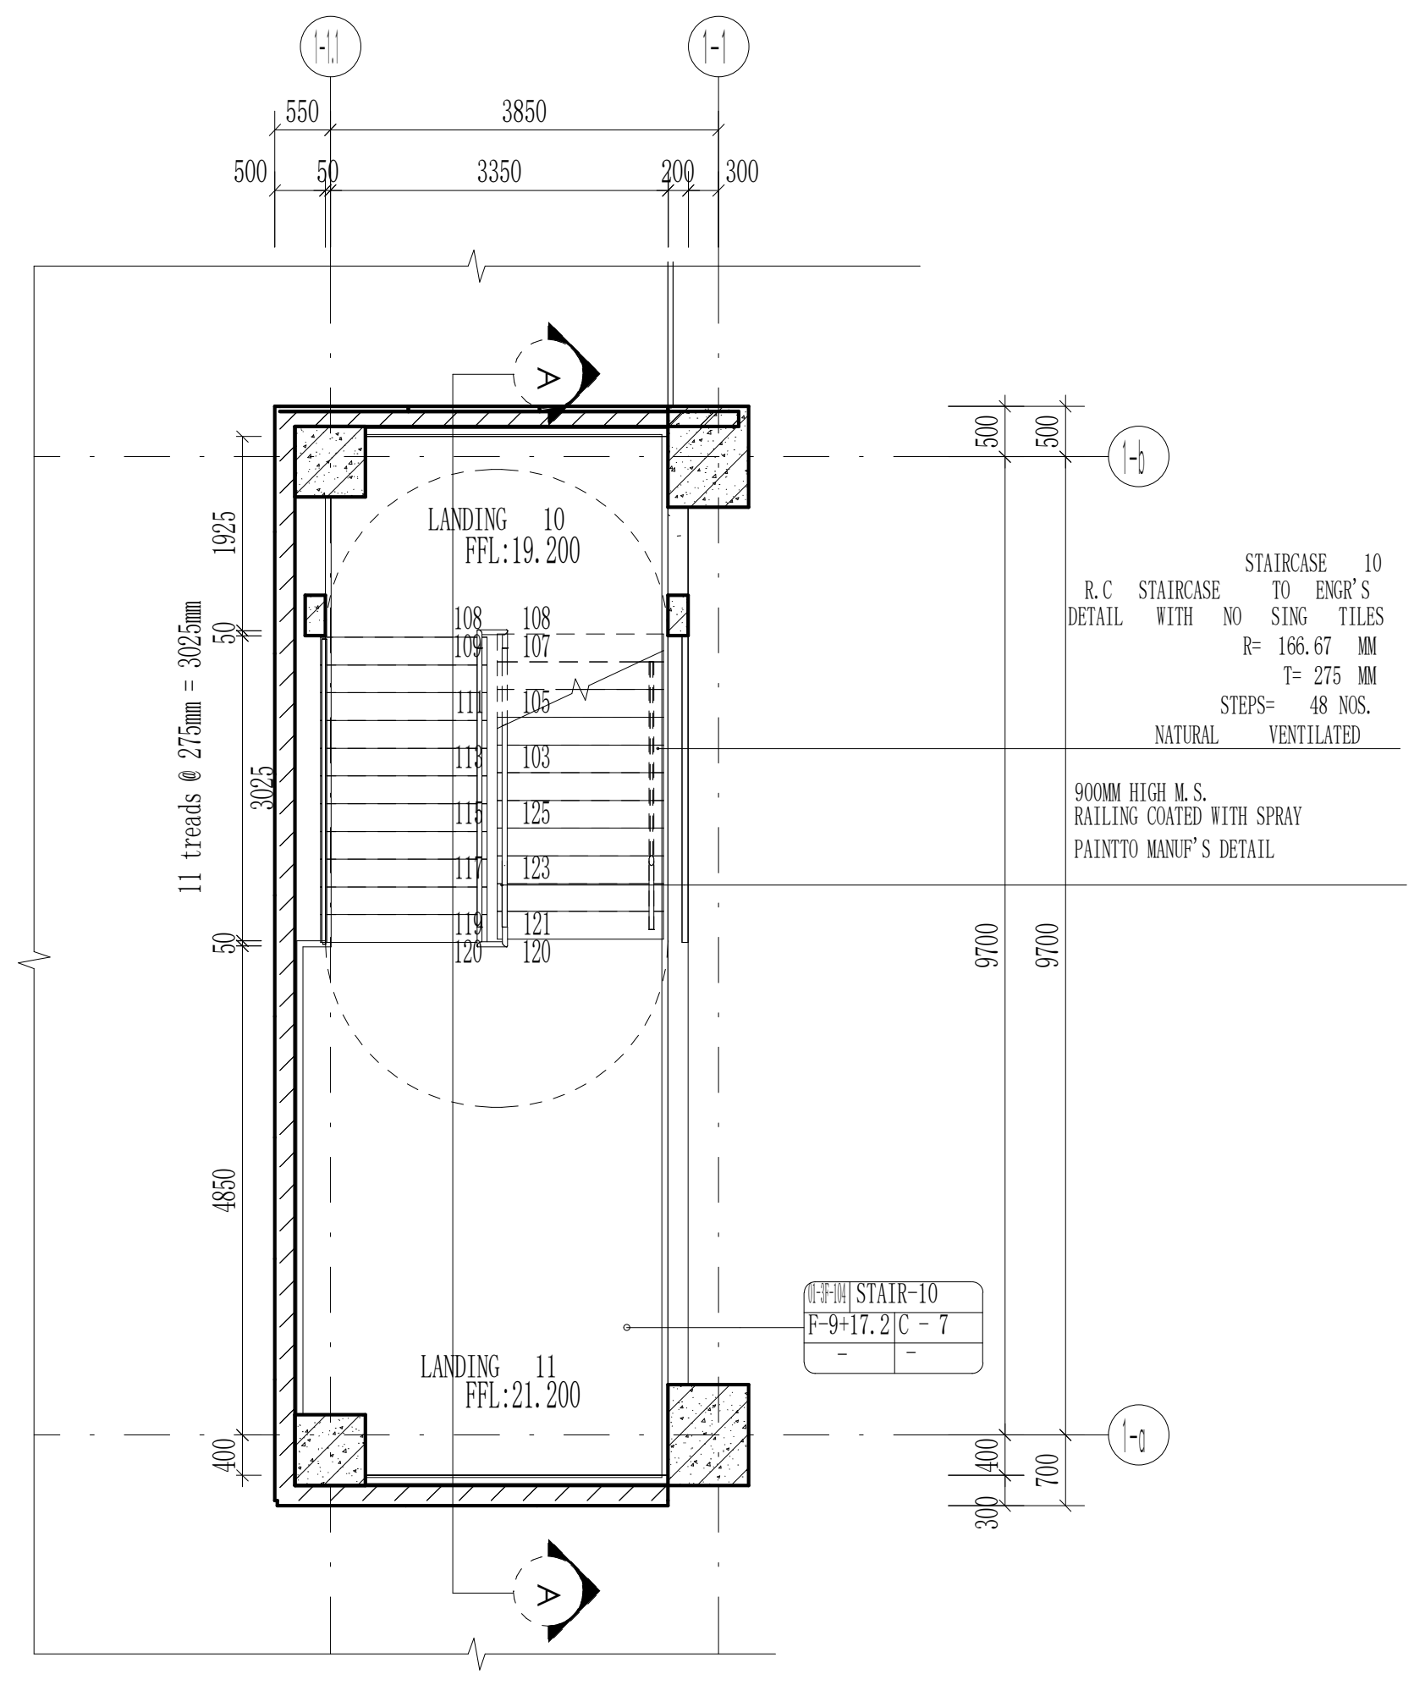
LANDING 10
FFL:19.200
LANDING 11
FFL:21.200
11 treads @ 275mm = 3025mm
STAIRCASE 10
R.C STAIRCASE TO ENGR'S DETAIL WITH NO SING TILES
R= 166.67 MM
T= 275 MM
STEPS= 48 NOS.
NATURAL VENTILATED
900MM HIGH M.S. RAILING COATED WITH SPRAY PAINTTO MANUF'S DETAIL
STAIR-10
F-9+17.20 C - 7
A

STAIR-10 21.200 ELEVATION PLAN FL
SCALE 1:75

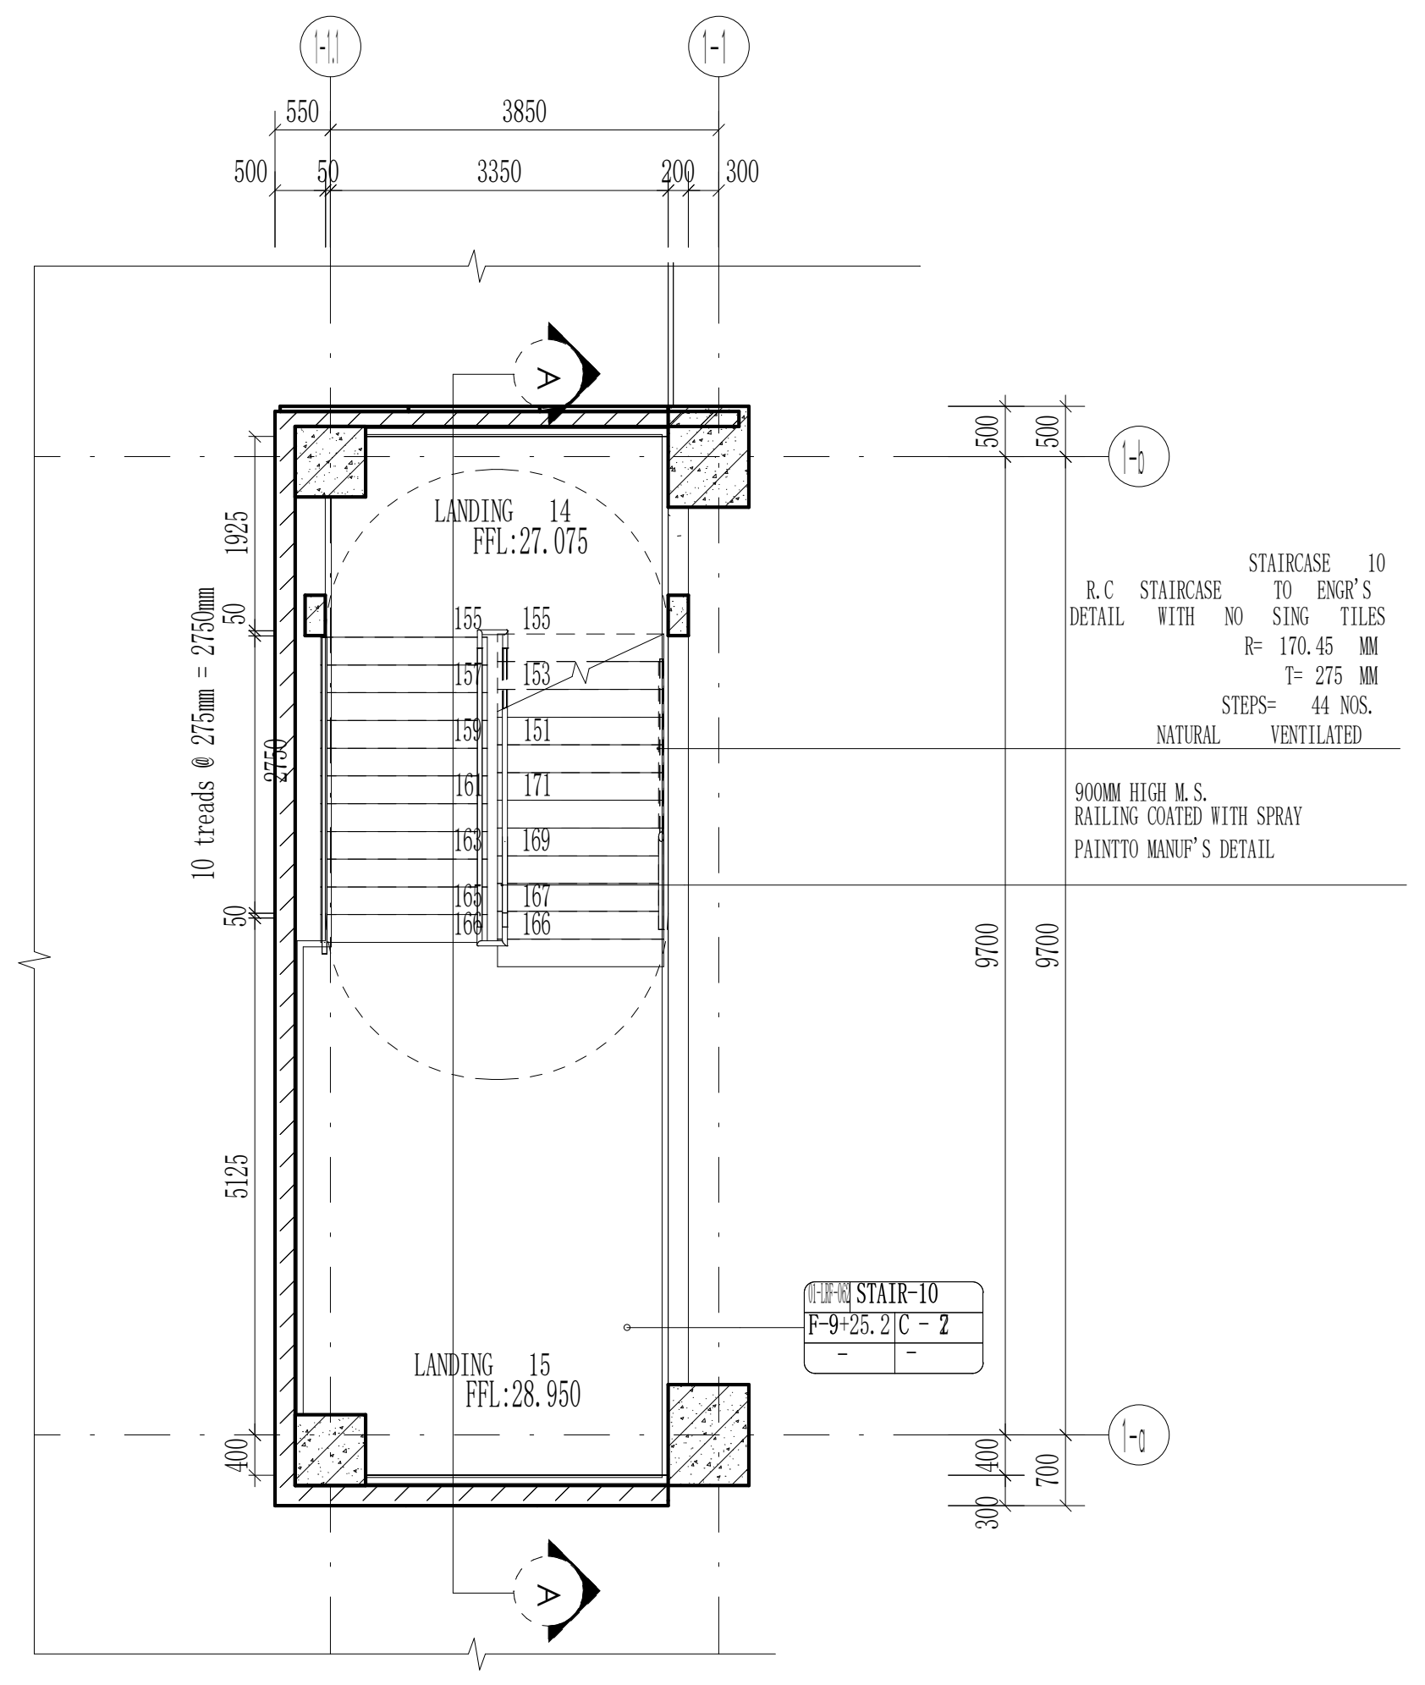
LANDING 14
FFL:27.075
LANDING 15
FFL:28.950
10 treads @ 275mm = 2750mm
STAIRCASE 10
R.C STAIRCASE TO ENGR'S DETAIL WITH NO SING TILES
R= 170.45 MM
T= 275 MM
STEPS= 44 NOS.
NATURAL VENTILATED
900MM HIGH M.S. RAILING COATED WITH SPRAY PAINTTO MANUF'S DETAIL
STAIR-10
F-9+25.20 C - 7
A

STAIR-10 28.950 ELEVATION PLANFL
SCALE 1:75

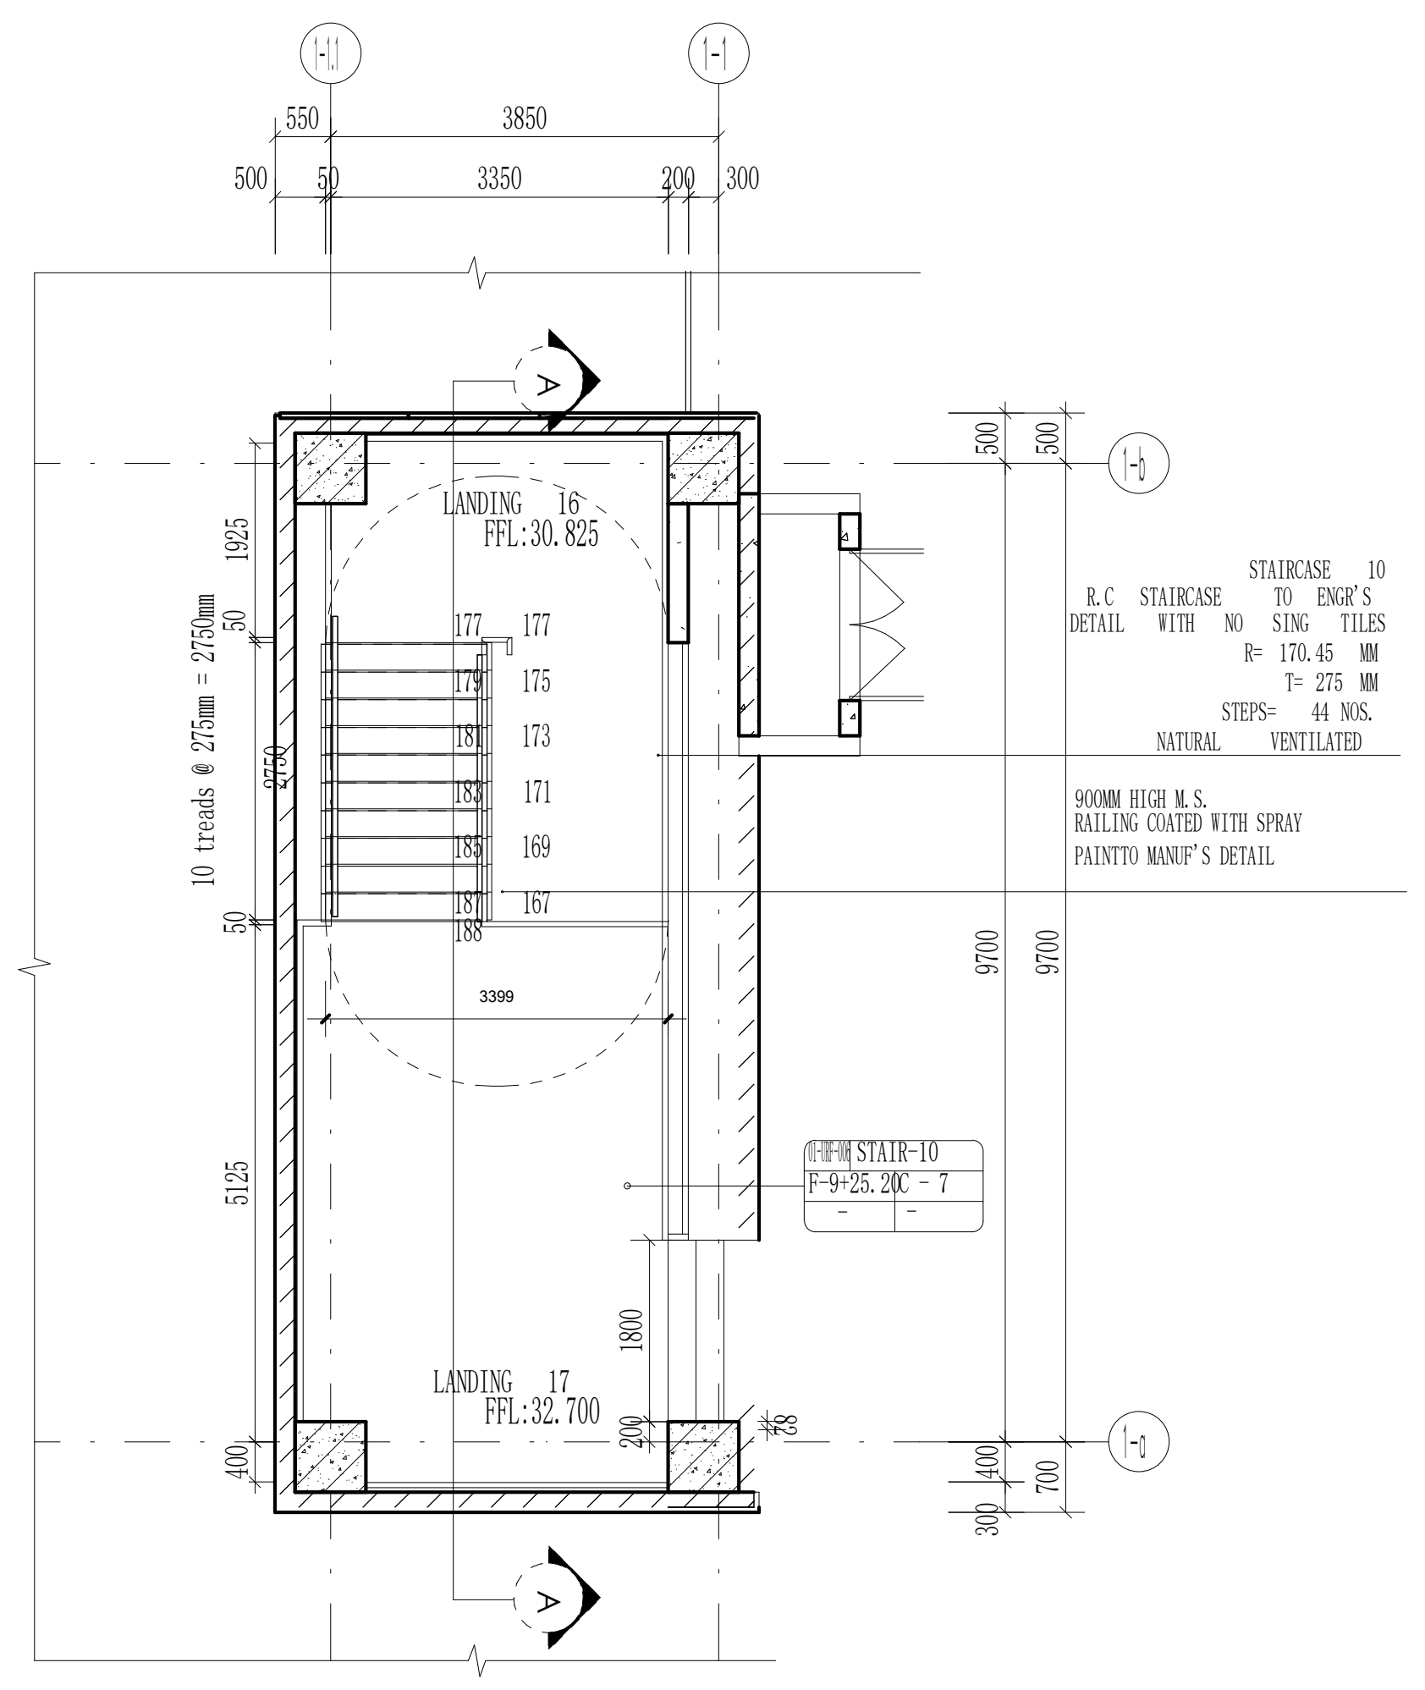
LANDING 16
FFL:30.825
LANDING 17
FFL:32.700
10 treads @ 275mm = 2750mm
STAIRCASE 10
R.C STAIRCASE TO ENGR'S DETAIL WITH NO SING TILES
R= 170.45 MM
T= 275 MM
STEPS= 44 NOS.
NATURAL VENTILATED
900MM HIGH M.S. RAILING COATED WITH SPRAY PAINTTO MANUF'S DETAIL
STAIR-10
F-9+25.20 C - 7
A

STAIR-10 UPPER ROOF FL
SCALE 1:75

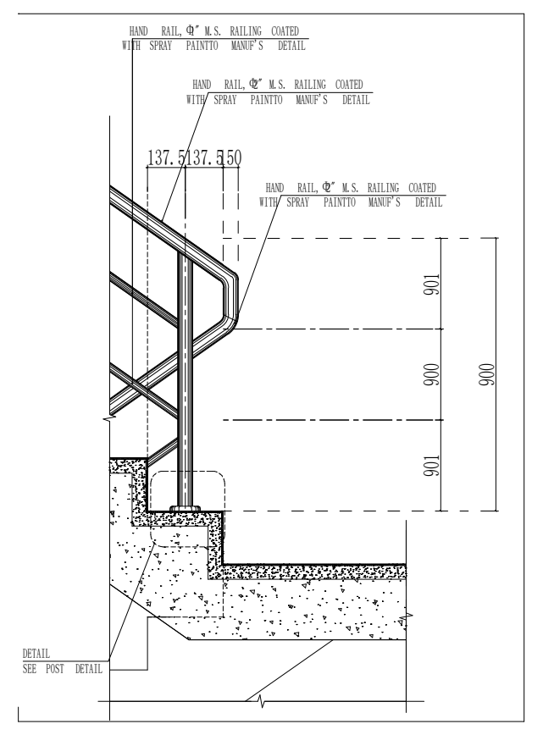

HANDRAIL DETAILS
SCALE

1:75

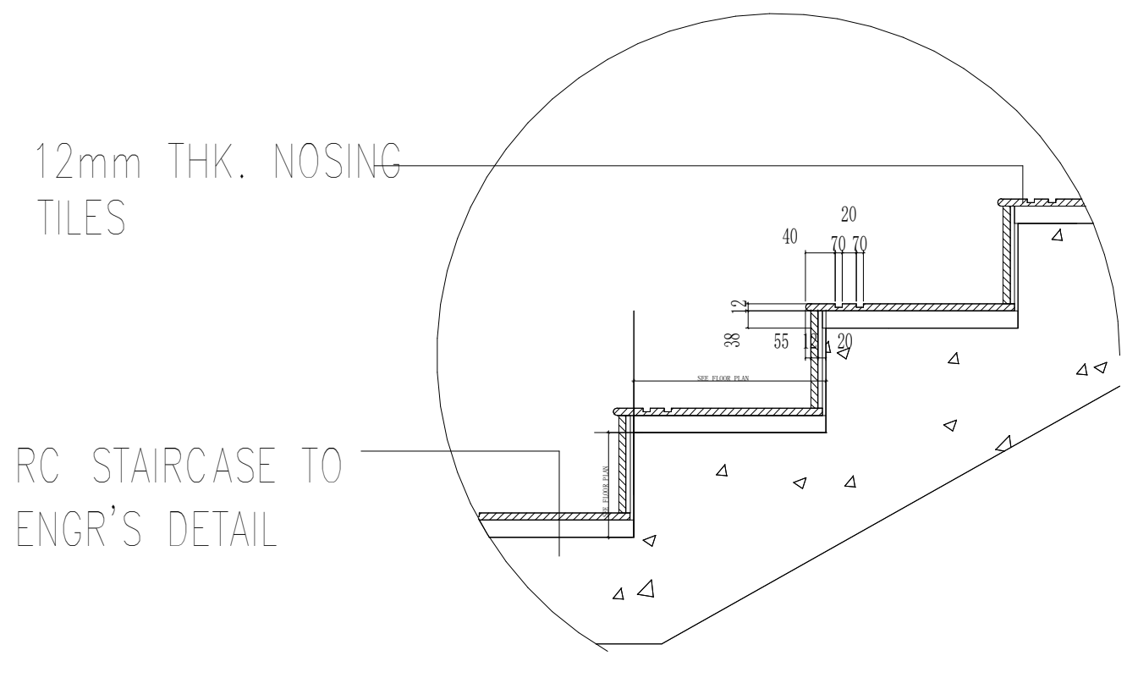

STEP DETAILS
SCALE

1:75

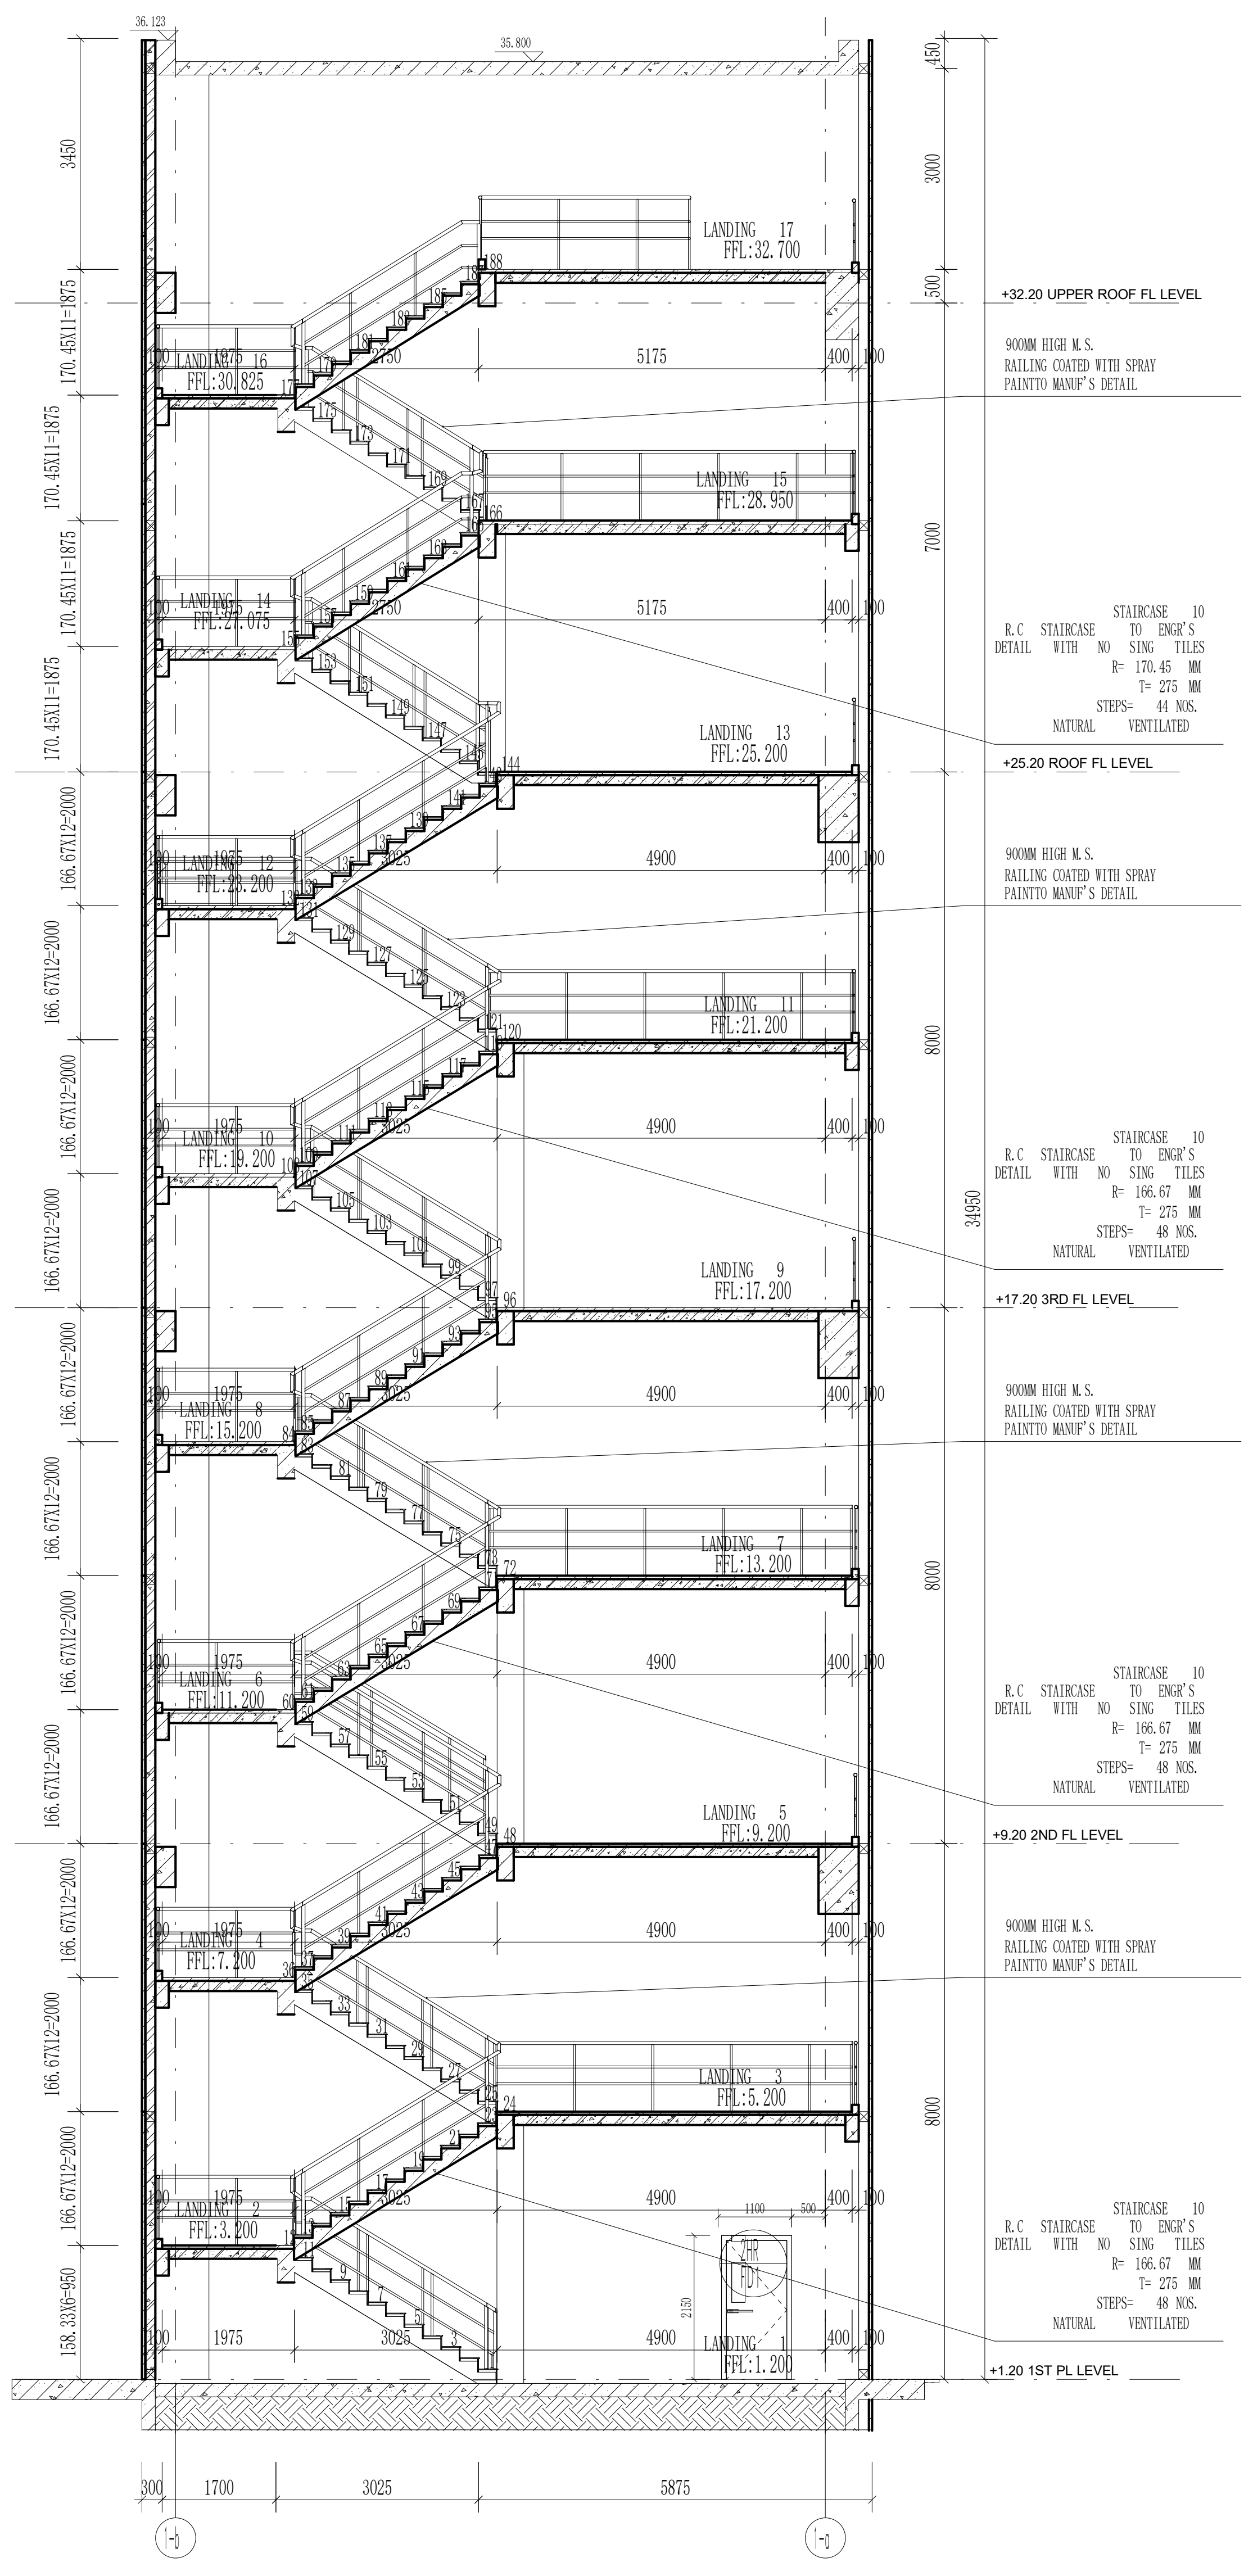

Section A
SCALE 1:75

CLIENT :

GULF EDGE DC 01

87 Wireless Road, M Thai Tower 11th. Floor, All Seasons Place, Lumpini,
Pathumwan, Bangkok 10330, Thailand

CONTRACTOR :

华西发展(泰国)有限公司
บริษัท หัวซือ ดีเวลลอปเม้นต์ (ประเทศไทย) จำกัด
HUASHI DEVELOPMENT CO.,LTD
No. 202, Room No. 1403, 14/F, Le Concorde Building,
Ratchadapisek Road, Huaykhwang Sub-District,
Huaykhwang District, Bangkok Metropolitan 10310.

CONSULTANT :

ARbay
บริษัท เอ อาร์ เบย์ จำกัด
ARbay Company Limited
31 st Floor Bangkok Insurance Building
25 South Sathorn road Thungmahamek
Sathorn Bangkok 10120 THAILAND
T +66 (0) 2286 8199
F +66 (0) 2286 2863
info@arbay.co.th

CONSULTANT :

Qbic Engineers & Architects Co.,Ltd.
8 Soi KALONG 4 SANAMBINNAM ROAD,
THASAI SUB-DISTRICT, MUANG NONTHABURI DISTRICT
, NONTHABURI.
Tel 662-950-4374
Fax 662-580-3231
E-Mail : qbic@qbic.co.th, www.qbic.co.th
QBIC ENGINEERS AND ARCHITECTS CO.,LTD.

CONSULTANT :

MITR
MITR TECHNICAL CONSULTANT CO.,LTD.
1168/8 12th FLOOR, LUMPINI TOWER BUILDING,
RAMA IV RD., THUNGMAHAMEK, SATHORN, BANGKOK 10120, THAILAND
TEL : 0-2679-9079-84
FAX : 0-2679-9085 E-mail: mitr_dd@mitr.com

Architect : SIGNATURE
ประกิต พนานุรัตน์ วสถ. 580
ที่อยู่
251/1 ถ.จารุเมือง แขวงรองเมือง เขตปทุมวัน
กรุงเทพมหานคร โทรศัพท์ 02-286-8199

Structural Engineer : SIGNATURE
วิศวกรผู้ออกแบบโครงสร้าง
ณัฐสม สงวนวงษ์ วย 1423
ที่อยู่
2/1 ซ.รามคำแหง 150 ถ.รามคำแหง
แขวง สะพานสูง เขต สะพานสูง กทม. 10240

Structural Inspector : SIGNATURE
วิศวกรผู้ตรวจสอบโครงสร้าง
โกมล จุฑาภัทร วย 964
ที่อยู่
24/18 ซ.นวมินทร์ 129 ถ. นวมินทร์
แขวง นวลจันทร์ เขต บึงกุ่ม กทม. 10230

Electrical Engineer : SIGNATURE
วิศวกรผู้ออกแบบระบบไฟฟ้ากำลัง
นายสุภัทร บูรณวิทย์ วฟก.1265
ที่อยู่
21 ซอยทานสัมฤทธิ์ 13
ตำบลท่าทราย อ.เมืองนนทบุรี จ.นนทบุรี 11000

Mechanical Engineer : SIGNATURE
วิศวกรผู้ออกแบบระบบเครื่องกลและปรับอากาศ
นายประสิทธิ์ เกี้ยวสุนทร วก.1221
ประสิทธิ์
ที่อยู่
44/372 ซอยบางกระดี่ 35/1 แขวงแสมดำ
เขตบางขุนเทียน กทม. 10150

Sanitary Engineer : SIGNATURE
วิศวกรผู้ออกแบบระบบสุขาภิบาล และดับเพลิง
นายทศวรรษ สนั่นฤทธิ์ วส. 215
ทศวรรษ
ที่อยู่
บ้านเลขที่ 99/107 หมู่ที่ 3 ต.ศีรษะจรเข้น้อย
อ.บางเสาธง จ.สมุทรปราการ 10540

ISSUE/REVISION

REV.	DESCRIPTION	DATE
A	90% DEVELOPED	09/05/2026

PROJECT NAME :

GEDC 01

LOCATION:
Nikhom Phattana district, Rayong ,industrial estate,CPGC

BUILDING :
MAIN BUILDING

90% DEVELOPED

TITLE :

STAIRCASE 10

JOB NO.	SCALE 1 : 75
DRAWN LW	REF.
CHECKED LJC	DWG. NO. MPK01A-90-A-ST-010
APPROVED LXD	
DATE 2026.05.09	

NOTE :THIS PRINT IS OF A CONFIDENTIAL NATURE, IT SHALL NOT BE TRACED, PHOTOGRAPHED, PHOTOSTATED OR REPRODUCED IN ANY MANER, NOR USED FOR ANY PURPOSE WHATSOEVER EXCEPT BY WRITTEN PERMISSION