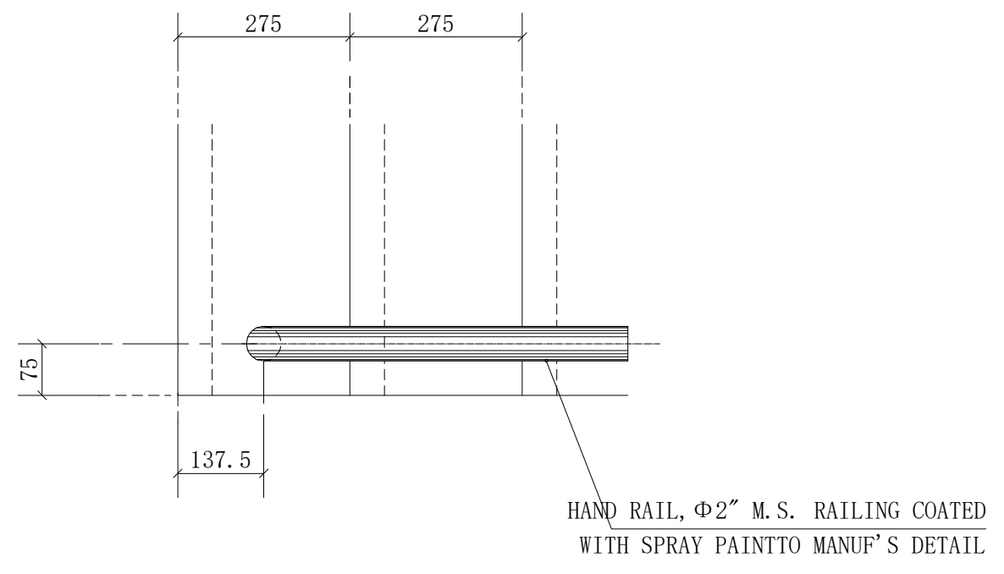
275
275
75
137.5
HAND RAIL, Φ2" M.S. RAILING COATED
WITH SPRAY PAINTTO MANUF'S DETAIL

PLAN

SCALE 1:10

A

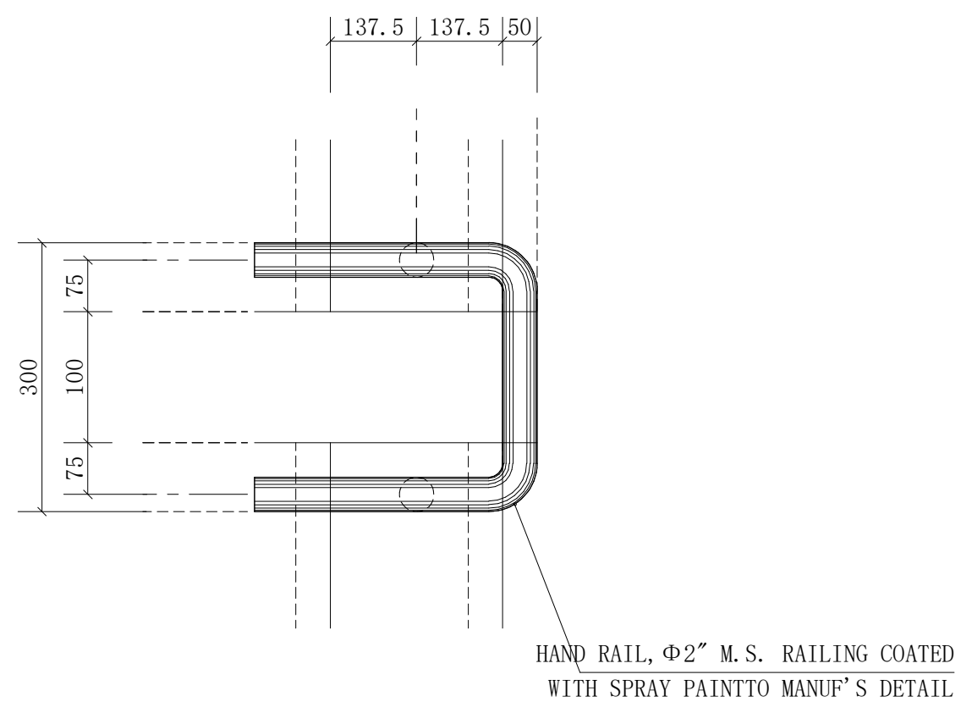
137.5
137.5
50
300
75
100
75
HAND RAIL, Φ2" M.S. RAILING COATED
WITH SPRAY PAINTTO MANUF'S DETAIL

PLAN

SCALE 1:10

A

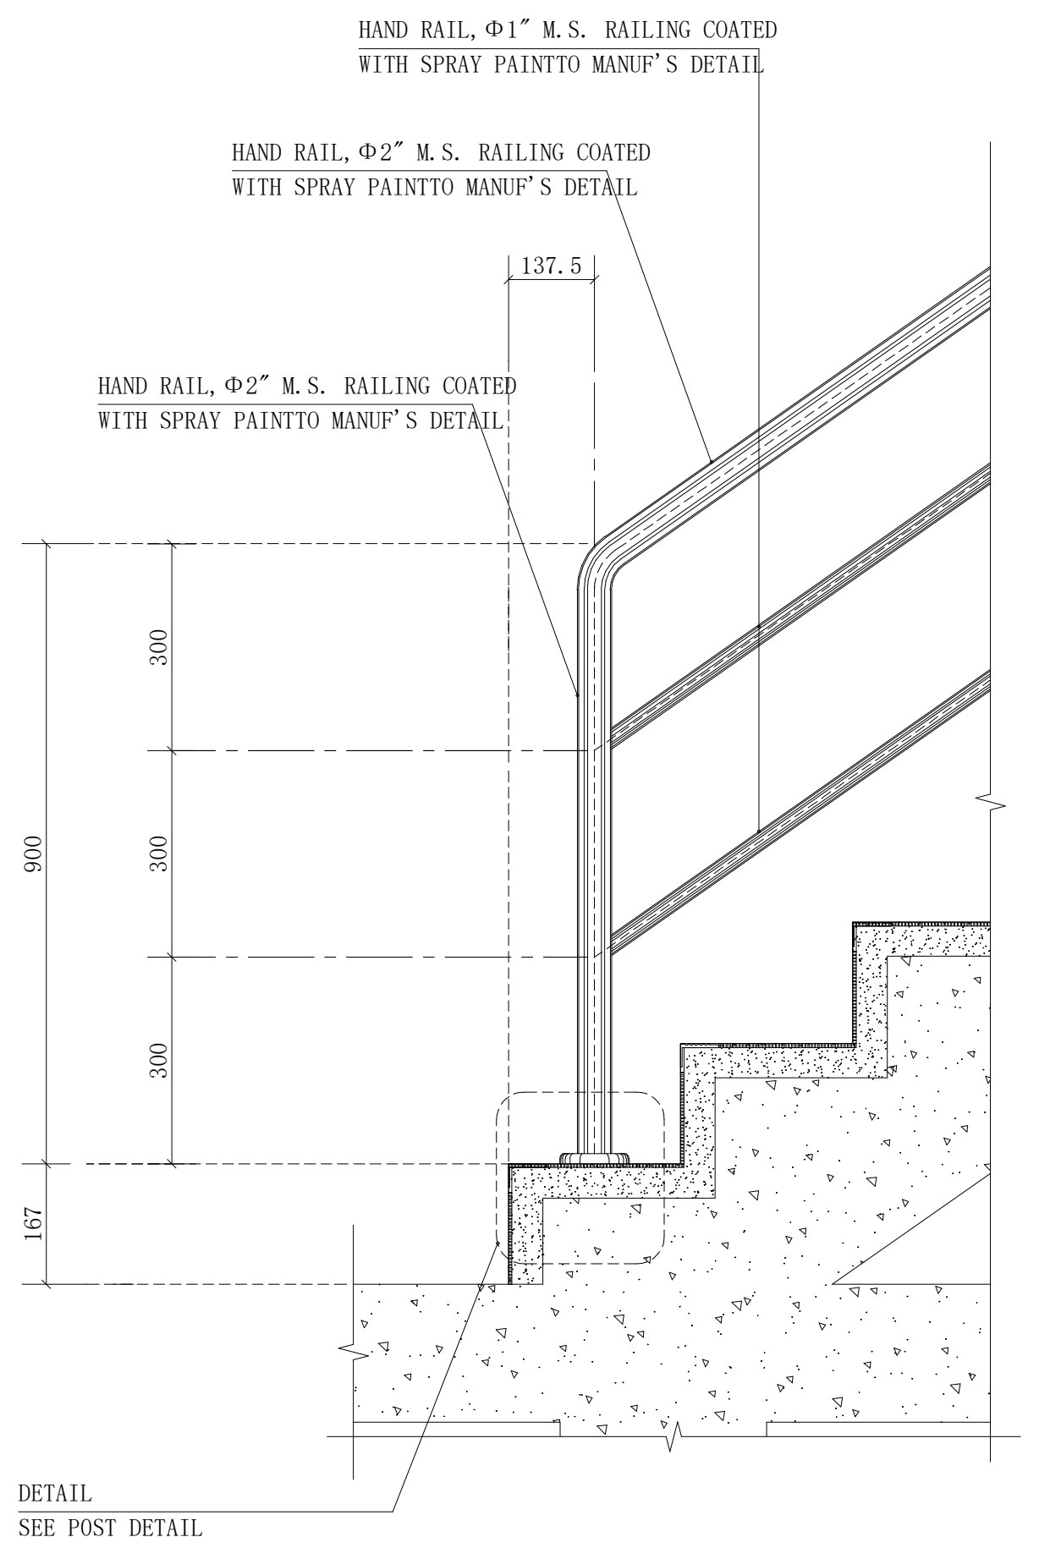
HAND RAIL, Φ1" M.S. RAILING COATED
WITH SPRAY PAINTTO MANUF'S DETAIL
HAND RAIL, Φ2" M.S. RAILING COATED
WITH SPRAY PAINTTO MANUF'S DETAIL
137.5
HAND RAIL, Φ2" M.S. RAILING COATED
WITH SPRAY PAINTTO MANUF'S DETAIL
900
300
300
300
167
DETAIL
SEE POST DETAIL

ELEVATION

SCALE 1:10

A

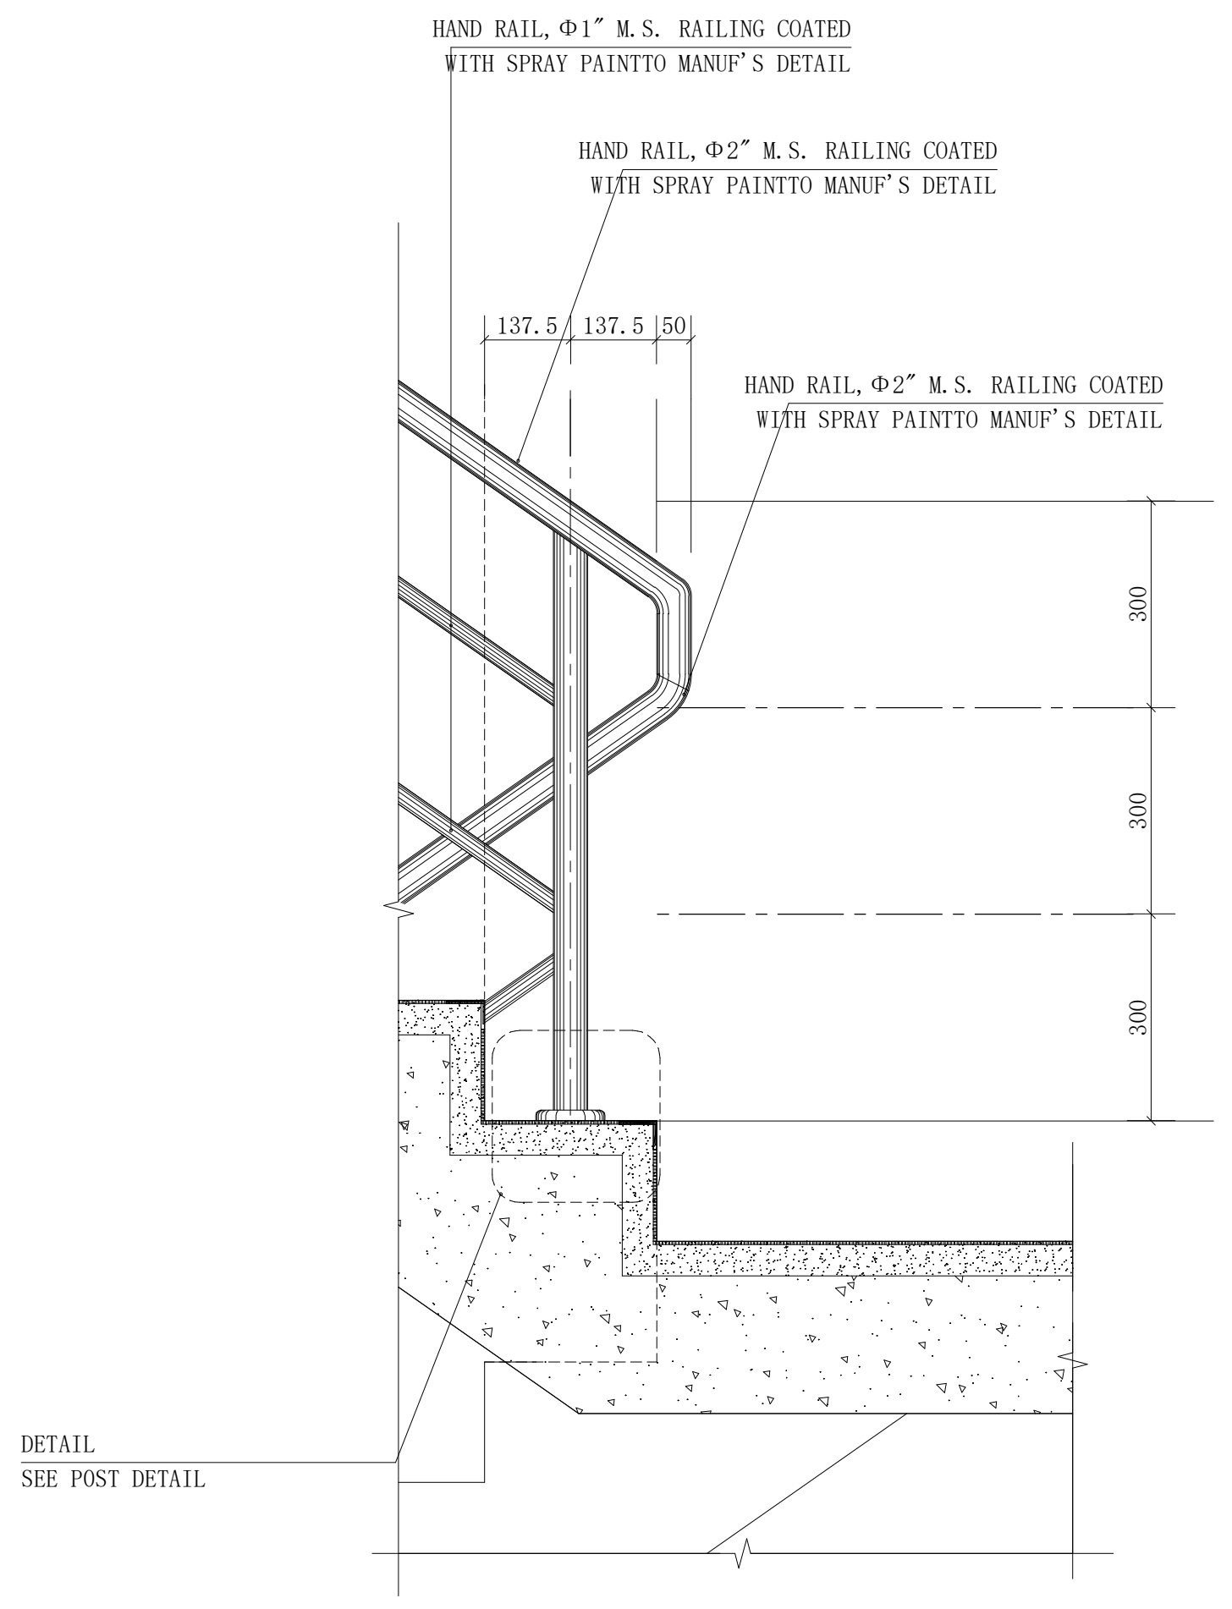
HAND RAIL, Φ1" M.S. RAILING COATED
WITH SPRAY PAINTTO MANUF'S DETAIL
HAND RAIL, Φ2" M.S. RAILING COATED
WITH SPRAY PAINTTO MANUF'S DETAIL
137.5
137.5
50
HAND RAIL, Φ2" M.S. RAILING COATED
WITH SPRAY PAINTTO MANUF'S DETAIL
300
300
300
900
DETAIL
SEE POST DETAIL

ELEVATION

SCALE 1:10

A

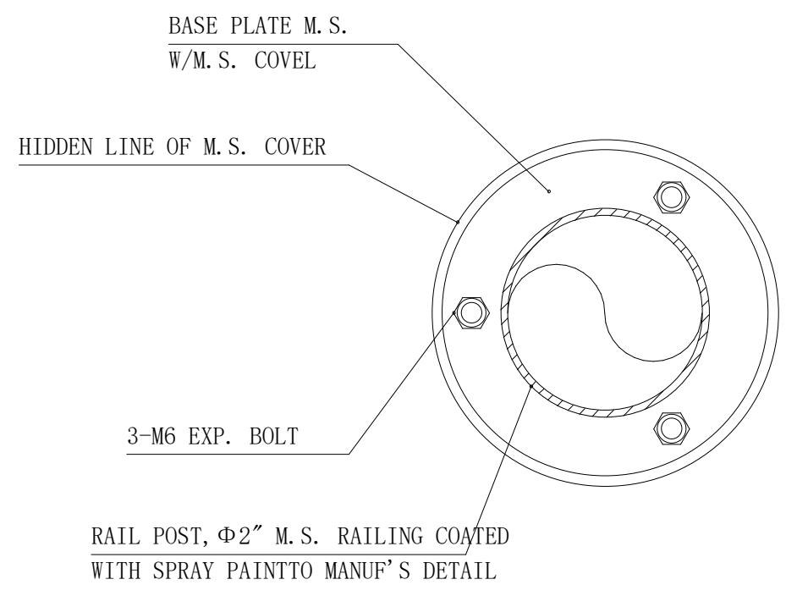
BASE PLATE M.S.
W/M.S. COVEL
HIDDEN LINE OF M.S. COVER
3-M6 EXP. BOLT
RAIL POST, Φ2" M.S. RAILING COATED
WITH SPRAY PAINTTO MANUF'S DETAIL

POST PLAN

SCALE 1:10

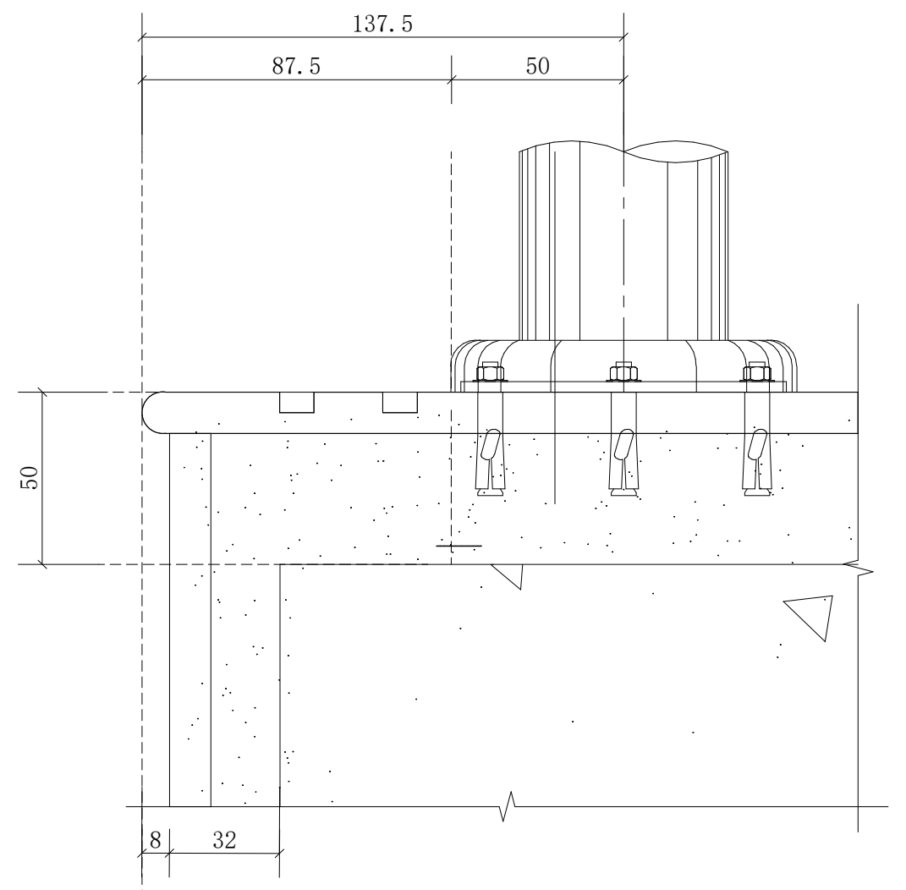
137.5
87.5
50
50
8
32

POST SECTION

SCALE 1:10

POST DETAIL

SCALE 1:10

A

NOTE :THIS PRINT IS OF A CONFIDENTIAL NATURE, IT SHALL NOT BE TRACED, PHOTOGRAPHED, PHOTOSTATED OR REPRODUCED IN ANY MANER, NOR USED FOR ANY PURPOSE WHATSOEVER EXCEPT BY WRITTEN PERMISSION

CLIENT :

GULF EDGE DC 01

87 Wireless Road, M Thai Tower 11th. Floor, All Seasons Place, Lumpini,
Pathumwan, Bangkok 10330, Thailand

CONTRACTOR :

华西发展(泰国)有限公司
บริษัท หัวซือ ดีเวลลอปเม้นต์ (ประเทศไทย) จำกัด
HUASHI DEVELOPMENT CO.,LTD
No. 202, Room No. 1403, 14/F, Le Concorde Building,
Ratchadapisek Road, Huaykhwang Sub-District,
Huaykhwang District, Bangkok Metropolitan 10310.

CONSULTANT :

ARbay
บริษัท เอ อาร์ เบย์ จำกัด
ARbay Company Limited
31 st Floor Bangkok Insurance Building
25 South Sathorn road Thungmahamek
Sathorn Bangkok 10120 THAILAND
T +66 (0) 2286 8199
F +66 (0) 2286 2863
info@arbay.co.th

CONSULTANT :

Qbic Engineers & Architects Co.,Ltd.
8 Soi KALONG 4 SANAMBINNAM ROAD,
THASAI SUB-DISTRICT, MUANG NONTHABURI DISTRICT
, NONTHABURI.
Tel 662-950-4374
Fax 662-580-3231
E-Mail : qbic@qbic.co.th, www.qbic.co.th
QBIC ENGINEERS AND ARCHITECTS CO.,LTD.

CONSULTANT :

MITR
MITR TECHNICAL CONSULTANT CO.,LTD.
1168/8 12th FLOOR, LUMPINI TOWER BUILDING,
RAMA IV RD., THUNGMAHAMEK, SATHORN, BANGKOK 10120, THAILAND
TEL : 0-2679-9079-84
FAX : 0-2679-9085 E-mail: mitr_dd@mitr.com

Architect : SIGNATURE

ประกิต พนานุรัตน์ วสถ. 580
ที่อยู่
251/1 ถ.จารุเมือง แขวงรองเมือง เขตปทุมวัน
กรุงเทพมหานคร โทรศัพท์ 02-286-8199

Structural Engineer : SIGNATURE

วิศวกรผู้ออกแบบโครงสร้าง

ณัฐสม สงวนวงษ์ วย 1423
ที่อยู่
2/1 ซ.รามคำแหง 150 ถ.รามคำแหง
แขวง สะพานสูง เขต สะพานสูง กทม. 10240

ณัฐสม สงวนวงษ์

Structural Inspector : SIGNATURE

วิศวกรผู้ตรวจสอบโครงสร้าง

โกมล จุฑาภัทร วย 964
ที่อยู่
24/18 ซ.นวมินทร์ 129 ถ. นวมินทร์
แขวง นวลจันทร์ เขต บึงกุ่ม กทม. 10230

Electrical Engineer : SIGNATURE

วิศวกรผู้ออกแบบระบบไฟฟ้ากำลัง

นายสุภัทร บูรณวิทย์ วฟก.1265
ที่อยู่
21 ซอยทานสัมฤทธิ์ 13
ตำบลท่าทราย อ.เมืองนนทบุรี จ.นนทบุรี 11000

Mechanical Engineer : SIGNATURE

วิศวกรผู้ออกแบบระบบเครื่องกลและปรับอากาศ

นายประสิทธิ์ เกี้ยวสุนทร วก.1221
ที่อยู่
44/372 ซอยบางกระดี่ 35/1 แขวงแสมดำ
เขตบางขุนเทียน กทม. 10150

ประสิทธิ์

Sanitary Engineer : SIGNATURE

วิศวกรผู้ออกแบบระบบสุขาภิบาล และดับเพลิง

นายทศวรรษ สนั่นฤทธิ์ วส. 215
ที่อยู่
บ้านเลขที่ 99/107 หมู่ที่ 3 ต.ศีรษะจรเข้น้อย
อ.บางเสาธง จ.สมุทรปราการ 10540

ทศวรรษ

ISSUE/REVISION

REV.	DESCRIPTION	DATE
A	90% DEVELOPED	09/05/2026

PROJECT NAME :

GEDC 01

LOCATION:
Nikhom Phattana district, Rayong ,industrial estate,CPGC

BUILDING :
MAIN BUILDING

90% DEVELOPED

TITLE :

HANDRAIL RAILING DETAIL

JOB NO.
SCALE
DRAWN LW
REF.
CHECKED LJC
DWG. NO. MPK01A-90-A-ST-012
APPROVED LXD
DATE 2026.05.09