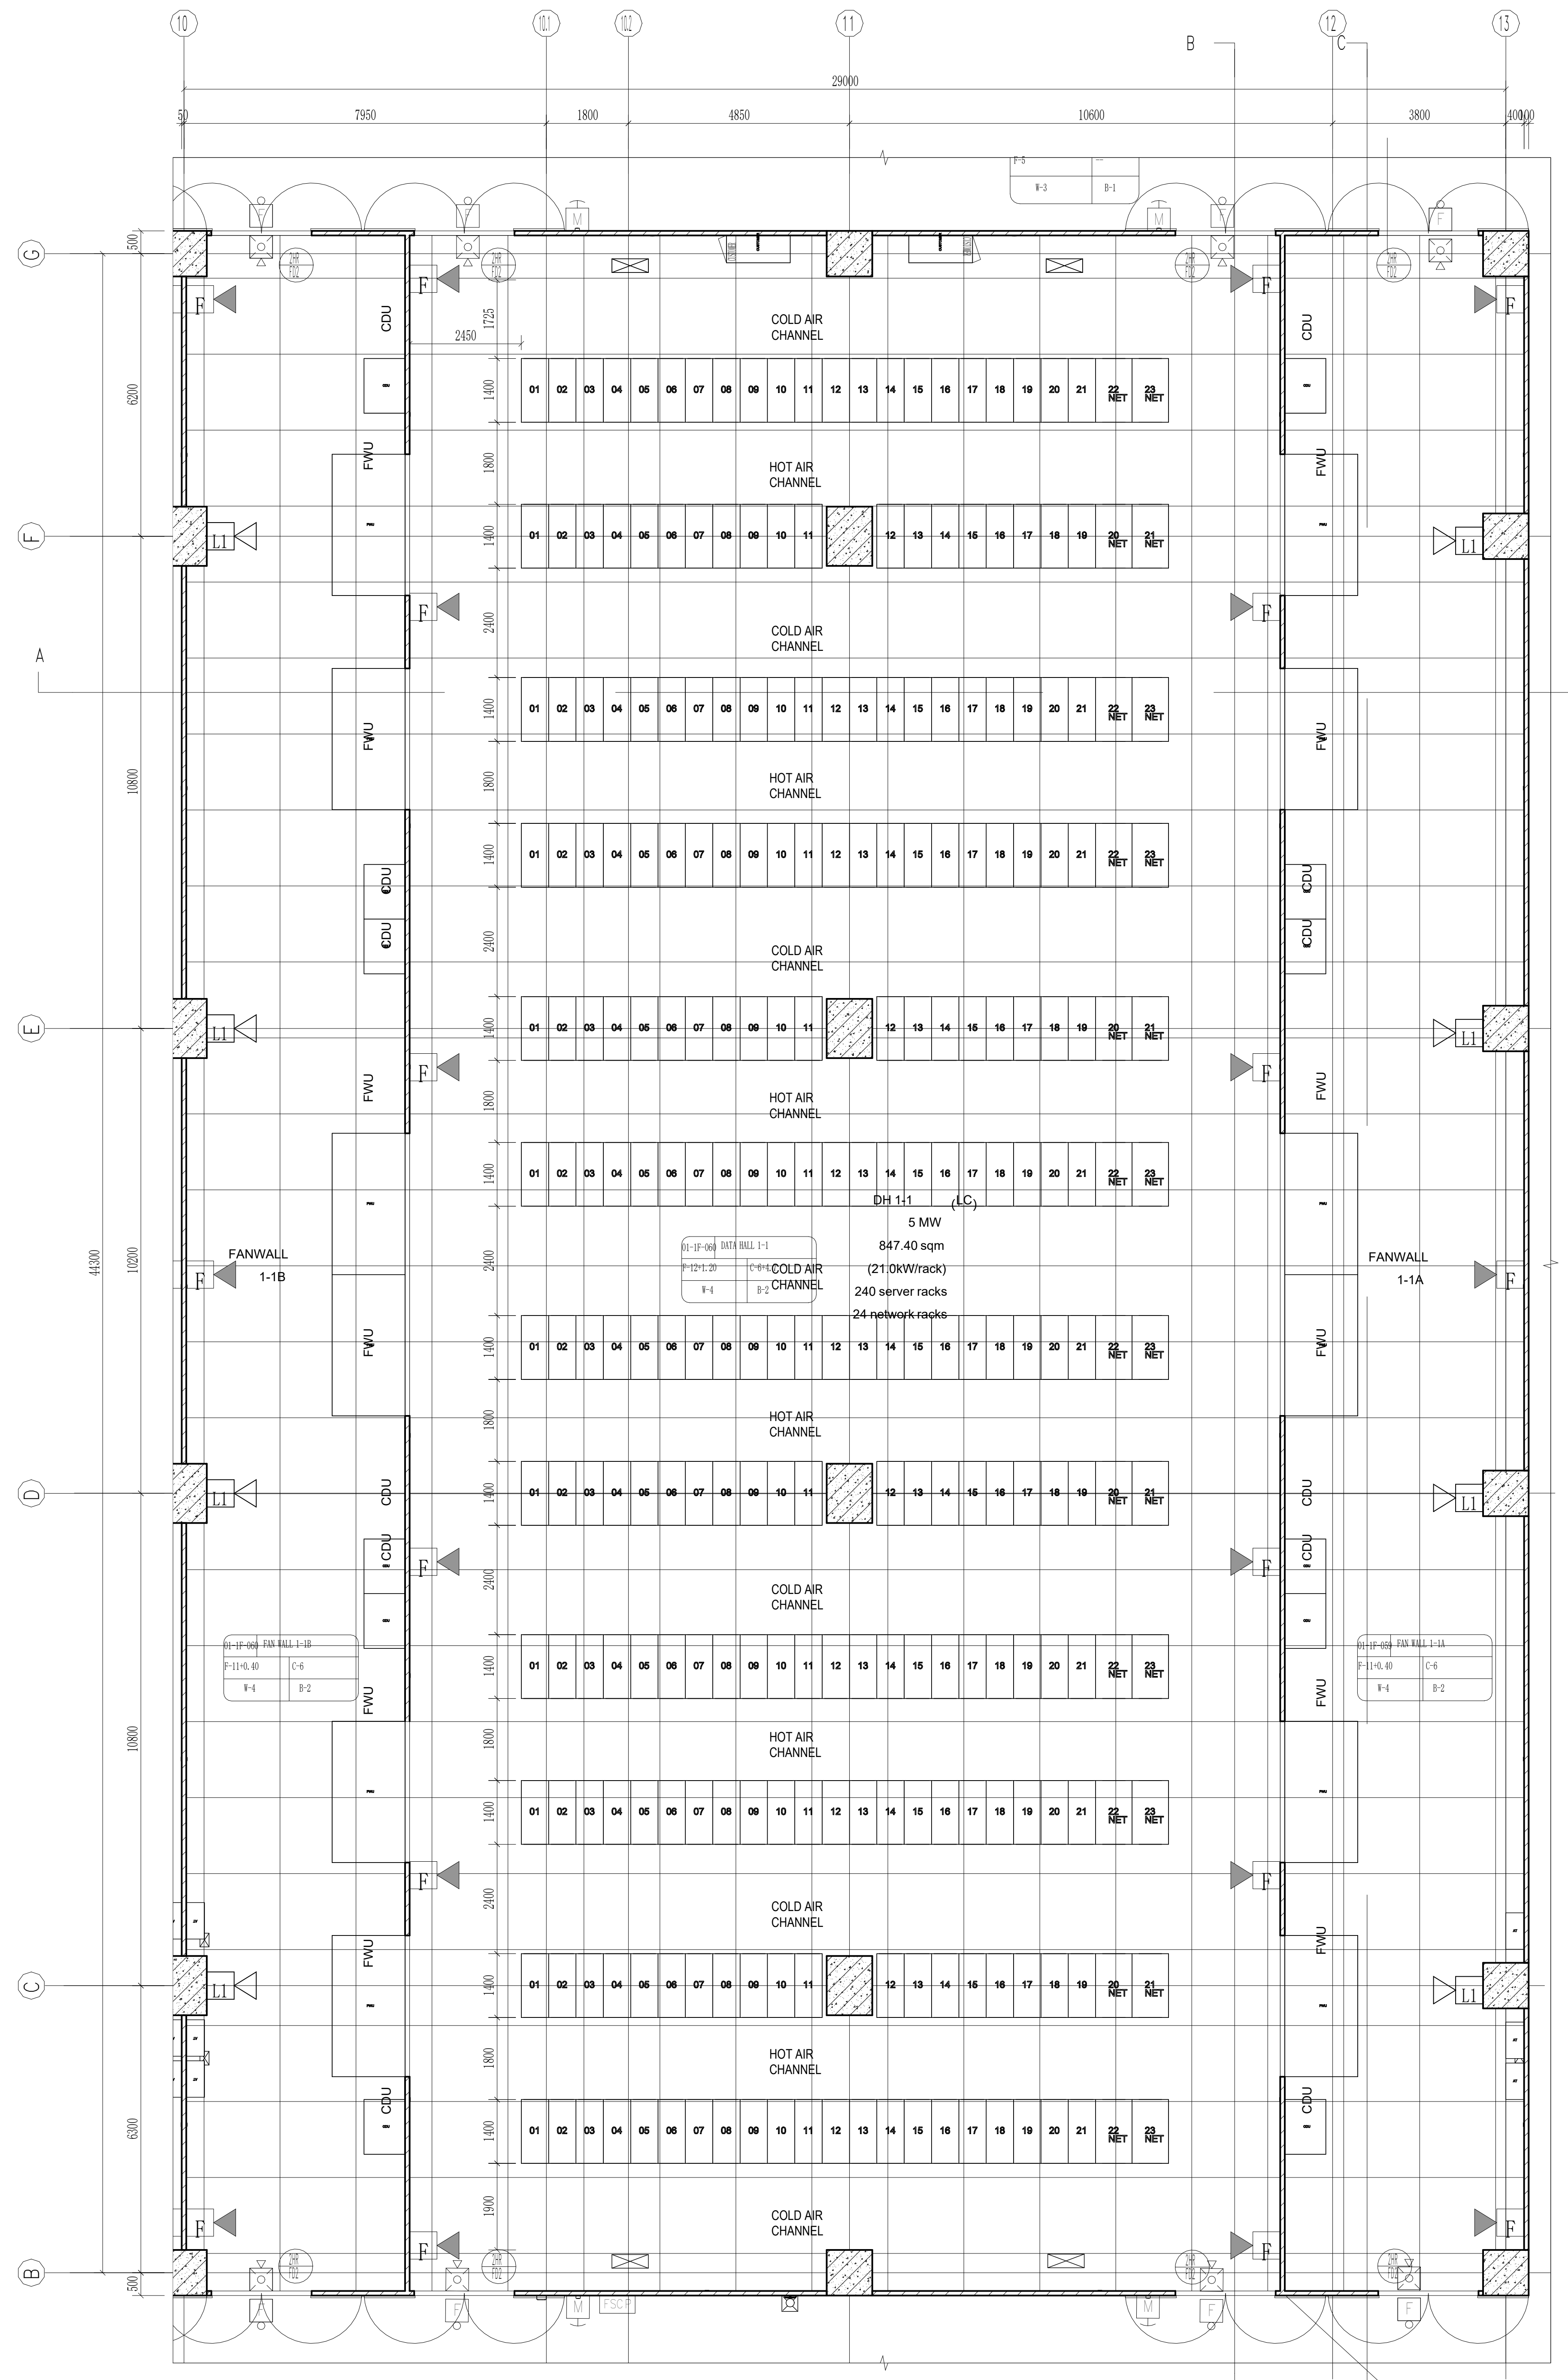
10
Q1
Q2
11
12
13
29000
7950
1800
4850
10600
3800
G
F
E
D
C
B
A
CDU
FWU
COLD AIR CHANNEL
HOT AIR CHANNEL
01 02 03 04 05 06 07 08 09 10 11 12 13 14 15 16 17 18 19 20 21
22 NET
23 NET
FANWALL 1-1B
FANWALL 1-1A
DH 1-1 (LC)
5 MW
847.40 sqm
(21.0kW/rack)
240 server racks
24 network racks
01-1F-060 DATA HALL 1-1
F-12+1.20
W-4
B-2
FSCP
2HR FD2

DH1-1 FAN WALL 1-1A 1-1B FLOOR PLAN

Scale 1:75

THE "SFL" MARKED IN THE DRAWING REFERS TO THE STRUCTURAL FLOOR LEVEL, WHILE THE FINISHED FLOOR LEVEL (FFL) IS DETERMINED BASED ON FLOOR FINISHES.

Room Number	Room Name	Room Type	0kW/RACK	12kW/RACK	16kW/RACK	21kW/RACK	Rack Count	Design IT Load (Mw)
01-1F-060	Data Hall1-1	Liquid-cooled	0	0	24	240	264	5

Note On Levels- All Levels Shown Are Absolute Elevation	
☒	0kW/RACK
▯	12kW/RACK
⊠	16kW/RACK
⧄	21kW/RACK

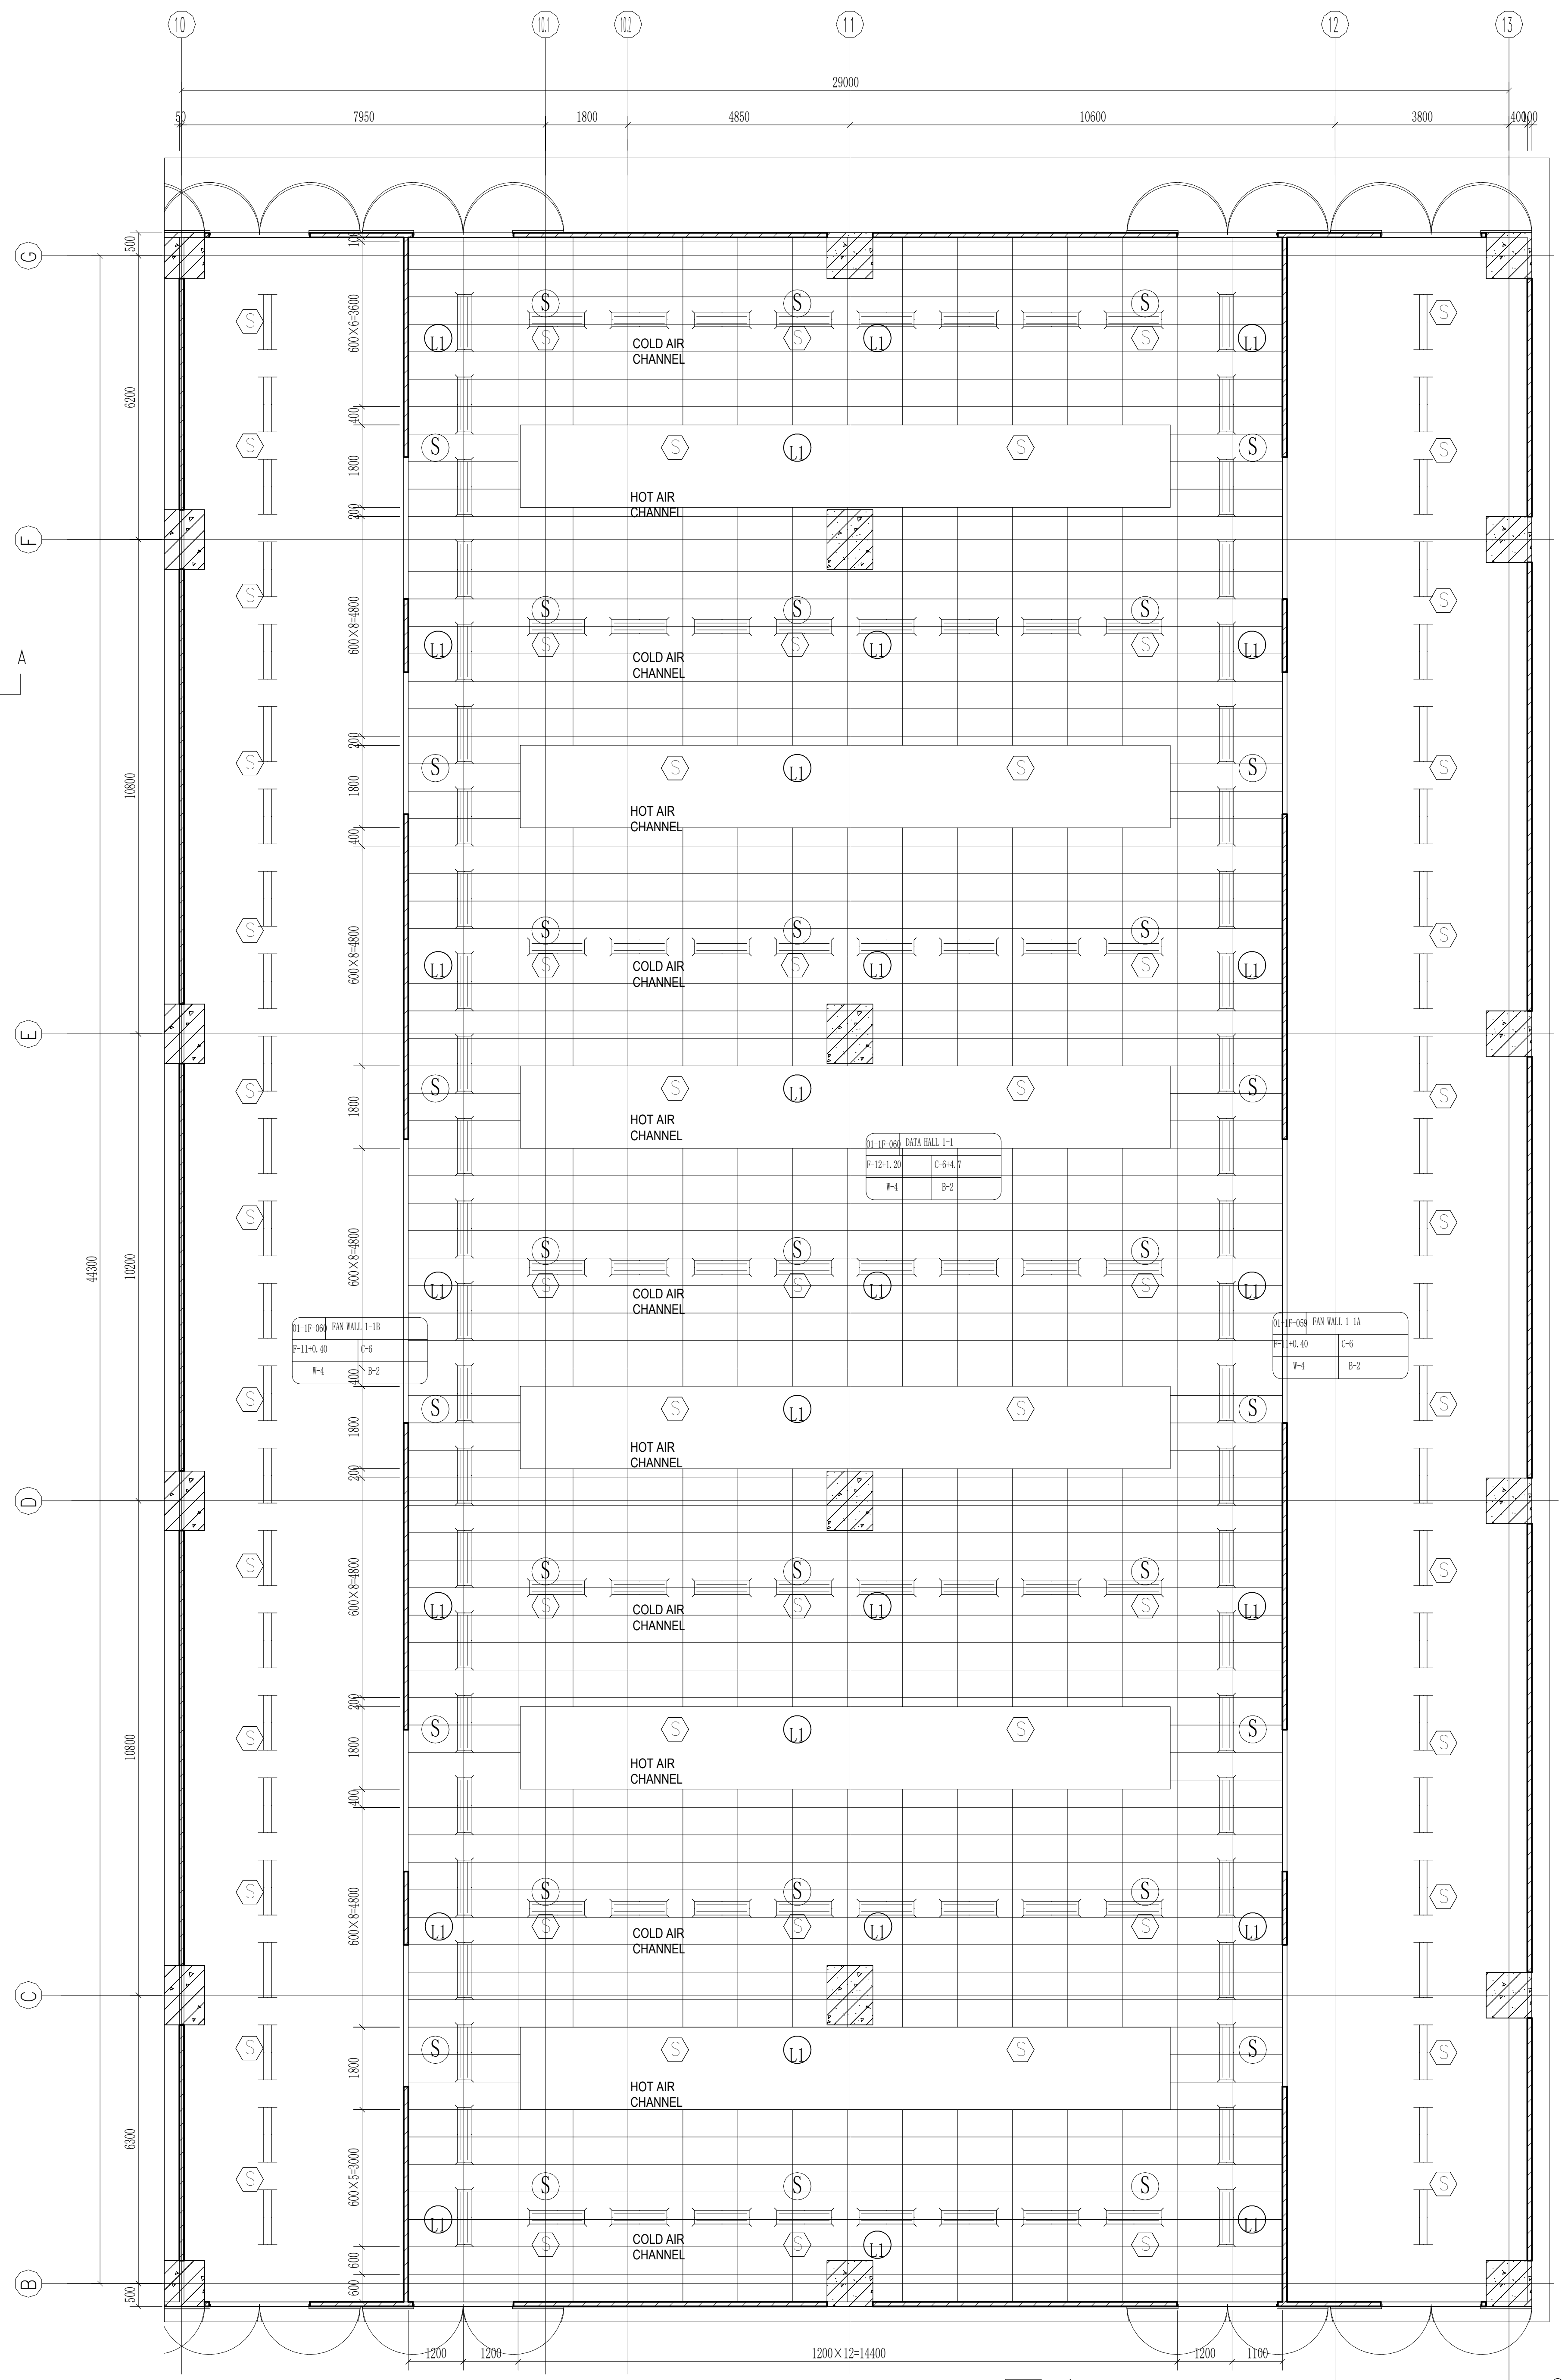
10
Q1
Q2
11
12
13
29000
7950
1800
4850
10600
3800
G
F
E
D
C
B
COLD AIR CHANNEL
HOT AIR CHANNEL
S
L1
600×6=3600
600×8=4800
600×5=3000
1800
1200
1100
1200×12=14400
01-1F-060 DATA HALL 1-1
FAN WALL 1-1B
FAN WALL 1-1A
W-4
B-2

DH1-1 CEILING LAYOUT

Scale 1:75

PROVIDE 100MM HIGH CONCRETE UPSTAND AT THE LOWER PART

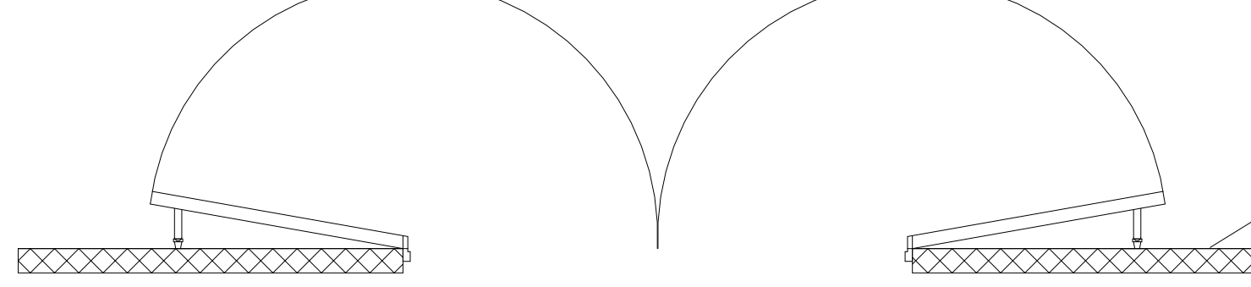

DOOR STOPPER
DETAILED IFC STAGE NODE DETAIL DRAWING

DOOR STOPPER DETAIL

2MM THICK STAINLESS STEEL PROTECTIVE PLATE IS INSTALLED FROM THE GROUND UP TO A HEIGHT OF 1.5 METERS. DETAILED IFC STAGE NODE DETAIL DRAWING

Scale 1:25

◀	FIRE ALARM SPEAKER WALL MOUNTED
⊡	COMBINATION HORN/VISIBLE
○	SURFACE MOUNTED SMOKE DETECTOR, PHOTOELECTRIC TYPE
⬡	PHOTOELECTRIC SMOKE DETECTOR
▤	LED double tube lamp; Ceiling Mounted; System Power 2x20W (+/-10% In Tolerance); System Lumens >2x2000lm (+/- 10% In Tolerance); Luminaire Efficacy >100lm/w; CCT 5000K; CRI>80; CPF>0.9; Input Voltage 220V-240V 50/60Hz (Mounting height 3.0m)
▭	LED double tube lamp; Ceiling Mounted; System Power 2x20W (+/-10% In Tolerance); System Lumens >2x2000lm (+/- 10% In Tolerance); Luminaire Efficacy >100lm/w; CCT 5000K; CRI>80; CPF>0.9; Input Voltage 220V-240V 50/60Hz (Mounting height 3.0m)
F	ALARM BELL
○	CEILING SPEAKER

CLIENT :

GULF EDGE DC 01

87 Wireless Road, M Thai Tower 11th. Floor, All Seasons Place, Lumpini,
Pathumwan, Bangkok 10330, Thailand

CONTRACTOR :

华西发展(泰国)有限公司
บริษัท หัวซือ ดีเวลลอปเม้นต์ (ประเทศไทย) จำกัด
HUASHI DEVELOPMENT CO.,LTD
No. 202, Room No. 1403, 14/F, Le Concorde Building,
Ratchadapisek Road, Huaykhwang Sub-District,
Huaykhwang District, Bangkok Metropolitan 10310.

CONSULTANT :

ARbay
บริษัท เอ อาร์ เบย์ จำกัด
ARbay Company Limited
31 st Floor Bangkok Insurance Building
25 South Sathorn road Thungmahamek
Sathorn Bangkok 10120 THAILAND
T +66 (0) 2286 8199
F +66 (0) 2286 2863
info@arbay.co.th

CONSULTANT :

Qbic Engineers & Architects Co.,Ltd.
8 Soi KALONG 4 SANAMBINNAM ROAD,
THASAI SUB-DISTRICT, MUANG NONTHABURI DISTRICT
, NONTHABURI.
Tel 662-950-4374
Fax 662-580-3231
E-Mail : qbic@qbic.co.th, www.qbic.co.th
QBIC ENGINEERS AND ARCHITECTS CO.,LTD.

CONSULTANT :

MITR
MITR TECHNICAL CONSULTANT CO.,LTD.
1168/8 12th FLOOR, LUMPINI TOWER BUILDING,
RAMA IV RD., THUNGMAHAMEK, SATHORN, BANGKOK 10120, THAILAND
TEL : 0-2679-9079-84
FAX : 0-2679-9085 E-mail: mitr_dd@mitr.com

	SIGNATURE
Architect :	SIGNATURE
ประกิด พนานุรัตน์ วสถ. 580 ที่อยู่ 251/1 ถ.จารุเมือง แขวงรองเมือง เขตปทุมวัน กรุงเทพมหานคร โทรศัพท์ 02-286-8199	
Structural Engineer :	SIGNATURE
วิศวกรผู้ออกแบบโครงสร้าง	
ณัฐสม สงวนวงษ์ วย 1423 ที่อยู่ 2/1 ซ.รามคำแหง 150 ถ.รามคำแหง แขวง สะพานสูง เขต สะพานสูง กทม. 10240	ณัฐสม สงวนวงษ์
Structural Inspector :	SIGNATURE
วิศวกรผู้ตรวจสอบโครงสร้าง	
โกมล จุฑาภัทร วย 964 ที่อยู่ 24/18 ซ.นวมินทร์ 129 ถ. นวมินทร์ แขวง นวลจันทร์ เขต บึงกุ่ม กทม. 10230	
Electrical Engineer :	SIGNATURE
วิศวกรผู้ออกแบบระบบไฟฟ้ากำลัง	
นายสุภัทร บูรณวิทย์ วฟก.1265 ที่อยู่ 21 ซอยทานสัมฤทธิ 13 ตำบลท่าทราย อ.เมืองนนทบุรี จ.นนทบุรี 11000	สุภัทร
Mechanical Engineer :	SIGNATURE
วิศวกรผู้ออกแบบระบบเครื่องกลและปรับอากาศ	
นายประสิทธิ์ เกียวสุนทร วก.1221 ที่อยู่ 44/372 ซอยบางกระดี 35/1 แขวงแสมดำ เขตบางขุนเทียน กทม. 10150	ประสิทธิ์
Sanitary Engineer :	SIGNATURE
วิศวกรผู้ออกแบบระบบสุขาภิบาล และดับเพลิง	
นายทศวรรษ สนันฤทธิ์ วส. 215 ที่อยู่ บ้านเลขที่ 99/107 หมู่ที่ 3 ต.ศีรษะจรเข้น้อย อ.บางเสาธง จ.สมุทรปราการ 10540	ทศวรรษ

ISSUE/REVISION

REV.	DESCRIPTION	DATE
A	90% DEVELOPED	09/05/2026

PROJECT NAME :

GEDC 01

LOCATION:
Nikhom Phattana district, Rayong ,industrial estate,CPGC

BUILDING :

90% DEVELOPED

TITLE :

ROOM DETAIL-1F-DATAHALL1-1(LC),
FAN WALLROOM 1-1A,1-1B PLAN

JOB NO.		SCALE	1 : 75
DRAWN	ZYY	REF.	
CHECKED	LJC	DWG. NO.	MPK01A-90-A-RD-101
APPROVED	LXD		
DATE	2026.05.09		

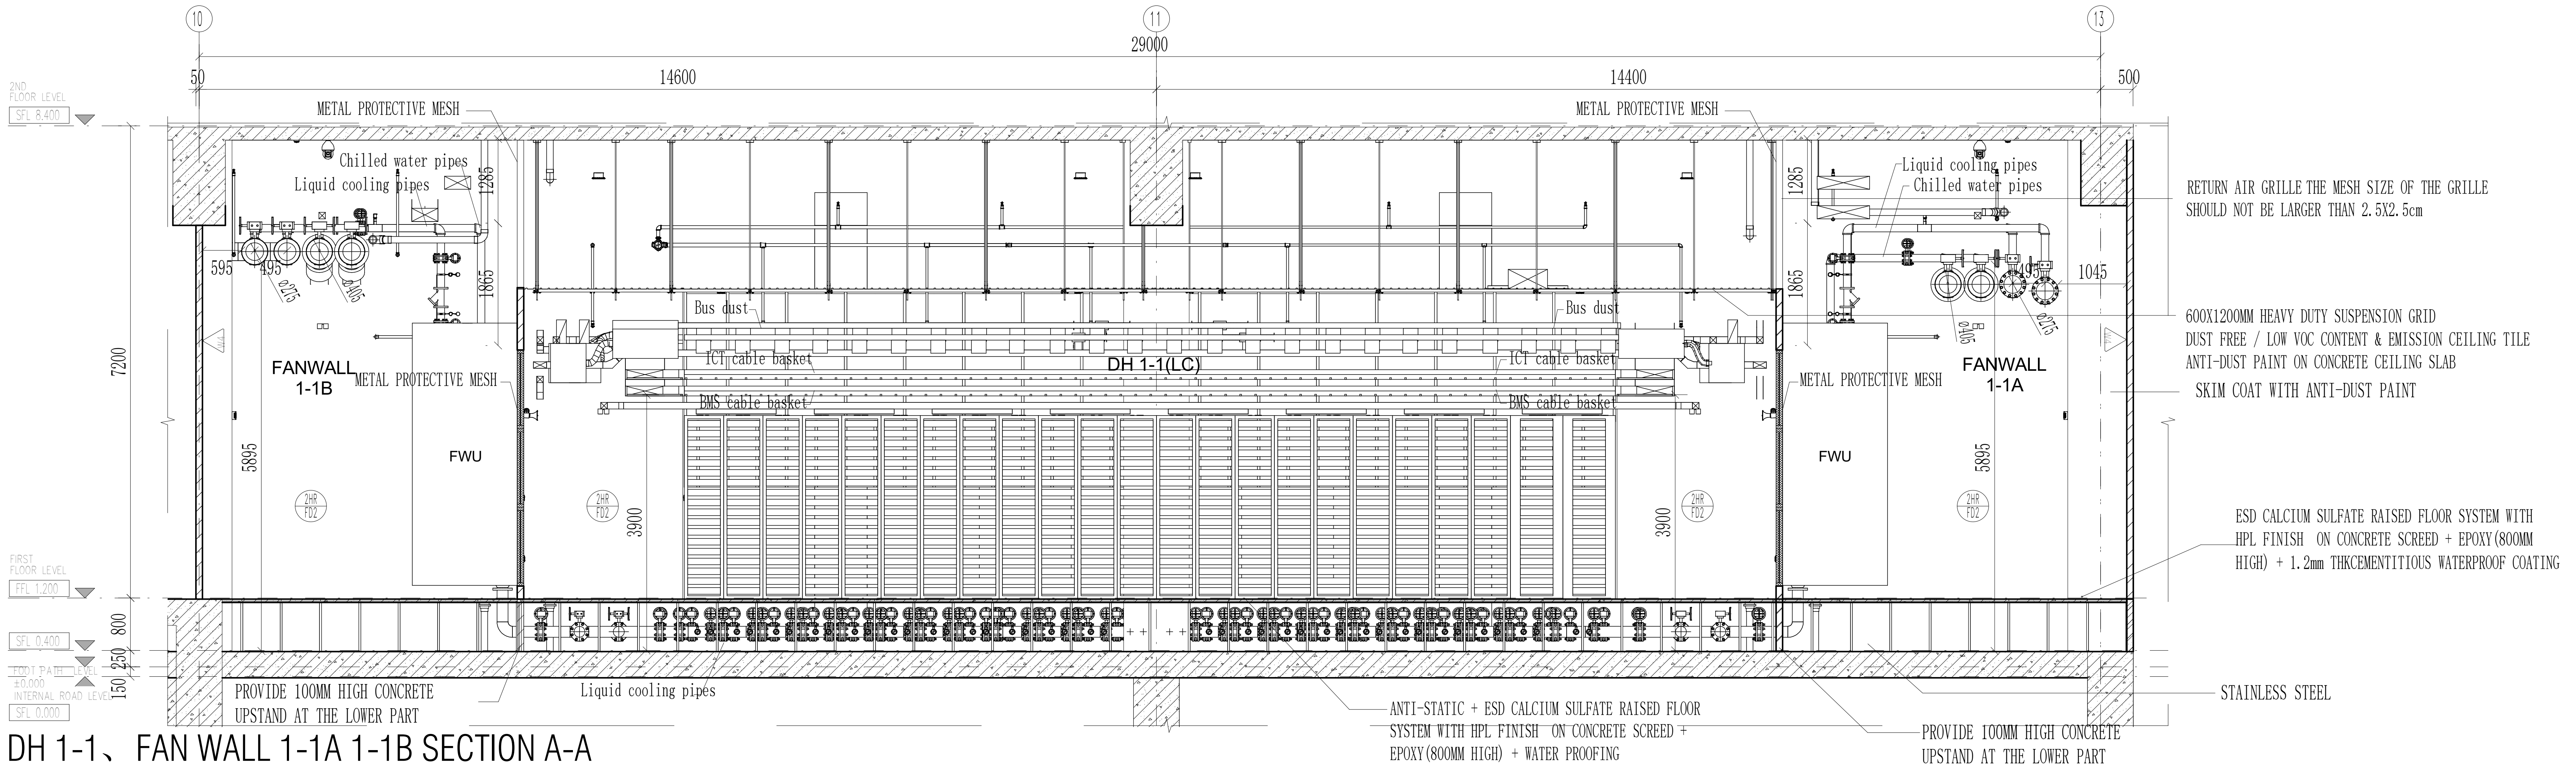
10
11
13
29000
50
14600
14400
500
2ND FLOOR LEVEL
SFL 8.400
METAL PROTECTIVE MESH
Chilled water pipes
Liquid cooling pipes
1285
595
495
Ø275
Ø405
1865
FANWALL 1-1B
METAL PROTECTIVE MESH
FWU
Bus dust
ICT cable basket
BMS cable basket
DH 1-1(LC)
7200
5895
3900
2HR FD2
1045
FANWALL 1-1A
FIRST FLOOR LEVEL
FFL 1.200
SFL 0.400
FOOT PATH LEVEL ±0.000
INTERNAL ROAD LEVEL
SFL 0.000
800
250
150
PROVIDE 100MM HIGH CONCRETE UPSTAND AT THE LOWER PART
Liquid cooling pipes
ANTI-STATIC + ESD CALCIUM SULFATE RAISED FLOOR SYSTEM WITH HPL FINISH ON CONCRETE SCREED + EPOXY(800MM HIGH) + WATER PROOFING
PROVIDE 100MM HIGH CONCRETE UPSTAND AT THE LOWER PART
RETURN AIR GRILLE THE MESH SIZE OF THE GRILLE SHOULD NOT BE LARGER THAN 2.5X2.5cm
600X1200MM HEAVY DUTY SUSPENSION GRID
DUST FREE / LOW VOC CONTENT & EMISSION CEILING TILE
ANTI-DUST PAINT ON CONCRETE CEILING SLAB
SKIM COAT WITH ANTI-DUST PAINT
ESD CALCIUM SULFATE RAISED FLOOR SYSTEM WITH HPL FINISH ON CONCRETE SCREED + EPOXY(800MM HIGH) + 1.2mm THKCEMENTITIOUS WATERPROOF COATING
STAINLESS STEEL

DH 1-1、FAN WALL 1-1A 1-1B SECTION A-A

Scale 1:50

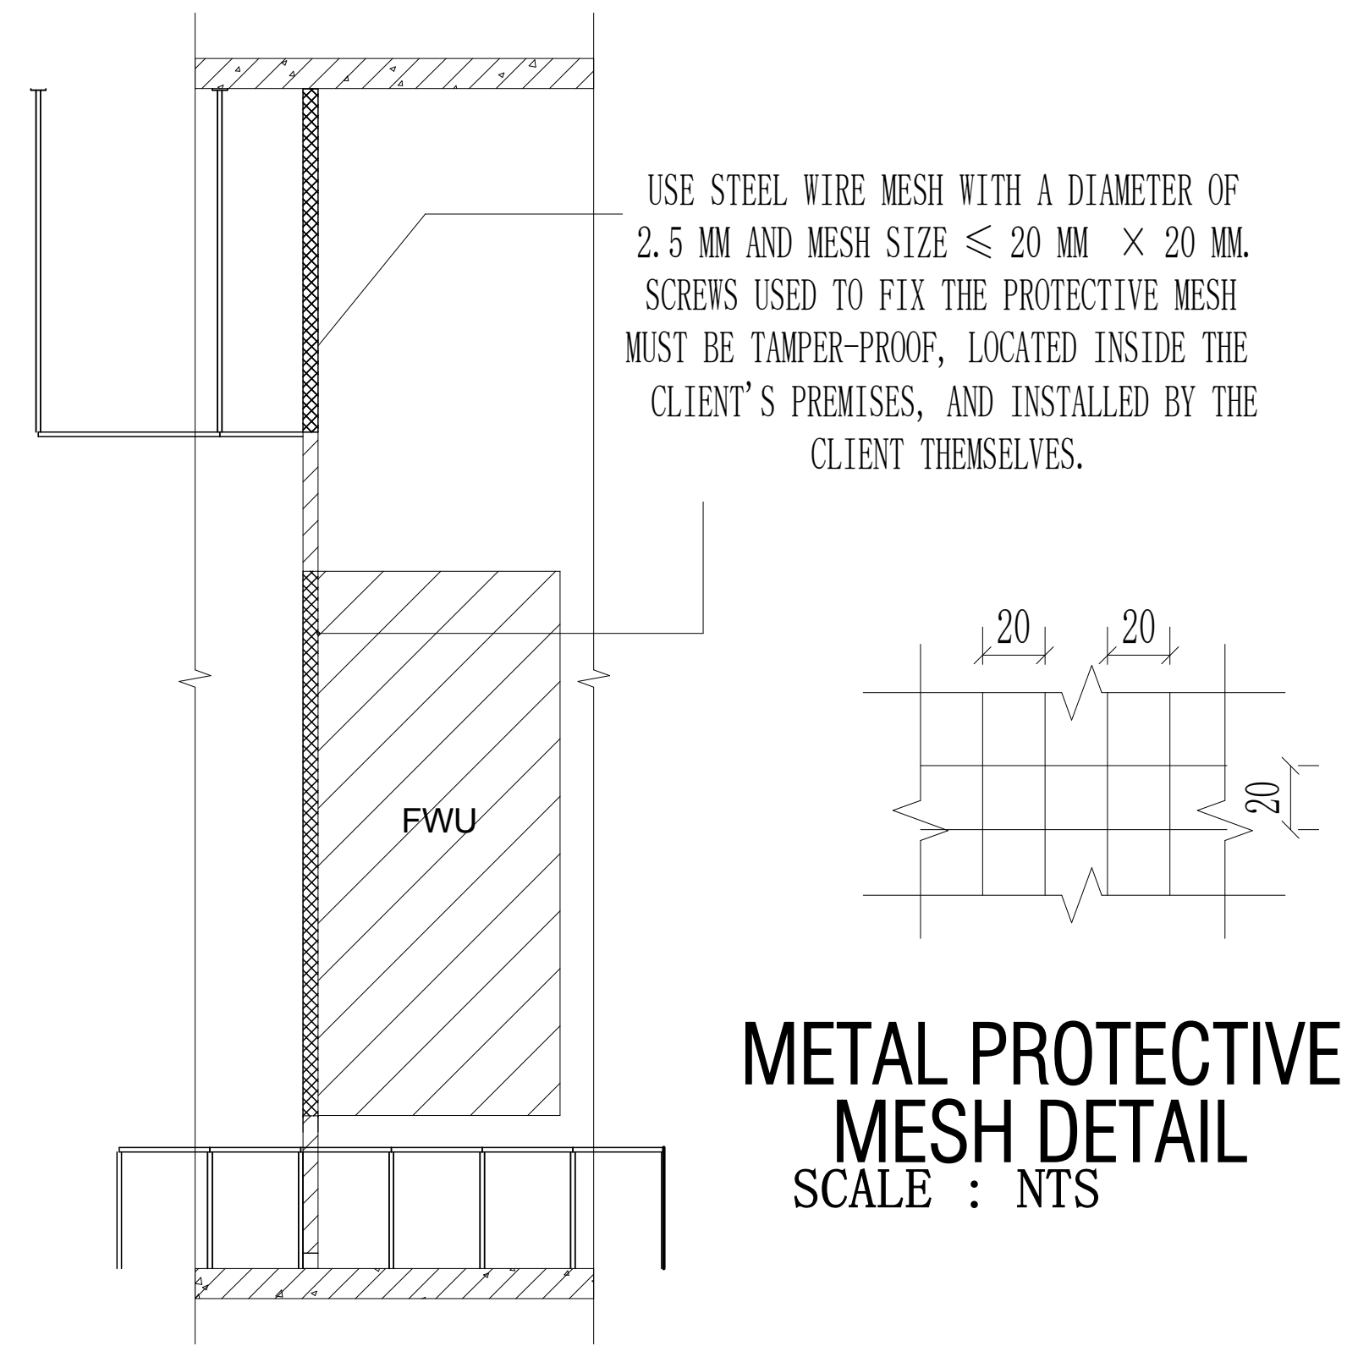
USE STEEL WIRE MESH WITH A DIAMETER OF 2.5 MM AND MESH SIZE ≤ 20 MM × 20 MM. SCREWS USED TO FIX THE PROTECTIVE MESH MUST BE TAMPER-PROOF, LOCATED INSIDE THE CLIENT'S PREMISES, AND INSTALLED BY THE CLIENT THEMSELVES.
20
20
20
FWU

METAL PROTECTIVE MESH DETAIL

SCALE : NTS

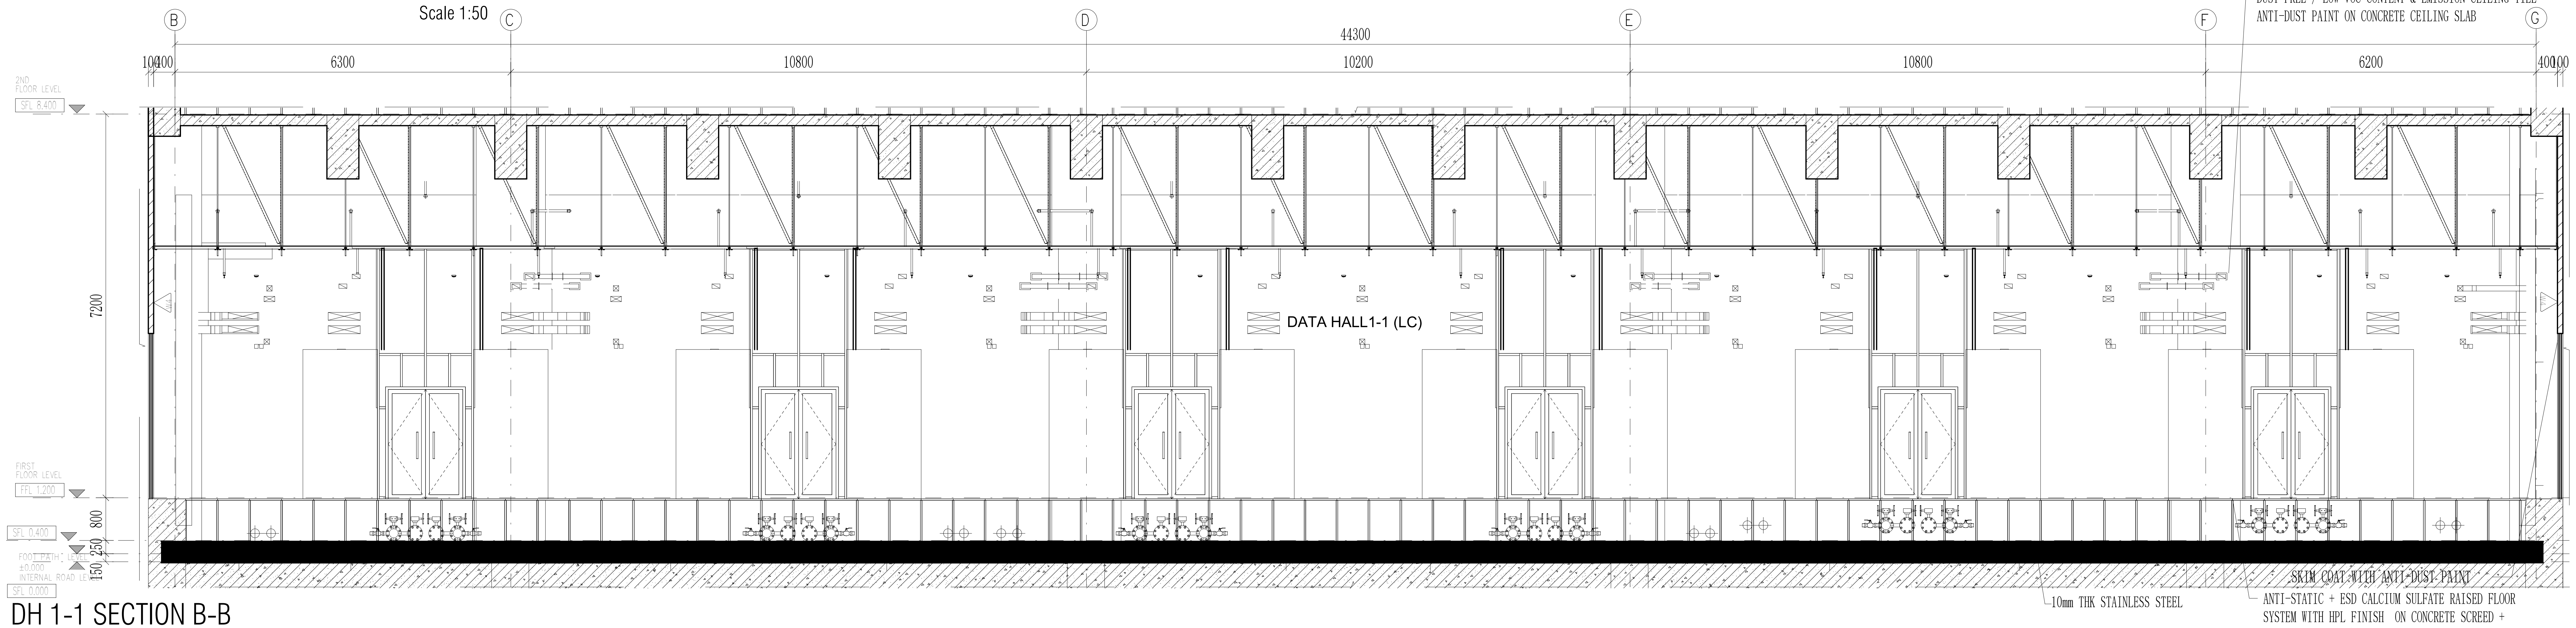
600X1200MM HEAVY DUTY SUSPENSION GRID
DUST FREE / LOW VOC CONTENT & EMISSION CEILING TILE
ANTI-DUST PAINT ON CONCRETE CEILING SLAB
B
C
D
E
F
G
44300
100
400
6300
10800
10200
10800
6200
400
100
2ND FLOOR LEVEL
SFL 8.400
7200
DATA HALL1-1 (LC)
FIRST FLOOR LEVEL
FFL 1.200
SFL 0.400
FOOT PATH LEVEL ±0.000
INTERNAL ROAD LEVEL
SFL 0.000
800
250
150
10mm THK STAINLESS STEEL
SKIM COAT WITH ANTI-DUST PAINT
ANTI-STATIC + ESD CALCIUM SULFATE RAISED FLOOR SYSTEM WITH HPL FINISH ON CONCRETE SCREED + EPOXY(800MM HIGH) + WATER PROOFING

DH 1-1 SECTION B-B

Scale 1:50

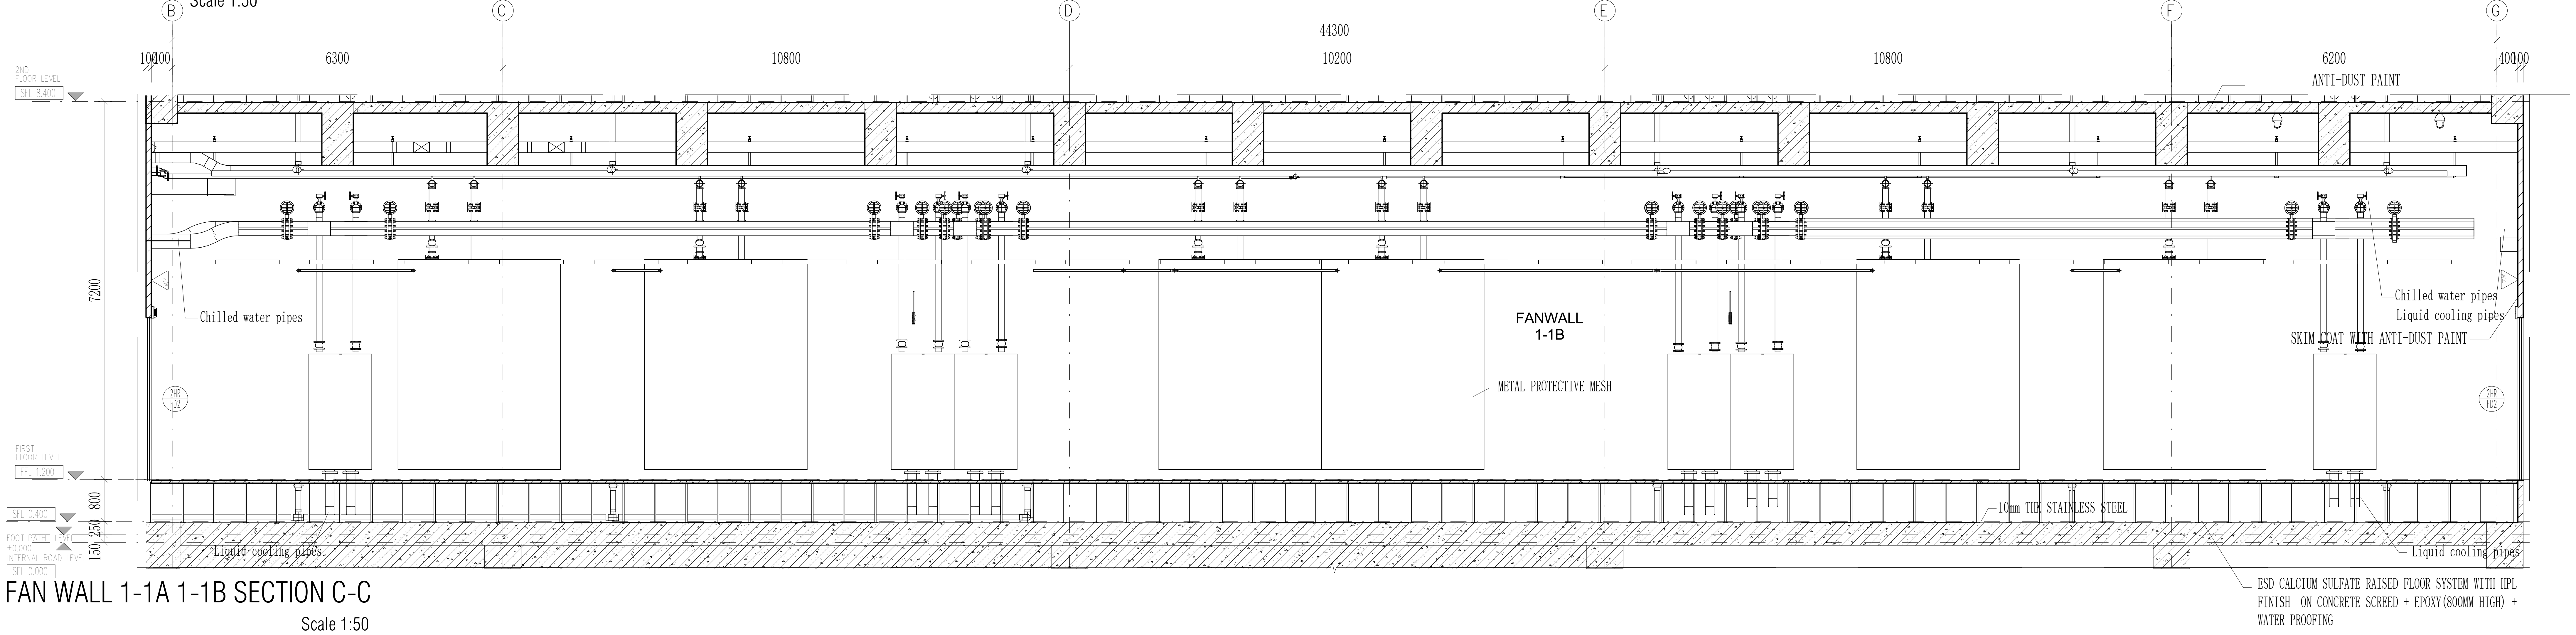
B
C
D
E
F
G
44300
100
400
6300
10800
10200
10800
6200
400
100
ANTI-DUST PAINT
2ND FLOOR LEVEL
SFL 8.400
7200
Chilled water pipes
FANWALL 1-1B
METAL PROTECTIVE MESH
Chilled water pipes
Liquid cooling pipes
SKIM COAT WITH ANTI-DUST PAINT
FIRST FLOOR LEVEL
FFL 1.200
SFL 0.400
FOOT PATH LEVEL ±0.000
INTERNAL ROAD LEVEL
SFL 0.000
800
250
150
10mm THK STAINLESS STEEL
Liquid cooling pipes
Liquid cooling pipes
ESD CALCIUM SULFATE RAISED FLOOR SYSTEM WITH HPL FINISH ON CONCRETE SCREED + EPOXY(800MM HIGH) + WATER PROOFING

FAN WALL 1-1A 1-1B SECTION C-C

Scale 1:50

CLIENT :

GULF EDGE DC 01

87 Wireless Road, M Thai Tower 11th. Floor, All Seasons Place, Lumpini,
Pathumwan, Bangkok 10330, Thailand

CONTRACTOR :

华西发展(泰国)有限公司
บริษัท หัวซือ ดีเวลลอปเม้นต์ (ประเทศไทย) จำกัด
HUASHI DEVELOPMENT CO.,LTD
No. 202, Room No. 1403, 14/F, Le Concorde Building,
Ratchadapisek Road, Huaykhwang Sub-District,
Huaykhwang District, Bangkok Metropolitan 10310.

CONSULTANT :

ARbay
บริษัท เอ อาร์ เบย์ จำกัด
ARbay Company Limited
31 st Floor Bangkok Insurance Building
25 South Sathorn road Thungmahamek
Sathorn Bangkok 10120 THAILAND
T +66 (0) 2286 8199
F +66 (0) 2286 2863
info@arbay.co.th

CONSULTANT :

Qbic Engineers & Architects Co.,Ltd.
8 Soi KALONG 4 SANAMBINNAM ROAD,
THASAI SUB-DISTRICT, MUANG NONTHABURI DISTRICT
, NONTHABURI.
Tel 662-950-4374
Fax 662-580-3231
E-Mail : qbic@qbic.co.th, www.qbic.co.th
QBIC ENGINEERS AND ARCHITECTS CO.,LTD.

CONSULTANT :

MITR
MITR TECHNICAL CONSULTANT CO.,LTD.
1168/8 12th FLOOR, LUMPINI TOWER BUILDING,
RAMA IV RD., THUNGMAHAMEK, SATHORN, BANGKOK 10120, THAILAND
TEL : 0-2679-9079-84
FAX : 0-2679-9085 E-mail: mitr_dd@mitr.com

Architect :	SIGNATURE
ประกิต พนานุรัตน์ วสถ. 580 ที่อยู่ 251/1 ถ.จารุเมือง แขวงรองเมือง เขตปทุมวัน กรุงเทพมหานคร โทรศัพท์ 02-286-8199	
Structural Engineer :	SIGNATURE
วิศวกรผู้ออกแบบโครงสร้าง	
ณัฐสม สงวนวงษ์ วย 1423 ที่อยู่ 2/1 ซ.รามคำแหง 150 ถ.รามคำแหง แขวง สะพานสูง เขต สะพานสูง กทม. 10240	ณัฐสม สงวนวงษ์
Structural Inspector :	SIGNATURE
วิศวกรผู้ตรวจสอบโครงสร้าง	
โกมล จุฑาภัทร วย 964 ที่อยู่ 24/18 ซ.นวมินทร์ 129 ถ. นวมินทร์ แขวง นวลจันทร์ เขต บึงกุ่ม กทม. 10230	
Electrical Engineer :	SIGNATURE
วิศวกรผู้ออกแบบระบบไฟฟ้ากำลัง	
นายสุภัทร บูรณวิทย์ วฟก.1265 ที่อยู่ 21 ซอยทานสัมฤทธิ์ 13 ตำบลท่าทราย อ.เมืองนนทบุรี จ.นนทบุรี 11000	
Mechanical Engineer :	SIGNATURE
วิศวกรผู้ออกแบบระบบเครื่องกลและปรับอากาศ	
นายประสิทธิ์ เกี้ยวสุนทร วก.1221 ที่อยู่ 44/372 ซอยบางกระดี่ 35/1 แขวงแสมดำ เขตบางขุนเทียน กทม. 10150	ประสิทธิ์
Sanitary Engineer :	SIGNATURE
วิศวกรผู้ออกแบบระบบสุขาภิบาล และดับเพลิง	
นายทศวรรษ สนั่นฤทธิ์ วส. 215 ที่อยู่ บ้านเลขที่ 99/107 หมู่ที่ 3 ต.ศีรษะจรเข้น้อย อ.บางเสาธง จ.สมุทรปราการ 10540	ทศวรรษ

ISSUE/REVISION

REV.	DESCRIPTION	DATE
A	90% DEVELOPED	09/05/2026

PROJECT NAME :

GEDC 01

LOCATION:
Nikhom Phattana district, Rayong ,industrial estate,CPGC

BUILDING :
MAIN BUILDING

90% DEVELOPED

TITLE :

ROOM DETAIL-1F-DATAHALL1-1(LC)、
FAN WALLROOM 1-1A,1-1BSECTION

JOB NO.		SCALE	1 : 50
DRAWN	ZYY	REF.	
CHECKED	LJC	DWG. NO.	MPK01A-90-A-RD-102
APPROVED	LXD		
DATE	2026.05.09		

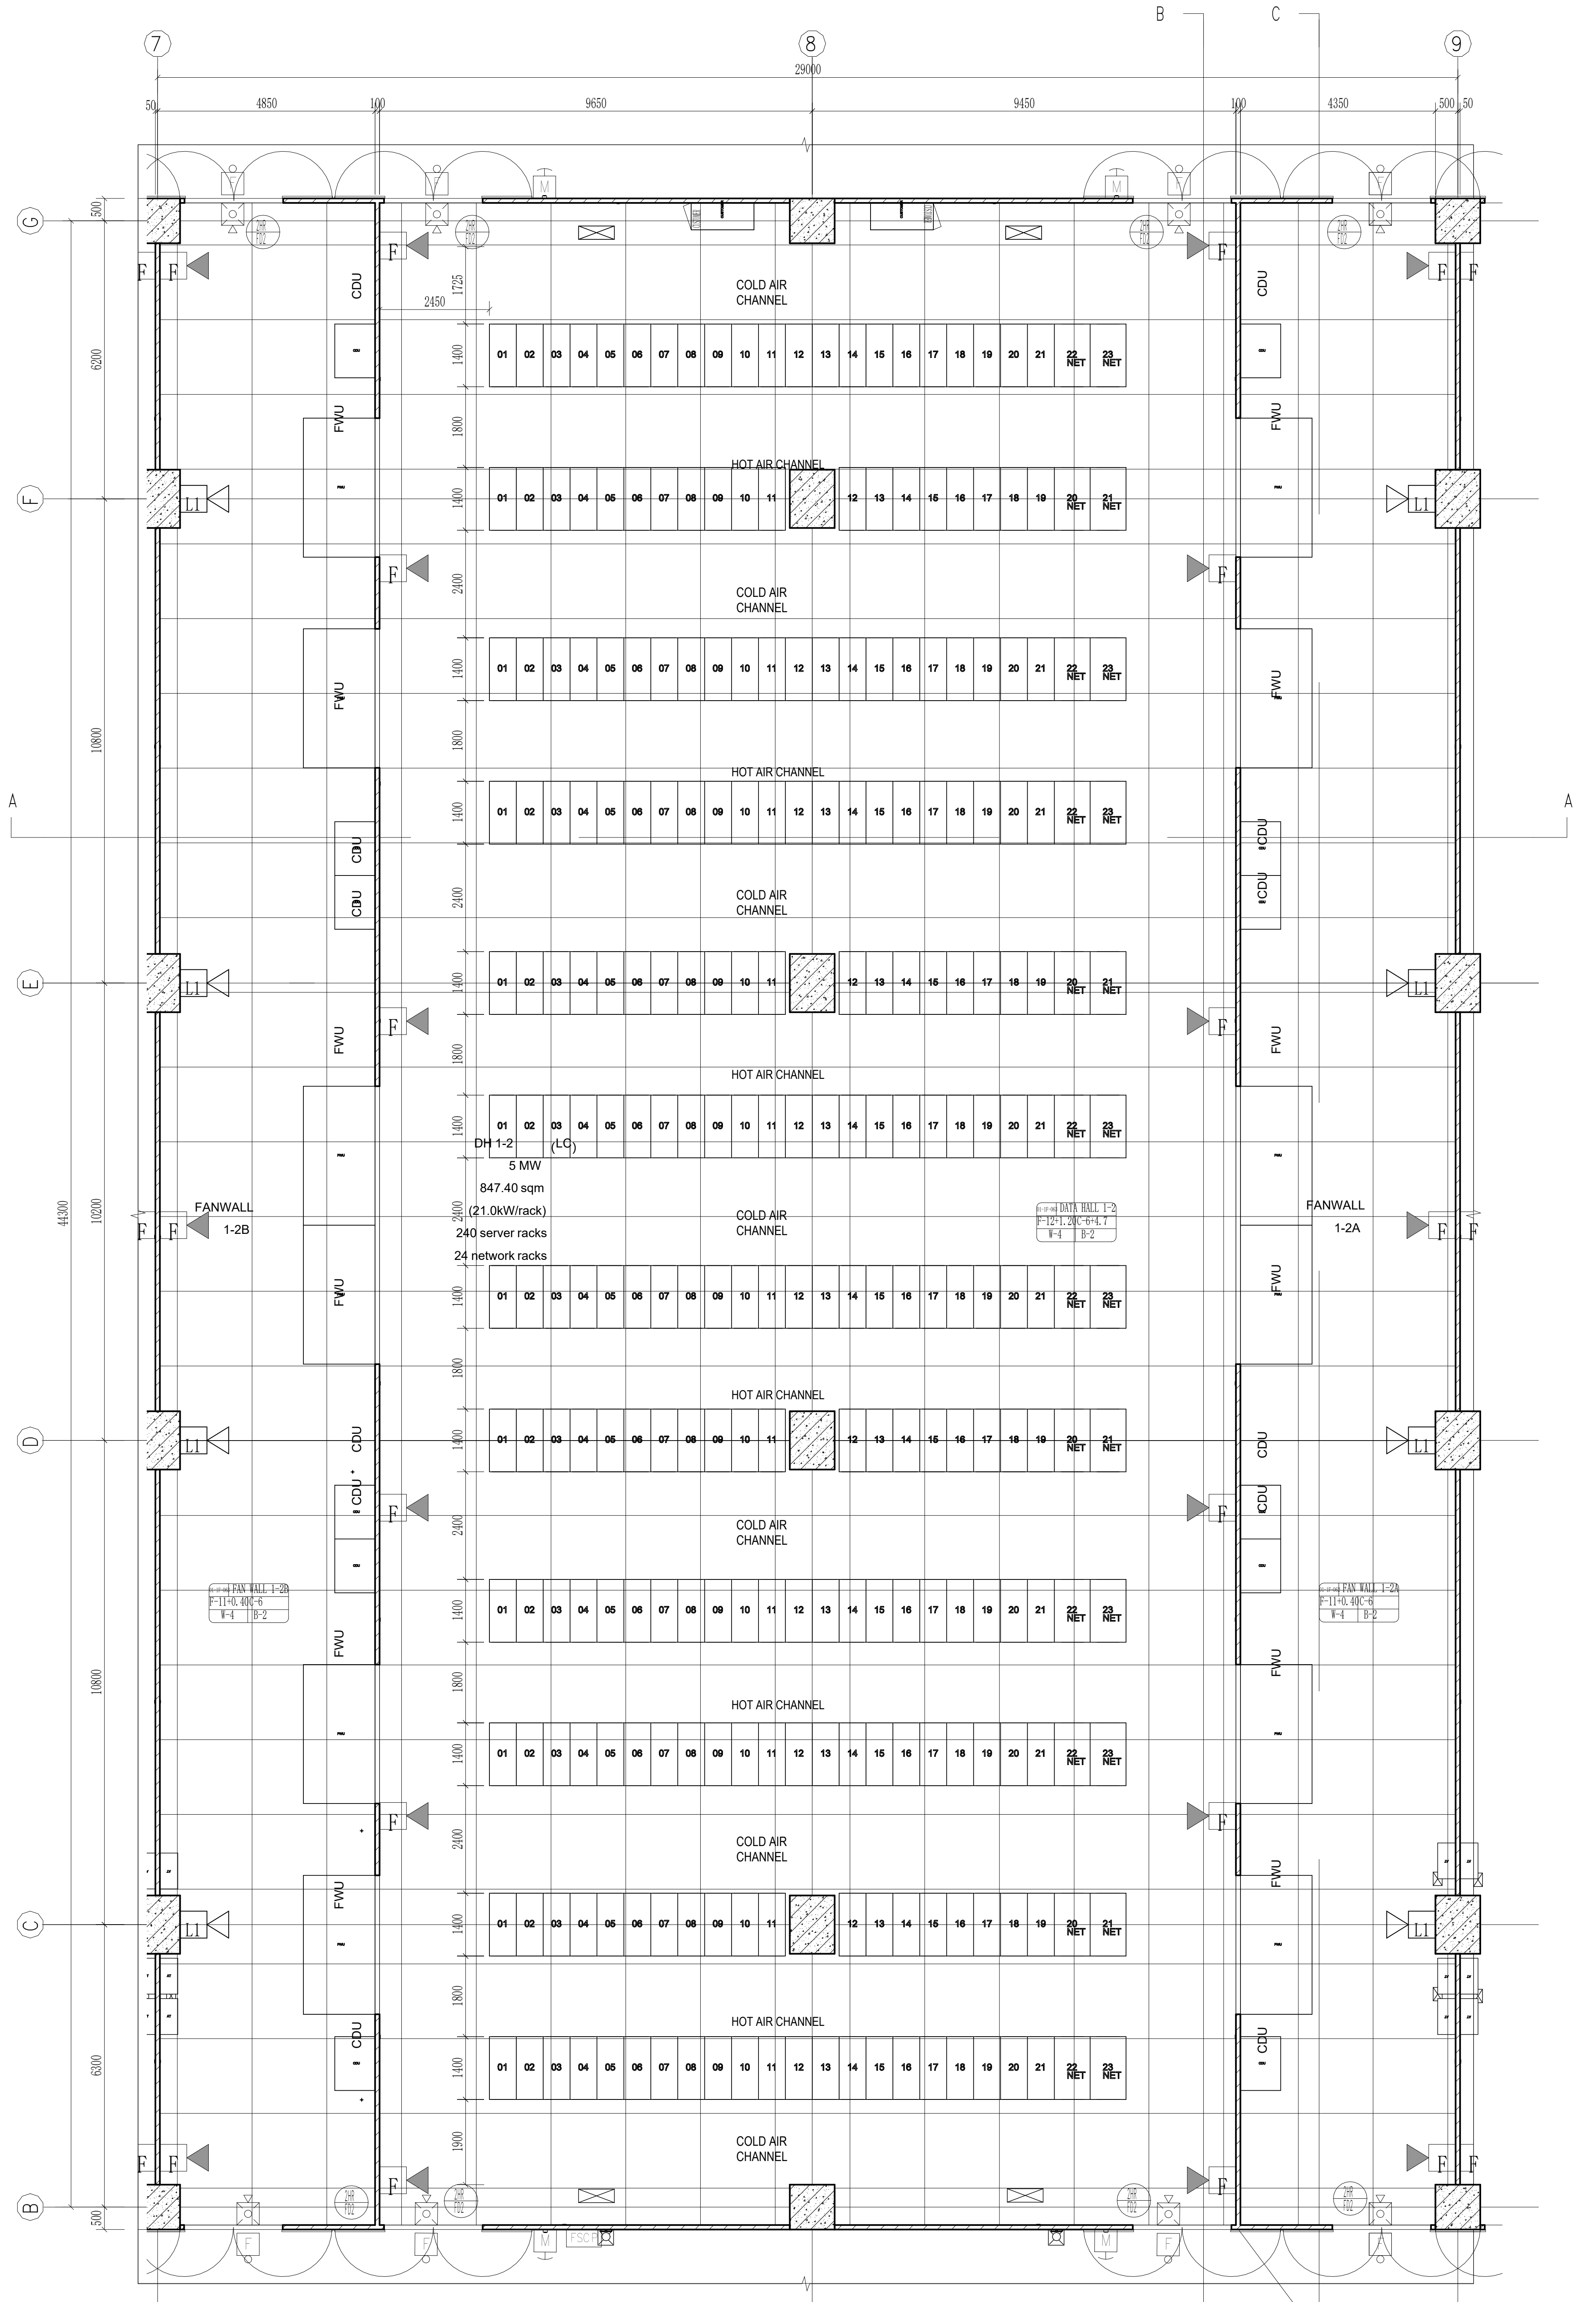

DH1-2、FAN WALL 1-2A、FAN WALL 1-2B FIRST FLOOR PLAN

Scale 1:75

THE "SFL" MARKED IN THE DRAWING REFERS TO THE STRUCTURAL FLOOR LEVEL, WHILE THE FINISHED FLOOR LEVEL (FFL) IS DETERMINED BASED ON FLOOR FINISHES.

PROVIDE 100MM HIGH CONCRETE
UPSTAND AT THE LOWER PART

Room Number	Room Name	Room Type	0kW/RACK	12kW/RACK	16kW/RACK	21kW/RACK	Rack Count	DesignITLoad (Mw)
01-1F-063	Data Hall1-2	Liquid-cooled	0	0	24	240	264	5

Note On Levels- All Levels Shown Are Absolute Elevation	
☒	0kW/RACK
▯	12kW/RACK
☒	16kW/RACK
⍁	21kW/RACK

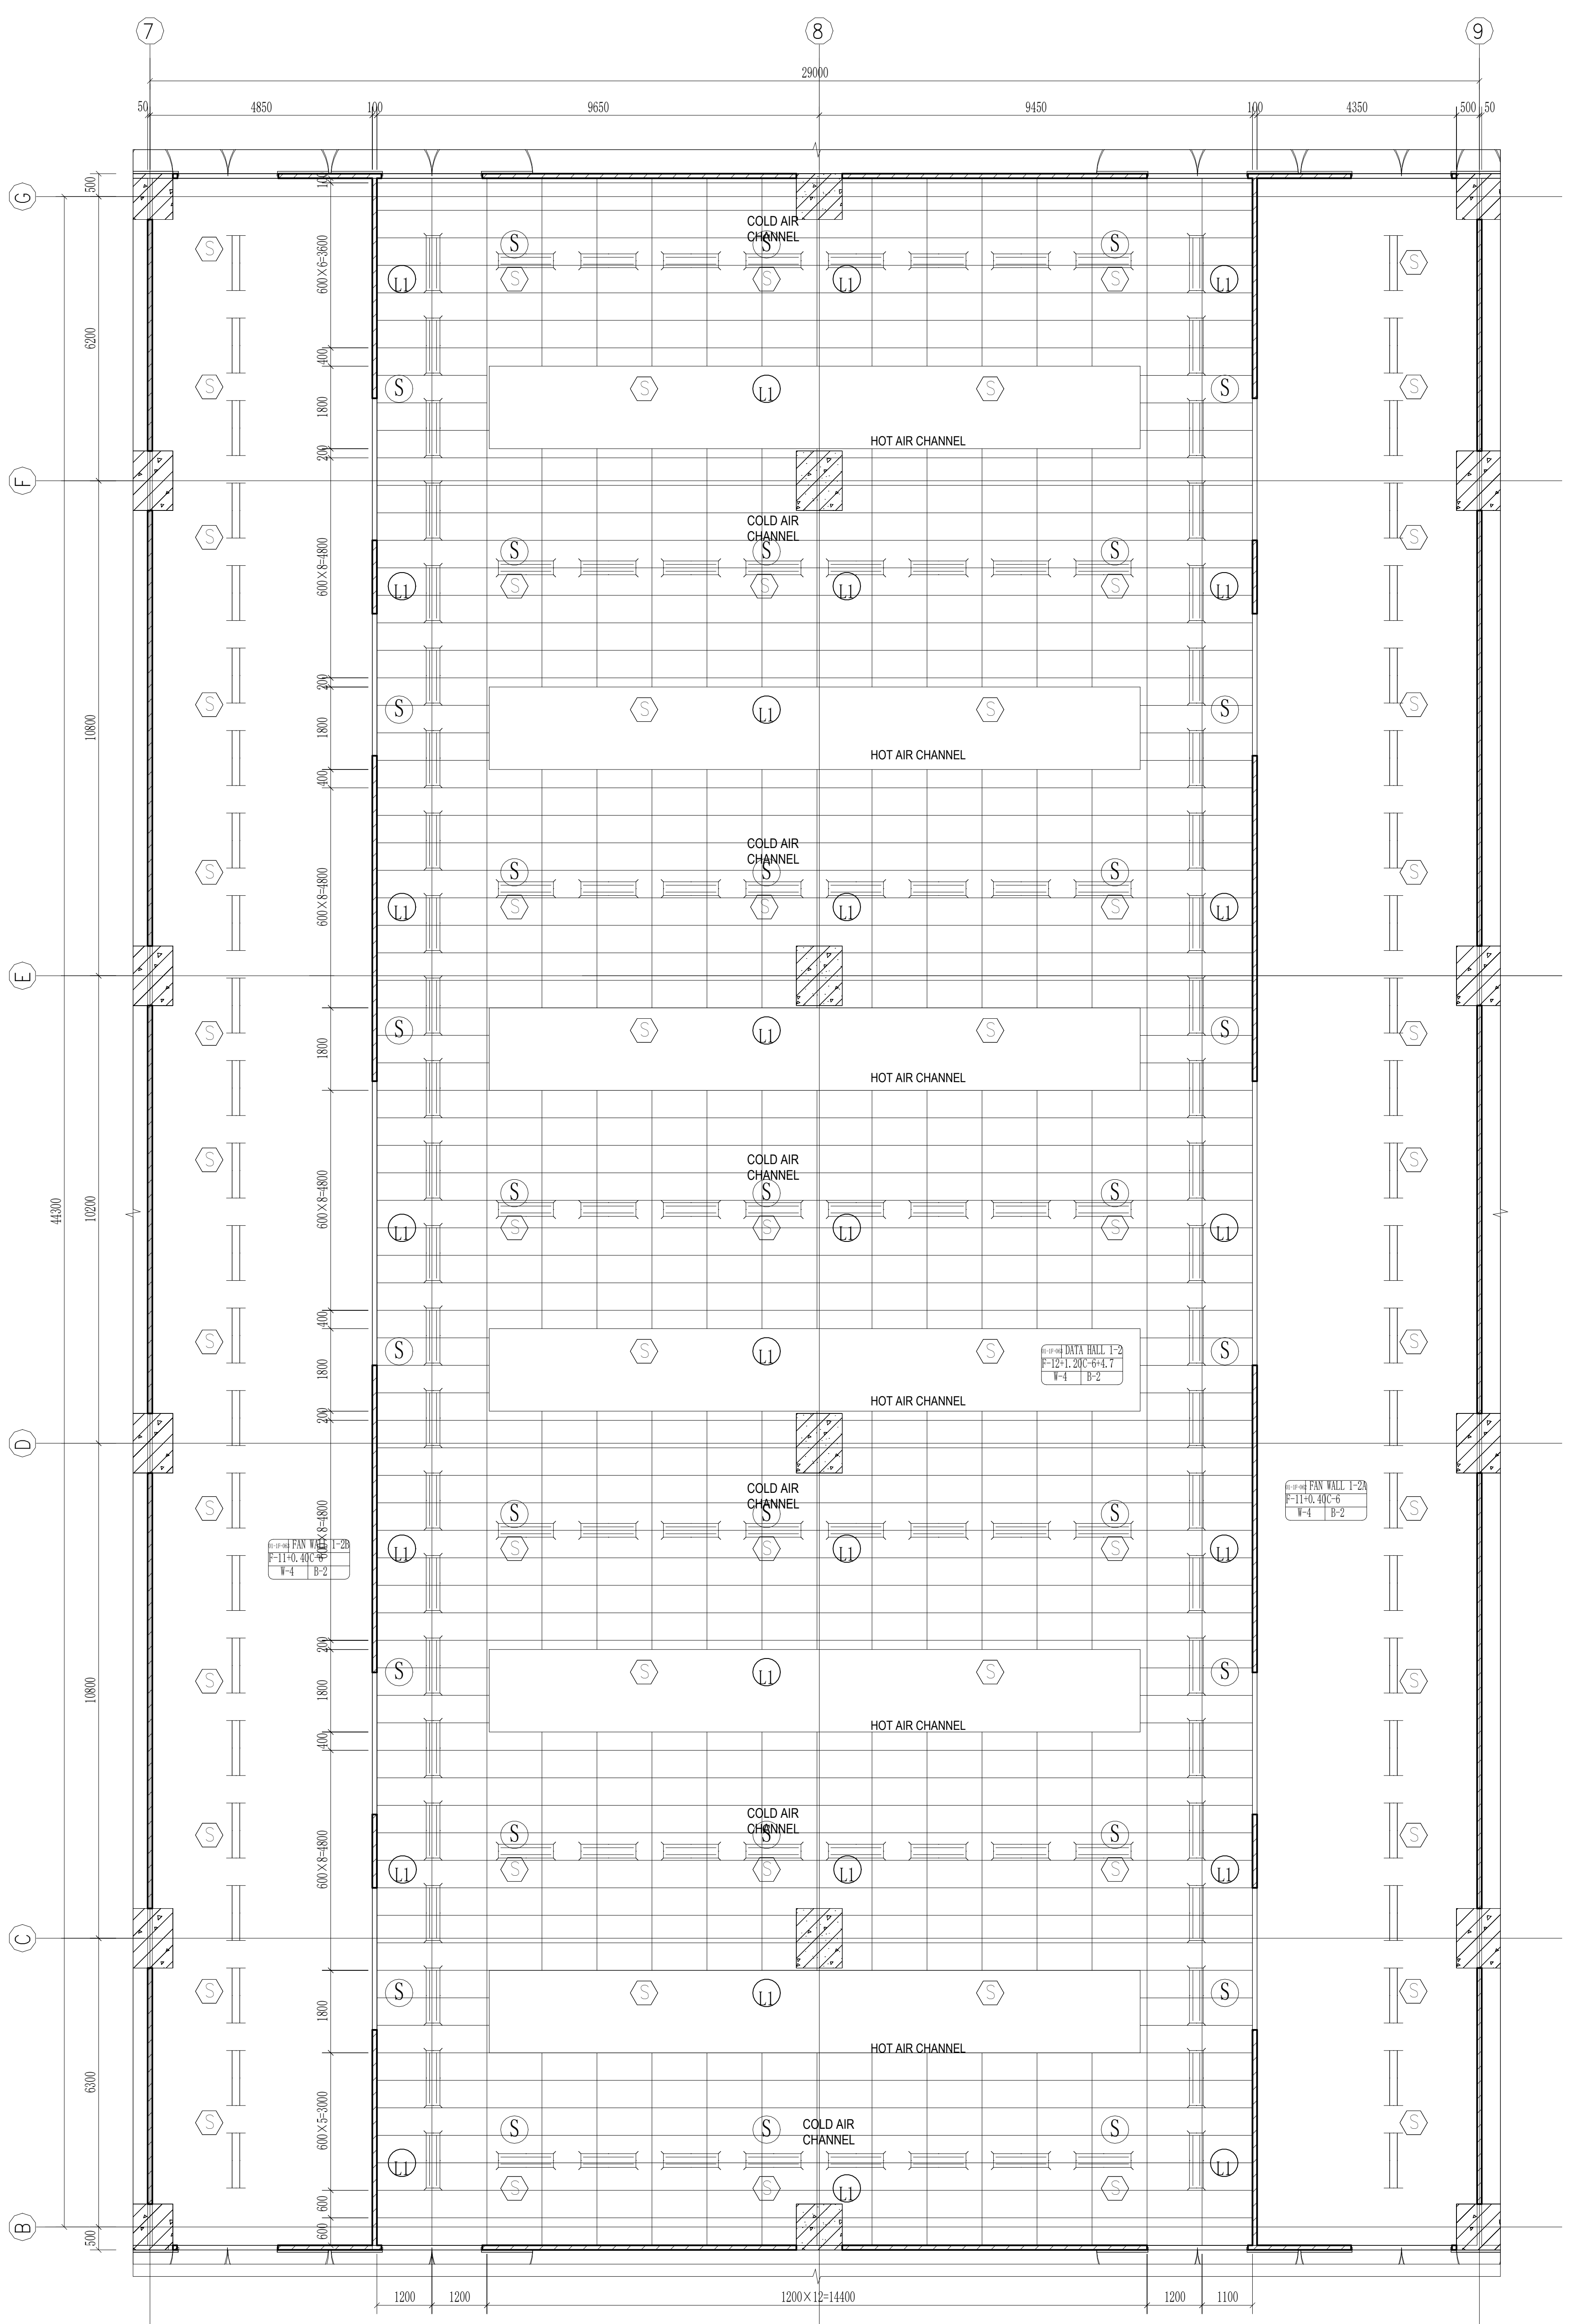

DH1-2 CEILING LAYOUT

Scale 1:75

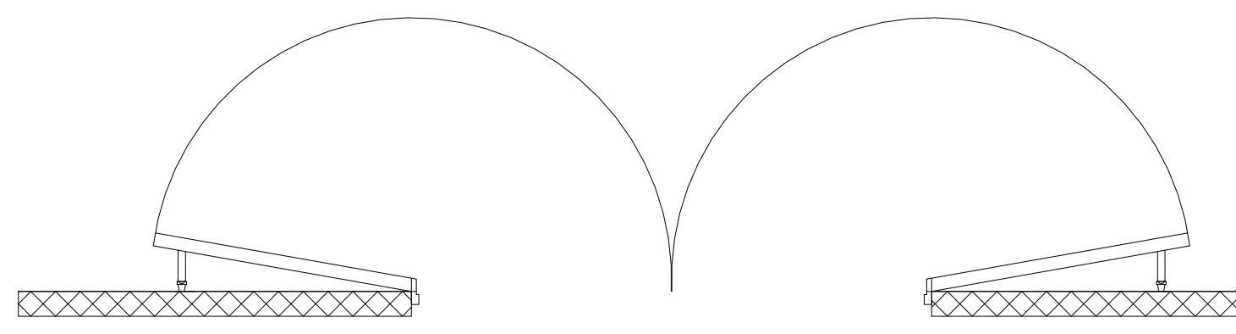

DOOR STOPPER
DETAILED IFC STAGE NODE DETAIL DRAWING

DOOR STOPPER DETAIL

2MM THICK STAINLESS STEEL PROTECTIVE PLATE IS INSTALLED FROM THE GROUND UP TO A HEIGHT OF 1.5 METERS. DETAILED IFC STAGE NODE DETAIL DRAWING

Scale 1:25

- ◀ FIRE ALARM SPEAKER WALL MOUNTED
- ☒ COMBINATION HORN/VISIBLE
- SURFACE MOUNTED SMOKE DETECTOR, PHOTOELECTRIC TYPE
- ⬡ PHOTOELECTRIC SMOKE DETECTOR
- ▭ LED double tube lamp; Ceiling Mounted; System Power 2x20W (+/- 10% In Tolerance); System Lumens >2x2000lm (+/- 10% In Tolerance); Luminaire Efficacy >100lm/w; CCT 5000K; CRI>80; CPF>0.9; Input Voltage 220V-240V 50/60Hz (Mounting height 3.0m)
- LED double tube lamp; Ceiling Mounted; System Power 2x20W (+/- 10% In Tolerance); System Lumens >2x2000lm (+/- 10% In Tolerance); Luminaire Efficacy >100lm/w; CCT 5000K; CRI>80; CPF>0.9; Input Voltage 220V-240V 50/60Hz (Mounting height 3.0m)
- F ALARM BELL
- ○ CEILING SPEAKER

CLIENT :
GULF EDGE DC 01
87 Wireless Road, M Thai Tower 11th. Floor, All Seasons Place, Lumpini, Pathumwan, Bangkok 10330, Thailand

CONTRACTOR :
华西发展(泰国)有限公司
บริษัท หัวซือ ดีเวลลอปเม้นต์ (ประเทศไทย) จำกัด
HUASHI DEVELOPMENT CO.,LTD
No. 202, Room No. 1403, 14/F, Le Concorde Building, Ratchadapisek Road, Huaykhwang Sub-District, Huaykhwang District, Bangkok Metropolitan 10310.

CONSULTANT :
ARbay
บริษัท เอ อาร์ เบย์ จำกัด
ARbay Company Limited
31 st Floor Bangkok Insurance Building
25 South Sathorn road Thungmahamek
Sathorn Bangkok 10120 THAILAND
T +66 (0) 2286 8199
F +66 (0) 2286 2863
info@arbay.co.th

CONSULTANT :
Qbic Engineers & Architects Co.,Ltd.
8 Soi KALONG 4 SANAMBINNAM ROAD,
THASAI SUB-DISTRICT, MUANG NONTHABURI DISTRICT
, NONTHABURI.
Tel 662-950-4374
Fax 662-580-3231
E-Mail : qbic@qbic.co.th, www.qbic.co.th
QBIC ENGINEERS AND ARCHITECTS CO.,LTD.

CONSULTANT :
MITR
MITR TECHNICAL CONSULTANT CO.,LTD.
1168/8 12th FLOOR, LUMPINI TOWER BUILDING,
RAMA IV RD., THUNGMAHAMEK, SATHORN, BANGKOK 10120, THAILAND
TEL : 0-2679-9079-84
FAX : 0-2679-9085 E-mail: mitr_dd@mitr.com

Architect :	SIGNATURE
ประกิต พนานุรัตน์ วสถ. 580 ที่อยู่ 251/1 ถ.จารุเมือง แขวงรองเมือง เขตปทุมวัน กรุงเทพมหานคร โทรศัพท์ 02-286-8199	
Structural Engineer :	SIGNATURE
วิศวกรผู้ออกแบบโครงสร้าง	
ณัฐสม สงวนวงษ์ วย 1423 ที่อยู่ 2/1 ซ.รามคำแหง 150 ถ.รามคำแหง แขวง สะพานสูง เขต สะพานสูง กทม. 10240	ณัฐสม สงวนวงษ์
Structural Inspector :	SIGNATURE
วิศวกรผู้ตรวจสอบโครงสร้าง	
โกมล จุฑาภัทร วย 964 ที่อยู่ 24/18 ซ.นวมินทร์ 129 ถ. นวมินทร์ แขวง นวลจันทร์ เขต บึงกุ่ม กทม. 10230	
Electrical Engineer :	SIGNATURE
วิศวกรผู้ออกแบบระบบไฟฟ้ากำลัง	
นายสุภัทร บูรณวิทย์ วฟก.1265 ที่อยู่ 21 ซอยทานสัมฤทธิ 13 ตำบลท่าทราย อ.เมืองนนทบุรี จ.นนทบุรี 11000	สุภัทร บูรณวิทย์
Mechanical Engineer :	SIGNATURE
วิศวกรผู้ออกแบบระบบเครื่องกลและปรับอากาศ	
นายประสิทธิ์ เกียวสุนทร วภ.1221 ที่อยู่ 44/372 ซอยบางกระดี 35/1 แขวงแสมดำ เขตบางขุนเทียน กทม. 10150	ประสิทธิ์
Sanitary Engineer :	SIGNATURE
วิศวกรผู้ออกแบบระบบสุขาภิบาล และดับเพลิง	
นายทศวรรษ สนันฤทธิ วส. 215 ที่อยู่ บ้านเลขที่ 99/107 หมู่ที่ 3 ต.ศีรษะจรเข้น้อย อ.บางเสาธง จ.สมุทรปราการ 10540	ทศวรรษ

ISSUE/REVISION

REV.	DESCRIPTION	DATE
A	90% DEVELOPED	09/05/2026

PROJECT NAME :
GEDC 01

LOCATION:
Nikhom Phattana district, Rayong ,industrial estate,CPGC

BUILDING :

90% DEVELOPED

TITLE :
ROOM DETAIL-1F-DATA HALL1-2 (LC)
、FAN WALL ROOM 1-2A,1-2B PLAN

JOB NO.		SCALE	1 : 75
DRAWN	NXR	REF.	
CHECKED	LJC	DWG. NO.	MPK01A-90-A-RD-103
APPROVED	LXD		
DATE	2026.05.09		

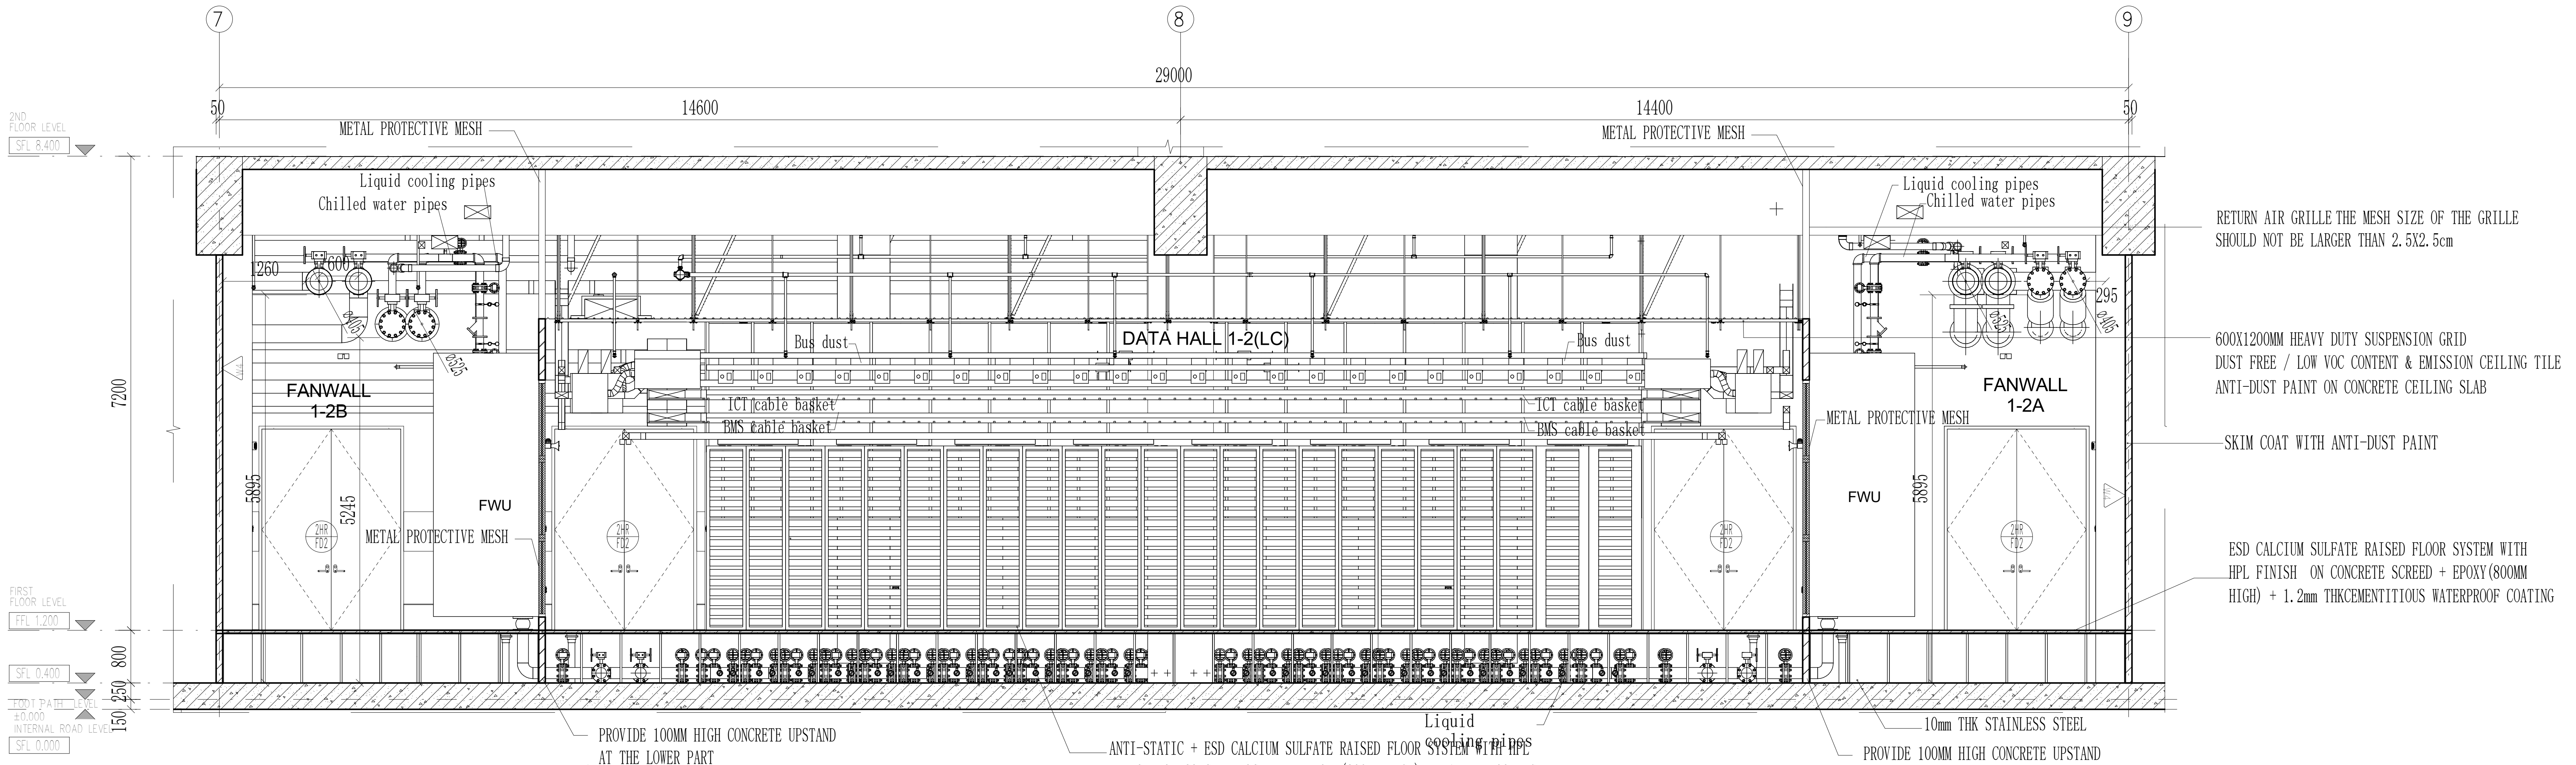
7
8
9
29000
50
14600
14400
50
2ND FLOOR LEVEL
SFL 8.400
METAL PROTECTIVE MESH
METAL PROTECTIVE MESH
Liquid cooling pipes
Chilled water pipes
Liquid cooling pipes
Chilled water pipes
1260
600
ø405
ø525
295
ø525
ø405
Bus dust
DATA HALL 1-2(LC)
Bus dust
ICT cable basket
BMS cable basket
ICT cable basket
BMS cable basket
FANWALL
1-2B
FANWALL
1-2A
FWU
FWU
METAL PROTECTIVE MESH
METAL PROTECTIVE MESH
7200
5895
5245
5895
2HR
FD2
FIRST FLOOR LEVEL
FFL 1.200
SFL 0.400
FOOT PATH LEVEL
±0.000
INTERNAL ROAD LEVEL
SFL 0.000
800
250
150
RETURN AIR GRILLE THE MESH SIZE OF THE GRILLE SHOULD NOT BE LARGER THAN 2.5X2.5cm
600X1200MM HEAVY DUTY SUSPENSION GRID
DUST FREE / LOW VOC CONTENT & EMISSION CEILING TILE
ANTI-DUST PAINT ON CONCRETE CEILING SLAB
SKIM COAT WITH ANTI-DUST PAINT
ESD CALCIUM SULFATE RAISED FLOOR SYSTEM WITH HPL FINISH ON CONCRETE SCREED + EPOXY(800MM HIGH) + 1.2mm THKCEMENTITIOUS WATERPROOF COATING
PROVIDE 100MM HIGH CONCRETE UPSTAND AT THE LOWER PART
ANTI-STATIC + ESD CALCIUM SULFATE RAISED FLOOR SYSTEM WITH HPL FINISH ON CONCRETE SCREED + EPOXY(800MM HIGH) + WATER PROOFING
Liquid cooling pipes
10mm THK STAINLESS STEEL
PROVIDE 100MM HIGH CONCRETE UPSTAND AT THE LOWER PART

DH 1-2、FANWALL 1-2A、FANWALL 1-2B SECTION A-A

Scale 1:50

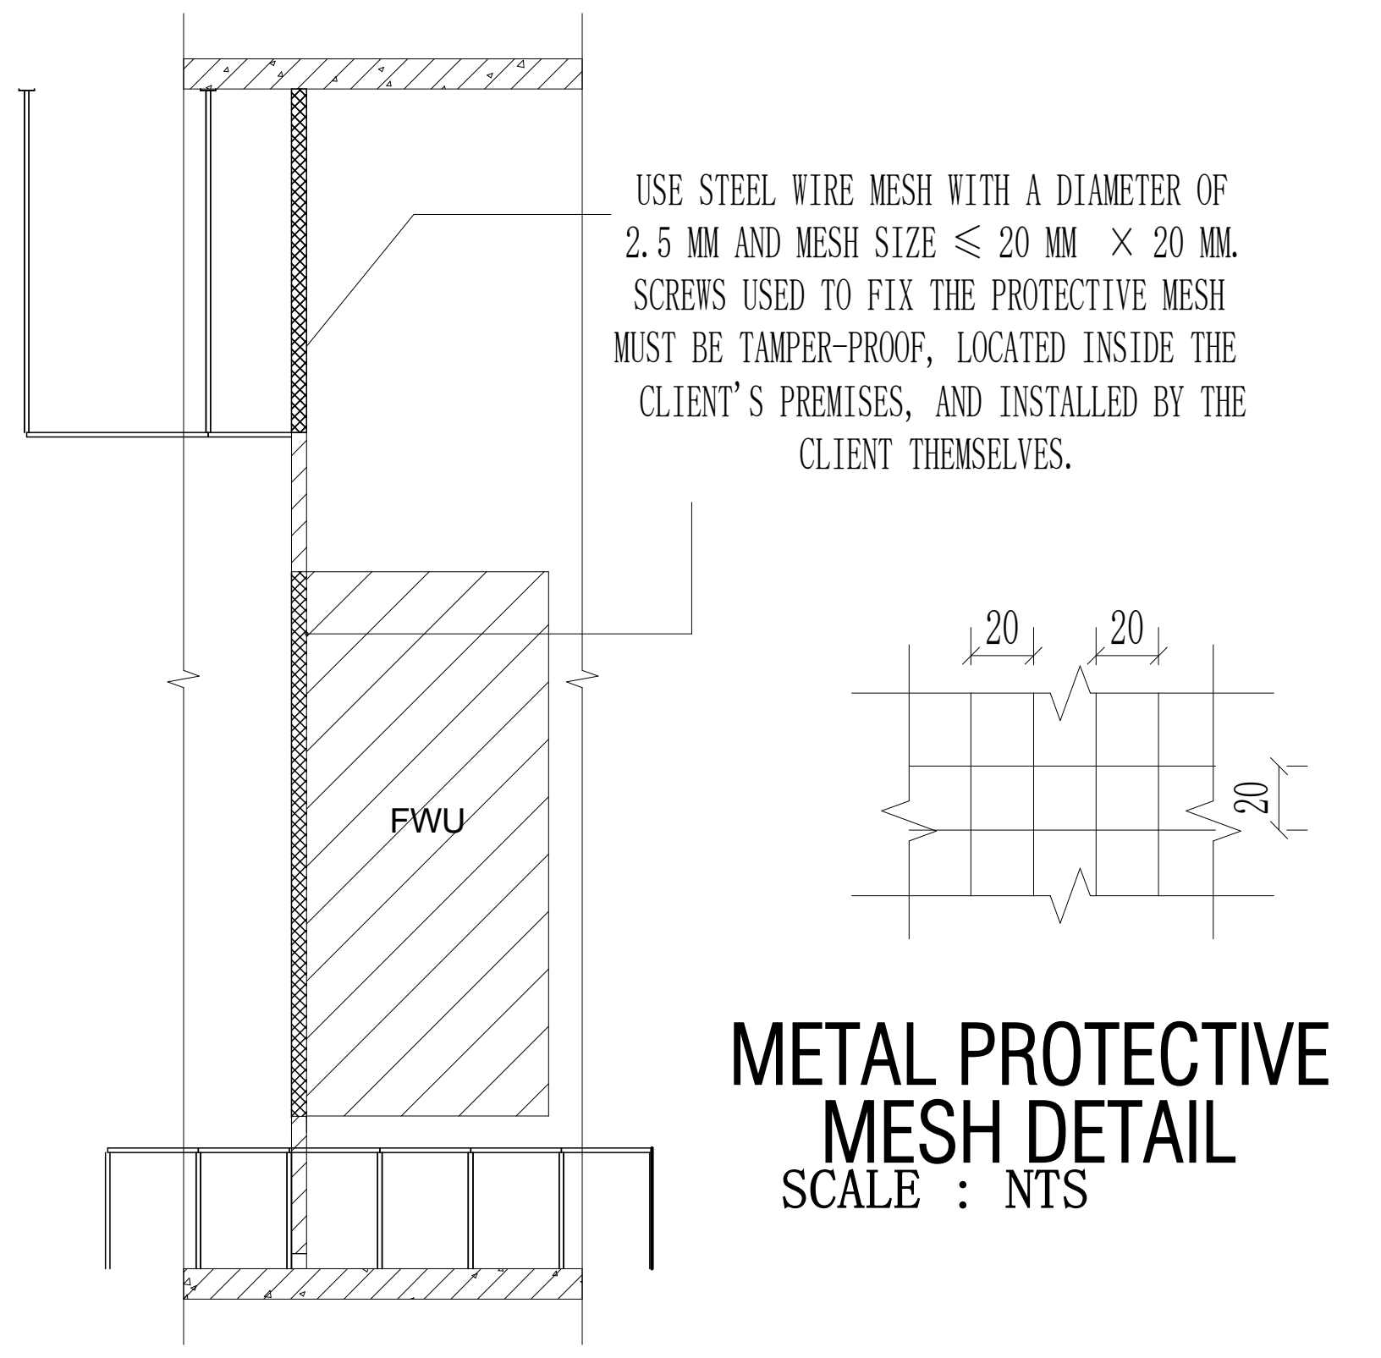
USE STEEL WIRE MESH WITH A DIAMETER OF 2.5 MM AND MESH SIZE ≤ 20 MM × 20 MM. SCREWS USED TO FIX THE PROTECTIVE MESH MUST BE TAMPER-PROOF, LOCATED INSIDE THE CLIENT'S PREMISES, AND INSTALLED BY THE CLIENT THEMSELVES.
FWU
20
20
20

METAL PROTECTIVE MESH DETAIL

SCALE : NTS

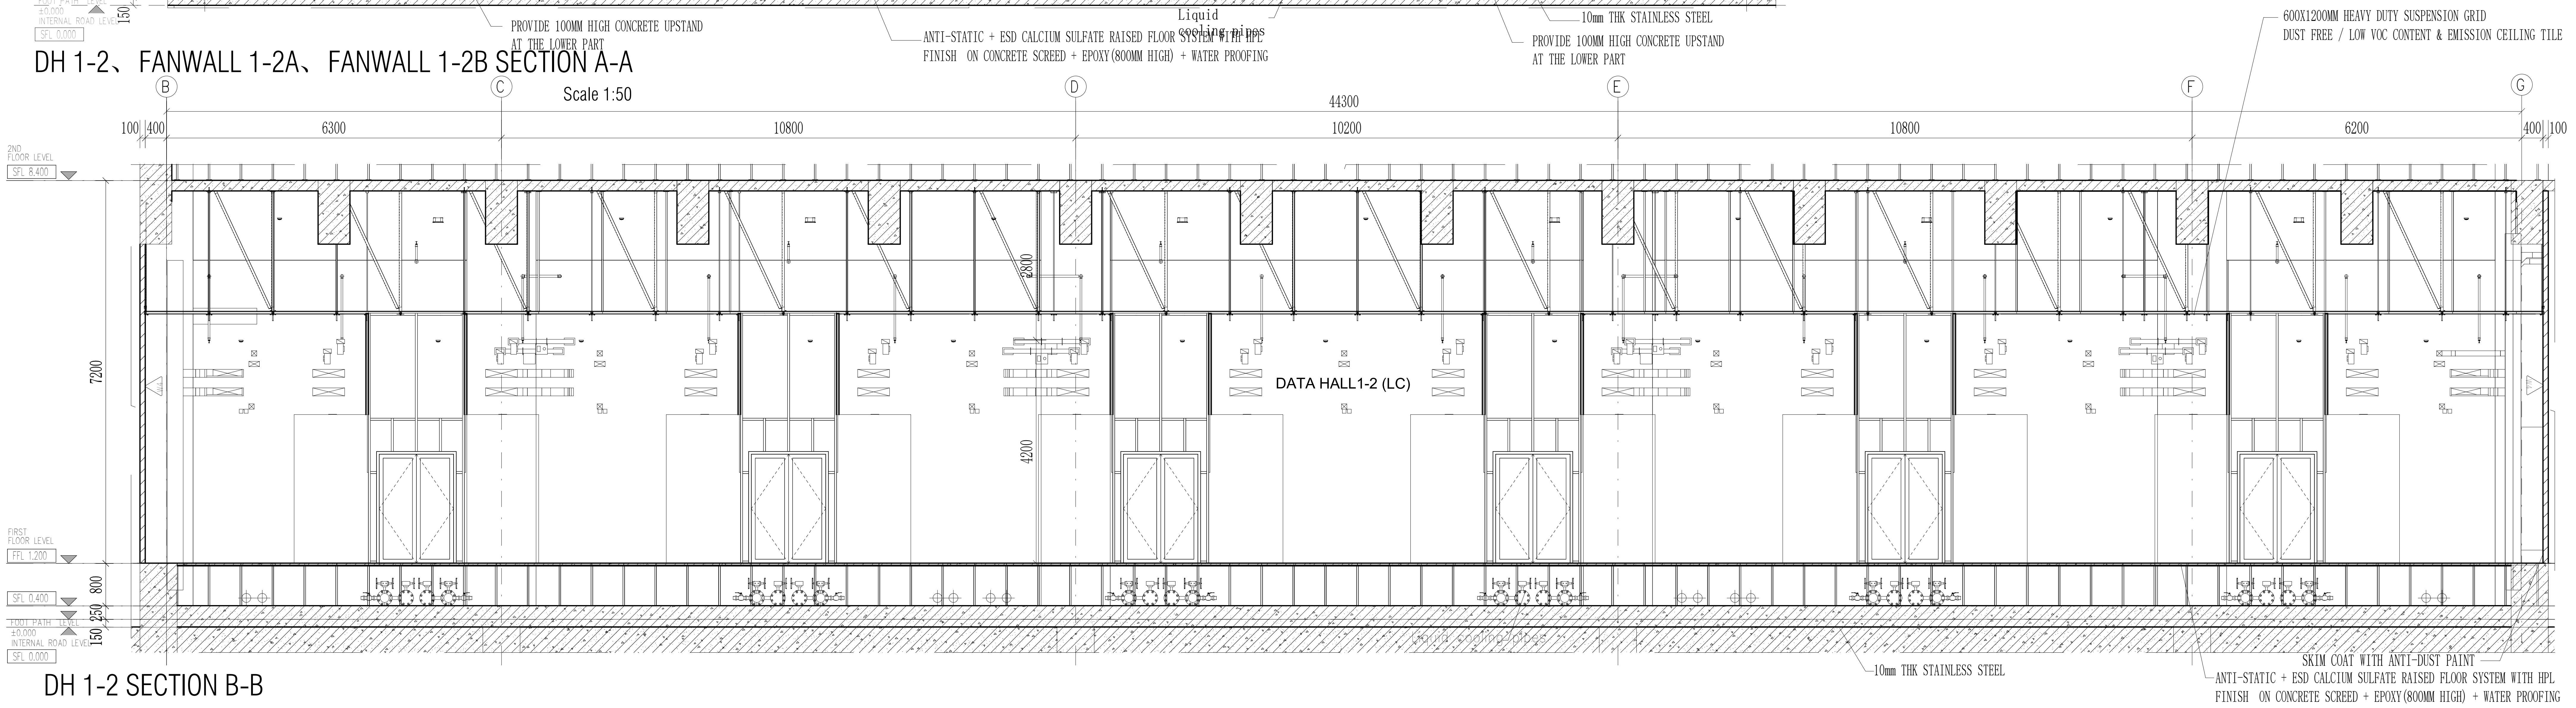
600X1200MM HEAVY DUTY SUSPENSION GRID
DUST FREE / LOW VOC CONTENT & EMISSION CEILING TILE
B
C
D
E
F
G
44300
100
400
6300
10800
10200
10800
6200
400
100
2ND FLOOR LEVEL
SFL 8.400
2800
7200
DATA HALL1-2 (LC)
4200
FIRST FLOOR LEVEL
FFL 1.200
SFL 0.400
FOOT PATH LEVEL
±0.000
INTERNAL ROAD LEVEL
SFL 0.000
800
250
150
SKIM COAT WITH ANTI-DUST PAINT
ANTI-STATIC + ESD CALCIUM SULFATE RAISED FLOOR SYSTEM WITH HPL FINISH ON CONCRETE SCREED + EPOXY(800MM HIGH) + WATER PROOFING
10mm THK STAINLESS STEEL

DH 1-2 SECTION B-B

Scale 1:50

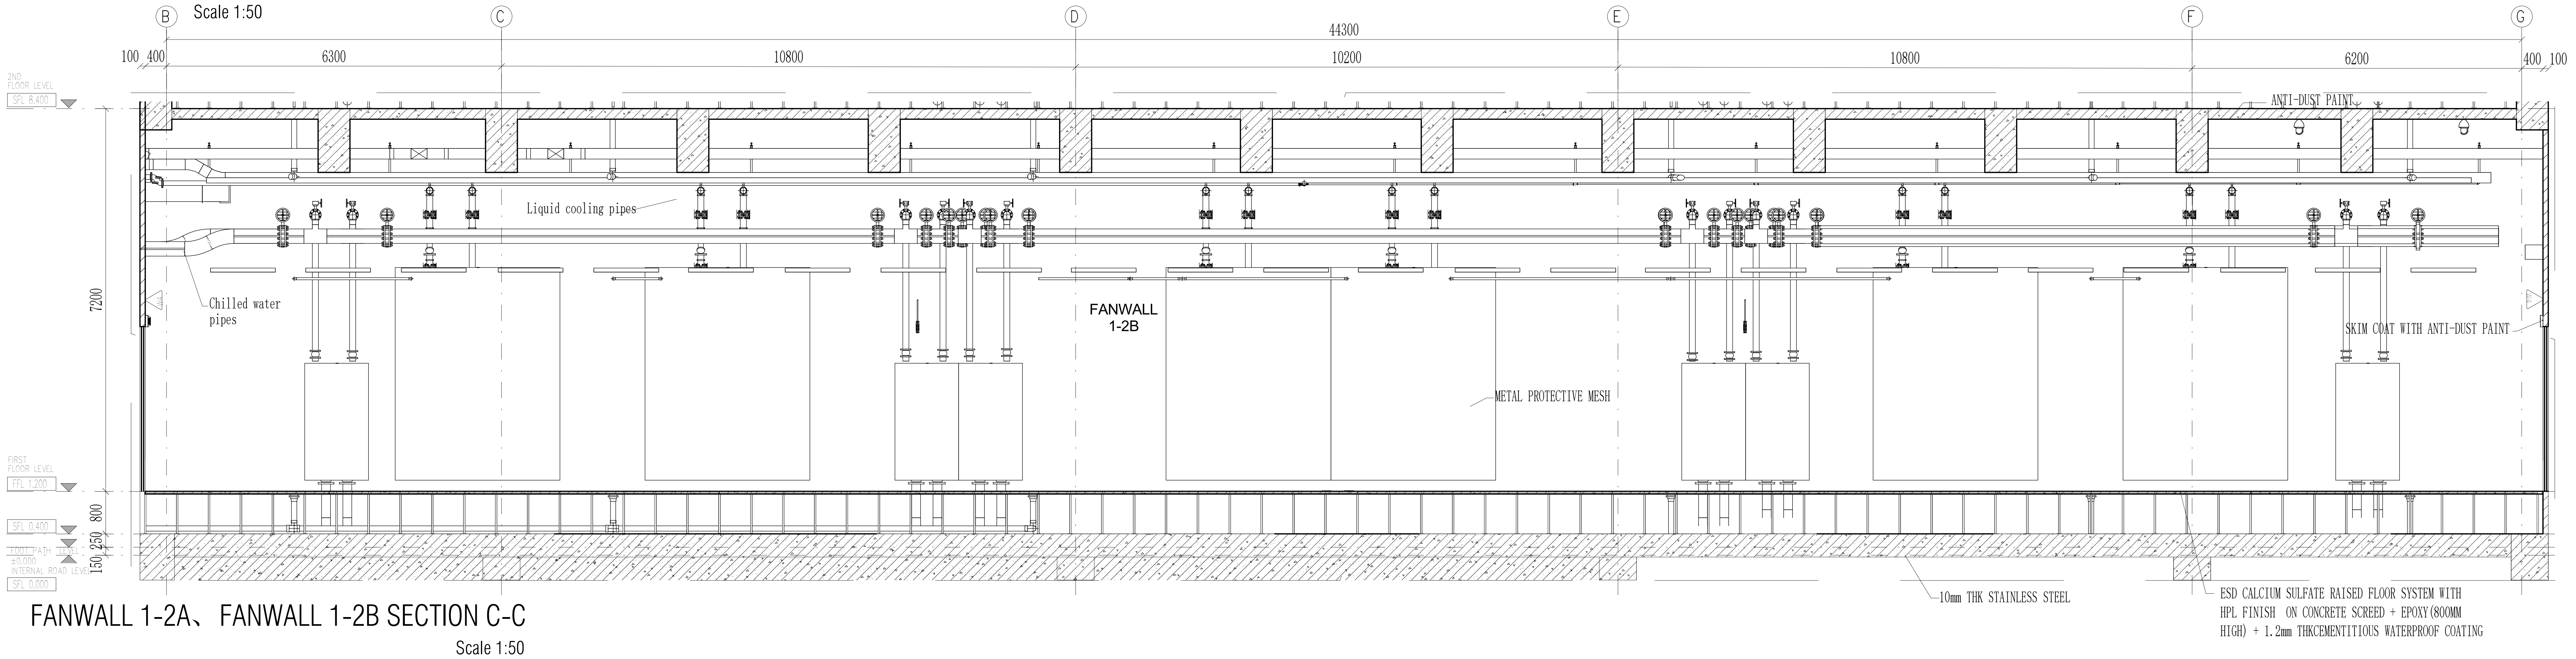
B
C
D
E
F
G
44300
100
400
6300
10800
10200
10800
6200
400
100
2ND FLOOR LEVEL
SFL 8.400
ANTI-DUST PAINT
Liquid cooling pipes
Chilled water pipes
7200
FANWALL
1-2B
METAL PROTECTIVE MESH
SKIM COAT WITH ANTI-DUST PAINT
FIRST FLOOR LEVEL
FFL 1.200
SFL 0.400
FOOT PATH LEVEL
±0.000
INTERNAL ROAD LEVEL
SFL 0.000
800
250
150
10mm THK STAINLESS STEEL
ESD CALCIUM SULFATE RAISED FLOOR SYSTEM WITH HPL FINISH ON CONCRETE SCREED + EPOXY(800MM HIGH) + 1.2mm THKCEMENTITIOUS WATERPROOF COATING

FANWALL 1-2A、FANWALL 1-2B SECTION C-C

Scale 1:50

CLIENT :

GULF EDGE DC 01

87 Wireless Road, M Thai Tower 11th. Floor, All Seasons Place, Lumpini,
Pathumwan, Bangkok 10330, Thailand

CONTRACTOR :

华西发展(泰国)有限公司
บริษัท หัวซือ ดีเวลลอปเม้นต์ (ประเทศไทย) จำกัด
HUASHI DEVELOPMENT CO.,LTD
No. 202, Room No. 1403, 14/F, Le Concorde Building,
Ratchadapisek Road, Huaykhwang Sub-District,
Huaykhwang District, Bangkok Metropolitan 10310.

CONSULTANT :

ARbay
บริษัท เอ อาร์ เบย์ จำกัด
ARbay Company Limited
31 st Floor Bangkok Insurance Building
25 South Sathorn road Thungmahamek
Sathorn Bangkok 10120 THAILAND
T +66 (0) 2286 8199
F +66 (0) 2286 2863
info@arbay.co.th

CONSULTANT :

Qbic Engineers & Architects Co.,Ltd.
8 Soi KALONG 4 SANAMBINNAM ROAD,
THASAI SUB-DISTRICT, MUANG NONTHABURI DISTRICT
, NONTHABURI.
Tel 662-950-4374
Fax 662-580-3231
E-Mail : qbic@qbic.co.th, www.qbic.co.th
QBIC ENGINEERS AND ARCHITECTS CO.,LTD.

CONSULTANT :

MITR
MITR TECHNICAL CONSULTANT CO.,LTD.
1168/8 12th FLOOR, LUMPINI TOWER BUILDING,
RAMA IV RD., THUNGMAHAMEK, SATHORN, BANGKOK 10120, THAILAND
TEL : 0-2679-9079-84
FAX : 0-2679-9085 E-mail: mitr_dd@mitr.com

Architect :	SIGNATURE
ประกิต พนานุรัตน์ วสถ. 580 ที่อยู่ 251/1 ถ.จารุเมือง แขวงรองเมือง เขตปทุมวัน กรุงเทพมหานคร โทรศัพท์ 02-286-8199	

Structural Engineer :	SIGNATURE
วิศวกรผู้ออกแบบโครงสร้าง	
ณัฐสม สงวนวงษ์ วย 1423 ที่อยู่ 2/1 ซ.รามคำแหง 150 ถ.รามคำแหง แขวง สะพานสูง เขต สะพานสูง กทม. 10240	ณัฐสม สงวนวงษ์

Structural Inspector :	SIGNATURE
วิศวกรผู้ตรวจสอบโครงสร้าง	
โกมล จุฑาภัทร วย 964 ที่อยู่ 24/18 ซ.นวมินทร์ 129 ถ. นวมินทร์ แขวง นวลจันทร์ เขต บึงกุ่ม กทม. 10230	

Electrical Engineer :	SIGNATURE
วิศวกรผู้ออกแบบระบบไฟฟ้ากำลัง	
นายสุภัทร บูรณวิทย์ วฟก.1265 ที่อยู่ 21 ซอยทานสัมฤทธิ์ 13 ตำบลท่าทราย อ.เมืองนนทบุรี จ.นนทบุรี 11000	

Mechanical Engineer :	SIGNATURE
วิศวกรผู้ออกแบบระบบเครื่องกลและปรับอากาศ	
นายประสิทธิ์ เกี้ยวสุนทร วก.1221 ที่อยู่ 44/372 ซอยบางกระดี่ 35/1 แขวงแสมดำ เขตบางขุนเทียน กทม. 10150	ประสิทธิ์

Sanitary Engineer :	SIGNATURE
วิศวกรผู้ออกแบบระบบสุขาภิบาล และดับเพลิง	
นายทศวรรษ สนั่นฤทธิ์ วส. 215 ที่อยู่ บ้านเลขที่ 99/107 หมู่ที่ 3 ต.ศีรษะจรเข้น้อย อ.บางเสาธง จ.สมุทรปราการ 10540	ทศวรรษ

ISSUE/REVISION

REV.	DESCRIPTION	DATE
A	90% DEVELOPED	09/05/2026

PROJECT NAME :

GEDC 01

LOCATION:
Nikhom Phattana district, Rayong ,industrial estate,CPGC

BUILDING :
MAIN BUILDING

90% DEVELOPED

TITLE :

ROOM DETAIL-1F-DATA HALL1-2 (LC)
、FAN WALL ROOM 1-2A,1-2B SECTION

JOB NO.	SCALE 1 : 50
DRAWN NXR	REF.
CHECKED LJC	DWG. NO. MPK01A-90-A-RD-104
APPROVED LXD	
DATE 2026.05.09	

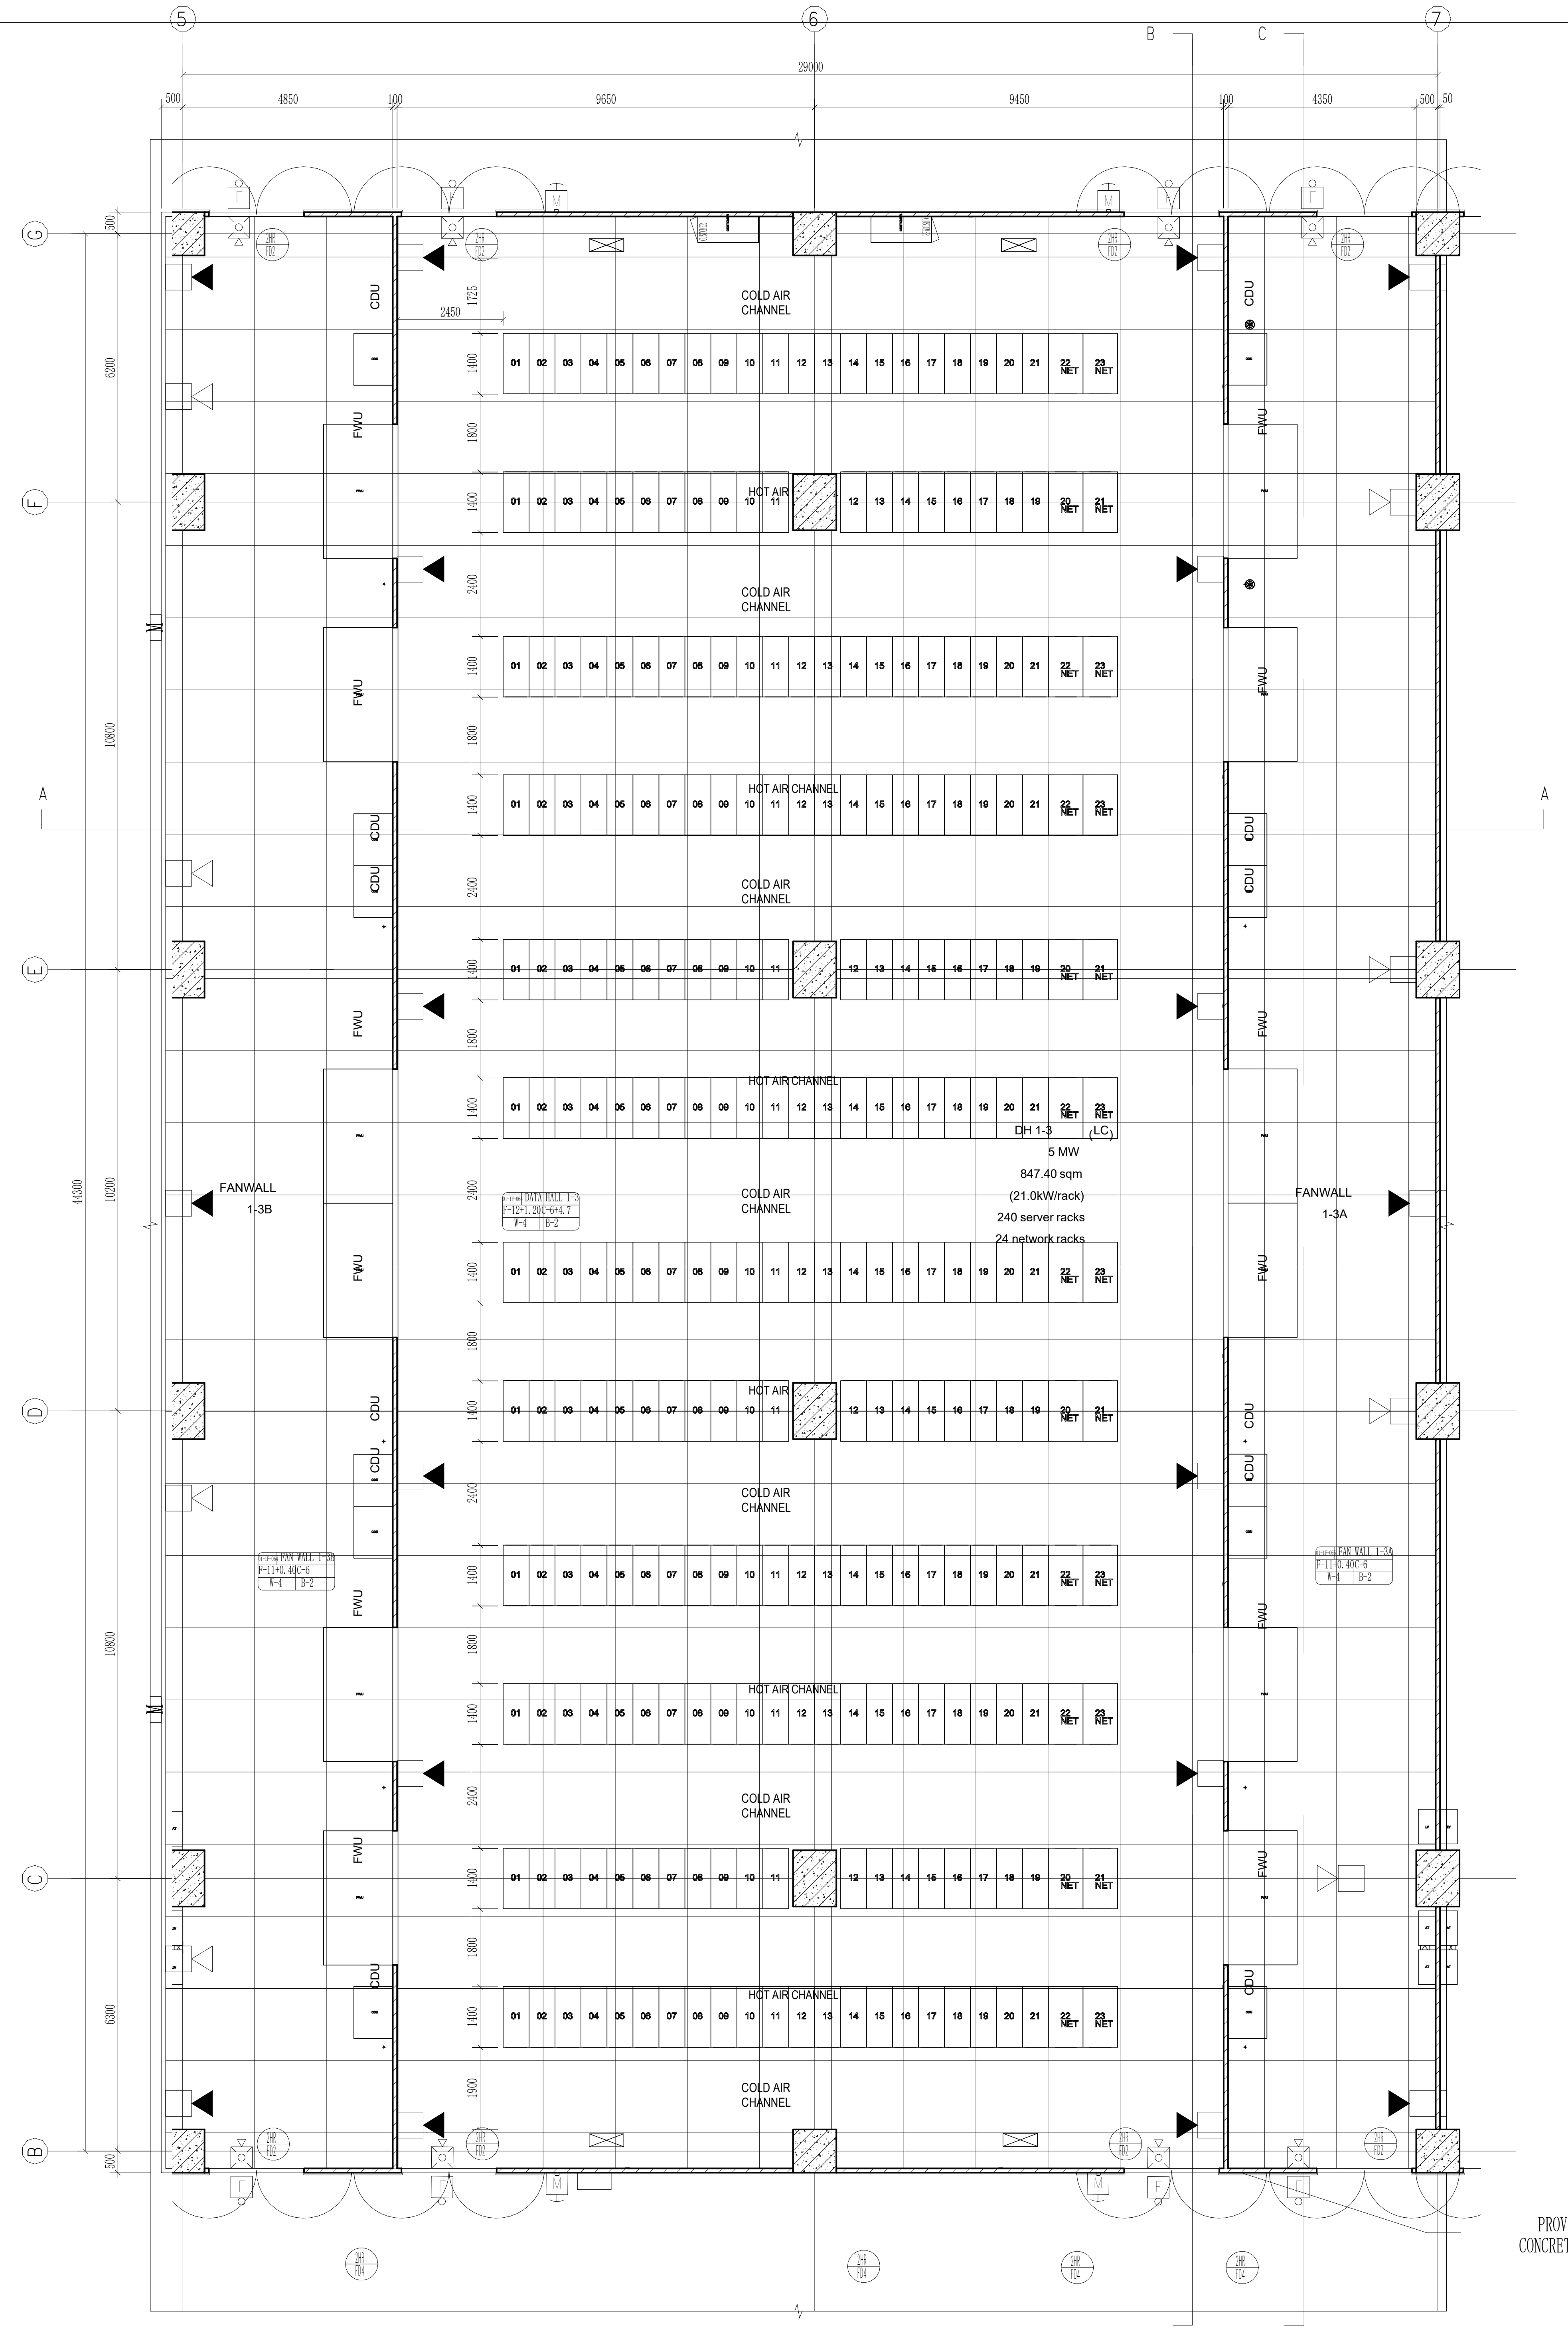
5
6
7
B
C
29000
500
4850
100
9650
9450
100
4350
500
50
G
F
E
D
C
B
A
A
COLD AIR CHANNEL
HOT AIR CHANNEL
HOT AIR
CDU
FWU
01 02 03 04 05 06 07 08 09 10 11 12 13 14 15 16 17 18 19 20 21 22 NET 23 NET
DH 1-3 (LC)
5 MW
847.40 sqm
(21.0kW/rack)
240 server racks
24 network racks
FANWALL 1-3B
FANWALL 1-3A
6200
18800
10200
41300
6300
2450

PROVIDE 100MM HIGH
CONCRETE UPSTAND AT THE
LOWER PART

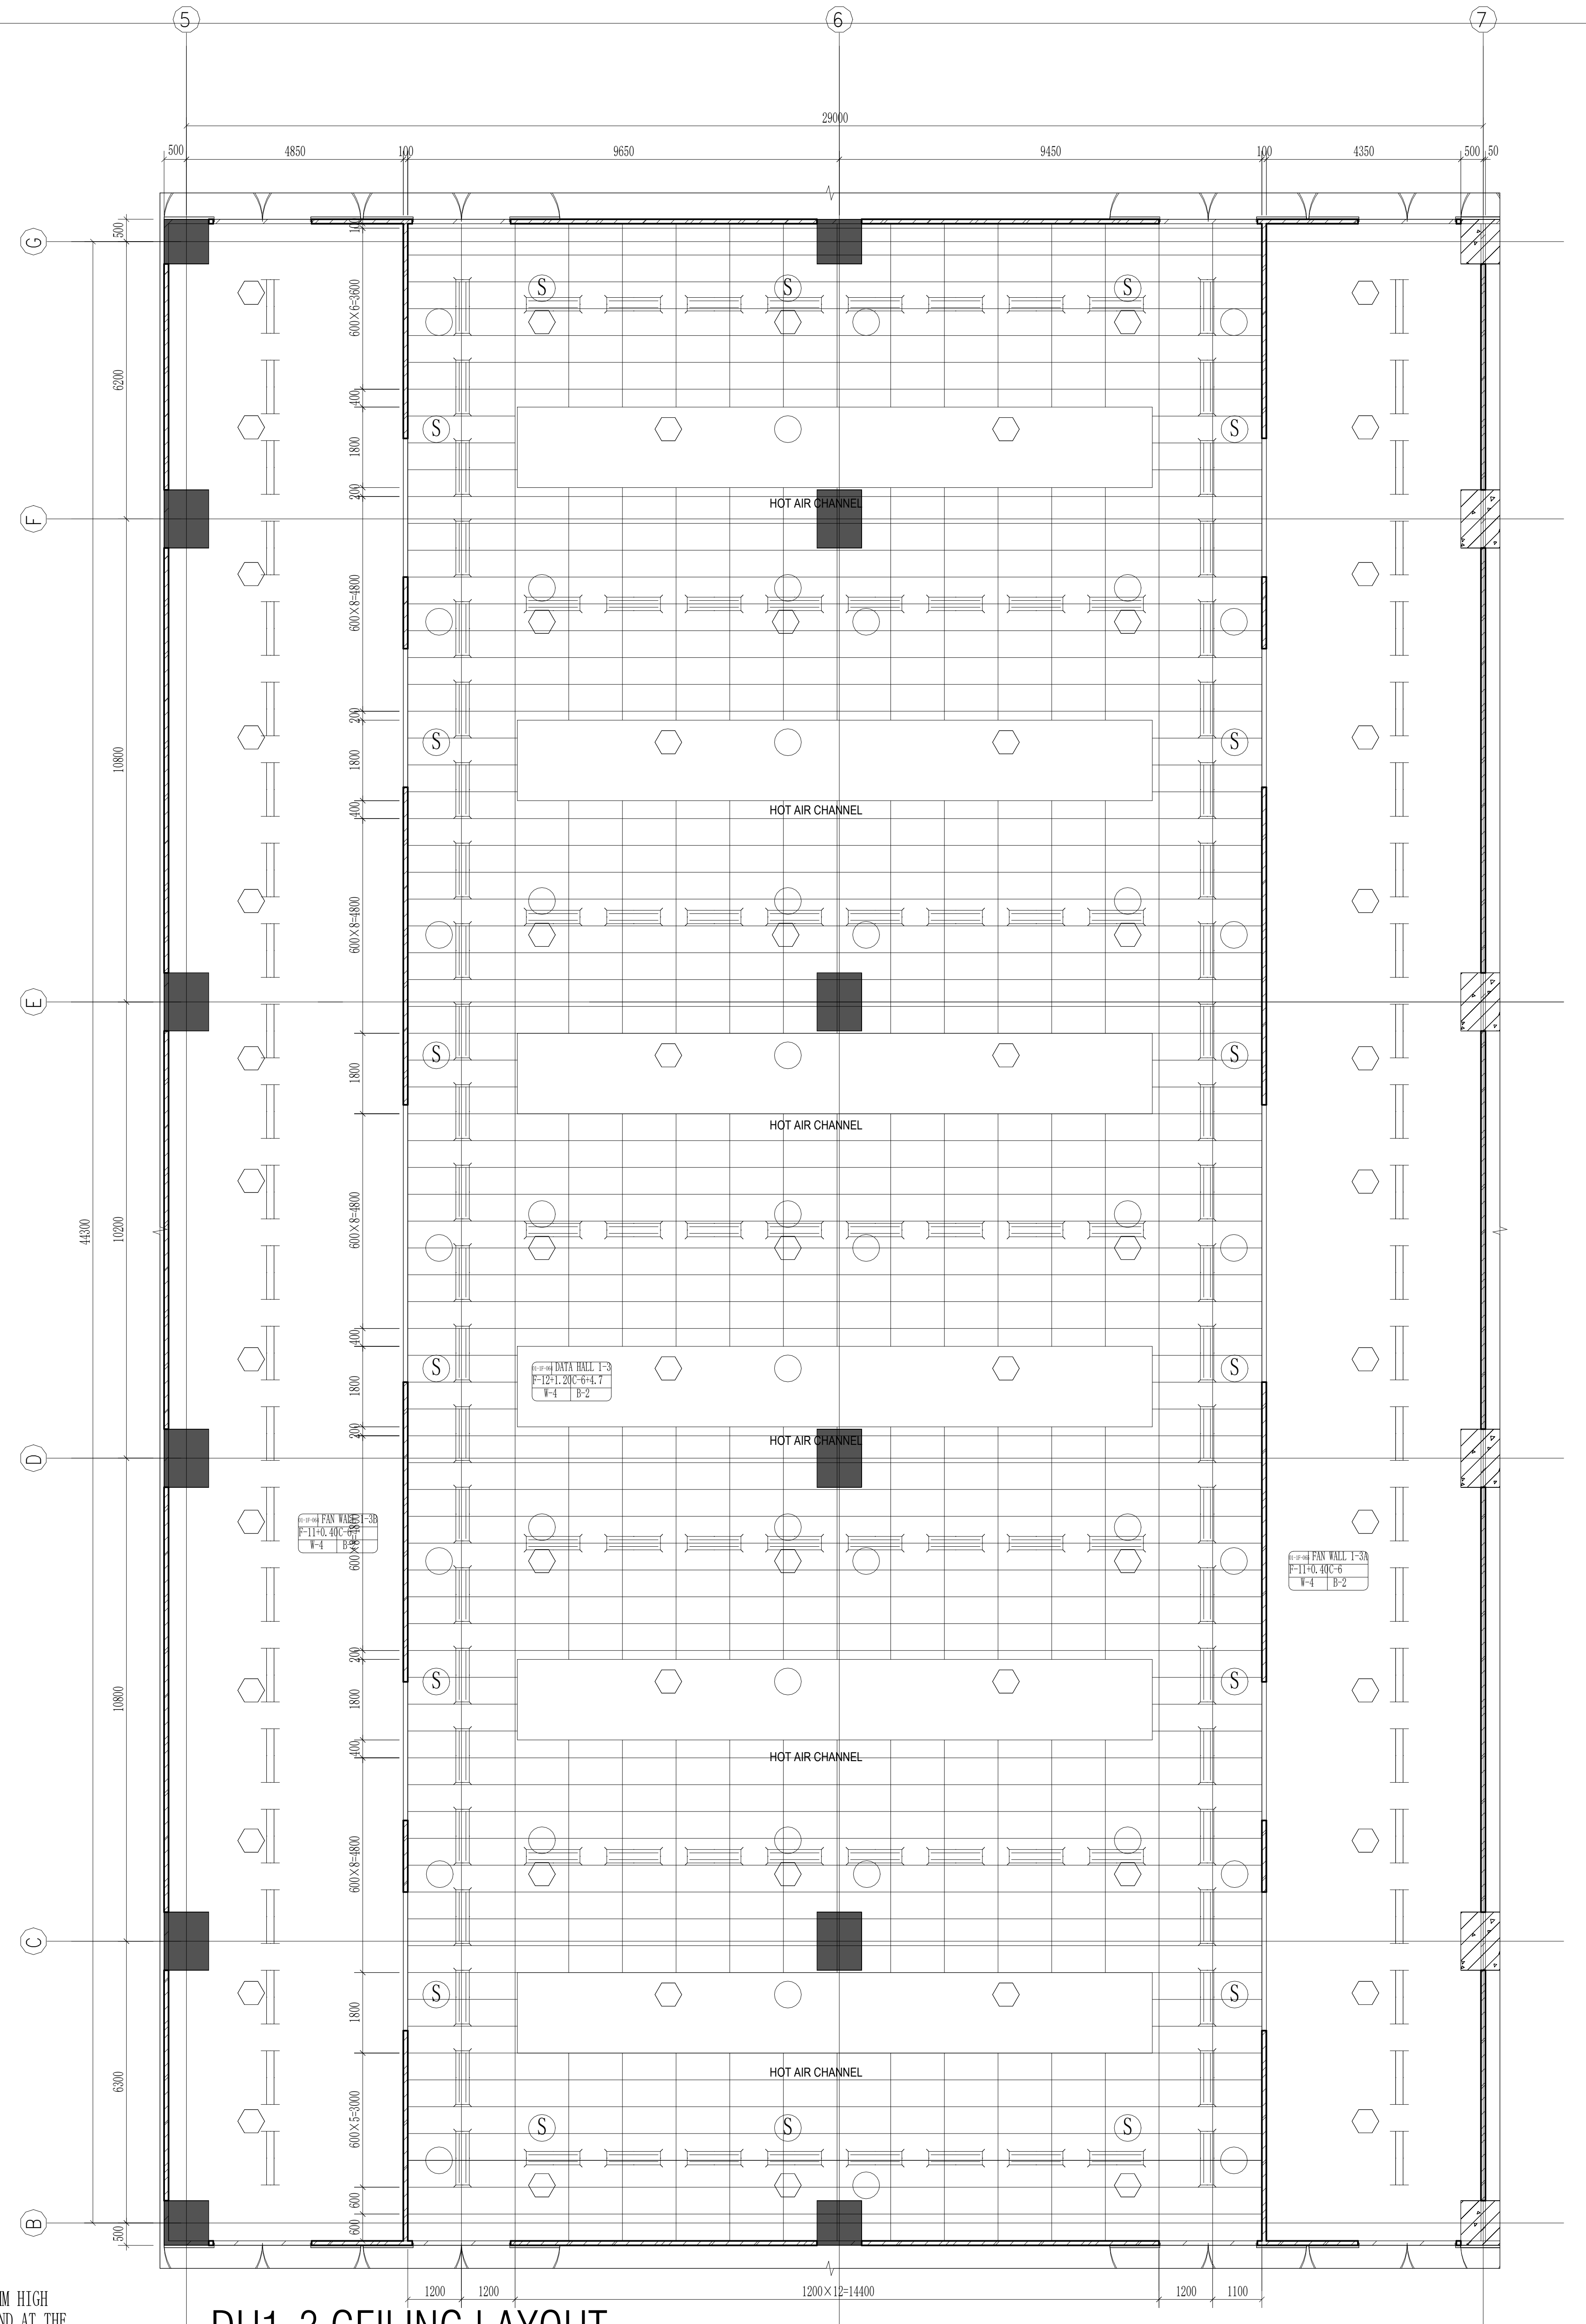
5
6
7
29000
500
4850
100
9650
9450
100
4350
500
50
G
F
E
D
C
B
S
HOT AIR CHANNEL
600×8=4800
600×5=3000
1800
1200
1100
1200×12=14400

DH1-3 CEILING LAYOUT

Scale 1:75

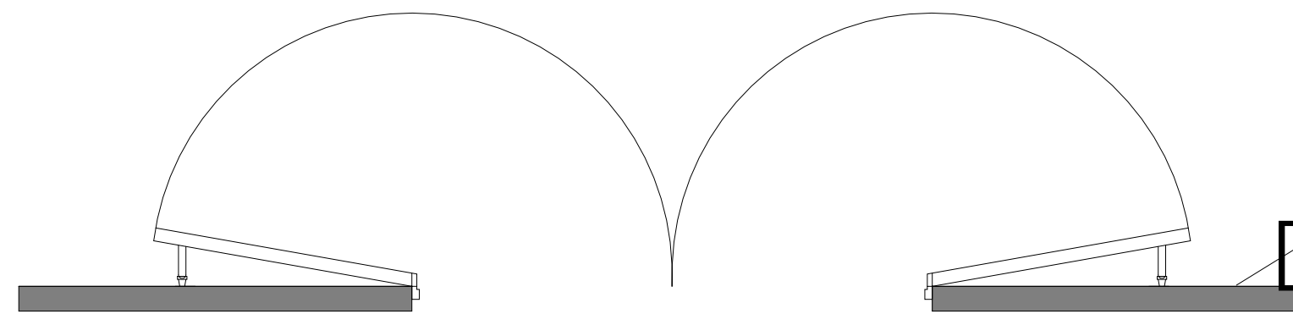
DOOR STOPPER
DETAILED IFC STAGE NODE DETAIL DRAWING

2MM THICK STAINLESS STEEL PROTECTIVE PLATE IS INSTALLED FROM THE GROUND UP TO A HEIGHT OF 1.5 METERS. DETAILED IFC STAGE NODE DETAIL DRAWING

DOOR STOPPER DETAIL

Scale 1:25

Room Number	Room Name	Room Type	0kW/RACK	12kW/RACK	16kW/RACK	21kW/RACK	Rack Count	Design IT Load (Mw)
01-3F-064	Data Hall1-3	Liquid-cooled	0	0	24	240	264	5

Note On Levels- All Levels Shown Are Absolute Elevation	
☒	0kW/RACK
▯	12kW/RACK
⊠	16kW/RACK
⧄	21kW/RACK

◀	FIRE ALARM SPEAKER WALL MOUNTED
⊠	COMBINATION HORN/VISIBLE
S	SURFACE MOUNTED SMOKE DETECTOR, PHOTOELECTRIC TYPE
⬡	PHOTOELECTRIC SMOKE DETECTOR
▭	LED double tube lamp; Ceiling Mounted; System Power 2x20W (+/- 10% In Tolerance); System Lumens >2x2000lm (+/- 10% In Tolerance); Luminaire Efficacy >100lm/w; CCT 5000K; CRI>80; CPF>0.9; Input Voltage 220V-240V 50/60Hz (Mounting height 3.0m)
▭	LED double tube lamp; Ceiling Mounted; System Power 2x20W (+/- 10% In Tolerance); System Lumens >2x2000lm (+/- 10% In Tolerance); Luminaire Efficacy >100lm/w; CCT 5000K; CRI>80; CPF>0.9; Input Voltage 220V-240V 50/60Hz (Mounting height 3.0m)
F	ALARM BELL
○	CEILING SPEAKER

CLIENT :

GULF EDGE DC 01

87 Wireless Road, M Thai Tower 11th. Floor, All Seasons Place, Lumpini, Pathumwan, Bangkok 10330, Thailand

CONTRACTOR :

华西发展(泰国)有限公司
บริษัท หัวซือ ดีเวลลอปเม้นต์ (ประเทศไทย) จำกัด
HUASHI DEVELOPMENT CO.,LTD
No. 202, Room No. 1403, 14/F, Le Concorde Building,
Ratchadapisek Road, Huaykhwang Sub-District,
Huaykhwang District, Bangkok Metropolitan 10310.

CONSULTANT :

ARbay
บริษัท เอ อาร์ เบย์ จำกัด
ARbay Company Limited
31 st Floor Bangkok Insurance Building
25 South Sathorn road Thungmahamek
Sathorn Bangkok 10120 THAILAND
T +66 (0) 2286 8199
F +66 (0) 2286 2863
info@arbay.co.th

CONSULTANT :

Qbic Engineers & Architects Co.,Ltd.
8 Soi KALONG 4 SANAMBINNAM ROAD,
THASAI SUB-DISTRICT, MUANG NONTHABURI DISTRICT
, NONTHABURI.
Tel 662-950-4374
Fax 662-580-3231
E-Mail : qbic@qbic.co.th, www.qbic.co.th
QBIC ENGINEERS AND ARCHITECTS CO.,LTD.

CONSULTANT :

MITR
MITR TECHNICAL CONSULTANT CO.,LTD.
1168/8 12th FLOOR, LUMPINI TOWER BUILDING,
RAMA IV RD., THUNGMAHAMEK, SATHORN, BANGKOK 10120, THAILAND
TEL : 0-2679-9079-84
FAX : 0-2679-9085 E-mail: mitr_dd@mitr.com

Architect :	SIGNATURE
ประกิต พนานุรัตน์ วสถ. 580 ที่อยู่ 251/1 ถ.จารุเมือง แขวงรองเมือง เขตปทุมวัน กรุงเทพมหานคร โทรศัพท์ 02-286-8199	

Structural Engineer :	SIGNATURE
วิศวกรผู้ออกแบบโครงสร้าง	
ณัฐสม สงวนวงษ์ วย 1423 ที่อยู่ 2/1 ซ.รามคำแหง 150 ถ.รามคำแหง แขวง สะพานสูง เขต สะพานสูง กทม. 10240	ณัฐสม สงวนวงษ์

Structural Inspector :	SIGNATURE
วิศวกรผู้ตรวจสอบโครงสร้าง	
โกมล จุฑาภัทร วย 964 ที่อยู่ 24/18 ซ.นวมินทร์ 129 ถ. นวมินทร์ แขวง นวลจันทร์ เขต บึงกุ่ม กทม. 10230	

Electrical Engineer :	SIGNATURE
วิศวกรผู้ออกแบบระบบไฟฟ้ากำลัง	
นายสุภัทร บูรณวิทย์ วฟก.1265 ที่อยู่ 21 ซอยทานสัมฤทธิ 13 ตำบลท่าทราย อ.เมืองนนทบุรี จ.นนทบุรี 11000	สุภัทร บูรณวิทย์

Mechanical Engineer :	SIGNATURE
วิศวกรผู้ออกแบบระบบเครื่องกลและปรับอากาศ	
นายประสิทธิ เกียวสุนทร วก.1221 ที่อยู่ 44/372 ซอยบางกระดี 35/1 แขวงแสมดำ เขตบางขุนเทียน กทม. 10150	ประสิทธิ์

Sanitary Engineer :	SIGNATURE
วิศวกรผู้ออกแบบระบบสุขาภิบาล และดับเพลิง	
นายทศวรรษ สนันฤทธิ วส. 215 ที่อยู่ บ้านเลขที่ 99/107 หมู่ที่ 3 ต.ศีรษะจรเข้น้อย อ.บางเสาธง จ.สมุทรปราการ 10540	ทศวรรษ

ISSUE/REVISION

REV.	DESCRIPTION	DATE
A	90% DEVELOPED	09/05/2026

PROJECT NAME :

GEDC 01

LOCATION:
Nikhom Phattana district, Rayong ,industrial estate,CPGC

BUILDING :

90% DEVELOPED

TITLE :

ROOM DETAIL-1F-DATA HALL1-3 (LC)
、FAN WALL ROOM 1-3A,1-3B PLAN

JOB NO.		SCALE	1 : 75
DRAWN	NXR	REF.	
CHECKED	LJC	DWG. NO.	MPK01A-90-A-RD-105
APPROVED	LXD		
DATE	2026.05.09		

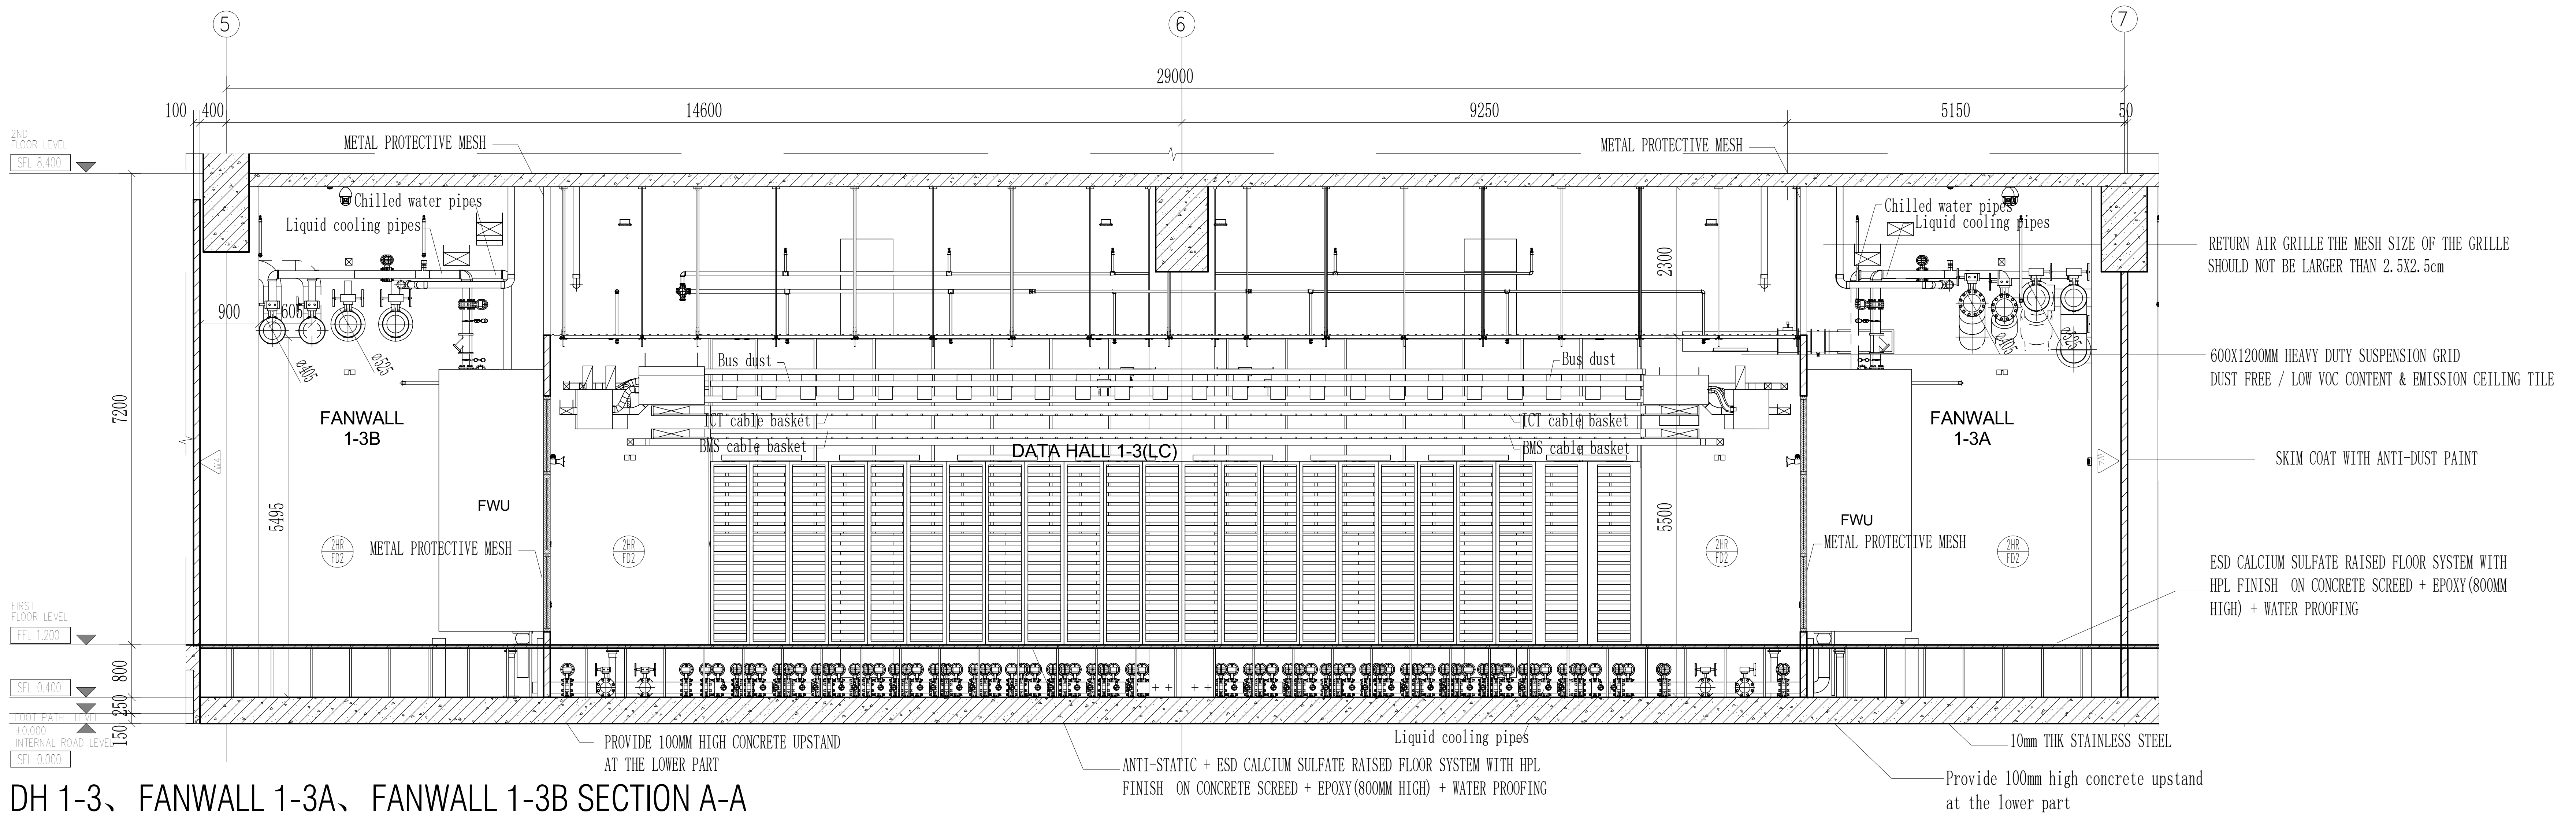
5
6
7
29000
100
400
14600
9250
5150
50
2ND FLOOR LEVEL
SFL 8.400
METAL PROTECTIVE MESH
Chilled water pipes
Liquid cooling pipes
900
605
ø405
ø525
2300
7200
5495
5500
FANWALL 1-3B
FWU
Bus dust
ICT cable basket
BMS cable basket
DATA HALL 1-3(LC)
FANWALL 1-3A
2HR FD2
FIRST FLOOR LEVEL
FFL 1.200
SFL 0.400
±0.000 INTERNAL ROAD LEVEL
SFL 0.000
800
250
150
RETURN AIR GRILLE THE MESH SIZE OF THE GRILLE SHOULD NOT BE LARGER THAN 2.5X2.5cm
600X1200MM HEAVY DUTY SUSPENSION GRID DUST FREE / LOW VOC CONTENT & EMISSION CEILING TILE
SKIM COAT WITH ANTI-DUST PAINT
ESD CALCIUM SULFATE RAISED FLOOR SYSTEM WITH HPL FINISH ON CONCRETE SCREED + EPOXY(800MM HIGH) + WATER PROOFING
PROVIDE 100MM HIGH CONCRETE UPSTAND AT THE LOWER PART
Liquid cooling pipes
ANTI-STATIC + ESD CALCIUM SULFATE RAISED FLOOR SYSTEM WITH HPL FINISH ON CONCRETE SCREED + EPOXY(800MM HIGH) + WATER PROOFING
10mm THK STAINLESS STEEL
Provide 100mm high concrete upstand at the lower part

DH 1-3、FANWALL 1-3A、FANWALL 1-3B SECTION A-A

Scale 1:50

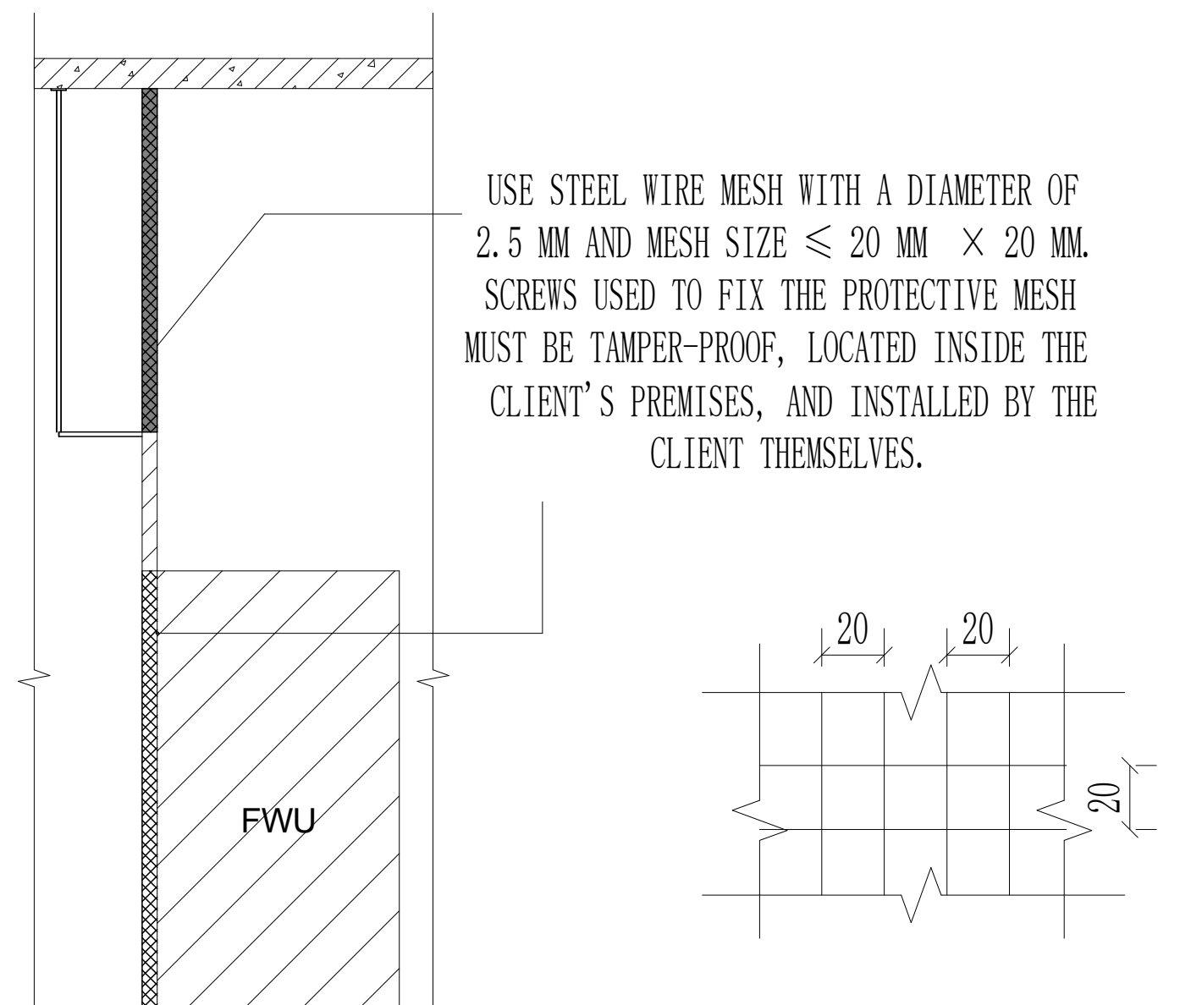
USE STEEL WIRE MESH WITH A DIAMETER OF 2.5 MM AND MESH SIZE ≤ 20 MM × 20 MM. SCREWS USED TO FIX THE PROTECTIVE MESH MUST BE TAMPER-PROOF, LOCATED INSIDE THE CLIENT'S PREMISES, AND INSTALLED BY THE CLIENT THEMSELVES.
FWU
20
20
20

METAL PROTECTIVE MESH DETAIL

SCALE : NTS

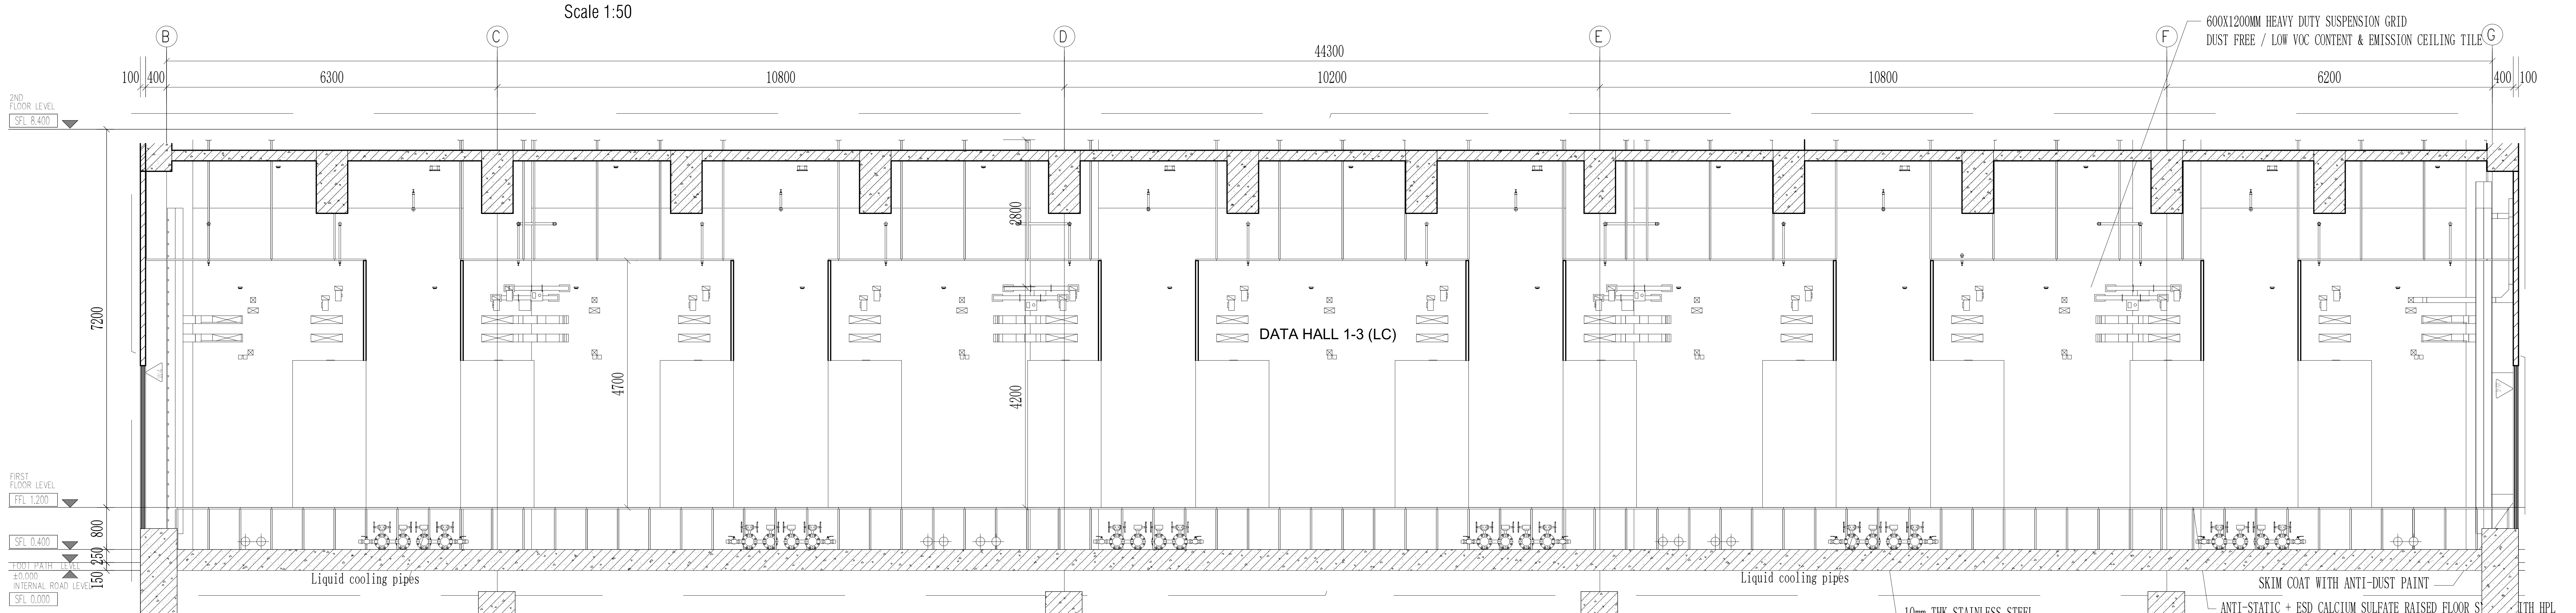
B
C
D
E
F
G
44300
100
400
6300
10800
10200
10800
6200
400
100
600X1200MM HEAVY DUTY SUSPENSION GRID DUST FREE / LOW VOC CONTENT & EMISSION CEILING TILE
2ND FLOOR LEVEL
SFL 8.400
7200
2800
4700
4200
DATA HALL 1-3 (LC)
FIRST FLOOR LEVEL
FFL 1.200
SFL 0.400
±0.000 INTERNAL ROAD LEVEL
SFL 0.000
800
250
150
Liquid cooling pipes
Liquid cooling pipes
10mm THK STAINLESS STEEL
SKIM COAT WITH ANTI-DUST PAINT
ANTI-STATIC + ESD CALCIUM SULFATE RAISED FLOOR SYSTEM WITH HPL FINISH ON CONCRETE SCREED + EPOXY(800MM HIGH) + WATER PROOFING

DH 1-3 SECTION B-B

Scale 1:50

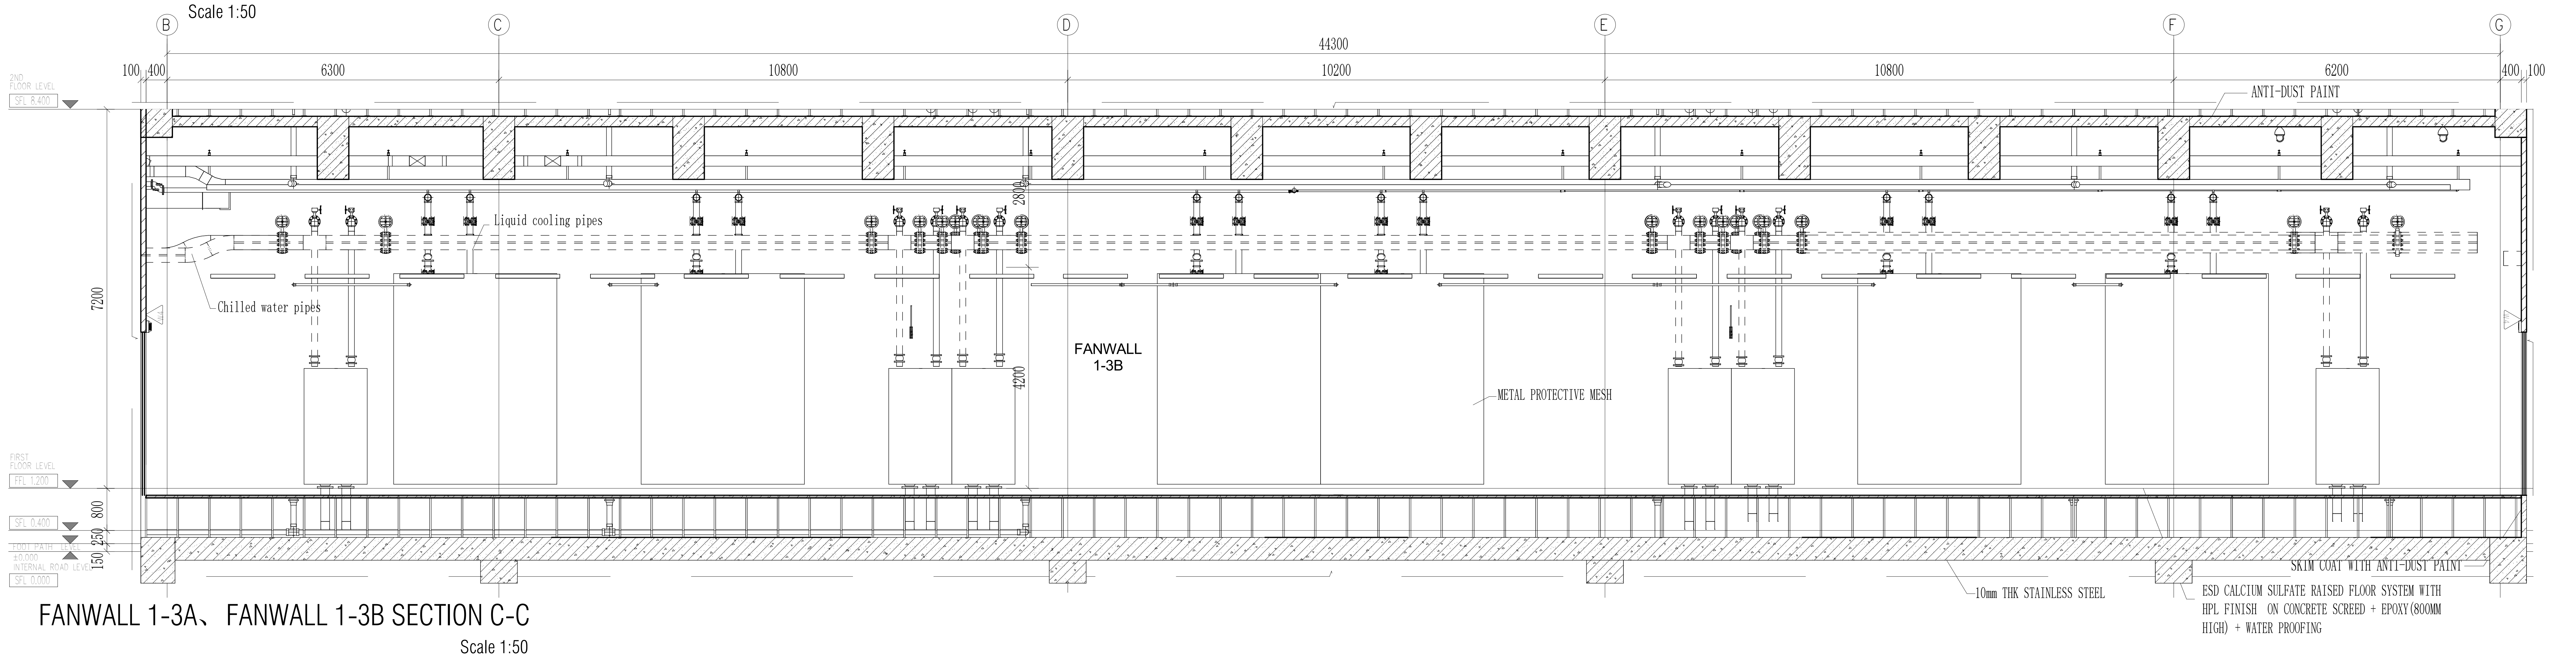
B
C
D
E
F
G
44300
100
400
6300
10800
10200
10800
6200
400
100
ANTI-DUST PAINT
2ND FLOOR LEVEL
SFL 8.400
Liquid cooling pipes
2800
7200
Chilled water pipes
FANWALL 1-3B
4200
METAL PROTECTIVE MESH
FIRST FLOOR LEVEL
FFL 1.200
SFL 0.400
±0.000 INTERNAL ROAD LEVEL
SFL 0.000
800
250
150
SKIM COAT WITH ANTI-DUST PAINT
10mm THK STAINLESS STEEL
ESD CALCIUM SULFATE RAISED FLOOR SYSTEM WITH HPL FINISH ON CONCRETE SCREED + EPOXY(800MM HIGH) + WATER PROOFING

FANWALL 1-3A、FANWALL 1-3B SECTION C-C

Scale 1:50

NOTE :THIS PRINT IS OF A CONFIDENTIAL NATURE, IT SHALL NOT BE TRACED,PHOTOGRAPHED,PHOTOSTATED OR REPRODUCED IN ANY MANER,NOR USED FOR ANY PURPOSE WHATSOEVER EXCEPT BY WRITTEN PERMISSION

CLIENT :

GULF EDGE DC 01

87 Wireless Road, M Thai Tower 11th. Floor, All Seasons Place, Lumpini,
Pathumwan, Bangkok 10330, Thailand

CONTRACTOR :

华西发展(泰国)有限公司
บริษัท หัวซือ ดีเวลลอปเม้นต์ (ประเทศไทย) จำกัด
HUASHI DEVELOPMENT CO.,LTD
No. 202, Room No. 1403, 14/F, Le Concorde Building,
Ratchadapisek Road, Huaykhwang Sub-District,
Huaykhwang District, Bangkok Metropolitan 10310.

CONSULTANT :

ARbay
บริษัท เอ อาร์ เบย์ จำกัด
ARbay Company Limited
31 st Floor Bangkok Insurance Building
25 South Sathorn road Thungmahamek
Sathorn Bangkok 10120 THAILAND
T +66 (0) 2286 8199
F +66 (0) 2286 2863
info@arbay.co.th

CONSULTANT :

Qbic Engineers & Architects Co.,Ltd.
8 Soi KALONG 4 SANAMBINNAM ROAD,
THASAI SUB-DISTRICT, MUANG NONTHABURI DISTRICT
, NONTHABURI.
Tel 662-950-4374
Fax 662-580-3231
E-Mail : qbic@qbic.co.th, www.qbic.co.th
QBIC ENGINEERS AND ARCHITECTS CO.,LTD.

CONSULTANT :

MITR
MITR TECHNICAL CONSULTANT CO.,LTD.
1168/8 12th FLOOR, LUMPINI TOWER BUILDING,
RAMA IV RD., THUNGMAHAMEK, SATHORN, BANGKOK 10120, THAILAND
TEL : 0-2679-9079-84
FAX : 0-2679-9085 E-mail: mitr_dd@mitr.com

Architect :	SIGNATURE
ประกิต พนานุรัตน์ วสถ. 580 ที่อยู่ 251/1 ถ.จารุเมือง แขวงรองเมือง เขตปทุมวัน กรุงเทพมหานคร โทรศัพท์ 02-286-8199	
Structural Engineer :	SIGNATURE
วิศวกรผู้ออกแบบโครงสร้าง	
ณัฐสม สงวนวงษ์ วย 1423 ที่อยู่ 2/1 ซ.รามคำแหง 150 ถ.รามคำแหง แขวง สะพานสูง เขต สะพานสูง กทม. 10240	ณัฐสม สงวนวงษ์
Structural Inspector :	SIGNATURE
วิศวกรผู้ตรวจสอบโครงสร้าง	
โกมล จุฑาภัทร วย 964 ที่อยู่ 24/18 ซ.นวมินทร์ 129 ถ. นวมินทร์ แขวง นวลจันทร์ เขต บึงกุ่ม กทม. 10230	
Electrical Engineer :	SIGNATURE
วิศวกรผู้ออกแบบระบบไฟฟ้ากำลัง	
นายสุภัทร บูรณวิทย์ วฟก.1265 ที่อยู่ 21 ซอยทานสัมฤทธิ์ 13 ตำบลท่าทราย อ.เมืองนนทบุรี จ.นนทบุรี 11000	
Mechanical Engineer :	SIGNATURE
วิศวกรผู้ออกแบบระบบเครื่องกลและปรับอากาศ	
นายประสิทธิ์ เกี้ยวสุนทร วก.1221 ที่อยู่ 44/372 ซอยบางกระดี่ 35/1 แขวงแสมดำ เขตบางขุนเทียน กทม. 10150	ประสิทธิ์
Sanitary Engineer :	SIGNATURE
วิศวกรผู้ออกแบบระบบสุขาภิบาล และดับเพลิง	
นายทศวรรษ สนั่นฤทธิ์ วส. 215 ที่อยู่ บ้านเลขที่ 99/107 หมู่ที่ 3 ต.ศีรษะจรเข้น้อย อ.บางเสาธง จ.สมุทรปราการ 10540	ทศวรรษ

ISSUE/REVISION

REV.	DESCRIPTION	DATE
A	90% DEVELOPED	09/05/2026

PROJECT NAME :

GEDC 01

LOCATION:
Nikhom Phattana district, Rayong ,industrial estate,CPGC

BUILDING :

90% DEVELOPED

TITLE :

ROOM DETAIL-1F-DATA HALL1-3 (LC)
、FAN WALL ROOM 1-3A,1-3B SECTION

JOB NO.	SCALE 1 : 50
DRAWN NXR	REF.
CHECKED LJC	DWG. NO. MPK01A-90-A-RD-106
APPROVED LXD	
DATE 2026.05.09	

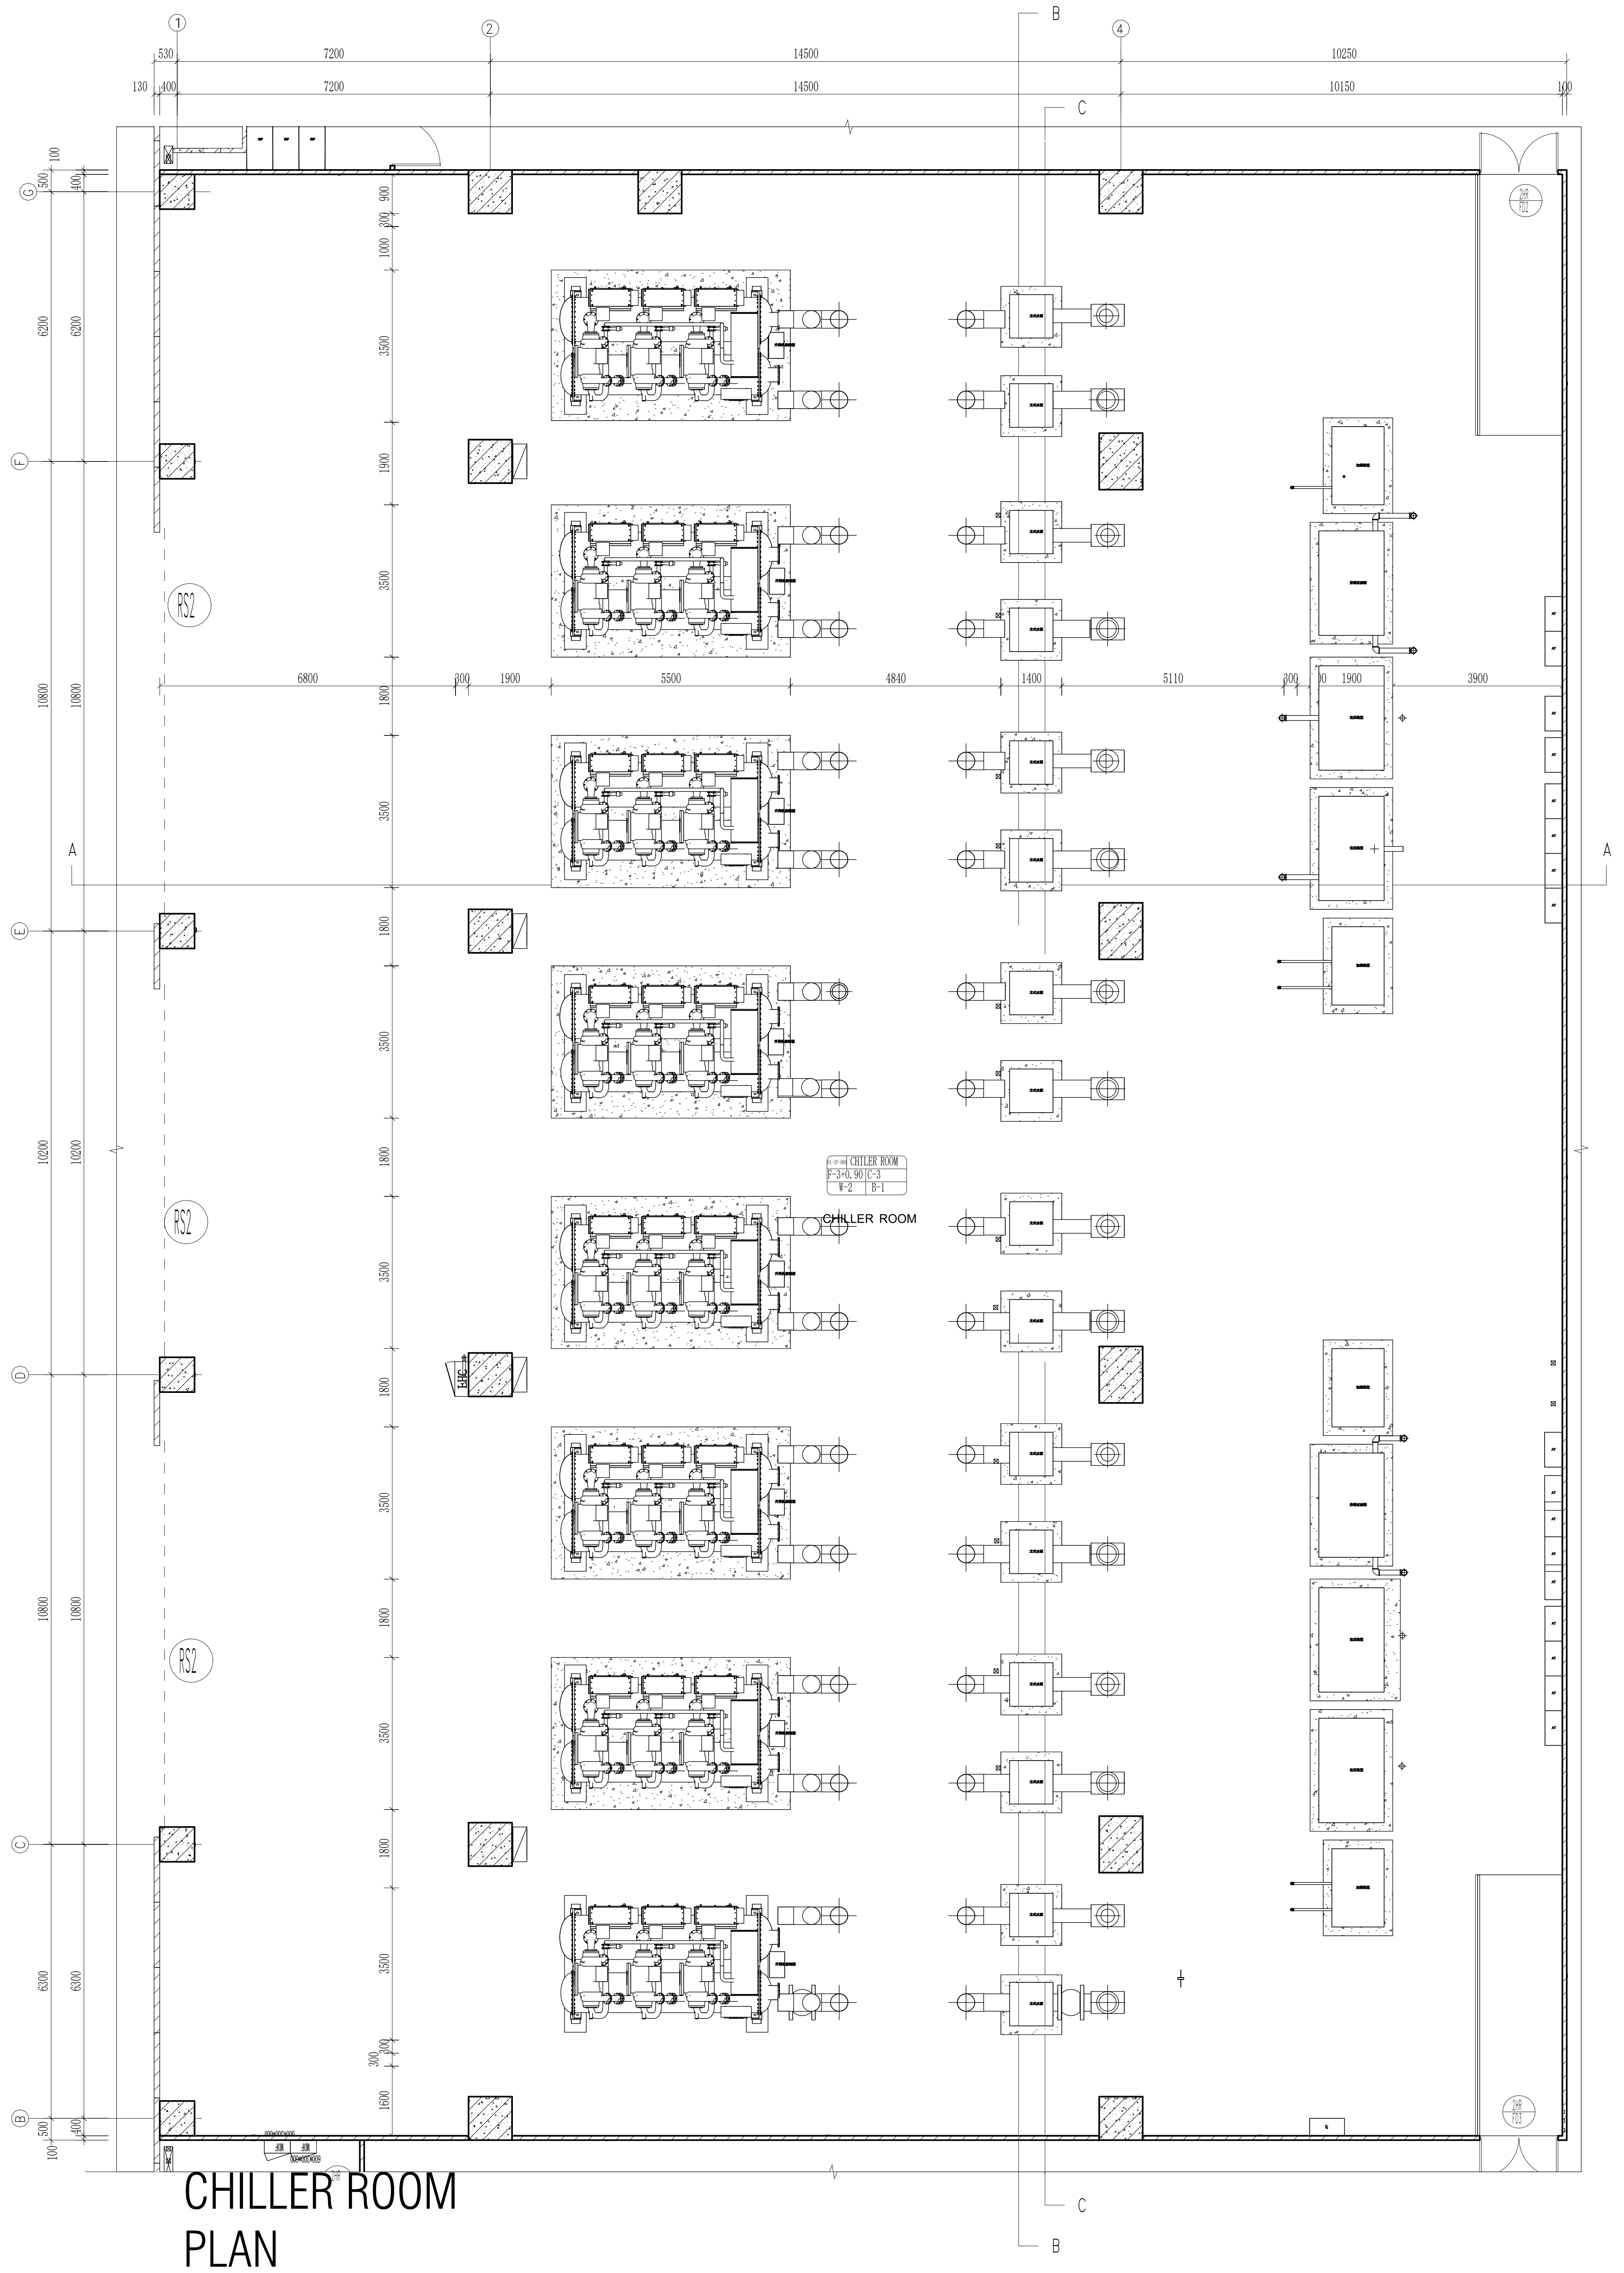

CHILLER ROOM PLAN

Scale 1:75

THE "SFL" MARKED IN THE DRAWING REFERS TO THE STRUCTURAL FLOOR LEVEL, WHILE THE FINISHED FLOOR LEVEL (FFL) IS DETERMINED BASED ON FLOOR FINISHES.

CLIENT :

GULF EDGE DC 01

87 Wireless Road, M Thai Tower 11th. Floor, All Seasons Place, Lumpini,
Pathumwan, Bangkok 10330, Thailand

CONTRACTOR :

华西发展(泰国)有限公司
บริษัท หัวซือ ดีเวลลอปเม้นต์ (ประเทศไทย) จำกัด
HUASHI DEVELOPMENT CO.,LTD
No. 202, Room No. 1403, 14/F, Le Concorde Building,
Ratchadapisek Road, Huaykhwang Sub-District,
Huaykhwang District, Bangkok Metropolitan 10310.

CONSULTANT :

บริษัท เอ อาร์ เบย์ จำกัด
ARbay Company Limited
31 st Floor Bangkok Insurance Building
25 South Sathorn road Thungmahamek
Sathorn Bangkok 10120 THAILAND
T +66 (0) 2286 8199
F +66 (0) 2286 2863
info@arbay.co.th

CONSULTANT :

Qbic Engineers & Architects Co.,Ltd.
8 Soi KALONG 4 SANAMBINNAM ROAD,
THASAI SUB-DISTRICT, MUANG NONTHABURI DISTRICT
, NONTHABURI.
Tel 662-950-4374
Fax 662-580-3231
E-Mail : qbic@qbic.co.th, www.qbic.co.th
QBIC ENGINEERS AND ARCHITECTS CO.,LTD.

CONSULTANT :

MITR TECHNICAL CONSULTANT CO.,LTD.
1168/8 12th FLOOR, LUMPINI TOWER BUILDING,
RAMA IV RD., THUNGMAHAMEK, SATHORN, BANGKOK 10120, THAILAND
TEL : 0-2679-9079-84
FAX : 0-2679-9085 E-mail: mitr_dd@mitr.com

Architect :	SIGNATURE
ประกิต พนานุรัตน์ วสถ. 580 ที่อยู่ 251/1 ถ.จารุเมือง แขวงรองเมือง เขตปทุมวัน กรุงเทพมหานคร โทรศัพท์ 02-286-8199	
Structural Engineer :	SIGNATURE
วิศวกรผู้ออกแบบโครงสร้าง	
ณัฐสม สงวนวงษ์ วย 1423 ที่อยู่ 2/1 ซ.รามคำแหง 150 ถ.รามคำแหง แขวง สะพานสูง เขต สะพานสูง กทม. 10240	ณัฐสม สงวนวงษ์
Structural Inspector :	SIGNATURE
วิศวกรผู้ตรวจสอบโครงสร้าง	
โกมล จุฑาภัทร วย 964 ที่อยู่ 24/18 ซ.นวมินทร์ 129 ถ. นวมินทร์ แขวง นวลจันทร์ เขต บึงกุ่ม กทม. 10230	
Electrical Engineer :	SIGNATURE
วิศวกรผู้ออกแบบระบบไฟฟ้ากำลัง	
นายสุภัทร บูรณวิทย์ วฟก.1265 ที่อยู่ 21 ซอยทานสัมฤทธิ์ 13 ตำบลท่าทราย อ.เมืองนนทบุรี จ.นนทบุรี 11000	สุภัทร บูรณวิทย์
Mechanical Engineer :	SIGNATURE
วิศวกรผู้ออกแบบระบบเครื่องกลและปรับอากาศ	
นายประสิทธิ์ เกียวสุนทร วก.1221 ที่อยู่ 44/372 ซอยบางกระดี 35/1 แขวงแสมดำ เขตบางขุนเทียน กทม. 10150	ประสิทธิ์
Sanitary Engineer :	SIGNATURE
วิศวกรผู้ออกแบบระบบสุขาภิบาล และดับเพลิง	
นายทศวรรษ สนันฤทธิ์ วส. 215 ที่อยู่ บ้านเลขที่ 99/107 หมู่ที่ 3 ต.ศีรษะจรเข้น้อย อ.บางเสาธง จ.สมุทรปราการ 10540	ทศวรรษ

ISSUE/REVISION

REV.	DESCRIPTION	DATE
A	90% DEVELOPED	09/05/2026

PROJECT NAME :

GEDC 01

LOCATION:
Nikhom Phattana district, Rayong ,industrial estate,CPGC

BUILDING :

90% DEVELOPED

TITLE :

ROOM DETAIL-1F-CHILLER ROOM PLAN

JOB NO.		SCALE	1 : 75
DRAWN	LYT	REF.	
CHECKED	LJC	DWG. NO.	MPK01A-90-A-RD-107
APPROVED	LXD		
DATE	2026.05.09		

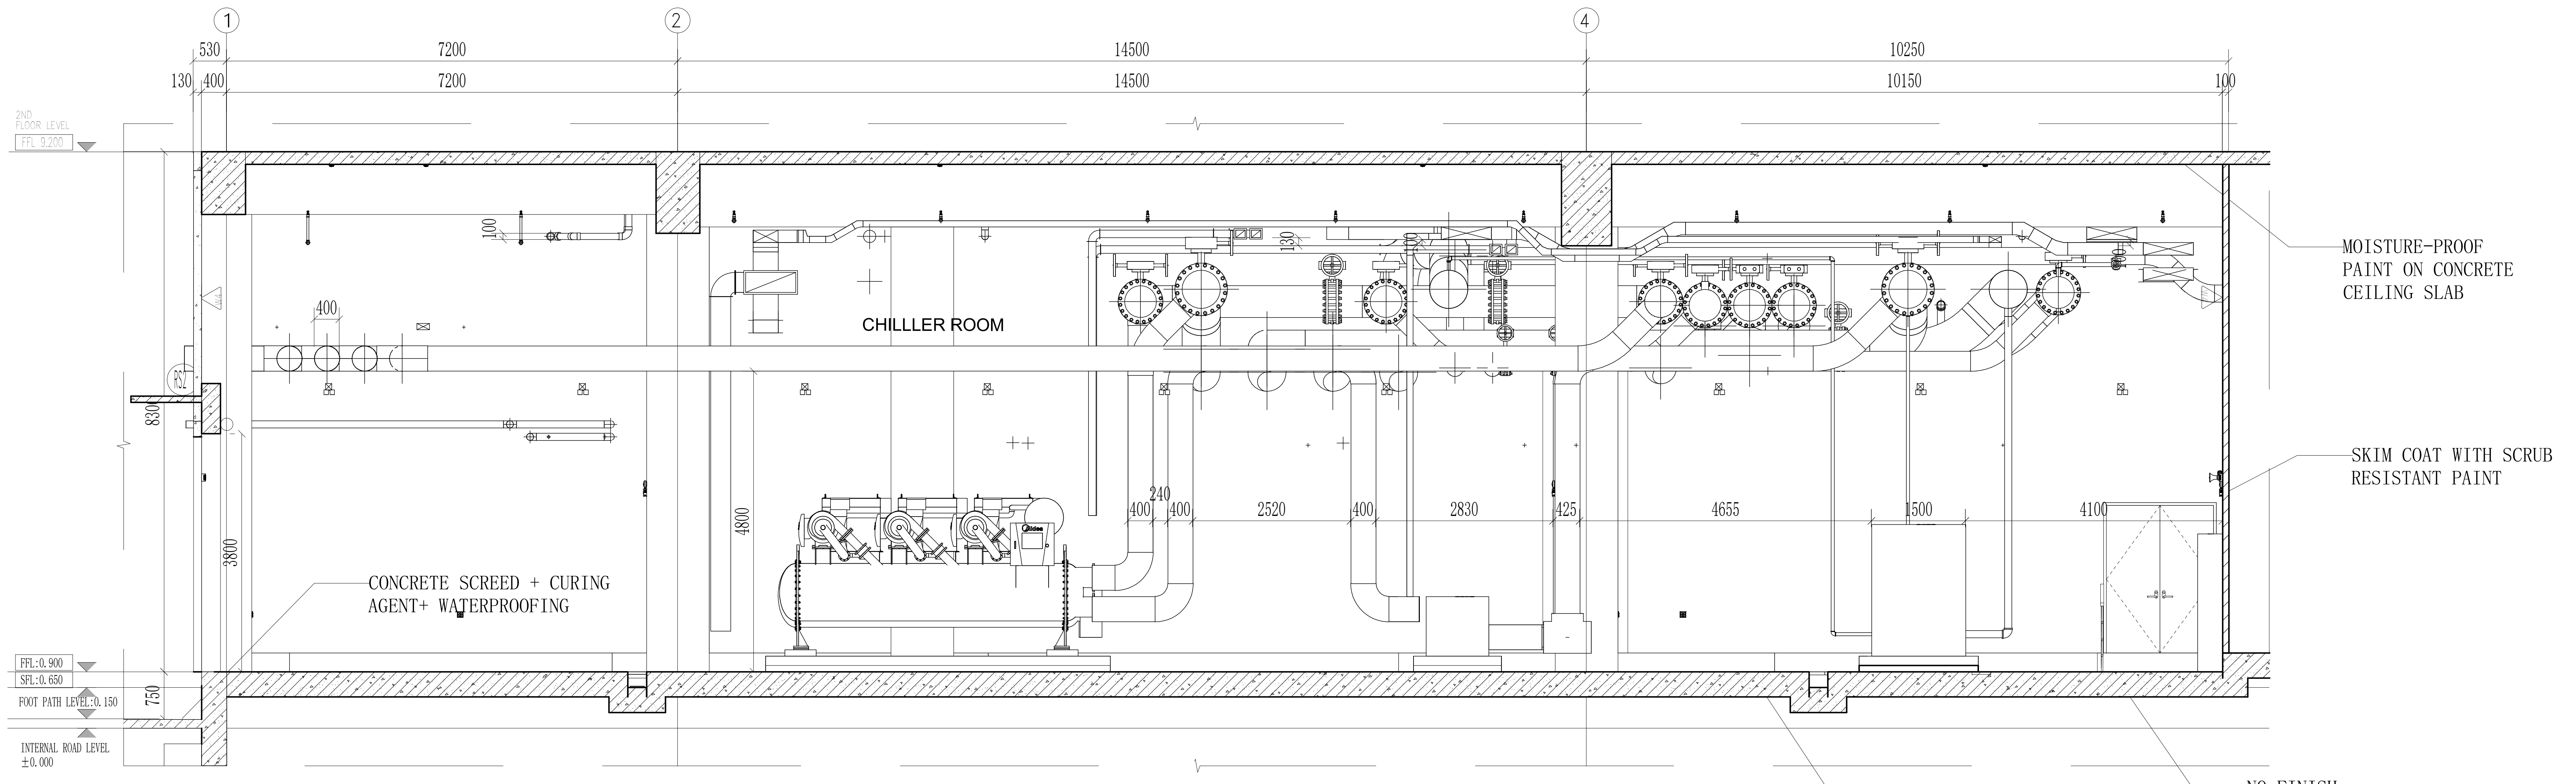
1
2
4
530
7200
14500
10250
130
400
7200
14500
10150
100
2ND FLOOR LEVEL
FFL:5.200
CHILLLER ROOM
MOISTURE-PROOF PAINT ON CONCRETE CEILING SLAB
SKIM COAT WITH SCRUB RESISTANT PAINT
CONCRETE SCREED + CURING AGENT+ WATERPROOFING
400
830
3800
4800
240
400
400
2520
400
2830
425
4655
1500
4100
FFL:0.900
SFL:0.650
FOOT PATH LEVEL:0.150
INTERNAL ROAD LEVEL ±0.000
750
CONCRETE SCREED + CURING AGENT+ WATERPROOFING
NO FINISH

CHILLER ROOM SECTION A-A Scale 1:50

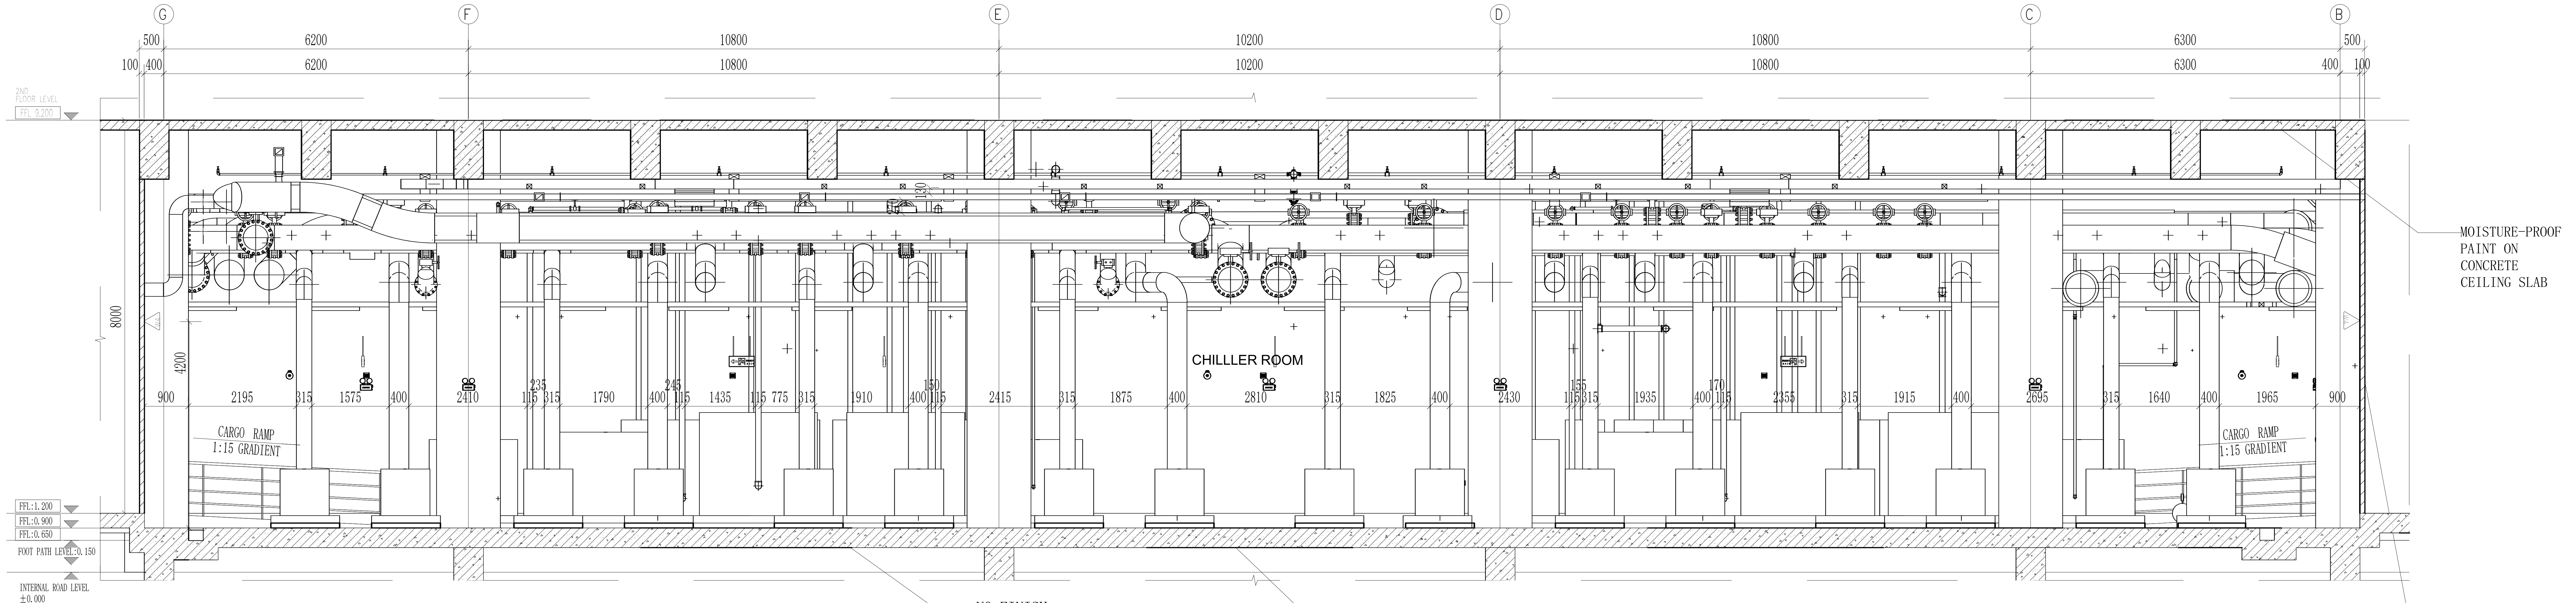
G
F
E
D
C
B
500
6200
10800
10200
10800
6300
500
100
400
6200
10800
10200
10800
6300
400
100
2ND FLOOR LEVEL
FFL:5.200
CHILLER ROOM
MOISTURE-PROOF PAINT ON CONCRETE CEILING SLAB
8000
4200
900
2195
315
1575
400
2410
115
235
315
1790
400
245
115
1435
115
775
315
1910
400
150
115
2415
315
1875
400
2810
315
1825
400
2430
115
155
315
1935
400
170
115
2355
315
1915
400
2695
315
1640
400
1965
900
CARGO RAMP 1:15 GRADIENT
CARGO RAMP 1:15 GRADIENT
FFL:1.200
FFL:0.900
FFL:0.650
FOOT PATH LEVEL:0.150
INTERNAL ROAD LEVEL ±0.000
NO FINISH
CONCRETE SCREED + CURING AGENT+ WATERPROOFING
SKIM COAT WITH SCRUB RESISTANT PAINT

CHILLER ROOM SECTION B-B Scale 1:50

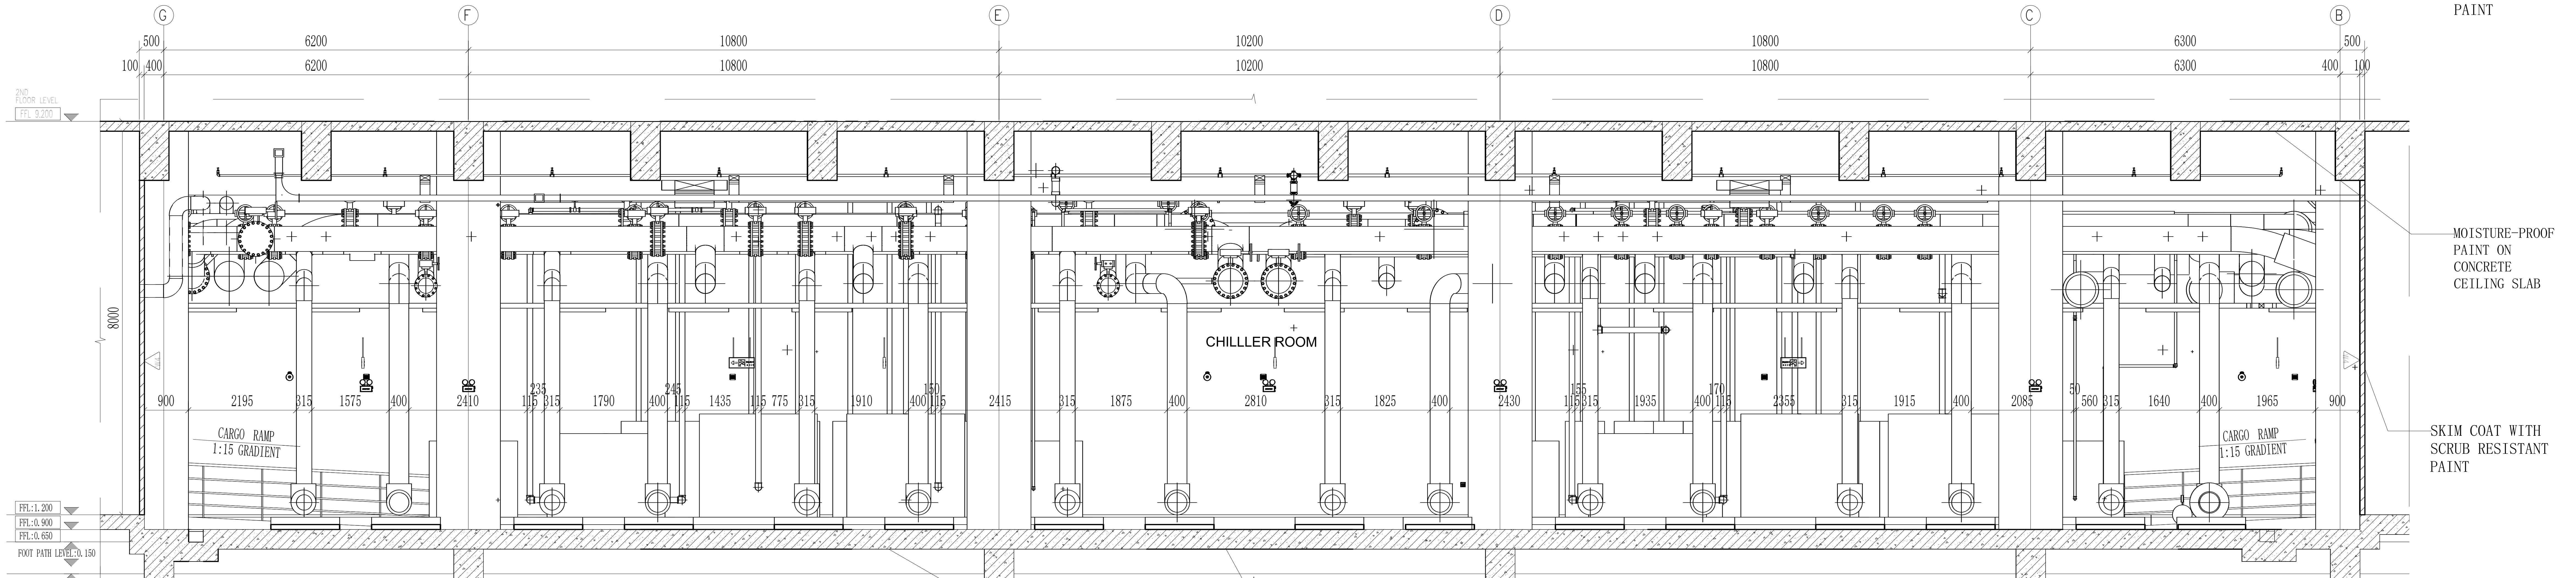
G
F
E
D
C
B
500
6200
10800
10200
10800
6300
500
100
400
6200
10800
10200
10800
6300
400
100
2ND FLOOR LEVEL
FFL:5.200
CHILLLER ROOM
MOISTURE-PROOF PAINT ON CONCRETE CEILING SLAB
SKIM COAT WITH SCRUB RESISTANT PAINT
8000
900
2195
315
1575
400
2410
115
235
315
1790
400
245
115
1435
115
775
315
1910
400
150
115
2415
315
1875
400
2810
315
1825
400
2430
115
155
315
1935
400
170
115
2355
315
1915
400
2085
50
560
315
1640
400
1965
900
CARGO RAMP 1:15 GRADIENT
CARGO RAMP 1:15 GRADIENT
FFL:1.200
FFL:0.900
FFL:0.650
FOOT PATH LEVEL:0.150
INTERNAL ROAD LEVEL ±0.000
NO FINISH
CONCRETE SCREED + CURING AGENT+ WATERPROOFING

CHILLER ROOM SECTION C-C Scale 1:50

CLIENT :

GULF EDGE DC 01

87 Wireless Road, M Thai Tower 11th. Floor, All Seasons Place, Lumpini,
Pathumwan, Bangkok 10330, Thailand

CONTRACTOR :

华西发展(泰国)有限公司
บริษัท หัวซือ ดีเวลลอปเม้นต์ (ประเทศไทย) จำกัด
HUASHI DEVELOPMENT CO.,LTD
No. 202, Room No. 1403, 14/F, Le Concorde Building,
Ratchadapisek Road, Huaykhwang Sub-District,
Huaykhwang District, Bangkok Metropolitan 10310.

CONSULTANT :

ARbay
บริษัท เอ อาร์ เบย์ จำกัด
ARbay Company Limited
31 st Floor Bangkok Insurance Building
25 South Sathorn road Thungmahamek
Sathorn Bangkok 10120 THAILAND
T +66 (0) 2286 8199
F +66 (0) 2286 2863
info@arbay.co.th

CONSULTANT :

Qbic Engineers & Architects Co.,Ltd.
8 Soi KALONG 4 SANAMBINNAM ROAD,
THASAI SUB-DISTRICT, MUANG NONTHABURI DISTRICT
, NONTHABURI.
Tel 662-950-4374
Fax 662-580-3231
E-Mail : qbic@qbic.co.th, www.qbic.co.th
QBIC ENGINEERS AND ARCHITECTS CO.,LTD.

CONSULTANT :

MITR
MITR TECHNICAL CONSULTANT CO.,LTD.
1168/8 12th FLOOR, LUMPINI TOWER BUILDING,
RAMA IV RD., THUNGMAHAMEK, SATHORN, BANGKOK 10120, THAILAND
TEL : 0-2679-9079-84
FAX : 0-2679-9085 E-mail: mitr_dd@mitr.com

Architect :	SIGNATURE
ประกิต พนานุรัตน์ วสถ. 580 ที่อยู่ 251/1 ถ.จารุเมือง แขวงรองเมือง เขตปทุมวัน กรุงเทพมหานคร โทรศัพท์ 02-286-8199	
Structural Engineer :	SIGNATURE
วิศวกรผู้ออกแบบโครงสร้าง	
ณัฐสม สงวนวงษ์ วย 1423 ที่อยู่ 2/1 ซ.รามคำแหง 150 ถ.รามคำแหง แขวง สะพานสูง เขต สะพานสูง กทม. 10240	ณัฐสม สงวนวงษ์
Structural Inspector :	SIGNATURE
วิศวกรผู้ตรวจสอบโครงสร้าง	
โกมล จุฑาภัทร วย 964 ที่อยู่ 24/18 ซ.นวมินทร์ 129 ถ. นวมินทร์ แขวง นวลจันทร์ เขต บึงกุ่ม กทม. 10230	
Electrical Engineer :	SIGNATURE
วิศวกรผู้ออกแบบระบบไฟฟ้ากำลัง	
นายสุภัทร บูรณวิทย์ วฟก.1265 ที่อยู่ 21 ซอยทานสัมฤทธิ์ 13 ตำบลท่าทราย อ.เมืองนนทบุรี จ.นนทบุรี 11000	สุภัทร
Mechanical Engineer :	SIGNATURE
วิศวกรผู้ออกแบบระบบเครื่องกลและปรับอากาศ	
นายประสิทธิ์ เกี้ยวสุนทร วก.1221 ที่อยู่ 44/372 ซอยบางกระดี่ 35/1 แขวงแสมดำ เขตบางขุนเทียน กทม. 10150	ประสิทธิ์
Sanitary Engineer :	SIGNATURE
วิศวกรผู้ออกแบบระบบสุขาภิบาล และดับเพลิง	
นายทศวรรษ สนั่นฤทธิ์ วส. 215 ที่อยู่ บ้านเลขที่ 99/107 หมู่ที่ 3 ต.ศีรษะจรเข้น้อย อ.บางเสาธง จ.สมุทรปราการ 10540	ทศวรรษ

ISSUE/REVISION

REV.	DESCRIPTION	DATE
A	90% DEVELOPED	09/05/2026

PROJECT NAME :

GEDC 01

LOCATION:
Nikhom Phattana district, Rayong ,industrial estate,CPGC

BUILDING :
MAIN BUILDING

90% DEVELOPED

TITLE :

ROOM DETAIL-1F-CHILLER ROOM SECTION

JOB NO.	SCALE 1 : 50
DRAWN LYT	REF.
CHECKED LJC	DWG. NO. MPK01A-90-A-RD-108
APPROVED LXD	
DATE 2026.05.09	

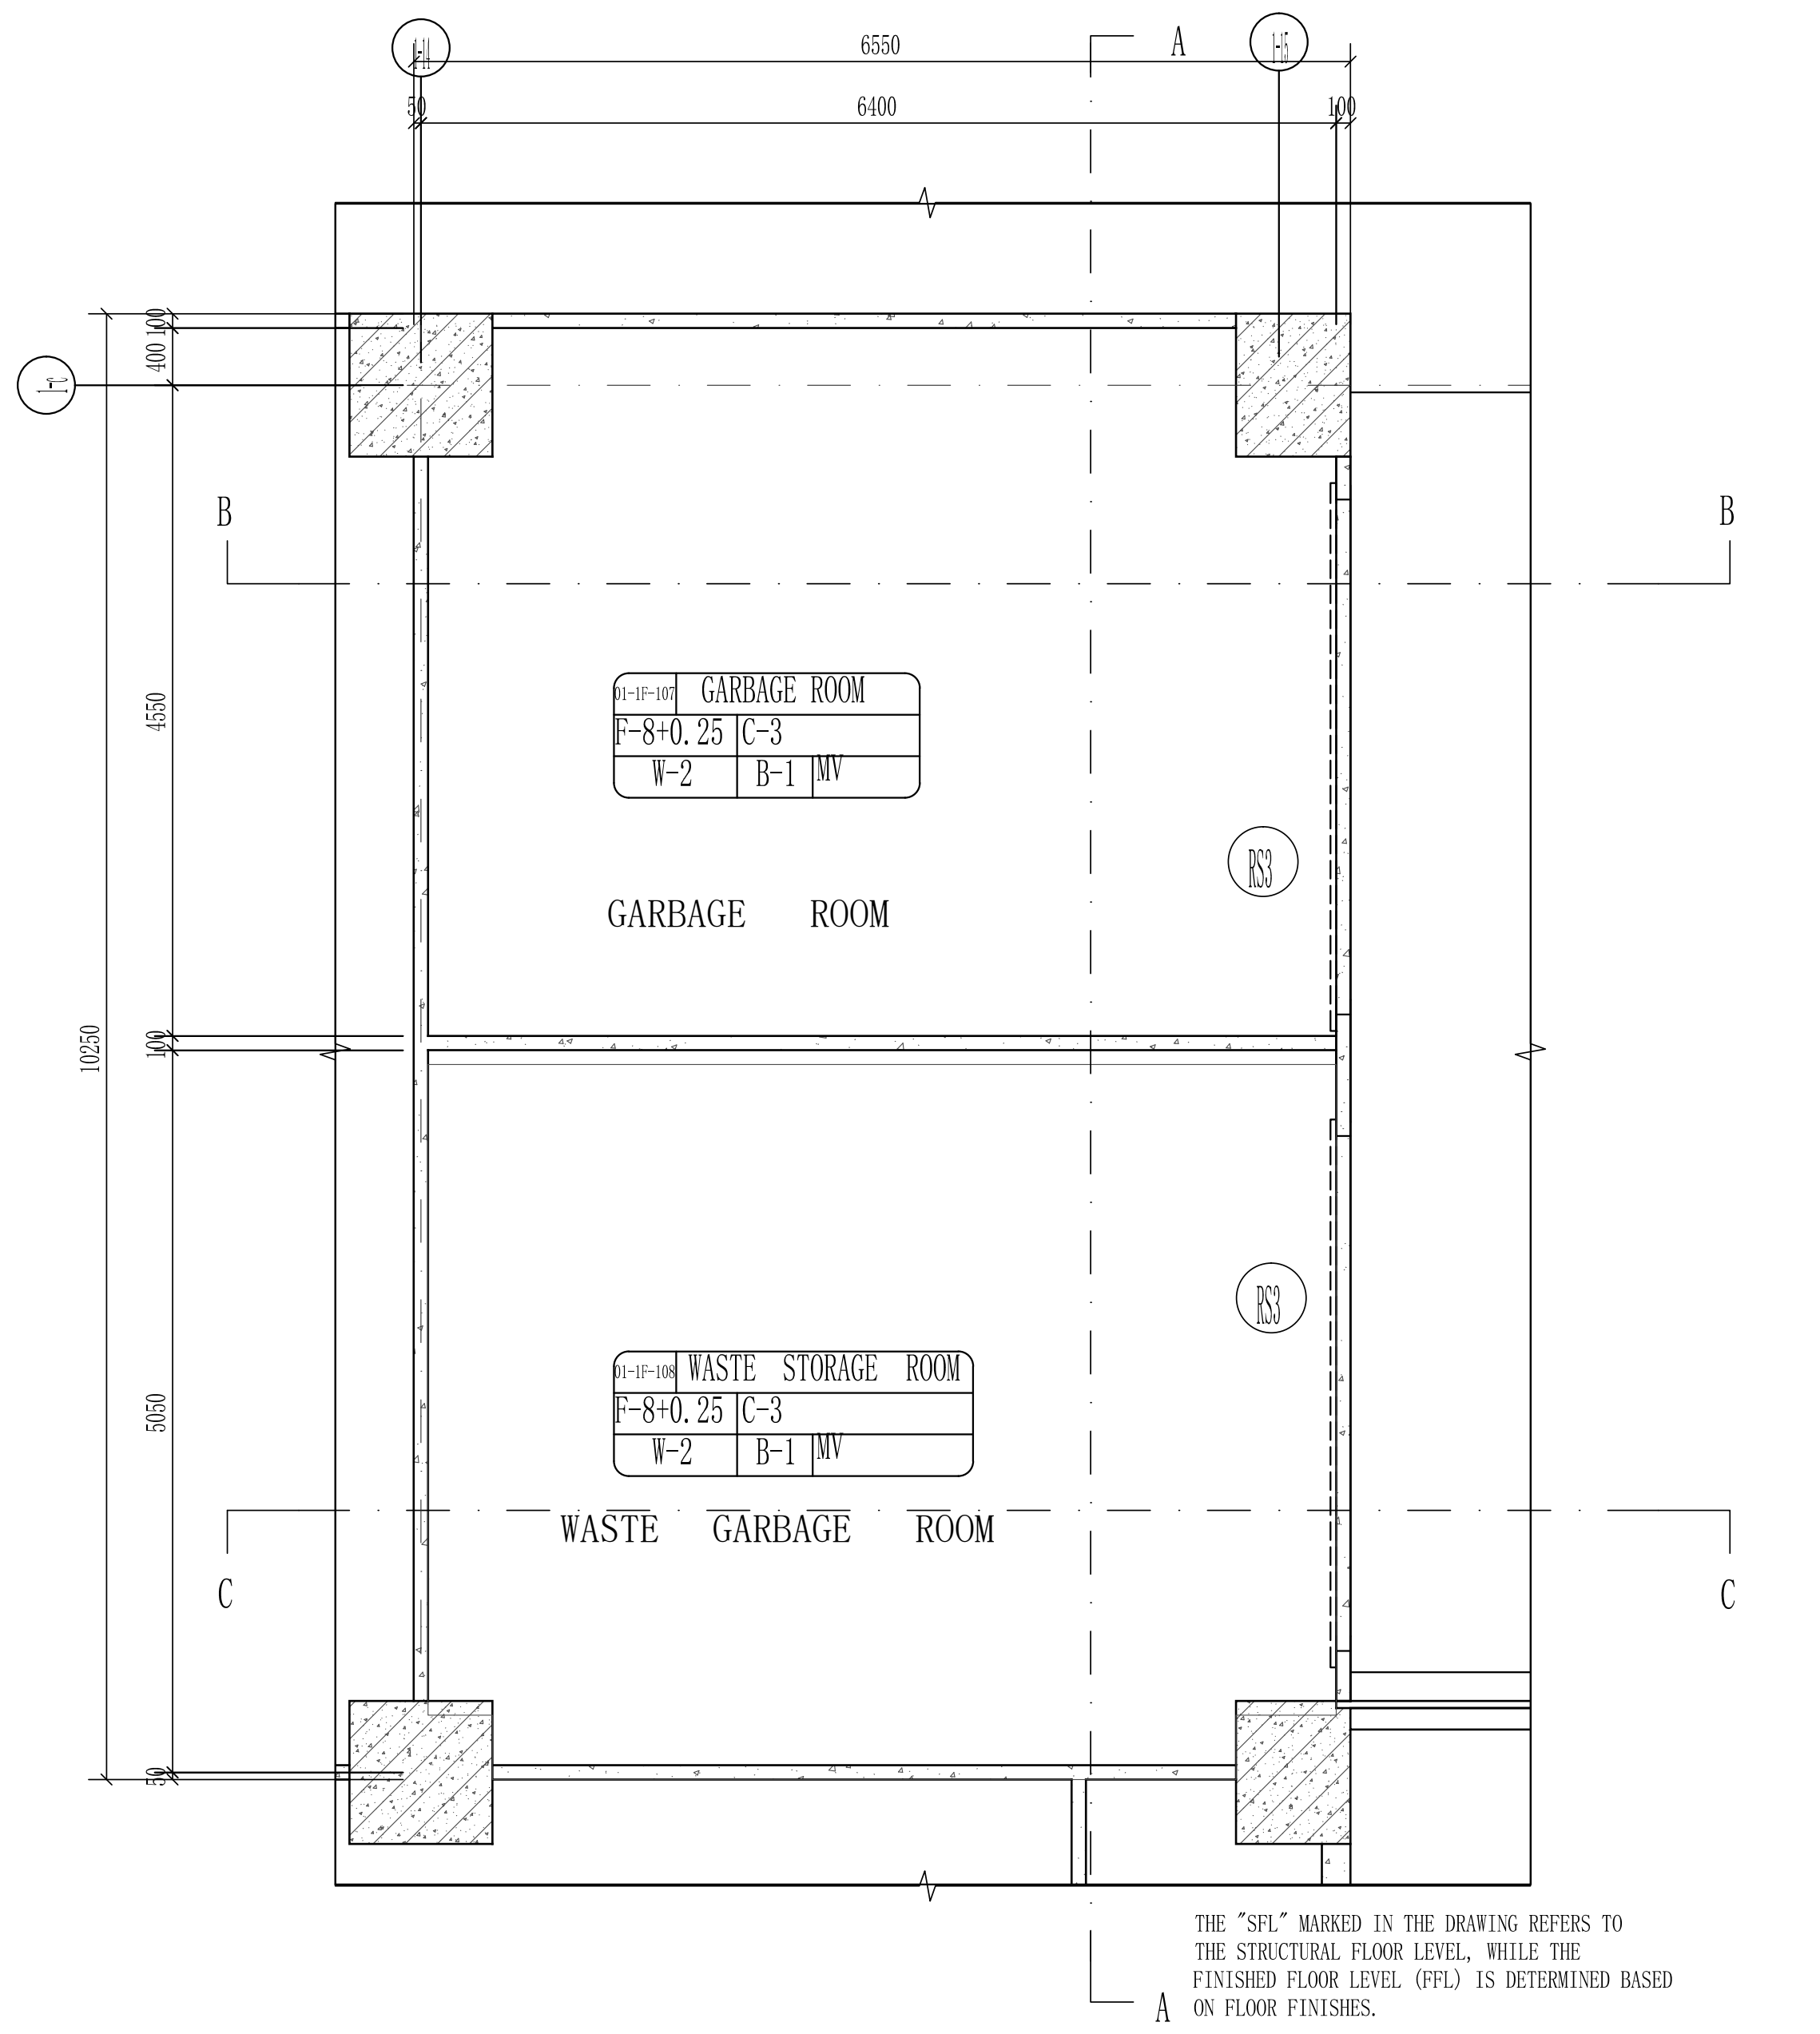
A
6550
6400
50
100
B
B
C
C
400
100
4550
5050
10250
01-1F-107 GARBAGE ROOM
F-8+0.25
C-3
W-2
B-1
MV
GARBAGE ROOM
RS3
RS3
01-1F-108 WASTE STORAGE ROOM
F-8+0.25
C-3
W-2
B-1
MV
WASTE GARBAGE ROOM
A

THE "SFL" MARKED IN THE DRAWING REFERS TO THE STRUCTURAL FLOOR LEVEL, WHILE THE FINISHED FLOOR LEVEL (FFL) IS DETERMINED BASED ON FLOOR FINISHES.

WET GARBAGE ROOM GARBAGE ROOM FIRST FLOOR PLAN

Scale 1:50

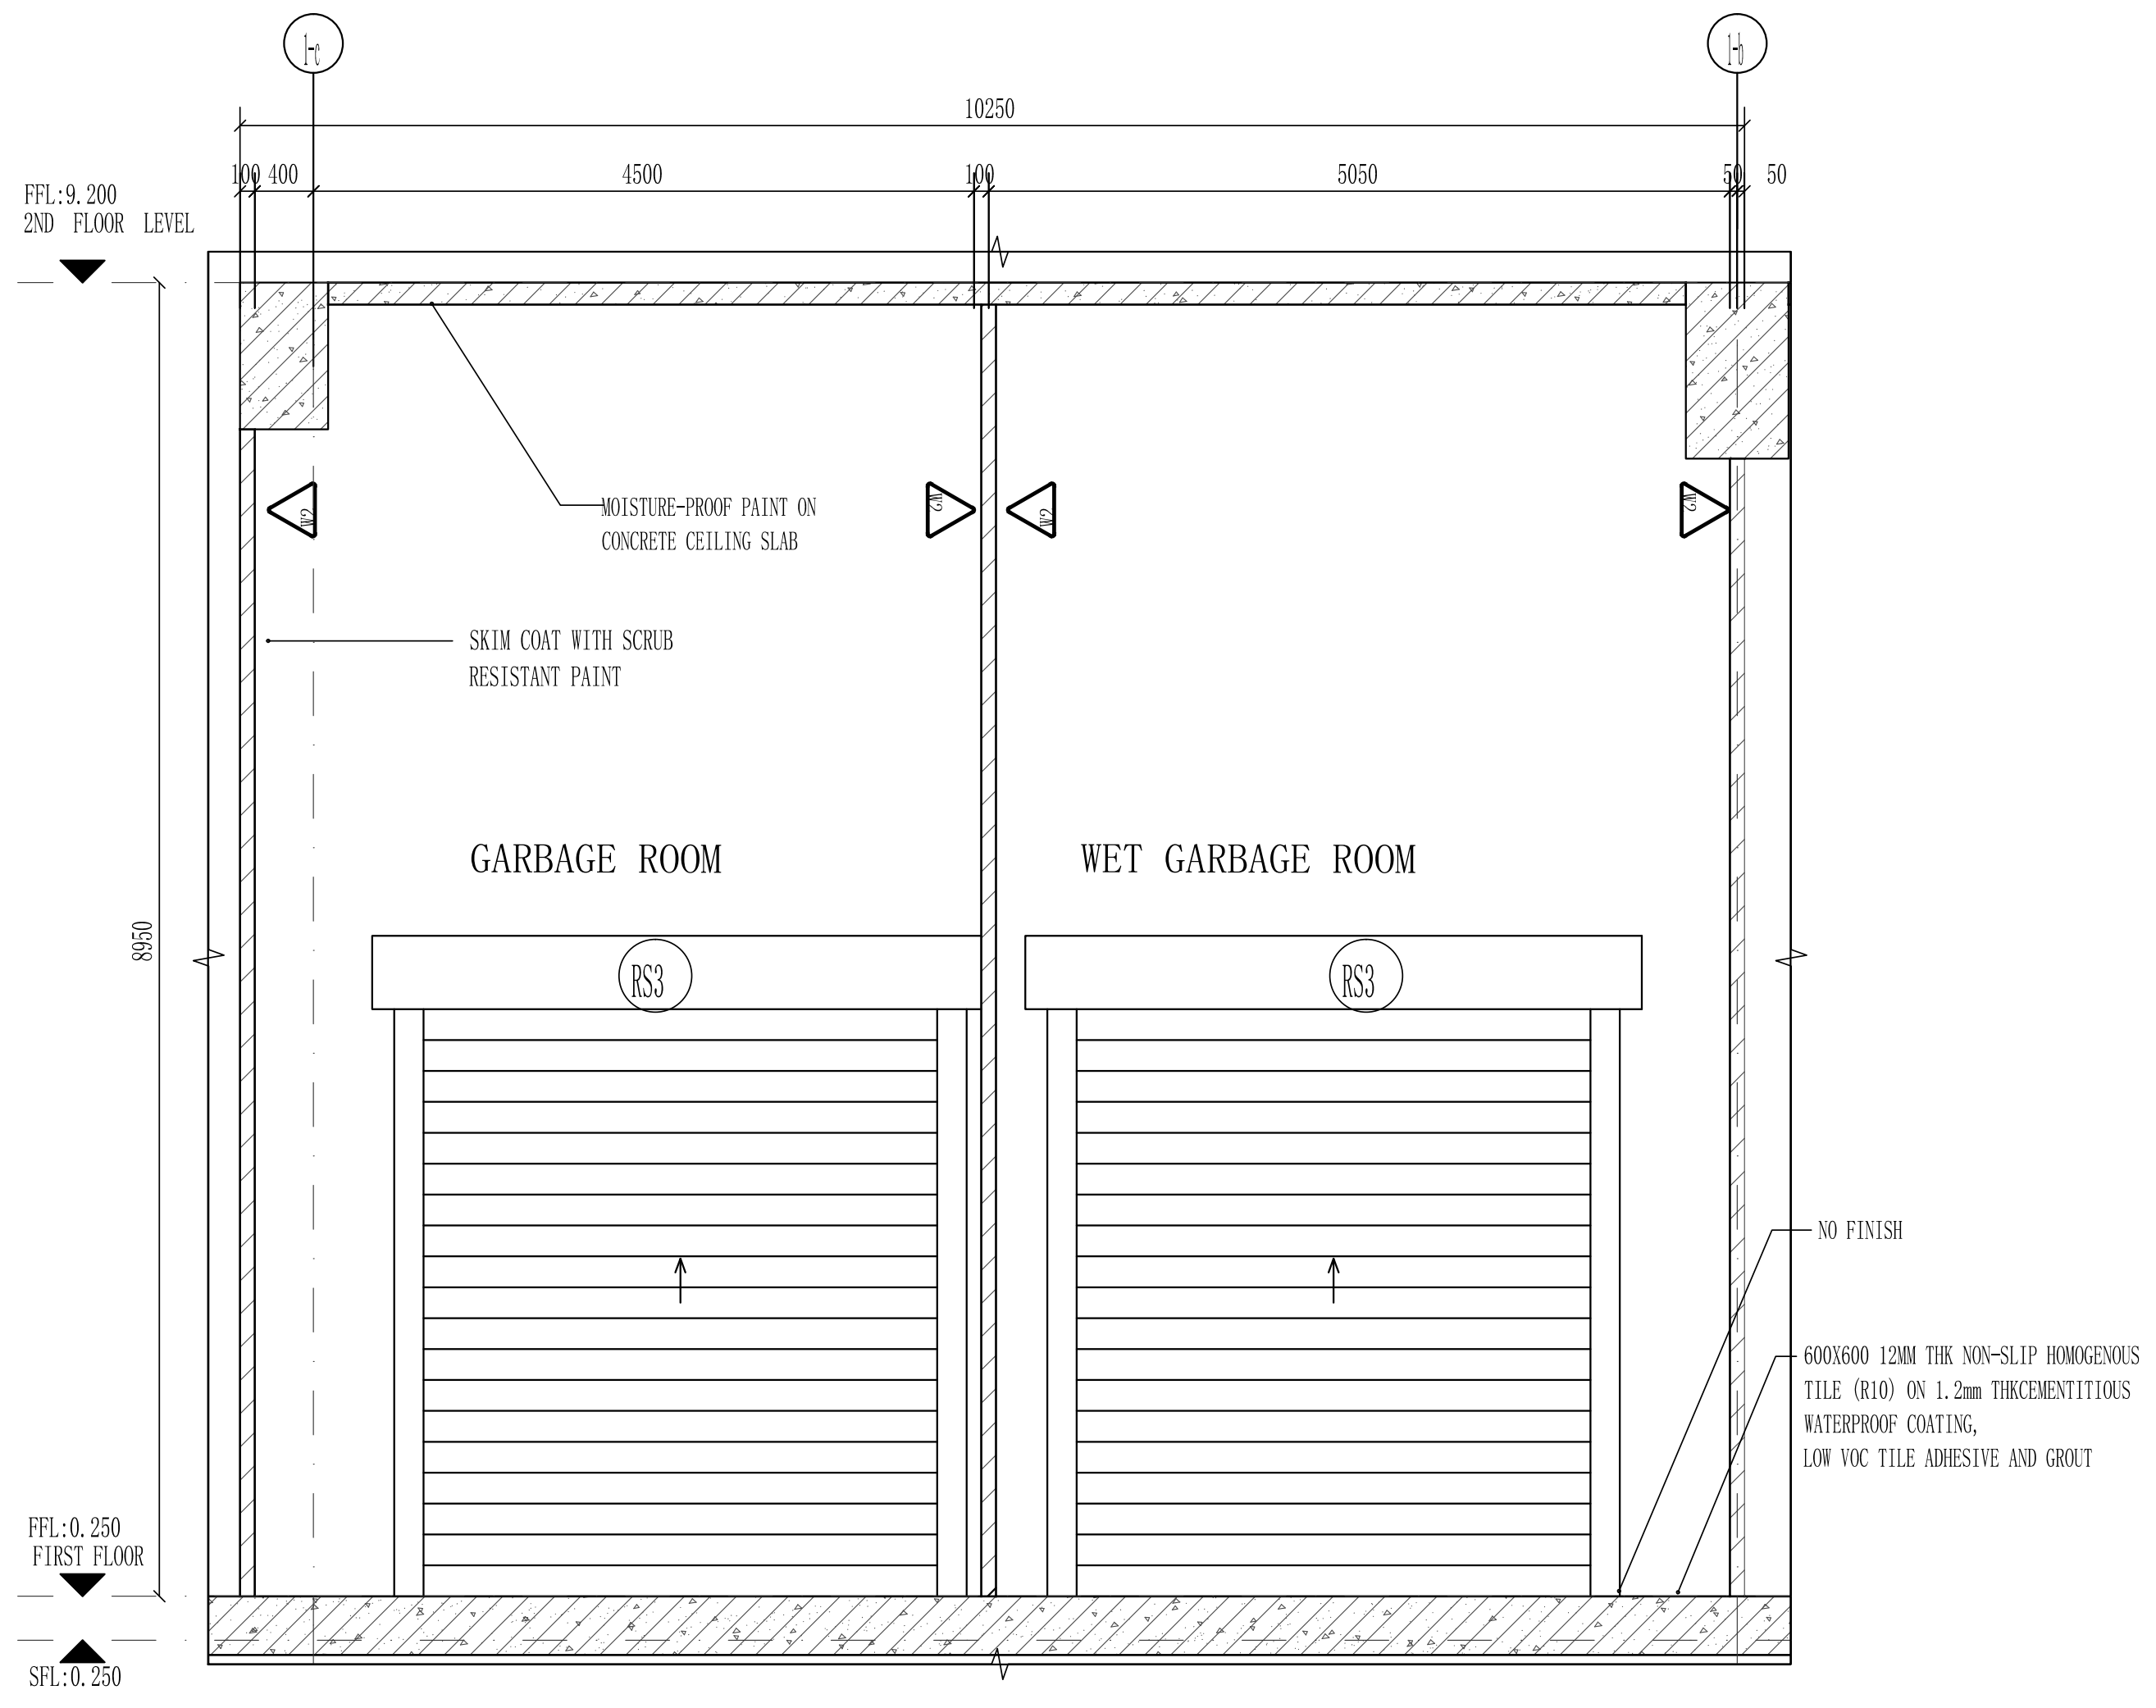
10250
100
400
4500
100
5050
50
50
FFL:9.200
2ND FLOOR LEVEL
MOISTURE-PROOF PAINT ON CONCRETE CEILING SLAB
SKIM COAT WITH SCRUB RESISTANT PAINT
W2
GARBAGE ROOM
WET GARBAGE ROOM
RS3
RS3
8950
NO FINISH
600X600 12MM THK NON-SLIP HOMOGENOUS TILE (R10) ON 1.2mm THKCEMENTITIOUS WATERPROOF COATING, LOW VOC TILE ADHESIVE AND GROUT
FFL:0.250
FIRST FLOOR
SFL:0.250

WET GARBAGE ROOM GARBAGE ROOM SECTION A-A

Scale 1:50

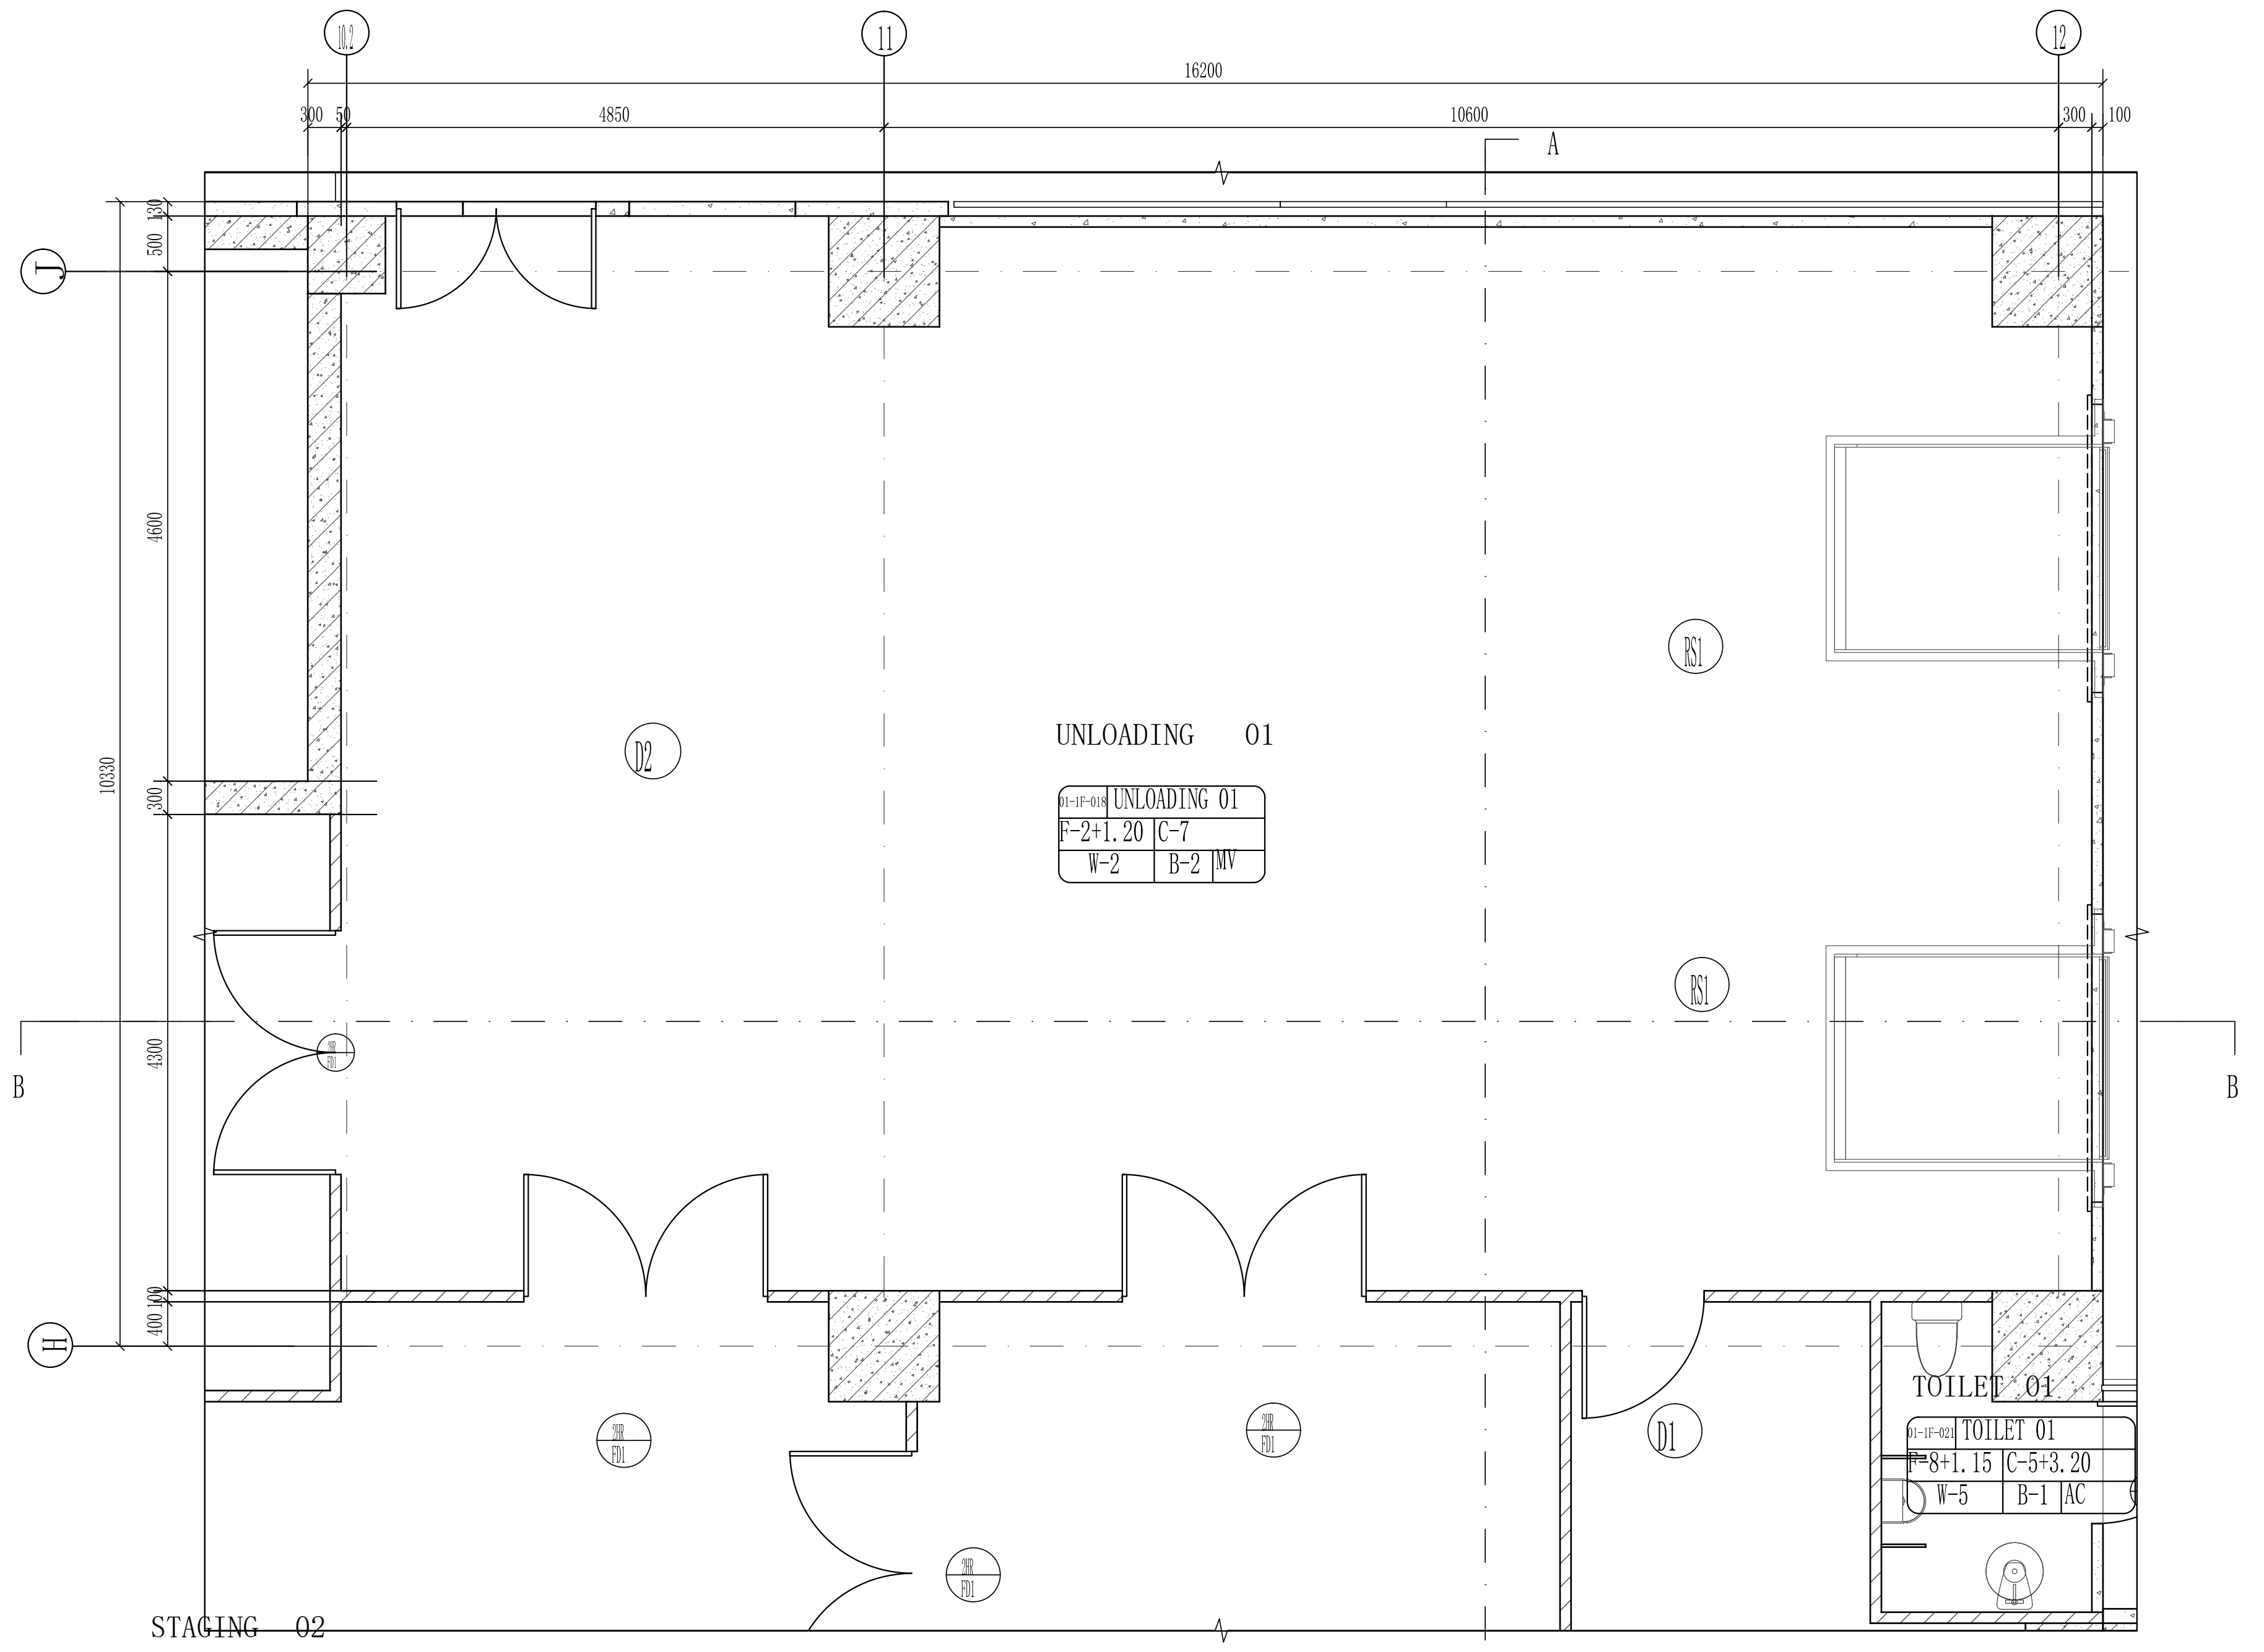
10.2
11
12
16200
300
50
4850
10600
300
100
A
J
H
500
4600
300
4300
400
100
10330
D2
UNLOADING 01
01-1F-018 UNLOADING 01
F-2+1.20
C-7
W-2
B-2
MV
RS1
RS1
B
B
FD1
D1
TOILET 01
01-1F-021 TOILET 01
F-8+1.15
C-5+3.20
W-5
B-1
AC
STAGING 02

UNLOADING 01 FIRST FLOOR PLAN

Scale 1:50

THE "SFL" MARKED IN THE DRAWING REFERS TO THE STRUCTURAL FLOOR LEVEL, WHILE THE FINISHED FLOOR LEVEL (FFL) IS DETERMINED BASED ON FLOOR FINISHES.

A

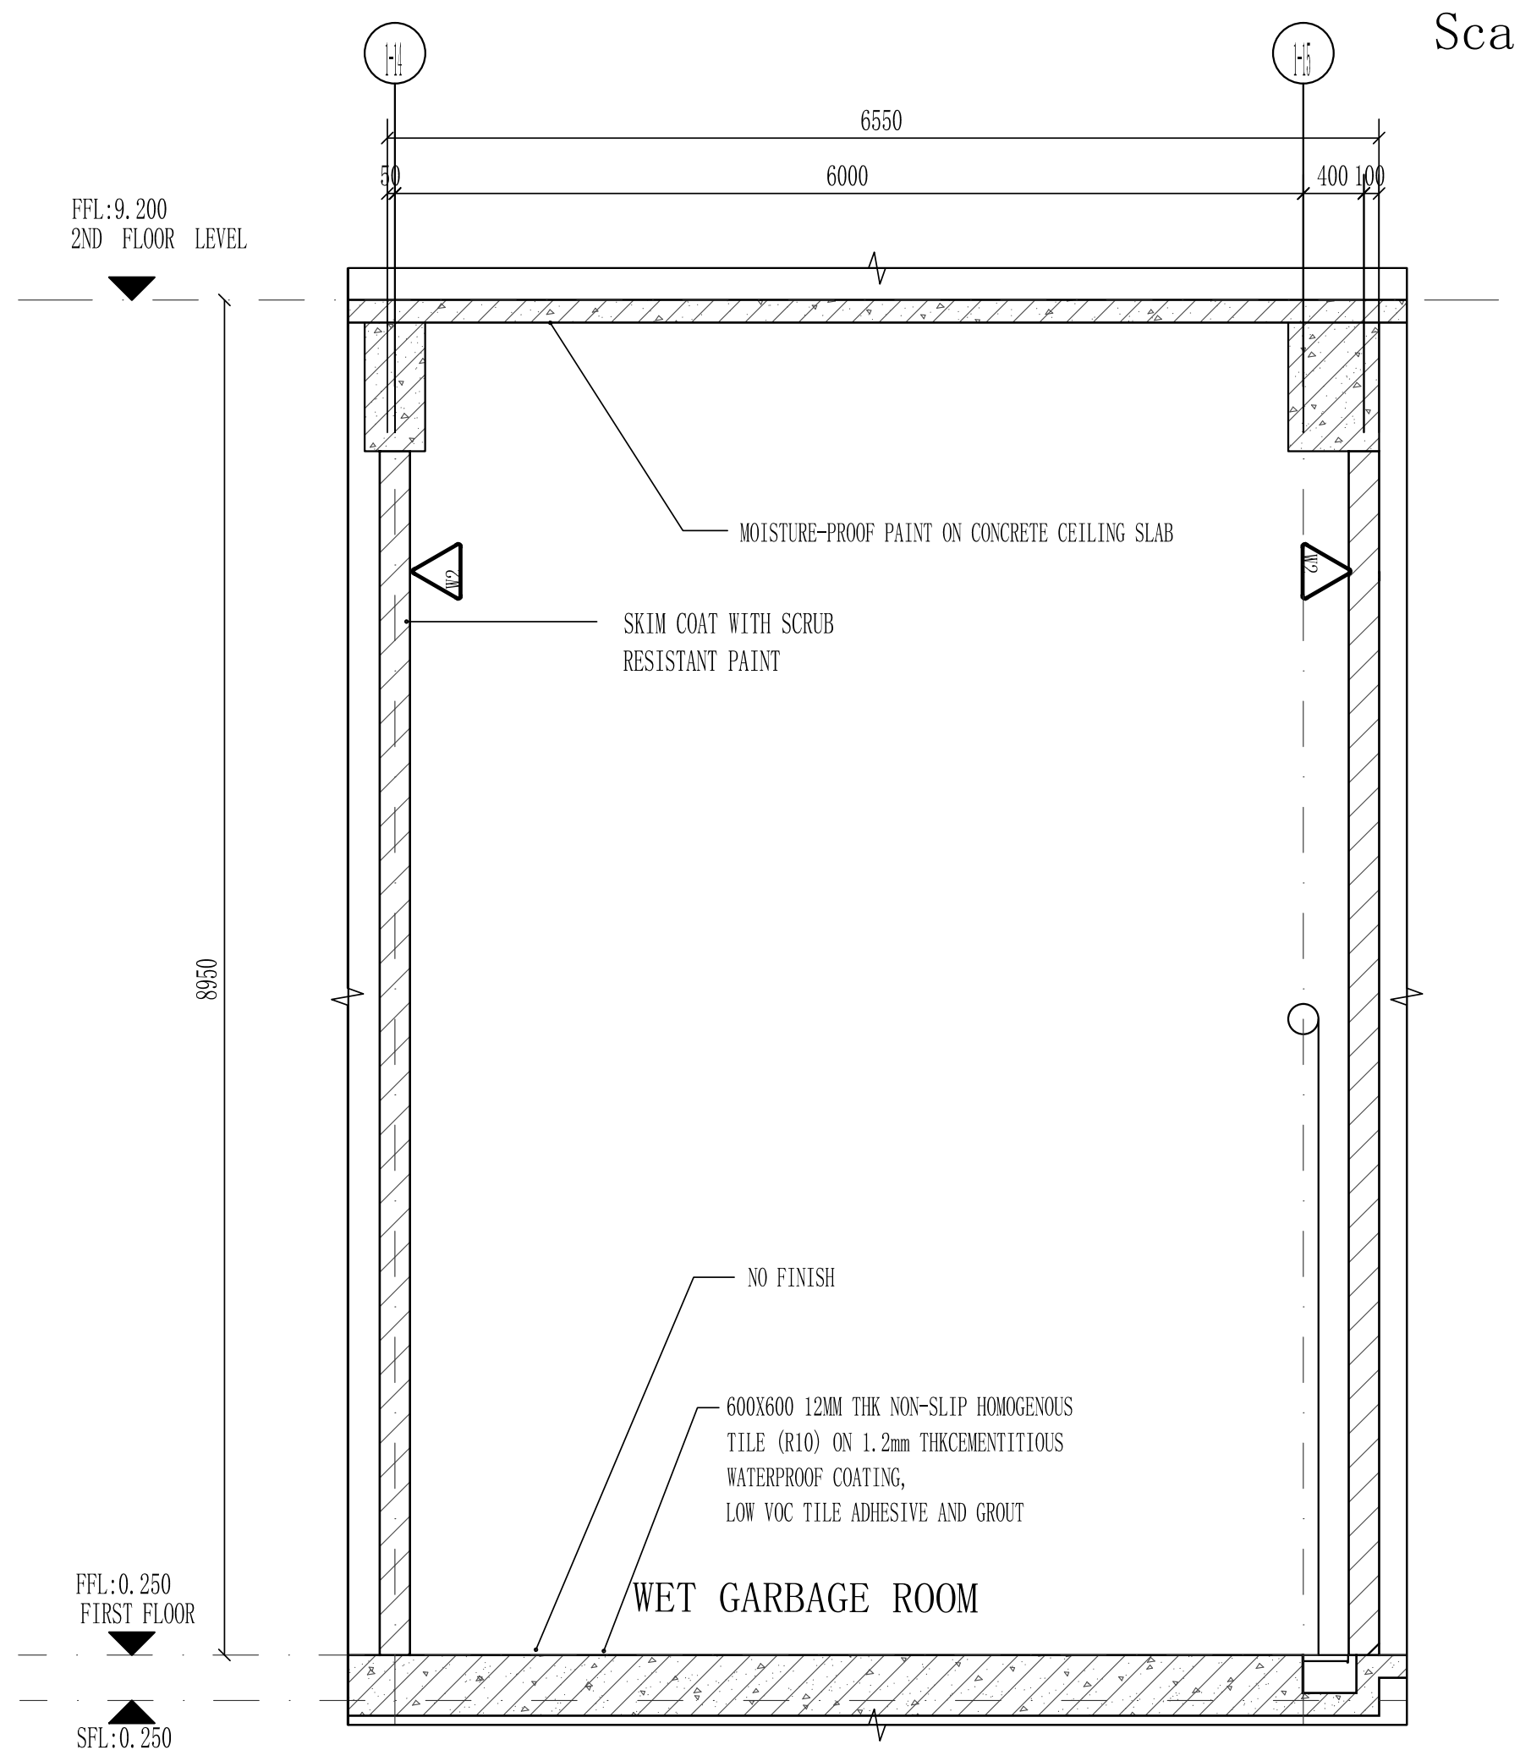
6550
50
6000
400
100
FFL:9.200
2ND FLOOR LEVEL
MOISTURE-PROOF PAINT ON CONCRETE CEILING SLAB
SKIM COAT WITH SCRUB RESISTANT PAINT
W2
8950
NO FINISH
600X600 12MM THK NON-SLIP HOMOGENOUS TILE (R10) ON 1.2mm THKCEMENTITIOUS WATERPROOF COATING, LOW VOC TILE ADHESIVE AND GROUT
WET GARBAGE ROOM
FFL:0.250
FIRST FLOOR
SFL:0.250

WET GARBAGE ROOMSECTION B-B

Scale 1:50

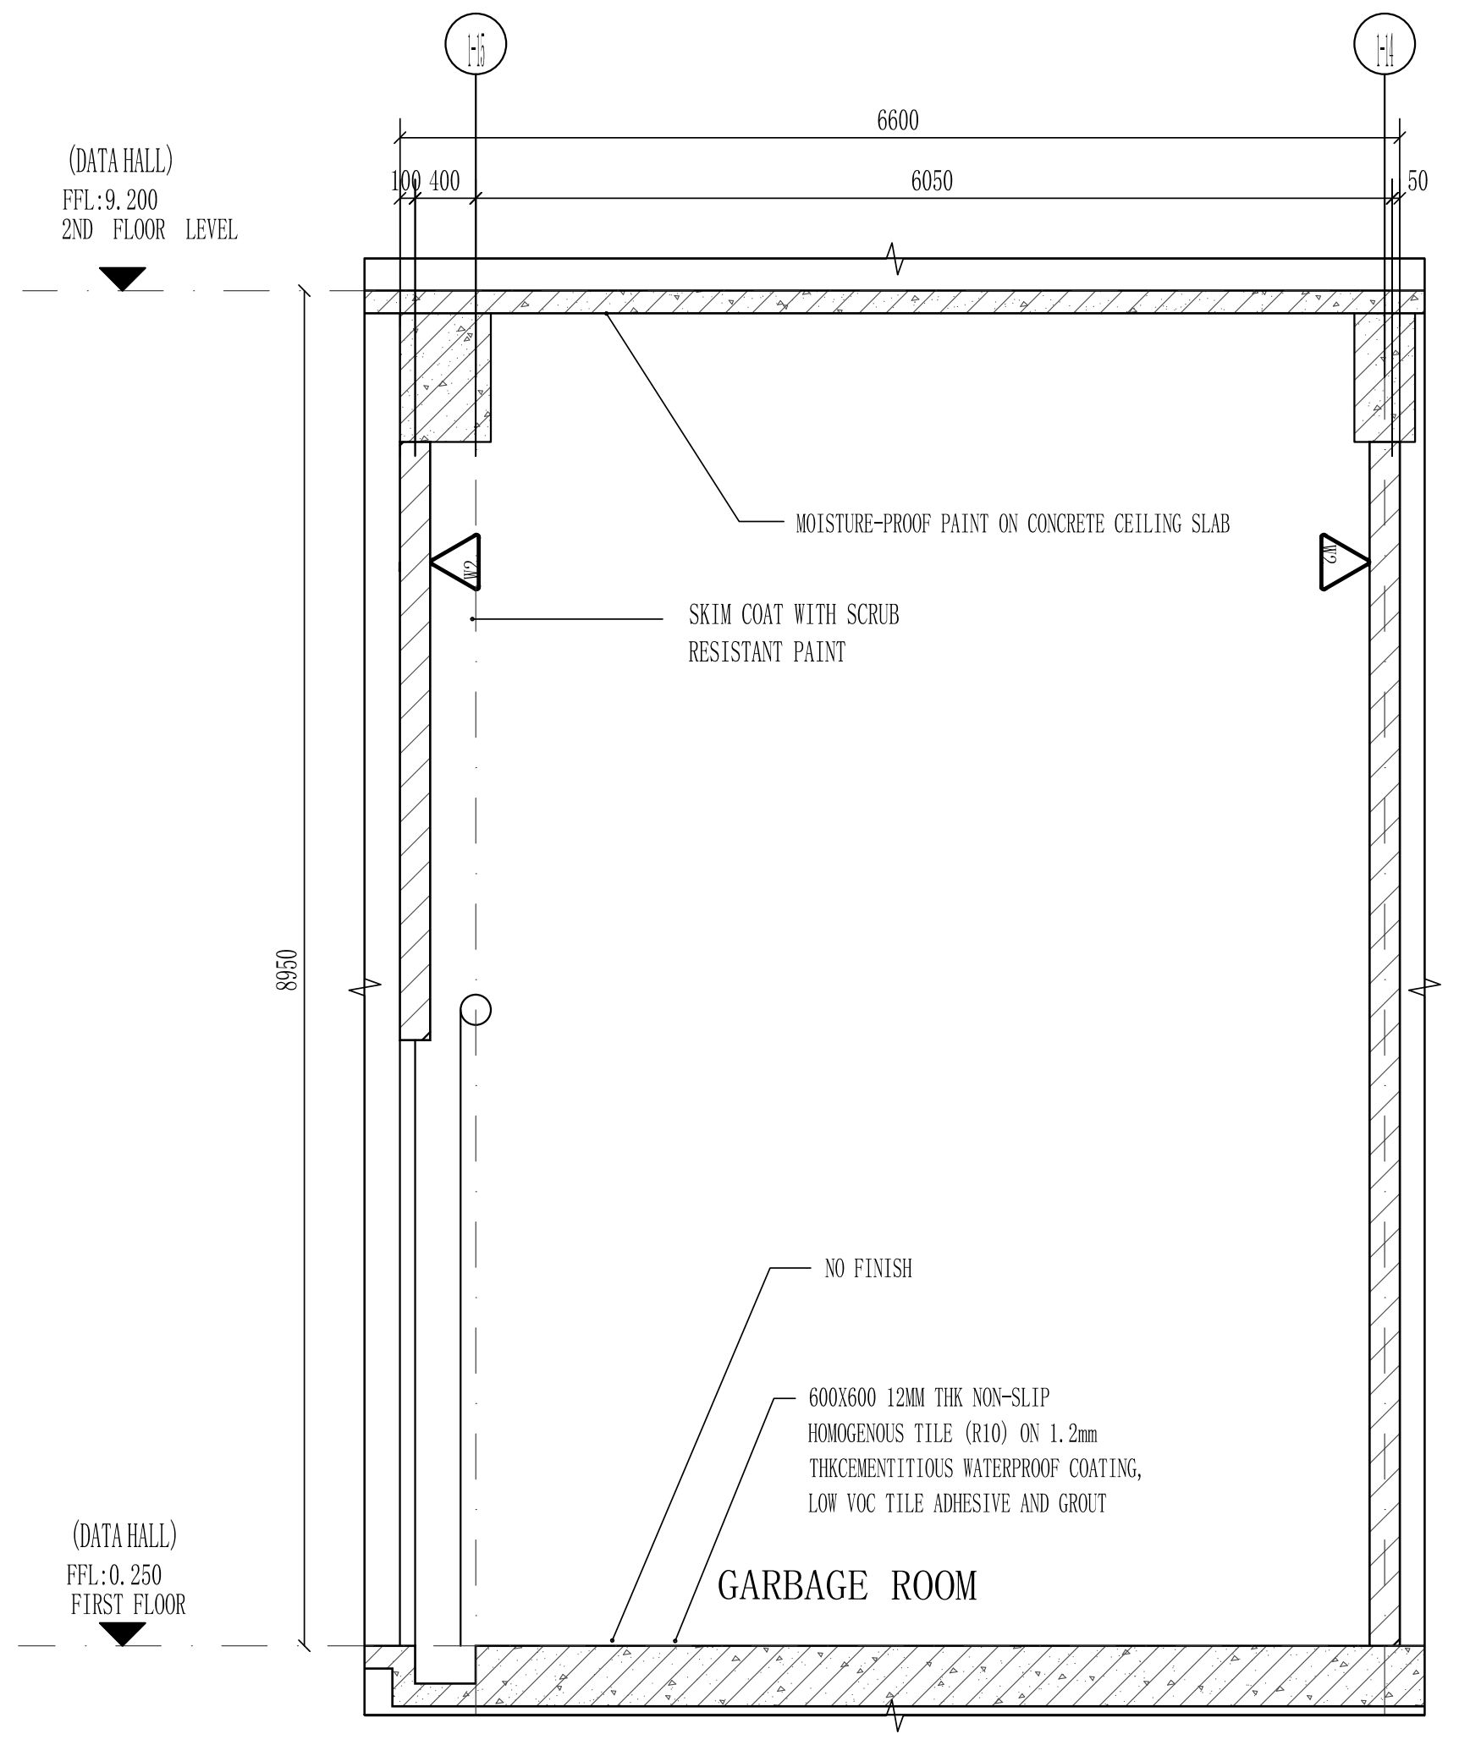
6600
100
400
6050
50
(DATA HALL)
FFL:9.200
2ND FLOOR LEVEL
MOISTURE-PROOF PAINT ON CONCRETE CEILING SLAB
SKIM COAT WITH SCRUB RESISTANT PAINT
W2
8950
NO FINISH
600X600 12MM THK NON-SLIP HOMOGENOUS TILE (R10) ON 1.2mm THKCEMENTITIOUS WATERPROOF COATING, LOW VOC TILE ADHESIVE AND GROUT
(DATA HALL)
FFL:0.250
FIRST FLOOR
GARBAGE ROOM

GARBAGE ROOM SECTION C-C

Scale 1:50

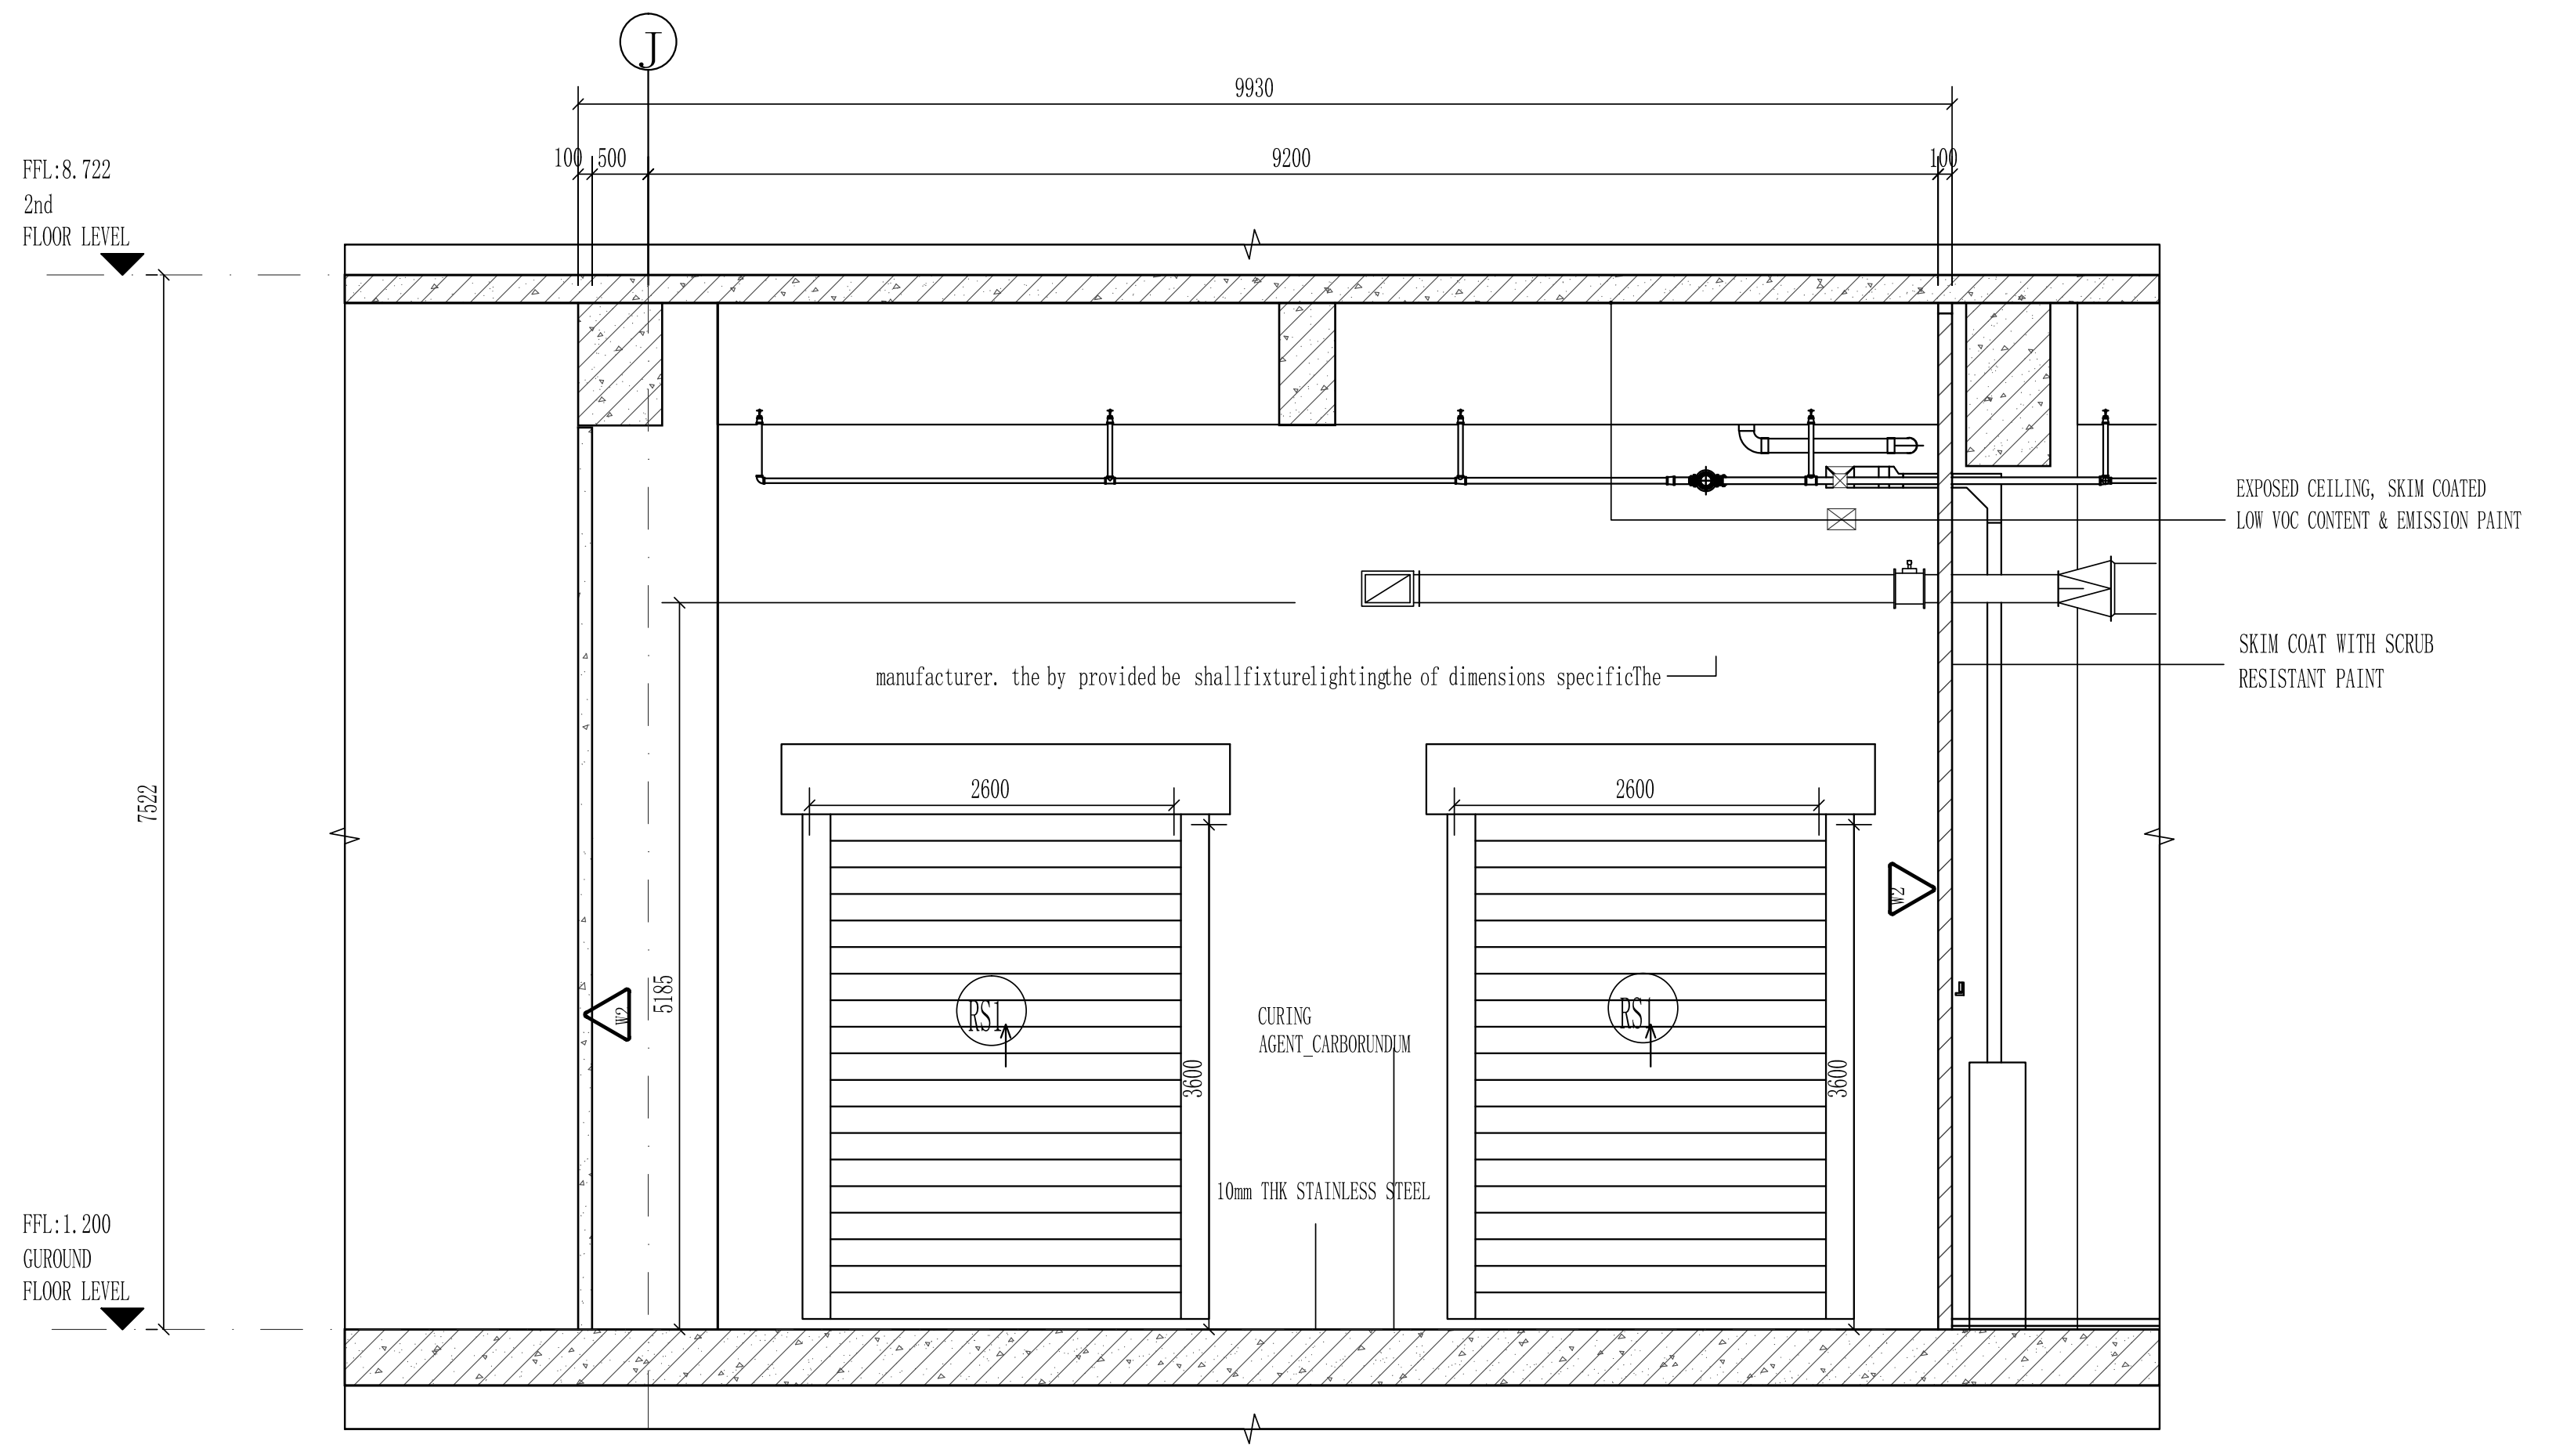
J
9930
100
500
9200
100
FFL:8.722
2nd
FLOOR LEVEL
EXPOSED CEILING, SKIM COATED LOW VOC CONTENT & EMISSION PAINT
SKIM COAT WITH SCRUB RESISTANT PAINT
manufacturer. the by provided be shallfixturelightingthe of dimensions specificThe
2600
2600
7522
5185
W2
RS1
RS1
3600
3600
CURING AGENT_CARBORUNDUM
10mm THK STAINLESS STEEL
FFL:1.200
GUROUND
FLOOR LEVEL

UNLOADING 01SECTION A-A

Scale 1:50

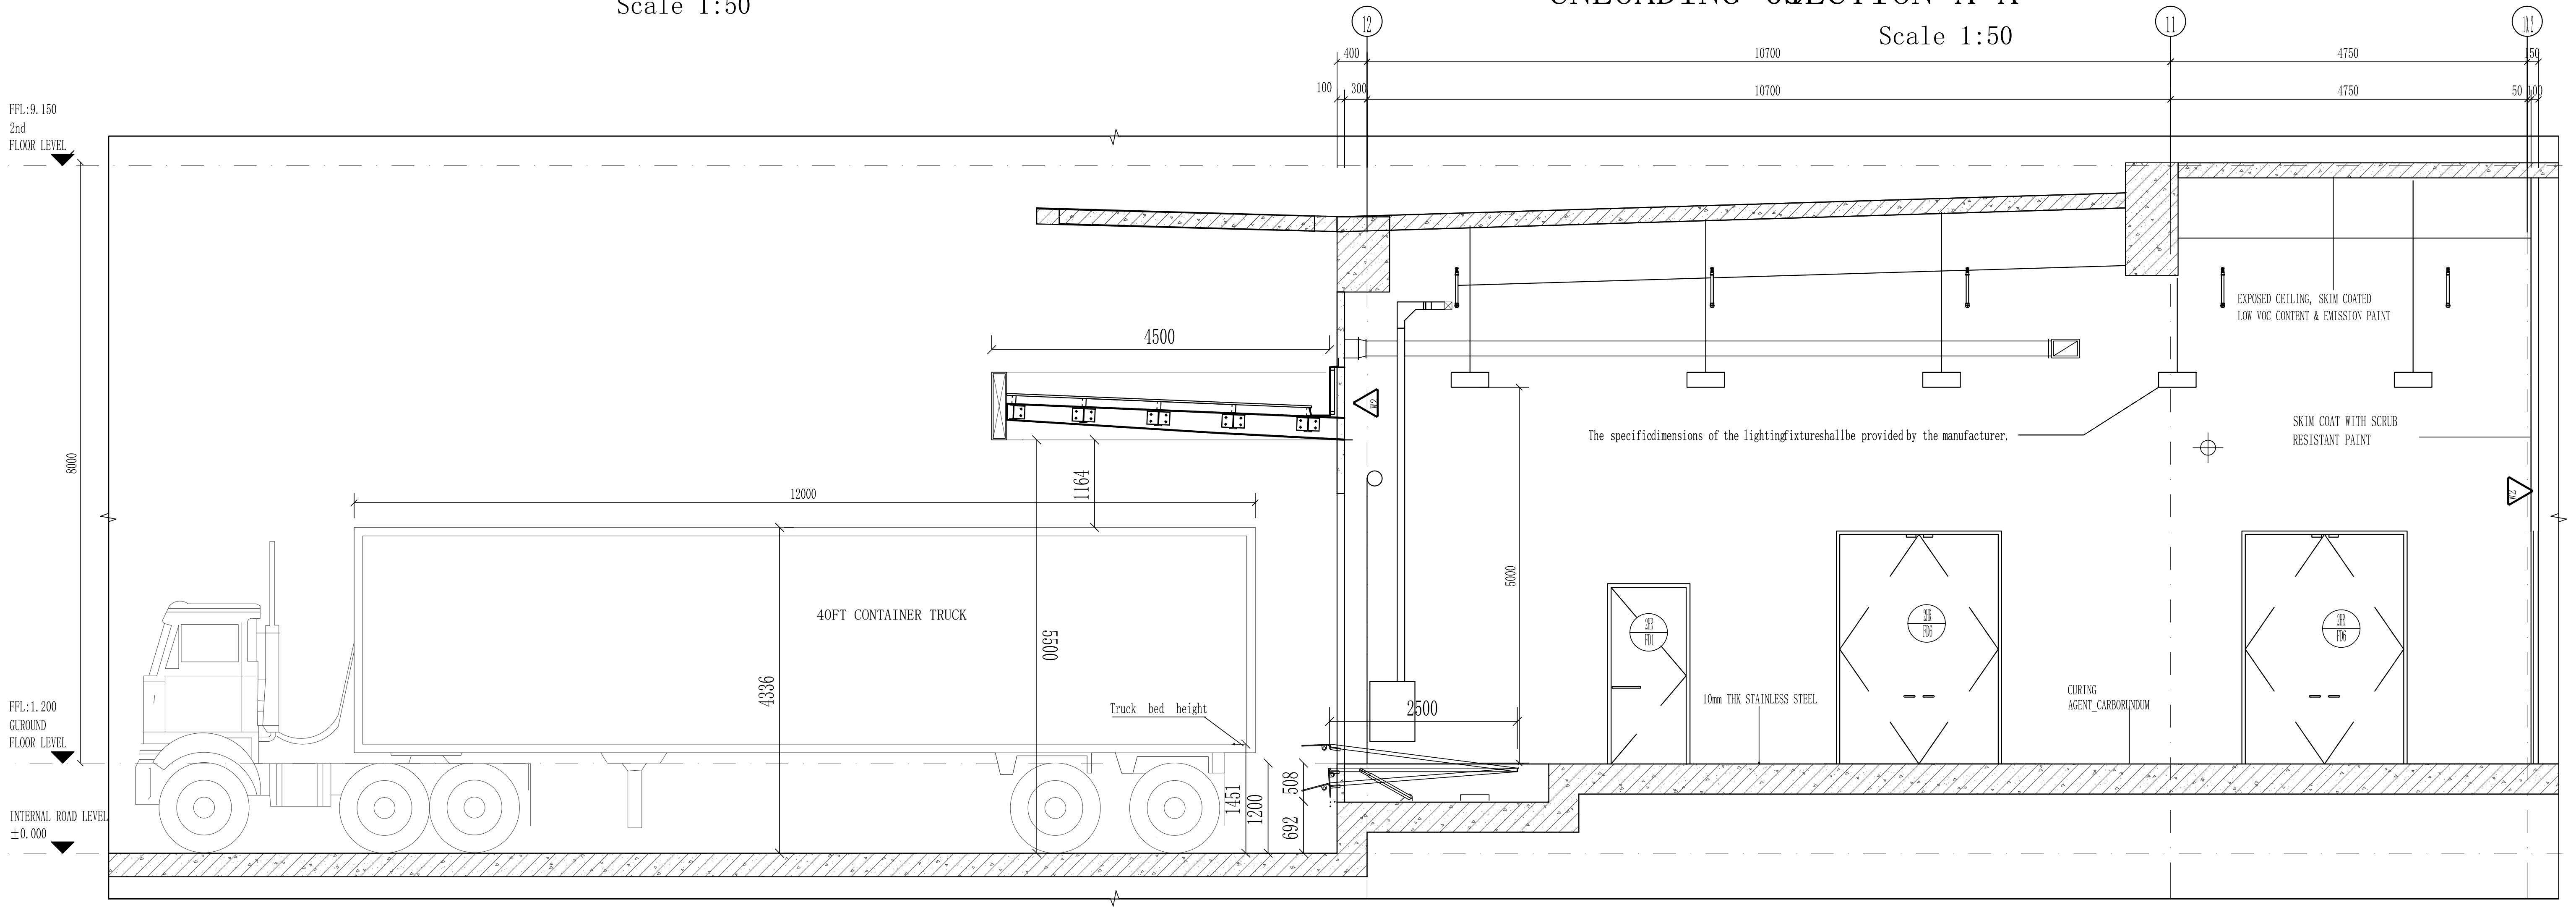
12
11
10.2
400
10700
4750
50
100
300
10700
4750
50
100
FFL:9.150
2nd
FLOOR LEVEL
4500
EXPOSED CEILING, SKIM COATED LOW VOC CONTENT & EMISSION PAINT
The specificdimensions of the lightingfixtureshallbe provided by the manufacturer.
SKIM COAT WITH SCRUB RESISTANT PAINT
8000
1164
12000
40FT CONTAINER TRUCK
5500
4336
5000
2500
Truck bed height
10mm THK STAINLESS STEEL
CURING AGENT_CARBORUNDUM
FFL:1.200
GUROUND
FLOOR LEVEL
INTERNAL ROAD LEVEL
±0.000
1451
1200
508
692

UNLOADING 01SECTION B-B

Scale 1:50

CLIENT :

GULF EDGE DC 01

87 Wireless Road, M Thai Tower 11th. Floor, All Seasons Place, Lumpini,
Pathumwan, Bangkok 10330, Thailand

CONTRACTOR :

华西发展(泰国)有限公司
บริษัท หัวซือ ดีเวลลอปเม้นต์ (ประเทศไทย) จำกัด
HUASHI DEVELOPMENT CO.,LTD
No. 202, Room No. 1403, 14/F, Le Concorde Building,
Ratchadapisek Road, Huaykhwang Sub-District,
Huaykhwang District, Bangkok Metropolitan 10310.

CONSULTANT :

ARbay
บริษัท เอ อาร์ เบย์ จำกัด
ARbay Company Limited
31 st Floor Bangkok Insurance Building
25 South Sathorn road Thungmahamek
Sathorn Bangkok 10120 THAILAND
T +66 (0) 2286 8199
F +66 (0) 2286 2863
info@arbay.co.th

CONSULTANT :

Qbic Engineers & Architects Co.,Ltd.
8 Soi KALONG 4 SANAMBINNAM ROAD,
THASAI SUB-DISTRICT, MUANG NONTHABURI DISTRICT
, NONTHABURI.
Tel 662-950-4374
Fax 662-580-3231
E-Mail : qbic@qbic.co.th, www.qbic.co.th
QBIC ENGINEERS AND ARCHITECTS CO.,LTD.

CONSULTANT :

MITR
MITR TECHNICAL CONSULTANT CO.,LTD.
1168/8 12th FLOOR, LUMPINI TOWER BUILDING,
RAMA IV RD., THUNGMAHAMEK, SATHORN, BANGKOK 10120, THAILAND
TEL : 0-2679-9079-84
FAX : 0-2679-9085 E-mail: mitr_dd@mitr.com

Architect : SIGNATURE
ประกิต พนานุรัตน์ วสถ. 580
ที่อยู่
251/1 ถ.จารุเมือง แขวงรองเมือง เขตปทุมวัน
กรุงเทพมหานคร โทรศัพท์ 02-286-8199

Structural Engineer : SIGNATURE
วิศวกรผู้ออกแบบโครงสร้าง
ณัฐสม สงวนวงษ์ วย 1423
ที่อยู่
2/1 ซ.รามคำแหง 150 ถ.รามคำแหง
แขวง สะพานสูง เขต สะพานสูง กทม. 10240

Structural Inspector : SIGNATURE
วิศวกรผู้ตรวจสอบโครงสร้าง
โกมล จุฑาภัทร วย 964
ที่อยู่
24/18 ซ.นวมินทร์ 129 ถ. นวมินทร์
แขวง นวลจันทร์ เขต บึงกุ่ม กทม. 10230

Electrical Engineer : SIGNATURE
วิศวกรผู้ออกแบบระบบไฟฟ้ากำลัง
นายสุภัทร บูรณวิทย์ วฟก.1265
ที่อยู่
21 ซอยทานสัมฤทธิ์ 13
ตำบลท่าทราย อ.เมืองนนทบุรี จ.นนทบุรี 11000

Mechanical Engineer : SIGNATURE
วิศวกรผู้ออกแบบระบบเครื่องกลและปรับอากาศ
นายประสิทธิ์ เกียวสุนทร วก.1221
ที่อยู่
44/372 ซอยบางกระดี่ 35/1 แขวงแสมดำ
เขตบางขุนเทียน กทม. 10150
ประสิทธิ์

Sanitary Engineer : SIGNATURE
วิศวกรผู้ออกแบบระบบสุขาภิบาล และดับเพลิง
นายทศวรรษ สันนฤทธิ์ วส. 215
ที่อยู่
บ้านเลขที่ 99/107 หมู่ที่ 3 ต.ศีรษะจรเข้น้อย
อ.บางเสาธง จ.สมุทรปราการ 10540
ทศวรรษ

ISSUE/REVISION

REV.	DESCRIPTION	DATE
A	90% DEVELOPED	09/05/2026

PROJECT NAME :
GEDC 01

LOCATION:
Nikhom Phattana district, Rayong ,industrial estate,CPGC

BUILDING :
MAIN BUILDING

90% DEVELOPED

TITLE :
ROOM DETAIL-1F-UNLOADING01 、WET GARBAGE ROOM 、GARBAGE ROOM

JOB NO.	SCALE 1 : 50
DRAWN ZYY	REF.
CHECKED LJC	DWG.NO. MPK01A-90-A-RD-109
APPROVED LXD	
DATE 2026.05.09	

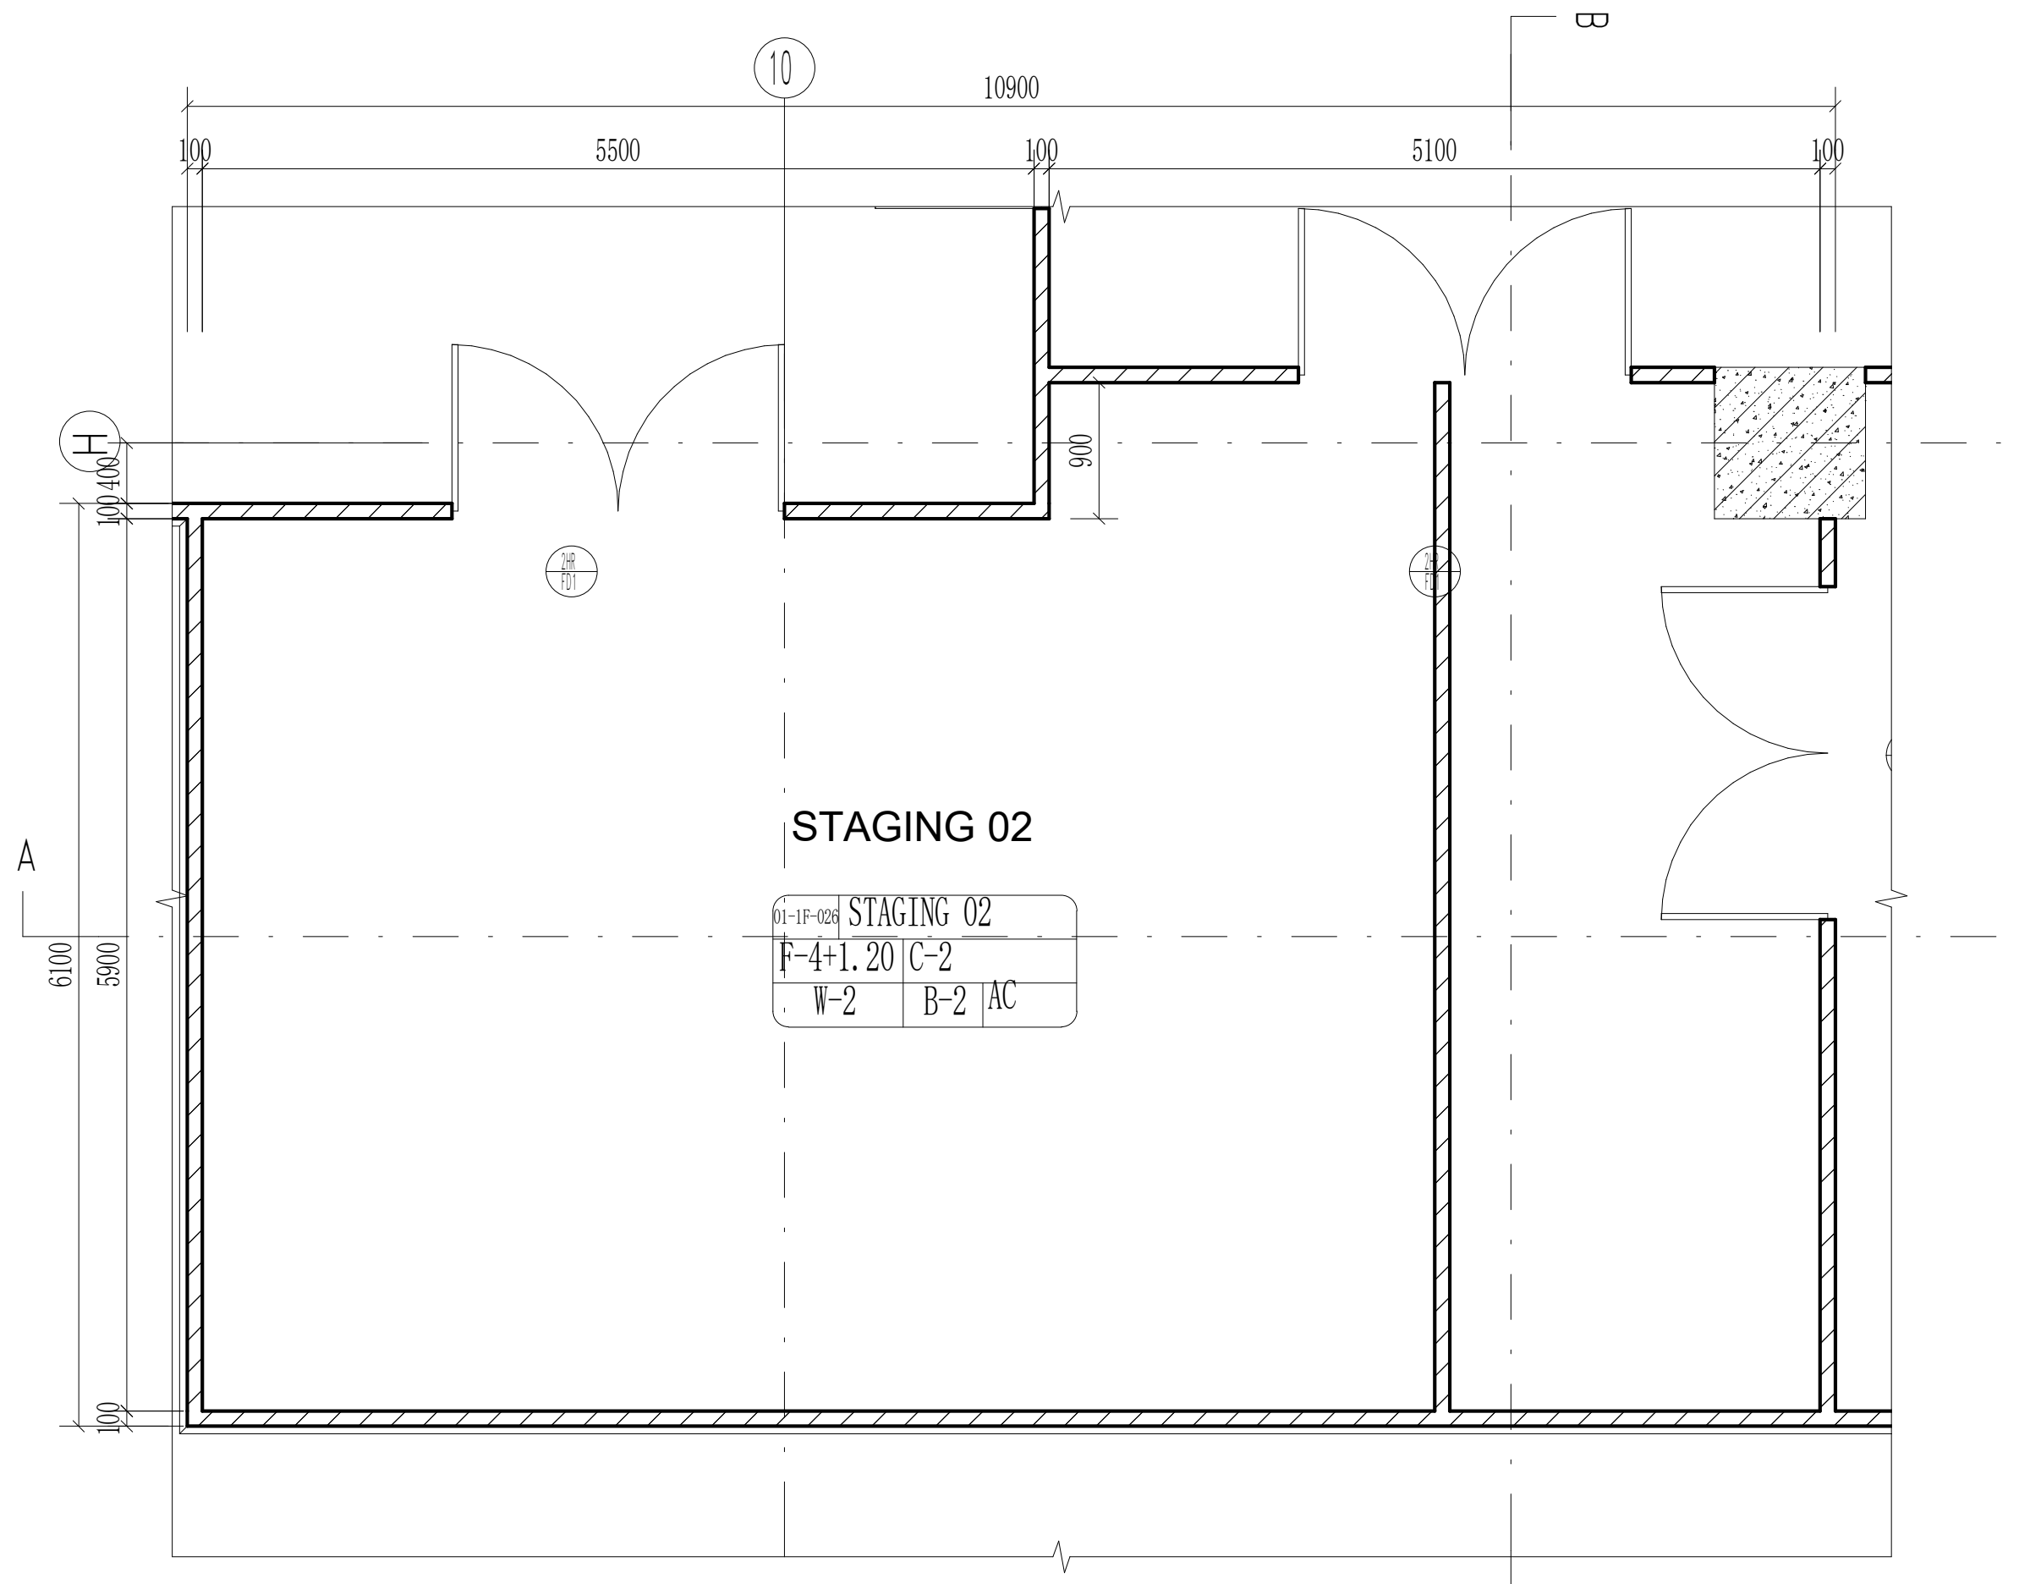
10
10900
100
5500
100
5100
100
H
100 400
900
A
6100
5900
100
B
STAGING 02
01-1F-026 STAGING 02
F-4+1.20 C-2
W-2 B-2 AC
2HR FD1

STAGING 02 FIRST FLOOR PLAN

Scale 1:50

THE "SFL" MARKED IN THE DRAWING REFERS TO THE STRUCTURAL FLOOR LEVEL, WHILE THE FINISHED FLOOR LEVEL (FFL) IS DETERMINED BASED ON FLOOR FINISHES.

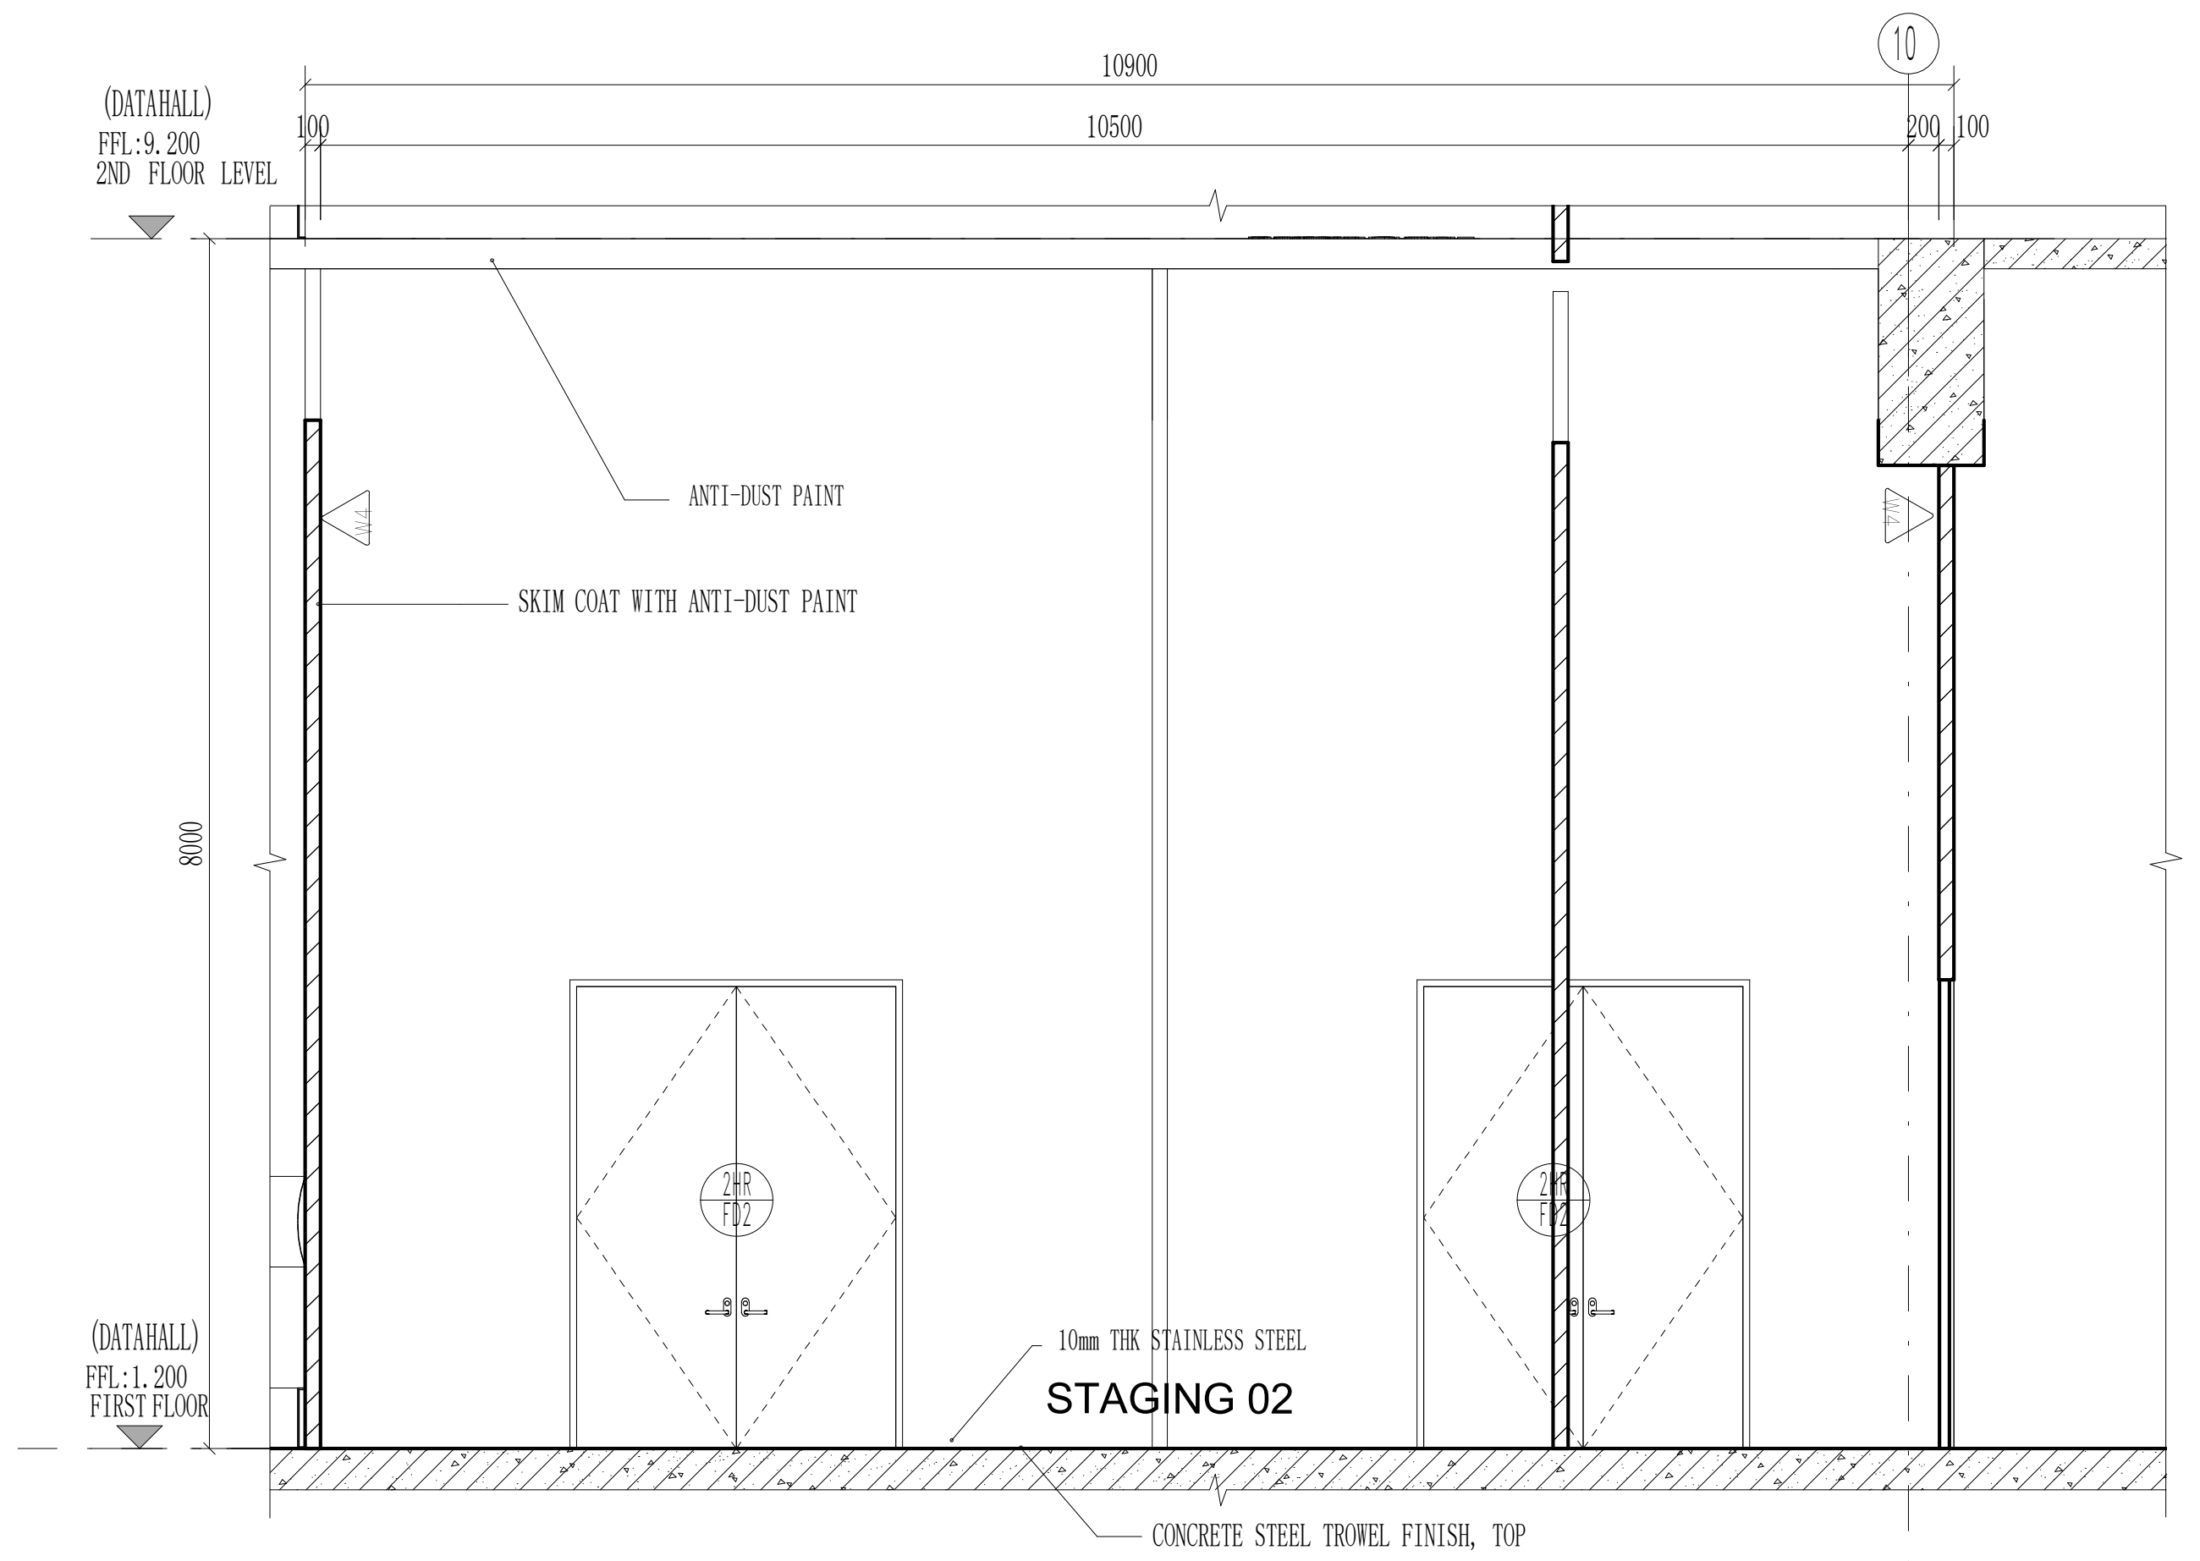
(DATAHALL)
FFL:9.200
2ND FLOOR LEVEL
10
10900
100
10500
200
100
8000
ANTI-DUST PAINT
SKIM COAT WITH ANTI-DUST PAINT
W4
2HR FD2
10mm THK STAINLESS STEEL
STAGING 02
(DATAHALL)
FFL:1.200
FIRST FLOOR
CONCRETE STEEL TROWEL FINISH, TOP PAINT WITH LOW VOC,EPOXY COATING; LOW VOC CONTENT & EMISSION PRIMER FOR EPOXY COATING

STAGING 02 SECTION A-A

Scale 1:50

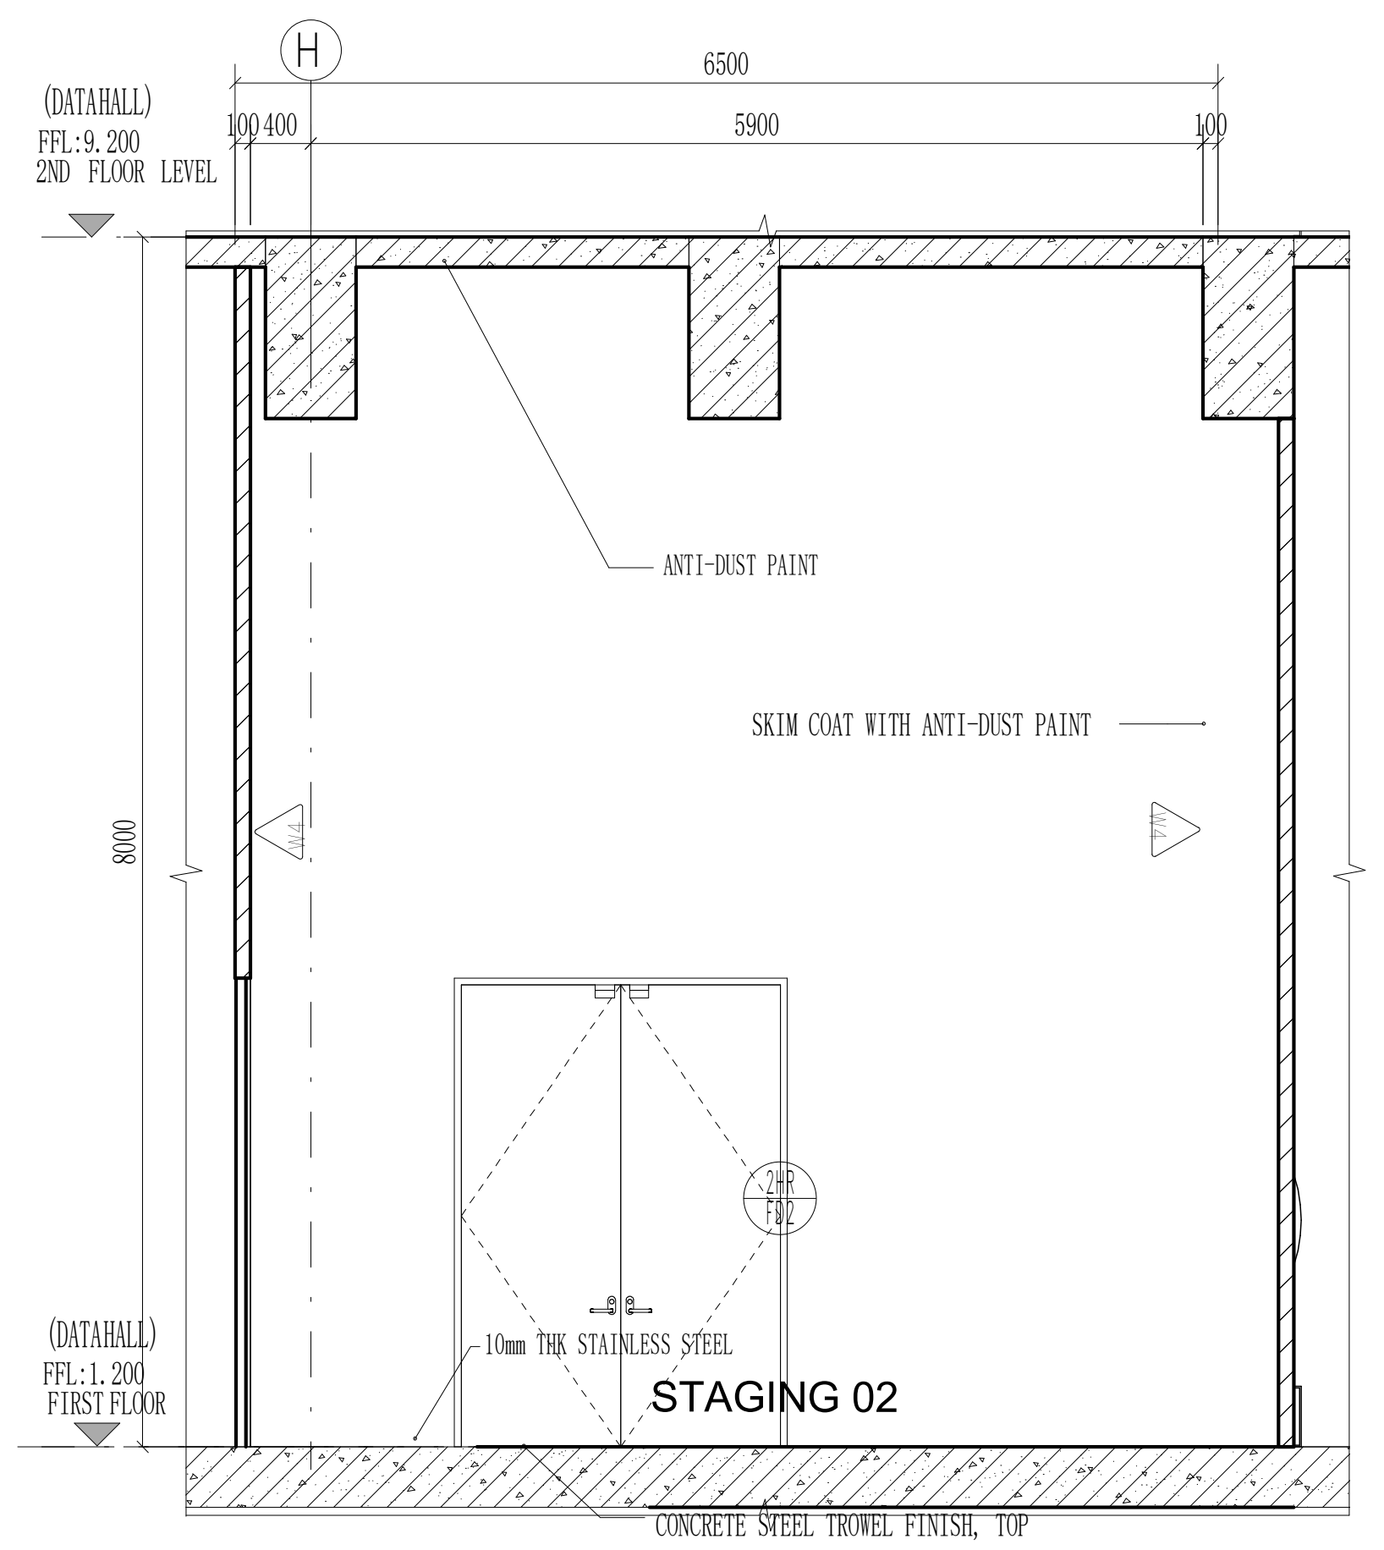
H
(DATAHALL)
FFL:9.200
2ND FLOOR LEVEL
6500
100 400
5900
100
8000
ANTI-DUST PAINT
SKIM COAT WITH ANTI-DUST PAINT
W4
2HR FD2
10mm THK STAINLESS STEEL
STAGING 02
(DATAHALL)
FFL:1.200
FIRST FLOOR
CONCRETE STEEL TROWEL FINISH, TOP PAINT WITH LOW VOC,EPOXY COATING; LOW VOC CONTENT & EMISSION PRIMER FOR EPOXY COATING

STAGING 02 SECTION B-B

Scale 1:50

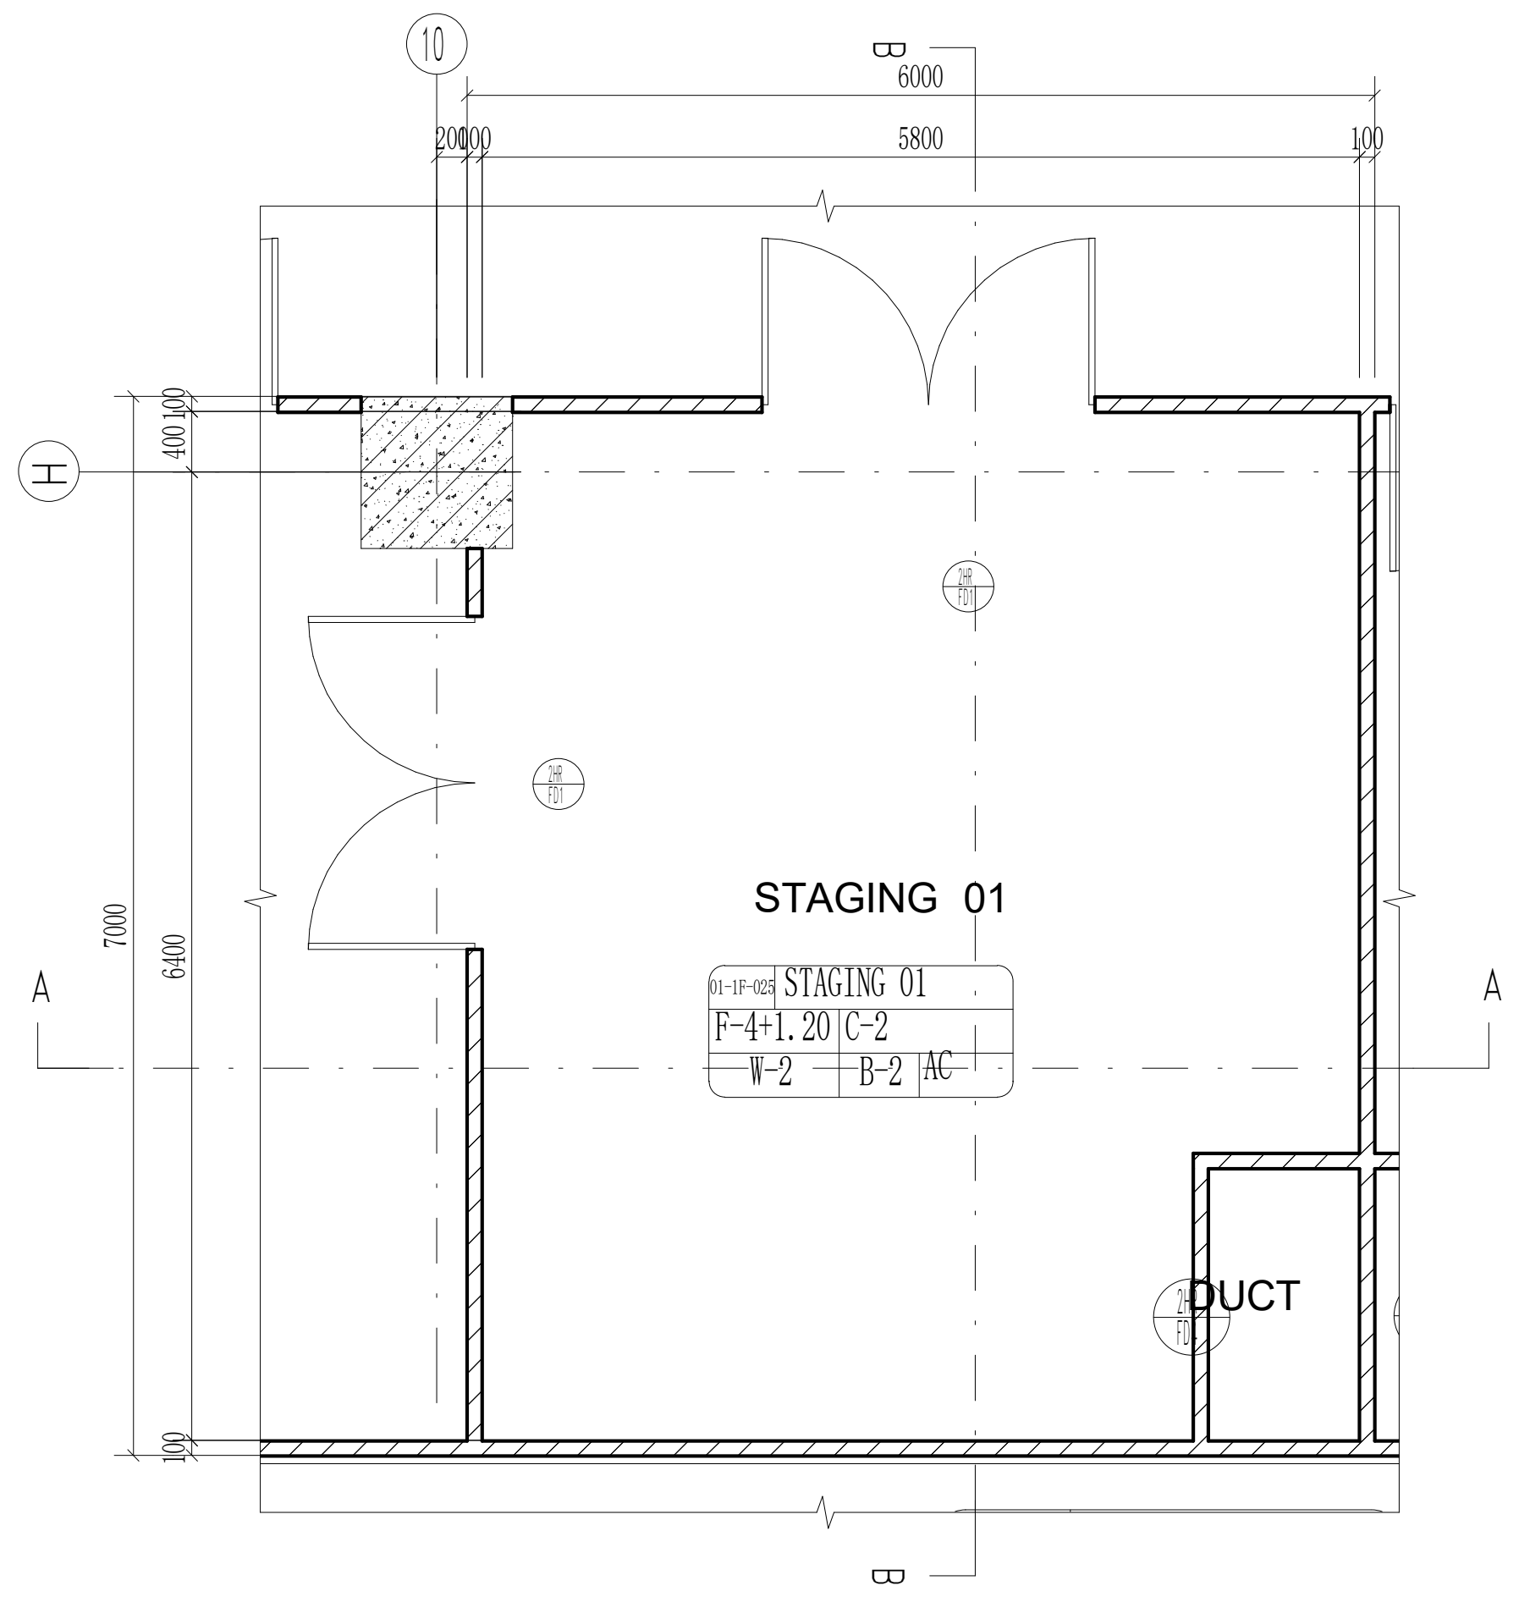
10
B
6000
200 100
5800
100
H
400 100
7000
6400
100
A
STAGING 01
01-1F-025 STAGING 01
F-4+1.20 C-2
W-2 B-2 AC
2HR FD1
DUCT

STAGING 01 FLOOR PLAN

Scale 1:50

THE "SFL" MARKED IN THE DRAWING REFERS TO THE STRUCTURAL FLOOR LEVEL, WHILE THE FINISHED FLOOR LEVEL (FFL) IS DETERMINED BASED ON FLOOR FINISHES.

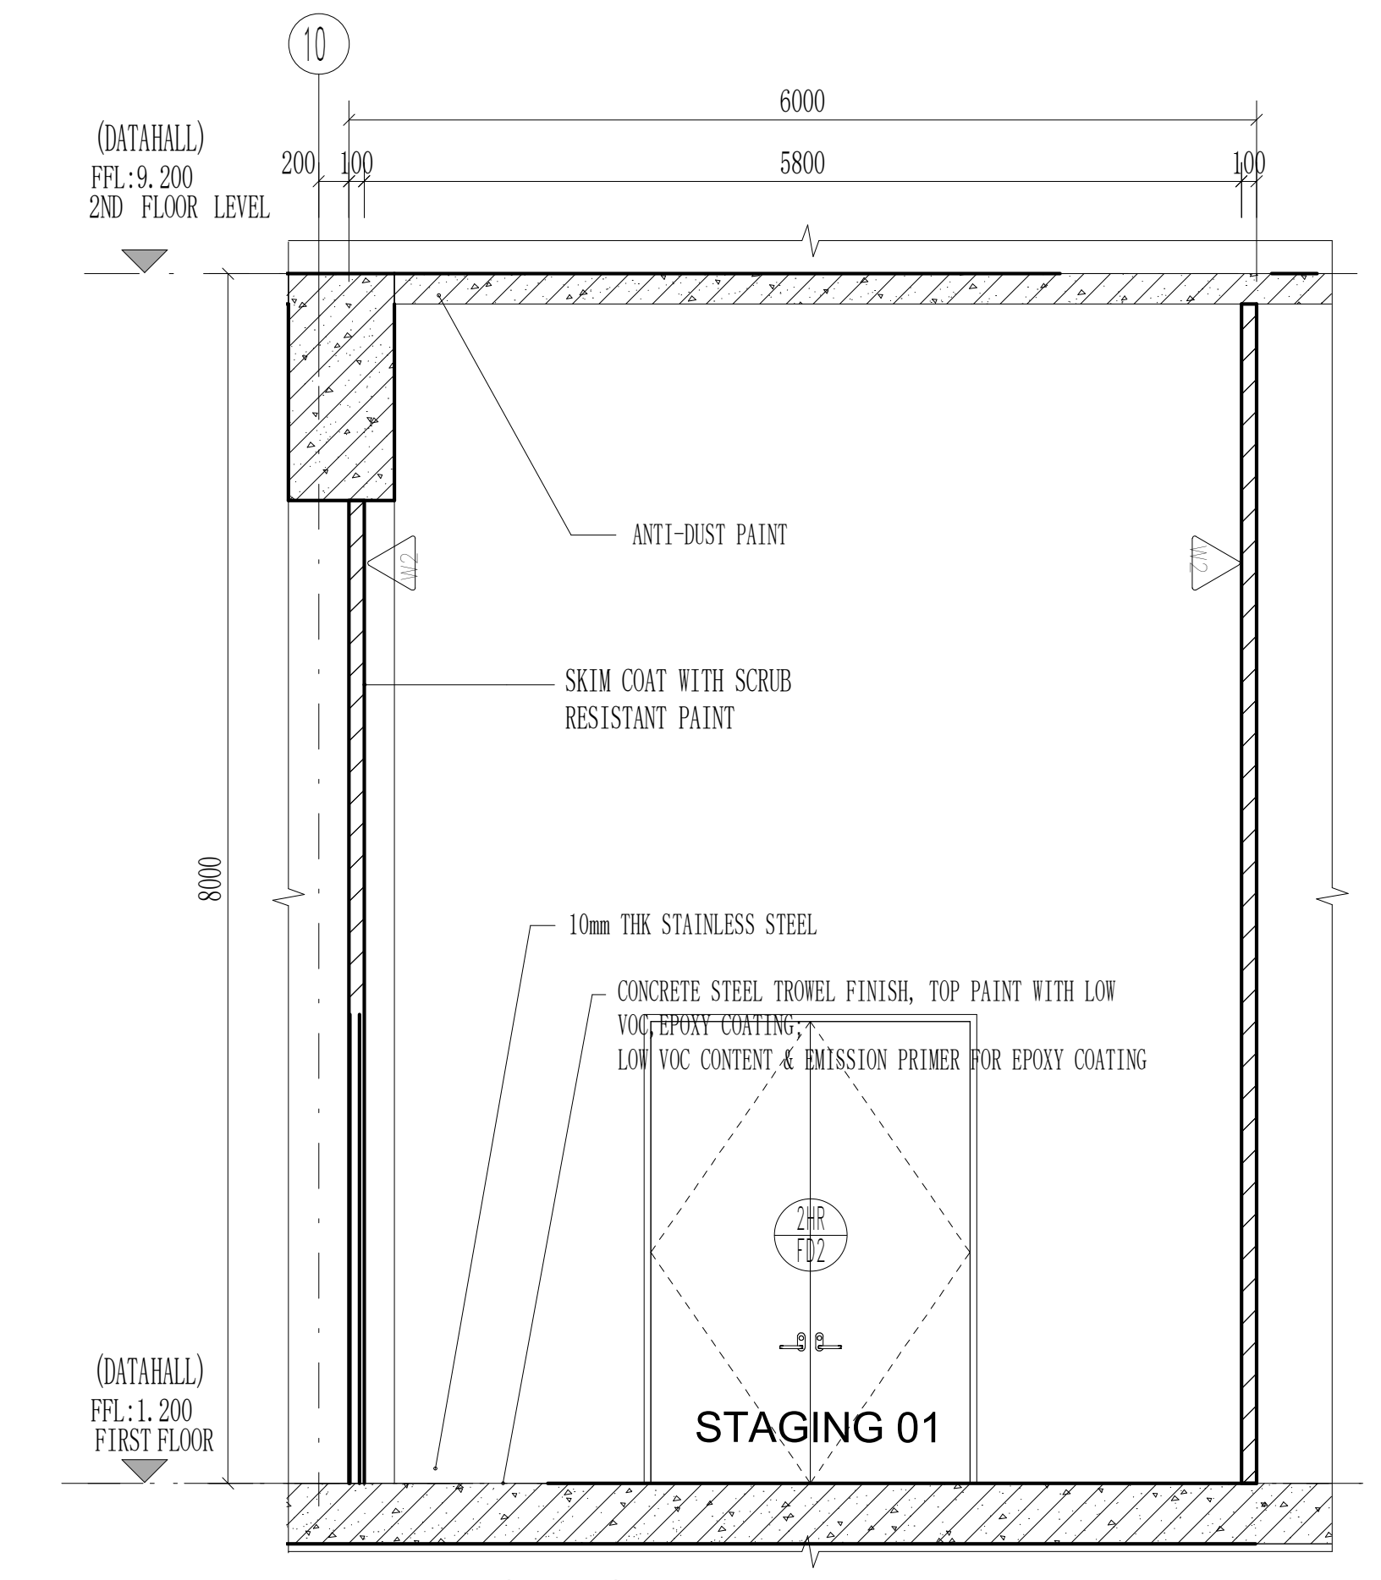
10
(DATAHALL)
FFL:9.200
2ND FLOOR LEVEL
6000
200 100
5800
100
8000
ANTI-DUST PAINT
SKIM COAT WITH SCRUB RESISTANT PAINT
W2
10mm THK STAINLESS STEEL
CONCRETE STEEL TROWEL FINISH, TOP PAINT WITH LOW VOC,EPOXY COATING; LOW VOC CONTENT & EMISSION PRIMER FOR EPOXY COATING
2HR FD2
STAGING 01
(DATAHALL)
FFL:1.200
FIRST FLOOR

STAGING 01SECTION A-A

Scale 1:50

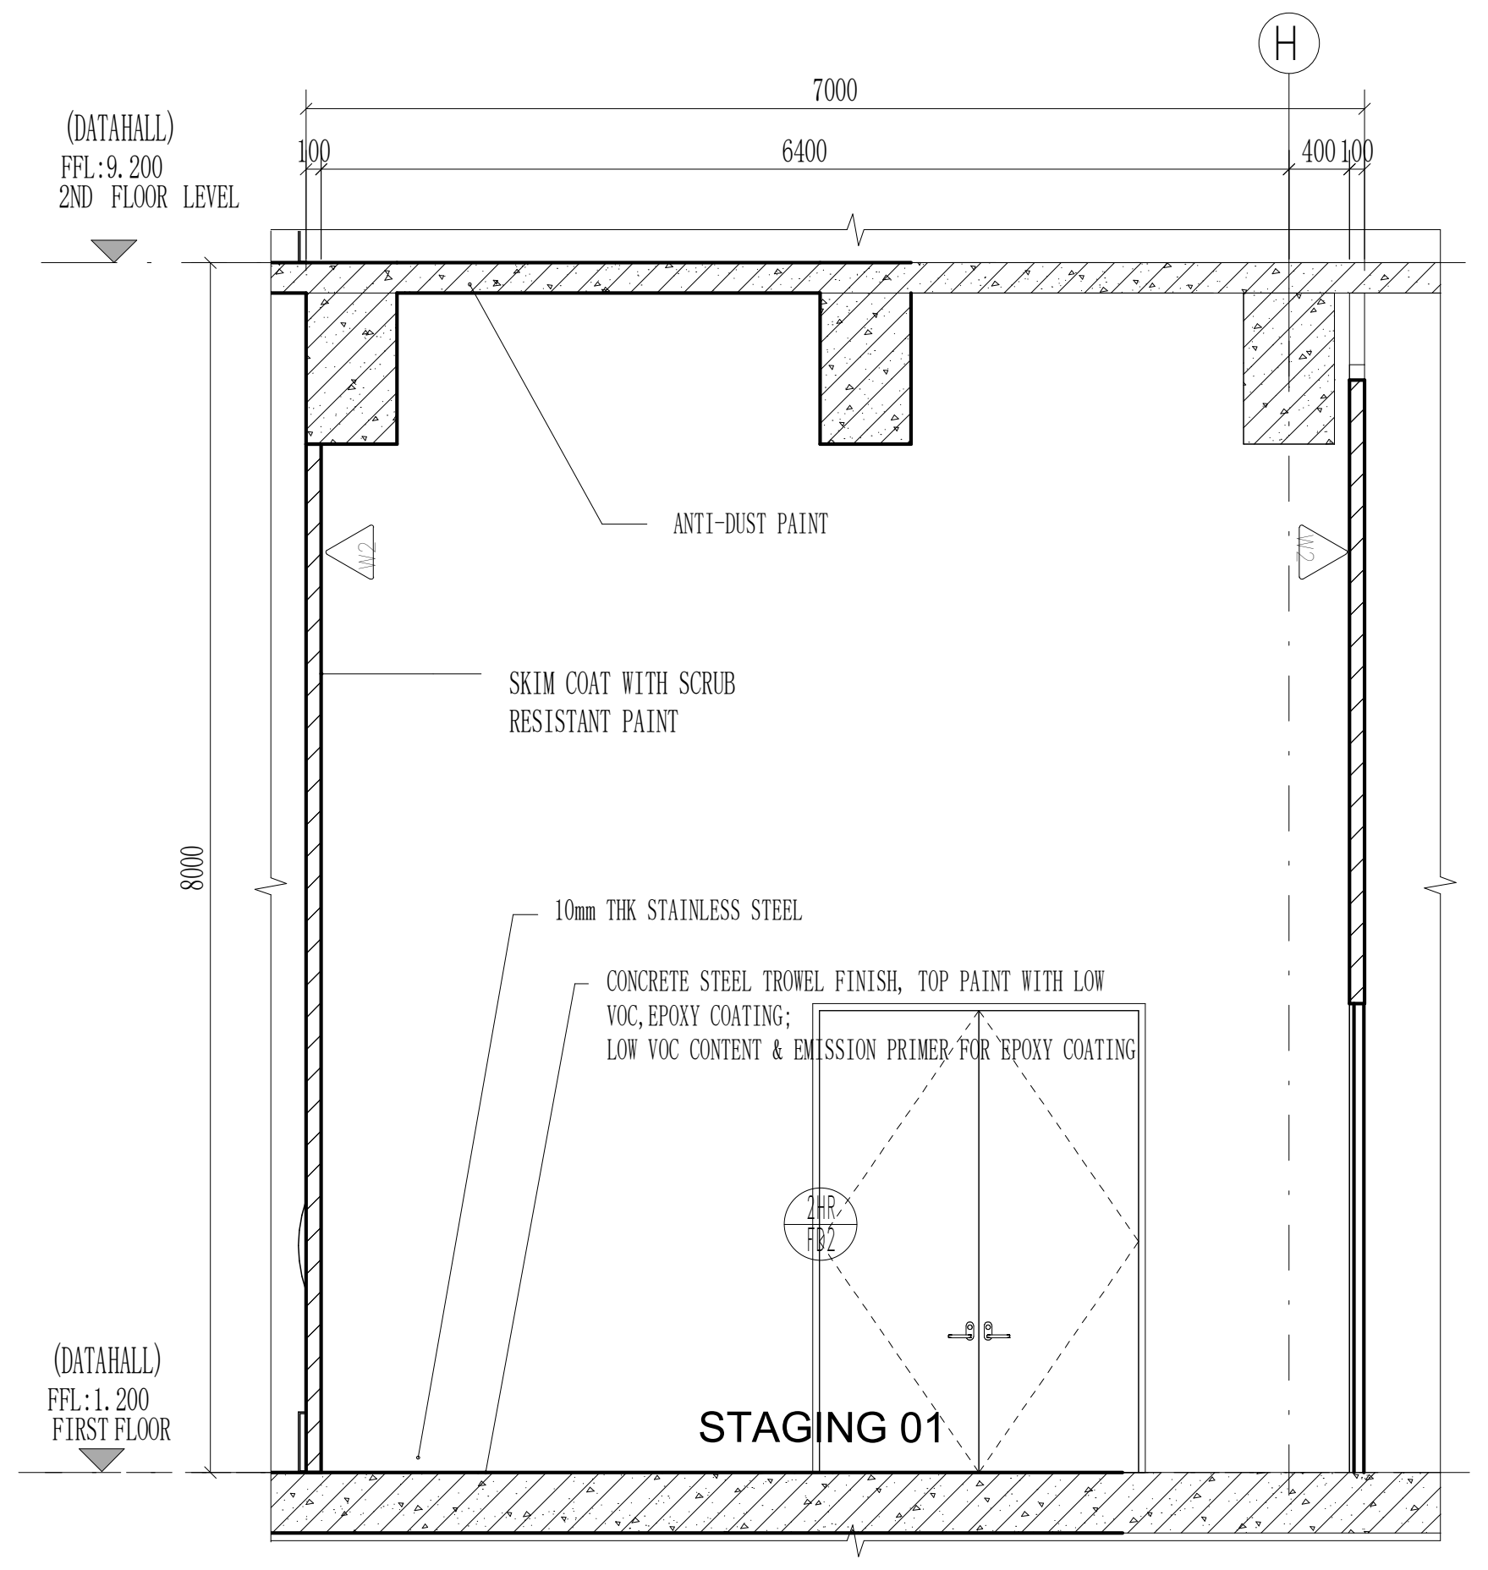
H
(DATAHALL)
FFL:9.200
2ND FLOOR LEVEL
7000
100
6400
400 100
8000
ANTI-DUST PAINT
SKIM COAT WITH SCRUB RESISTANT PAINT
W2
10mm THK STAINLESS STEEL
CONCRETE STEEL TROWEL FINISH, TOP PAINT WITH LOW VOC,EPOXY COATING; LOW VOC CONTENT & EMISSION PRIMER FOR EPOXY COATING
2HR FB2
STAGING 01
(DATAHALL)
FFL:1.200
FIRST FLOOR

STAGING 01 SECTION B-B

Scale 1:50

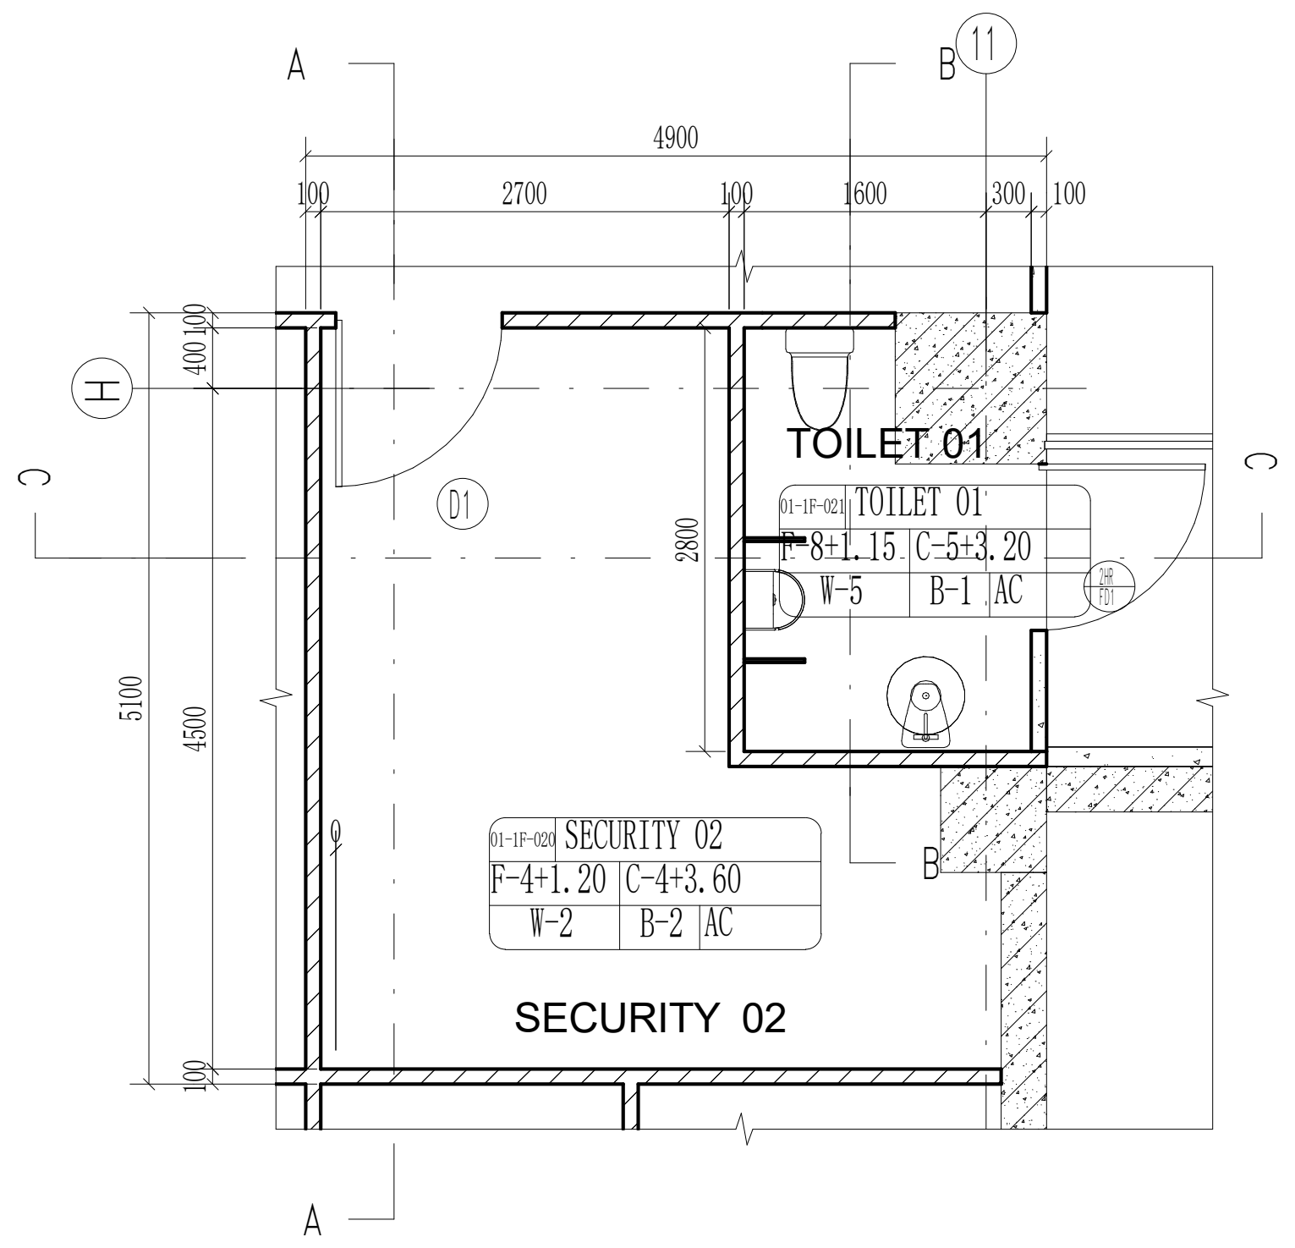
A
B
11
4900
100
2700
100
1600
300
100
H
400 100
C
D1
2800
TOILET 01
01-1F-021 TOILET 01
F-8+1.15 C-5+3.20
W-5 B-1 AC
2HR FD1
5100
4500
100
01-1F-020 SECURITY 02
F-4+1.20 C-4+3.60
W-2 B-2 AC
SECURITY 02

SECURITY 02、 TOILET 01 FLOOR PLAN

Scale 1:50

THE "SFL" MARKED IN THE DRAWING REFERS TO THE STRUCTURAL FLOOR LEVEL, WHILE THE FINISHED FLOOR LEVEL (FFL) IS DETERMINED BASED ON FLOOR FINISHES.

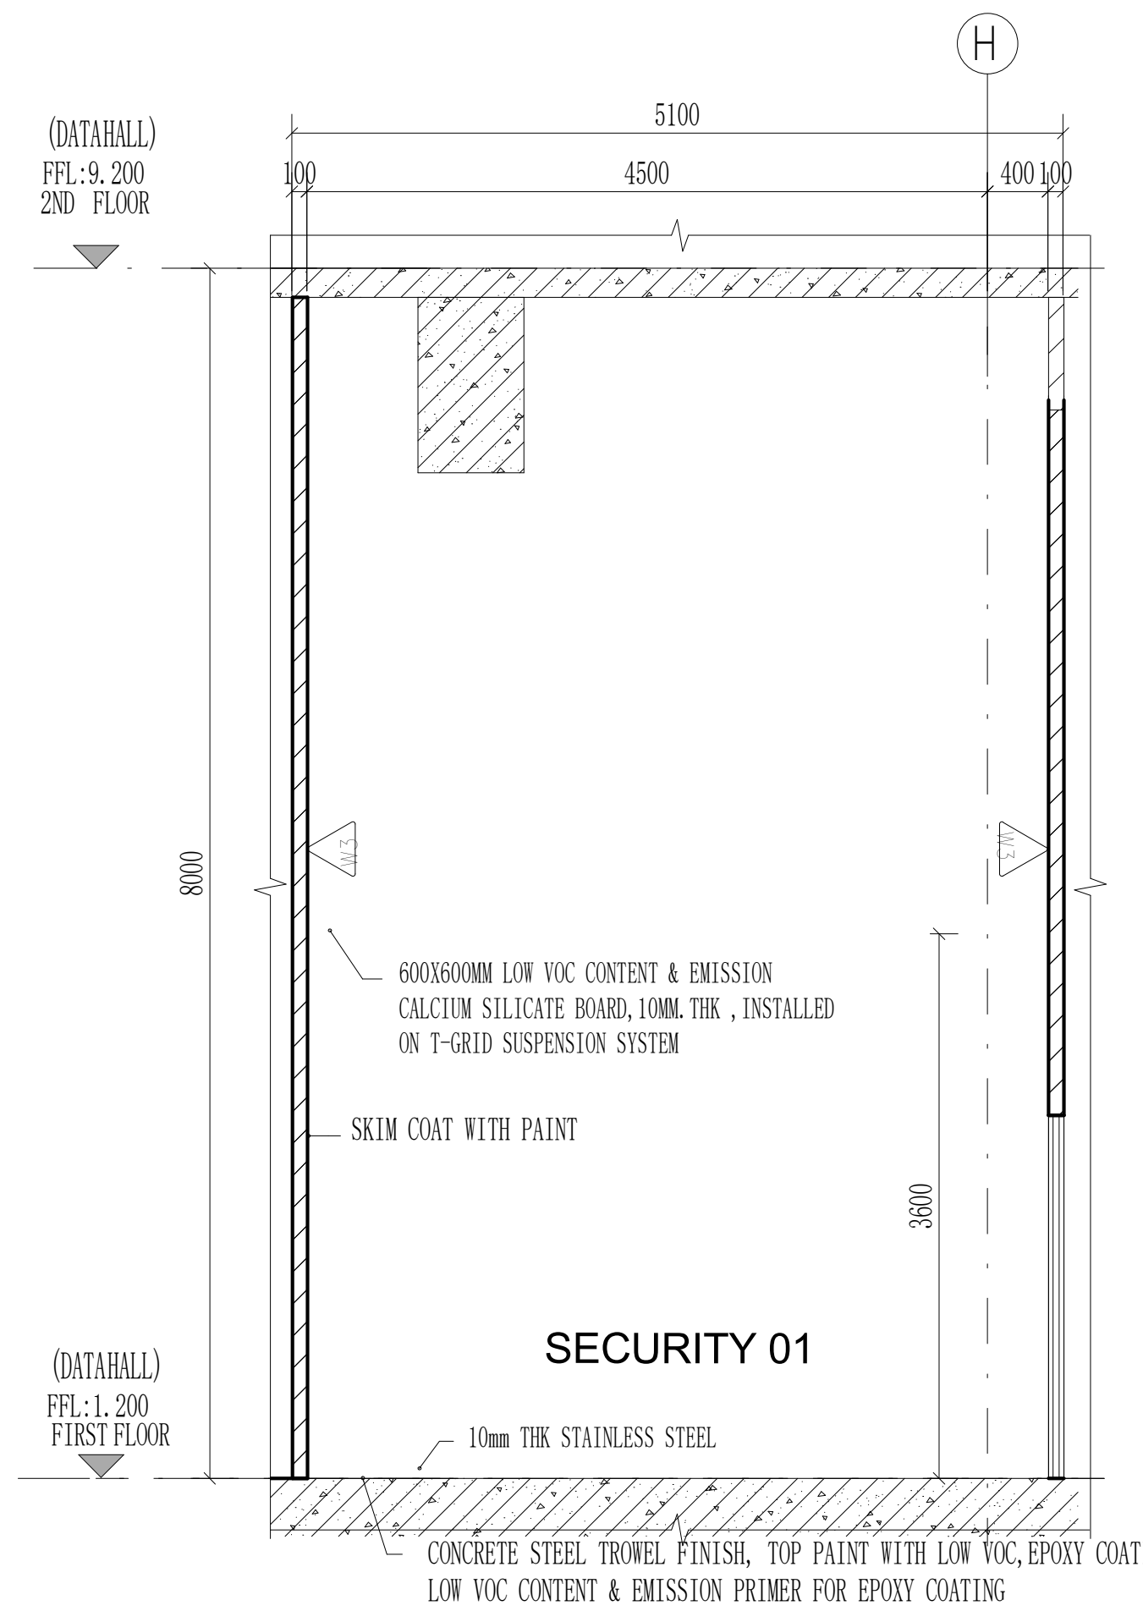
H
(DATAHALL)
FFL:9.200
2ND FLOOR
5100
100
4500
400 100
8000
W3
600X600MM LOW VOC CONTENT & EMISSION CALCIUM SILICATE BOARD,10MM.THK , INSTALLED ON T-GRID SUSPENSION SYSTEM
SKIM COAT WITH PAINT
3600
SECURITY 01
(DATAHALL)
FFL:1.200
FIRST FLOOR
10mm THK STAINLESS STEEL
CONCRETE STEEL TROWEL FINISH, TOP PAINT WITH LOW VOC,EPOXY COATING; LOW VOC CONTENT & EMISSION PRIMER FOR EPOXY COATING

SECURITY 01 TOILET 01 SECTION A-A

Scale 1:50

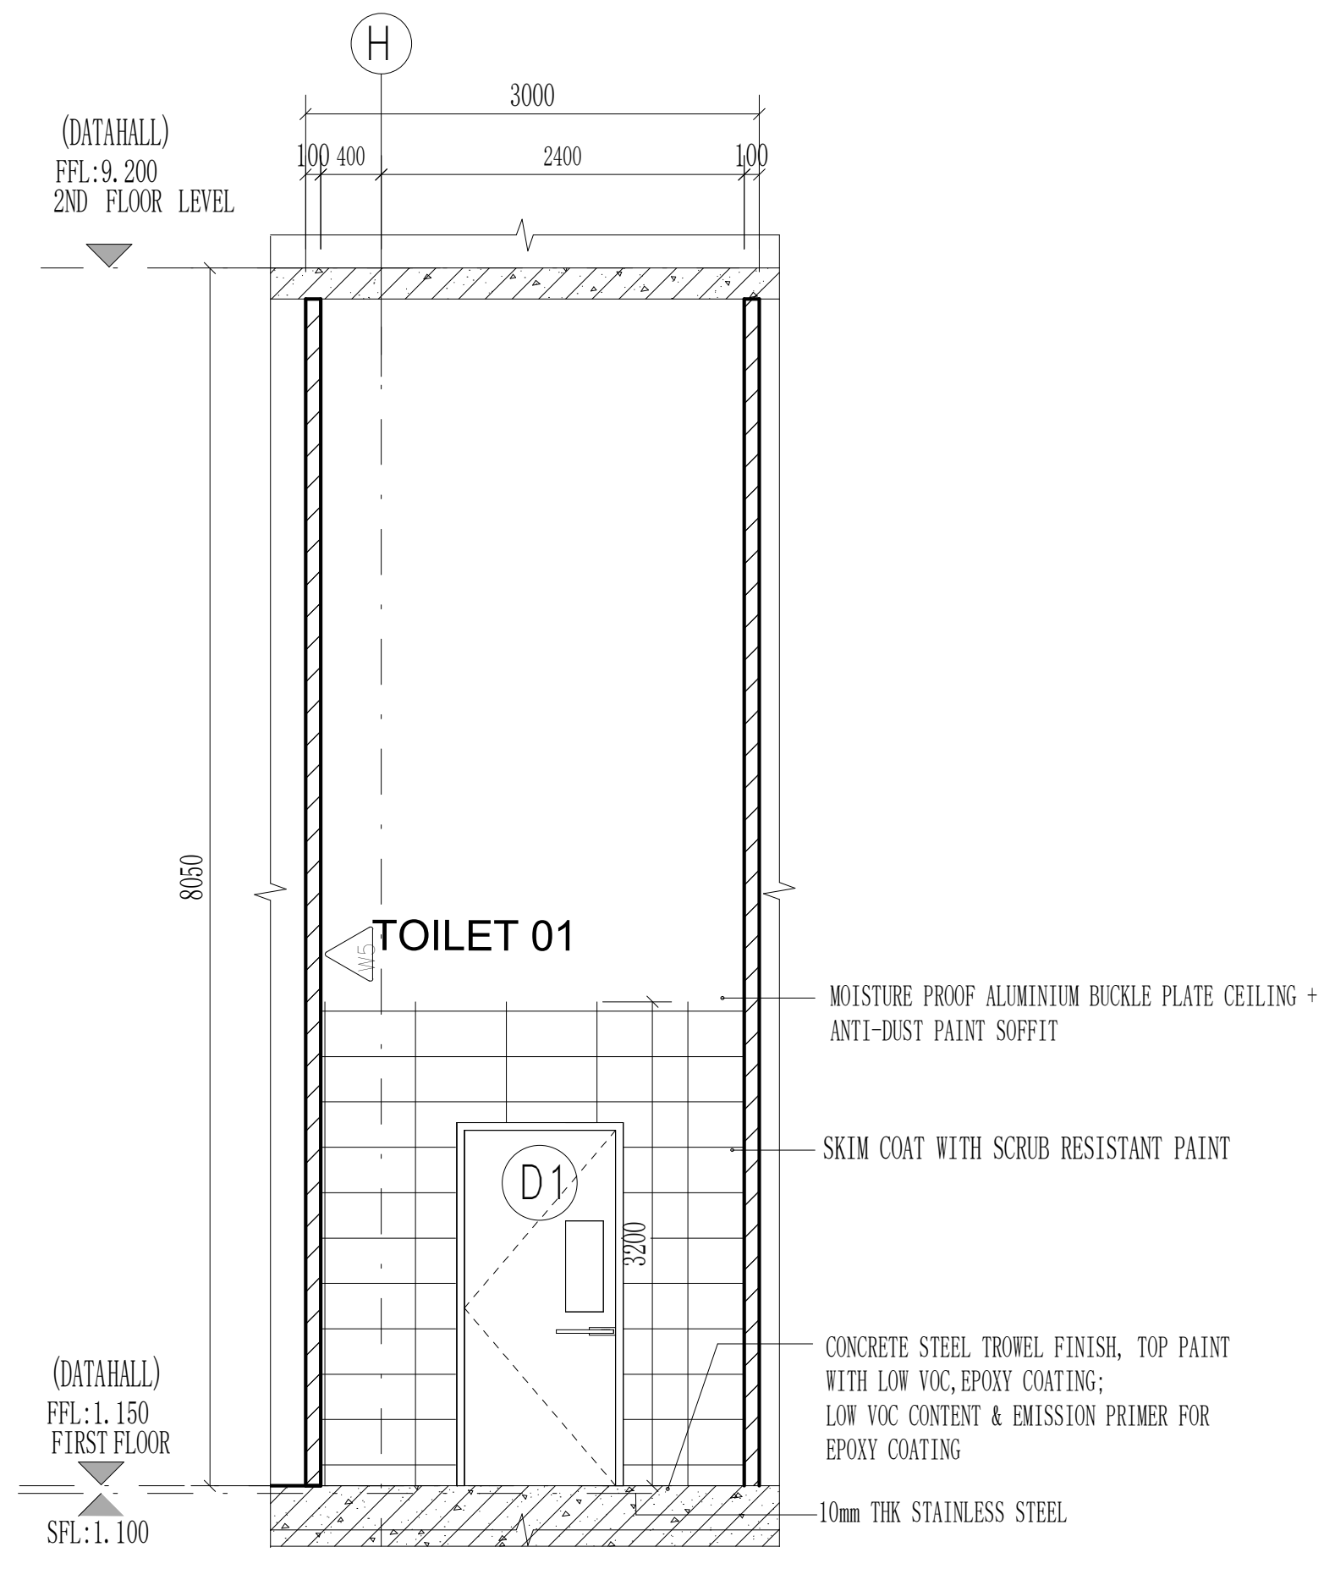
H
(DATAHALL)
FFL:9.200
2ND FLOOR LEVEL
3000
100 400
2400
100
8050
TOILET 01
W5
MOISTURE PROOF ALUMINIUM BUCKLE PLATE CEILING + ANTI-DUST PAINT SOFFIT
SKIM COAT WITH SCRUB RESISTANT PAINT
D1
3200
CONCRETE STEEL TROWEL FINISH, TOP PAINT WITH LOW VOC,EPOXY COATING; LOW VOC CONTENT & EMISSION PRIMER FOR EPOXY COATING
(DATAHALL)
FFL:1.150
FIRST FLOOR
SFL:1.100
10mm THK STAINLESS STEEL

TOILET 01 SECTION B-B

Scale 1:50

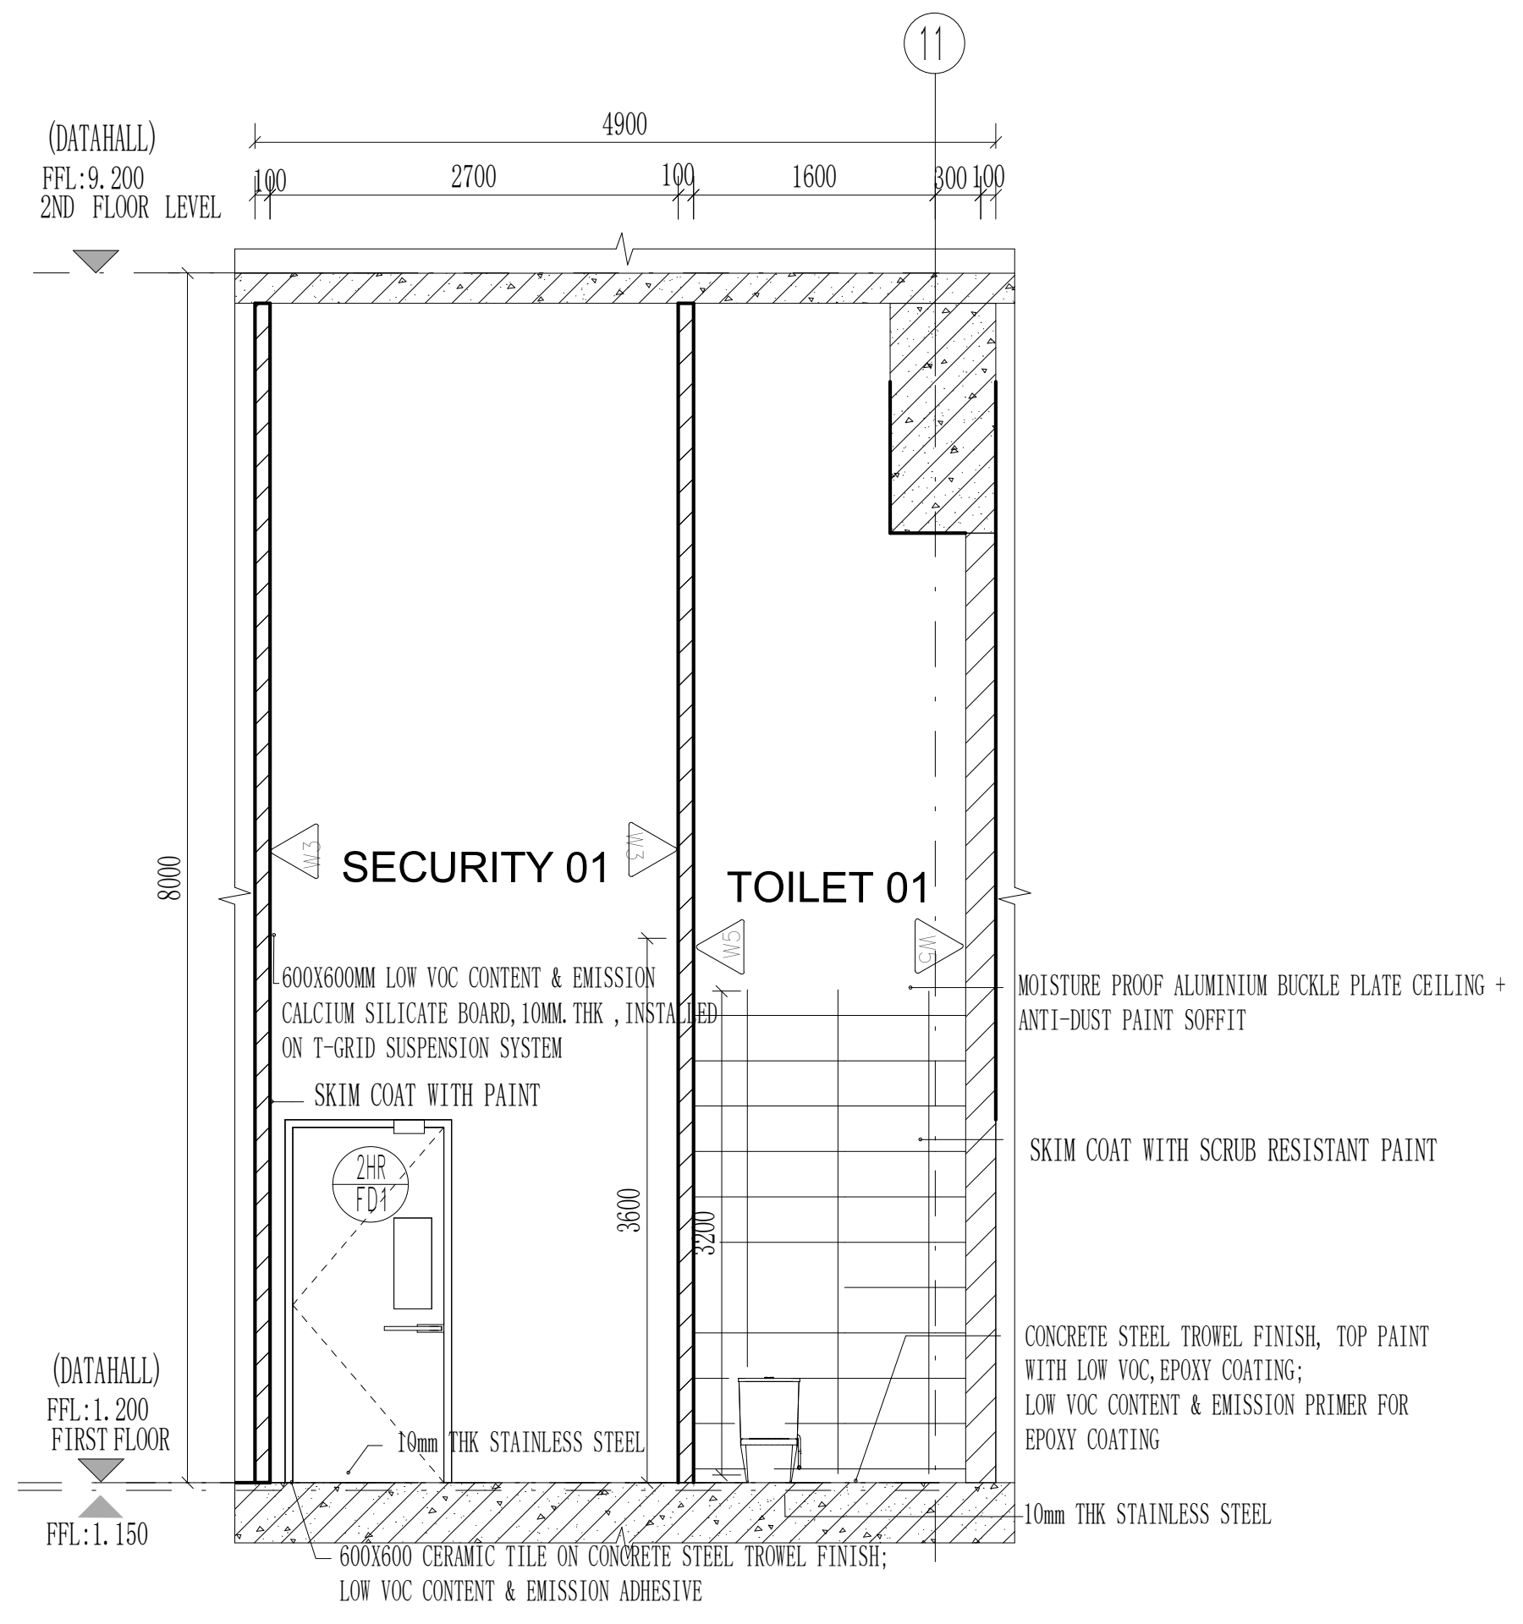
11
(DATAHALL)
FFL:9.200
2ND FLOOR LEVEL
4900
100
2700
100
1600
300 100
8000
SECURITY 01
TOILET 01
W3
W5
600X600MM LOW VOC CONTENT & EMISSION CALCIUM SILICATE BOARD,10MM.THK , INSTALLED ON T-GRID SUSPENSION SYSTEM
SKIM COAT WITH PAINT
MOISTURE PROOF ALUMINIUM BUCKLE PLATE CEILING + ANTI-DUST PAINT SOFFIT
SKIM COAT WITH SCRUB RESISTANT PAINT
2HR FD1
3600
3200
CONCRETE STEEL TROWEL FINISH, TOP PAINT WITH LOW VOC,EPOXY COATING; LOW VOC CONTENT & EMISSION PRIMER FOR EPOXY COATING
(DATAHALL)
FFL:1.200
FIRST FLOOR
FFL:1.150
10mm THK STAINLESS STEEL
600X600 CERAMIC TILE ON CONCRETE STEEL TROWEL FINISH; LOW VOC CONTENT & EMISSION ADHESIVE

SECURITY 01 TOILET 01 SECTION C-C

Scale 1:50

CLIENT :

GULF EDGE DC 01

87 Wireless Road, M Thai Tower 11th. Floor, All Seasons Place, Lumpini,
Pathumwan, Bangkok 10330, Thailand

CONTRACTOR :

华西发展(泰国)有限公司
บริษัท หัวซือ ดีเวลลอปเม้นต์ (ประเทศไทย) จำกัด
HUASHI DEVELOPMENT CO.,LTD
No. 202, Room No. 1403, 14/F, Le Concorde Building,
Ratchadapisek Road, Huaykhwang Sub-District,
Huaykhwang District, Bangkok Metropolitan 10310.

CONSULTANT :

ARbay
บริษัท เอ อาร์ เบย์ จำกัด
ARbay Company Limited
31 st Floor Bangkok Insurance Building
25 South Sathorn road Thungmahamek
Sathorn Bangkok 10120 THAILAND
T +66 (0) 2286 8199
F +66 (0) 2286 2863
info@arbay.co.th

CONSULTANT :

Qbic Engineers & Architects Co.,Ltd.
8 Soi KALONG 4 SANAMBINNAM ROAD,
THASAI SUB-DISTRICT, MUANG NONTHABURI DISTRICT
, NONTHABURI.
Tel 662-950-4374
Fax 662-580-3231
E-Mail : qbic@qbic.co.th, www.qbic.co.th
QBIC ENGINEERS AND ARCHITECTS CO.,LTD.

CONSULTANT :

MITR
MITR TECHNICAL CONSULTANT CO.,LTD.
1168/8 12th FLOOR, LUMPINI TOWER BUILDING,
RAMA IV RD., THUNGMAHAMEK, SATHORN, BANGKOK 10120, THAILAND
TEL : 0-2679-9079-84
FAX : 0-2679-9085 E-mail: mitr_dd@mitr.com

Architect : SIGNATURE
ประกิต พนานุรัตน์ วสถ. 580
ที่อยู่
251/1 ถ.จารุเมือง แขวงรองเมือง เขตปทุมวัน
กรุงเทพมหานคร โทรศัพท์ 02-286-8199

Structural Engineer : SIGNATURE
วิศวกรผู้ออกแบบโครงสร้าง
ณัฐสม สงวนวงษ์ วย 1423
ที่อยู่
2/1 ซ.รามคำแหง 150 ถ.รามคำแหง
แขวง สะพานสูง เขต สะพานสูง กทม. 10240

Structural Inspector : SIGNATURE
วิศวกรผู้ตรวจสอบโครงสร้าง
โกมล จุฑาภัทร วย 964
ที่อยู่
24/18 ซ.นวมินทร์ 129 ถ. นวมินทร์
แขวง นวลจันทร์ เขต บึงกุ่ม กทม. 10230

Electrical Engineer : SIGNATURE
วิศวกรผู้ออกแบบระบบไฟฟ้ากำลัง
นายสุภัทร บูรณวิทย์ วฟก.1265
ที่อยู่
21 ซอยทานสัมฤทธิ์ 13
ตำบลท่าทราย อ.เมืองนนทบุรี จ.นนทบุรี 11000

Mechanical Engineer : SIGNATURE
วิศวกรผู้ออกแบบระบบเครื่องกลและปรับอากาศ
นายประสิทธิ์ เกี้ยวสุนทร วก.1221
ที่อยู่
44/372 ซอยบางกระดี่ 35/1 แขวงแสมดำ
เขตบางขุนเทียน กทม. 10150
ประสิทธิ์

Sanitary Engineer : SIGNATURE
วิศวกรผู้ออกแบบระบบสุขาภิบาล และดับเพลิง
นายทศวรรษ สนั่นฤทธิ์ วส. 215
ที่อยู่
บ้านเลขที่ 99/107 หมู่ที่ 3 ต.ศีรษะจรเข้น้อย
อ.บางเสาธง จ.สมุทรปราการ 10540
ทศวรรษ

ISSUE/REVISION

REV.	DESCRIPTION	DATE
A	90% DEVELOPED	09/05/2026

PROJECT NAME :

GEDC 01

LOCATION:
Nikhom Phattana district, Rayong ,industrial estate,CPGC

BUILDING :
MAIN BUILDING

90% DEVELOPED

TITLE :

ROOM DETAIL-1F-STAGING 01、STAGING02、SECURITY02、TOILET 01

JOB NO.		SCALE	1 : 50
DRAWN	ZYY	REF.	
CHECKED	LJC	DWG. NO.	
APPROVED	LXD		MPK01A-90-A-RD-110
DATE	2026.05.09		

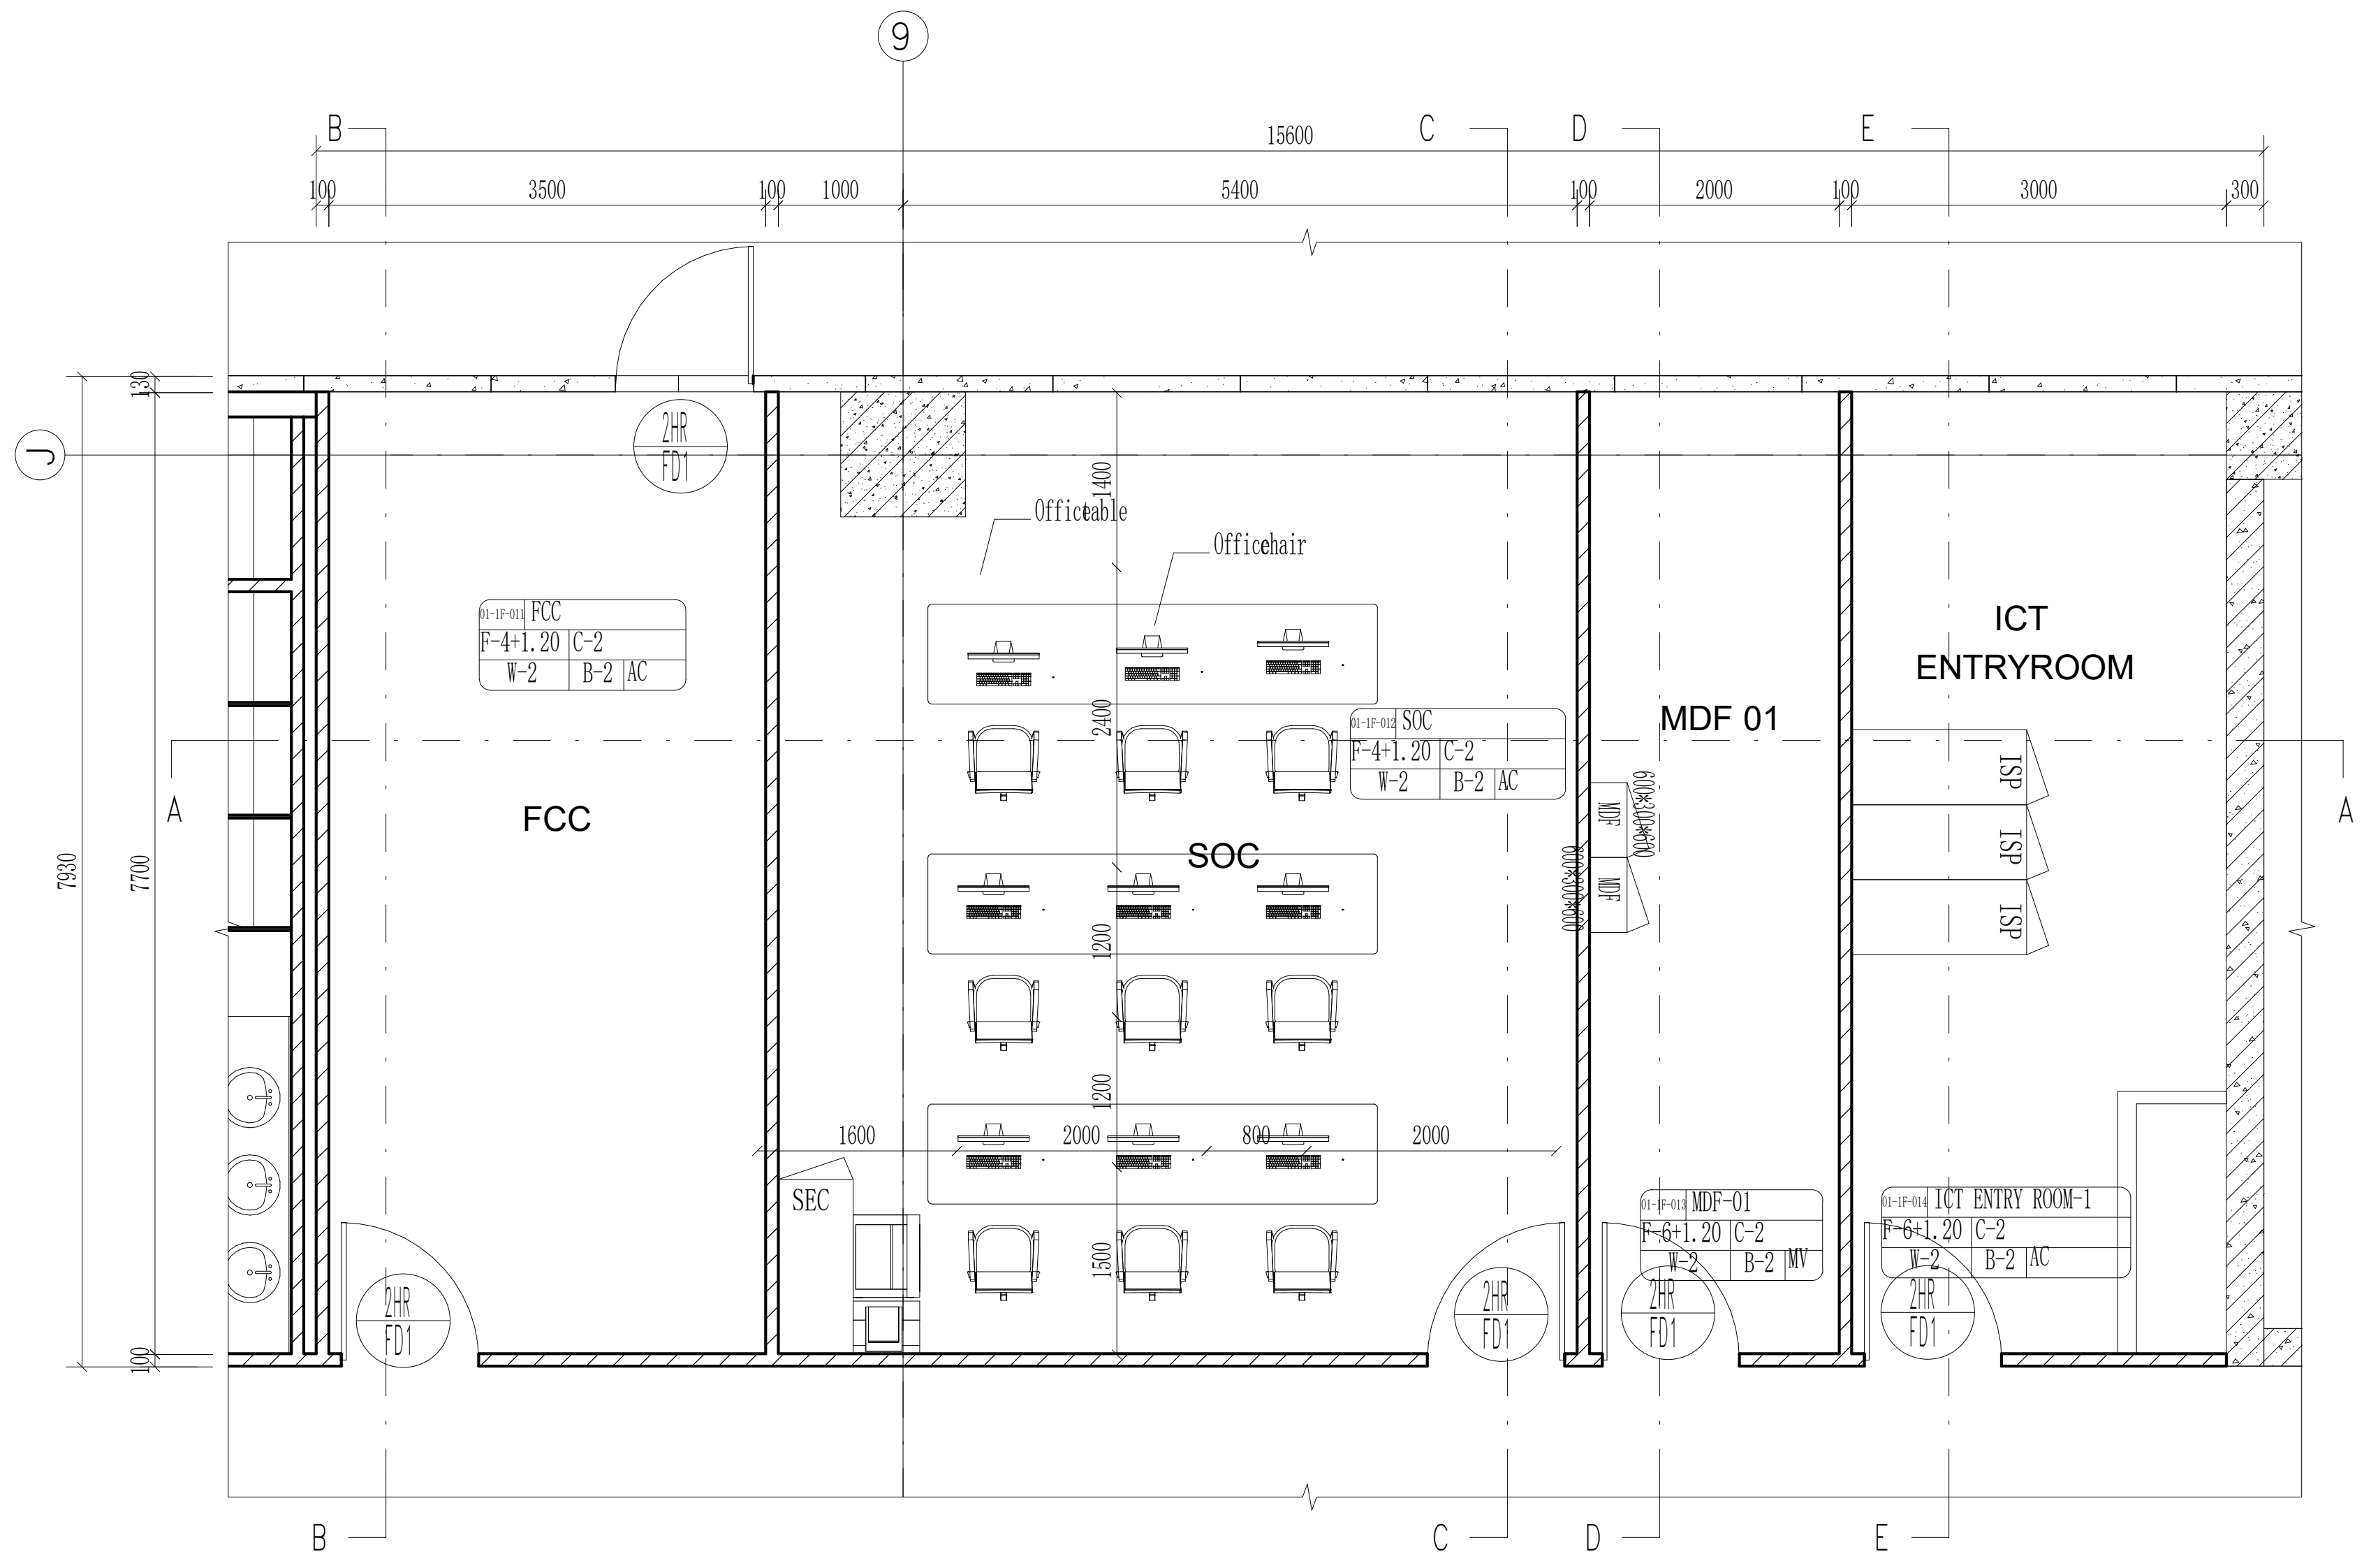
9
B
C
D
E
A
J
15600
100
3500
1000
5400
2000
3000
300
7930
7700
FCC
SOC
MDF 01
ICT
ENTRYROOM
Officetable
Officehair
SEC
1600
2000
800
F-4+1.20 C-2
W-2 B-2 AC
MDF-01
ICT ENTRY ROOM-1
ISP
FD1

ICT、FCC、SOC、MDF 01 FIRST FLOOR PLAN

Scale 1:50

THE "SFL" MARKED IN THE DRAWING REFERS TO THE STRUCTURAL FLOOR LEVEL, WHILE THE FINISHED FLOOR LEVEL (FFL) IS DETERMINED BASED ON FLOOR FINISHES.

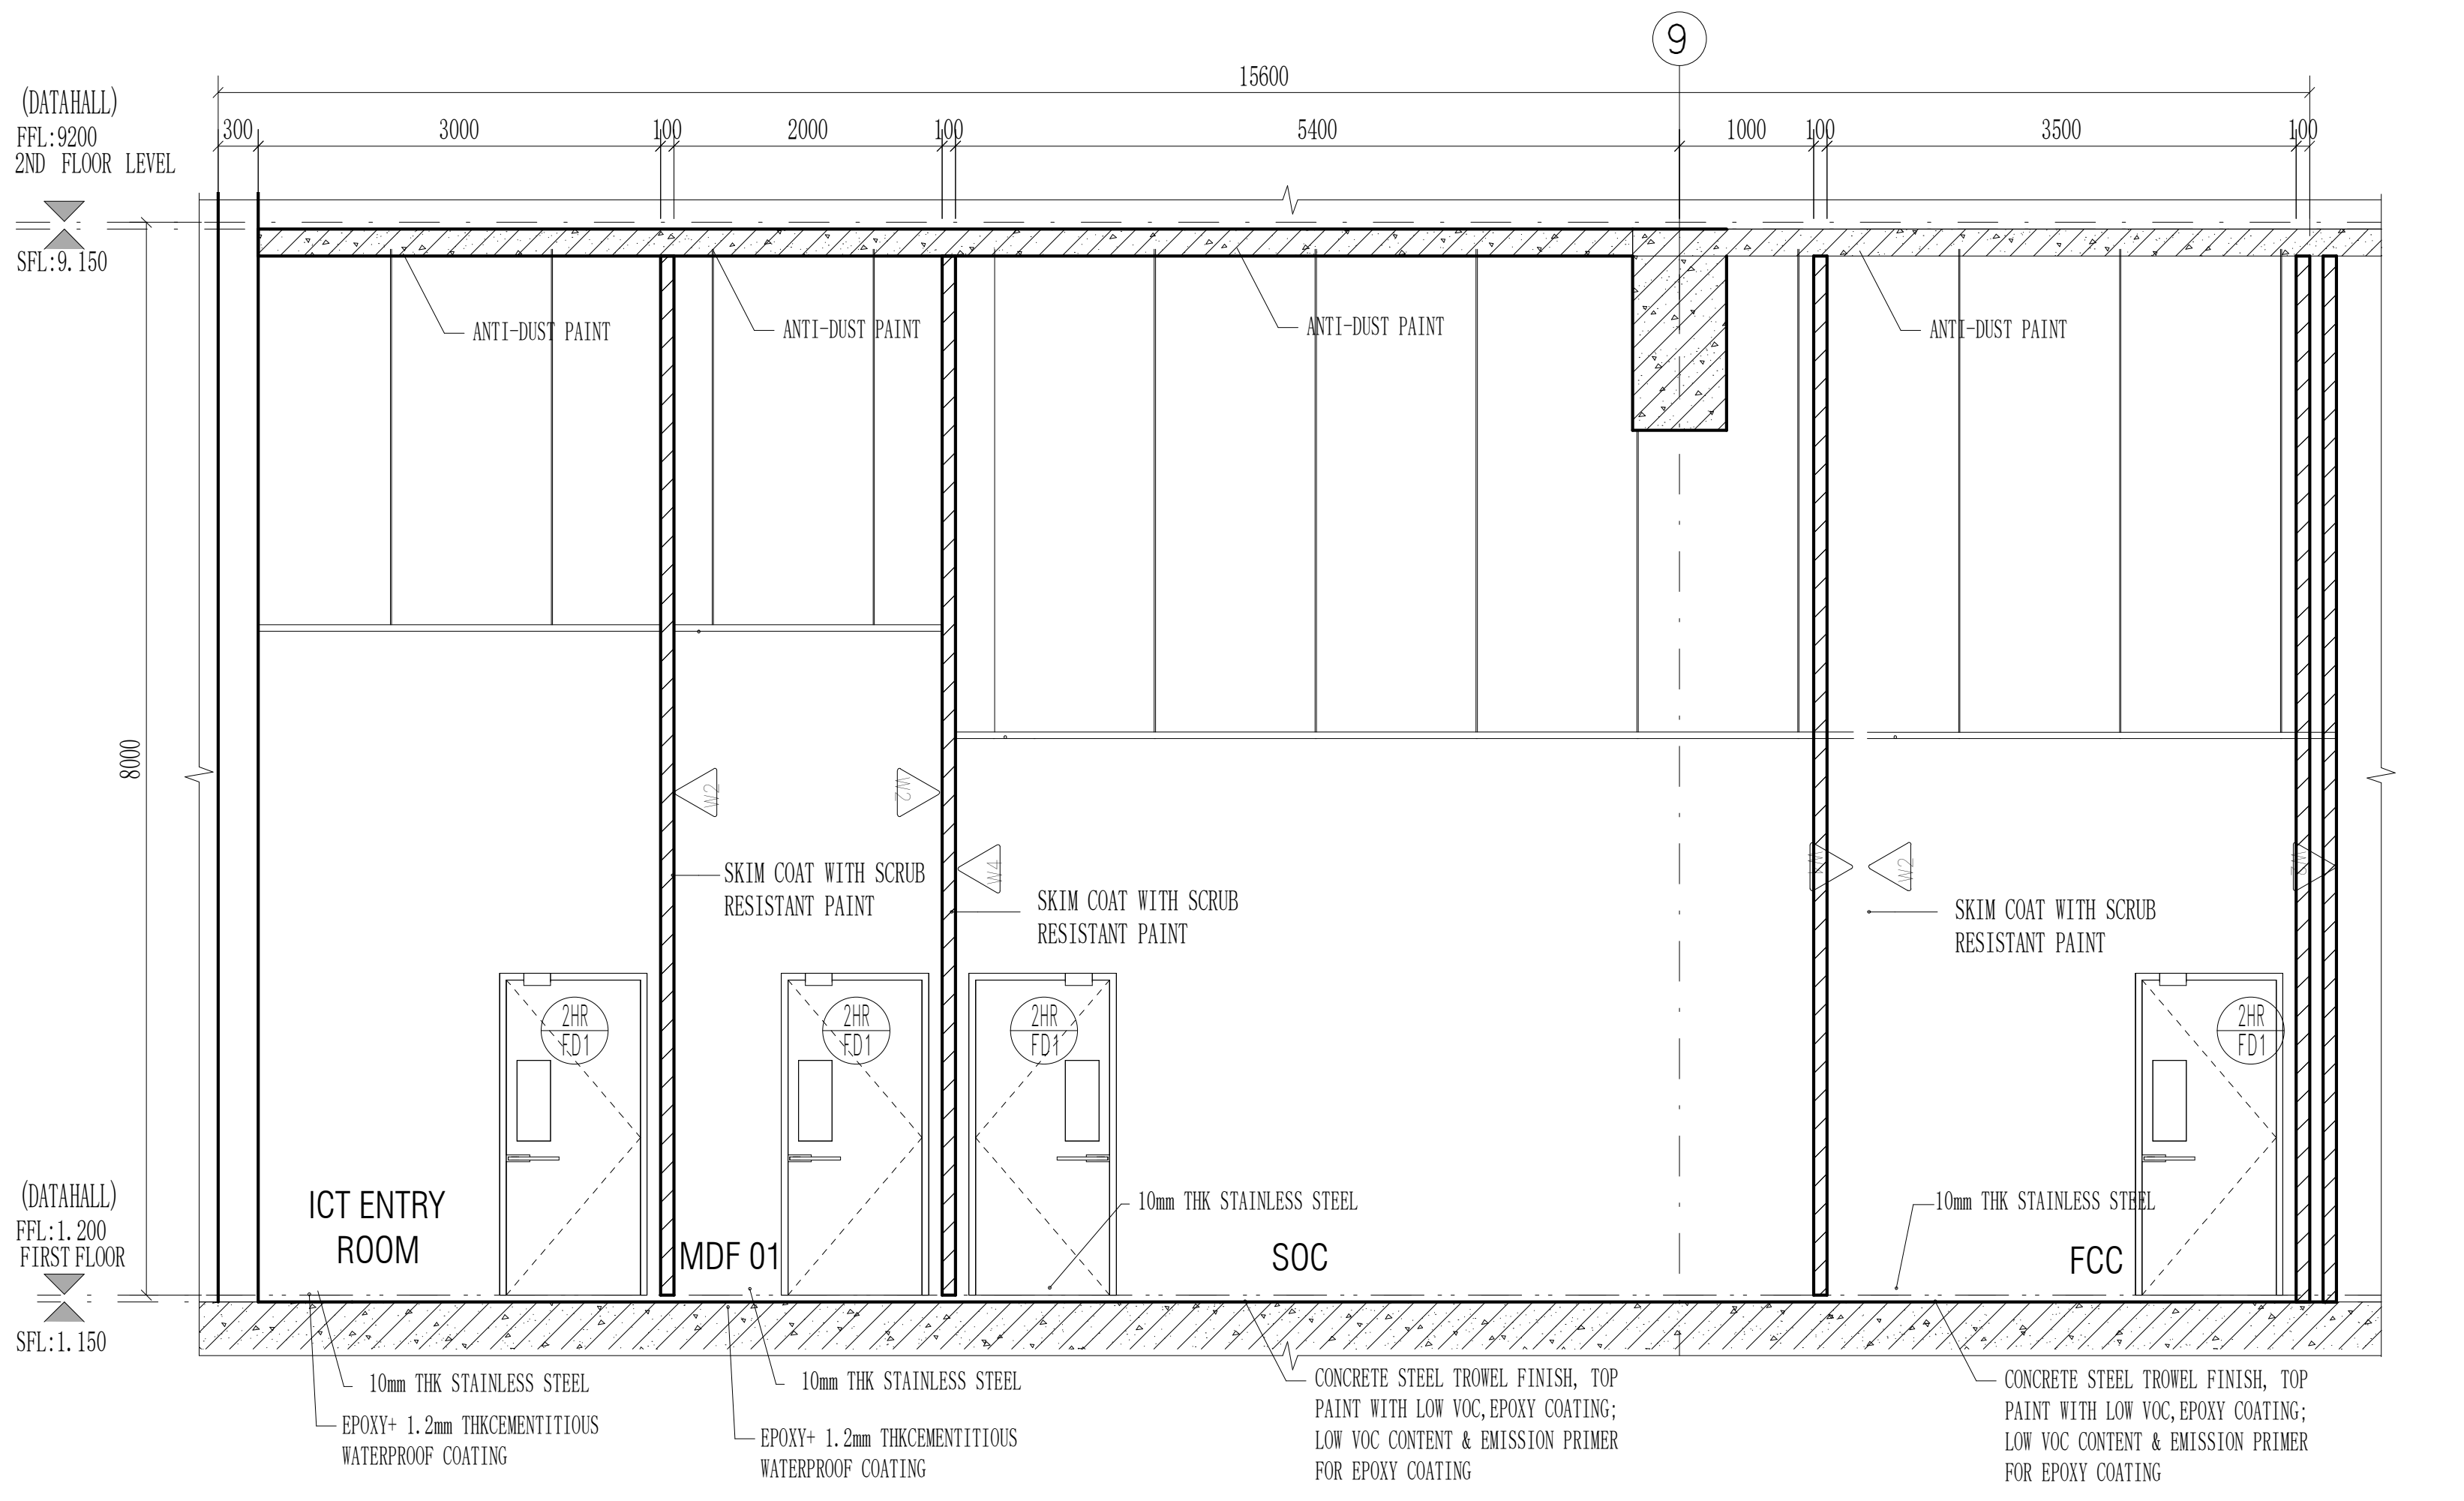
9
15600
300
3000
100
2000
5400
1000
3500
(DATAHALL)
FFL:9200
2ND FLOOR LEVEL
SFL:9.150
8000
ANTI-DUST PAINT
SKIM COAT WITH SCRUB RESISTANT PAINT
(DATAHALL)
FFL:1.200
FIRST FLOOR
SFL:1.150
ICT ENTRY ROOM
MDF 01
SOC
FCC
10mm THK STAINLESS STEEL
EPOXY+ 1.2mm THKCEMENTITIOUS WATERPROOF COATING
CONCRETE STEEL TROWEL FINISH, TOP PAINT WITH LOW VOC,EPOXY COATING; LOW VOC CONTENT & EMISSION PRIMER FOR EPOXY COATING

ICT、FCC、SOC、MDF 01 SECTION A-A

Scale 1:50

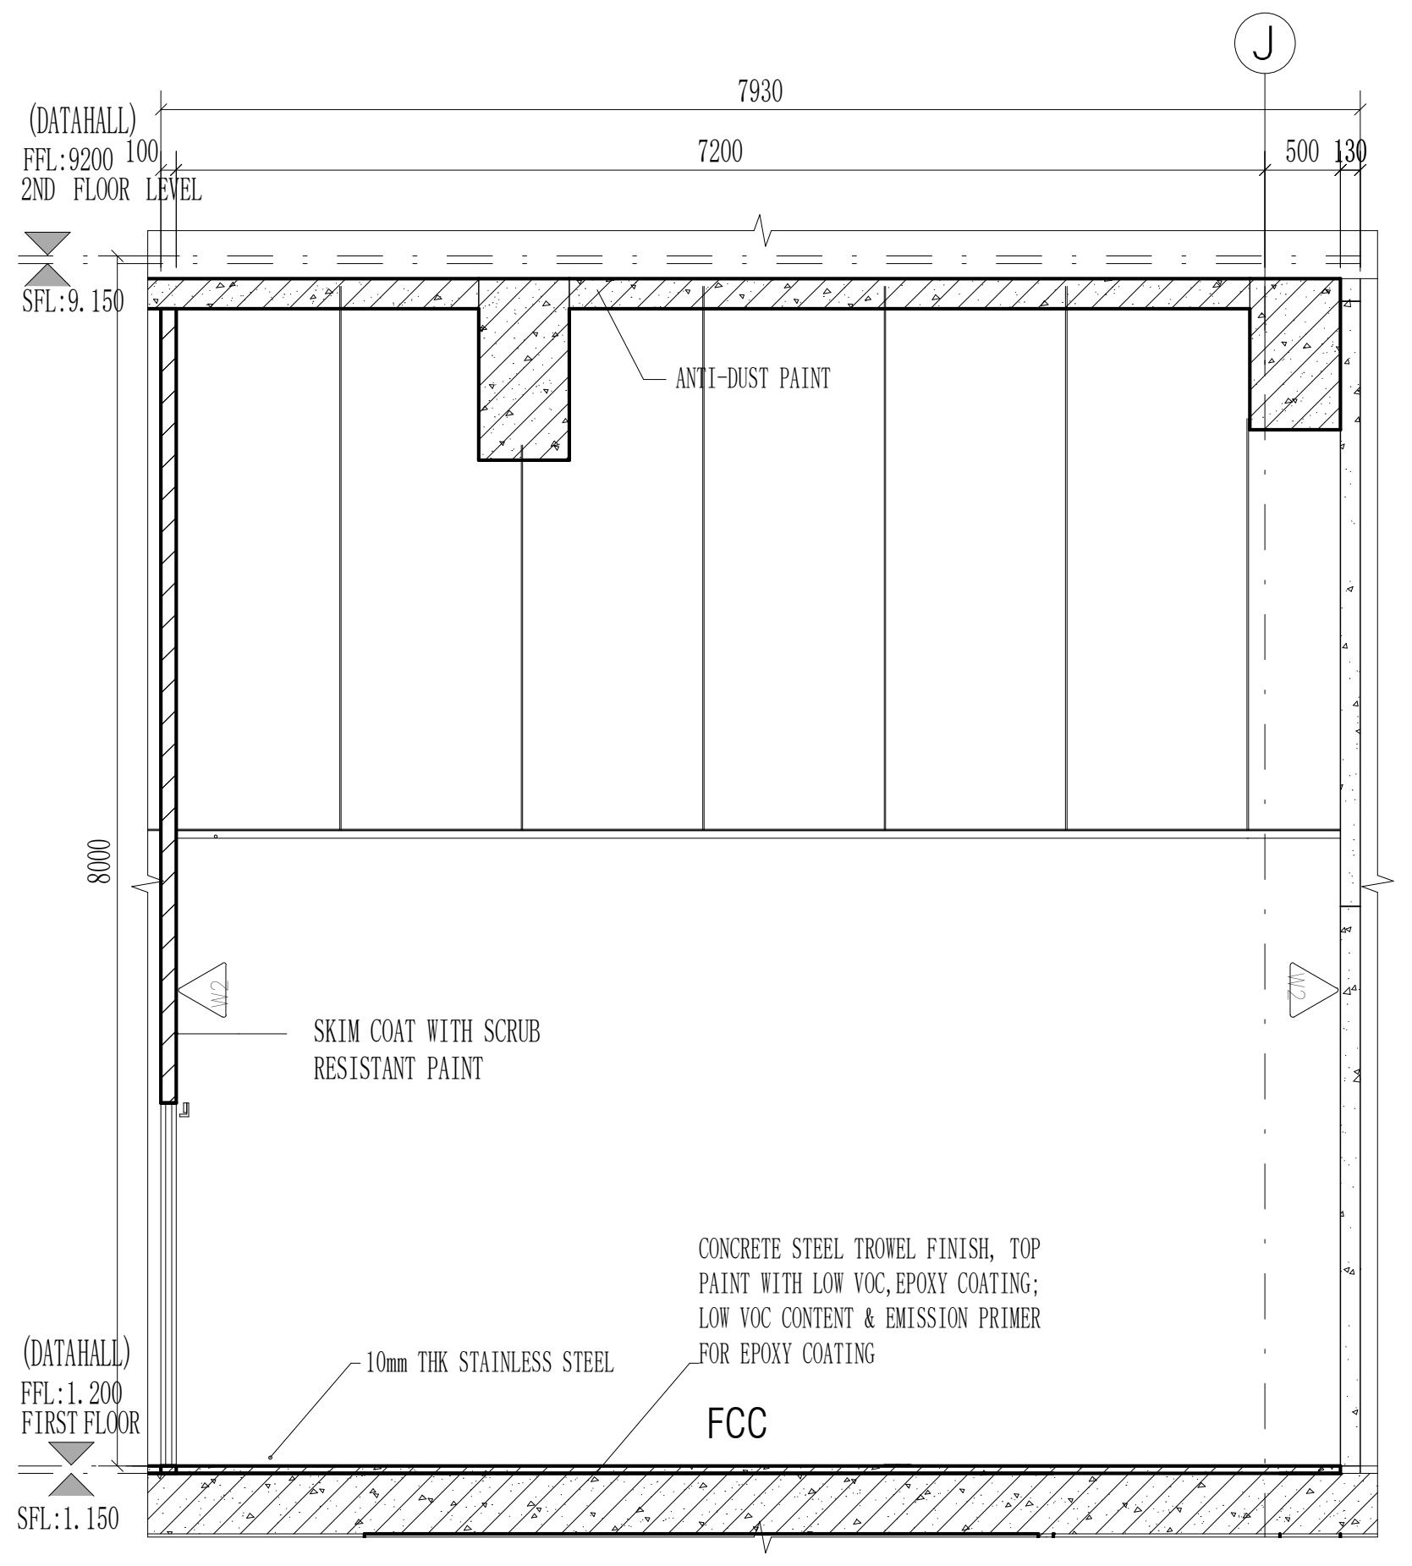
J
7930
100
7200
500
130
(DATAHALL)
FFL:9200
2ND FLOOR LEVEL
SFL:9.150
8000
ANTI-DUST PAINT
SKIM COAT WITH SCRUB RESISTANT PAINT
CONCRETE STEEL TROWEL FINISH, TOP PAINT WITH LOW VOC,EPOXY COATING; LOW VOC CONTENT & EMISSION PRIMER FOR EPOXY COATING
(DATAHALL)
FFL:1.200
FIRST FLOOR
SFL:1.150
10mm THK STAINLESS STEEL
FCC

FCC SECTION B-B

Scale 1:50

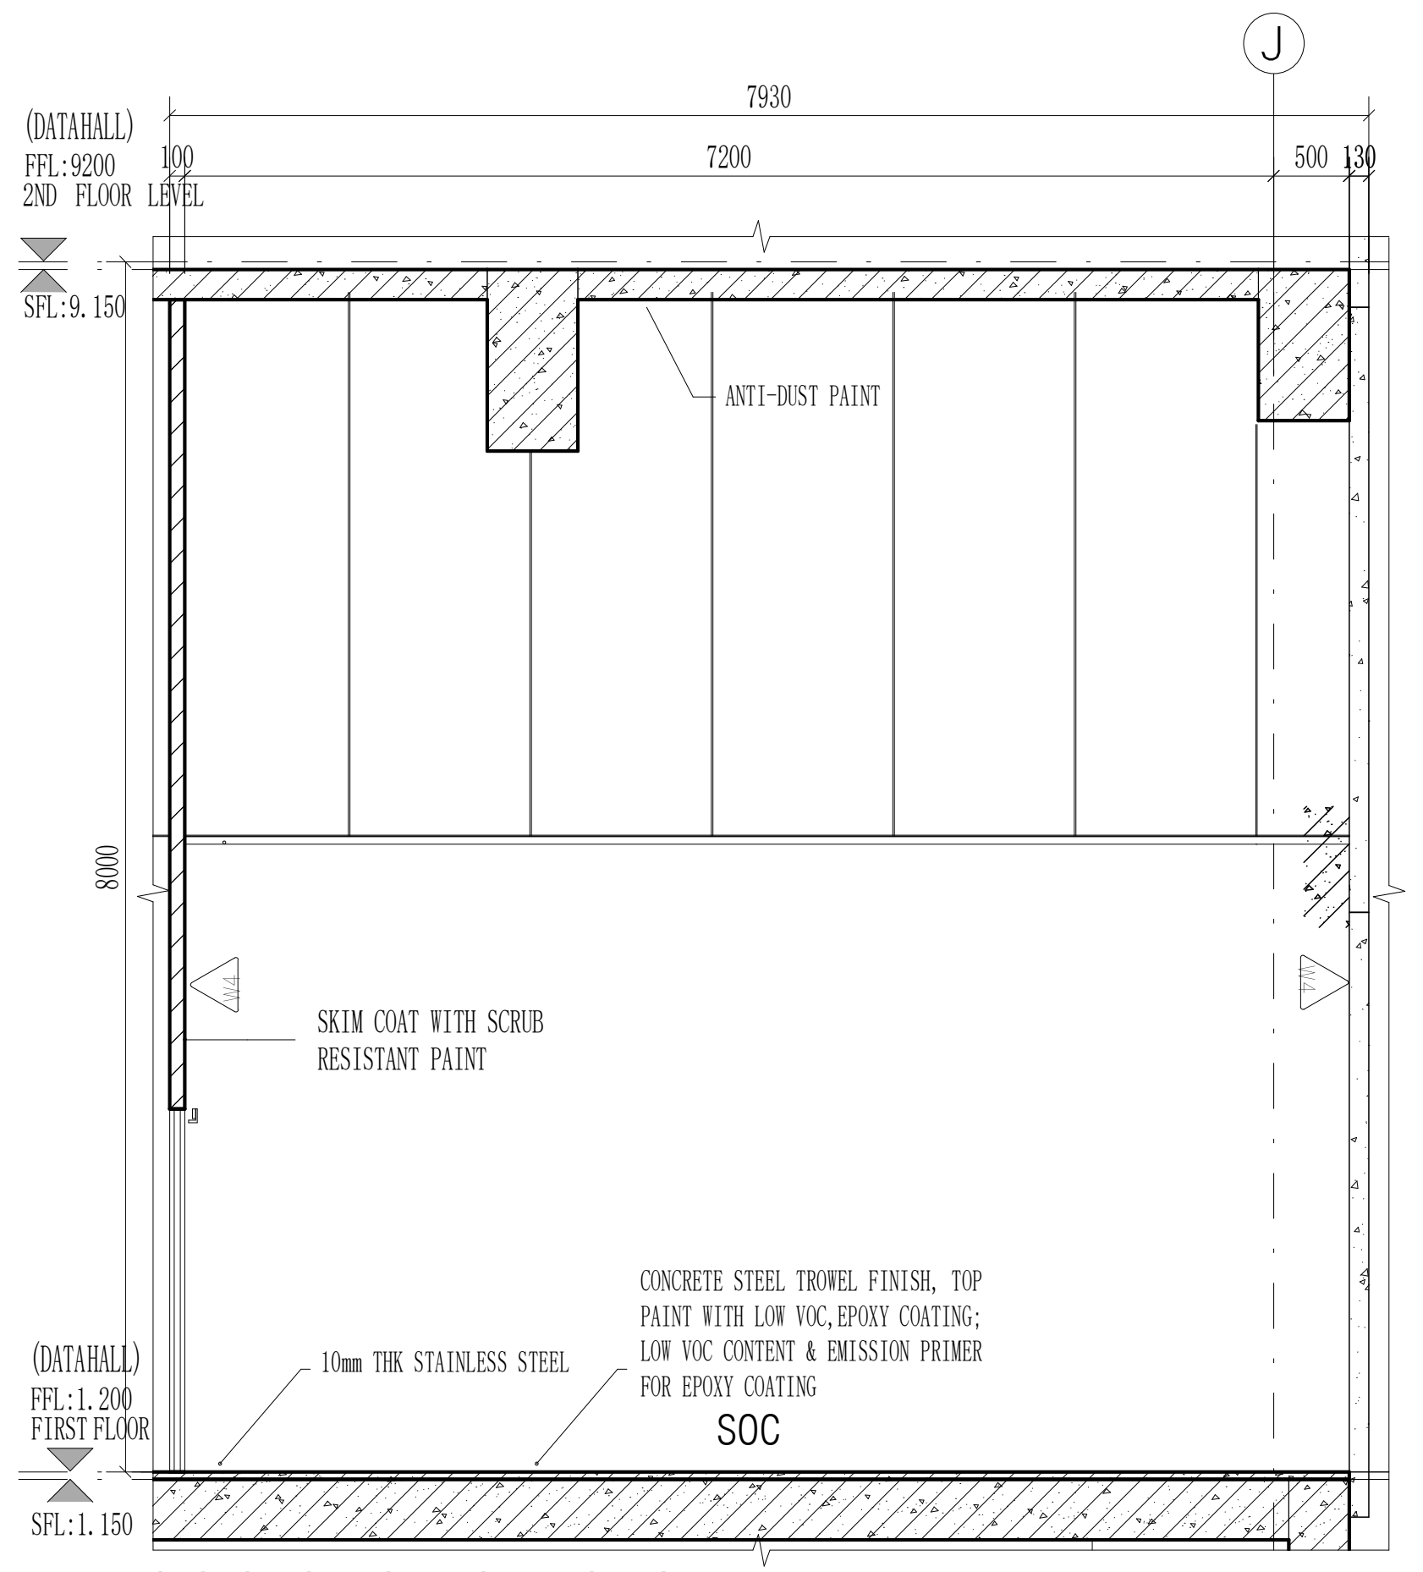
J
7930
7200
500
130
(DATAHALL)
FFL:9200
2ND FLOOR LEVEL
SFL:9.150
8000
ANTI-DUST PAINT
SKIM COAT WITH SCRUB RESISTANT PAINT
CONCRETE STEEL TROWEL FINISH, TOP PAINT WITH LOW VOC,EPOXY COATING; LOW VOC CONTENT & EMISSION PRIMER FOR EPOXY COATING
(DATAHALL)
FFL:1.200
FIRST FLOOR
SFL:1.150
10mm THK STAINLESS STEEL
SOC

SOC SECTION C-C

Scale 1:50

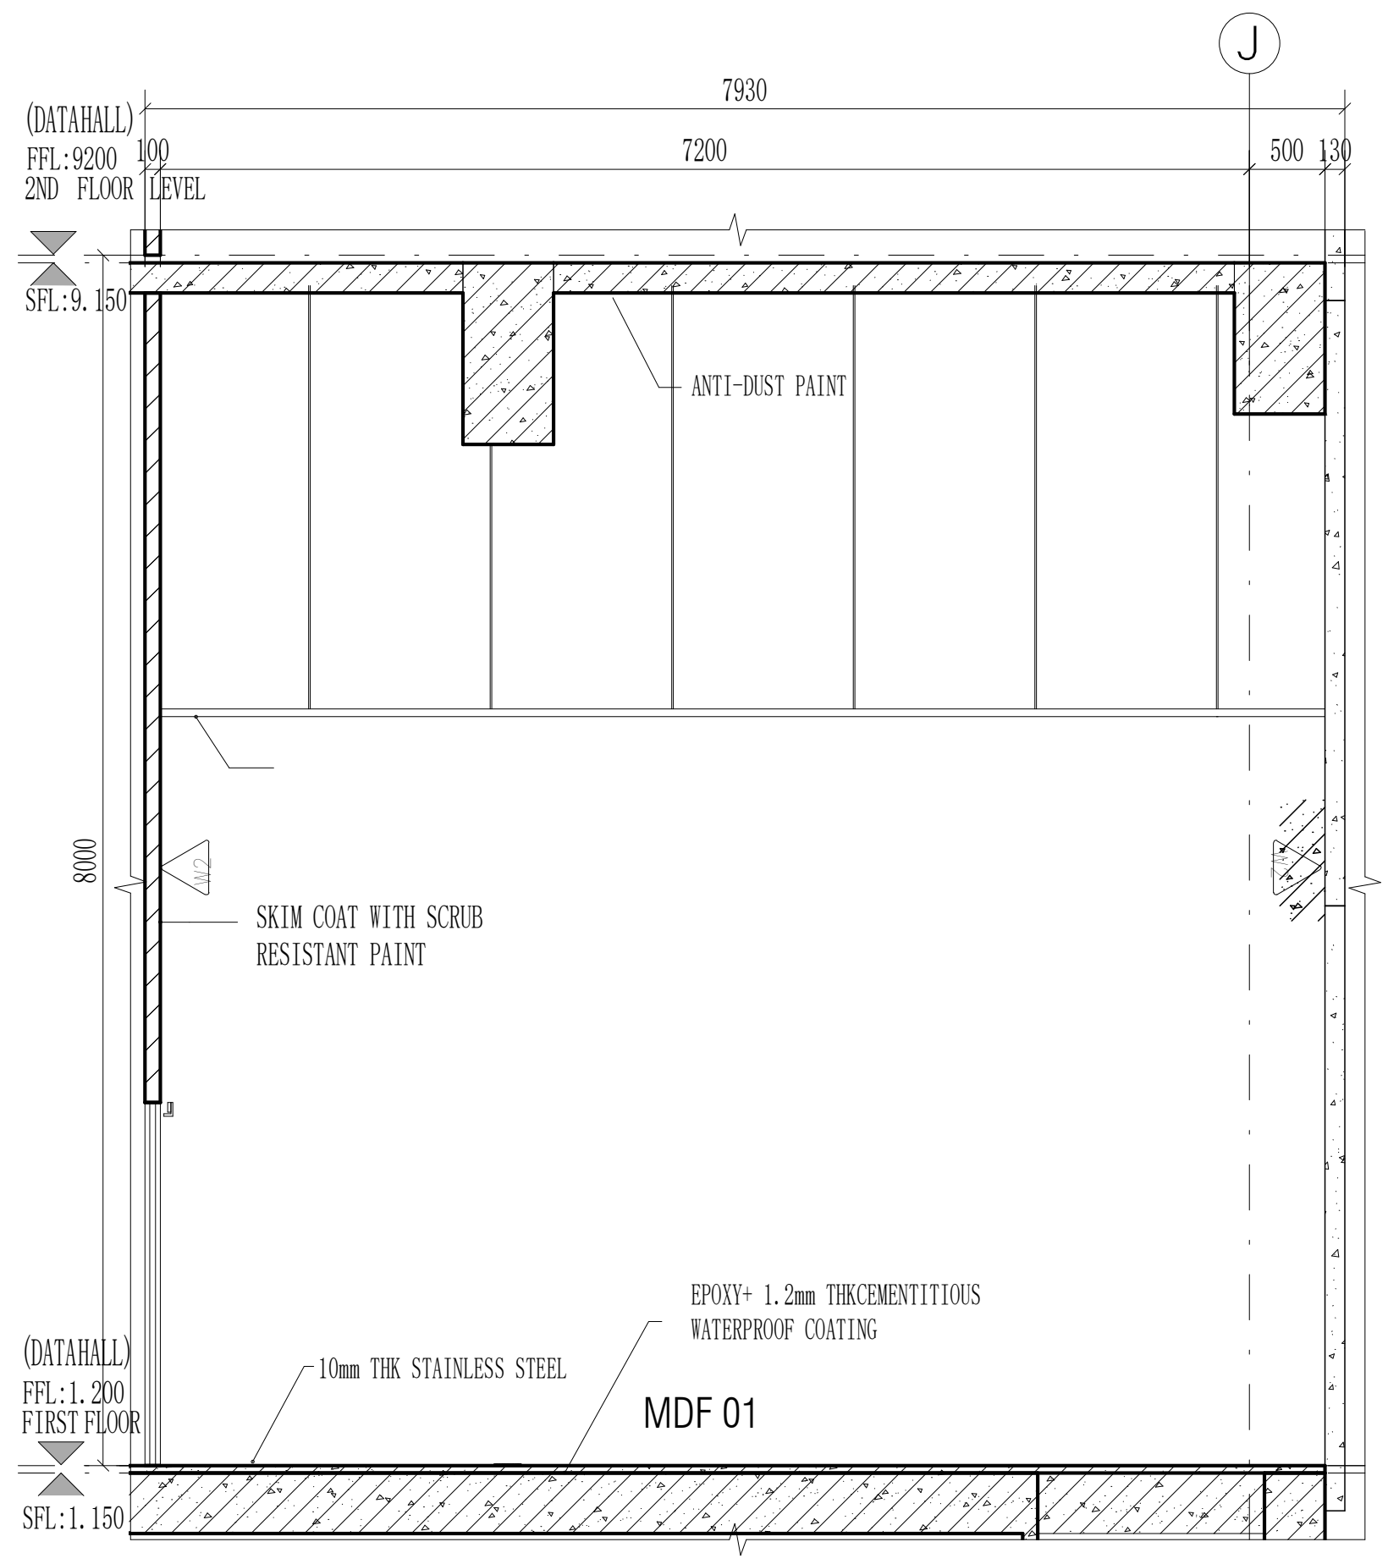
J
7930
7200
500
130
(DATAHALL)
FFL:9200
2ND FLOOR LEVEL
SFL:9.150
8000
ANTI-DUST PAINT
SKIM COAT WITH SCRUB RESISTANT PAINT
EPOXY+ 1.2mm THKCEMENTITIOUS WATERPROOF COATING
(DATAHALL)
FFL:1.200
FIRST FLOOR
SFL:1.150
10mm THK STAINLESS STEEL
MDF 01

MDF 01 SECTION D-D

Scale 1:50

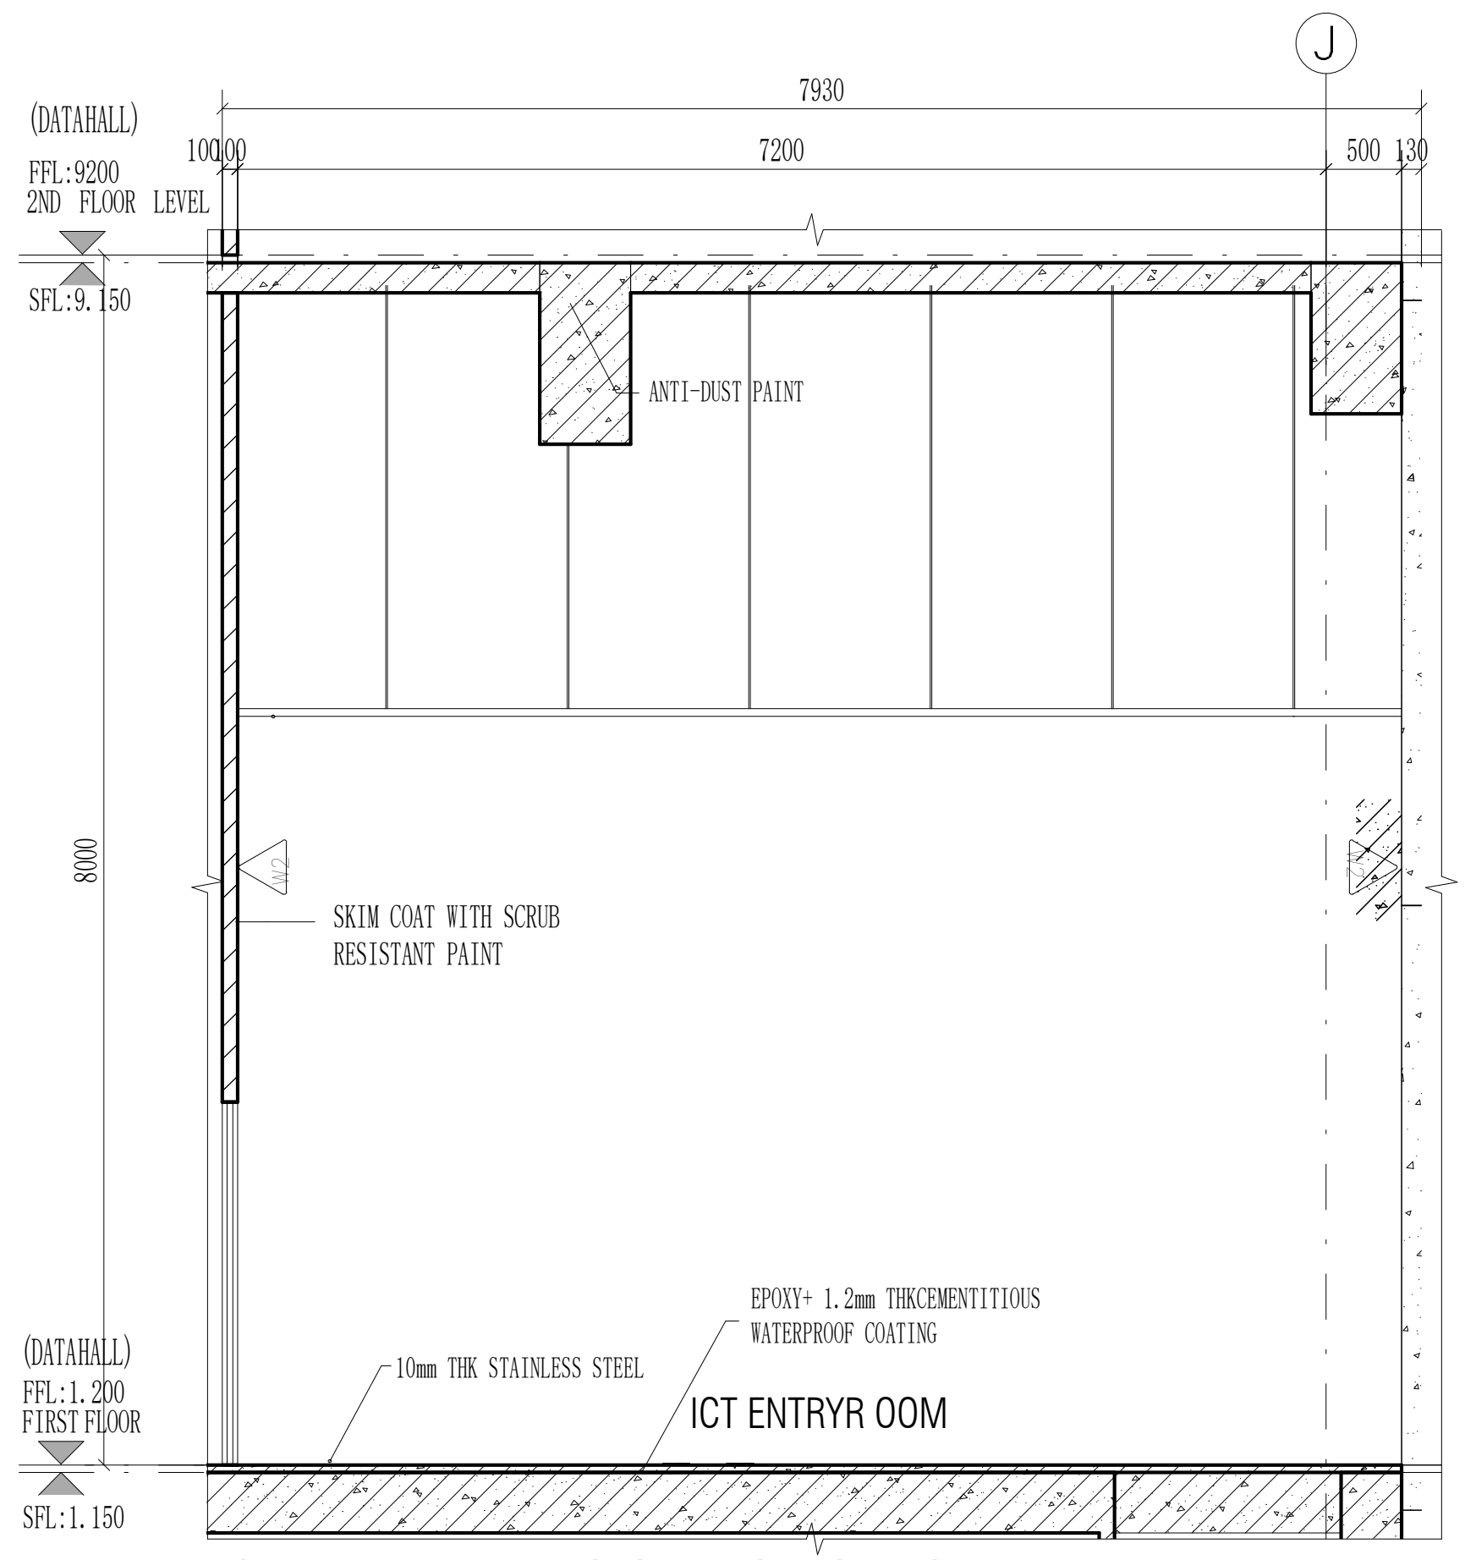
J
7930
100
7200
500
130
(DATAHALL)
FFL:9200
2ND FLOOR LEVEL
SFL:9.150
8000
ANTI-DUST PAINT
SKIM COAT WITH SCRUB RESISTANT PAINT
EPOXY+ 1.2mm THKCEMENTITIOUS WATERPROOF COATING
(DATAHALL)
FFL:1.200
FIRST FLOOR
SFL:1.150
10mm THK STAINLESS STEEL
ICT ENTRYR OOM

ICT ENTRY ROOM SECTION E-E

Scale 1:50

CLIENT :

GULF EDGE DC 01

87 Wireless Road, M Thai Tower 11th. Floor, All Seasons Place, Lumpini,
Pathumwan, Bangkok 10330, Thailand

CONTRACTOR :

华西发展(泰国)有限公司
บริษัท หัวซือ ดีเวลลอปเม้นต์ (ประเทศไทย) จำกัด
HUASHI DEVELOPMENT CO.,LTD
No. 202, Room No. 1403, 14/F, Le Concorde Building,
Ratchadapisek Road, Huaykhwang Sub-District,
Huaykhwang District, Bangkok Metropolitan 10310.

CONSULTANT :

ARbay
บริษัท เอ อาร์ เบย์ จำกัด
ARbay Company Limited
31 st Floor Bangkok Insurance Building
25 South Sathorn road Thungmahamek
Sathorn Bangkok 10120 THAILAND
T +66 (0) 2286 8199
F +66 (0) 2286 2863
info@arbay.co.th

CONSULTANT :

Qbic Engineers & Architects Co.,Ltd.
8 Soi KALONG 4 SANAMBINNAM ROAD,
THASAI SUB-DISTRICT, MUANG NONTHABURI DISTRICT
, NONTHABURI.
Tel 662-950-4374
Fax 662-580-3231
E-Mail : qbic@qbic.co.th, www.qbic.co.th
QBIC ENGINEERS AND ARCHITECTS CO.,LTD.

CONSULTANT :

MITR
MITR TECHNICAL CONSULTANT CO.,LTD.
1168/8 12th FLOOR, LUMPINI TOWER BUILDING,
RAMA IV RD., THUNGMAHAMEK, SATHORN, BANGKOK 10120, THAILAND
TEL : 0-2679-9079-84
FAX : 0-2679-9085 E-mail: mitr_dd@mitr.com

Architect : SIGNATURE
ประกิต พนานุรัตน์ วสถ. 580
ที่อยู่
251/1 ถ.จารุเมือง แขวงรองเมือง เขตปทุมวัน
กรุงเทพมหานคร โทรศัพท์ 02-286-8199

Structural Engineer : SIGNATURE
วิศวกรผู้ออกแบบโครงสร้าง
ณัฐสม สงวนวงษ์ วย 1423
ที่อยู่
2/1 ซ.รามคำแหง 150 ถ.รามคำแหง
แขวง สะพานสูง เขต สะพานสูง กทม. 10240

Structural Inspector : SIGNATURE
วิศวกรผู้ตรวจสอบโครงสร้าง
โกมล จุฑาภัทร วย 964
ที่อยู่
24/18 ซ.นวมินทร์ 129 ถ. นวมินทร์
แขวง นวลจันทร์ เขต บึงกุ่ม กทม. 10230

Electrical Engineer : SIGNATURE
วิศวกรผู้ออกแบบระบบไฟฟ้ากำลัง
นายสุภัทร บูรณวิทย์ วฟก.1265
ที่อยู่
21 ซอยทานสัมฤทธิ์ 13
ตำบลท่าทราย อ.เมืองนนทบุรี จ.นนทบุรี 11000

Mechanical Engineer : SIGNATURE
วิศวกรผู้ออกแบบระบบเครื่องกลและปรับอากาศ
นายประสิทธิ์ เกี้ยวสุนทร วก.1221
ประสิทธิ์
ที่อยู่
44/372 ซอยบางกระดี่ 35/1 แขวงแสมดำ
เขตบางขุนเทียน กทม. 10150

Sanitary Engineer : SIGNATURE
วิศวกรผู้ออกแบบระบบสุขาภิบาล และดับเพลิง
นายทศวรรษ สนั่นฤทธิ์ วส. 215
ทศวรรษ
ที่อยู่
บ้านเลขที่ 99/107 หมู่ที่ 3 ต.ศีรษะจรเข้น้อย
อ.บางเสาธง จ.สมุทรปราการ 10540

ISSUE/REVISION

REV.	DESCRIPTION	DATE
A	90% DEVELOPED	09/05/2026

PROJECT NAME :
GEDC 01
LOCATION:
Nikhom Phattana district, Rayong ,industrial estate,CPGC

BUILDING :
MAIN BUILDING

90% DEVELOPED

TITLE :
ROOM
DETAIL-1F-FCC、SOC、MDF01、ICT

JOB NO.	SCALE 1 : 50
DRAWN ZYY	REF.
CHECKED LJC	DWG. NO. MPK01A-90-A-RD-111
APPROVED LXD	
DATE 2026.05.09	

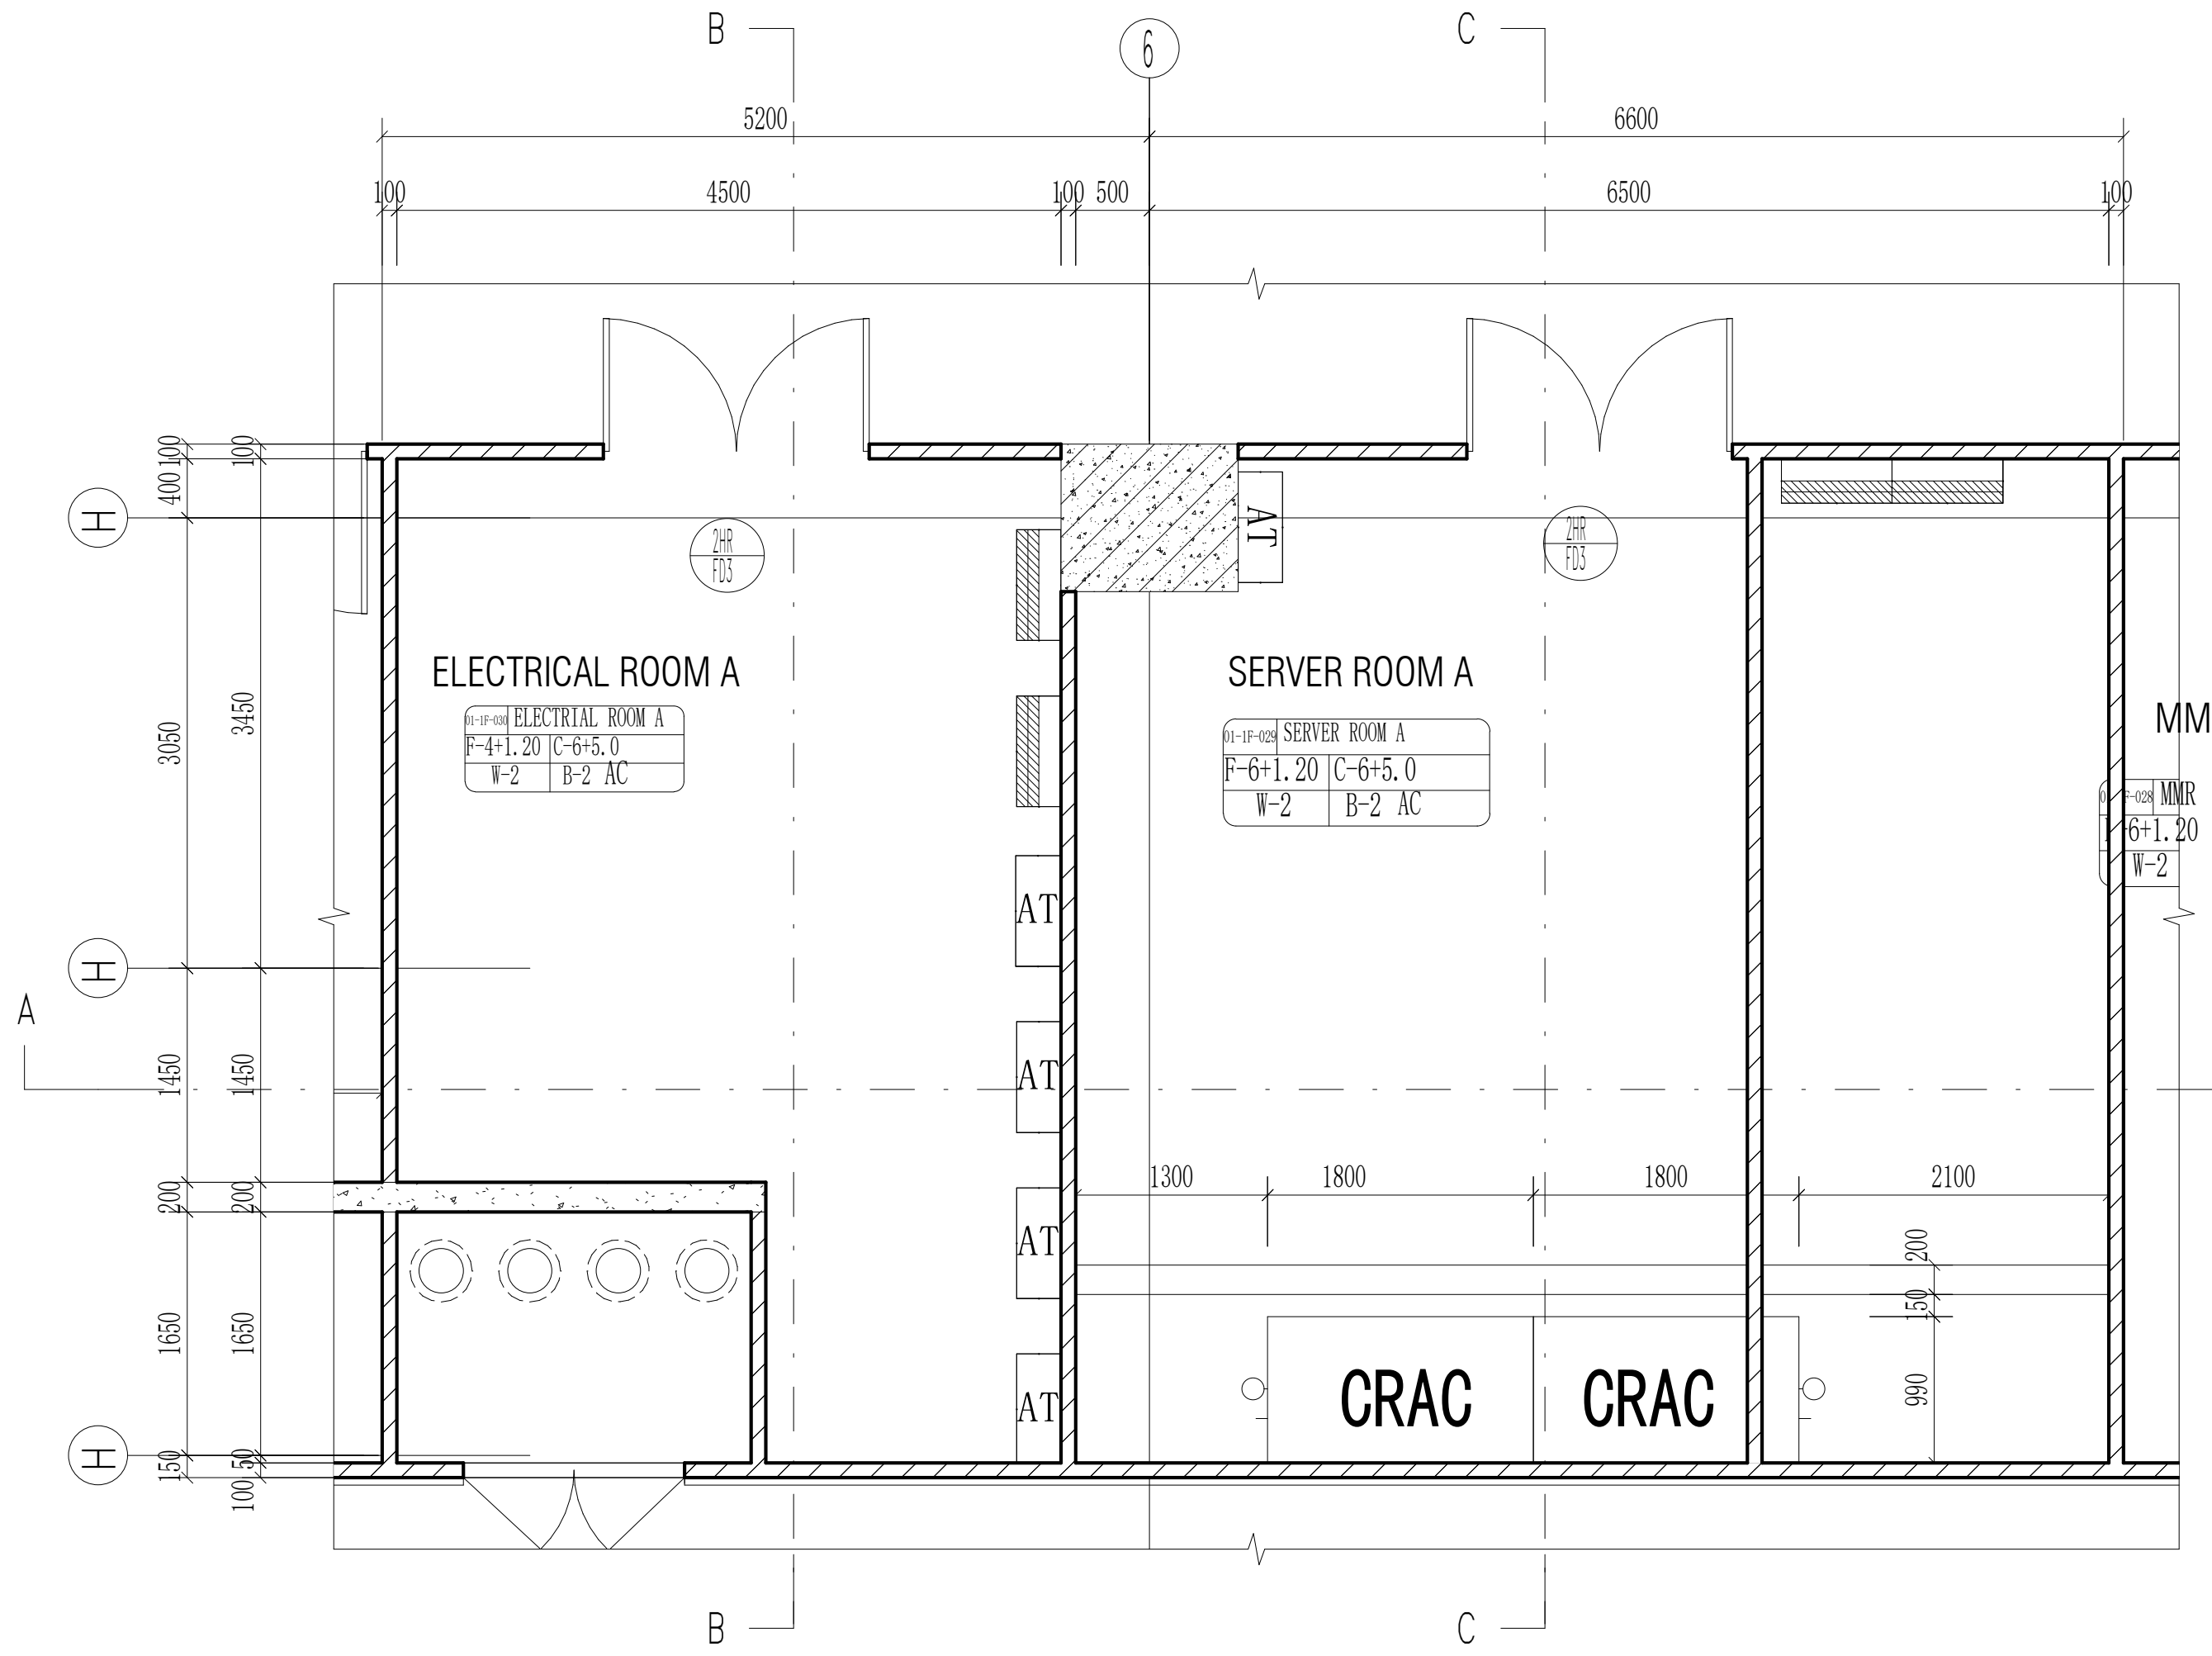
B
6
C
5200
6600
100
4500
100 500
6500
100
ELECTRICAL ROOM A
01-1F-030 ELECTRIAL ROOM A
F-4+1.20 C-6+5.0
W-2 B-2 AC
SERVER ROOM A
01-1F-029 SERVER ROOM A
F-6+1.20 C-6+5.0
W-2 B-2 AC
MMR A
MMR
F-6+1.20
W-2
2HR FD3
AT
H
A
3050
3450
1450
200
1650
150
1300
1800
1800
2100
990
CRAC
CRAC

ELECTRICAL ROOM A、SERVER ROOM A PLAN
Scale 1:50

THE "SFL" MARKED IN THE DRAWING REFERS TO
THE STRUCTURAL FLOOR LEVEL, WHILE THE
FINISHED FLOOR LEVEL (FFL) IS DETERMINED BASED
ON FLOOR FINISHES.

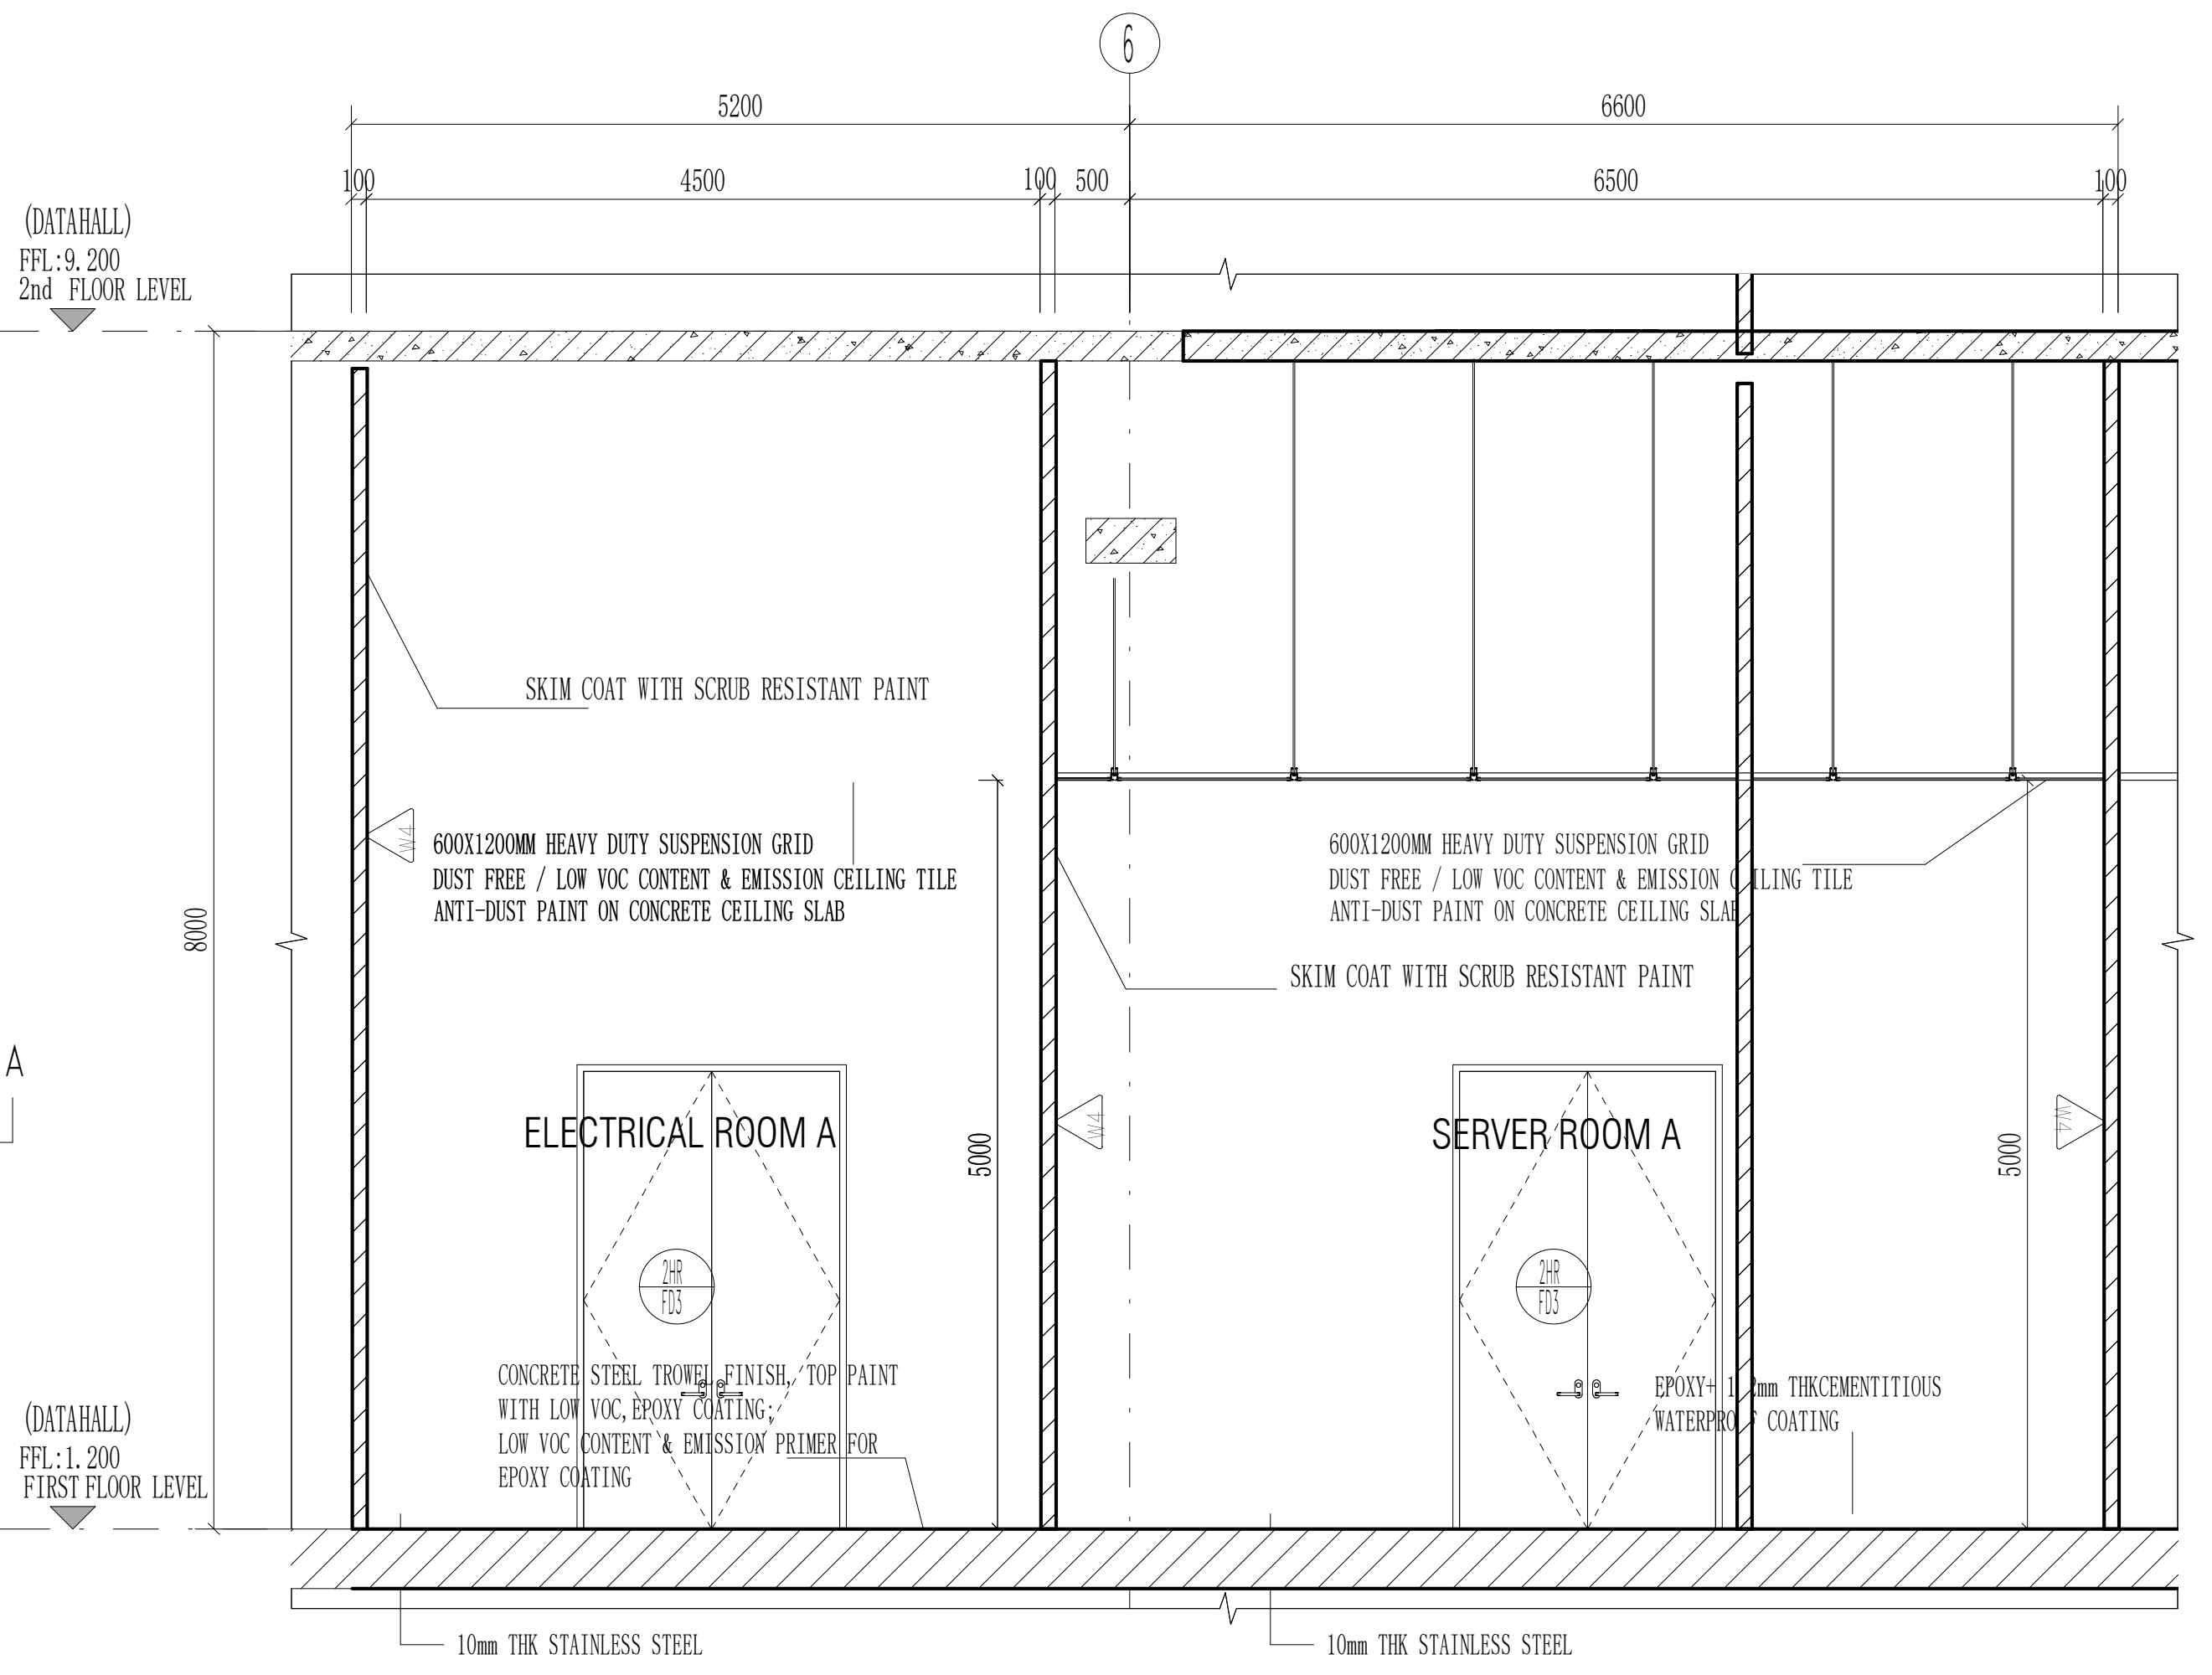
6
5200
6600
100
4500
100 500
6500
100
(DATAHALL)
FFL:9.200
2nd FLOOR LEVEL
(DATAHALL)
FFL:1.200
FIRST FLOOR LEVEL
8000
5000
SKIM COAT WITH SCRUB RESISTANT PAINT
600X1200MM HEAVY DUTY SUSPENSION GRID
DUST FREE / LOW VOC CONTENT & EMISSION CEILING TILE
ANTI-DUST PAINT ON CONCRETE CEILING SLAB
ELECTRICAL ROOM A
SERVER ROOM A
2HR FD3
CONCRETE STEEL TROWEL FINISH, TOP PAINT
WITH LOW VOC,EPOXY COATING;
LOW VOC CONTENT & EMISSION PRIMER FOR
EPOXY COATING
EPOXY+ 1.2mm THKCEMENTITIOUS
WATERPROOF COATING
10mm THK STAINLESS STEEL

ELECTRICAL ROOM A、SERVER ROOM A SECTION A-A
Scale 1:50

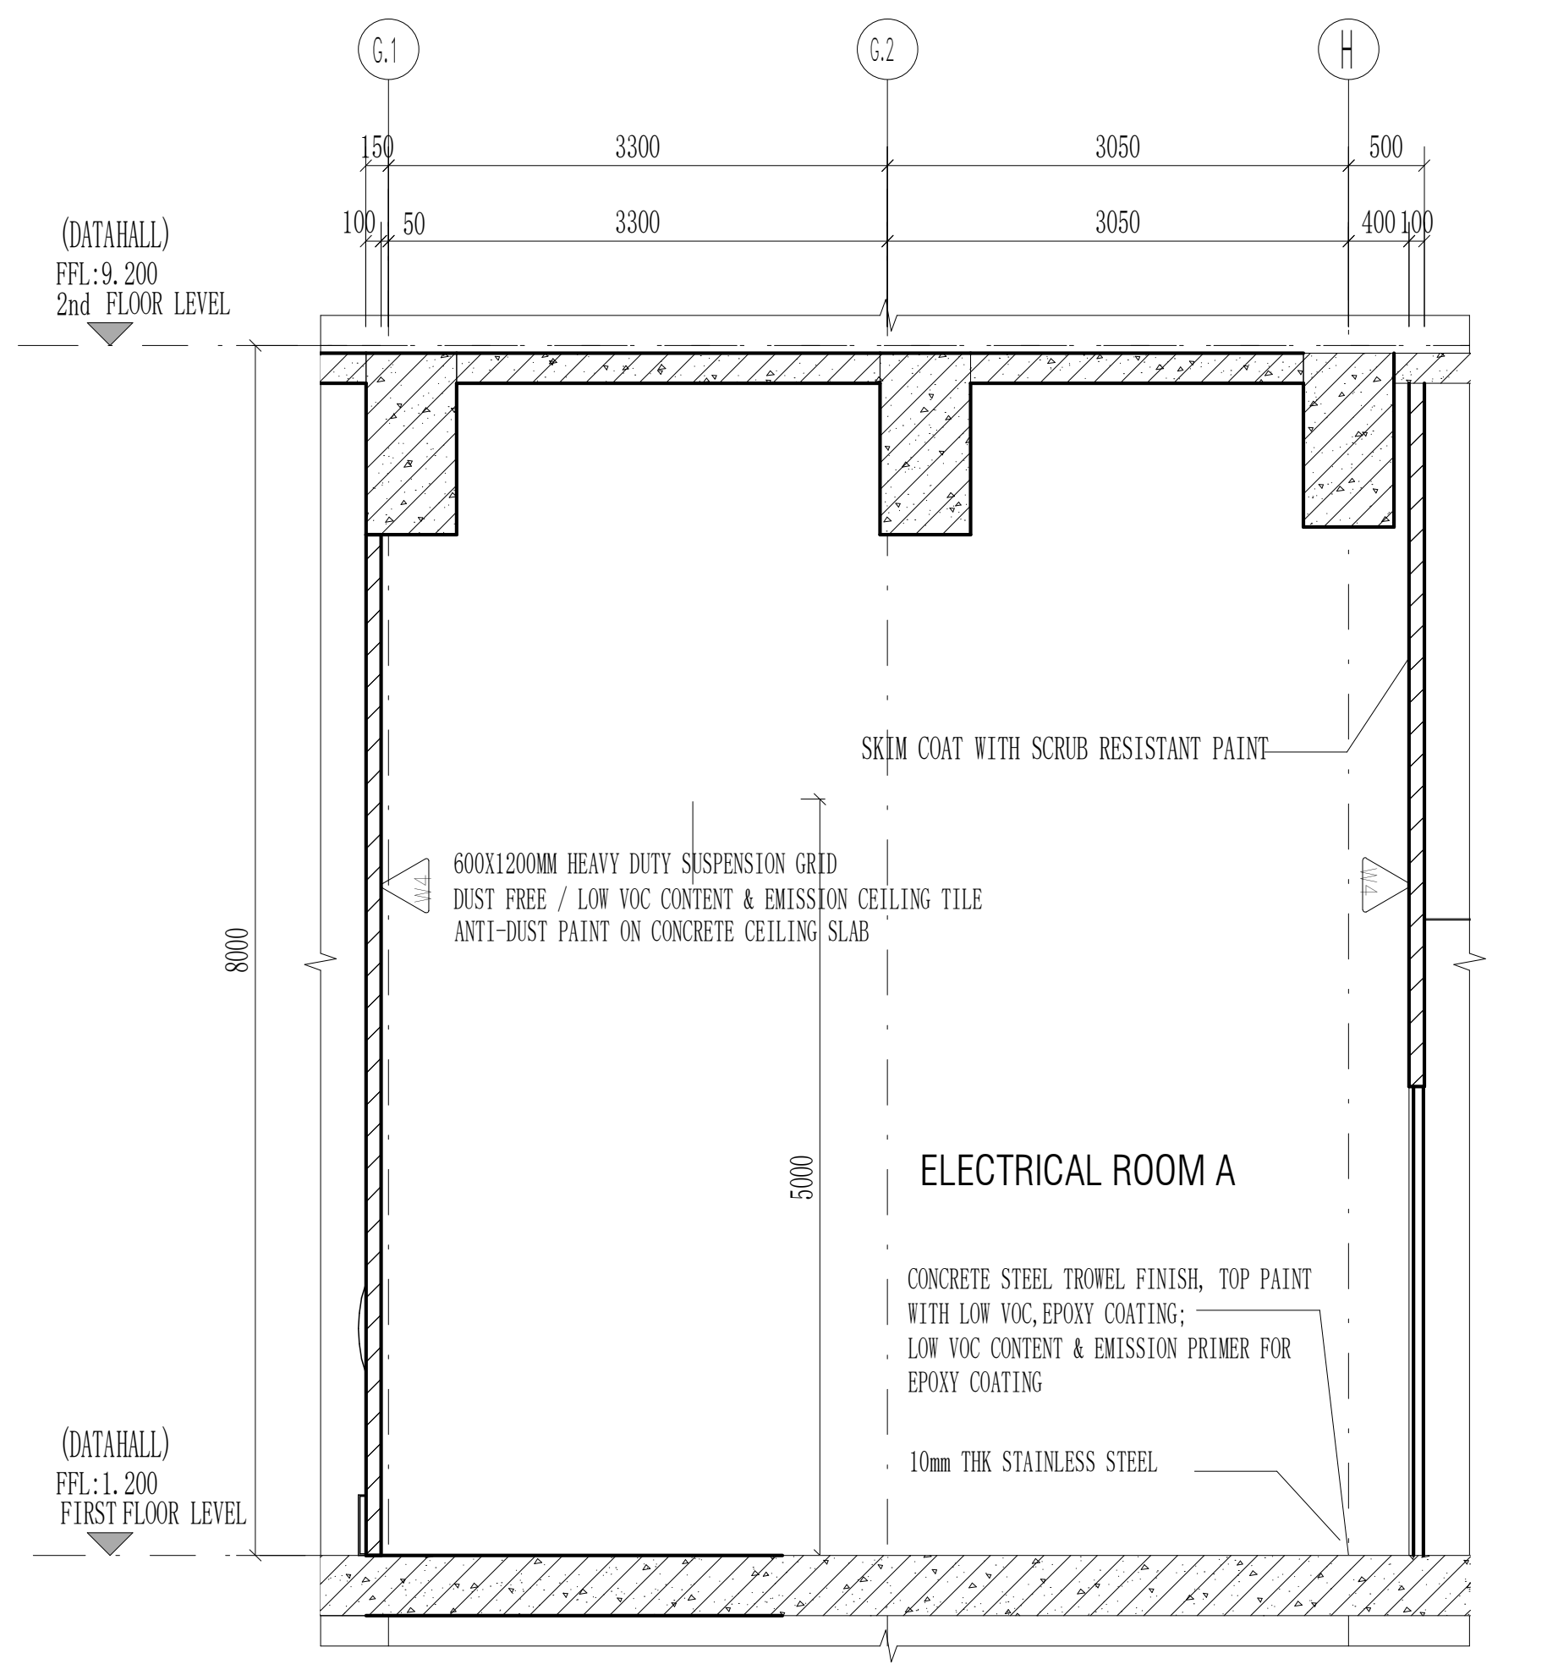
G.1
G.2
H
150
3300
3050
500
100
50
400 100
(DATAHALL)
FFL:9.200
2nd FLOOR LEVEL
(DATAHALL)
FFL:1.200
FIRST FLOOR LEVEL
8000
5000
SKIM COAT WITH SCRUB RESISTANT PAINT
600X1200MM HEAVY DUTY SUSPENSION GRID
DUST FREE / LOW VOC CONTENT & EMISSION CEILING TILE
ANTI-DUST PAINT ON CONCRETE CEILING SLAB
ELECTRICAL ROOM A
CONCRETE STEEL TROWEL FINISH, TOP PAINT
WITH LOW VOC,EPOXY COATING;
LOW VOC CONTENT & EMISSION PRIMER FOR
EPOXY COATING
10mm THK STAINLESS STEEL

ELECTRICAL ROOM A SECTION B-B
Scale 1:50

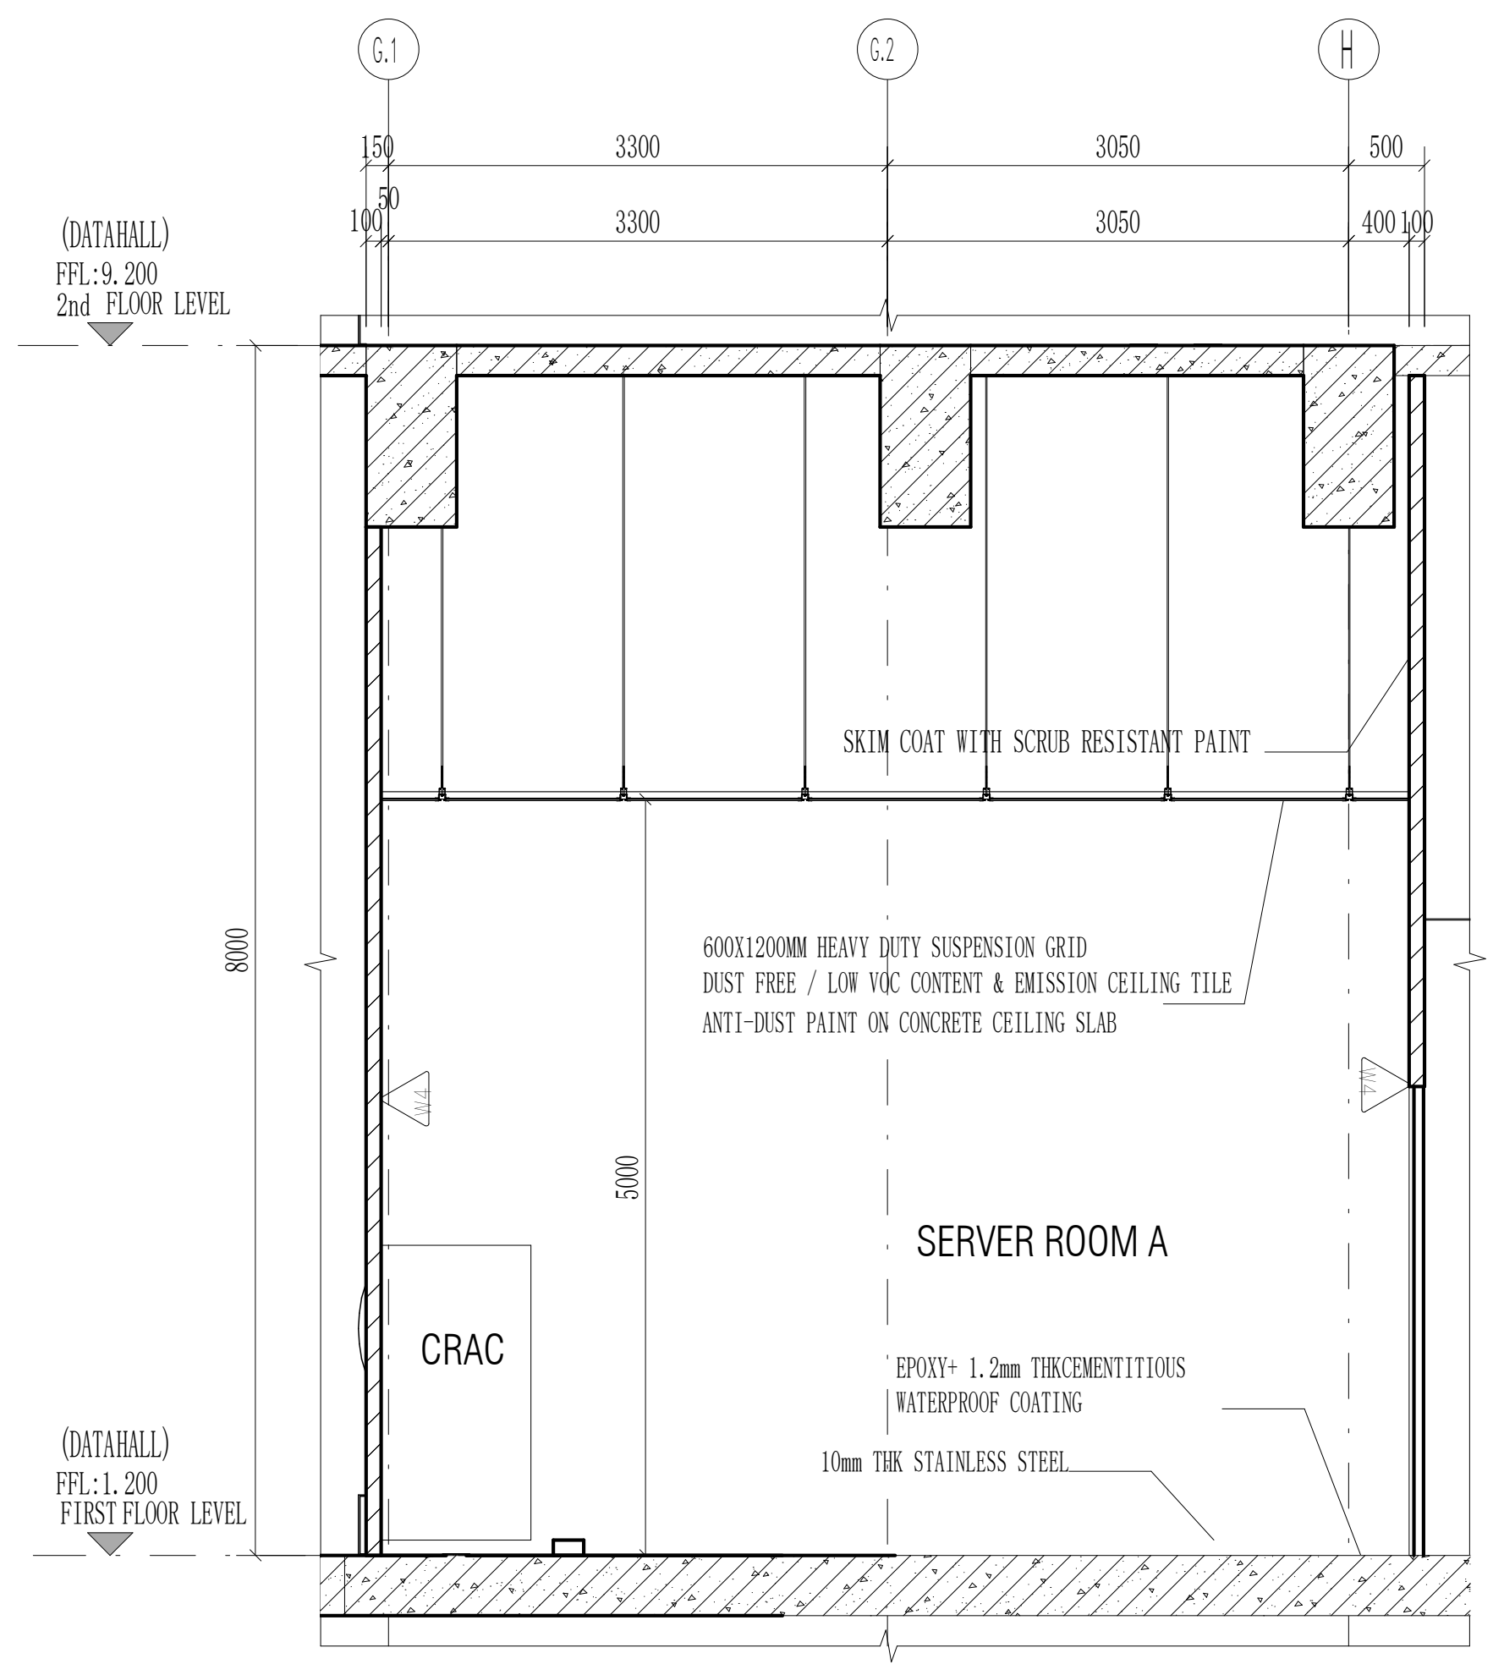
G.1
G.2
H
150
3300
3050
500
100
50
400 100
(DATAHALL)
FFL:9.200
2nd FLOOR LEVEL
(DATAHALL)
FFL:1.200
FIRST FLOOR LEVEL
8000
5000
SKIM COAT WITH SCRUB RESISTANT PAINT
600X1200MM HEAVY DUTY SUSPENSION GRID
DUST FREE / LOW VOC CONTENT & EMISSION CEILING TILE
ANTI-DUST PAINT ON CONCRETE CEILING SLAB
CRAC
SERVER ROOM A
EPOXY+ 1.2mm THKCEMENTITIOUS
WATERPROOF COATING
10mm THK STAINLESS STEEL

SERVER ROOM A SECTION C-C
Scale 1:50

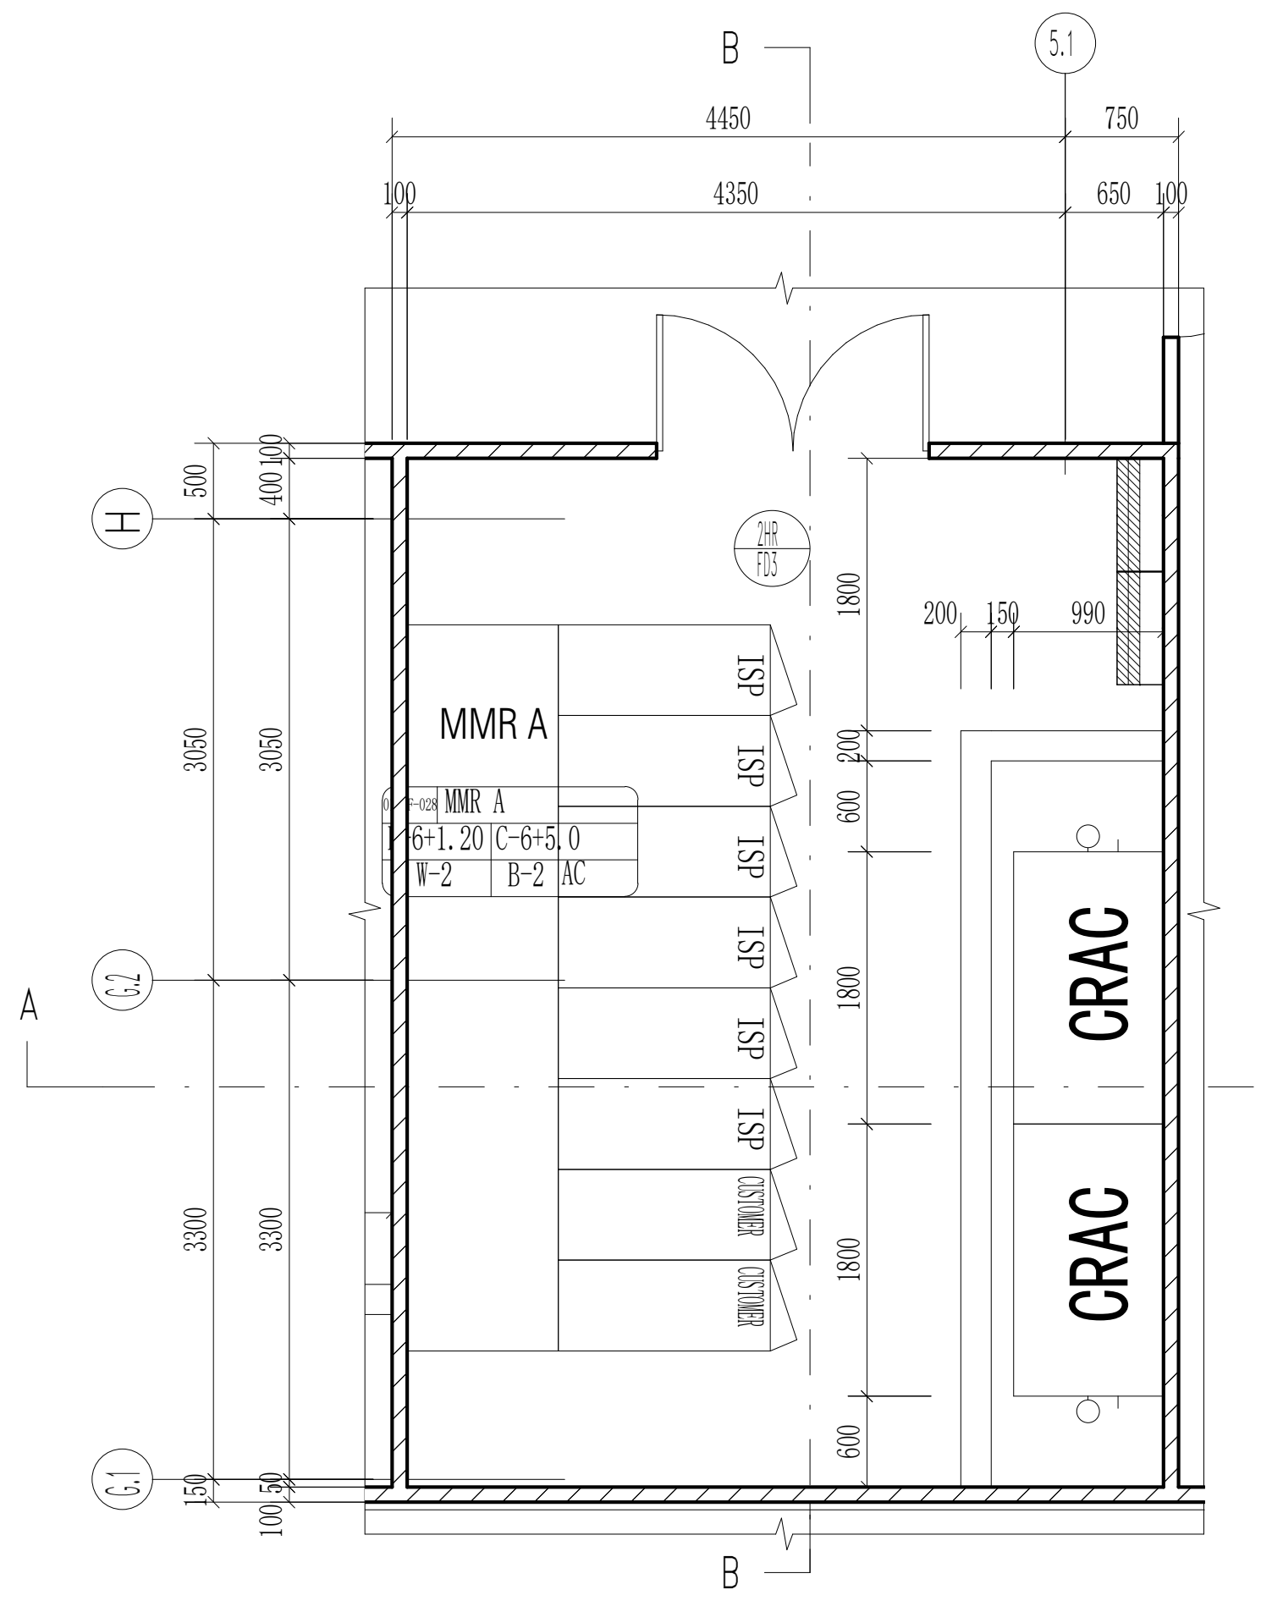
B
5.1
4450
750
100
4350
650
100
H
G.2
G.1
A
500
400
3050
3300
150
MMR A
MMR A
6+1.20 C-6+5.0
W-2 B-2 AC
2HR FD3
ISP
CUSTOMER
1800
200
150
990
600
CRAC
CRAC

MMR A PLAN
Scale 1:50

THE "SFL" MARKED IN THE DRAWING REFERS TO
THE STRUCTURAL FLOOR LEVEL, WHILE THE
FINISHED FLOOR LEVEL (FFL) IS DETERMINED BASED
ON FLOOR FINISHES.

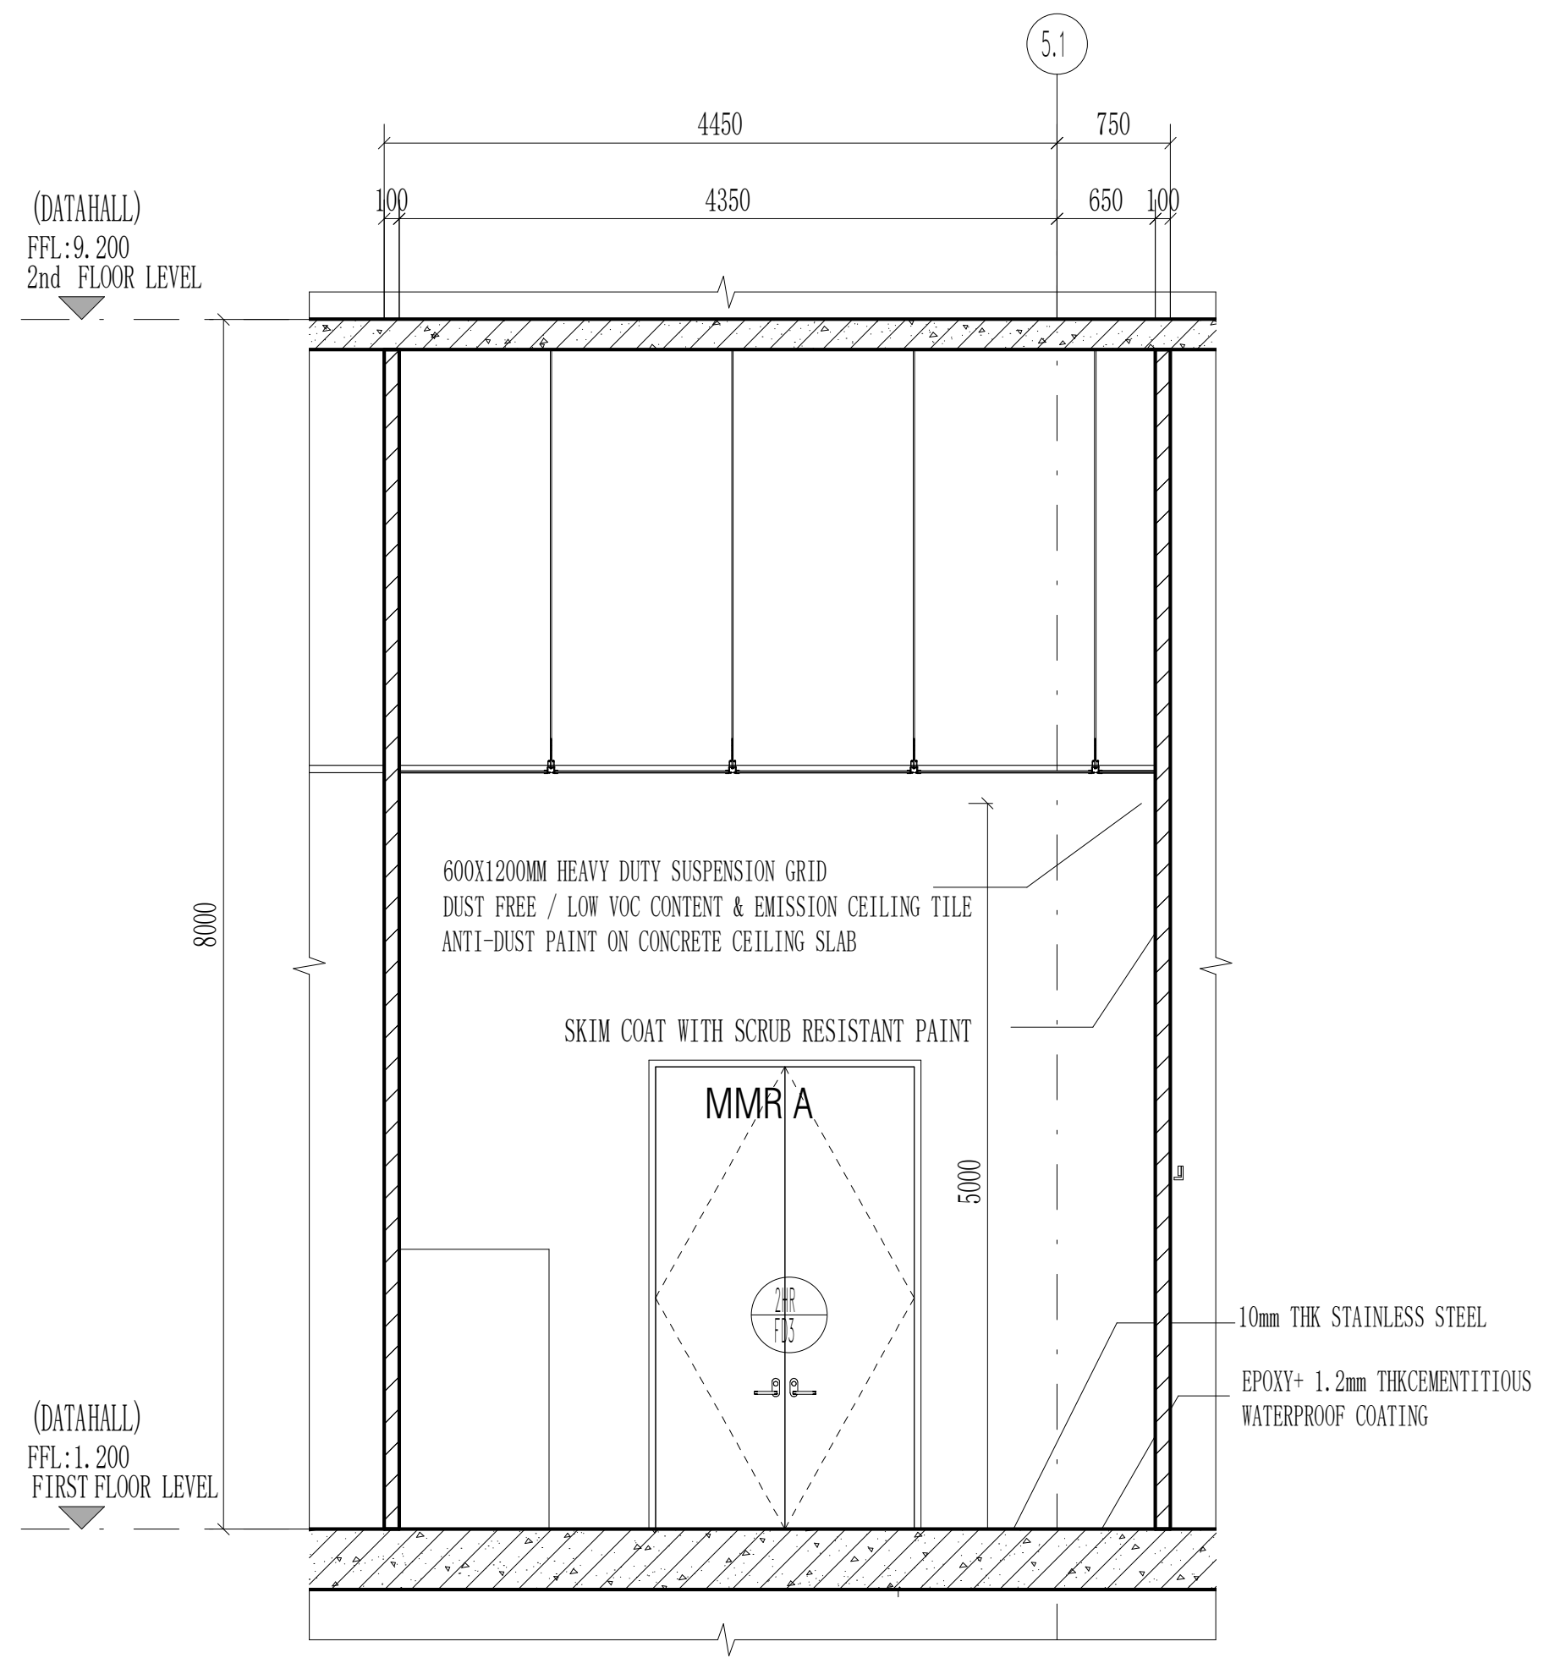
5.1
4450
750
100
4350
650
100
(DATAHALL)
FFL:9.200
2nd FLOOR LEVEL
(DATAHALL)
FFL:1.200
FIRST FLOOR LEVEL
8000
5000
600X1200MM HEAVY DUTY SUSPENSION GRID
DUST FREE / LOW VOC CONTENT & EMISSION CEILING TILE
ANTI-DUST PAINT ON CONCRETE CEILING SLAB
SKIM COAT WITH SCRUB RESISTANT PAINT
MMR A
2HR FD3
10mm THK STAINLESS STEEL
EPOXY+ 1.2mm THKCEMENTITIOUS
WATERPROOF COATING

MMR A SECTION A-A
Scale 1:50

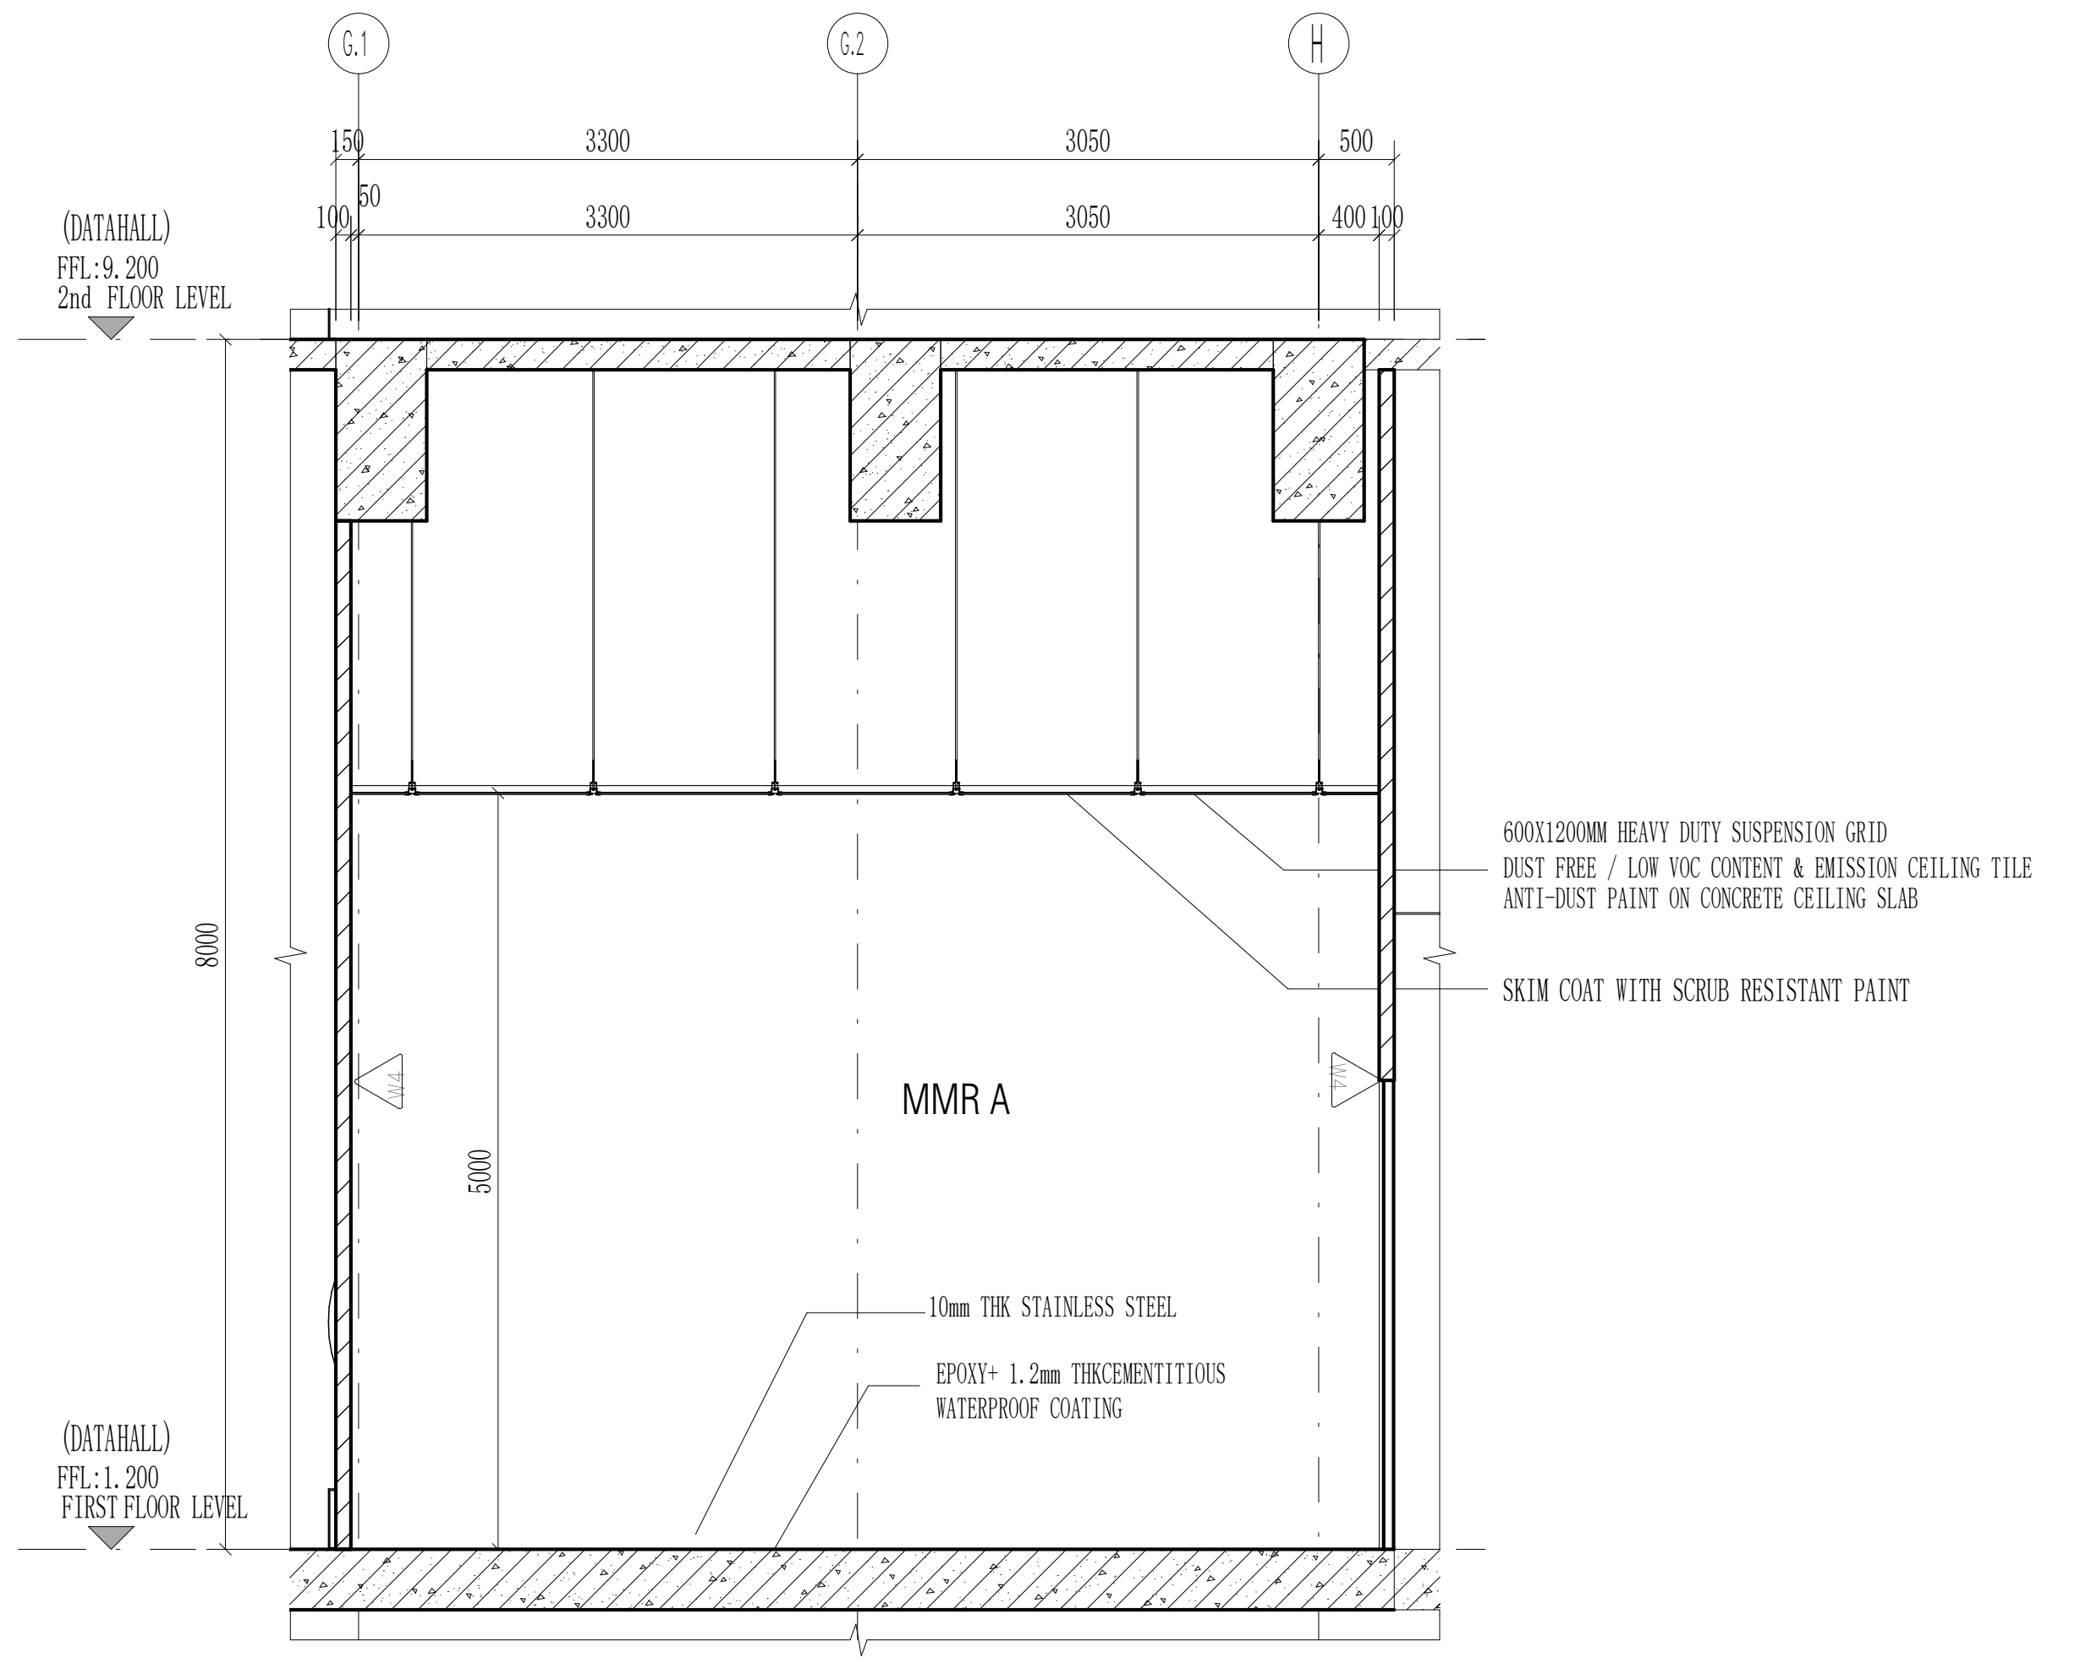
G.1
G.2
H
150
3300
3050
500
100
50
400 100
(DATAHALL)
FFL:9.200
2nd FLOOR LEVEL
(DATAHALL)
FFL:1.200
FIRST FLOOR LEVEL
8000
5000
600X1200MM HEAVY DUTY SUSPENSION GRID
DUST FREE / LOW VOC CONTENT & EMISSION CEILING TILE
ANTI-DUST PAINT ON CONCRETE CEILING SLAB
SKIM COAT WITH SCRUB RESISTANT PAINT
MMR A
10mm THK STAINLESS STEEL
EPOXY+ 1.2mm THKCEMENTITIOUS
WATERPROOF COATING

MMR A SECTION B-B
Scale 1:50

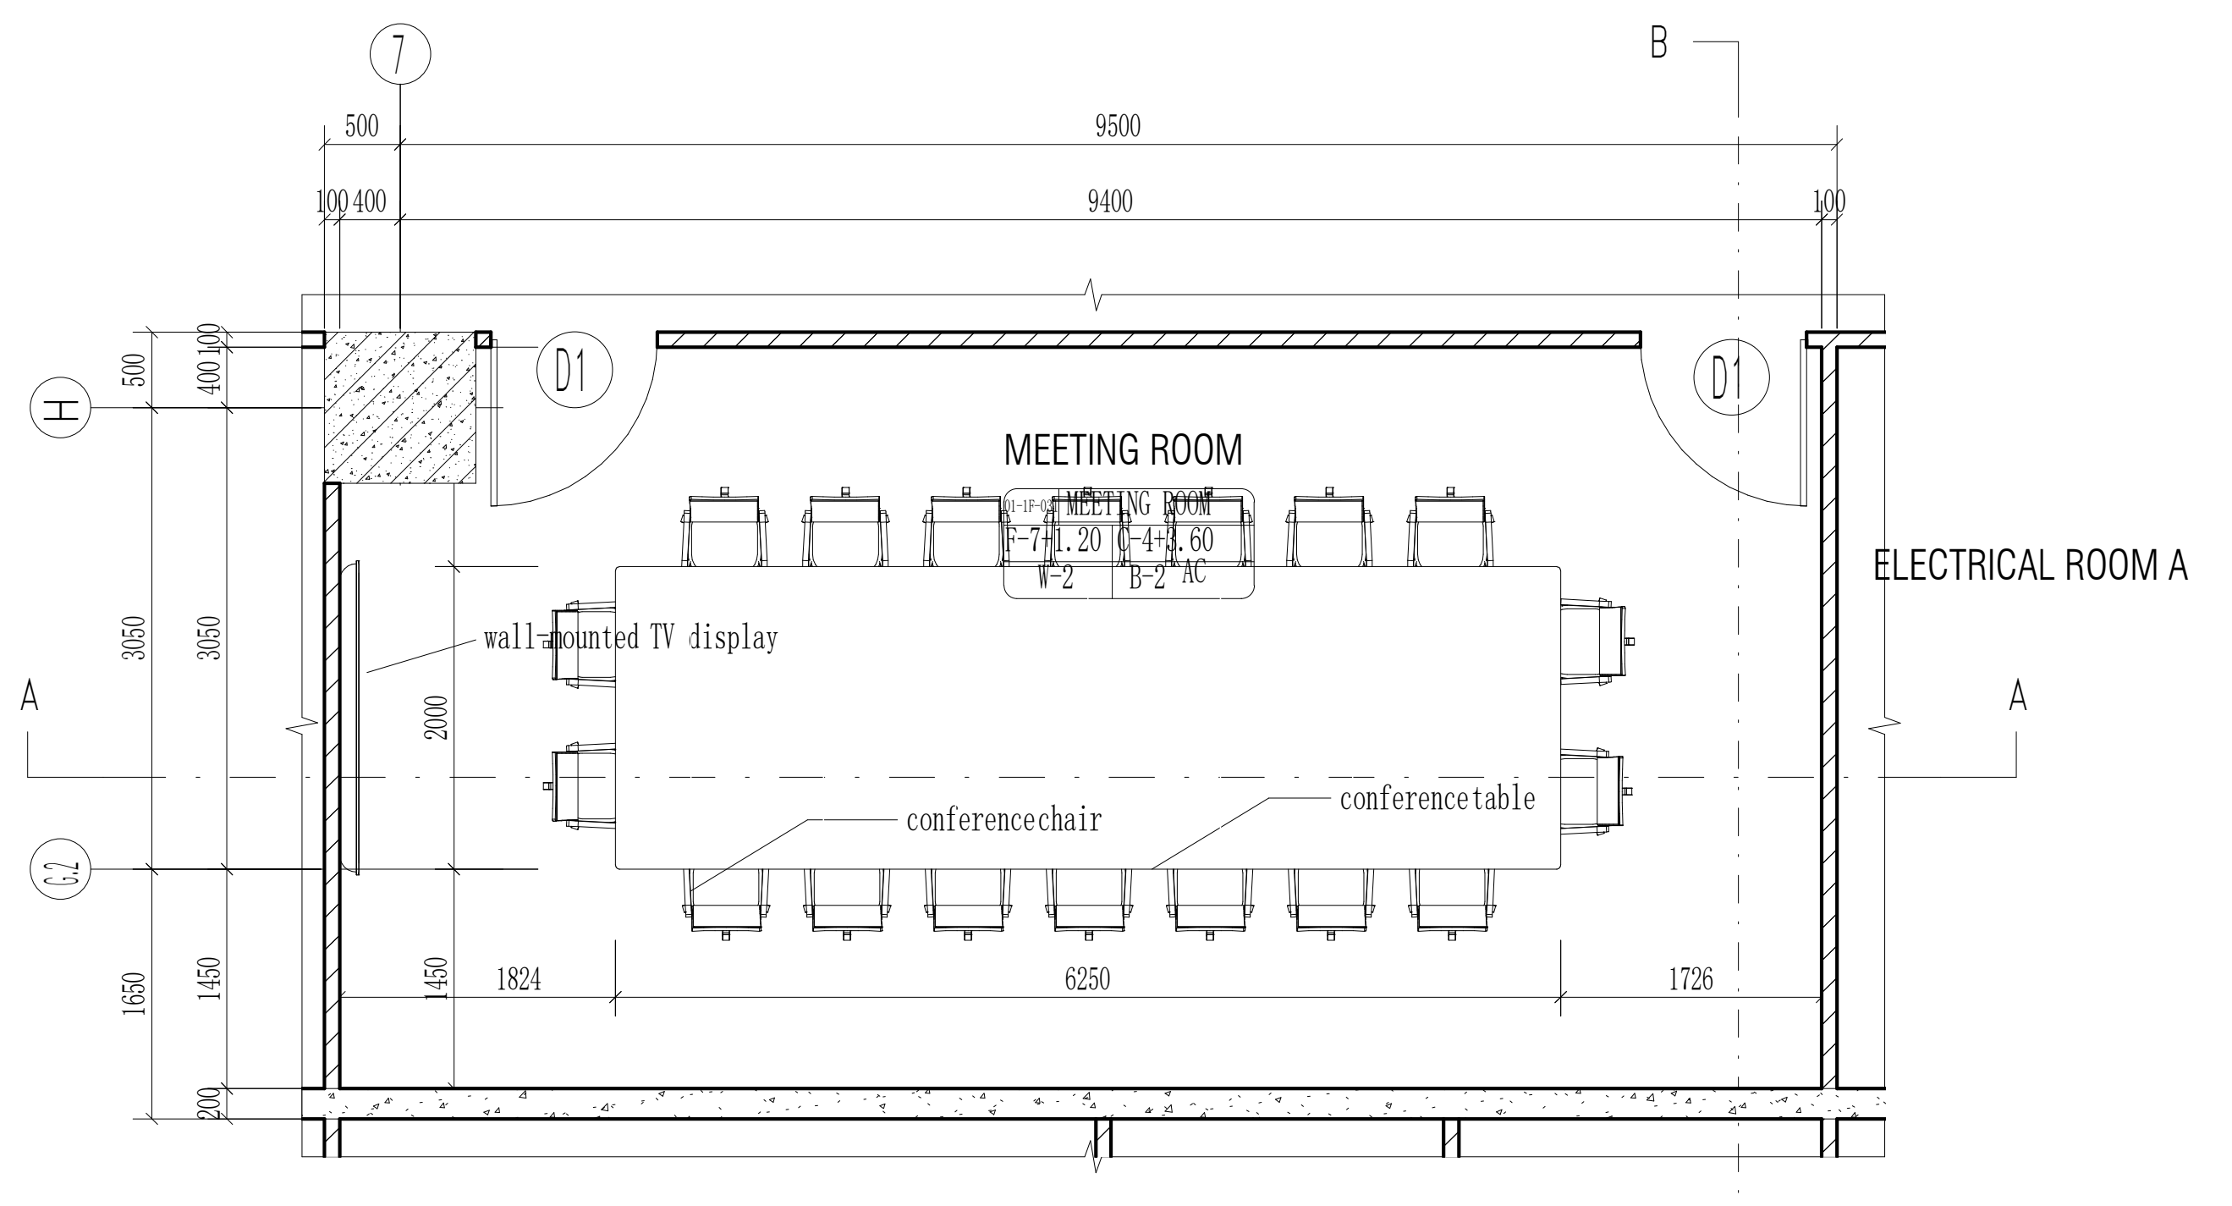
7
B
500
9500
100 400
9400
100
H
G.2
A
D1
D1
MEETING ROOM
MEETING ROOM
F-7+1.20 C-4+3.60
W-2 B-2 AC
ELECTRICAL ROOM A
wall-mounted TV display
conferencechair
conferencetable
3050
1650
1450
2000
200
1824
6250
1726

MEETING ROOM PLAN
Scale 1:50

THE "SFL" MARKED IN THE DRAWING REFERS TO
THE STRUCTURAL FLOOR LEVEL, WHILE THE
FINISHED FLOOR LEVEL (FFL) IS DETERMINED BASED
ON FLOOR FINISHES.

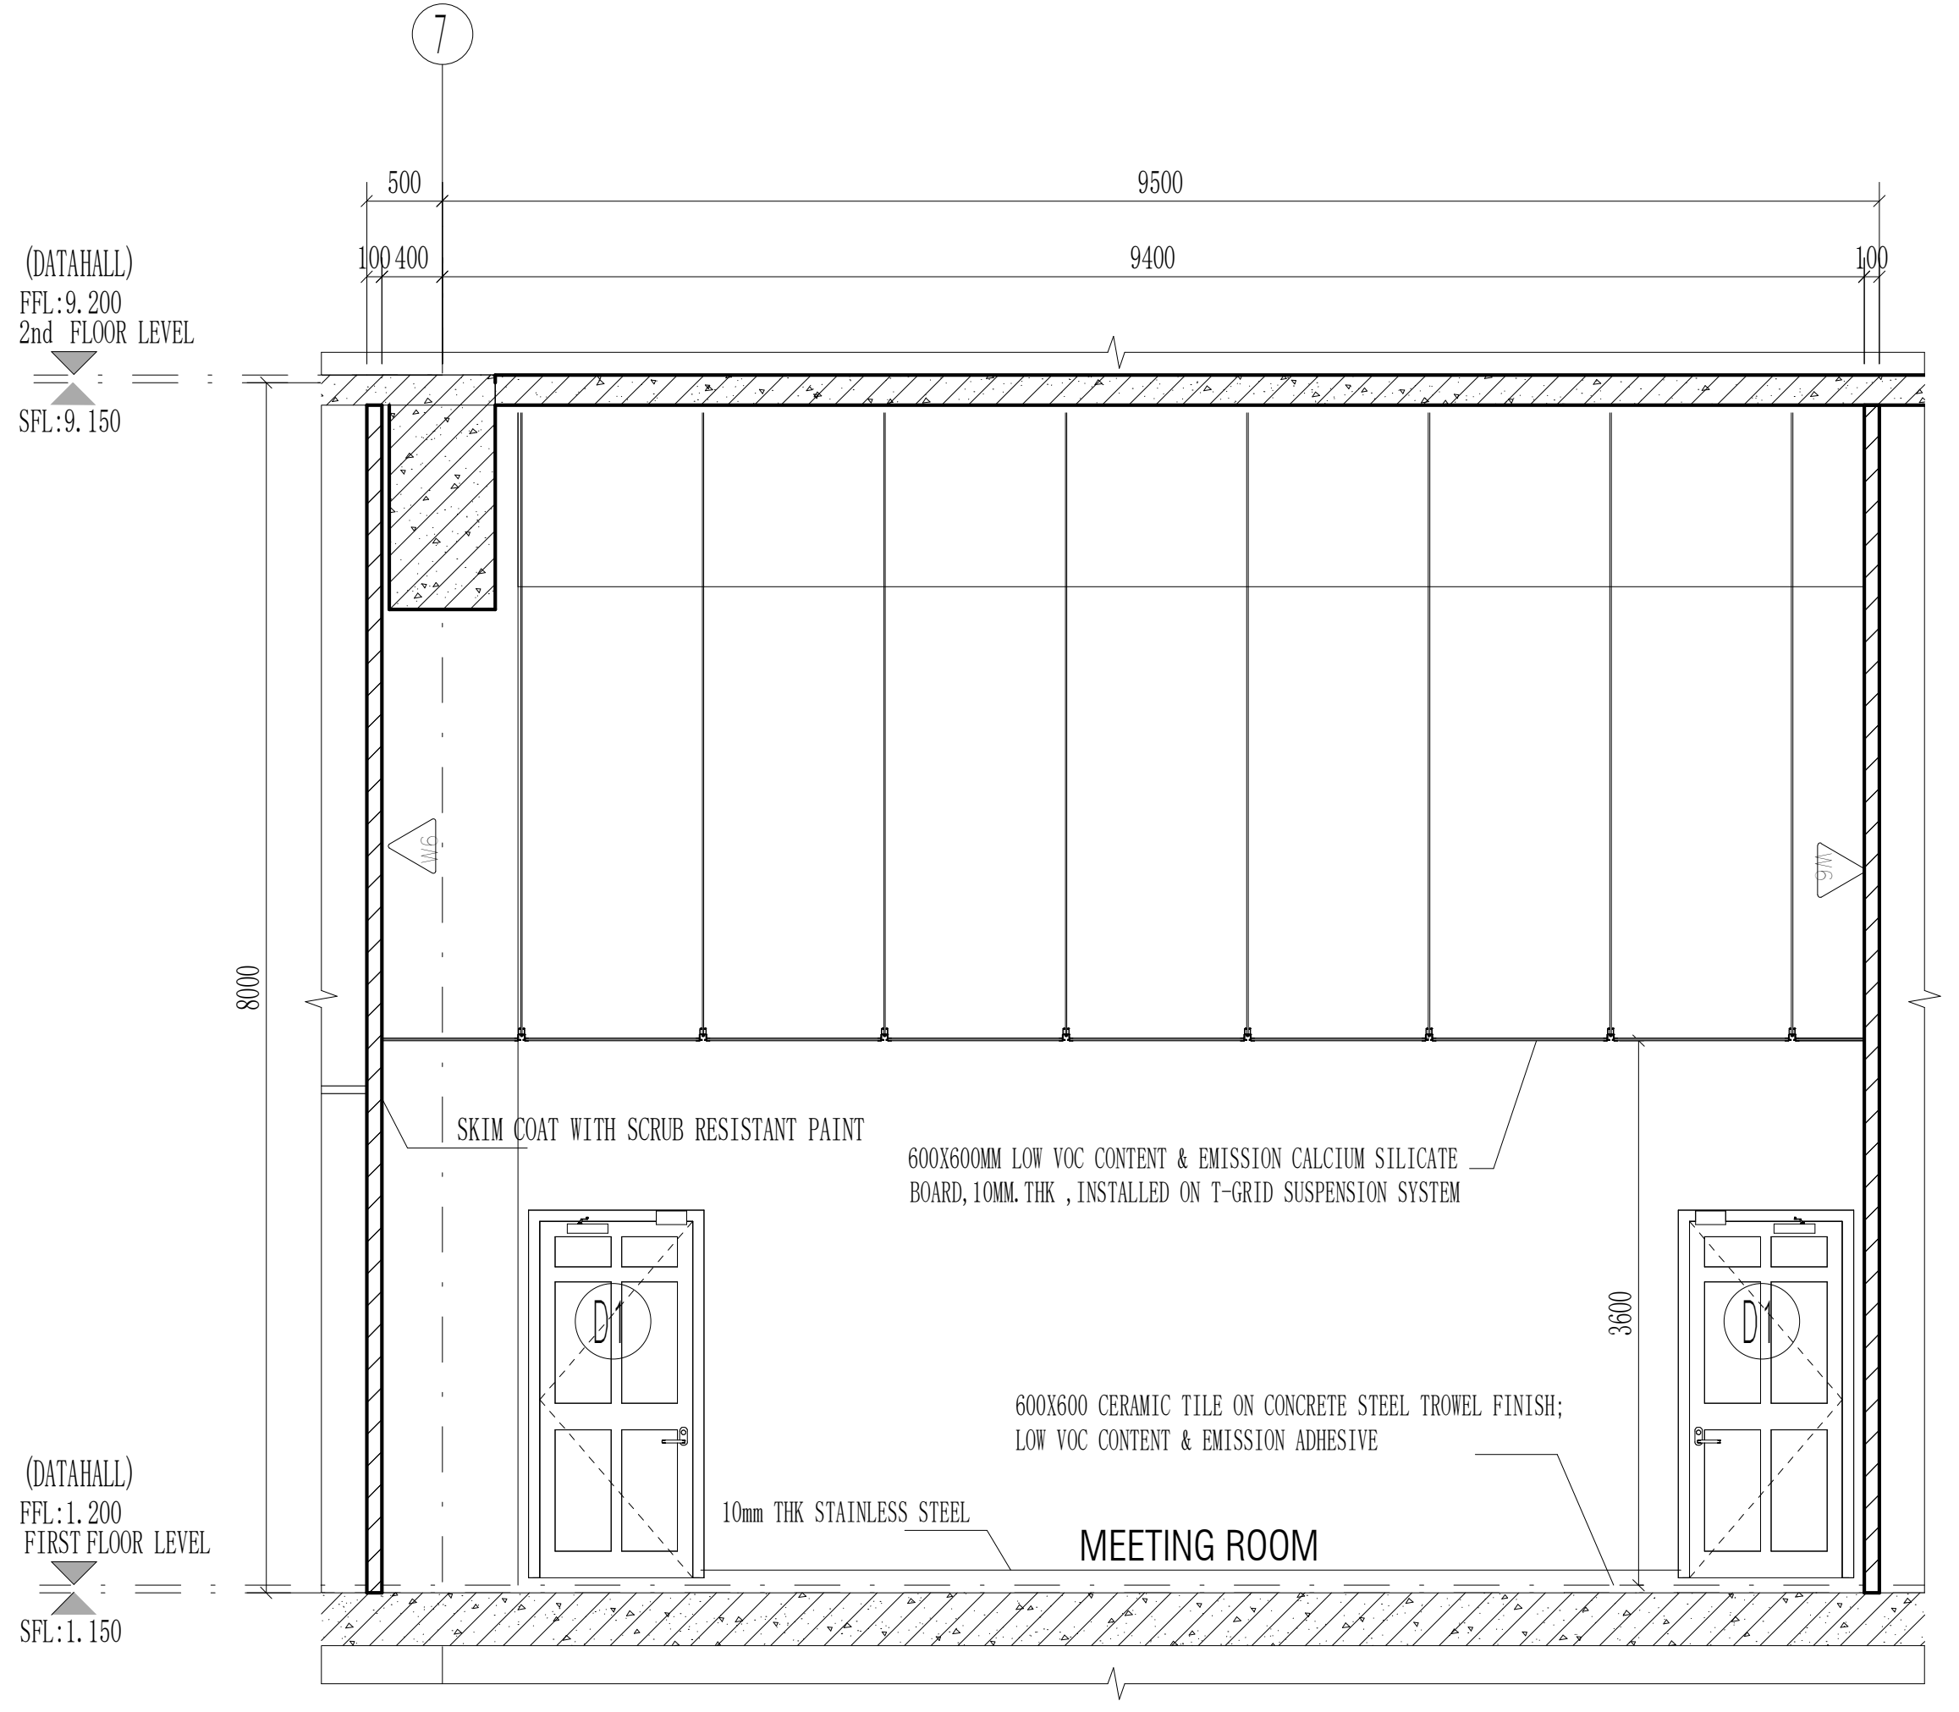
7
500
9500
100 400
9400
100
(DATAHALL)
FFL:9.200
2nd FLOOR LEVEL
SFL:9.150
(DATAHALL)
FFL:1.200
FIRST FLOOR LEVEL
SFL:1.150
8000
3600
SKIM COAT WITH SCRUB RESISTANT PAINT
600X600MM LOW VOC CONTENT & EMISSION CALCIUM SILICATE
BOARD,10MM.THK ,INSTALLED ON T-GRID SUSPENSION SYSTEM
D1
D1
600X600 CERAMIC TILE ON CONCRETE STEEL TROWEL FINISH;
LOW VOC CONTENT & EMISSION ADHESIVE
10mm THK STAINLESS STEEL
MEETING ROOM

MEETING ROOM SECTION A-A
Scale 1:50

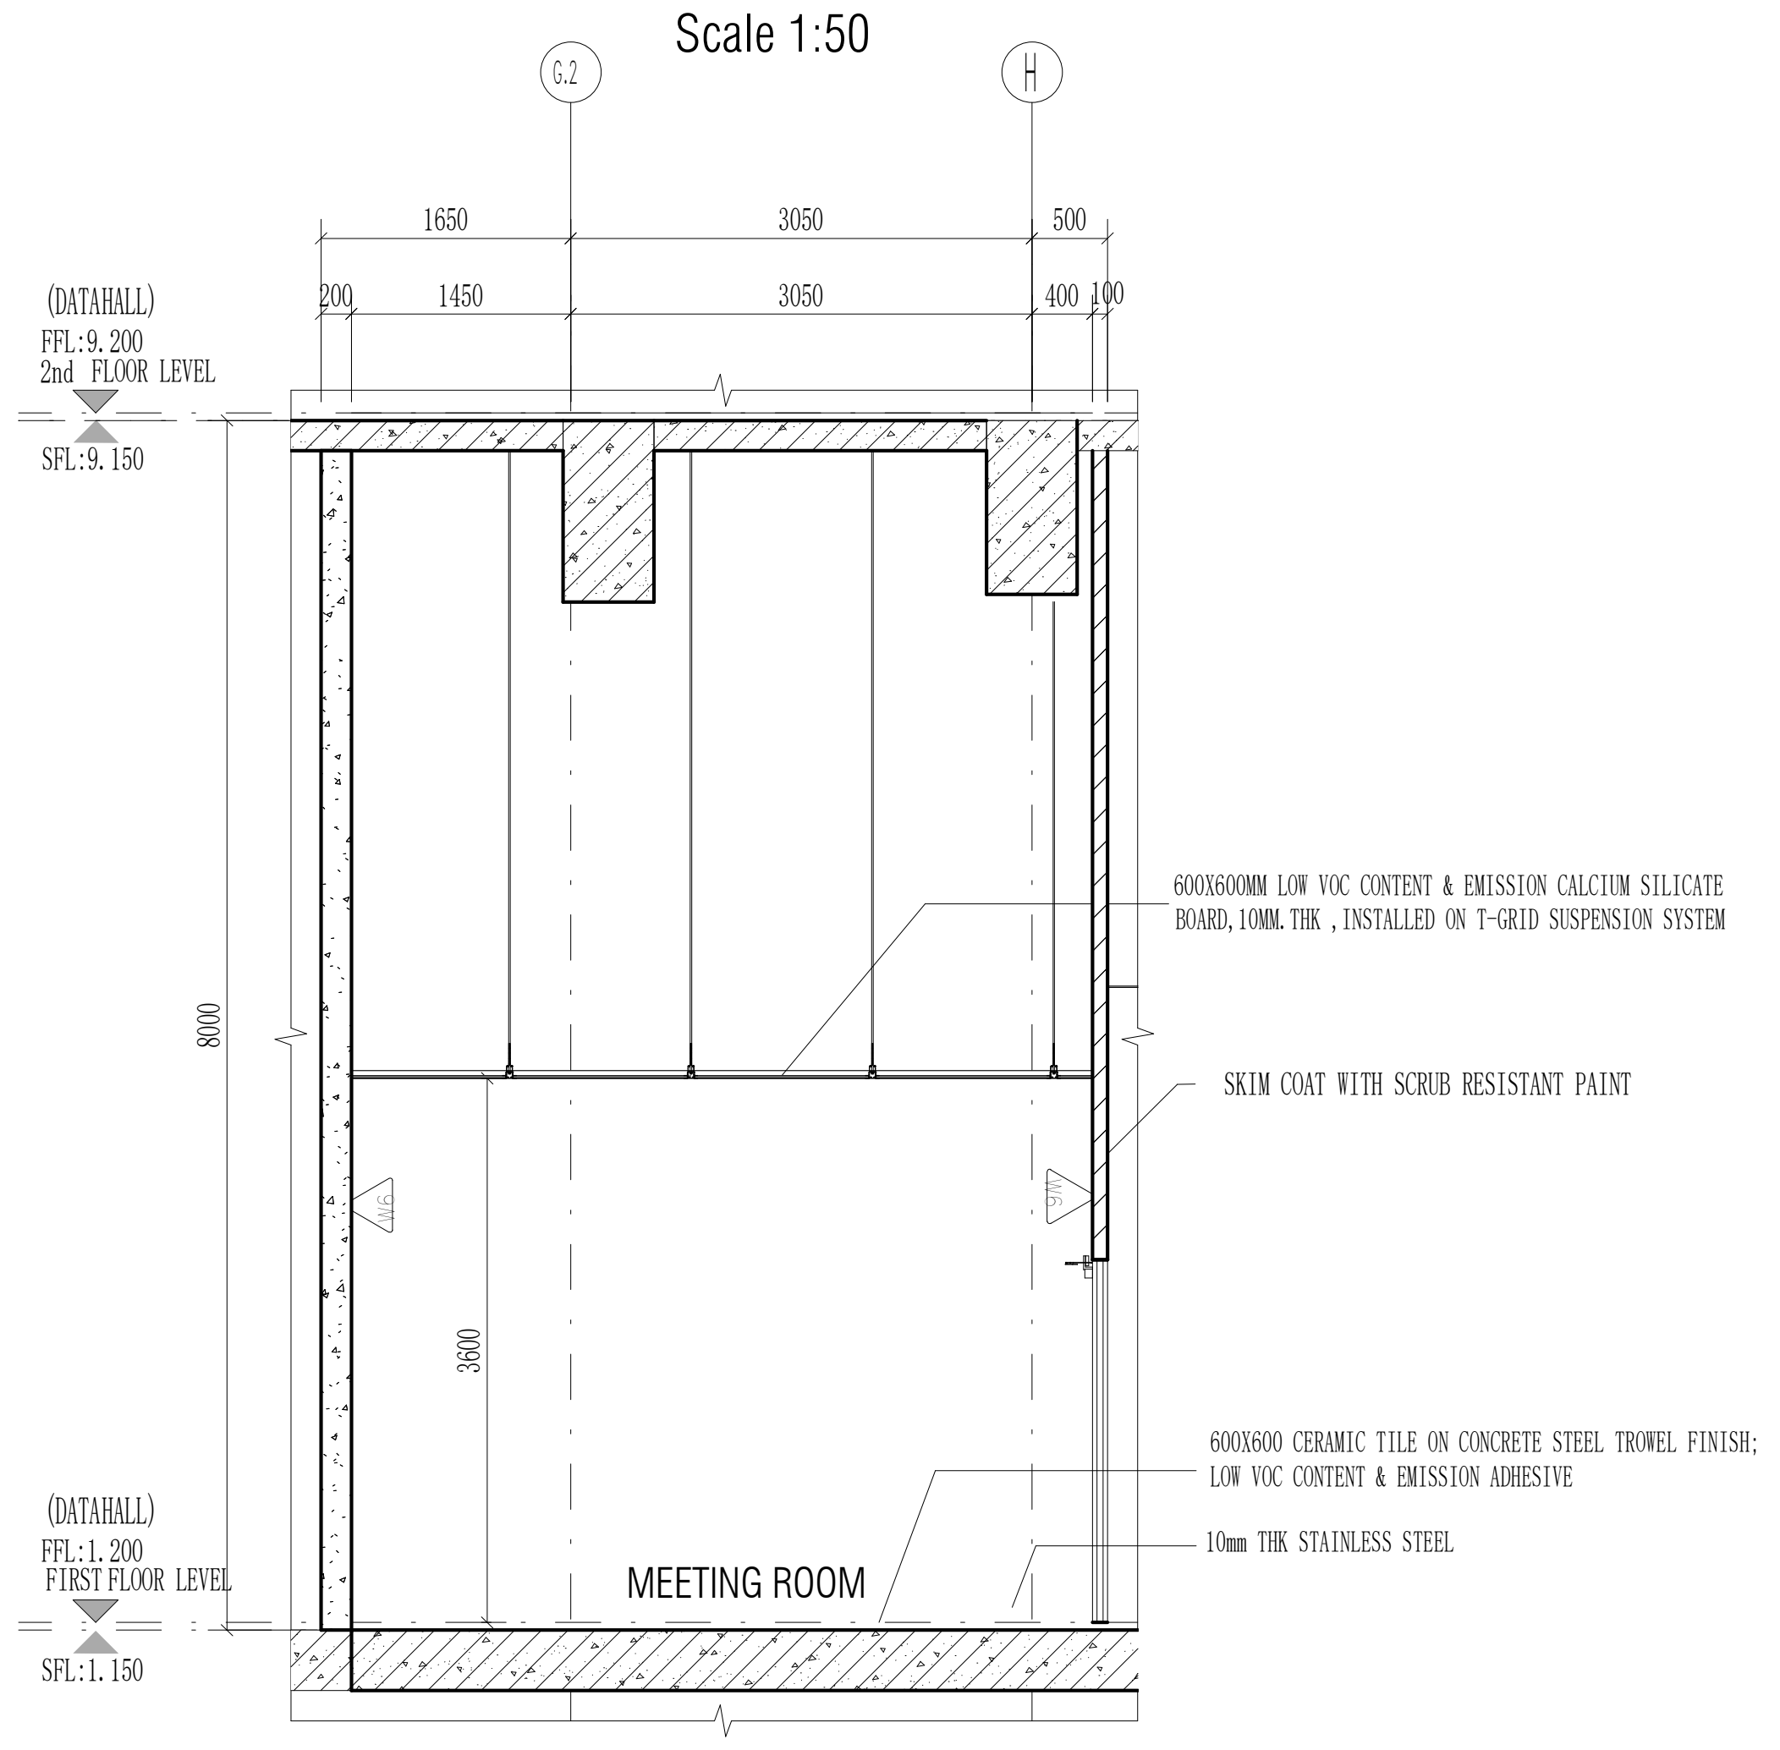
G.2
H
1650
3050
500
200
1450
3050
400 100
(DATAHALL)
FFL:9.200
2nd FLOOR LEVEL
SFL:9.150
(DATAHALL)
FFL:1.200
FIRST FLOOR LEVEL
SFL:1.150
8000
3600
600X600MM LOW VOC CONTENT & EMISSION CALCIUM SILICATE
BOARD,10MM.THK ,INSTALLED ON T-GRID SUSPENSION SYSTEM
SKIM COAT WITH SCRUB RESISTANT PAINT
600X600 CERAMIC TILE ON CONCRETE STEEL TROWEL FINISH;
LOW VOC CONTENT & EMISSION ADHESIVE
10mm THK STAINLESS STEEL
MEETING ROOM

MEETING ROOM SECTION B-B
Scale 1:50

CLIENT :
GULF EDGE DC 01
87 Wireless Road, M Thai Tower 11th. Floor, All Seasons Place, Lumpini,
Pathumwan, Bangkok 10330, Thailand

CONTRACTOR :
华西发展(泰国)有限公司
บริษัท หัวซือ ดีเวลลอปเม้นต์ (ประเทศไทย) จำกัด
HUASHI DEVELOPMENT CO.,LTD
No. 202, Room No. 1403, 14/F, Le Concorde Building,
Ratchadapisek Road, Huaykhwang Sub-District,
Huaykhwang District, Bangkok Metropolitan 10310.

CONSULTANT :
ARbay
บริษัท เอ อาร์ เบย์ จำกัด
ARbay Company Limited
31 st Floor Bangkok Insurance Building
25 South Sathorn road Thungmahamek
Sathorn Bangkok 10120 THAILAND
T +66 (0) 2286 8199
F +66 (0) 2286 2863
info@arbay.co.th

CONSULTANT :
Qbic Engineers & Architects Co.,Ltd.
8 Soi KALONG 4 SANAMBINNAM ROAD,
THASAI SUB-DISTRICT, MUANG NONTHABURI DISTRICT
, NONTHABURI.
Tel 662-950-4374
Fax 662-580-3231
E-Mail : qbic@qbic.co.th, www.qbic.co.th
QBIC ENGINEERS AND ARCHITECTS CO.,LTD.

CONSULTANT :
MITR
MITR TECHNICAL CONSULTANT CO.,LTD.
1168/8 12th FLOOR, LUMPINI TOWER BUILDING,
RAMA IV RD., THUNGMAHAMEK, SATHORN, BANGKOK 10120, THAILAND
TEL : 0-2679-9079-84
FAX : 0-2679-9085 E-mail: mitr_dd@mitr.com

Architect : SIGNATURE
ประกิต พนานุรัตน์ วสถ. 580
ที่อยู่
251/1 ถ.จารุเมือง แขวงรองเมือง เขตปทุมวัน
กรุงเทพมหานคร โทรศัพท์ 02-286-8199

Structural Engineer : SIGNATURE
วิศวกรผู้ออกแบบโครงสร้าง
ณัฐสม สงวนวงษ์ วย 1423
ที่อยู่
2/1 ซ.รามคำแหง 150 ถ.รามคำแหง
แขวง สะพานสูง เขต สะพานสูง กทม. 10240

Structural Inspector : SIGNATURE
วิศวกรผู้ตรวจสอบโครงสร้าง
โกมล จุฑาภัทร วย 964
ที่อยู่
24/18 ซ.นวมินทร์ 129 ถ. นวมินทร์
แขวง นวลจันทร์ เขต บึงกุ่ม กทม. 10230

Electrical Engineer : SIGNATURE
วิศวกรผู้ออกแบบระบบไฟฟ้ากำลัง
นายสุภัทร บูรณวิทย์ วฟก.1265
ที่อยู่
21 ซอยทานสัมฤทธิ์ 13
ตำบลท่าทราย อ.เมืองนนทบุรี จ.นนทบุรี 11000

Mechanical Engineer : SIGNATURE
วิศวกรผู้ออกแบบระบบเครื่องกลและปรับอากาศ
นายประสิทธิ์ เกี้ยวสุนทร วก.1221
ที่อยู่
44/372 ซอยบางกระดี่ 35/1 แขวงแสมดำ
เขตบางขุนเทียน กทม. 10150
ประสิทธิ์

Sanitary Engineer : SIGNATURE
วิศวกรผู้ออกแบบระบบสุขาภิบาล และดับเพลิง
นายทศวรรษ สนั่นฤทธิ์ วส. 215
ที่อยู่
บ้านเลขที่ 99/107 หมู่ที่ 3 ต.ศีรษะจรเข้น้อย
อ.บางเสาธง จ.สมุทรปราการ 10540
ทศวรรษ

ISSUE/REVISION

REV.	DESCRIPTION	DATE
A	90% DEVELOPED	09/05/2026

PROJECT NAME :
GEDC 01

LOCATION:
Nikhom Phattana district, Rayong ,industrial estate,CPGC

BUILDING :
MAIN BUILDING

90% DEVELOPED

TITLE :
ROOM DETAIL-1F-SERVER ROOM A、ELECTRICAL ROOM A、MMR A、MEETING ROOM

JOB NO.
SCALE 1 : 50
DRAWN NXR
REF.
CHECKED LJC
DWG. NO. MPK01A-90-A-RD-112
APPROVED LXD
DATE 2026.05.09

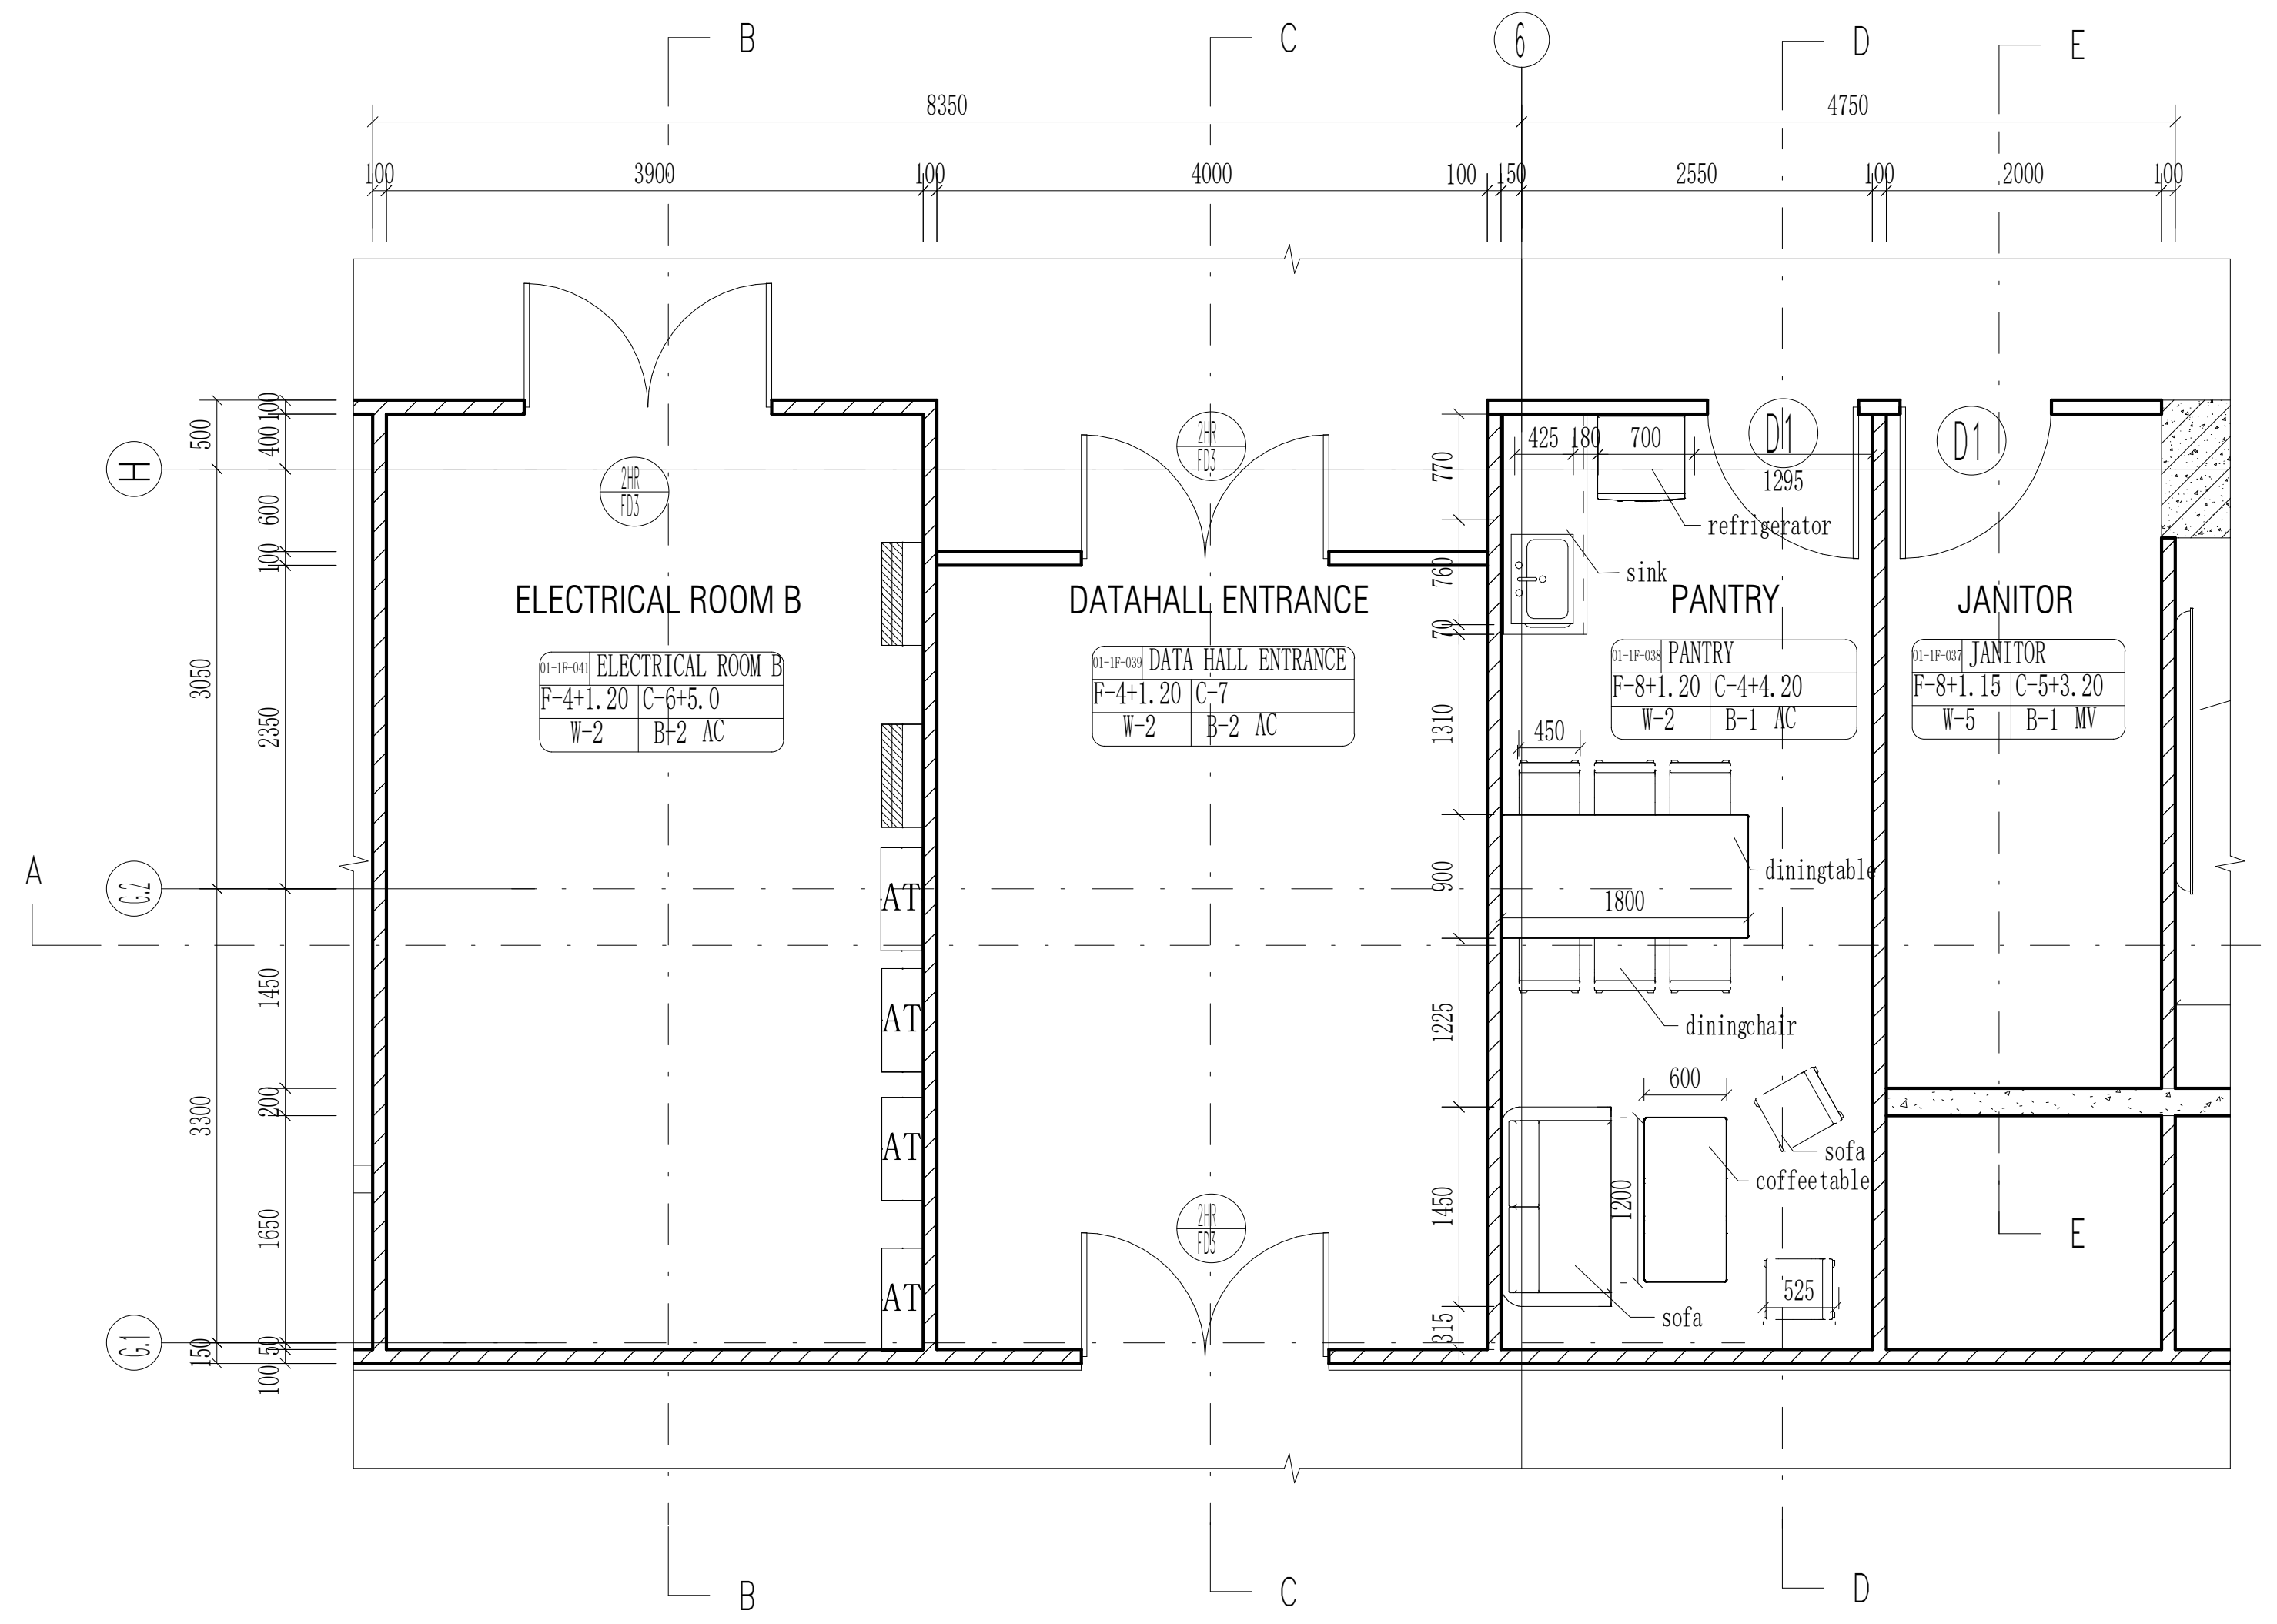
B
C
6
D
E
8350
4750
100
3900
100
4000
100
150
2550
100
2000
100
H
G.2
G.1
A
A
500
400
100
600
100
3050
2350
1450
200
3300
1650
150
50
100
770
760
70
1310
900
1225
1450
315
425
180
700
1295
D1
D1
refrigerator
sink
ELECTRICAL ROOM B
01-1F-041 ELECTRICAL ROOM B
F-4+1.20 C-6+5.0
W-2 B-2 AC
DATAHALL ENTRANCE
01-1F-039 DATA HALL ENTRANCE
F-4+1.20 C-7
W-2 B-2 AC
PANTRY
01-1F-038 PANTRY
F-8+1.20 C-4+4.20
W-2 B-1 AC
JANITOR
01-1F-037 JANITOR
F-8+1.15 C-5+3.20
W-5 B-1 MV
2HR FD3
2HR FD3
2HR FD3
AT
AT
AT
AT
450
diningtable
1800
diningchair
600
sofa
coffeetable
1200
525
sofa
E
B
C
D

ELECTRICAL ROOM B、DATAHALLENTRANCE、PANTRY、JANITOR PLAN

Scale 1:50

THE "SFL" MARKED IN THE DRAWING REFERS TO THE STRUCTURAL FLOOR LEVEL, WHILE THE FINISHED FLOOR LEVEL (FFL) IS DETERMINED BASED ON FLOOR FINISHES.

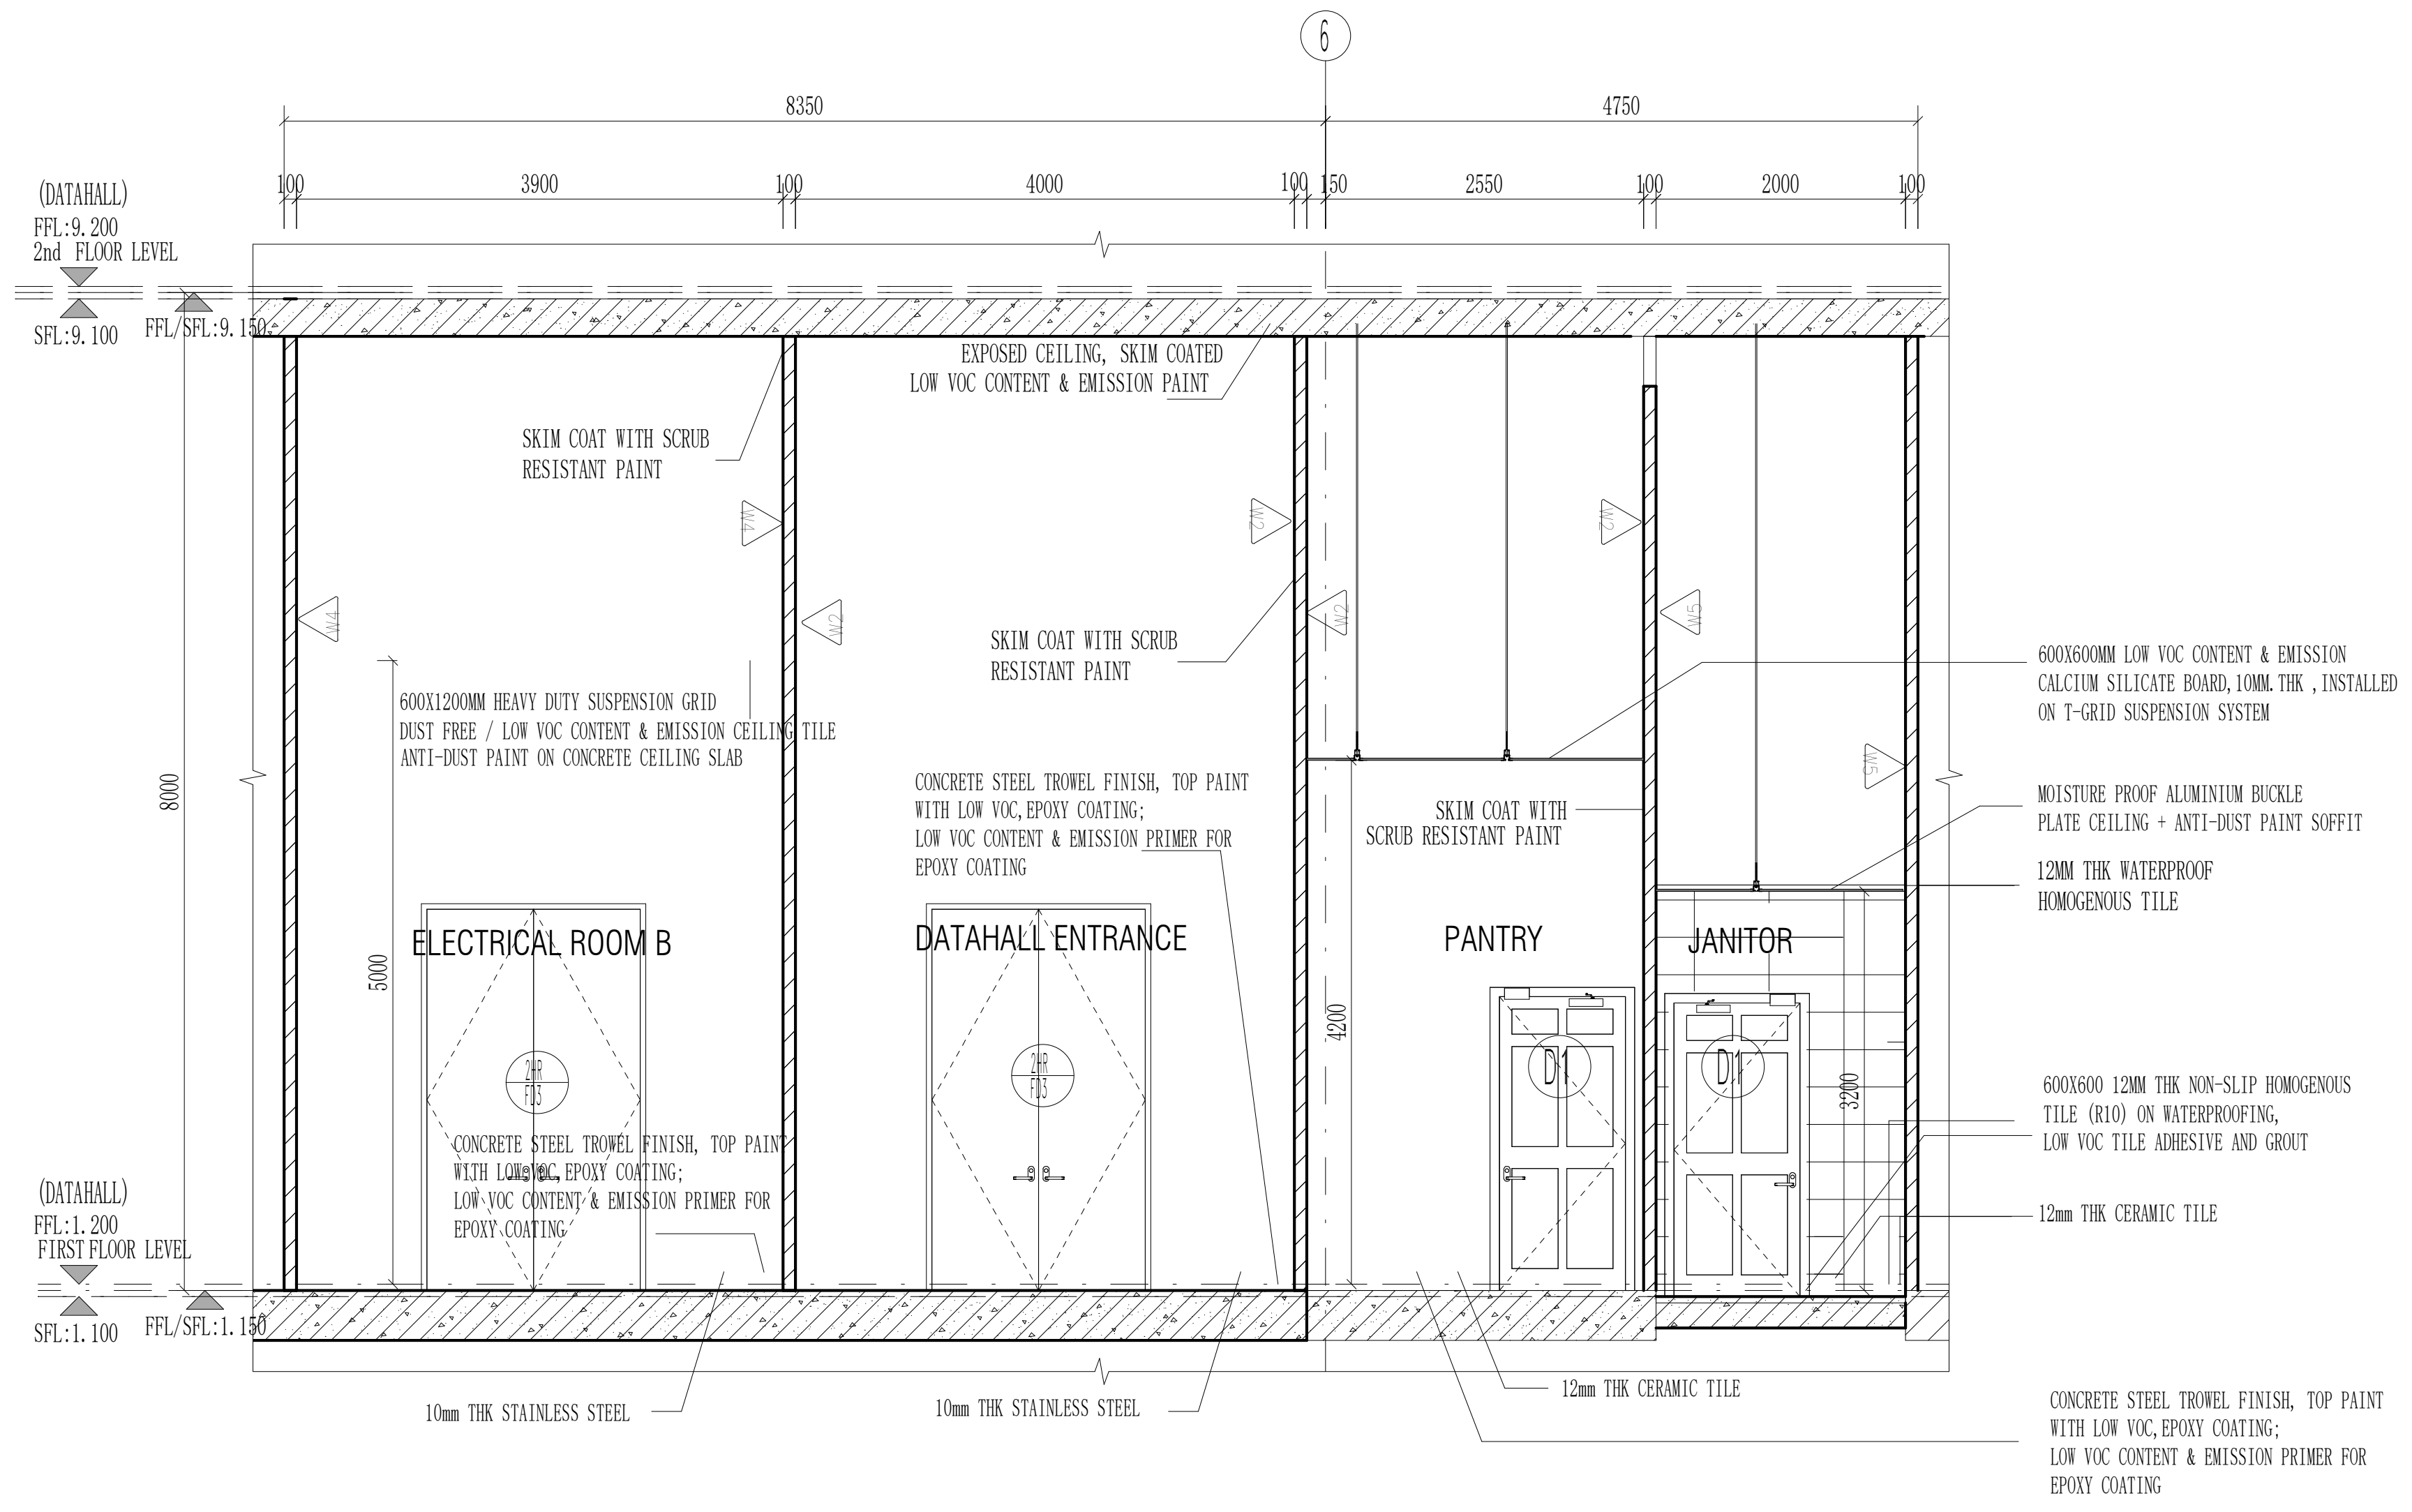
6
8350
4750
100
3900
100
4000
100
150
2550
100
2000
100
(DATAHALL)
FFL:9.200
2nd FLOOR LEVEL
SFL:9.100
FFL/SFL:9.150
EXPOSED CEILING, SKIM COATED
LOW VOC CONTENT & EMISSION PAINT
SKIM COAT WITH SCRUB
RESISTANT PAINT
W4
W2
W2
W2
W2
W5
W5
SKIM COAT WITH SCRUB
RESISTANT PAINT
600X1200MM HEAVY DUTY SUSPENSION GRID
DUST FREE / LOW VOC CONTENT & EMISSION CEILING TILE
ANTI-DUST PAINT ON CONCRETE CEILING SLAB
600X600MM LOW VOC CONTENT & EMISSION
CALCIUM SILICATE BOARD,10MM.THK ,INSTALLED
ON T-GRID SUSPENSION SYSTEM
8000
CONCRETE STEEL TROWEL FINISH, TOP PAINT
WITH LOW VOC,EPOXY COATING;
LOW VOC CONTENT & EMISSION PRIMER FOR
EPOXY COATING
SKIM COAT WITH
SCRUB RESISTANT PAINT
MOISTURE PROOF ALUMINIUM BUCKLE
PLATE CEILING + ANTI-DUST PAINT SOFFIT
12MM THK WATERPROOF
HOMOGENOUS TILE
ELECTRICAL ROOM B
DATAHALL ENTRANCE
PANTRY
JANITOR
5000
4200
3200
2HR FD3
2HR FD3
D1
D1
600X600 12MM THK NON-SLIP HOMOGENOUS
TILE (R10) ON WATERPROOFING,
LOW VOC TILE ADHESIVE AND GROUT
CONCRETE STEEL TROWEL FINISH, TOP PAINT
WITH LOW VOC,EPOXY COATING;
LOW VOC CONTENT & EMISSION PRIMER FOR
EPOXY COATING
12mm THK CERAMIC TILE
(DATAHALL)
FFL:1.200
FIRST FLOOR LEVEL
SFL:1.100
FFL/SFL:1.150
10mm THK STAINLESS STEEL
10mm THK STAINLESS STEEL
12mm THK CERAMIC TILE
CONCRETE STEEL TROWEL FINISH, TOP PAINT
WITH LOW VOC,EPOXY COATING;
LOW VOC CONTENT & EMISSION PRIMER FOR
EPOXY COATING

ELECTRICAL ROOM B、DATAHALLENTRANCE、PANTRY、JANITOR SECTION A-A

Scale 1:50

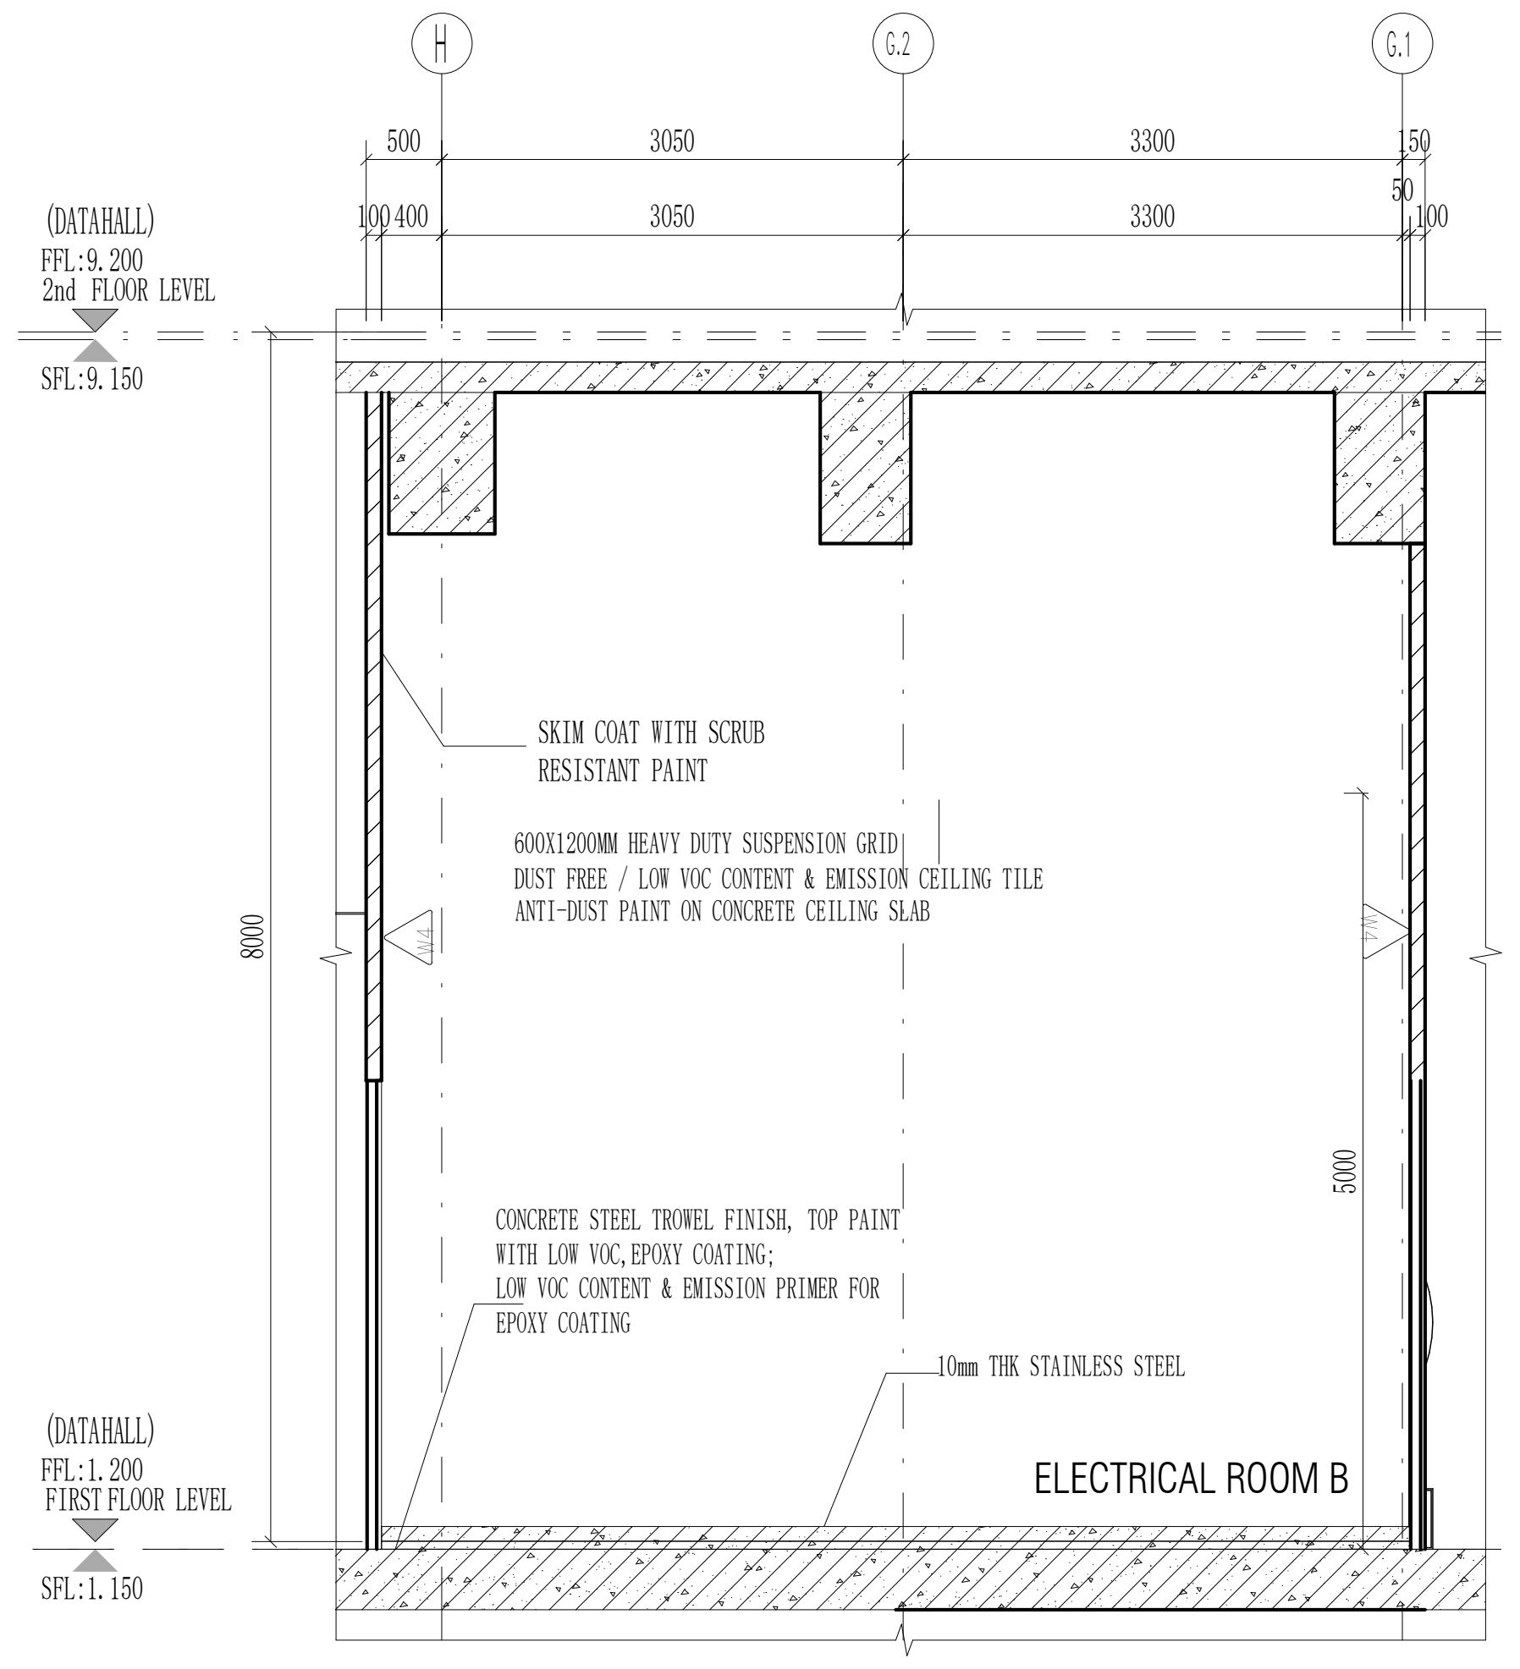
H
G.2
G.1
500
3050
3300
150
50
100 400
3050
3300
100
(DATAHALL)
FFL:9.200
2nd FLOOR LEVEL
SFL:9.150
SKIM COAT WITH SCRUB
RESISTANT PAINT
600X1200MM HEAVY DUTY SUSPENSION GRID
DUST FREE / LOW VOC CONTENT & EMISSION CEILING TILE
ANTI-DUST PAINT ON CONCRETE CEILING SLAB
8000
W4
W4
5000
CONCRETE STEEL TROWEL FINISH, TOP PAINT
WITH LOW VOC,EPOXY COATING;
LOW VOC CONTENT & EMISSION PRIMER FOR
EPOXY COATING
10mm THK STAINLESS STEEL
(DATAHALL)
FFL:1.200
FIRST FLOOR LEVEL
SFL:1.150
ELECTRICAL ROOM B

ELECTRICAL ROOM B SECTION B-B

Scale 1:50

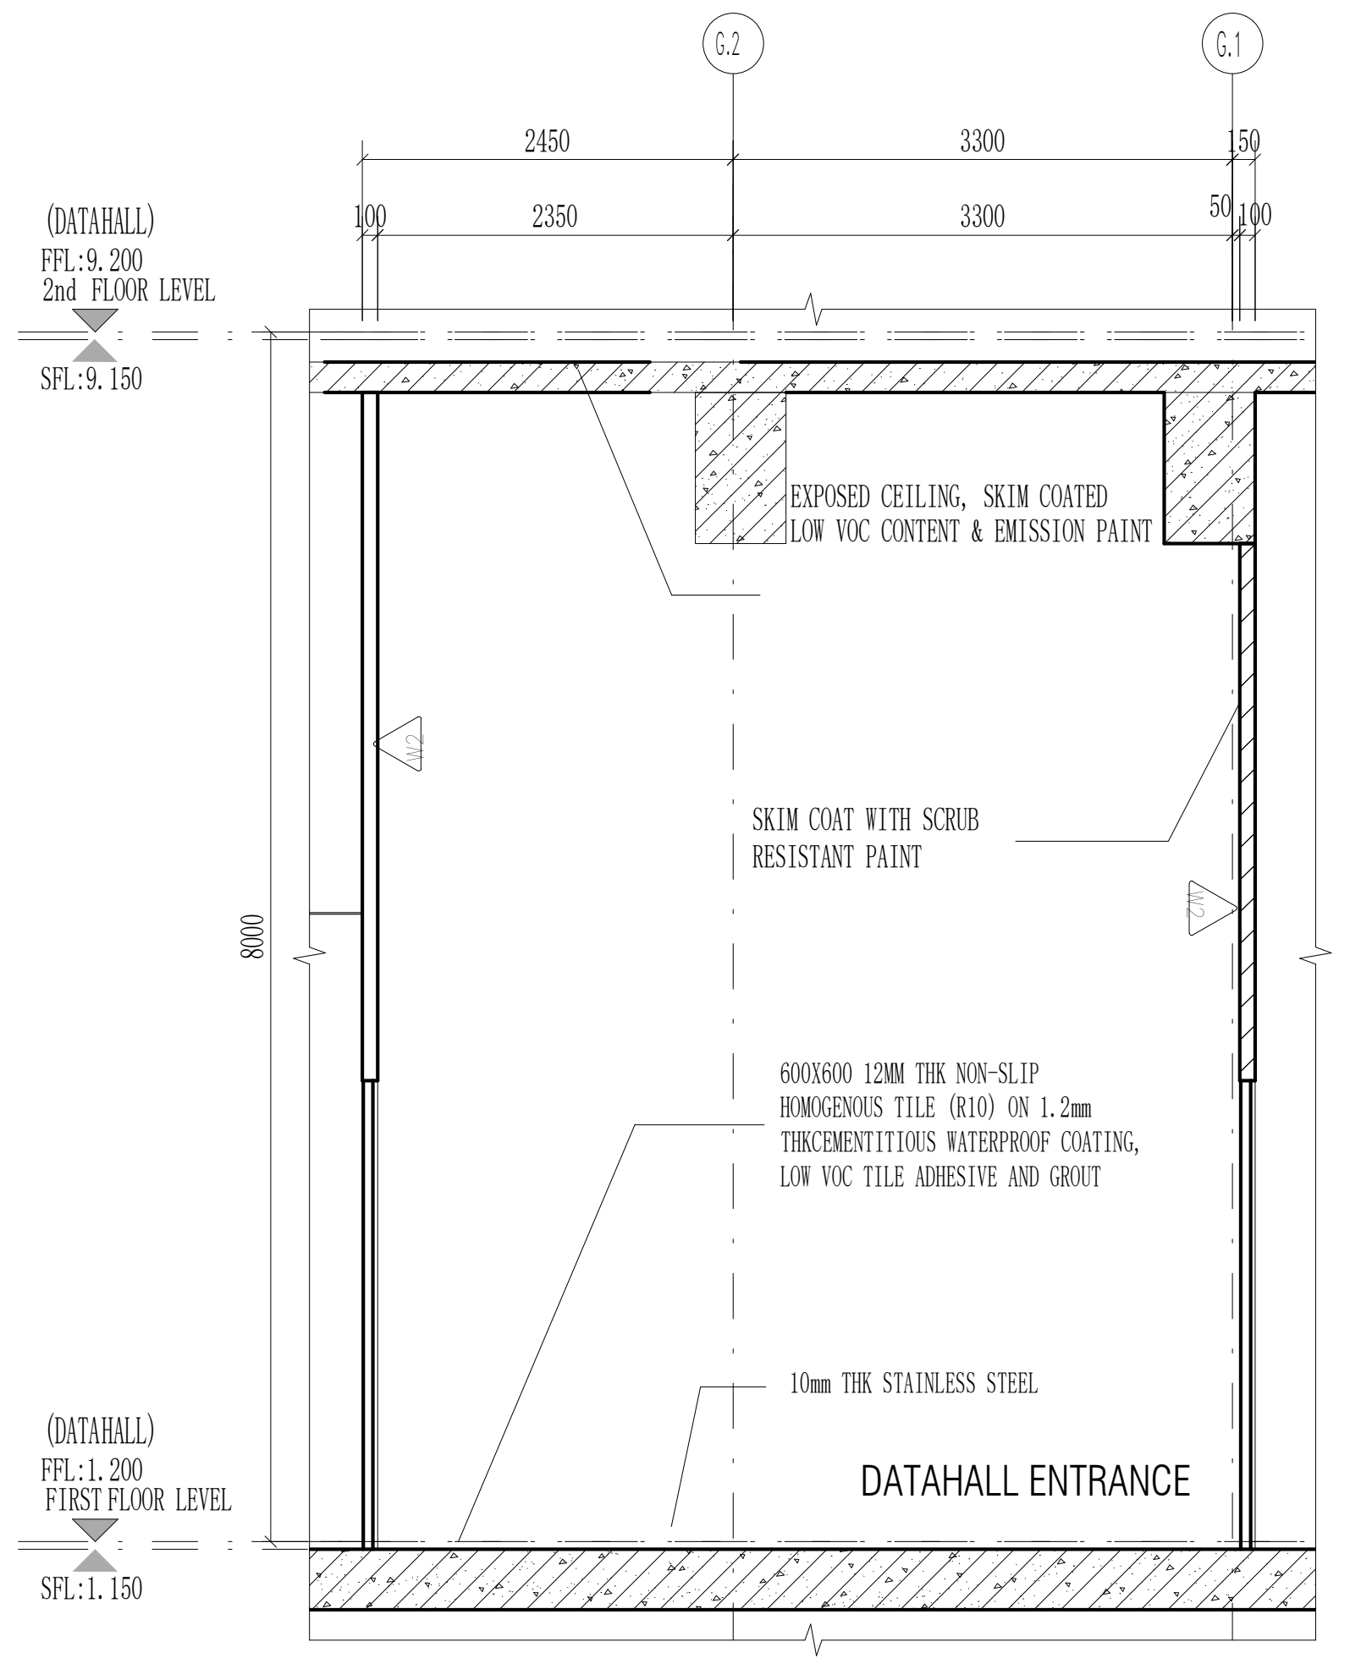
G.2
G.1
2450
3300
150
100
2350
3300
50
100
(DATAHALL)
FFL:9.200
2nd FLOOR LEVEL
SFL:9.150
EXPOSED CEILING, SKIM COATED
LOW VOC CONTENT & EMISSION PAINT
W2
SKIM COAT WITH SCRUB
RESISTANT PAINT
W2
8000
600X600 12MM THK NON-SLIP
HOMOGENOUS TILE (R10) ON 1.2mm
THKCEMENTITIOUS WATERPROOF COATING,
LOW VOC TILE ADHESIVE AND GROUT
10mm THK STAINLESS STEEL
(DATAHALL)
FFL:1.200
FIRST FLOOR LEVEL
SFL:1.150
DATAHALL ENTRANCE

DATAHALLENTRANCE SECTION C-C

Scale 1:50

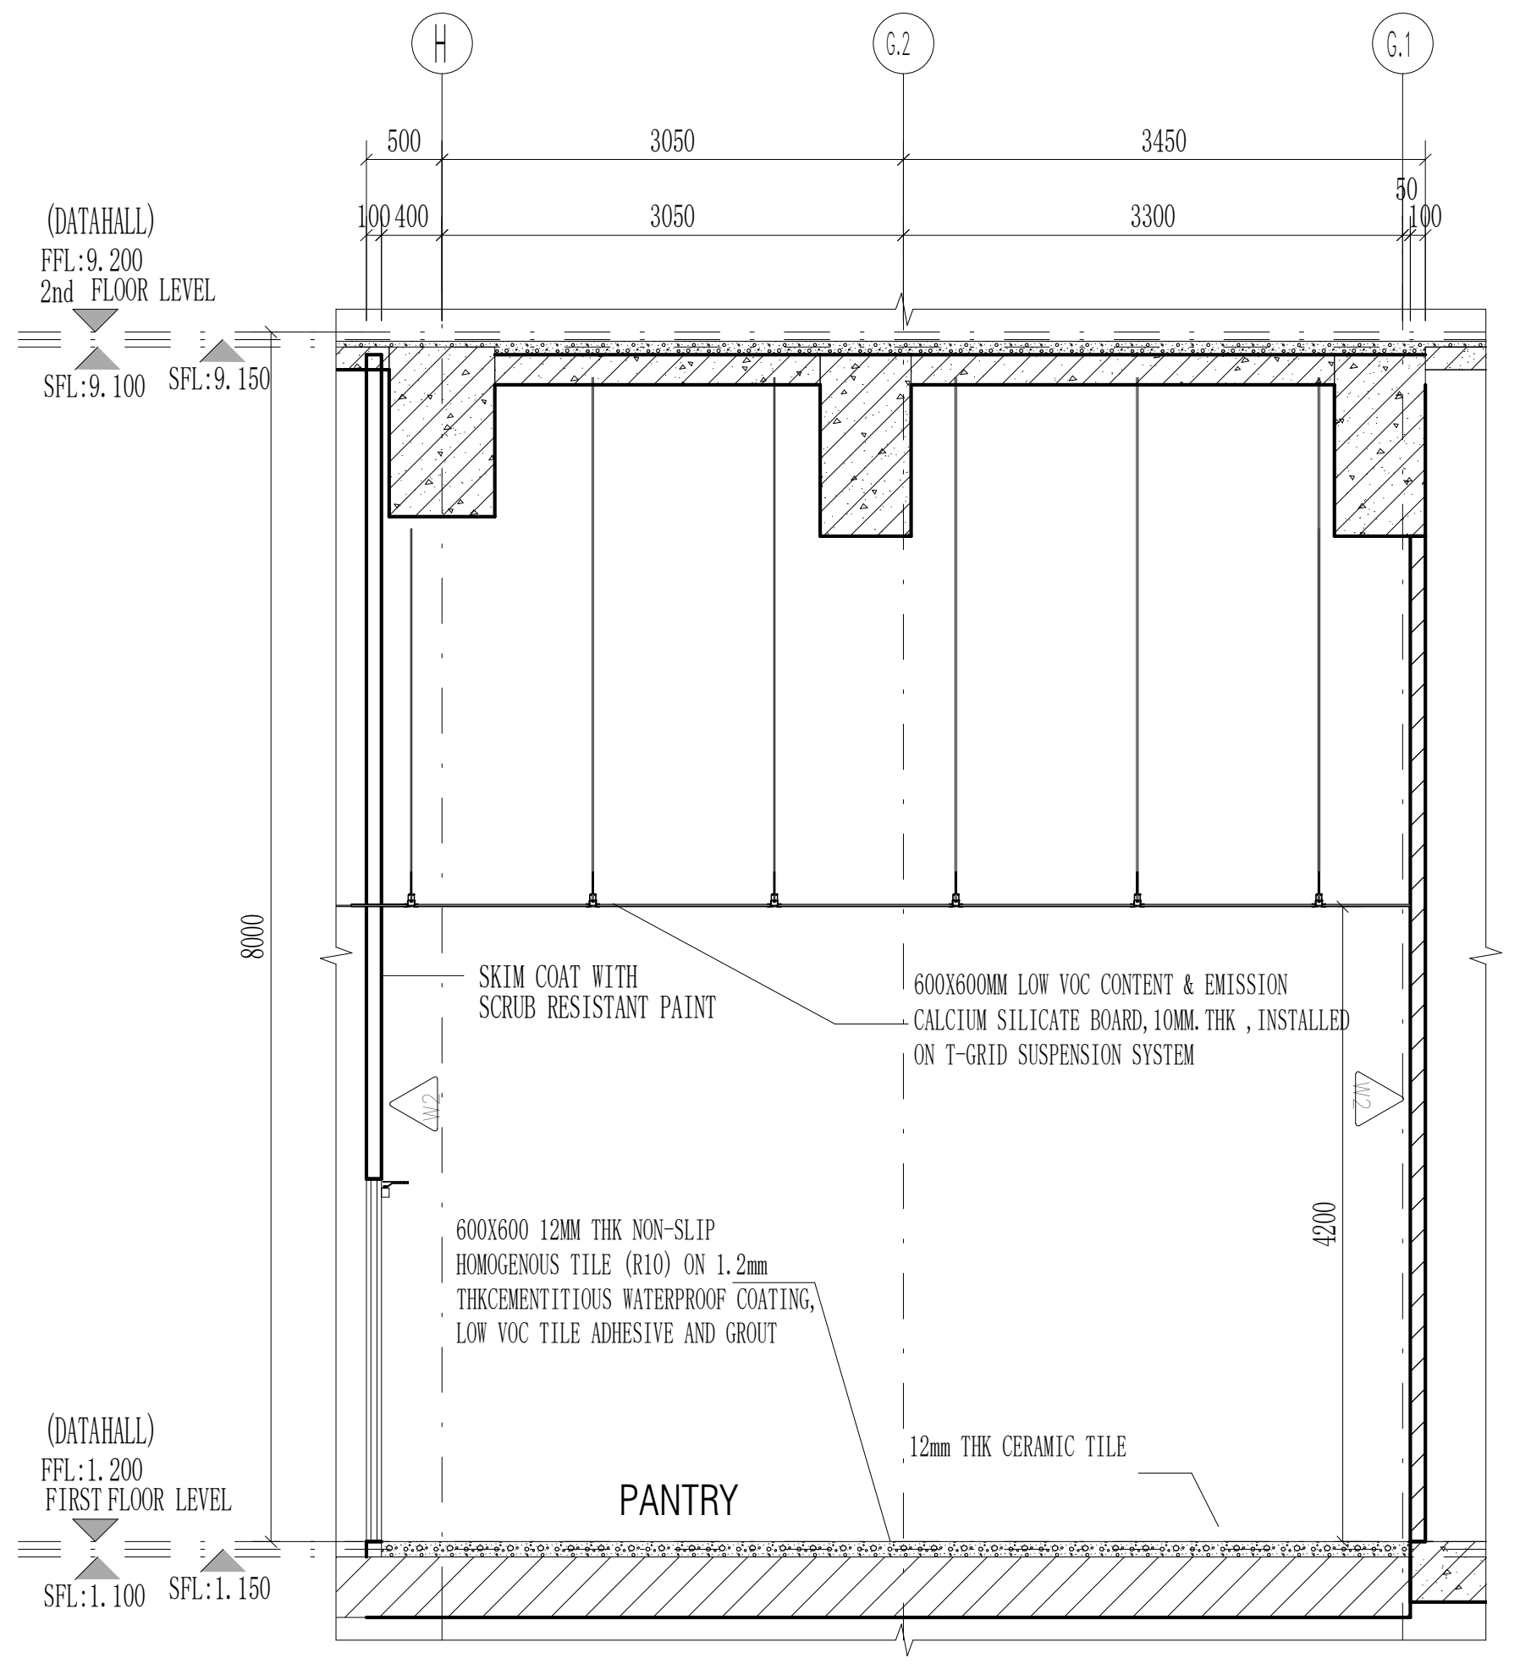
H
G.2
G.1
500
3050
3450
50
100 400
3050
3300
100
(DATAHALL)
FFL:9.200
2nd FLOOR LEVEL
SFL:9.100
SFL:9.150
8000
SKIM COAT WITH
SCRUB RESISTANT PAINT
600X600MM LOW VOC CONTENT & EMISSION
CALCIUM SILICATE BOARD,10MM.THK ,INSTALLED
ON T-GRID SUSPENSION SYSTEM
W2
W2
4200
600X600 12MM THK NON-SLIP
HOMOGENOUS TILE (R10) ON 1.2mm
THKCEMENTITIOUS WATERPROOF COATING,
LOW VOC TILE ADHESIVE AND GROUT
12mm THK CERAMIC TILE
(DATAHALL)
FFL:1.200
FIRST FLOOR LEVEL
SFL:1.100
SFL:1.150
PANTRY

PANTRY SECTION D-D

Scale 1:50

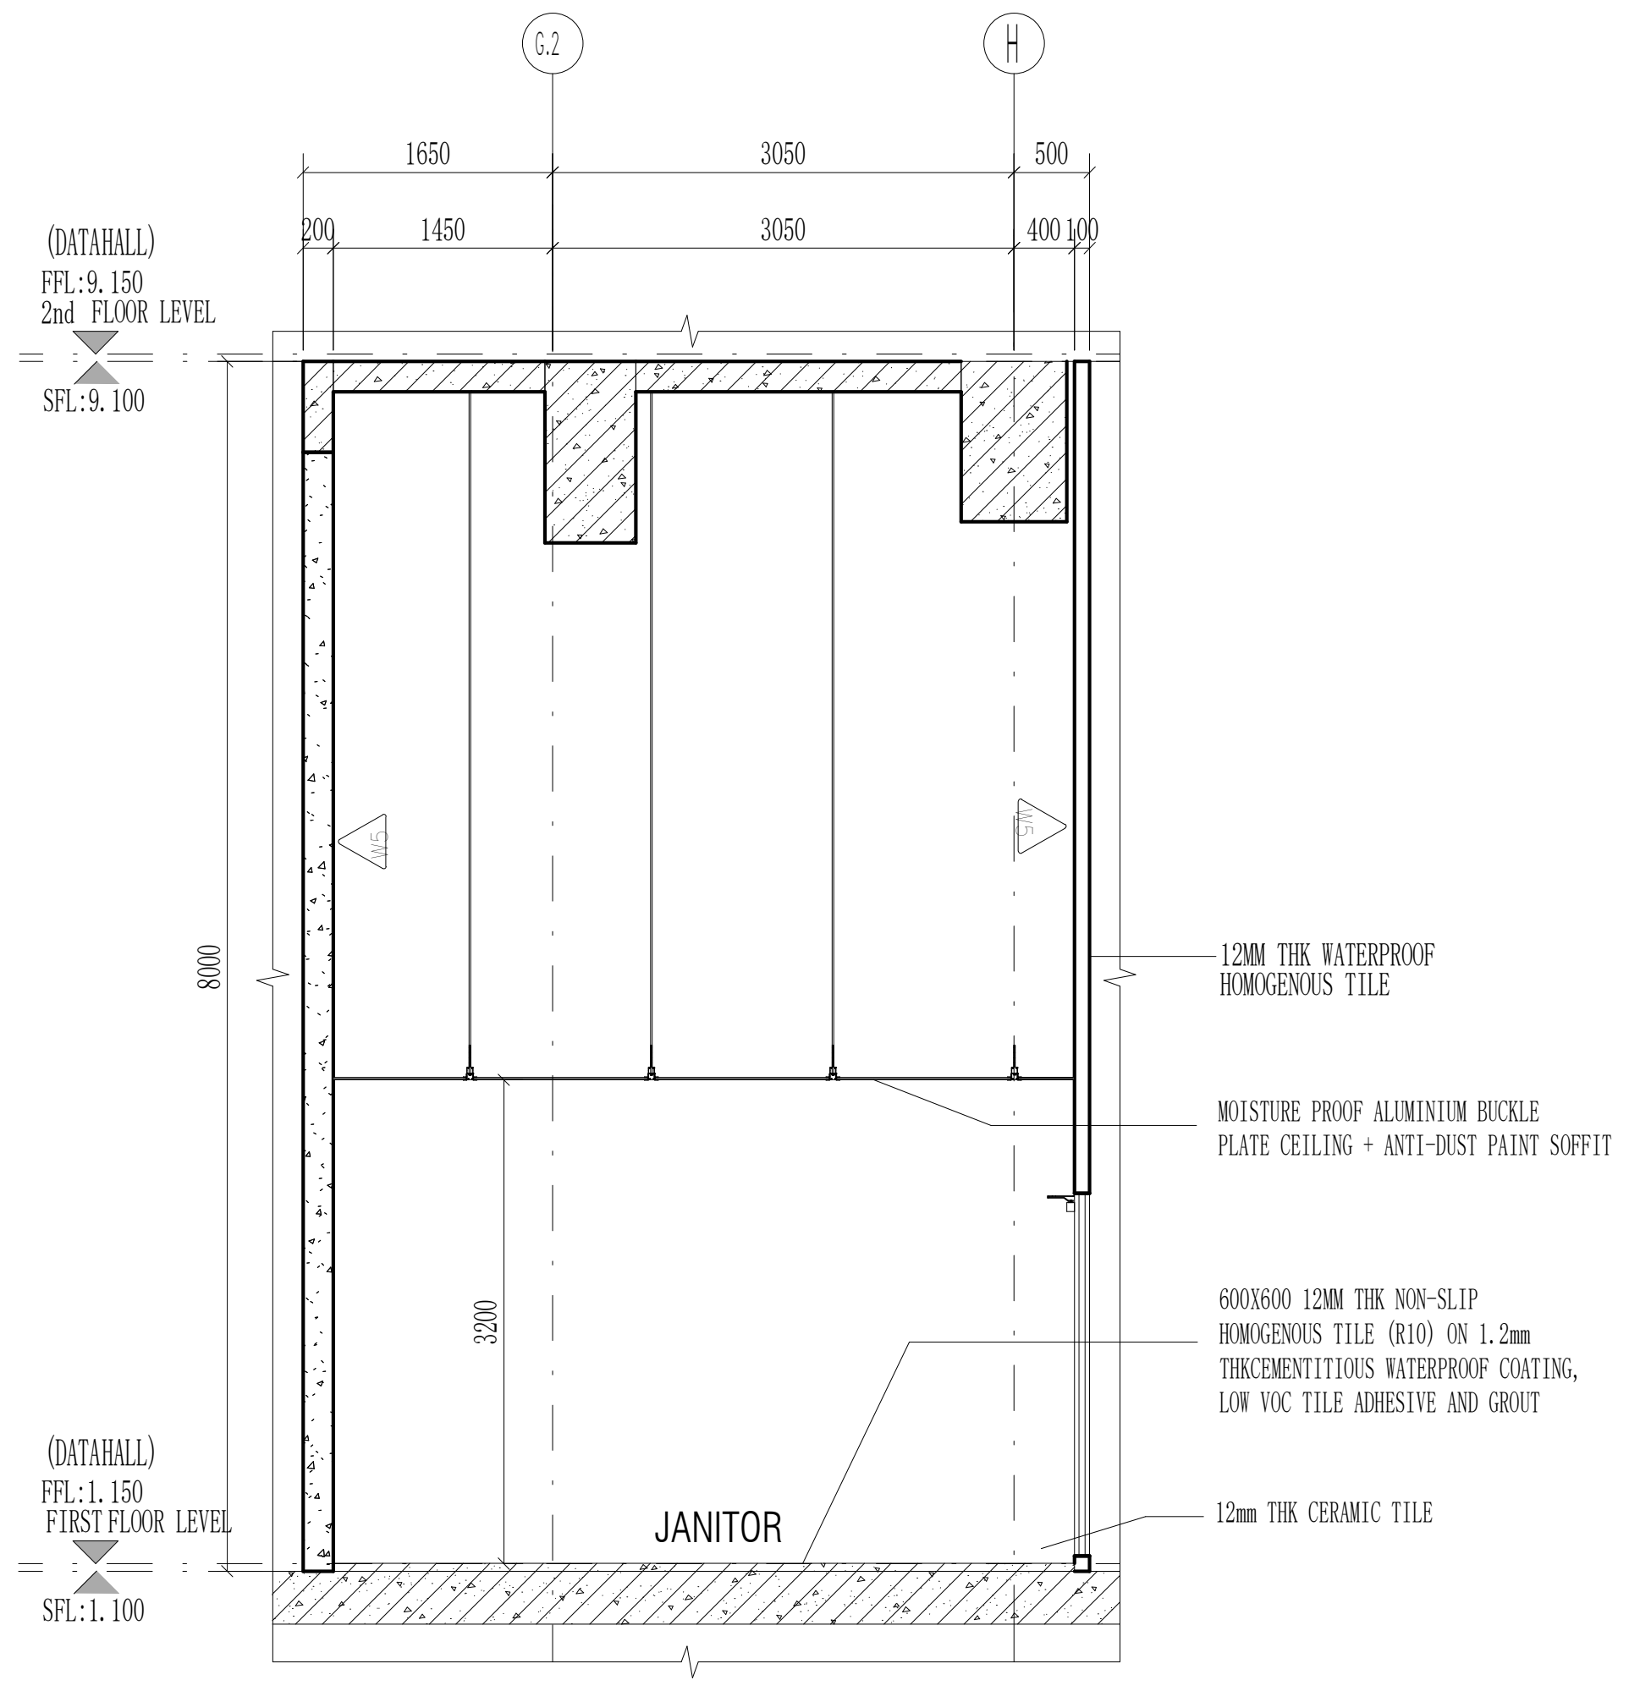
G.2
H
1650
3050
500
200
1450
3050
400 100
(DATAHALL)
FFL:9.150
2nd FLOOR LEVEL
SFL:9.100
W5
W5
8000
12MM THK WATERPROOF
HOMOGENOUS TILE
MOISTURE PROOF ALUMINIUM BUCKLE
PLATE CEILING + ANTI-DUST PAINT SOFFIT
3200
600X600 12MM THK NON-SLIP
HOMOGENOUS TILE (R10) ON 1.2mm
THKCEMENTITIOUS WATERPROOF COATING,
LOW VOC TILE ADHESIVE AND GROUT
(DATAHALL)
FFL:1.150
FIRST FLOOR LEVEL
SFL:1.100
JANITOR
12mm THK CERAMIC TILE

JANITOR SECTION E-E

Scale 1:50

NOTE :THIS PRINT IS OF A CONFIDENTIAL NATURE, IT SHALL NOT BE TRACED,PHOTOGRAPHED,PHOTOSTATED OR REPRODUCED IN ANY MANER,NOR USED FOR ANY PURPOSE WHATSOEVER EXCEPT BY WRITTEN PERMISSION

CLIENT :

GULF EDGE DC 01

87 Wireless Road, M Thai Tower 11th. Floor, All Seasons Place, Lumpini,
Pathumwan, Bangkok 10330, Thailand

CONTRACTOR :

华西发展(泰国)有限公司
บริษัท หัวซือ ดีเวลลอปเม้นต์ (ประเทศไทย) จำกัด
HUASHI DEVELOPMENT CO.,LTD
No. 202, Room No. 1403, 14/F, Le Concorde Building,
Ratchadapisek Road, Huaykhwang Sub-District,
Huaykhwang District, Bangkok Metropolitan 10310.

CONSULTANT :

ARbay
บริษัท เอ อาร์ เบย์ จำกัด
ARbay Company Limited
31 st Floor Bangkok Insurance Building
25 South Sathorn road Thungmahamek
Sathorn Bangkok 10120 THAILAND
T +66 (0) 2286 8199
F +66 (0) 2286 2863
info@arbay.co.th

CONSULTANT :

Qbic Engineers & Architects Co.,Ltd.
8 Soi KALONG 4 SANAMBINNAM ROAD,
THASAI SUB-DISTRICT, MUANG NONTHABURI DISTRICT
, NONTHABURI.
Tel 662-950-4374
Fax 662-580-3231
E-Mail : qbic@qbic.co.th, www.qbic.co.th
QBIC ENGINEERS AND ARCHITECTS CO.,LTD.

CONSULTANT :

MITR
MITR TECHNICAL CONSULTANT CO.,LTD.
1168/8 12th FLOOR, LUMPINI TOWER BUILDING,
RAMA IV RD., THUNGMAHAMEK, SATHORN, BANGKOK 10120, THAILAND
TEL : 0-2679-9079-84
FAX : 0-2679-9085 E-mail: mitr_dd@mitr.com

Architect :	SIGNATURE
ประกิต พนานุรัตน์ วสถ. 580 ที่อยู่ 251/1 ถ.จารุเมือง แขวงรองเมือง เขตปทุมวัน กรุงเทพมหานคร โทรศัพท์ 02-286-8199	
Structural Engineer :	SIGNATURE
วิศวกรผู้ออกแบบโครงสร้าง	
ณัฐสม สงวนวงษ์ วย 1423 ที่อยู่ 2/1 ซ.รามคำแหง 150 ถ.รามคำแหง แขวง สะพานสูง เขต สะพานสูง กทม. 10240	
Structural Inspector :	SIGNATURE
วิศวกรผู้ตรวจสอบโครงสร้าง	
โกมล จุฑาภัทร วย 964 ที่อยู่ 24/18 ซ.นวมินทร์ 129 ถ. นวมินทร์ แขวง นวลจันทร์ เขต บึงกุ่ม กทม. 10230	
Electrical Engineer :	SIGNATURE
วิศวกรผู้ออกแบบระบบไฟฟ้ากำลัง	
นายสุภัทร บูรณวิทย์ วฟก.1265 ที่อยู่ 21 ซอยทานสัมฤทธิ์ 13 ตำบลท่าทราย อ.เมืองนนทบุรี จ.นนทบุรี 11000	
Mechanical Engineer :	SIGNATURE
วิศวกรผู้ออกแบบระบบเครื่องกลและปรับอากาศ	
นายประสิทธิ์ เกี้ยวสุนทร วก.1221 ที่อยู่ 44/372 ซอยบางกระดี่ 35/1 แขวงแสมดำ เขตบางขุนเทียน กทม. 10150	ประสิทธิ์
Sanitary Engineer :	SIGNATURE
วิศวกรผู้ออกแบบระบบสุขาภิบาล และดับเพลิง	
นายทศวรรษ สนั่นฤทธิ์ วส. 215 ที่อยู่ บ้านเลขที่ 99/107 หมู่ที่ 3 ต.ศีรษะจรเข้น้อย อ.บางเสาธง จ.สมุทรปราการ 10540	ทศวรรษ

ISSUE/REVISION

REV.	DESCRIPTION	DATE
A	90% DEVELOPED	09/05/2026

PROJECT NAME :

GEDC 01

LOCATION:
Nikhom Phattana district, Rayong ,industrial estate,CPGC

BUILDING :
MAIN BUILDING

90% DEVELOPED

TITLE :

ROOM
DETAIL-1F-JANITOR、PANTRY、DATAHALL
ENTRANCE、ELECTRICAL ROOM B

JOB NO.	SCALE 1 : 50
DRAWN NXR	REF.
CHECKED LJC	DWG. NO. MPK01A-90-A-RD-113
APPROVED LXD	
DATE 2026.05.09	

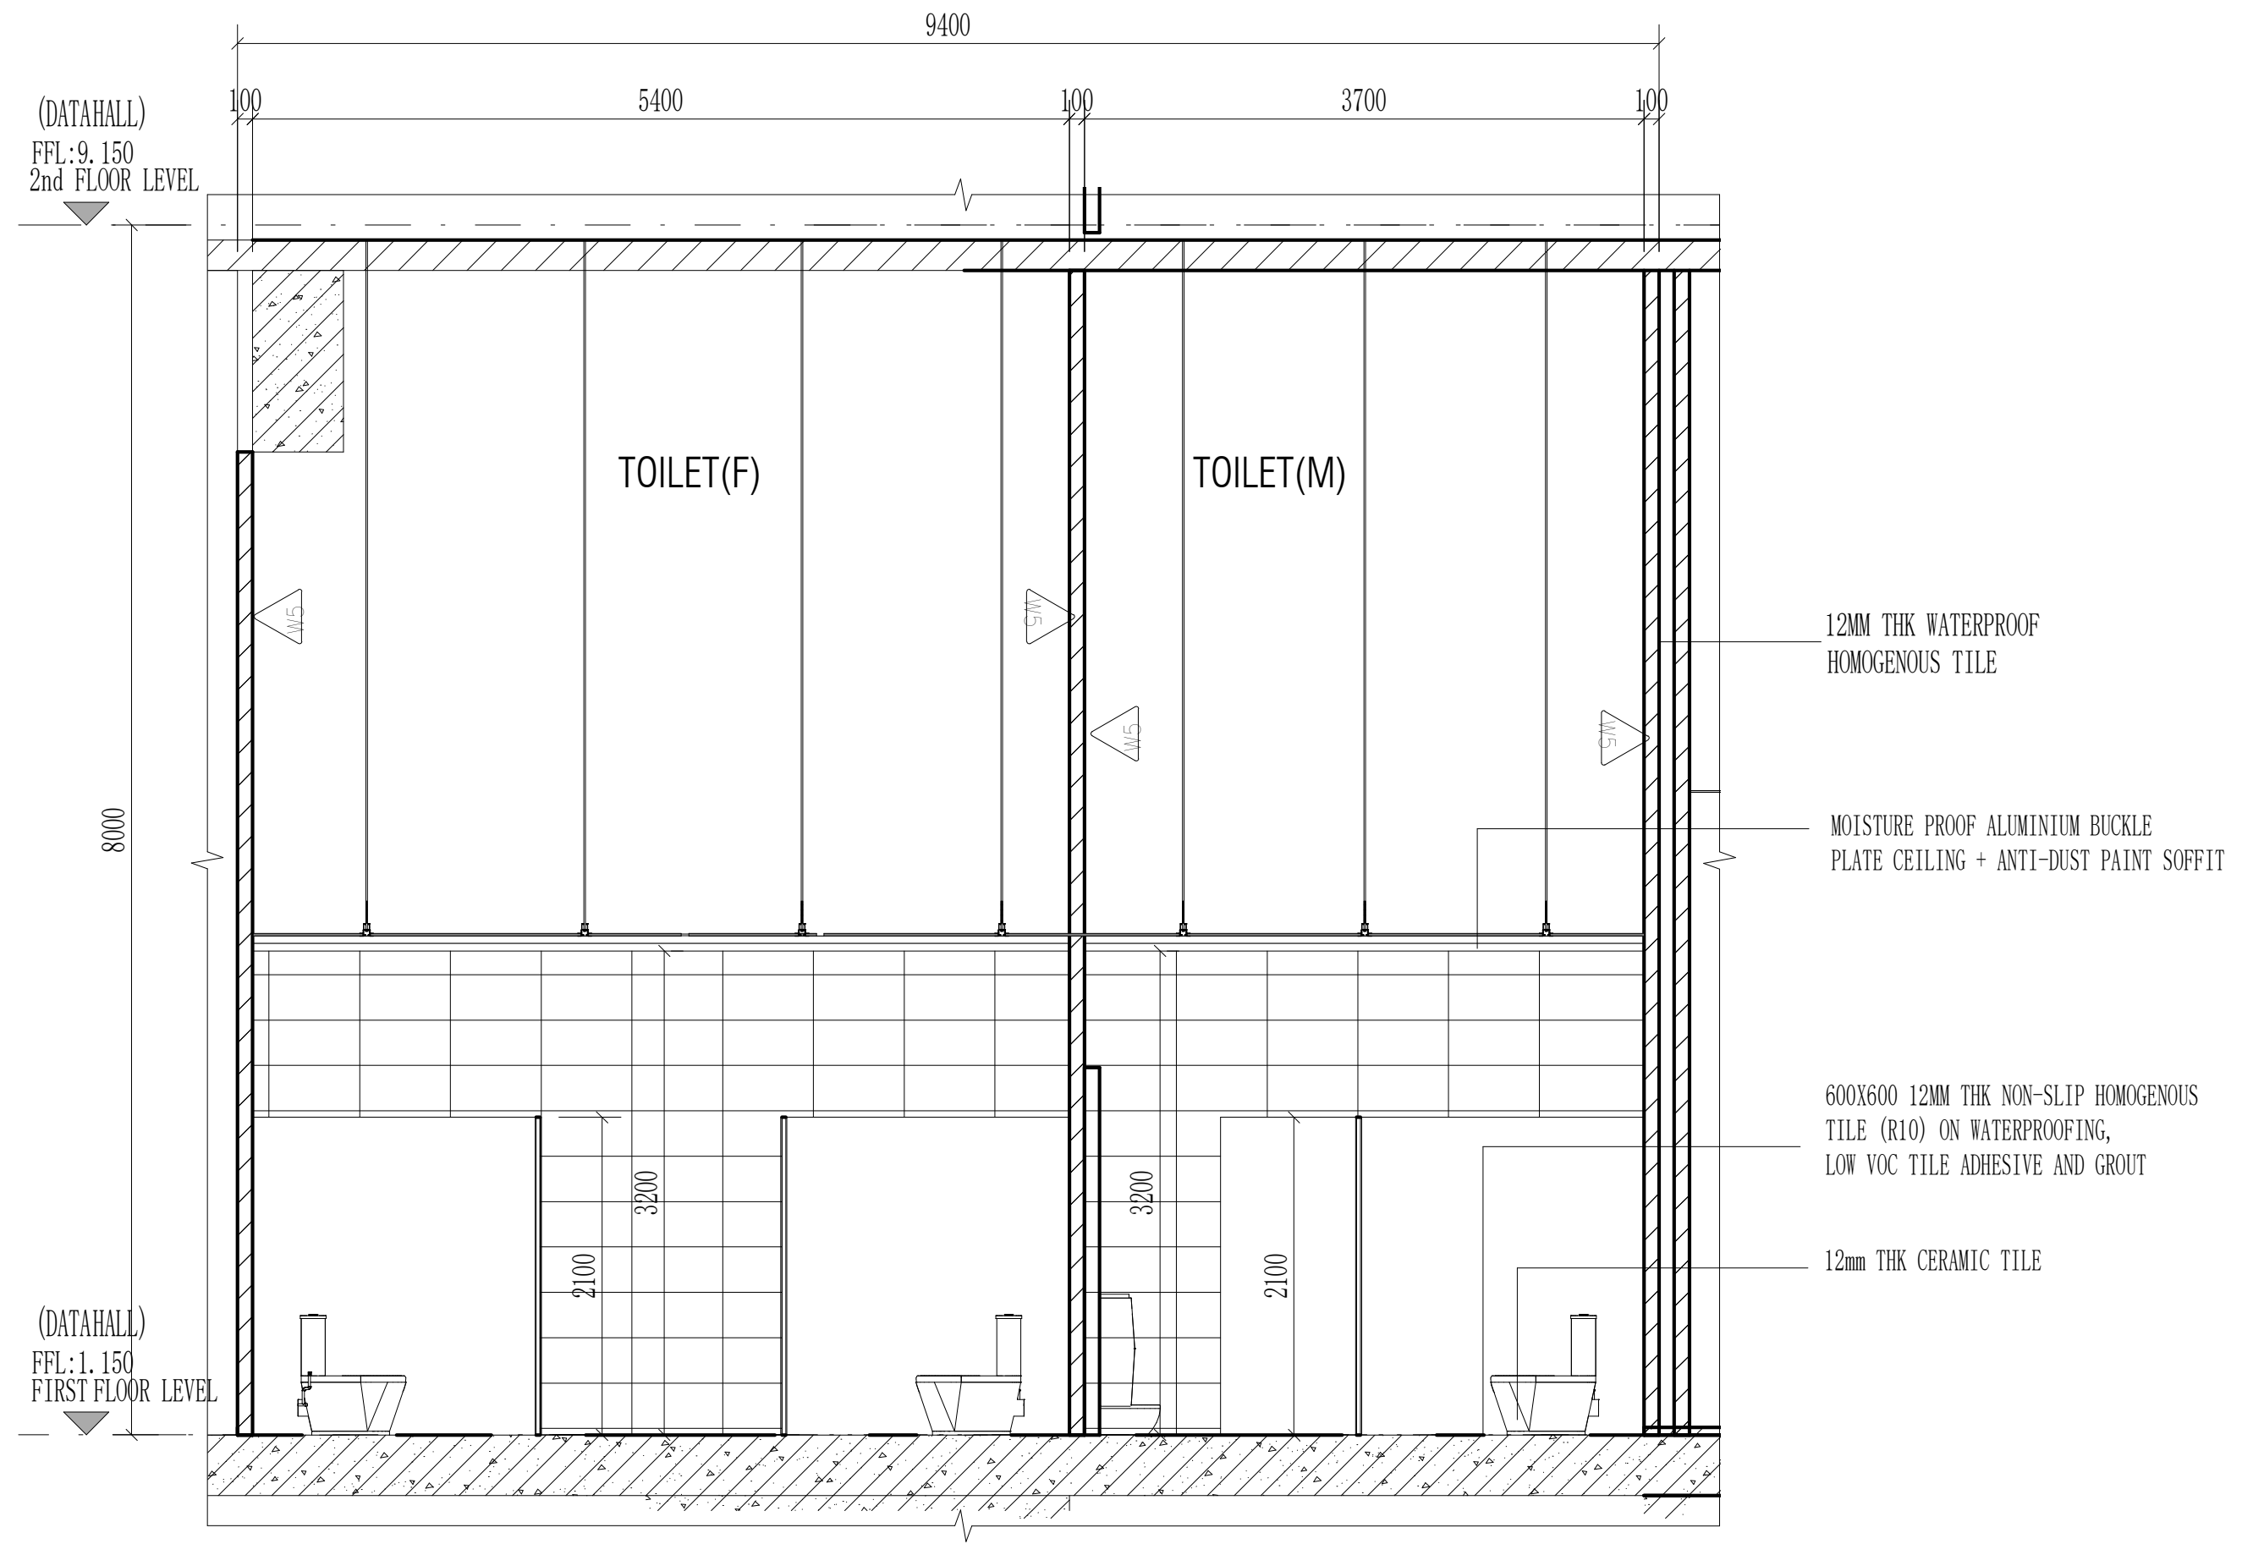
9400
100
5400
100
3700
100
(DATAHALL)
FFL:9.150
2nd FLOOR LEVEL
TOILET(F)
TOILET(M)
W5
8000
3200
2100
(DATAHALL)
FFL:1.150
FIRST FLOOR LEVEL
12MM THK WATERPROOF
HOMOGENOUS TILE
MOISTURE PROOF ALUMINIUM BUCKLE
PLATE CEILING + ANTI-DUST PAINT SOFFIT
600X600 12MM THK NON-SLIP HOMOGENOUS
TILE (R10) ON WATERPROOFING,
LOW VOC TILE ADHESIVE AND GROUT
12mm THK CERAMIC TILE

TOILET(F)、 TOILET(M) SECTIONA-A

Scale 1:50

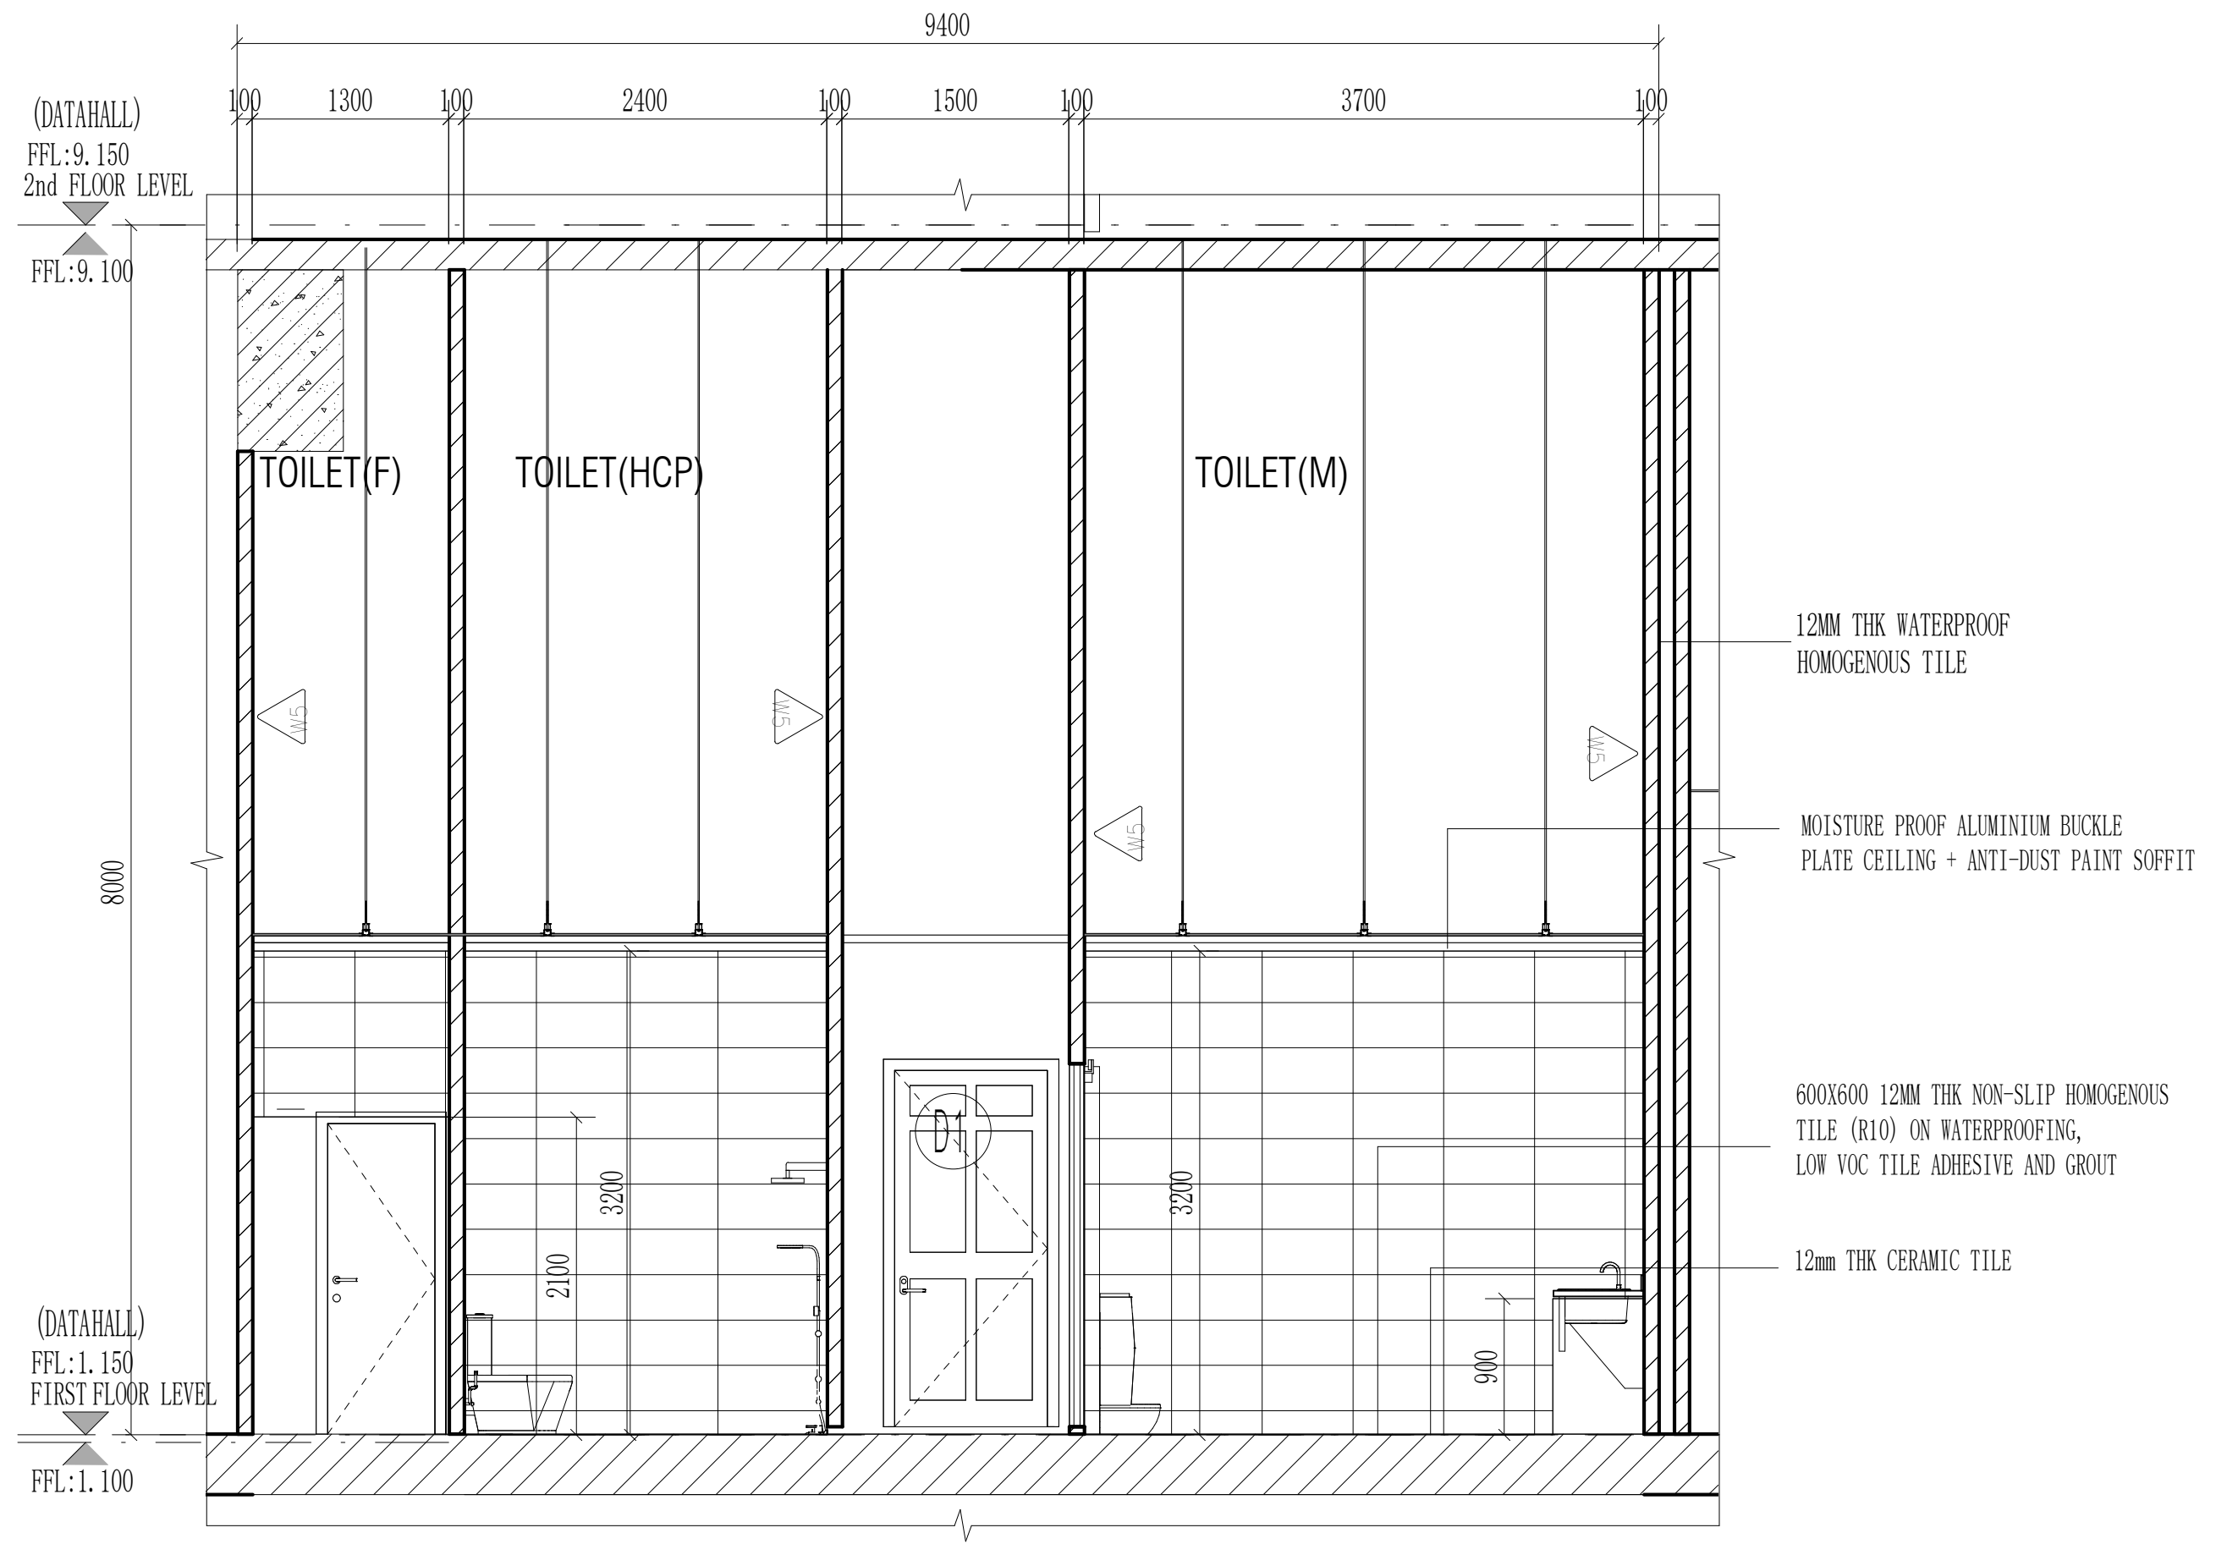
9400
100
1300
100
2400
100
1500
100
3700
100
(DATAHALL)
FFL:9.150
2nd FLOOR LEVEL
FFL:9.100
TOILET(F)
TOILET(HCP)
TOILET(M)
W5
D1
8000
3200
2100
900
(DATAHALL)
FFL:1.150
FIRST FLOOR LEVEL
FFL:1.100
12MM THK WATERPROOF
HOMOGENOUS TILE
MOISTURE PROOF ALUMINIUM BUCKLE
PLATE CEILING + ANTI-DUST PAINT SOFFIT
600X600 12MM THK NON-SLIP HOMOGENOUS
TILE (R10) ON WATERPROOFING,
LOW VOC TILE ADHESIVE AND GROUT
12mm THK CERAMIC TILE

SHOWER(F) TOILET(HCP) TOILET(M) SECTION B-B

Scale 1:50

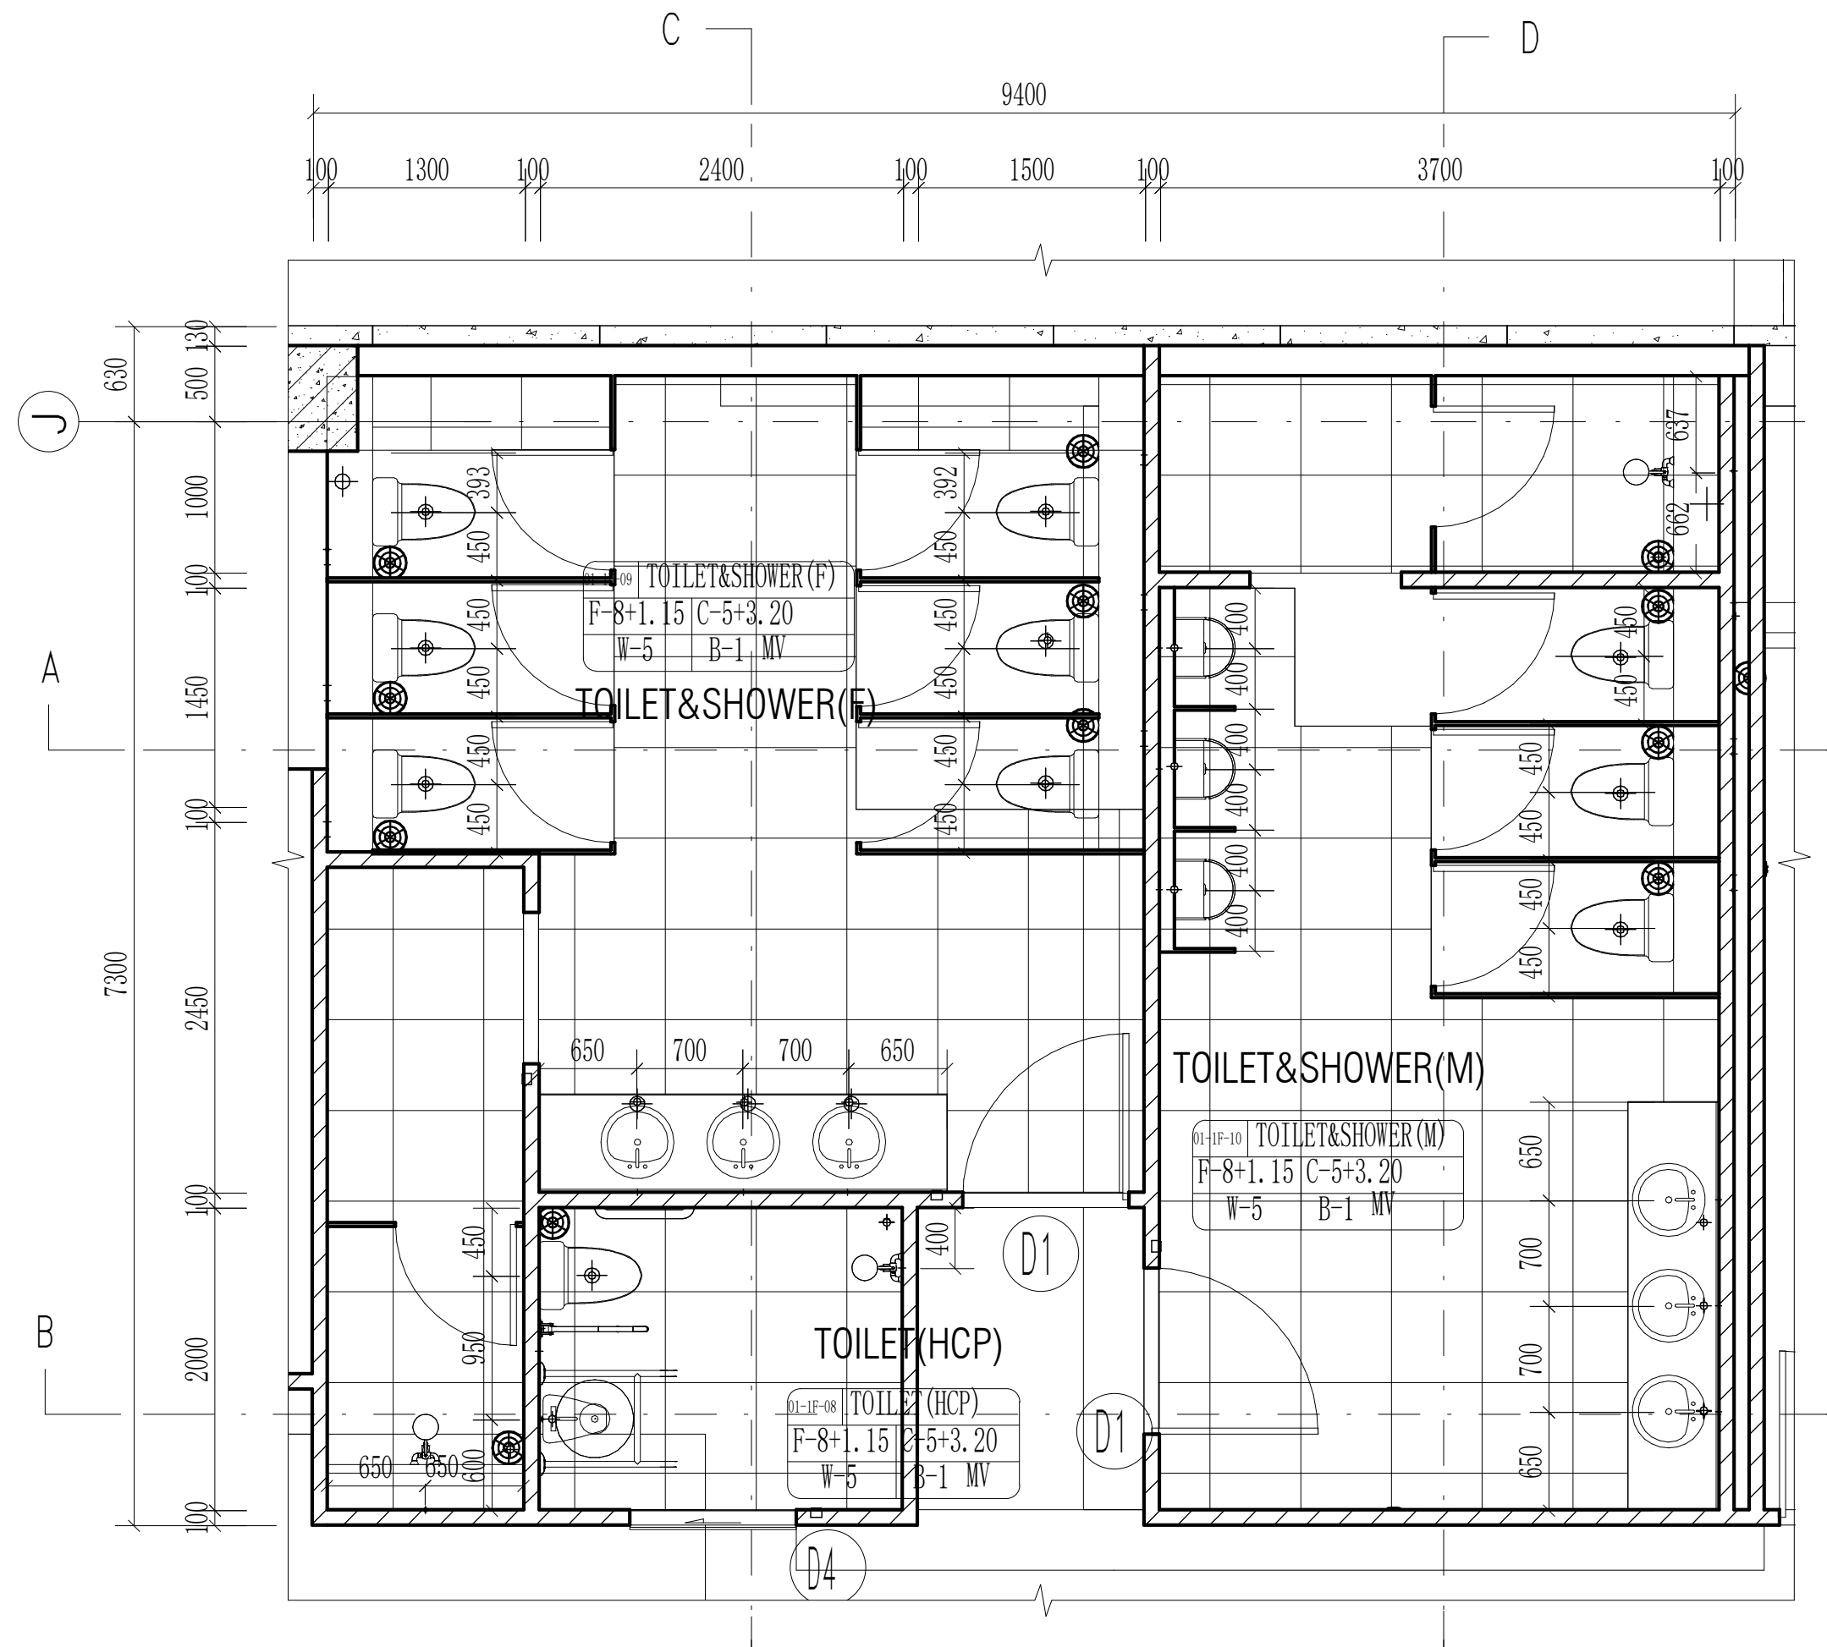
C
D
9400
100
1300
100
2400
100
1500
100
3700
100
J
A
B
630
130
500
1000
1450
2450
2000
7300
TOILET&SHOWER(F)
01-1F-09 TOILET&SHOWER(F)
F-8+1.15 C-5+3.20
W-5 B-1 MV
TOILET&SHOWER(M)
01-1F-10 TOILET&SHOWER(M)
F-8+1.15 C-5+3.20
W-5 B-1 MV
TOILET(HCP)
01-1F-08 TOILET(HCP)
F-8+1.15 C-5+3.20
W-5 B-1 MV
393
392
450
400
637
662
650
700
950
600
D1
D4

TOILET&SHOWER(F)、 TOILET&SHOWER(M)、 TOILE(HCP) PLAN

Scale 1:50

THE "SFL" MARKED IN THE DRAWING REFERS TO THE STRUCTURAL FLOOR LEVEL, WHILE THE FINISHED FLOOR LEVEL (FFL) IS DETERMINED BASED ON FLOOR FINISHES.

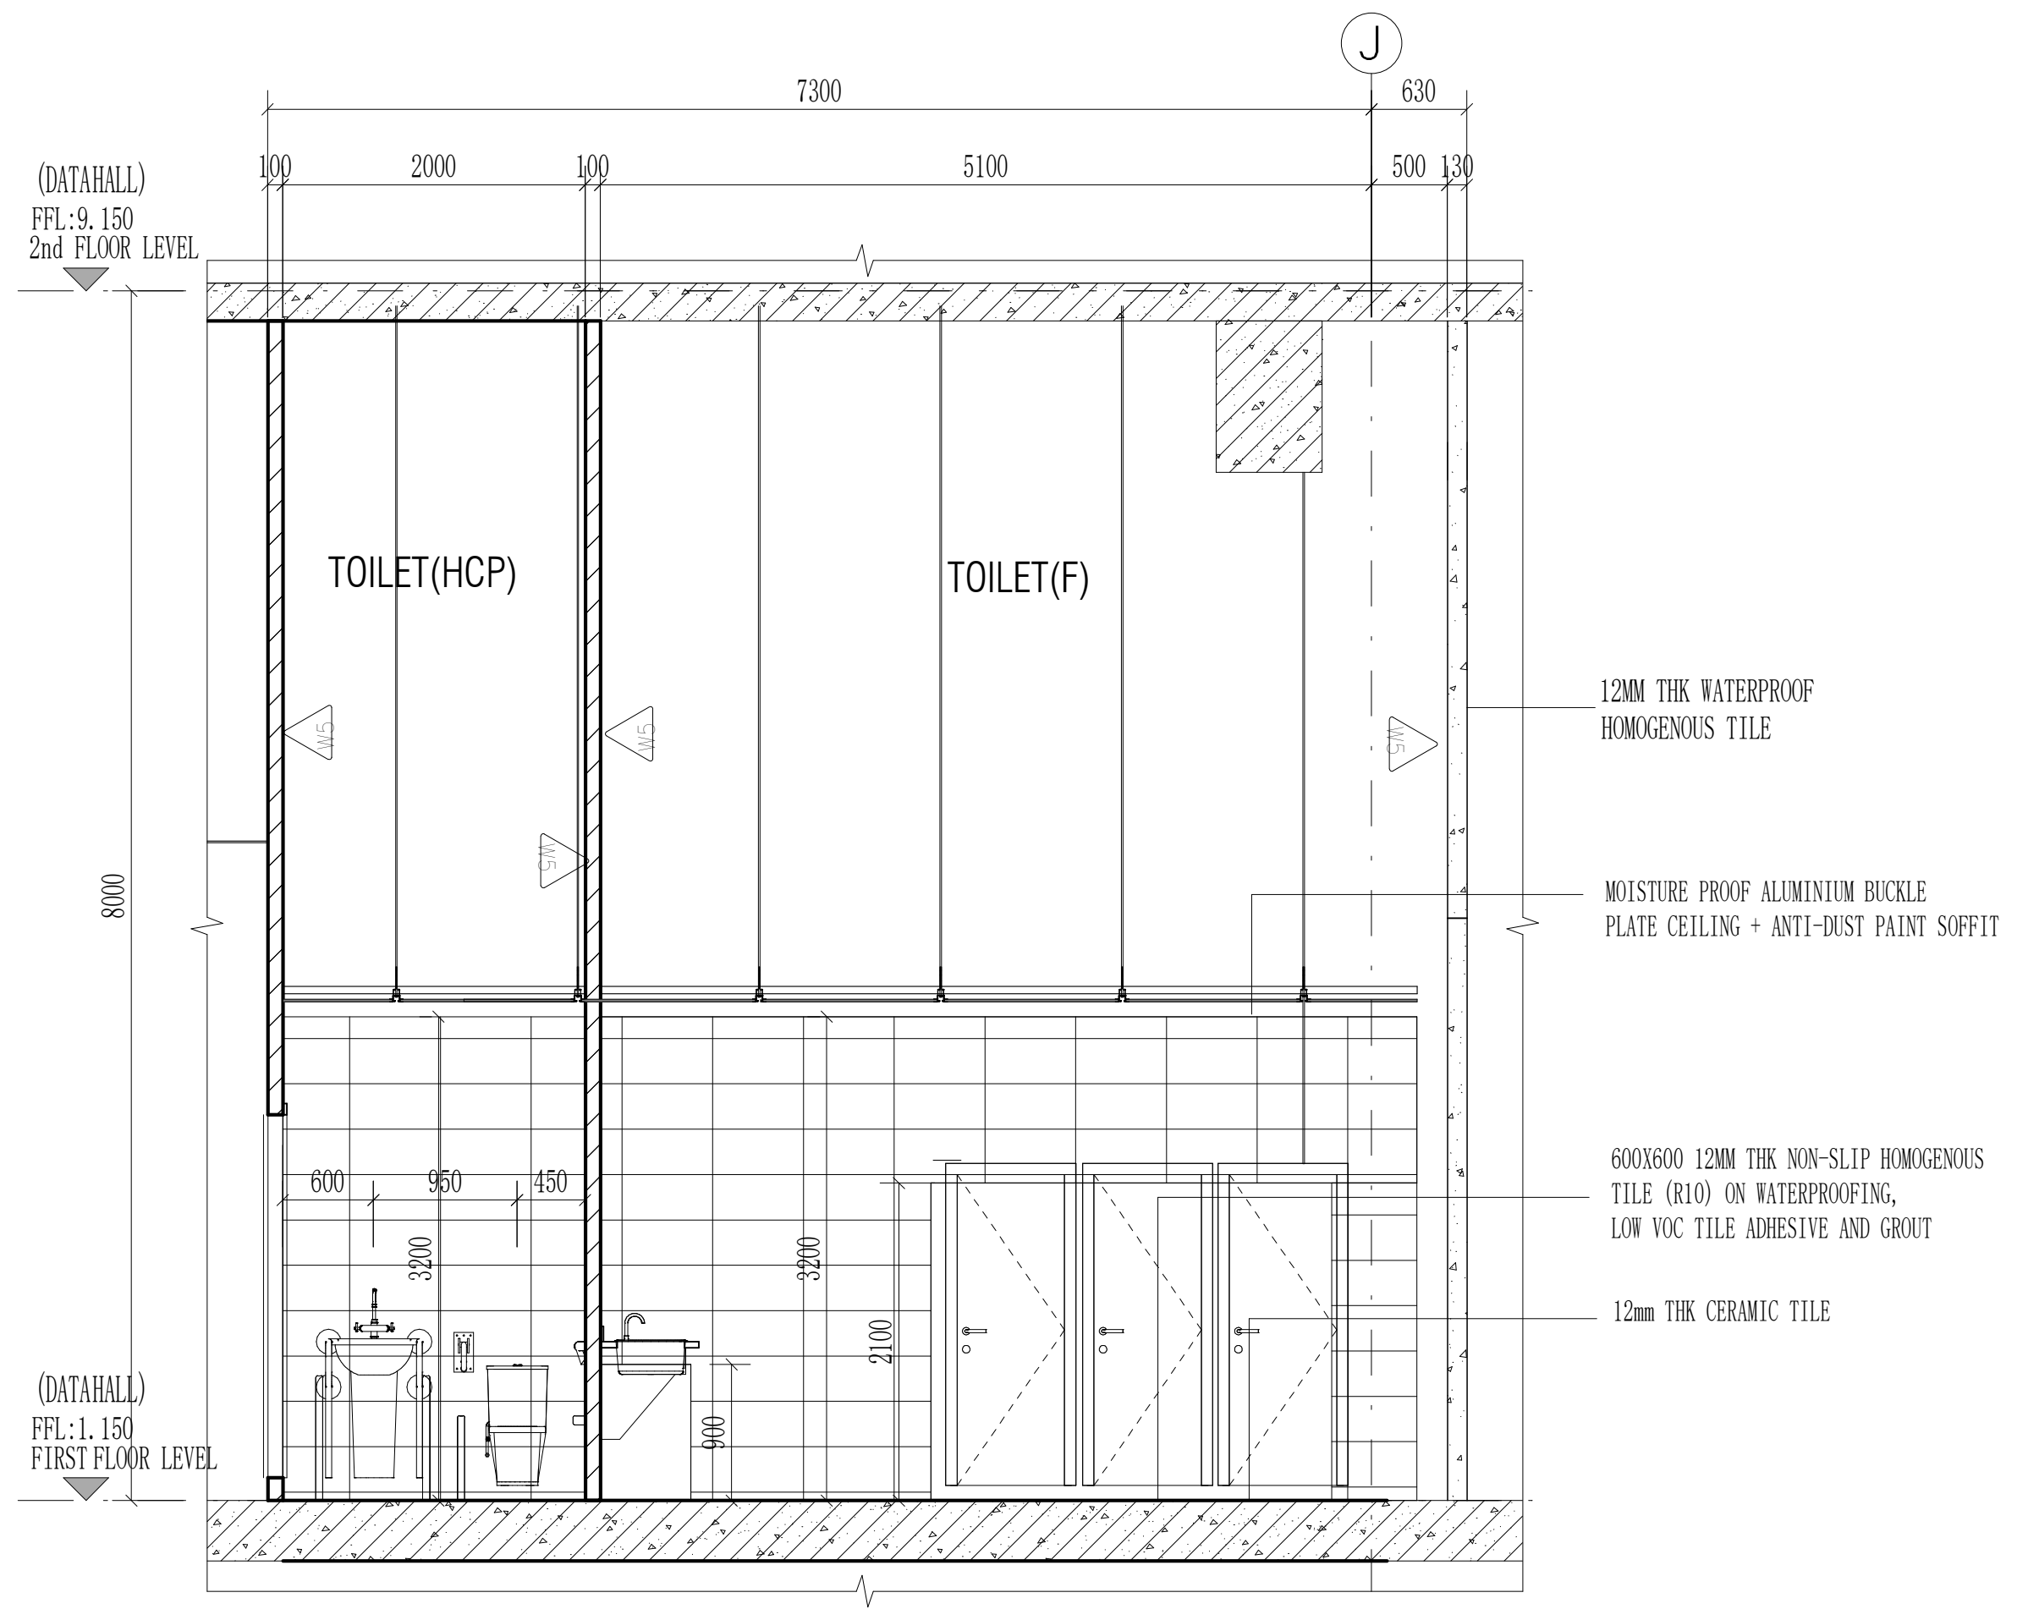
J
7300
630
100
2000
100
5100
500
130
(DATAHALL)
FFL:9.150
2nd FLOOR LEVEL
TOILET(HCP)
TOILET(F)
W5
8000
600
950
450
3200
2100
900
(DATAHALL)
FFL:1.150
FIRST FLOOR LEVEL
12MM THK WATERPROOF
HOMOGENOUS TILE
MOISTURE PROOF ALUMINIUM BUCKLE
PLATE CEILING + ANTI-DUST PAINT SOFFIT
600X600 12MM THK NON-SLIP HOMOGENOUS
TILE (R10) ON WATERPROOFING,
LOW VOC TILE ADHESIVE AND GROUT
12mm THK CERAMIC TILE

TOILET(F) TOILET(HCP) SECTION C-C

Scale 1:50

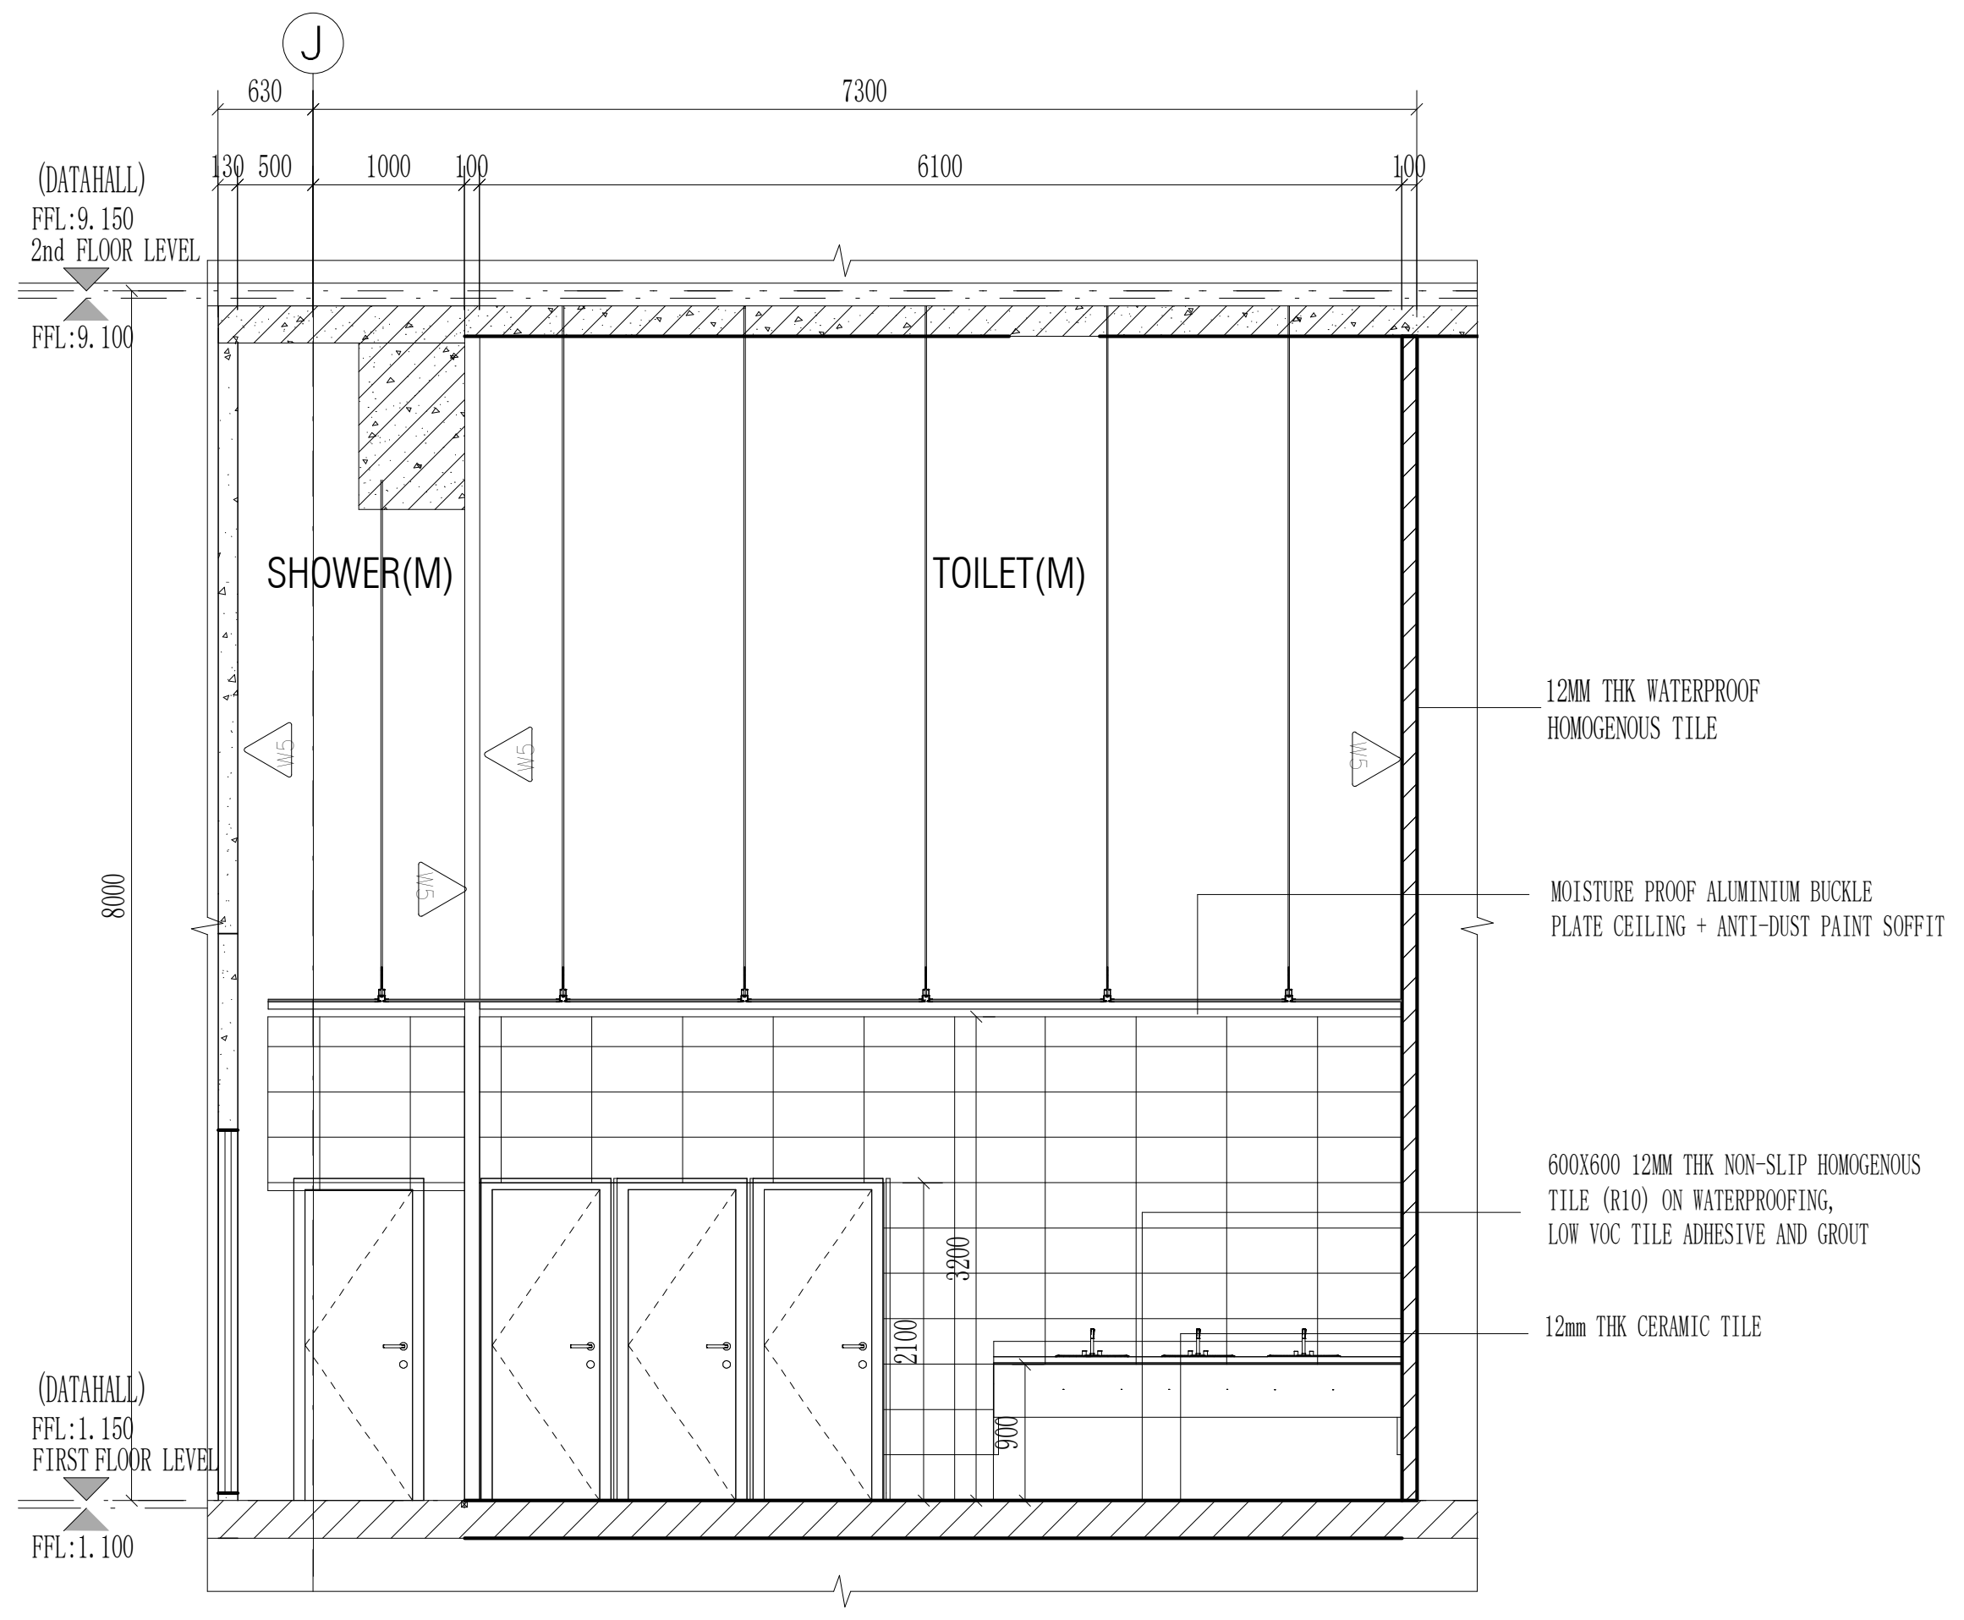
J
630
7300
130
500
1000
100
6100
100
(DATAHALL)
FFL:9.150
2nd FLOOR LEVEL
FFL:9.100
SHOWER(M)
TOILET(M)
W5
8000
3200
2100
900
(DATAHALL)
FFL:1.150
FIRST FLOOR LEVEL
FFL:1.100
12MM THK WATERPROOF
HOMOGENOUS TILE
MOISTURE PROOF ALUMINIUM BUCKLE
PLATE CEILING + ANTI-DUST PAINT SOFFIT
600X600 12MM THK NON-SLIP HOMOGENOUS
TILE (R10) ON WATERPROOFING,
LOW VOC TILE ADHESIVE AND GROUT
12mm THK CERAMIC TILE

SHOWER(M) TOILET(M) SECTION D-D

Scale 1:50

CLIENT :

GULF EDGE DC 01

87 Wireless Road, M Thai Tower 11th. Floor, All Seasons Place, Lumpini,
Pathumwan, Bangkok 10330, Thailand

CONTRACTOR :

华西发展(泰国)有限公司
บริษัท หัวซือ ดีเวลลอปเม้นต์ (ประเทศไทย) จำกัด
HUASHI DEVELOPMENT CO.,LTD
No. 202, Room No. 1403, 14/F, Le Concorde Building,
Ratchadapisek Road, Huaykhwang Sub-District,
Huaykhwang District, Bangkok Metropolitan 10310.

CONSULTANT :

บริษัท เอ อาร์ เบย์ จำกัด
ARbay Company Limited
31 st Floor Bangkok Insurance Building
25 South Sathorn road Thungmahamek
Sathorn Bangkok 10120 THAILAND
T +66 (0) 2286 8199
F +66 (0) 2286 2863
info@arbay.co.th

CONSULTANT :

Qbic Engineers & Architects Co.,Ltd.
8 Soi KALONG 4 SANAMBINNAM ROAD,
THASAI SUB-DISTRICT, MUANG NONTHABURI DISTRICT
, NONTHABURI.
Tel 662-950-4374
Fax 662-580-3231
E-Mail : qbic@qbic.co.th, www.qbic.co.th
QBIC ENGINEERS AND ARCHITECTS CO.,LTD.

CONSULTANT :

MITR TECHNICAL CONSULTANT CO.,LTD.
1168/8 12th FLOOR, LUMPINI TOWER BUILDING,
RAMA IV RD., THUNGMAHAMEK, SATHORN, BANGKOK 10120, THAILAND
TEL : 0-2679-9079-84
FAX : 0-2679-9085 E-mail: mitr_dd@mitr.com

Architect : SIGNATURE
ประกิต พนานุรัตน์ วสถ. 580
ที่อยู่
251/1 ถ.จารุเมือง แขวงรองเมือง เขตปทุมวัน
กรุงเทพมหานคร โทรศัพท์ 02-286-8199

Structural Engineer : SIGNATURE
วิศวกรผู้ออกแบบโครงสร้าง
ณัฐสม สงวนวงษ์ วย 1423
ที่อยู่
2/1 ซ.รามคำแหง 150 ถ.รามคำแหง
แขวง สะพานสูง เขต สะพานสูง กทม. 10240

Structural Inspector : SIGNATURE
วิศวกรผู้ตรวจสอบโครงสร้าง
โกมล จุฑาภัทร วย 964
ที่อยู่
24/18 ซ.นวมินทร์ 129 ถ. นวมินทร์
แขวง นวลจันทร์ เขต บึงกุ่ม กทม. 10230

Electrical Engineer : SIGNATURE
วิศวกรผู้ออกแบบระบบไฟฟ้ากำลัง
นายสุภัทร บูรณวิทย์ วฟก.1265
ที่อยู่
21 ซอยทานสัมฤทธิ์ 13
ตำบลท่าทราย อ.เมืองนนทบุรี จ.นนทบุรี 11000

Mechanical Engineer : SIGNATURE
วิศวกรผู้ออกแบบระบบเครื่องกลและปรับอากาศ
นายประสิทธิ์ เกี้ยวสุนทร วก.1221
ที่อยู่
44/372 ซอยบางกระดี่ 35/1 แขวงแสมดำ
เขตบางขุนเทียน กทม. 10150
ประสิทธิ์

Sanitary Engineer : SIGNATURE
วิศวกรผู้ออกแบบระบบสุขาภิบาล และดับเพลิง
นายทศวรรษ สนั่นฤทธิ์ วส. 215
ที่อยู่
บ้านเลขที่ 99/107 หมู่ที่ 3 ต.ศีรษะจรเข้น้อย
อ.บางเสาธง จ.สมุทรปราการ 10540
ทศวรรษ

ISSUE/REVISION

REV.	DESCRIPTION	DATE
A	90% DEVELOPED	09/05/2026

PROJECT NAME :

GEDC 01

LOCATION:
Nikhom Phattana district, Rayong ,industrial estate,CPGC

BUILDING :
MAIN BUILDING

90% DEVELOPED

TITLE :

ROOM DETAIL-1F-TOILET &
SHOWER(F)、TOILET &
SHOWER(M)、TOILET(HCP)

JOB NO.
SCALE 1 : 50
DRAWN NXR
REF.
CHECKED LJC
DWG. NO. MPK01A-90-A-RD-114
APPROVED LXD
DATE 2026.05.09

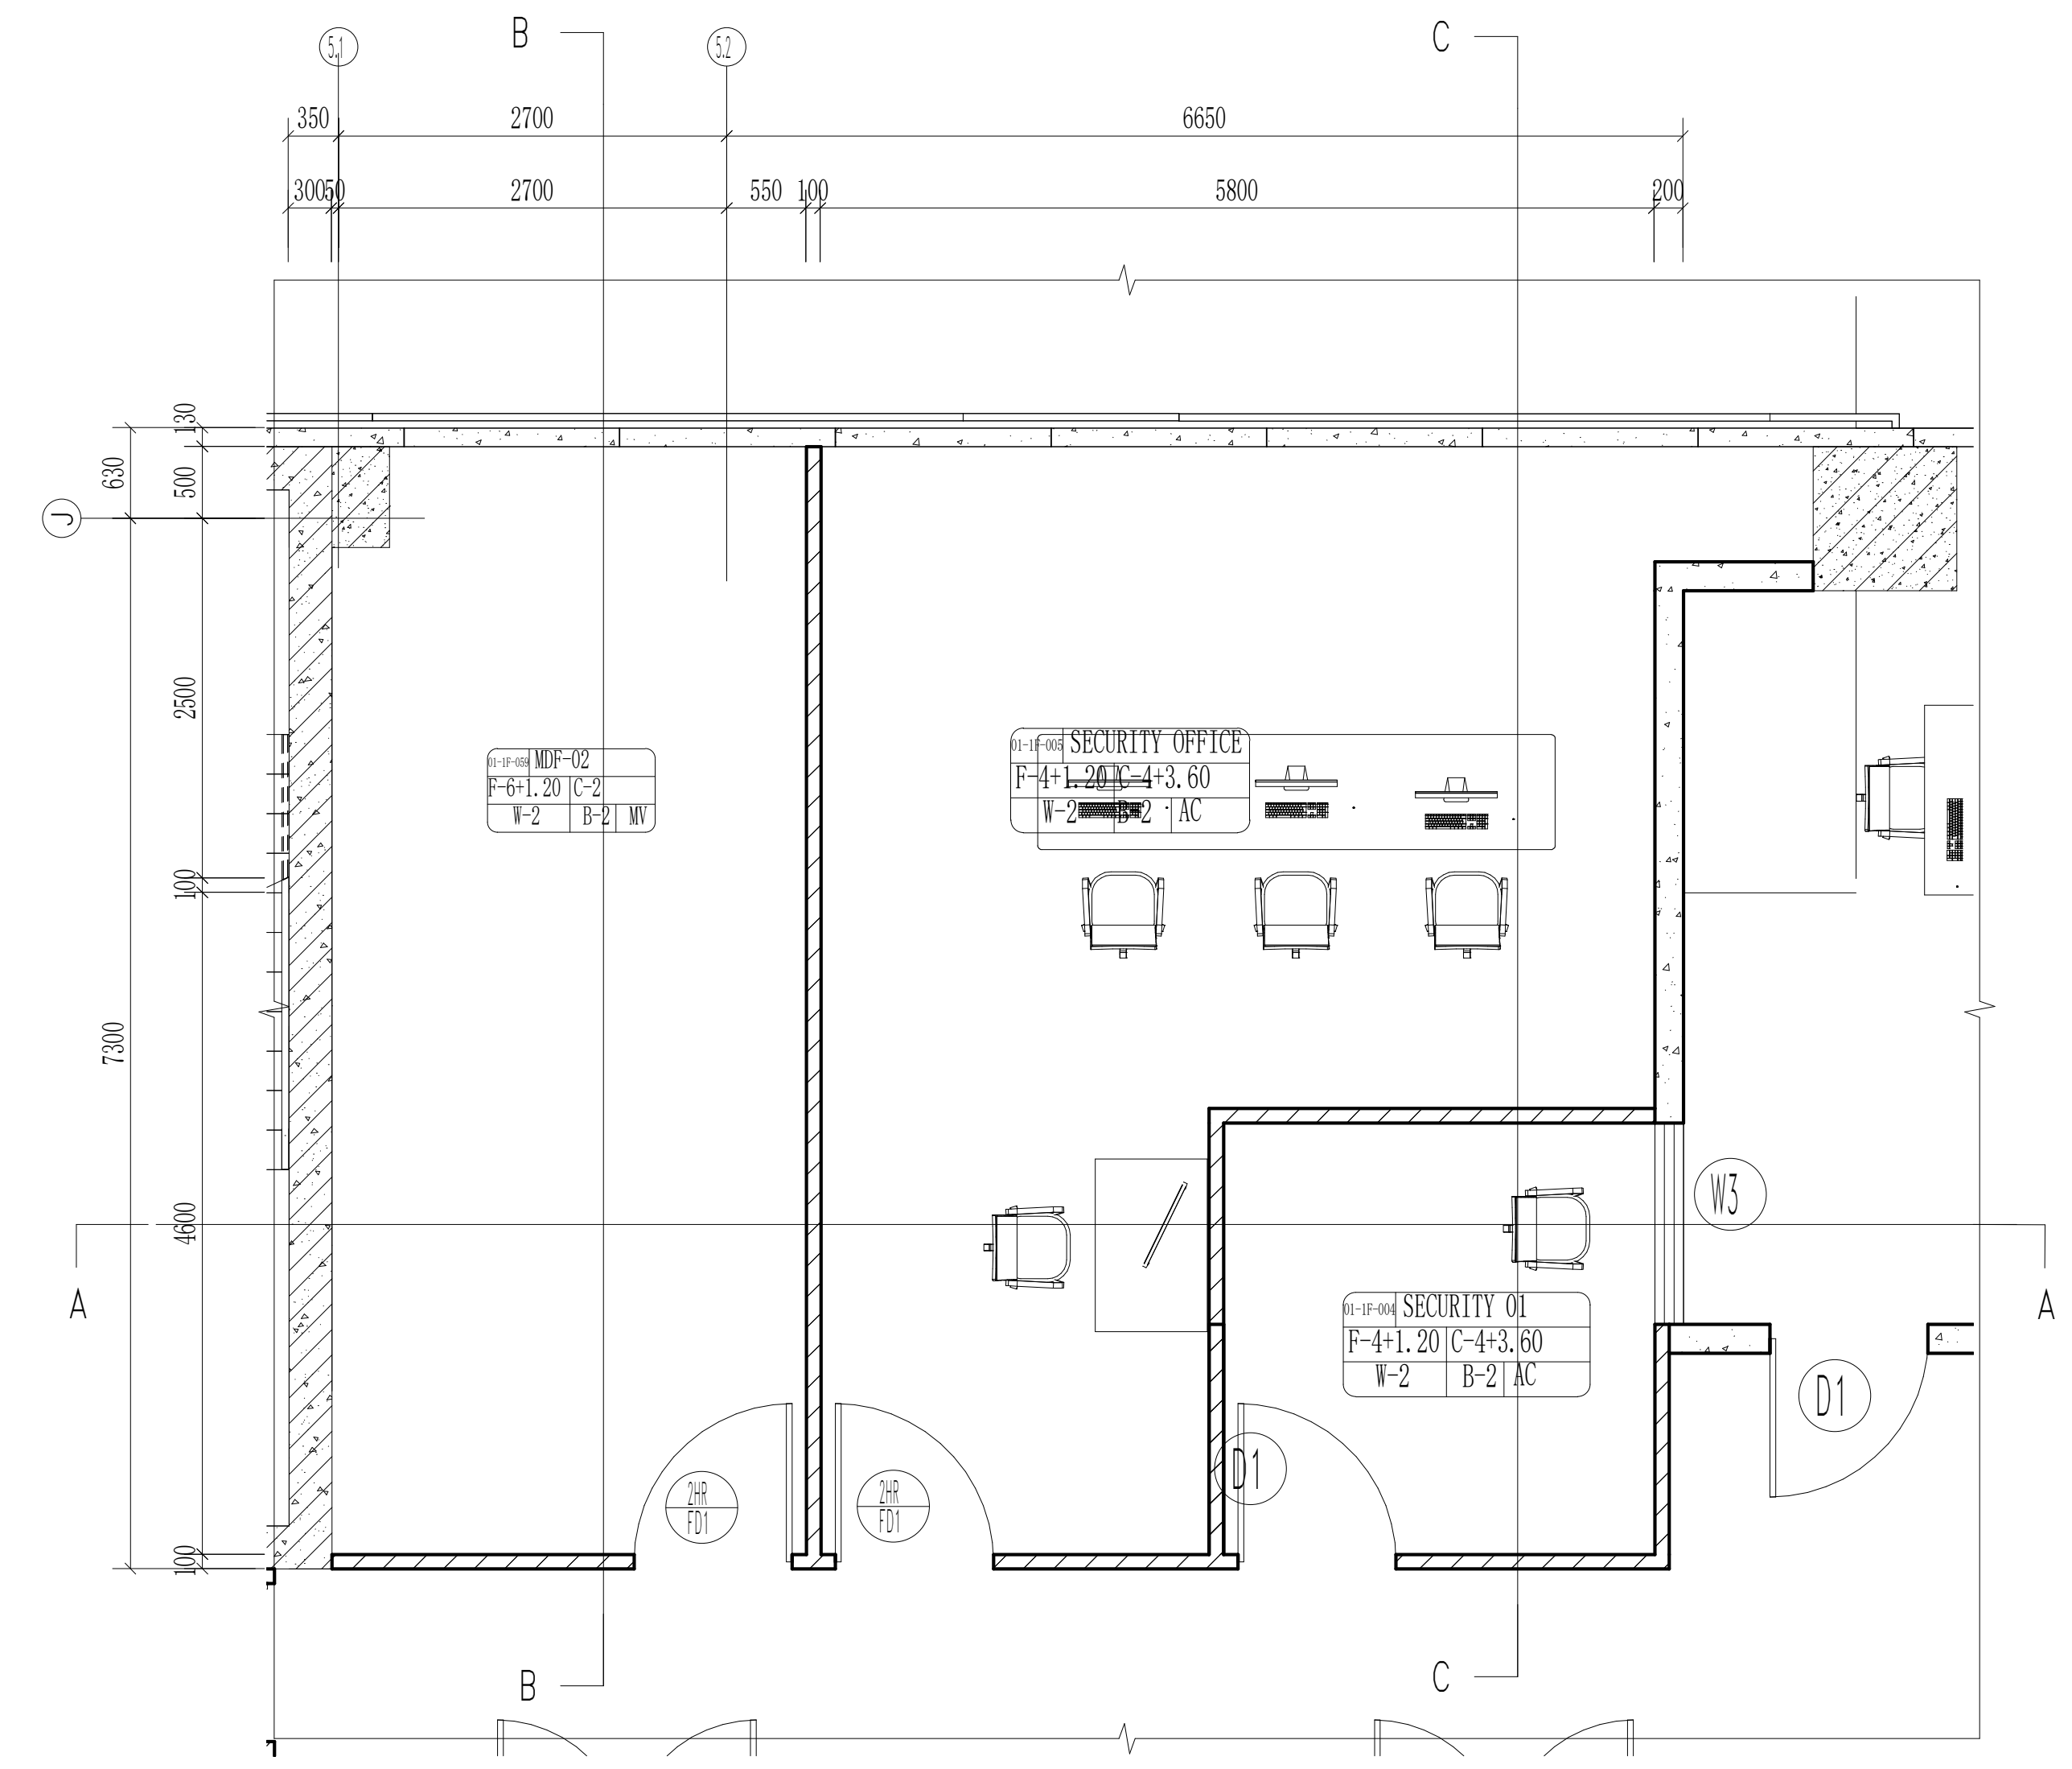
B
C
A
A
D1
D1
W3
MDF 02
SECURITY OFFICE
SECURITY 01
350
2700
6650
300
550
5800
200
7300

MDF 02、SECURITY 01、SECURITY OFFICE FLOOR PLAN

Scale 1:50

THE "SFL" MARKED IN THE DRAWING REFERS TO THE STRUCTURAL FLOOR LEVEL, WHILE THE FINISHED FLOOR LEVEL (FFL) IS DETERMINED BASED ON FLOOR FINISHES.

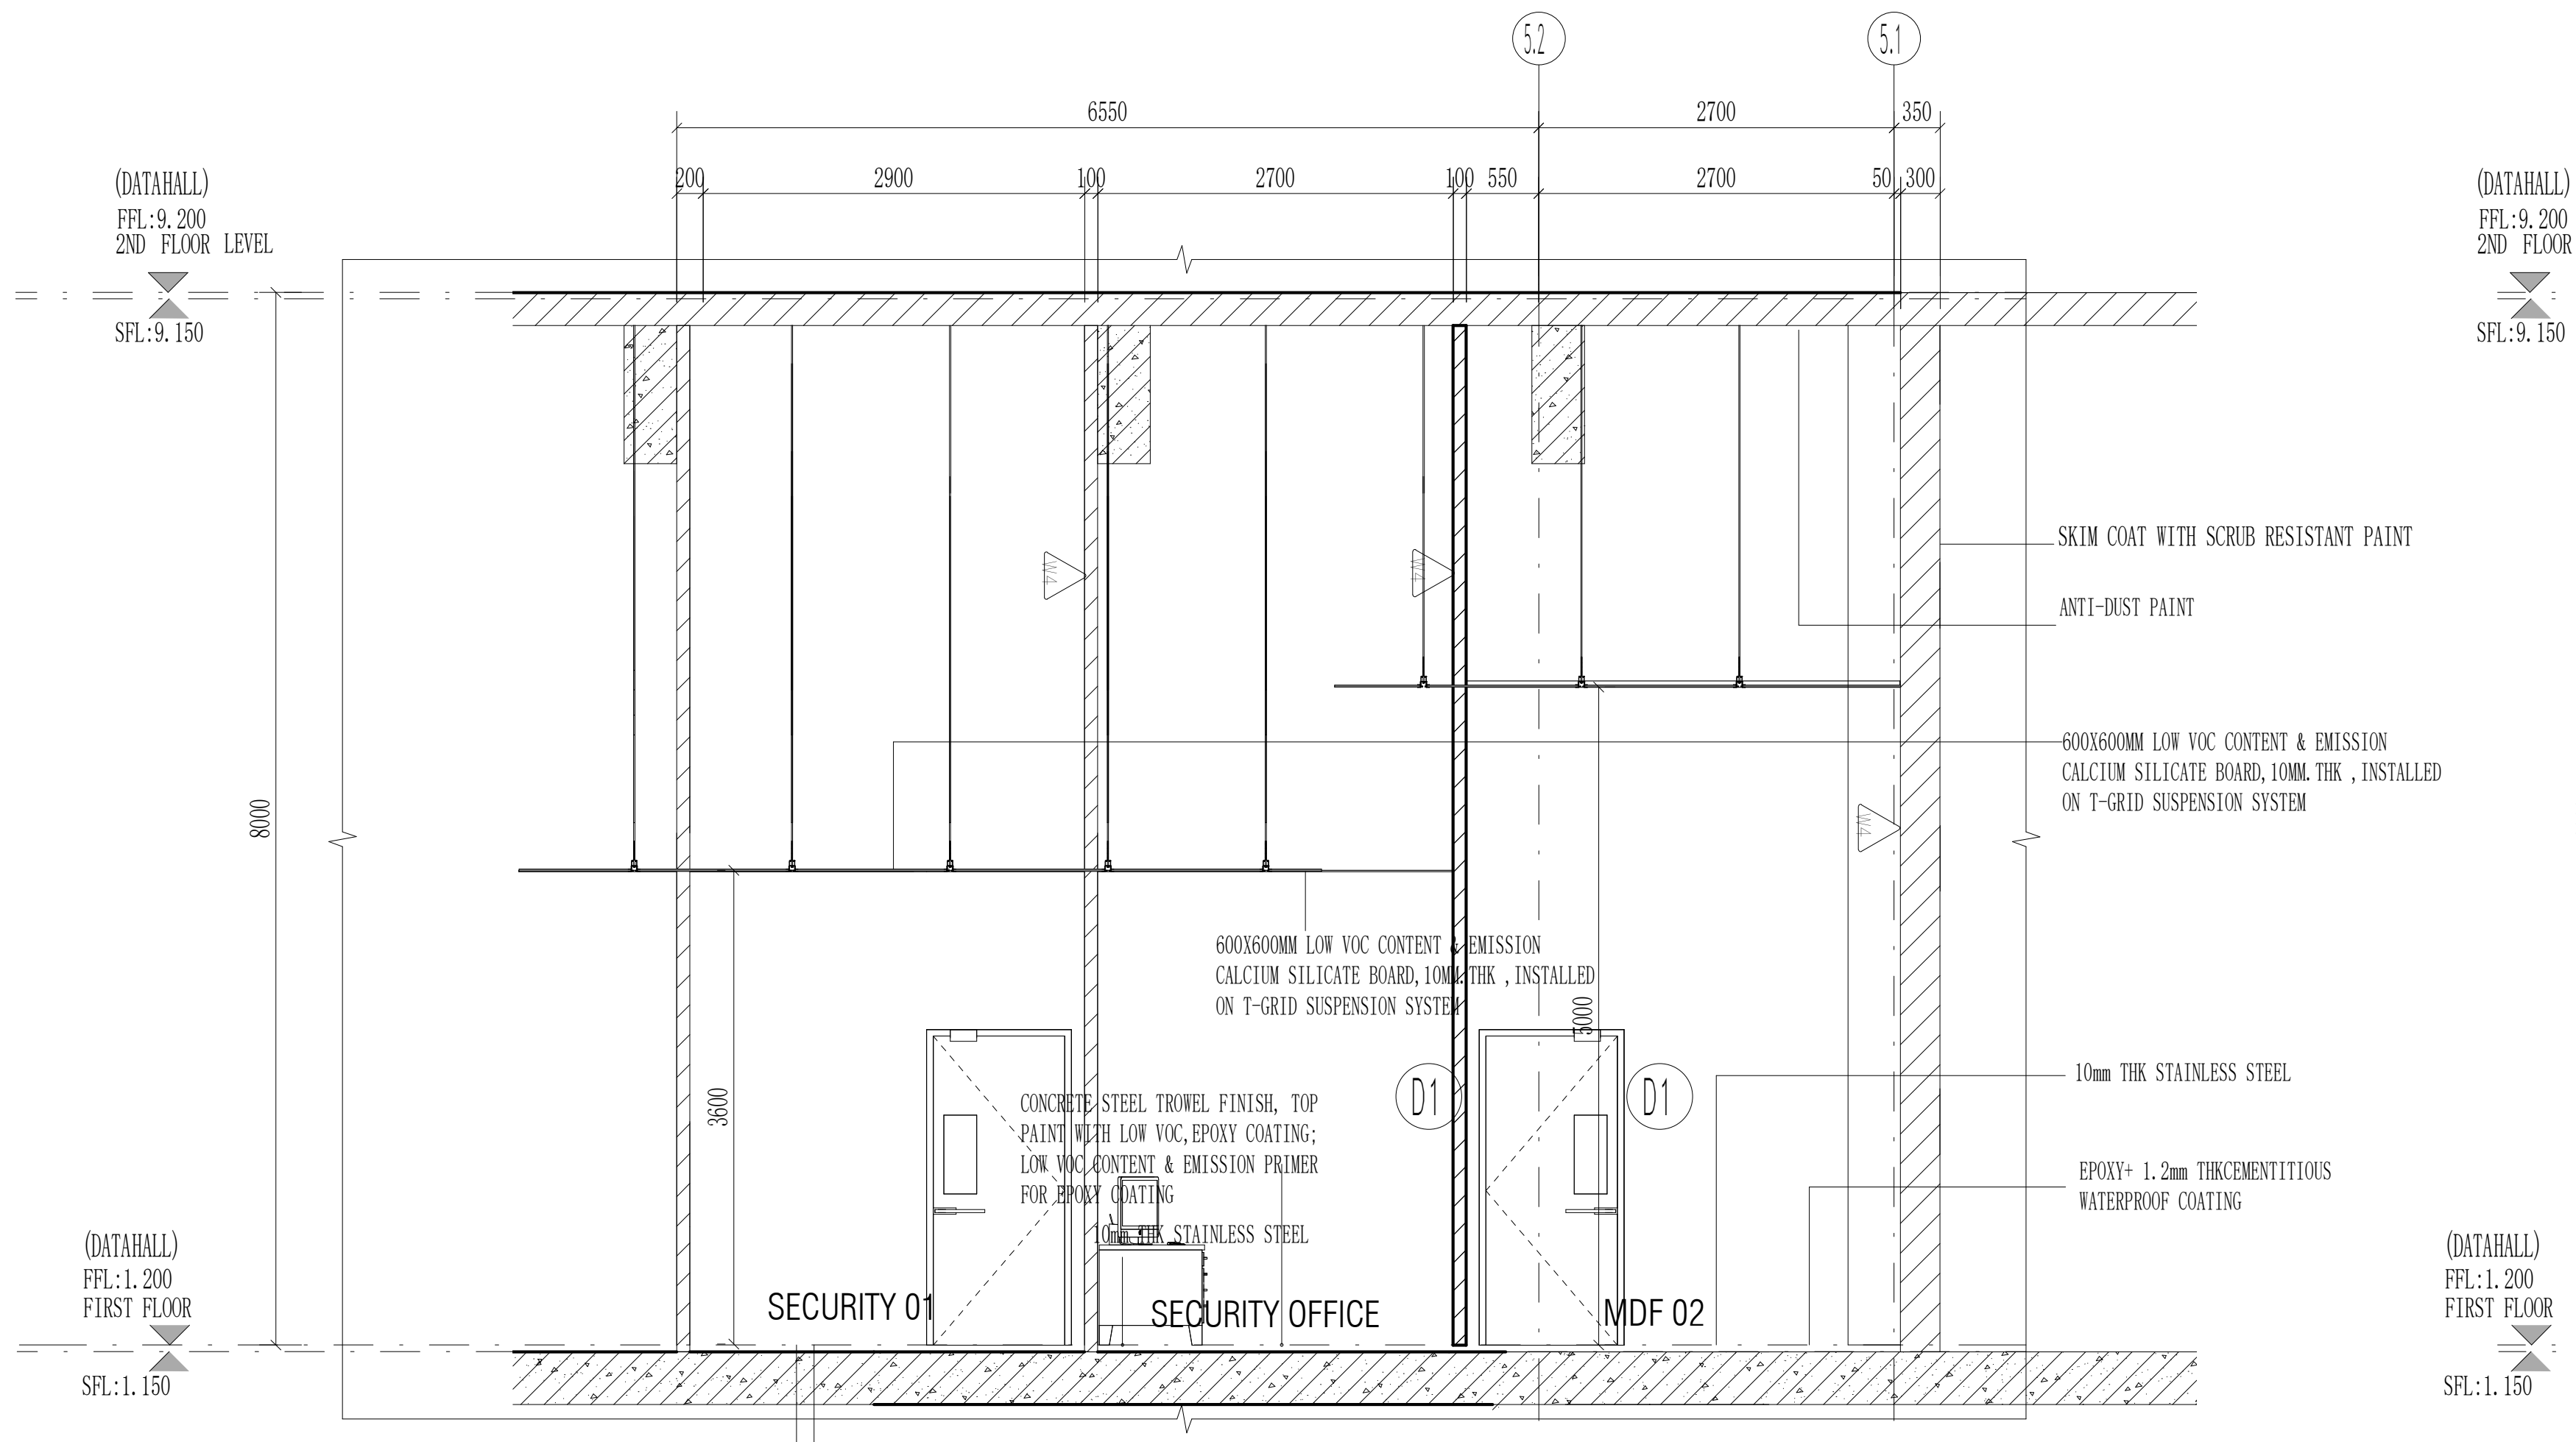
5.2
5.1
6550
2700
350
200
2900
100
2700
100 550
2700
50 300
(DATAHALL)
FFL:9.200
2ND FLOOR LEVEL
SFL:9.150
(DATAHALL)
FFL:1.200
FIRST FLOOR
SFL:1.150
8000
3600
3000
SKIM COAT WITH SCRUB RESISTANT PAINT
ANTI-DUST PAINT
600X600MM LOW VOC CONTENT & EMISSION CALCIUM SILICATE BOARD,10MM.THK ,INSTALLED ON T-GRID SUSPENSION SYSTEM
10mm THK STAINLESS STEEL
EPOXY+ 1.2mm THKCEMENTITIOUS WATERPROOF COATING
CONCRETE STEEL TROWEL FINISH, TOP PAINT WITH LOW VOC,EPOXY COATING; LOW VOC CONTENT & EMISSION PRIMER FOR EPOXY COATING
D1
D1
SECURITY 01
SECURITY OFFICE
MDF 02
10mm THK STAINLESS STEEL
CONCRETE STEEL TROWEL FINISH, TOP PAINT WITH LOW VOC,EPOXY COATING; LOW VOC CONTENT & EMISSION PRIMER FOR EPOXY COATING

MDF 02、SECURITY 01、SECURITY OFFICE SECTION A-A

Scale 1:50

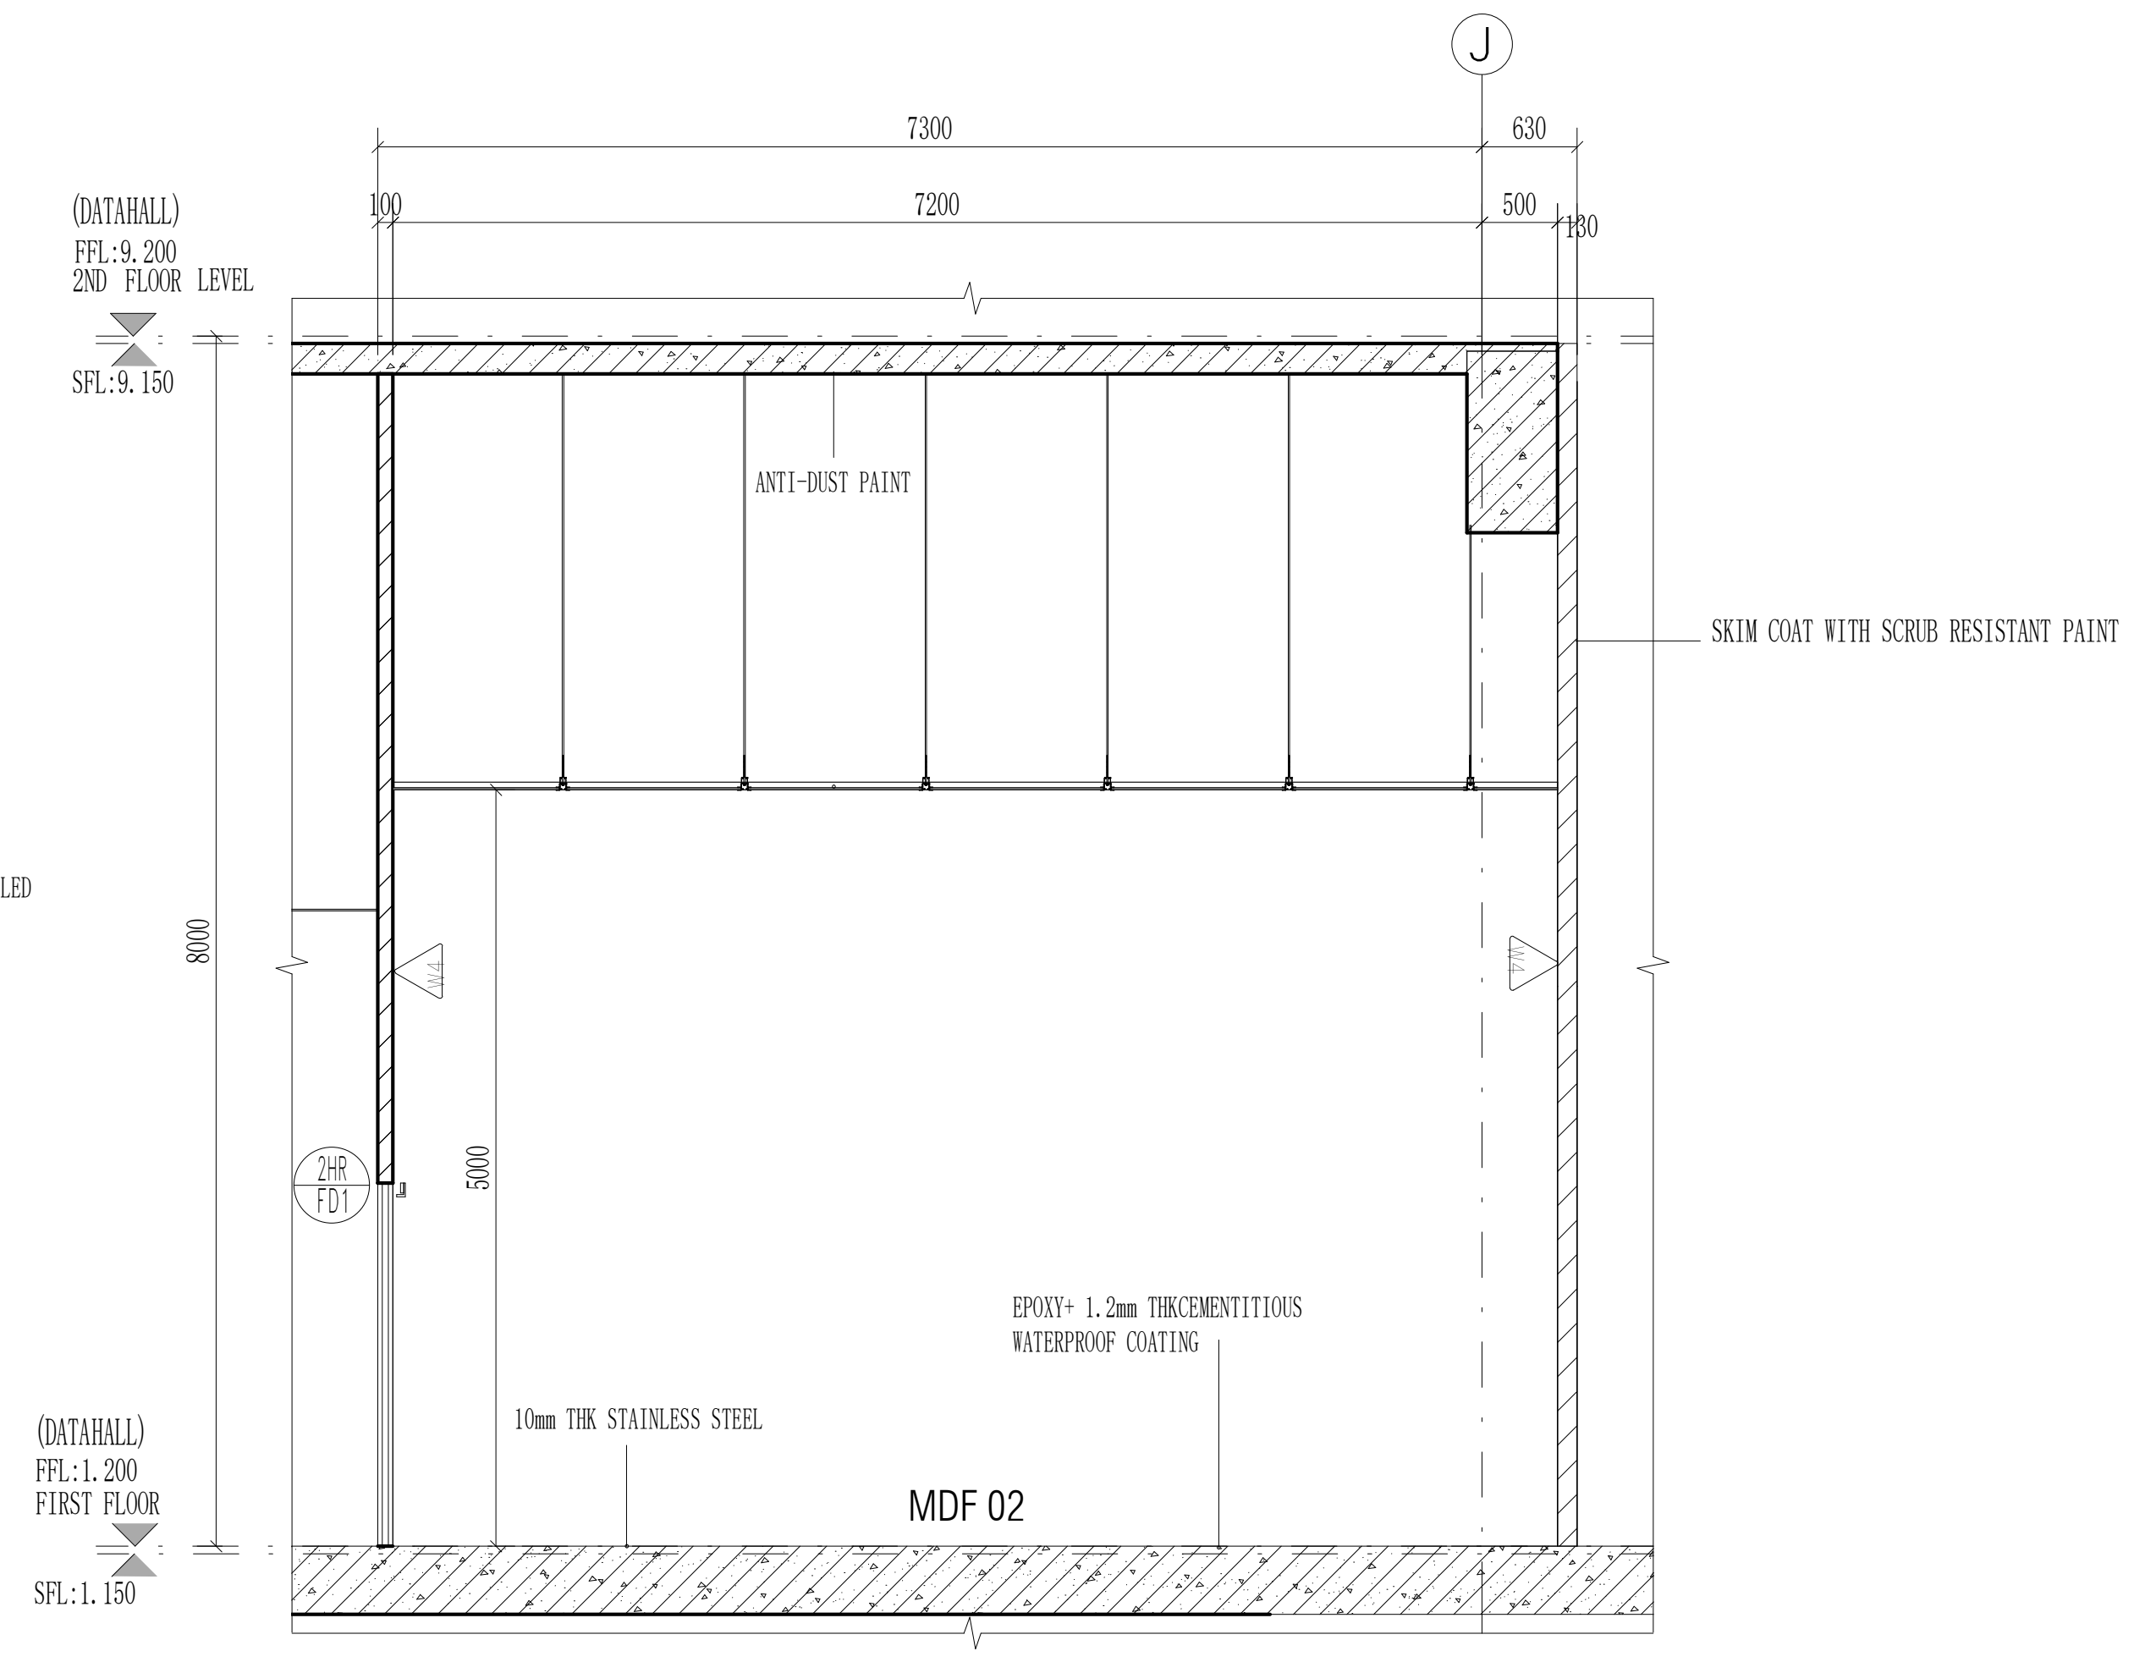
J
7300
630
100
7200
500
130
(DATAHALL)
FFL:9.200
2ND FLOOR LEVEL
SFL:9.150
(DATAHALL)
FFL:1.200
FIRST FLOOR
SFL:1.150
8000
5000
ANTI-DUST PAINT
SKIM COAT WITH SCRUB RESISTANT PAINT
2HR
FD1
EPOXY+ 1.2mm THKCEMENTITIOUS WATERPROOF COATING
10mm THK STAINLESS STEEL
MDF 02

MDF 02 SECTION B-B

Scale 1:50

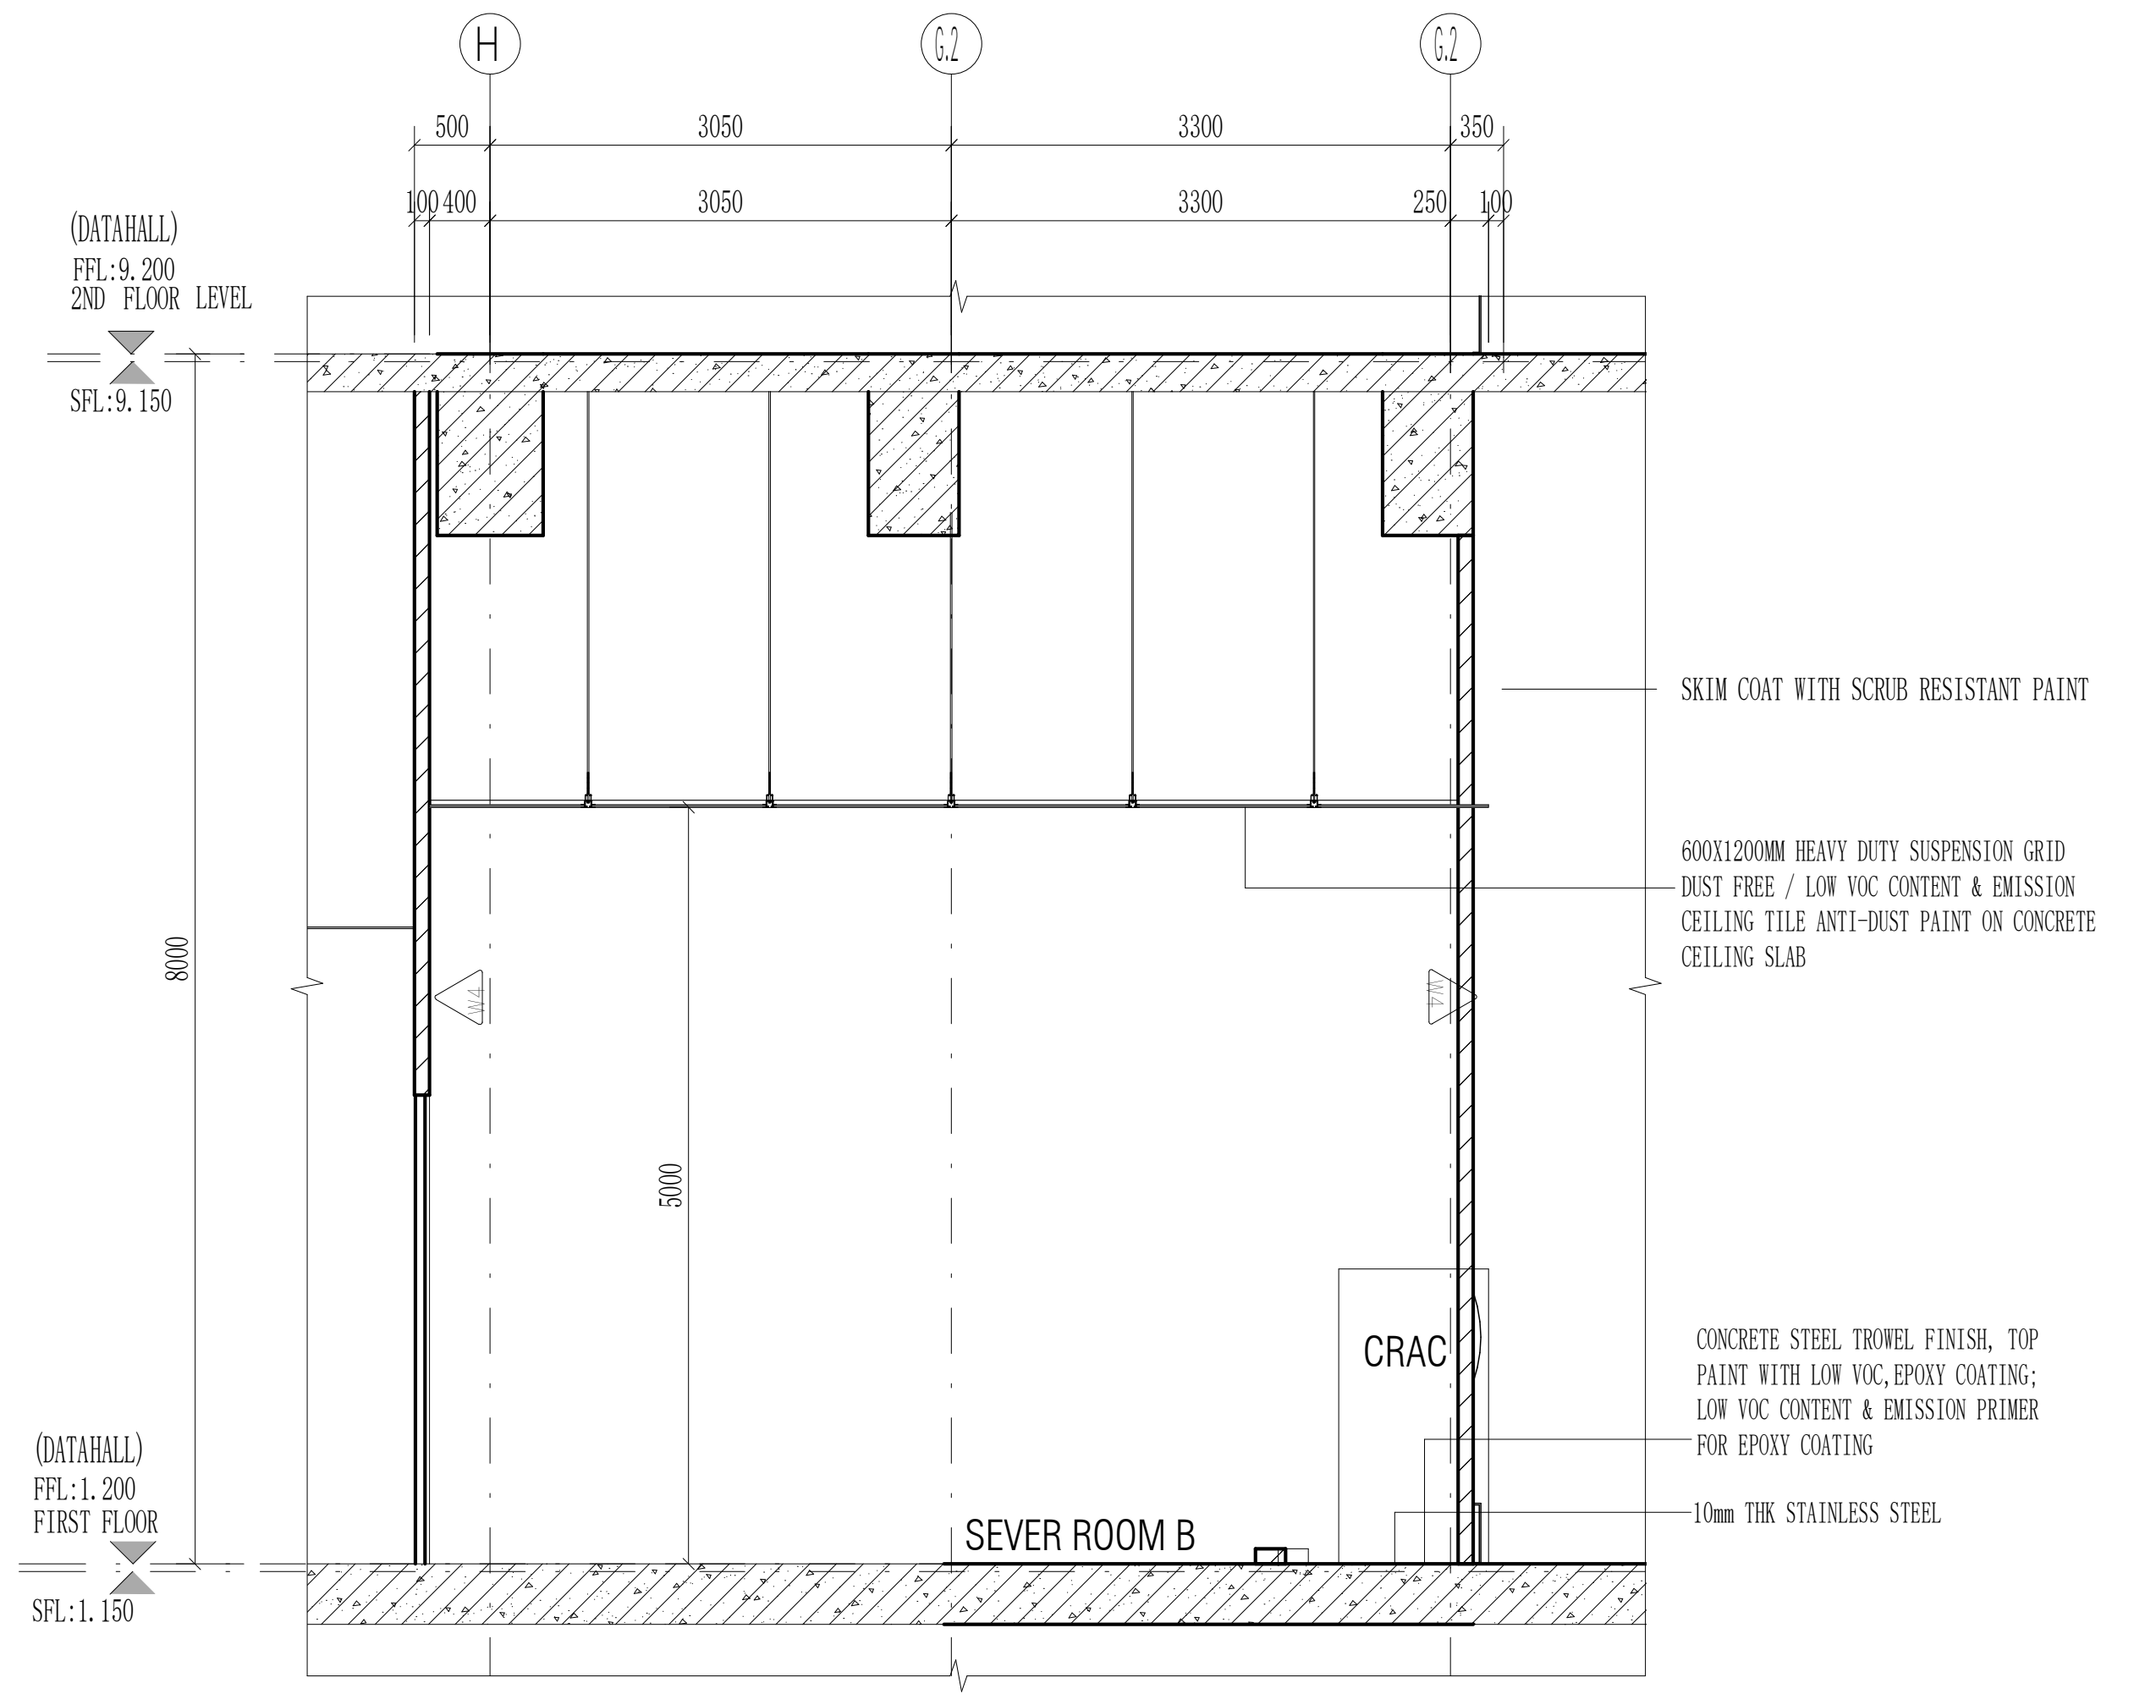
H
G.2
G.2
500
3050
3300
350
100 400
3050
3300
250
100
(DATAHALL)
FFL:9.200
2ND FLOOR LEVEL
SFL:9.150
(DATAHALL)
FFL:1.200
FIRST FLOOR
SFL:1.150
8000
5000
SKIM COAT WITH SCRUB RESISTANT PAINT
600X1200MM HEAVY DUTY SUSPENSION GRID DUST FREE / LOW VOC CONTENT & EMISSION CEILING TILE ANTI-DUST PAINT ON CONCRETE CEILING SLAB
CRAC
CONCRETE STEEL TROWEL FINISH, TOP PAINT WITH LOW VOC,EPOXY COATING; LOW VOC CONTENT & EMISSION PRIMER FOR EPOXY COATING
10mm THK STAINLESS STEEL
SEVER ROOM B

SERVER ROOM B SECTION C-C

Scale 1:50

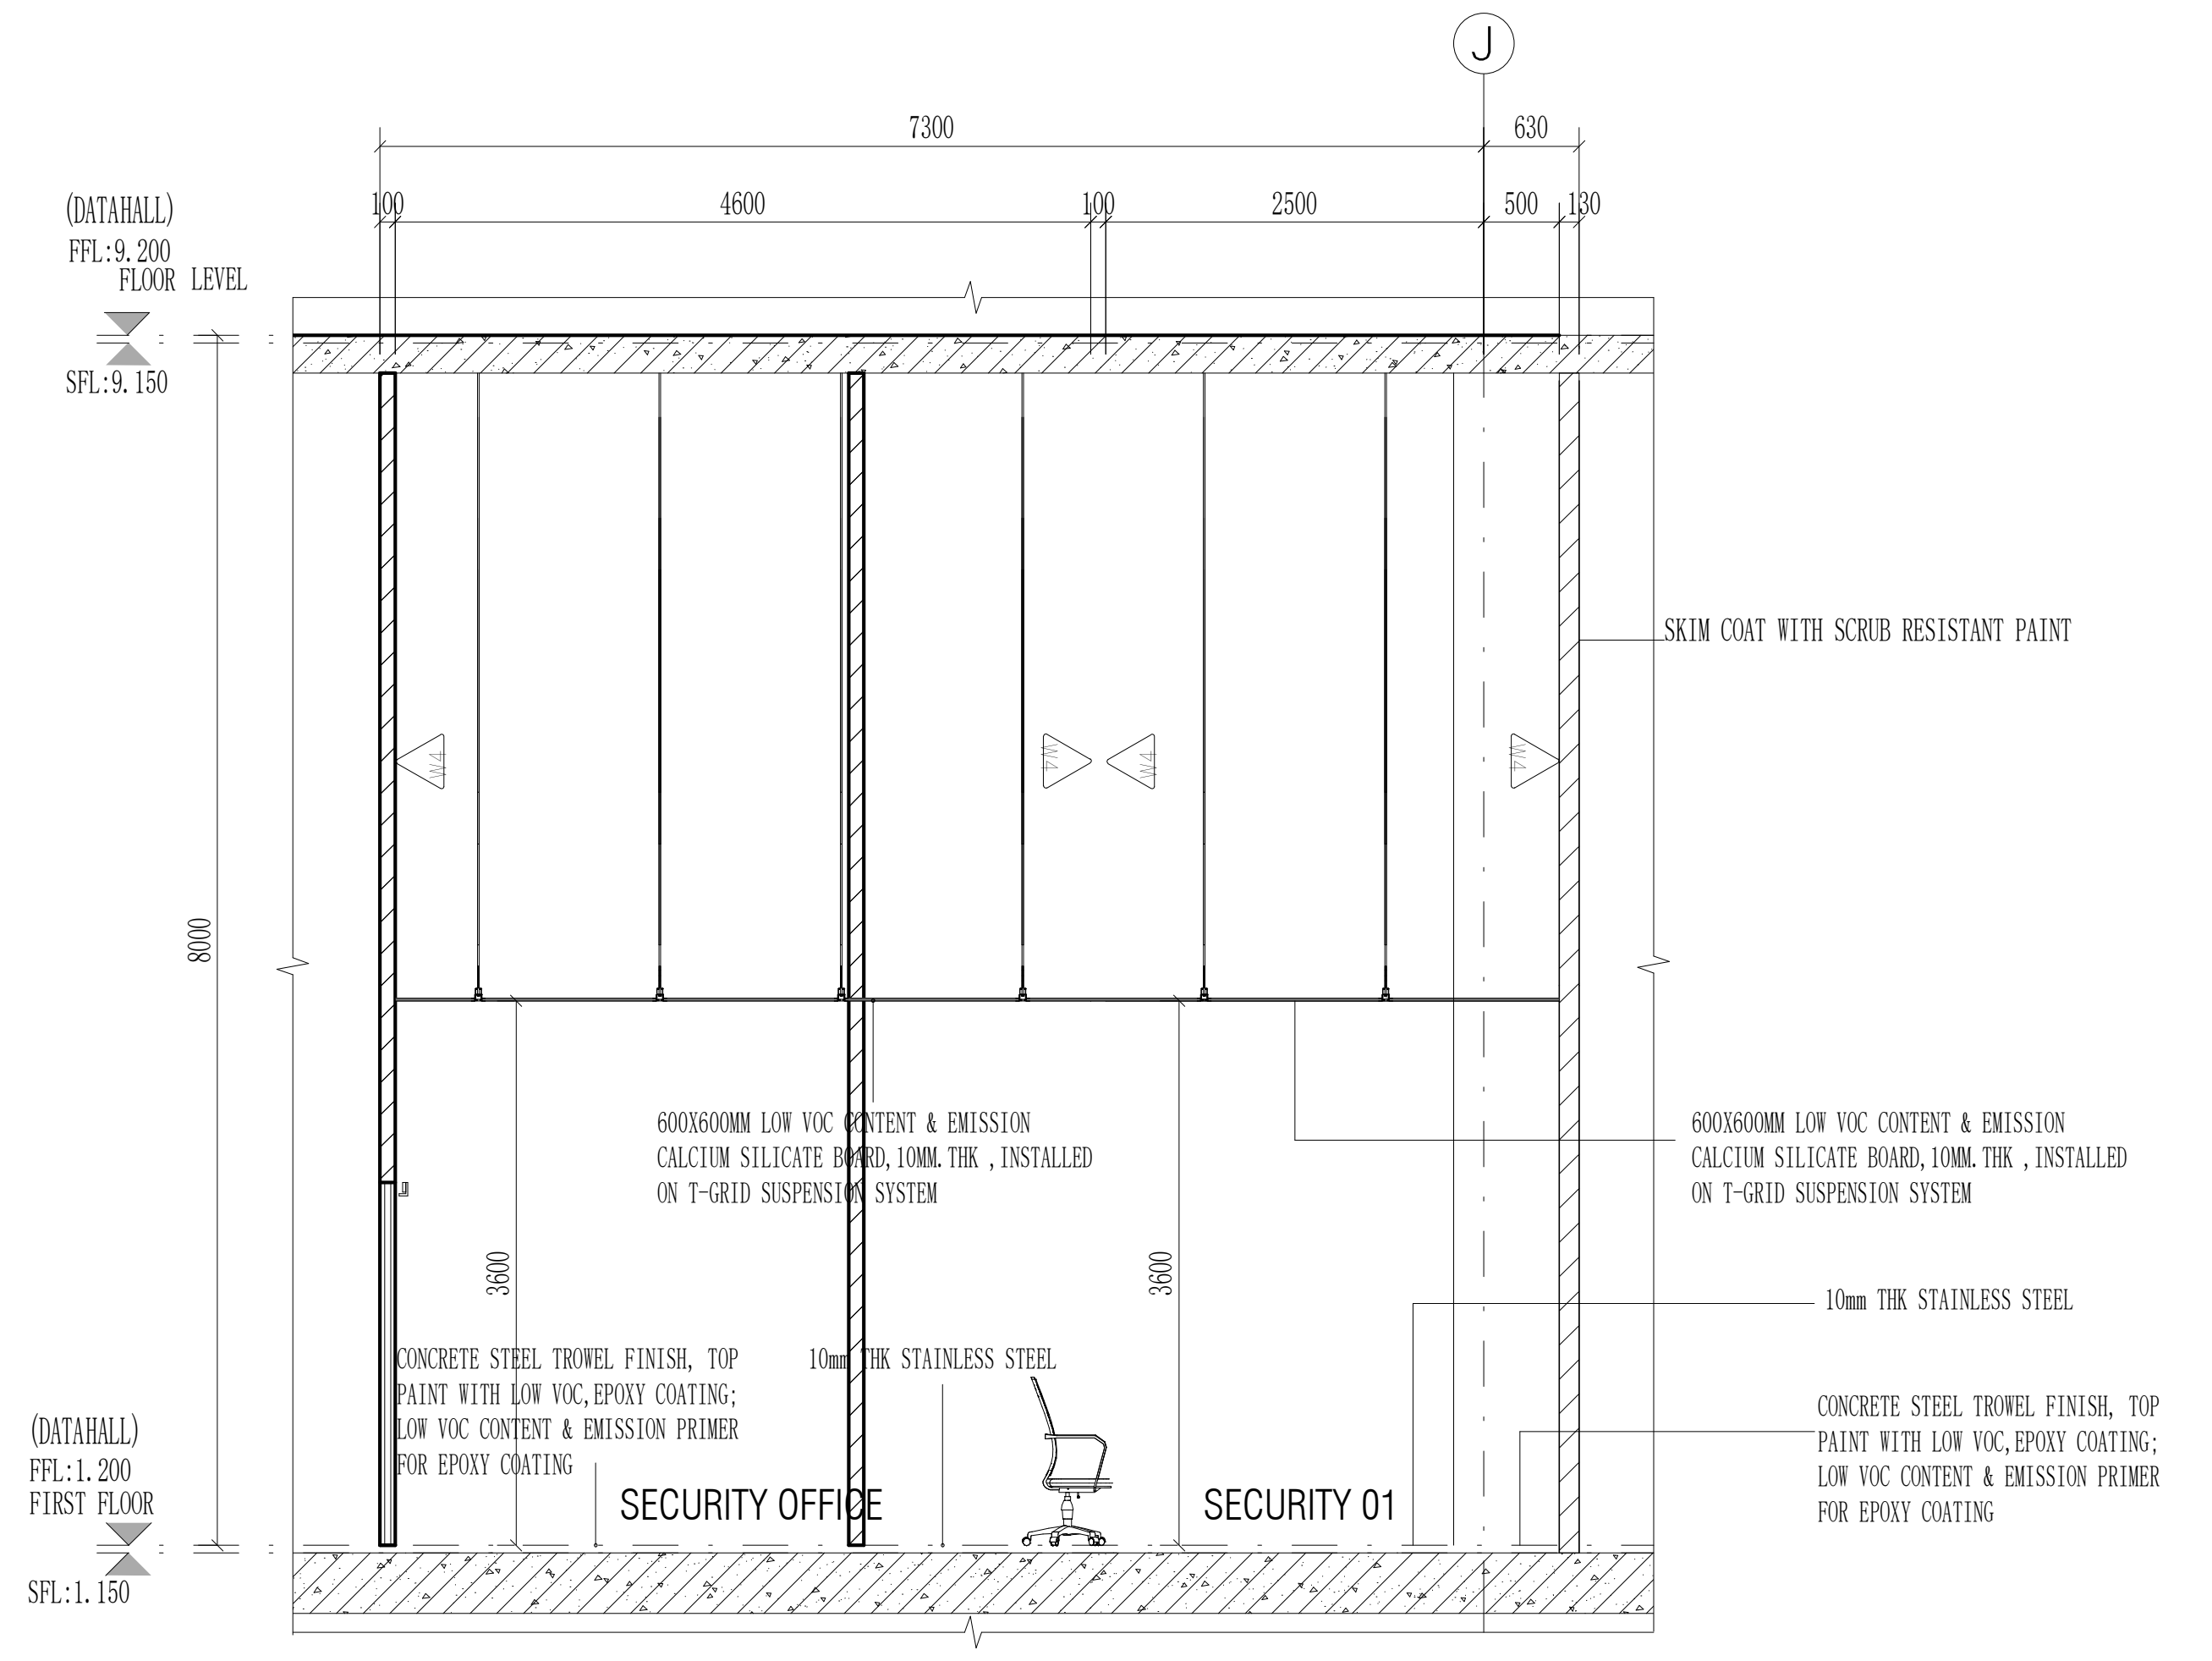
J
7300
630
100
4600
100
2500
500
130
(DATAHALL)
FFL:9.200
FLOOR LEVEL
SFL:9.150
(DATAHALL)
FFL:1.200
FIRST FLOOR
SFL:1.150
8000
3600
3600
SKIM COAT WITH SCRUB RESISTANT PAINT
600X600MM LOW VOC CONTENT & EMISSION CALCIUM SILICATE BOARD,10MM.THK ,INSTALLED ON T-GRID SUSPENSION SYSTEM
600X600MM LOW VOC CONTENT & EMISSION CALCIUM SILICATE BOARD,10MM.THK ,INSTALLED ON T-GRID SUSPENSION SYSTEM
10mm THK STAINLESS STEEL
CONCRETE STEEL TROWEL FINISH, TOP PAINT WITH LOW VOC,EPOXY COATING; LOW VOC CONTENT & EMISSION PRIMER FOR EPOXY COATING
10mm THK STAINLESS STEEL
CONCRETE STEEL TROWEL FINISH, TOP PAINT WITH LOW VOC,EPOXY COATING; LOW VOC CONTENT & EMISSION PRIMER FOR EPOXY COATING
SECURITY OFFICE
SECURITY 01

SECURITY 01、SECURITY OFFICE SECTION C-C

Scale 1:50

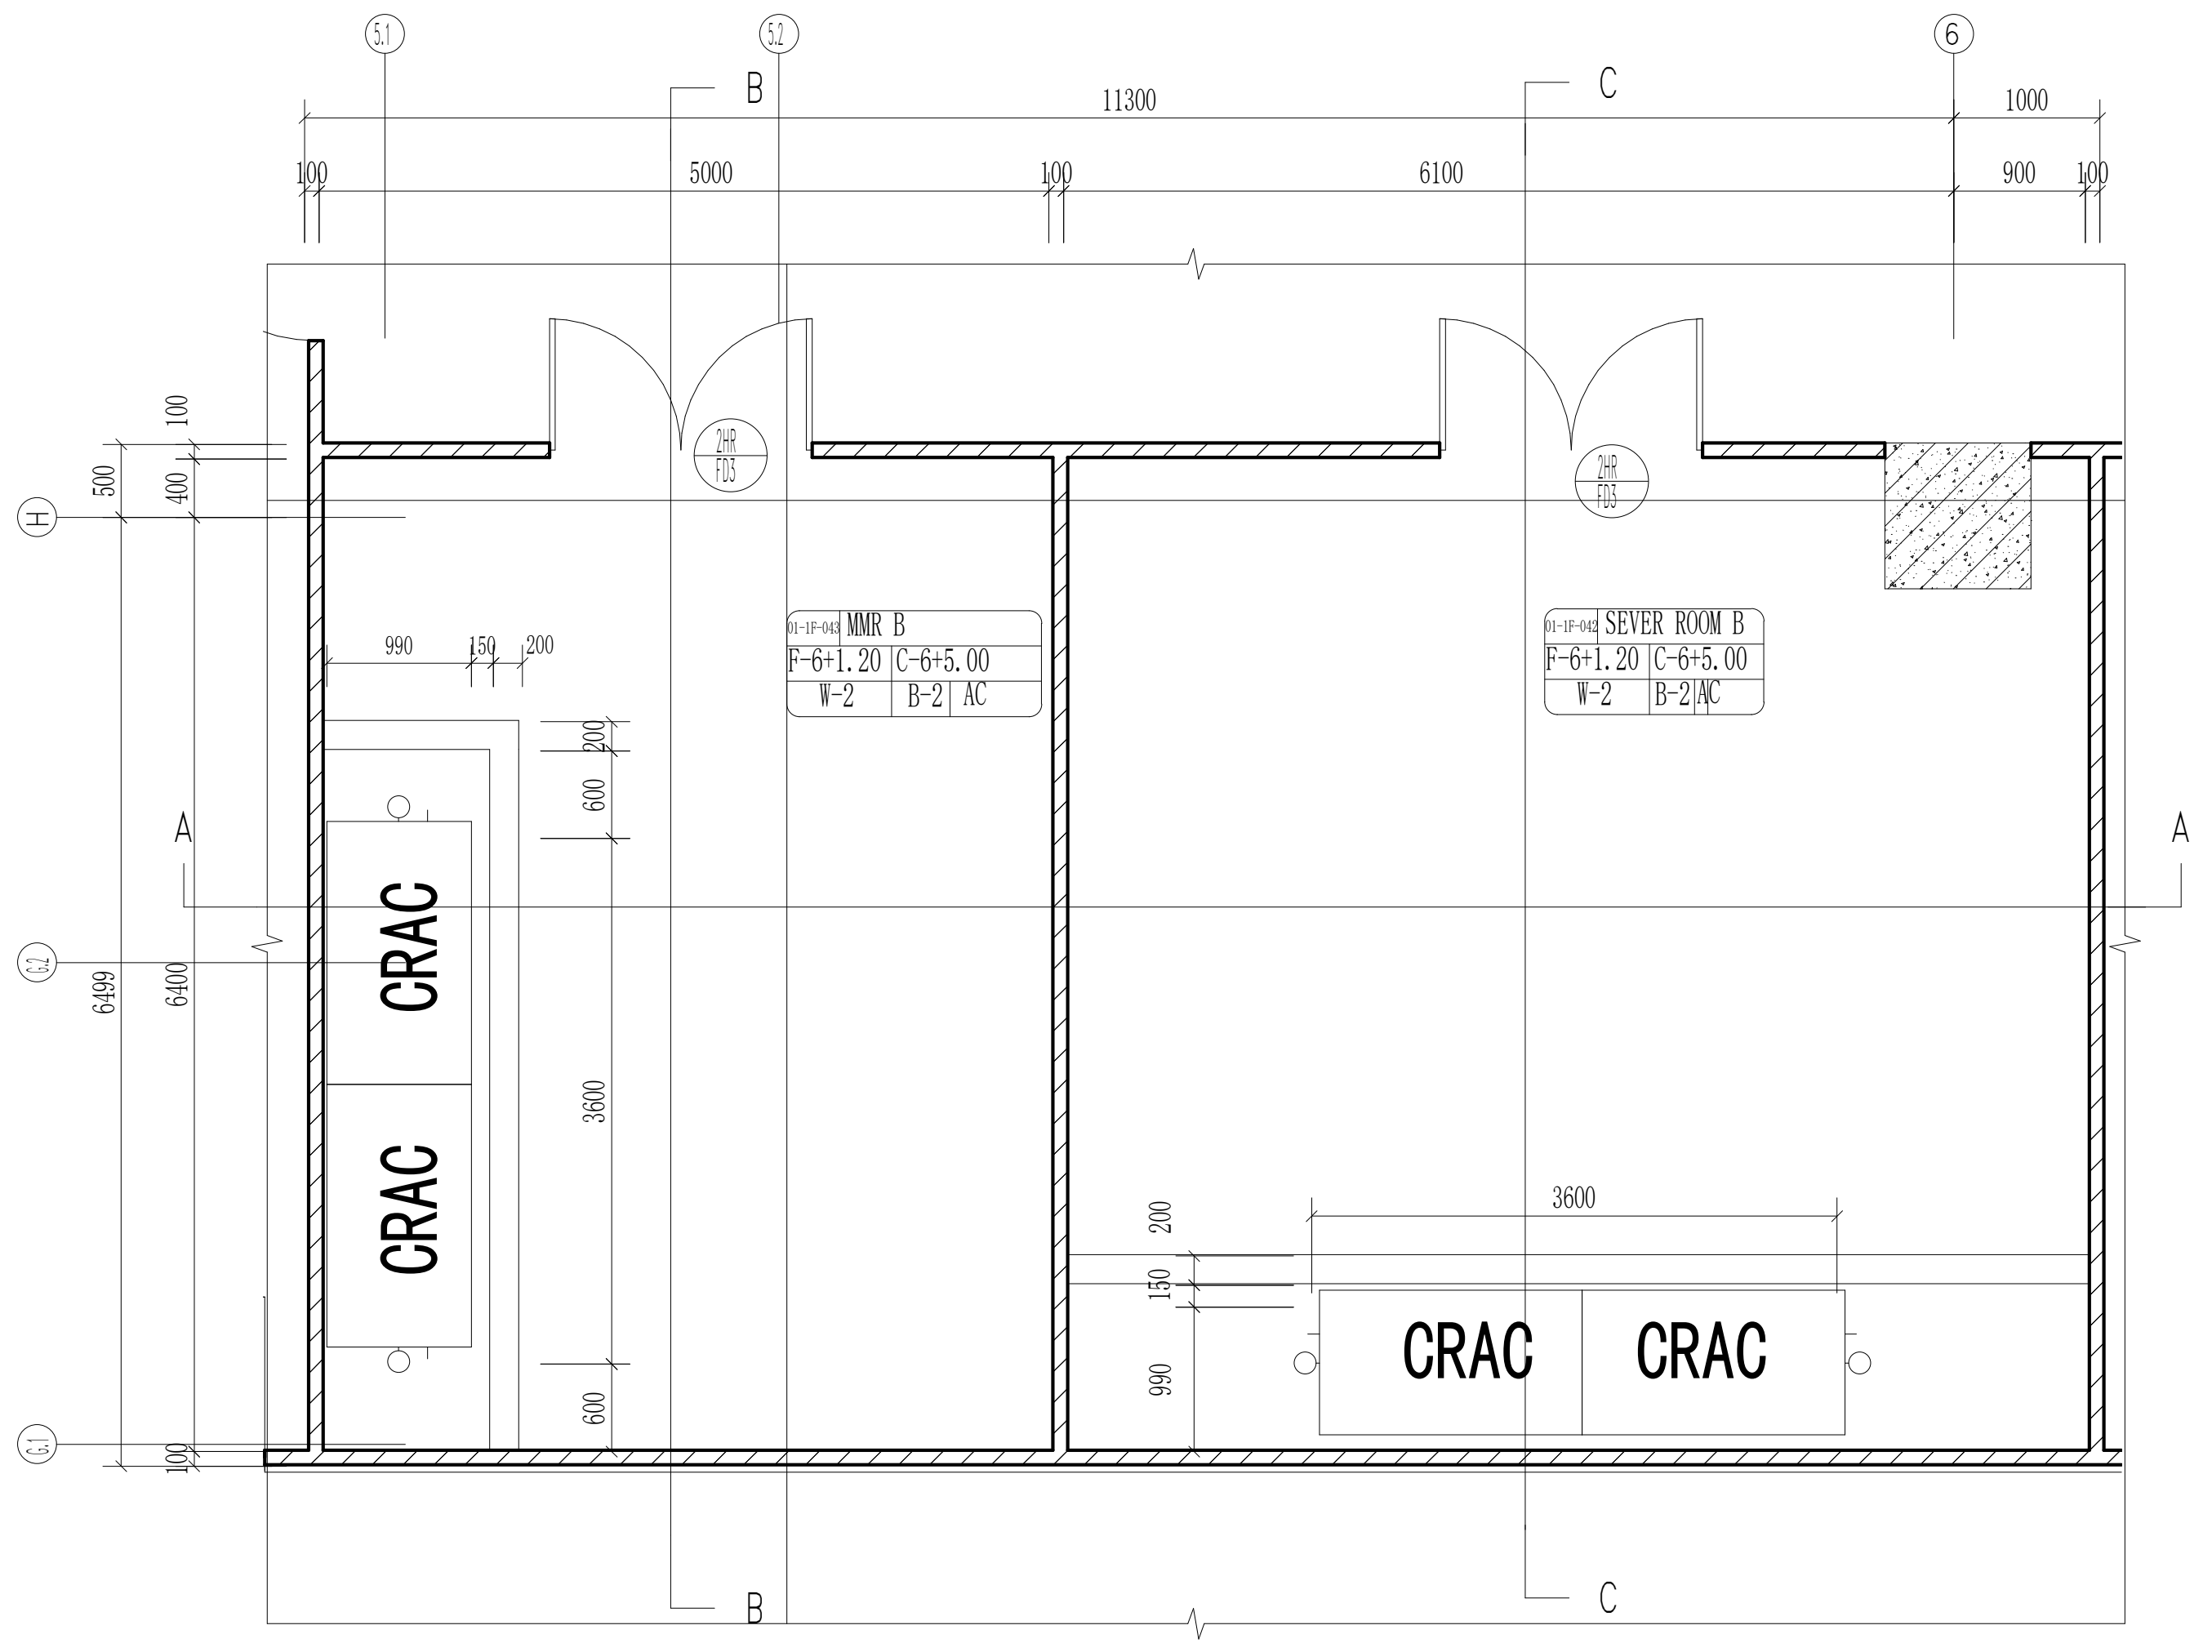
B
C
A
A
6
11300
1000
300
5000
100
6100
900
MMR B
SEVER ROOM B
CRAC
CRAC
CRAC
CRAC
3600
6400
6499

MMR B、SERVER ROOM B FLOOR PLAN

Scale 1:50

THE "SFL" MARKED IN THE DRAWING REFERS TO THE STRUCTURAL FLOOR LEVEL, WHILE THE FINISHED FLOOR LEVEL (FFL) IS DETERMINED BASED ON FLOOR FINISHES.

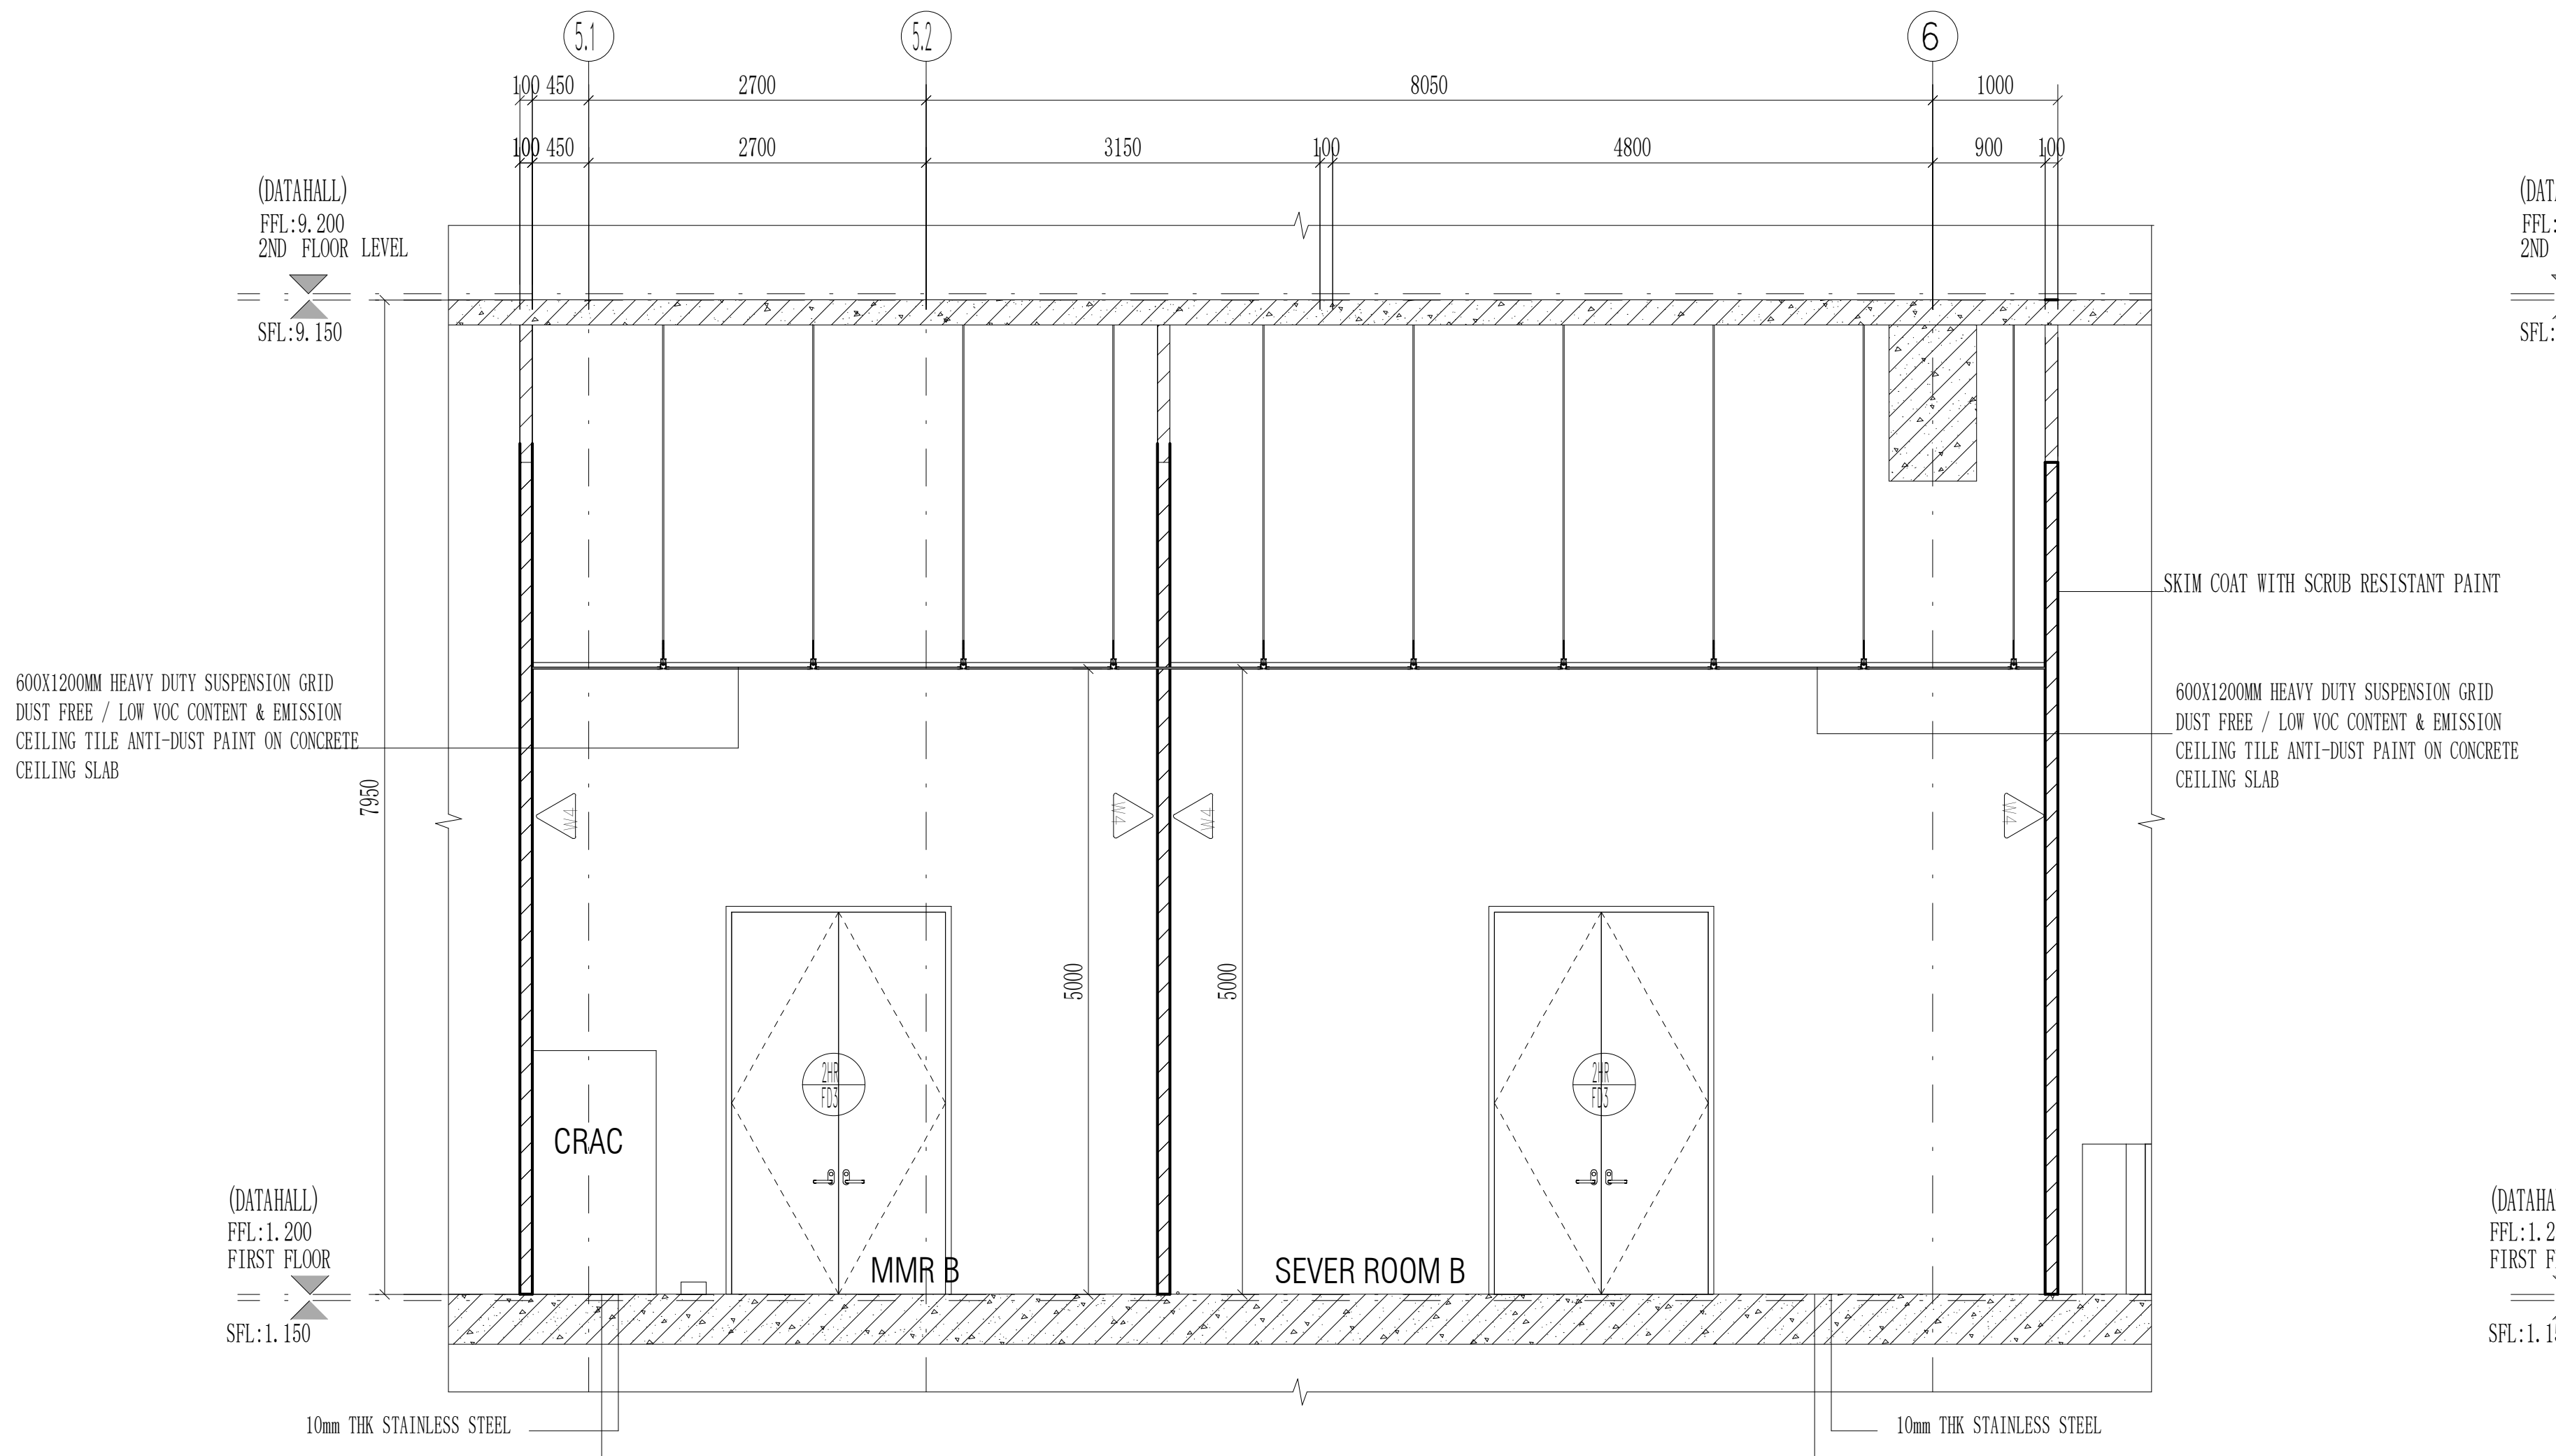
5.1
5.2
6
100 450
2700
8050
1000
100 450
2700
3150
100
4800
900
100
(DATAHALL)
FFL:9.200
2ND FLOOR LEVEL
SFL:9.150
(DATAHALL)
FFL:1.200
FIRST FLOOR
SFL:1.150
7950
5000
5000
600X1200MM HEAVY DUTY SUSPENSION GRID DUST FREE / LOW VOC CONTENT & EMISSION CEILING TILE ANTI-DUST PAINT ON CONCRETE CEILING SLAB
SKIM COAT WITH SCRUB RESISTANT PAINT
600X1200MM HEAVY DUTY SUSPENSION GRID DUST FREE / LOW VOC CONTENT & EMISSION CEILING TILE ANTI-DUST PAINT ON CONCRETE CEILING SLAB
CRAC
MMR B
SEVER ROOM B
10mm THK STAINLESS STEEL
EPOXY+ 1.2mm THKCEMENTITIOUS WATERPROOF COATING
10mm THK STAINLESS STEEL
EPOXY+ 1.2mm THKCEMENTITIOUS WATERPROOF COATING

MMR B、SERVER ROOM B SECTION A-A

Scale 1:50

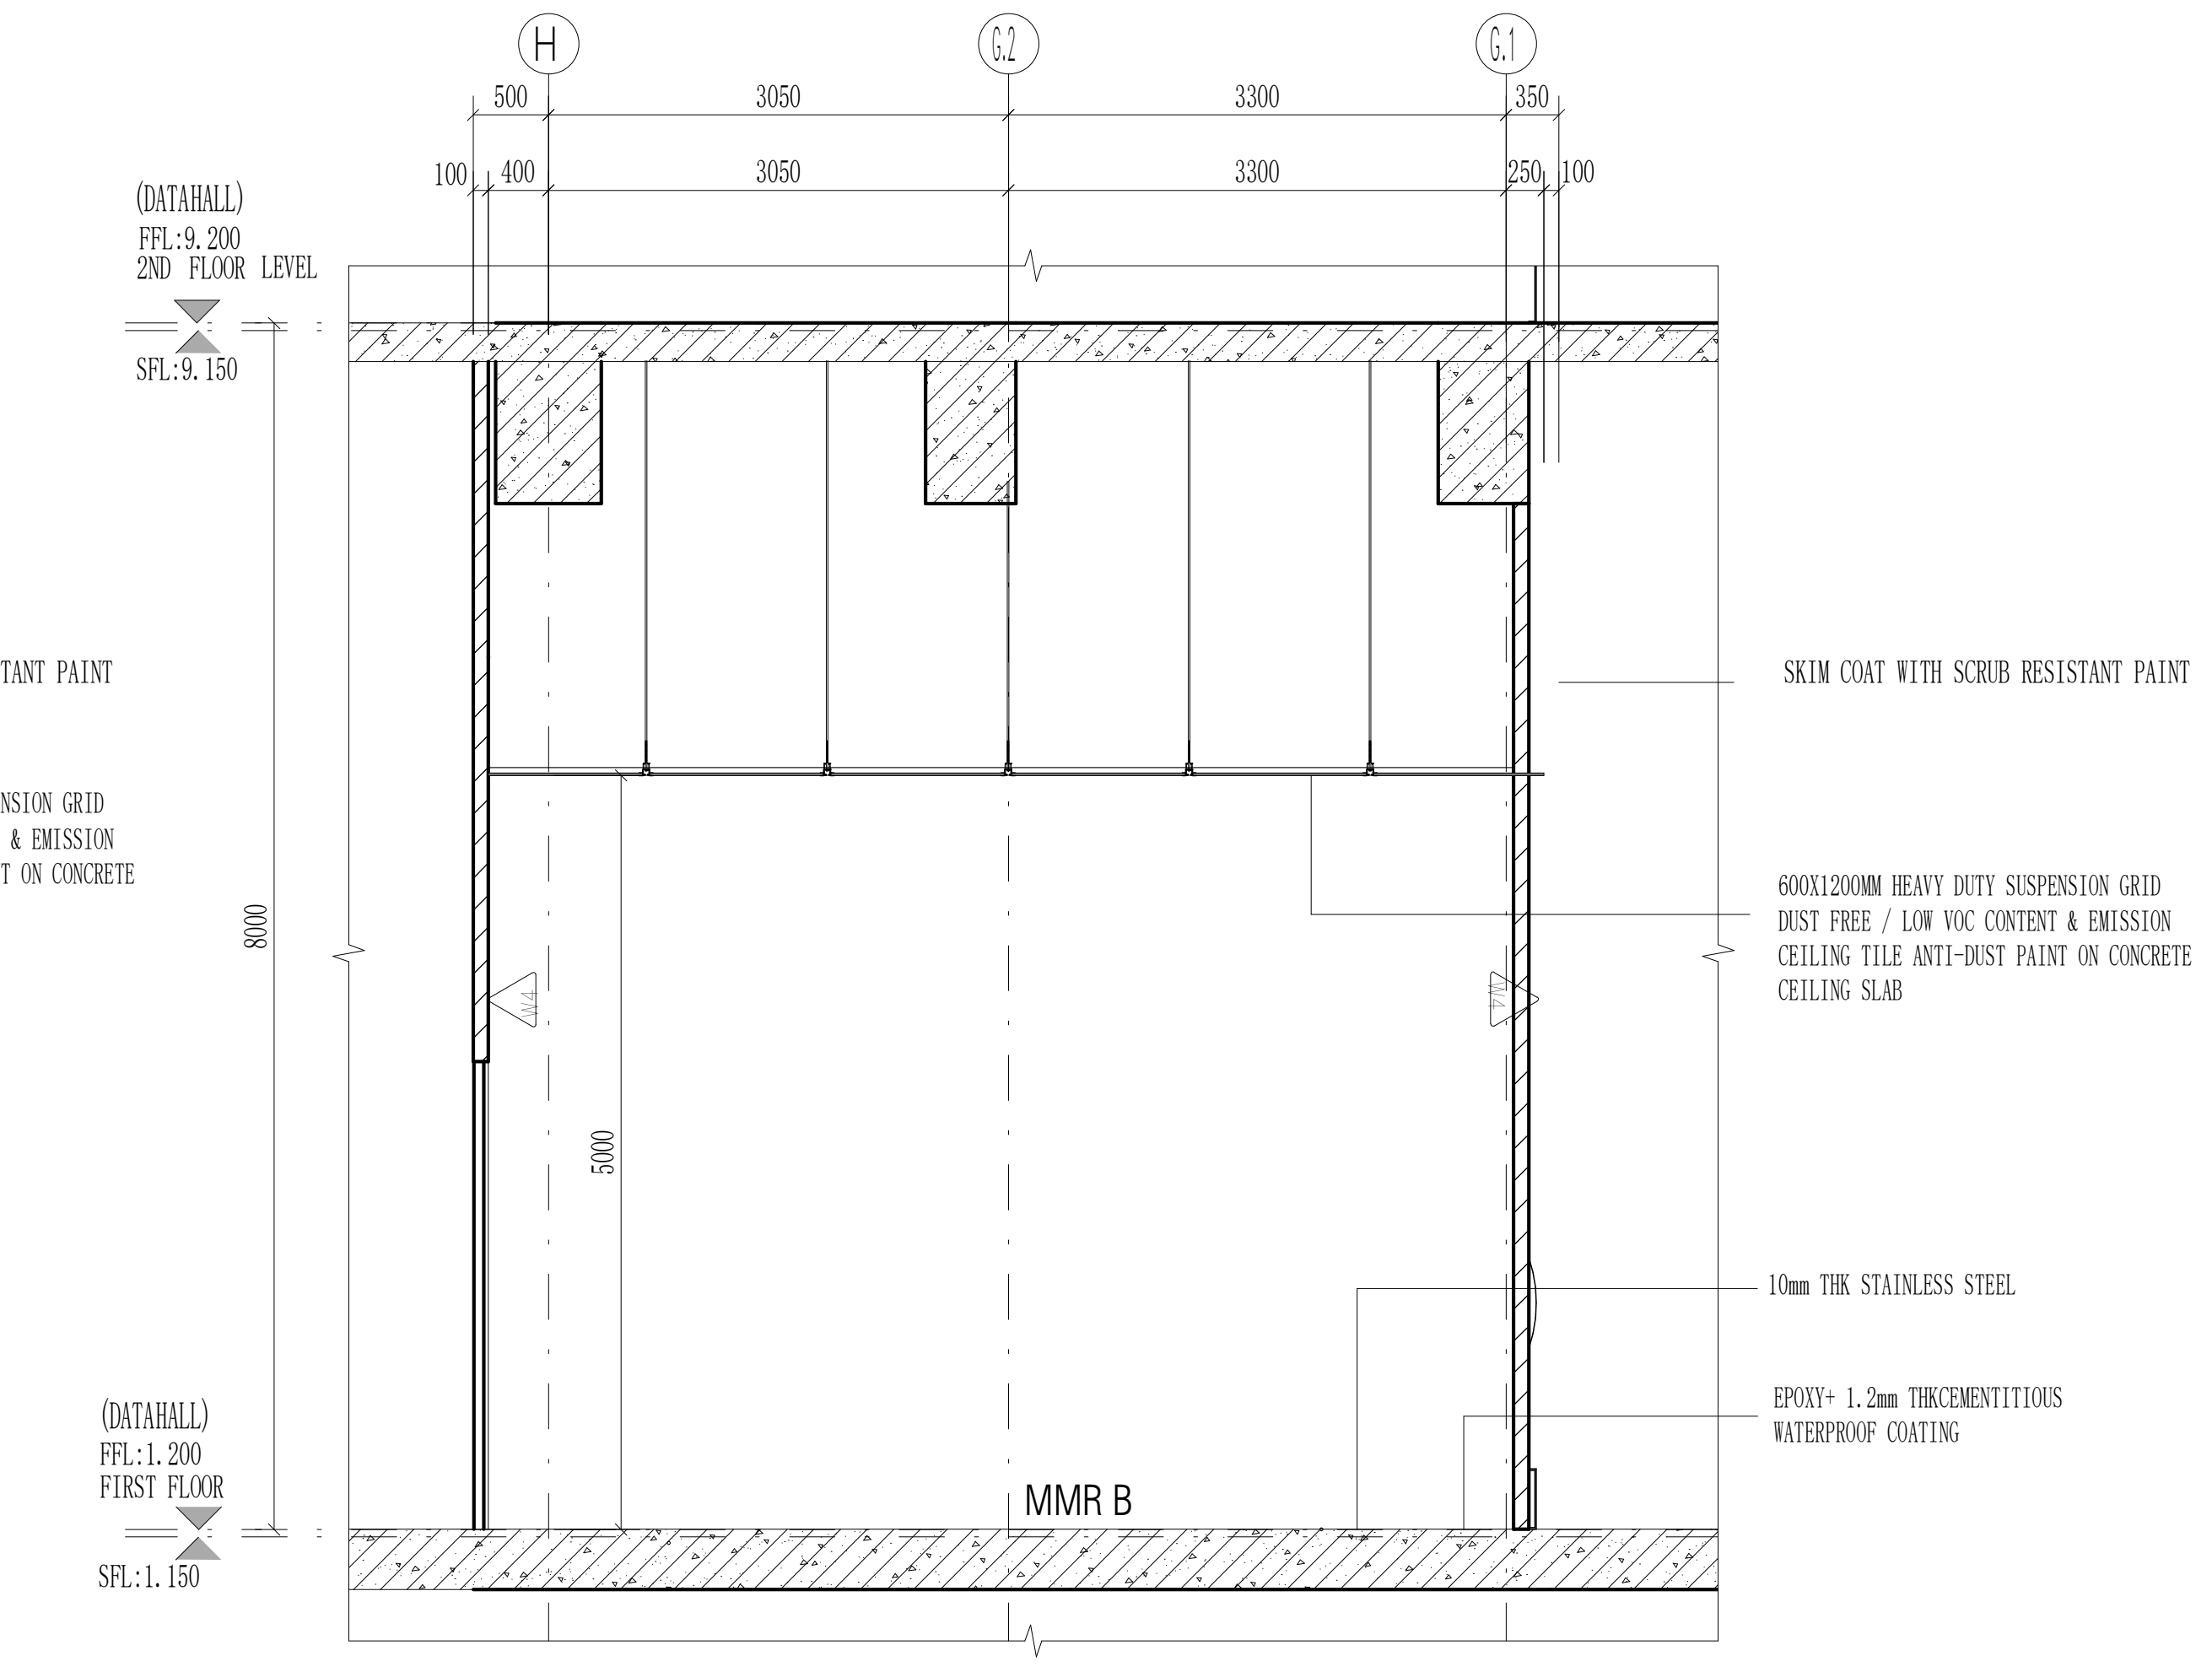
H
G.2
G.1
500
3050
3300
350
100
400
3050
3300
250
100
(DATAHALL)
FFL:9.200
2ND FLOOR LEVEL
SFL:9.150
(DATAHALL)
FFL:1.200
FIRST FLOOR
SFL:1.150
8000
5000
SKIM COAT WITH SCRUB RESISTANT PAINT
600X1200MM HEAVY DUTY SUSPENSION GRID DUST FREE / LOW VOC CONTENT & EMISSION CEILING TILE ANTI-DUST PAINT ON CONCRETE CEILING SLAB
10mm THK STAINLESS STEEL
EPOXY+ 1.2mm THKCEMENTITIOUS WATERPROOF COATING
MMR B

MMR B SECTION B-B

Scale 1:50

1F-MMR B SECTION B-B

NOTE :THIS PRINT IS OF A CONFIDENTIAL NATURE, IT SHALL NOT BE TRACED,PHOTOGRAPHED,PHOTOSTATED OR REPRODUCED IN ANY MANER,NOR USED FOR ANY PURPOSE WHATSOEVER EXCEPT BY WRITTEN PERMISSION

CLIENT :

GULF EDGE DC 01

87 Wireless Road, M Thai Tower 11th. Floor, All Seasons Place, Lumpini,
Pathumwan, Bangkok 10330, Thailand

CONTRACTOR :

华西发展(泰国)有限公司
บริษัท หัวซือ ดีเวลลอปเม้นต์ (ประเทศไทย) จำกัด
HUASHI DEVELOPMENT CO.,LTD
No. 202, Room No. 1403, 14/F, Le Concorde Building,
Ratchadapisek Road, Huaykhwang Sub-District,
Huaykhwang District, Bangkok Metropolitan 10310.

CONSULTANT :

ARbay
บริษัท เอ อาร์ เบย์ จำกัด
ARbay Company Limited
31 st Floor Bangkok Insurance Building
25 South Sathorn road Thungmahamek
Sathorn Bangkok 10120 THAILAND
T +66 (0) 2286 8199
F +66 (0) 2286 2863
info@arbay.co.th

CONSULTANT :

Qbic Engineers & Architects Co.,Ltd.
8 Soi KALONG 4 SANAMBINNAM ROAD,
THASAI SUB-DISTRICT, MUANG NONTHABURI DISTRICT
, NONTHABURI.
Tel 662-950-4374
Fax 662-580-3231
E-Mail : qbic@qbic.co.th, www.qbic.co.th
QBIC ENGINEERS AND ARCHITECTS CO.,LTD.

CONSULTANT :

MITR
MITR TECHNICAL CONSULTANT CO.,LTD.
1168/8 12th FLOOR, LUMPINI TOWER BUILDING,
RAMA IV RD., THUNGMAHAMEK, SATHORN, BANGKOK 10120, THAILAND
TEL : 0-2679-9079-84
FAX : 0-2679-9085 E-mail: mitr_dd@mitr.com

Architect :	SIGNATURE
ประกิต พนานุรัตน์ วสถ. 580 ที่อยู่ 251/1 ถ.จารุเมือง แขวงรองเมือง เขตปทุมวัน กรุงเทพมหานคร โทรศัพท์ 02-286-8199	
Structural Engineer :	SIGNATURE
วิศวกรผู้ออกแบบโครงสร้าง	
ณัฐสม สงวนวงษ์ วย 1423 ที่อยู่ 2/1 ซ.รามคำแหง 150 ถ.รามคำแหง แขวง สะพานสูง เขต สะพานสูง กทม. 10240	ณัฐสม สงวนวงษ์
Structural Inspector :	SIGNATURE
วิศวกรผู้ตรวจสอบโครงสร้าง	
โกมล จุฑาภัทร วย 964 ที่อยู่ 24/18 ซ.นวมินทร์ 129 ถ. นวมินทร์ แขวง นวลจันทร์ เขต บึงกุ่ม กทม. 10230	
Electrical Engineer :	SIGNATURE
วิศวกรผู้ออกแบบระบบไฟฟ้ากำลัง	
นายสุภัทร บูรณวิทย์ วฟก.1265 ที่อยู่ 21 ซอยทานสัมฤทธิ์ 13 ตำบลท่าทราย อ.เมืองนนทบุรี จ.นนทบุรี 11000	
Mechanical Engineer :	SIGNATURE
วิศวกรผู้ออกแบบระบบเครื่องกลและปรับอากาศ	
นายประสิทธิ์ เกี้ยวสุนทร วก.1221 ที่อยู่ 44/372 ซอยบางกระดี่ 35/1 แขวงแสมดำ เขตบางขุนเทียน กทม. 10150	ประสิทธิ์
Sanitary Engineer :	SIGNATURE
วิศวกรผู้ออกแบบระบบสุขาภิบาล และดับเพลิง	
นายทศวรรษ สนั่นฤทธิ์ วส. 215 ที่อยู่ บ้านเลขที่ 99/107 หมู่ที่ 3 ต.ศีรษะจรเข้น้อย อ.บางเสาธง จ.สมุทรปราการ 10540	ทศวรรษ

ISSUE/REVISION

REV.	DESCRIPTION	DATE
A	90% DEVELOPED	09/05/2026

PROJECT NAME :

GEDC 01

LOCATION:
Nikhom Phattana district, Rayong ,industrial estate,CPGC

BUILDING :
MAIN BUILDING

90% DEVELOPED

TITLE :

ROOM DETAIL-1F-SECURITY OFFICE、SECURITY 01、MDF02、MMR B、SEVER ROOM B

JOB NO.	SCALE 1 : 50
DRAWN LYT	REF.
CHECKED LJC	DWG. NO. MPK01A-90-A-RD-115
APPROVED LXD	
DATE 2026.05.09	

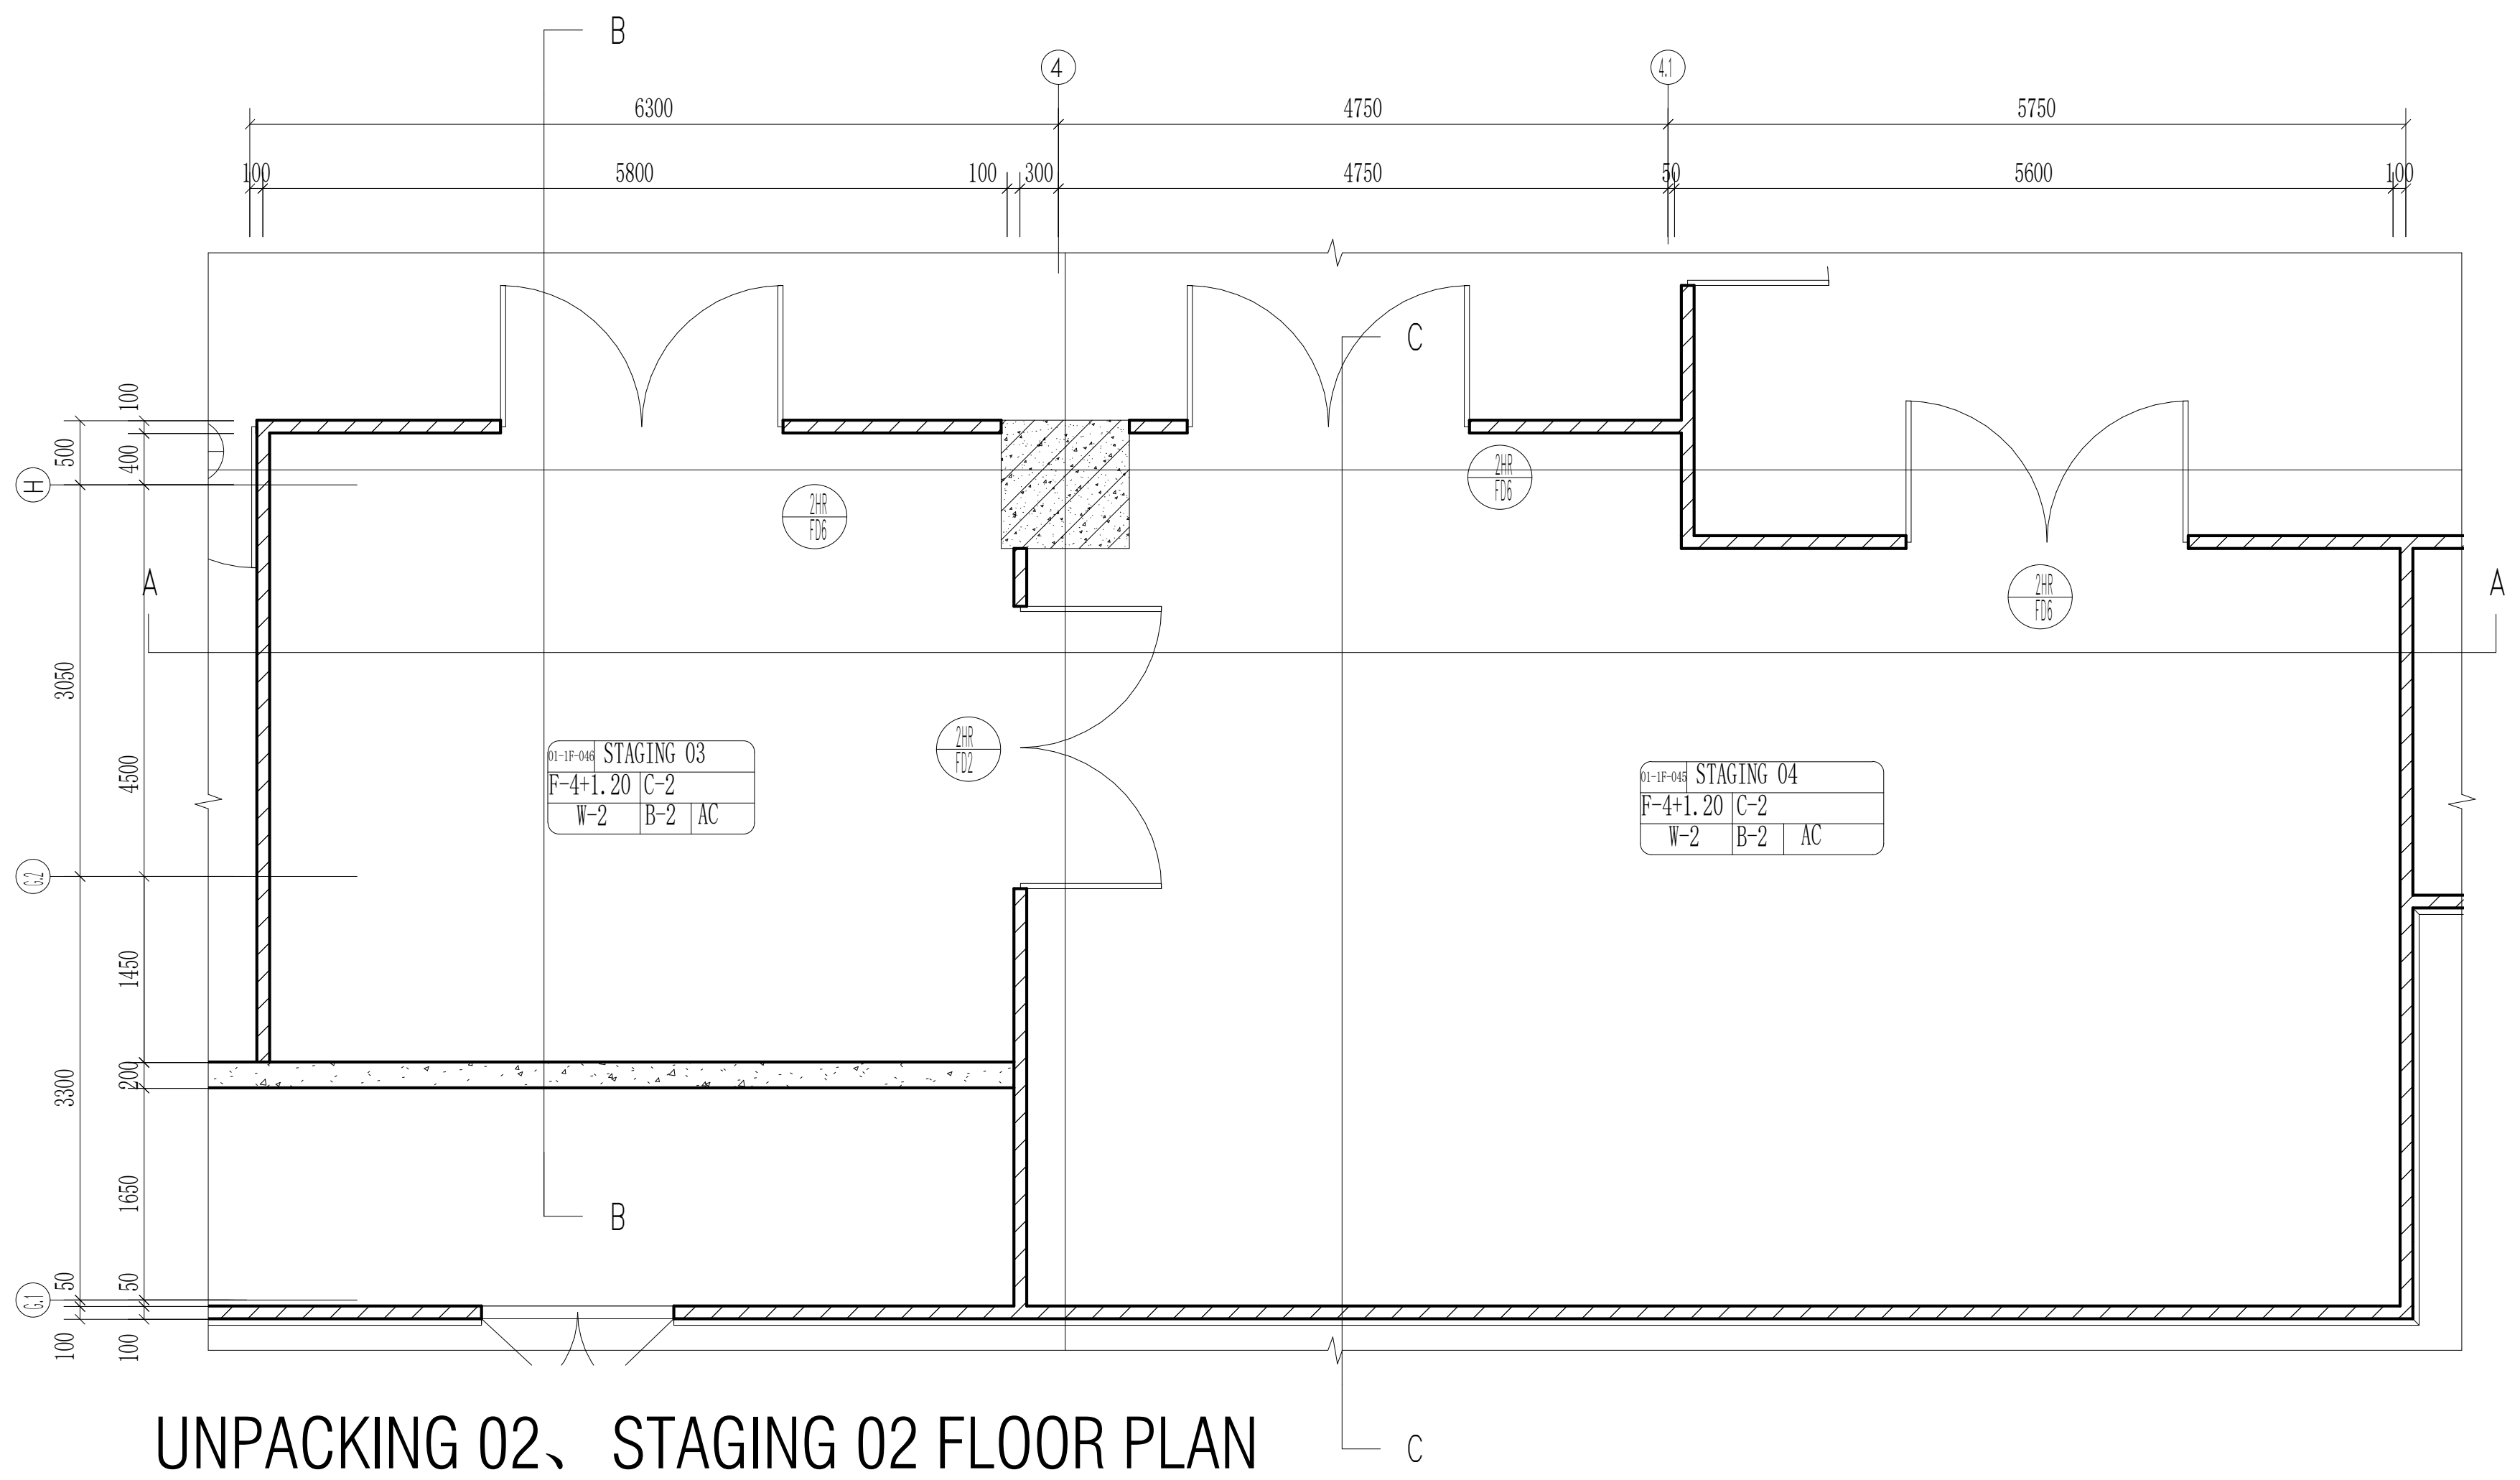
B
4
4.1
6300
4730
5730
5800
4730
5600
100
300
50
C
A
STAGING 03
F-4+1.20 C-2
W-2 B-2 AC
STAGING 04
F-4+1.20 C-2
W-2 B-2 AC
B
C
3050
6500
1650
3300
1650

UNPACKING 02、STAGING 02 FLOOR PLAN

Scale 1:50

THE "SFL" MARKED IN THE DRAWING REFERS TO THE STRUCTURAL FLOOR LEVEL, WHILE THE FINISHED FLOOR LEVEL (FFL) IS DETERMINED BASED ON FLOOR FINISHES.

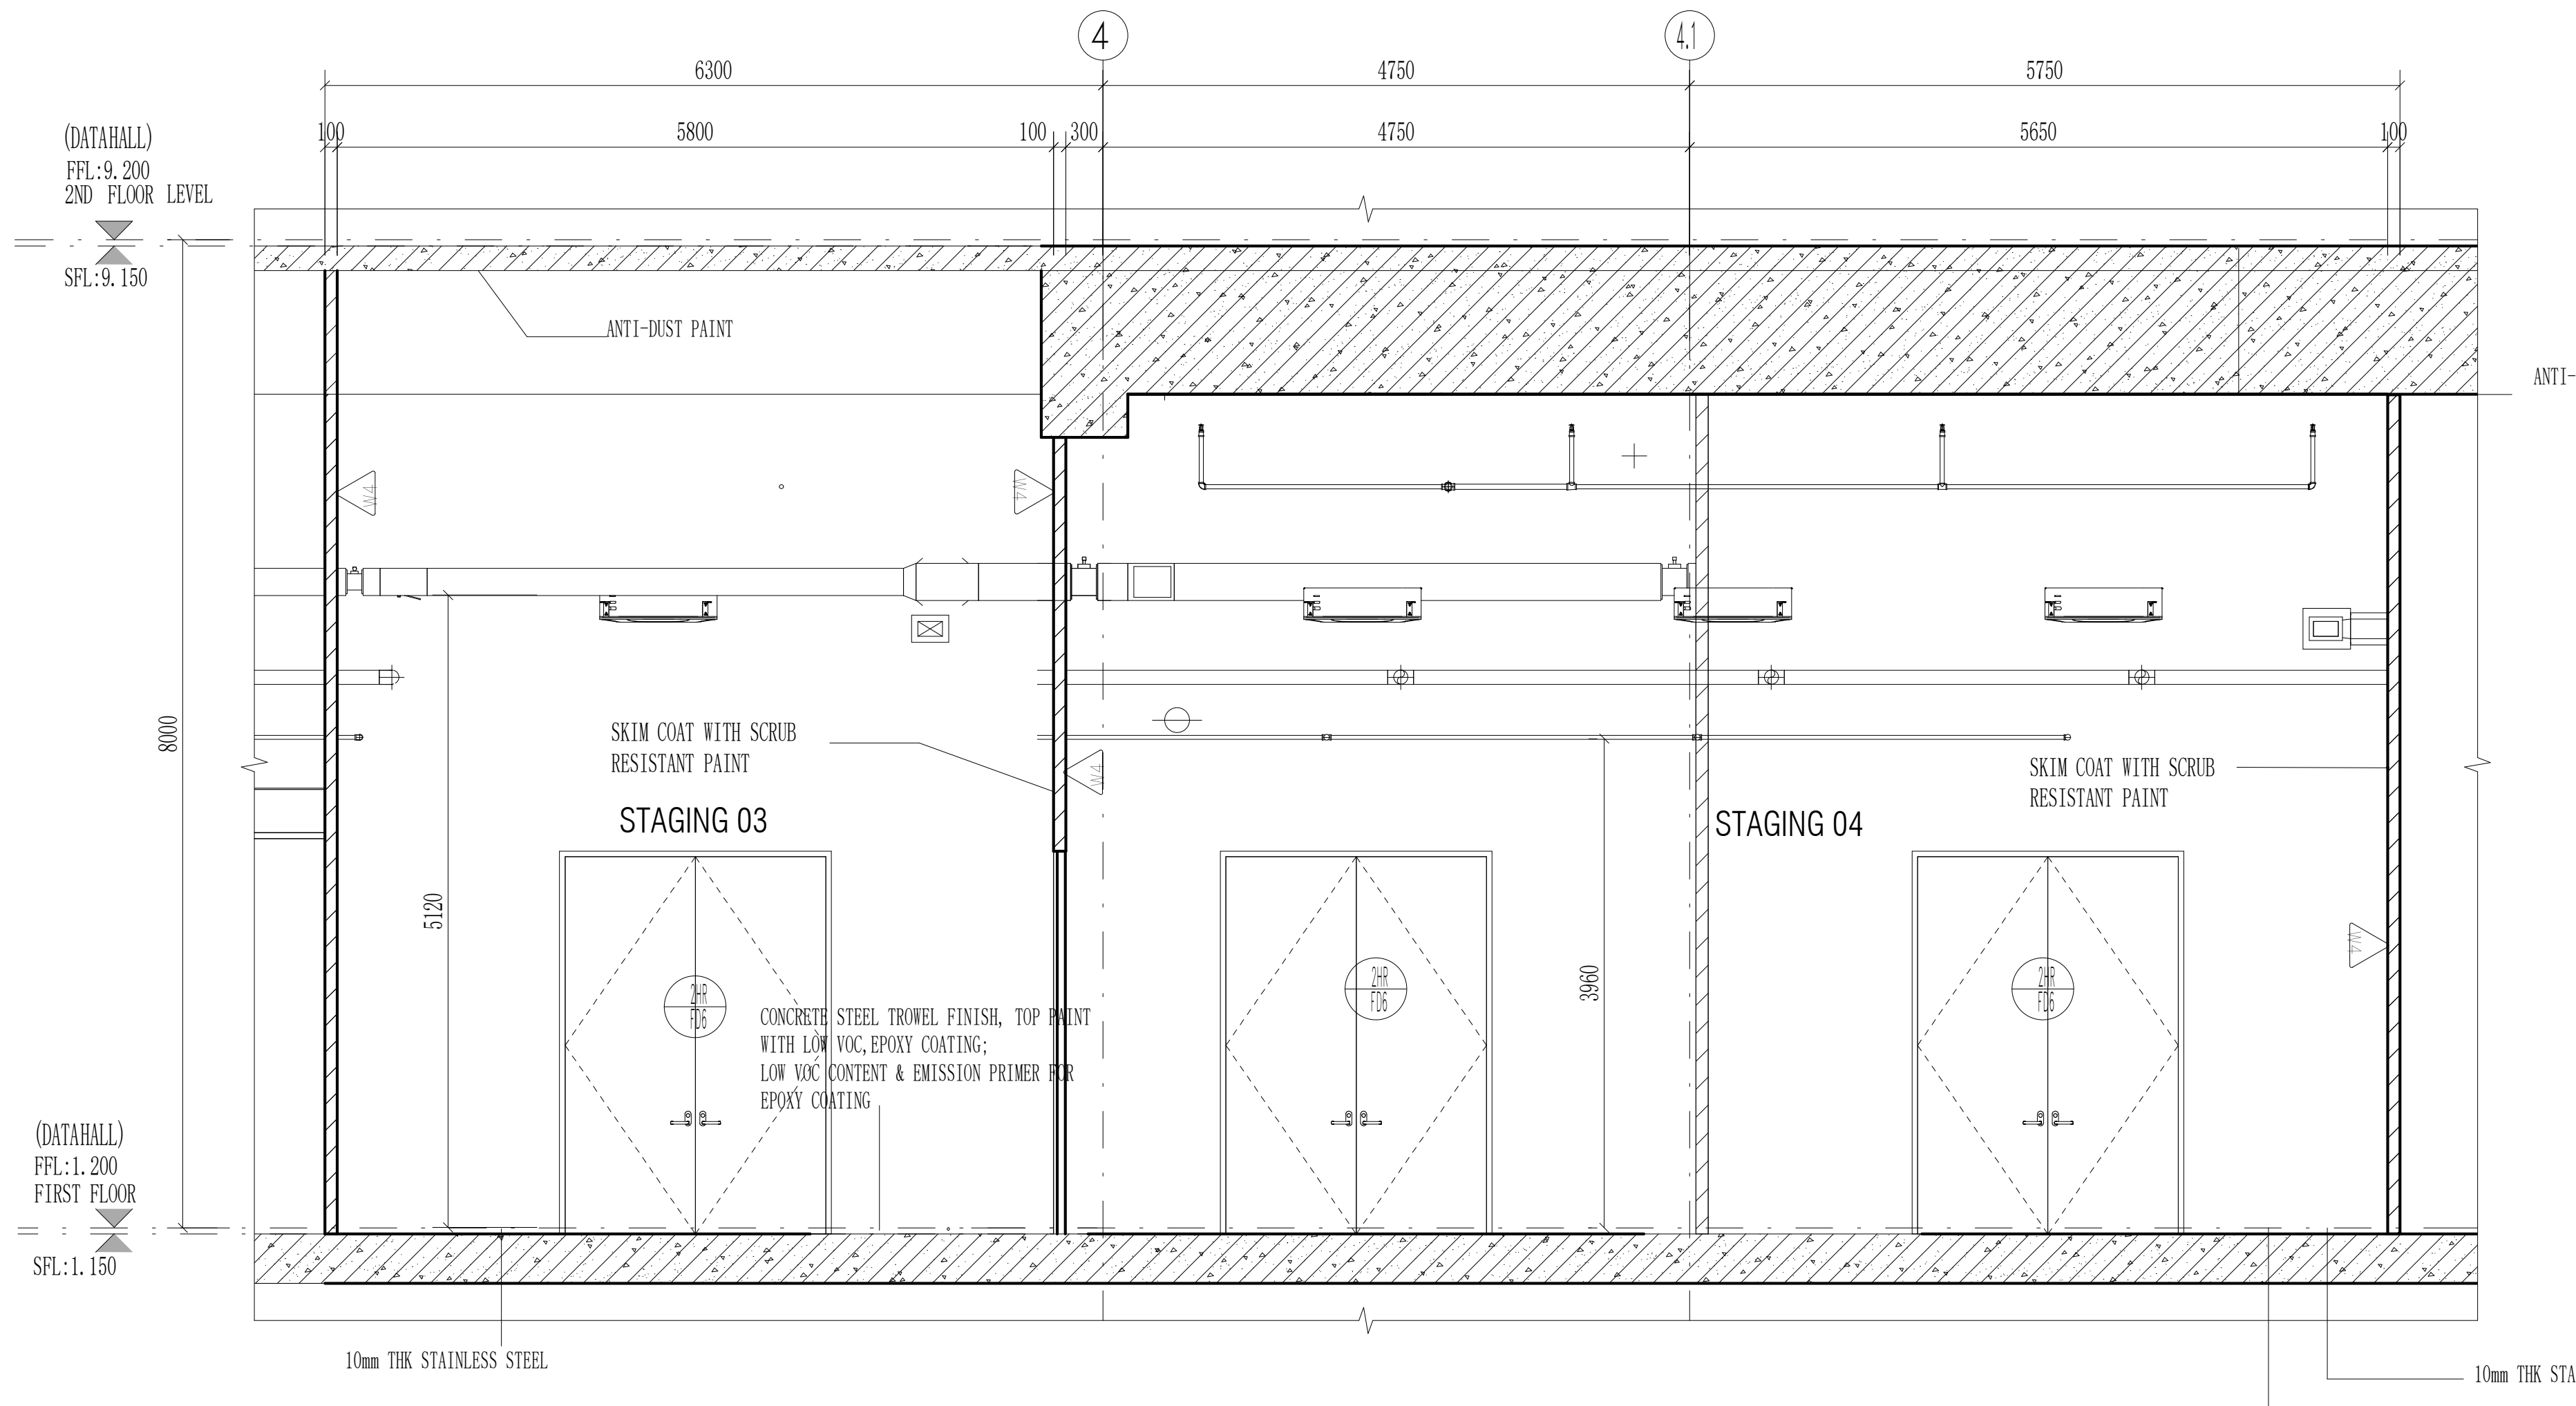
4
4.1
6300
4750
5750
5800
4750
5650
(DATAHALL)
FFL:9.200
2ND FLOOR LEVEL
SFL:9.150
ANTI-DUST PAINT
ANTI-DUST PAINT
SKIM COAT WITH SCRUB RESISTANT PAINT
SKIM COAT WITH SCRUB RESISTANT PAINT
STAGING 03
STAGING 04
CONCRETE STEEL TROWEL FINISH, TOP PAINT WITH LOW VOC,EPOXY COATING; LOW VOC CONTENT & EMISSION PRIMER FOR EPOXY COATING
8000
5120
3960
(DATAHALL)
FFL:1.200
FIRST FLOOR
SFL:1.150
10mm THK STAINLESS STEEL
10mm THK STAINLESS STEEL
CONCRETE STEEL TROWEL FINISH, TOP PAINT WITH LOW VOC,EPOXY COATING; LOW VOC CONTENT & EMISSION PRIMER FOR EPOXY COATING

UNPACKING 02、STAGING 02 SECTION A-A

Scale 1:50

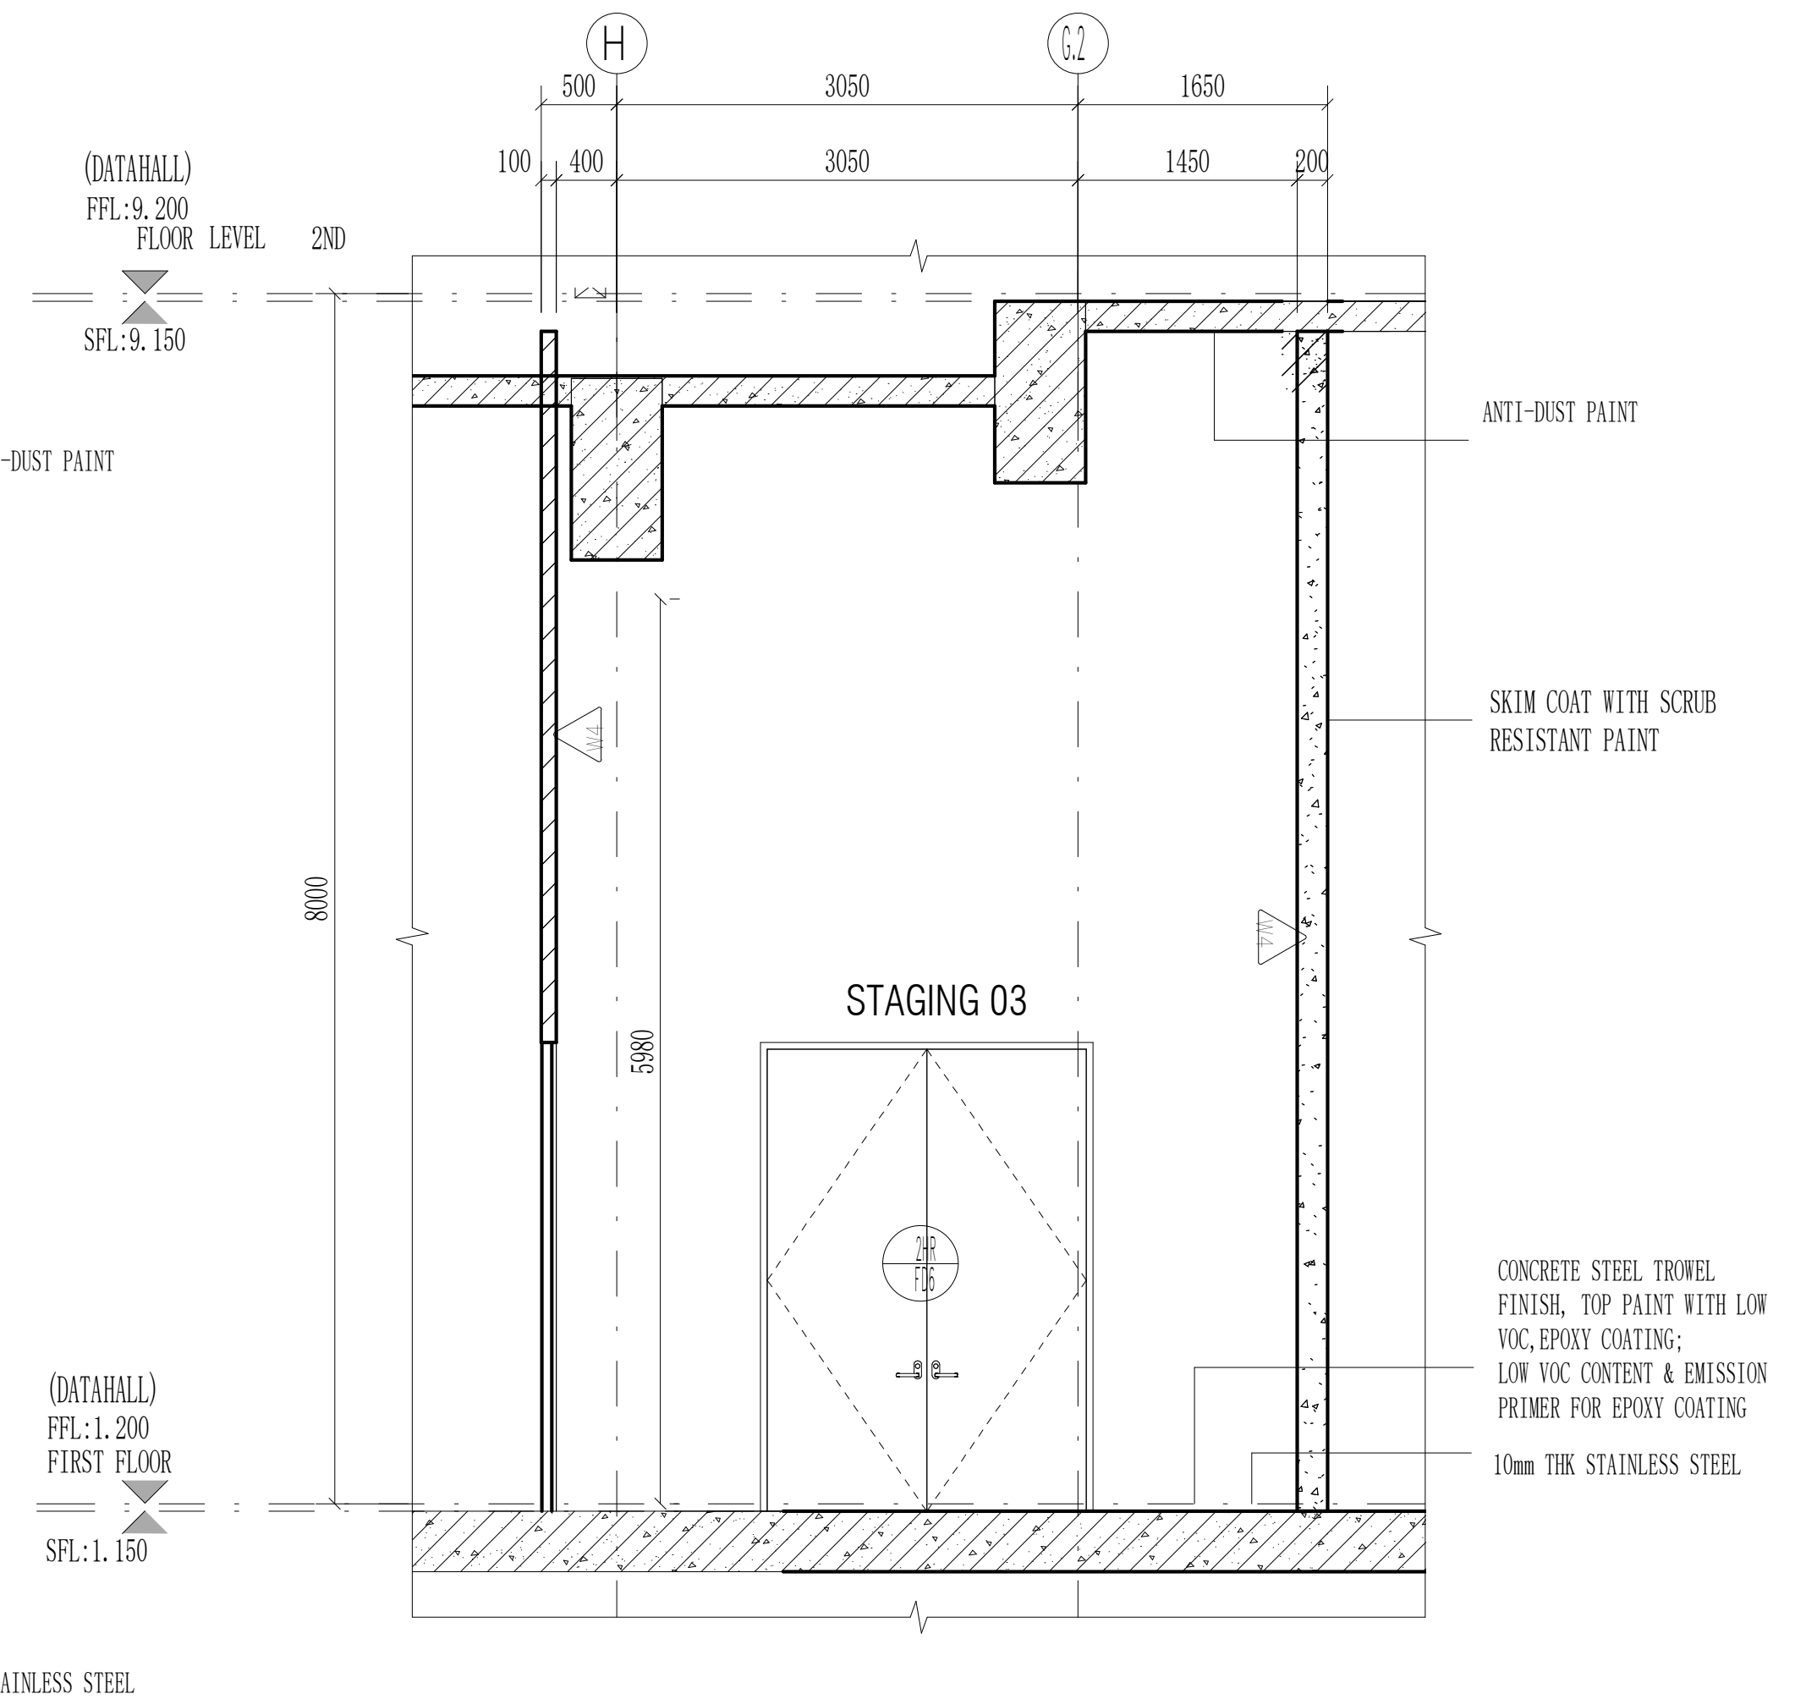
H
G.2
500
3050
1650
100
400
3050
1450
200
(DATAHALL)
FFL:9.200
FLOOR LEVEL
2ND
SFL:9.150
ANTI-DUST PAINT
SKIM COAT WITH SCRUB RESISTANT PAINT
STAGING 03
8000
5960
CONCRETE STEEL TROWEL FINISH, TOP PAINT WITH LOW VOC,EPOXY COATING; LOW VOC CONTENT & EMISSION PRIMER FOR EPOXY COATING
10mm THK STAINLESS STEEL
(DATAHALL)
FFL:1.200
FIRST FLOOR
SFL:1.150

UNPACKING 02 SECTION B-B

Scale 1:50

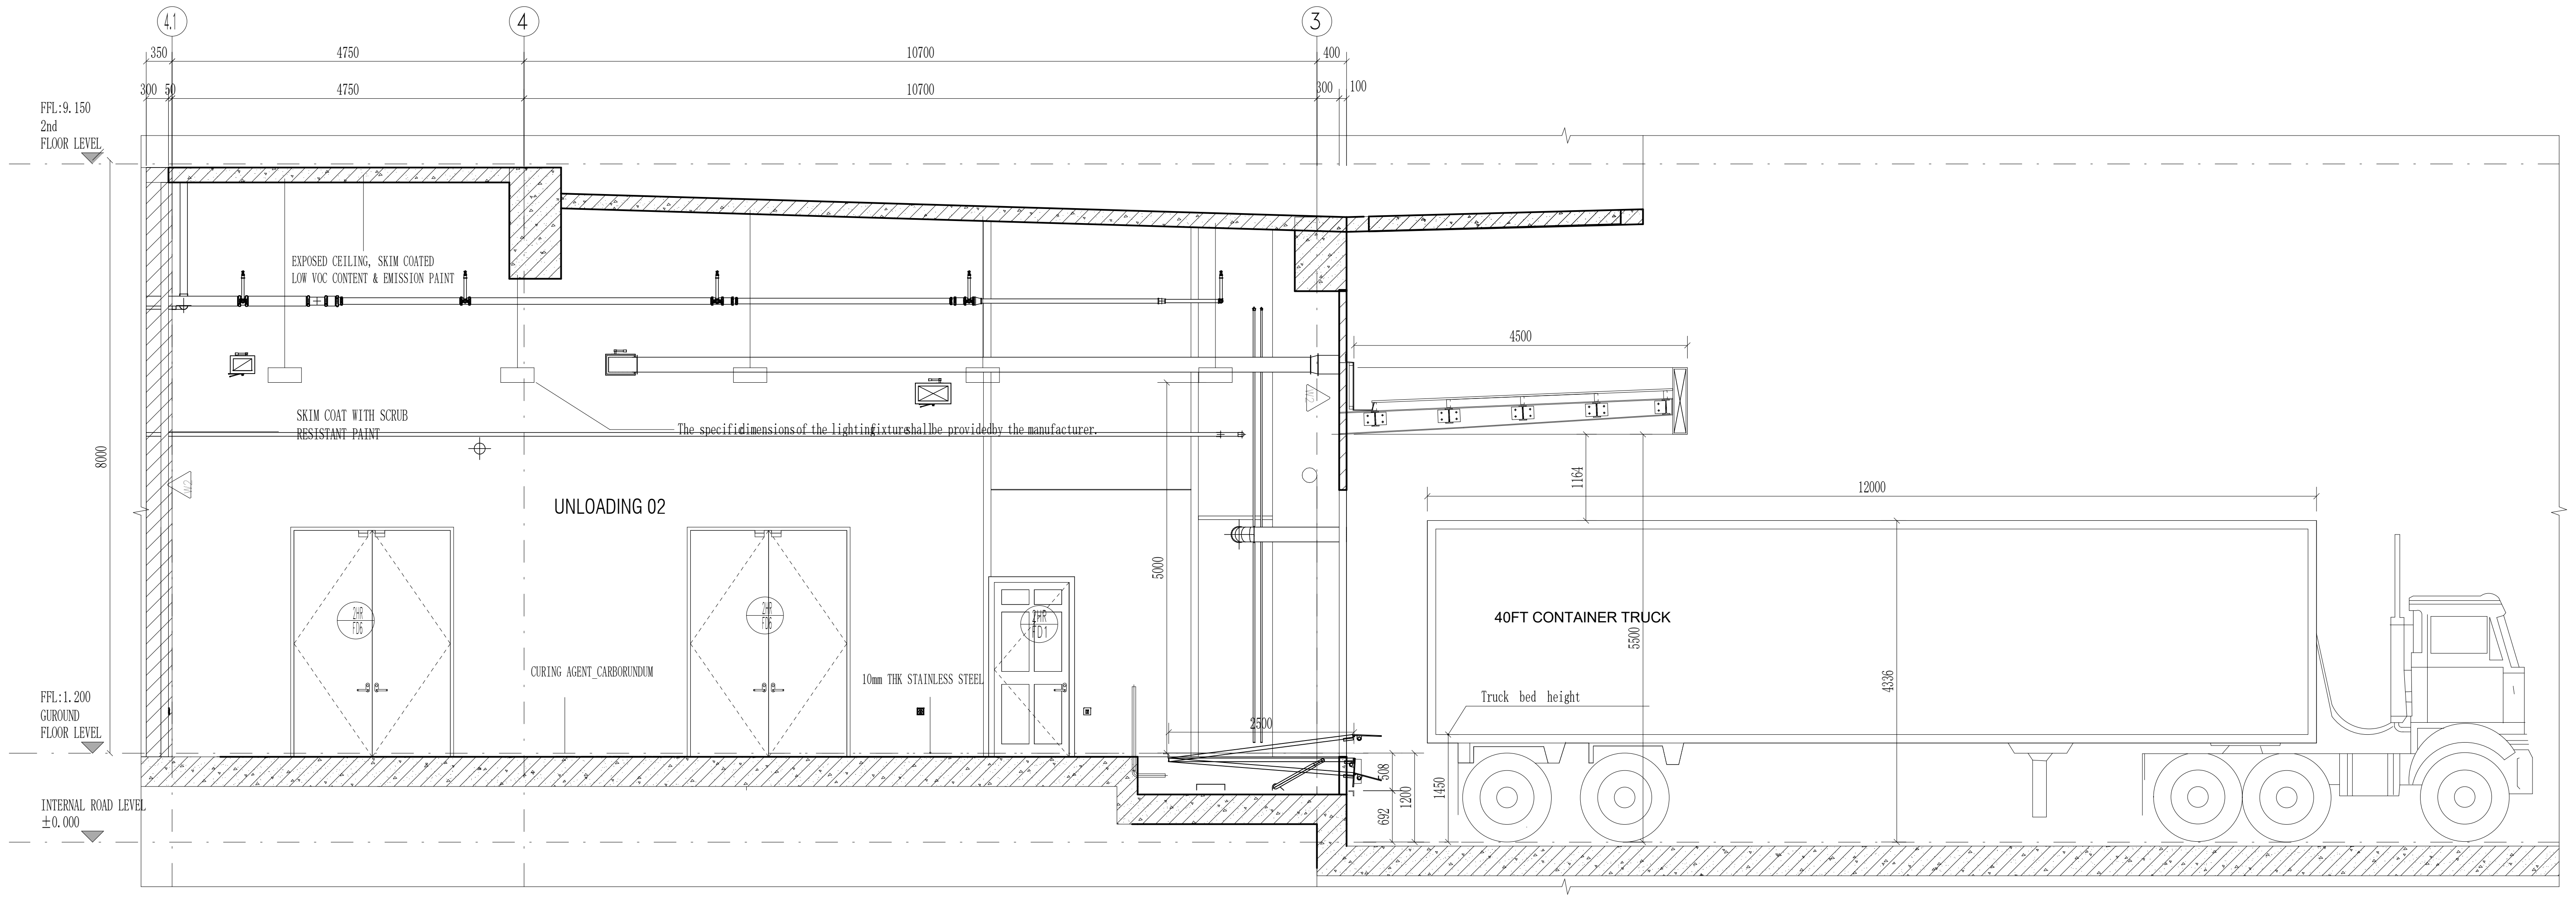
4.1
4
3
350
4750
10700
400
300
50
4750
10700
300
100
FFL:9.150
2nd
FLOOR LEVEL
EXPOSED CEILING, SKIM COATED LOW VOC CONTENT & EMISSION PAINT
SKIM COAT WITH SCRUB RESISTANT PAINT
The specific dimensions of the lighting fixture shall be provided by the manufacturer.
4500
UNLOADING 02
12000
1164
8000
5000
5500
4336
40FT CONTAINER TRUCK
CURING AGENT_CARBORUNDUM
10mm THK STAINLESS STEEL
Truck bed height
FFL:1.200
GUROUND
FLOOR LEVEL
INTERNAL ROAD LEVEL
±0.000
2500
1450
692
1200

UNLOADING 02 SECTION A-A

Scale 1:50

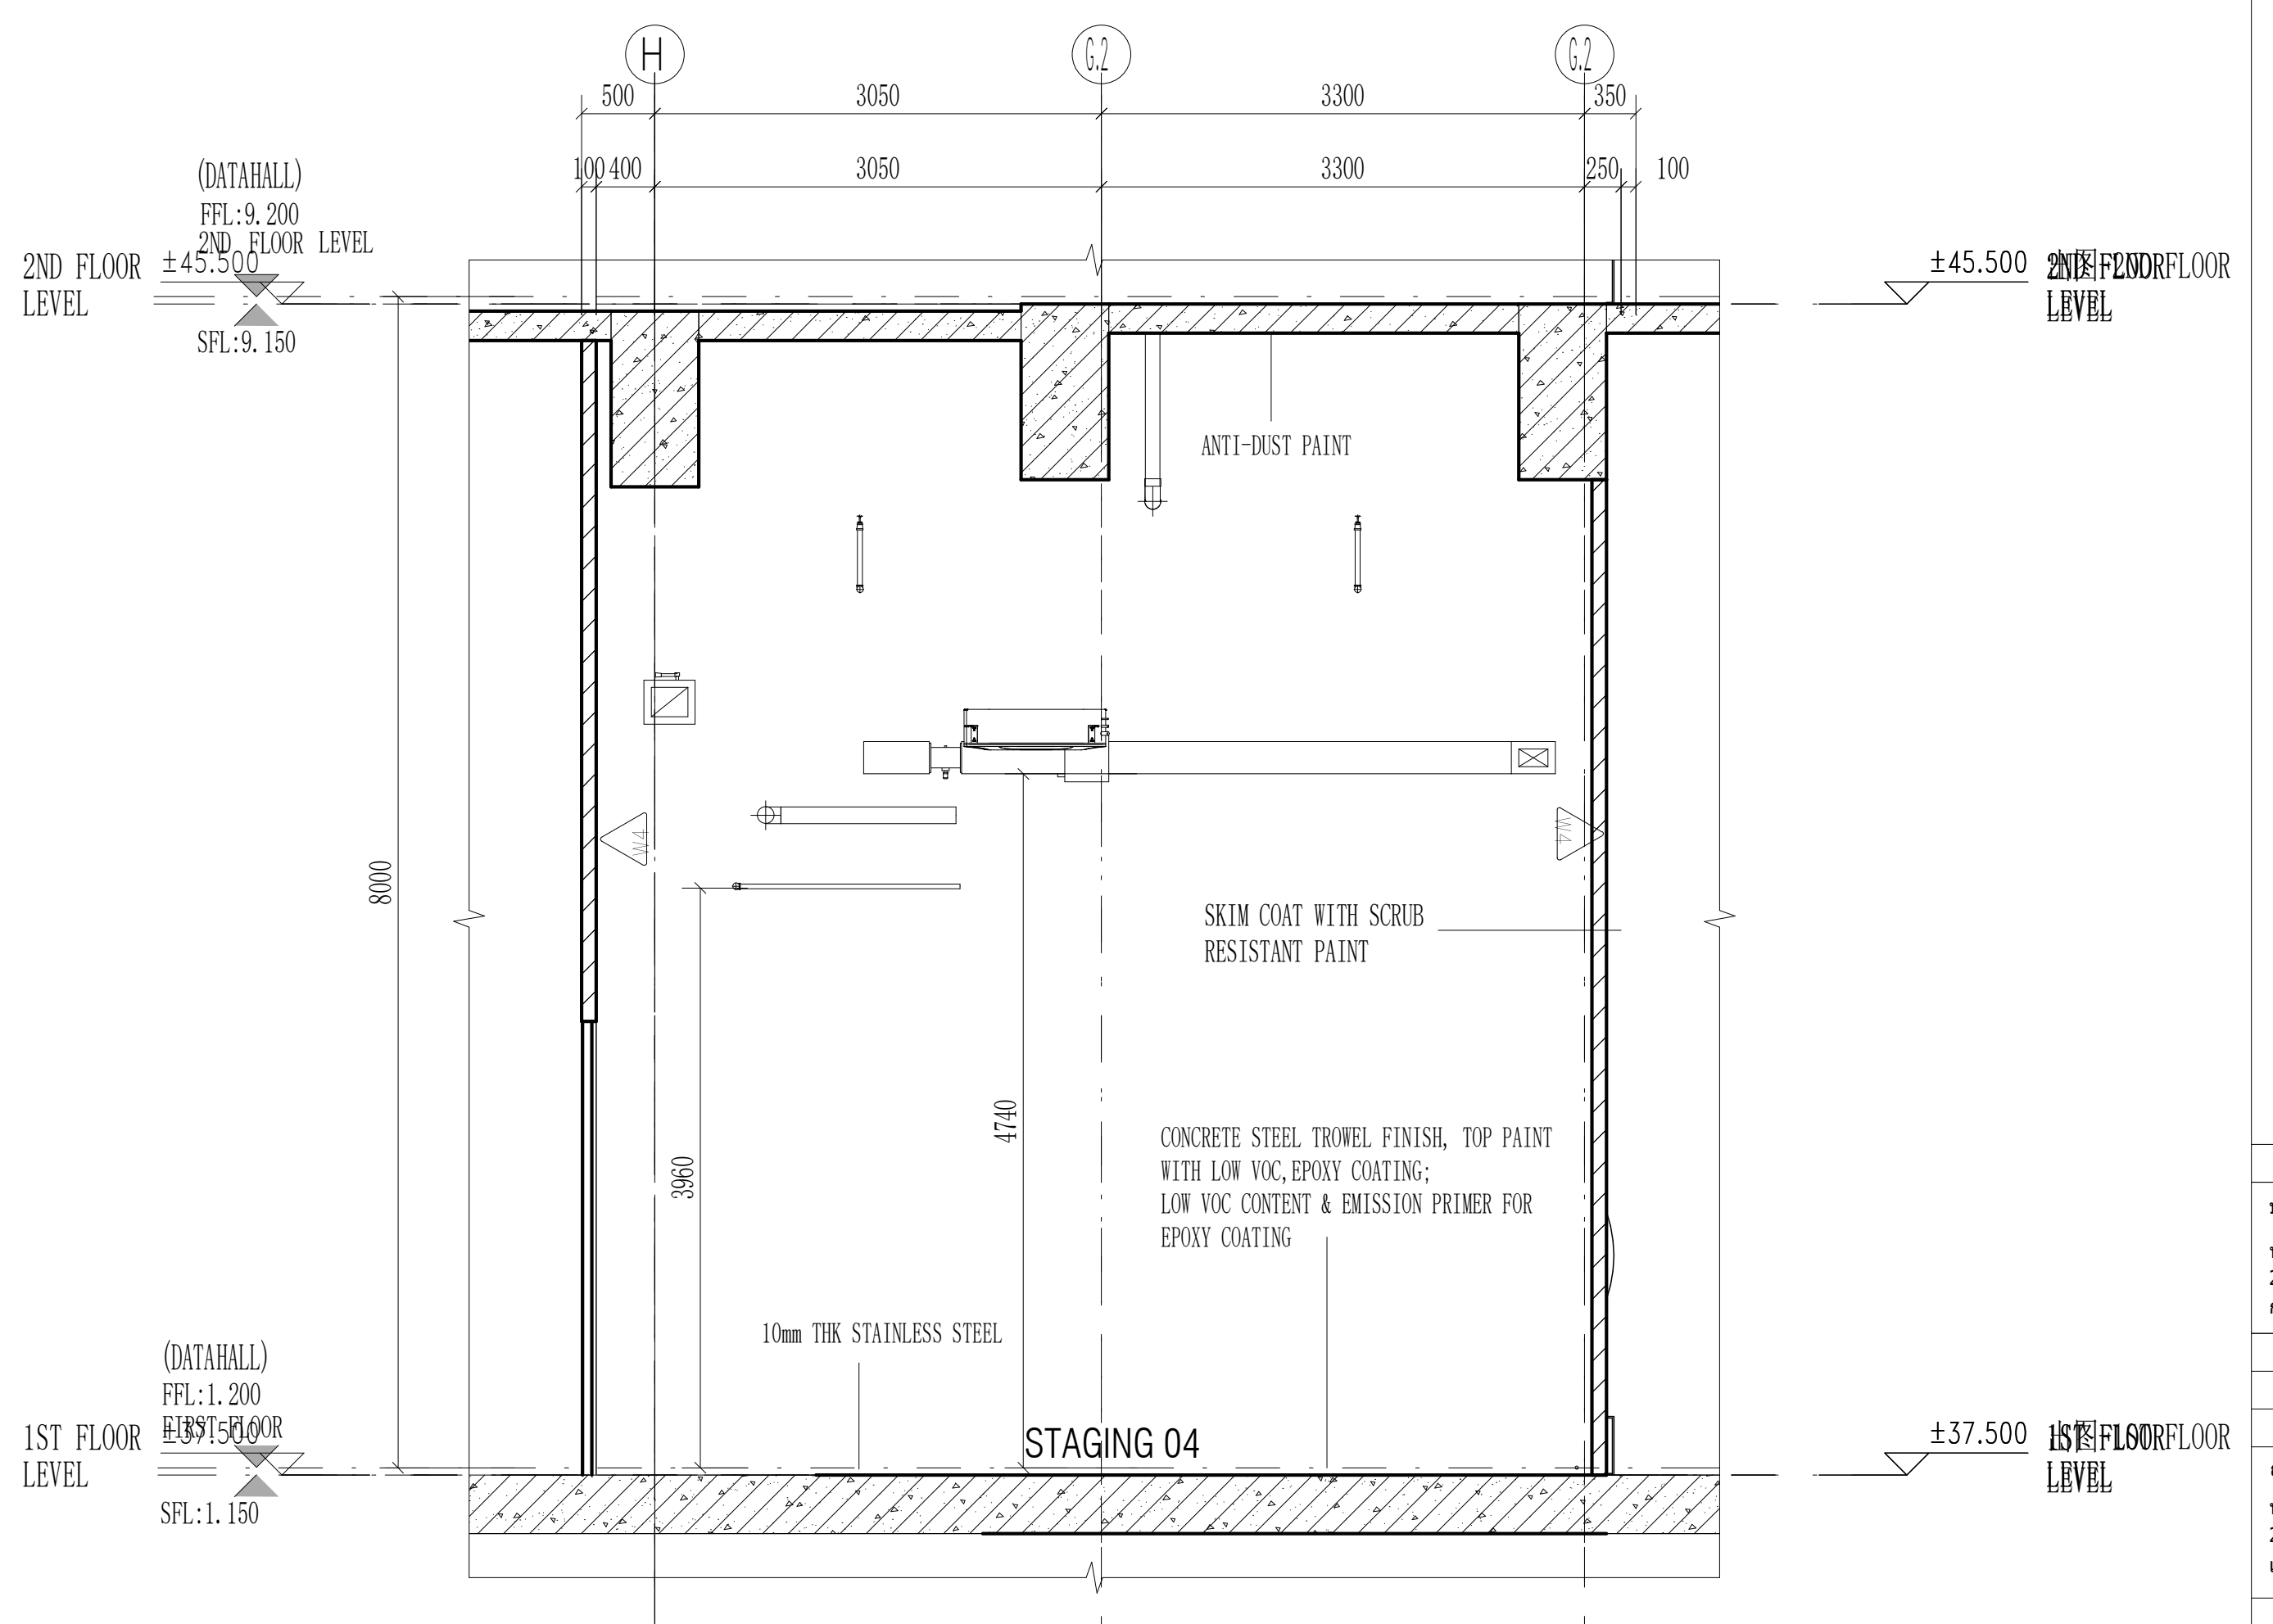
H
G.2
G.1
500
3050
3300
350
100
400
3050
3300
250
100
(DATAHALL)
FFL:9.200
2ND FLOOR LEVEL
SFL:9.150
2ND FLOOR LEVEL
±45.500
2ND FLOOR LEVEL
ANTI-DUST PAINT
SKIM COAT WITH SCRUB RESISTANT PAINT
CONCRETE STEEL TROWEL FINISH, TOP PAINT WITH LOW VOC,EPOXY COATING; LOW VOC CONTENT & EMISSION PRIMER FOR EPOXY COATING
10mm THK STAINLESS STEEL
8000
4740
3960
STAGING 04
(DATAHALL)
FFL:1.200
FIRST FLOOR
SFL:1.150
1ST FLOOR LEVEL
±37.500
1ST FLOOR LEVEL

STRAGING 02 SECTION C-C

Scale 1:50

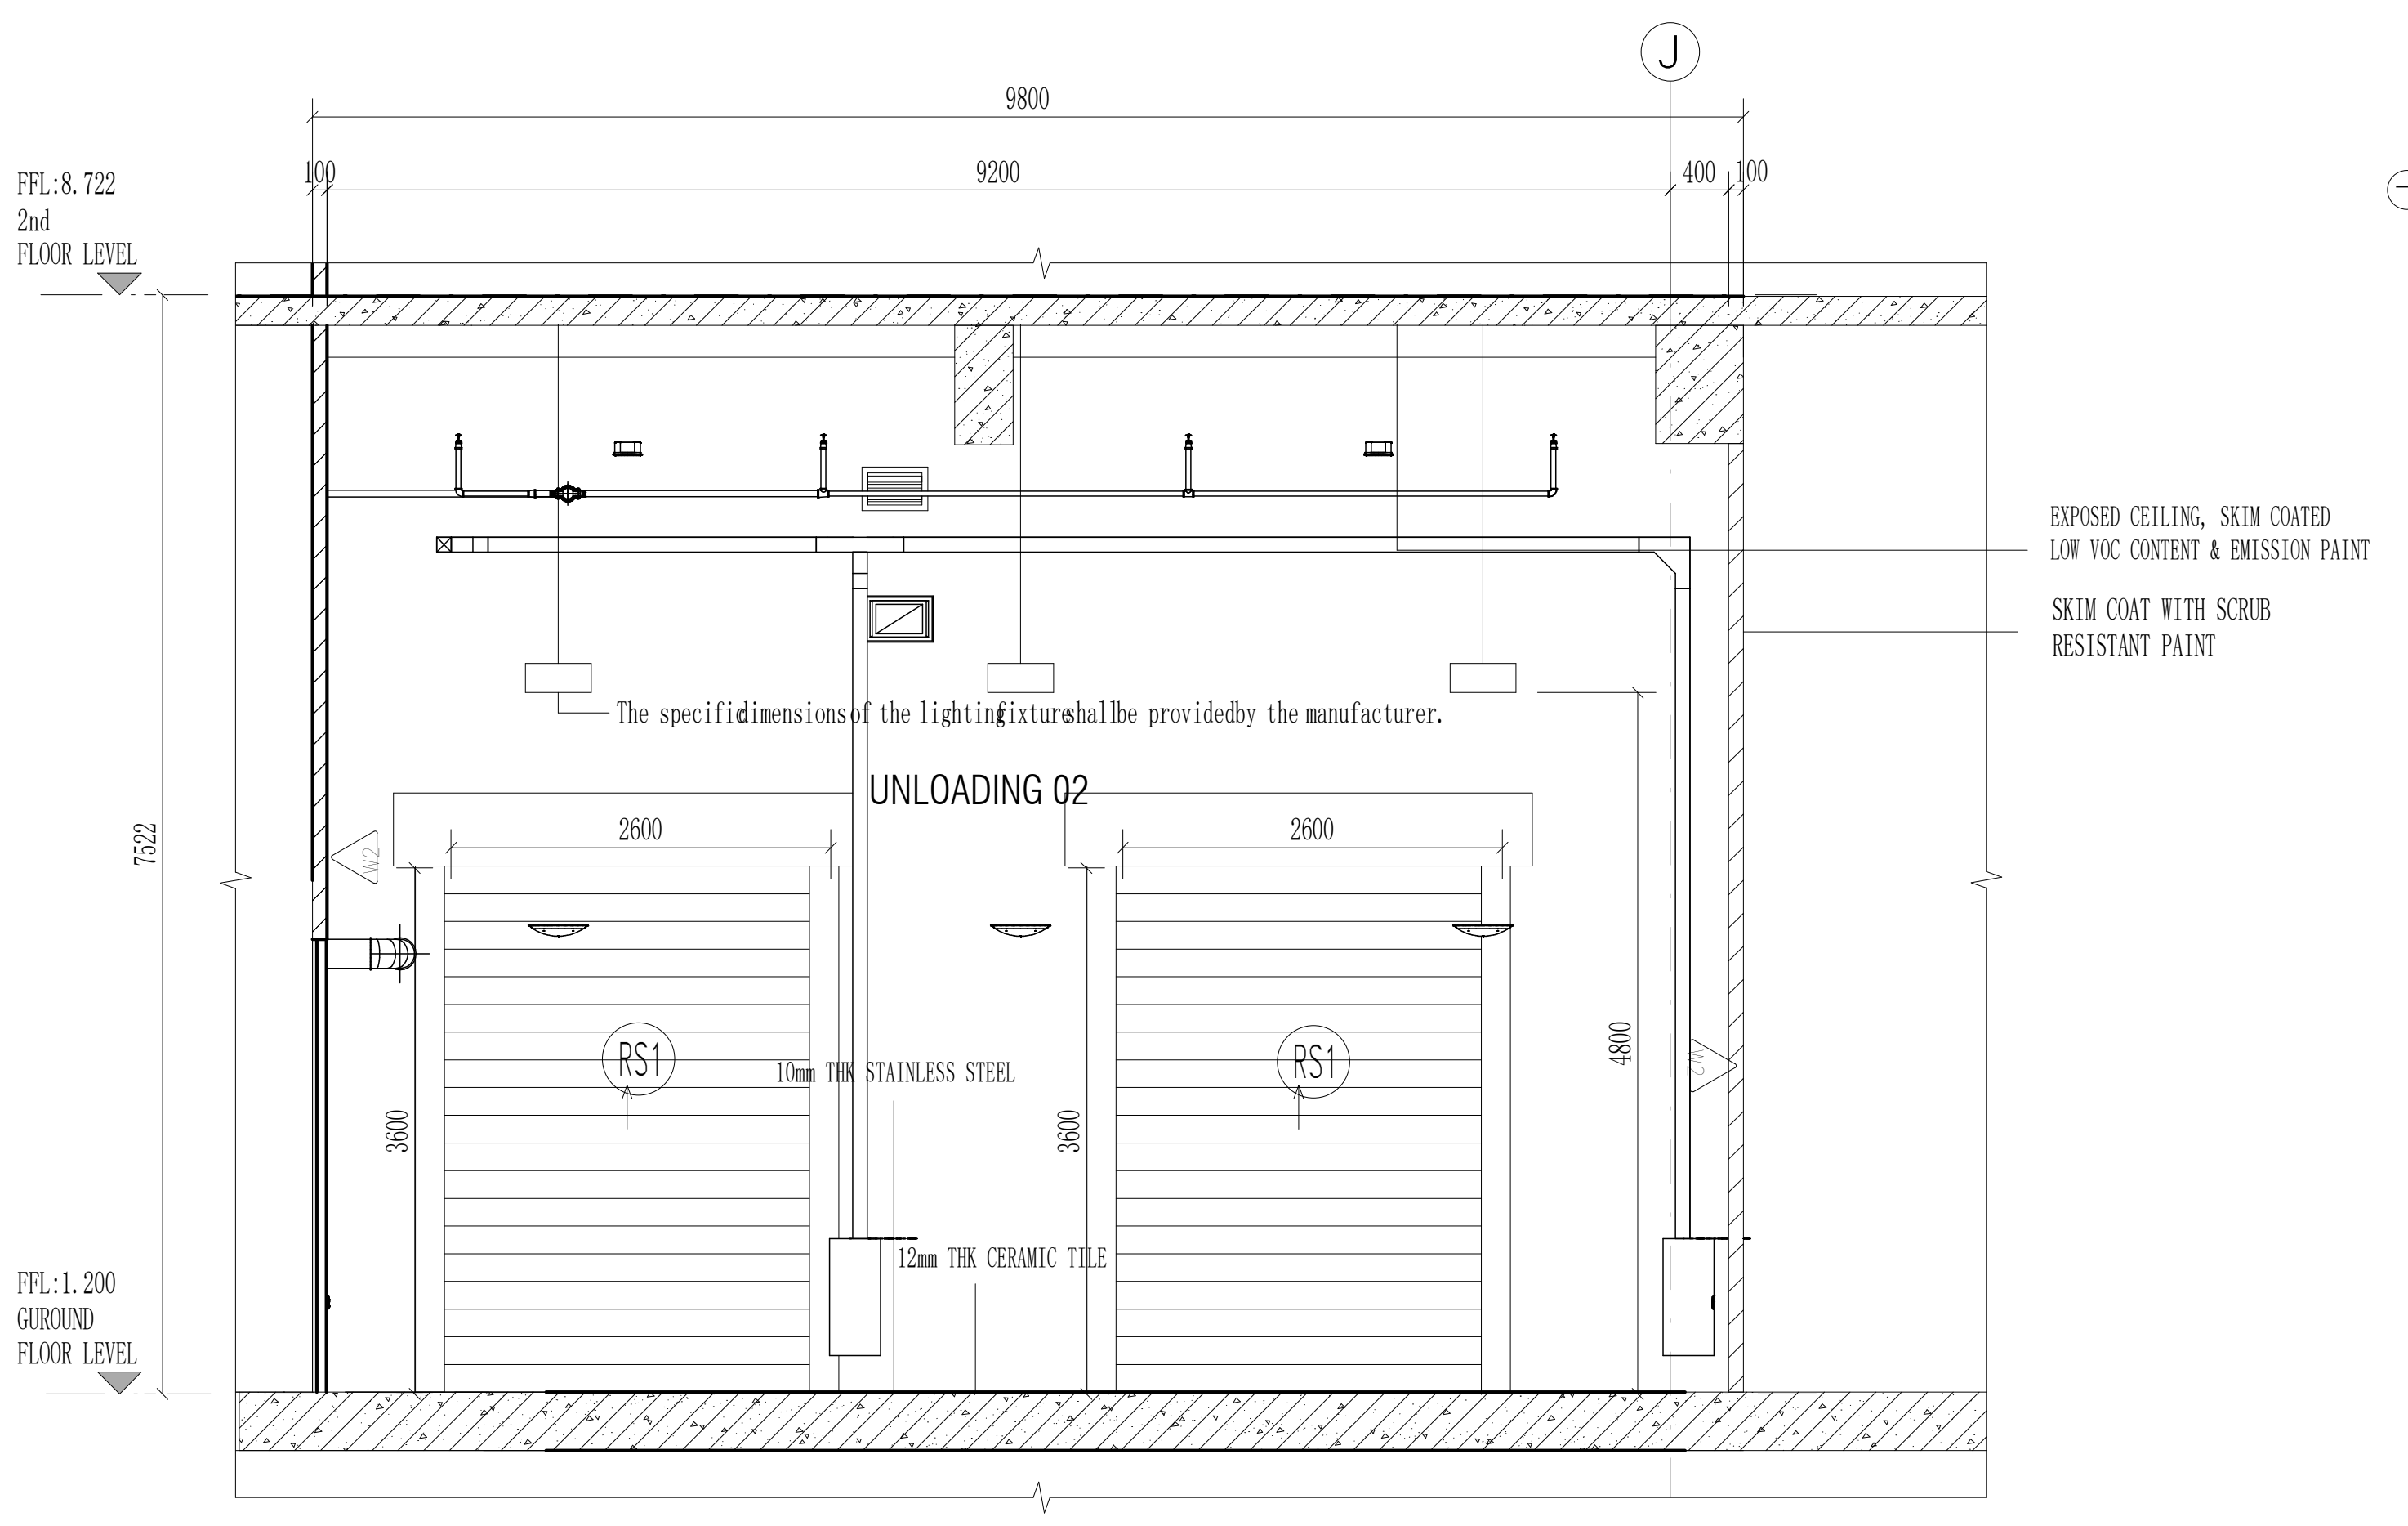
J
9800
9200
400
100
FFL:8.722
2nd
FLOOR LEVEL
EXPOSED CEILING, SKIM COATED LOW VOC CONTENT & EMISSION PAINT
SKIM COAT WITH SCRUB RESISTANT PAINT
The specific dimensions of the lighting fixture shall be provided by the manufacturer.
UNLOADING 02
2600
2600
RS1
RS1
10mm THK STAINLESS STEEL
12mm THK CERAMIC TILE
7522
4800
3600
FFL:1.200
GUROUND
FLOOR LEVEL

UNLOADING 02 SECTION B-B

Scale 1:50

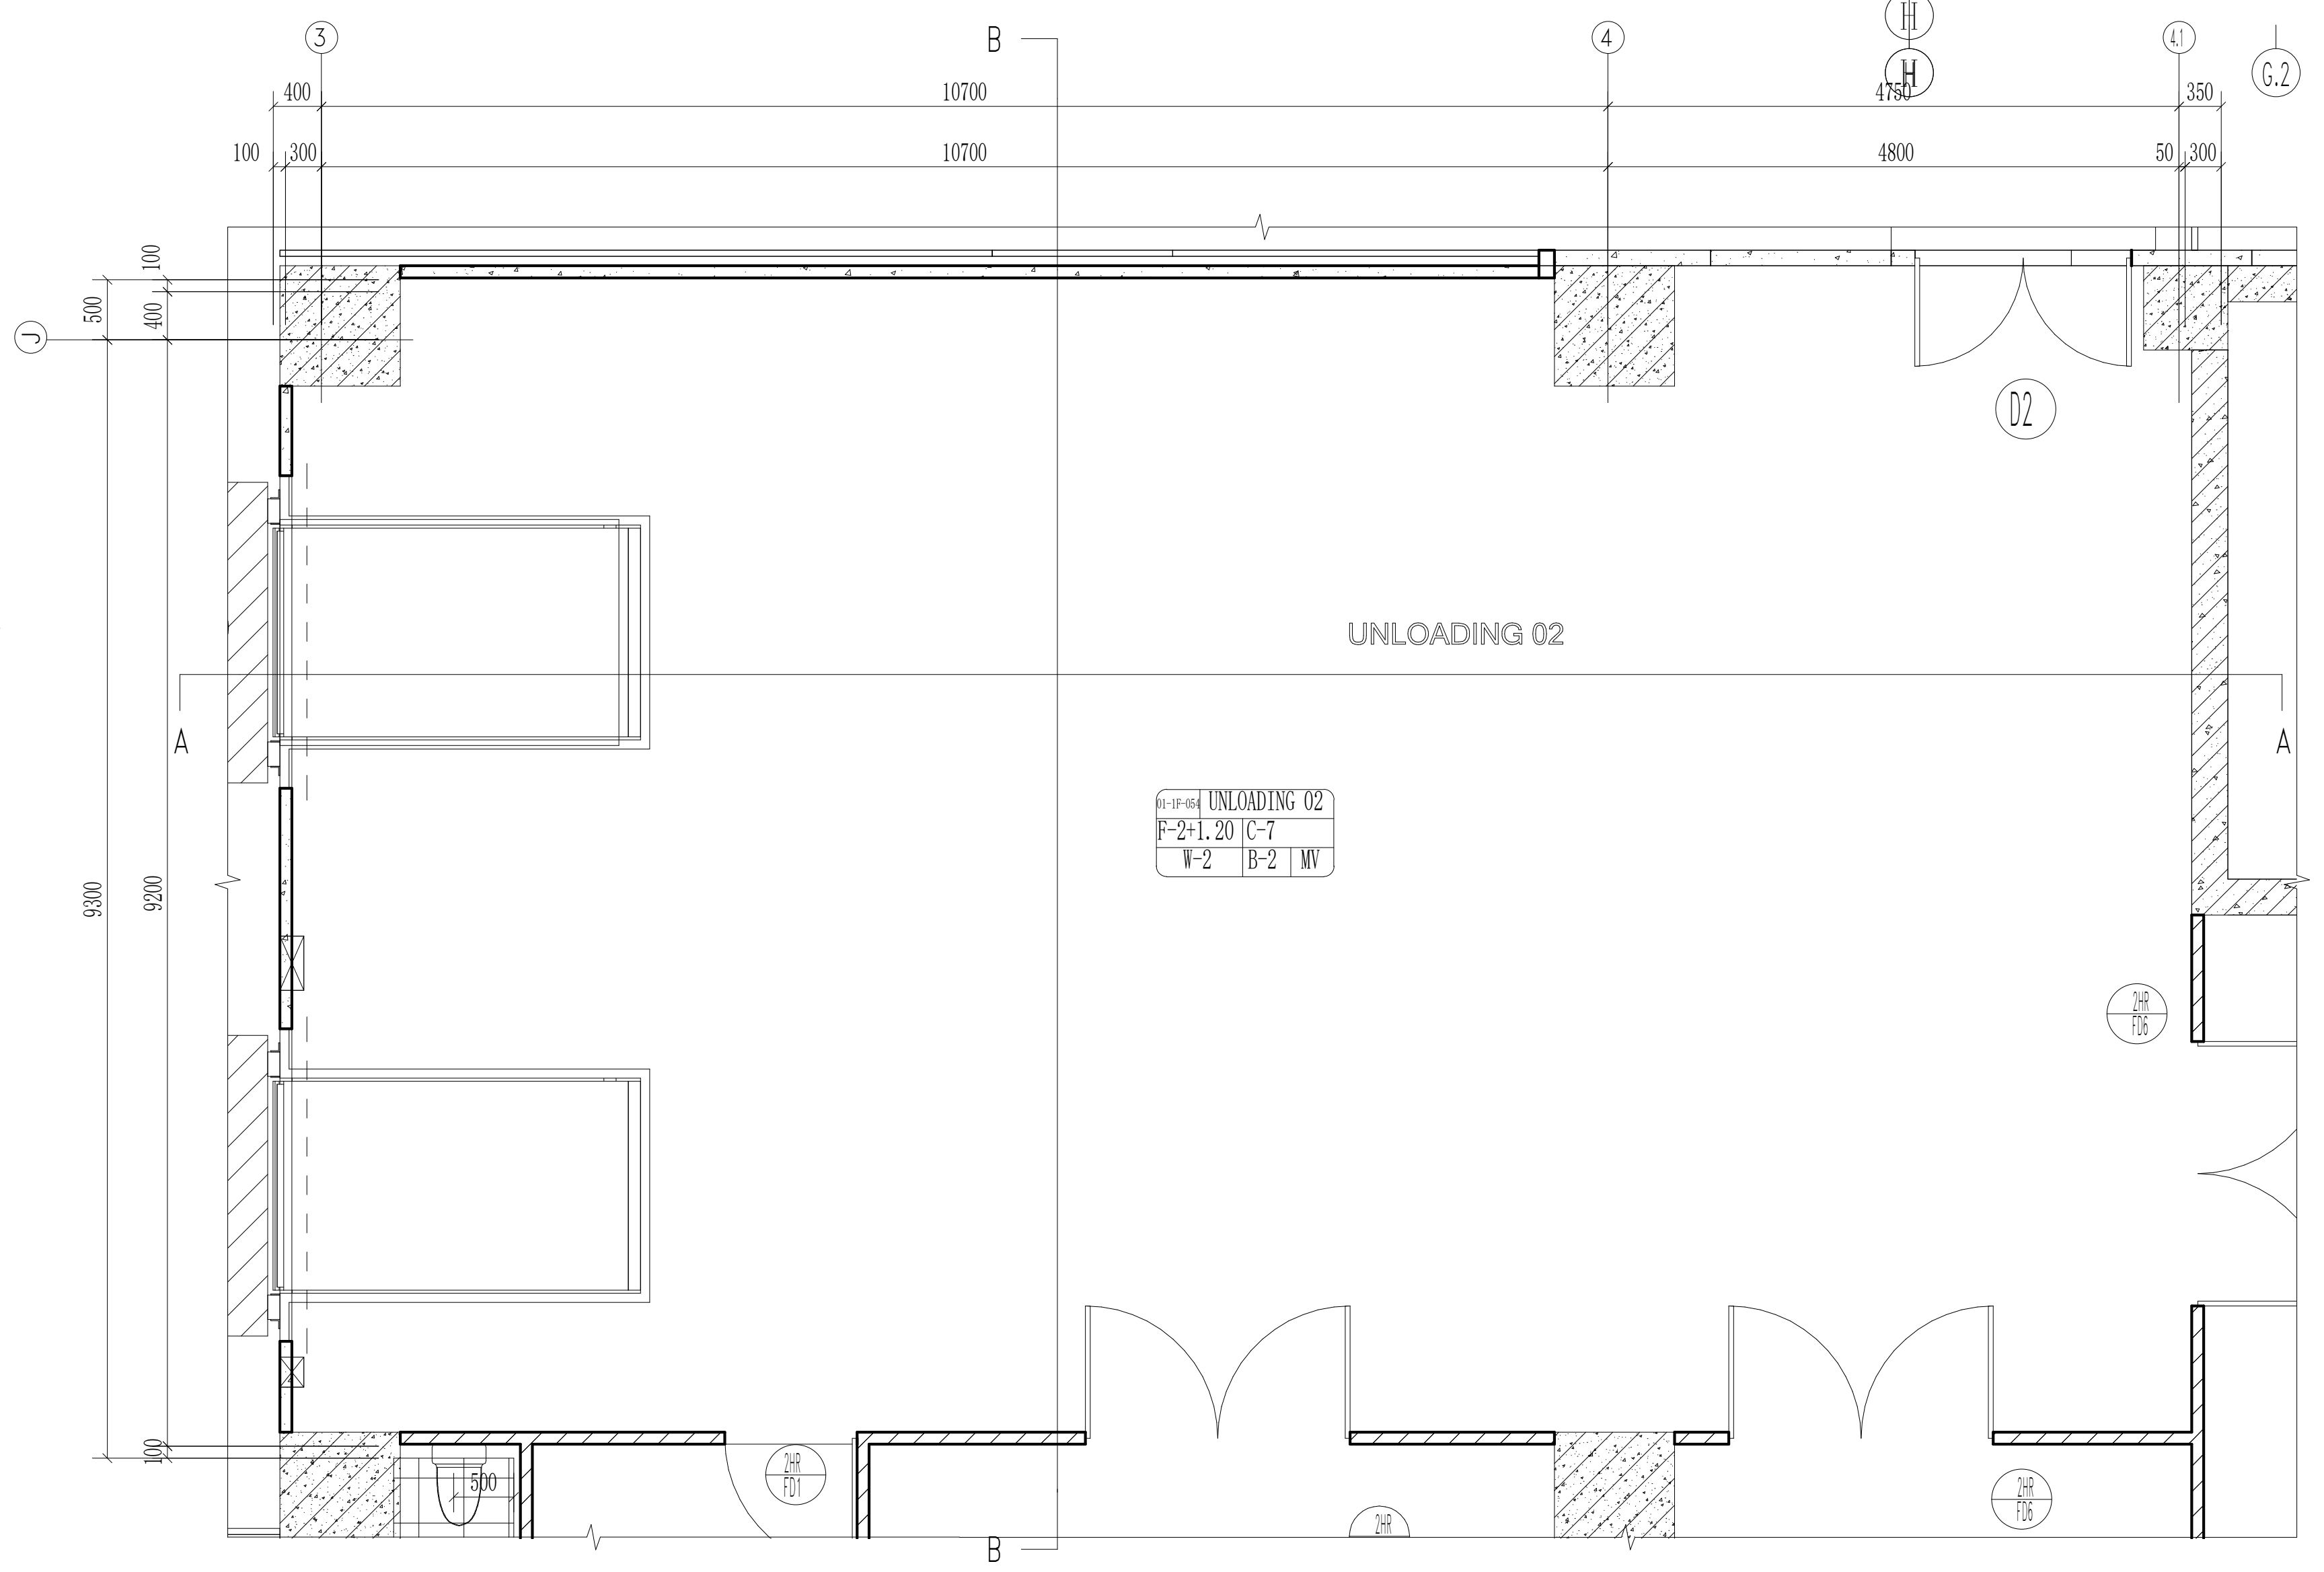
3
B
4
H
G.2
G.1
400
10700
4800
350
100
300
10700
4800
50
300
J
D2
UNLOADING 02
A
A
UNLOADING 02
F-2+1.20 C-7
W-2 B-2 W
9300
B

UNLOADING 02 FLOOR PLAN

Scale 1:50

THE "SFL" MARKED IN THE DRAWING REFERS TO THE STRUCTURAL FLOOR LEVEL, WHILE THE FINISHED FLOOR LEVEL (FFL) IS DETERMINED BASED ON FLOOR FINISHES.

NOTE :THIS PRINT IS OF A CONFIDENTIAL NATURE, IT SHALL NOT BE TRACED,PHOTOGRAPHED,PHOTOSTATED OR REPRODUCED IN ANY MANNER,NOR USED FOR ANY PURPOSE WHATSOEVER EXCEPT BY WRITTEN PERMISSION

CLIENT :

GULF EDGE DC 01

87 Wireless Road, M Thai Tower 11th. Floor, All Seasons Place, Lumpini,
Pathumwan, Bangkok 10330, Thailand

CONTRACTOR :

华西发展(泰国)有限公司
บริษัท หัวซือ ดีเวลลอปเม้นต์ (ประเทศไทย) จำกัด
HUASHI DEVELOPMENT CO.,LTD
No. 202, Room No. 1403, 14/F, Le Concorde Building,
Ratchadapisek Road, Huaykhwang Sub-District,
Huaykhwang District, Bangkok Metropolitan 10310.

CONSULTANT :

ARbay
บริษัท เอ อาร์ เบย์ จำกัด
ARbay Company Limited
31 st Floor Bangkok Insurance Building
25 South Sathorn road Thungmahamek
Sathorn Bangkok 10120 THAILAND
T +66 (0) 2286 8199
F +66 (0) 2286 2863
info@arbay.co.th

CONSULTANT :

Qbic Engineers & Architects Co.,Ltd.
8 Soi KALONG 4 SANAMBINNAM ROAD,
THASAI SUB-DISTRICT, MUANG NONTHABURI DISTRICT
, NONTHABURI.
Tel 662-950-4374
Fax 662-580-3231
E-Mail : qbic@qbic.co.th, www.qbic.co.th
QBIC ENGINEERS AND ARCHITECTS CO.,LTD.

CONSULTANT :

MITR
MITR TECHNICAL CONSULTANT CO.,LTD.
1168/8 12th FLOOR, LUMPINI TOWER BUILDING,
RAMA IV RD., THUNGMAHAMEK, SATHORN, BANGKOK 10120, THAILAND
TEL : 0-2679-9079-84
FAX : 0-2679-9085 E-mail: mitr_dd@mitr.com

Architect :	SIGNATURE
ประกิต พนานุรัตน์ วสถ. 580 ที่อยู่ 251/1 ถ.จารุเมือง แขวงรองเมือง เขตปทุมวัน กรุงเทพมหานคร โทรศัพท์ 02-286-8199	
Structural Engineer :	SIGNATURE
วิศวกรผู้ออกแบบโครงสร้าง	
ณัฐสม สงวนวงษ์ วย 1423 ที่อยู่ 2/1 ซ.รามคำแหง 150 ถ.รามคำแหง แขวง สะพานสูง เขต สะพานสูง กทม. 10240	ณัฐสม สงวนวงษ์
Structural Inspector :	SIGNATURE
วิศวกรผู้ตรวจสอบโครงสร้าง	
โกมล จุฑาภัทร วย 964 ที่อยู่ 24/18 ซ.นวมินทร์ 129 ถ. นวมินทร์ แขวง นวลจันทร์ เขต บึงกุ่ม กทม. 10230	
Electrical Engineer :	SIGNATURE
วิศวกรผู้ออกแบบระบบไฟฟ้ากำลัง	
นายสุภัทร บูรณวิทย์ วฟก.1265 ที่อยู่ 21 ซอยทานสัมฤทธิ์ 13 ตำบลท่าทราย อ.เมืองนนทบุรี จ.นนทบุรี 11000	
Mechanical Engineer :	SIGNATURE
วิศวกรผู้ออกแบบระบบเครื่องกลและปรับอากาศ	
นายประสิทธิ์ เกี้ยวสุนทร วก.1221 ที่อยู่ 44/372 ซอยบางกระดี่ 35/1 แขวงแสมดำ เขตบางขุนเทียน กทม. 10150	ประสิทธิ์
Sanitary Engineer :	SIGNATURE
วิศวกรผู้ออกแบบระบบสุขาภิบาล และดับเพลิง	
นายทศวรรษ สนั่นฤทธิ์ วส. 215 ที่อยู่ บ้านเลขที่ 99/107 หมู่ที่ 3 ต.ศีรษะจรเข้น้อย อ.บางเสาธง จ.สมุทรปราการ 10540	ทศวรรษ

ISSUE/REVISION

REV.	DESCRIPTION	DATE
A	90% DEVELOPED	09/05/2026

PROJECT NAME :

GEDC 01

LOCATION:
Nikhom Phattana district, Rayong ,industrial estate,CPGC

BUILDING :
MAIN BUILDING

90% DEVELOPED

TITLE :

ROOM DETAIL-1F-UNLOADING
02、STAGING 03、STAGING 04

JOB NO.	SCALE 1 : 50
DRAWN LYT	REF.
CHECKED LJC	DWG. NO. MPK01A-90-A-RD-116
APPROVED LXD	
DATE 2026.05.09	

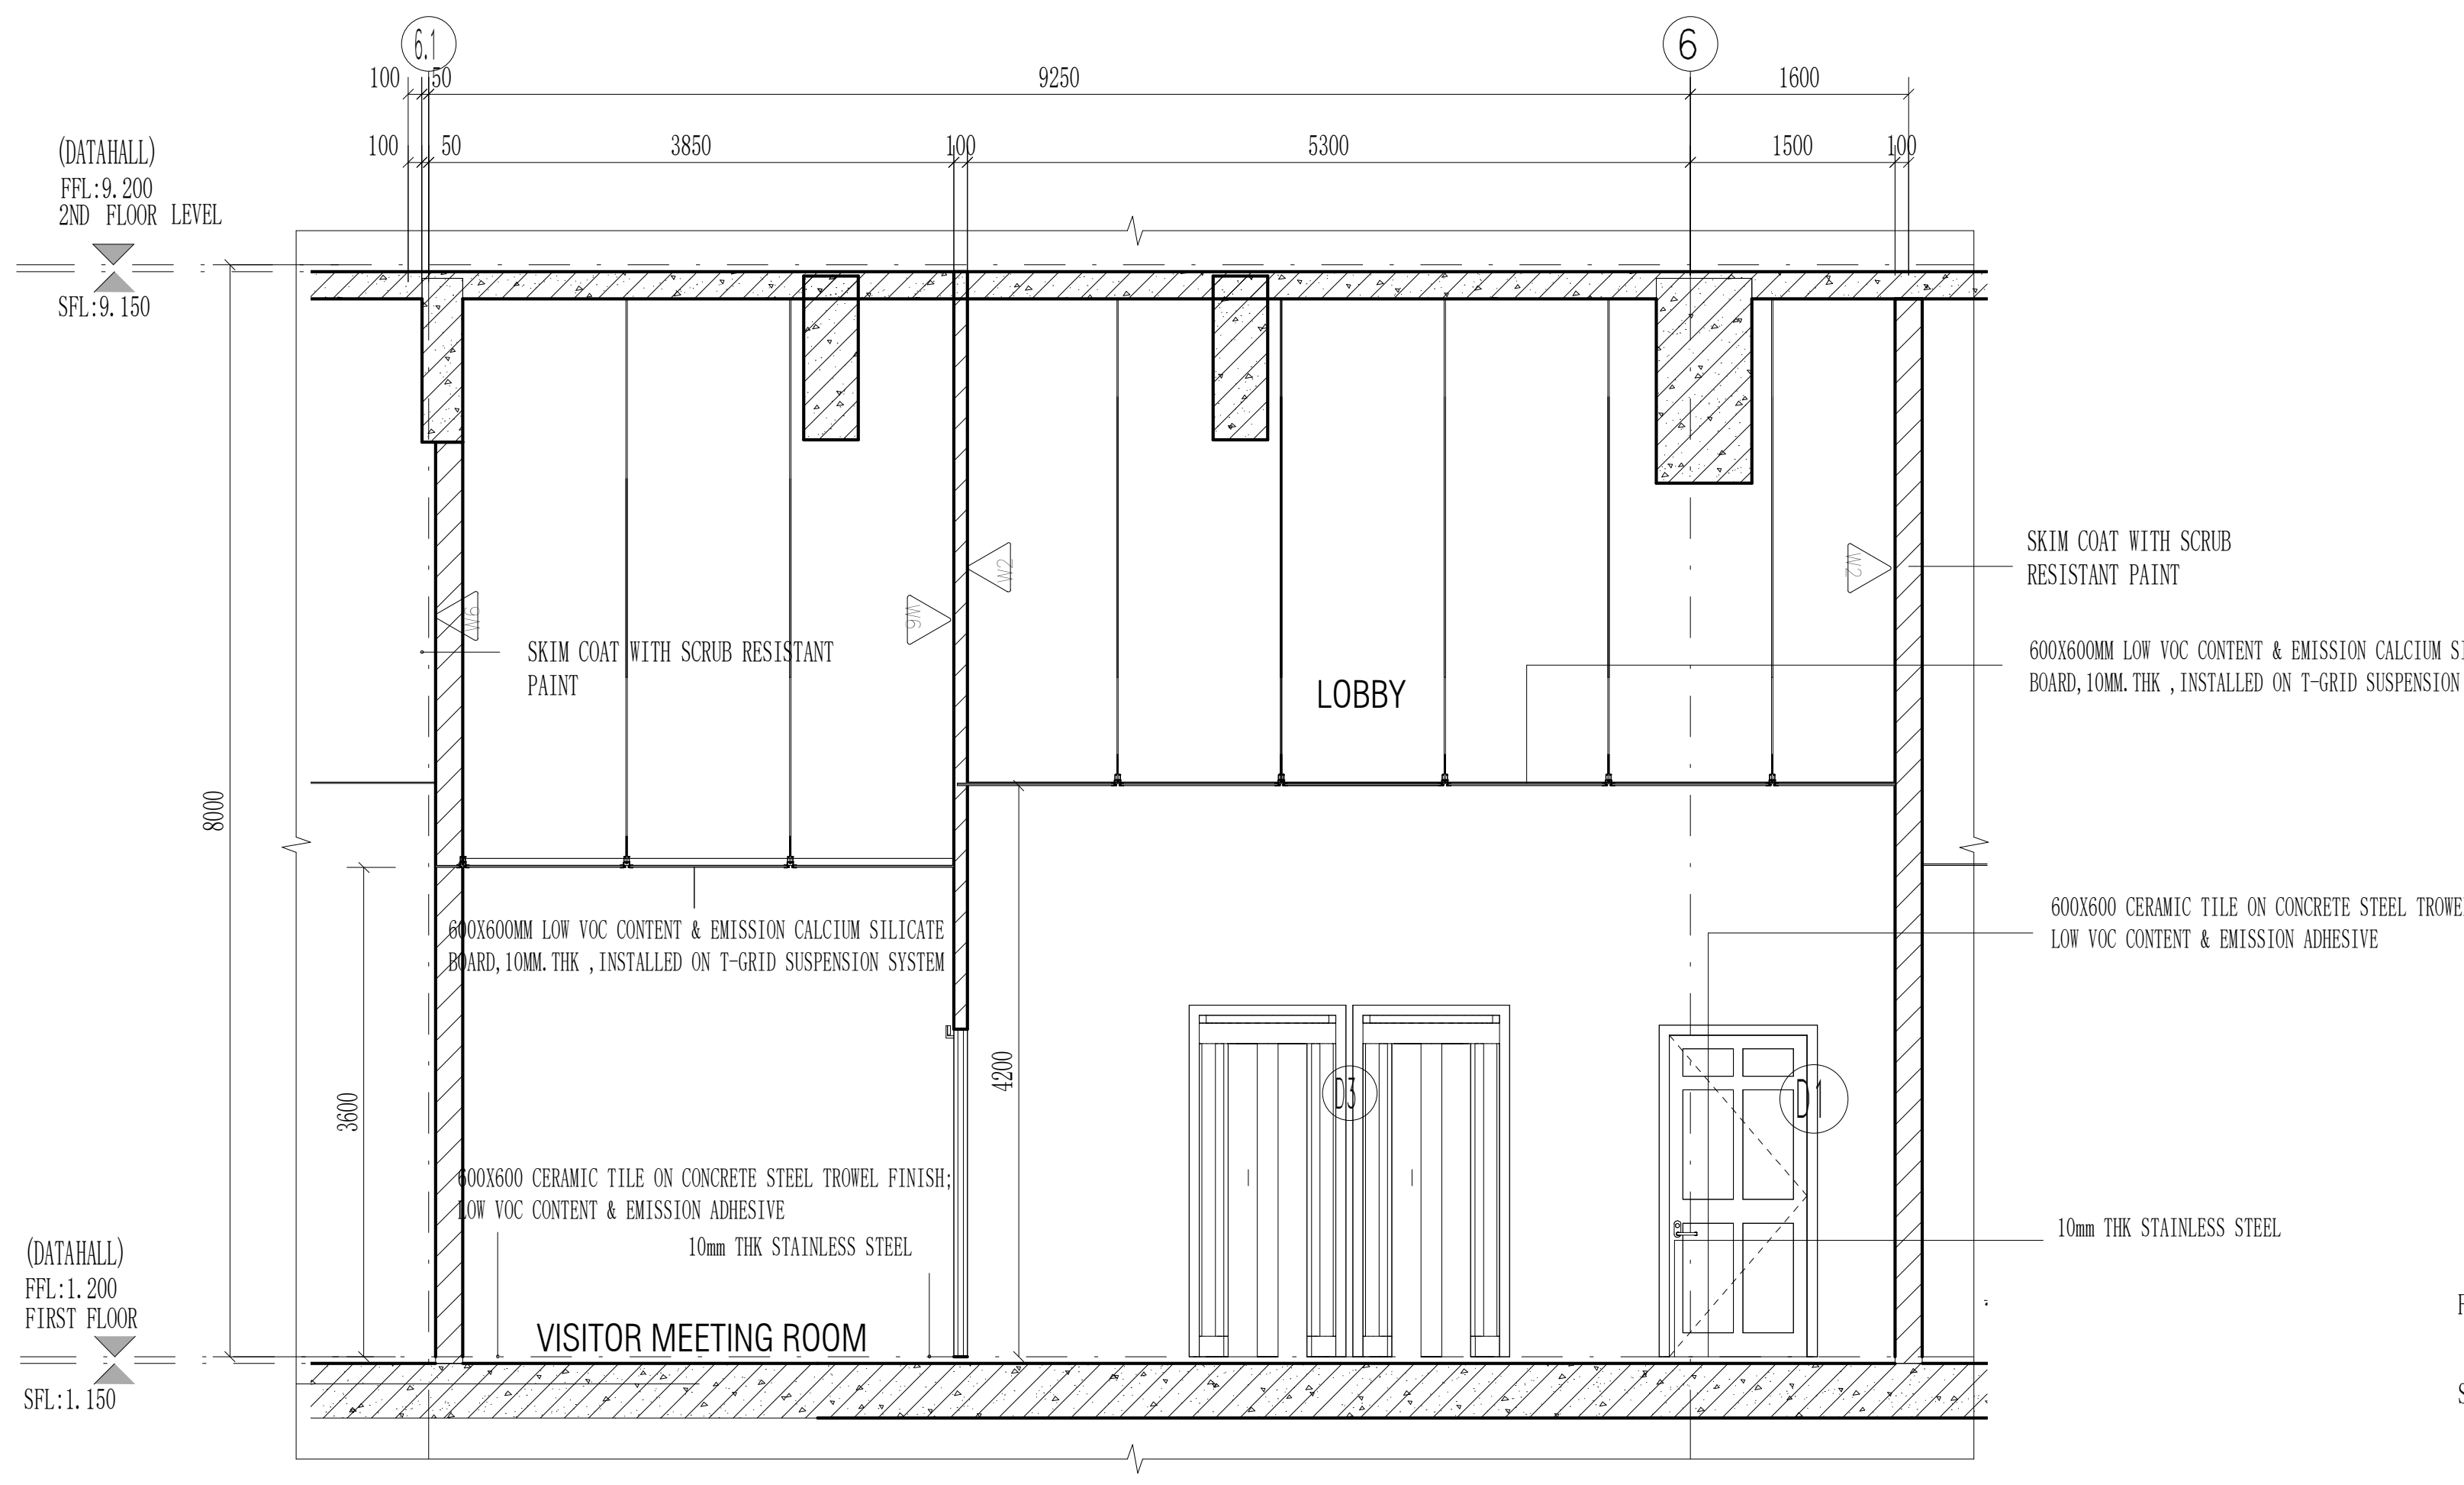
6.1
6
100
50
9250
1600
100
3850
5300
1500
(DATAHALL)
FFL:9.200
2ND FLOOR LEVEL
SFL:9.150
SKIM COAT WITH SCRUB RESISTANT PAINT
LOBBY
SKIM COAT WITH SCRUB RESISTANT PAINT
600X600MM LOW VOC CONTENT & EMISSION CALCIUM SILICATE BOARD,10MM.THK ,INSTALLED ON T-GRID SUSPENSION SYSTEM
600X600MM LOW VOC CONTENT & EMISSION CALCIUM SILICATE BOARD,10MM.THK ,INSTALLED ON T-GRID SUSPENSION SYSTEM
600X600 CERAMIC TILE ON CONCRETE STEEL TROWEL FINISH; LOW VOC CONTENT & EMISSION ADHESIVE
600X600 CERAMIC TILE ON CONCRETE STEEL TROWEL FINISH; LOW VOC CONTENT & EMISSION ADHESIVE
10mm THK STAINLESS STEEL
10mm THK STAINLESS STEEL
8000
3600
4200
D3
D1
(DATAHALL)
FFL:1.200
FIRST FLOOR
SFL:1.150
VISITOR MEETING ROOM

LOBBY、VISITOR MEETING ROOM SEECTION A-A

Scale 1:50

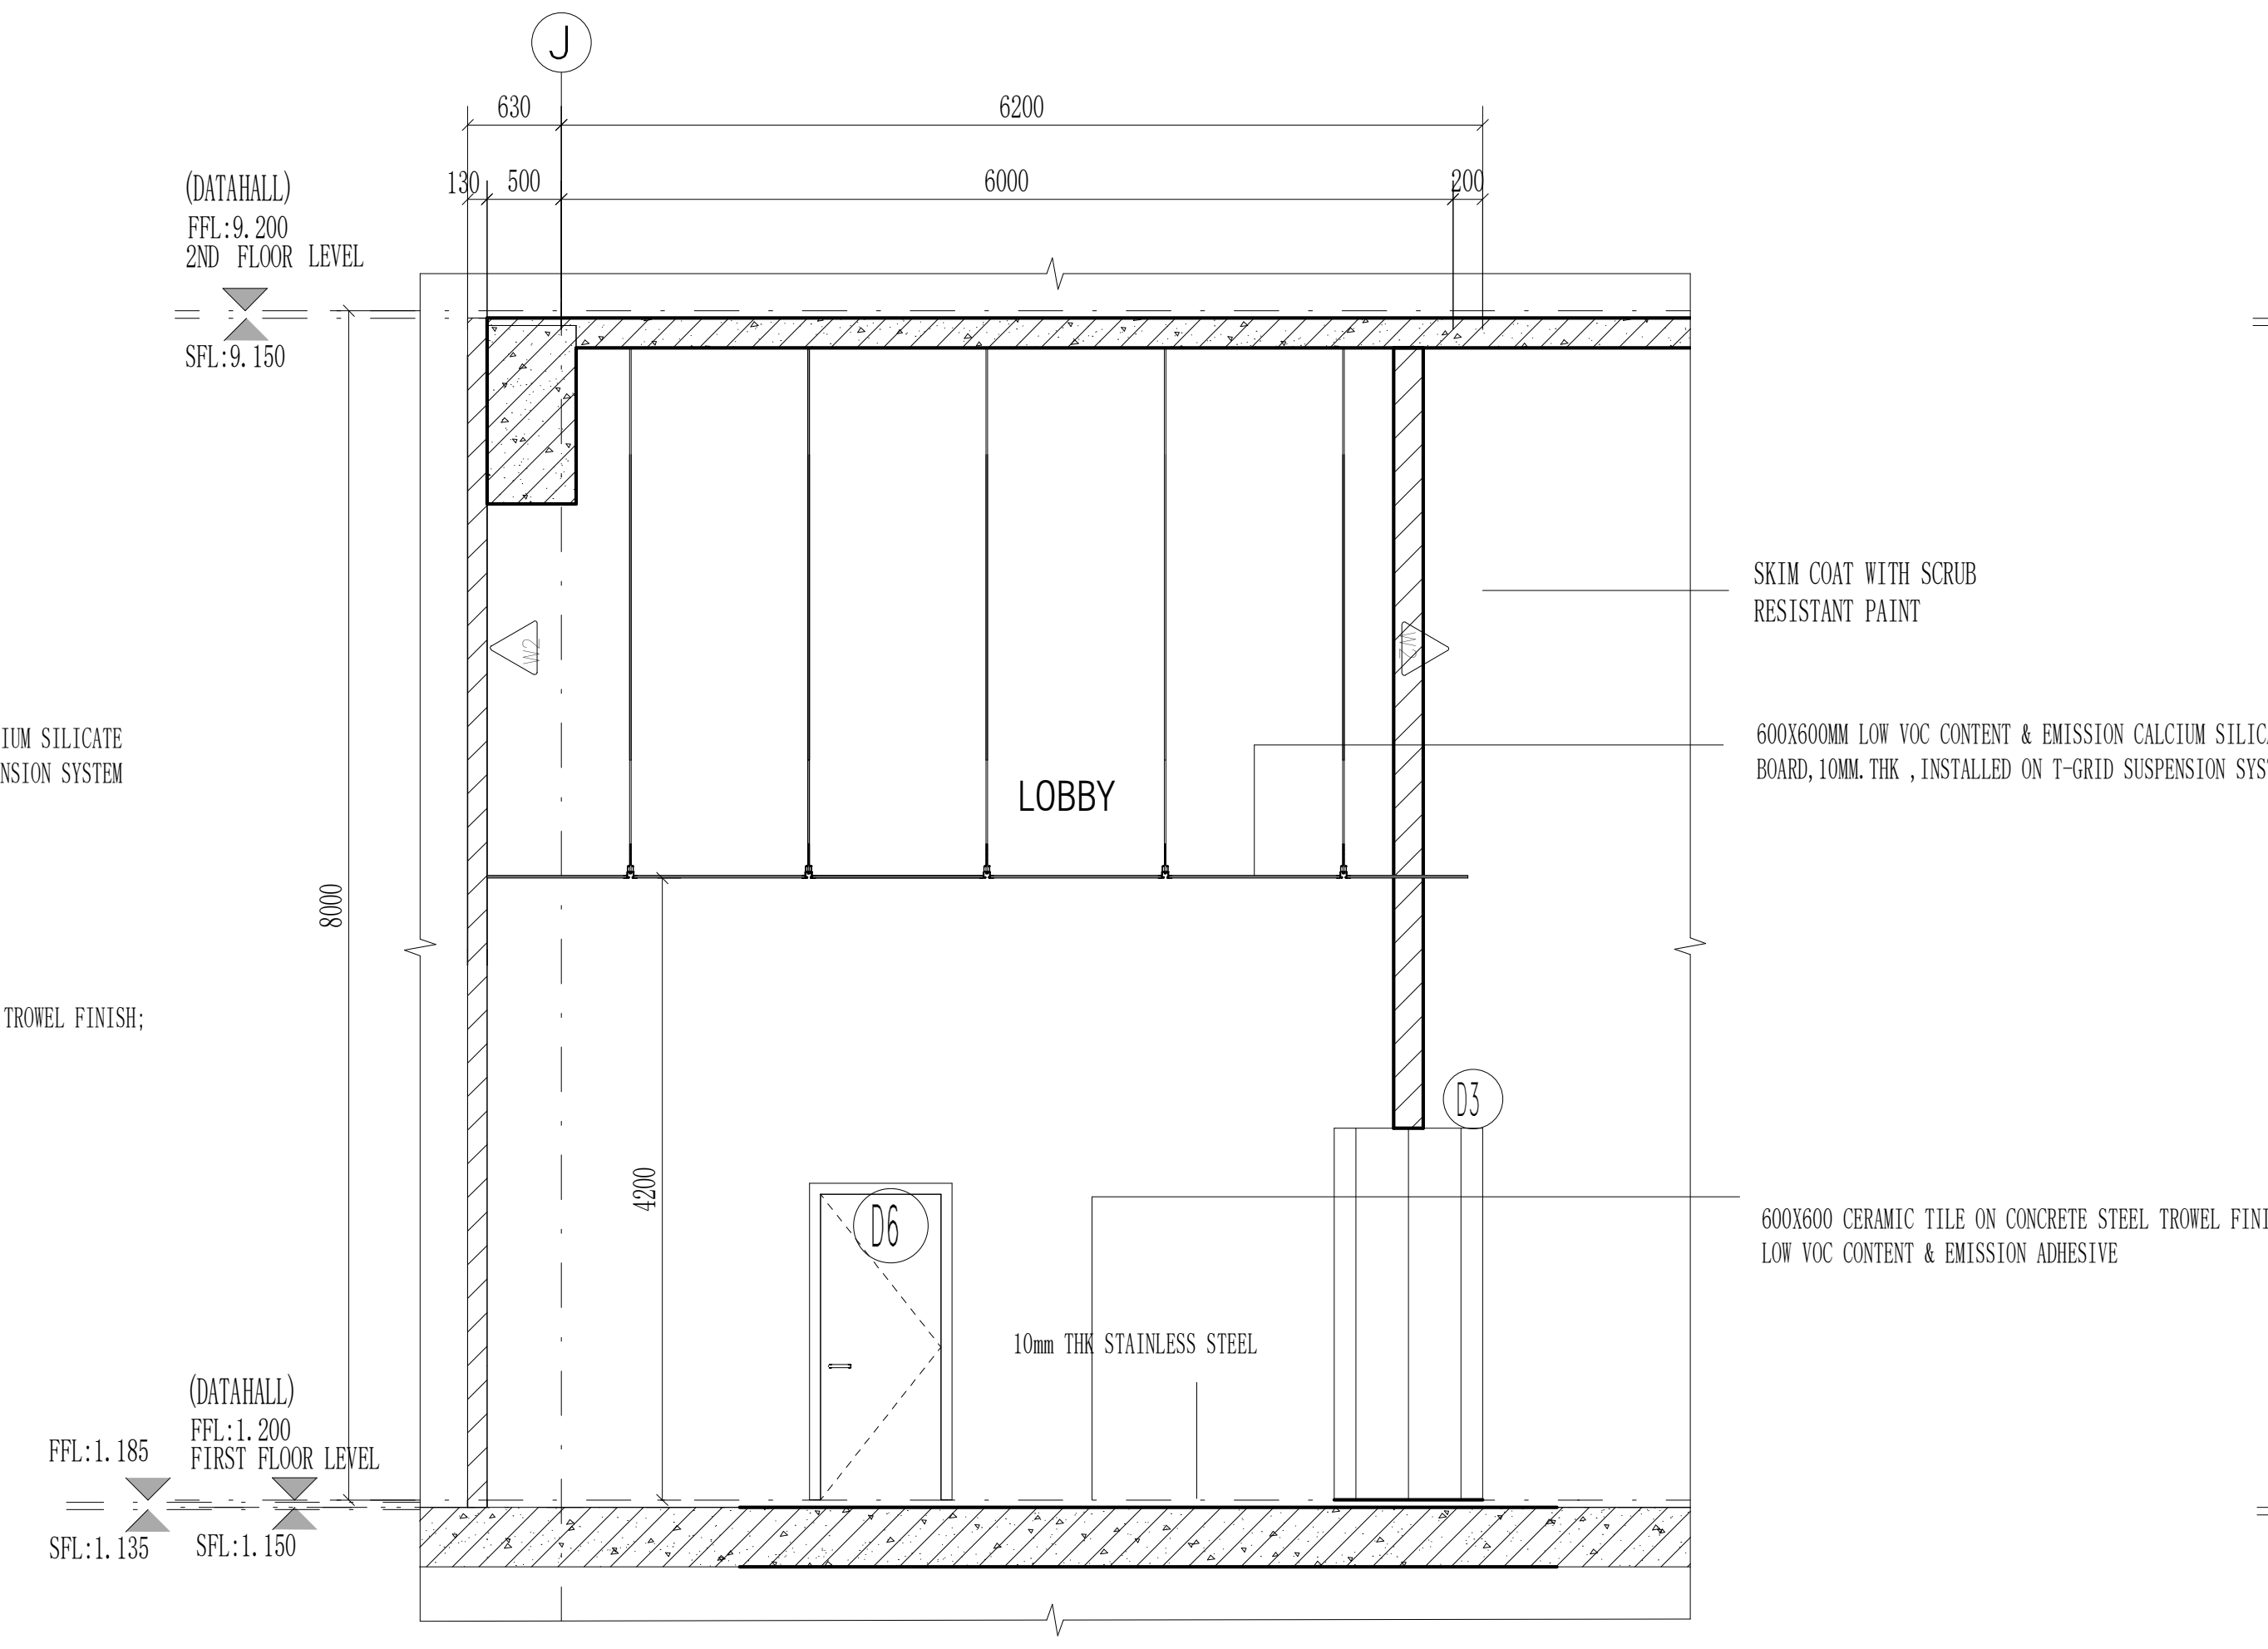
J
630
6200
130
500
6000
200
(DATAHALL)
FFL:9.200
2ND FLOOR LEVEL
SFL:9.150
SKIM COAT WITH SCRUB RESISTANT PAINT
600X600MM LOW VOC CONTENT & EMISSION CALCIUM SILICATE BOARD,10MM.THK ,INSTALLED ON T-GRID SUSPENSION SYSTEM
LOBBY
8000
4200
D6
D3
10mm THK STAINLESS STEEL
600X600 CERAMIC TILE ON CONCRETE STEEL TROWEL FINISH; LOW VOC CONTENT & EMISSION ADHESIVE
FFL:1.185
SFL:1.135
(DATAHALL)
FFL:1.200
FIRST FLOOR LEVEL
SFL:1.150

LOBBY SECTION B-B

Scale 1:50

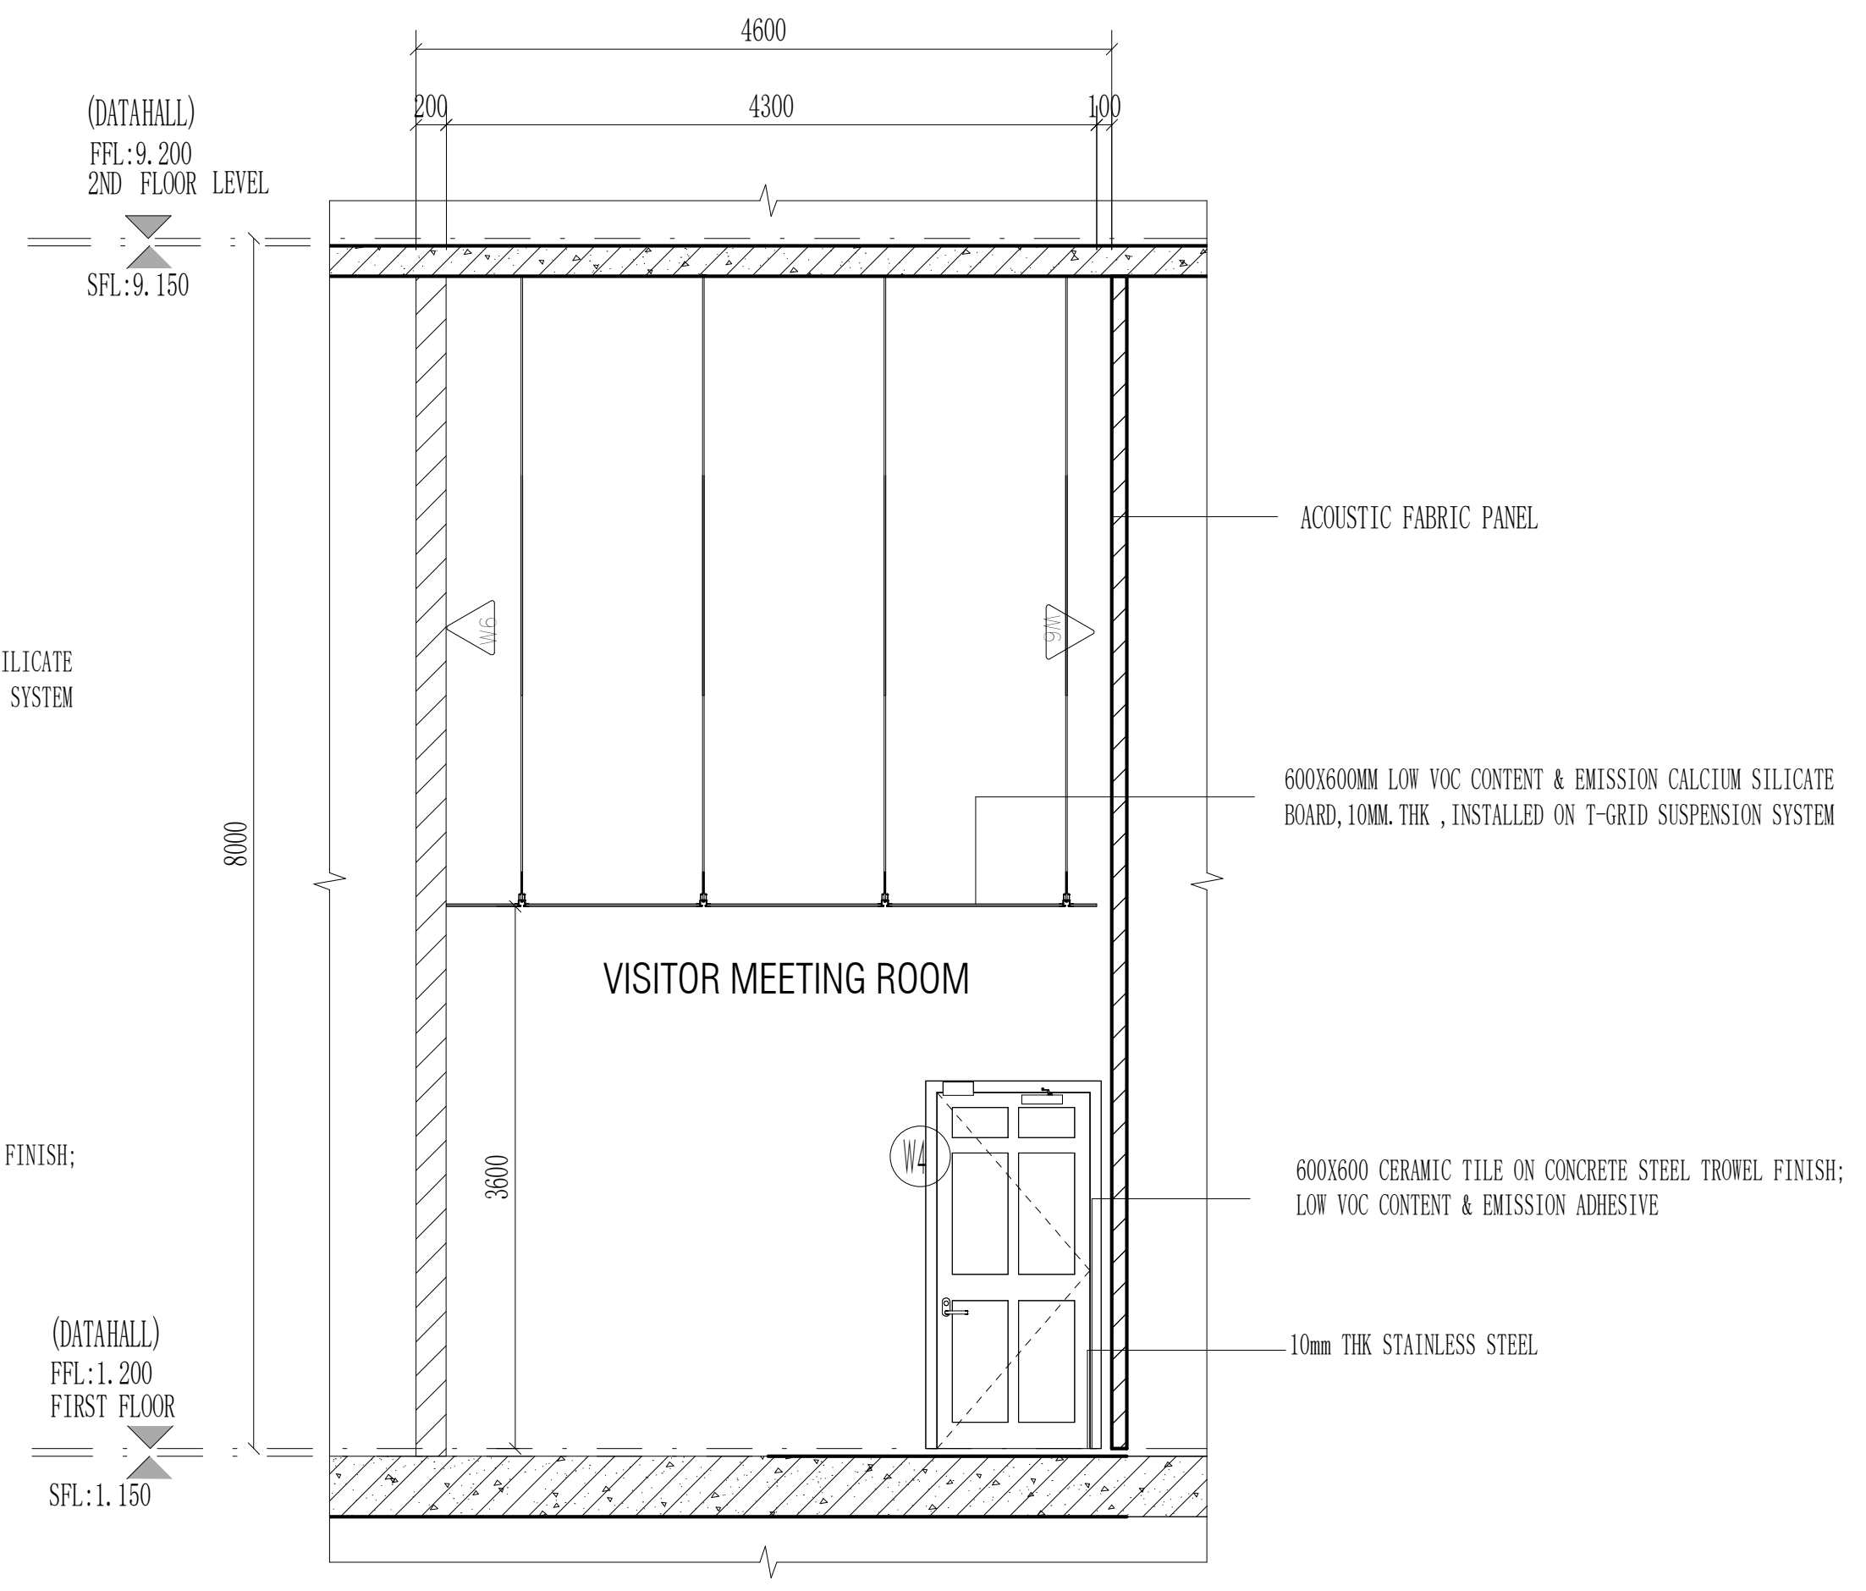
4600
200
4300
100
(DATAHALL)
FFL:9.200
2ND FLOOR LEVEL
SFL:9.150
ACOUSTIC FABRIC PANEL
600X600MM LOW VOC CONTENT & EMISSION CALCIUM SILICATE BOARD,10MM.THK ,INSTALLED ON T-GRID SUSPENSION SYSTEM
VISITOR MEETING ROOM
8000
3600
W4
600X600 CERAMIC TILE ON CONCRETE STEEL TROWEL FINISH; LOW VOC CONTENT & EMISSION ADHESIVE
10mm THK STAINLESS STEEL
(DATAHALL)
FFL:1.200
FIRST FLOOR
SFL:1.150

VISITOR MEETING ROOM SECTION C-C

Scale 1:50

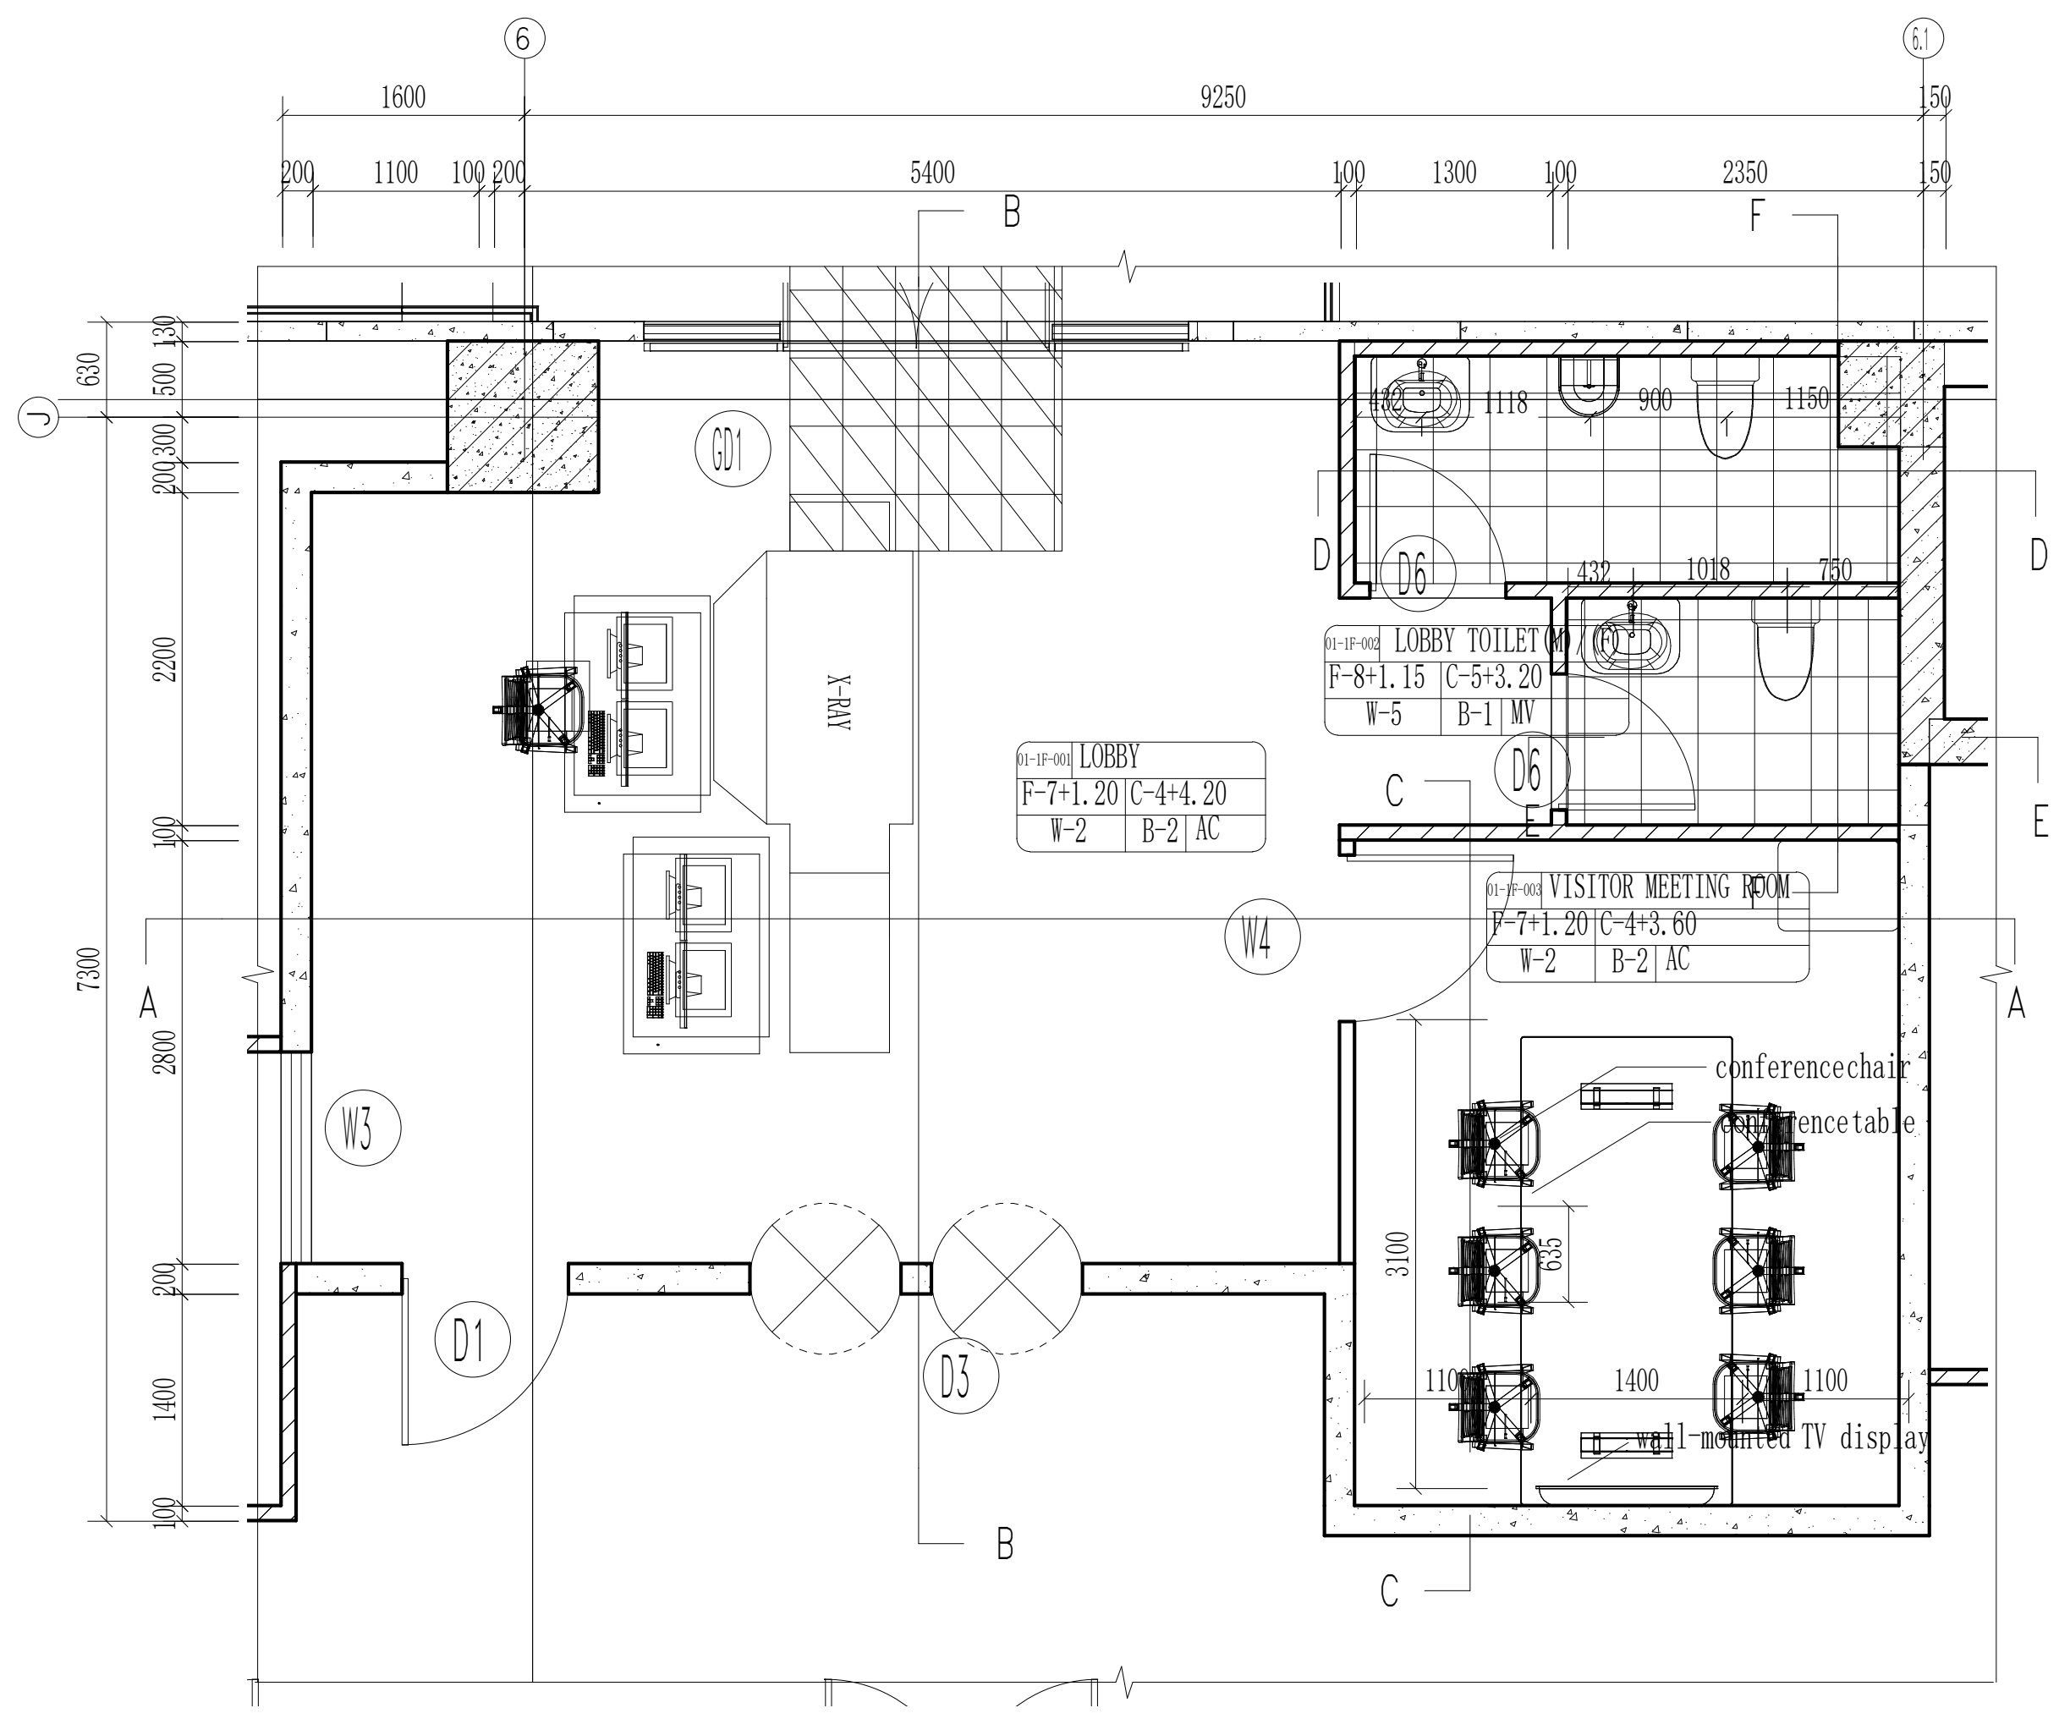
6
6.1
1600
9250
5400
1300
2350
B
F
D
E
A
C
B
C
D
J
LOBBY
LOBBY TOILET
VISITOR MEETING ROOM
F-F+1.15
C-5+3.20
W-5
B-1
W4
W5
D1
D3
D5
D6
conferencechair
conferencetable
TV display

LOBBY、LOBBY TOILET、VISITOR MEETING ROOM FLOOR PLAN

Scale 1:50

THE "SFL" MARKED IN THE DRAWING REFERS TO THE STRUCTURAL FLOOR LEVEL, WHILE THE FINISHED FLOOR LEVEL (FFL) IS DETERMINED BASED ON FLOOR FINISHES.

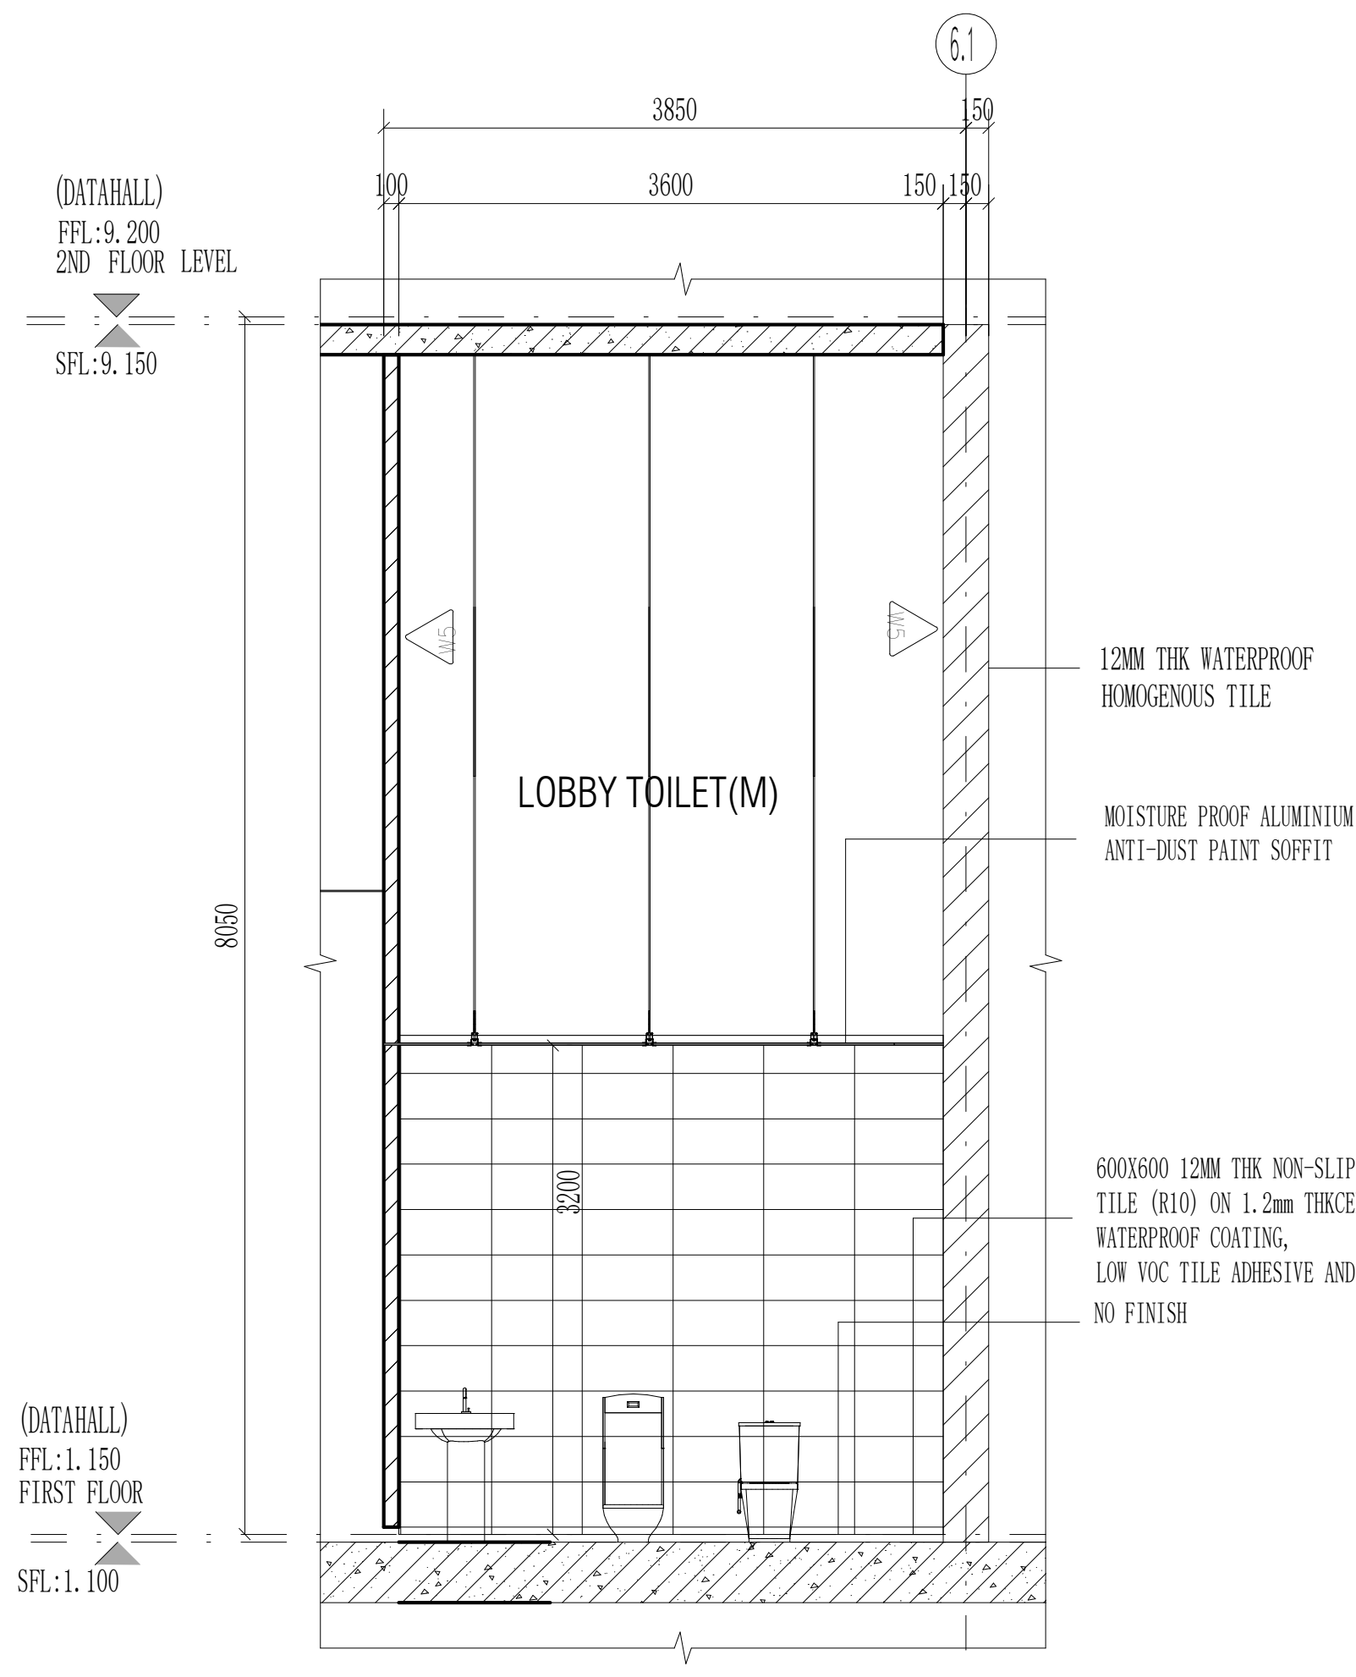
6.1
3850
150
100
3600
150
(DATAHALL)
FFL:9.200
2ND FLOOR LEVEL
SFL:9.150
W5
LOBBY TOILET(M)
12MM THK WATERPROOF HOMOGENOUS TILE
MOISTURE PROOF ALUMINIUM BUCKLE PLATE CEILING + ANTI-DUST PAINT SOFFIT
8050
3200
600X600 12MM THK NON-SLIP HOMOGENOUS TILE (R10) ON 1.2mm THKCEMENTITIOUS WATERPROOF COATING, LOW VOC TILE ADHESIVE AND GROUT
NO FINISH
(DATAHALL)
FFL:1.150
FIRST FLOOR
SFL:1.100

LOBBY TOILET SECTION D-D

Scale 1:50

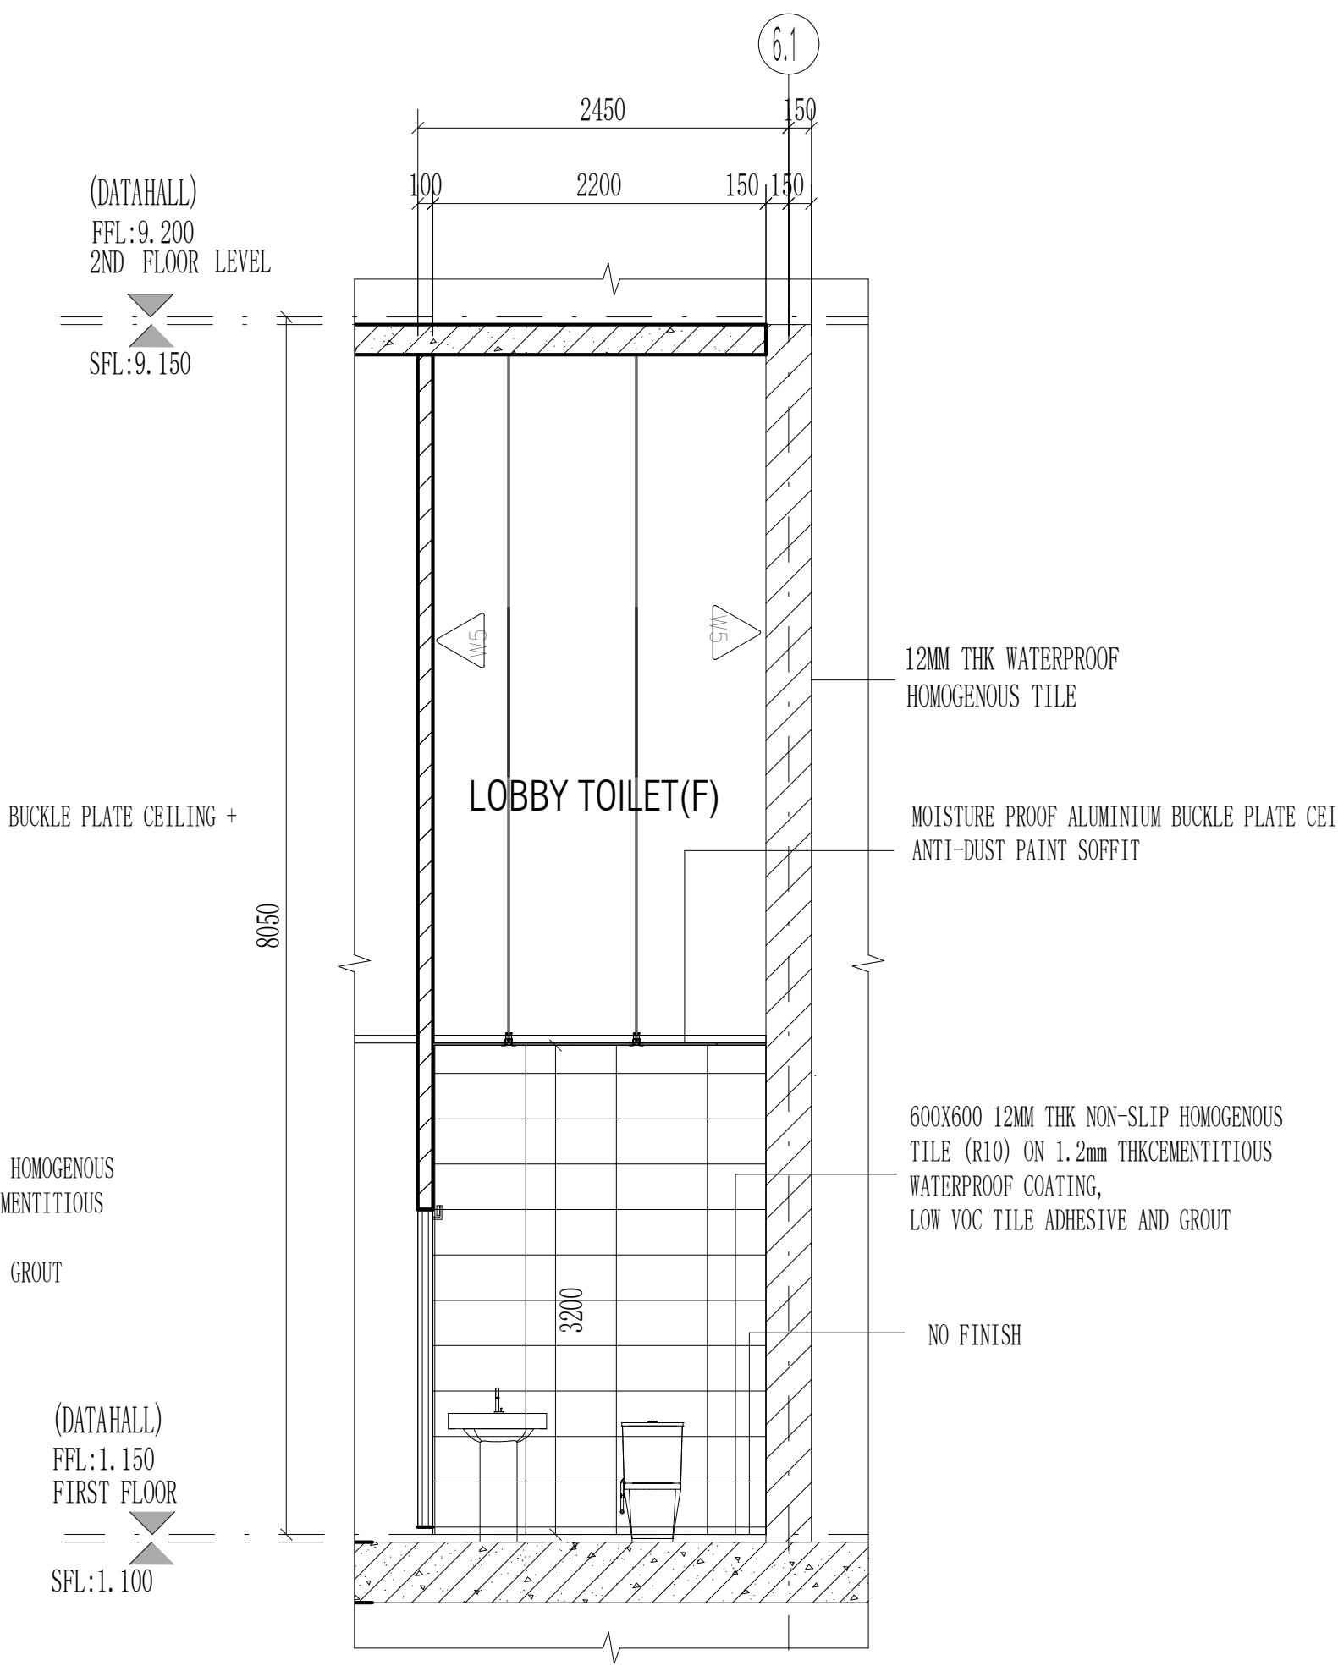
6.1
2450
100
2200
150
(DATAHALL)
FFL:9.200
2ND FLOOR LEVEL
SFL:9.150
LOBBY TOILET(F)
12MM THK WATERPROOF HOMOGENOUS TILE
MOISTURE PROOF ALUMINIUM BUCKLE PLATE CEILING + ANTI-DUST PAINT SOFFIT
8050
3200
600X600 12MM THK NON-SLIP HOMOGENOUS TILE (R10) ON 1.2mm THKCEMENTITIOUS WATERPROOF COATING, LOW VOC TILE ADHESIVE AND GROUT
NO FINISH
(DATAHALL)
FFL:1.150
FIRST FLOOR
SFL:1.100

LOBBY TOILET SECTION E-E

Scale 1:50

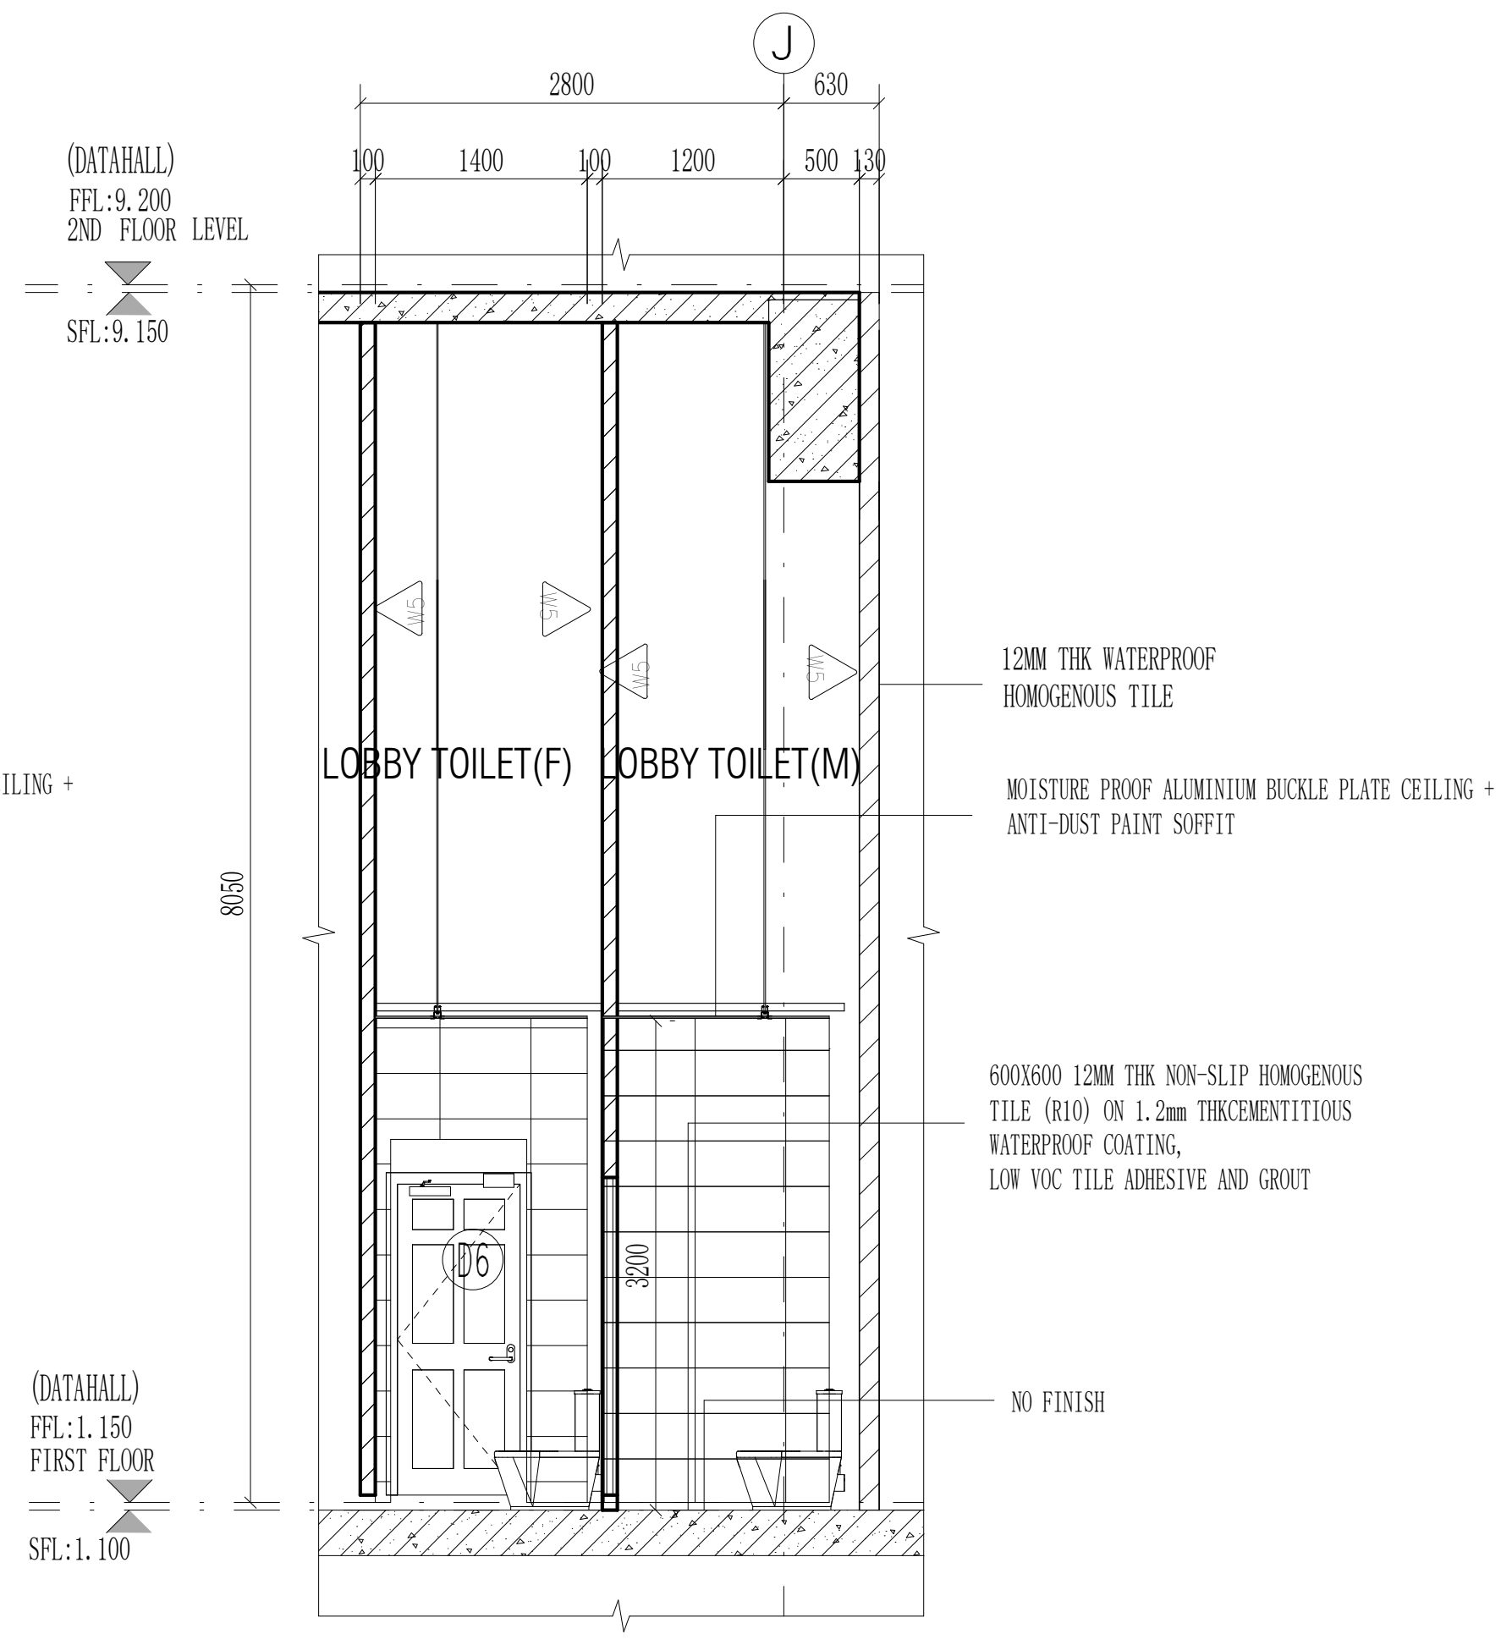
J
2800
630
100
1400
1200
500
130
(DATAHALL)
FFL:9.200
2ND FLOOR LEVEL
SFL:9.150
LOBBY TOILET(F)
LOBBY TOILET(M)
12MM THK WATERPROOF HOMOGENOUS TILE
MOISTURE PROOF ALUMINIUM BUCKLE PLATE CEILING + ANTI-DUST PAINT SOFFIT
8050
3200
D6
600X600 12MM THK NON-SLIP HOMOGENOUS TILE (R10) ON 1.2mm THKCEMENTITIOUS WATERPROOF COATING, LOW VOC TILE ADHESIVE AND GROUT
NO FINISH
(DATAHALL)
FFL:1.150
FIRST FLOOR
SFL:1.100

LOBBY TOILET SECTION F-F

Scale 1:50

CLIENT :

GULF EDGE DC 01

87 Wireless Road, M Thai Tower 11th. Floor, All Seasons Place, Lumpini,
Pathumwan, Bangkok 10330, Thailand

CONTRACTOR :

华西发展(泰国)有限公司
บริษัท หัวซือ ดีเวลลอปเม้นต์ (ประเทศไทย) จำกัด
HUASHI DEVELOPMENT CO.,LTD
No. 202, Room No. 1403, 14/F, Le Concorde Building,
Ratchadapisek Road, Huaykhwang Sub-District,
Huaykhwang District, Bangkok Metropolitan 10310.

CONSULTANT :

ARbay
บริษัท เอ อาร์ เบย์ จำกัด
ARbay Company Limited
31 st Floor Bangkok Insurance Building
25 South Sathorn road Thungmahamek
Sathorn Bangkok 10120 THAILAND
T +66 (0) 2286 8199
F +66 (0) 2286 2863
info@arbay.co.th

CONSULTANT :

Qbic Engineers & Architects Co.,Ltd.
8 Soi KALONG 4 SANAMBINNAM ROAD,
THASAI SUB-DISTRICT, MUANG NONTHABURI DISTRICT
, NONTHABURI.
Tel 662-950-4374
Fax 662-580-3231
E-Mail : qbic@qbic.co.th, www.qbic.co.th
QBIC ENGINEERS AND ARCHITECTS CO.,LTD.

CONSULTANT :

MITR
MITR TECHNICAL CONSULTANT CO.,LTD.
1168/8 12th FLOOR, LUMPINI TOWER BUILDING,
RAMA IV RD., THUNGMAHAMEK, SATHORN, BANGKOK 10120, THAILAND
TEL : 0-2679-9079-84
FAX : 0-2679-9085 E-mail: mitr_dd@mitr.com

Architect :	SIGNATURE
ประกิต พนานุรัตน์ วสถ. 580 ที่อยู่ 251/1 ถ.จารุเมือง แขวงรองเมือง เขตปทุมวัน กรุงเทพมหานคร โทรศัพท์ 02-286-8199	
Structural Engineer :	SIGNATURE
วิศวกรผู้ออกแบบโครงสร้าง	
ณัฐสม สงวนวงษ์ วย 1423 ที่อยู่ 2/1 ซ.รามคำแหง 150 ถ.รามคำแหง แขวง สะพานสูง เขต สะพานสูง กทม. 10240	ณัฐสม สงวนวงษ์
Structural Inspector :	SIGNATURE
วิศวกรผู้ตรวจสอบโครงสร้าง	
โกมล จุฑาภัทร วย 964 ที่อยู่ 24/18 ซ.นวมินทร์ 129 ถ. นวมินทร์ แขวง นวลจันทร์ เขต บึงกุ่ม กทม. 10230	
Electrical Engineer :	SIGNATURE
วิศวกรผู้ออกแบบระบบไฟฟ้ากำลัง	
นายสุภัทร บูรณวิทย์ วฟก.1265 ที่อยู่ 21 ซอยทานสัมฤทธิ์ 13 ตำบลท่าทราย อ.เมืองนนทบุรี จ.นนทบุรี 11000	สุภัทร บูรณวิทย์
Mechanical Engineer :	SIGNATURE
วิศวกรผู้ออกแบบระบบเครื่องกลและปรับอากาศ	
นายประสิทธิ์ เกี้ยวสุนทร วก.1221 ที่อยู่ 44/372 ซอยบางกระดี่ 35/1 แขวงแสมดำ เขตบางขุนเทียน กทม. 10150	ประสิทธิ์
Sanitary Engineer :	SIGNATURE
วิศวกรผู้ออกแบบระบบสุขาภิบาล และดับเพลิง	
นายทศวรรษ สนั่นฤทธิ์ วส. 215 ที่อยู่ บ้านเลขที่ 99/107 หมู่ที่ 3 ต.ศีรษะจรเข้น้อย อ.บางเสาธง จ.สมุทรปราการ 10540	ทศวรรษ

ISSUE/REVISION

REV.	DESCRIPTION	DATE
A	90% DEVELOPED	09/05/2026

PROJECT NAME :

GEDC 01

LOCATION:
Nikhom Phattana district, Rayong ,industrial estate,CPGC

BUILDING :
MAIN BUILDING

90% DEVELOPED

TITLE :

ROOM DETAIL-1F-LOBBY、LOBBY TOILET、VISITOR MEETING ROOM

JOB NO.	SCALE 1 : 50
DRAWN LYT	REF.
CHECKED LJC	DWG. NO. MPK01A-90-A-RD-117
APPROVED LXD	
DATE 2026.05.09	

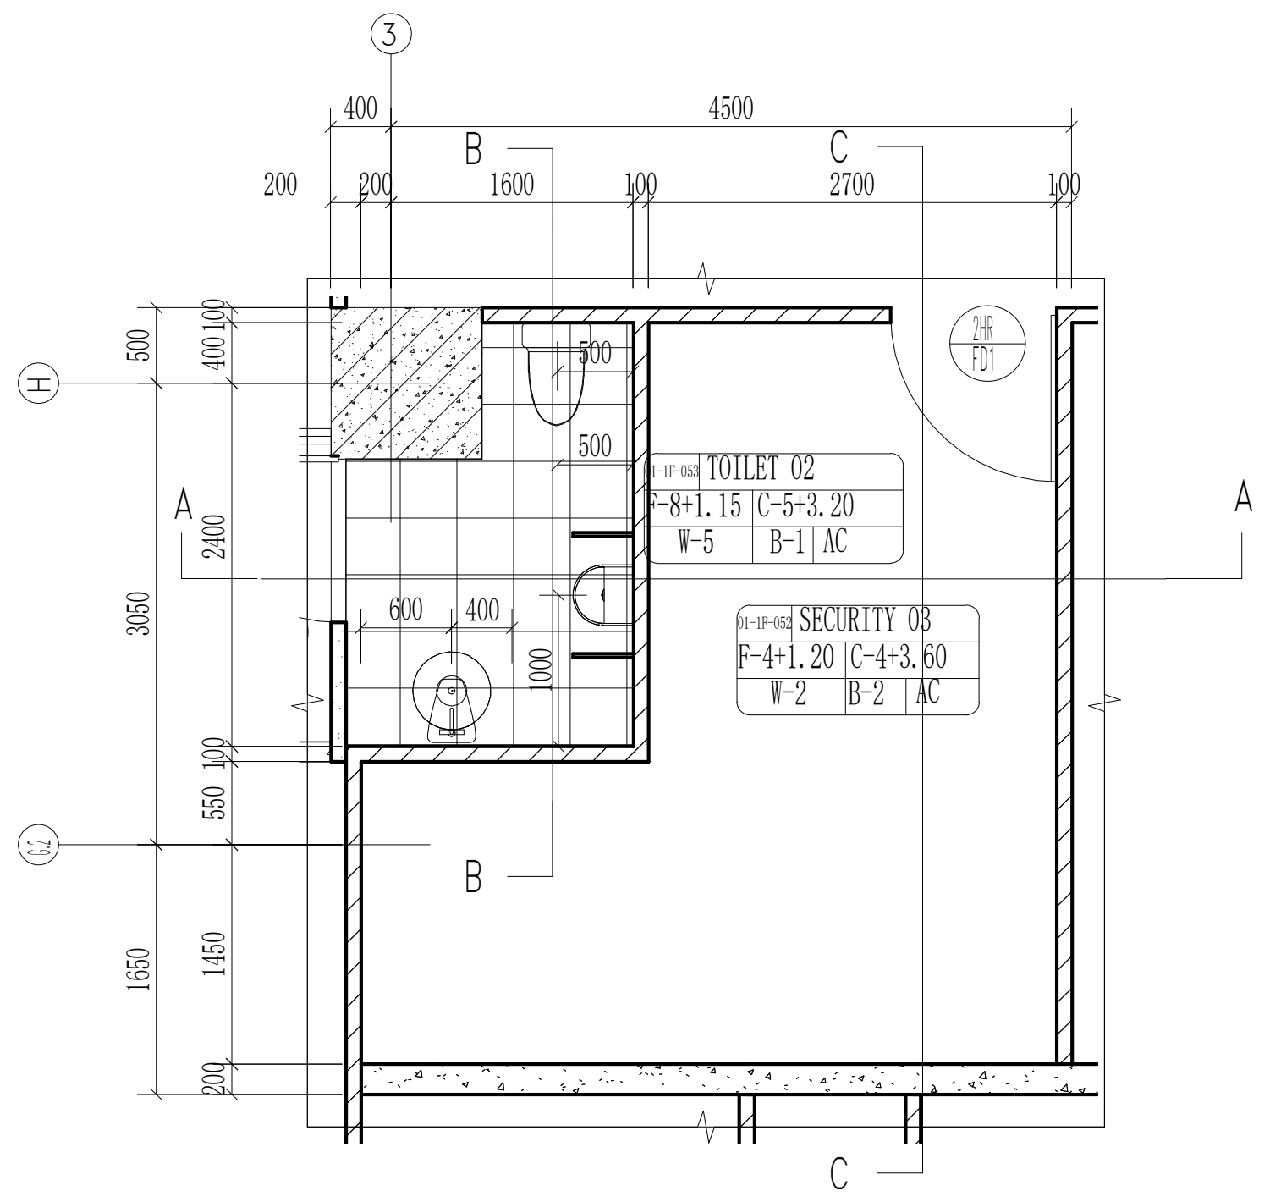
3
400
4500
B
C
200
200
1600
100
2700
100
H
500
400
100
01-1F-053 TOILET 02
F-8+1.15
C-5+3.20
W-5
B-1
AC
A
A
2400
3050
600
400
1000
01-1F-052 SECURITY 03
F-4+1.20
C-4+3.60
W-2
B-2
AC
2HR
FD1
500
500
100
550
G.2
B
1650
1450
200
C

TOILET 02、 SECURITY 03 FLOOR PLAN

Scale 1:50

THE "SFL" MARKED IN THE DRAWING REFERS TO THE STRUCTURAL FLOOR LEVEL, WHILE THE FINISHED FLOOR LEVEL (FFL) IS DETERMINED BASED ON FLOOR FINISHES.

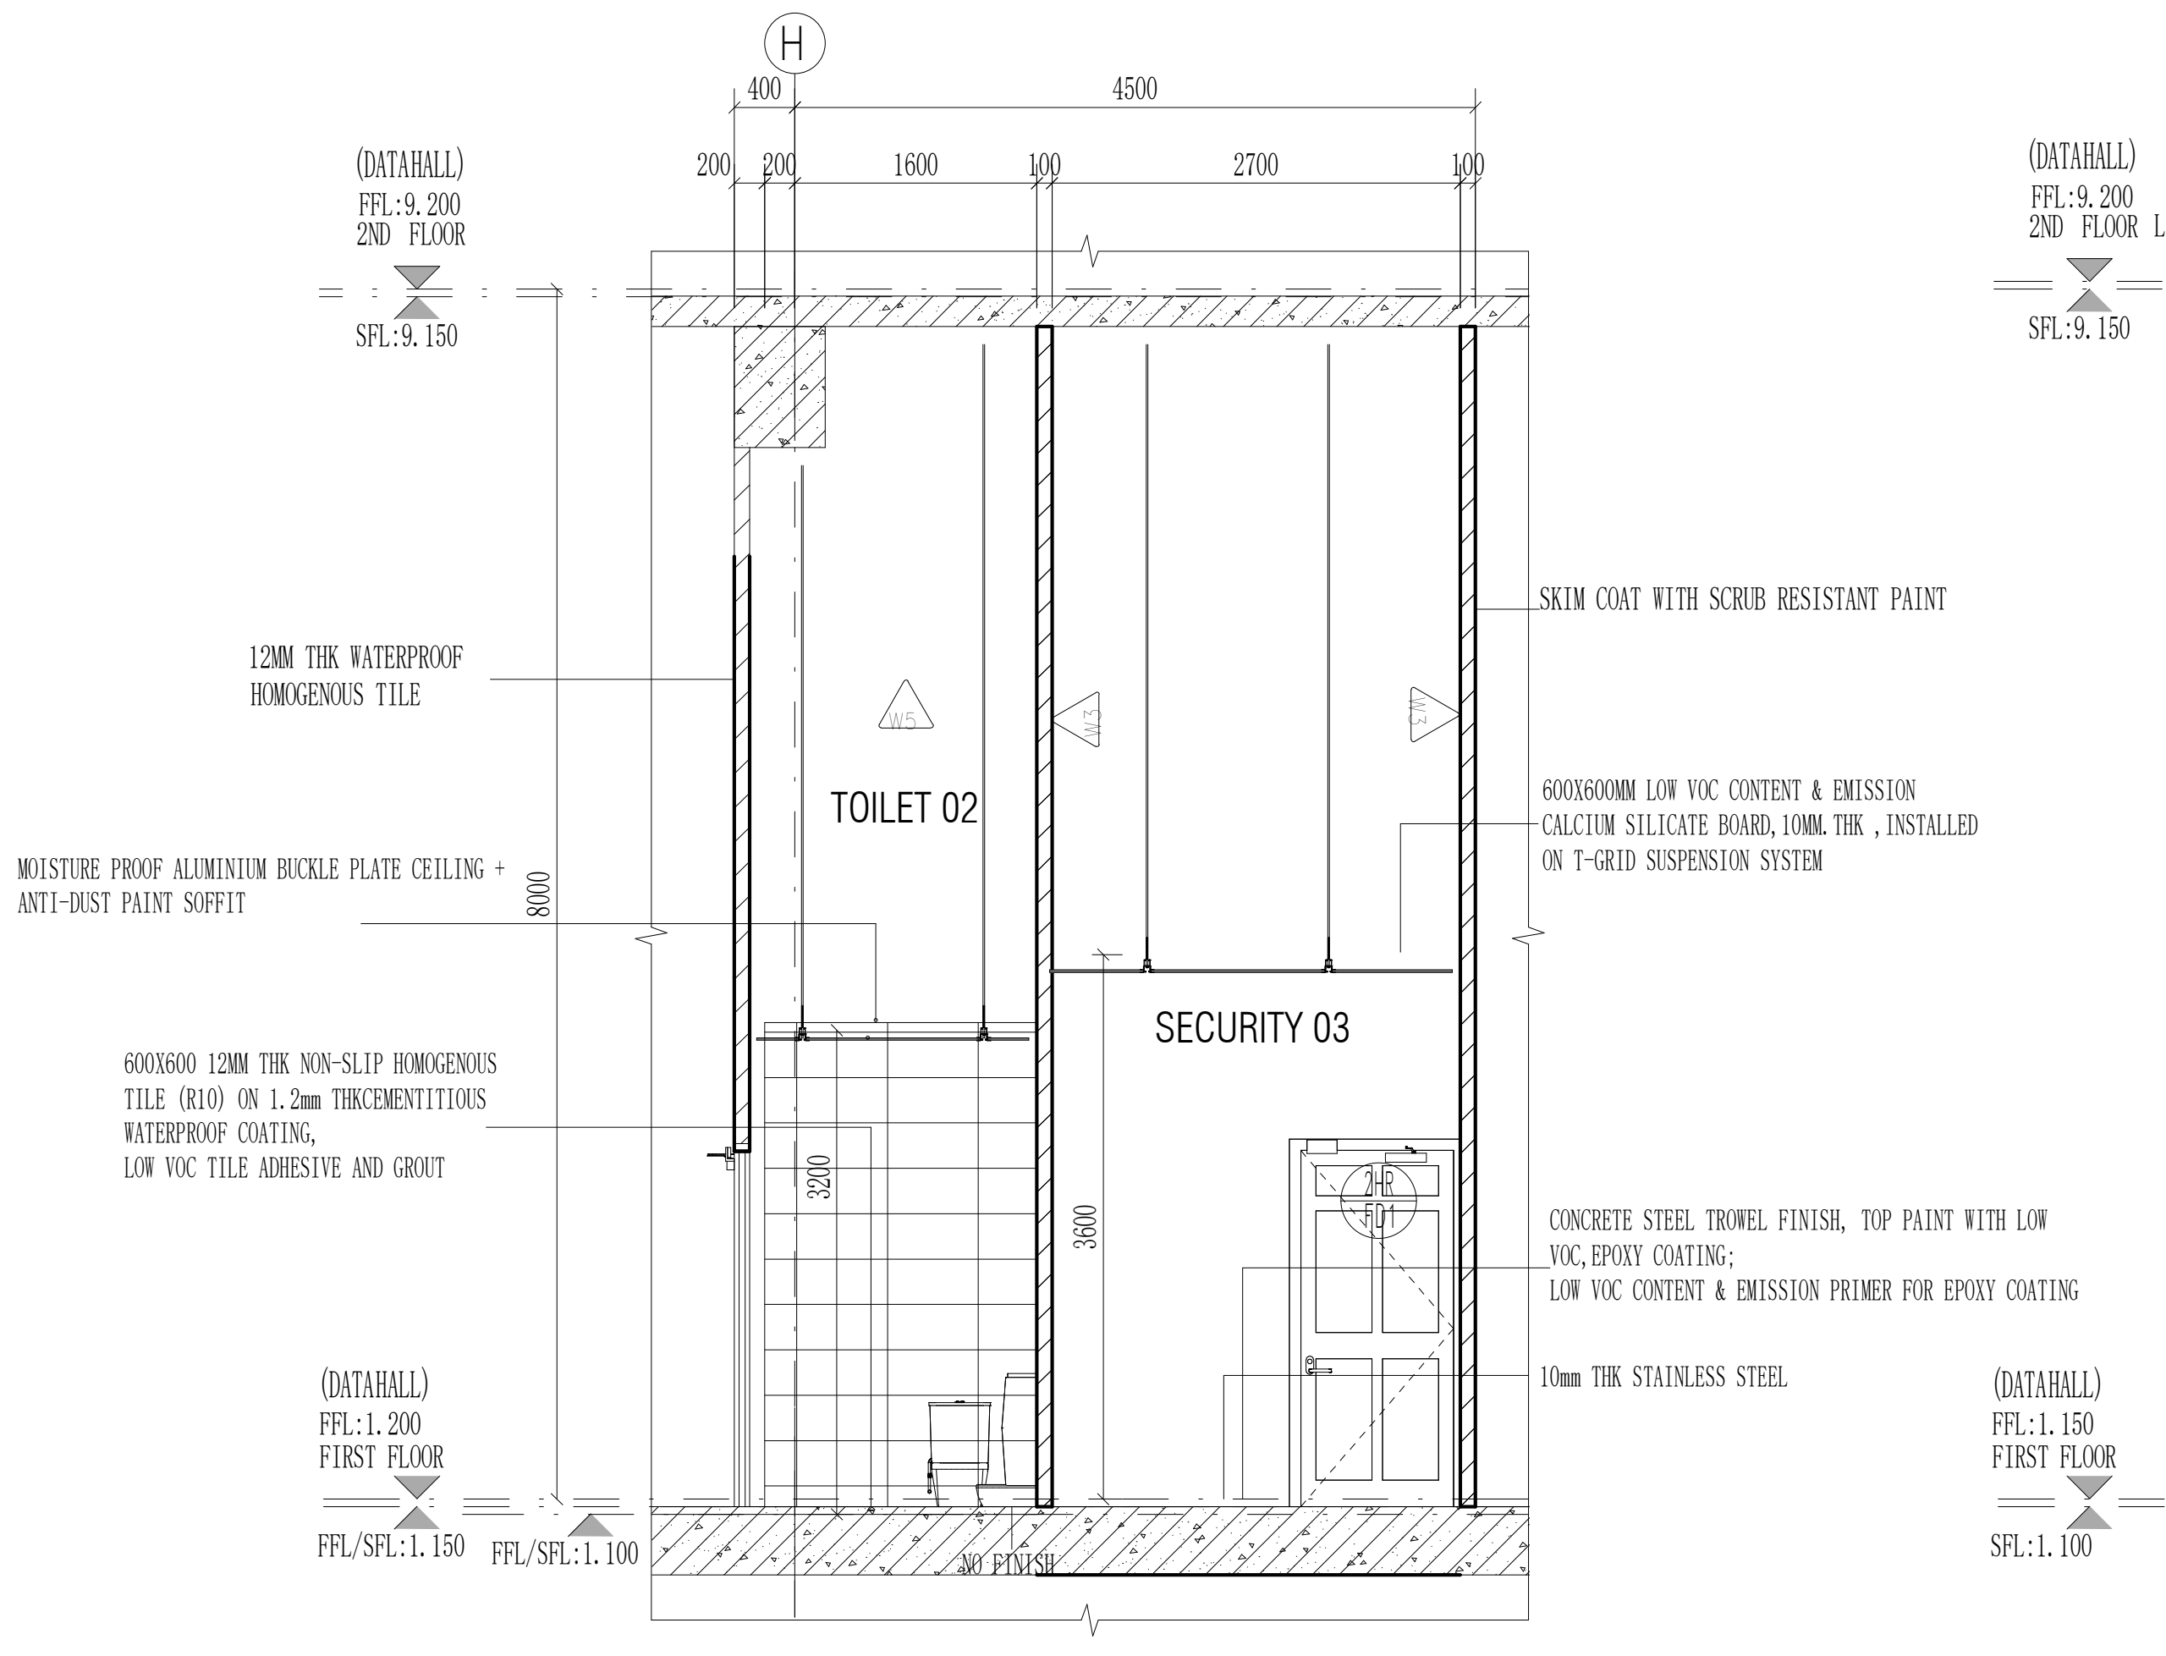
H
400
4500
200
200
1600
100
2700
100
(DATAHALL)
FFL:9.200
2ND FLOOR
SFL:9.150
12MM THK WATERPROOF
HOMOGENOUS TILE
W5
W3
W2
TOILET 02
SKIM COAT WITH SCRUB RESISTANT PAINT
600X600MM LOW VOC CONTENT & EMISSION
CALCIUM SILICATE BOARD,10MM.THK , INSTALLED
ON T-GRID SUSPENSION SYSTEM
MOISTURE PROOF ALUMINIUM BUCKLE PLATE CEILING +
ANTI-DUST PAINT SOFFIT
8000
SECURITY 03
600X600 12MM THK NON-SLIP HOMOGENOUS
TILE (R10) ON 1.2mm THKCEMENTITIOUS
WATERPROOF COATING,
LOW VOC TILE ADHESIVE AND GROUT
3200
3600
2HR
FD1
CONCRETE STEEL TROWEL FINISH, TOP PAINT WITH LOW
VOC,EPOXY COATING;
LOW VOC CONTENT & EMISSION PRIMER FOR EPOXY COATING
10mm THK STAINLESS STEEL
(DATAHALL)
FFL:1.200
FIRST FLOOR
FFL/SFL:1.150
FFL/SFL:1.100
NO FINISH

TOILET 02、 SECURITY 03 SECTION A-A

Scale 1:50

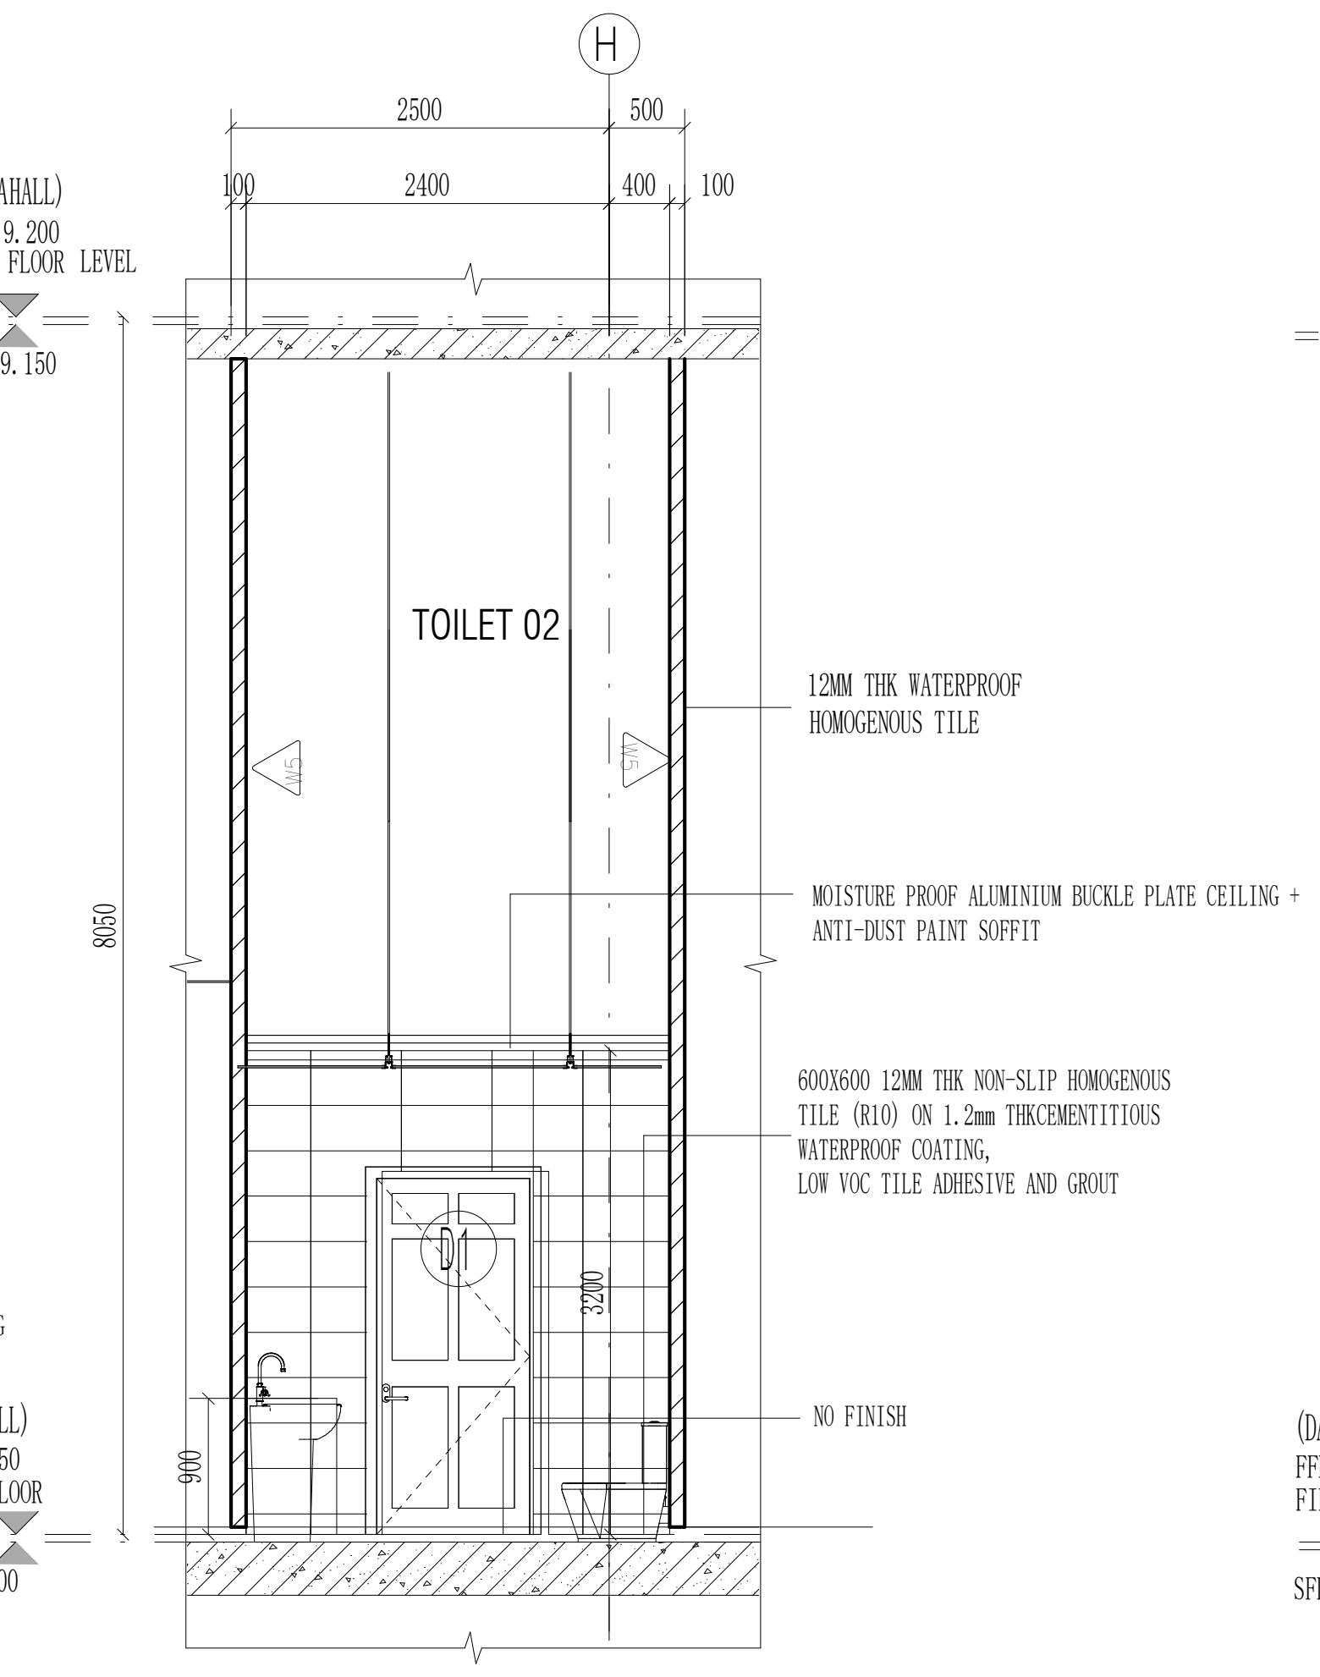
H
2500
500
(DATAHALL)
FFL:9.200
2ND FLOOR LEVEL
100
2400
400
100
SFL:9.150
TOILET 02
12MM THK WATERPROOF
HOMOGENOUS TILE
W5
W5
8050
MOISTURE PROOF ALUMINIUM BUCKLE PLATE CEILING +
ANTI-DUST PAINT SOFFIT
600X600 12MM THK NON-SLIP HOMOGENOUS
TILE (R10) ON 1.2mm THKCEMENTITIOUS
WATERPROOF COATING,
LOW VOC TILE ADHESIVE AND GROUT
D1
3200
NO FINISH
(DATAHALL)
FFL:1.150
FIRST FLOOR
900
SFL:1.100

TOILET 02 SECTION B-B

Scale 1:50

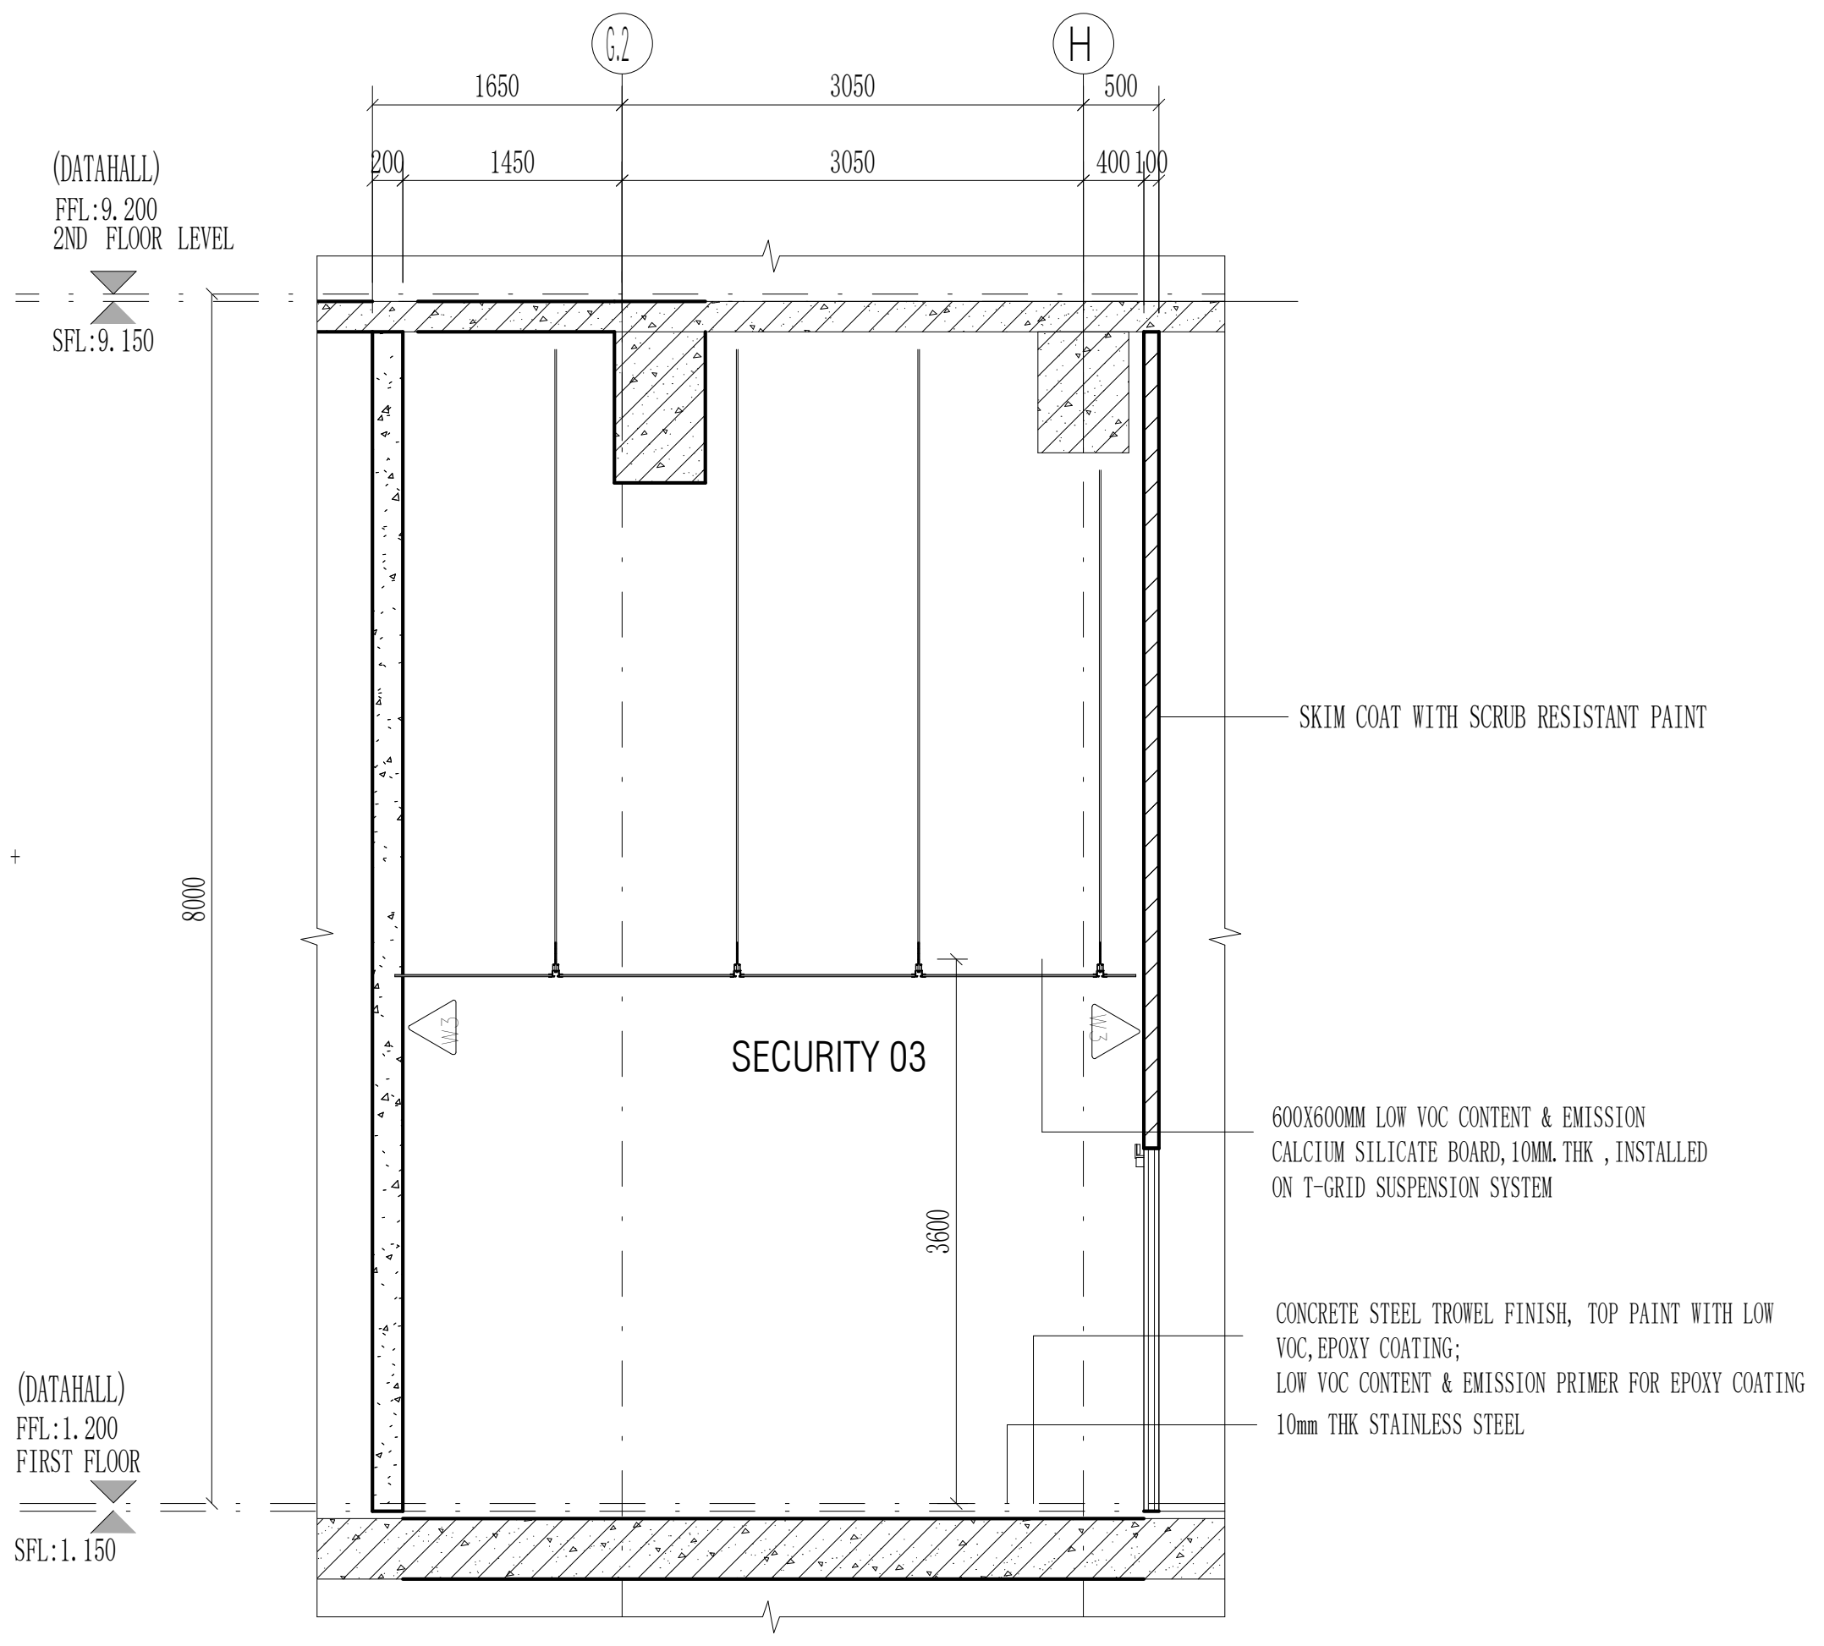
G.2
H
1650
3050
500
(DATAHALL)
FFL:9.200
2ND FLOOR LEVEL
200
1450
3050
400
100
SFL:9.150
SKIM COAT WITH SCRUB RESISTANT PAINT
8000
W3
W3
SECURITY 03
600X600MM LOW VOC CONTENT & EMISSION
CALCIUM SILICATE BOARD,10MM.THK , INSTALLED
ON T-GRID SUSPENSION SYSTEM
3600
CONCRETE STEEL TROWEL FINISH, TOP PAINT WITH LOW
VOC,EPOXY COATING;
LOW VOC CONTENT & EMISSION PRIMER FOR EPOXY COATING
10mm THK STAINLESS STEEL
(DATAHALL)
FFL:1.200
FIRST FLOOR
SFL:1.150

SECURITY 03 SECTION C-C

Scale 1:50

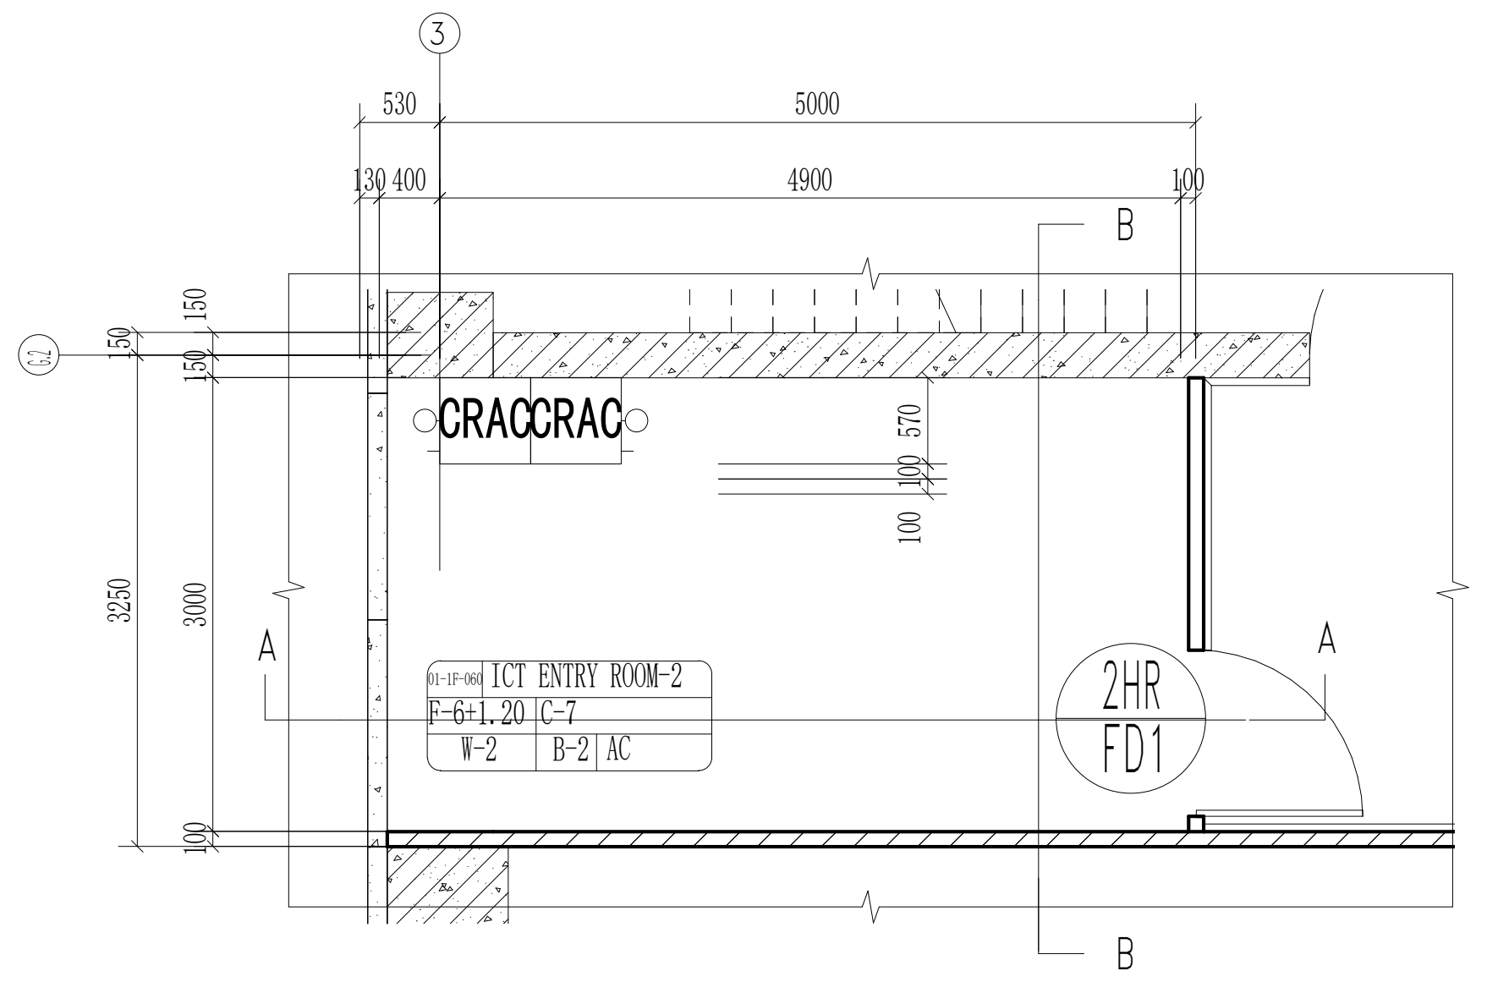
3
530
5000
130
400
4900
100
B
G.2
150
150
150
CRAC
CRAC
570
100
100
3250
3000
A
A
01-1F-060 ICT ENTRY ROOM-2
F-6+1.20
C-7
W-2
B-2
AC
2HR
FD1
100
B

ICT ENTRY ROOM FLOOR PLAN

Scale 1:50

THE "SFL" MARKED IN THE DRAWING REFERS TO THE STRUCTURAL FLOOR LEVEL, WHILE THE FINISHED FLOOR LEVEL (FFL) IS DETERMINED BASED ON FLOOR FINISHES.

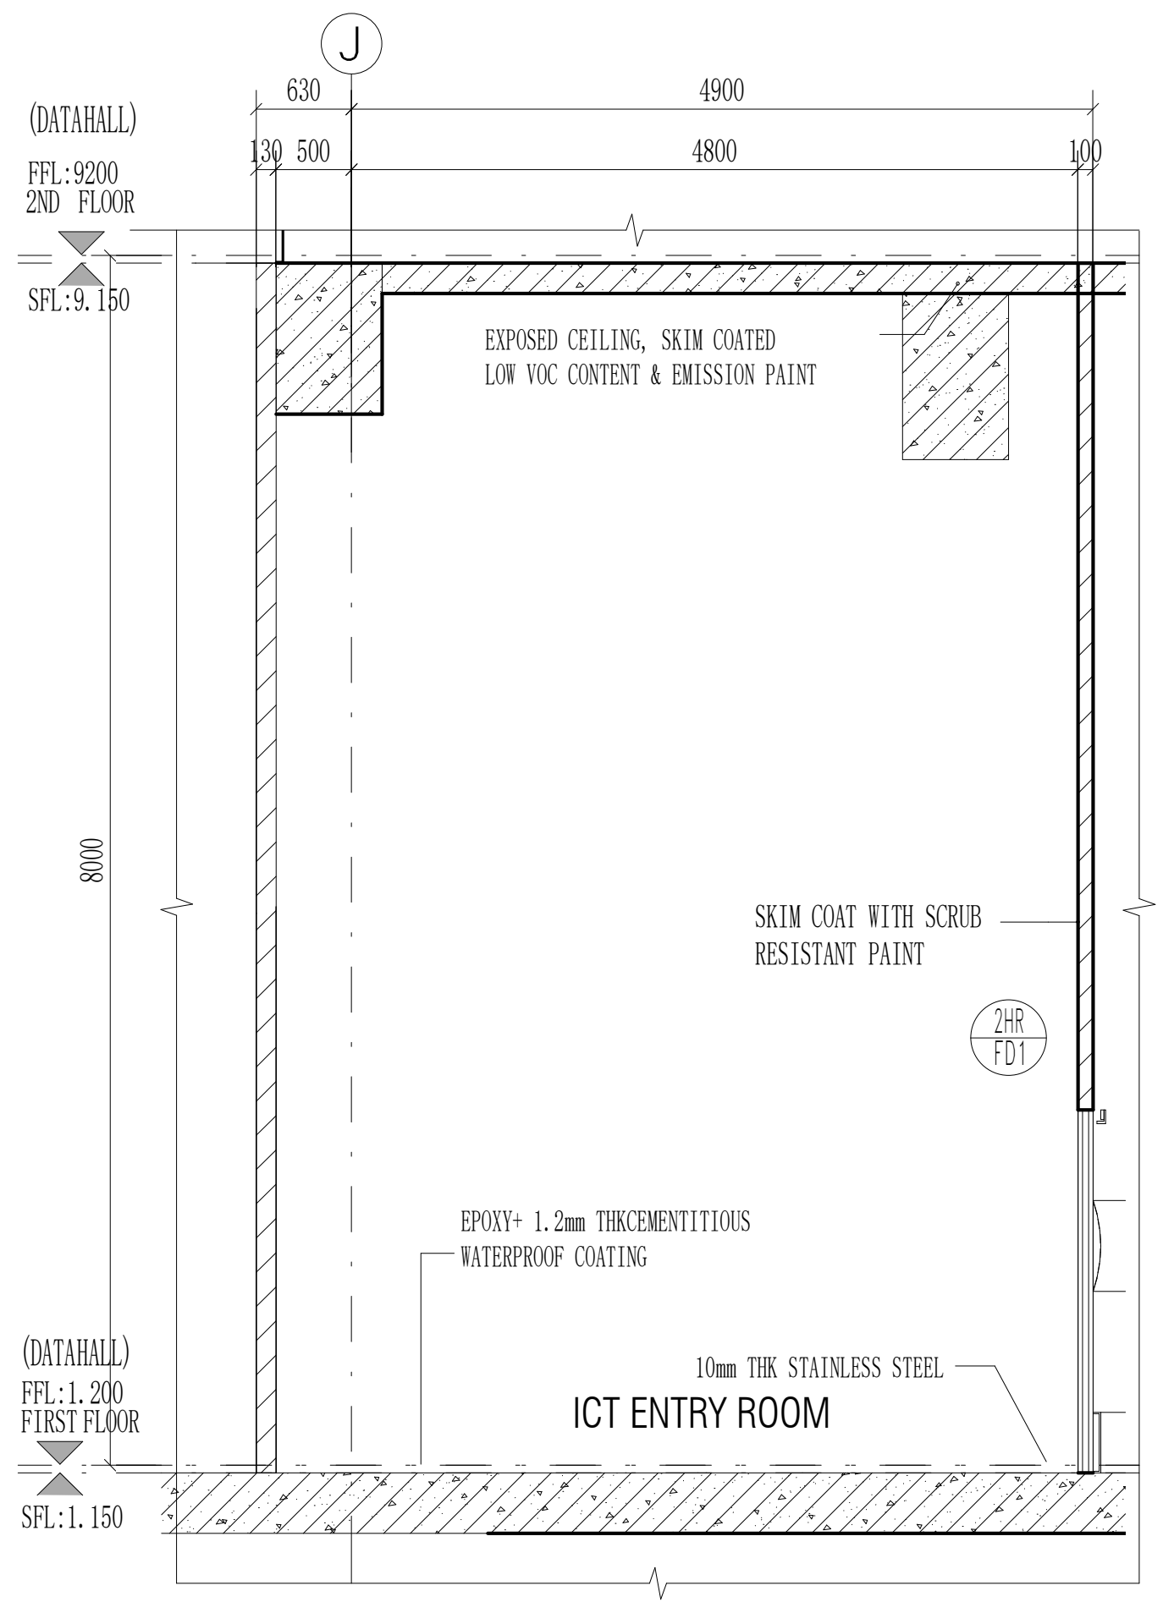
J
630
4900
(DATAHALL)
130
500
4800
100
FFL:9200
2ND FLOOR
SFL:9.150
EXPOSED CEILING, SKIM COATED
LOW VOC CONTENT & EMISSION PAINT
8000
SKIM COAT WITH SCRUB
RESISTANT PAINT
2HR
FD1
EPOXY+ 1.2mm THKCEMENTITIOUS
WATERPROOF COATING
10mm THK STAINLESS STEEL
(DATAHALL)
FFL:1.200
FIRST FLOOR
ICT ENTRY ROOM
SFL:1.150

ICT ENTRY ROOM SECTION A-A

Scale 1:50

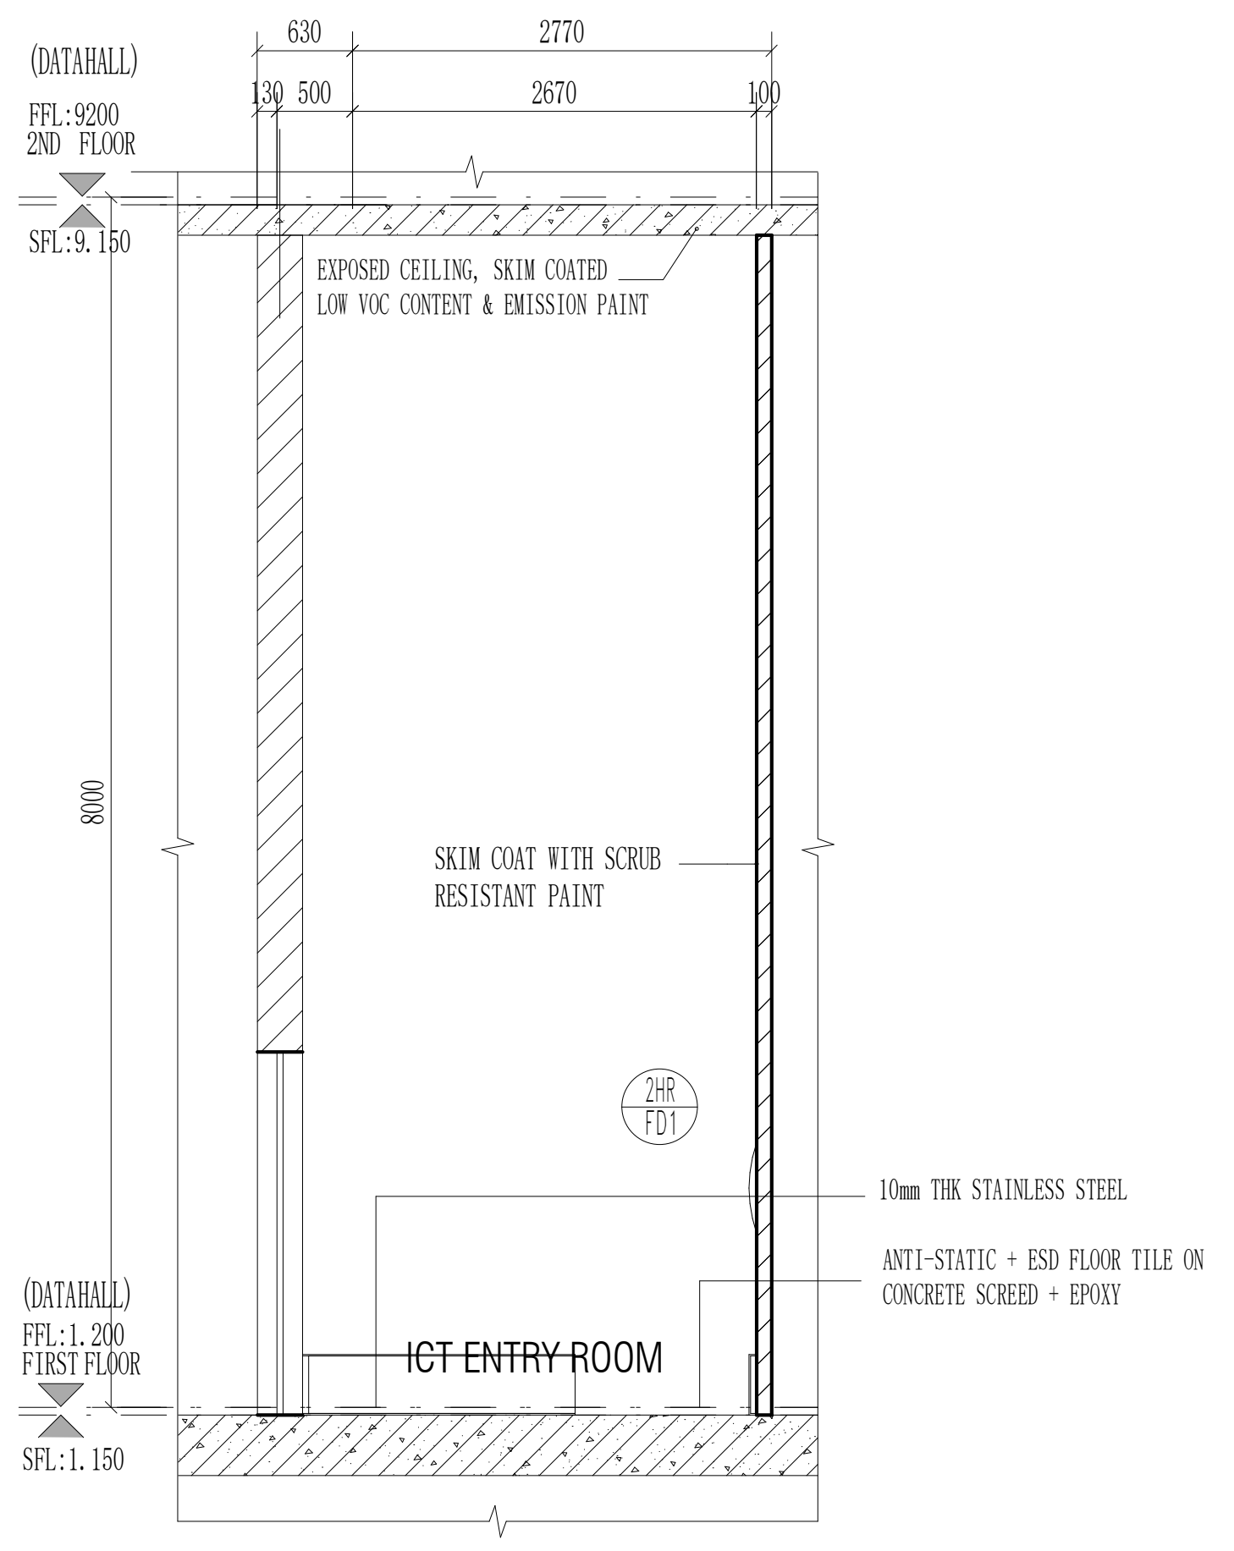
630
2770
(DATAHALL)
130
500
2670
100
FFL:9200
2ND FLOOR
SFL:9.150
EXPOSED CEILING, SKIM COATED
LOW VOC CONTENT & EMISSION PAINT
8000
SKIM COAT WITH SCRUB
RESISTANT PAINT
2HR
FD1
10mm THK STAINLESS STEEL
ANTI-STATIC + ESD FLOOR TILE ON
CONCRETE SCREED + EPOXY
(DATAHALL)
FFL:1.200
FIRST FLOOR
ICT ENTRY ROOM
SFL:1.150

ICT ENTRY ROOM SECTION B-B

Scale 1:50

CLIENT :

GULF EDGE DC 01

87 Wireless Road, M Thai Tower 11th. Floor, All Seasons Place, Lumpini,
Pathumwan, Bangkok 10330, Thailand

CONTRACTOR :

华西发展(泰国)有限公司
บริษัท หัวซือ ดีเวลลอปเม้นต์ (ประเทศไทย) จำกัด
HUASHI DEVELOPMENT CO.,LTD
No. 202, Room No. 1403, 14/F, Le Concorde Building,
Ratchadapisek Road, Huaykhwang Sub-District,
Huaykhwang District, Bangkok Metropolitan 10310.

CONSULTANT :

ARbay
บริษัท เอ อาร์ เบย์ จำกัด
ARbay Company Limited
31 st Floor Bangkok Insurance Building
25 South Sathorn road Thungmahamek
Sathorn Bangkok 10120 THAILAND
T +66 (0) 2286 8199
F +66 (0) 2286 2863
info@arbay.co.th

CONSULTANT :

Qbic Engineers & Architects Co.,Ltd.
8 Soi KALONG 4 SANAMBINNAM ROAD,
THASAI SUB-DISTRICT, MUANG NONTHABURI DISTRICT
, NONTHABURI.
Tel 662-950-4374
Fax 662-580-3231
E-Mail : qbic@qbic.co.th, www.qbic.co.th
QBIC ENGINEERS AND ARCHITECTS CO.,LTD.

CONSULTANT :

MITR
MITR TECHNICAL CONSULTANT CO.,LTD.
1168/8 12th FLOOR, LUMPINI TOWER BUILDING,
RAMA IV RD., THUNGMAHAMEK, SATHORN, BANGKOK 10120, THAILAND
TEL : 0-2679-9079-84
FAX : 0-2679-9085 E-mail: mitr_dd@mitr.com

Architect : SIGNATURE
ประกิต พนานุรัตน์ วสถ. 580
ที่อยู่
251/1 ถ.จารุเมือง แขวงรองเมือง เขตปทุมวัน
กรุงเทพมหานคร โทรศัพท์ 02-286-8199

Structural Engineer : SIGNATURE
วิศวกรผู้ออกแบบโครงสร้าง
ณัฐสม สงวนวงษ์ วย 1423
ที่อยู่
2/1 ซ.รามคำแหง 150 ถ.รามคำแหง
แขวง สะพานสูง เขต สะพานสูง กทม. 10240

Structural Inspector : SIGNATURE
วิศวกรผู้ตรวจสอบโครงสร้าง
โกมล จุฑาภัทร วย 964
ที่อยู่
24/18 ซ.นวมินทร์ 129 ถ. นวมินทร์
แขวง นวลจันทร์ เขต บึงกุ่ม กทม. 10230

Electrical Engineer : SIGNATURE
วิศวกรผู้ออกแบบระบบไฟฟ้ากำลัง
นายสุภัทร บูรณวิทย์ วฟก.1265
ที่อยู่
21 ซอยทานสัมฤทธิ์ 13
ตำบลท่าทราย อ.เมืองนนทบุรี จ.นนทบุรี 11000

Mechanical Engineer : SIGNATURE
วิศวกรผู้ออกแบบระบบเครื่องกลและปรับอากาศ
นายประสิทธิ์ เกี้ยวสุนทร วก.1221
ที่อยู่
44/372 ซอยบางกระดี่ 35/1 แขวงแสมดำ
เขตบางขุนเทียน กทม. 10150
ประสิทธิ์

Sanitary Engineer : SIGNATURE
วิศวกรผู้ออกแบบระบบสุขาภิบาล และดับเพลิง
นายทศวรรษ สนั่นฤทธิ์ วส. 215
ที่อยู่
บ้านเลขที่ 99/107 หมู่ที่ 3 ต.ศีรษะจรเข้น้อย
อ.บางเสาธง จ.สมุทรปราการ 10540
ทศวรรษ

ISSUE/REVISION

REV.	DESCRIPTION	DATE
A	90% DEVELOPED	09/05/2026

PROJECT NAME :

GEDC 01

LOCATION:
Nikhom Phattana district, Rayong ,industrial estate,CPGC

BUILDING :
MAIN BUILDING

90% DEVELOPED

TITLE :

ROOM DETAIL-1F-TOILET 02、SECURITY 03、ICT

JOB NO.
SCALE 1 : 50
DRAWN LYT
REF.
CHECKED LJC
DWG. NO. MPK01A-90-A-RD-118
APPROVED LXD
DATE 2026.05.09

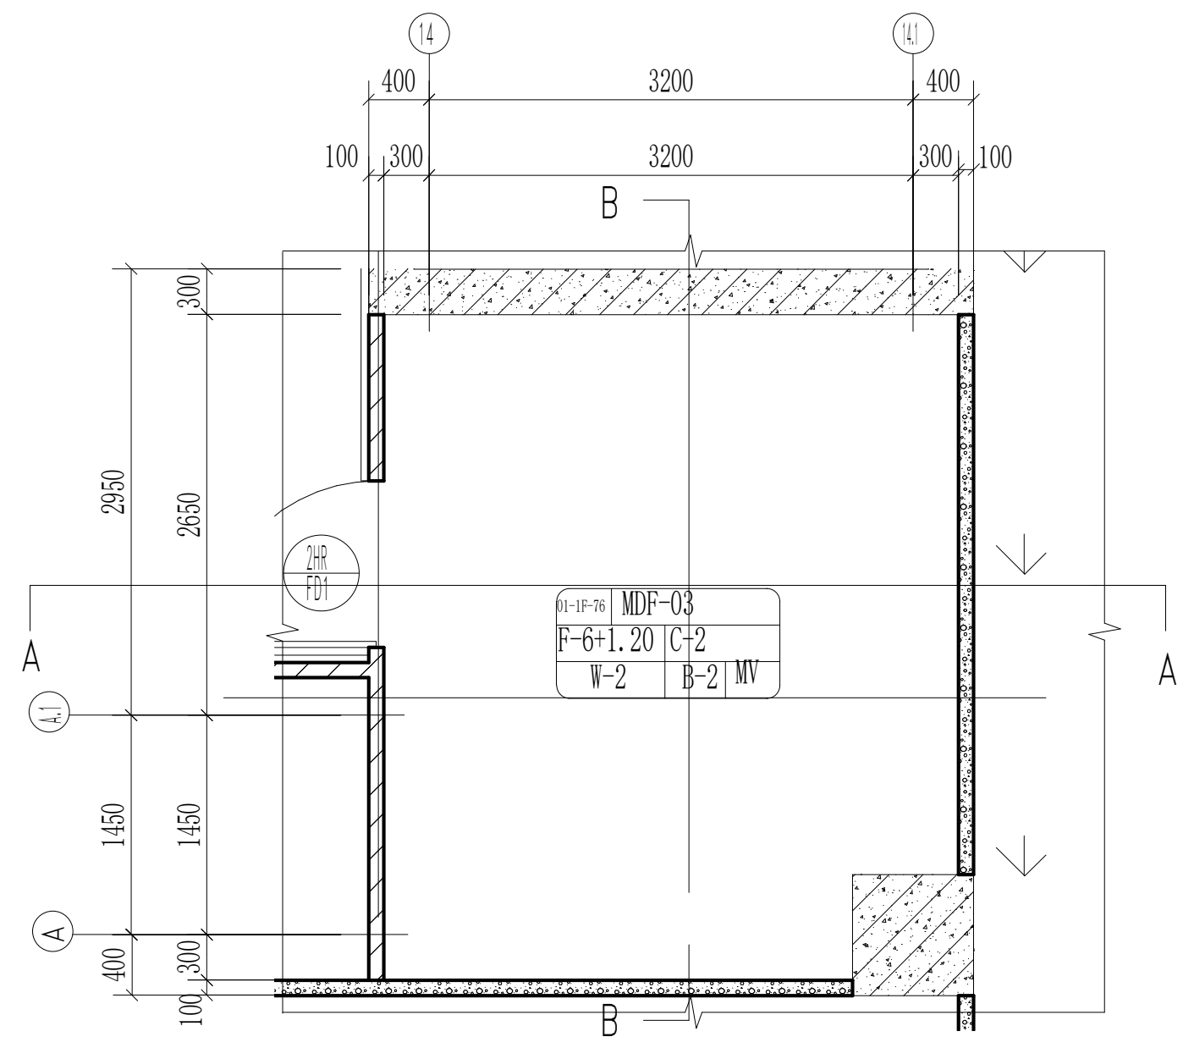
14
14.1
400
3200
100
300
B
A
A.1
2950
2650
1450
400
2HR
FD1
01-1F-76
MDF-03
F-6+1.20
C-2
W-2
B-2
MV

MDF 03 FLOOR PLAN Scale 1:50

THE "SFL" MARKED IN THE DRAWING REFERS TO THE STRUCTURAL FLOOR LEVEL, WHILE THE FINISHED FLOOR LEVEL (FFL) IS DETERMINED BASED ON FLOOR FINISHES.

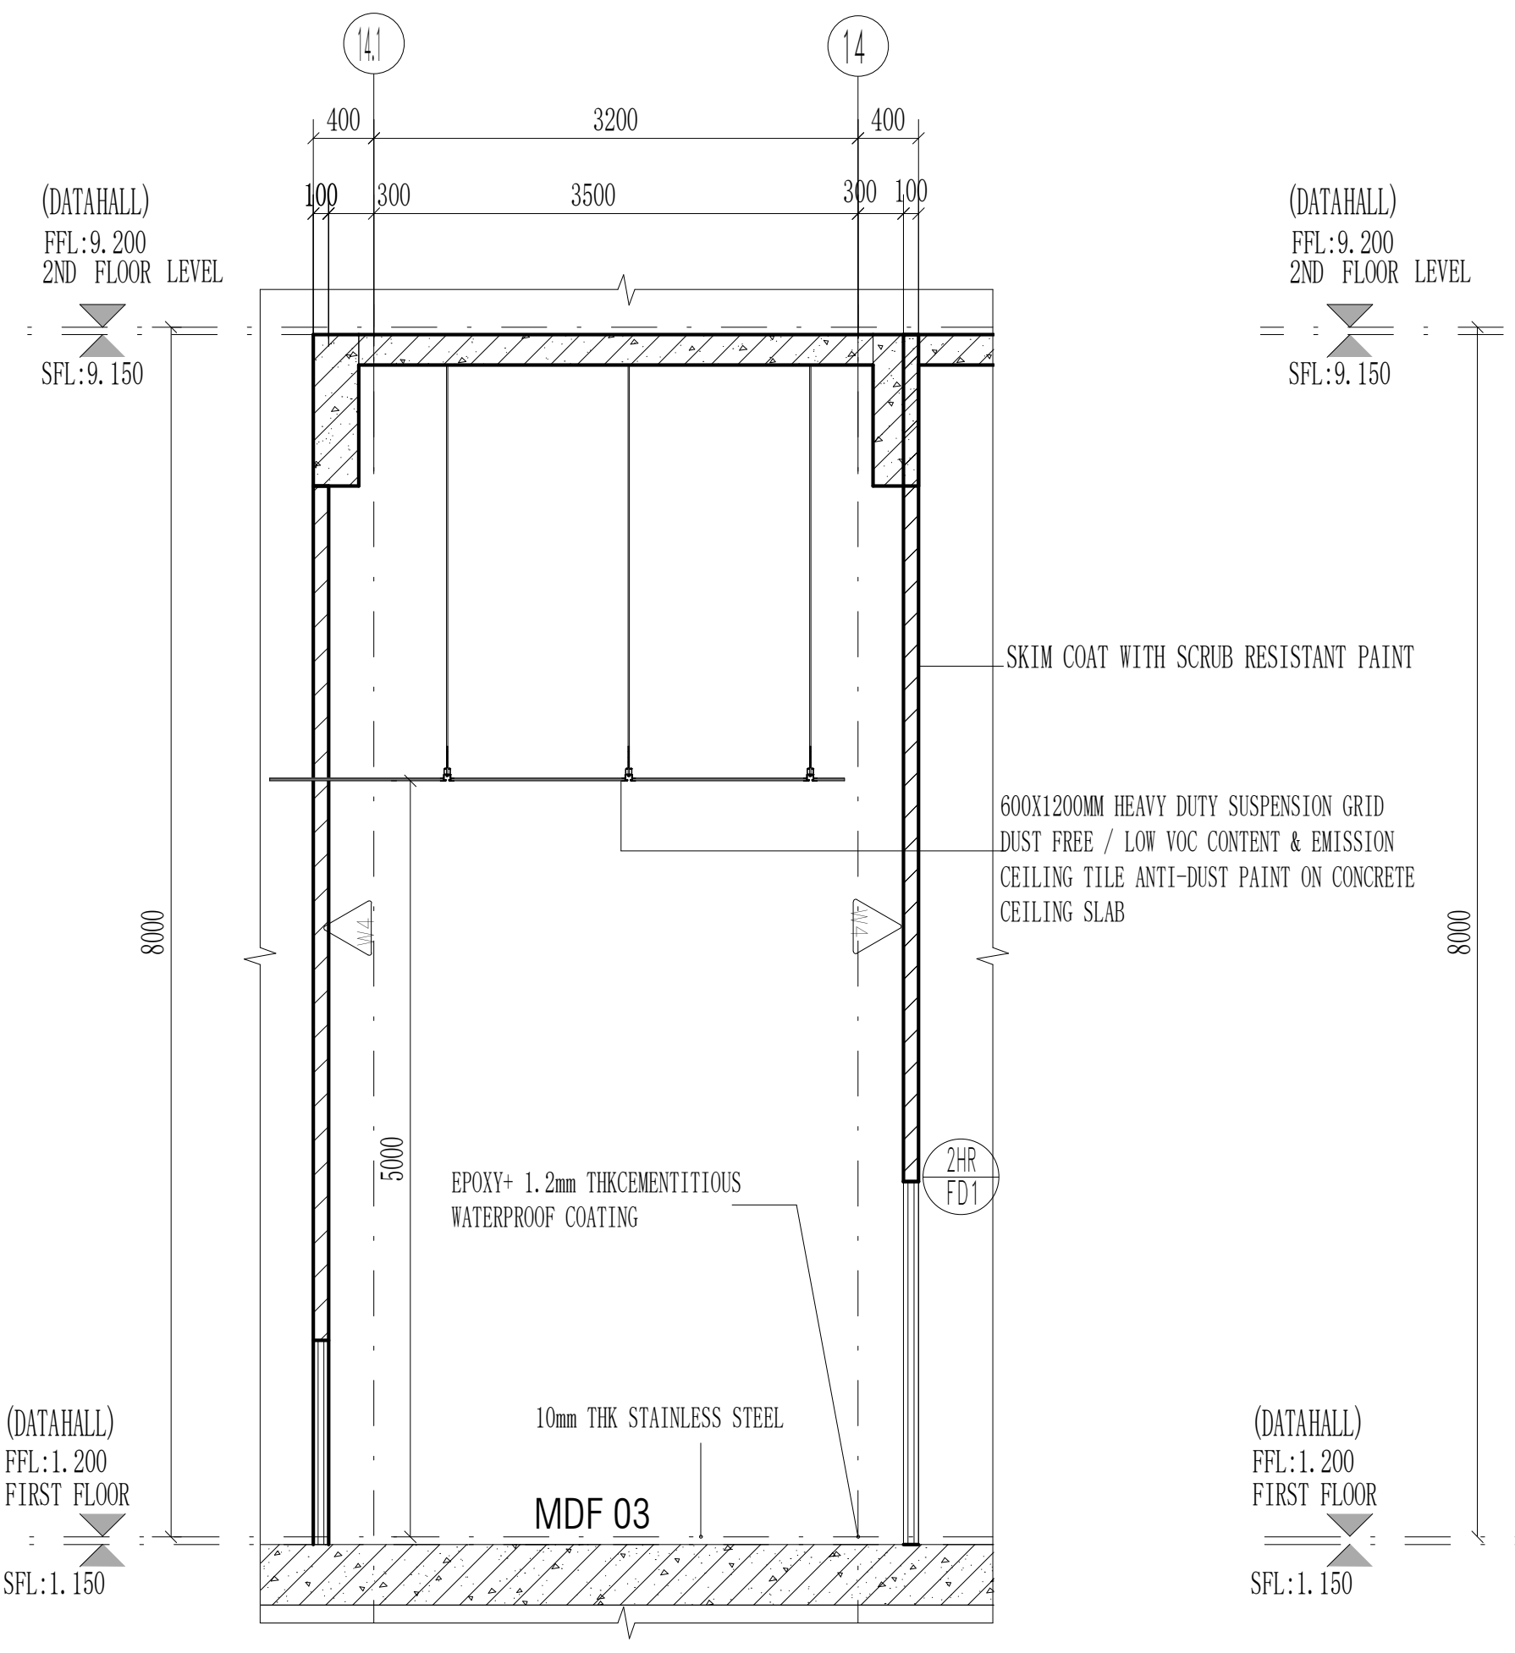
14.1
14
400
3200
100
300
3500
(DATAHALL)
FFL:9.200
2ND FLOOR LEVEL
SFL:9.150
8000
5000
SKIM COAT WITH SCRUB RESISTANT PAINT
600X1200MM HEAVY DUTY SUSPENSION GRID DUST FREE / LOW VOC CONTENT & EMISSION CEILING TILE ANTI-DUST PAINT ON CONCRETE CEILING SLAB
EPOXY+ 1.2mm THKCEMENTITIOUS WATERPROOF COATING
10mm THK STAINLESS STEEL
2HR
FD1
(DATAHALL)
FFL:1.200
FIRST FLOOR
SFL:1.150
MDF 03

MDF 03 SECTION A-A Scale 1:50

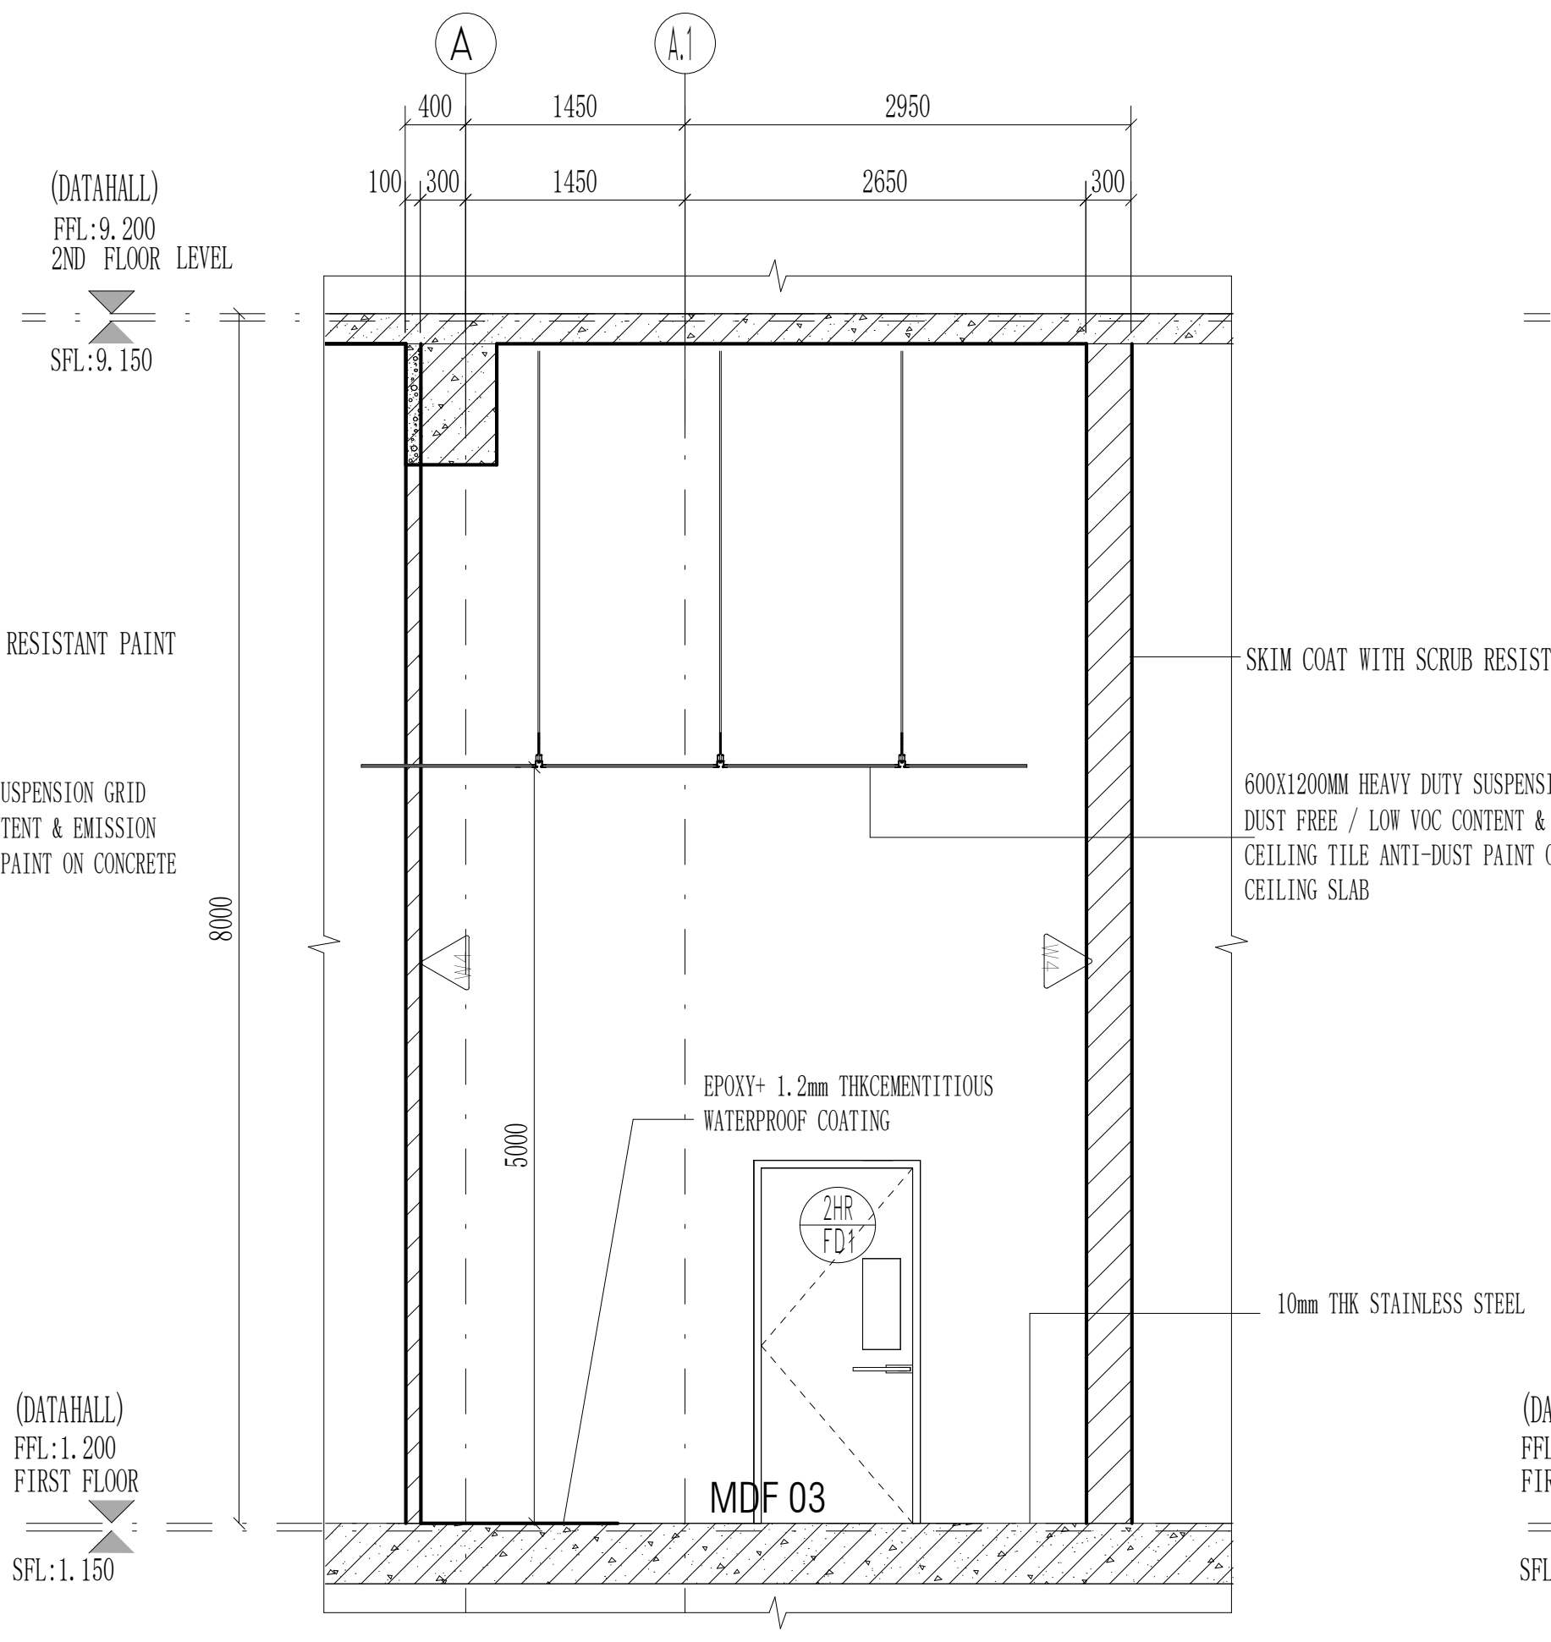
A
A.1
400
1450
2950
100
300
2650
(DATAHALL)
FFL:9.200
2ND FLOOR LEVEL
SFL:9.150
8000
5000
SKIM COAT WITH SCRUB RESISTANT PAINT
600X1200MM HEAVY DUTY SUSPENSION GRID DUST FREE / LOW VOC CONTENT & EMISSION CEILING TILE ANTI-DUST PAINT ON CONCRETE CEILING SLAB
EPOXY+ 1.2mm THKCEMENTITIOUS WATERPROOF COATING
10mm THK STAINLESS STEEL
(DATAHALL)
FFL:1.200
FIRST FLOOR
SFL:1.150
MDF 03

MDF 03 SECTION B-B Scale 1:50

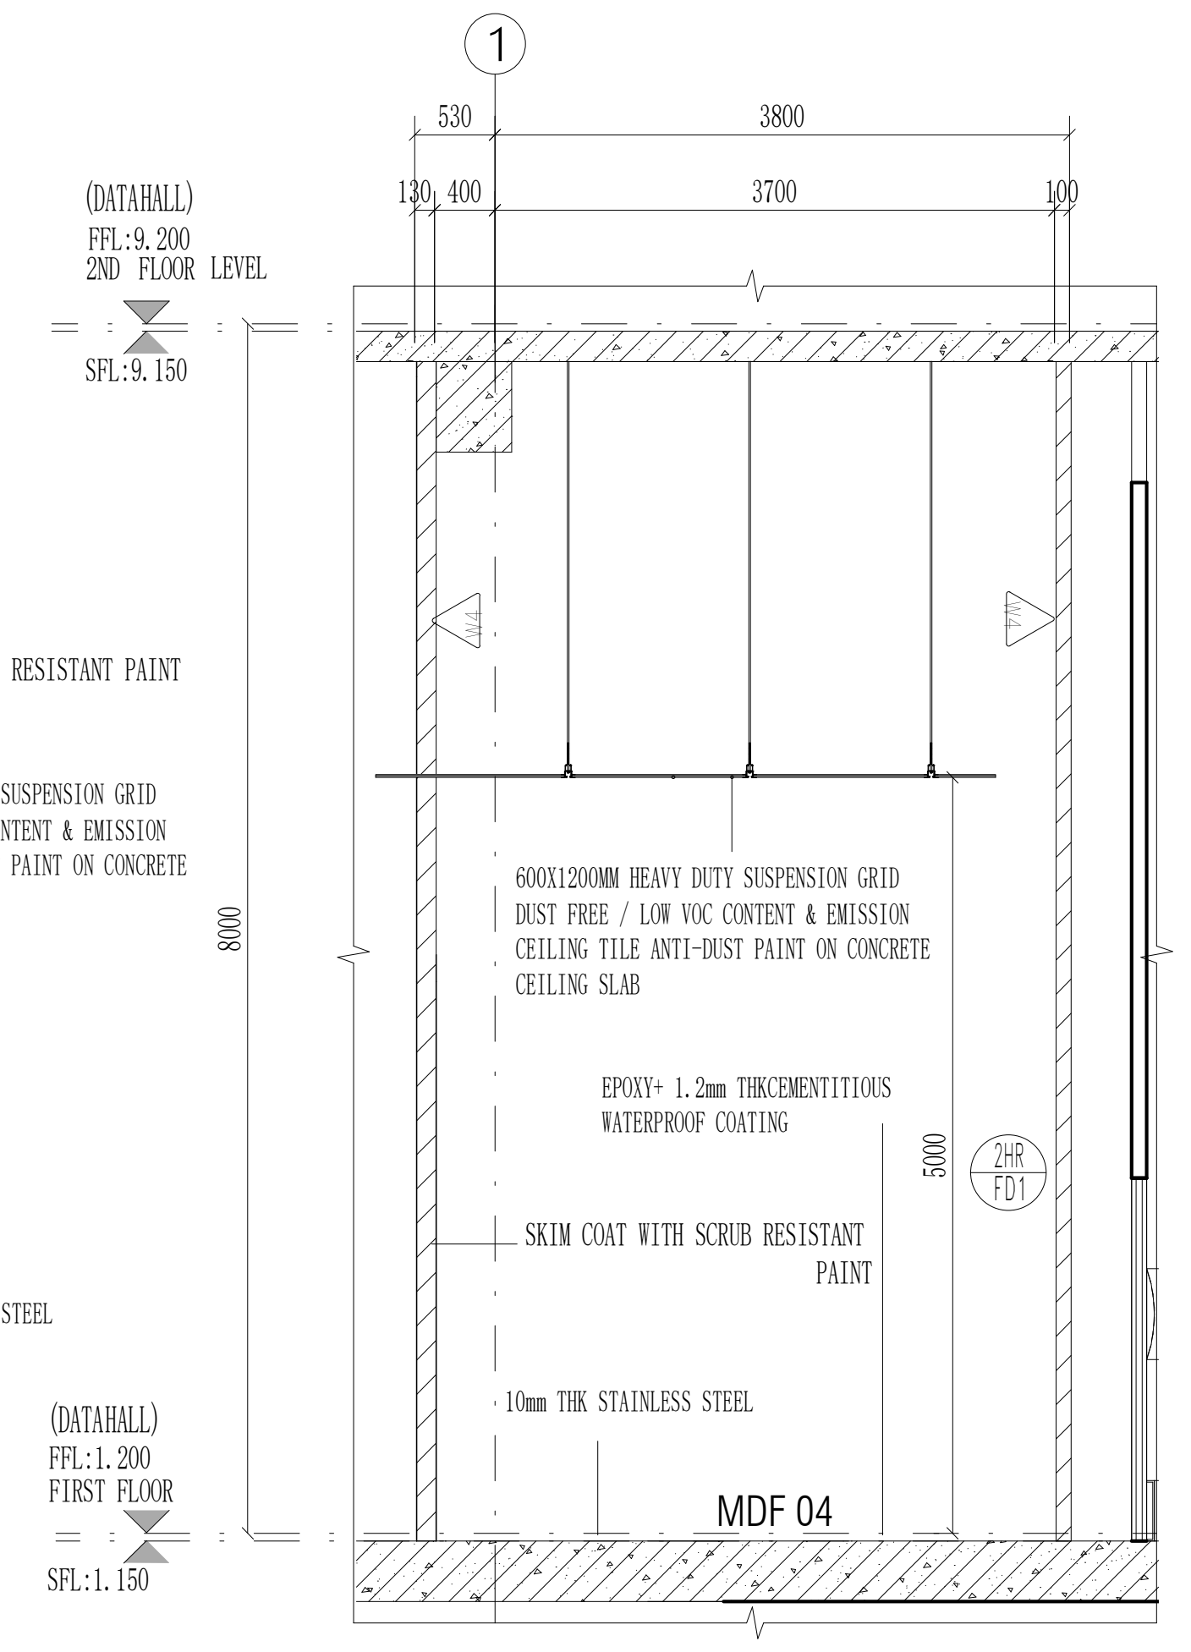
1
530
3800
130
400
3700
100
(DATAHALL)
FFL:9.200
2ND FLOOR LEVEL
SFL:9.150
8000
5000
600X1200MM HEAVY DUTY SUSPENSION GRID DUST FREE / LOW VOC CONTENT & EMISSION CEILING TILE ANTI-DUST PAINT ON CONCRETE CEILING SLAB
EPOXY+ 1.2mm THKCEMENTITIOUS WATERPROOF COATING
SKIM COAT WITH SCRUB RESISTANT PAINT
10mm THK STAINLESS STEEL
(DATAHALL)
FFL:1.200
FIRST FLOOR
SFL:1.150
MDF 04

MDF 04 SECTION A-A Scale 1:50

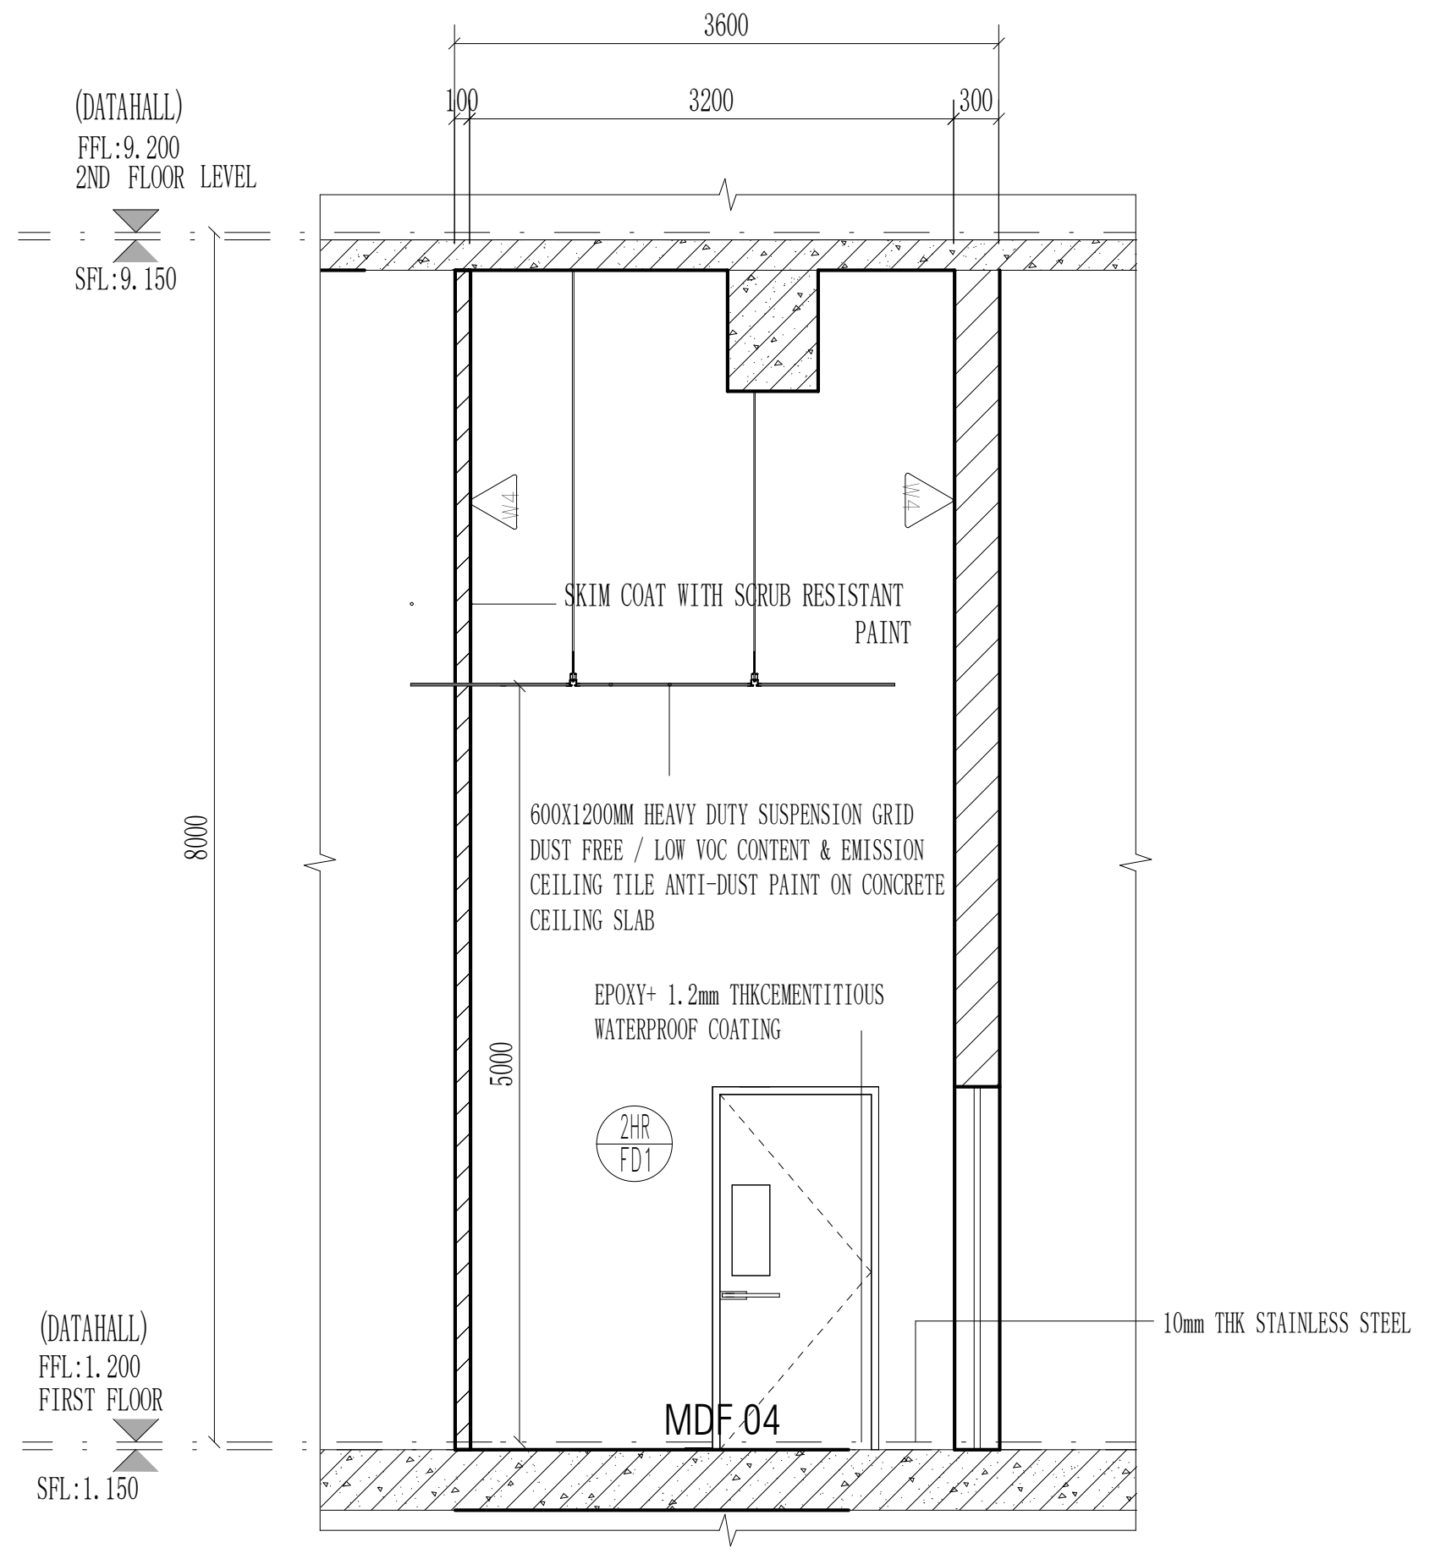
3600
100
3200
300
(DATAHALL)
FFL:9.200
2ND FLOOR LEVEL
SFL:9.150
8000
SKIM COAT WITH SCRUB RESISTANT PAINT
600X1200MM HEAVY DUTY SUSPENSION GRID DUST FREE / LOW VOC CONTENT & EMISSION CEILING TILE ANTI-DUST PAINT ON CONCRETE CEILING SLAB
EPOXY+ 1.2mm THKCEMENTITIOUS WATERPROOF COATING
2HR
FD1
10mm THK STAINLESS STEEL
(DATAHALL)
FFL:1.200
FIRST FLOOR
SFL:1.150
MDF 04

MDF 04 AECTION B-B Scale 1:50

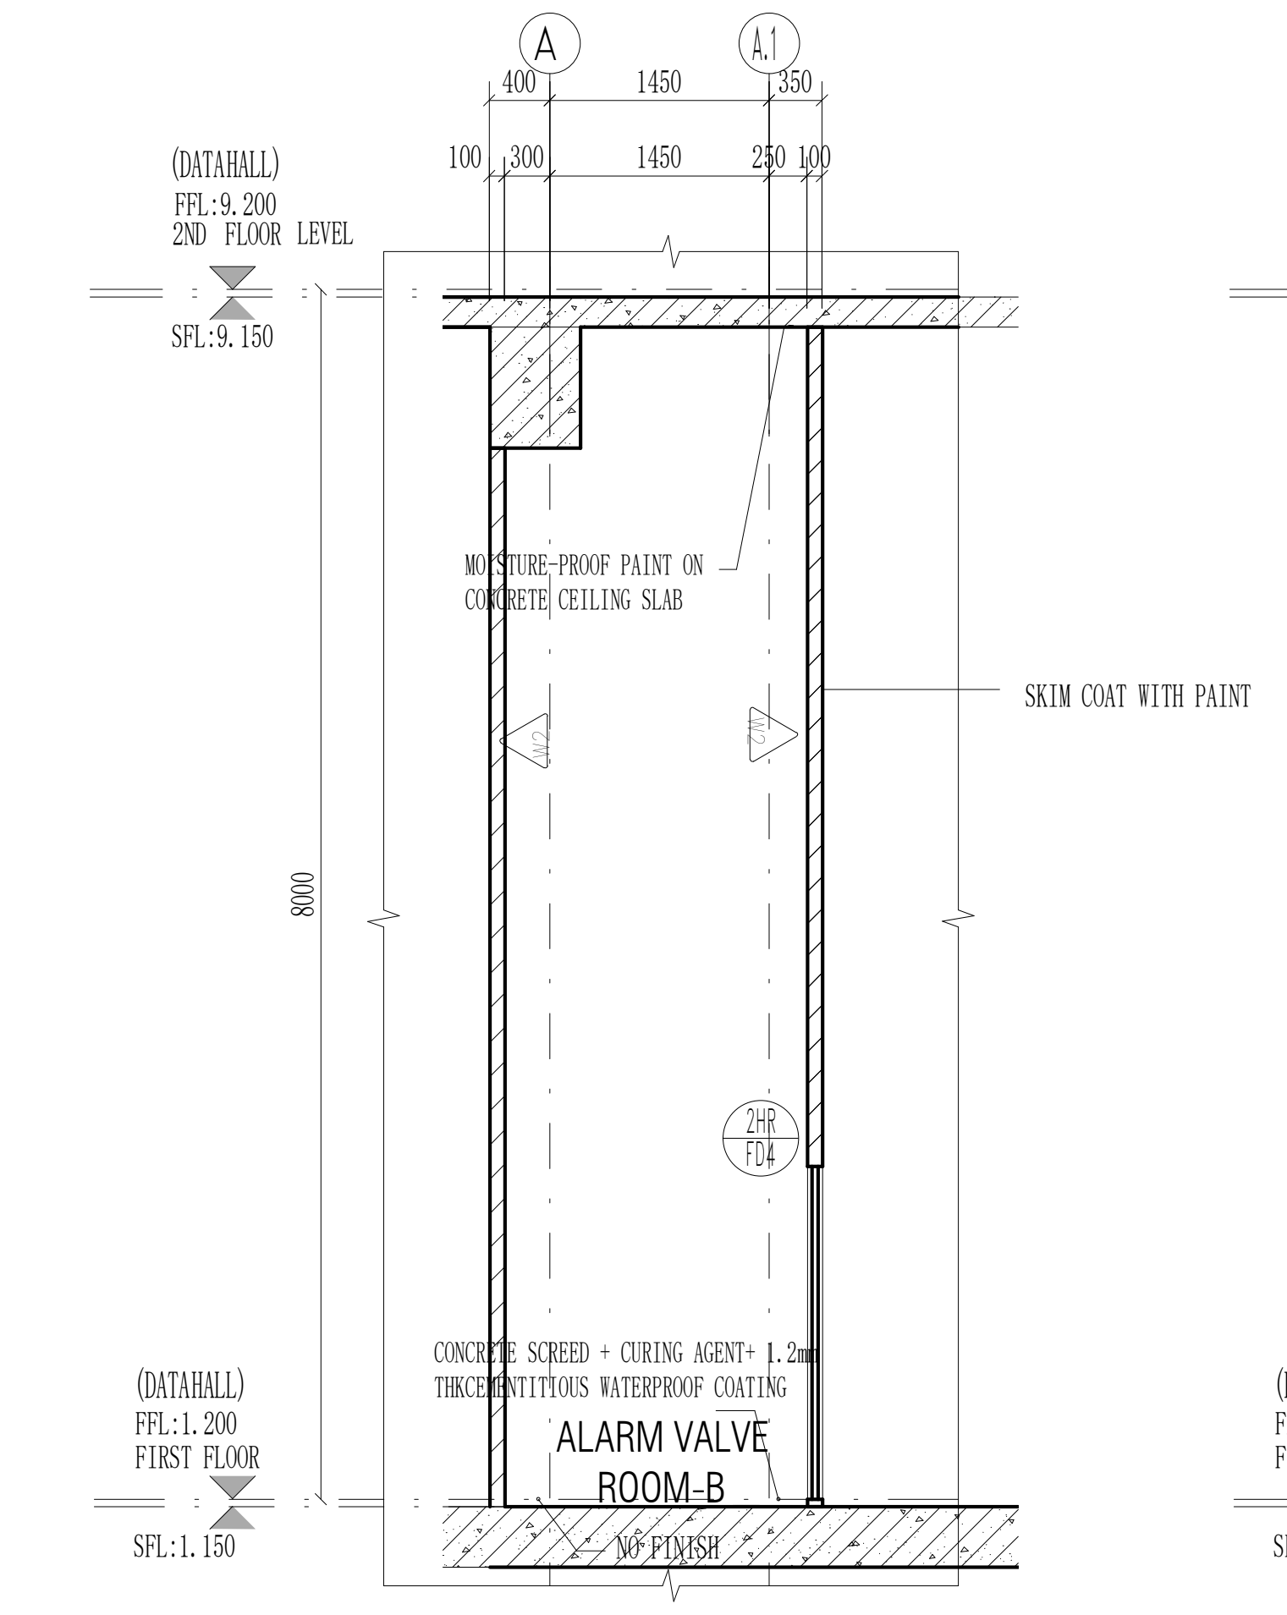
A
A.1
400
1450
330
100
300
250
(DATAHALL)
FFL:9.200
2ND FLOOR LEVEL
SFL:9.150
8000
MOISTURE-PROOF PAINT ON CONCRETE CEILING SLAB
SKIM COAT WITH PAINT
2HR
FD4
CONCRETE SCREED + CURING AGENT+ 1.2mm THKCEMENTITIOUS WATERPROOF COATING
(DATAHALL)
FFL:1.200
FIRST FLOOR
SFL:1.150
ALARM VALVE ROOM-B
NO FINISH

ALARM VALVE ROOM-B SECTION B-B Scale 1:50

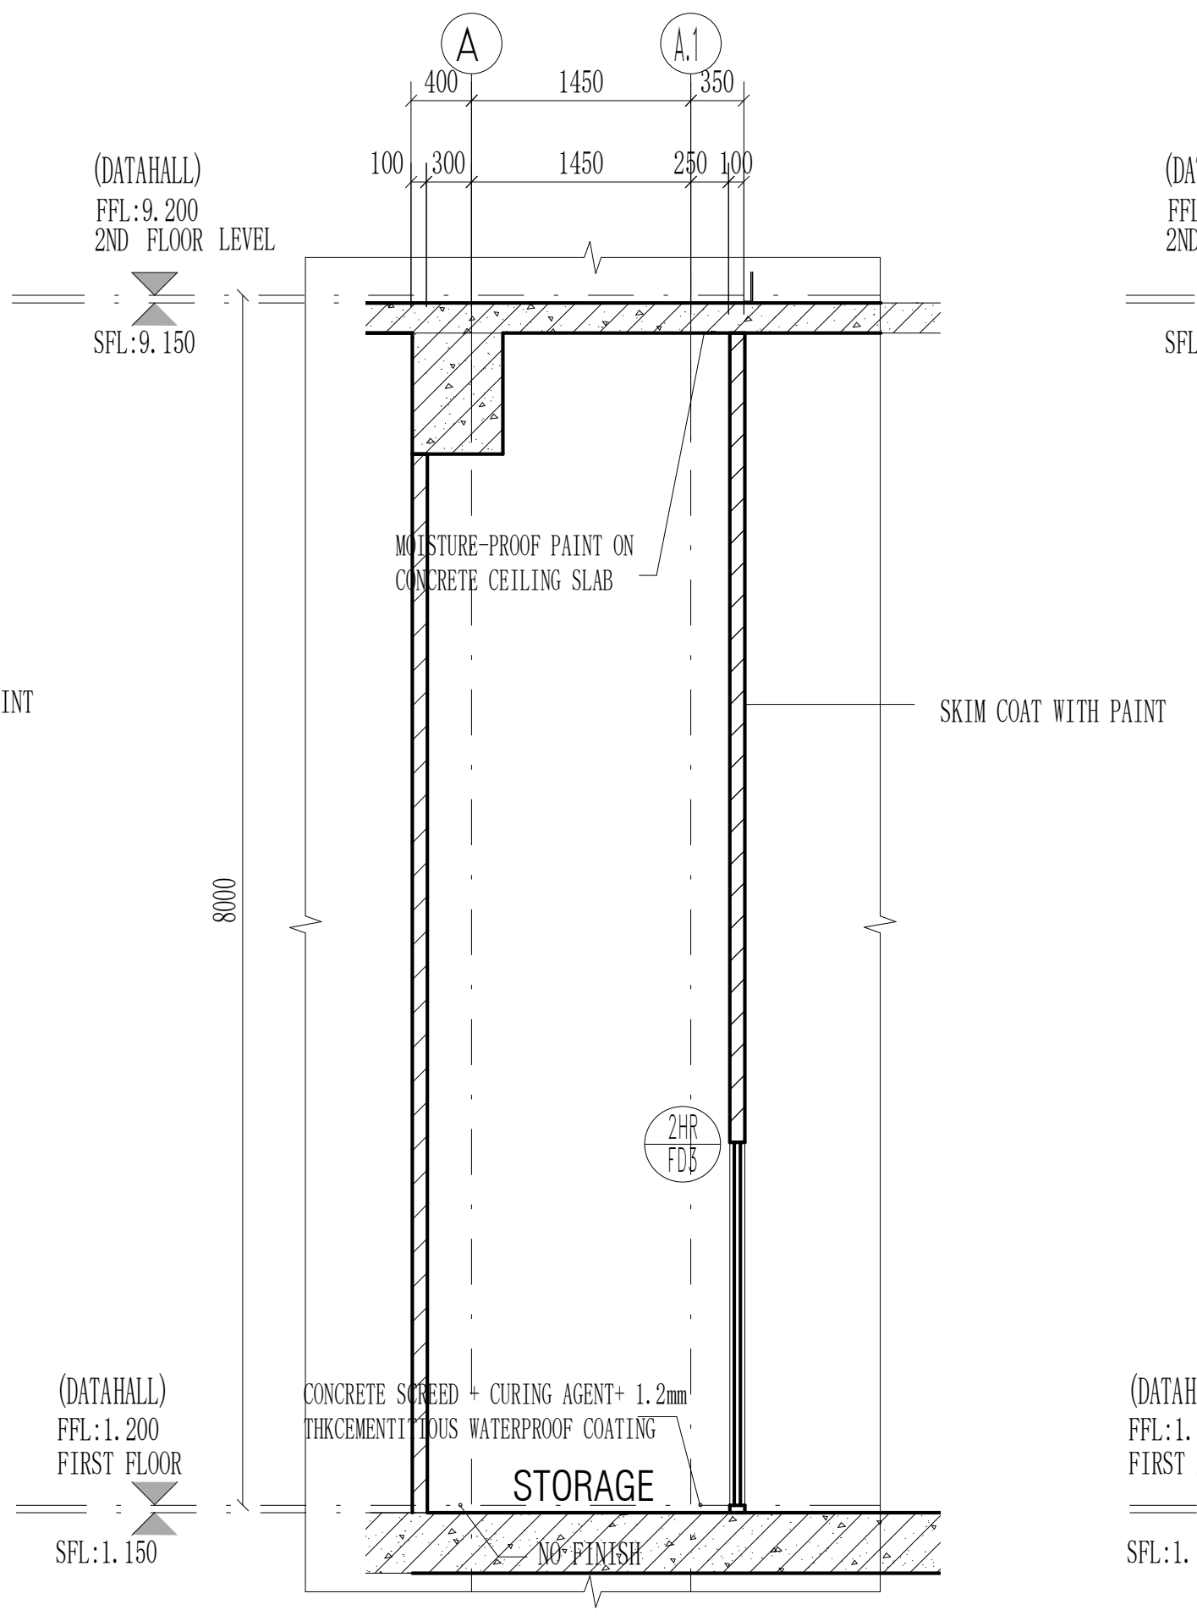
A
A.1
400
1450
330
100
300
250
(DATAHALL)
FFL:9.200
2ND FLOOR LEVEL
SFL:9.150
8000
MOISTURE-PROOF PAINT ON CONCRETE CEILING SLAB
SKIM COAT WITH PAINT
2HR
FD4
CONCRETE SCREED + CURING AGENT+ 1.2mm THKCEMENTITIOUS WATERPROOF COATING
(DATAHALL)
FFL:1.200
FIRST FLOOR
SFL:1.150
STORAGE
NO FINISH

STORAGE 02 SECTION B-B Scale 1:50

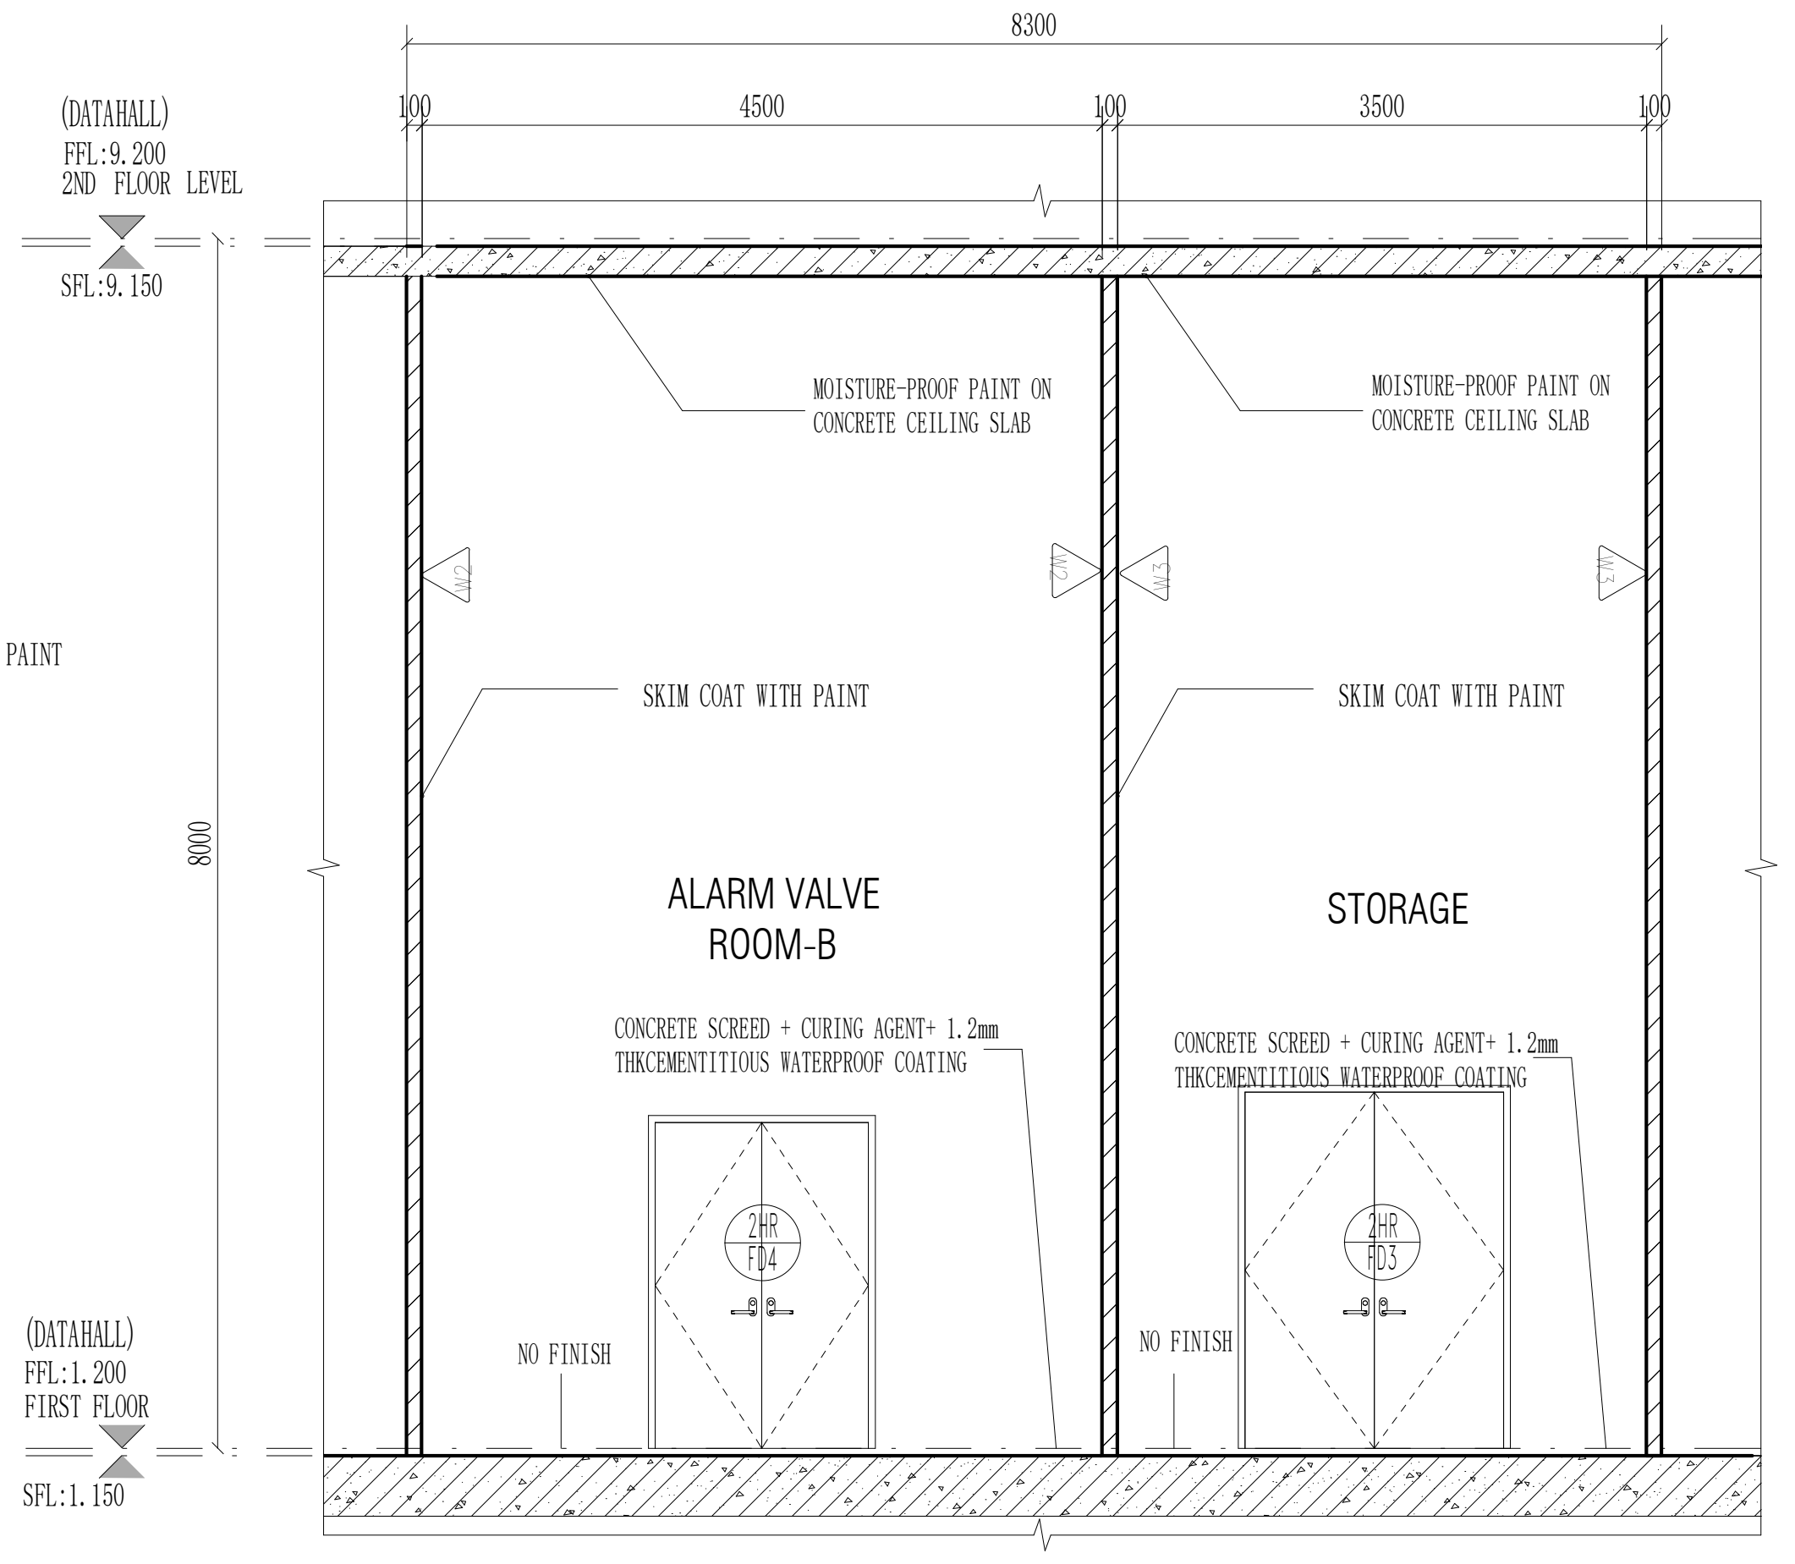
8300
100
4500
3500
(DATAHALL)
FFL:9.200
2ND FLOOR LEVEL
SFL:9.150
8000
MOISTURE-PROOF PAINT ON CONCRETE CEILING SLAB
SKIM COAT WITH PAINT
ALARM VALVE ROOM-B
STORAGE
CONCRETE SCREED + CURING AGENT+ 1.2mm THKCEMENTITIOUS WATERPROOF COATING
2HR
FD4
NO FINISH

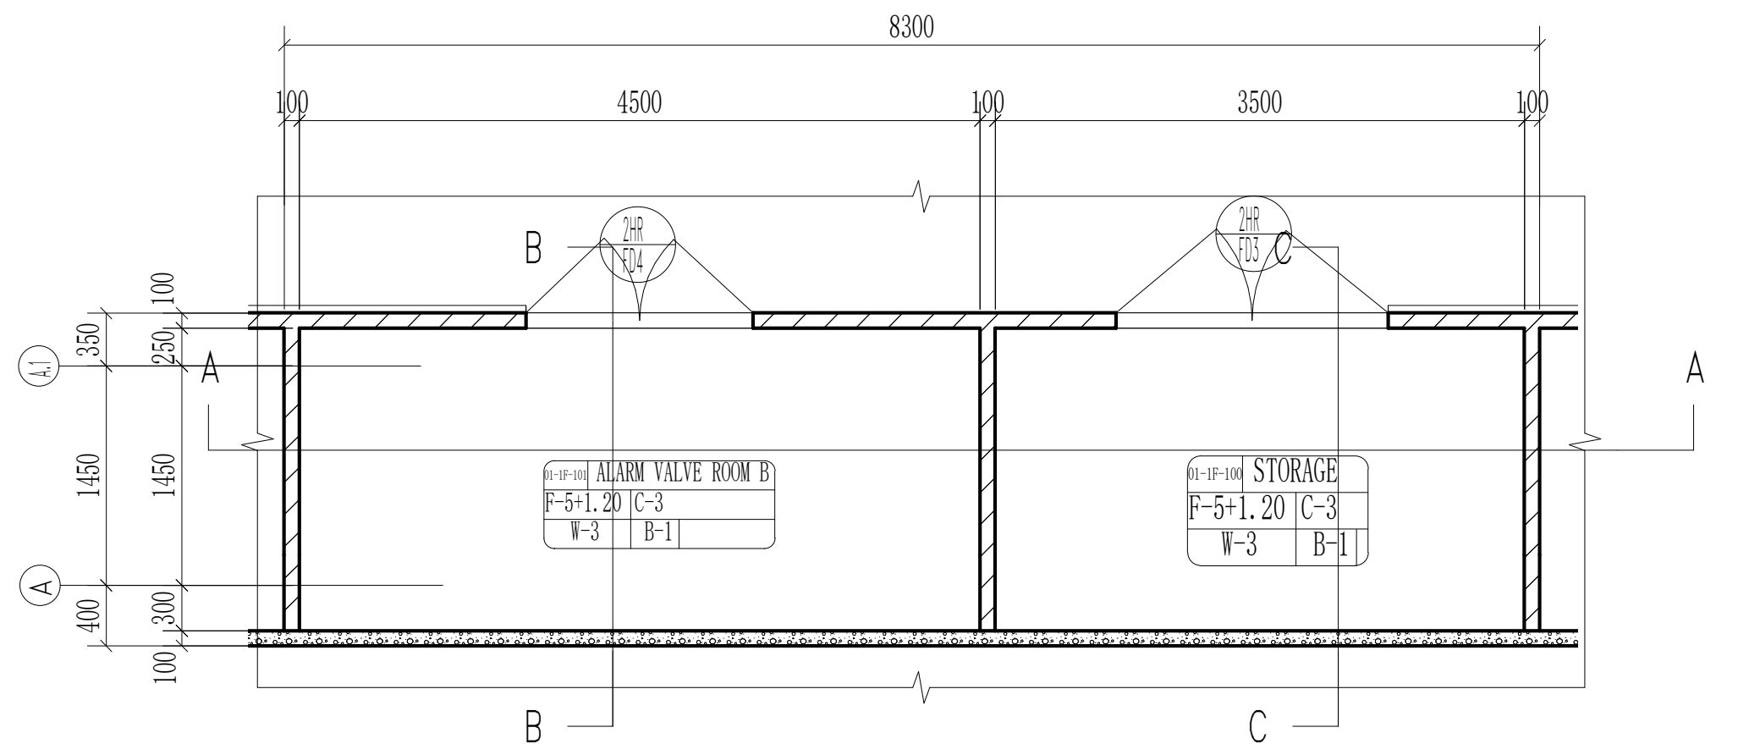
8300
100
4500
3500
B
C
A
A.1
150
100
1450
1650
400
300
ALARM VALVE ROOM-B
F-5+1.20
C-3
W-3
B-1
STORAGE

ALARM VALVE ROOM-B、STORAGE 02 FLOOR PLAN Scale 1:50

THE "SFL" MARKED IN THE DRAWING REFERS TO THE STRUCTURAL FLOOR LEVEL, WHILE THE FINISHED FLOOR LEVEL (FFL) IS DETERMINED BASED ON FLOOR FINISHES.

ALARM VALVE ROOM-B SECTION B-B Scale 1:50

STORAGE 02 SECTION B-B Scale 1:50

ALARM VALVE ROOM-B、STORAGE 02 SECTION A-A Scale 1:50

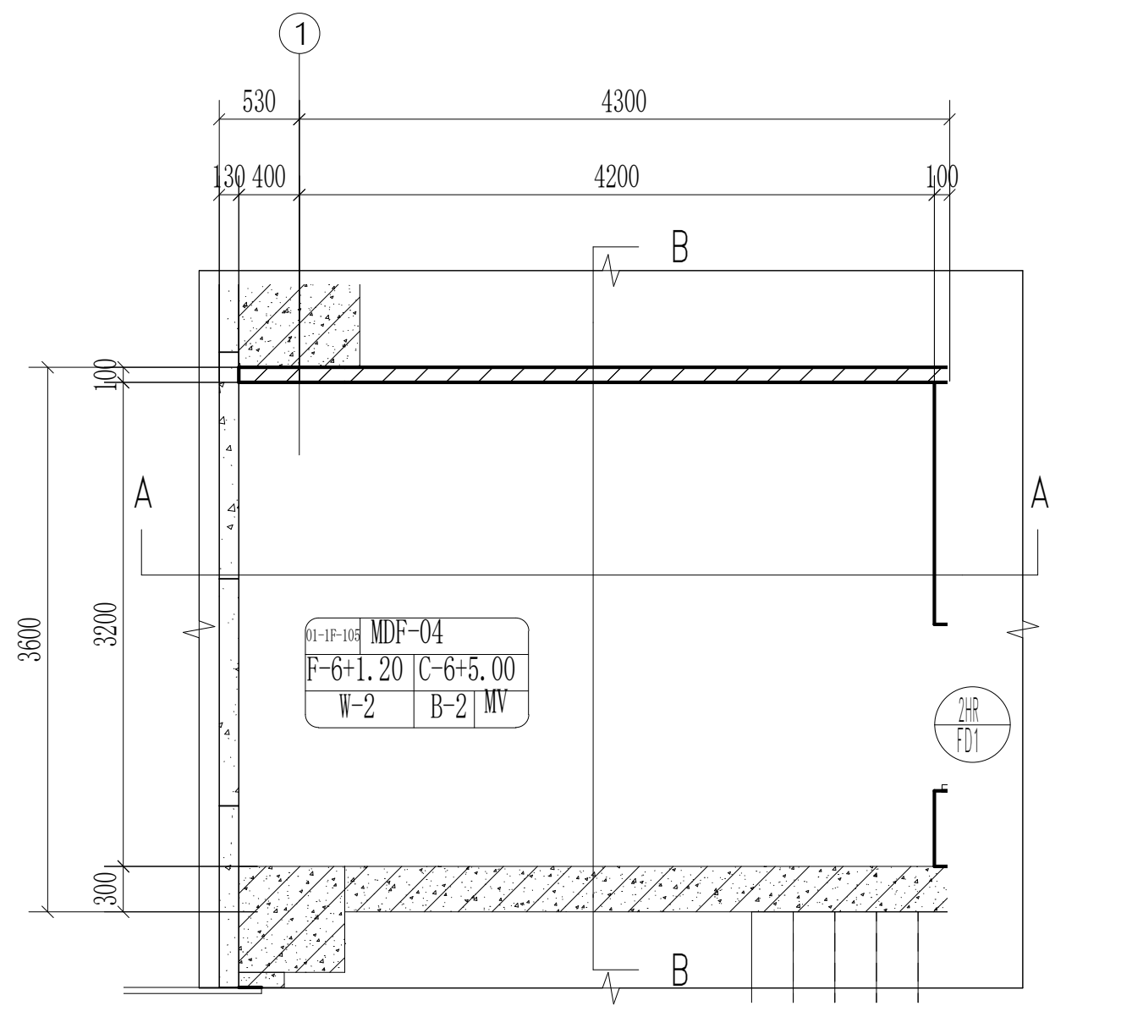
1
530
4300
130
400
4200
100
B
A
3600
3200
300
MDF-04
F-6+1.20
C-6+5.00
W-2
B-2
MV

MDF 04 FLOOR PLAN Scale 1:50

THE "SFL" MARKED IN THE DRAWING REFERS TO THE STRUCTURAL FLOOR LEVEL, WHILE THE FINISHED FLOOR LEVEL (FFL) IS DETERMINED BASED ON FLOOR FINISHES.

CLIENT :

GULF EDGE DC 01

87 Wireless Road, M Thai Tower 11th. Floor, All Seasons Place, Lumpini,
Pathumwan, Bangkok 10330, Thailand

CONTRACTOR :

华西发展(泰国)有限公司
บริษัท หัวซือ ดีเวลลอปเม้นต์ (ประเทศไทย) จำกัด
HUASHI DEVELOPMENT CO.,LTD
No. 202, Room No. 1403, 14/F, Le Concorde Building,
Ratchadapisek Road, Huaykhwang Sub-District,
Huaykhwang District, Bangkok Metropolitan 10310.

CONSULTANT :

ARbay
บริษัท เอ อาร์ เบย์ จำกัด
ARbay Company Limited
31 st Floor Bangkok Insurance Building
25 South Sathorn road Thungmahamek
Sathorn Bangkok 10120 THAILAND
T +66 (0) 2286 8199
F +66 (0) 2286 2863
info@arbay.co.th

CONSULTANT :

Qbic Engineers & Architects Co.,Ltd.
8 Soi KALONG 4 SANAMBINNAM ROAD,
THASAI SUB-DISTRICT, MUANG NONTHABURI DISTRICT
, NONTHABURI.
Tel 662-950-4374
Fax 662-580-3231
E-Mail : qbic@qbic.co.th, www.qbic.co.th
QBIC ENGINEERS AND ARCHITECTS CO.,LTD.

CONSULTANT :

MITR
MITR TECHNICAL CONSULTANT CO.,LTD.
1168/8 12th FLOOR, LUMPINI TOWER BUILDING,
RAMA IV RD., THUNGMAHAMEK, SATHORN, BANGKOK 10120, THAILAND
TEL : 0-2679-9079-84
FAX : 0-2679-9085 E-mail: mitr_dd@mitr.com

Architect : SIGNATURE
ประกิต พนานุรัตน์ วสถ. 580
ที่อยู่
251/1 ถ.จารุเมือง แขวงรองเมือง เขตปทุมวัน
กรุงเทพมหานคร โทรศัพท์ 02-286-8199

Structural Engineer : SIGNATURE
วิศวกรผู้ออกแบบโครงสร้าง
ณัฐสม สงวนวงษ์ วย 1423
ที่อยู่
2/1 ซ.รามคำแหง 150 ถ.รามคำแหง
แขวง สะพานสูง เขต สะพานสูง กทม. 10240

Structural Inspector : SIGNATURE
วิศวกรผู้ตรวจสอบโครงสร้าง
โกมล จุฑาภัทร วย 964
ที่อยู่
24/18 ซ.นวมินทร์ 129 ถ. นวมินทร์
แขวง นวลจันทร์ เขต บึงกุ่ม กทม. 10230

Electrical Engineer : SIGNATURE
วิศวกรผู้ออกแบบระบบไฟฟ้ากำลัง
นายสุภัทร บูรณวิทย์ วฟก.1265
ที่อยู่
21 ซอยทานสัมฤทธิ์ 13
ตำบลท่าทราย อ.เมืองนนทบุรี จ.นนทบุรี 11000

Mechanical Engineer : SIGNATURE
วิศวกรผู้ออกแบบระบบเครื่องกลและปรับอากาศ
นายประสิทธิ์ เกี้ยวสุนทร วก.1221
ที่อยู่
44/372 ซอยบางกระดี่ 35/1 แขวงแสมดำ
เขตบางขุนเทียน กทม. 10150
ประสิทธิ์

Sanitary Engineer : SIGNATURE
วิศวกรผู้ออกแบบระบบสุขาภิบาล และดับเพลิง
นายทศวรรษ สนั่นฤทธิ์ วส. 215
ที่อยู่
บ้านเลขที่ 99/107 หมู่ที่ 3 ต.ศีรษะจรเข้น้อย
อ.บางเสาธง จ.สมุทรปราการ 10540
ทศวรรษ

ISSUE/REVISION

REV.	DESCRIPTION	DATE
A	90% DEVELOPED	09/05/2026

PROJECT NAME :
GEDC 01

LOCATION:
Nikhom Phattana district, Rayong ,industrial estate,CPGC

BUILDING :
MAIN BUILDING

90% DEVELOPED

TITLE :
ROOM DETAIL-1F-MDF 03,MDF 04,ALARM VALVE ROOM-B,STORAGE 02

JOB NO.		SCALE	1 : 50
DRAWN	LYT	REF.	
CHECKED	LJC	DWG. NO.	MPK01A-90-A-RD-119
APPROVED	LXD		
DATE	2026.05.09		

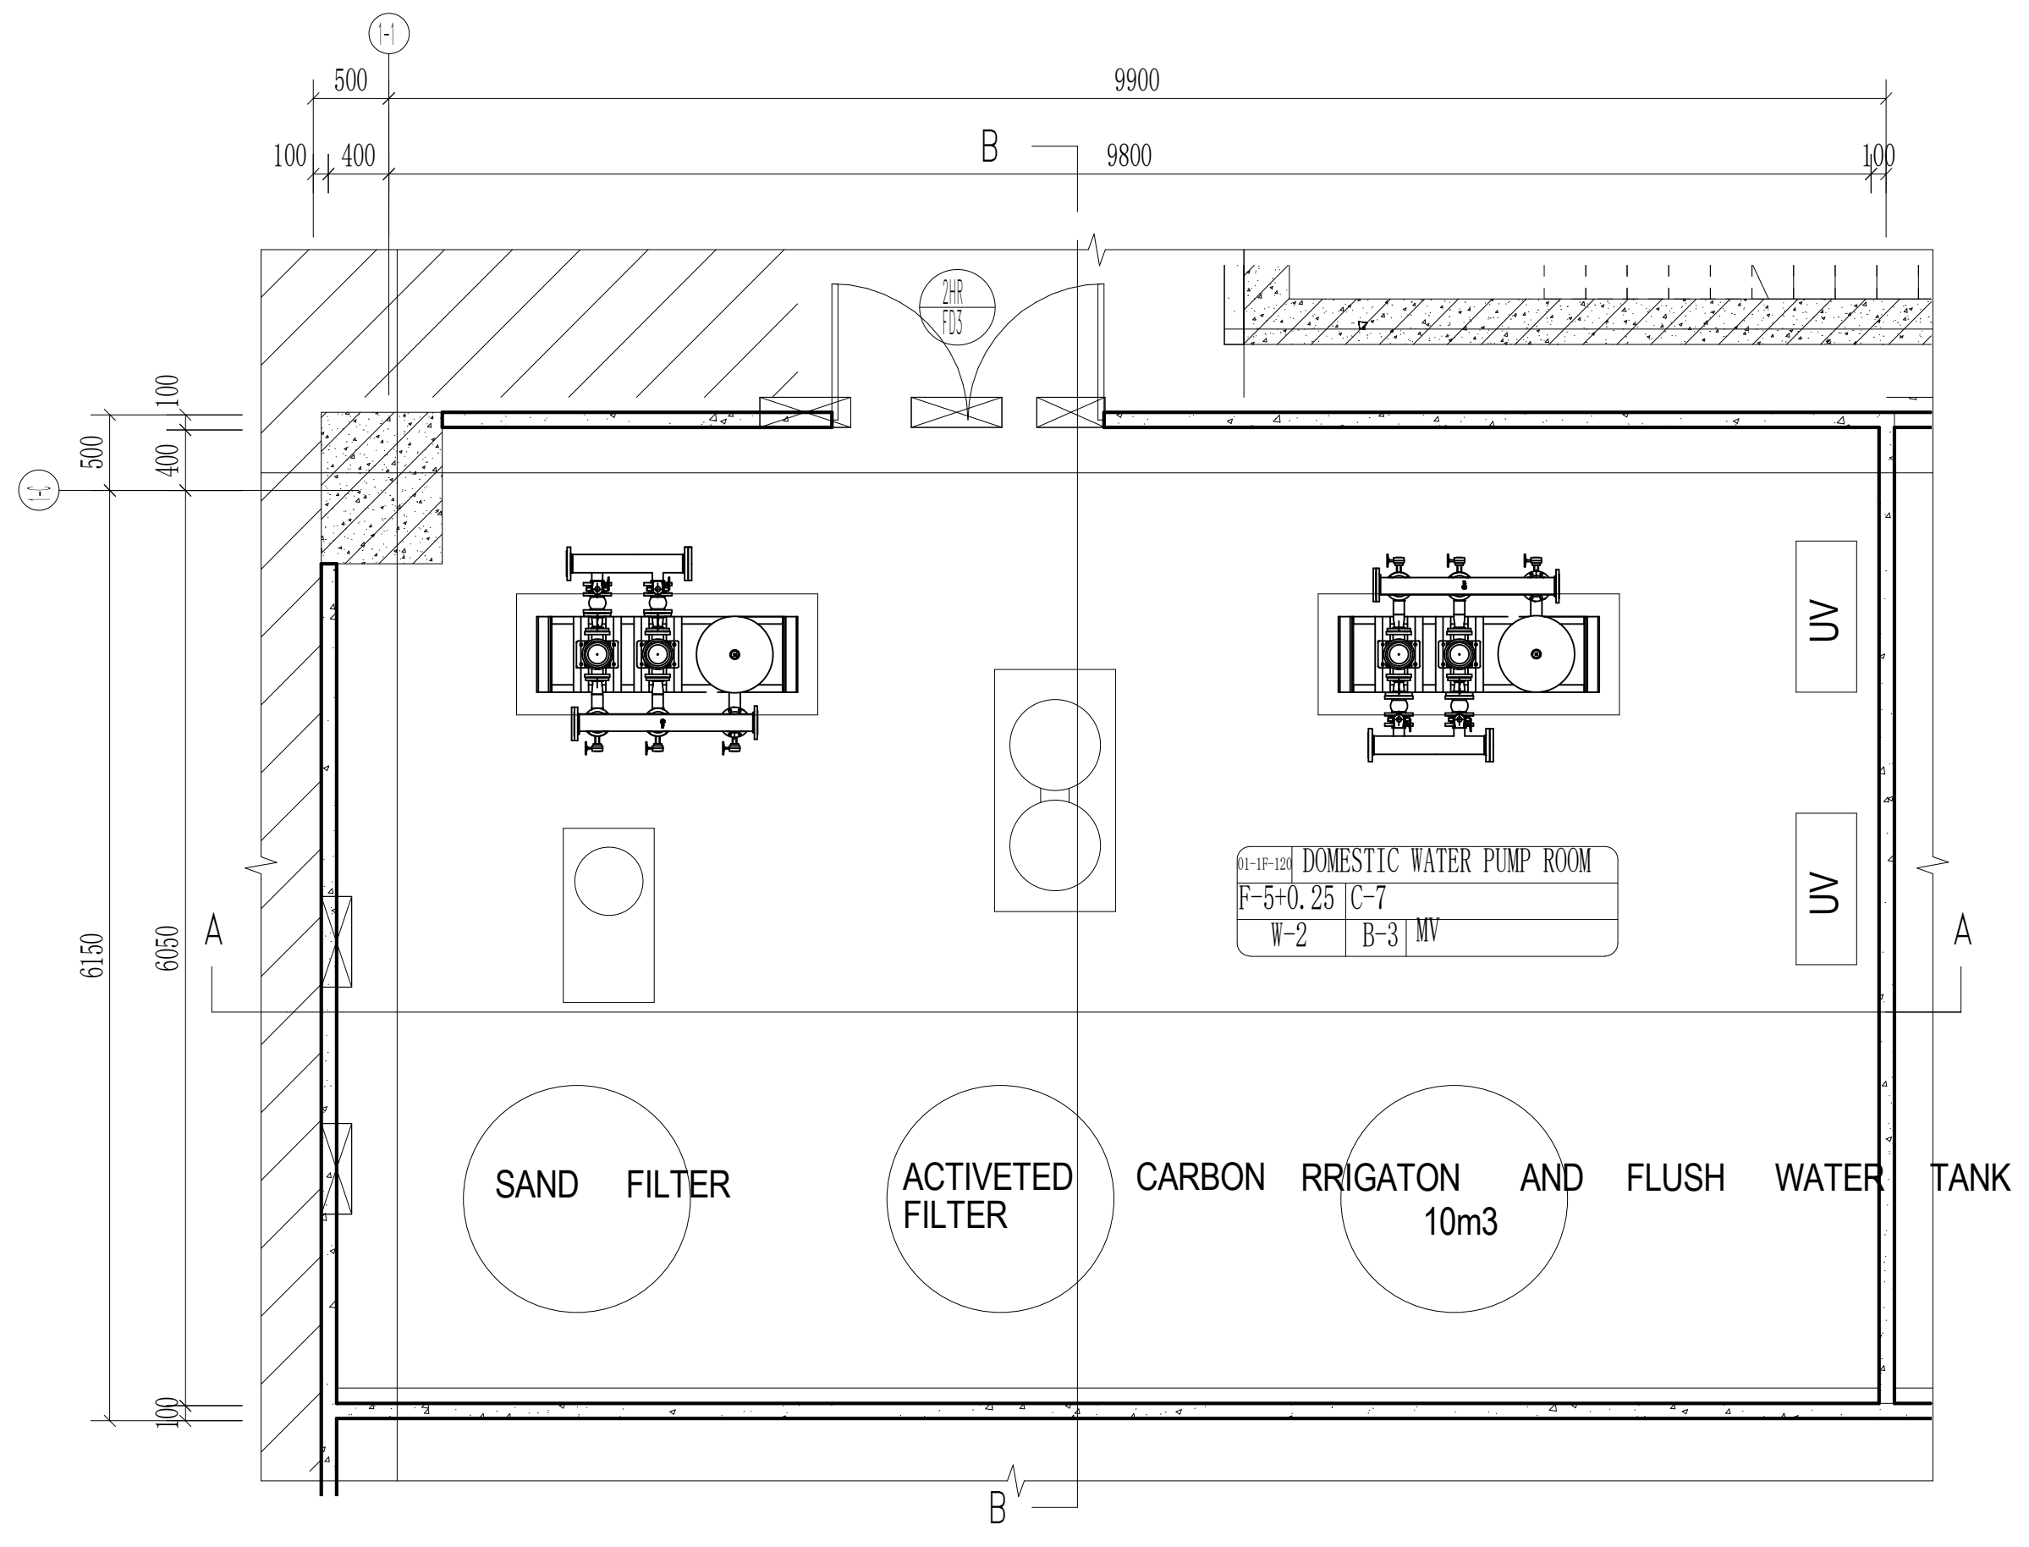
9900
500
B
9800
100
400
6150
6650
A
A
UV
UV
DOMESTIC WATER PUMP ROOM
F-5=0.25
C-7
W-2
B-3
SAND FILTER
ACTIVETED FILTER
CARBON
RRIGATON AND FLUSH WATER TANK
10m3
B

DOMESTIC WATER PUMP ROOM FLOOR PLAN

Scale 1:50

THE "SFL" MARKED IN THE DRAWING REFERS TO THE STRUCTURAL FLOOR LEVEL, WHILE THE FINISHED FLOOR LEVEL (FFL) IS DETERMINED BASED ON FLOOR FINISHES.

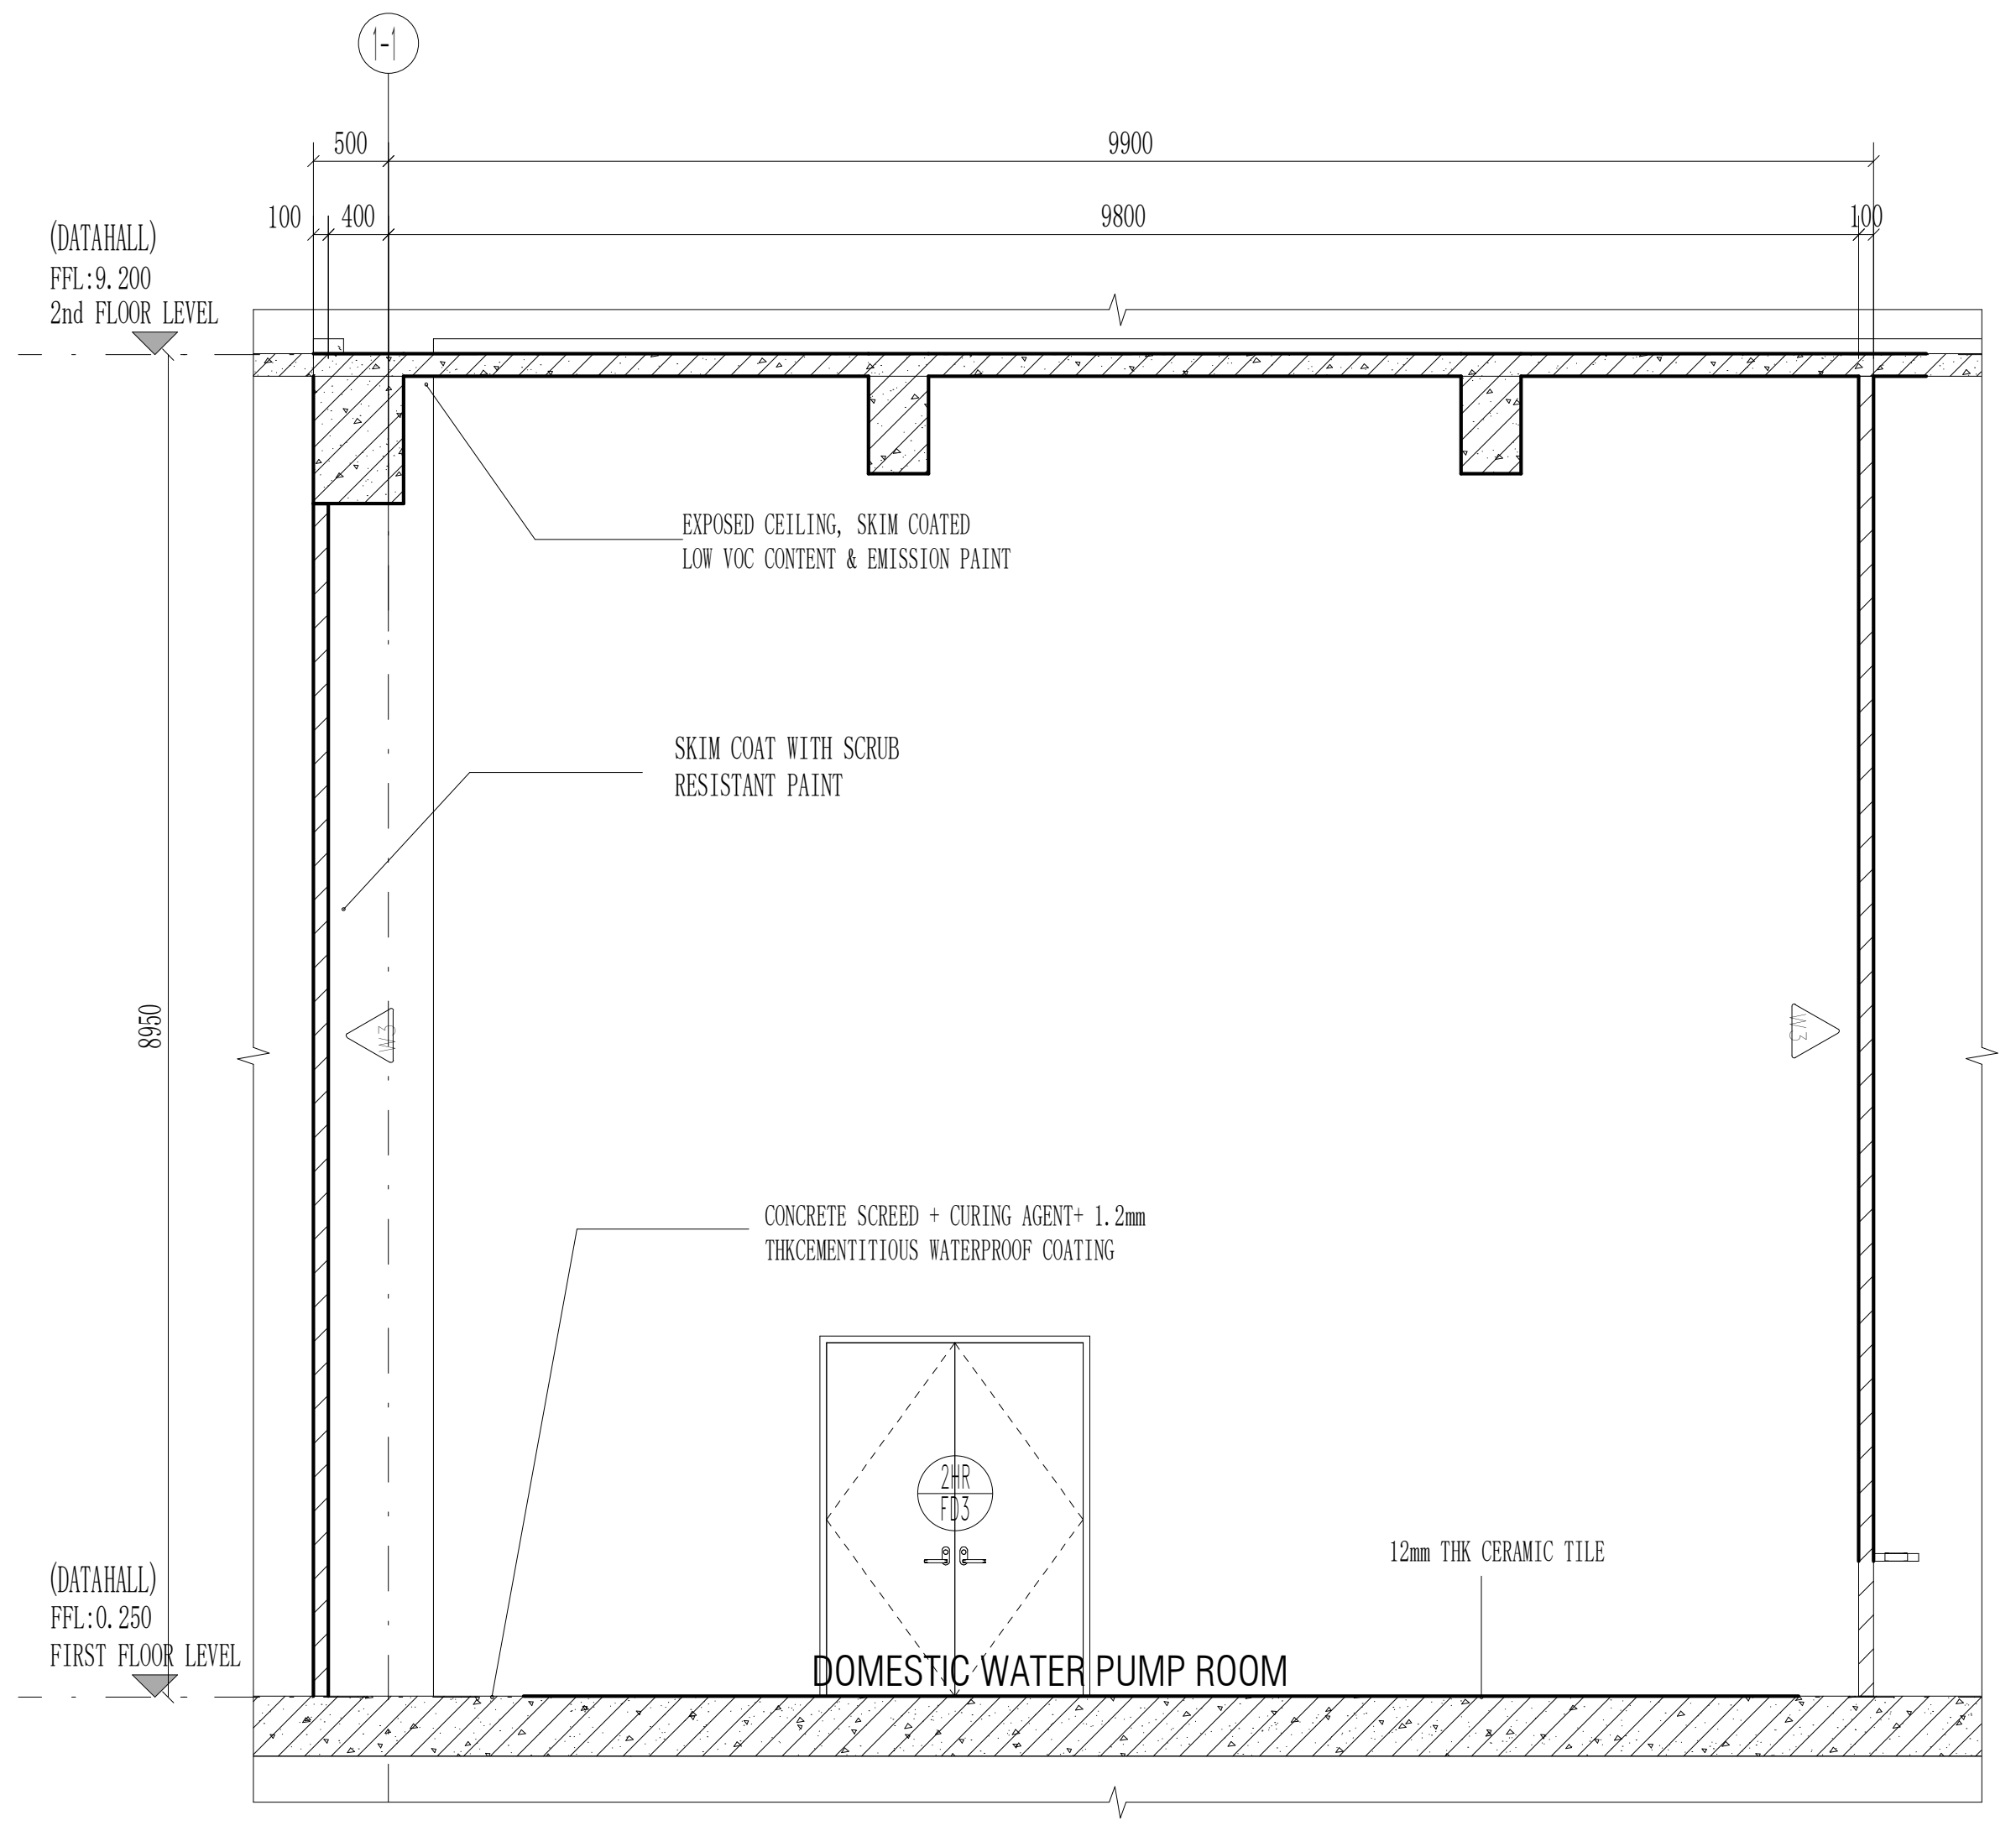
9900
500
9800
100
400
(DATAHALL)
FFL:9.200
2nd FLOOR LEVEL
EXPOSED CEILING, SKIM COATED
LOW VOC CONTENT & EMISSION PAINT
SKIM COAT WITH SCRUB
RESISTANT PAINT
8650
CONCRETE SCREED + CURING AGENT+ 1.2mm
THKCEMENTITIOUS WATERPROOF COATING
12mm THK CERAMIC TILE
(DATAHALL)
FFL:0.250
FIRST FLOOR LEVEL
DOMESTIC WATER PUMP ROOM

DOMESTIC WATER PUMP ROOM SECTION A-A

Scale 1:50

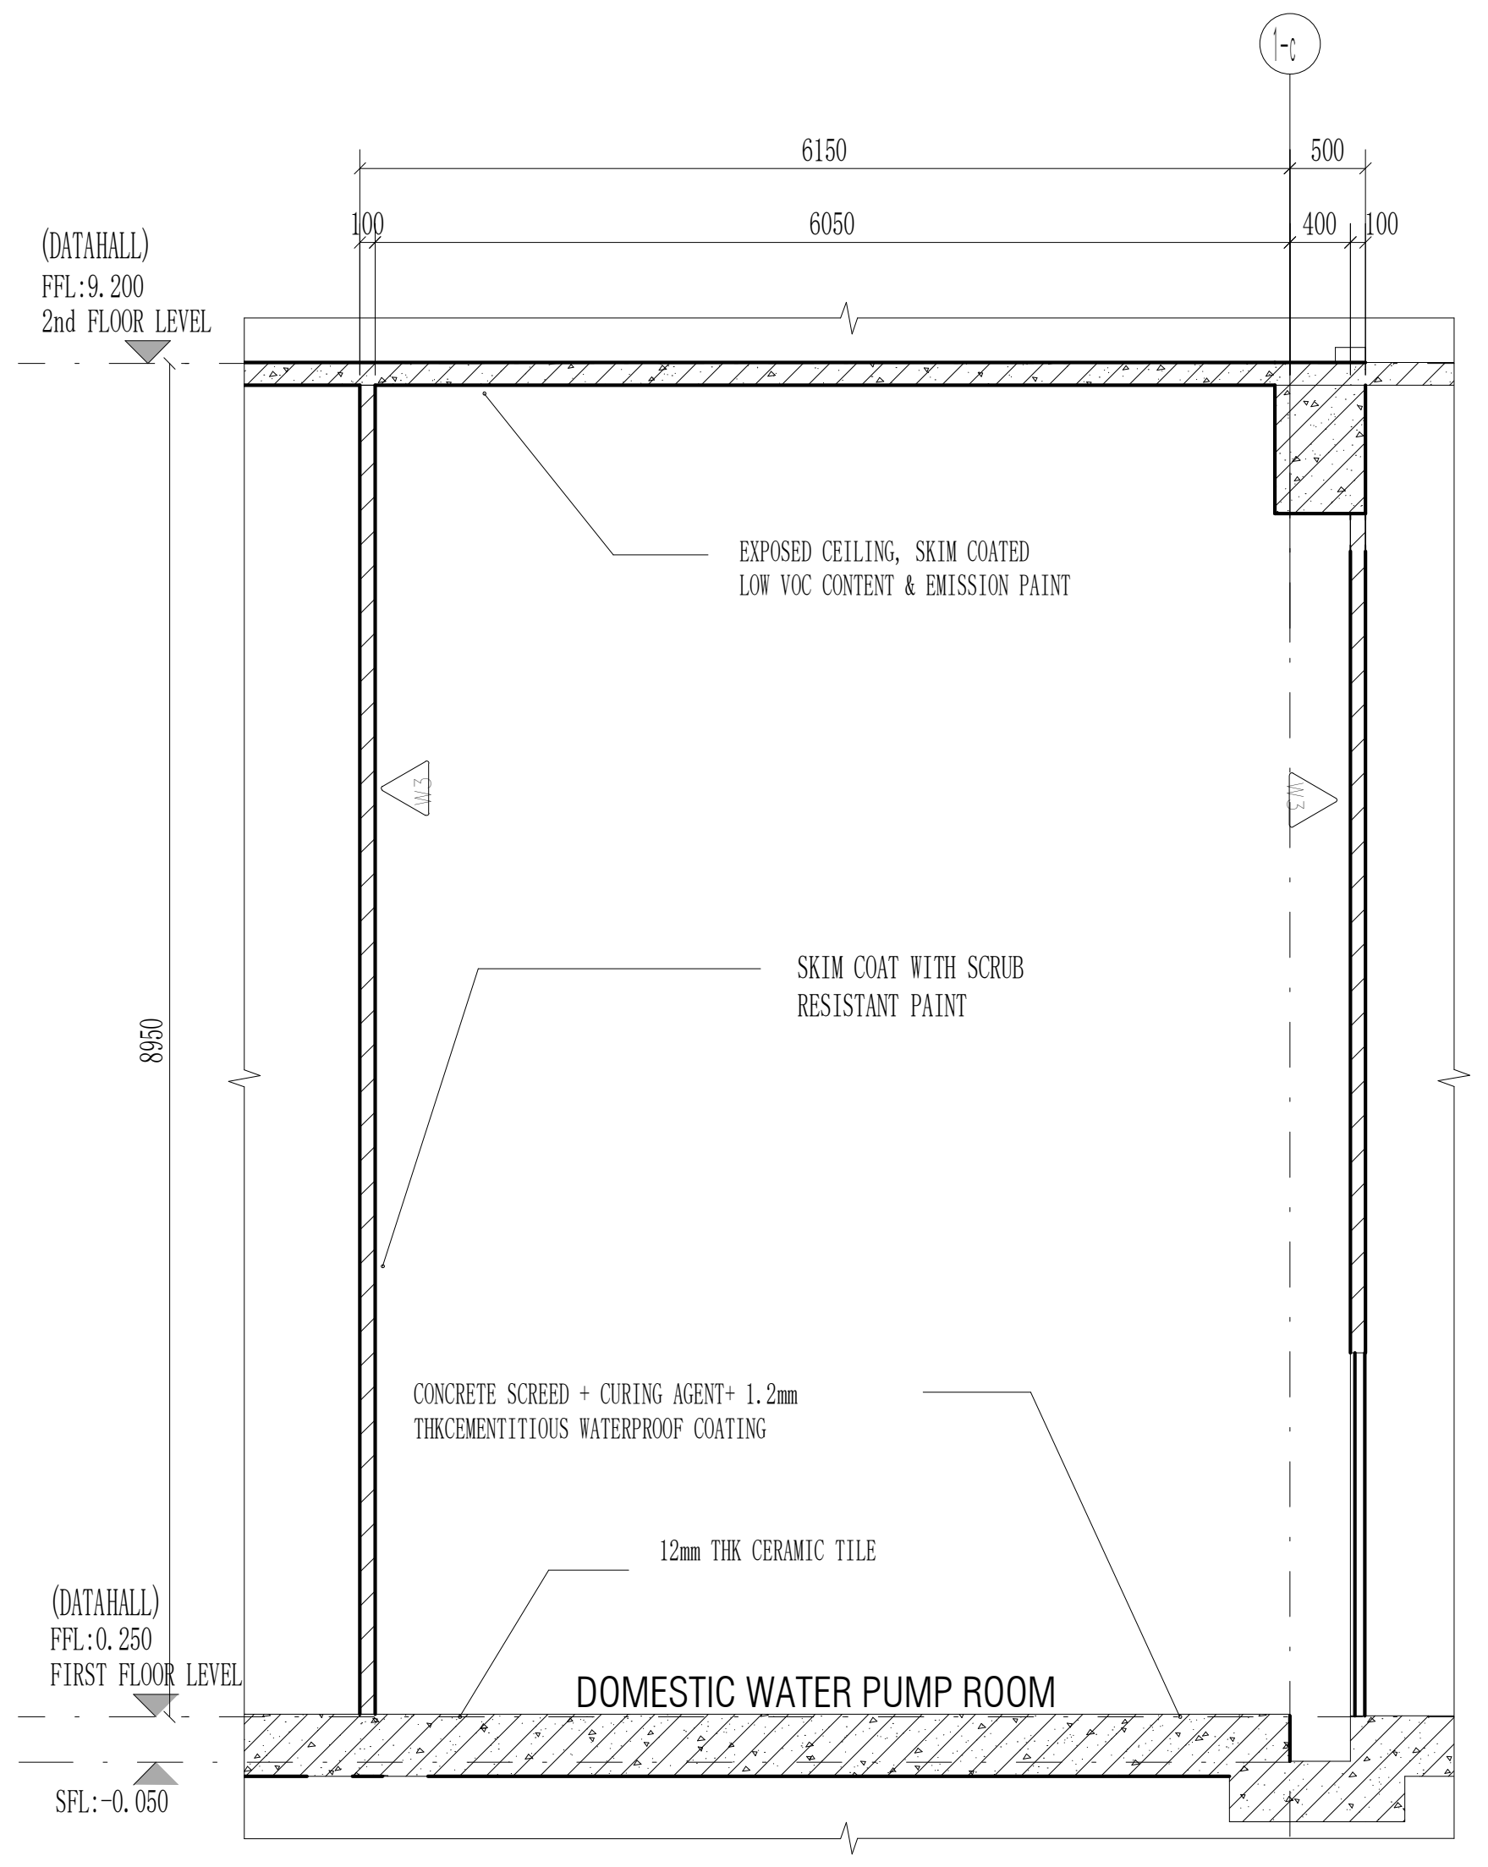
6150
500
6050
100
400
(DATAHALL)
FFL:9.200
2nd FLOOR LEVEL
EXPOSED CEILING, SKIM COATED
LOW VOC CONTENT & EMISSION PAINT
SKIM COAT WITH SCRUB
RESISTANT PAINT
8650
CONCRETE SCREED + CURING AGENT+ 1.2mm
THKCEMENTITIOUS WATERPROOF COATING
12mm THK CERAMIC TILE
(DATAHALL)
FFL:0.250
FIRST FLOOR LEVEL
SFL:-0.050
DOMESTIC WATER PUMP ROOM

DOMESTIC WATER PUMP ROOM SECTION B-B

Scale 1:50

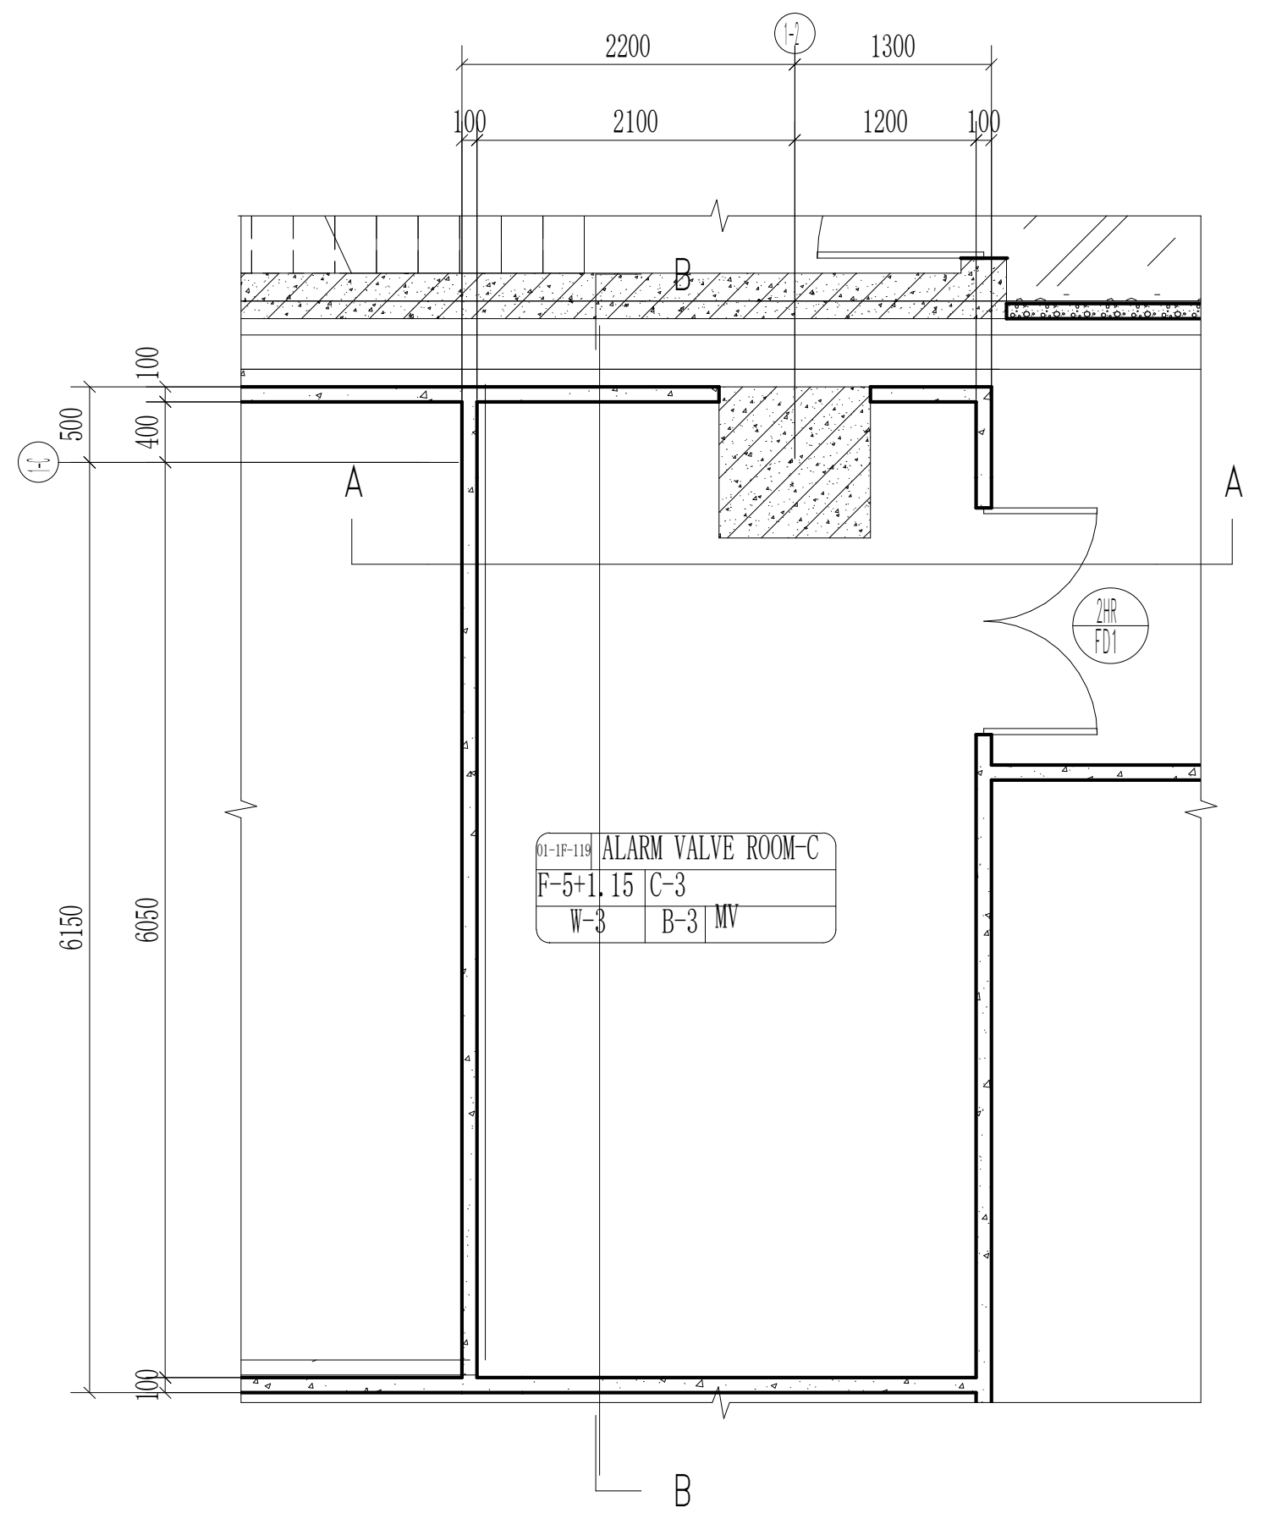
2200
1300
100
2100
1200
100
B
A
A
300
6130
6650
ALARM VALVE ROOM-C
F-5=1.15
C-3
W-3
B-3
B

ALARM VALVE ROOM FLOOR PLAN

Scale 1:50

THE "SFL" MARKED IN THE DRAWING REFERS TO THE STRUCTURAL FLOOR LEVEL, WHILE THE FINISHED FLOOR LEVEL (FFL) IS DETERMINED BASED ON FLOOR FINISHES.

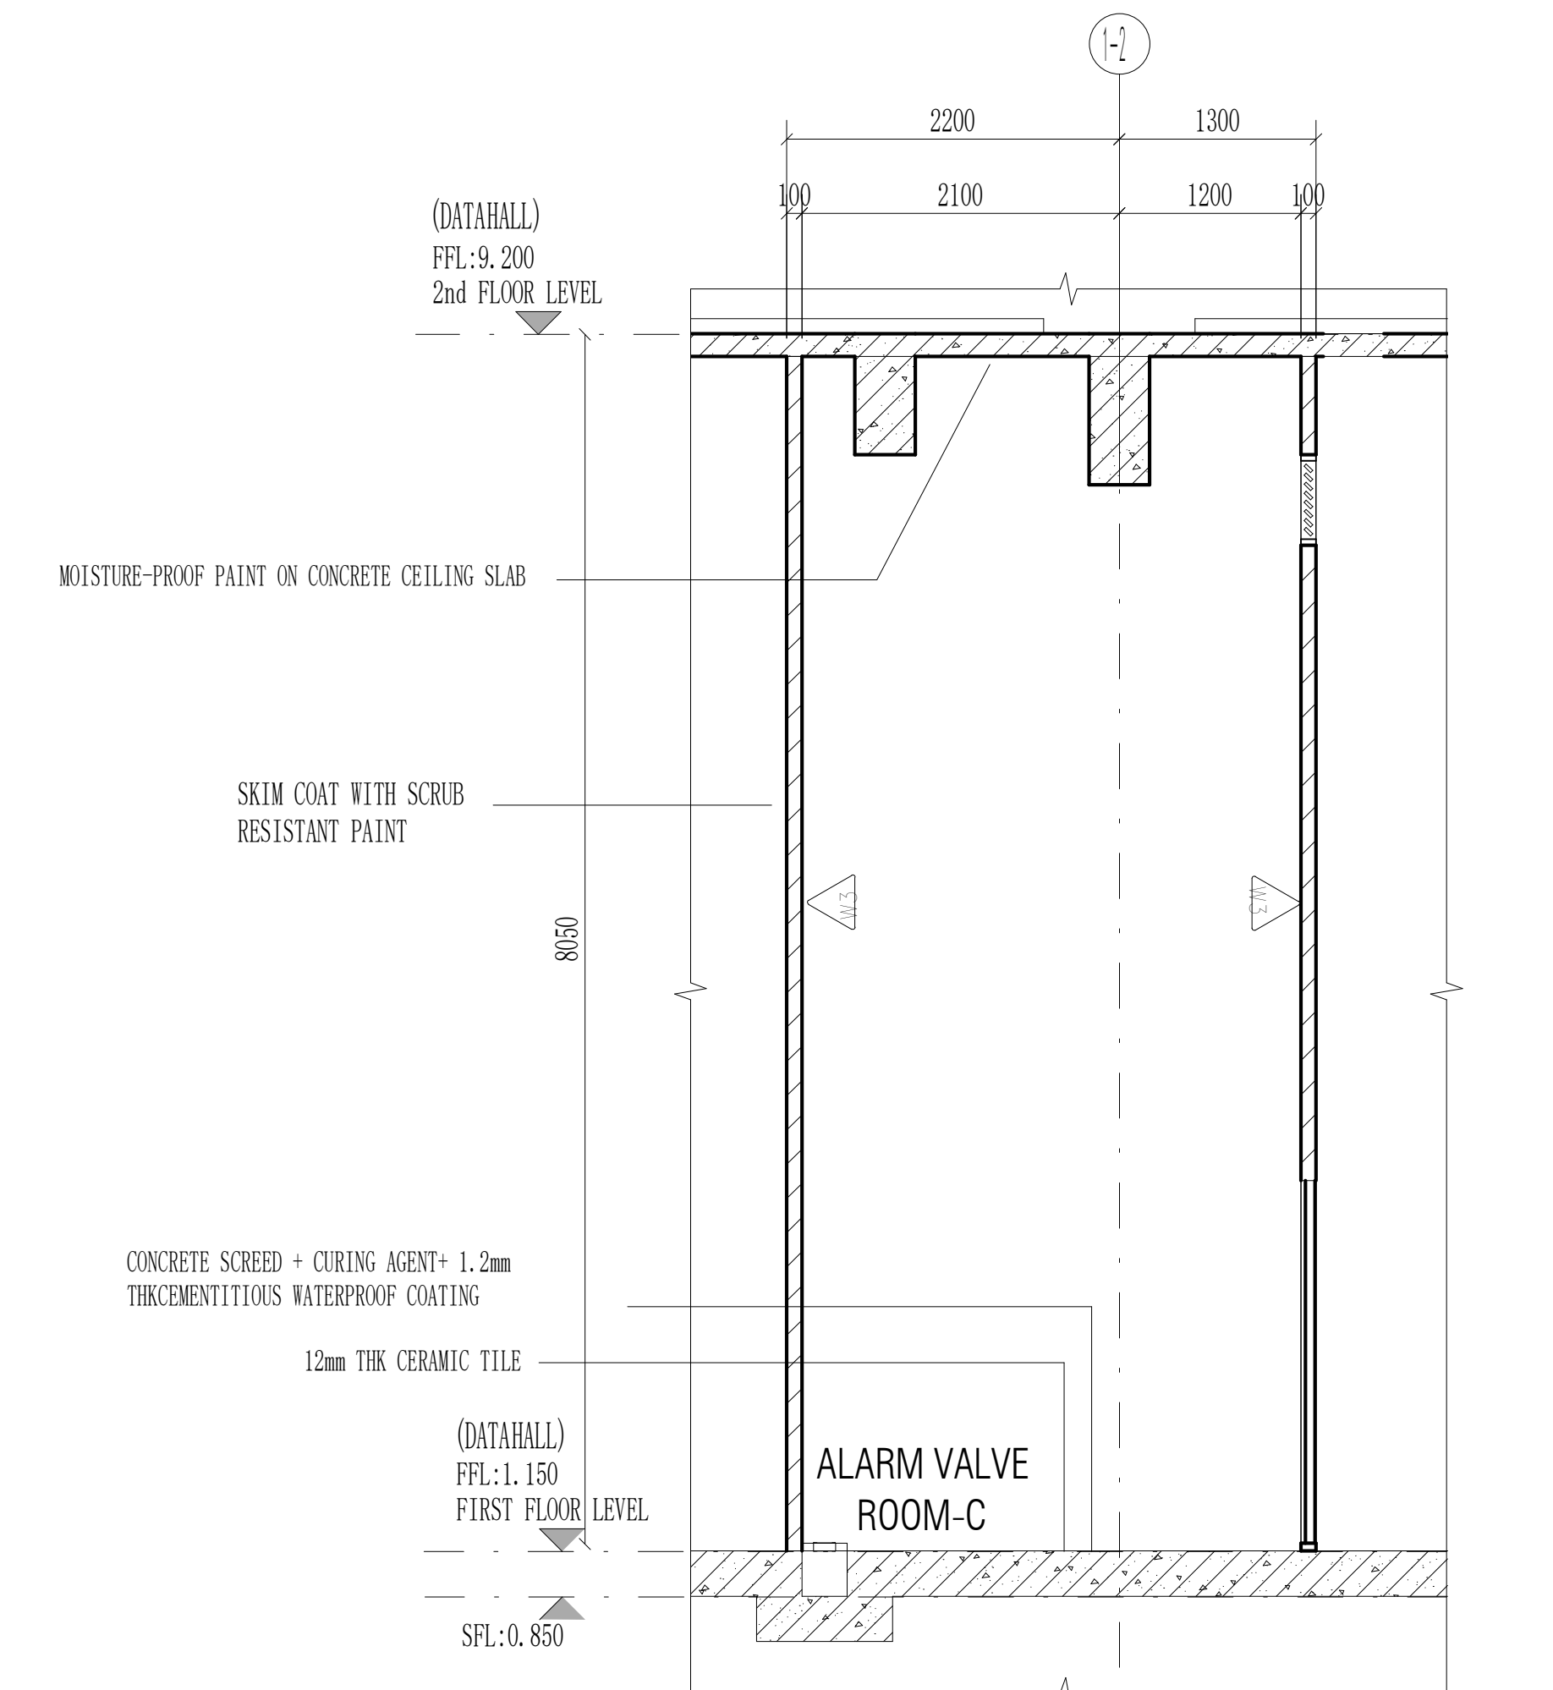
2200
1300
100
2100
1200
100
(DATAHALL)
FFL:9.200
2nd FLOOR LEVEL
MOISTURE-PROOF PAINT ON CONCRETE CEILING SLAB
SKIM COAT WITH SCRUB
RESISTANT PAINT
8650
CONCRETE SCREED + CURING AGENT+ 1.2mm
THKCEMENTITIOUS WATERPROOF COATING
12mm THK CERAMIC TILE
(DATAHALL)
FFL:1.150
FIRST FLOOR LEVEL
SFL:0.850
ALARM VALVE ROOM-C

ALARM VALVE ROOM SECTION B-B

Scale 1:50

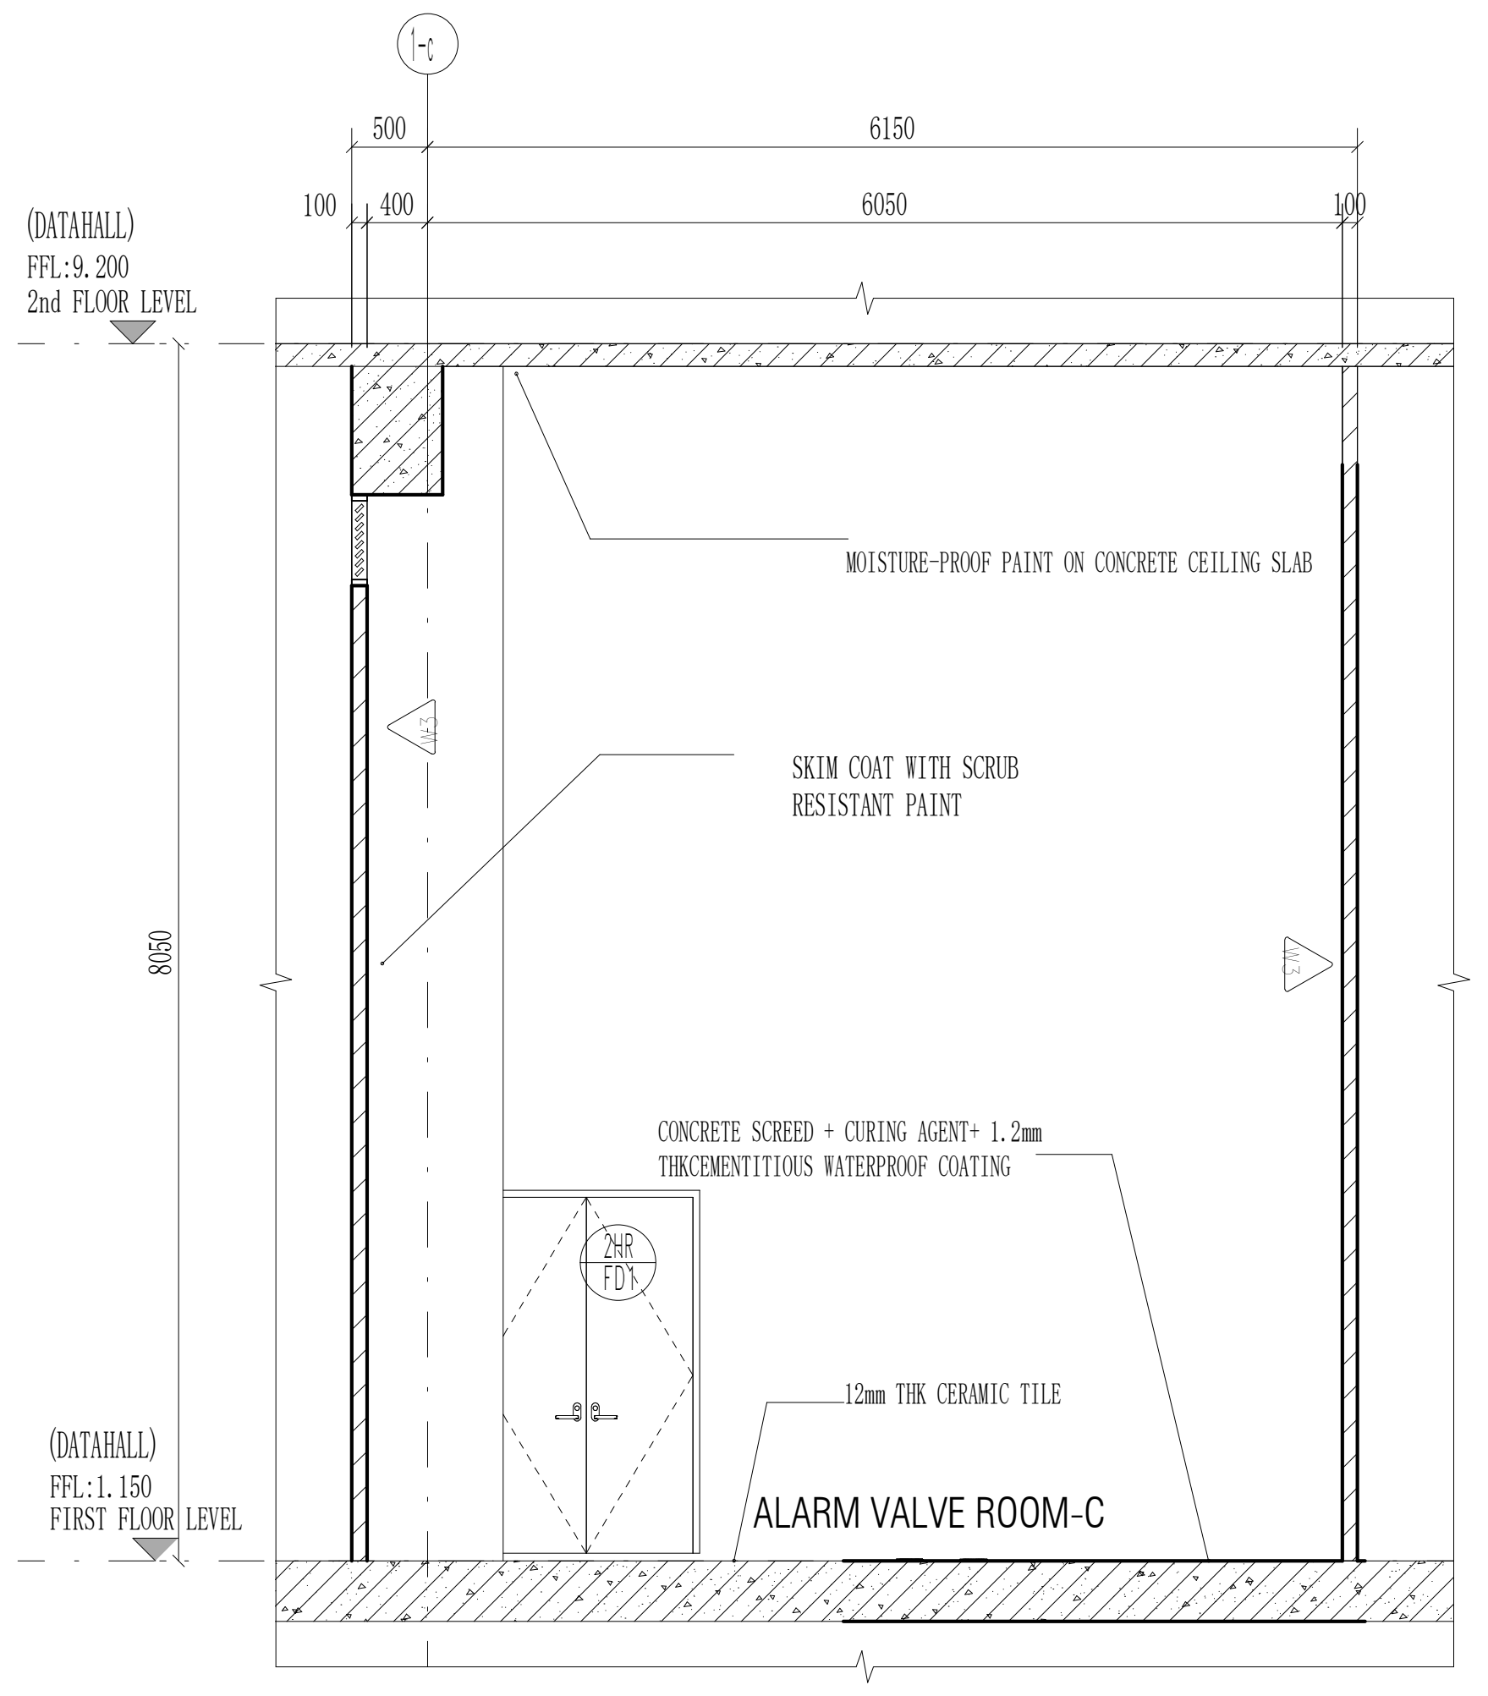
500
6150
100
400
6050
(DATAHALL)
FFL:9.200
2nd FLOOR LEVEL
MOISTURE-PROOF PAINT ON CONCRETE CEILING SLAB
SKIM COAT WITH SCRUB
RESISTANT PAINT
8650
CONCRETE SCREED + CURING AGENT+ 1.2mm
THKCEMENTITIOUS WATERPROOF COATING
12mm THK CERAMIC TILE
(DATAHALL)
FFL:1.150
FIRST FLOOR LEVEL
ALARM VALVE ROOM-C

ALARM VALVE ROOM SECTION A-A

Scale 1:50

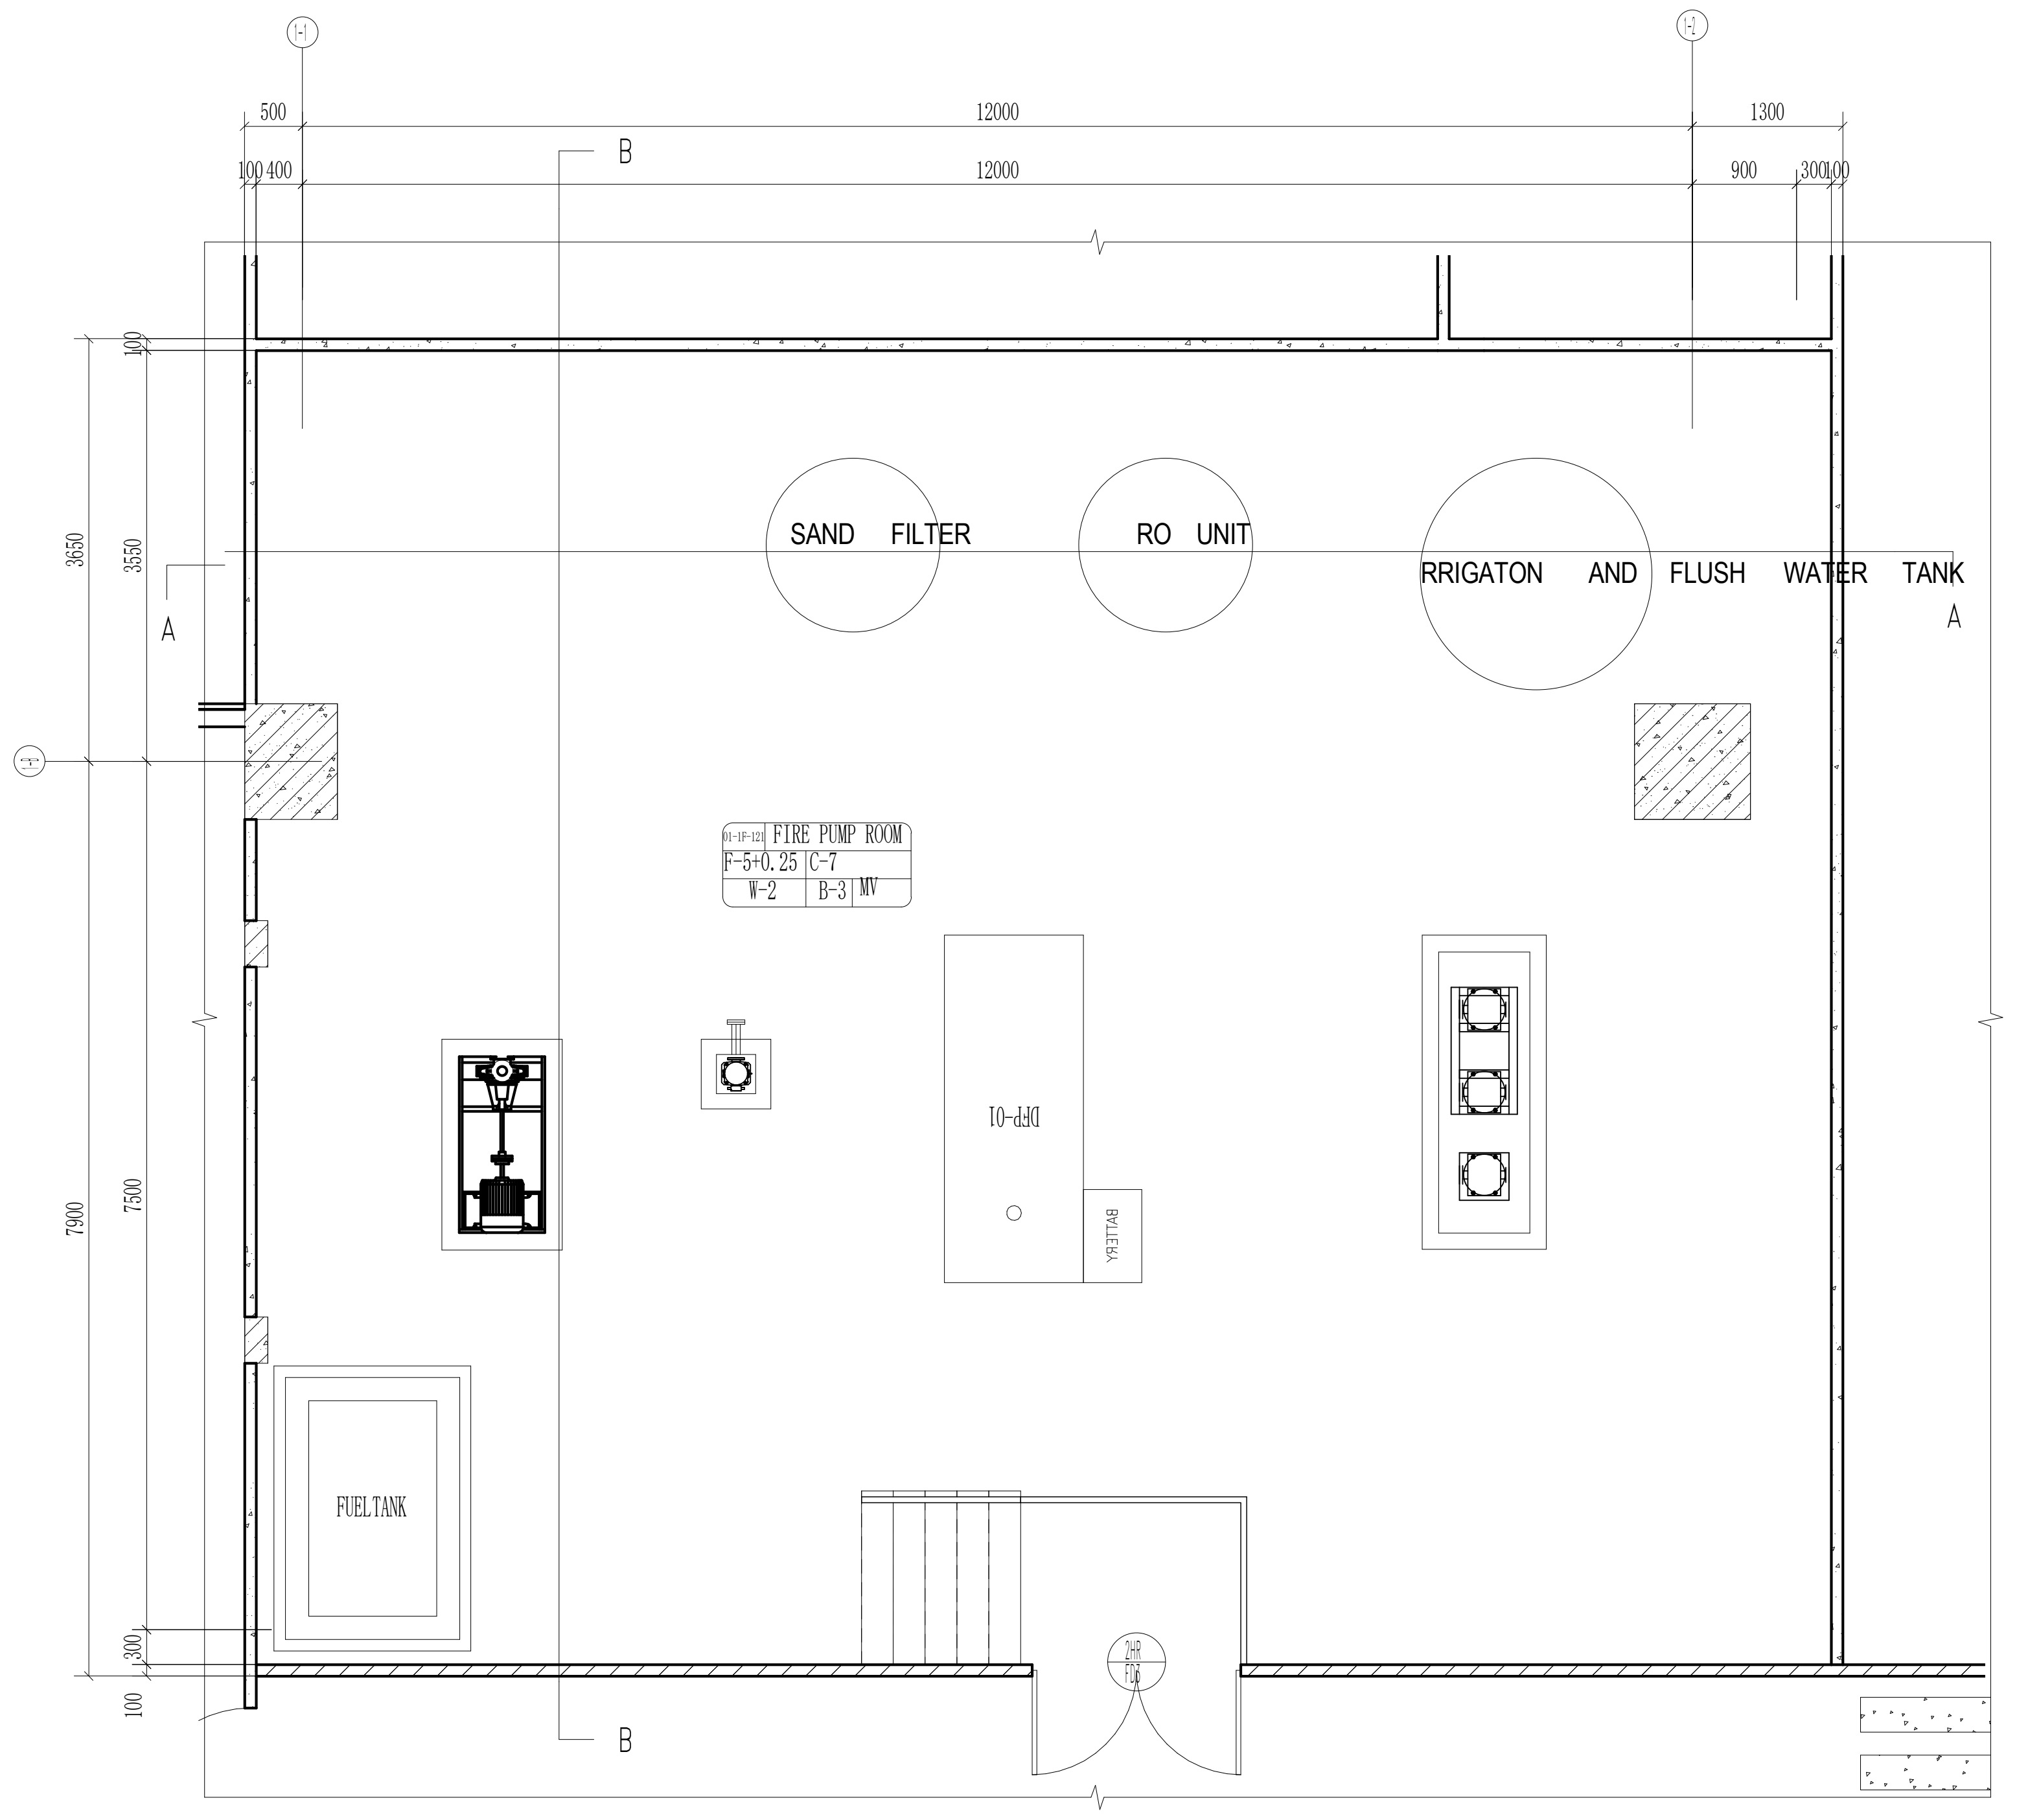
500
12000
1300
100
400
12000
900
300
100
B
3650
3550
A
A
SAND FILTER
RO UNIT
RRIGATON AND FLUSH WATER TANK
FIRE PUMP ROOM
F-5=0.25
C-7
W-2
B-3
7900
7500
FUELTANK
B

FIRE PUMP ROOMPUMP ROOM FLOOR PLAN

Scale 1:50

THE "SFL" MARKED IN THE DRAWING REFERS TO THE STRUCTURAL FLOOR LEVEL, WHILE THE FINISHED FLOOR LEVEL (FFL) IS DETERMINED BASED ON FLOOR FINISHES.

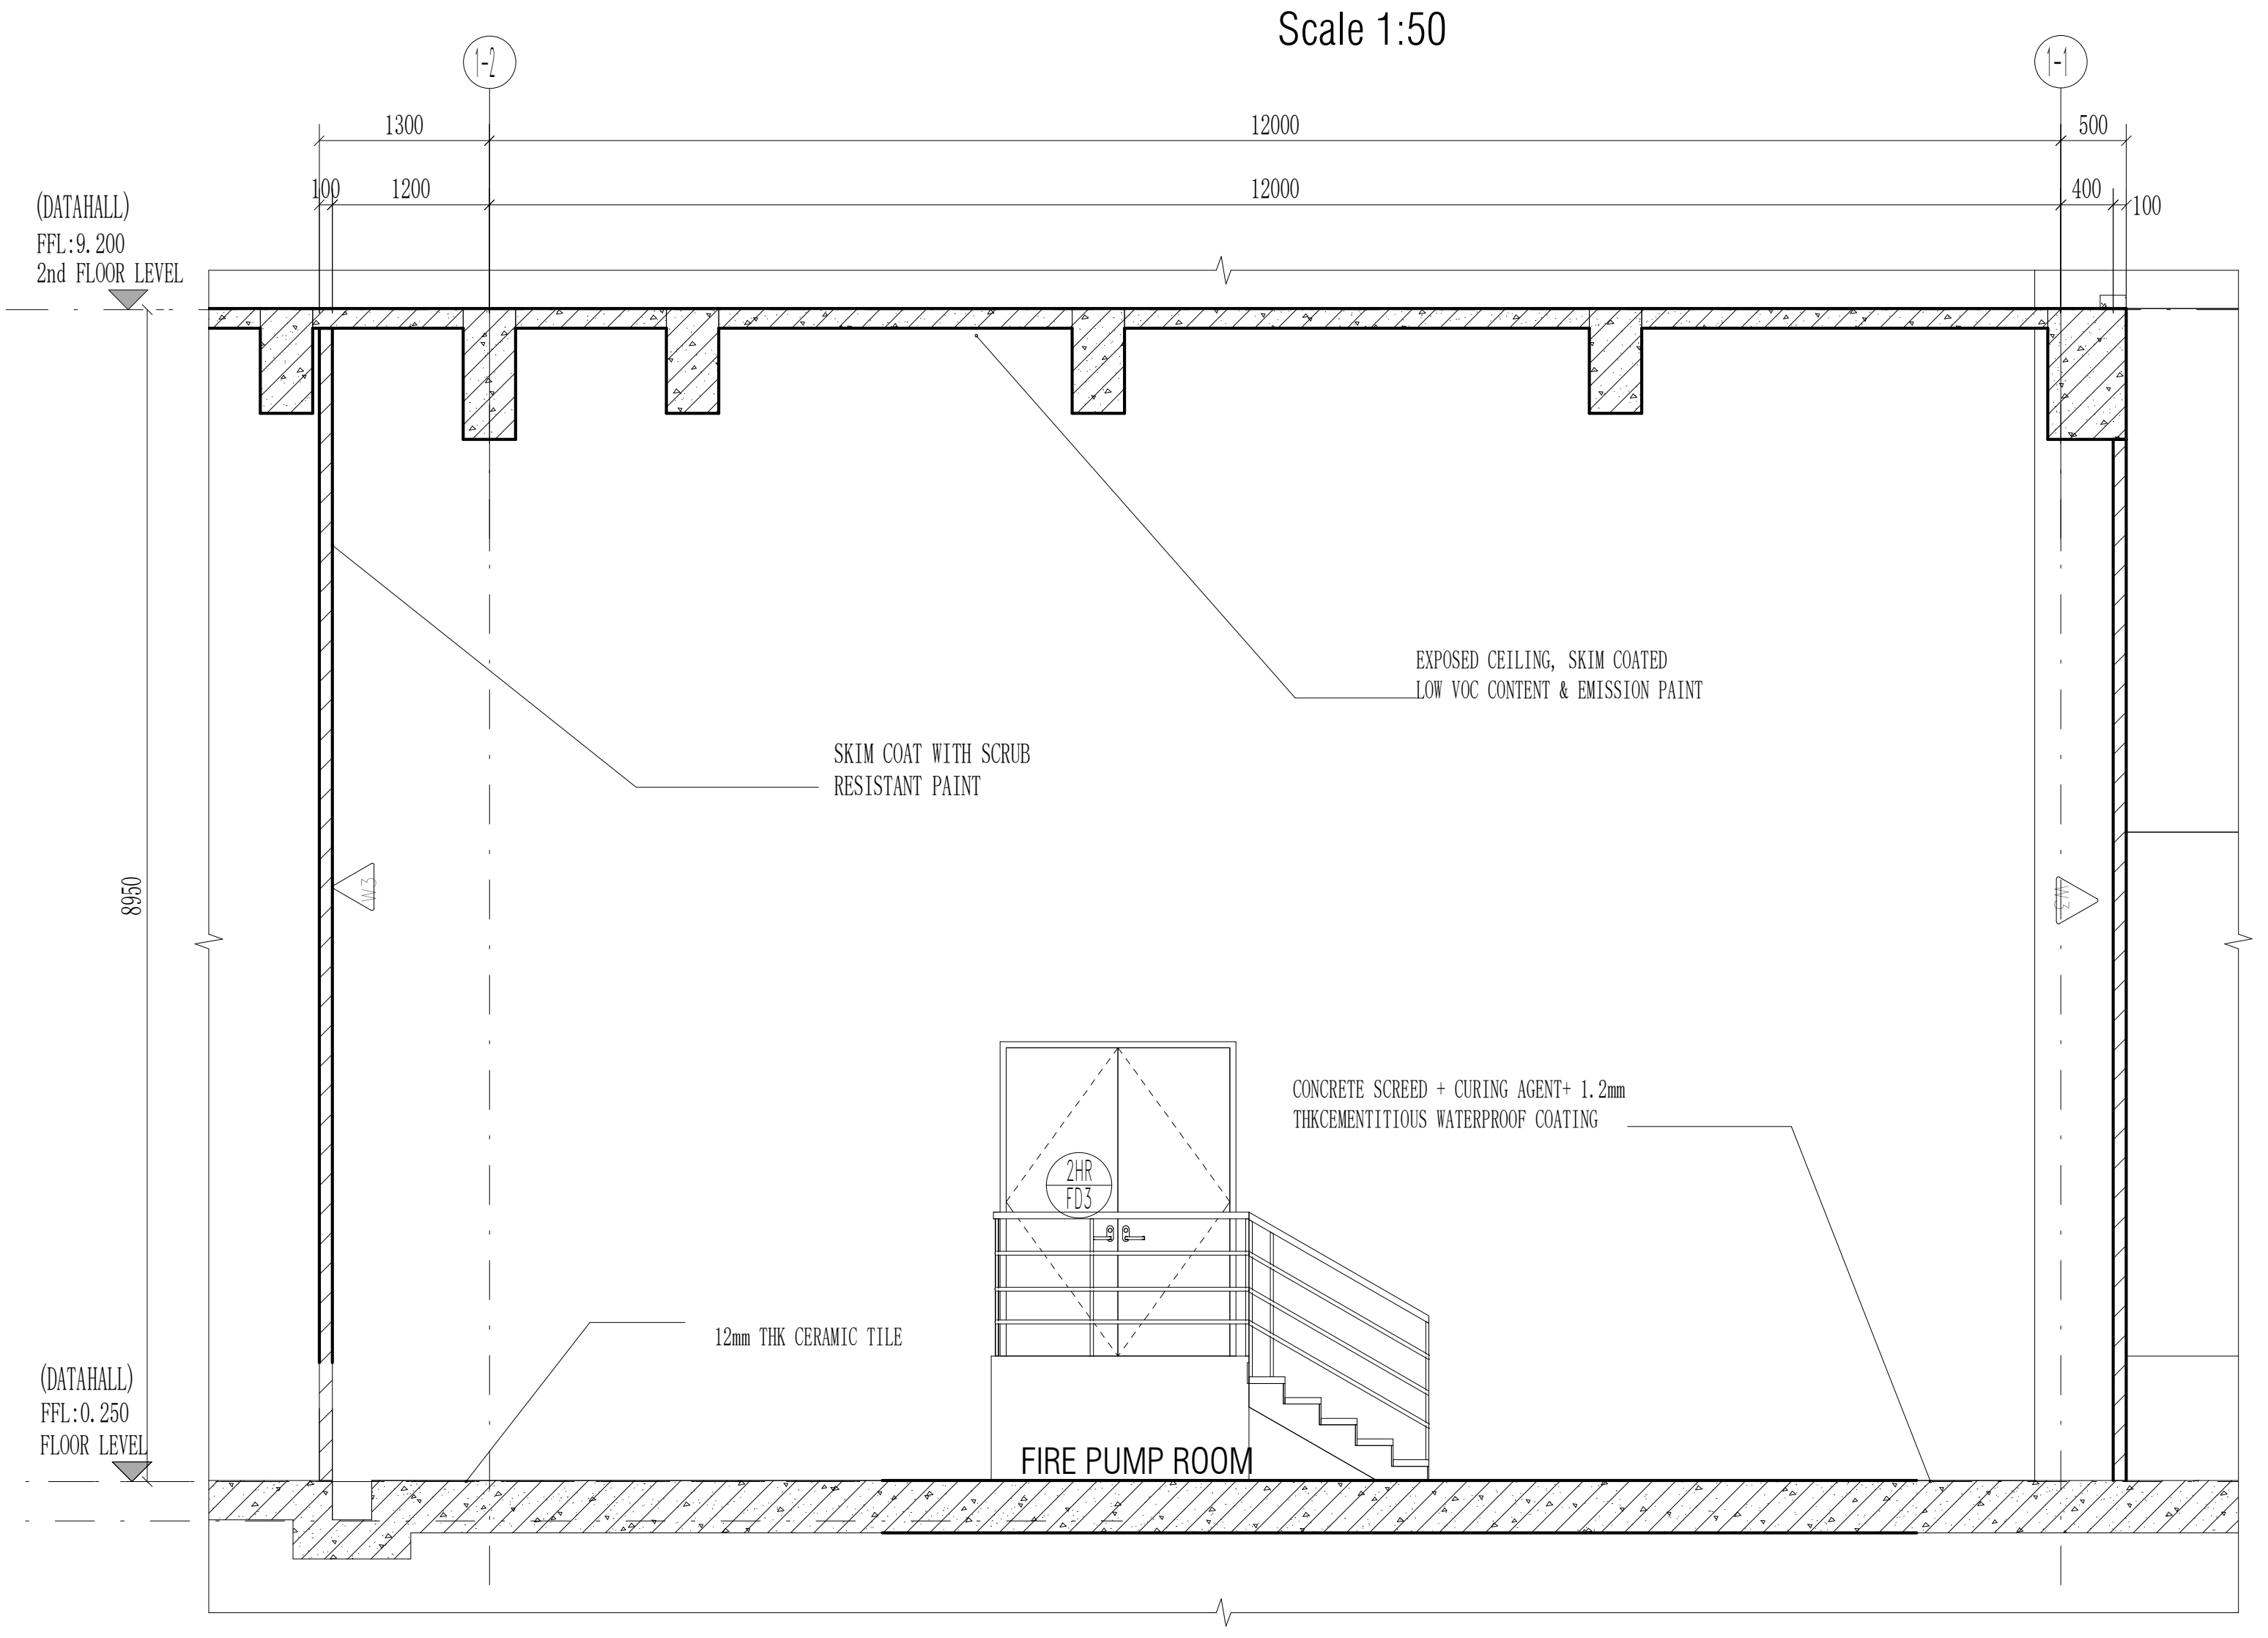
1300
12000
500
100
1200
12000
400
100
(DATAHALL)
FFL:9.200
2nd FLOOR LEVEL
EXPOSED CEILING, SKIM COATED
LOW VOC CONTENT & EMISSION PAINT
SKIM COAT WITH SCRUB
RESISTANT PAINT
8650
CONCRETE SCREED + CURING AGENT+ 1.2mm
THKCEMENTITIOUS WATERPROOF COATING
12mm THK CERAMIC TILE
(DATAHALL)
FFL:0.250
FLOOR LEVEL
FIRE PUMP ROOM

FIRE PUMP ROOMPUMP ROOM SECTIONA-A

Scale 1:50

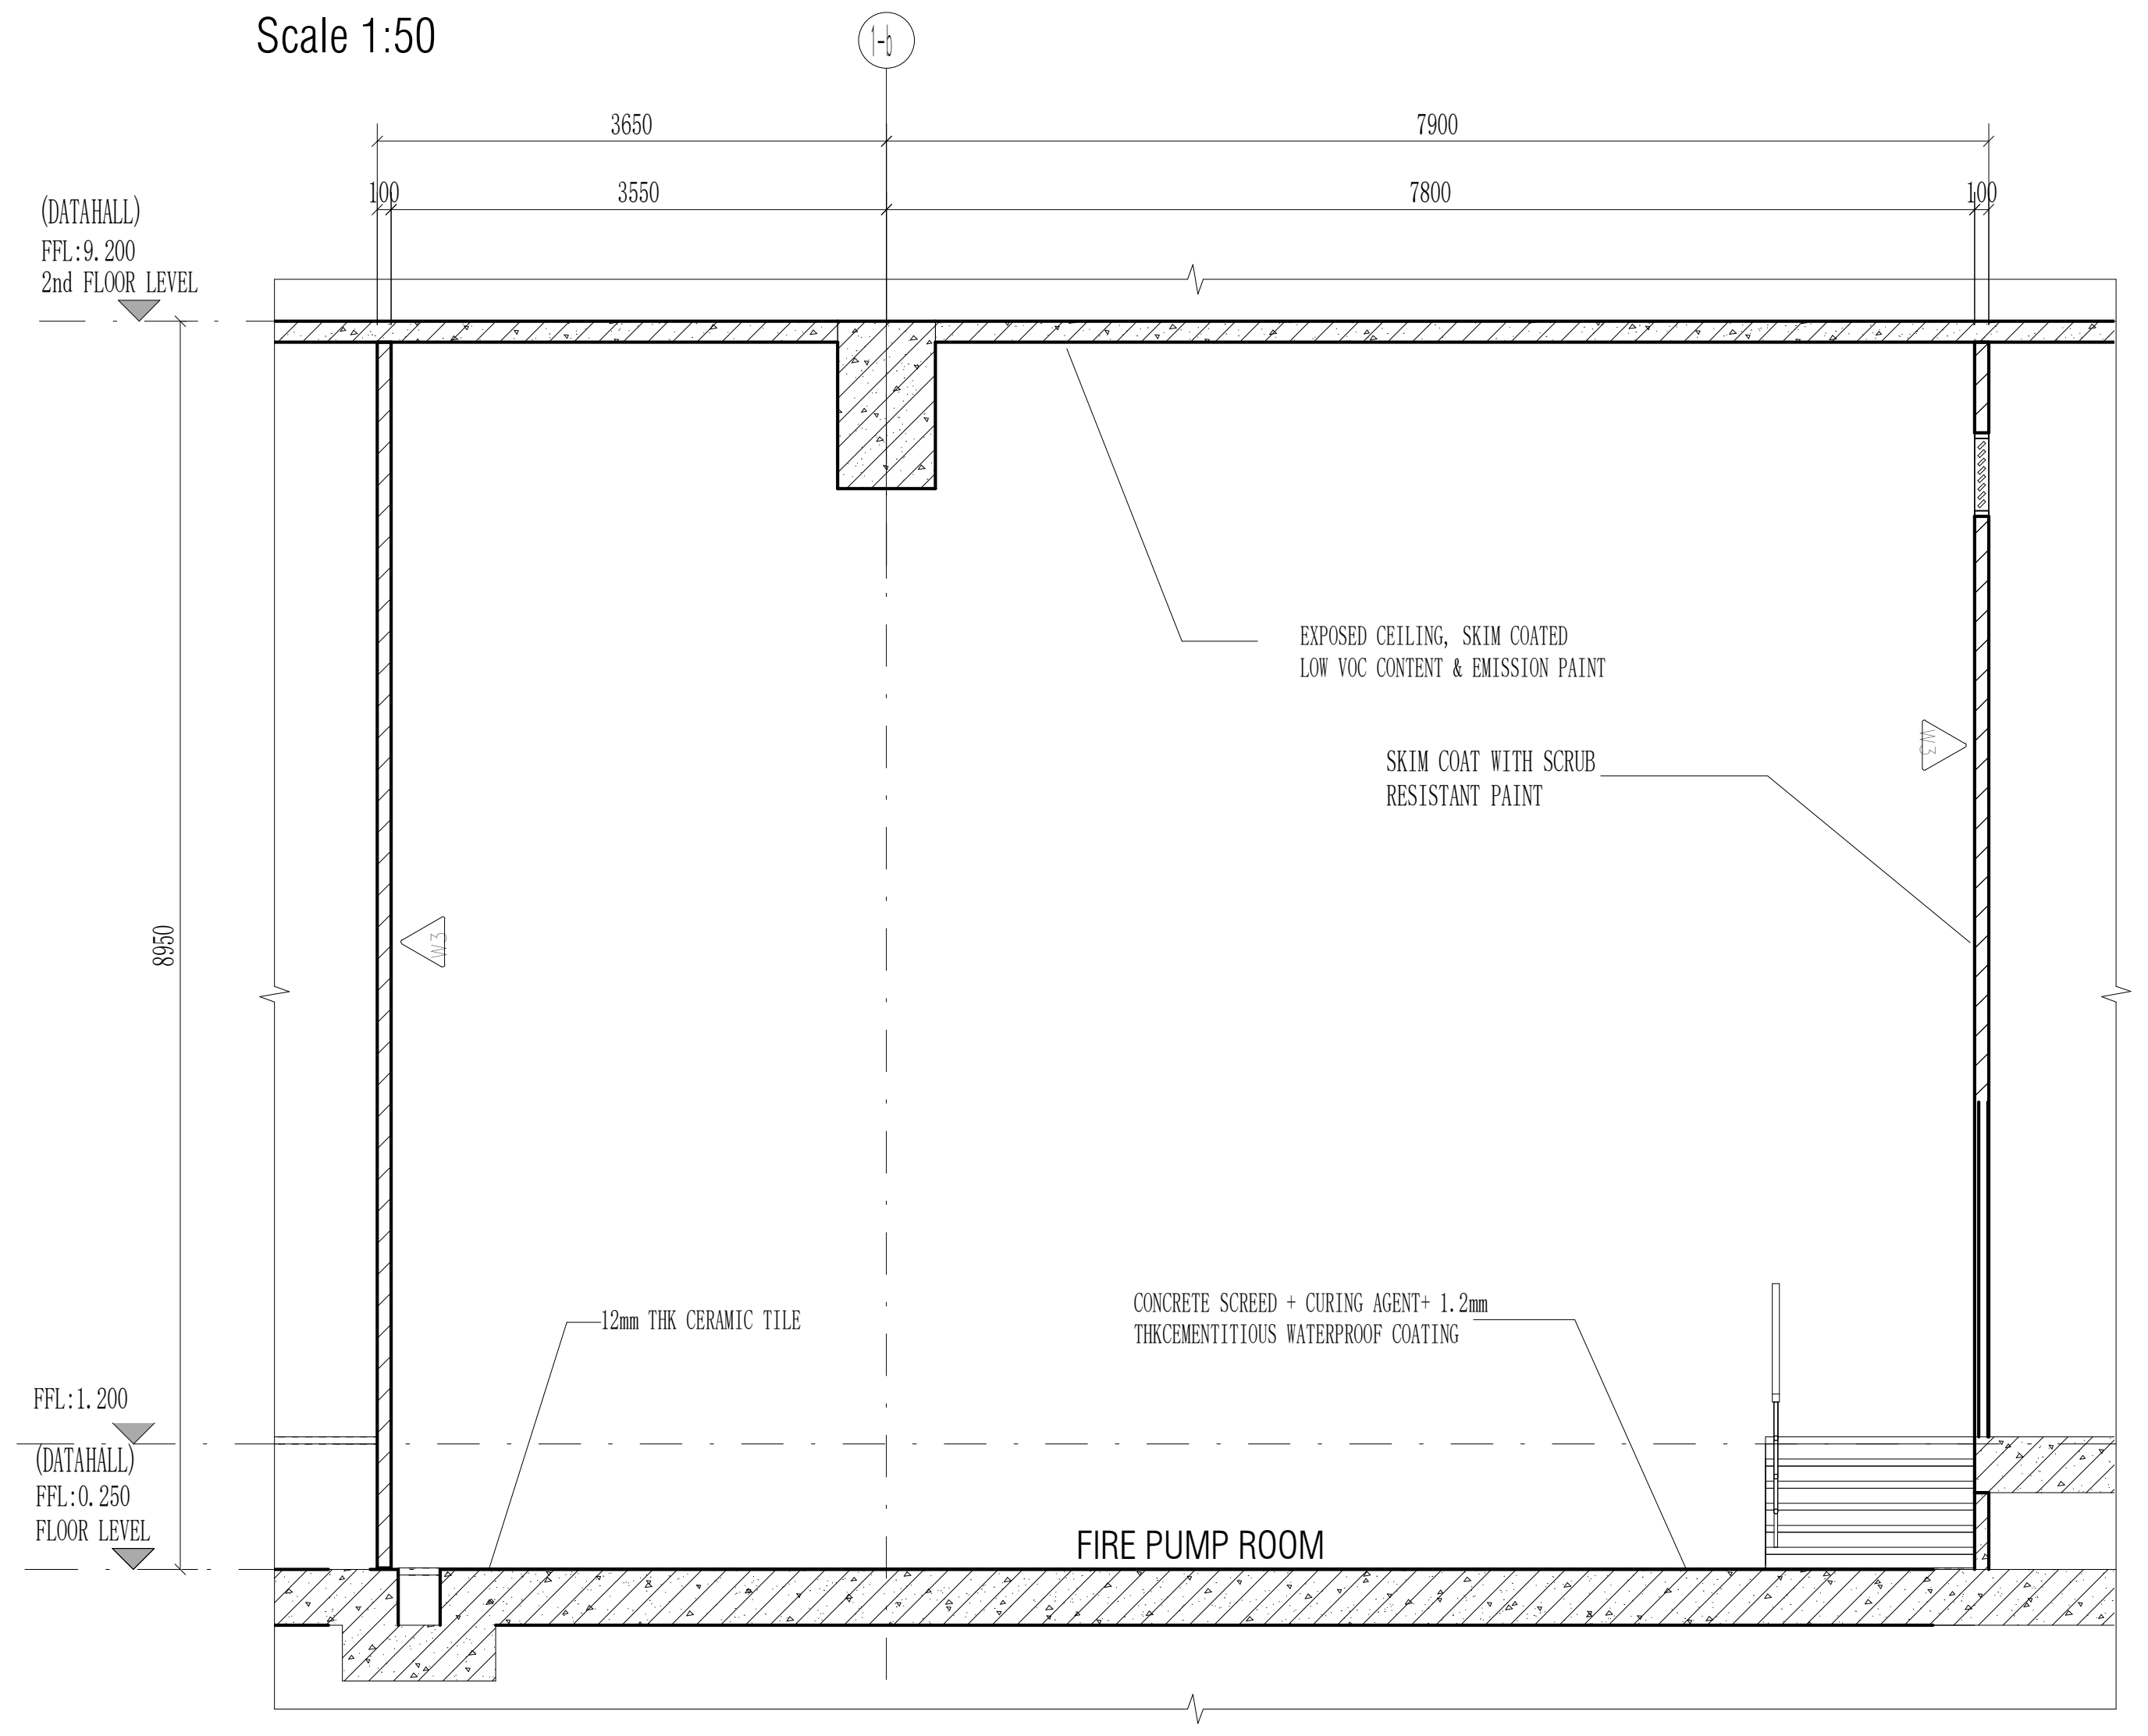
3650
7900
100
3550
7800
100
(DATAHALL)
FFL:9.200
2nd FLOOR LEVEL
EXPOSED CEILING, SKIM COATED
LOW VOC CONTENT & EMISSION PAINT
SKIM COAT WITH SCRUB
RESISTANT PAINT
8650
12mm THK CERAMIC TILE
CONCRETE SCREED + CURING AGENT+ 1.2mm
THKCEMENTITIOUS WATERPROOF COATING
FFL:1.200
(DATAHALL)
FFL:0.250
FLOOR LEVEL
FIRE PUMP ROOM

FIRE PUMP ROOMPUMP ROOM SECTIONB-B

Scale 1:50

CLIENT :

GULF EDGE DC 01

87 Wireless Road, M Thai Tower 11th. Floor, All Seasons Place, Lumpini,
Pathumwan, Bangkok 10330, Thailand

CONTRACTOR :

华西发展(泰国)有限公司
บริษัท หัวซือ ดีเวลลอปเม้นต์ (ประเทศไทย) จำกัด
HUASHI DEVELOPMENT CO.,LTD
No. 202, Room No. 1403, 14/F, Le Concorde Building,
Ratchadapisek Road, Huaykhwang Sub-District,
Huaykhwang District, Bangkok Metropolitan 10310.

CONSULTANT :

ARbay
บริษัท เอ อาร์ เบย์ จำกัด
ARbay Company Limited
31 st Floor Bangkok Insurance Building
25 South Sathorn road Thungmahamek
Sathorn Bangkok 10120 THAILAND
T +66 (0) 2286 8199
F +66 (0) 2286 2863
info@arbay.co.th

CONSULTANT :

Qbic Engineers & Architects Co.,Ltd.
8 Soi KALONG 4 SANAMBINNAM ROAD,
THASAI SUB-DISTRICT, MUANG NONTHABURI DISTRICT
, NONTHABURI.
Tel 662-950-4374
Fax 662-580-3231
E-Mail : qbic@qbic.co.th, www.qbic.co.th
QBIC ENGINEERS AND ARCHITECTS CO.,LTD.

CONSULTANT :

MITR
MITR TECHNICAL CONSULTANT CO.,LTD.
1168/8 12th FLOOR, LUMPINI TOWER BUILDING,
RAMA IV RD., THUNGMAHAMEK, SATHORN, BANGKOK 10120, THAILAND
TEL : 0-2679-9079-84
FAX : 0-2679-9085 E-mail: mitr_dd@mitr.com

Architect :	SIGNATURE
ประกิต พนานุรัตน์ วสถ. 580 ที่อยู่ 251/1 ถ.จารุเมือง แขวงรองเมือง เขตปทุมวัน กรุงเทพมหานคร โทรศัพท์ 02-286-8199	
Structural Engineer :	SIGNATURE
วิศวกรผู้ออกแบบโครงสร้าง	
ณัฐสม สงวนวงษ์ วย 1423 ที่อยู่ 2/1 ซ.รามคำแหง 150 ถ.รามคำแหง แขวง สะพานสูง เขต สะพานสูง กทม. 10240	ณัฐสม สงวนวงษ์
Structural Inspector :	SIGNATURE
วิศวกรผู้ตรวจสอบโครงสร้าง	
โกมล จุฑาภัทร วย 964 ที่อยู่ 24/18 ซ.นวมินทร์ 129 ถ. นวมินทร์ แขวง นวลจันทร์ เขต บึงกุ่ม กทม. 10230	
Electrical Engineer :	SIGNATURE
วิศวกรผู้ออกแบบระบบไฟฟ้ากำลัง	
นายสุภัทร บูรณวิทย์ วฟก.1265 ที่อยู่ 21 ซอยทานสัมฤทธิ์ 13 ตำบลท่าทราย อ.เมืองนนทบุรี จ.นนทบุรี 11000	
Mechanical Engineer :	SIGNATURE
วิศวกรผู้ออกแบบระบบเครื่องกลและปรับอากาศ	
นายประสิทธิ์ เกี้ยวสุนทร วก.1221 ที่อยู่ 44/372 ซอยบางกระดี่ 35/1 แขวงแสมดำ เขตบางขุนเทียน กทม. 10150	ประสิทธิ์
Sanitary Engineer :	SIGNATURE
วิศวกรผู้ออกแบบระบบสุขาภิบาล และดับเพลิง	
นายทศวรรษ สนั่นฤทธิ์ วส. 215 ที่อยู่ บ้านเลขที่ 99/107 หมู่ที่ 3 ต.ศีรษะจรเข้น้อย อ.บางเสาธง จ.สมุทรปราการ 10540	ทศวรรษ

ISSUE/REVISION

REV.	DESCRIPTION	DATE
A	90% DEVELOPED	09/05/2026

PROJECT NAME :

GEDC 01

LOCATION:
Nikhom Phattana district, Rayong ,industrial estate,CPGC

BUILDING :
MAIN BUILDING

90% DEVELOPED

TITLE :

ROOM DETAIL-1F-DOMESTICWATER PUMP ROOM ALARM VALVE ROOM,FIRE PUMP ROOM

JOB NO.	SCALE 1 : 50
DRAWN LYT	REF.
CHECKED LJC	DWG. NO. MPK01A-90-A-RD-120
APPROVED LXD	
DATE 2026.05.09	

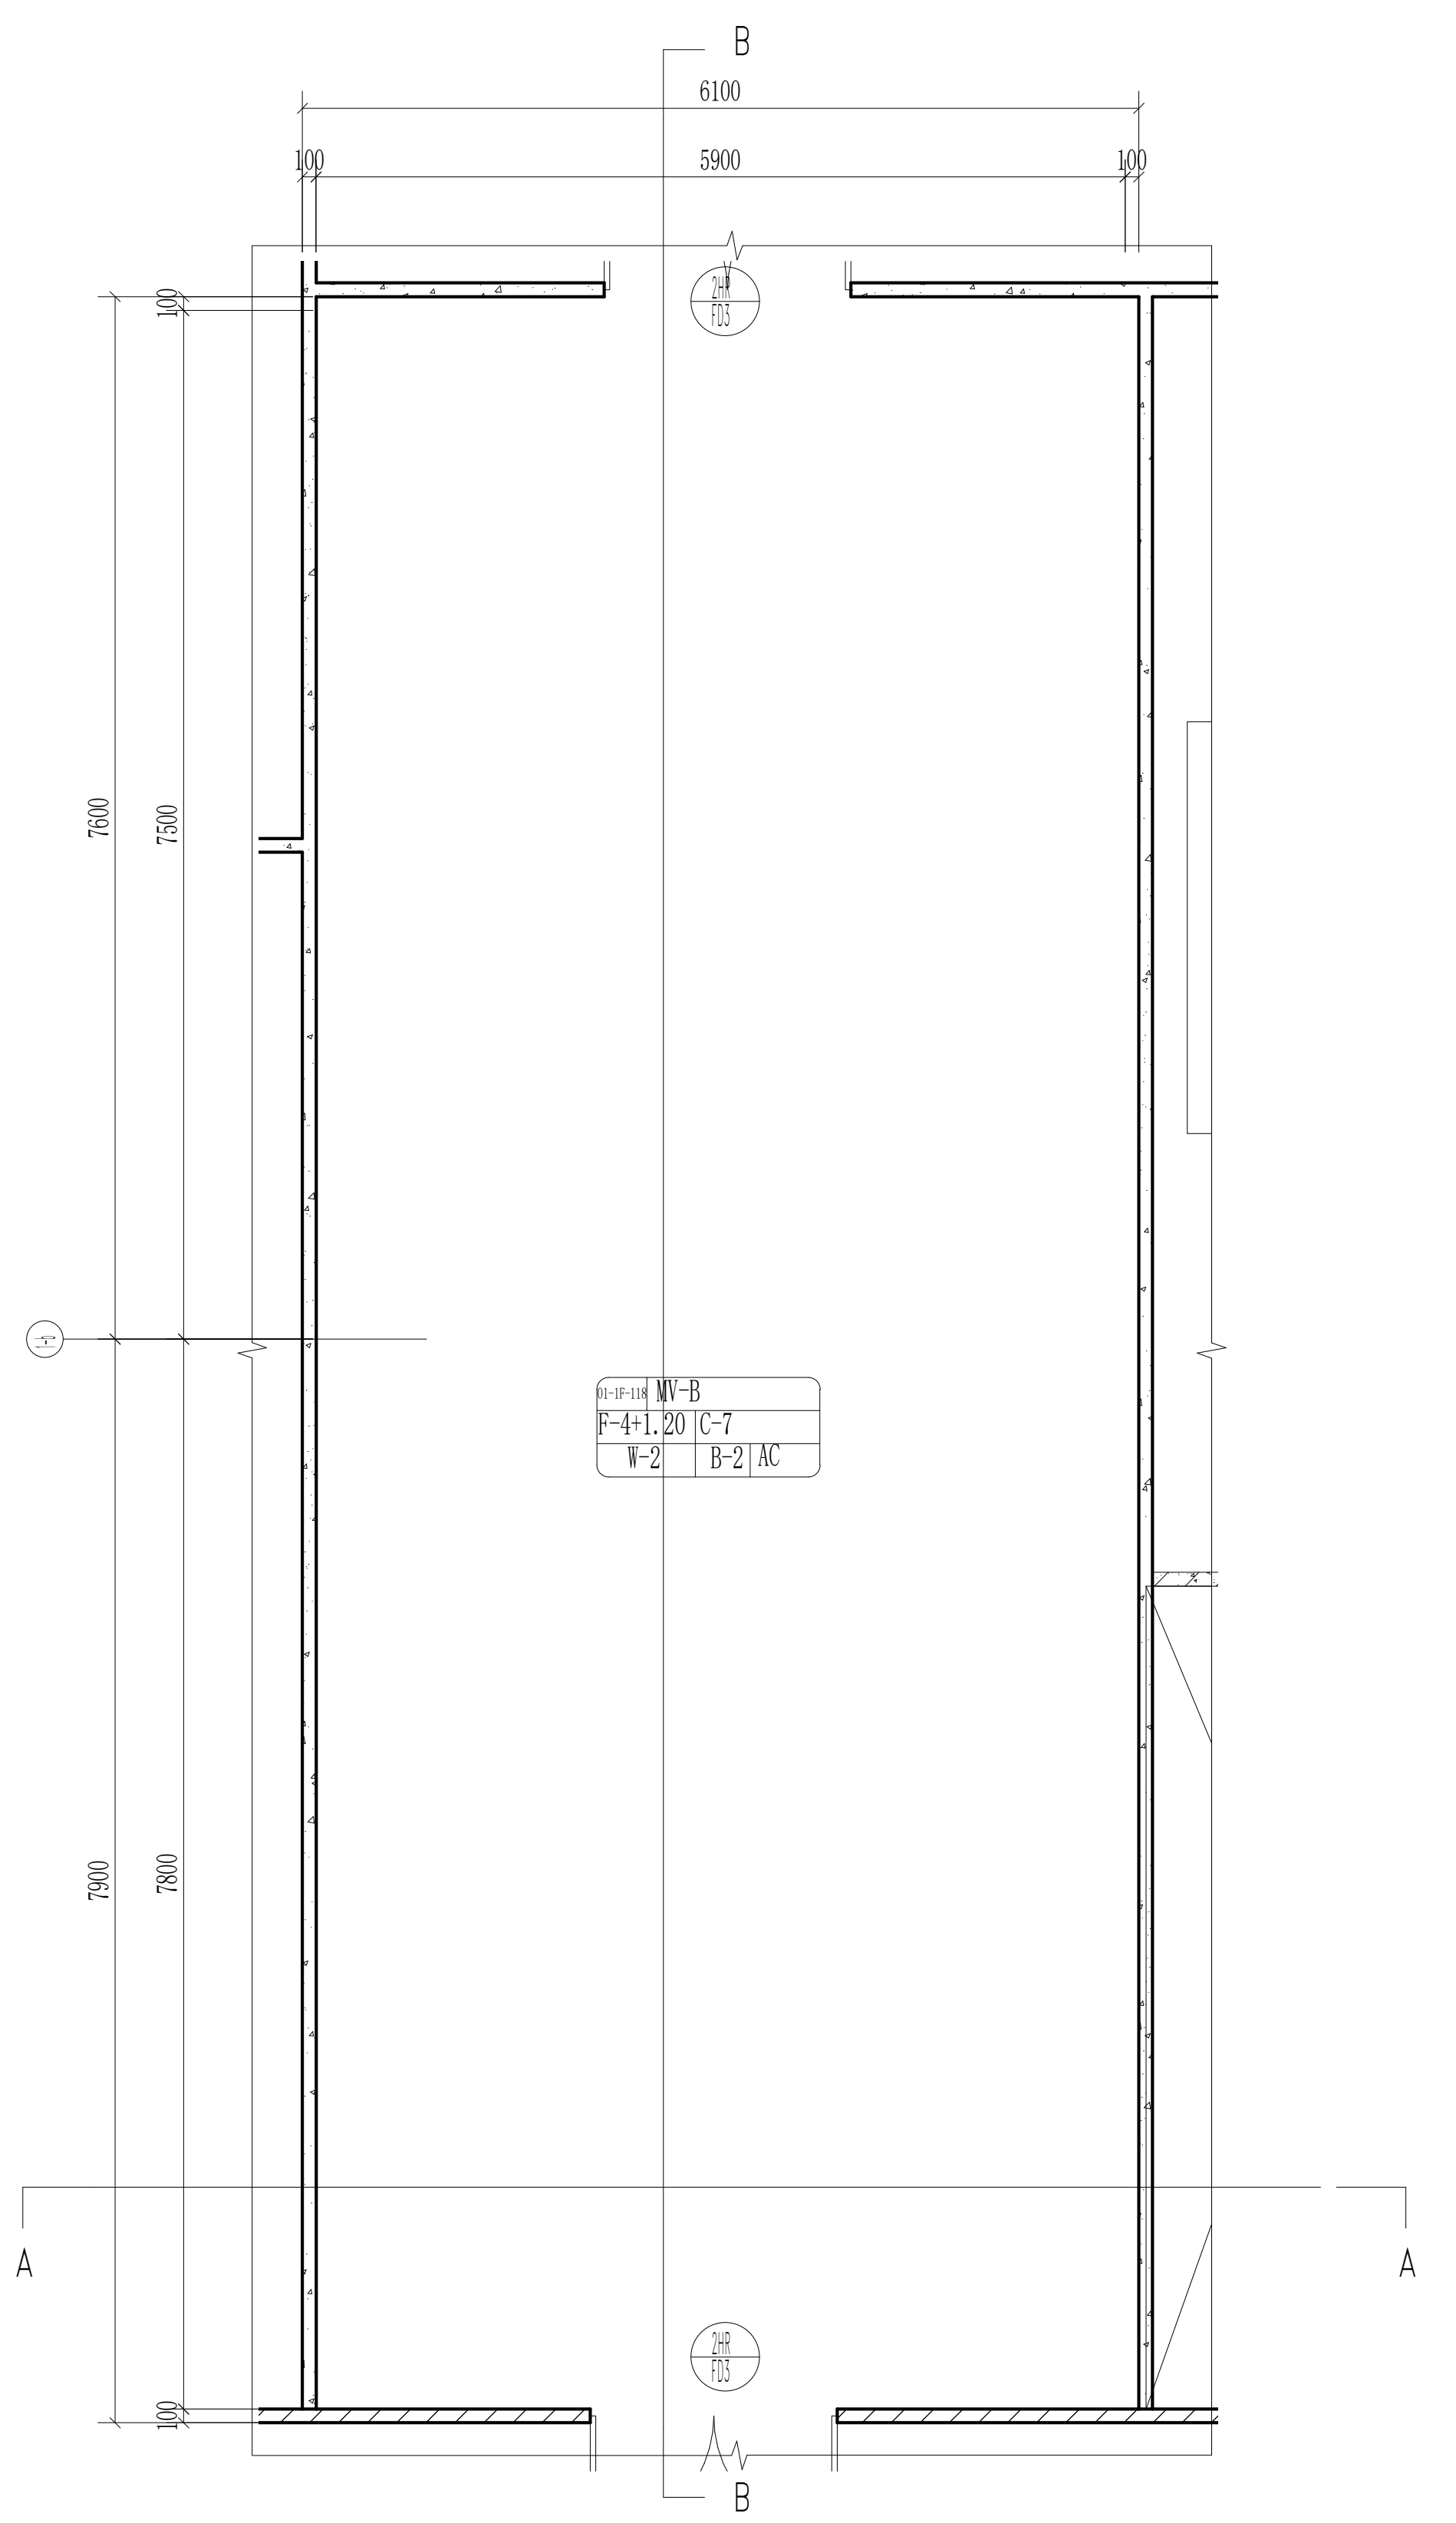

B
6100
100
5900
100
7500
7300
7900
7800
100
01-1F-118
MV-B
F-4+1.20
C-7
W-2
B-2
AC
A
A
B
FD3

MV-B FLOOR PLAN Scale 1:50

THE "SFL" MARKED IN THE DRAWING REFERS TO THE STRUCTURAL FLOOR LEVEL, WHILE THE FINISHED FLOOR LEVEL (FFL) IS DETERMINED BASED ON FLOOR FINISHES.

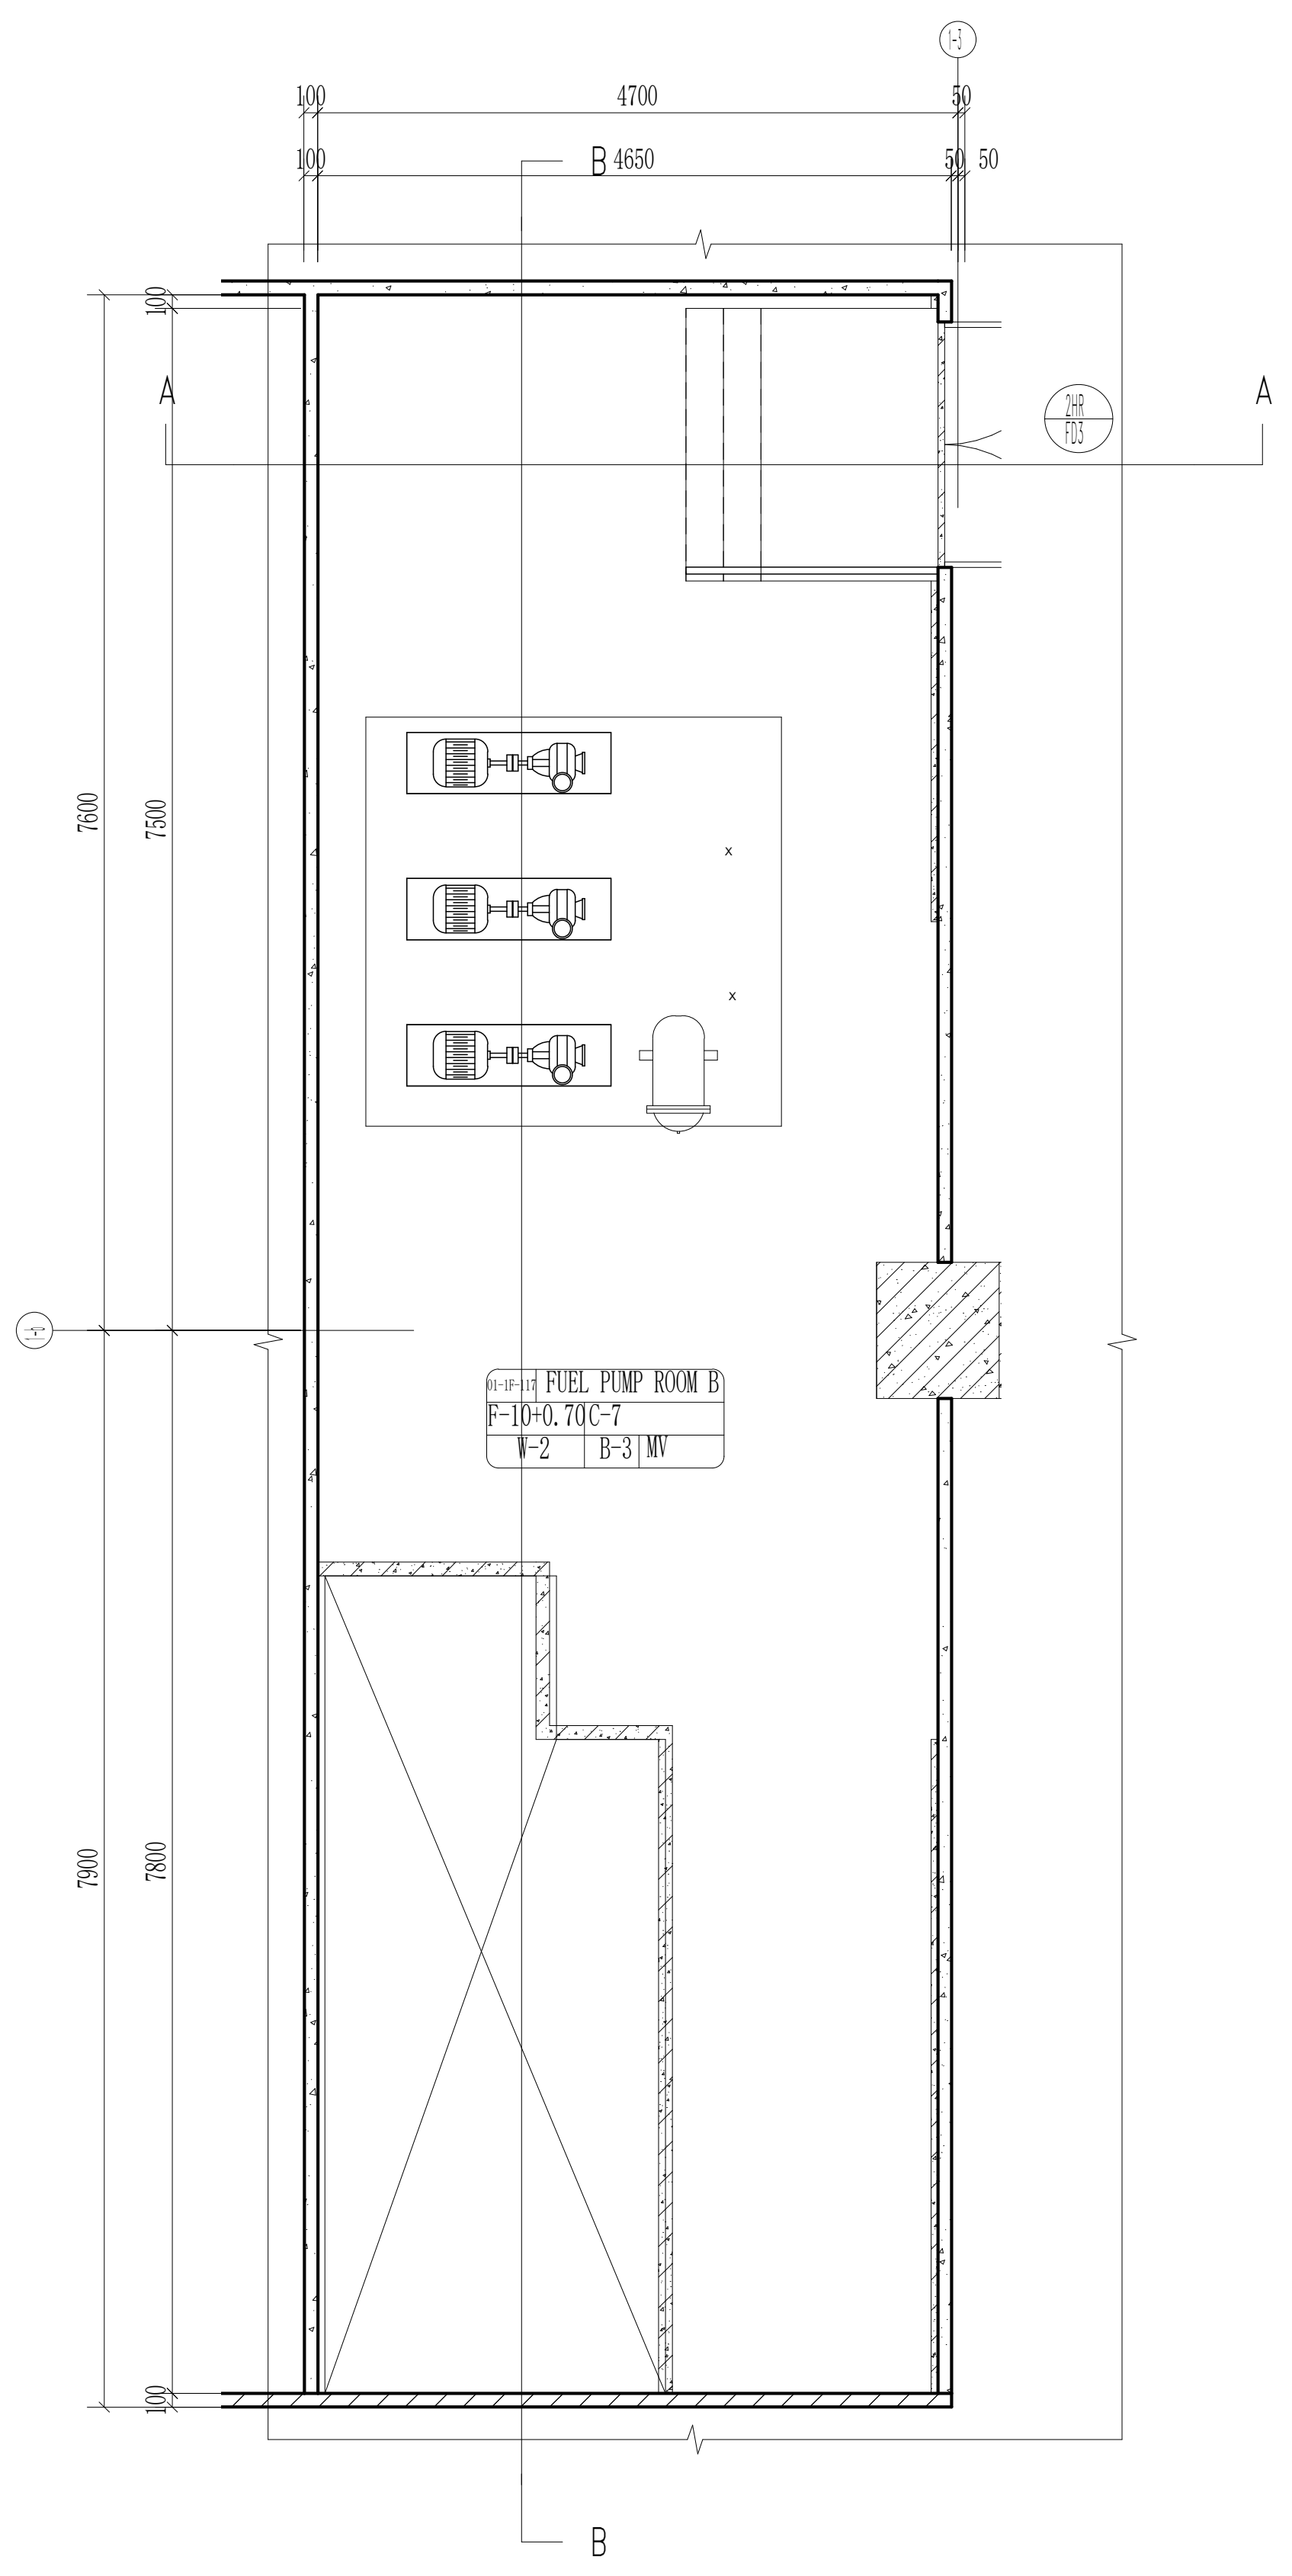

100
4700
50
100
B 4650
50
50
A
A
7500
7300
7900
7800
100
01-1F-117
FUEL PUMP ROOM B
F-10+0.70
C-7
W-2
B-3
MV
B

FUEL PUMP ROOM B FLOOR PLAN Scale 1:50

THE "SFL" MARKED IN THE DRAWING REFERS TO THE STRUCTURAL FLOOR LEVEL, WHILE THE FINISHED FLOOR LEVEL (FFL) IS DETERMINED BASED ON FLOOR FINISHES.

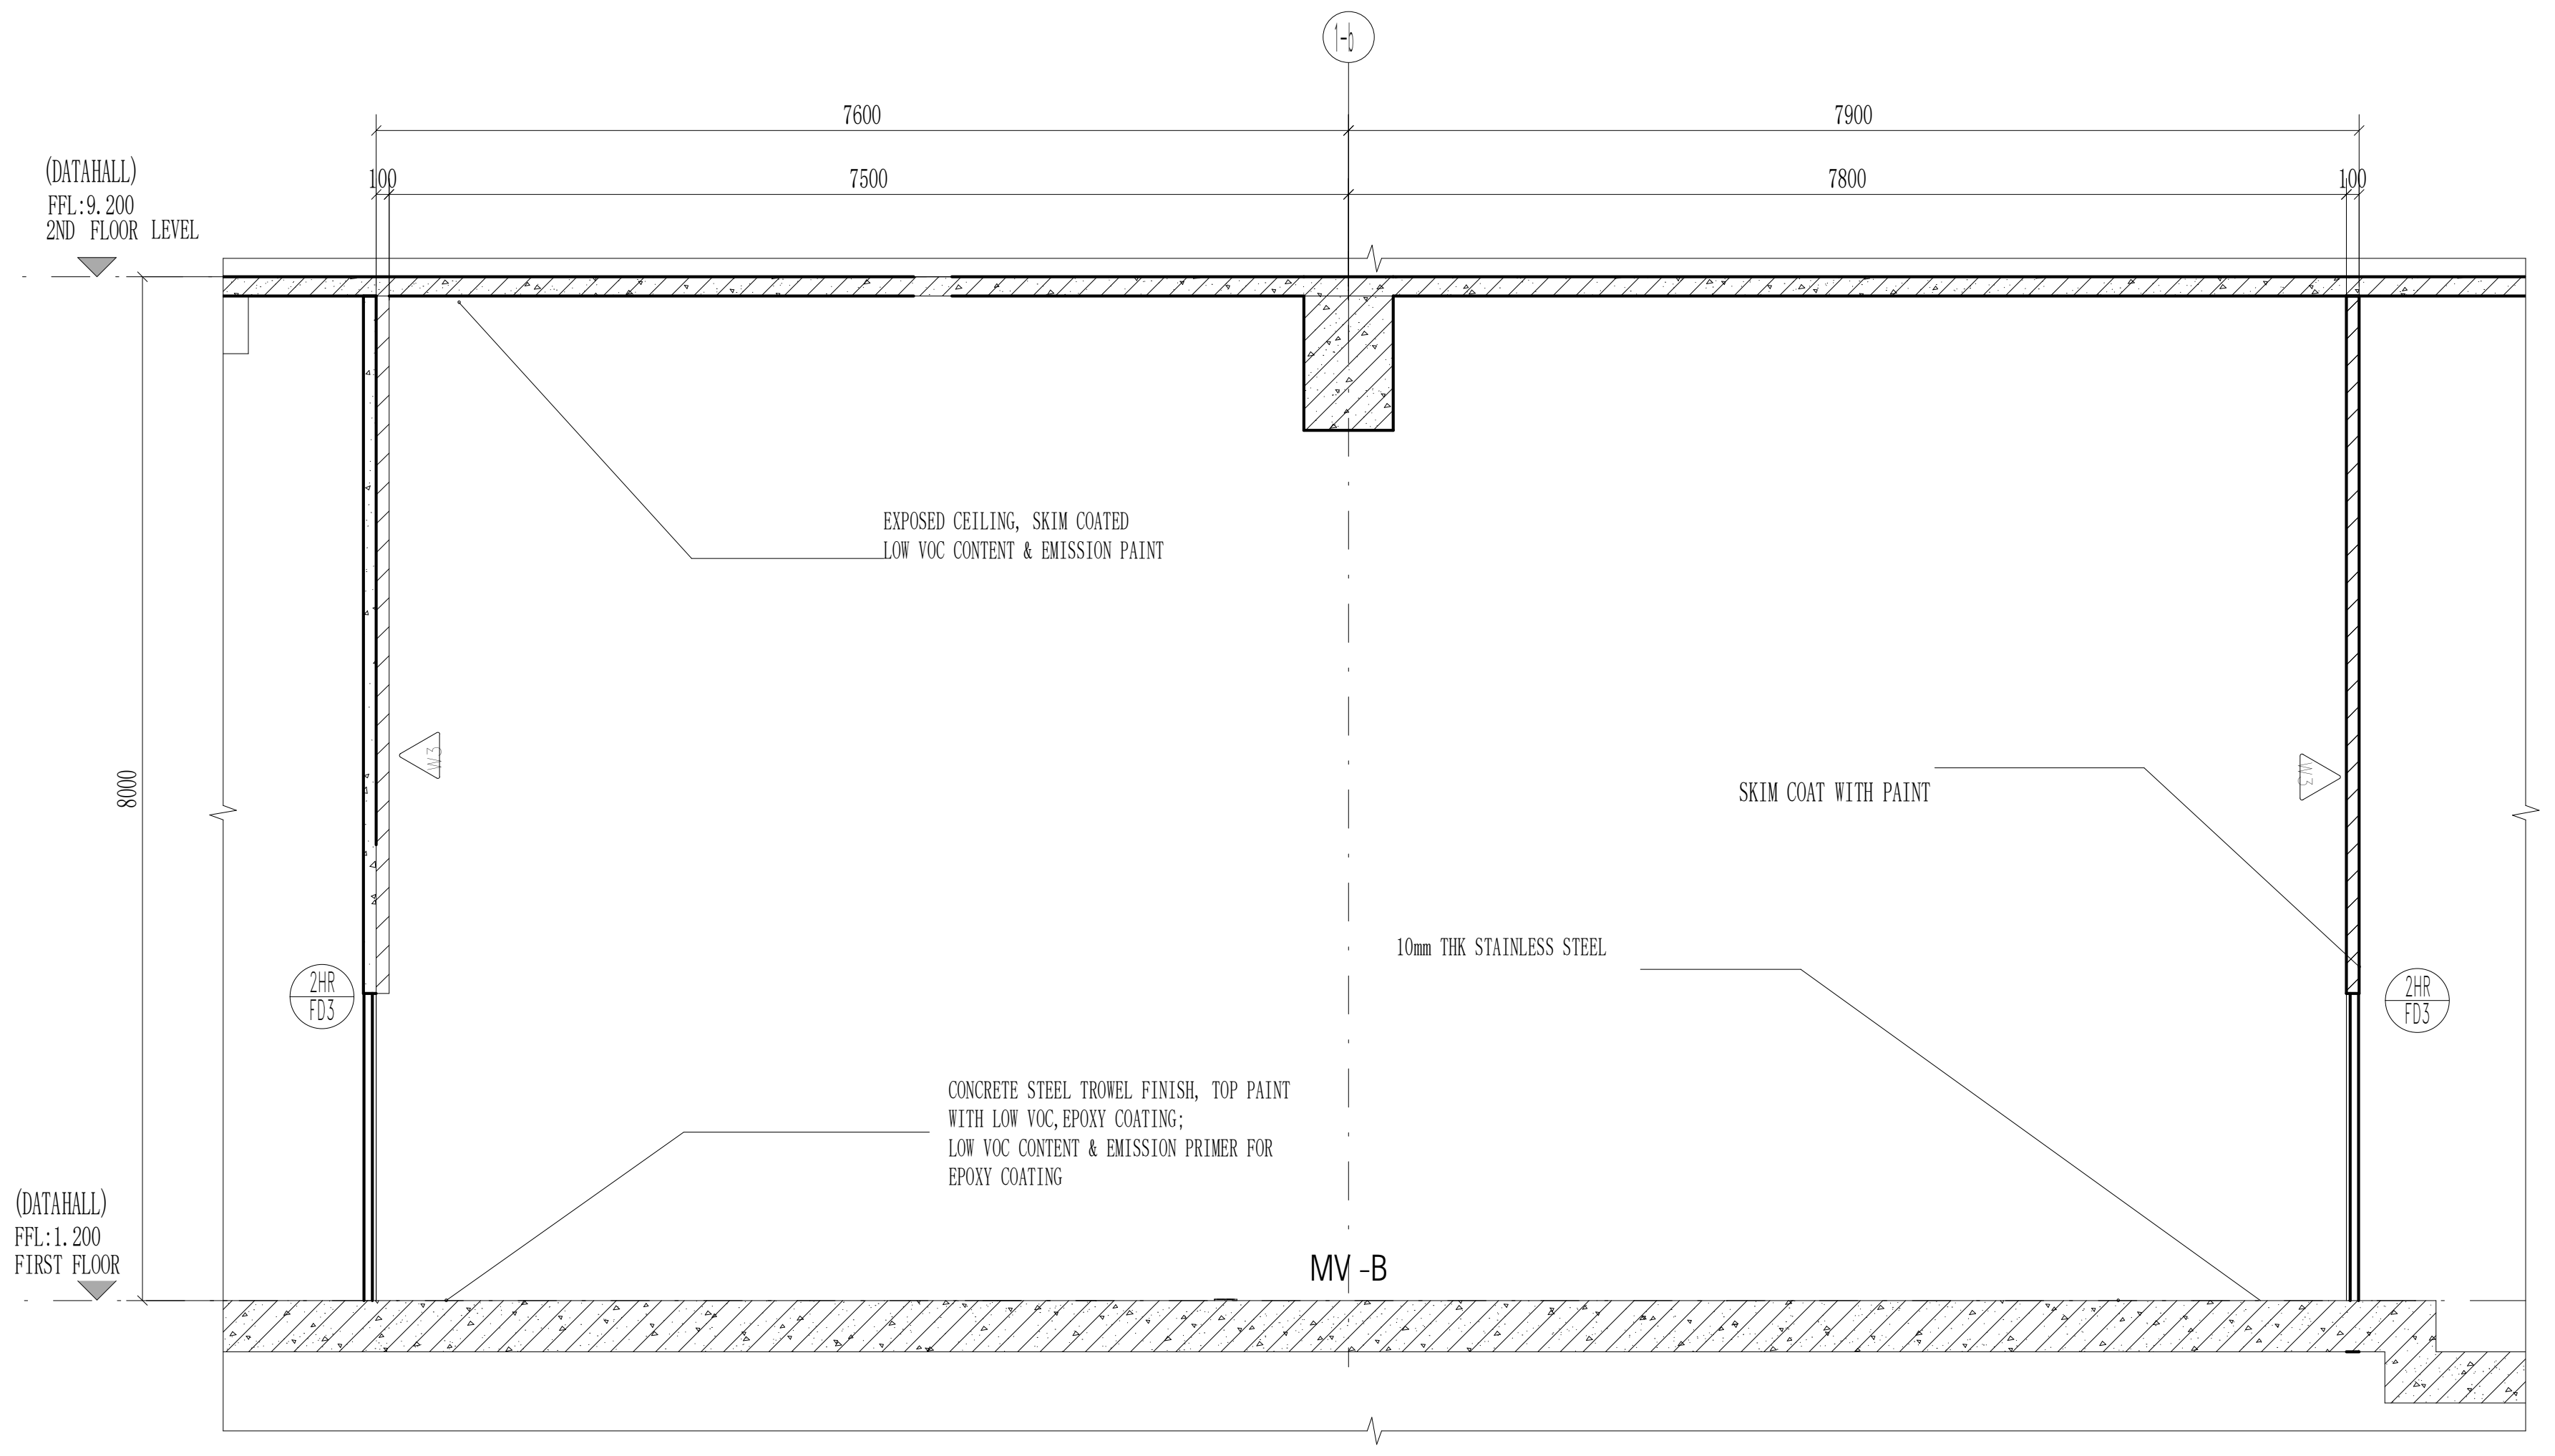

1-b
7600
7900
100
7500
7800
100
(DATAHALL)
FFL:9.200
2ND FLOOR LEVEL
EXPOSED CEILING, SKIM COATED
LOW VOC CONTENT & EMISSION PAINT
W3
SKIM COAT WITH PAINT
W2
8000
10mm THK STAINLESS STEEL
2HR
FD3
2HR
FD3
CONCRETE STEEL TROWEL FINISH, TOP PAINT
WITH LOW VOC,EPOXY COATING;
LOW VOC CONTENT & EMISSION PRIMER FOR
EPOXY COATING
(DATAHALL)
FFL:1.200
FIRST FLOOR
MV -B

MV-B SECTION B-B

Scale 1:50

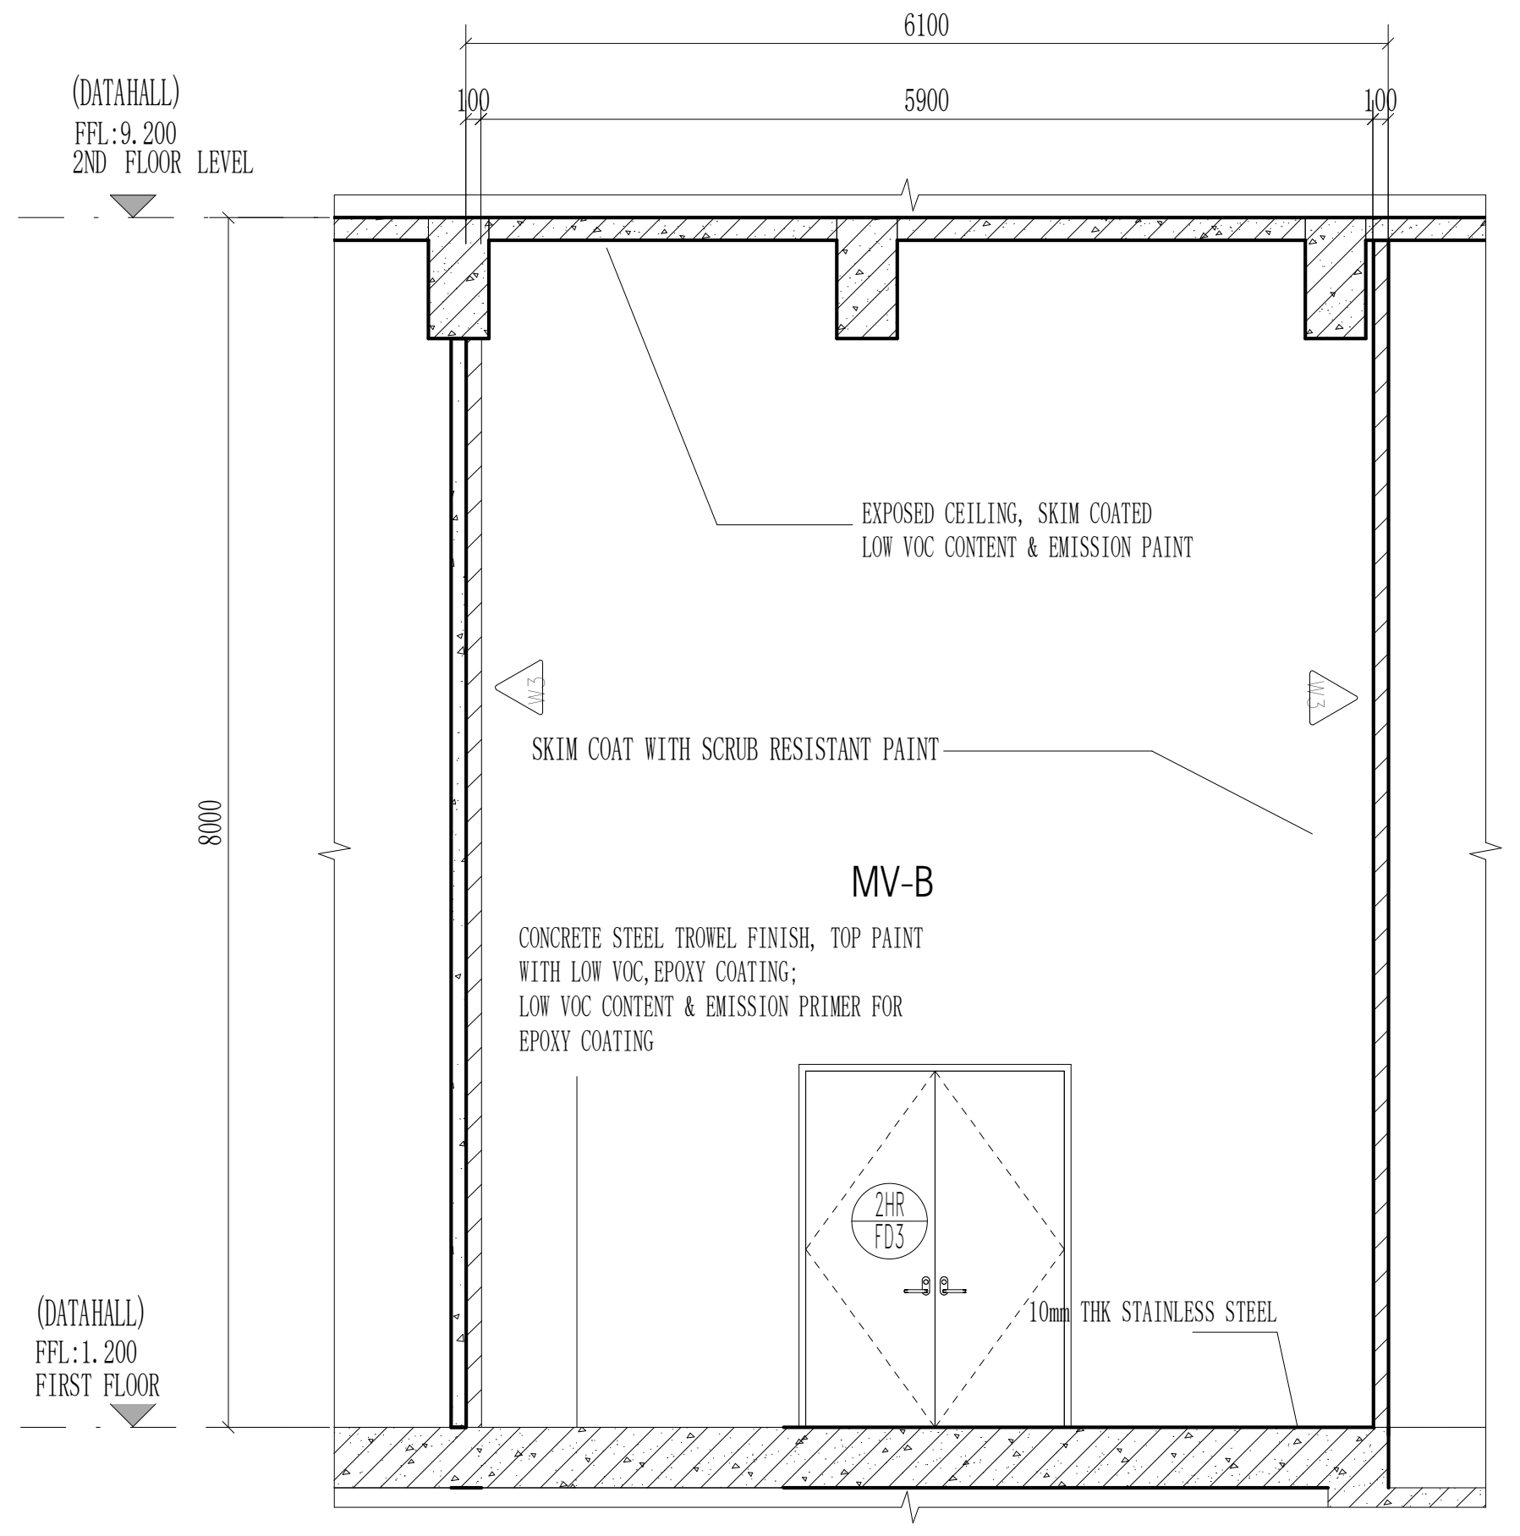

6100
100
5900
100
(DATAHALL)
FFL:9.200
2ND FLOOR LEVEL
EXPOSED CEILING, SKIM COATED
LOW VOC CONTENT & EMISSION PAINT
W3
W3
SKIM COAT WITH SCRUB RESISTANT PAINT
8000
MV-B
CONCRETE STEEL TROWEL FINISH, TOP PAINT
WITH LOW VOC,EPOXY COATING;
LOW VOC CONTENT & EMISSION PRIMER FOR
EPOXY COATING
2HR
FD3
10mm THK STAINLESS STEEL
(DATAHALL)
FFL:1.200
FIRST FLOOR

MV-B SECTION A-A Scale 1:50

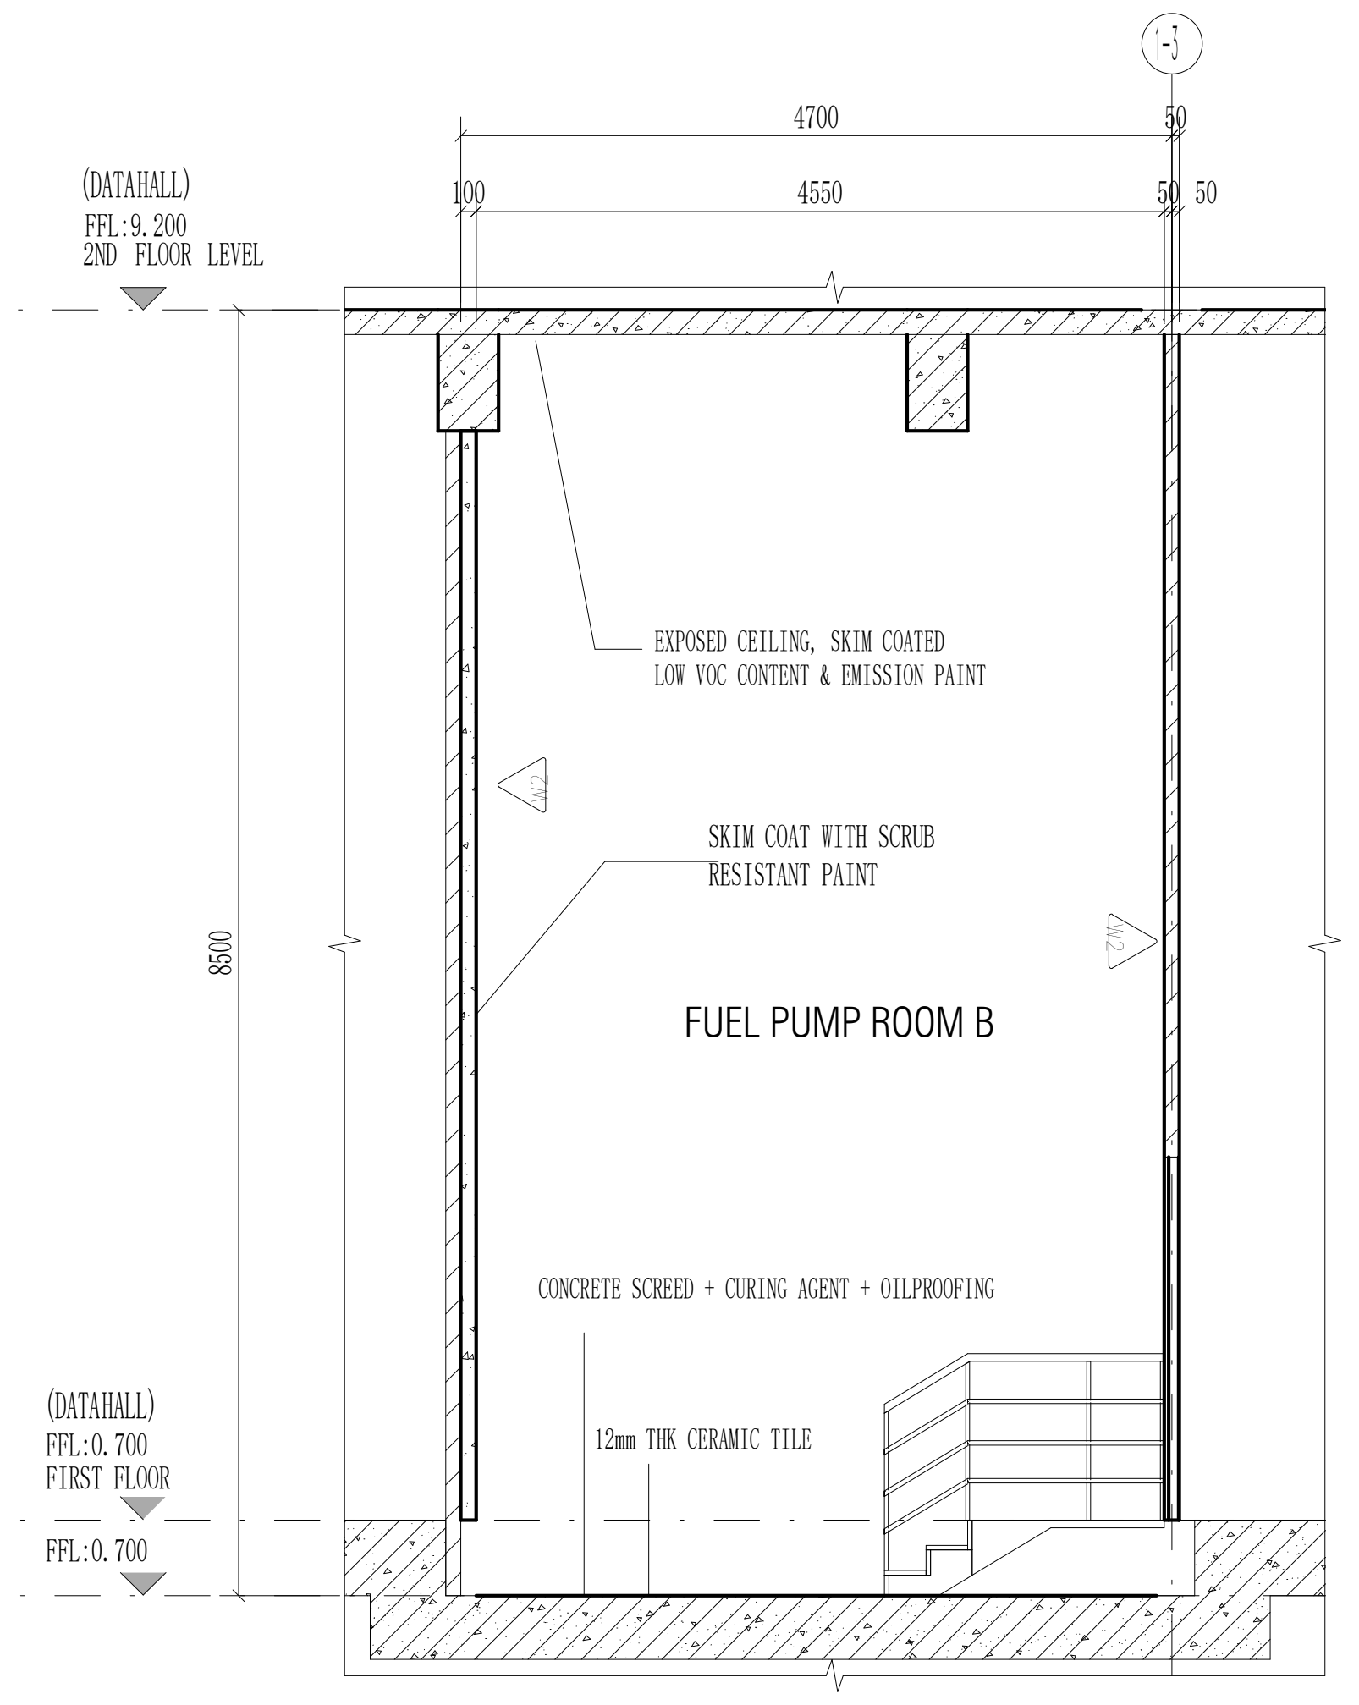

1-3
4700
50
100
4550
50
50
(DATAHALL)
FFL:9.200
2ND FLOOR LEVEL
EXPOSED CEILING, SKIM COATED
LOW VOC CONTENT & EMISSION PAINT
W2
SKIM COAT WITH SCRUB
RESISTANT PAINT
W2
8500
FUEL PUMP ROOM B
CONCRETE SCREED + CURING AGENT + OILPROOFING
12mm THK CERAMIC TILE
(DATAHALL)
FFL:0.700
FIRST FLOOR
FFL:0.700

FUEL PUMP ROOM B SECTION A-A Scale 1:50

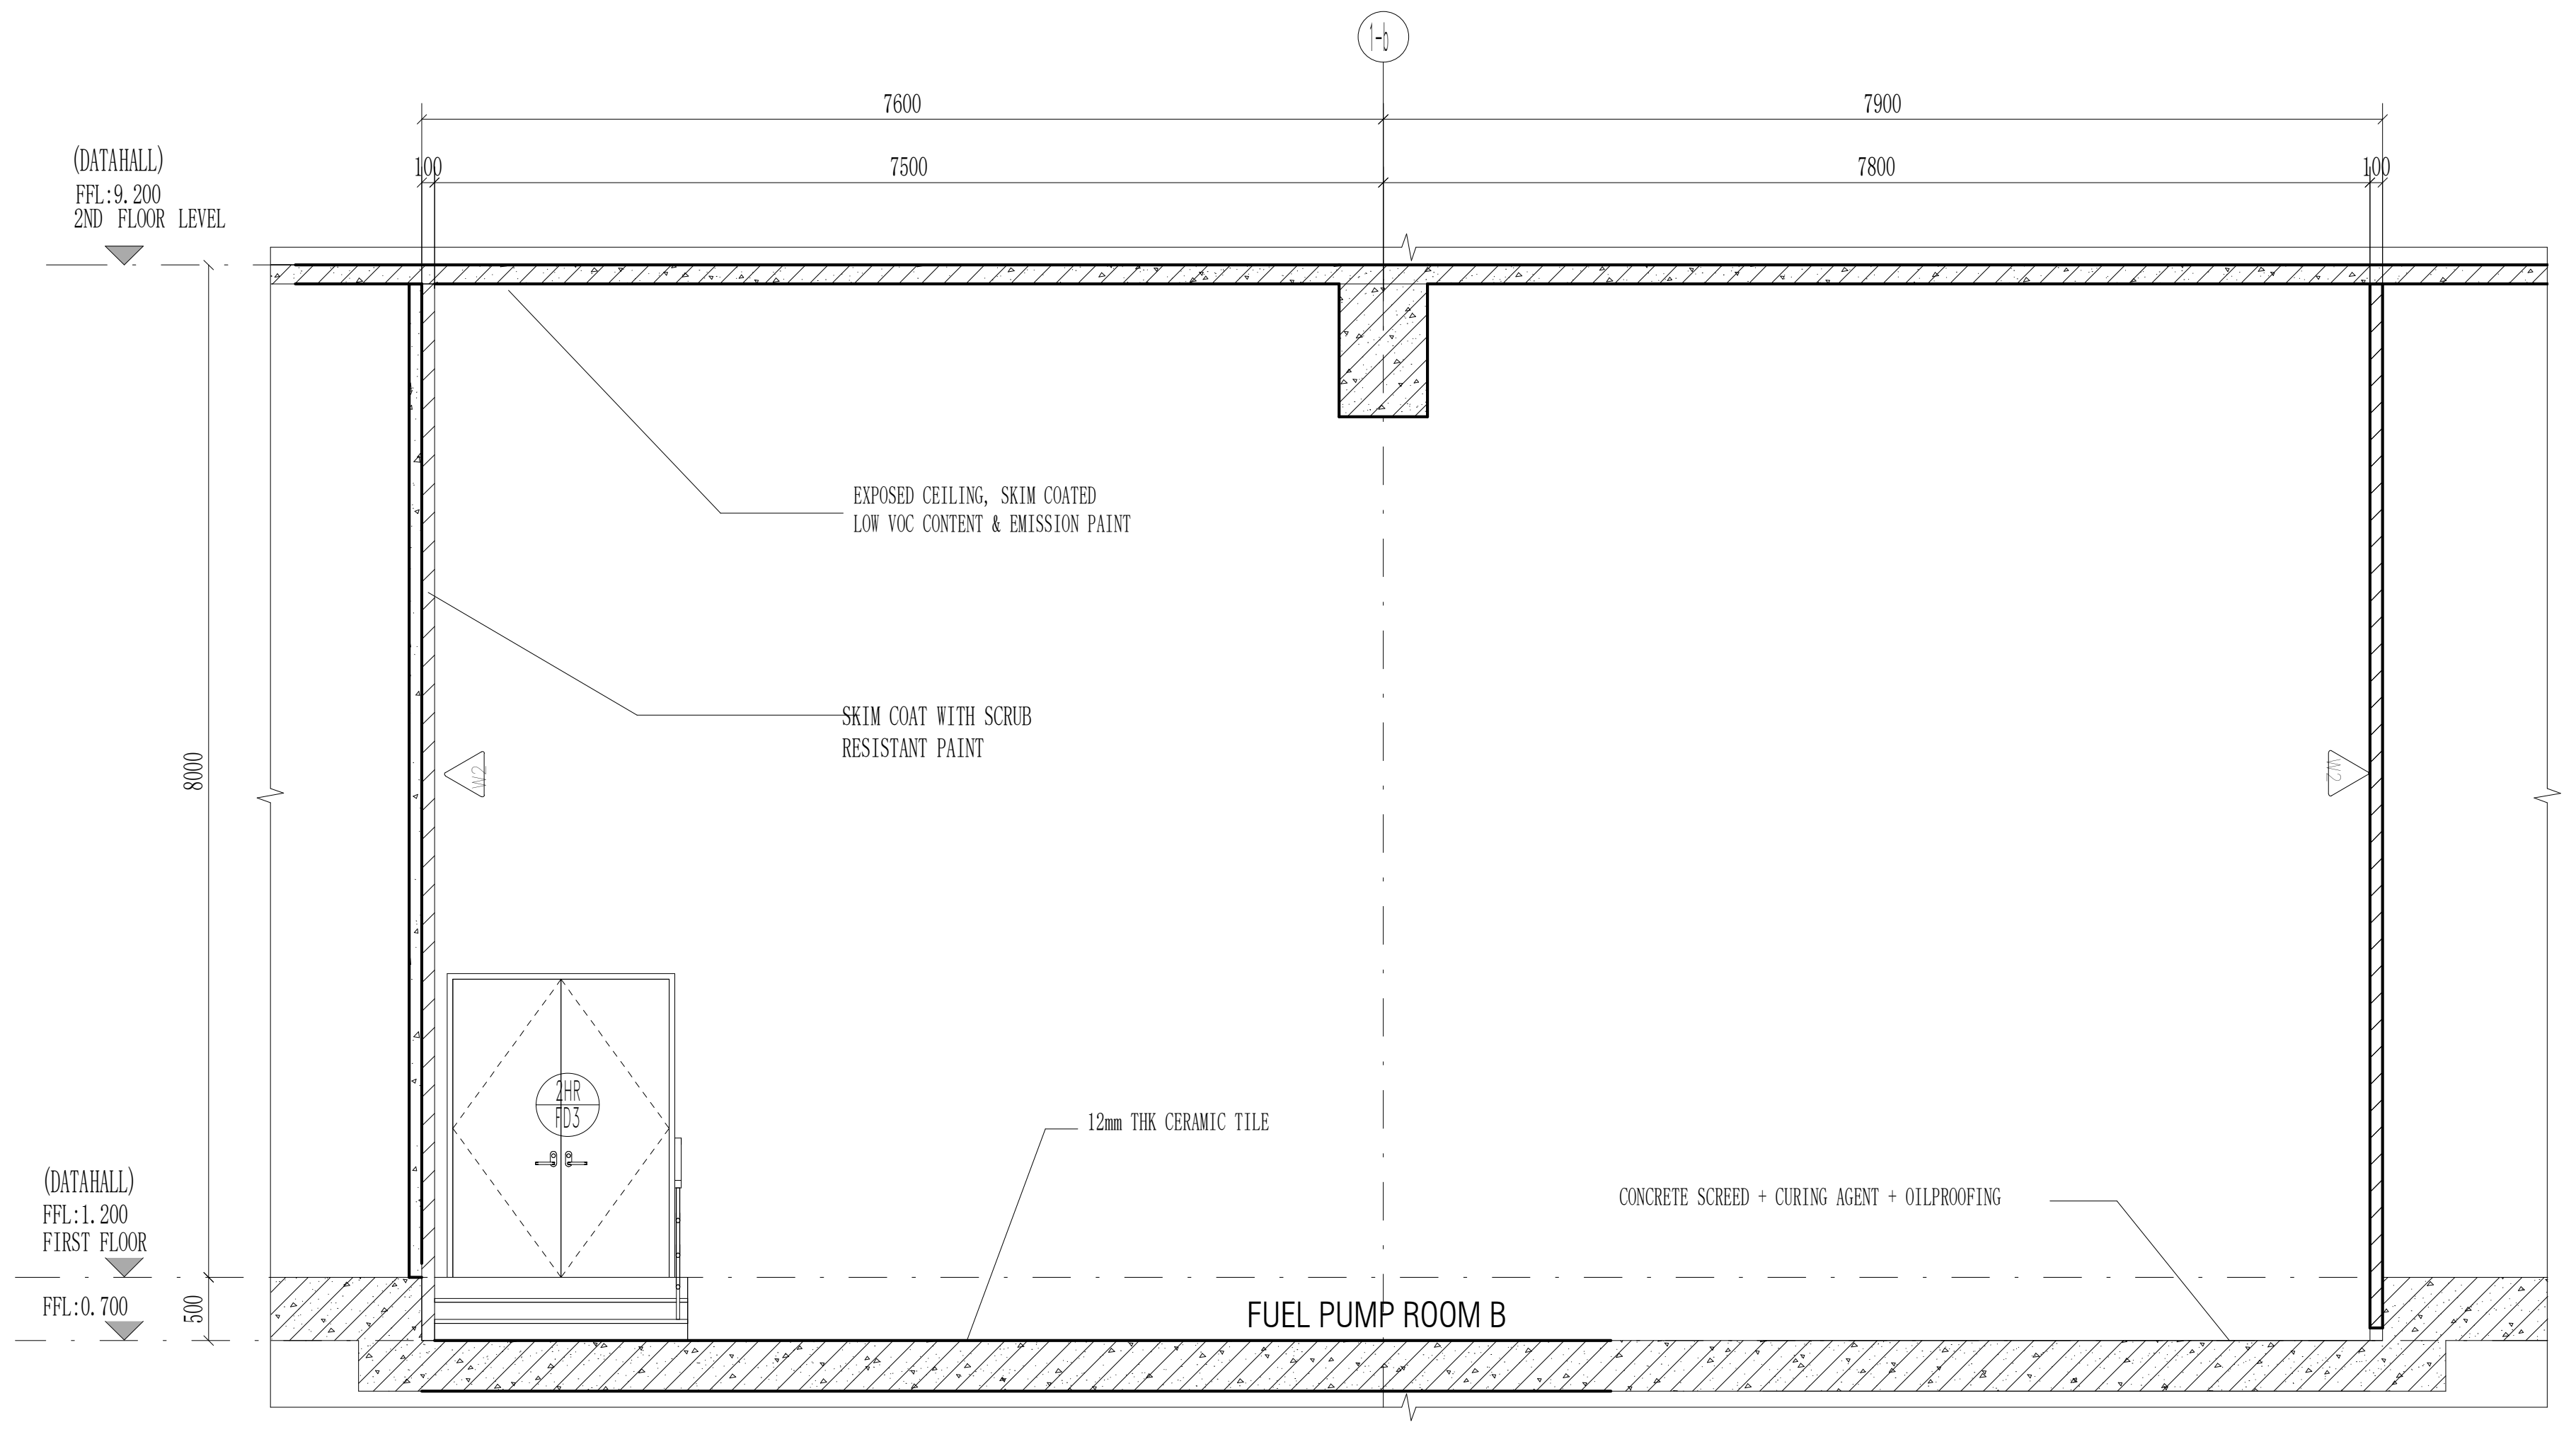

1-b
7600
7900
100
7500
7800
100
(DATAHALL)
FFL:9.200
2ND FLOOR LEVEL
EXPOSED CEILING, SKIM COATED
LOW VOC CONTENT & EMISSION PAINT
SKIM COAT WITH SCRUB
RESISTANT PAINT
W2
W2
8000
2HR
FD3
12mm THK CERAMIC TILE
CONCRETE SCREED + CURING AGENT + OILPROOFING
(DATAHALL)
FFL:1.200
FIRST FLOOR
500
FFL:0.700
FUEL PUMP ROOM B

FUEL PUMP ROOM B SECTION B-B Scale 1:50

CLIENT :

GULF EDGE DC 01

87 Wireless Road, M Thai Tower 11th. Floor, All Seasons Place, Lumpini,
Pathumwan, Bangkok 10330, Thailand

CONTRACTOR :

华西发展(泰国)有限公司
บริษัท หัวซือ ดีเวลลอปเม้นต์ (ประเทศไทย) จำกัด
HUASHI DEVELOPMENT CO.,LTD
No. 202, Room No. 1403, 14/F, Le Concorde Building,
Ratchadapisek Road, Huaykhwang Sub-District,
Huaykhwang District, Bangkok Metropolitan 10310.

CONSULTANT :

ARbay
บริษัท เอ อาร์ เบย์ จำกัด
ARbay Company Limited
31 st Floor Bangkok Insurance Building
25 South Sathorn road Thungmahamek
Sathorn Bangkok 10120 THAILAND
T +66 (0) 2286 8199
F +66 (0) 2286 2863
info@arbay.co.th

CONSULTANT :

Qbic Engineers & Architects Co.,Ltd.
8 Soi KALONG 4 SANAMBINNAM ROAD,
THASAI SUB-DISTRICT, MUANG NONTHABURI DISTRICT
, NONTHABURI.
Tel 662-950-4374
Fax 662-580-3231
E-Mail : qbic@qbic.co.th, www.qbic.co.th
QBIC ENGINEERS AND ARCHITECTS CO.,LTD.

CONSULTANT :

MITR
MITR TECHNICAL CONSULTANT CO.,LTD.
1168/8 12th FLOOR, LUMPINI TOWER BUILDING,
RAMA IV RD., THUNGMAHAMEK, SATHORN, BANGKOK 10120, THAILAND
TEL : 0-2679-9079-84
FAX : 0-2679-9085 E-mail: mitr_dd@mitr.com

Architect : SIGNATURE
ประกิต พนานุรัตน์ วสถ. 580
ที่อยู่
251/1 ถ.จารุเมือง แขวงรองเมือง เขตปทุมวัน
กรุงเทพมหานคร โทรศัพท์ 02-286-8199

Structural Engineer : SIGNATURE
วิศวกรผู้ออกแบบโครงสร้าง
ณัฐสม สงวนวงษ์ วย 1423
ที่อยู่
2/1 ซ.รามคำแหง 150 ถ.รามคำแหง
แขวง สะพานสูง เขต สะพานสูง กทม. 10240

Structural Inspector : SIGNATURE
วิศวกรผู้ตรวจสอบโครงสร้าง
โกมล จุฑาภัทร วย 964
ที่อยู่
24/18 ซ.นวมินทร์ 129 ถ. นวมินทร์
แขวง นวลจันทร์ เขต บึงกุ่ม กทม. 10230

Electrical Engineer : SIGNATURE
วิศวกรผู้ออกแบบระบบไฟฟ้ากำลัง
นายสุภัทร บูรณวิทย์ วฟก.1265
ที่อยู่
21 ซอยทานสัมฤทธิ์ 13
ตำบลท่าทราย อ.เมืองนนทบุรี จ.นนทบุรี 11000

Mechanical Engineer : SIGNATURE
วิศวกรผู้ออกแบบระบบเครื่องกลและปรับอากาศ
นายประสิทธิ์ เกี้ยวสุนทร วก.1221
ที่อยู่
44/372 ซอยบางกระดี่ 35/1 แขวงแสมดำ
เขตบางขุนเทียน กทม. 10150
ประสิทธิ์

Sanitary Engineer : SIGNATURE
วิศวกรผู้ออกแบบระบบสุขาภิบาล และดับเพลิง
นายทศวรรษ สนั่นฤทธิ์ วส. 215
ที่อยู่
บ้านเลขที่ 99/107 หมู่ที่ 3 ต.ศีรษะจรเข้น้อย
อ.บางเสาธง จ.สมุทรปราการ 10540
ทศวรรษ

ISSUE/REVISION

REV.	DESCRIPTION	DATE
A	90% DEVELOPED	09/05/2026

PROJECT NAME :
GEDC 01

LOCATION:
Nikhom Phattana district, Rayong ,industrial estate,CPGC

BUILDING :
MAIN BUILDING

90% DEVELOPED

TITLE :
ROOMDETAIL-1F-FUELPUMP ROOM B.MV-B

JOB NO.	SCALE 1 : 50
DRAWN LYT	REF.
CHECKED LJC	DWG. NO. MPK01A-90-A-RD-121
APPROVED LXD	
DATE 2026.05.09	

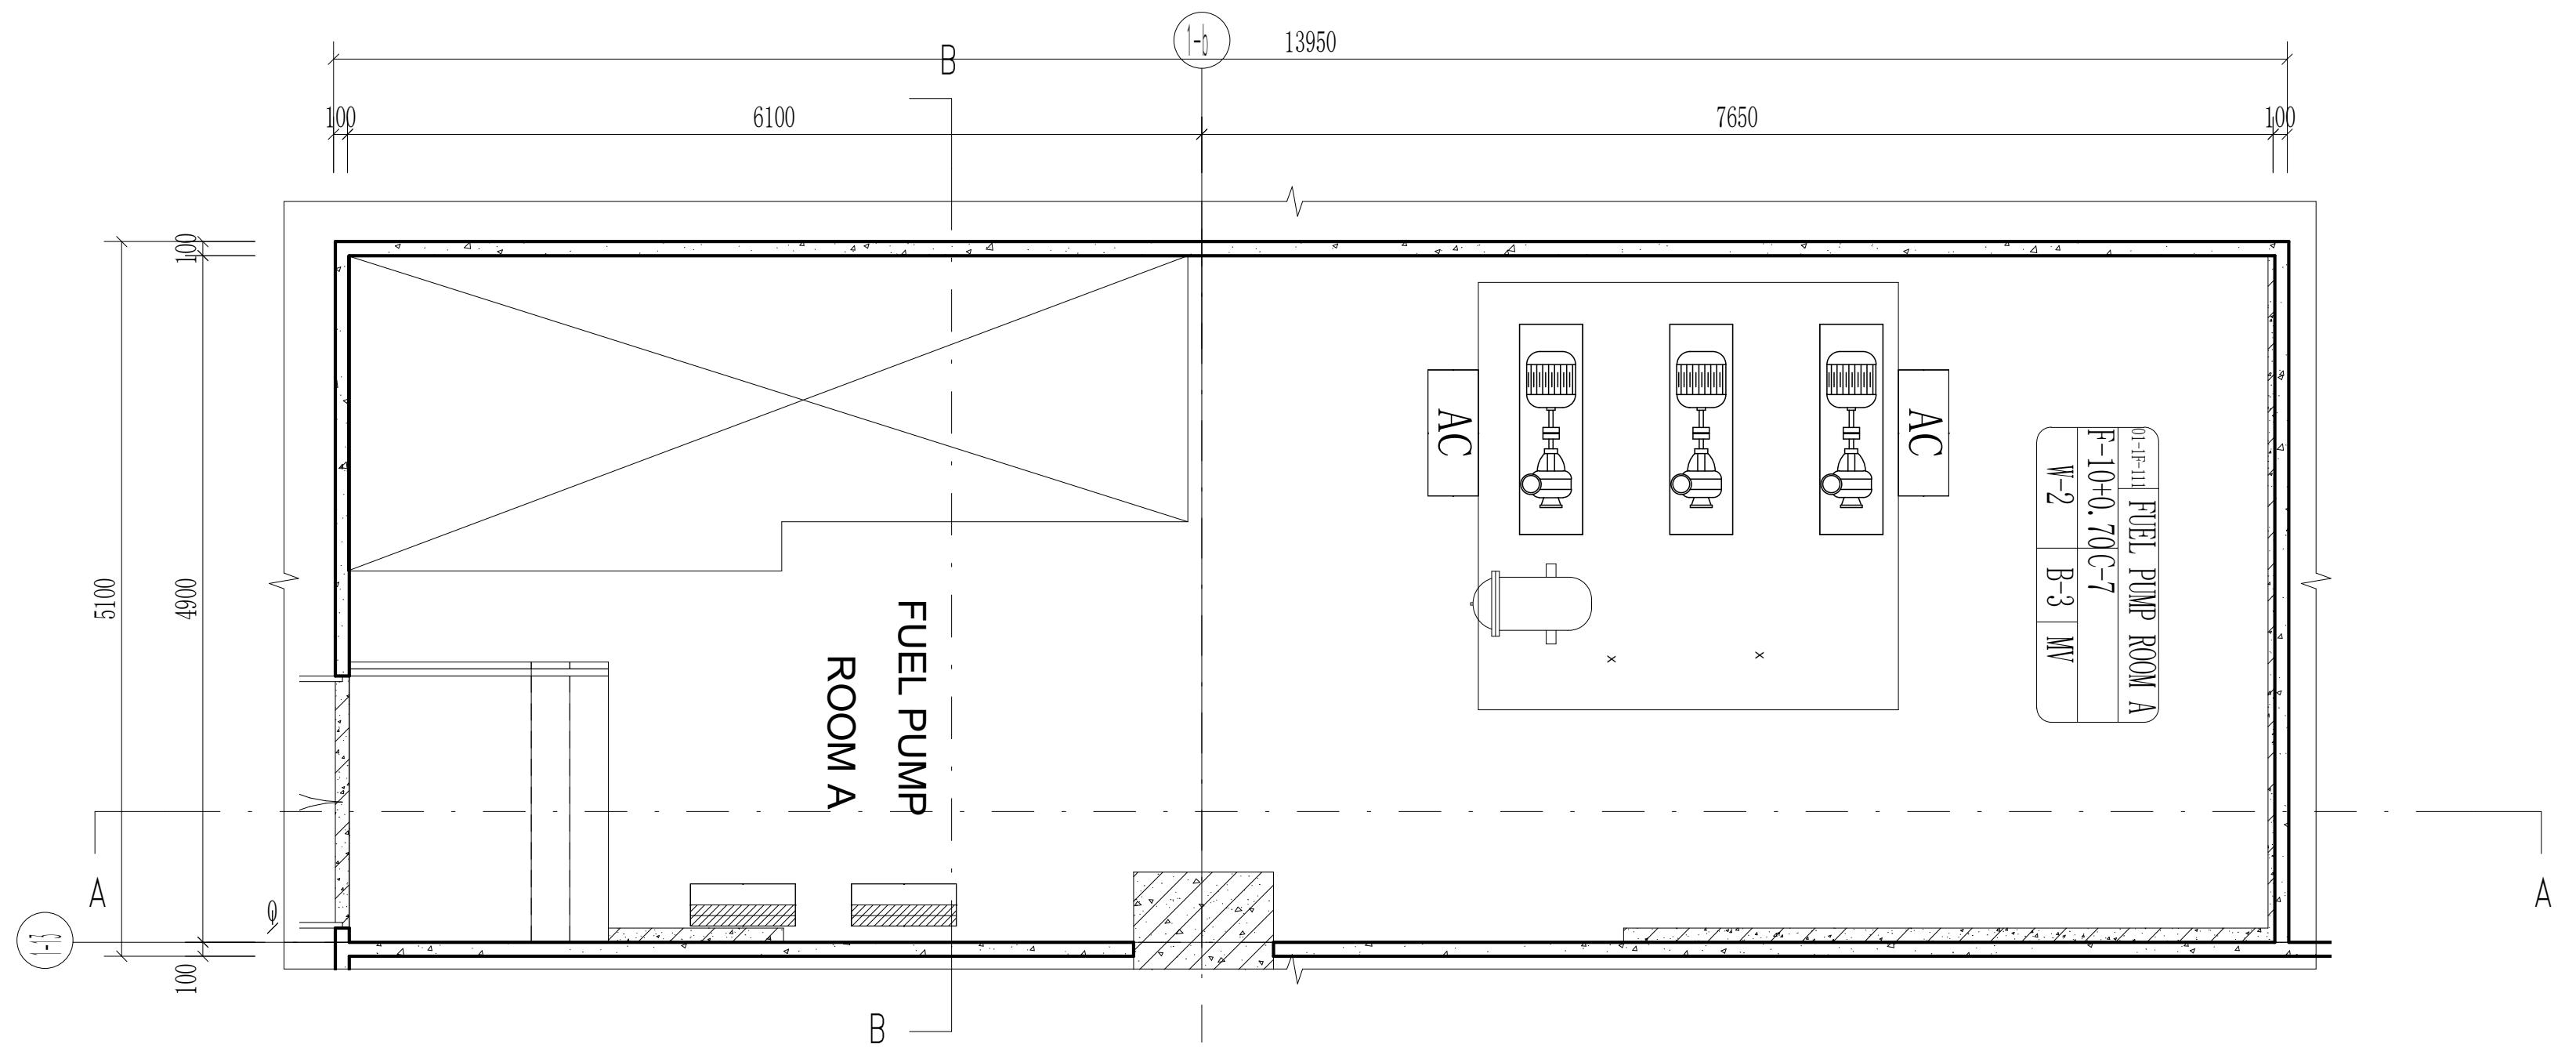
13950
100
6100
7650
100
5100
4900
100
A
B
A
B
FUEL PUMP ROOM A
AC
AC
01-1F-111
FUEL PUMP ROOM A
F-10+0.70
C-7
W-2
B-3
MV

FUEL PUMP ROOM A FIRST FLOOR PLAN

Scale 1:50

THE "SFL" MARKED IN THE DRAWING REFERS TO THE STRUCTURAL FLOOR LEVEL, WHILE THE FINISHED FLOOR LEVEL (FFL) IS DETERMINED BASED ON FLOOR FINISHES.

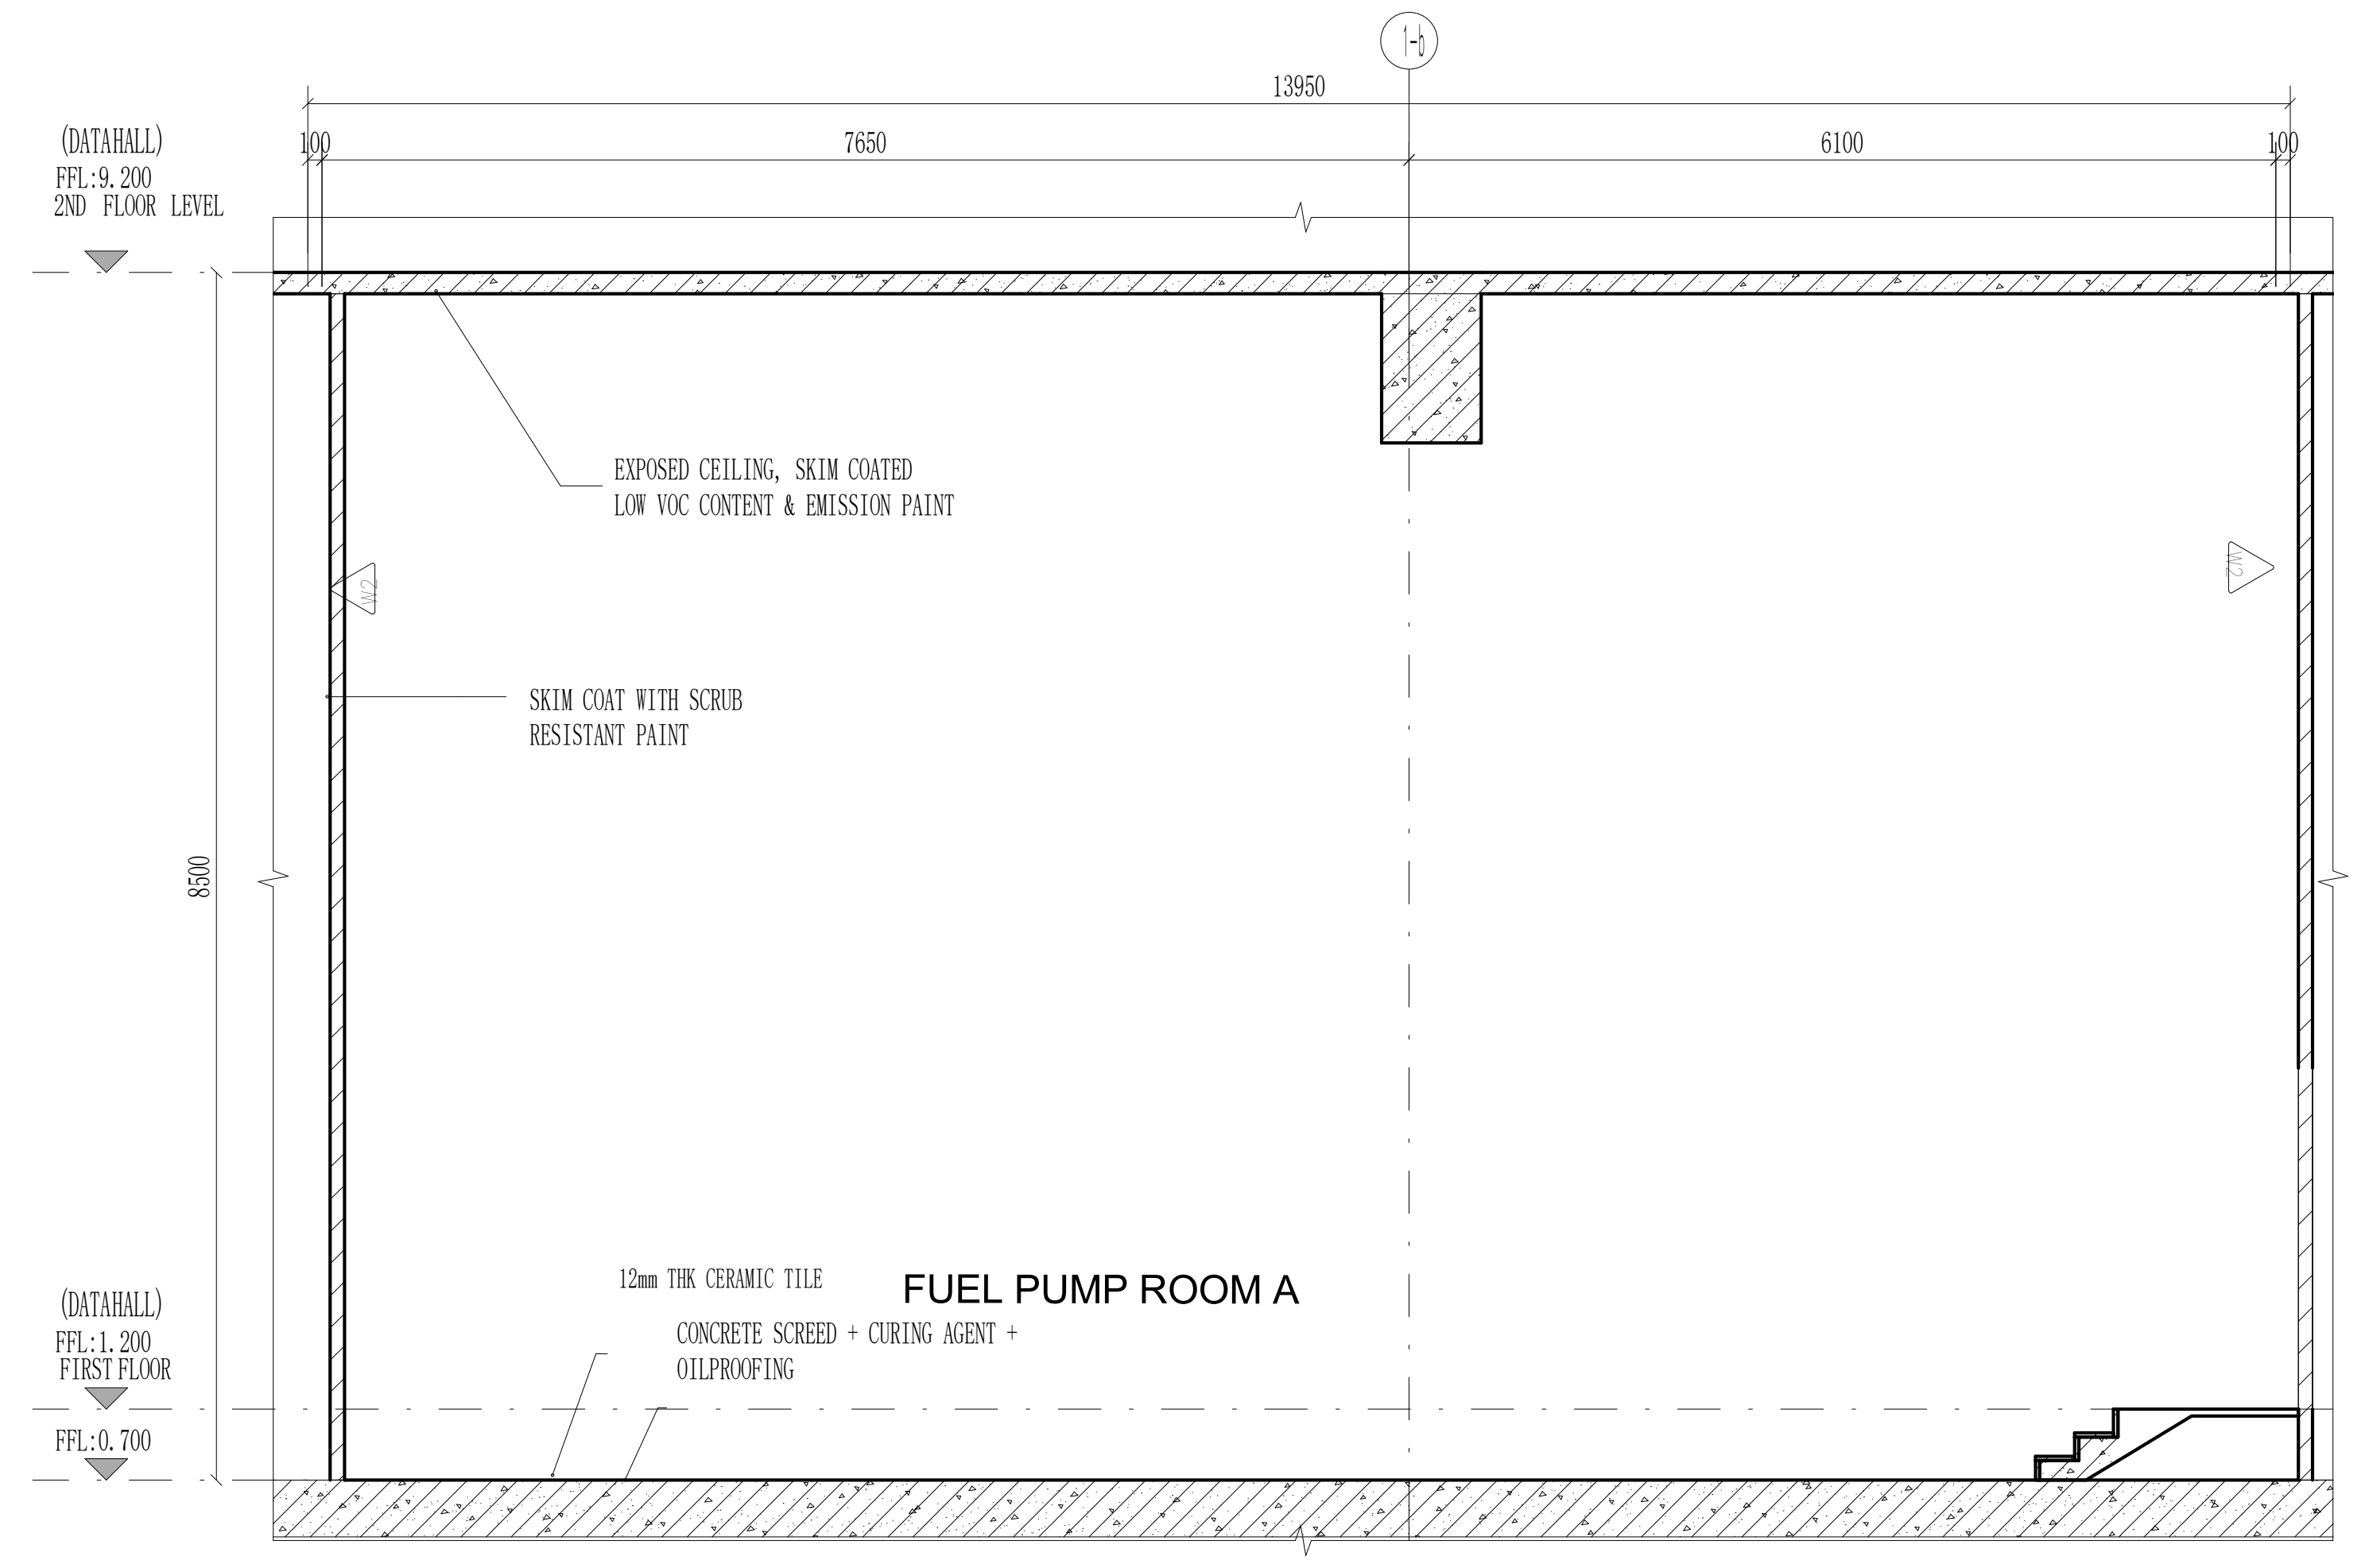
13950
100
7650
6100
100
(DATAHALL)
FFL:9.200
2ND FLOOR LEVEL
EXPOSED CEILING, SKIM COATED
LOW VOC CONTENT & EMISSION PAINT
SKIM COAT WITH SCRUB
RESISTANT PAINT
8500
(DATAHALL)
FFL:1.200
FIRST FLOOR
FFL:0.700
12mm THK CERAMIC TILE
FUEL PUMP ROOM A
CONCRETE SCREED + CURING AGENT +
OILPROOFING

FUEL PUMP ROOM SECTION A-A

Scale 1:50

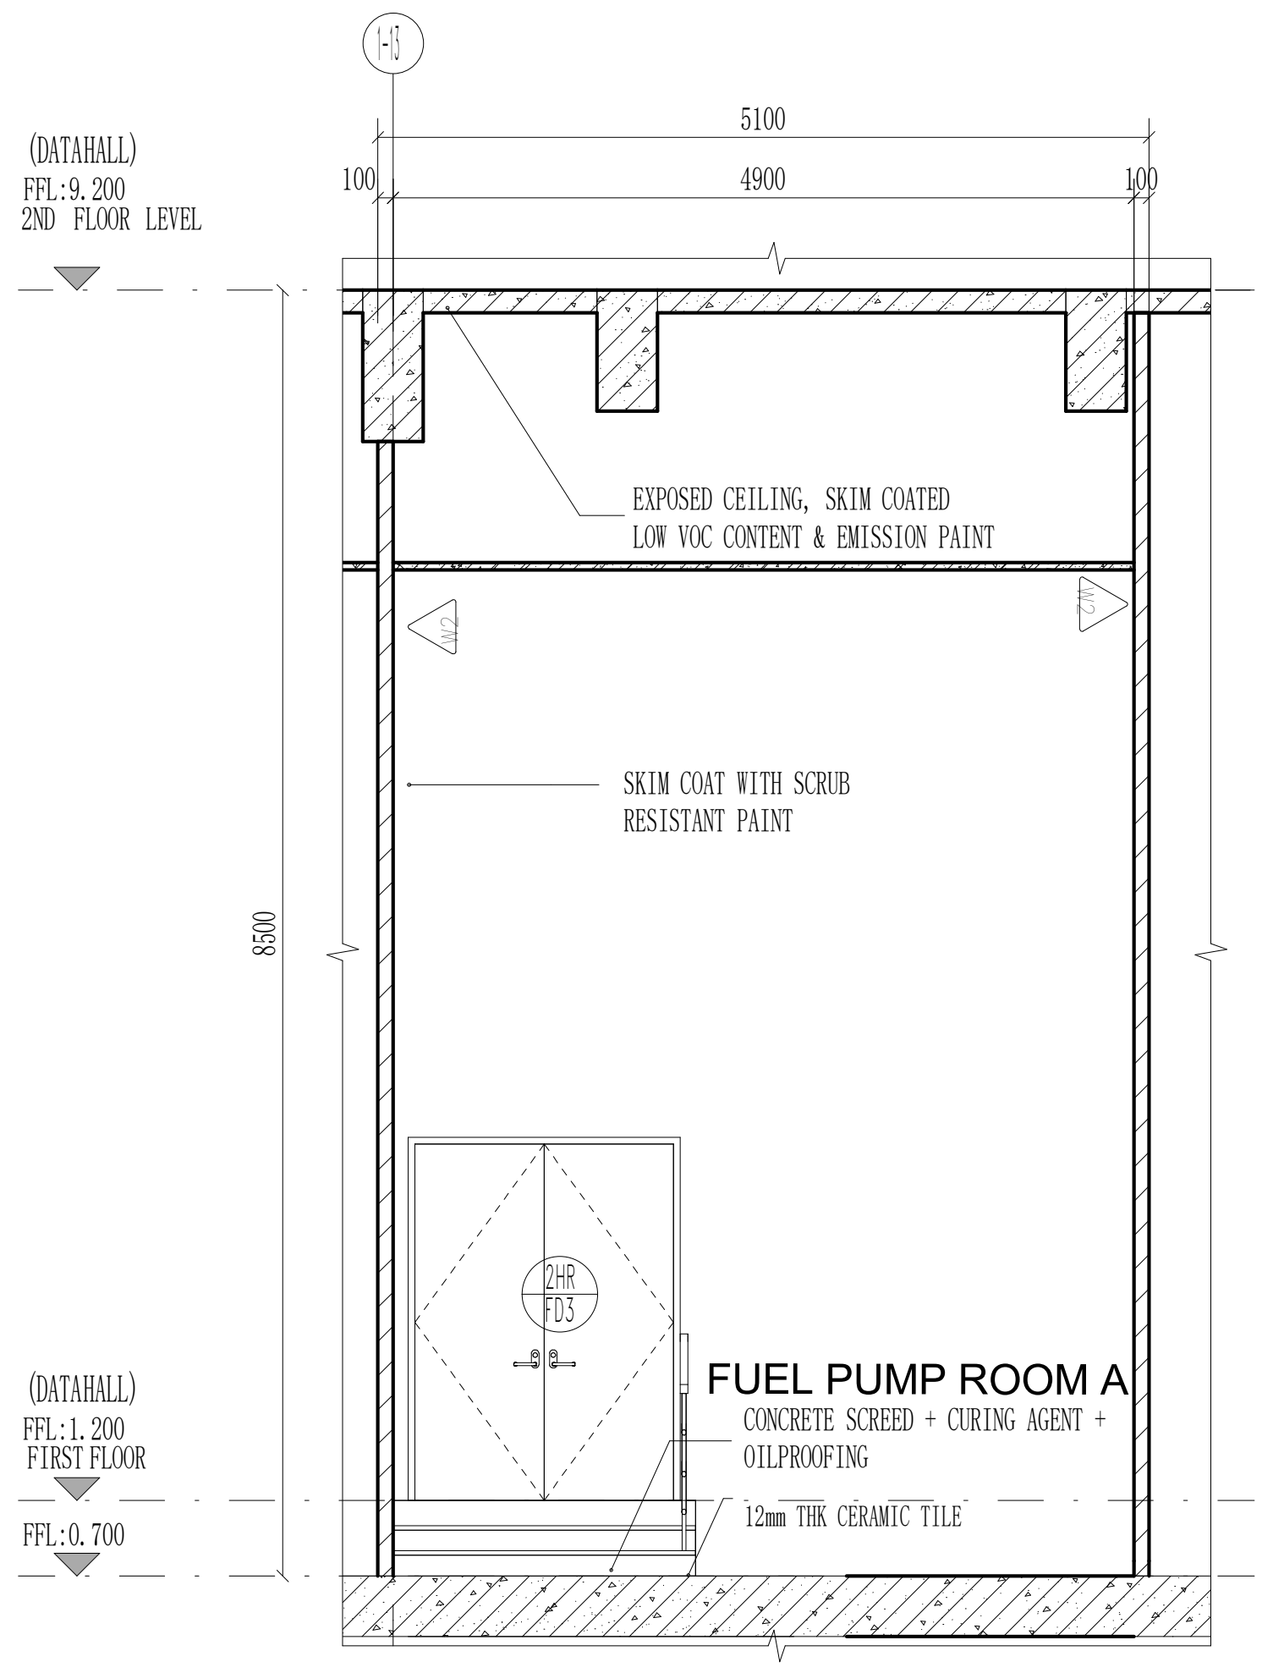
5100
100
4900
100
(DATAHALL)
FFL:9.200
2ND FLOOR LEVEL
EXPOSED CEILING, SKIM COATED
LOW VOC CONTENT & EMISSION PAINT
SKIM COAT WITH SCRUB
RESISTANT PAINT
8500
(DATAHALL)
FFL:1.200
FIRST FLOOR
FFL:0.700
FUEL PUMP ROOM A
CONCRETE SCREED + CURING AGENT +
OILPROOFING
12mm THK CERAMIC TILE

FUEL PUMP ROOM SECTION B-B

Scale 1:50

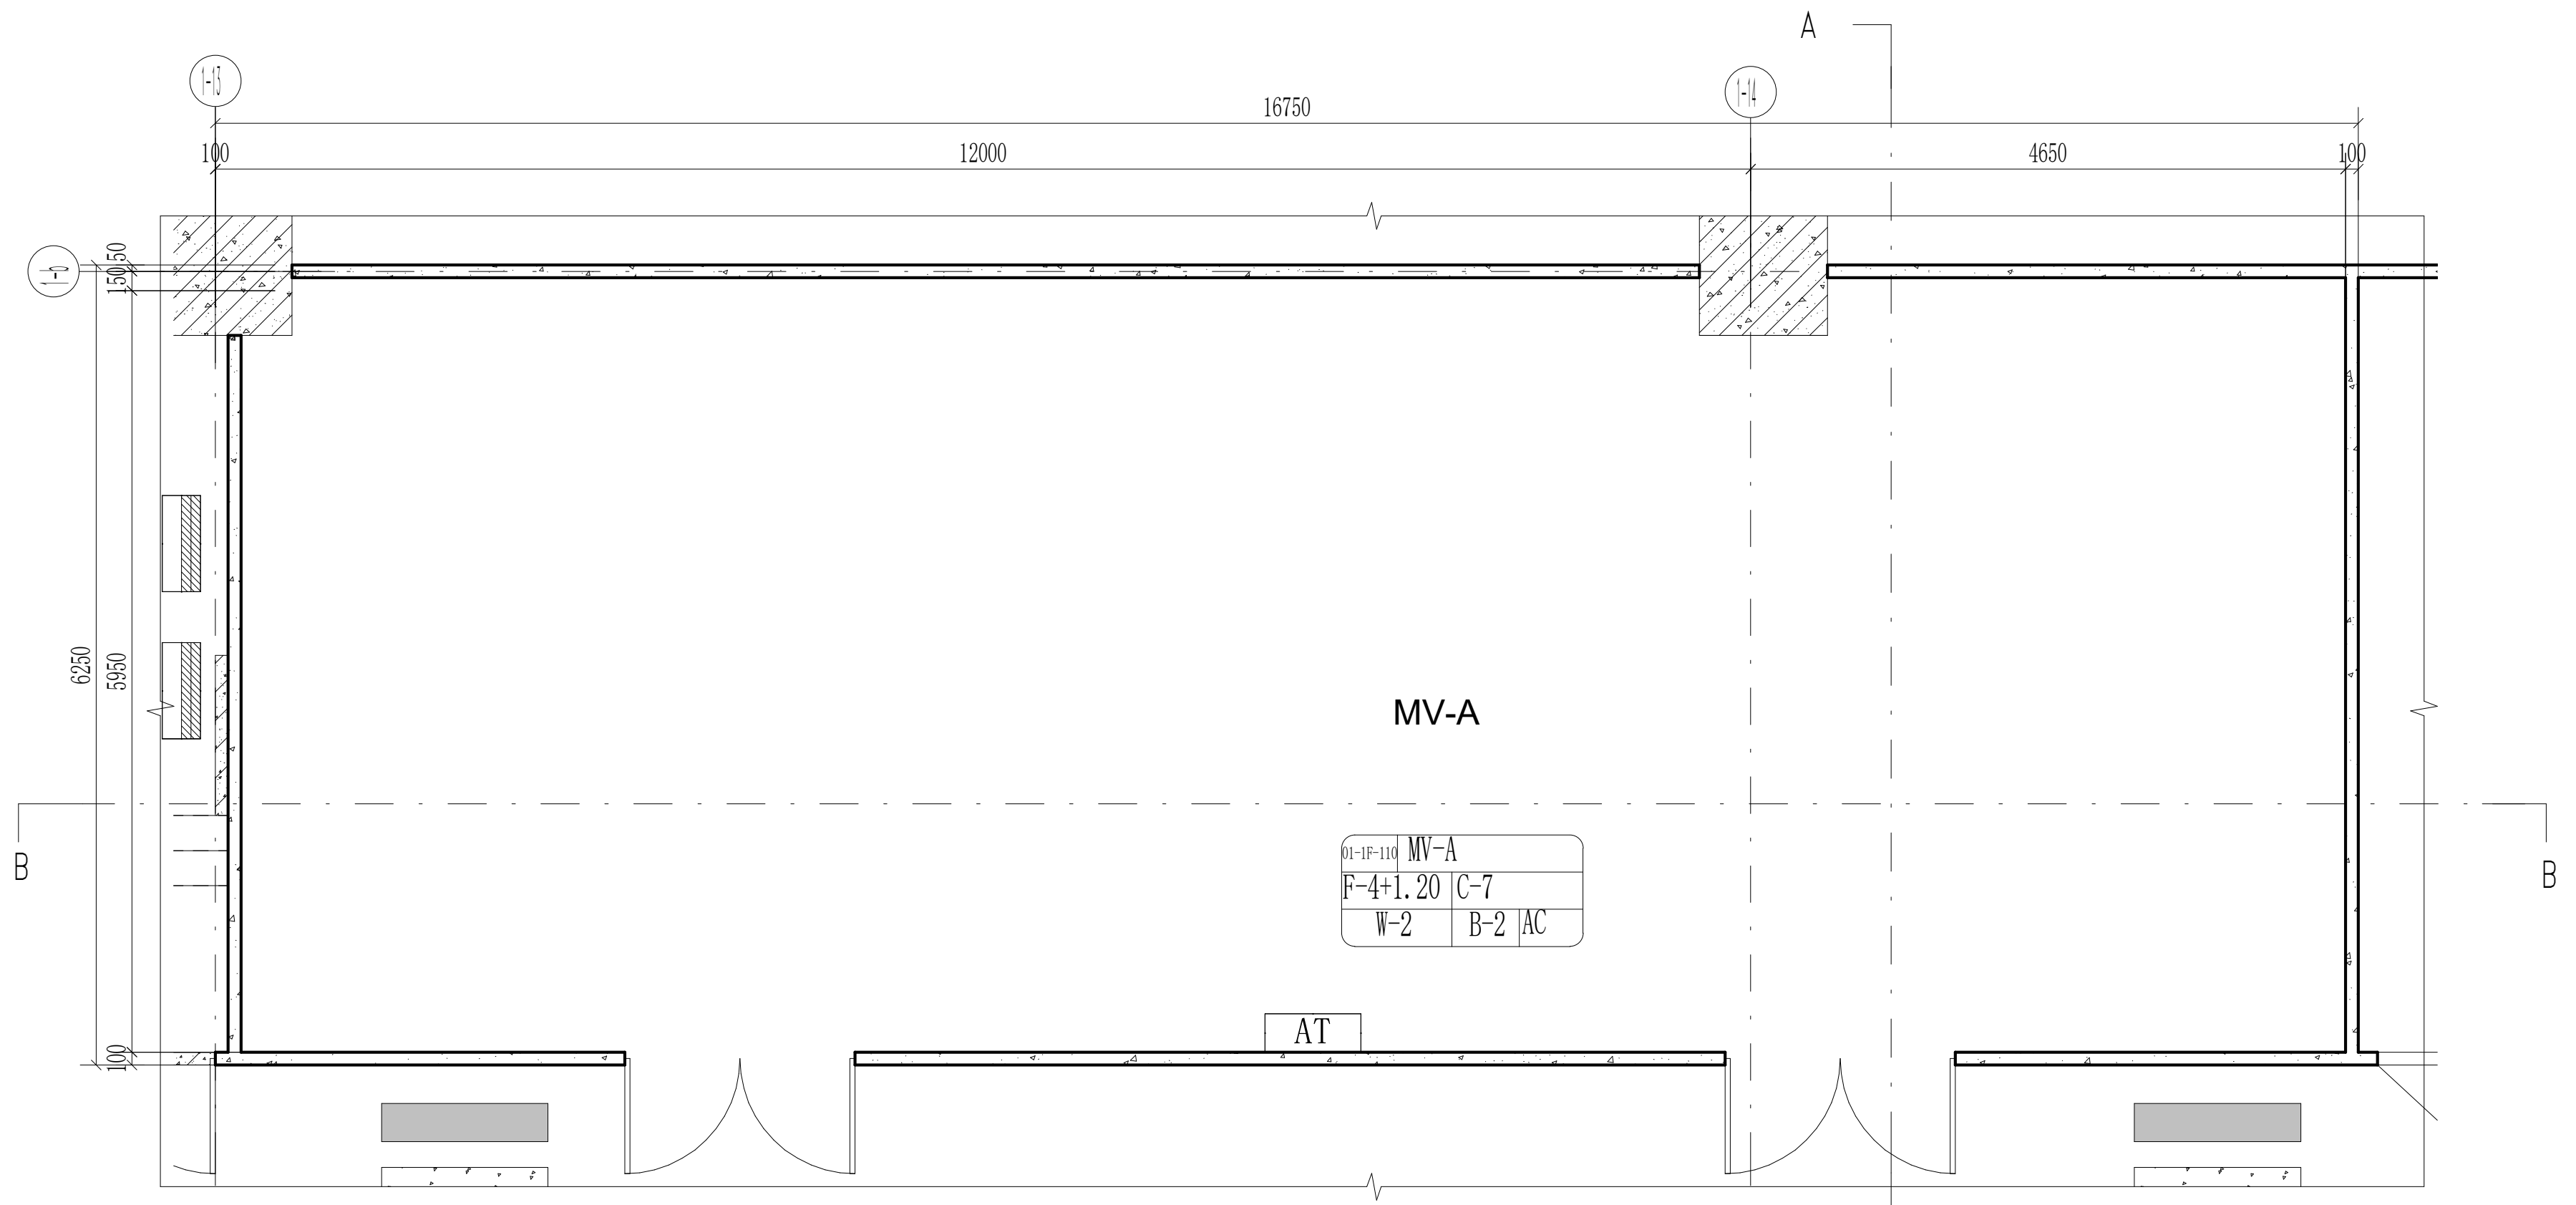
16750
100
12000
4650
100
6250
5950
A
A
B
B
MV-A
01-1F-108
MV-A
F-4+1.20
C-7
W-2
B-2
AC
AT

MV-A FIRST FLOOR PLAN

Scale 1:50

THE "SFL" MARKED IN THE DRAWING REFERS TO THE STRUCTURAL FLOOR LEVEL, WHILE THE FINISHED FLOOR LEVEL (FFL) IS DETERMINED BASED ON FLOOR FINISHES.

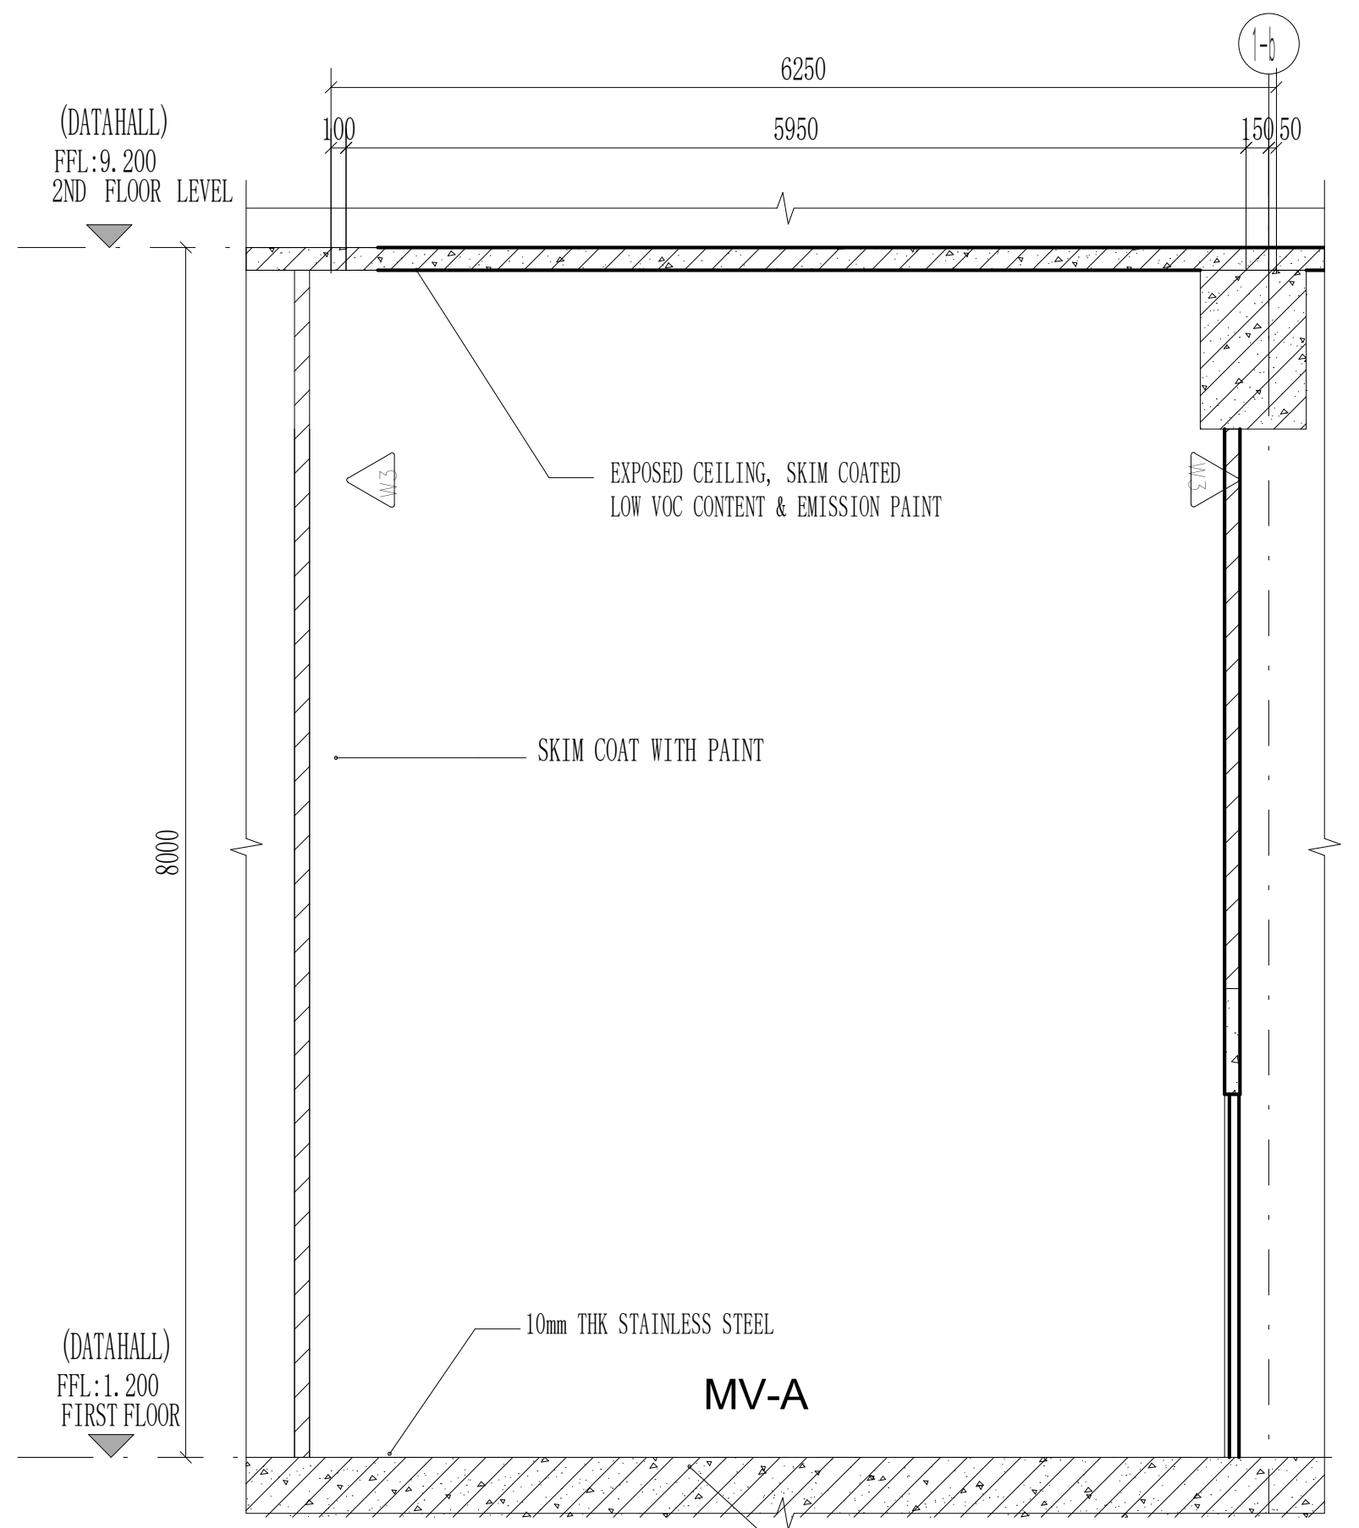
6250
100
5950
150
50
(DATAHALL)
FFL:9.200
2ND FLOOR LEVEL
EXPOSED CEILING, SKIM COATED
LOW VOC CONTENT & EMISSION PAINT
SKIM COAT WITH PAINT
8000
(DATAHALL)
FFL:1.200
FIRST FLOOR
10mm THK STAINLESS STEEL
MV-A
CONCRETE STEEL TROWEL FINISH, TOP
PAINT WITH LOW VOC,EPOXY COATING;
LOW VOC CONTENT & EMISSION PRIMER
FOR EPOXY COATING

MV-A SECTION A-A

Scale 1:50

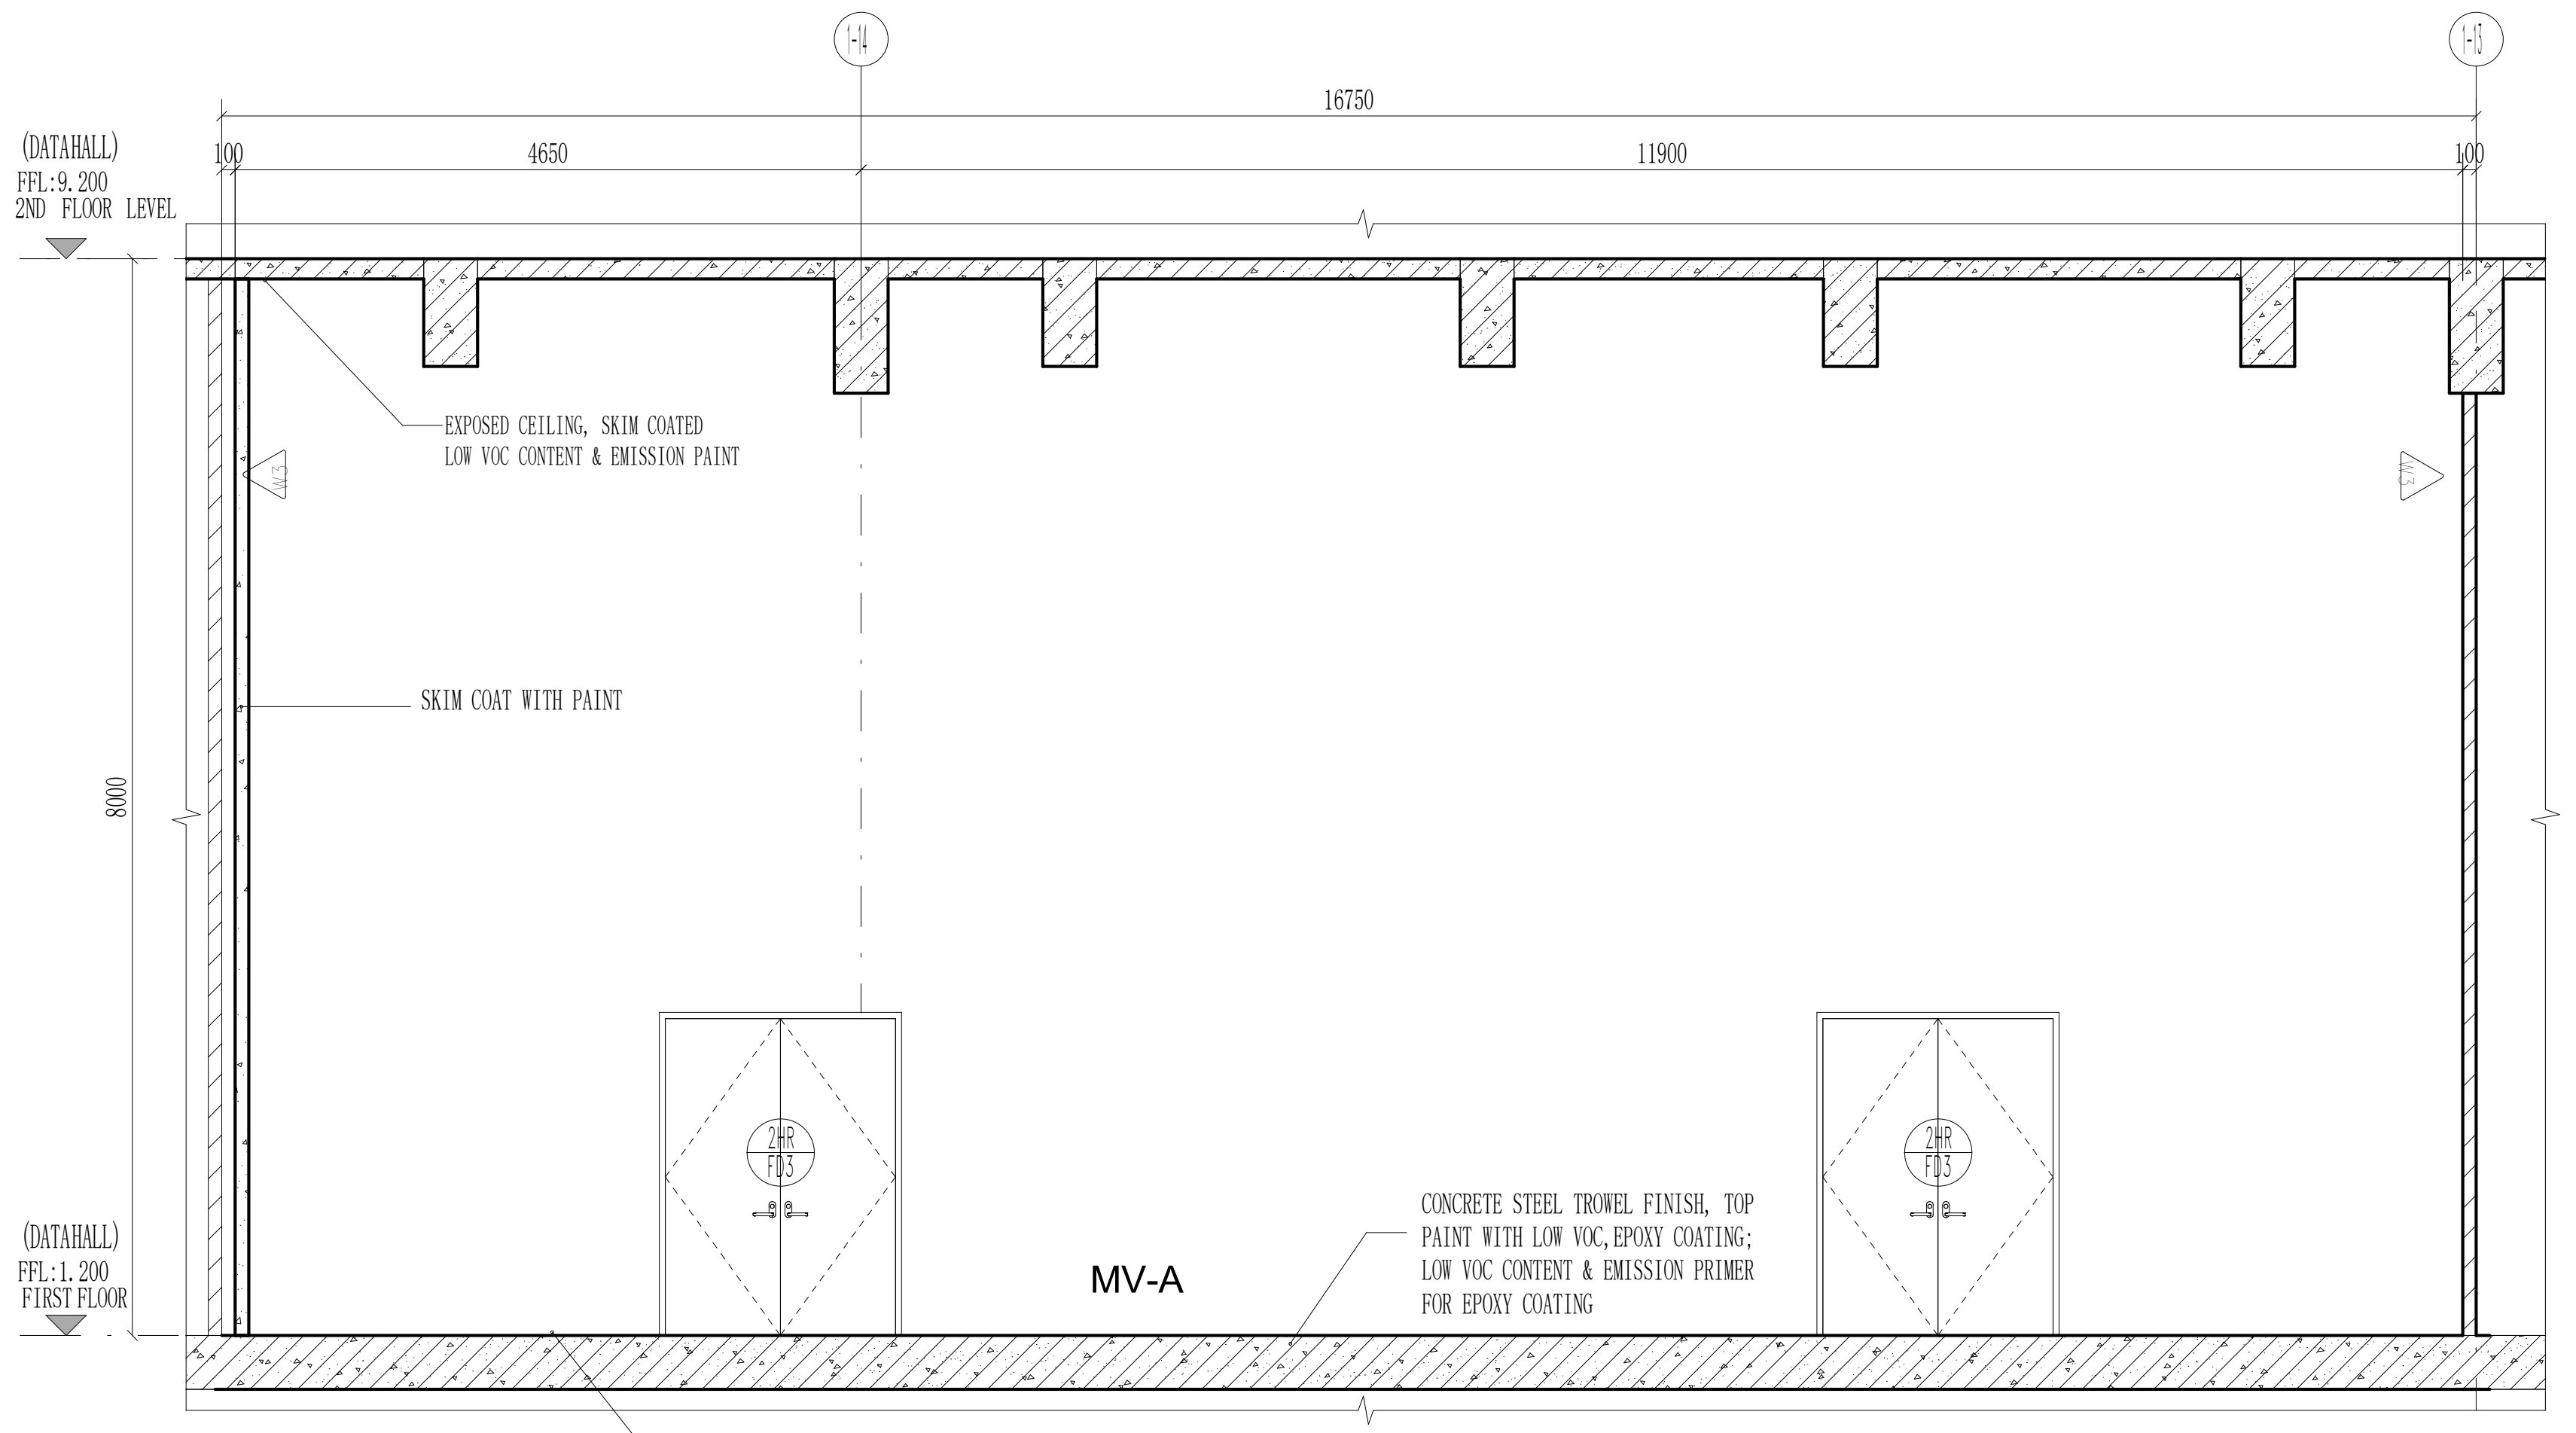
16750
100
4650
11900
100
(DATAHALL)
FFL:9.200
2ND FLOOR LEVEL
EXPOSED CEILING, SKIM COATED
LOW VOC CONTENT & EMISSION PAINT
SKIM COAT WITH PAINT
8000
(DATAHALL)
FFL:1.200
FIRST FLOOR
MV-A
CONCRETE STEEL TROWEL FINISH, TOP
PAINT WITH LOW VOC,EPOXY COATING;
LOW VOC CONTENT & EMISSION PRIMER
FOR EPOXY COATING
10mm THK STAINLESS STEEL

MV-A SECTION B-B

Scale 1:50

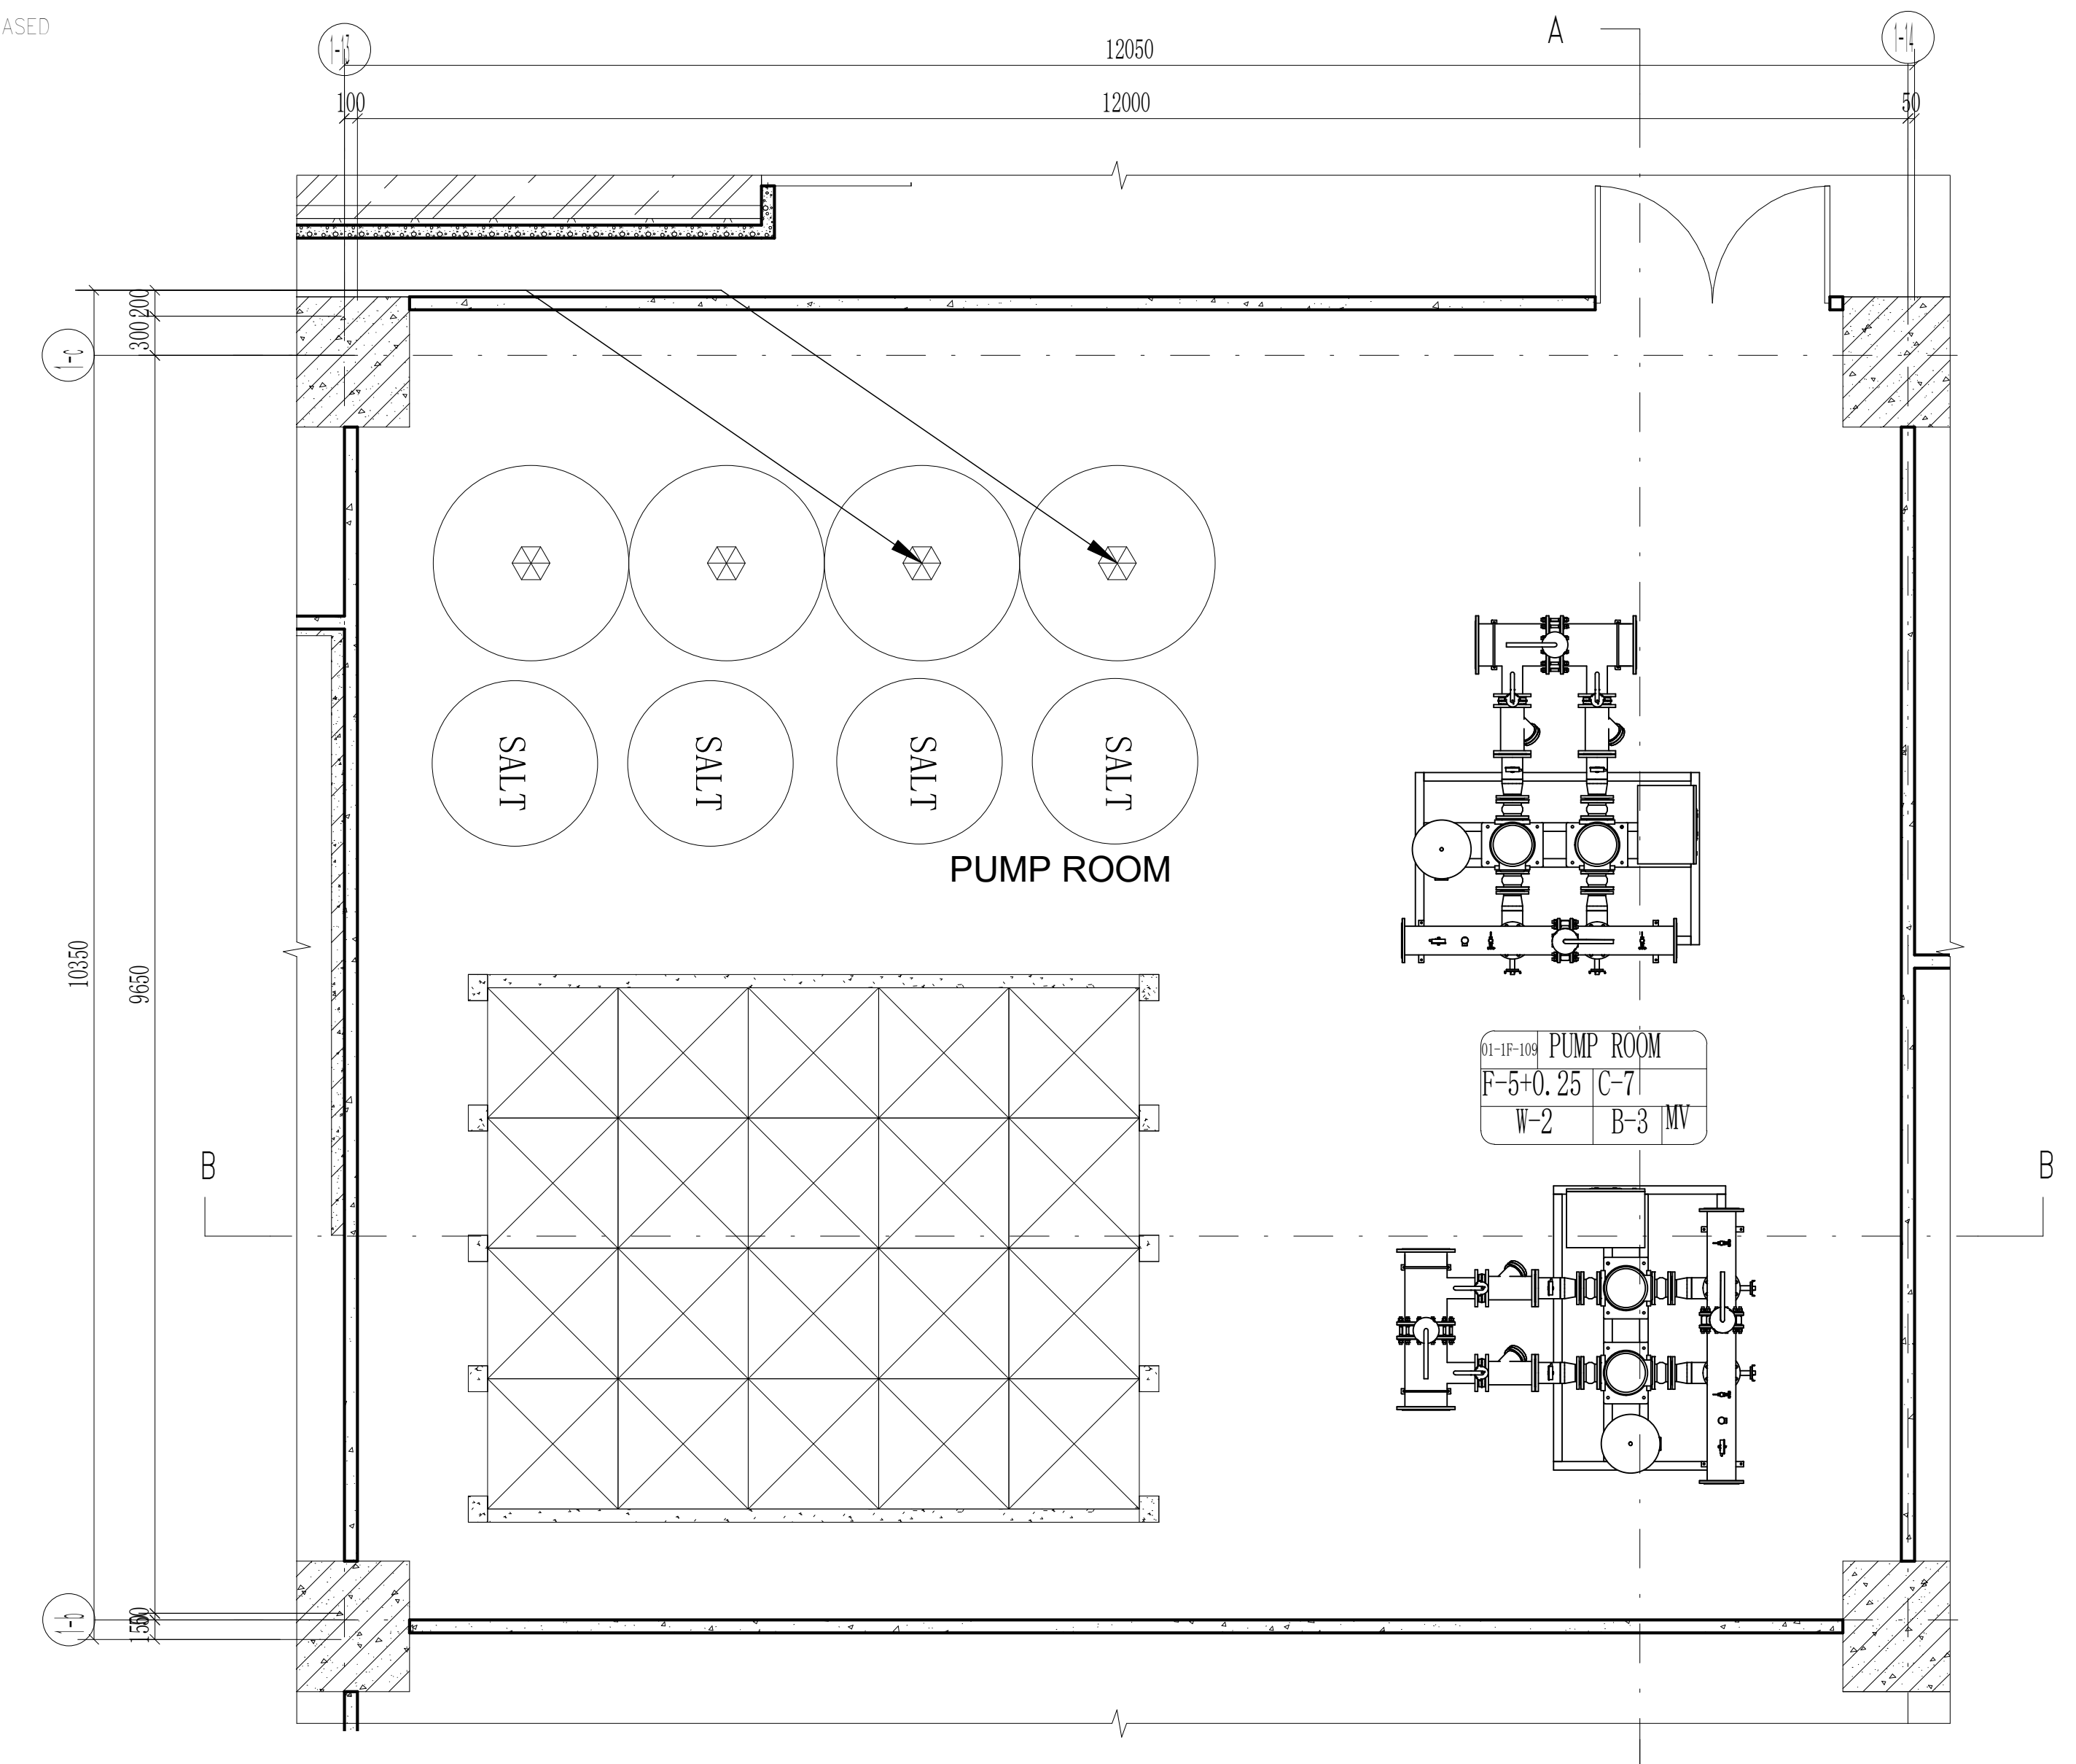
12050
100
12000
50
A
A
B
B
300
200
10350
9650
SALT
SALT
SALT
SALT
PUMP ROOM
01-1F-106
PUMP ROOM
F-5+0.25
C-7
W-2
B-3
MV

PUMP ROOM FIRST FLOOR PLAN

Scale 1:50

THE "SFL" MARKED IN THE DRAWING REFERS TO THE STRUCTURAL FLOOR LEVEL, WHILE THE FINISHED FLOOR LEVEL (FFL) IS DETERMINED BASED ON FLOOR FINISHES.

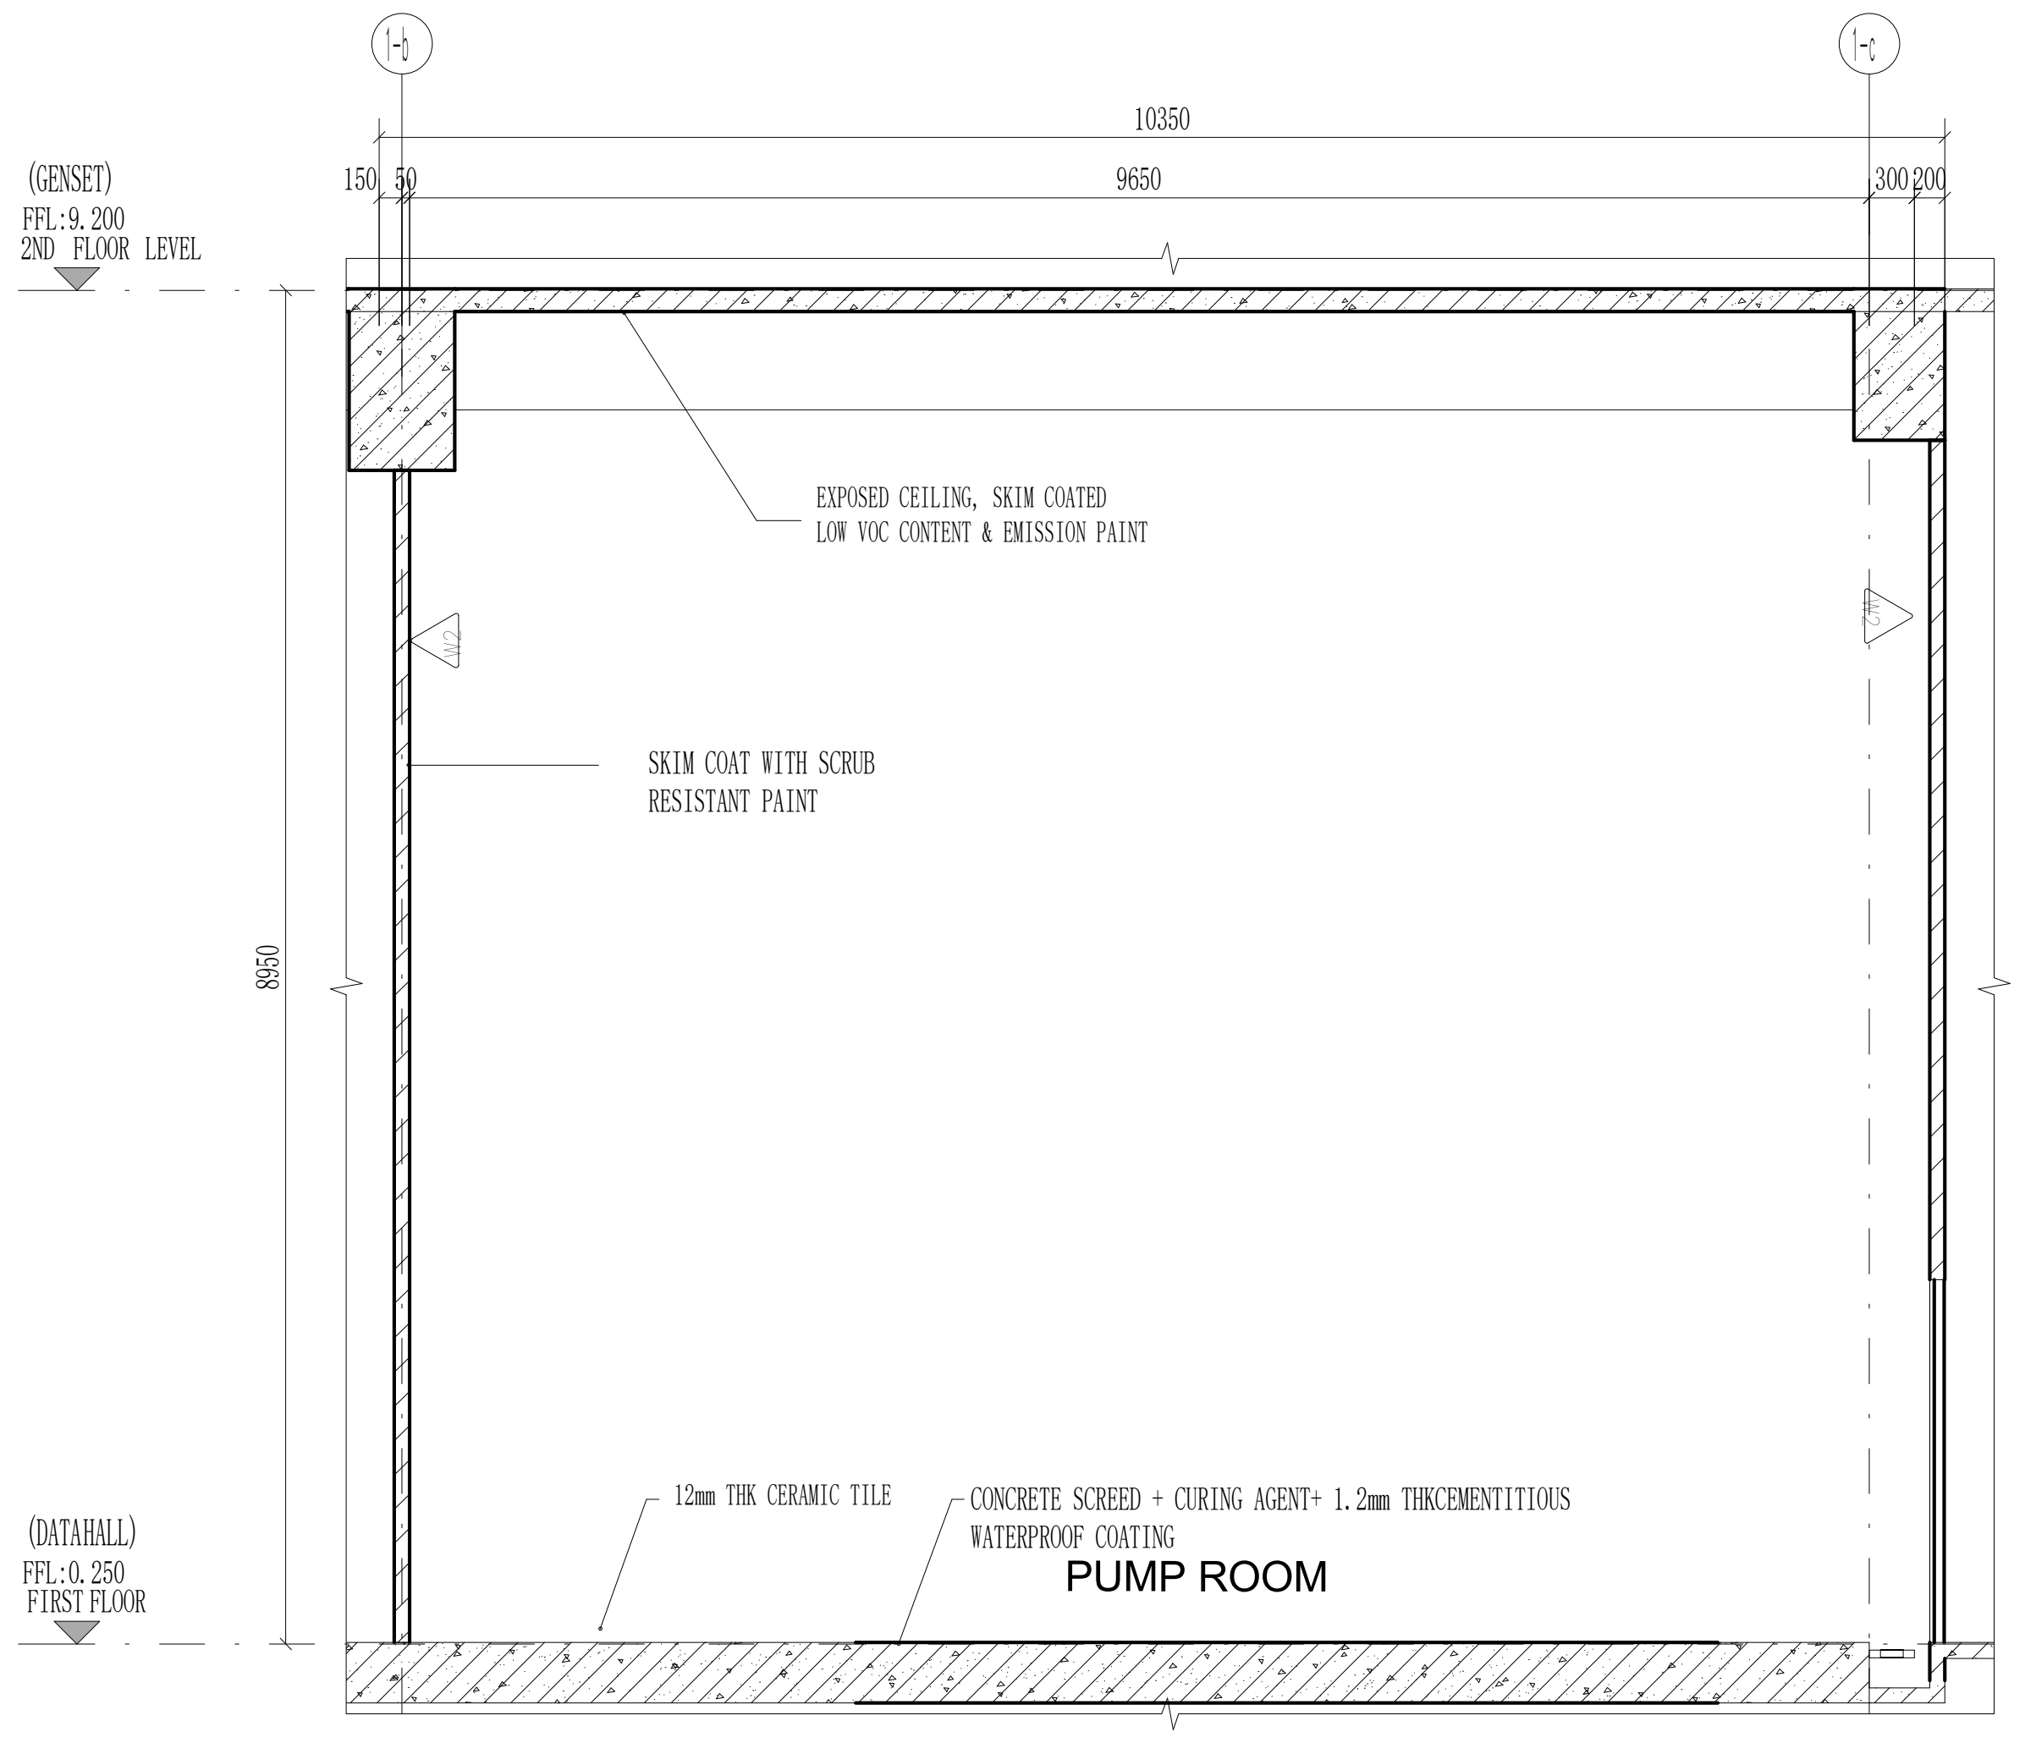
10350
130
50
9650
300
200
(GENSET)
FFL:9.200
2ND FLOOR LEVEL
EXPOSED CEILING, SKIM COATED
LOW VOC CONTENT & EMISSION PAINT
SKIM COAT WITH SCRUB
RESISTANT PAINT
8950
(DATAHALL)
FFL:0.250
FIRST FLOOR
12mm THK CERAMIC TILE
CONCRETE SCREED + CURING AGENT+ 1.2mm THKCEMENTITIOUS
WATERPROOF COATING
PUMP ROOM

PUMP ROOM SECTION A-A

Scale 1:50

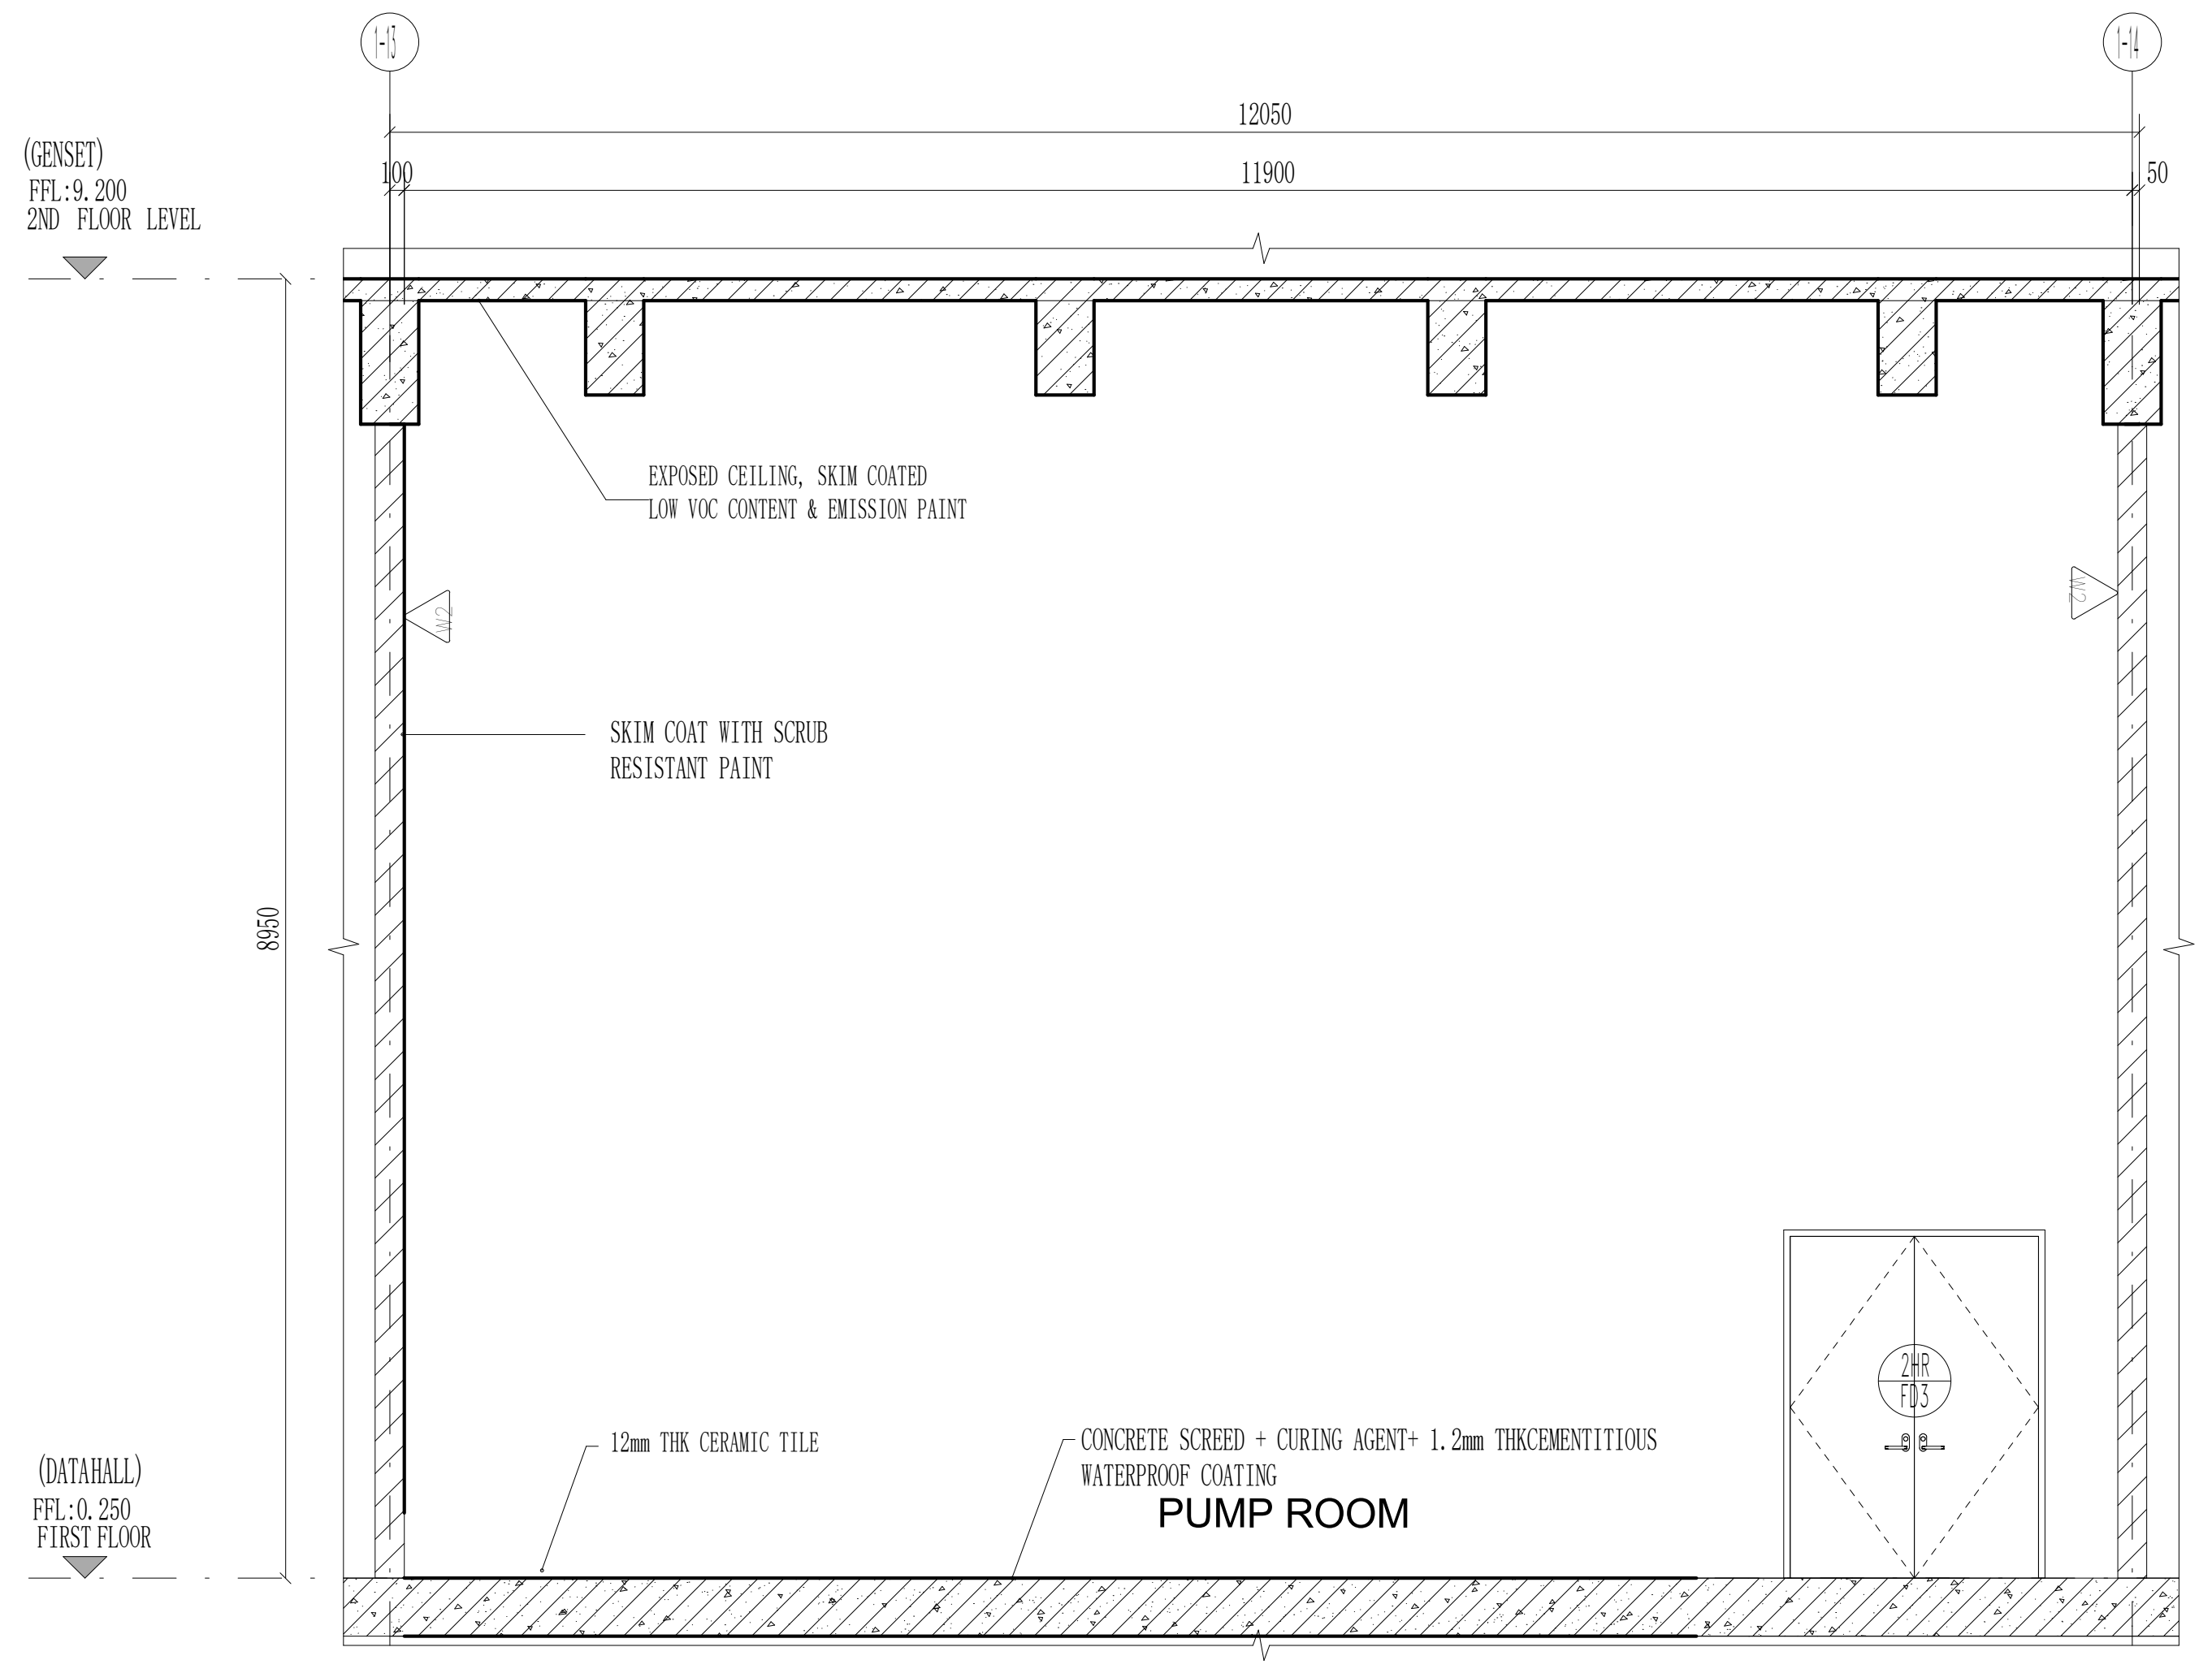
12050
100
11900
50
(GENSET)
FFL:9.200
2ND FLOOR LEVEL
EXPOSED CEILING, SKIM COATED
LOW VOC CONTENT & EMISSION PAINT
SKIM COAT WITH SCRUB
RESISTANT PAINT
8950
(DATAHALL)
FFL:0.250
FIRST FLOOR
12mm THK CERAMIC TILE
CONCRETE SCREED + CURING AGENT+ 1.2mm THKCEMENTITIOUS
WATERPROOF COATING
PUMP ROOM

PUMP ROOM SECTION B-B

Scale 1:50

CLIENT :

GULF EDGE DC 01

87 Wireless Road, M Thai Tower 11th. Floor, All Seasons Place, Lumpini,
Pathumwan, Bangkok 10330, Thailand

CONTRACTOR :

华西发展(泰国)有限公司
บริษัท หัวซือ ดีเวลลอปเม้นต์ (ประเทศไทย) จำกัด
HUASHI DEVELOPMENT CO.,LTD
No. 202, Room No. 1403, 14/F, Le Concorde Building,
Ratchadapisek Road, Huaykhwang Sub-District,
Huaykhwang District, Bangkok Metropolitan 10310.

CONSULTANT :

ARbay
บริษัท เอ อาร์ เบย์ จำกัด
ARbay Company Limited
31 st Floor Bangkok Insurance Building
25 South Sathorn road Thungmahamek
Sathorn Bangkok 10120 THAILAND
T +66 (0) 2286 8199
F +66 (0) 2286 2863
info@arbay.co.th

CONSULTANT :

Qbic Engineers & Architects Co.,Ltd.
8 Soi KALONG 4 SANAMBINNAM ROAD,
THASAI SUB-DISTRICT, MUANG NONTHABURI DISTRICT
, NONTHABURI.
Tel 662-950-4374
Fax 662-580-3231
E-Mail : qbic@qbic.co.th, www.qbic.co.th
QBIC ENGINEERS AND ARCHITECTS CO.,LTD.

CONSULTANT :

MITR
MITR TECHNICAL CONSULTANT CO.,LTD.
1168/8 12th FLOOR, LUMPINI TOWER BUILDING,
RAMA IV RD., THUNGMAHAMEK, SATHORN, BANGKOK 10120, THAILAND
TEL : 0-2679-9079-84
FAX : 0-2679-9085 E-mail: mitr_dd@mitr.com

Architect : SIGNATURE
ประกิต พนานุรัตน์ วสถ. 580
ที่อยู่
251/1 ถ.จารุเมือง แขวงรองเมือง เขตปทุมวัน
กรุงเทพมหานคร โทรศัพท์ 02-286-8199

Structural Engineer : SIGNATURE
วิศวกรผู้ออกแบบโครงสร้าง
ณัฐสม สงวนวงษ์ วย 1423
ที่อยู่
2/1 ซ.รามคำแหง 150 ถ.รามคำแหง
แขวง สะพานสูง เขต สะพานสูง กทม. 10240

Structural Inspector : SIGNATURE
วิศวกรผู้ตรวจสอบโครงสร้าง
โกมล จุฑาภัทร วย 964
ที่อยู่
24/18 ซ.นวมินทร์ 129 ถ. นวมินทร์
แขวง นวลจันทร์ เขต บึงกุ่ม กทม. 10230

Electrical Engineer : SIGNATURE
วิศวกรผู้ออกแบบระบบไฟฟ้ากำลัง
นายสุภัทร บูรณวิทย์ วฟก.1265
ที่อยู่
21 ซอยทานสัมฤทธิ์ 13
ตำบลท่าทราย อ.เมืองนนทบุรี จ.นนทบุรี 11000

Mechanical Engineer : SIGNATURE
วิศวกรผู้ออกแบบระบบเครื่องกลและปรับอากาศ
นายประสิทธิ์ เกี้ยวสุนทร วก.1221
ประสิทธิ์
ที่อยู่
44/372 ซอยบางกระดี่ 35/1 แขวงแสมดำ
เขตบางขุนเทียน กทม. 10150

Sanitary Engineer : SIGNATURE
วิศวกรผู้ออกแบบระบบสุขาภิบาล และดับเพลิง
นายทศวรรษ สนั่นฤทธิ์ วส. 215
ทศวรรษ
ที่อยู่
บ้านเลขที่ 99/107 หมู่ที่ 3 ต.ศีรษะจรเข้น้อย
อ.บางเสาธง จ.สมุทรปราการ 10540

ISSUE/REVISION

REV.	DESCRIPTION	DATE
A	90% DEVELOPED	09/05/2026

PROJECT NAME :

GEDC 01

LOCATION:
Nikhom Phattana district, Rayong ,industrial estate,CPGC

BUILDING :
MAIN BUILDING

90% DEVELOPED

TITLE :

ROOMDETAIL-1F-FUEL PUMPROOMA.
MV-A, PUMP ROOM

JOB NO.		SCALE	1 : 50
DRAWN	ZYY	REF.	
CHECKED	LJC	DWG. NO.	MPK01A-90-A-RD-122
APPROVED	LXD		
DATE	2026.05.09		