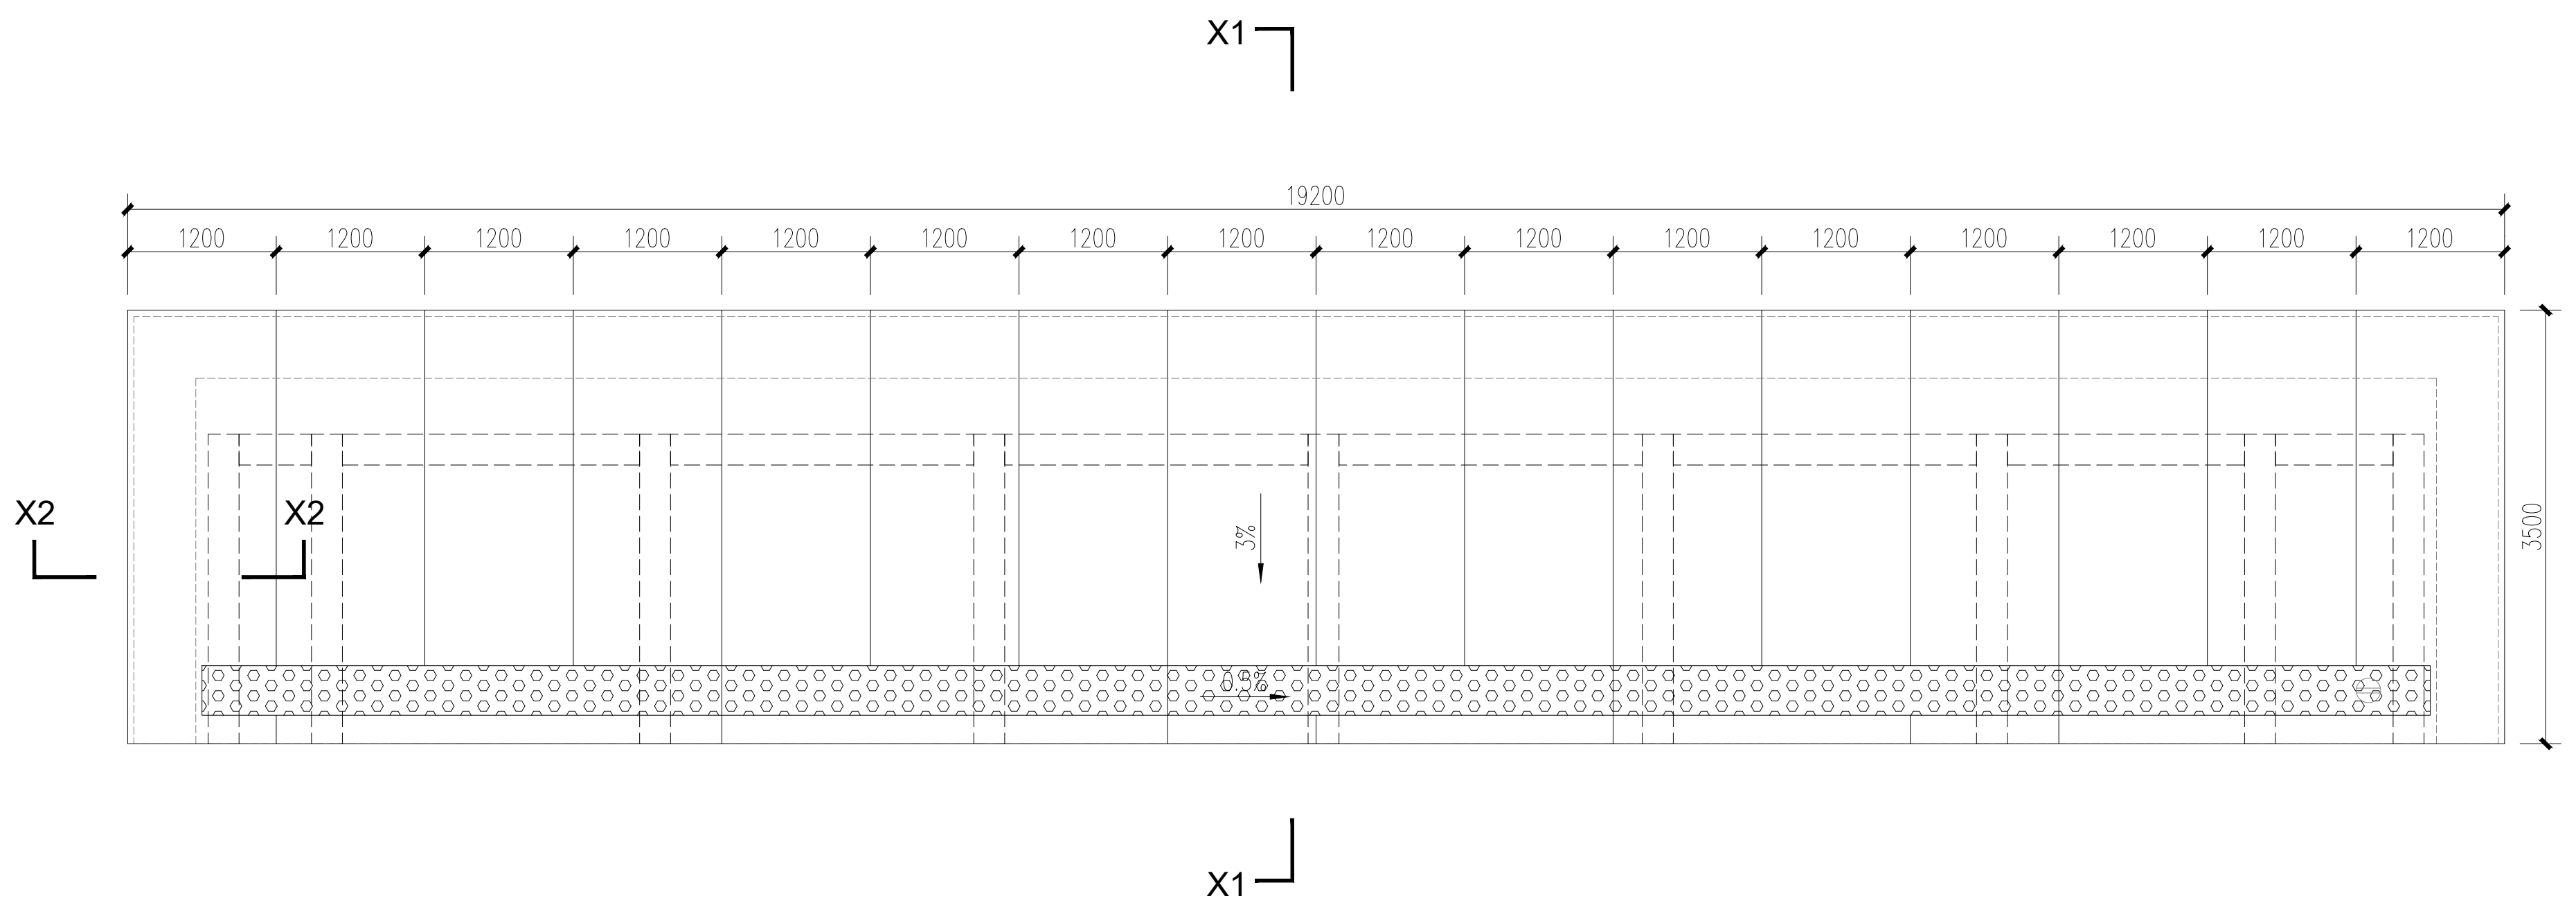
X1
X2
X2
X1
19200
1200
1200
1200
1200
1200
1200
1200
1200
1200
1200
1200
1200
1200
1200
1200
1200
3500
3%

PLAN VIEW OF CANOPY 01 1:50

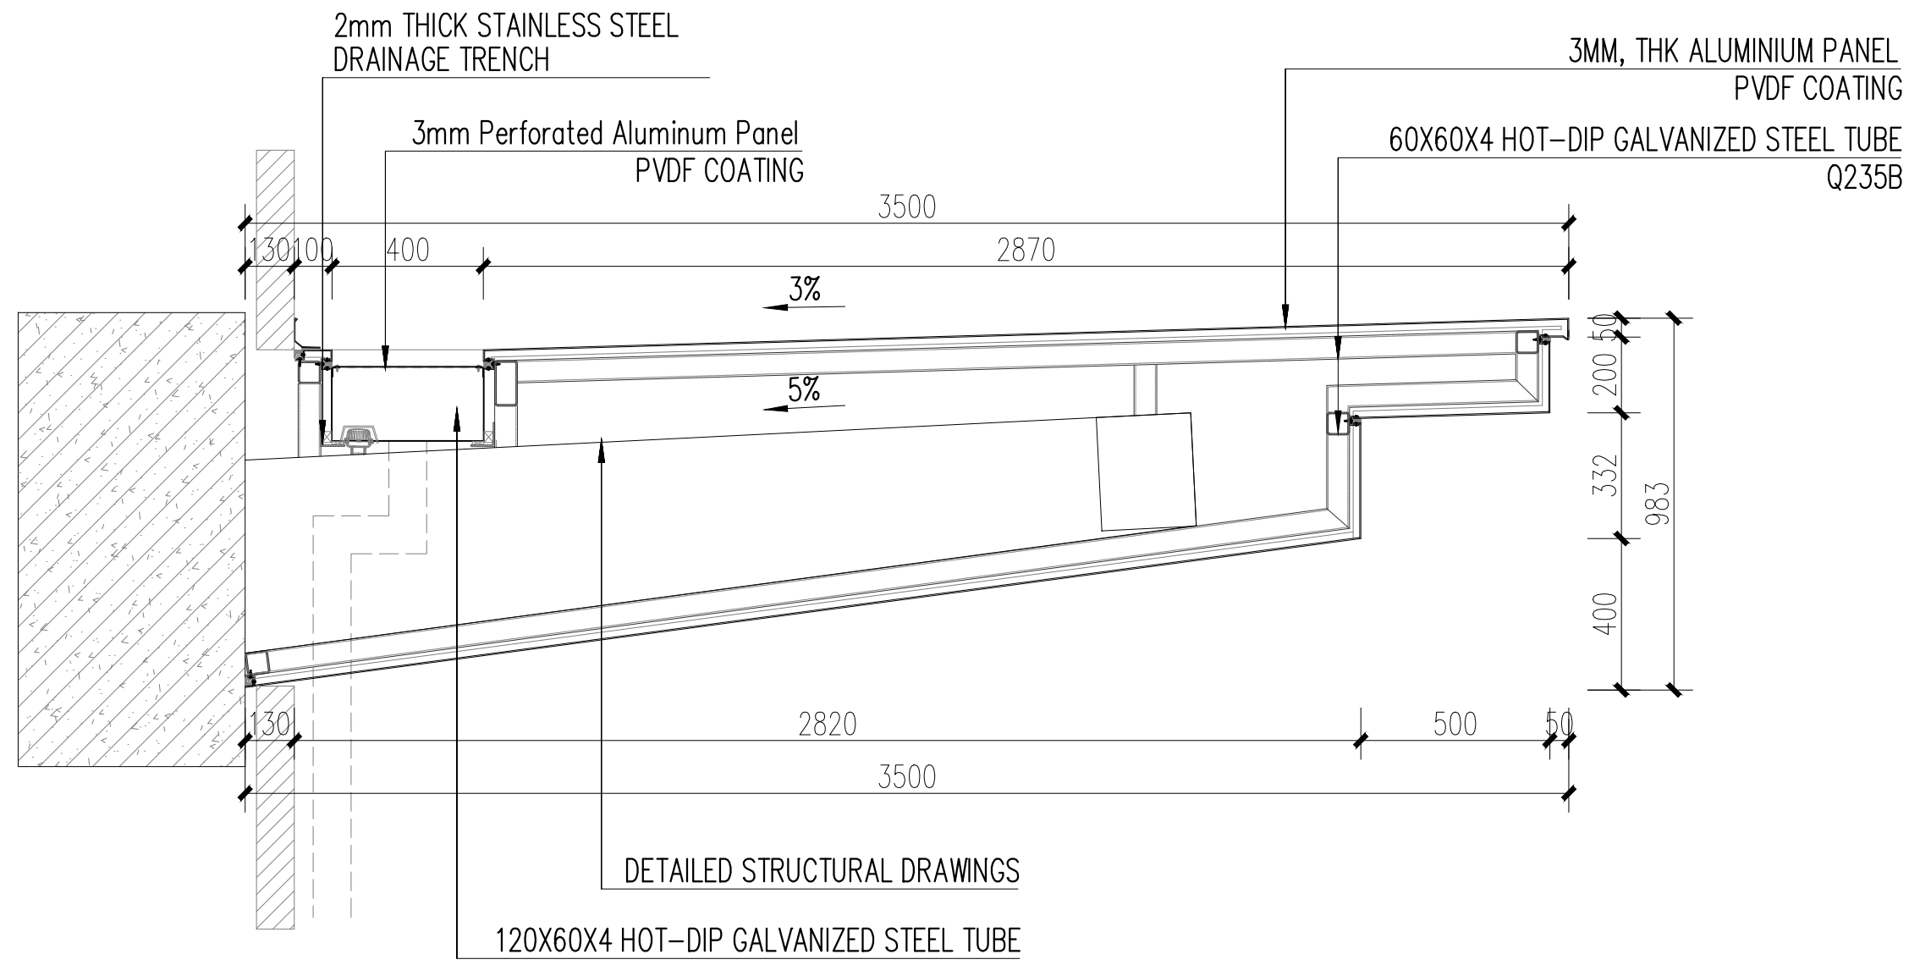
2mm THICK STAINLESS STEEL
DRAINAGE TRENCH
3mm Perforated Aluminum Panel
PVDF COATING
3MM, THK ALUMINIUM PANEL
PVDF COATING
60X60X4 HOT–DIP GALVANIZED STEEL TUBE
Q235B
3500
130
100
400
2870
3%
5%
50
200
332
400
983
130
2820
500
50
3500
DETAILED STRUCTURAL DRAWINGS
120X60X4 HOT–DIP GALVANIZED STEEL TUBE
Q235B

SECTION X1-X1 1:50

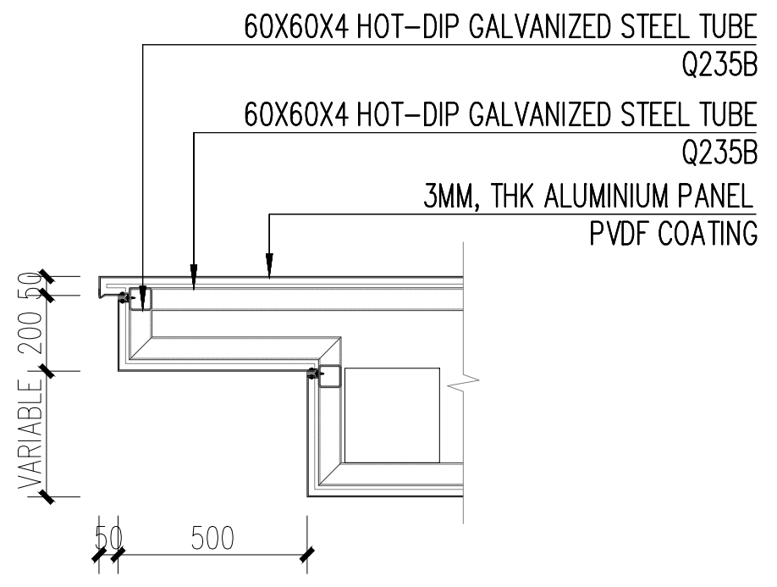
60X60X4 HOT–DIP GALVANIZED STEEL TUBE
Q235B
60X60X4 HOT–DIP GALVANIZED STEEL TUBE
Q235B
3MM, THK ALUMINIUM PANEL
PVDF COATING
200
VARIABLE
50
500

SECTION X2-X2 1:50

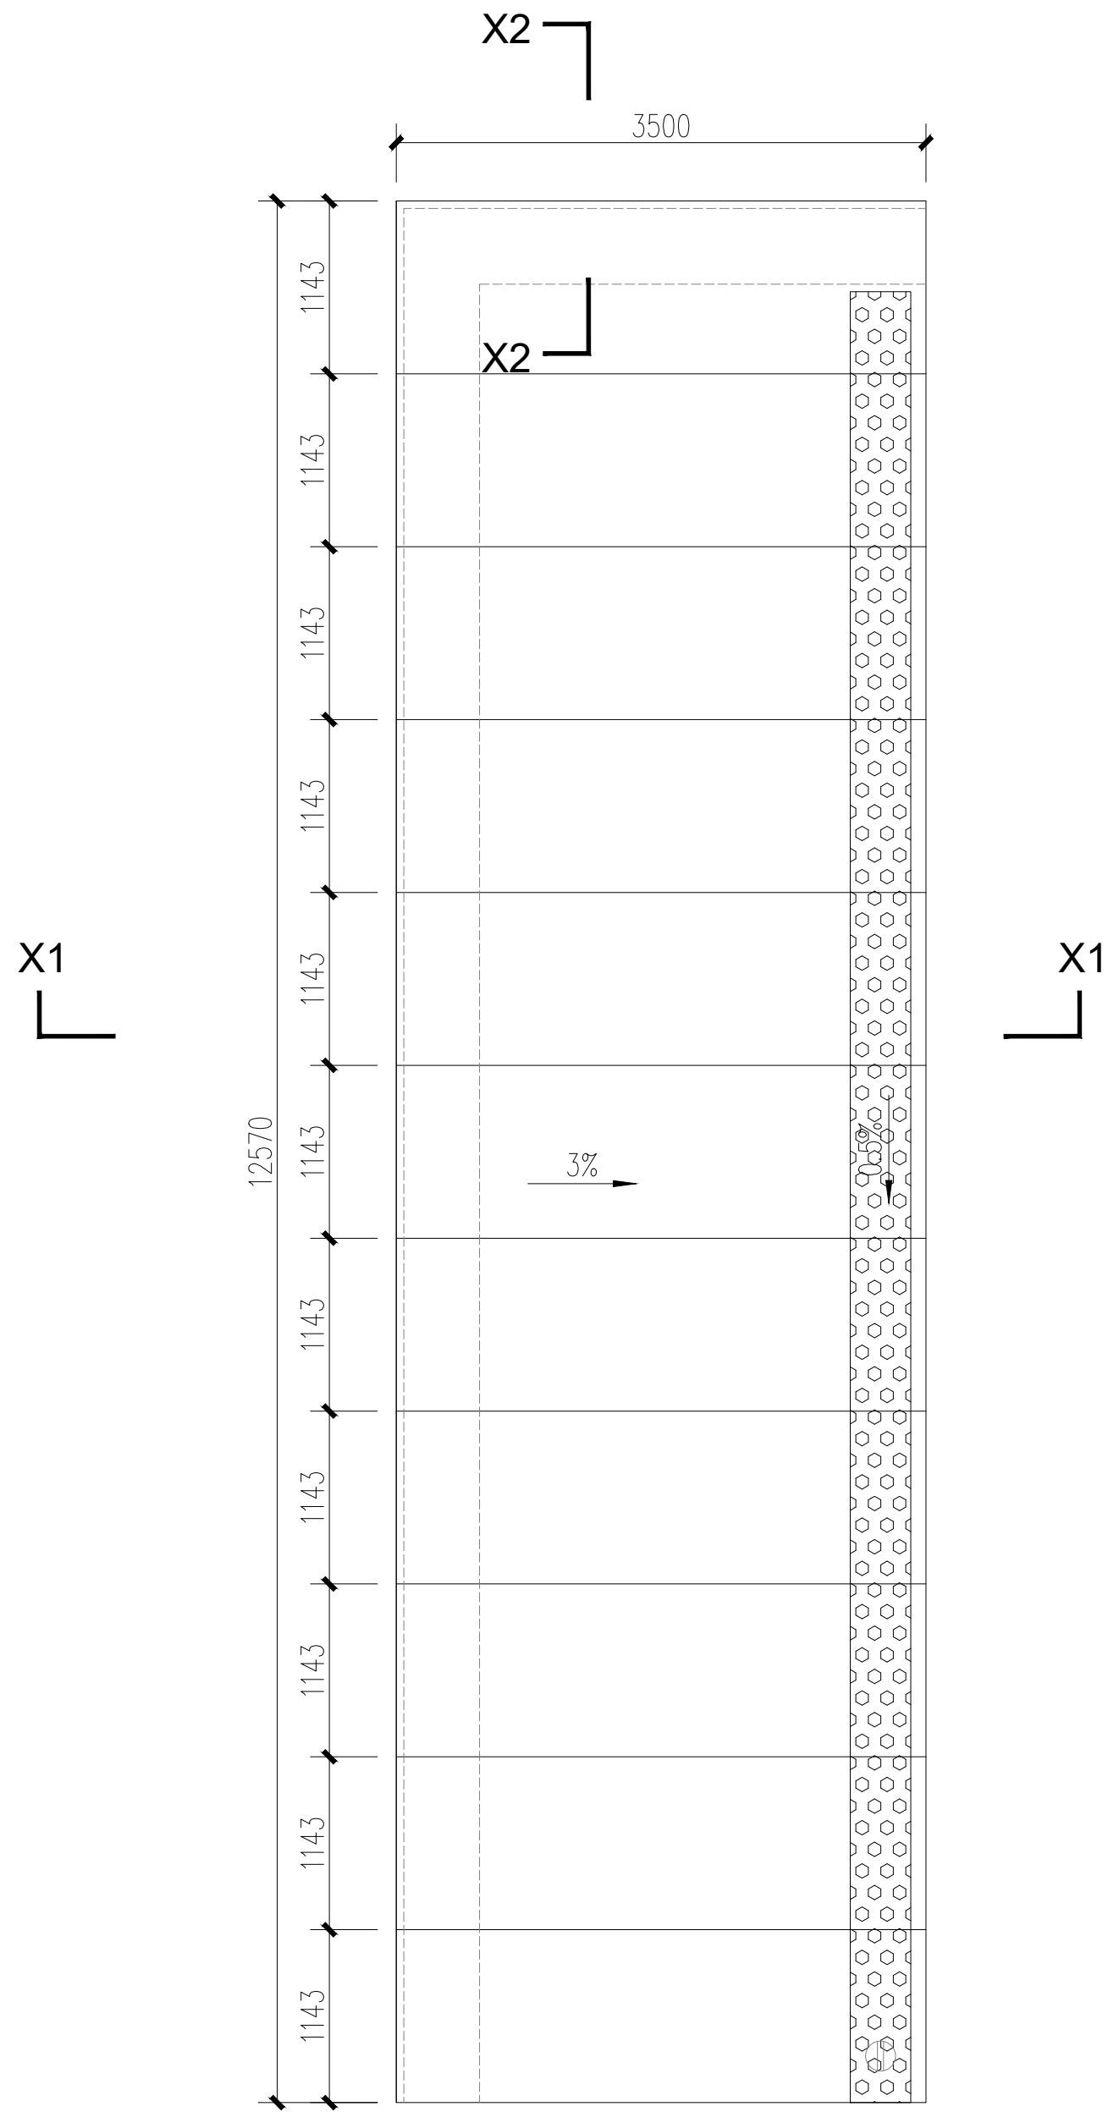
X2
X2
X1
X1
3500
1143
1143
1143
1143
1143
1143
1143
1143
1143
1143
1143
12570
3%

PLAN VIEW OF CANOPY 02 1:50

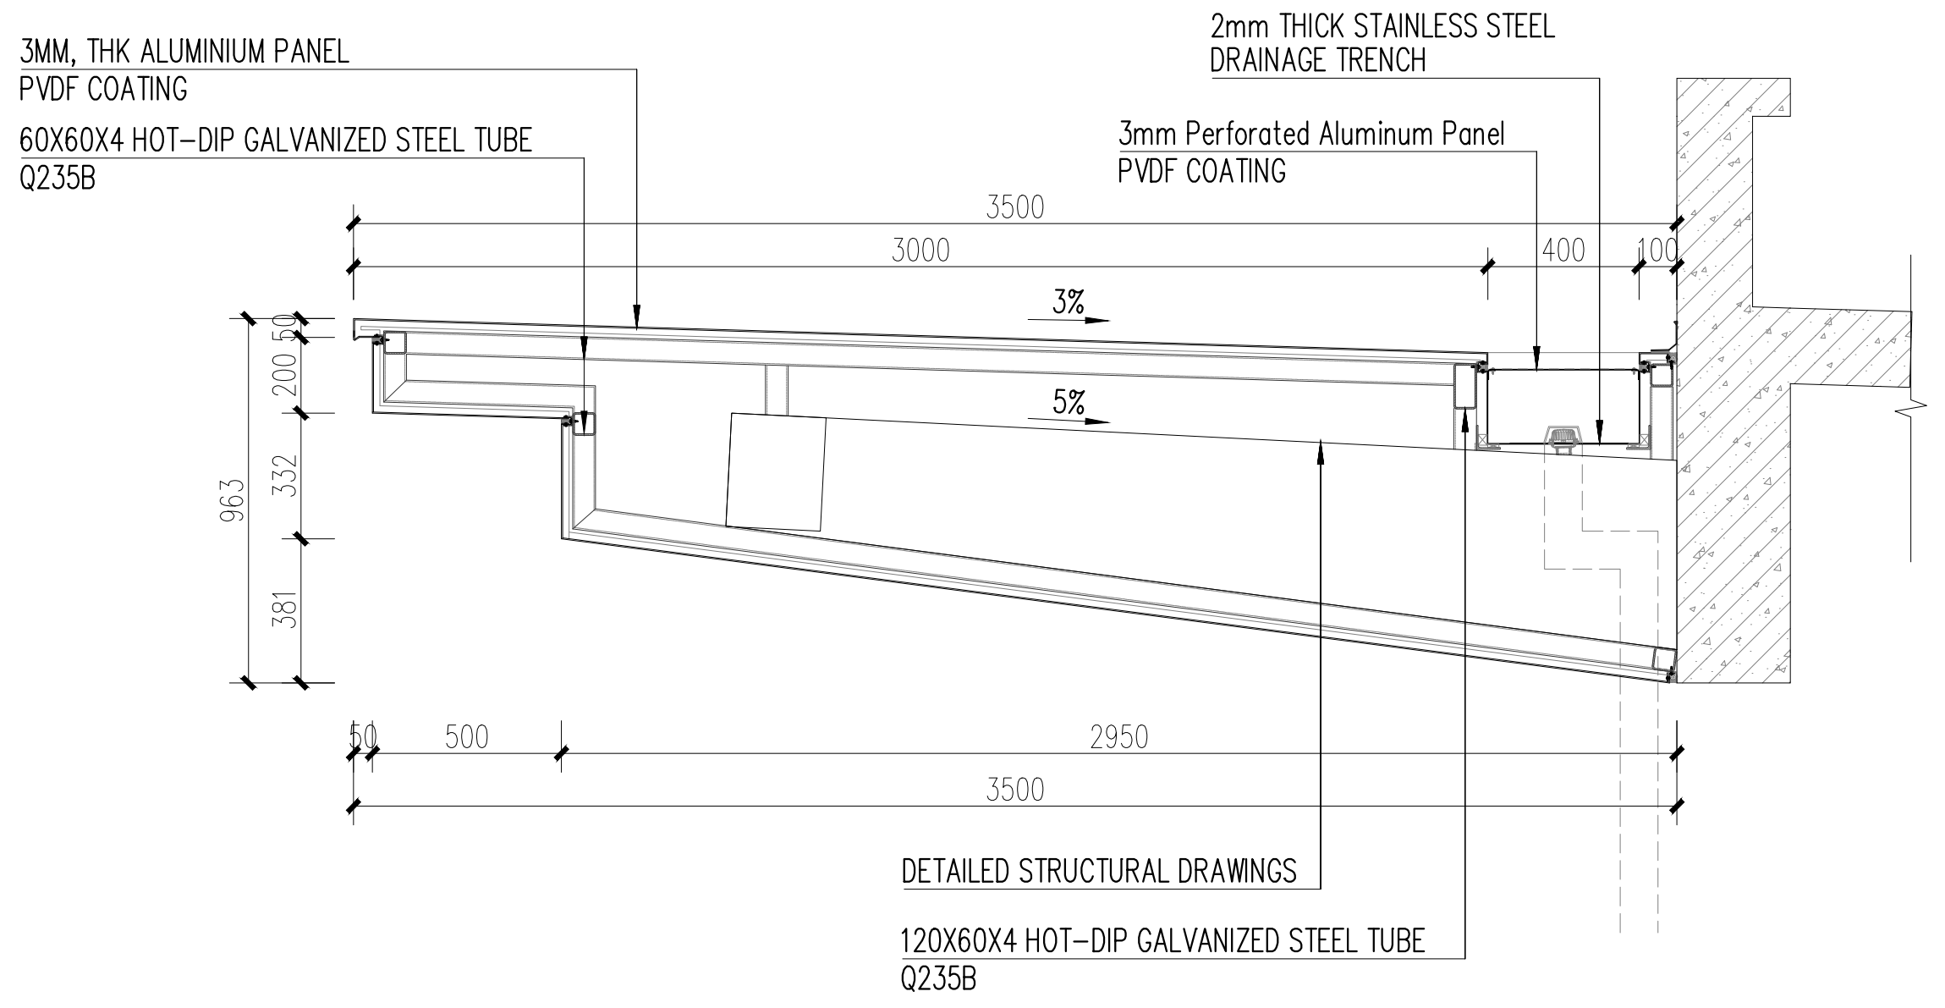
3MM, THK ALUMINIUM PANEL
PVDF COATING
60X60X4 HOT–DIP GALVANIZED STEEL TUBE
Q235B
2mm THICK STAINLESS STEEL
DRAINAGE TRENCH
3mm Perforated Aluminum Panel
PVDF COATING
3500
3000
400
100
3%
5%
50
200
332
381
963
50
500
2950
3500
DETAILED STRUCTURAL DRAWINGS
120X60X4 HOT–DIP GALVANIZED STEEL TUBE
Q235B

SECTION X1-X1 1:50

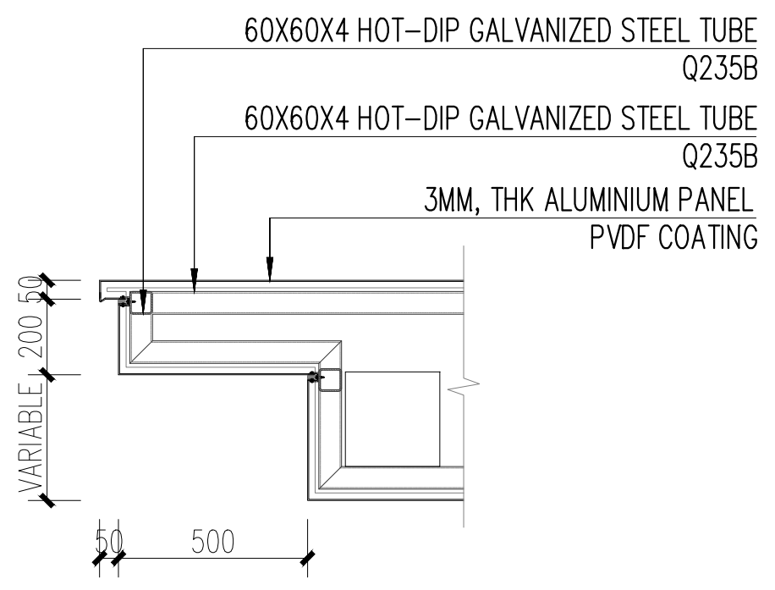
60X60X4 HOT–DIP GALVANIZED STEEL TUBE
Q235B
60X60X4 HOT–DIP GALVANIZED STEEL TUBE
Q235B
3MM, THK ALUMINIUM PANEL
PVDF COATING
200
VARIABLE
50
500

SECTION X2-X2 1:50

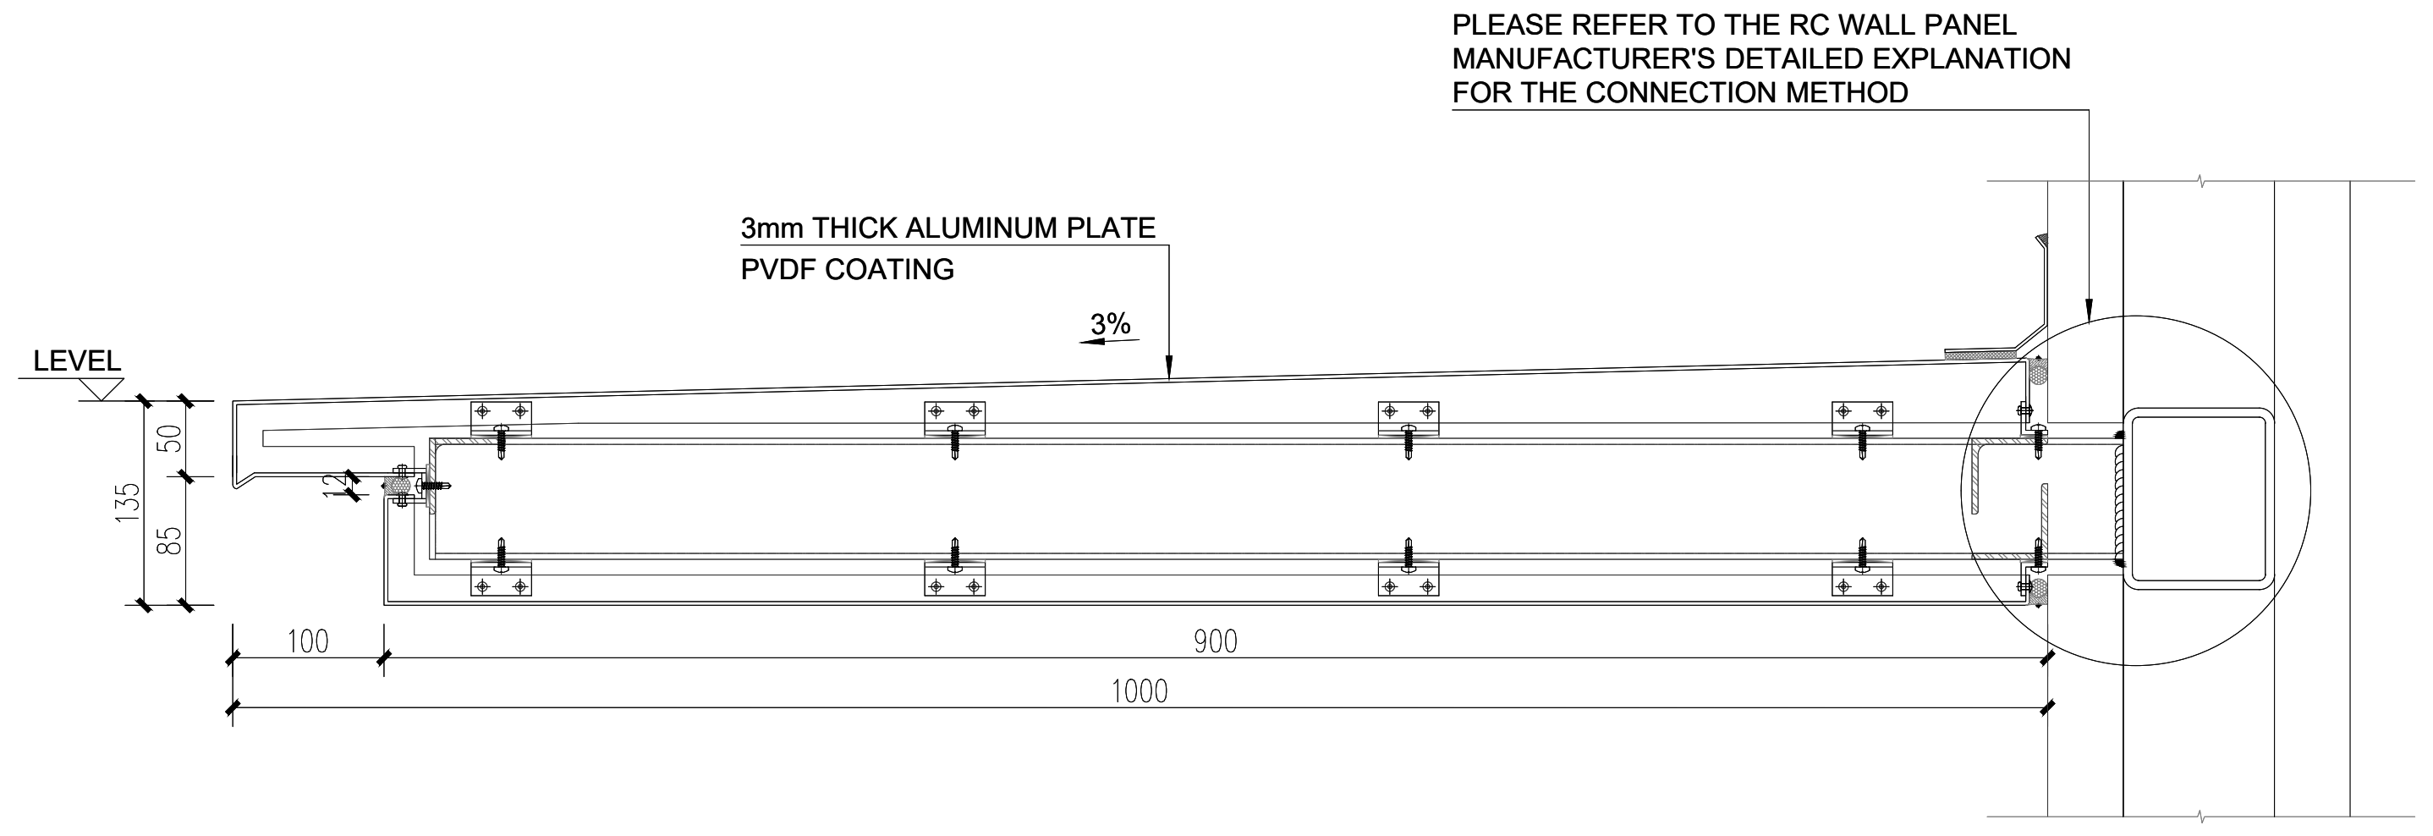
PLEASE REFER TO THE RC WALL PANEL
MANUFACTURER'S DETAILED EXPLANATION
FOR THE CONNECTION METHOD
3mm THICK ALUMINUM PLATE
PVDF COATING
3%
LEVEL
50
135
85
100
900
1000

SMALL CANOPY DETAIL 01 1:5

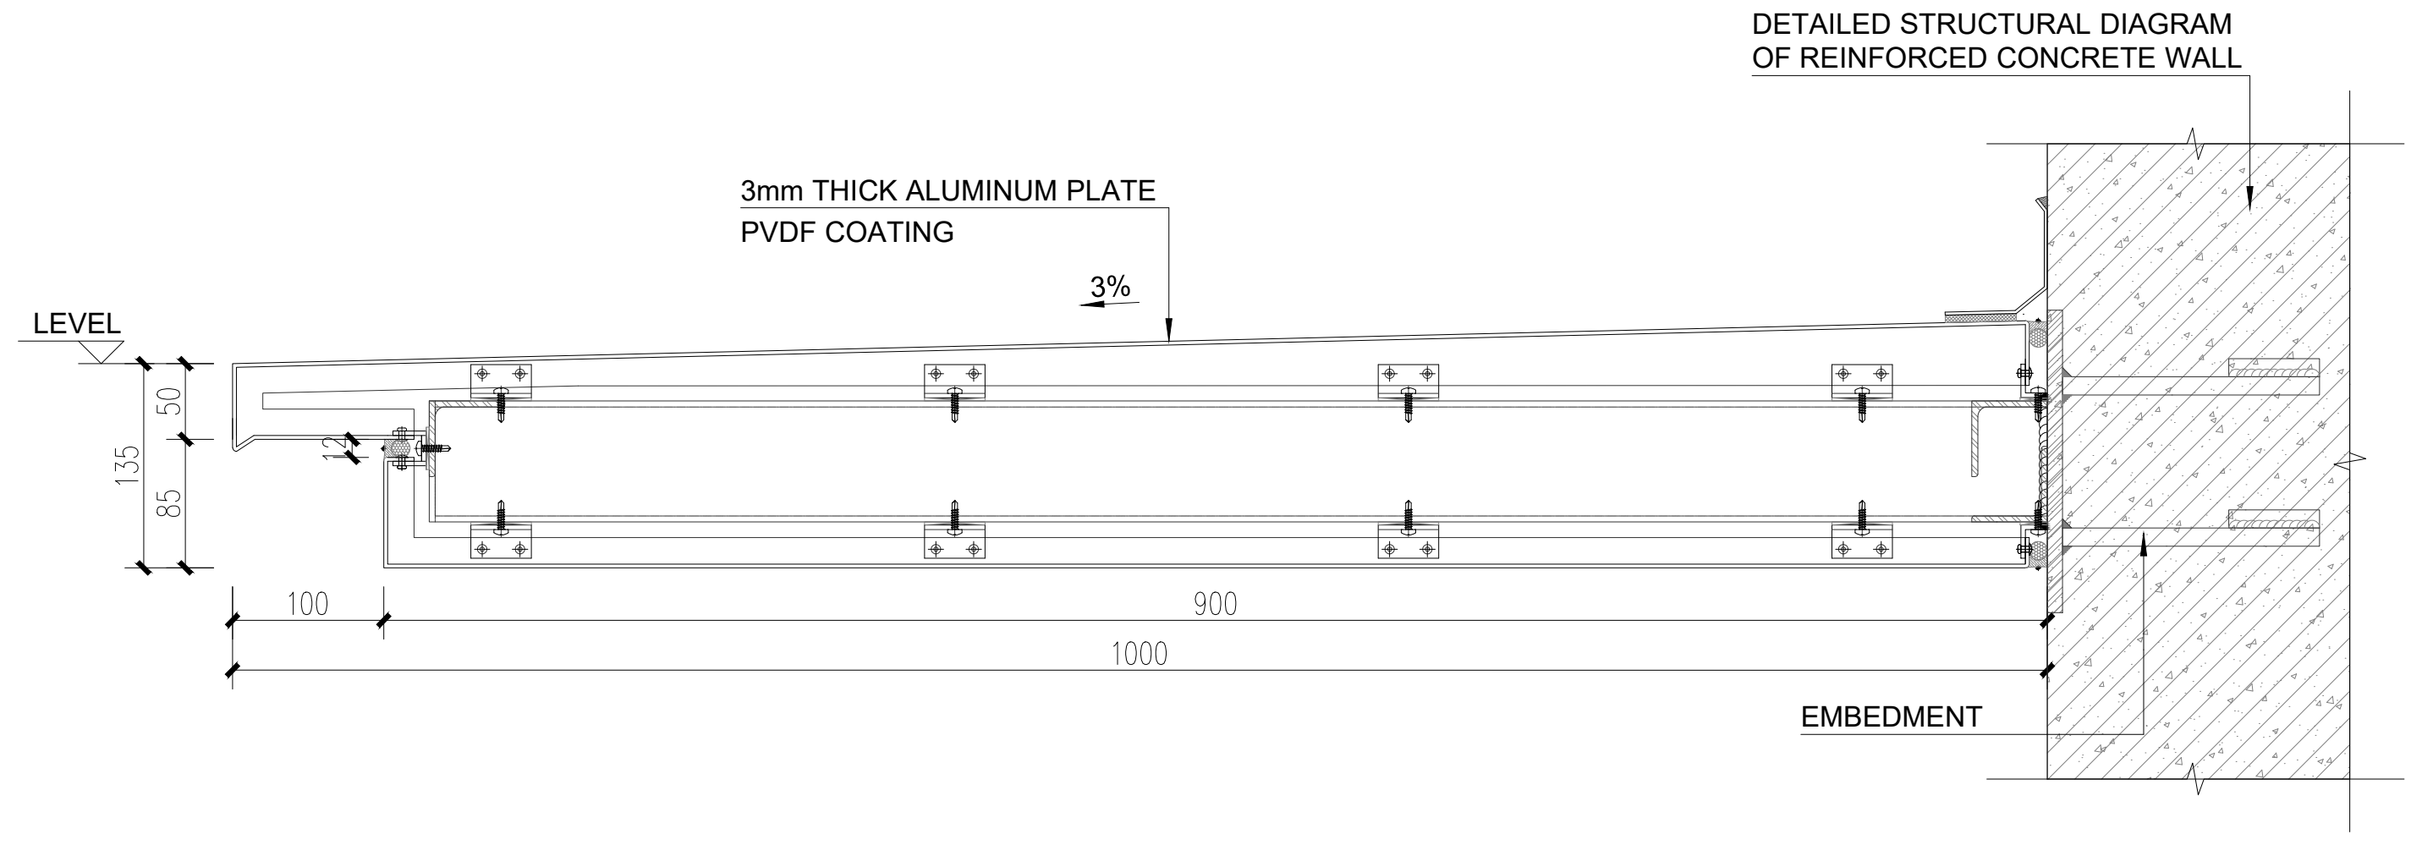
DETAILED STRUCTURAL DIAGRAM
OF REINFORCED CONCRETE WALL
3mm THICK ALUMINUM PLATE
PVDF COATING
3%
LEVEL
50
135
85
100
900
1000
EMBEDMENT

SMALL CANOPY DETAIL 02 1:5

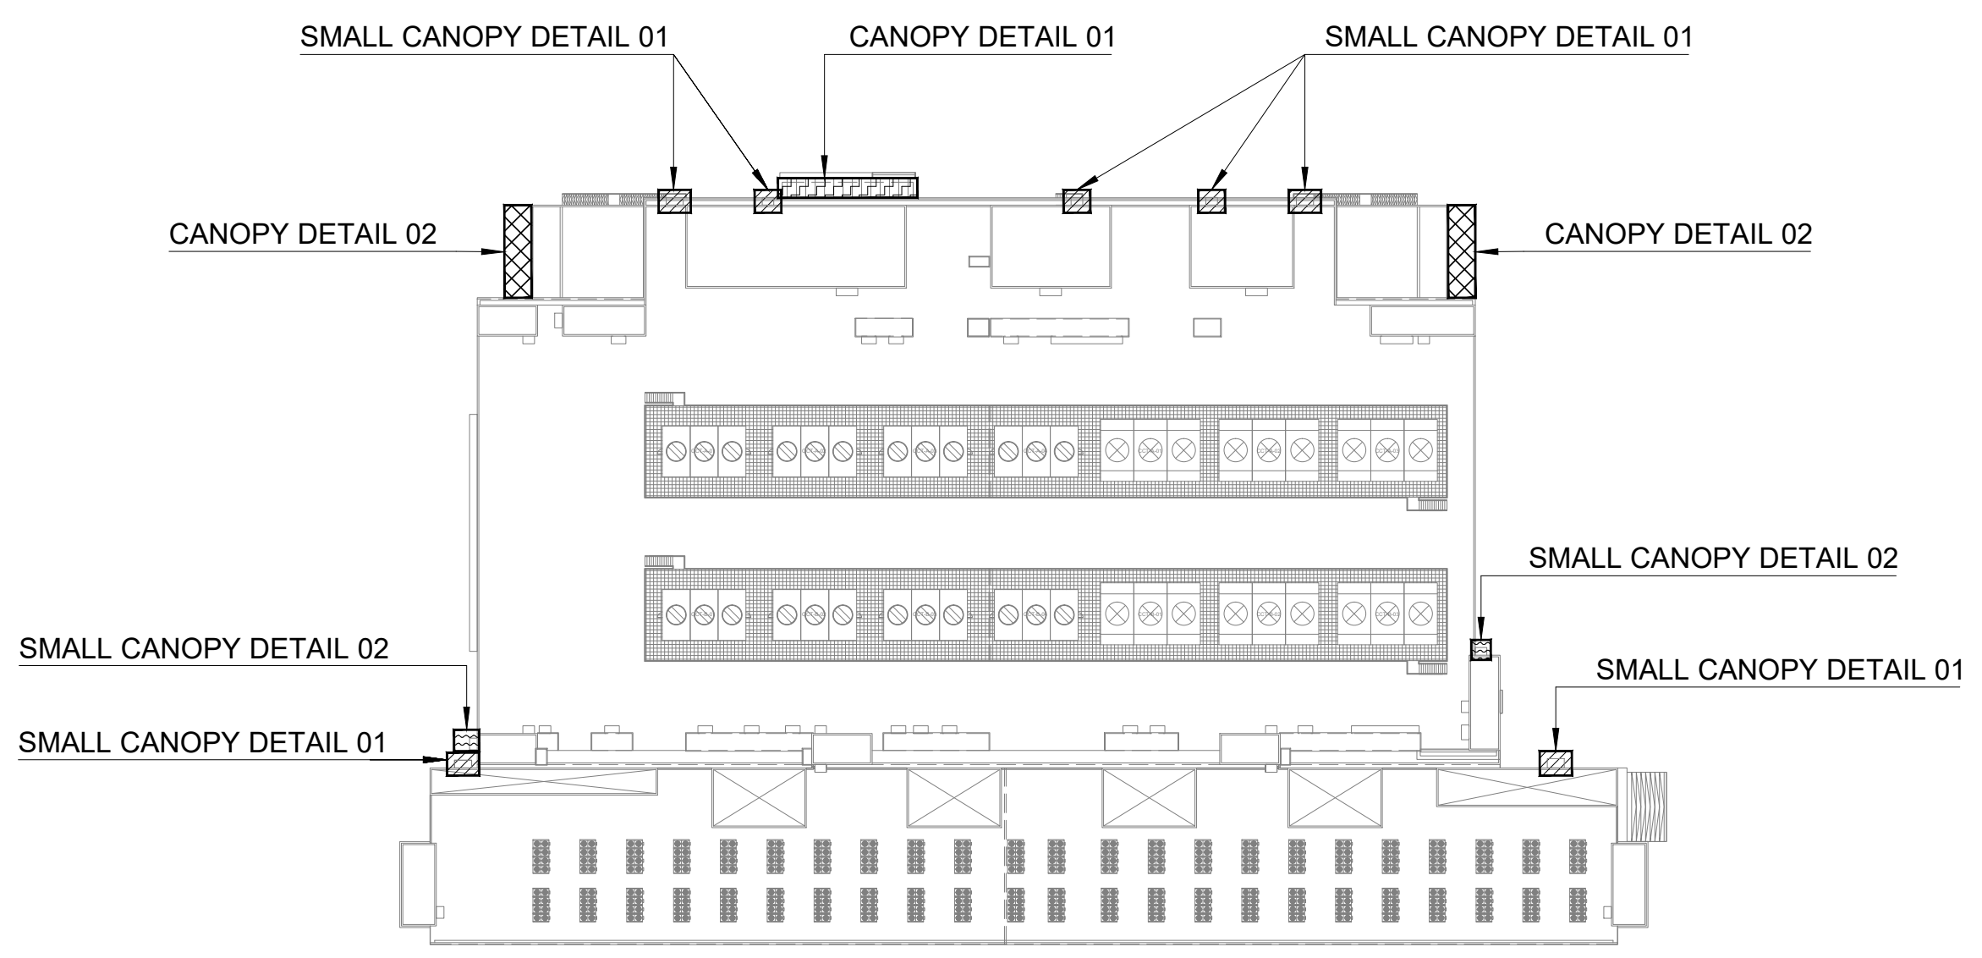
SMALL CANOPY DETAIL 01
CANOPY DETAIL 01
SMALL CANOPY DETAIL 01
CANOPY DETAIL 02
CANOPY DETAIL 02
SMALL CANOPY DETAIL 02
SMALL CANOPY DETAIL 02
SMALL CANOPY DETAIL 01
SMALL CANOPY DETAIL 01

NOTE : THIS PRINT IS OF A CONFIDENTIAL NATURE, IT SHALL NOT BE TRACED,PHOTOGRAPHED,PHOTOSTATED OR REPRODUCED IN ANY MANER,NOR USED FOR ANY PURPOSE WHATSOEVER EXCEPT BY WRITTEN PERMISSION

CLIENT :

GULF EDGE DC 01

87 Wireless Road, M Thai Tower 11th. Floor, All Seasons Place, Lumpini,
Pathumwan, Bangkok 10330, Thailand

CONTRACTOR :

华西发展(泰国)有限公司
บริษัท หัวซือ ดีเวลลอปเม้นต์ (ประเทศไทย) จำกัด
HUASHI DEVELOPMENT CO.,LTD
No. 202, Room No. 1403, 14/F, Le Concorde Building,
Ratchadapisek Road, Huaykhwang Sub-District,
Huaykhwang District, Bangkok Metropolitan 10310.

CONSULTANT :

ARbay
บริษัท เอ อาร์ เบย์ จำกัด
ARbay Company Limited
31 st Floor Bangkok Insurance Building
25 South Sathorn road Thungmahamek
Sathorn Bangkok 10120 THAILAND
T +66 (0) 2286 8199
F +66 (0) 2286 2863
info@arbay.co.th

CONSULTANT :

Qbic Engineers & Architects Co.,Ltd.
8 Soi KALONG 4 SANAMBINNAM ROAD,
THASAI SUB-DISTRICT, MUANG NONTHABURI DISTRICT
, NONTHABURI.
Tel 662-950-4374
Fax 662-580-3231
E-Mail : qbic@qbic.co.th, www.qbic.co.th
QBIC ENGINEERS AND ARCHITECTS CO.,LTD.

CONSULTANT :

MITR
MITR TECHNICAL CONSULTANT CO.,LTD.
1168/8 12th FLOOR, LUMPINI TOWER BUILDING,
RAMA IV RD., THUNGMAHAMEK, SATHORN, BANGKOK 10120, THAILAND
TEL : 0-2679-9079-84
FAX : 0-2679-9085 E-mail: mitr_dd@mitr.com

Architect :	SIGNATURE
ประกิต พนานุรัตน์ วสถ. 580 ที่อยู่ 251/1 ถ.จารุเมือง แขวงรองเมือง เขตปทุมวัน กรุงเทพมหานคร โทรศัพท์ 02-286-8199	
Structural Engineer :	SIGNATURE
วิศวกรผู้ออกแบบโครงสร้าง	
ณัฐสม สงวนวงษ์ วย 1423 ที่อยู่ 2/1 ซ.รามคำแหง 150 ถ.รามคำแหง แขวง สะพานสูง เขต สะพานสูง กทม. 10240	
Structural Inspector :	SIGNATURE
วิศวกรผู้ตรวจสอบโครงสร้าง	
โกมล จุฑาภัทร วย 964 ที่อยู่ 24/18 ซ.นวมินทร์ 129 ถ. นวมินทร์ แขวง นวลจันทร์ เขต บึงกุ่ม กทม. 10230	
Electrical Engineer :	SIGNATURE
วิศวกรผู้ออกแบบระบบไฟฟ้ากำลัง	
นายสุภัทร บูรณวิทย์ วฟก.1265 ที่อยู่ 21 ซอยทานสัมฤทธิ์ 13 ตำบลท่าทราย อ.เมืองนนทบุรี จ.นนทบุรี 11000	
Mechanical Engineer :	SIGNATURE
วิศวกรผู้ออกแบบระบบเครื่องกลและปรับอากาศ	
นายประสิทธิ์ เกียวสุนทร วก.1221 ที่อยู่ 44/372 ซอยบางกระดี่ 35/1 แขวงแสมดำ เขตบางขุนเทียน กทม. 10150	ประสิทธิ์
Sanitary Engineer :	SIGNATURE
วิศวกรผู้ออกแบบระบบสุขาภิบาล และดับเพลิง	
นายทศวรรษ สันนฤทธิ์ วส. 215 ที่อยู่ บ้านเลขที่ 99/107 หมู่ที่ 3 ต.ศีรษะจรเข้น้อย อ.บางเสาธง จ.สมุทรปราการ 10540	ทศวรรษ

ISSUE/REVISION

REV.	DESCRIPTION	DATE
A	90% DEVELOPED	09/05/2026

PROJECT NAME :

GEDC 01

LOCATION:
Nikhom Phattana district, Rayong ,industrial estate,CPGC

BUILDING :
MAIN BUILDING

90% DEVELOPED

TITLE :

CANOPY DETAILS

JOB NO.	SCALE 1:50
DRAWN FLY	REF.
CHECKED LJC	DWG.NO. MPK01A-90-A-CD-001
APPROVED LXD	
DATE 2026.05.09	