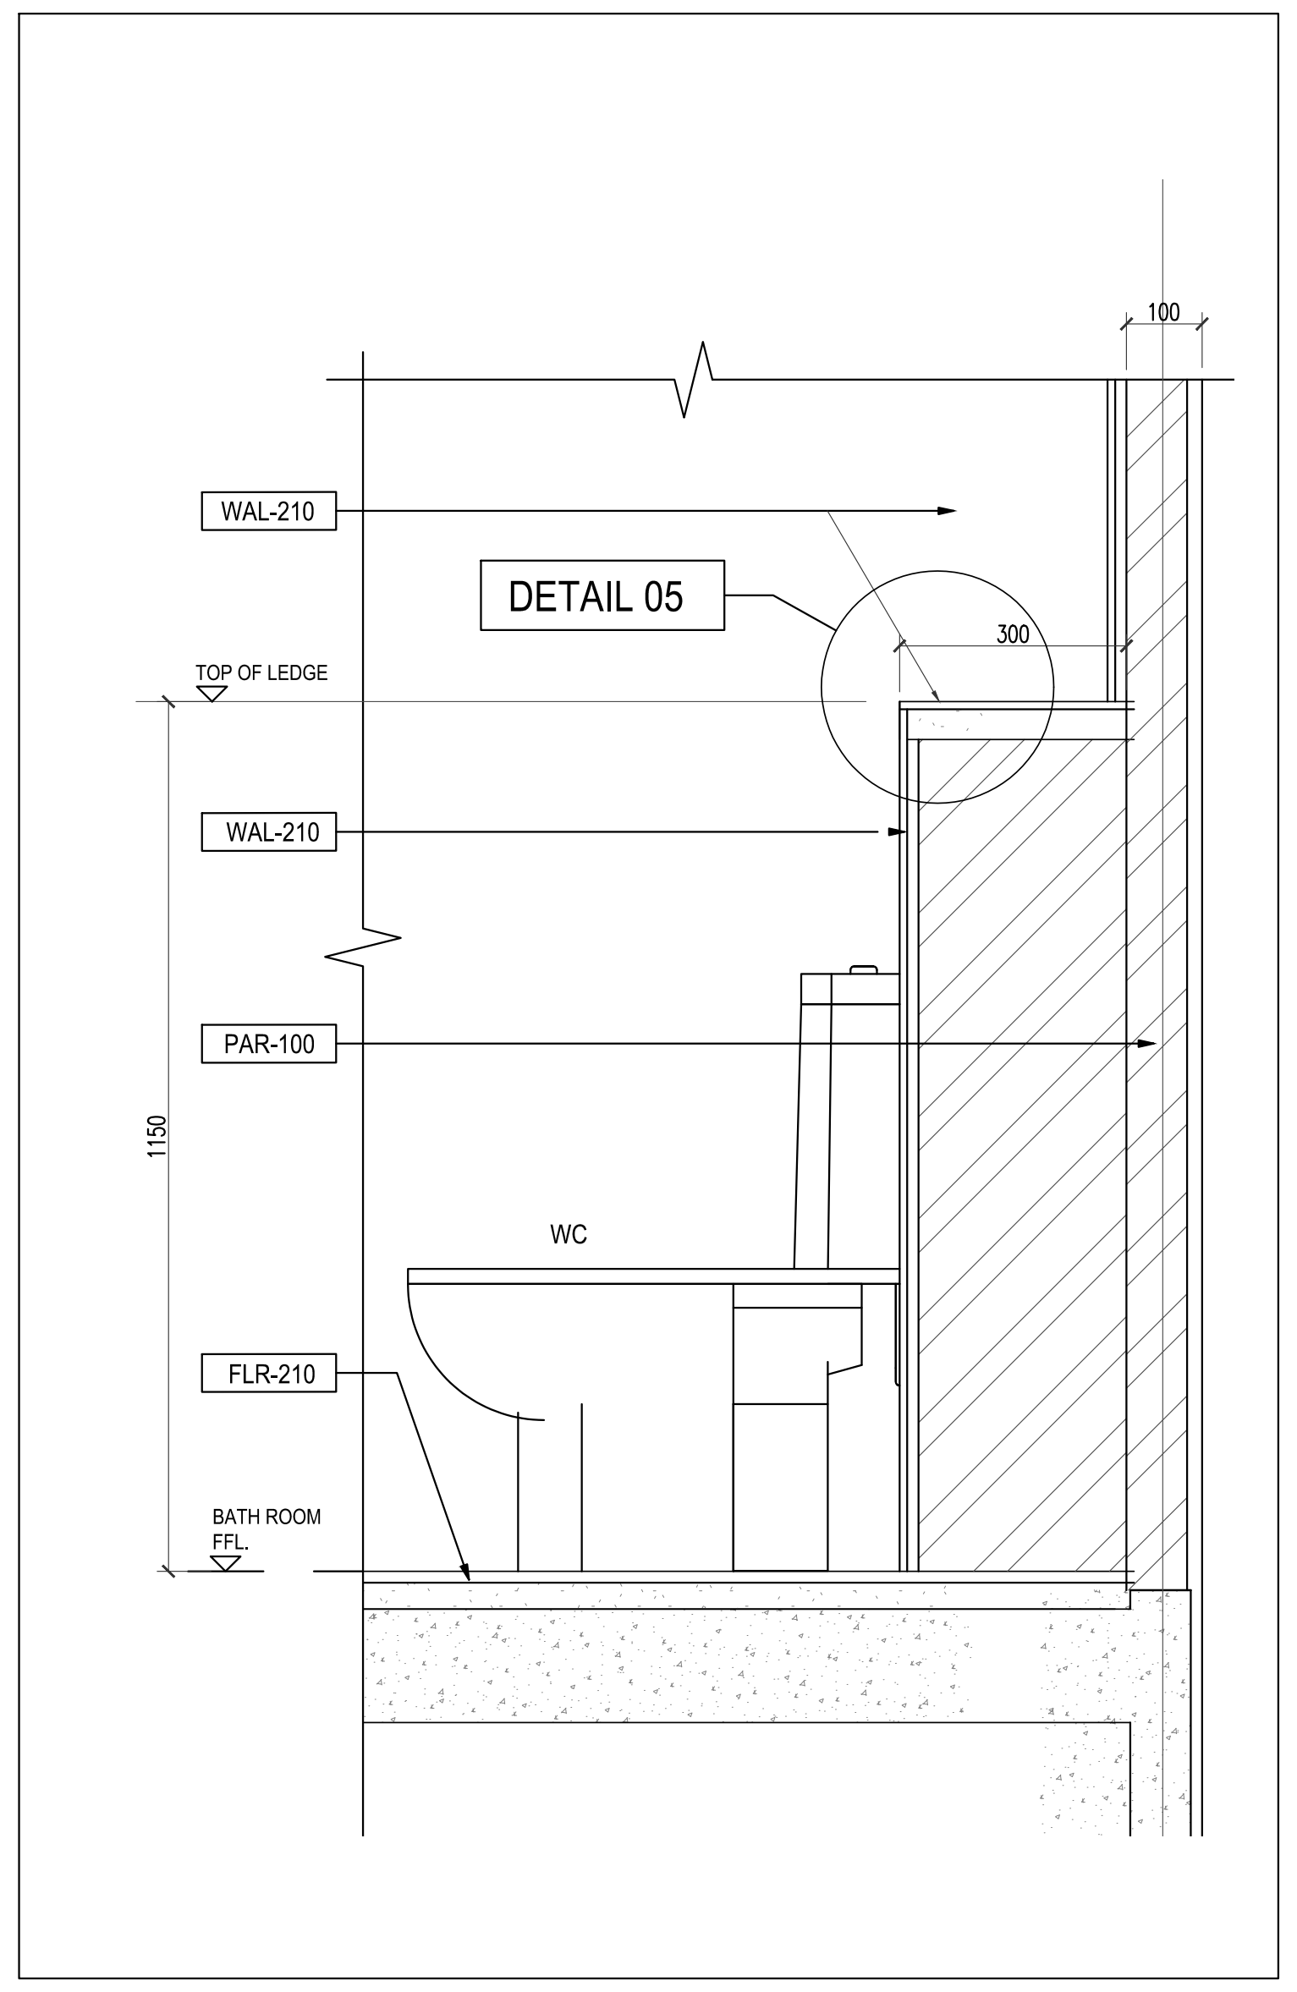

01 DETAIL
1 : 10

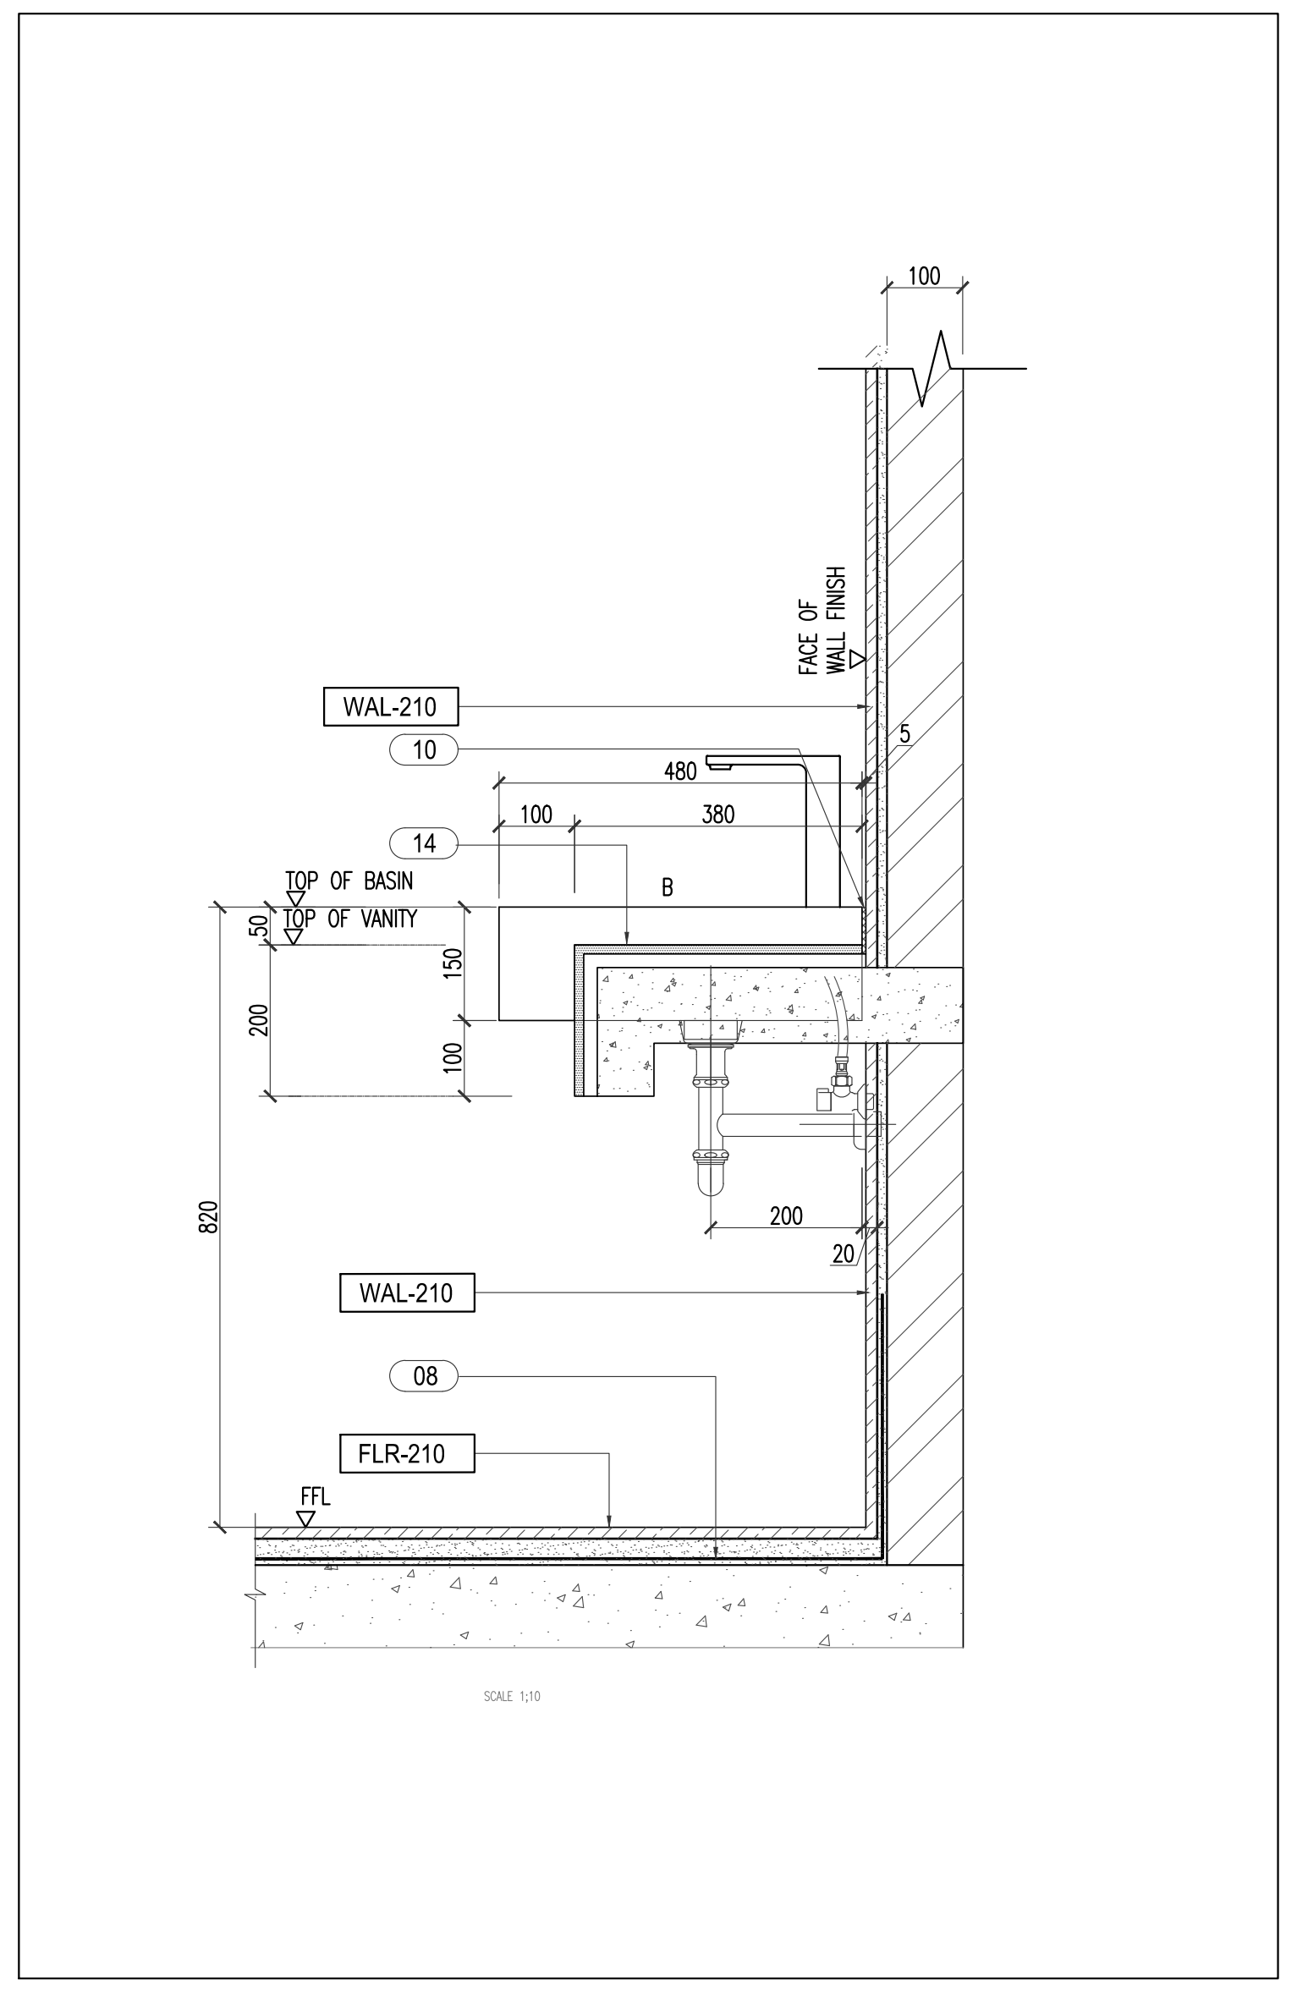

02 VANITY DETAIL (APARTMENT UNIT)
SCALE 1 : 10

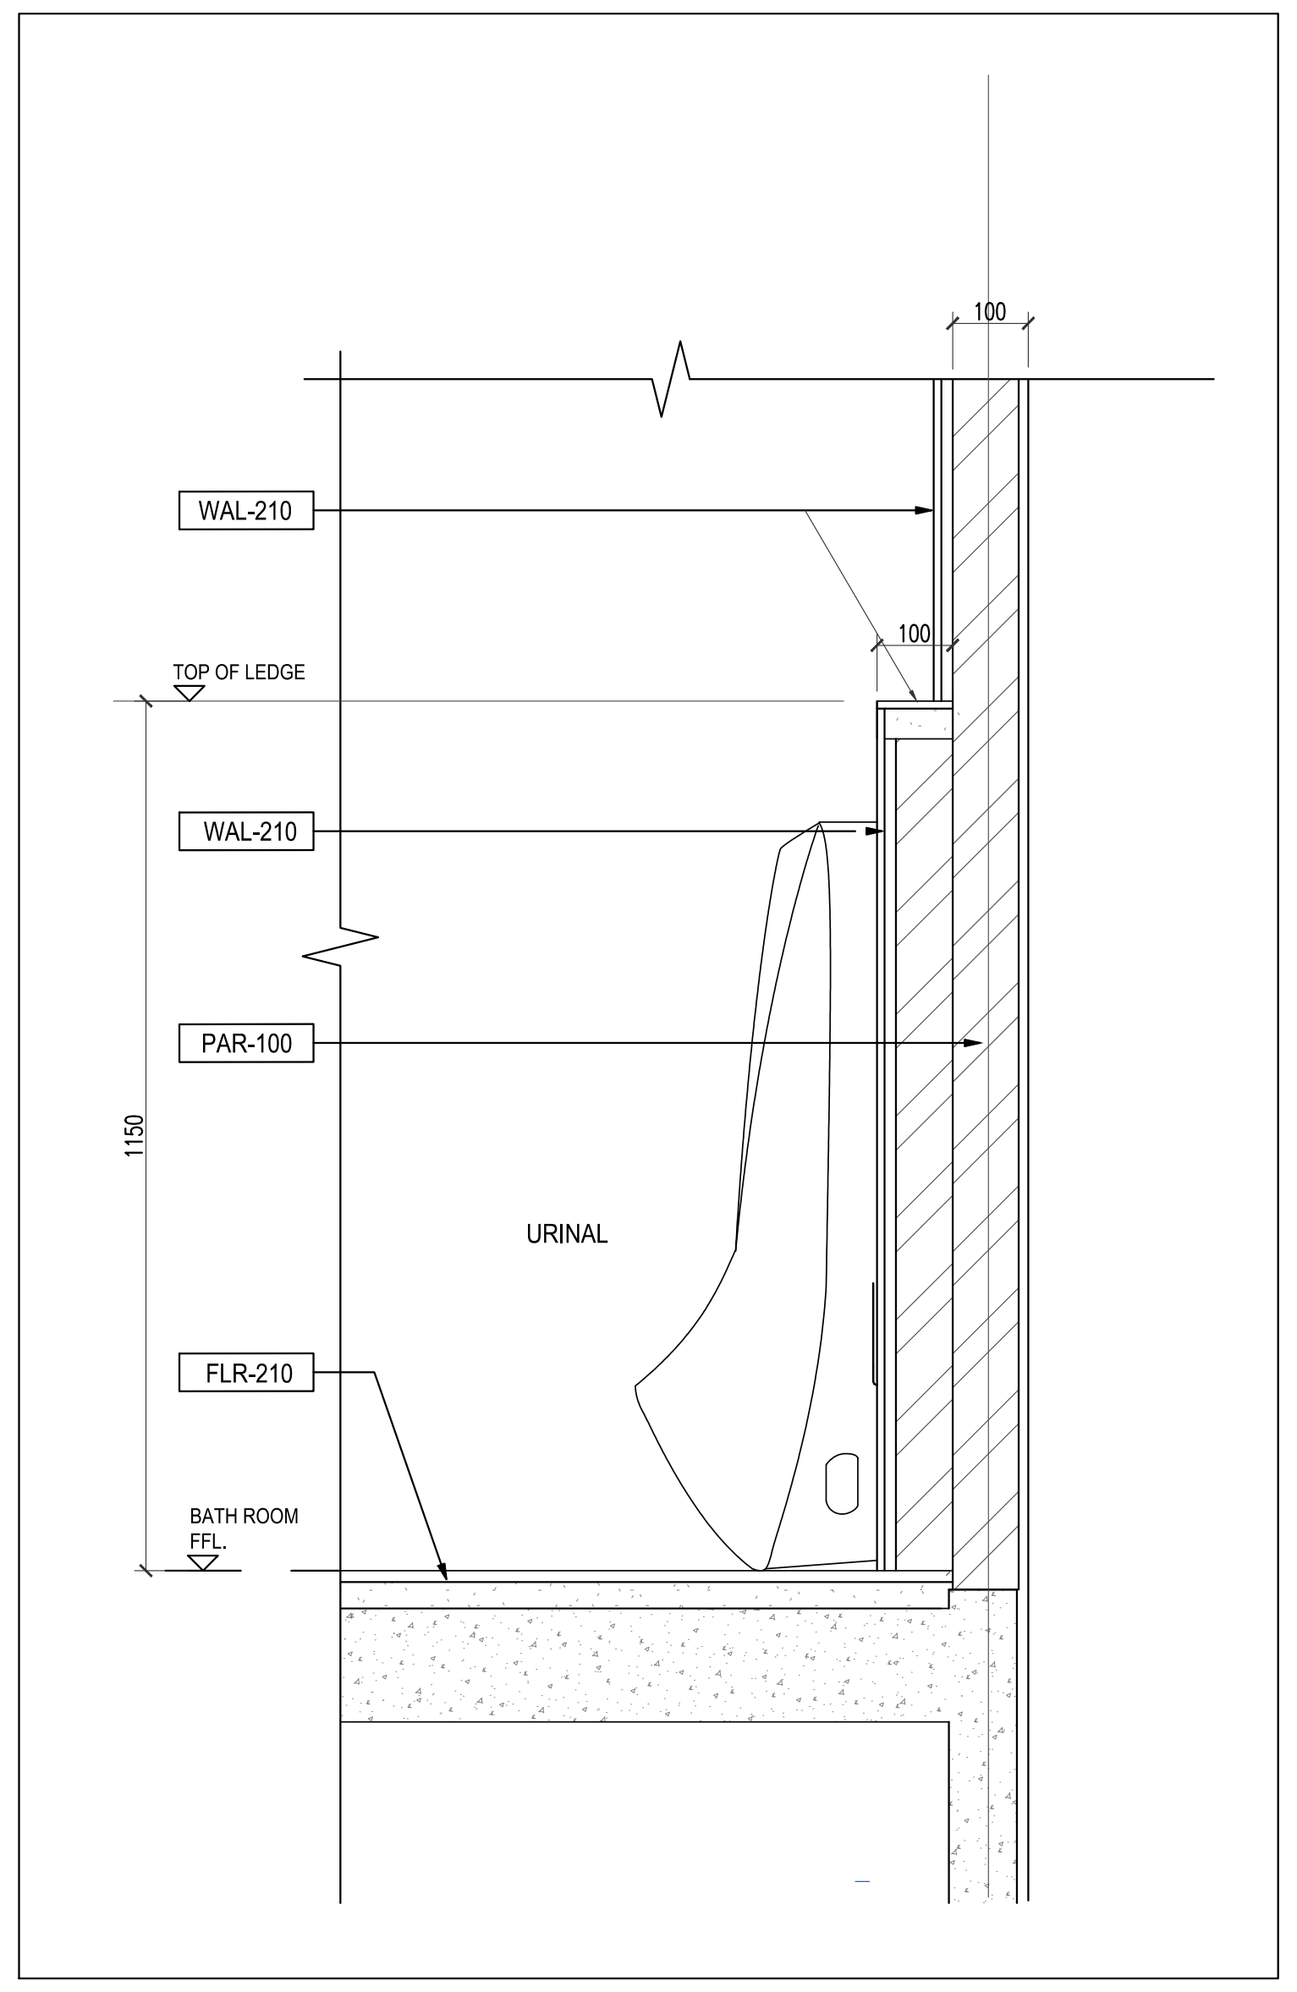

11 URINAL DETAIL
1 : 10

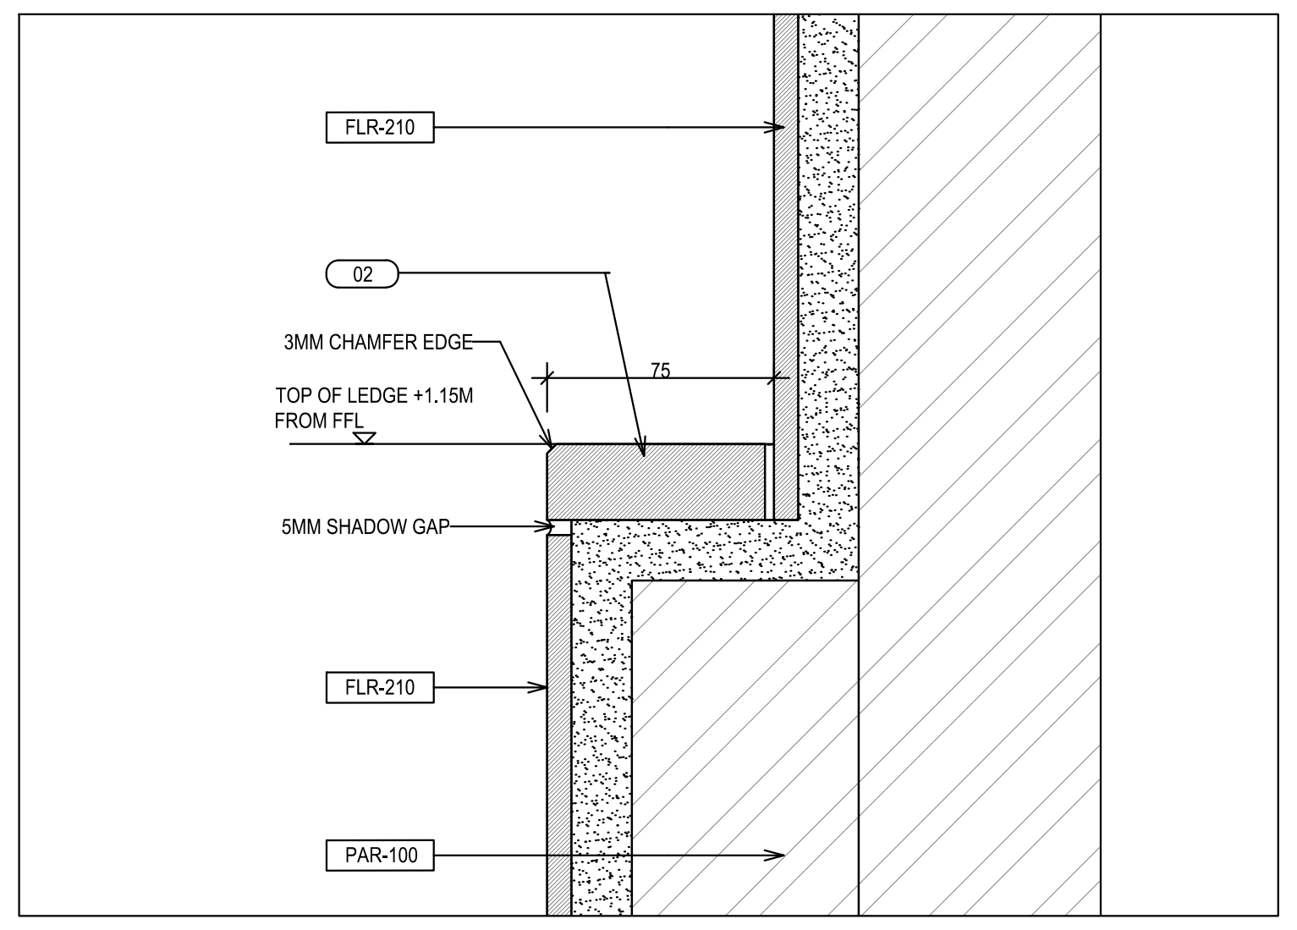

05 DETAIL
1 : 2.5

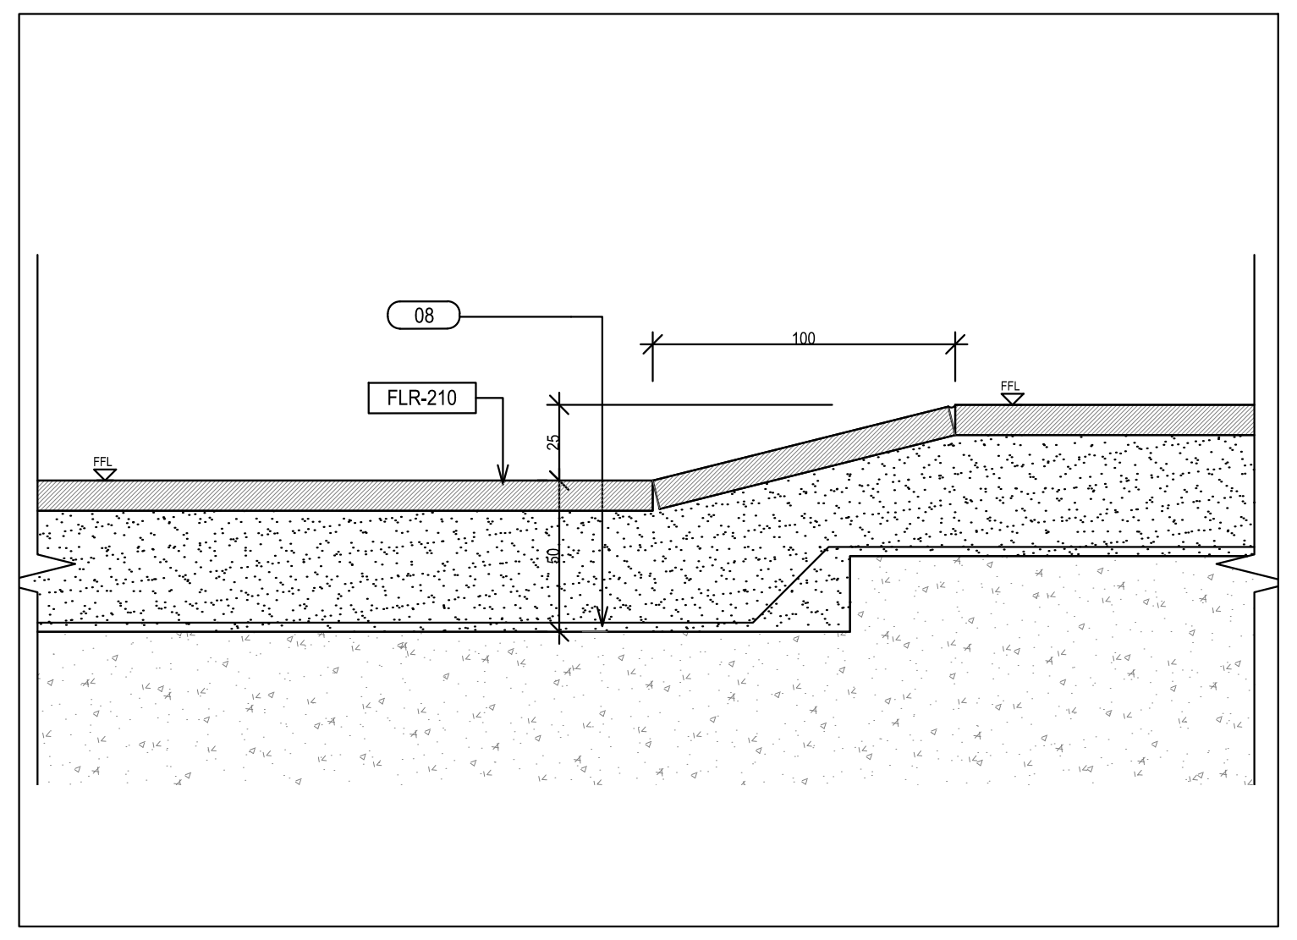

06 DETAIL
SCALE 1 : 2.5

REFERENCE	DESCRIPTION
SFC-100	SKIM COAT AND PAINT
CLG-102	MOISTURE RESISTANT GYPSUM PLASTERBOARD CEILING
FLR-210 FLR-213	600 X 300MM PORCELAIN FLOOR TILE (SELECTED TILES REF. TO SCHEDULE OF FINISHES)
PAR-200	SUSPENDED FROM CEILING TYPE TOILET CUBICLE SYSTEM
PAR-602	10MM THK. FROSTED TEMPERED GLASS SHOWER SCREEN/DOOR C/W S.S FIXING
PAR-100	BRICK/RC WALL AS INDICATED IN PLAN
ST-100	RC COLUMN/WALL TO ENGR'S DETAIL
WAL-101	PLASTER AND PAINT FINISH
WAL-210 WAL-213	600 X 300MM PORCELAIN WALL TILE (SELECTED TILES REF. TO SCHEDULE OF FINISHES)
01	SCUPPER DRAIN WITH S.S GRATING COVER
02	25MM THK. SOLID SURFACE WITH STEEL BRACING
03	SUSPENDED CEILING SYSTEM, METAL FURRINGS
04	RC LINTEL TO ENGR.'S DETAIL
05	RC SLAB WITH WATERPROOFING TO ENGR.'S DETAIL
06	CONCEALED S.S 'U' CHANNEL
07	DOOR/WINDOW DETAIL REFER TO DOOR/WINDOW SCHEDULE
08	SELECTED CEMENTITIOUS WATERPROOFING COMPOUND ON SEMENT SCREED, 300MM HT. (MIN.) UPTURN TO WALL & 1200MM @ SHOWER AREA BEFORE TILING COMMENCE
09	450mm X 450mm MAINHOLE COVER
10	CLEAR SEALANT
11	6MM THK. MIRROR WITH CHAMFERED EDGE ON 6MM THK. WATER RESISTANT MARINE PLYWOOD BACKING WITH PERIMETER ALUMINIUM TRIM EDGING
12	RECESSED WARM WHITE COLOR FLUORESCENT LIGHT
13	20 X 20MM S.S ANGLE AT MIRROR PERIMETER EDGE
14	TILE FINISH RC VANITY TOP
B	BASIN
FT	FLOOR TRAP
TRH	TOILET ROLL HOLDER
WC	WATER CLOSET
HB	HAND BIDET
MR	MIRROR
UR	URINAL
SH	SHOWER HEAD
HDR	HAND DRYER
SD	SOAP DISPENSER
GB	S.S GRAB BAR
s.o.p	TILES SETTING OUT POINTS
☒	450 X 450MM CEILING ACCESS PANEL

LEED:Water Consumption Requirements
Water closet < 4 Liters per flush
Urinal < 0.9 Liters per flush
Shower < 5.2 Liters per minute @ 80 psi
Lavatory faucet < 1 Liters per minute @ 60 psi
Metering faucet < 1 Liters per minute @ 60 psi
Pantry faucets < 4.8 Liters per minute @ 60 psi
All sanitary ware shall comply with LEED TOR.

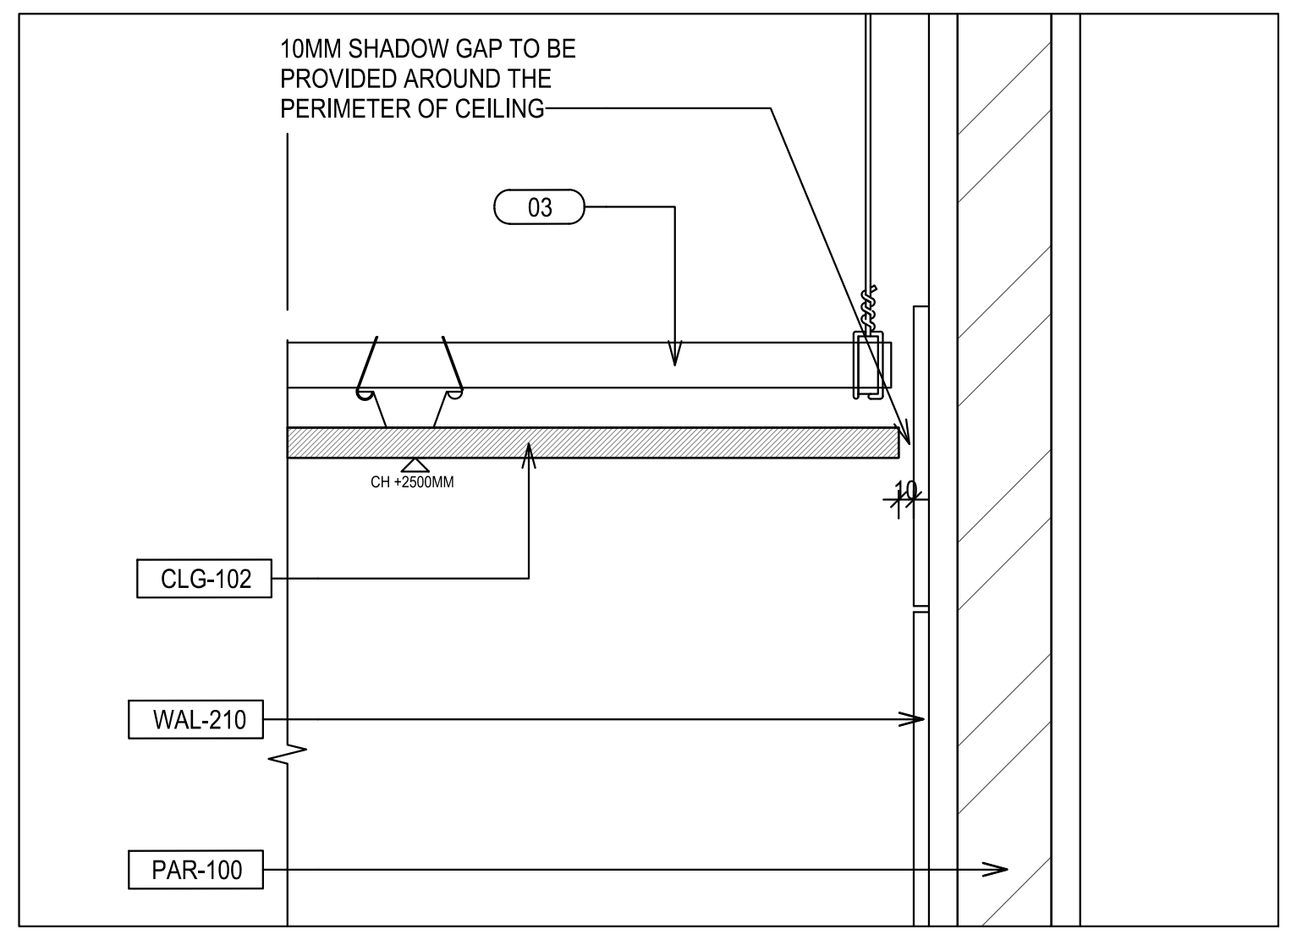
10MM SHADOW GAP TO BE PROVIDED AROUND THE PERIMETER OF CEILING
03
CH +2500MM
10
CLG-102
WAL-210
PAR-100

03 DETAIL
SCALE 1 : 5

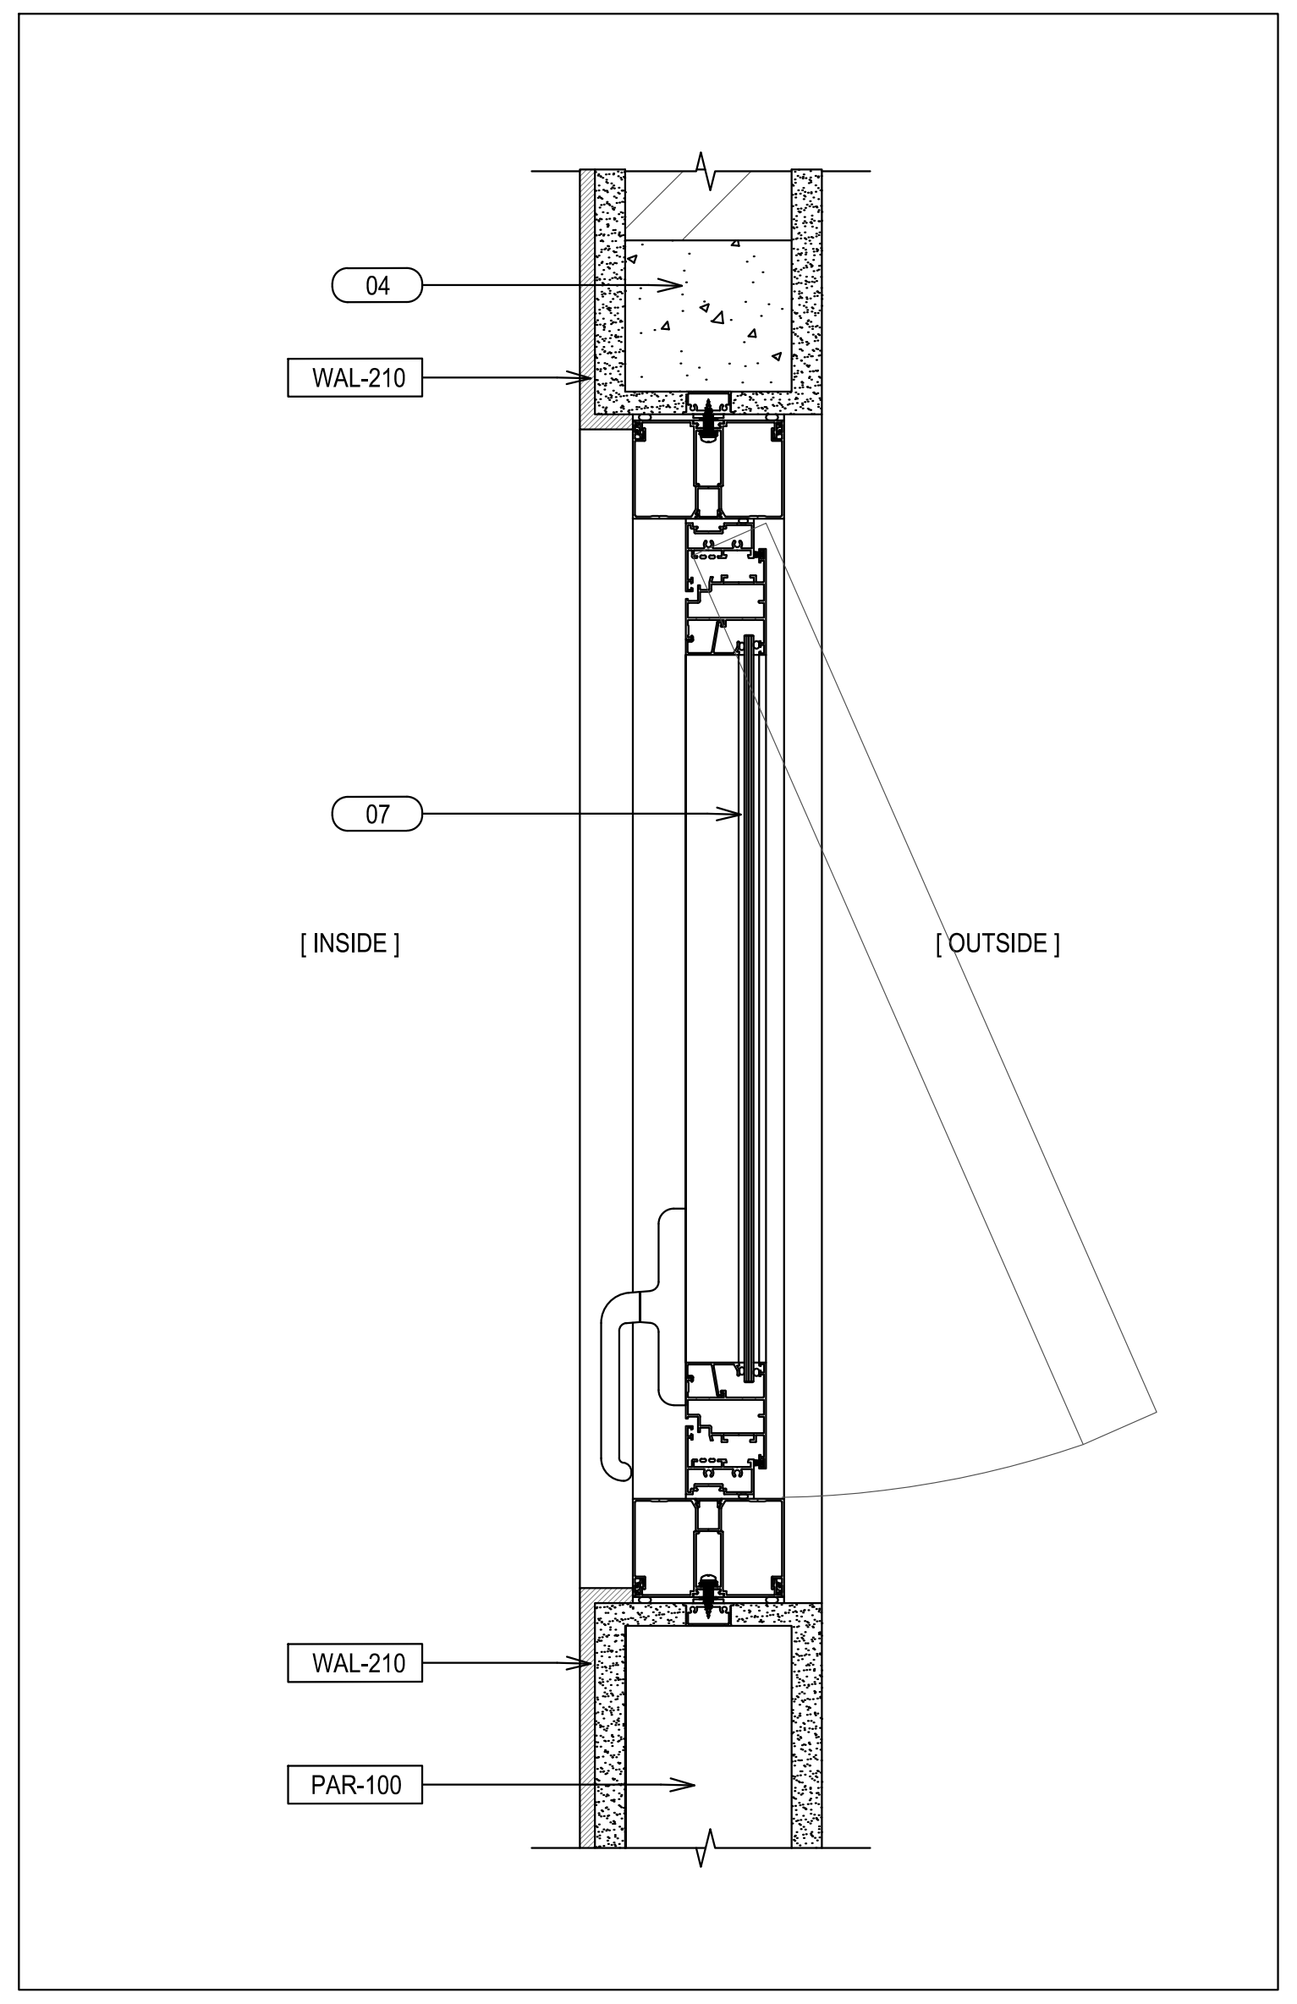

04 DETAIL
SCALE 1 : 5

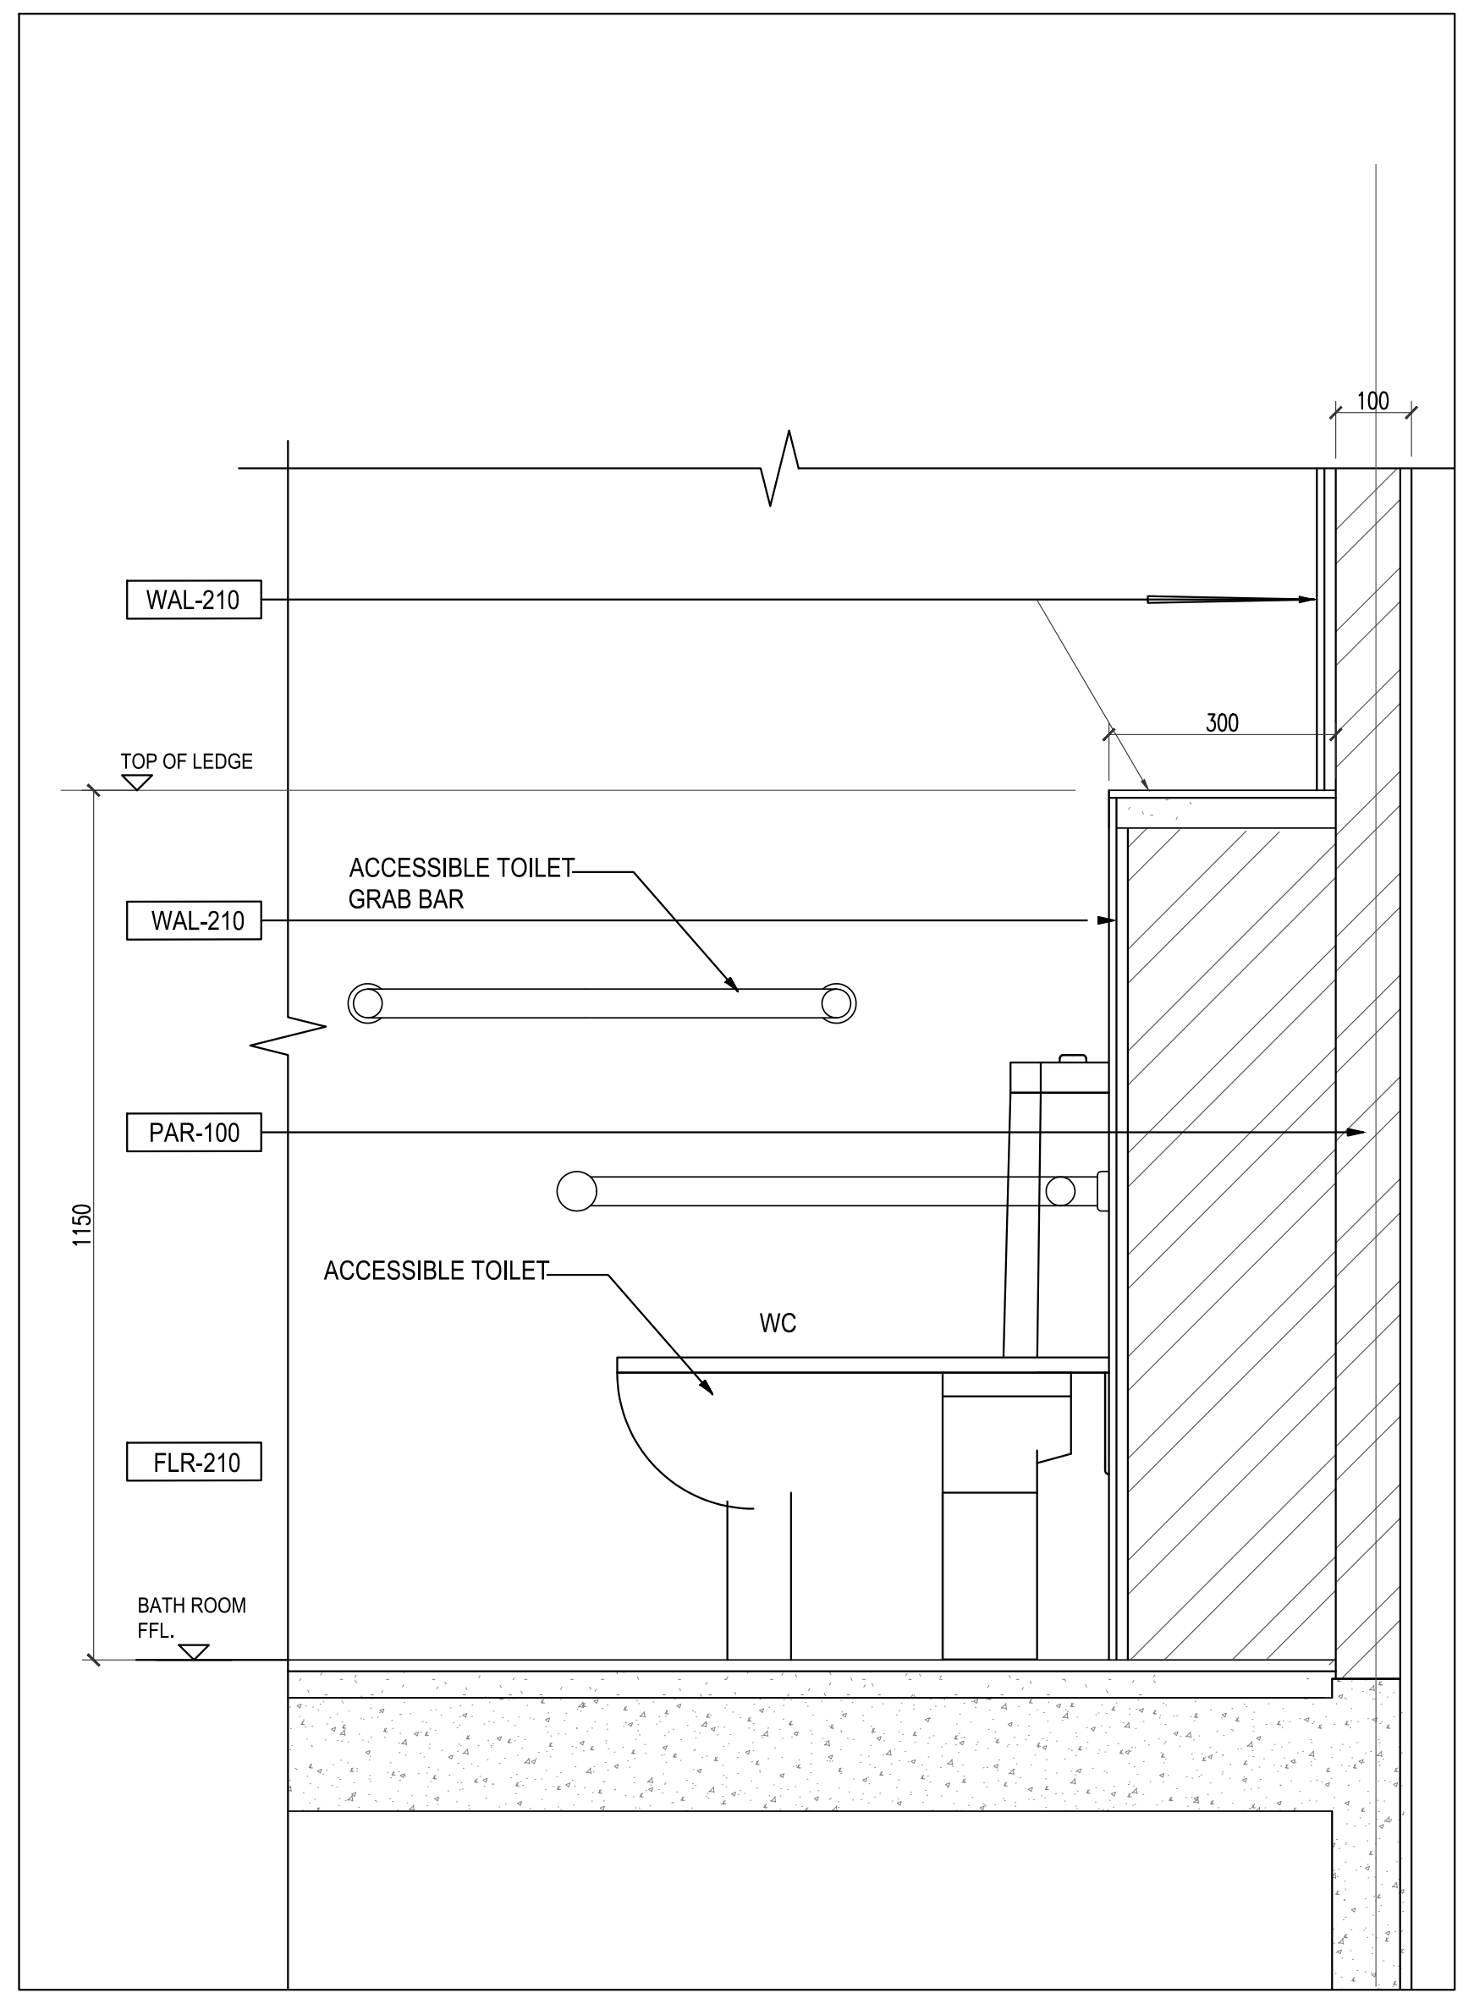

12 ACCESSIBLE TOILET DETAIL
SCALE 1 : 10

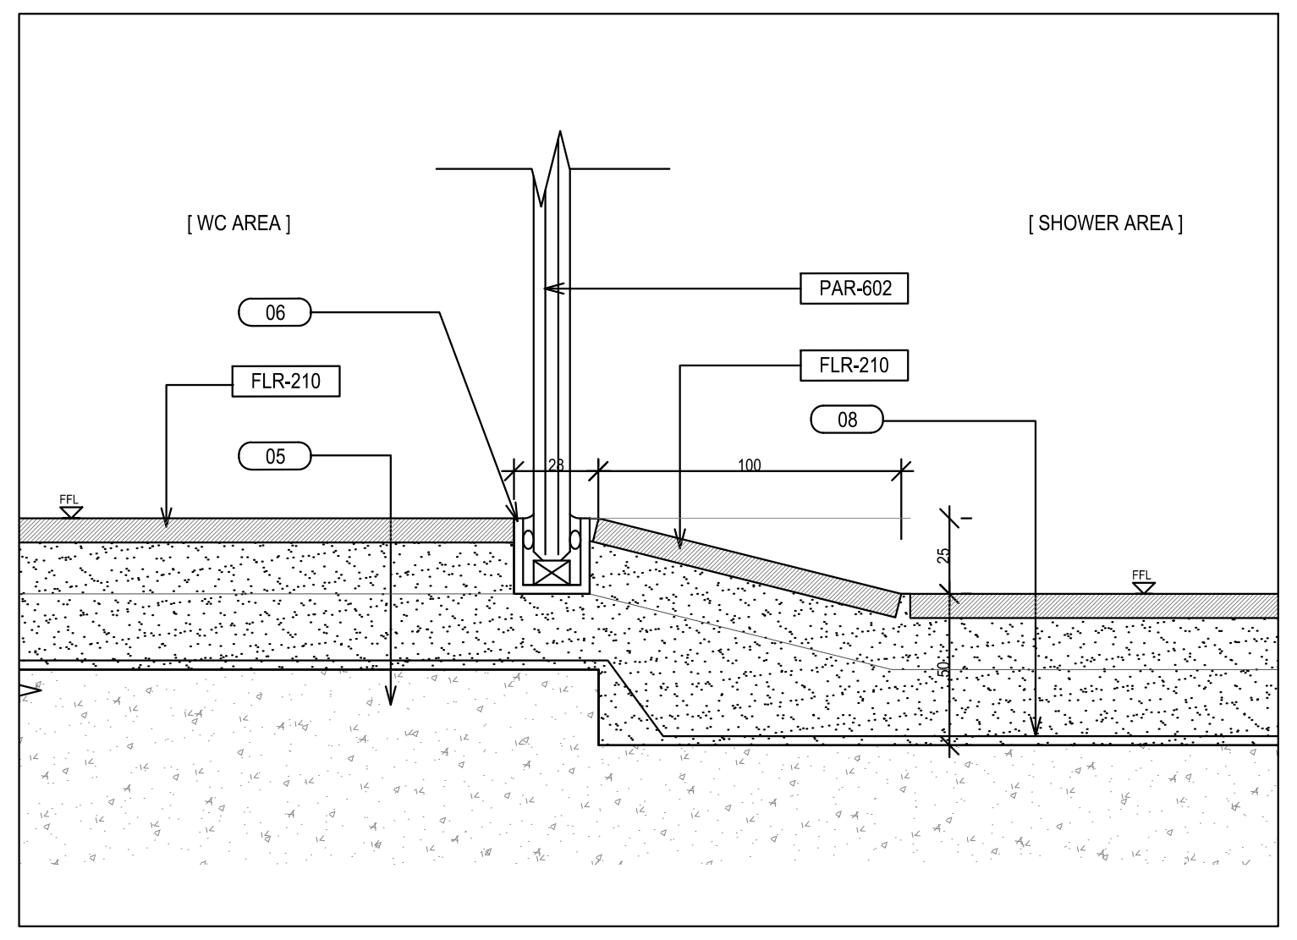

07 DETAIL
SCALE 1 : 2.5

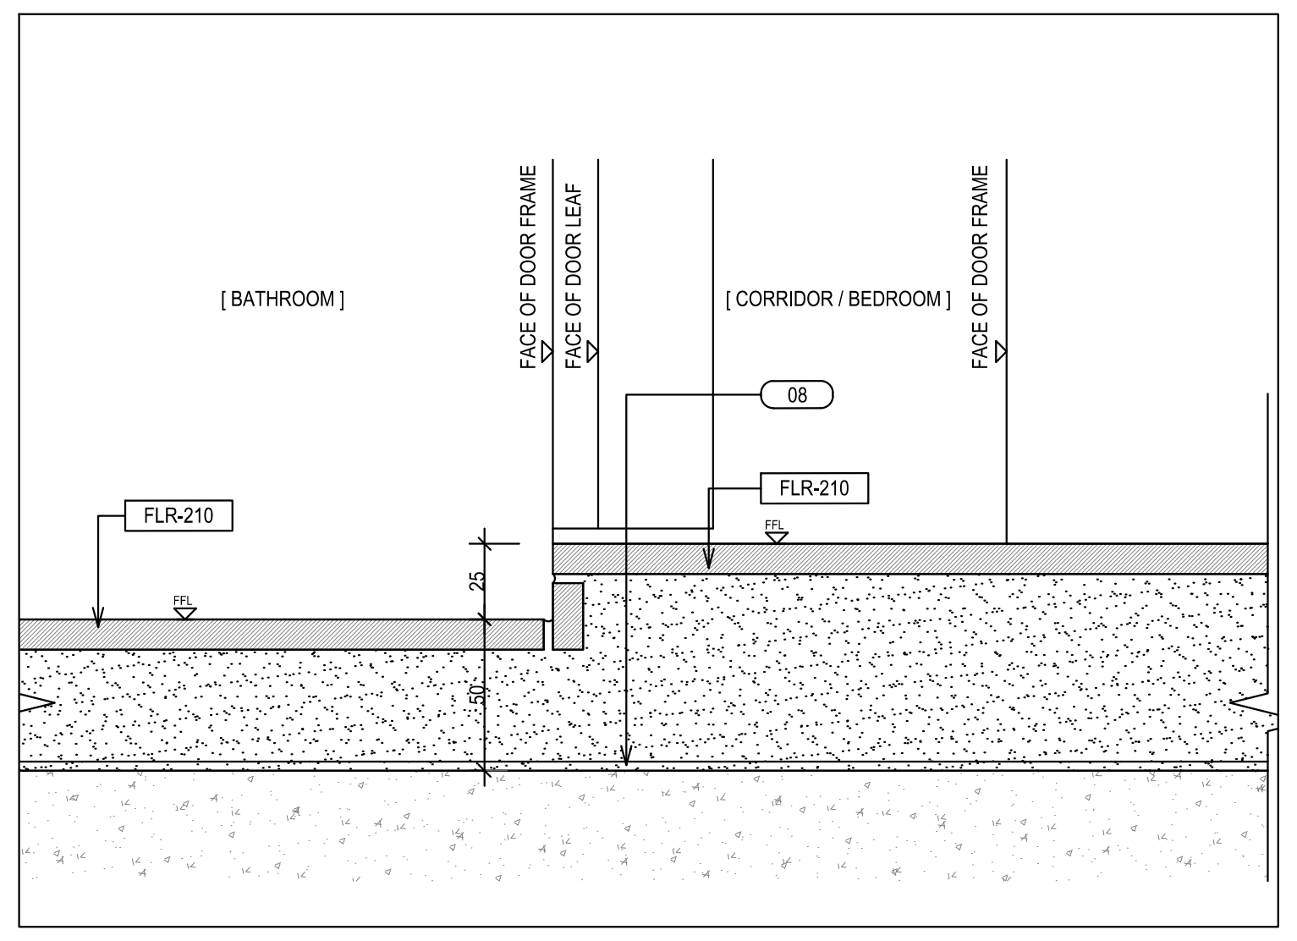

08 DETAIL
SCALE 1 : 2.5

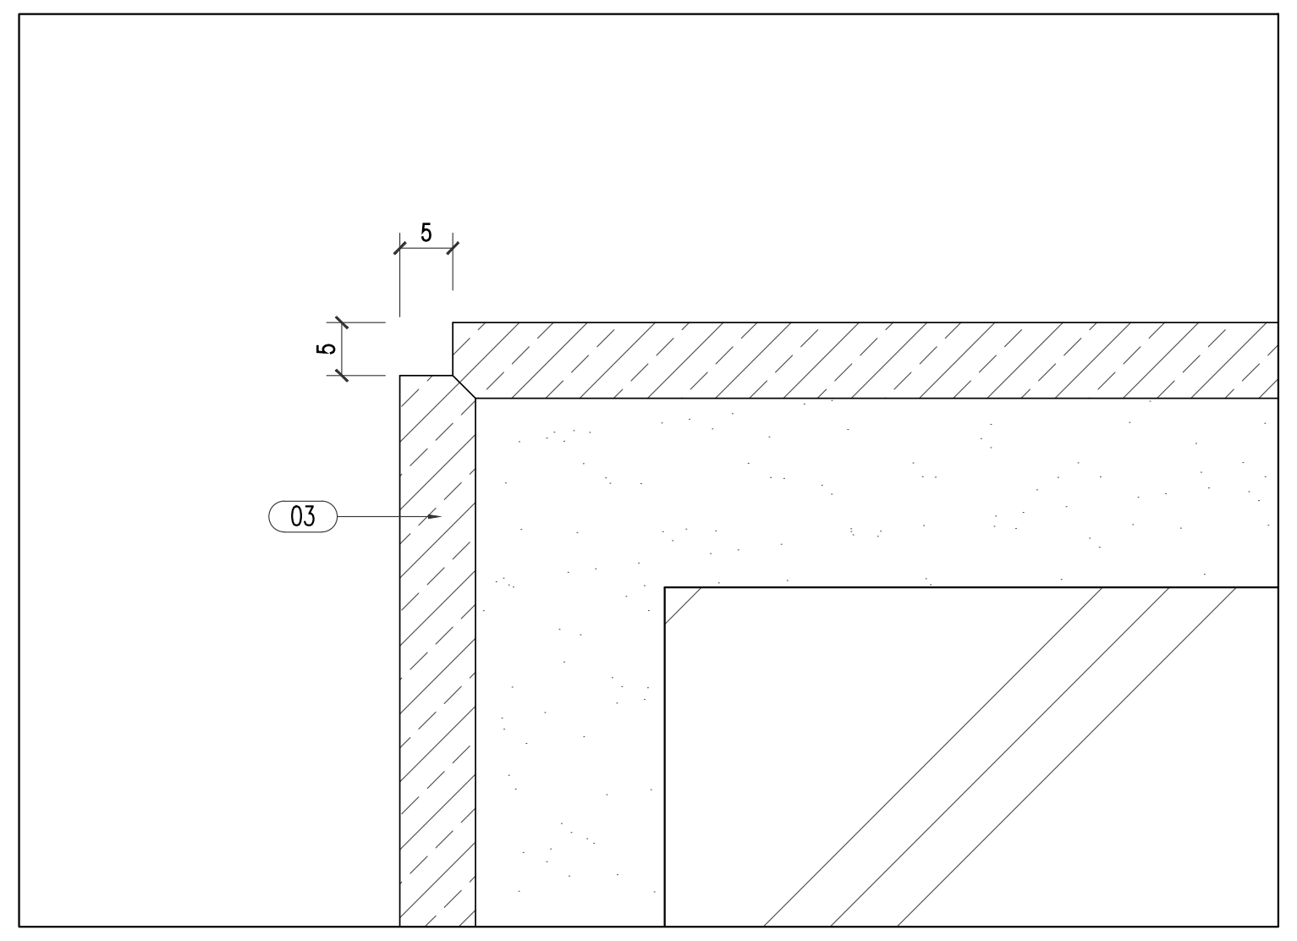

10 TYPICAL TILE JOINT DETAIL 'BRID-MOUTH'
1 : 1

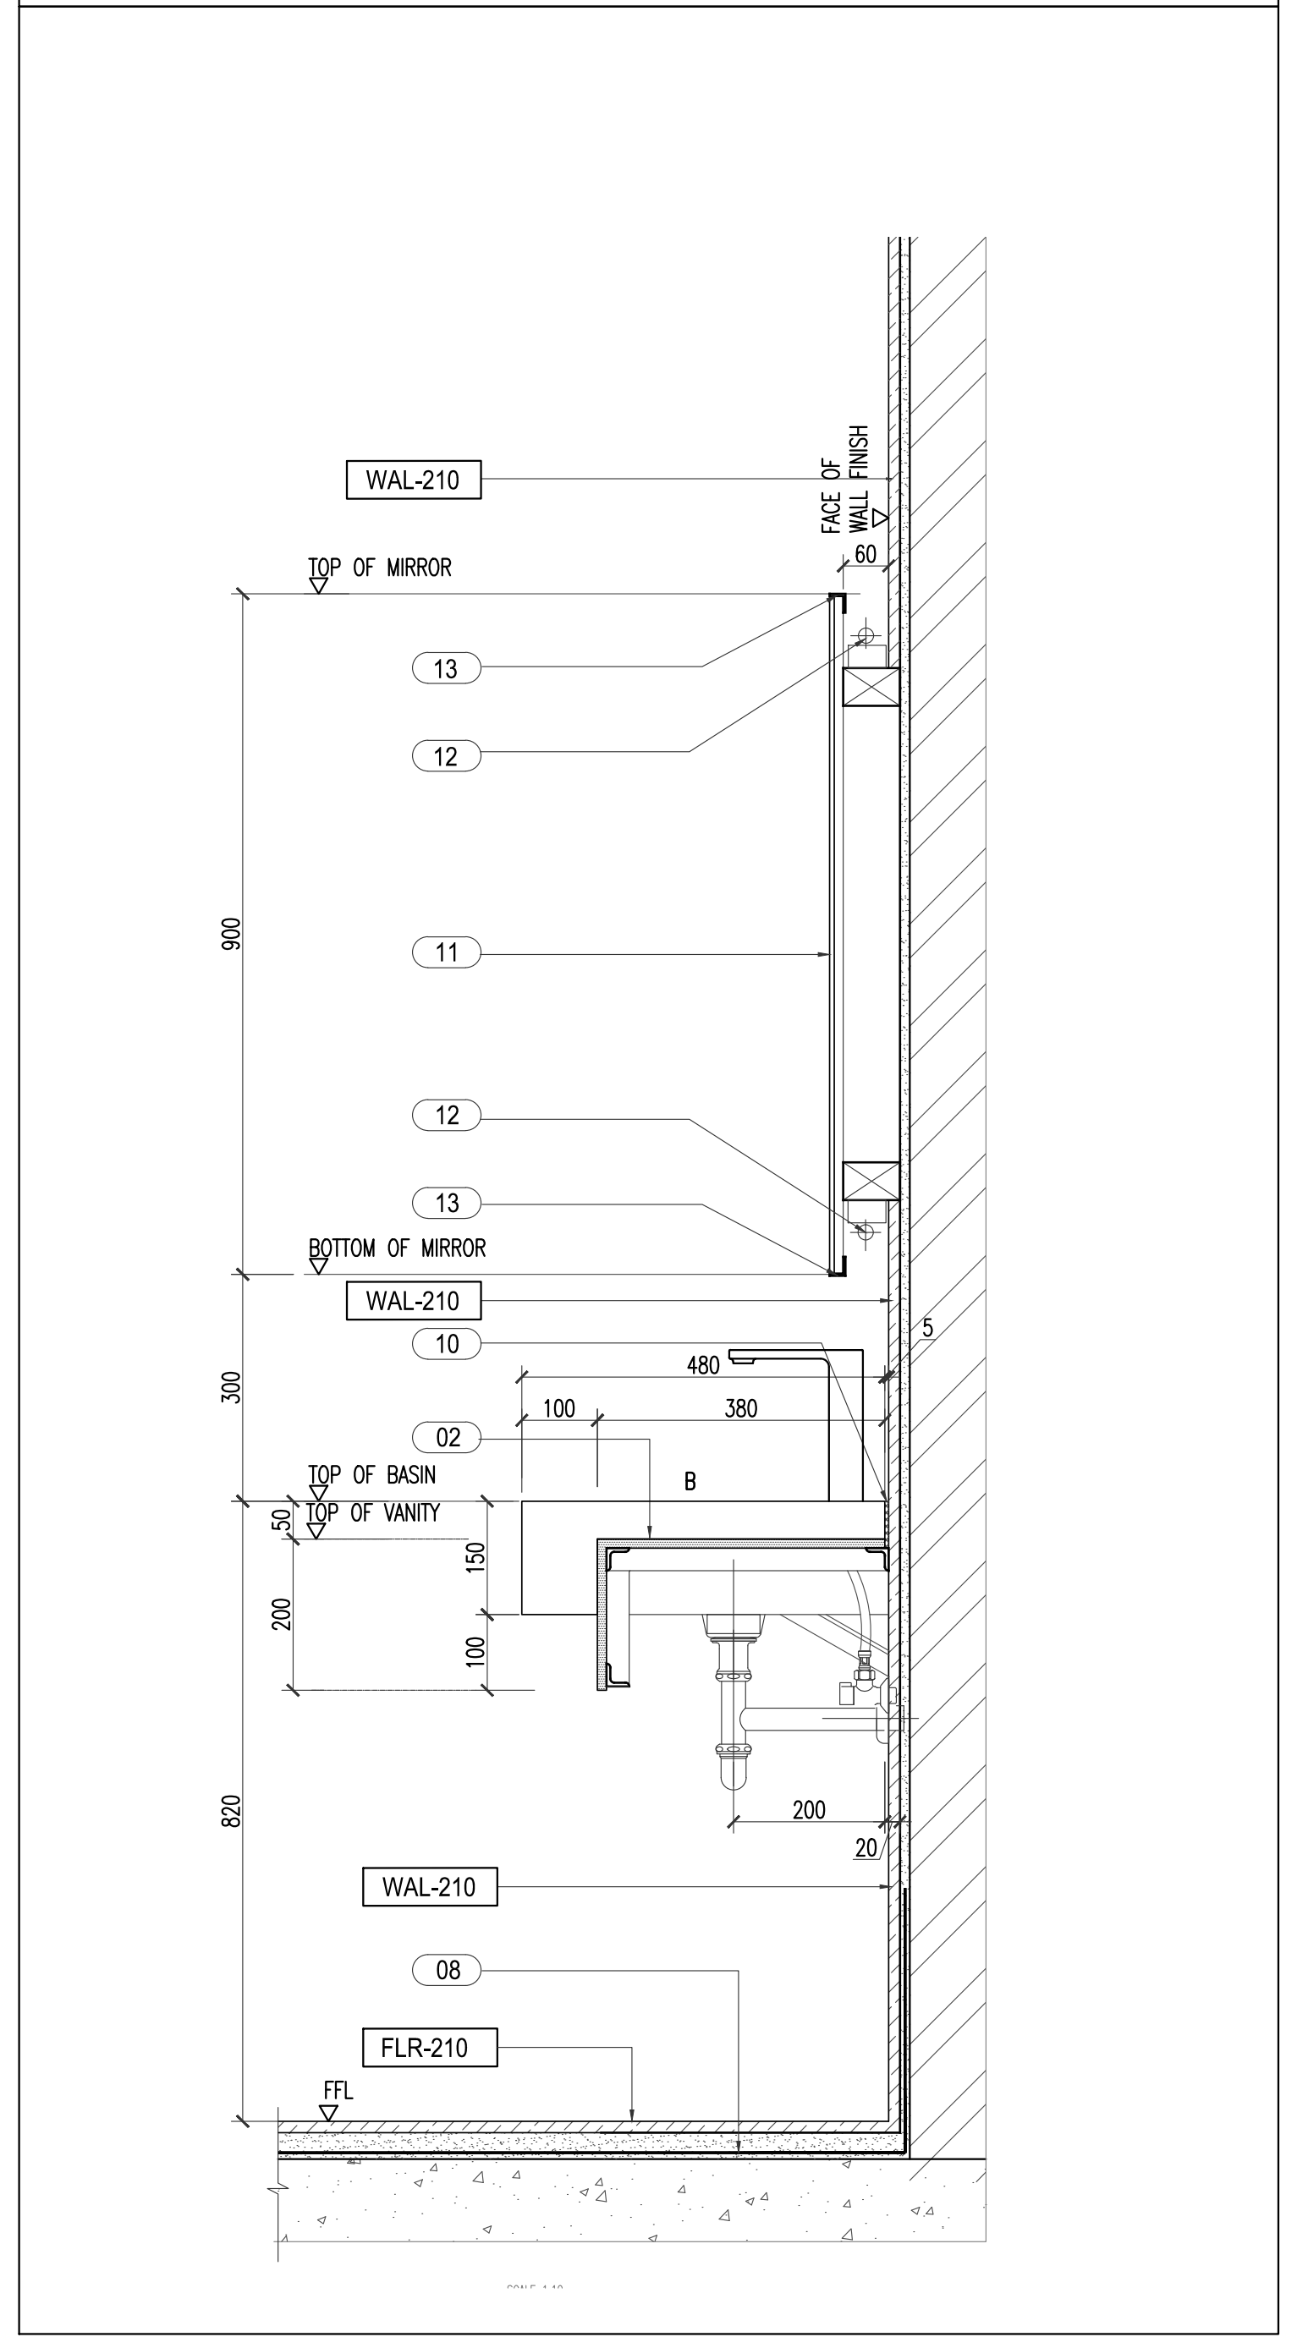

09 VANITY DETAIL (COMMON AREA)
SCALE 1 : 10

CLIENT :

GULF EDGE DC 01

87 Wireless Road, M Thai Tower 11th. Floor, All Seasons Place, Lumpini,
Pathumwan, Bangkok 10330, Thailand

CONTRACTOR :

华西发展(泰国)有限公司
บริษัท หัวซือ ดีเวลลอปเม้นต์ (ประเทศไทย) จำกัด
HUASHI DEVELOPMENT CO.,LTD
No. 202, Room No. 1403, 14/F, Le Concorde Building,
Ratchadapisek Road, Huaykhwang Sub-District,
Huaykhwang District, Bangkok Metropolitan 10310.

CONSULTANT :

ARbay
บริษัท เอ อาร์ เบย์ จำกัด
ARbay Company Limited
31 st Floor Bangkok Insurance Building
25 South Sathorn road Thungmahamek
Sathorn Bangkok 10120 THAILAND
T +66 (0) 2286 8199
F +66 (0) 2286 2863
info@arbay.co.th

CONSULTANT :

Qbic Engineers & Architects Co.,Ltd.
8 Soi KALONG 4 SANAMBINNAM ROAD,
THASAI SUB-DISTRICT, MUANG NONTHABURI DISTRICT
, NONTHABURI.
Tel 662-950-4374
Fax 662-580-3231
E-Mail : qbic@qbic.co.th, www.qbic.co.th
QBIC ENGINEERS AND ARCHITECTS CO.,LTD.

CONSULTANT :

MITR
MITR TECHNICAL CONSULTANT CO.,LTD.
1168/8 12th FLOOR, LUMPINI TOWER BUILDING,
RAMA IV RD., THUNGMAHAMEK, SATHORN, BANGKOK 10120, THAILAND
TEL : 0-2679-9079-84
FAX : 0-2679-9085 E-mail: mitr_dd@mitr.com

Architect : SIGNATURE
ประกิต พนานุรัตน์ วสถ. 580
ที่อยู่
251/1 ถ.จารุเมือง แขวงรองเมือง เขตปทุมวัน
กรุงเทพมหานคร โทรศัพท์ 02-286-8199

Structural Engineer : SIGNATURE
วิศวกรผู้ออกแบบโครงสร้าง
ณัฐสม สงวนวงษ์ วย 1423
ที่อยู่
2/1 ซ.รามคำแหง 150 ถ.รามคำแหง
แขวง สะพานสูง เขต สะพานสูง กทม. 10240

Structural Inspector : SIGNATURE
วิศวกรผู้ตรวจสอบโครงสร้าง
โกมล จุฑาภัทร วย 964
ที่อยู่
24/18 ซ.นวมินทร์ 129 ถ. นวมินทร์
แขวง นวลจันทร์ เขต บึงกุ่ม กทม. 10230

Electrical Engineer : SIGNATURE
วิศวกรผู้ออกแบบระบบไฟฟ้ากำลัง
นายสุภัทร บูรณวิทย์ วฟก.1265
ที่อยู่
21 ซอยทานสัมฤทธิ์ 13
ตำบลท่าทราย อ.เมืองนนทบุรี จ.นนทบุรี 11000

Mechanical Engineer : SIGNATURE
วิศวกรผู้ออกแบบระบบเครื่องกลและปรับอากาศ
นายประสิทธิ์ เกียวสุนทร วก.1221
ที่อยู่
44/372 ซอยบางกระดี่ 35/1 แขวงแสมดำ
เขตบางขุนเทียน กทม. 10150
ประสิทธิ์

Sanitary Engineer : SIGNATURE
วิศวกรผู้ออกแบบระบบสุขาภิบาล และดับเพลิง
นายทศวรรษ สนันฤทธิ์ วส. 215
ที่อยู่
บ้านเลขที่ 99/107 หมู่ที่ 3 ต.ศีรษะจรเข้น้อย
อ.บางเสาธง จ.สมุทรปราการ 10540
ทศวรรษ

ISSUE/REVISION

REV.	DESCRIPTION	DATE
A	90% DEVELOPED	09/05/2026

PROJECT NAME :
GEDC 01

LOCATION:
Nikhom Phattana district, Rayong ,industrial estate,CPGC

BUILDING :
DETAILS

90% DEVELOPED

TITLE :
SANITARY FITTINGS DETAILS

JOB NO.	SCALE 1:10
DRAWN LYT	REF.
CHECKED LJC	DWG.NO. MPK01A-60-A-SF-001
APPROVED LXD	
DATE 2026.05.09	

NOTE : THIS PRINT IS OF A CONFIDENTIAL NATURE, IT SHALL NOT BE TRACED,PHOTOGRAPHED,PHOTOSTATED OR REPRODUCED IN ANY MANER,NOR USED FOR ANY PURPOSE WHATSOEVER EXCEPT BY WRITTEN PERMISSION