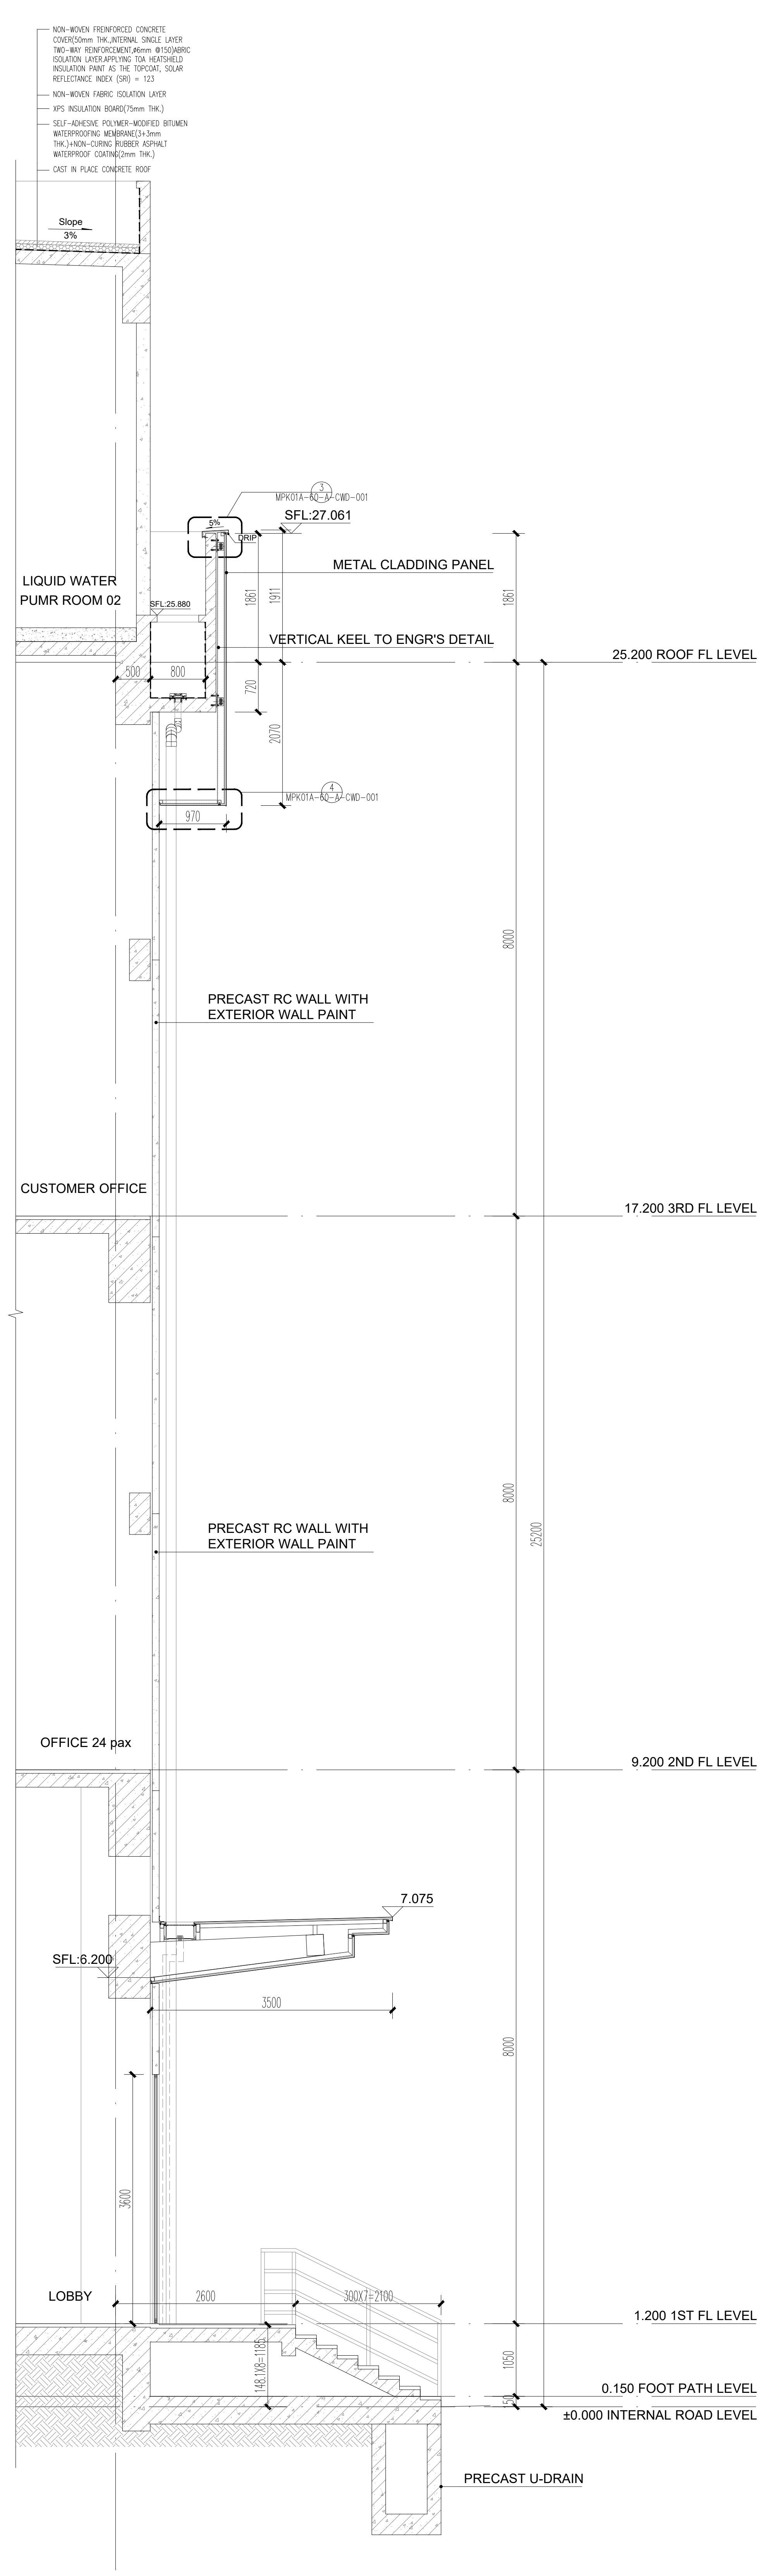
NON-WOVEN FREINFORCED CONCRETE COVER(50mm THK.,INTERNAL SINGLE LAYER TWO-WAY REINFORCEMENT,ø6mm @150)ABRIC ISOLATION LAYER.APPLYING TOA HEATSHIELD INSULATION PAINT AS THE TOPCOAT, SOLAR REFLECTANCE INDEX (SRI) = 123
NON-WOVEN FABRIC ISOLATION LAYER
XPS INSULATION BOARD(75mm THK.)
SELF-ADHESIVE POLYMER-MODIFIED BITUMEN WATERPROOFING MEMBRANE(3+3mm THK.)+NON-CURING RUBBER ASPHALT WATERPROOF COATING(2mm THK.)
CAST IN PLACE CONCRETE ROOF
Slope
3%
MPK01A-60-A-CWD-001
SFL:27.061
DRIP
METAL CLADDING PANEL
LIQUID WATER PUMR ROOM 02
SFL:25.880
VERTICAL KEEL TO ENGR'S DETAIL
25.200 ROOF FL LEVEL
PRECAST RC WALL WITH EXTERIOR WALL PAINT
CUSTOMER OFFICE
17.200 3RD FL LEVEL
PRECAST RC WALL WITH EXTERIOR WALL PAINT
OFFICE 24 pax
9.200 2ND FL LEVEL
7.075
SFL:6.200
3500
LOBBY
1.200 1ST FL LEVEL
0.150 FOOT PATH LEVEL
±0.000 INTERNAL ROAD LEVEL
PRECAST U-DRAIN

EXTERNAL WALL DETAIL 01

Scale 1:50

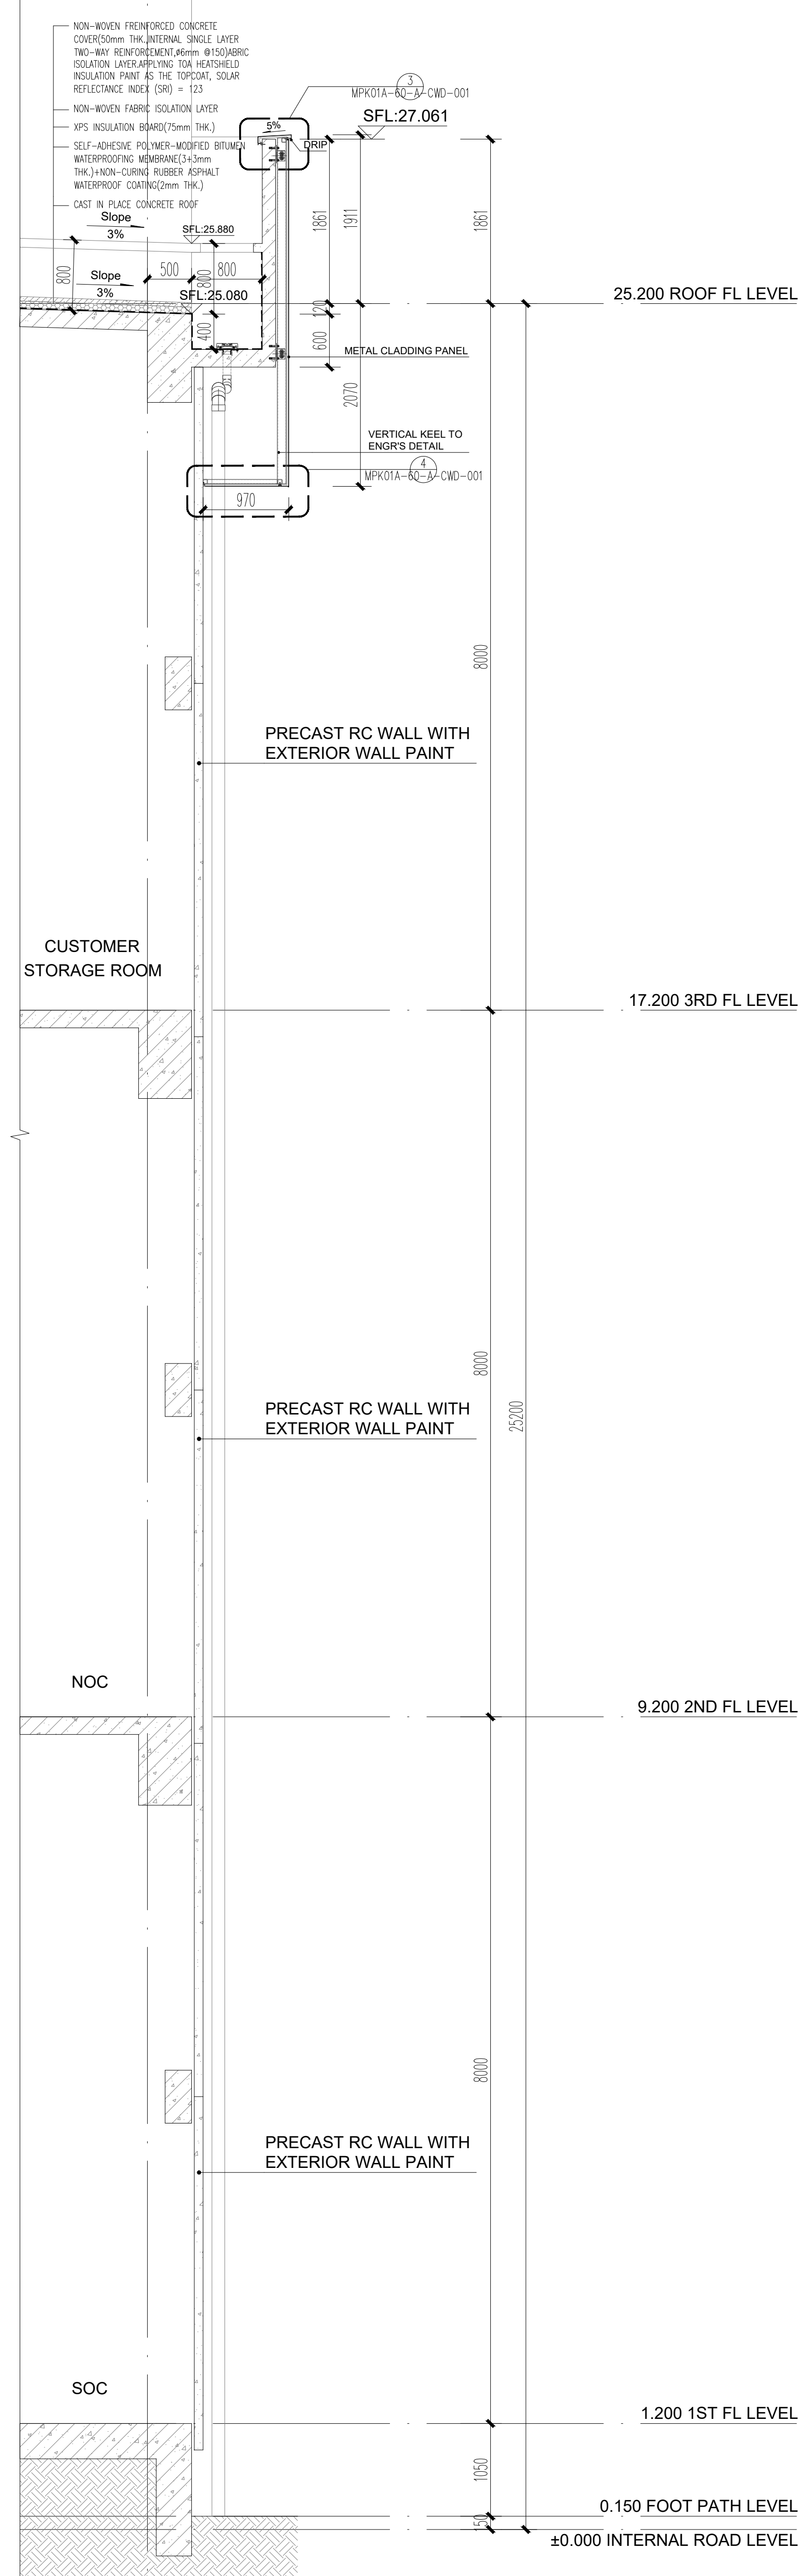

EXTERNAL WALL DETAIL 02

Scale 1:50

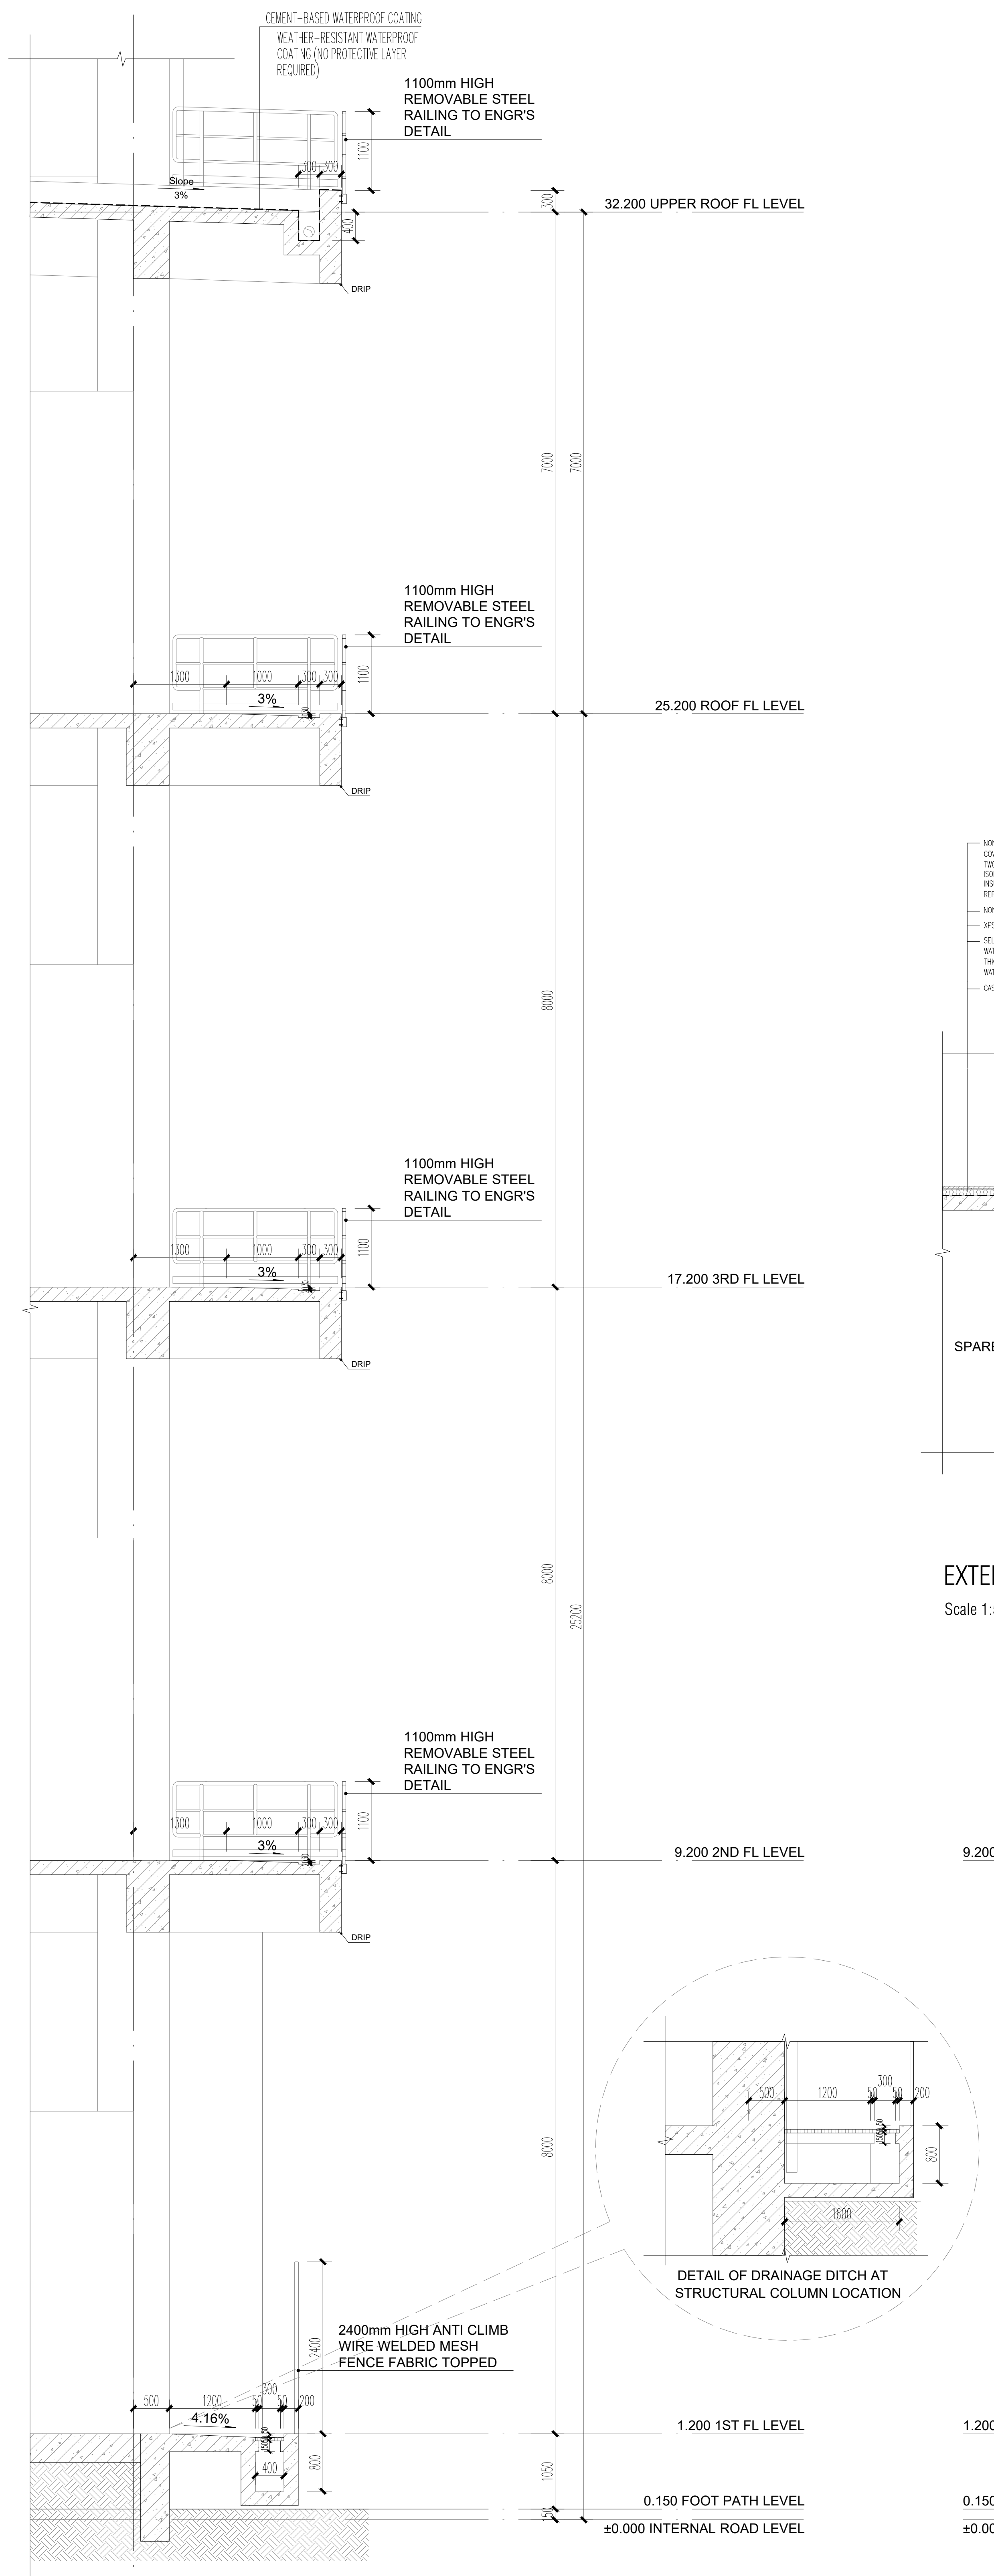
CEMENT-BASED WATERPROOF COATING
WEATHER-RESISTANT WATERPROOF COATING (NO PROTECTIVE LAYER REQUIRED)
1100mm HIGH REMOVABLE STEEL RAILING TO ENGR'S DETAIL
Slope
3%
DRIP
32.200 UPPER ROOF FL LEVEL
1100mm HIGH REMOVABLE STEEL RAILING TO ENGR'S DETAIL
25.200 ROOF FL LEVEL
1100mm HIGH REMOVABLE STEEL RAILING TO ENGR'S DETAIL
17.200 3RD FL LEVEL
1100mm HIGH REMOVABLE STEEL RAILING TO ENGR'S DETAIL
9.200 2ND FL LEVEL
DETAIL OF DRAINAGE DITCH AT STRUCTURAL COLUMN LOCATION
2400mm HIGH ANTI CLIMB WIRE WELDED MESH FENCE FABRIC TOPPED
4.16%
1.200 1ST FL LEVEL
0.150 FOOT PATH LEVEL
±0.000 INTERNAL ROAD LEVEL

EXTERNAL WALL DETAIL 03

Scale 1:50

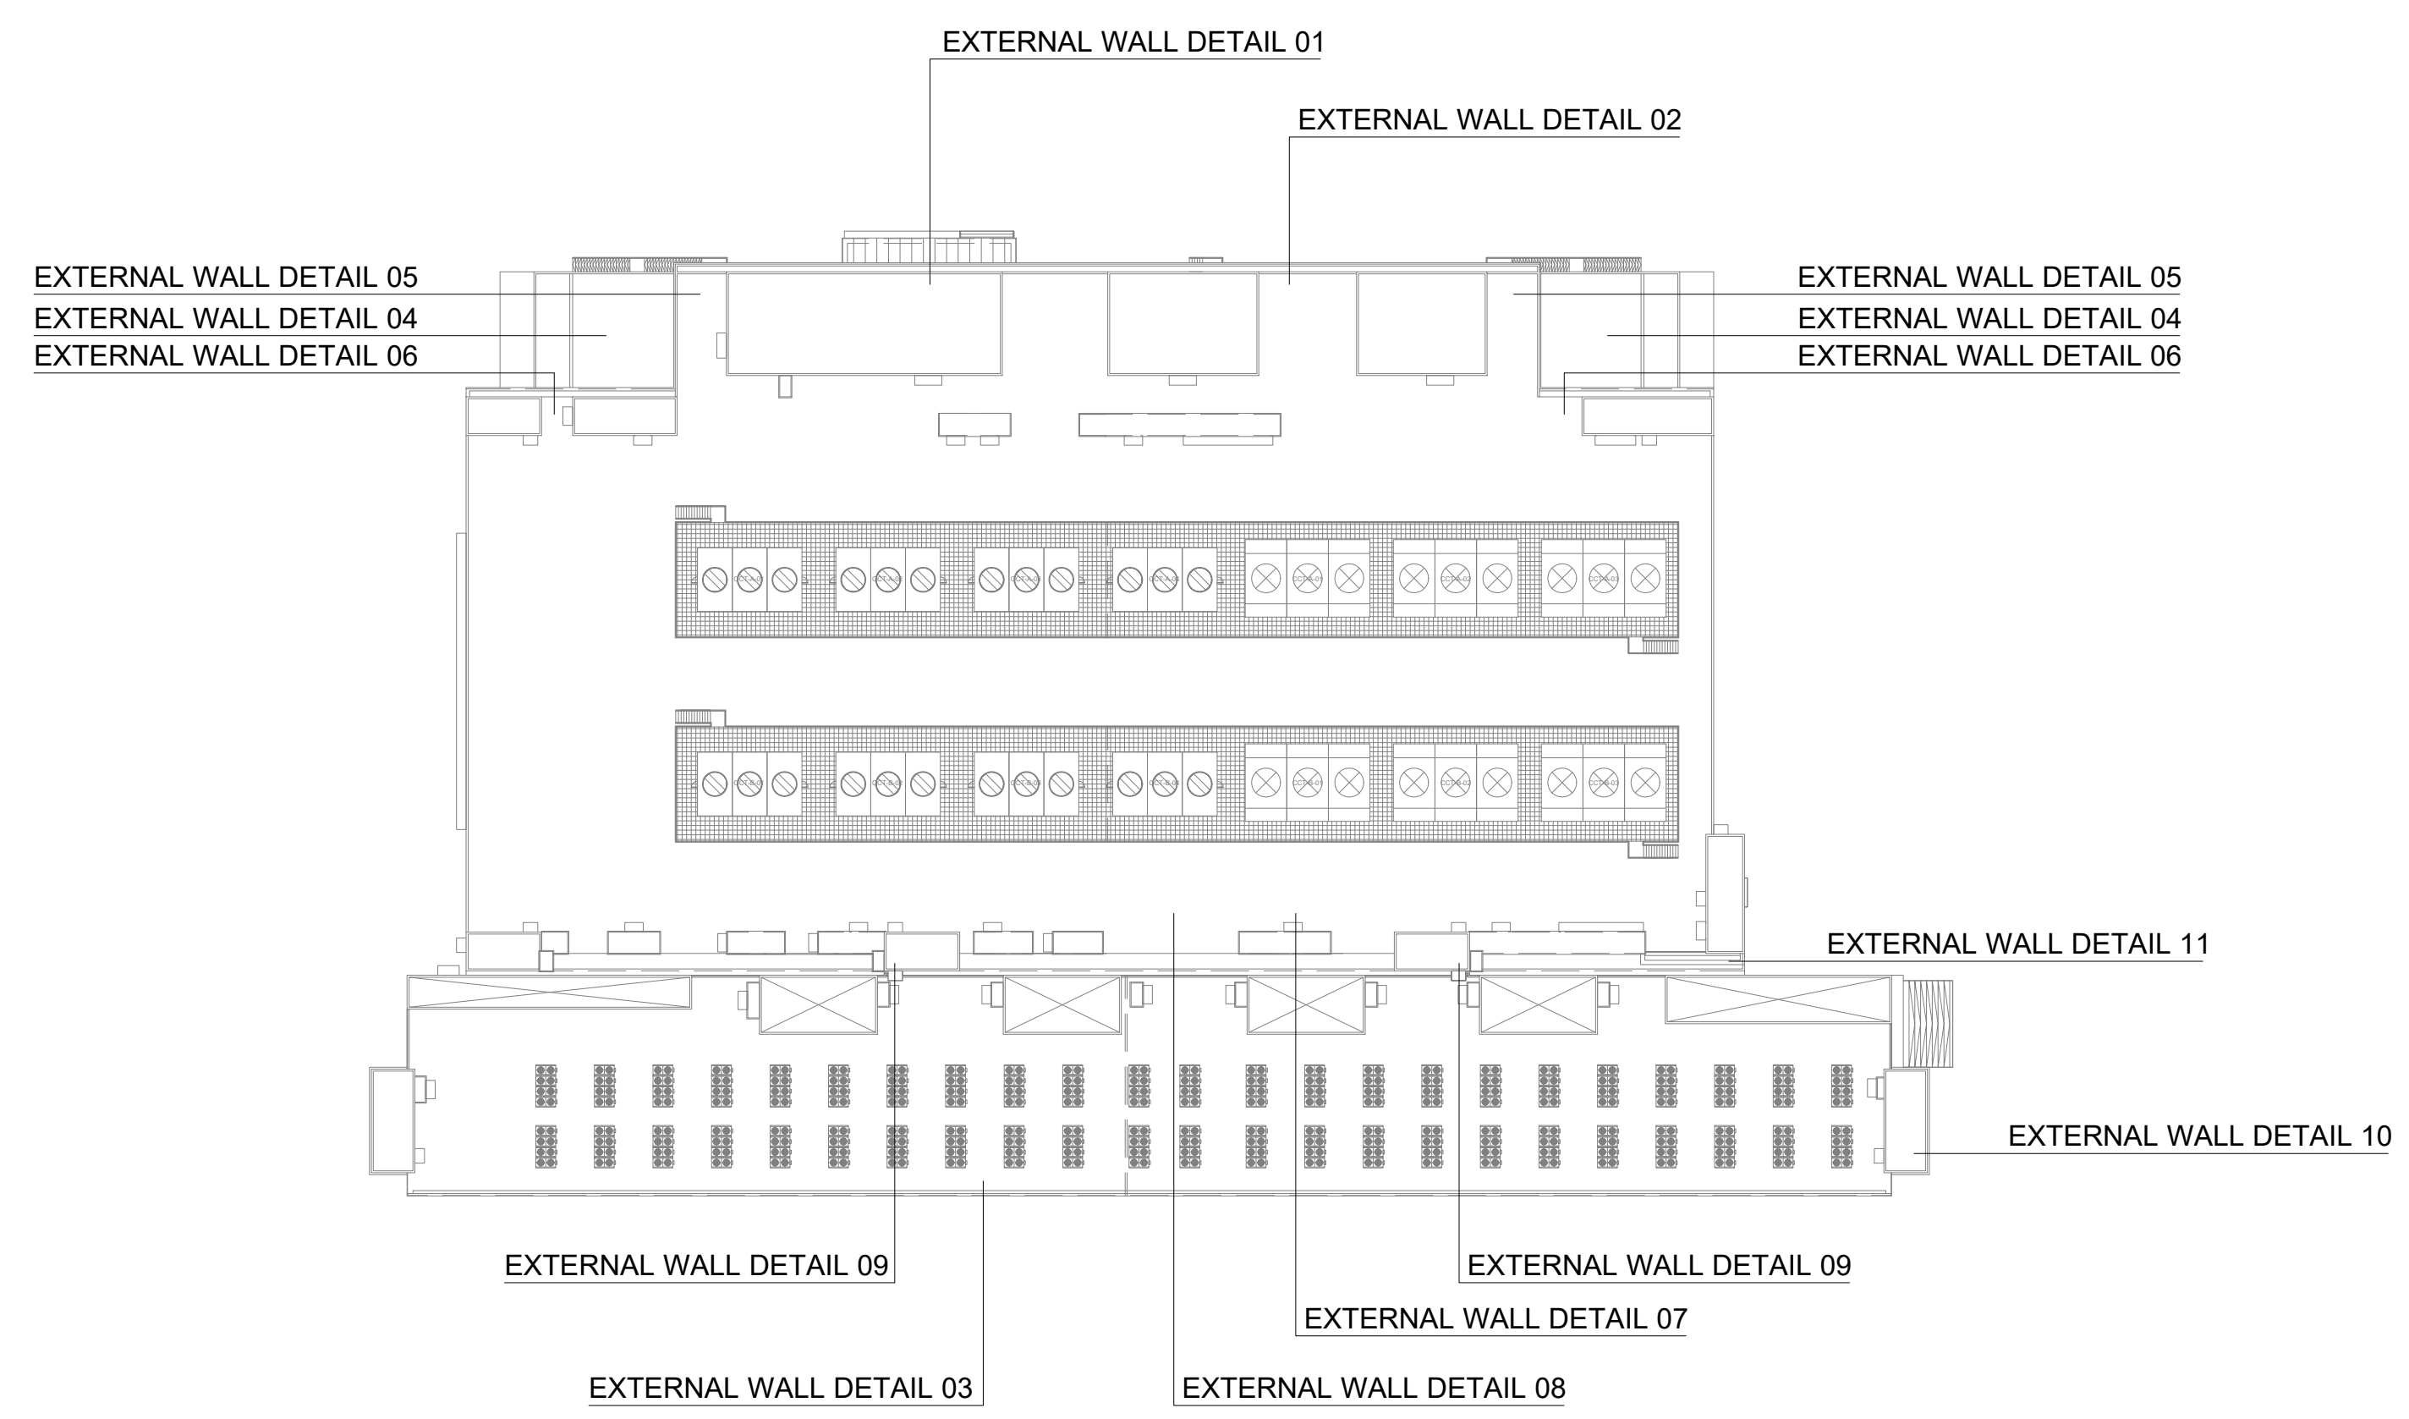

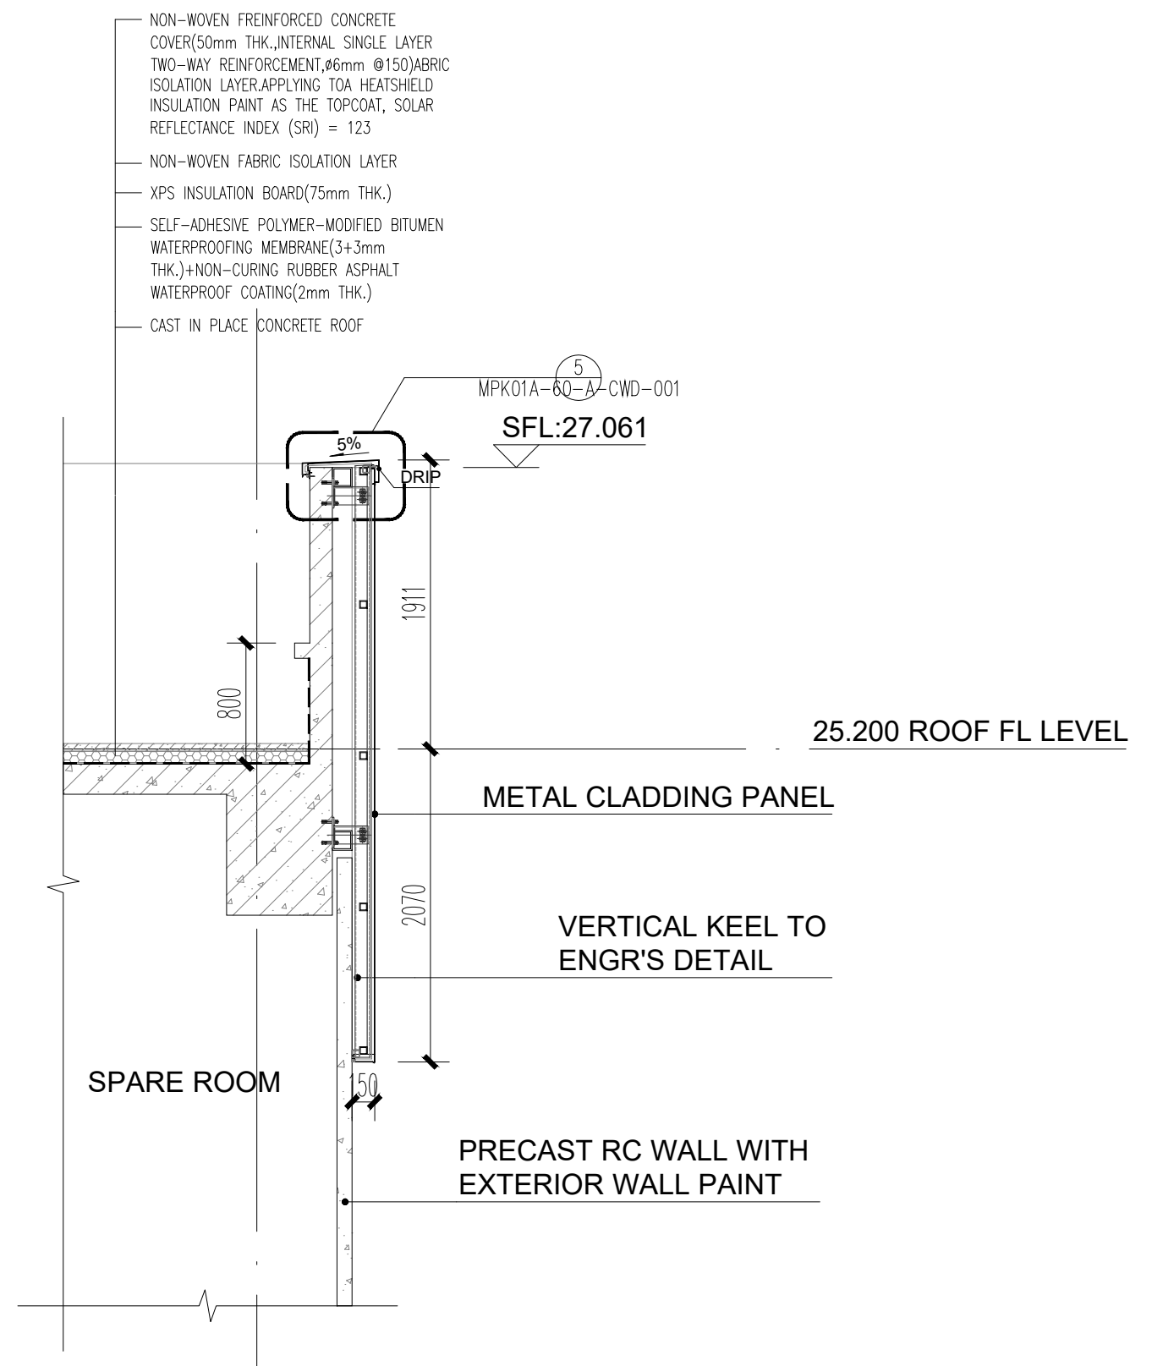
NON-WOVEN FREINFORCED CONCRETE COVER(50mm THK.,INTERNAL SINGLE LAYER TWO-WAY REINFORCEMENT,ø6mm @150)ABRIC ISOLATION LAYER.APPLYING TOA HEATSHIELD INSULATION PAINT AS THE TOPCOAT, SOLAR REFLECTANCE INDEX (SRI) = 123
NON-WOVEN FABRIC ISOLATION LAYER
XPS INSULATION BOARD(75mm THK.)
SELF-ADHESIVE POLYMER-MODIFIED BITUMEN WATERPROOFING MEMBRANE(3+3mm THK.)+NON-CURING RUBBER ASPHALT WATERPROOF COATING(2mm THK.)
CAST IN PLACE CONCRETE ROOF
MPK01A-60-A-CWD-001
SFL:27.061
25.200 ROOF FL LEVEL
METAL CLADDING PANEL
VERTICAL KEEL TO ENGR'S DETAIL
SPARE ROOM
PRECAST RC WALL WITH EXTERIOR WALL PAINT

EXTERNAL WALL DETAIL 05

Scale 1:50

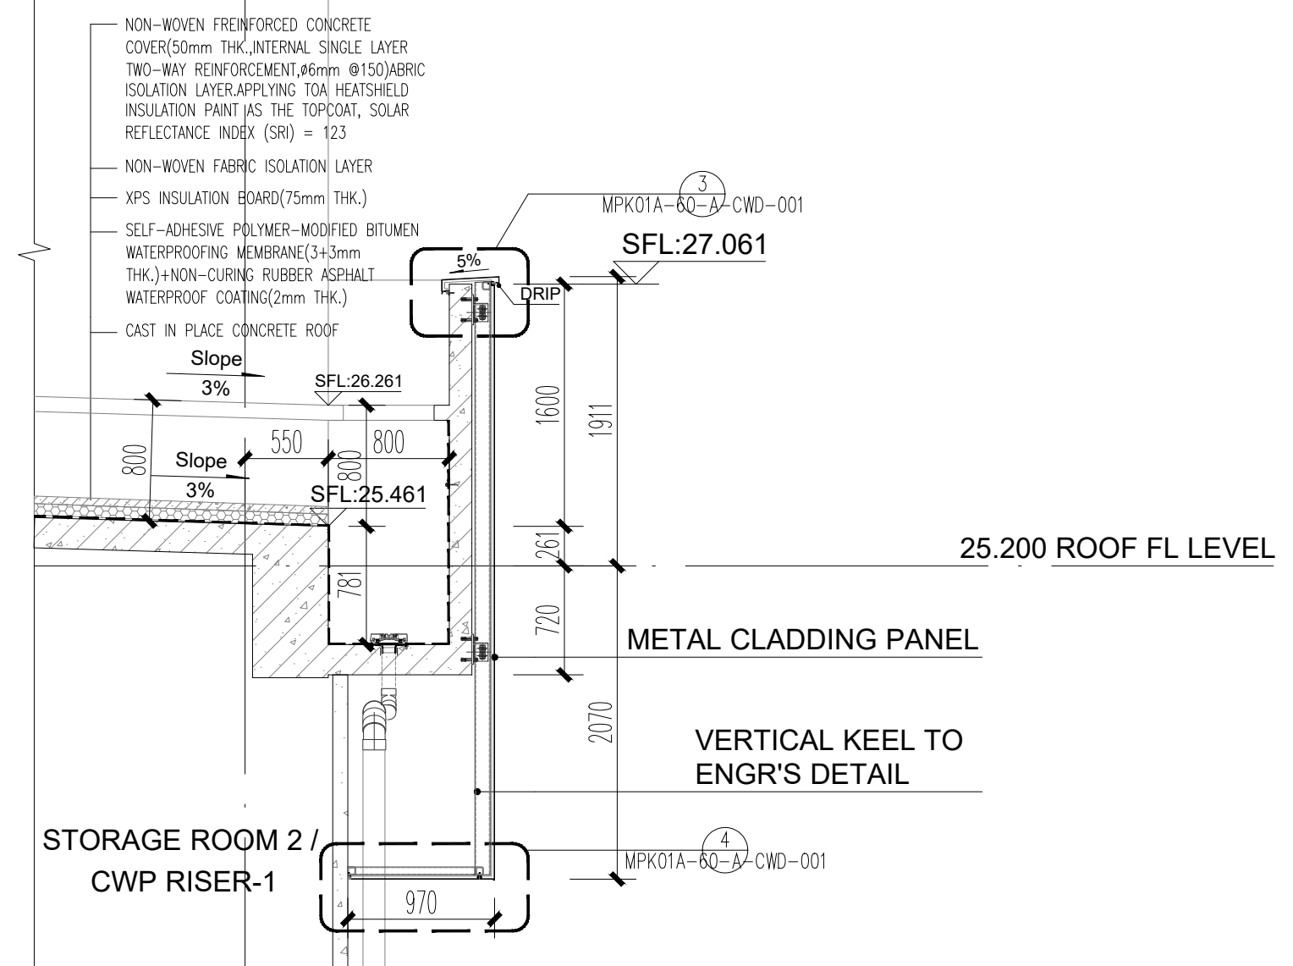
NON-WOVEN FREINFORCED CONCRETE COVER(50mm THK.,INTERNAL SINGLE LAYER TWO-WAY REINFORCEMENT,ø6mm @150)ABRIC ISOLATION LAYER.APPLYING TOA HEATSHIELD INSULATION PAINT AS THE TOPCOAT, SOLAR REFLECTANCE INDEX (SRI) = 123
NON-WOVEN FABRIC ISOLATION LAYER
XPS INSULATION BOARD(75mm THK.)
SELF-ADHESIVE POLYMER-MODIFIED BITUMEN WATERPROOFING MEMBRANE(3+3mm THK.)+NON-CURING RUBBER ASPHALT WATERPROOF COATING(2mm THK.)
CAST IN PLACE CONCRETE ROOF
MPK01A-60-A-CWD-001
SFL:27.061
Slope
3%
SFL:26.261
Slope
3%
SFL:25.461
25.200 ROOF FL LEVEL
METAL CLADDING PANEL
VERTICAL KEEL TO ENGR'S DETAIL
STORAGE ROOM 2 / CWP RISER-1

EXTERNAL WALL DETAIL 06

Scale 1:50

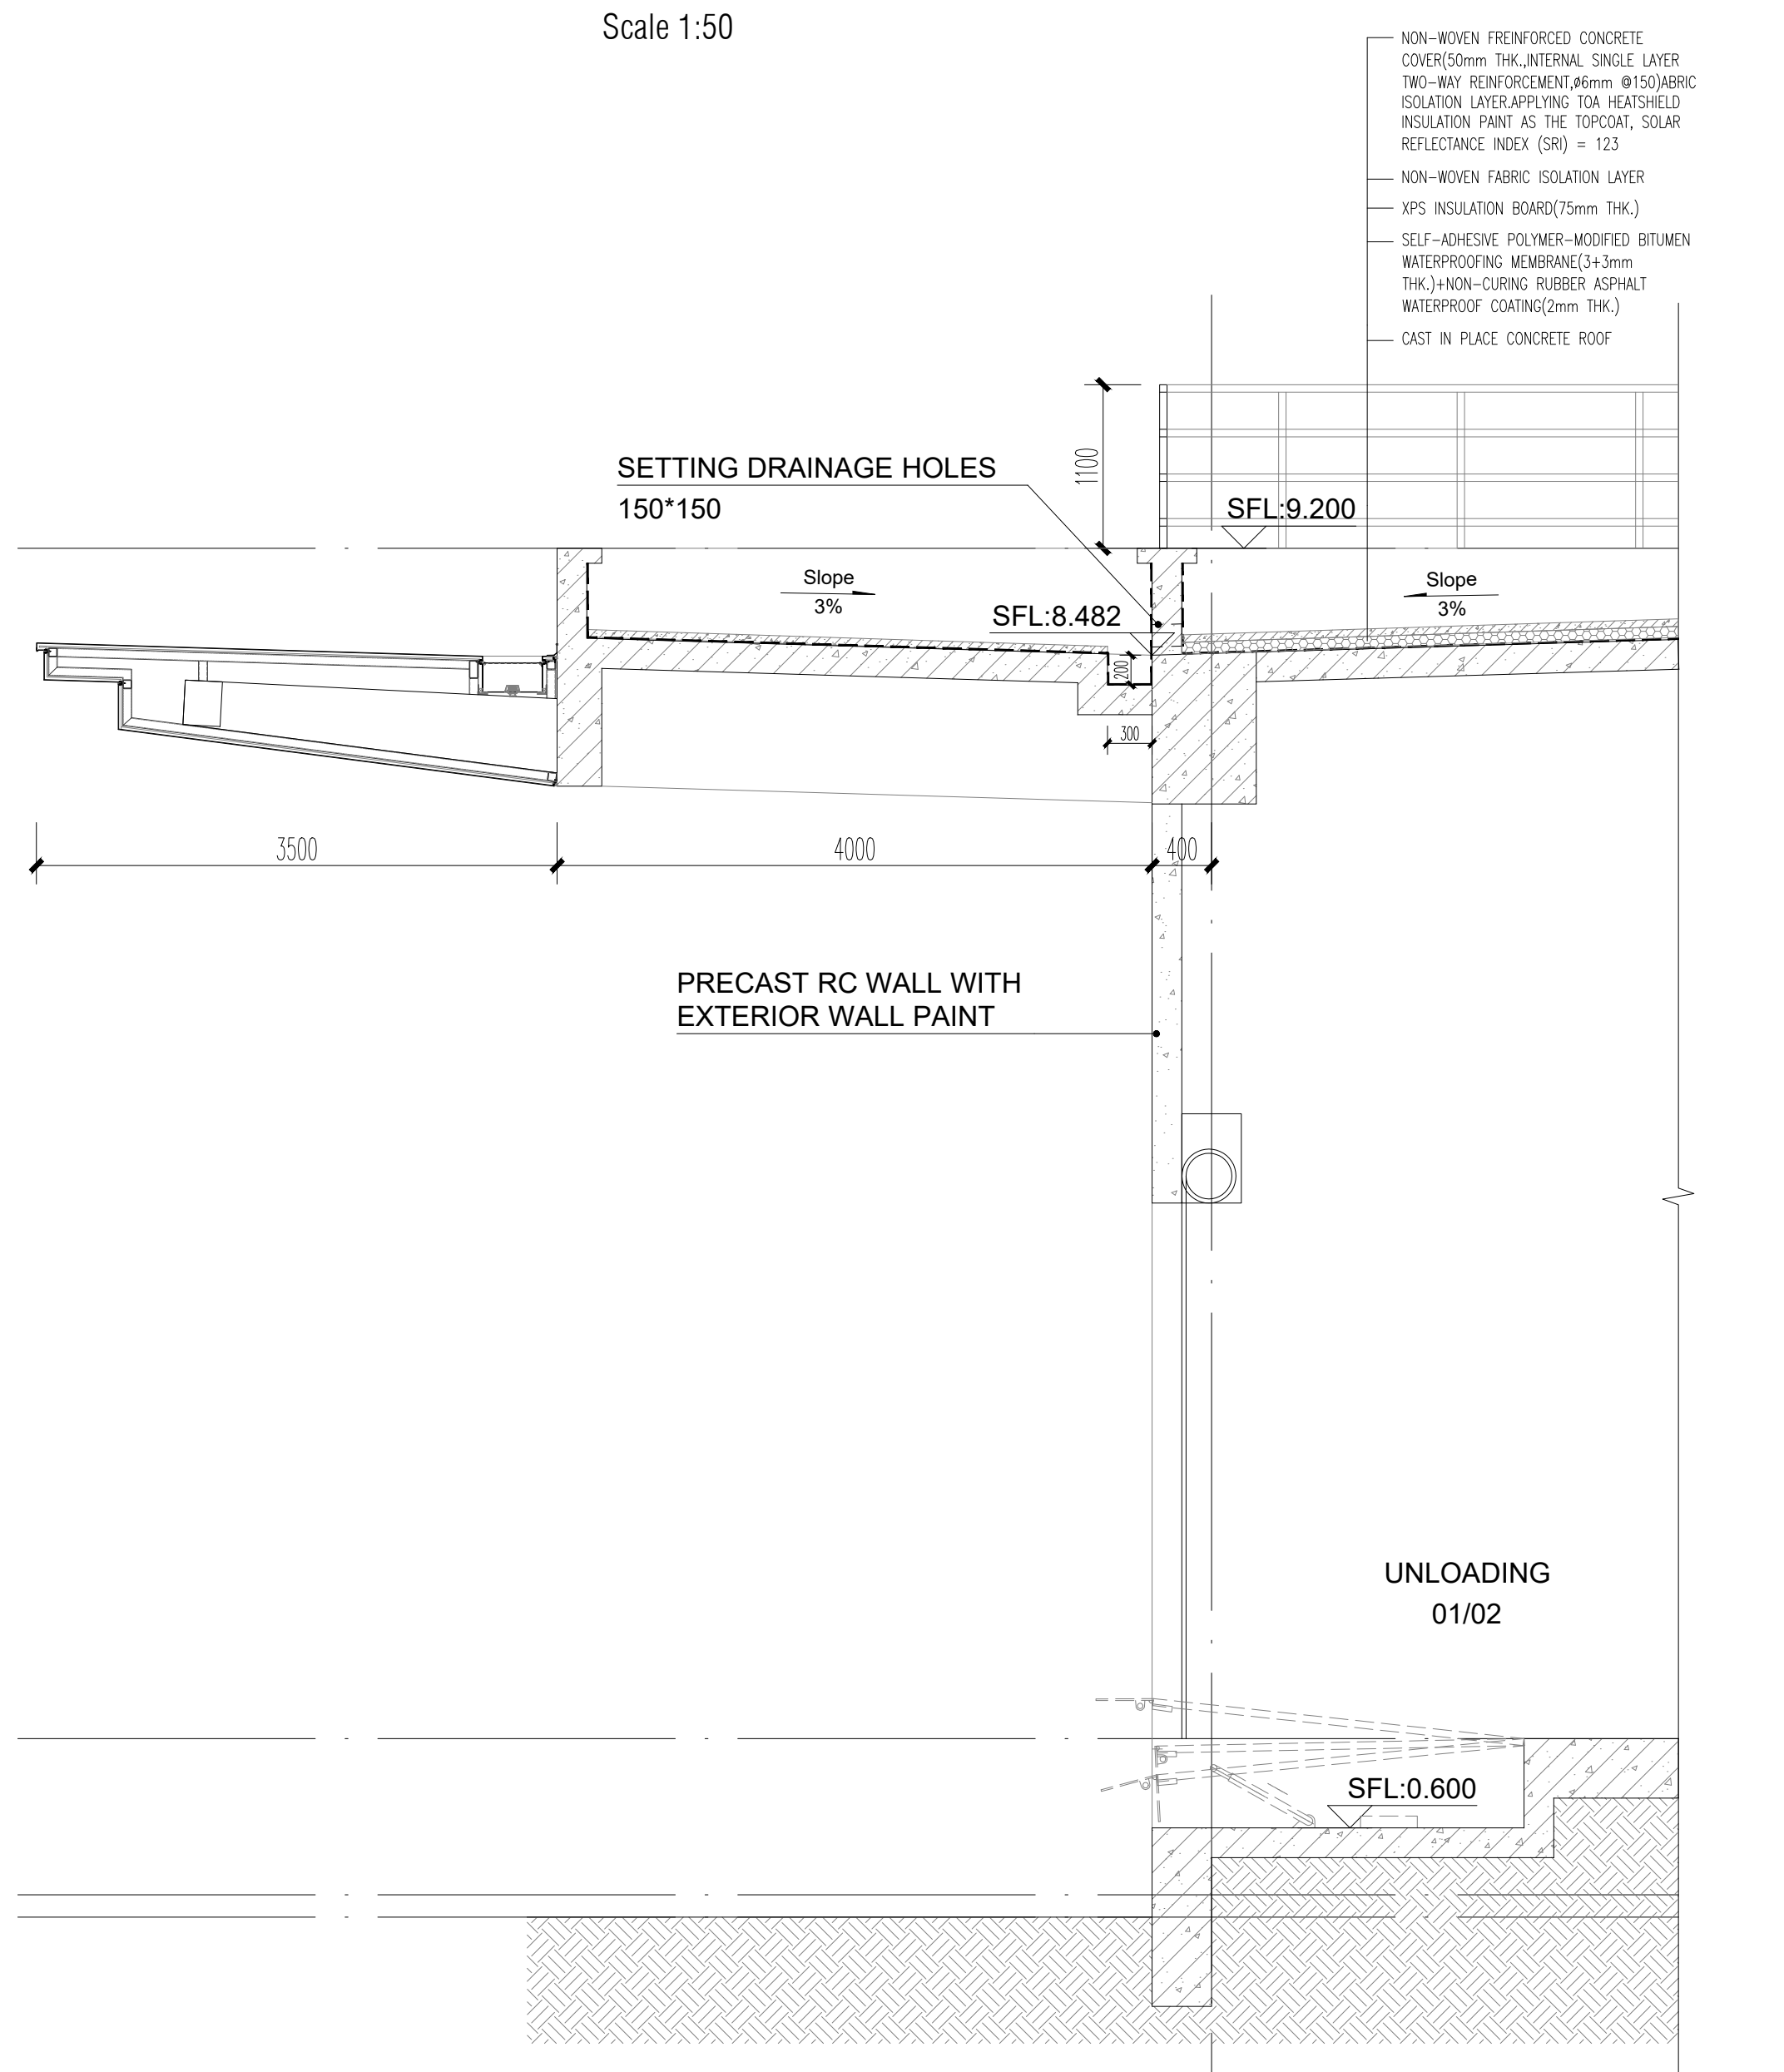
NON-WOVEN FREINFORCED CONCRETE COVER(50mm THK.,INTERNAL SINGLE LAYER TWO-WAY REINFORCEMENT,ø6mm @150)ABRIC ISOLATION LAYER.APPLYING TOA HEATSHIELD INSULATION PAINT AS THE TOPCOAT, SOLAR REFLECTANCE INDEX (SRI) = 123
NON-WOVEN FABRIC ISOLATION LAYER
XPS INSULATION BOARD(75mm THK.)
SELF-ADHESIVE POLYMER-MODIFIED BITUMEN WATERPROOFING MEMBRANE(3+3mm THK.)+NON-CURING RUBBER ASPHALT WATERPROOF COATING(2mm THK.)
CAST IN PLACE CONCRETE ROOF
SETTING DRAINAGE HOLES 150*150
SFL:9.200
9.200 2ND FL LEVEL
Slope
3%
SFL:8.482
Slope
3%
3500
4000
PRECAST RC WALL WITH EXTERIOR WALL PAINT
UNLOADING 01/02
1.200 1ST FL LEVEL
SFL:0.600
0.150 FOOT PATH LEVEL
±0.000 INTERNAL ROAD LEVEL

EXTERNAL WALL DETAIL 04

Scale 1:50

NOTE : THIS PRINT IS OF A CONFIDENTIAL NATURE, IT SHALL NOT BE TRACED,PHOTOGRAPHED,PHOTOSTATED OR REPRODUCED IN ANY MANER,NOR USED FOR ANY PURPOSE WHATSOEVER EXCEPT BY WRITTEN PERMISSION

CLIENT :

GULF EDGE DC 01

87 Wireless Road, M Thai Tower 11th. Floor, All Seasons Place, Lumpini,
Pathumwan, Bangkok 10330, Thailand

CONTRACTOR :

华西发展(泰国)有限公司
บริษัท หัวซือ ดีเวลลอปเม้นต์ (ประเทศไทย) จำกัด
HUASHI DEVELOPMENT CO.,LTD
No. 202, Room No. 1403, 14/F, Le Concorde Building,
Ratchadapisek Road, Huaykhwang Sub-District,
Huaykhwang District, Bangkok Metropolitan 10310.

CONSULTANT :

ARbay
บริษัท เอ อาร์ เบย์ จำกัด
ARbay Company Limited
31 st Floor Bangkok Insurance Building
25 South Sathorn road Thungmahamek
Sathorn Bangkok 10120 THAILAND
T +66 (0) 2286 8199
F +66 (0) 2286 2863
info@arbay.co.th

CONSULTANT :

Qbic Engineers & Architects Co.,Ltd.
8 Soi KALONG 4 SANAMBINNAM ROAD,
THASAI SUB-DISTRICT, MUANG NONTHABURI DISTRICT
, NONTHABURI.
Tel 662-950-4374
Fax 662-580-3231
E-Mail : qbic@qbic.co.th, www.qbic.co.th
QBIC ENGINEERS AND ARCHITECTS CO.,LTD.

CONSULTANT :

MITR
MITR TECHNICAL CONSULTANT CO.,LTD.
1168/8 12th FLOOR, LUMPINI TOWER BUILDING,
RAMA IV RD., THUNGMAHAMEK, SATHORN, BANGKOK 10120, THAILAND
TEL : 0-2679-9079-84
FAX : 0-2679-9085 E-mail: mitr_dd@mitr.com

Architect :	SIGNATURE
ประกิต พนานุรัตน์ วสถ. 580 ที่อยู่ 251/1 ถ.จารุเมือง แขวงรองเมือง เขตปทุมวัน กรุงเทพมหานคร โทรศัพท์ 02-286-8199	

Structural Engineer :	SIGNATURE
วิศวกรผู้ออกแบบโครงสร้าง	
ณัฐสม สงวนวงษ์ วย 1423 ที่อยู่ 2/1 ซ.รามคำแหง 150 ถ.รามคำแหง แขวง สะพานสูง เขต สะพานสูง กทม. 10240	

Structural Inspector :	SIGNATURE
วิศวกรผู้ตรวจสอบโครงสร้าง	
โกมล จุฑาภัทร วย 964 ที่อยู่ 24/18 ซ.นวมินทร์ 129 ถ. นวมินทร์ แขวง นวลจันทร์ เขต บึงกุ่ม กทม. 10230	

Electrical Engineer :	SIGNATURE
วิศวกรผู้ออกแบบระบบไฟฟ้ากำลัง	
นายสุภัทร บูรณวิทย์ วฟก.1265 ที่อยู่ 21 ซอยทานสัมฤทธิ์ 13 ตำบลท่าทราย อ.เมืองนนทบุรี จ.นนทบุรี 11000	

Mechanical Engineer :	SIGNATURE
วิศวกรผู้ออกแบบระบบเครื่องกลและปรับอากาศ	
นายประสิทธิ์ เกียวสุนทร วก.1221 ที่อยู่ 44/372 ซอยบางกระดี่ 35/1 แขวงแสมดำ เขตบางขุนเทียน กทม. 10150	ประสิทธิ์

Sanitary Engineer :	SIGNATURE
วิศวกรผู้ออกแบบระบบสุขาภิบาล และดับเพลิง	
นายทศวรรษ สนั่นฤทธิ์ วส. 215 ที่อยู่ บ้านเลขที่ 99/107 หมู่ที่ 3 ต.ศีรษะจรเข้น้อย อ.บางเสาธง จ.สมุทรปราการ 10540	ทศวรรษ

ISSUE/REVISION

REV.	DESCRIPTION	DATE
A	90% DEVELOPED	09/05/2026

PROJECT NAME :

GEDC 01

LOCATION:
Nikhom Phattana district, Rayong ,industrial estate,CPGC

BUILDING :
MAIN BUILDING

90% DEVELOPED

TITLE :

EXTERNAL WALL DETAILS A

JOB NO.	SCALE 1:50
DRAWN FLY	REF.
CHECKED LJC	DWG.NO.
APPROVED LXD	MPK01A-90-A-EW-001
DATE 2026.05.09	