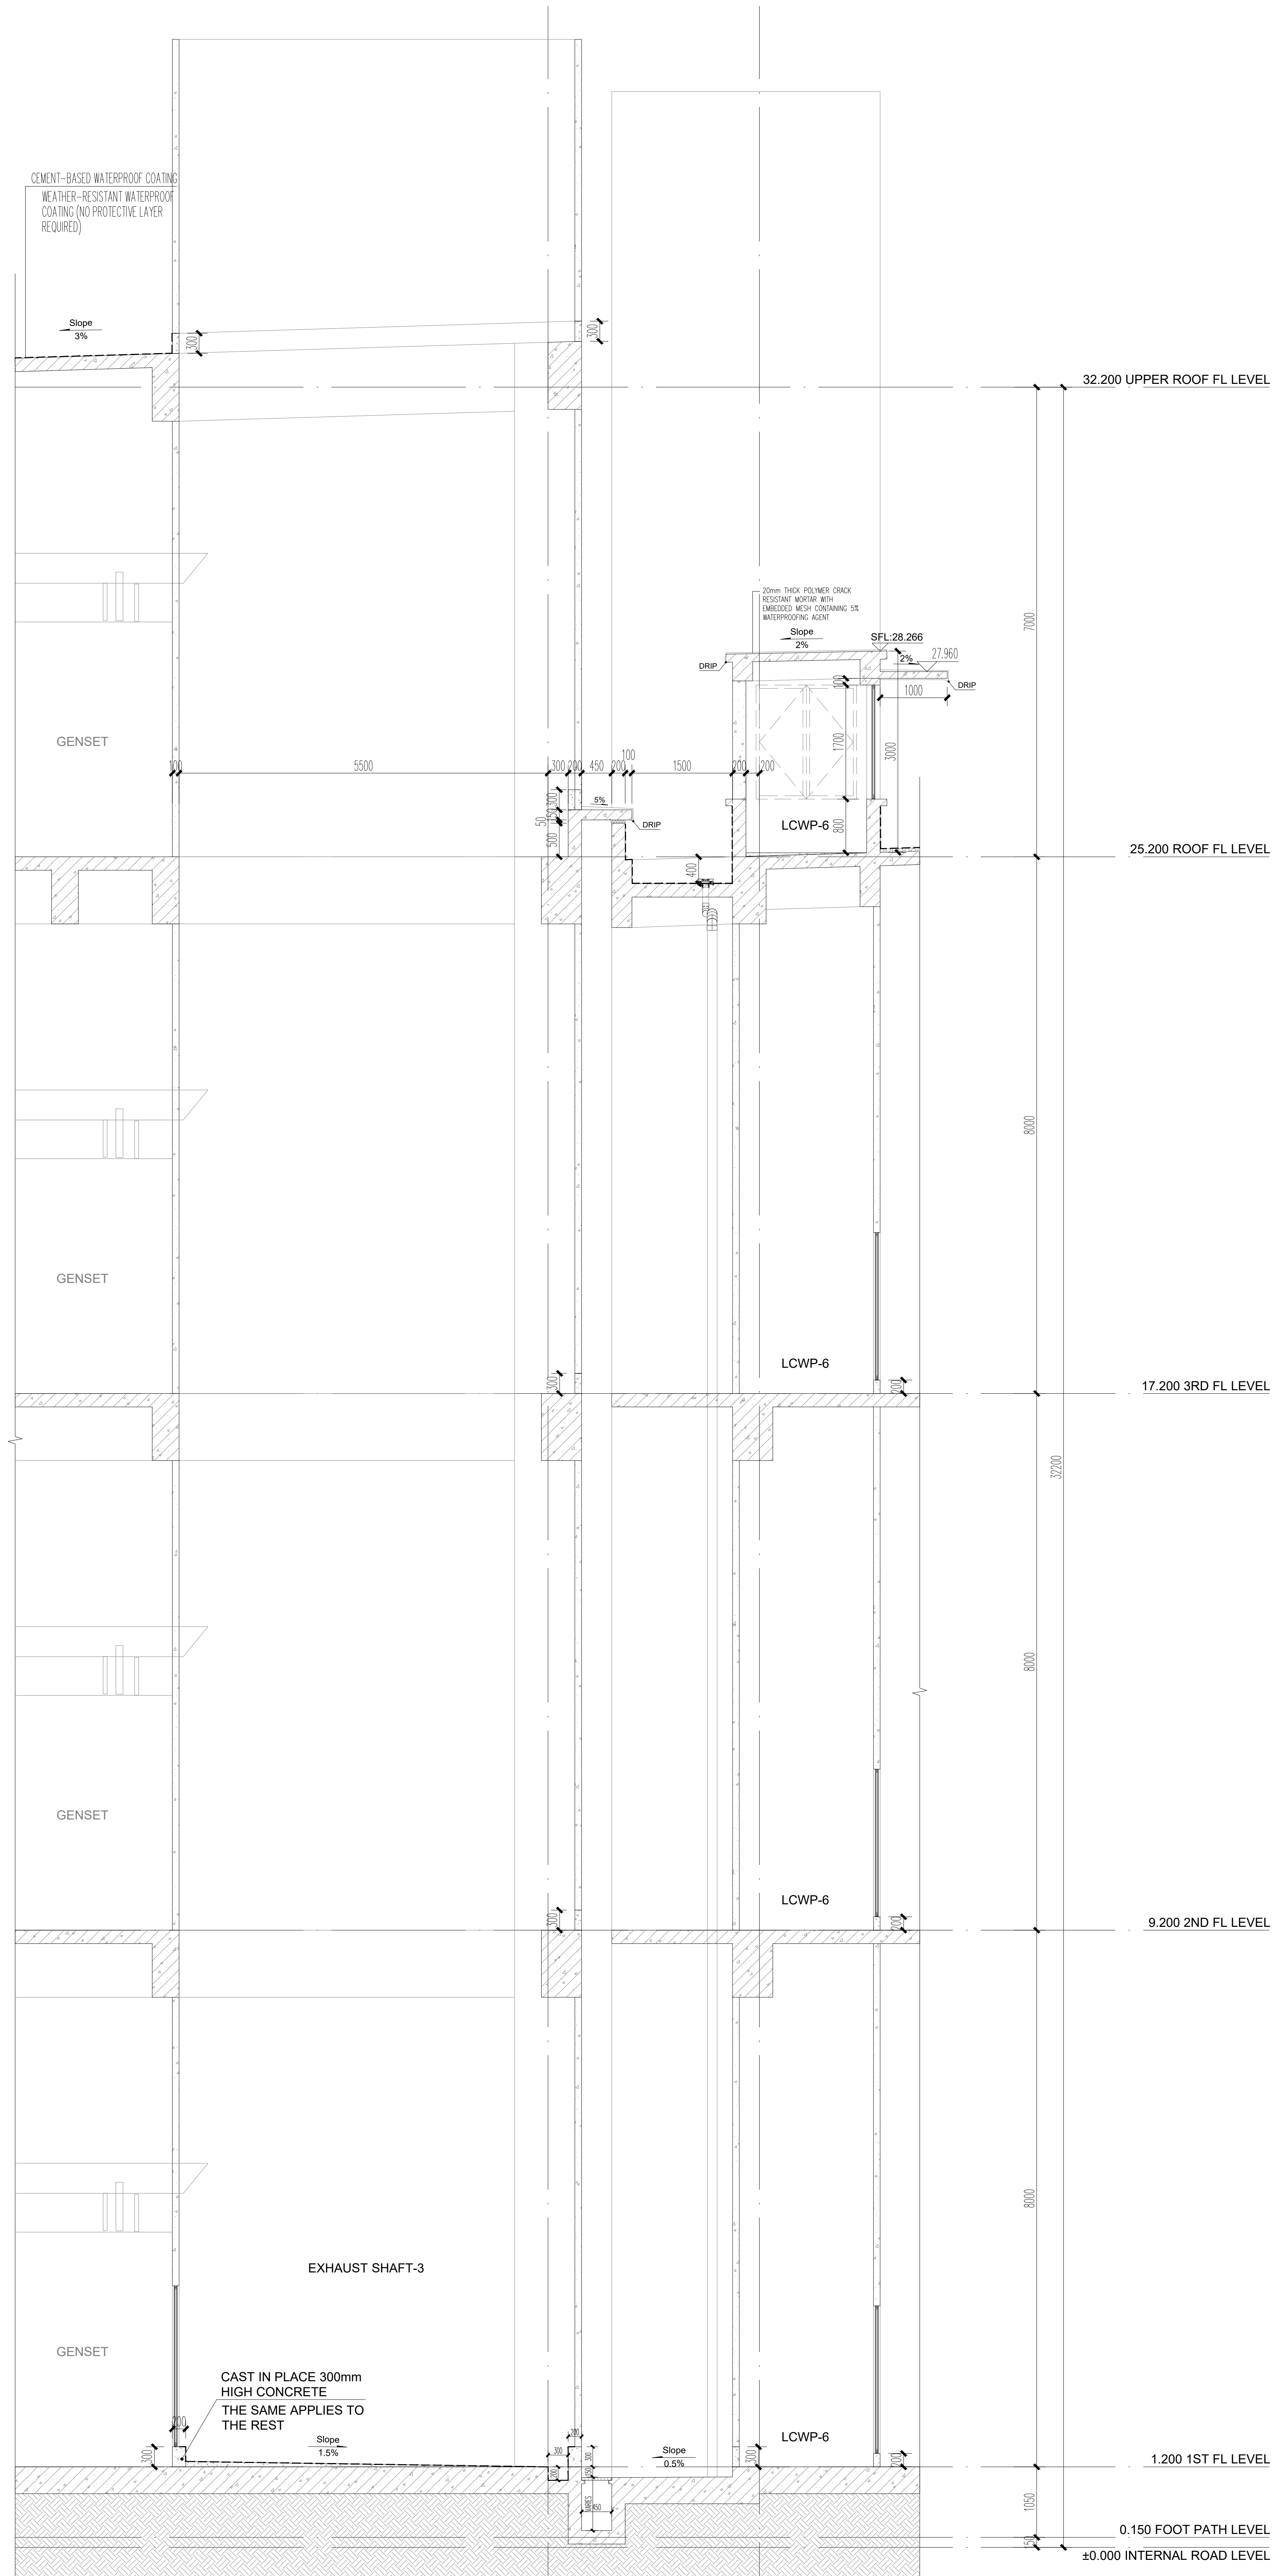
CEMENT-BASED WATERPROOF COATING
WEATHER-RESISTANT WATERPROOF COATING (NO PROTECTIVE LAYER REQUIRED)
Slope 3%
32.200 UPPER ROOF FL LEVEL
20mm THICK POLYMER CRACK RESISTANT MORTAR WITH EMBEDDED MESH CONTAINING 5% WATERPROOFING AGENT
Slope 2%
SFL:28.266
27.960
DRIP
1000
7000
GENSET
5500
1500
LCWP-6
25.200 ROOF FL LEVEL
8000
17.200 3RD FL LEVEL
32200
9.200 2ND FL LEVEL
EXHAUST SHAFT-3
CAST IN PLACE 300mm HIGH CONCRETE
THE SAME APPLIES TO THE REST
Slope 1.5%
Slope 0.5%
1.200 1ST FL LEVEL
0.150 FOOT PATH LEVEL
±0.000 INTERNAL ROAD LEVEL
1050

EXTERNAL WALL DETAIL 07

Scale 1:50

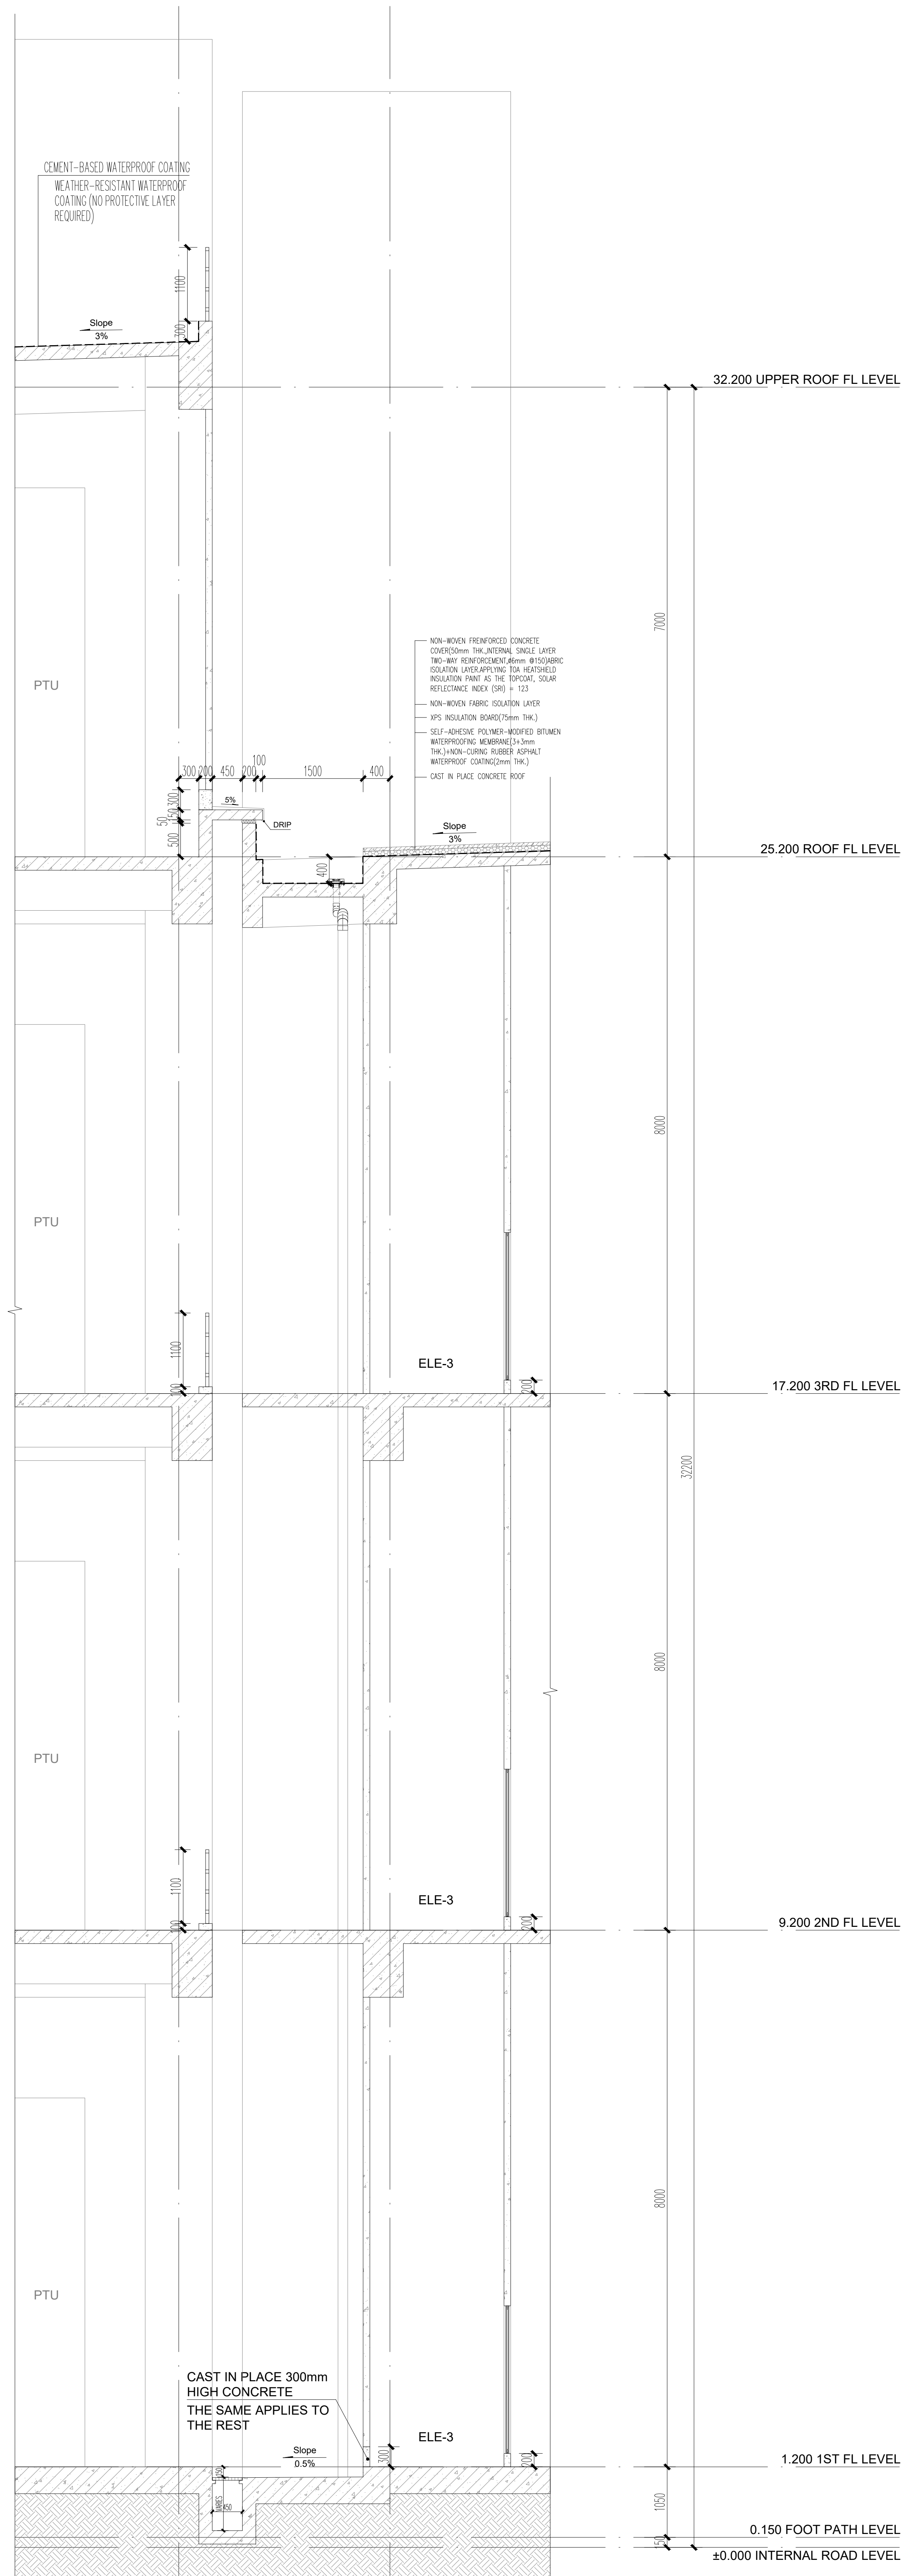
CEMENT-BASED WATERPROOF COATING
WEATHER-RESISTANT WATERPROOF COATING (NO PROTECTIVE LAYER REQUIRED)
Slope 3%
32.200 UPPER ROOF FL LEVEL
NON-WOVEN FREINFORCED CONCRETE COVER(50mm THK.,INTERNAL SINGLE LAYER TWO-WAY REINFORCEMENT,ø6mm @150)ABRIC ISOLATION LAYER.APPLYING TOA HEATSHIELD INSULATION PAINT AS THE TOPCOAT, SOLAR REFLECTANCE INDEX (SRI) = 123
NON-WOVEN FABRIC ISOLATION LAYER
XPS INSULATION BOARD(75mm THK.)
SELF-ADHESIVE POLYMER-MODIFIED BITUMEN WATERPROOFING MEMBRANE(3+3mm THK.)+NON-CURING RUBBER ASPHALT WATERPROOF COATING(2mm THK.)
CAST IN PLACE CONCRETE ROOF
PTU
1500
400
DRIP
Slope 3%
25.200 ROOF FL LEVEL
7000
8000
ELE-3
17.200 3RD FL LEVEL
32200
9.200 2ND FL LEVEL
CAST IN PLACE 300mm HIGH CONCRETE
THE SAME APPLIES TO THE REST
Slope 0.5%
1.200 1ST FL LEVEL
0.150 FOOT PATH LEVEL
±0.000 INTERNAL ROAD LEVEL
1050

EXTERNAL WALL DETAIL 08

Scale 1:50

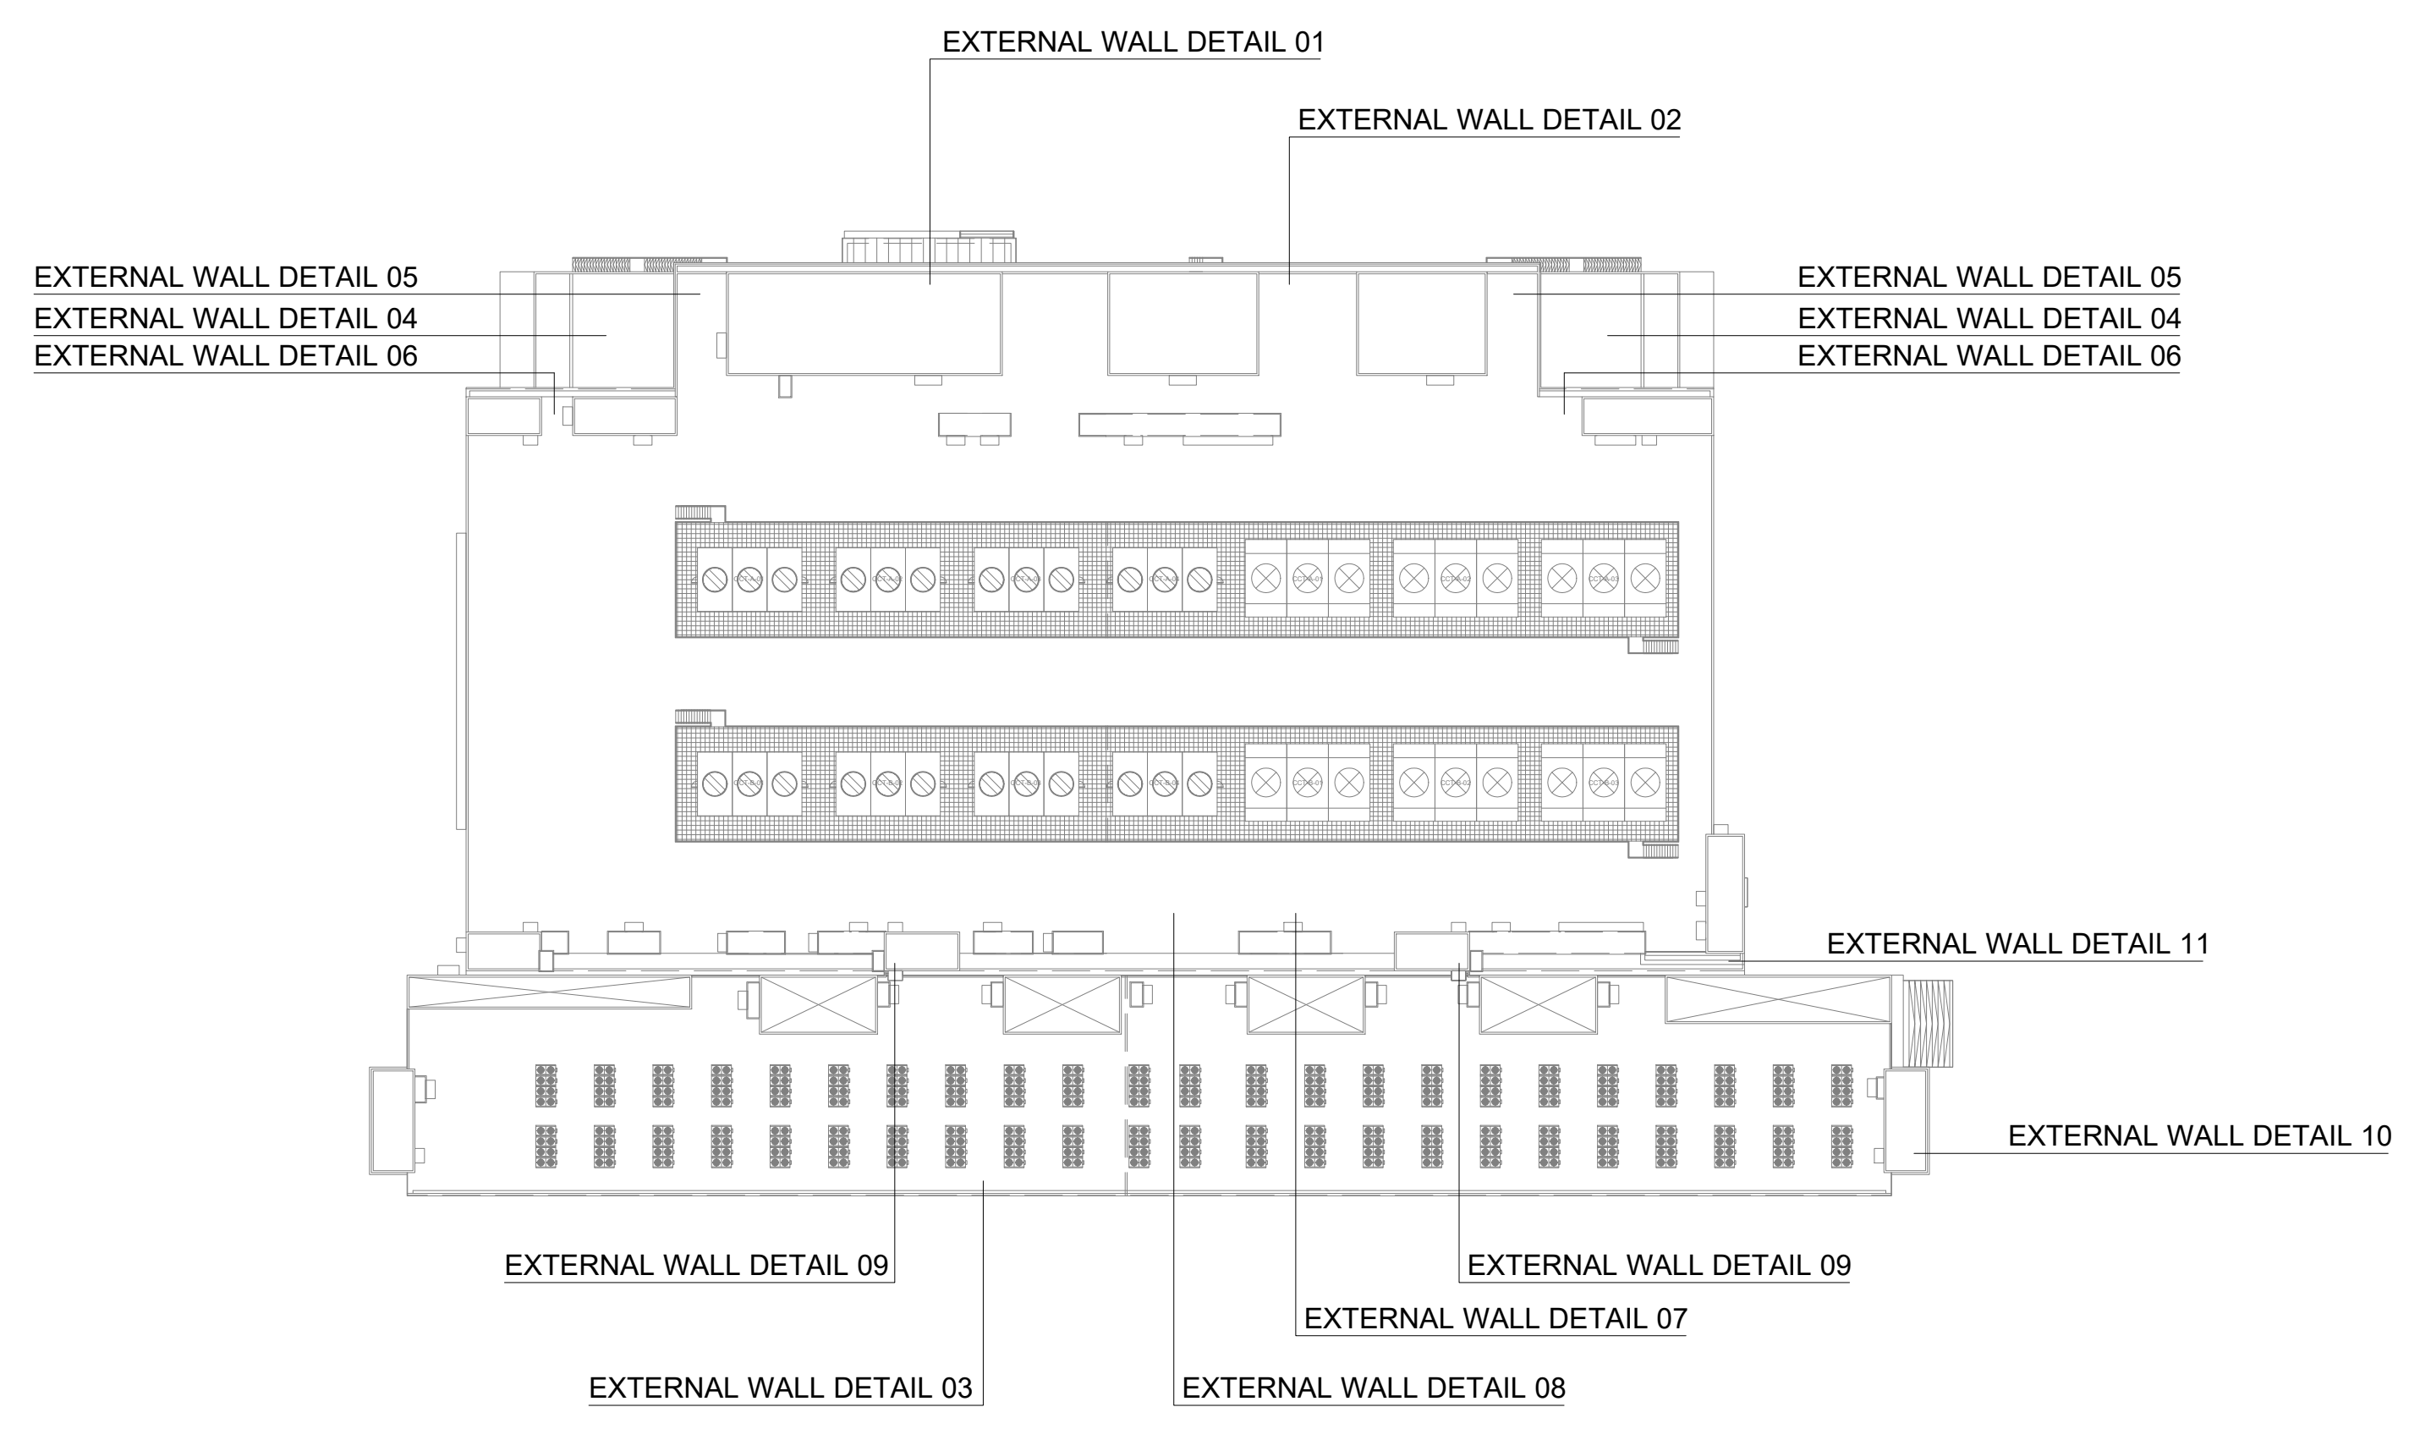

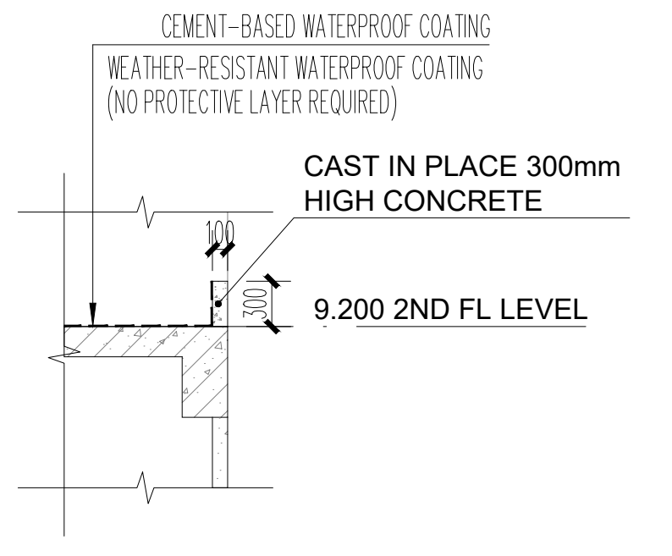
CEMENT-BASED WATERPROOF COATING
WEATHER-RESISTANT WATERPROOF COATING (NO PROTECTIVE LAYER REQUIRED)
CAST IN PLACE 300mm HIGH CONCRETE
100
300
9.200 2ND FL LEVEL

EXTERNAL WALL DETAIL 11

Scale 1:50

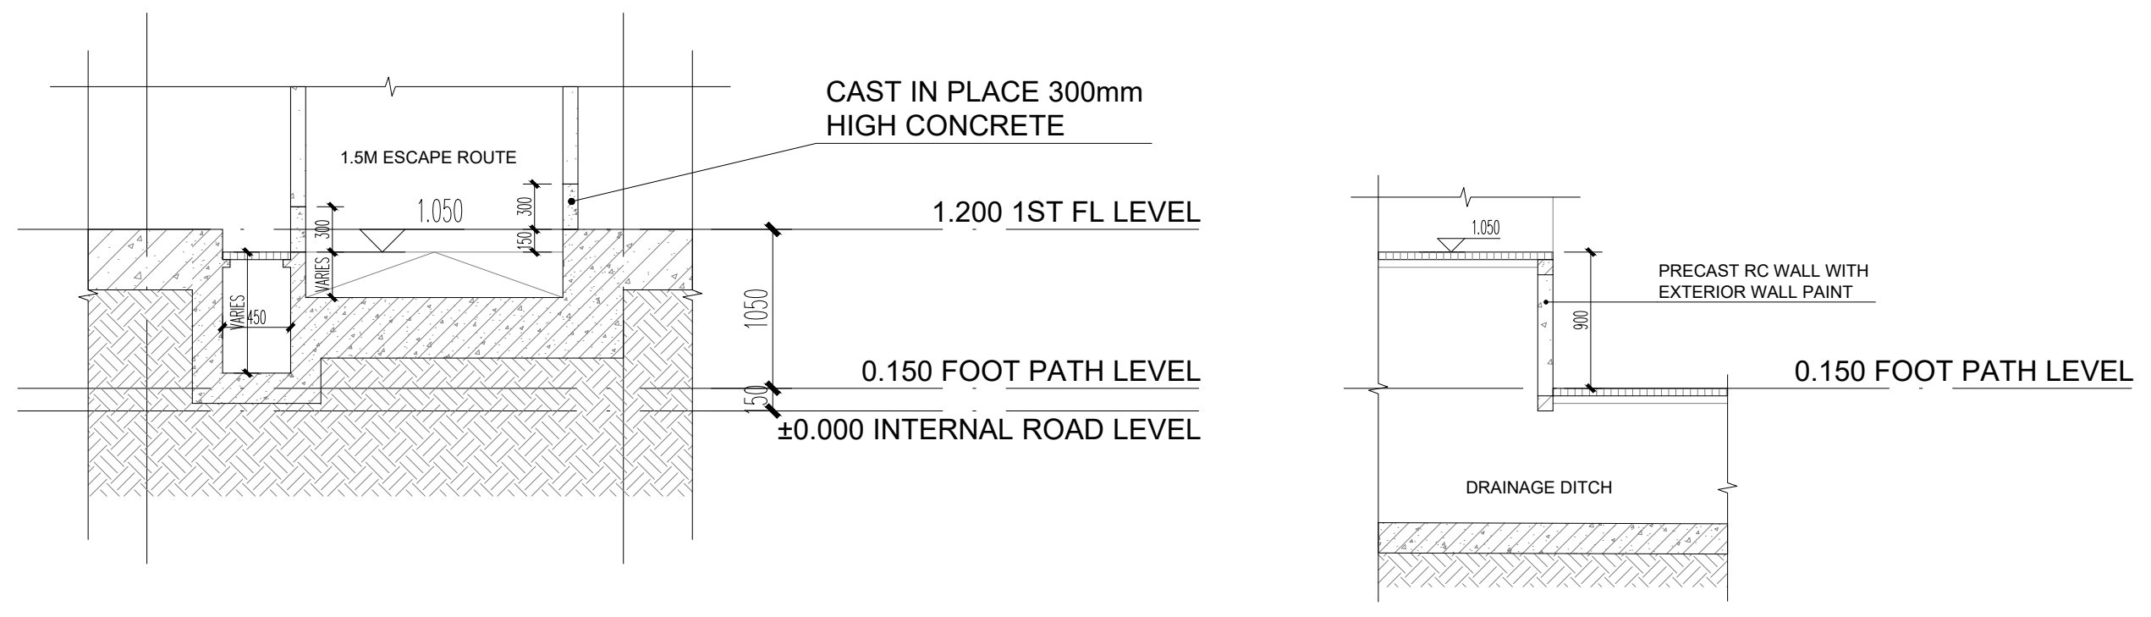
CAST IN PLACE 300mm HIGH CONCRETE
1.5M ESCAPE ROUTE
1.050
300
150
VARIES
450
1.200 1ST FL LEVEL
1050
0.150 FOOT PATH LEVEL
±0.000 INTERNAL ROAD LEVEL
PRECAST RC WALL WITH EXTERIOR WALL PAINT
900
DRAINAGE DITCH

EXTERNAL WALL DETAIL 12

Scale 1:50

(DETAIL OF DRAINAGE DITCH CONSTRUCTION METHOD AT 1.5m ESCAPE ROUTE LOCATION ON 1ST FLOOR)

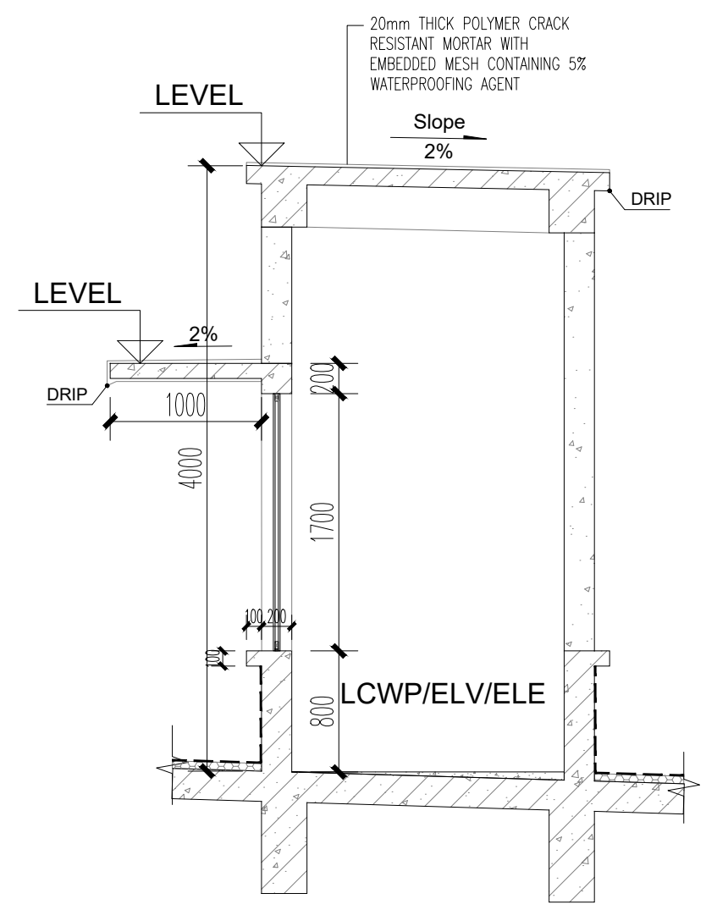
20mm THICK POLYMER CRACK RESISTANT MORTAR WITH EMBEDDED MESH CONTAINING 5% WATERPROOFING AGENT
LEVEL
Slope 2%
DRIP
LEVEL
2%
1000
4000
200
1700
100 200
100
800
LCWP/ELV/ELE

SHEFT DETAIL 01

Scale 1:50
(THE LEVEL IS DETAILED IN THE FLOOR PLAN)

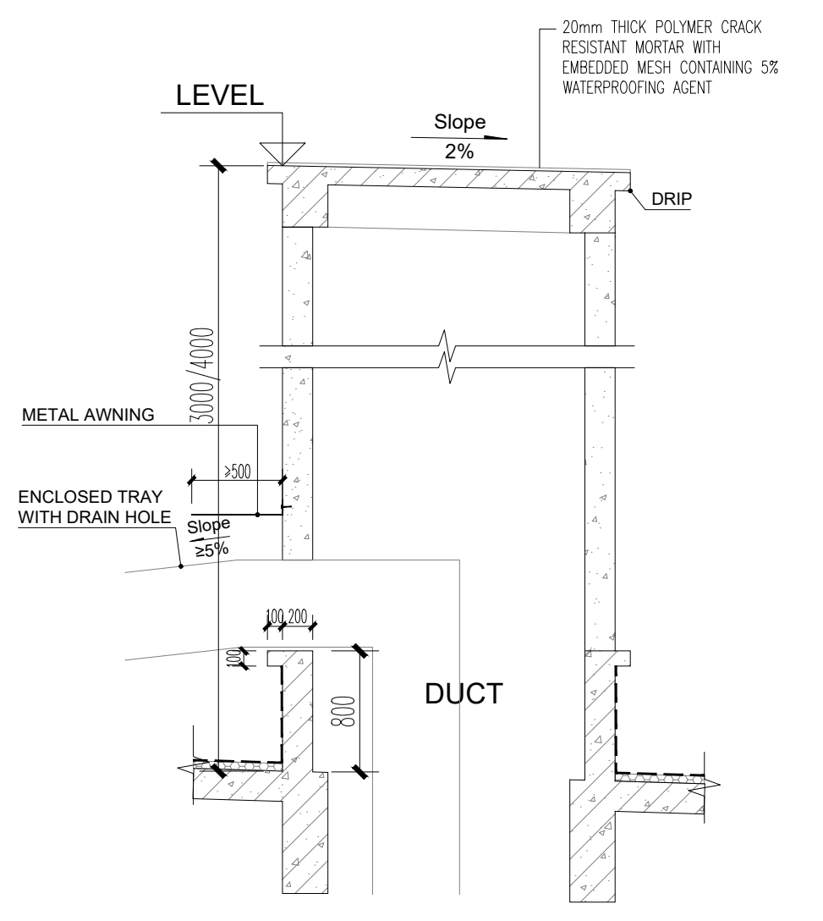
20mm THICK POLYMER CRACK RESISTANT MORTAR WITH EMBEDDED MESH CONTAINING 5% WATERPROOFING AGENT
LEVEL
Slope 2%
DRIP
3000/4000
METAL AWNING
ENCLOSED TRAY WITH DRAIN HOLE
>500
Slope ≥5%
100 200
100
800
DUCT

SHEFT DETAIL 02

Scale 1:50
(THE LEVEL IS DETAILED IN THE FLOOR PLAN)

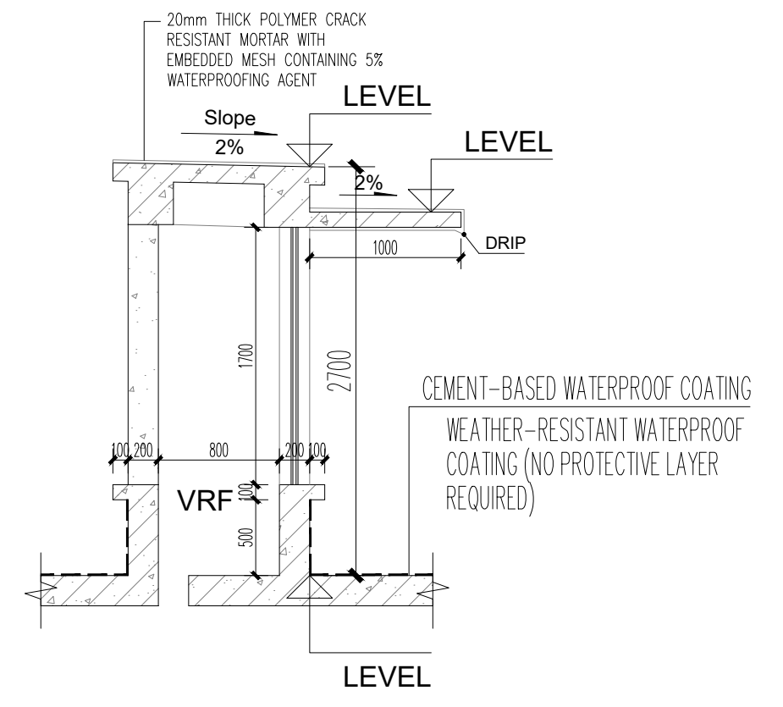
20mm THICK POLYMER CRACK RESISTANT MORTAR WITH EMBEDDED MESH CONTAINING 5% WATERPROOFING AGENT
LEVEL
Slope 2%
LEVEL
2%
DRIP
1000
1700
2700
CEMENT-BASED WATERPROOF COATING
WEATHER-RESISTANT WATERPROOF COATING (NO PROTECTIVE LAYER REQUIRED)
100 200
800
200 100
VRF
100
500
LEVEL

SHEFT DETAIL 03

Scale 1:50
(FOR DIESEL GENERATOR PLATFORM ROOF)
(THE LEVEL IS DETAILED IN THE FLOOR PLAN)

CLIENT :

GULF EDGE DC 01

87 Wireless Road, M Thai Tower 11th. Floor, All Seasons Place, Lumpini,
Pathumwan, Bangkok 10330, Thailand

CONTRACTOR :

华西发展(泰国)有限公司
บริษัท หัวซือ ดีเวลลอปเม้นต์ (ประเทศไทย) จำกัด
HUASHI DEVELOPMENT CO.,LTD
No. 202, Room No. 1403, 14/F, Le Concorde Building,
Ratchadapisek Road, Huaykhwang Sub-District,
Huaykhwang District, Bangkok Metropolitan 10310.

CONSULTANT :

ARbay
บริษัท เอ อาร์ เบย์ จำกัด
ARbay Company Limited
31 st Floor Bangkok Insurance Building
25 South Sathorn road Thungmahamek
Sathorn Bangkok 10120 THAILAND
T +66 (0) 2286 8199
F +66 (0) 2286 2863
info@arbay.co.th

CONSULTANT :

Qbic Engineers & Architects Co.,Ltd.
8 Soi KALONG 4 SANAMBINNAM ROAD,
THASAI SUB-DISTRICT, MUANG NONTHABURI DISTRICT
, NONTHABURI.
Tel 662-950-4374
Fax 662-580-3231
E-Mail : qbic@qbic.co.th, www.qbic.co.th
QBIC ENGINEERS AND ARCHITECTS CO.,LTD.

CONSULTANT :

MITR
MITR TECHNICAL CONSULTANT CO.,LTD.
1168/8 12th FLOOR, LUMPINI TOWER BUILDING,
RAMA IV RD., THUNGMAHAMEK, SATHORN, BANGKOK 10120, THAILAND
TEL : 0-2679-9079-84
FAX : 0-2679-9085 E-mail: mitr_dd@mitr.com

Architect :	SIGNATURE
ประกิต พนานุรัตน์ วสถ. 580 ที่อยู่ 251/1 ถ.จารุเมือง แขวงรองเมือง เขตปทุมวัน กรุงเทพมหานคร โทรศัพท์ 02-286-8199	
Structural Engineer :	SIGNATURE
วิศวกรผู้ออกแบบโครงสร้าง	
ณัฐสม สงวนวงษ์ วย 1423 ที่อยู่ 2/1 ซ.รามคำแหง 150 ถ.รามคำแหง แขวง สะพานสูง เขต สะพานสูง กทม. 10240	
Structural Inspector :	SIGNATURE
วิศวกรผู้ตรวจสอบโครงสร้าง	
โกมล จุฑาภัทร วย 964 ที่อยู่ 24/18 ซ.นวมินทร์ 129 ถ. นวมินทร์ แขวง นวลจันทร์ เขต บึงกุ่ม กทม. 10230	
Electrical Engineer :	SIGNATURE
วิศวกรผู้ออกแบบระบบไฟฟ้ากำลัง	
นายสุภัทร บูรณวิทย์ วฟก.1265 ที่อยู่ 21 ซอยทานสัมฤทธิ์ 13 ตำบลท่าทราย อ.เมืองนนทบุรี จ.นนทบุรี 11000	
Mechanical Engineer :	SIGNATURE
วิศวกรผู้ออกแบบระบบเครื่องกลและปรับอากาศ	
นายประสิทธิ์ เกียวสุนทร วก.1221 ที่อยู่ 44/372 ซอยบางกระดี่ 35/1 แขวงแสมดำ เขตบางขุนเทียน กทม. 10150	ประสิทธิ์
Sanitary Engineer :	SIGNATURE
วิศวกรผู้ออกแบบระบบสุขาภิบาล และดับเพลิง	
นายทศวรรษ สันนฤทธิ์ วส. 215 ที่อยู่ บ้านเลขที่ 99/107 หมู่ที่ 3 ต.ศีรษะจรเข้น้อย อ.บางเสาธง จ.สมุทรปราการ 10540	ทศวรรษ

ISSUE/REVISION

REV.	DESCRIPTION	DATE
A	90% DEVELOPED	09/05/2026

PROJECT NAME :
GEDC 01

LOCATION:
Nikhom Phattana district, Rayong ,industrial estate,CPGC

BUILDING :
MAIN BUILDING

90% DEVELOPED

TITLE :
EXTERNAL WALL DETAILS B

JOB NO.	SCALE 1:50
DRAWN FLY	REF.
CHECKED LJC	DWG.NO. MPK01A-90-A-EW-002
APPROVED LXD	
DATE 2026.05.09	

NOTE : THIS PRINT IS OF A CONFIDENTIAL NATURE, IT SHALL NOT BE TRACED,PHOTOGRAPHED,PHOTOSTATED OR REPRODUCED IN ANY MANER,NOR USED FOR ANY PURPOSE WHATSOEVER EXCEPT BY WRITTEN PERMISSION