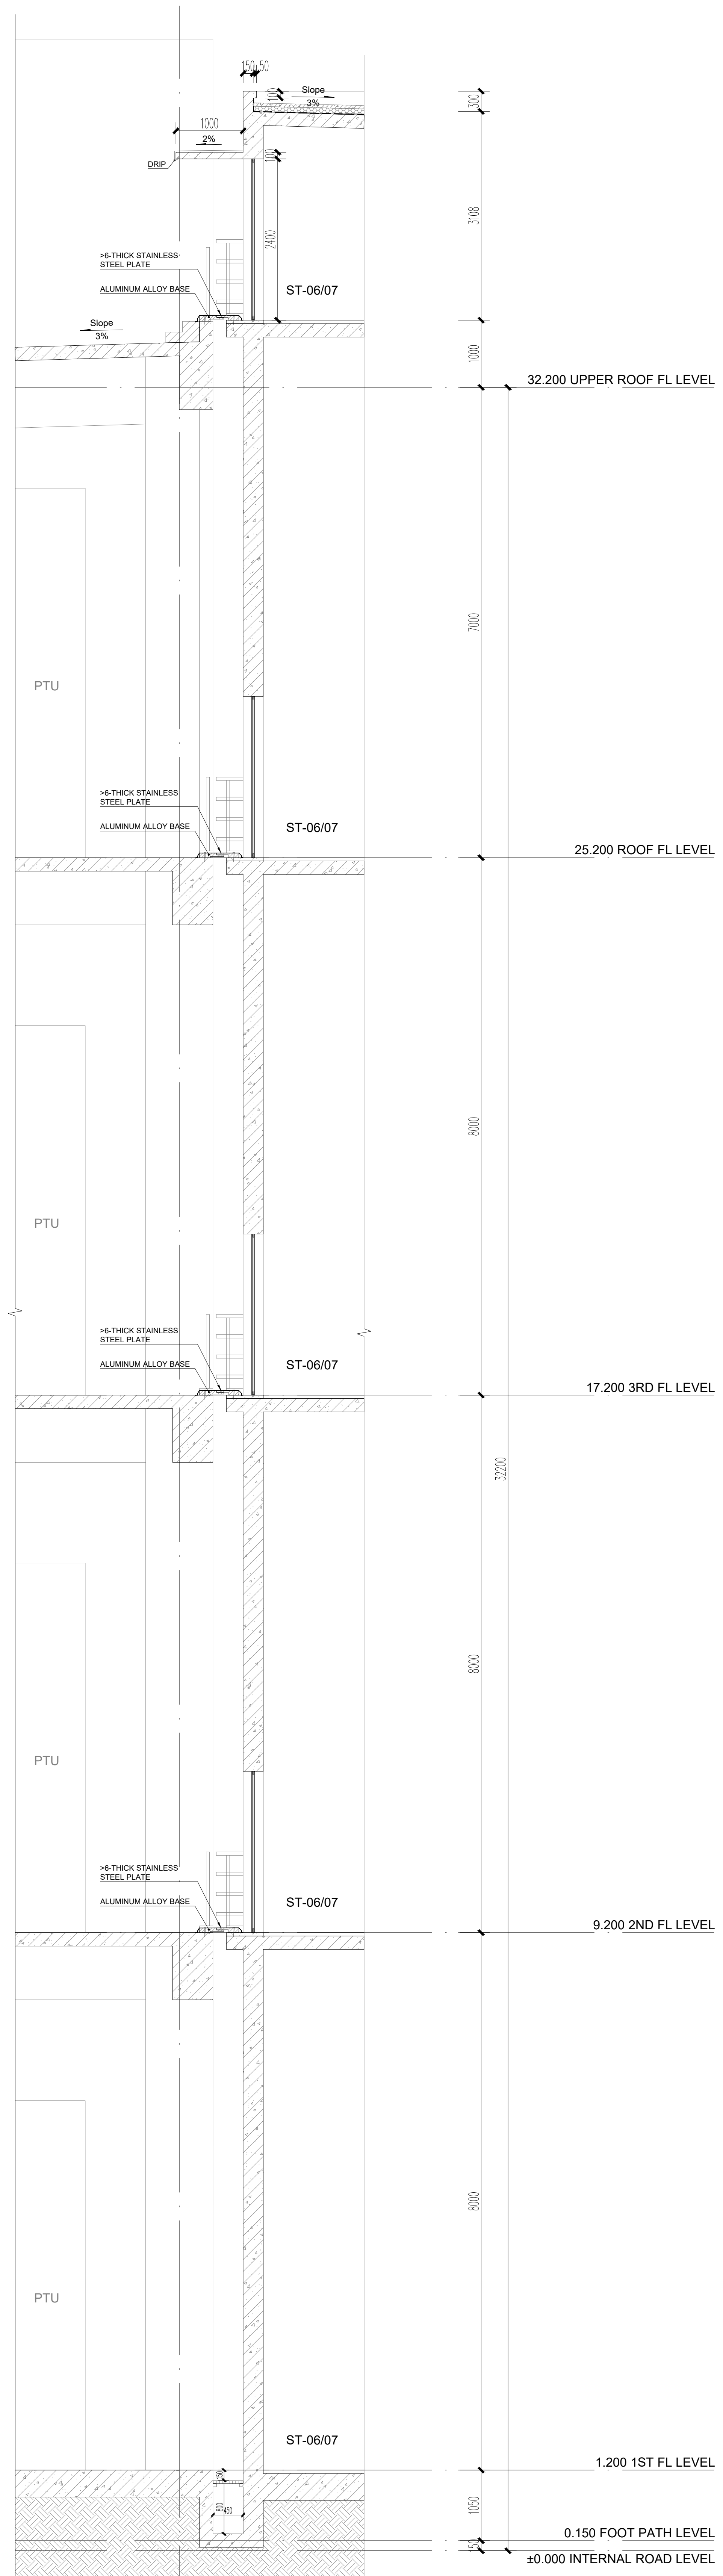

EXTERNAL WALL DETAIL 09

Scale 1:50

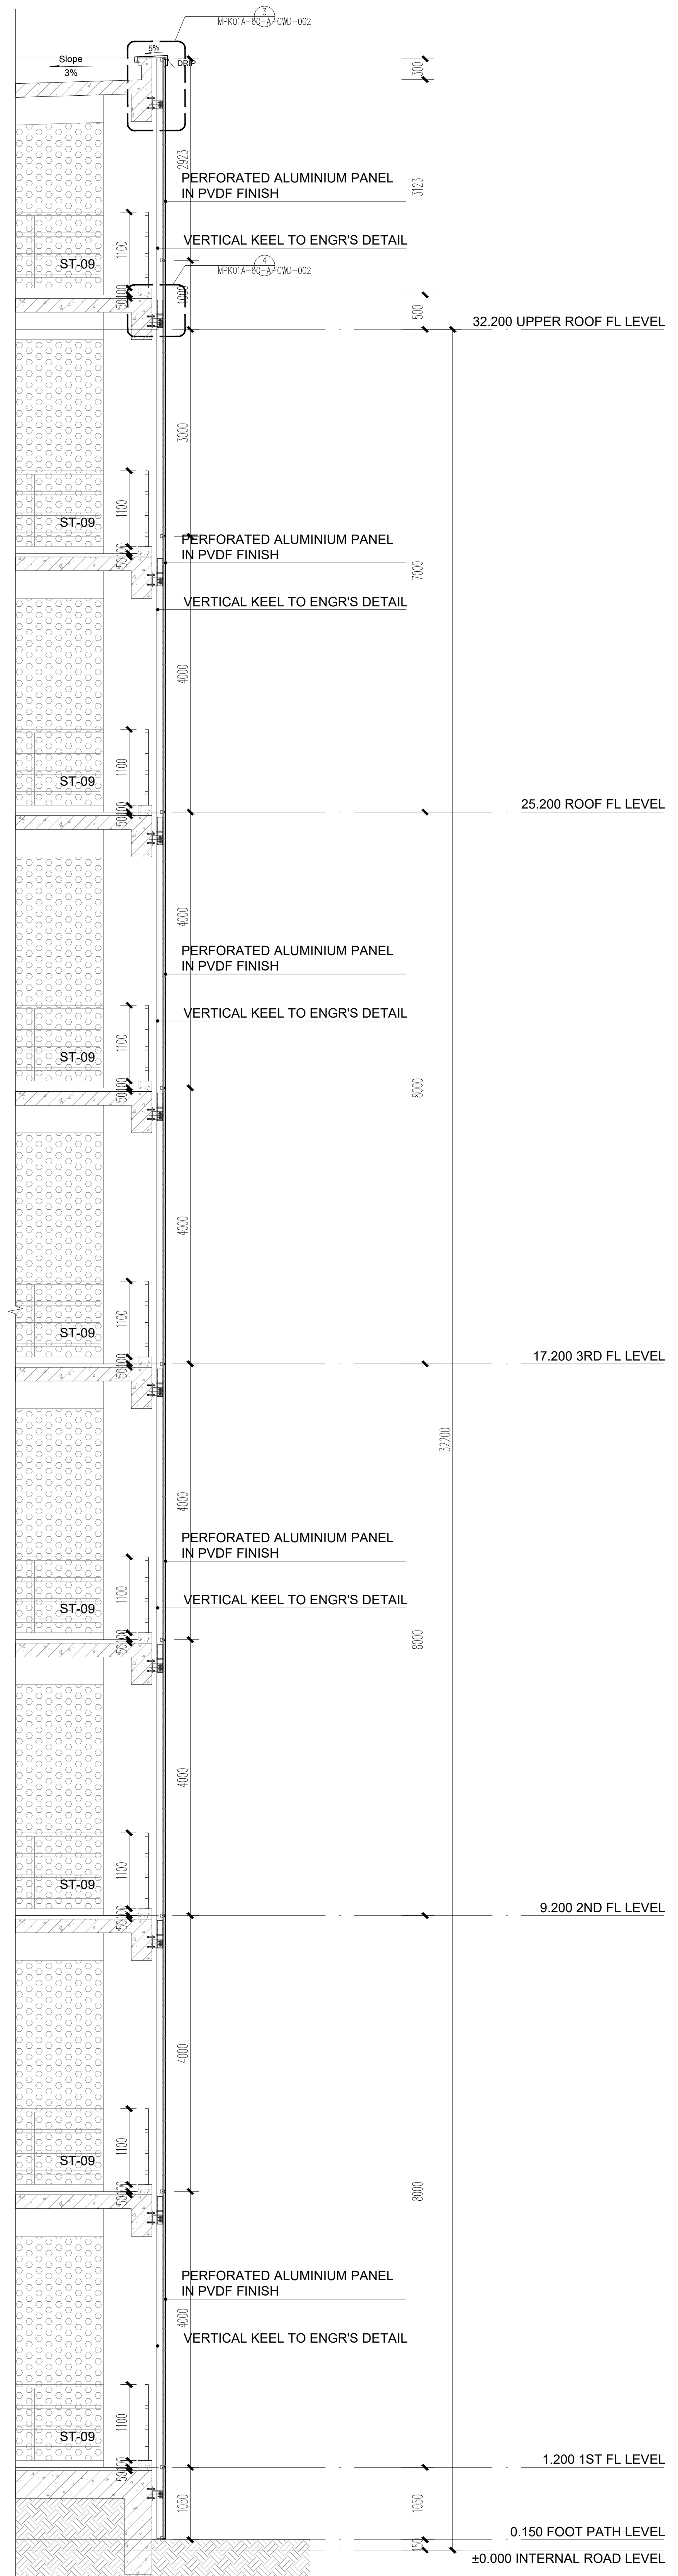

EXTERNAL WALL DETAIL 10

Scale 1:50

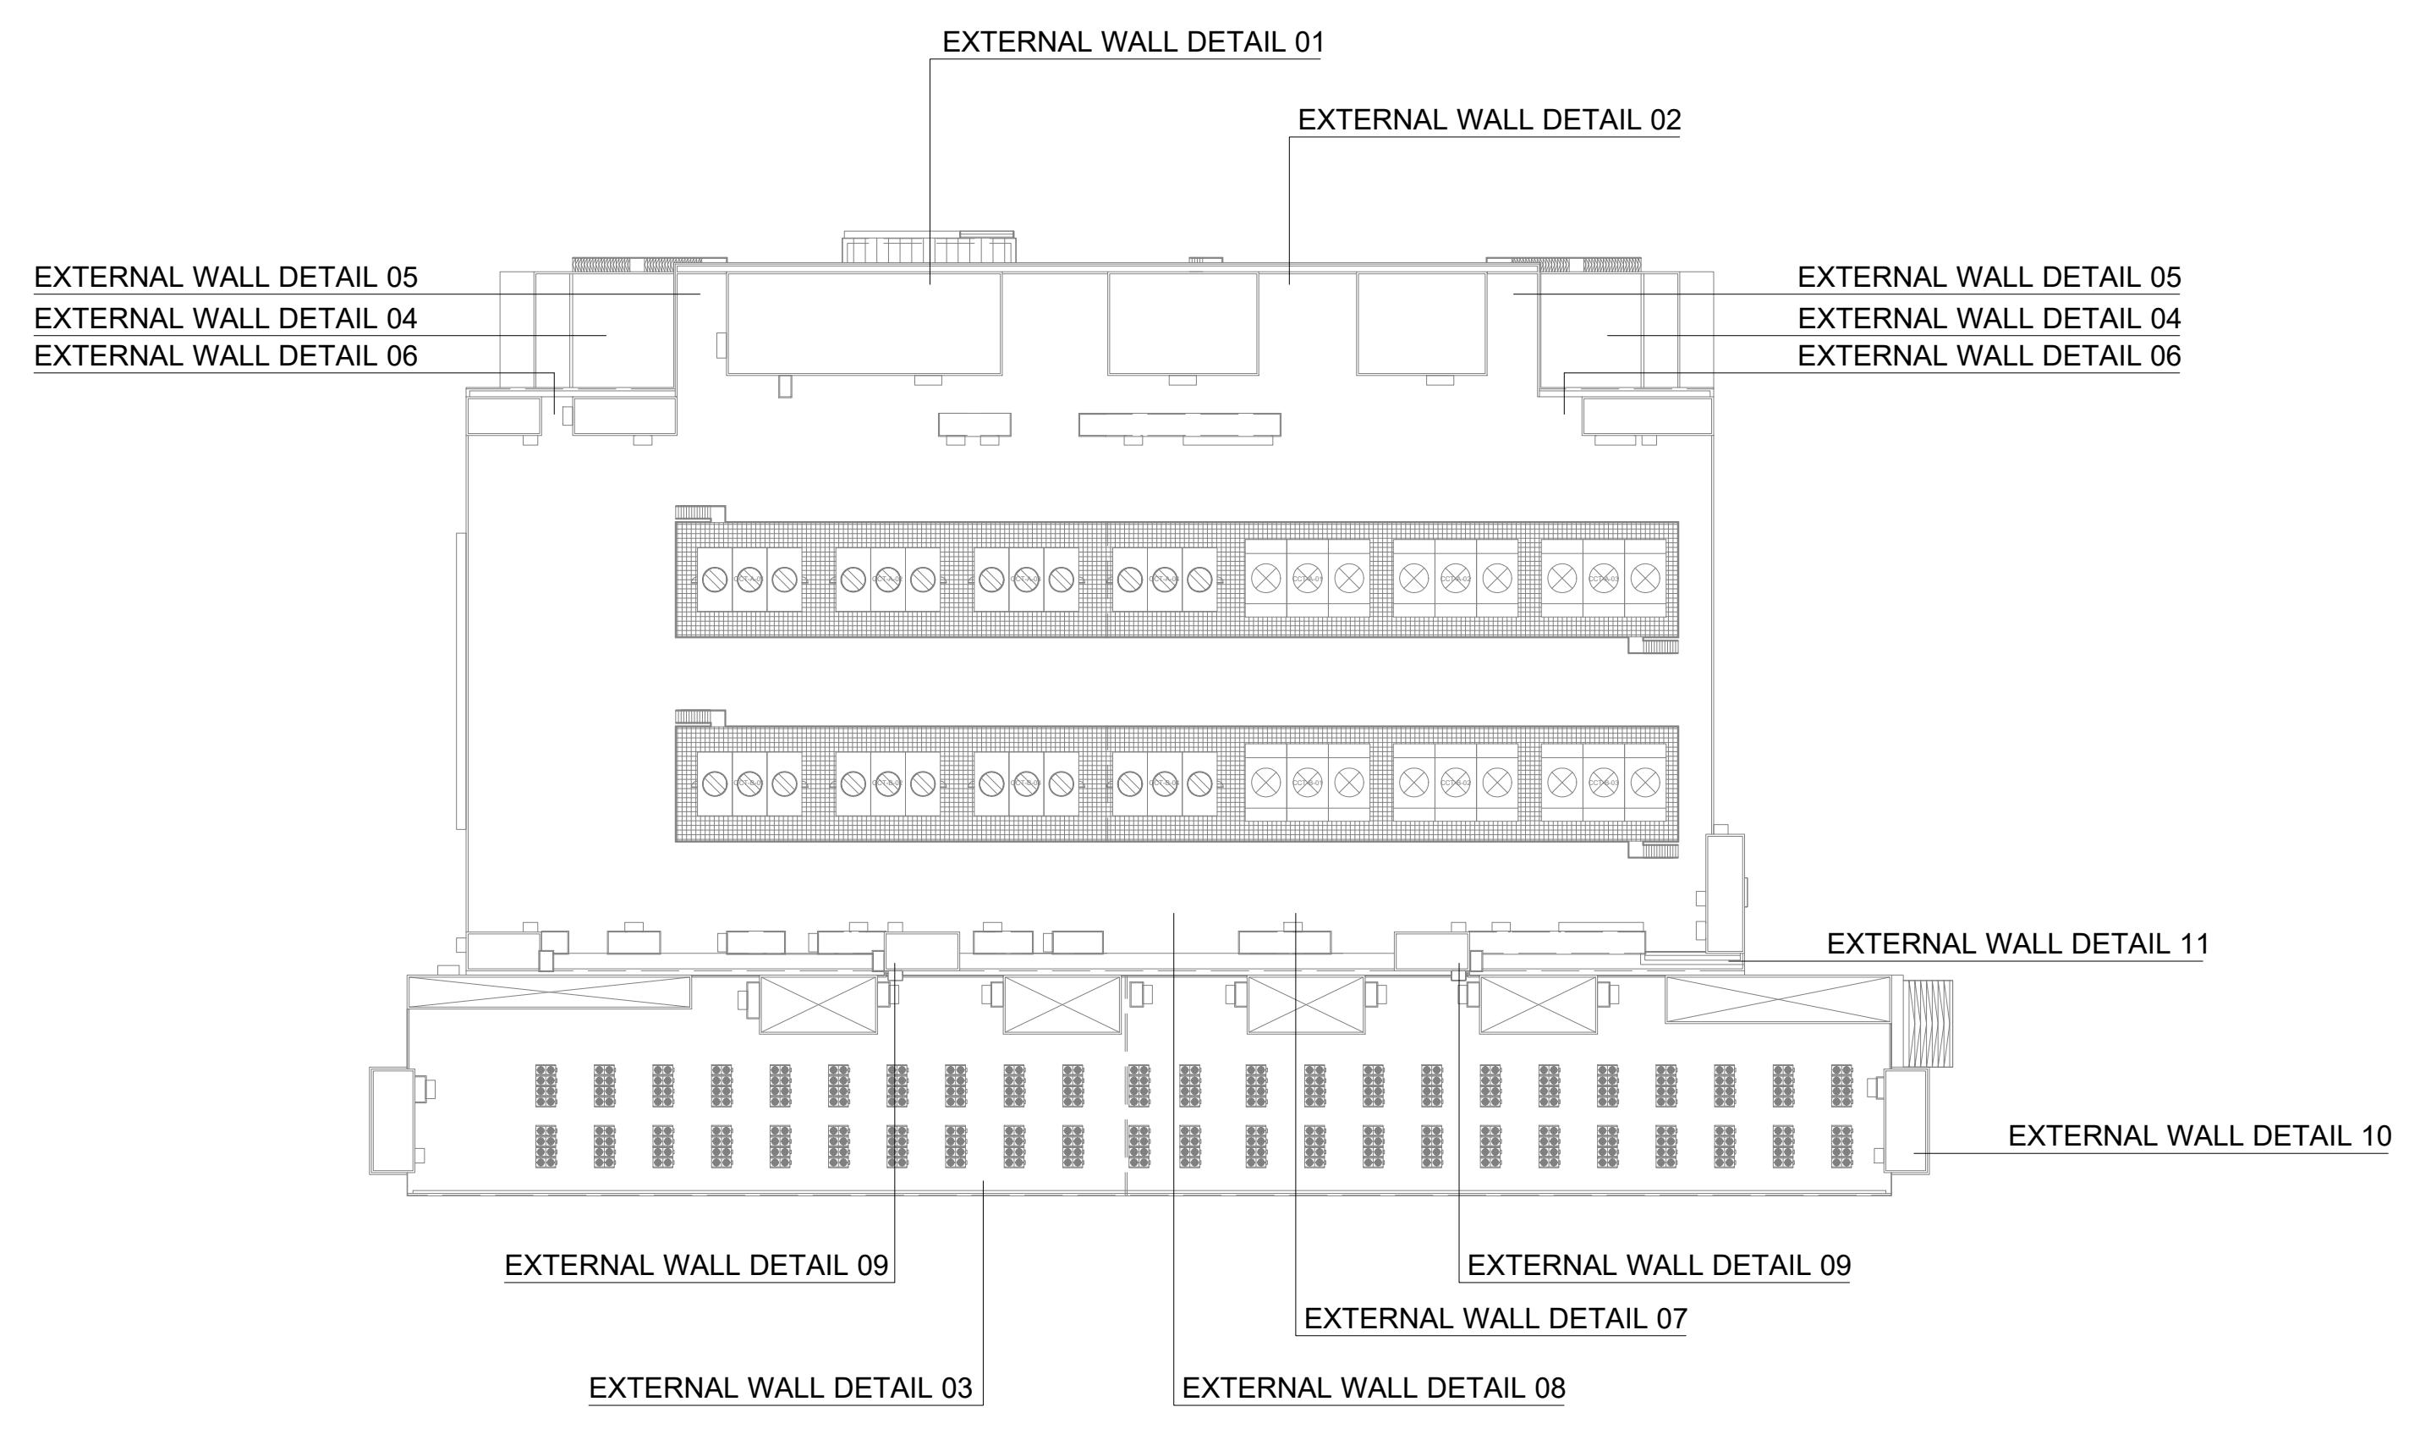

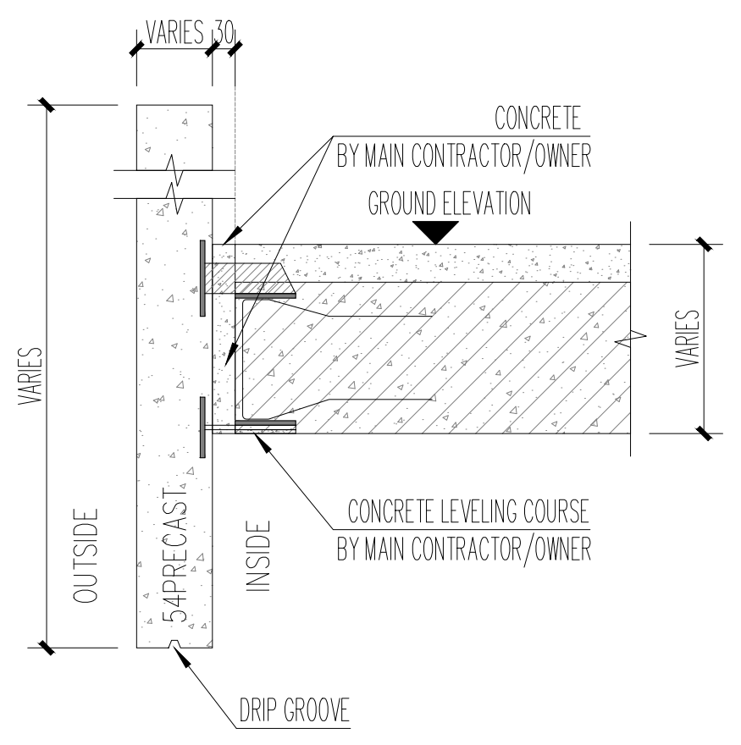
VARIES 30
CONCRETE BY MAIN CONTRACTOR/OWNER
GROUND ELEVATION
VARIES
VARIES
OUTSIDE
54PRECAST
INSIDE
CONCRETE LEVELING COURSE BY MAIN CONTRACTOR/OWNER
DRIP GROOVE

DETAIL 01

-PRECAST WALL PANEL AND FLOOR SLAB CONNECTION

Scale 1:10

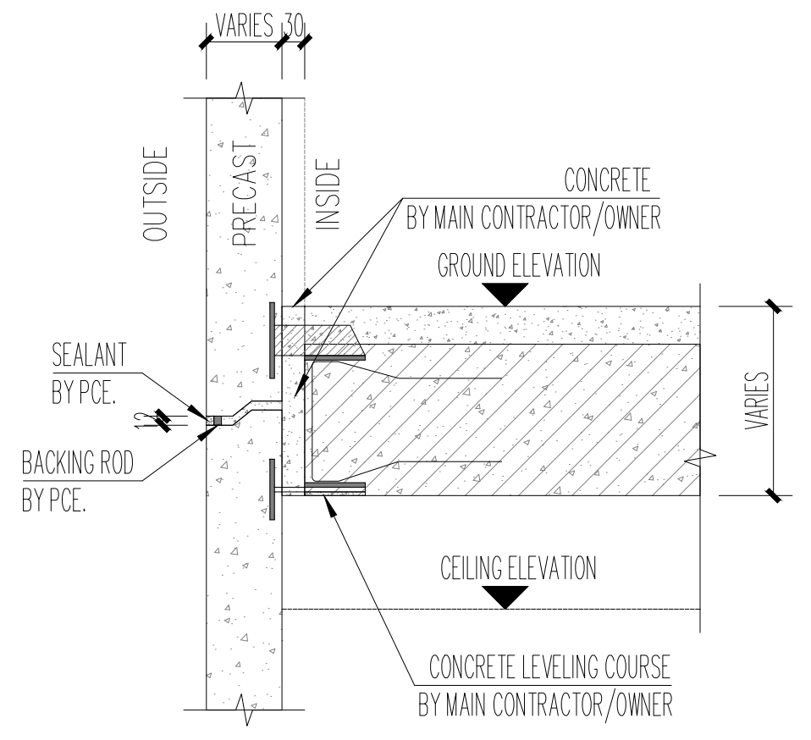

DETAIL 02

-PRECAST WALL PANEL JOINT AND FLOOR CONNECTION

Scale 1:10

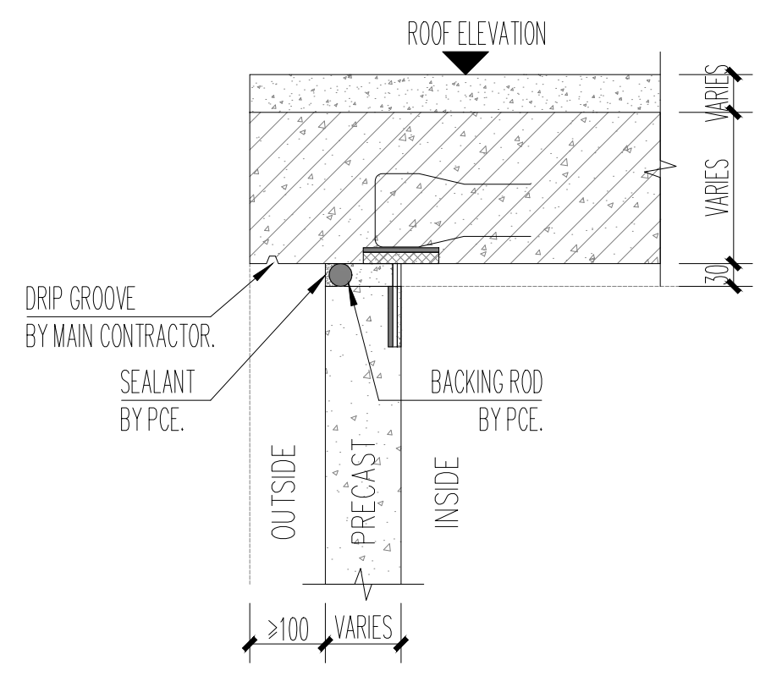

DETAIL 03

-PRECAST WALL PANEL AND ROOF SLAB CONNECTION

Scale 1:10

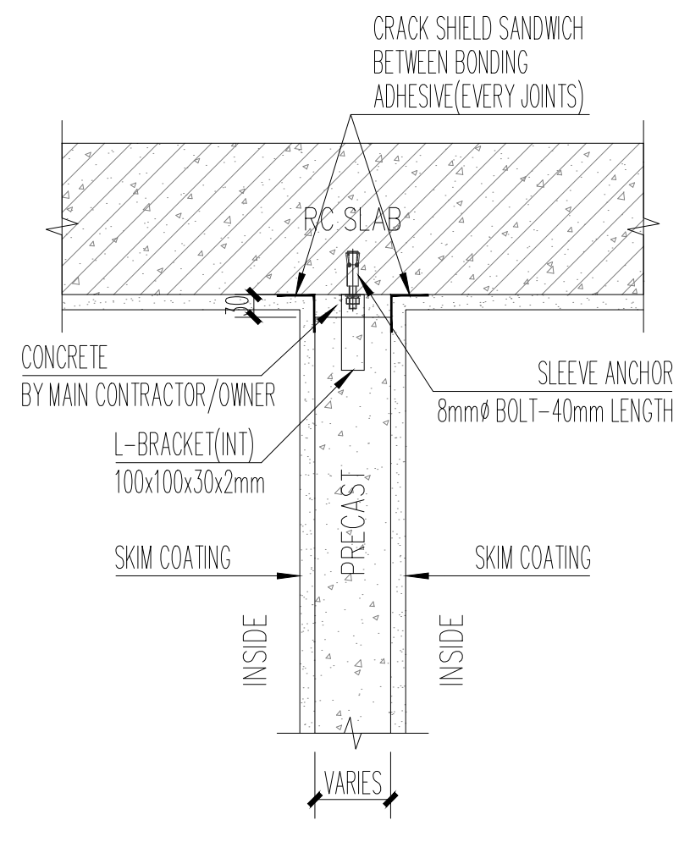
CRACK SHIELD SANDWICH BETWEEN BONDING ADHESIVE(EVERY JOINTS)
RC SLAB
30
CONCRETE BY MAIN CONTRACTOR/OWNER
SLEEVE ANCHOR 8mmø BOLT-40mm LENGTH
L-BRACKET(INT) 100x100x30x2mm
SKIM COATING
SKIM COATING
PRECAST
INSIDE
INSIDE
VARIES

DETAIL 04

-PRECAST INTERIOR WALL PANEL TO TOP SLAB CONNECTION

Scale 1:10

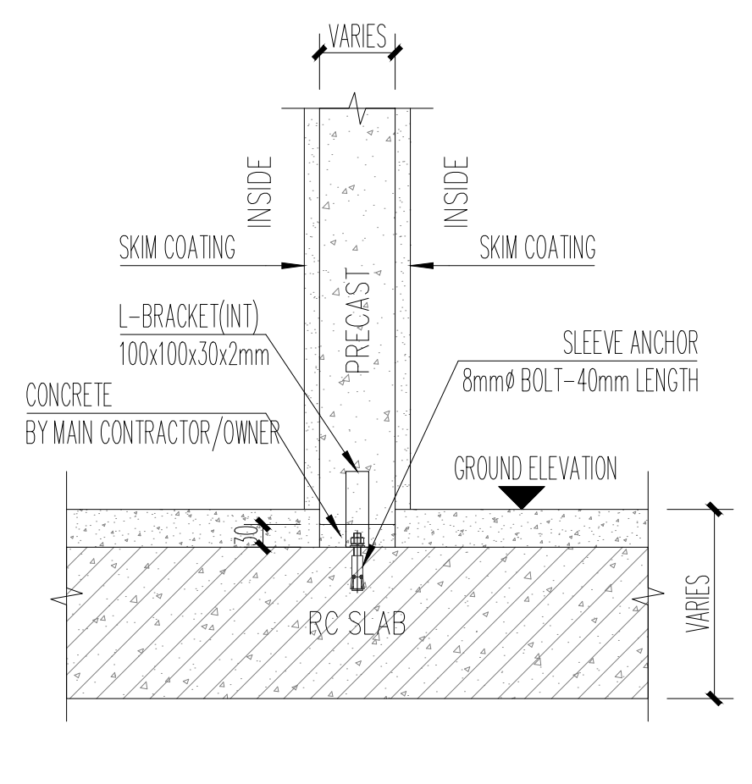
VARIES
INSIDE
INSIDE
SKIM COATING
SKIM COATING
PRECAST
L-BRACKET(INT) 100x100x30x2mm
SLEEVE ANCHOR 8mmø BOLT-40mm LENGTH
CONCRETE BY MAIN CONTRACTOR/OWNER
GROUND ELEVATION
30
RC SLAB
VARIES

DETAIL 05

-PRECAST INTERIOR WALL PANEL AND SLAB CONNECTION

Scale 1:10

NOTE : THIS PRINT IS OF A CONFIDENTIAL NATURE, IT SHALL NOT BE TRACED,PHOTOGRAPHED,PHOTOSTATED OR REPRODUCED IN ANY MANER,NOR USED FOR ANY PURPOSE WHATSOEVER EXCEPT BY WRITTEN PERMISSION

CLIENT :

GULF EDGE DC 01

87 Wireless Road, M Thai Tower 11th. Floor, All Seasons Place, Lumpini,
Pathumwan, Bangkok 10330, Thailand

CONTRACTOR :

华西发展(泰国)有限公司
บริษัท หัวซือ ดีเวลลอปเม้นต์ (ประเทศไทย) จำกัด
HUASHI DEVELOPMENT CO.,LTD
No. 202, Room No. 1403, 14/F, Le Concorde Building,
Ratchadapisek Road, Huaykhwang Sub-District,
Huaykhwang District, Bangkok Metropolitan 10310.

CONSULTANT :

ARbay
บริษัท เอ อาร์ เบย์ จำกัด
ARbay Company Limited
31 st Floor Bangkok Insurance Building
25 South Sathorn road Thungmahamek
Sathorn Bangkok 10120 THAILAND
T +66 (0) 2286 8199
F +66 (0) 2286 2863
info@arbay.co.th

CONSULTANT :

Qbic Engineers & Architects Co.,Ltd.
8 Soi KALONG 4 SANAMBINNAM ROAD,
THASAI SUB-DISTRICT, MUANG NONTHABURI DISTRICT
, NONTHABURI.
Tel 662-950-4374
Fax 662-580-3231
E-Mail : qbic@qbic.co.th, www.qbic.co.th
QBIC ENGINEERS AND ARCHITECTS CO.,LTD.

CONSULTANT :

MITR
MITR TECHNICAL CONSULTANT CO.,LTD.
1168/8 12th FLOOR, LUMPINI TOWER BUILDING,
RAMA IV RD., THUNGMAHAMEK, SATHORN, BANGKOK 10120, THAILAND
TEL : 0-2679-9079-84
FAX : 0-2679-9085 E-mail: mitr_dd@mitr.com

Architect : SIGNATURE
ประกิต พนานุรัตน์ วสถ. 580
ที่อยู่
251/1 ถ.จารุเมือง แขวงรองเมือง เขตปทุมวัน
กรุงเทพมหานคร โทรศัพท์ 02-286-8199

Structural Engineer : SIGNATURE
วิศวกรผู้ออกแบบโครงสร้าง
ณัฐสม สงวนวงษ์ วย 1423
ที่อยู่
2/1 ซ.รามคำแหง 150 ถ.รามคำแหง
แขวง สะพานสูง เขต สะพานสูง กทม. 10240

Structural Inspector : SIGNATURE
วิศวกรผู้ตรวจสอบโครงสร้าง
โกมล จุฑาภัทร วย 964
ที่อยู่
24/18 ซ.นวมินทร์ 129 ถ. นวมินทร์
แขวง นวลจันทร์ เขต บึงกุ่ม กทม. 10230

Electrical Engineer : SIGNATURE
วิศวกรผู้ออกแบบระบบไฟฟ้ากำลัง
นายสุภัทร บูรณวิทย์ วฟก.1265
ที่อยู่
21 ซอยทานสัมฤทธิ์ 13
ตำบลท่าทราย อ.เมืองนนทบุรี จ.นนทบุรี 11000

Mechanical Engineer : SIGNATURE
วิศวกรผู้ออกแบบระบบเครื่องกลและปรับอากาศ
นายประสิทธิ์ โกยวสุนทร วก.1221 ประสิทธิ์
ที่อยู่
44/372 ซอยบางกระดี่ 35/1 แขวงแสมดำ
เขตบางขุนเทียน กทม. 10150

Sanitary Engineer : SIGNATURE
วิศวกรผู้ออกแบบระบบสุขาภิบาล และดับเพลิง
นายทศวรรษ สันนฤทธิ์ วส. 215 ทศวรรษ
ที่อยู่
บ้านเลขที่ 99/107 หมู่ที่ 3 ต.ศีรษะจรเข้น้อย
อ.บางเสาธง จ.สมุทรปราการ 10540

ISSUE/REVISION

REV.	DESCRIPTION	DATE
A	90% DEVELOPED	09/05/2026

PROJECT NAME :

GEDC 01

LOCATION:
Nikhom Phattana district, Rayong ,industrial estate,CPGC

BUILDING :
MAIN BUILDING

90% DEVELOPED

TITLE :

EXTERNAL WALL DETAILS C

JOB NO.
SCALE 1:50
DRAWN FLY
REF.
CHECKED LJC
DWG.NO. MPK01A-90-A-EW-003
APPROVED LXD
DATE 2026.05.09