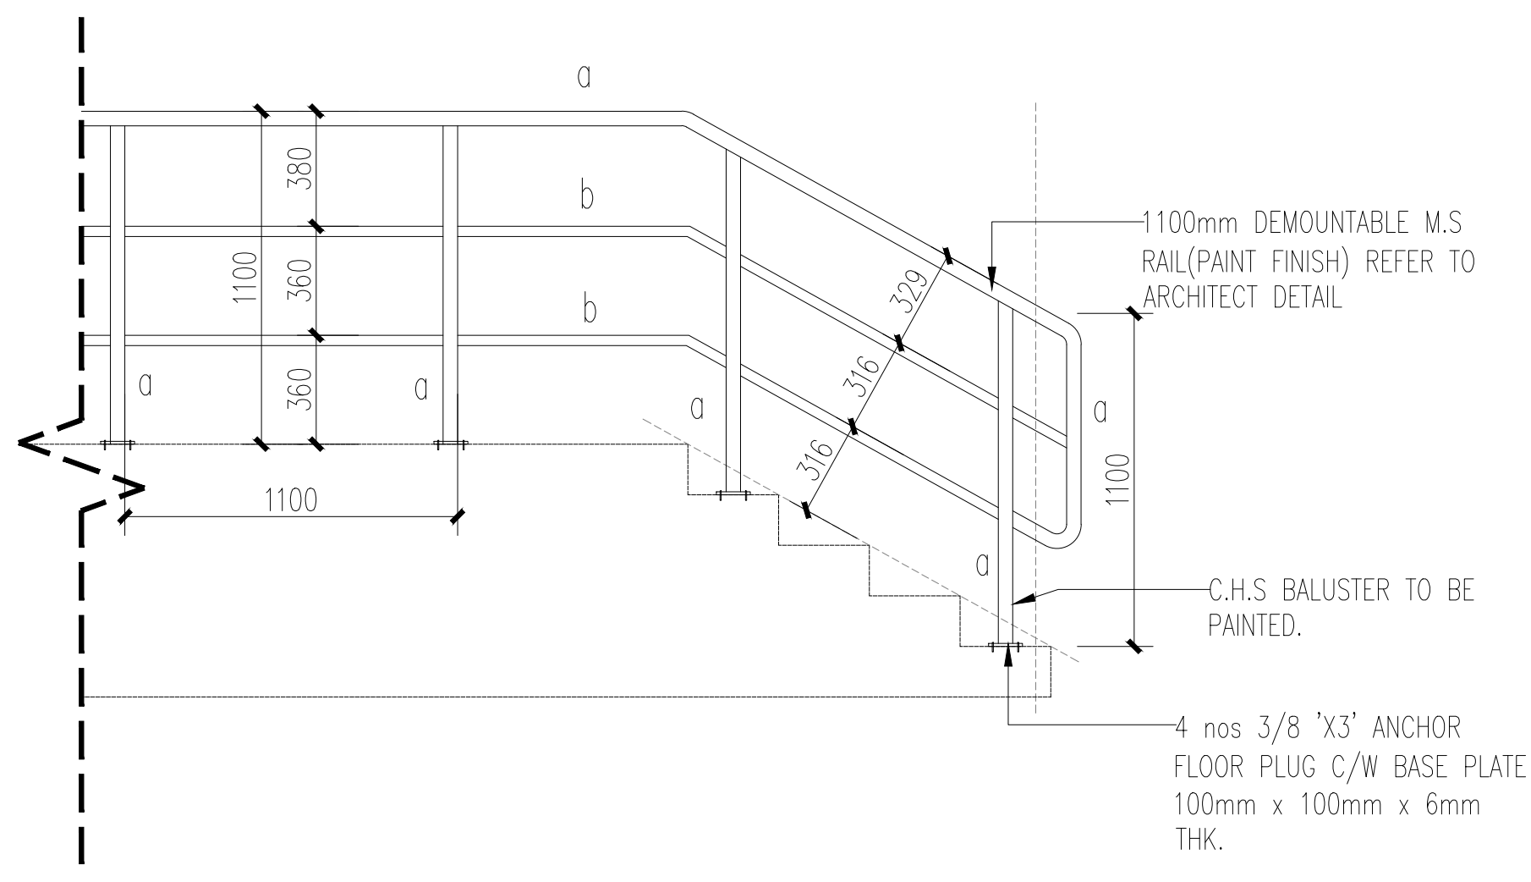
a
b
b
a
a
a
a
a
380
360
360
1100
1100
1100
329
316
316
1100mm DEMOUNTABLE M.S RAIL(PAINT FINISH) REFER TO ARCHITECT DETAIL
C.H.S BALUSTER TO BE PAINTED.
4 nos 3/8 'X3' ANCHOR FLOOR PLUG C/W BASE PLATE 100mm x 100mm x 6mm THK.

TYPICAL RAILING DETAIL
Scale 1:25

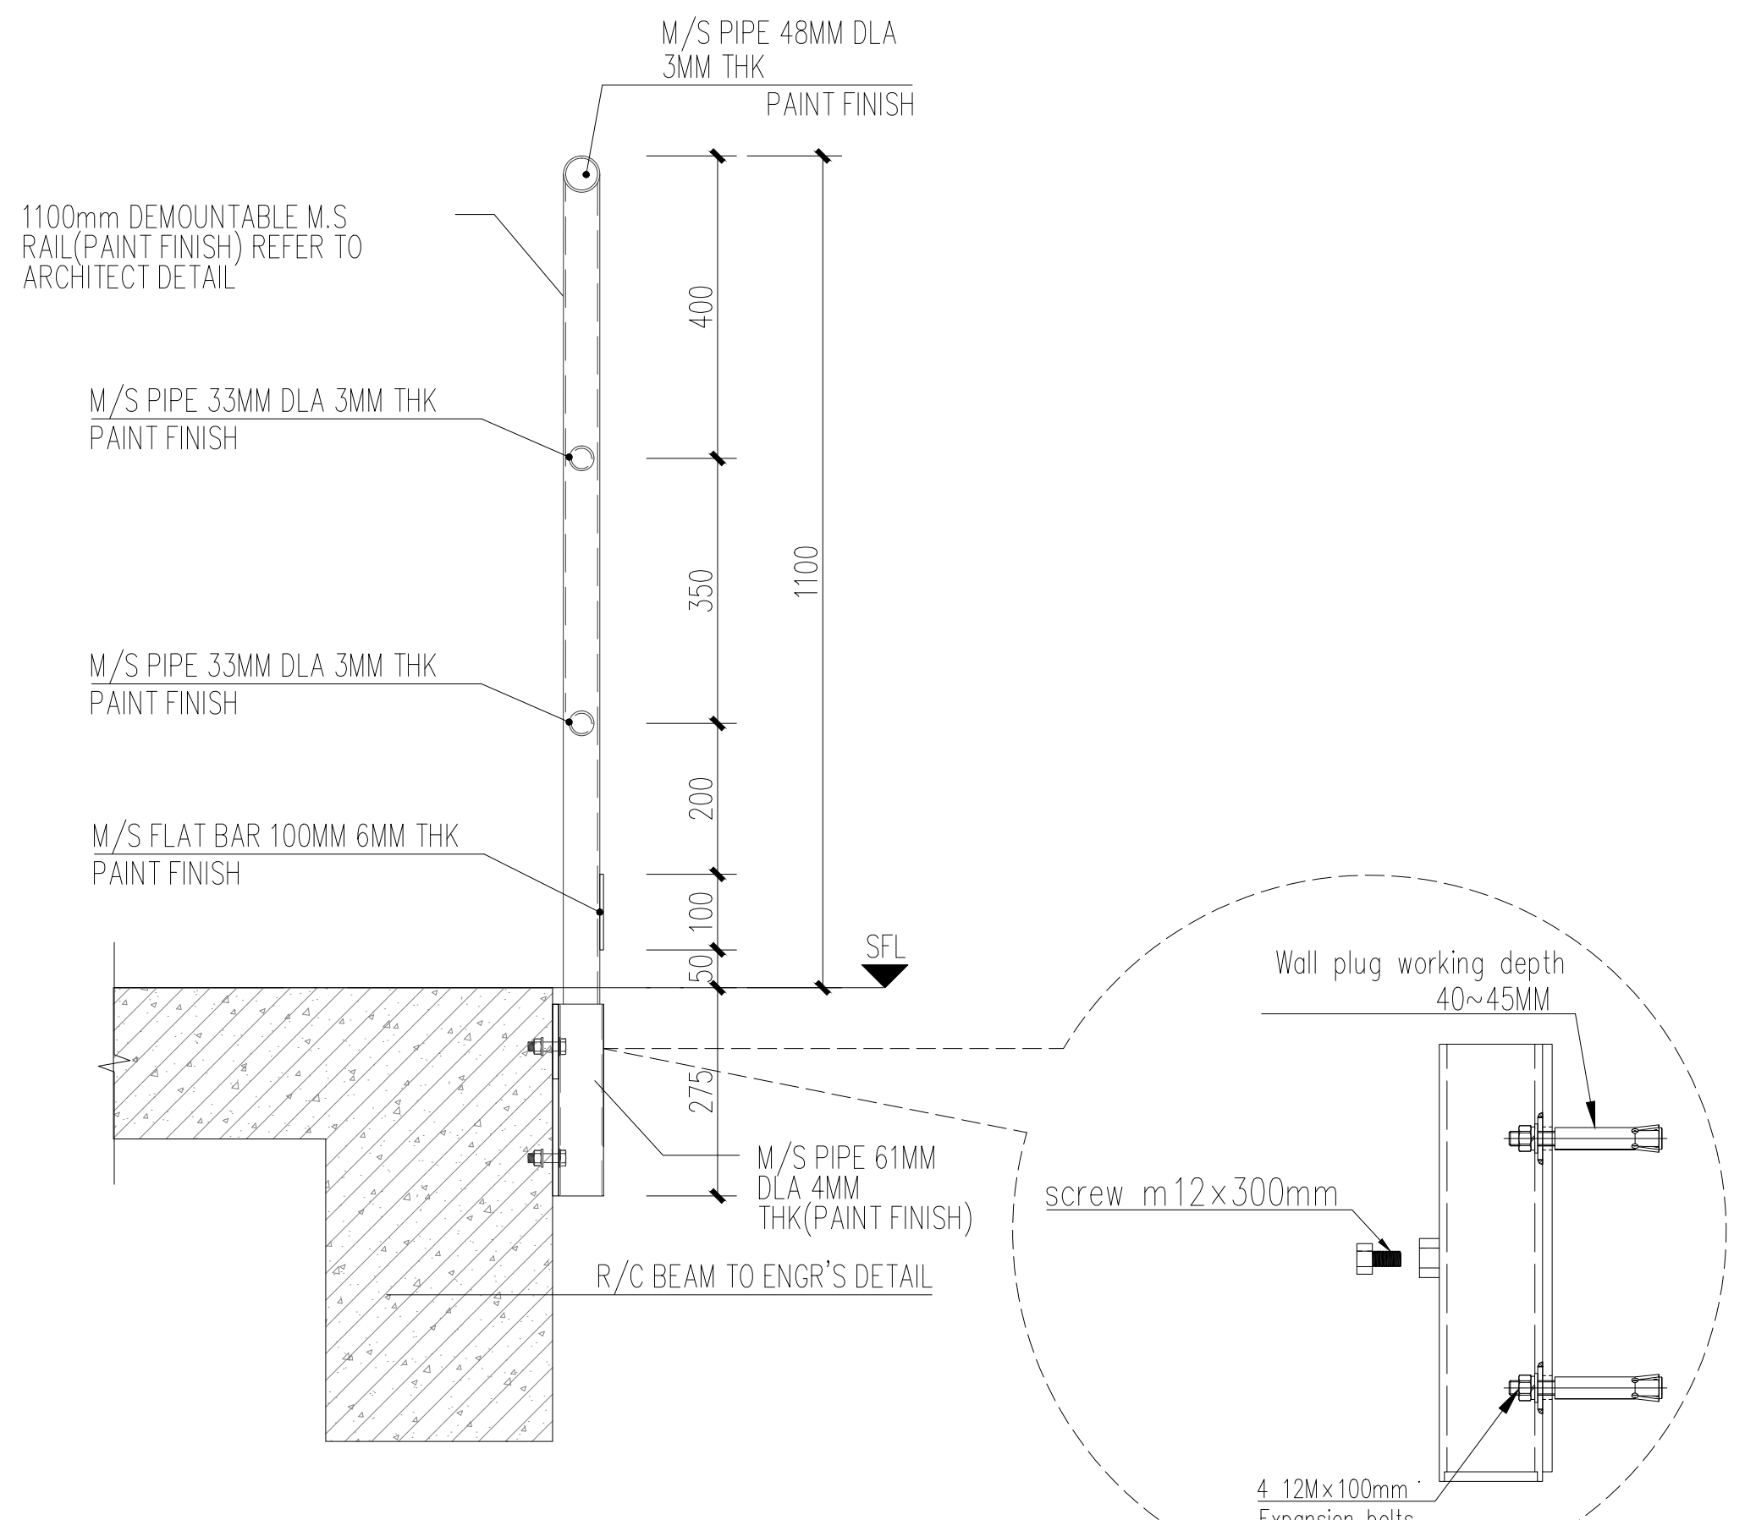
M/S PIPE 48MM DLA 3MM THK PAINT FINISH
1100mm DEMOUNTABLE M.S RAIL(PAINT FINISH) REFER TO ARCHITECT DETAIL
M/S PIPE 33MM DLA 3MM THK PAINT FINISH
M/S PIPE 33MM DLA 3MM THK PAINT FINISH
M/S FLAT BAR 100MM 6MM THK PAINT FINISH
400
350
200
100
50
275
1100
SFL
M/S PIPE 61MM DLA 4MM THK(PAINT FINISH)
R/C BEAM TO ENGR'S DETAIL
Wall plug working depth 40~45MM
screw m12×300mm
4 12M×100mm Expansion bolts

B-B
Scale 1:10

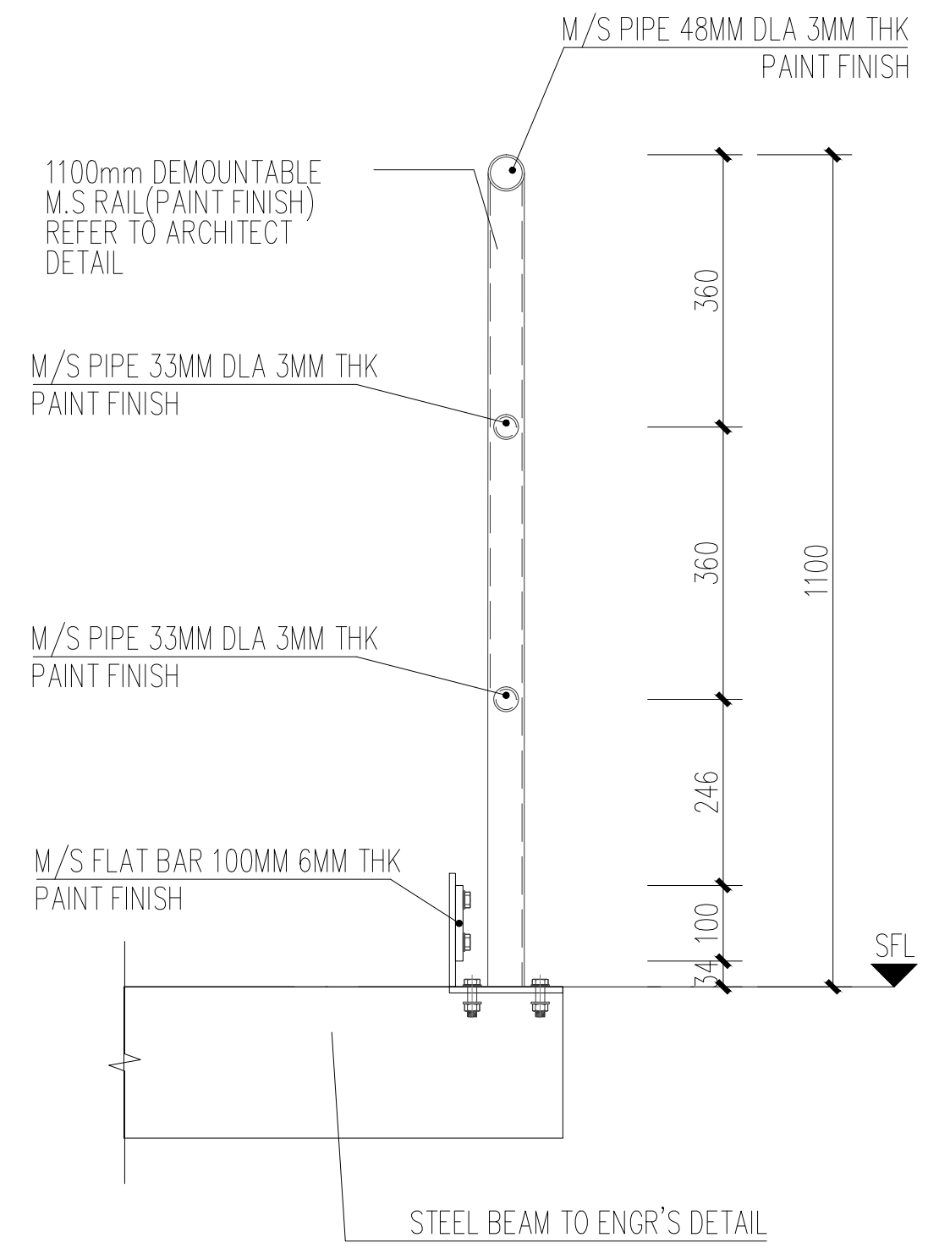
M/S PIPE 48MM DLA 3MM THK PAINT FINISH
1100mm DEMOUNTABLE M.S RAIL(PAINT FINISH) REFER TO ARCHITECT DETAIL
M/S PIPE 33MM DLA 3MM THK PAINT FINISH
M/S PIPE 33MM DLA 3MM THK PAINT FINISH
M/S FLAT BAR 100MM 6MM THK PAINT FINISH
360
360
246
100
34
1100
SFL
STEEL BEAM TO ENGR'S DETAIL

C-C
Scale 1:10

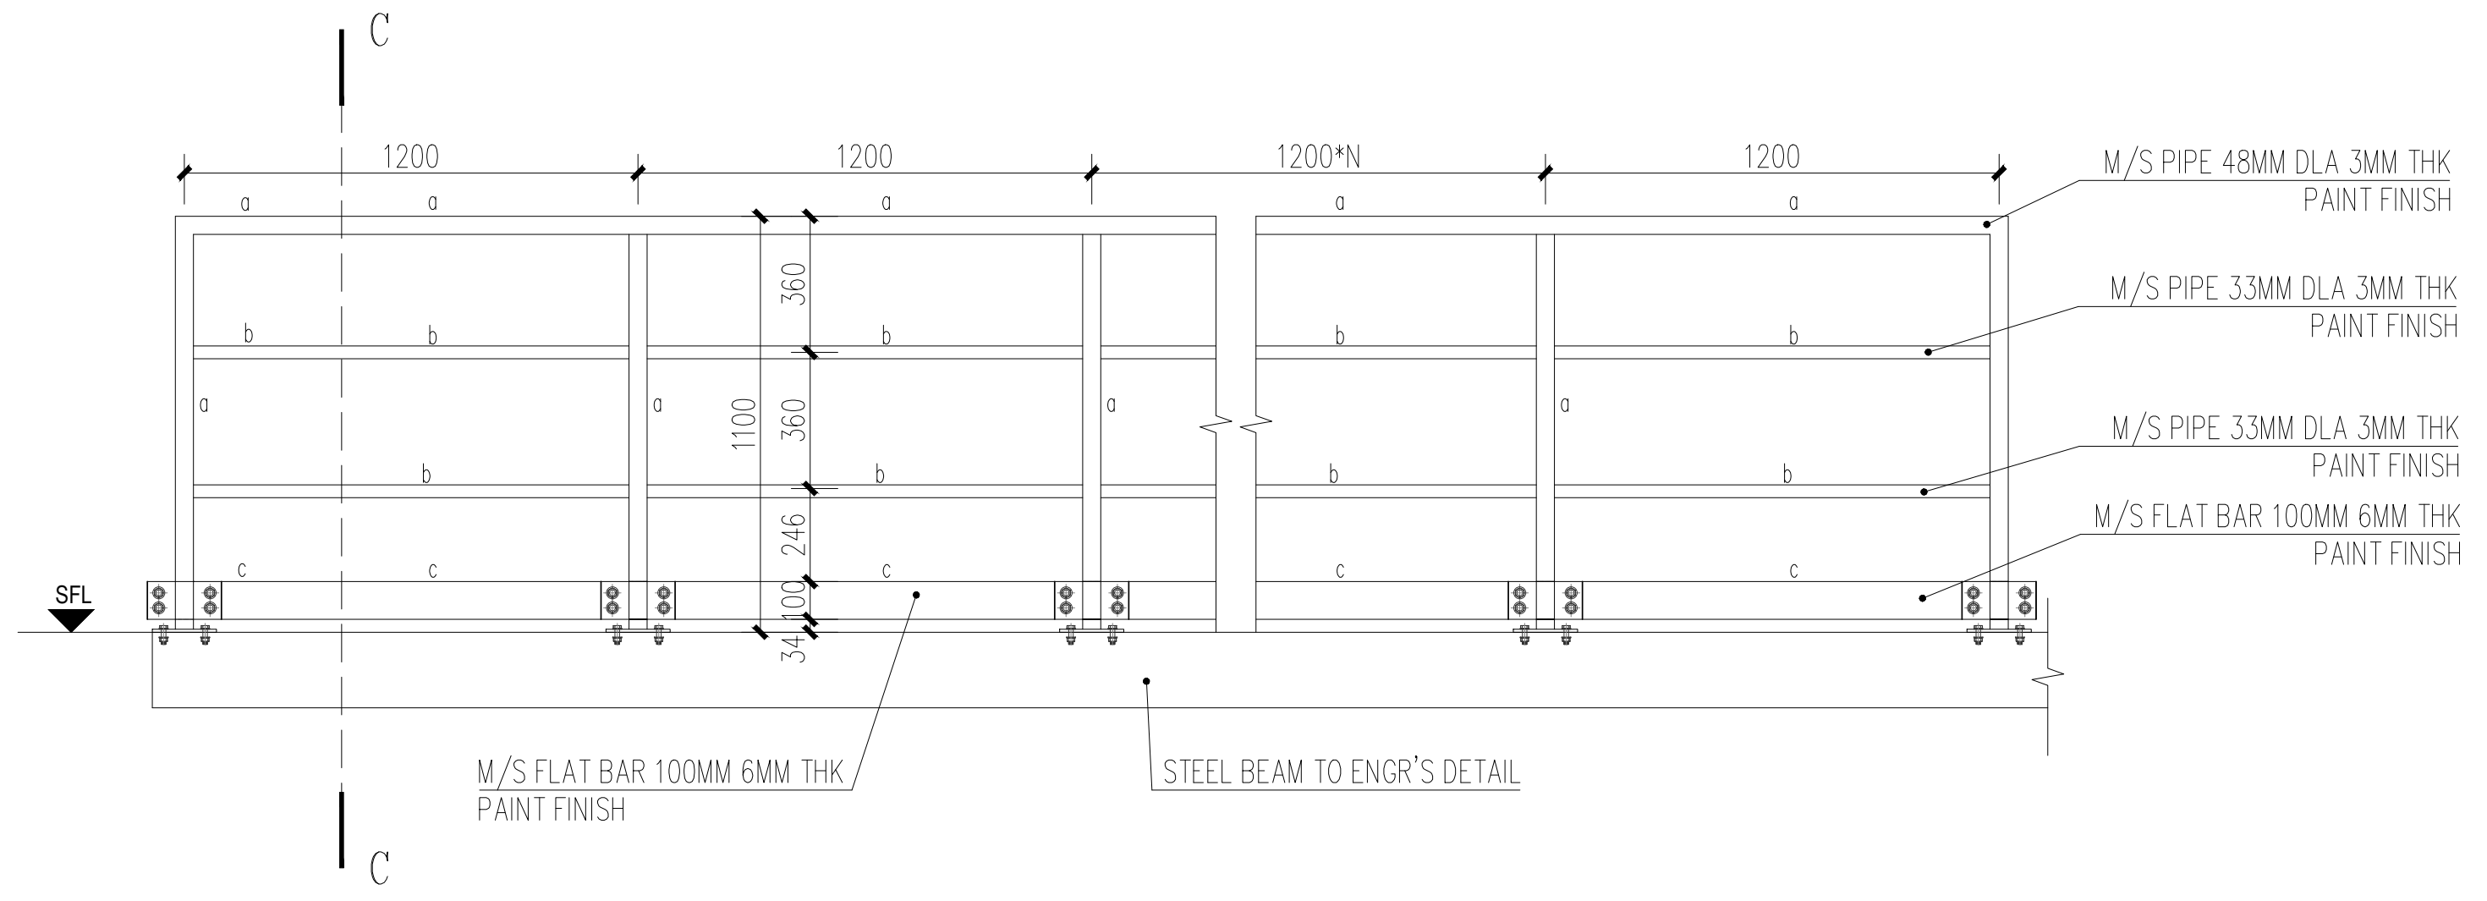
C
C
1200
1200
1200*N
1200
a
b
c
360
360
246
100
34
1100
SFL
M/S PIPE 48MM DLA 3MM THK PAINT FINISH
M/S PIPE 33MM DLA 3MM THK PAINT FINISH
M/S PIPE 33MM DLA 3MM THK PAINT FINISH
M/S FLAT BAR 100MM 6MM THK PAINT FINISH
M/S FLAT BAR 100MM 6MM THK PAINT FINISH
STEEL BEAM TO ENGR'S DETAIL

RAILING DETAIL
Scale 1:20

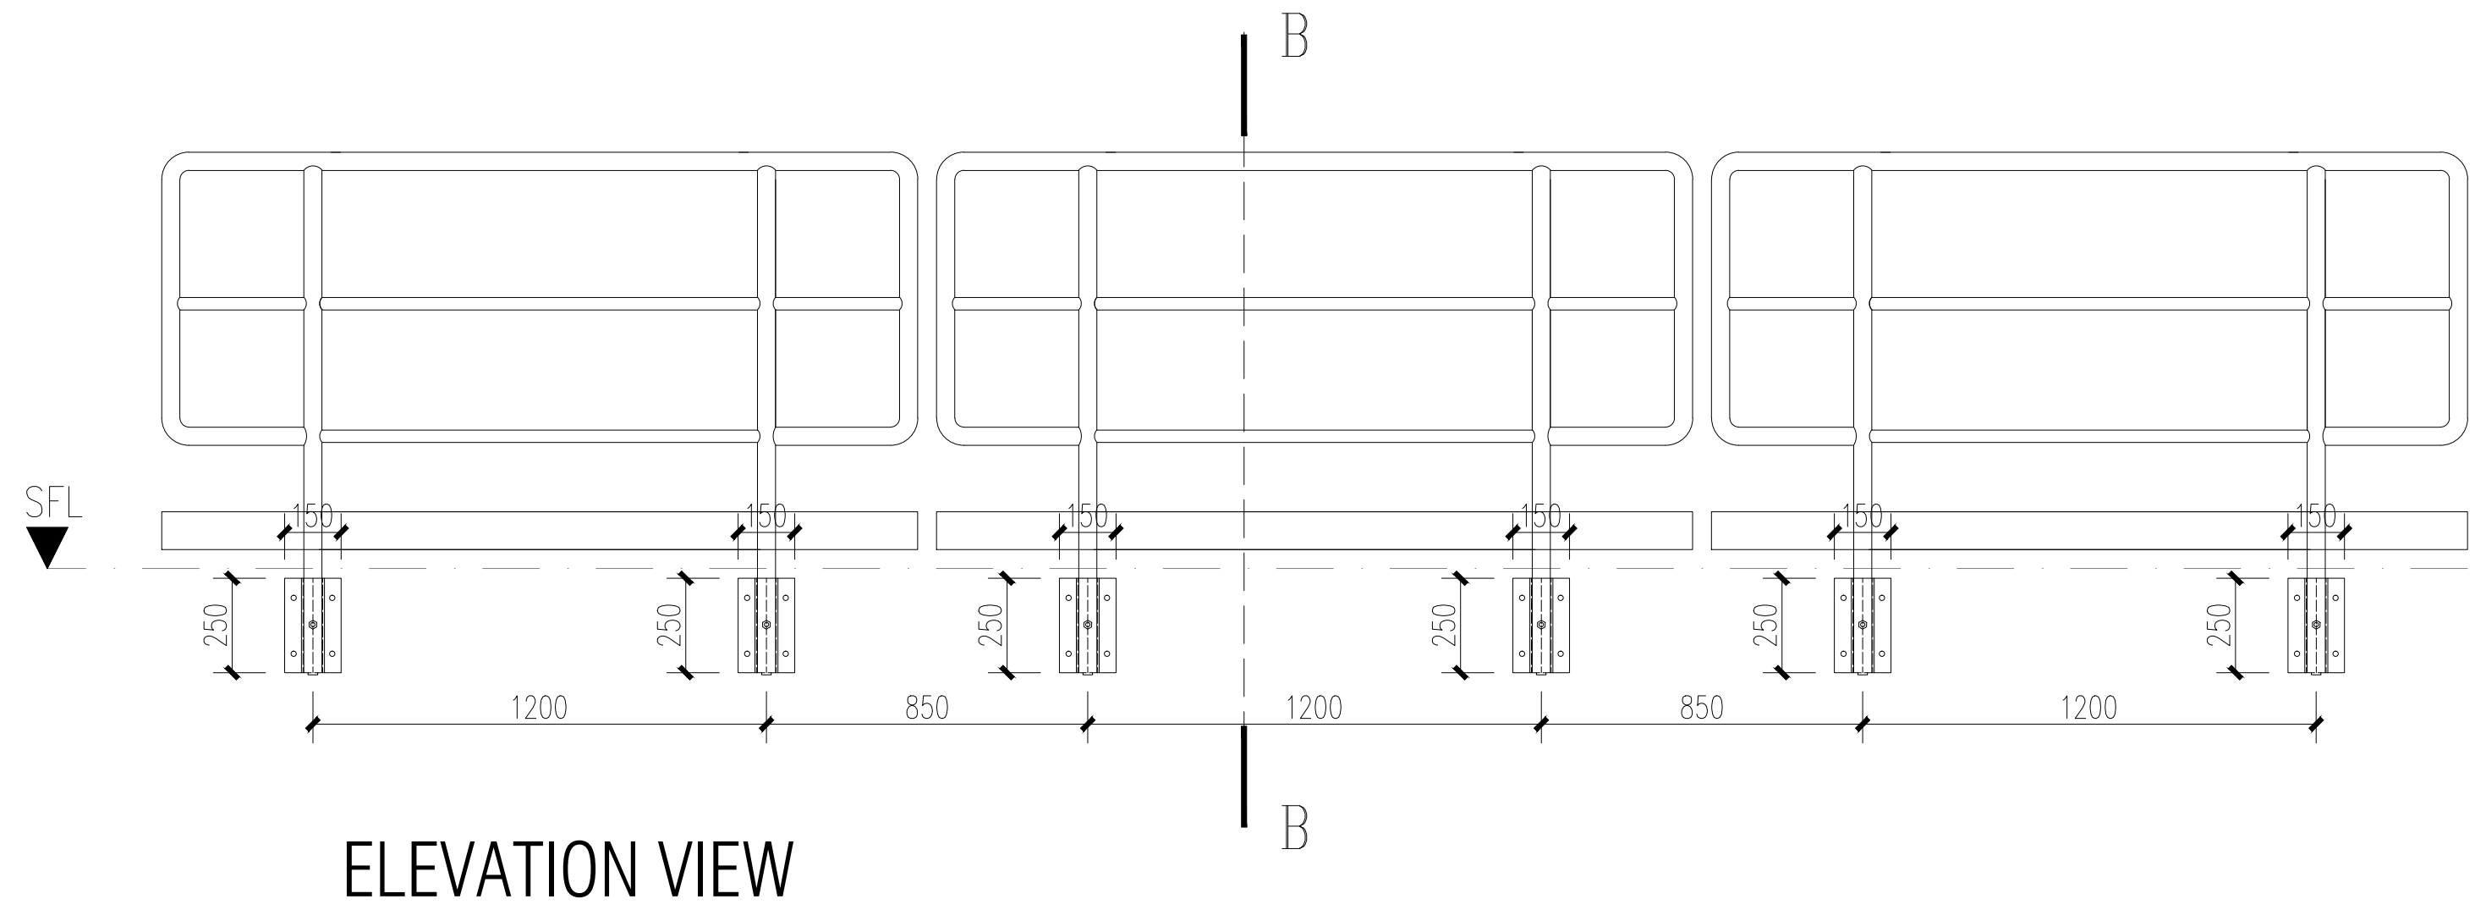
B
B
SFL
150
250
1200
850
1200
850
1200

ELEVATION VIEW
Scale 1:20

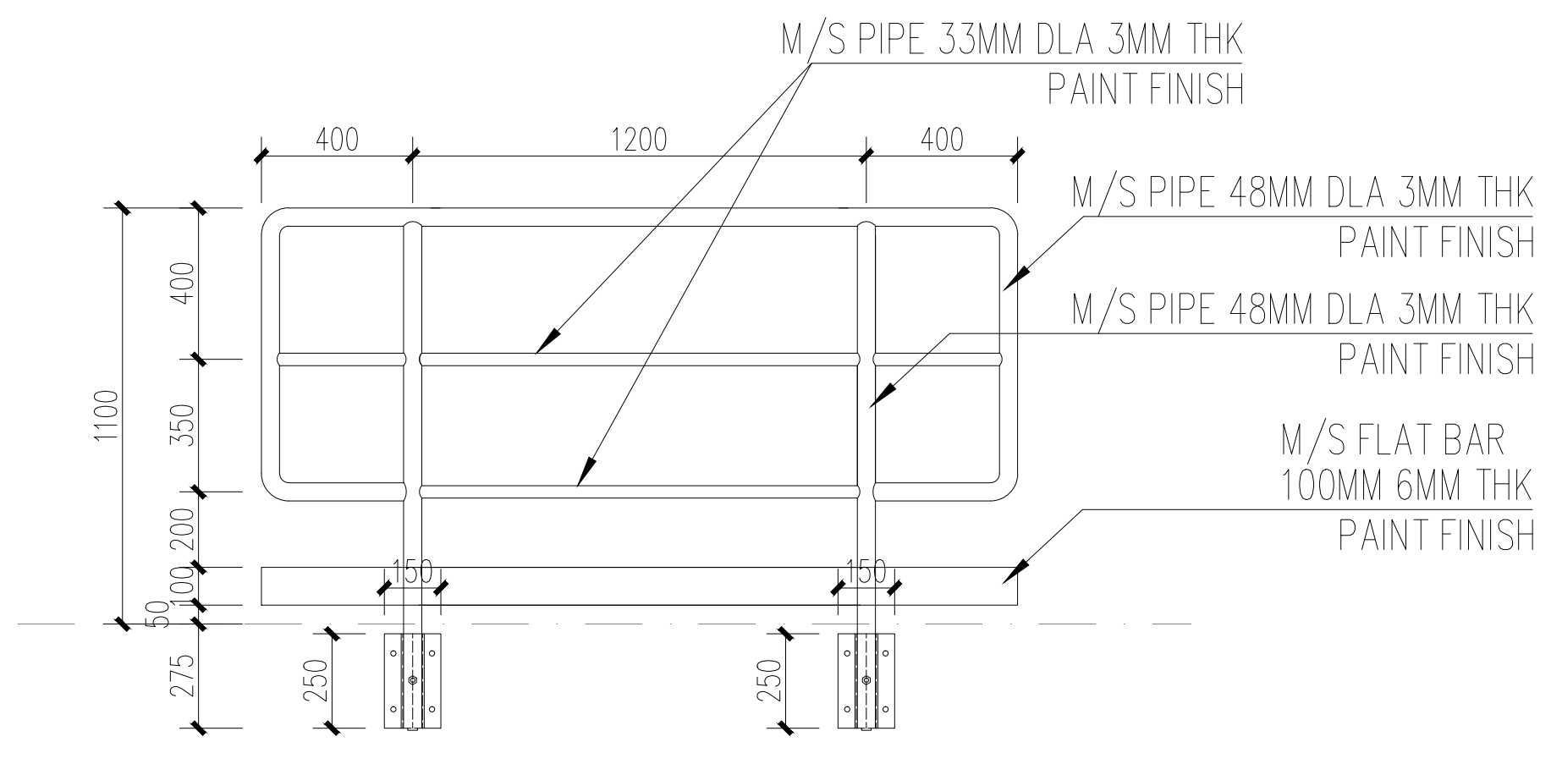
M/S PIPE 33MM DLA 3MM THK PAINT FINISH
400
1200
400
M/S PIPE 48MM DLA 3MM THK PAINT FINISH
M/S PIPE 48MM DLA 3MM THK PAINT FINISH
M/S FLAT BAR 100MM 6MM THK PAINT FINISH
1100
400
350
200
100
50
275
150
250

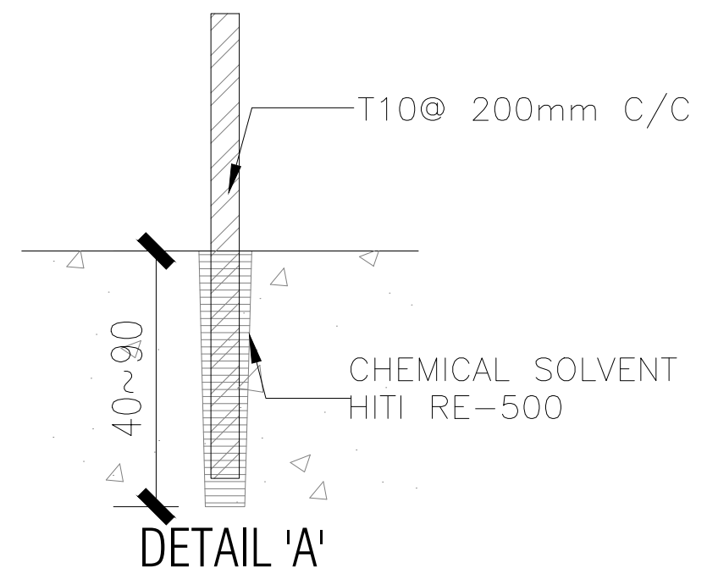
T10@ 200mm C/C
CHEMICAL SOLVENT HITI RE-500
40~90

DETAIL 'A'
Scale 1:4

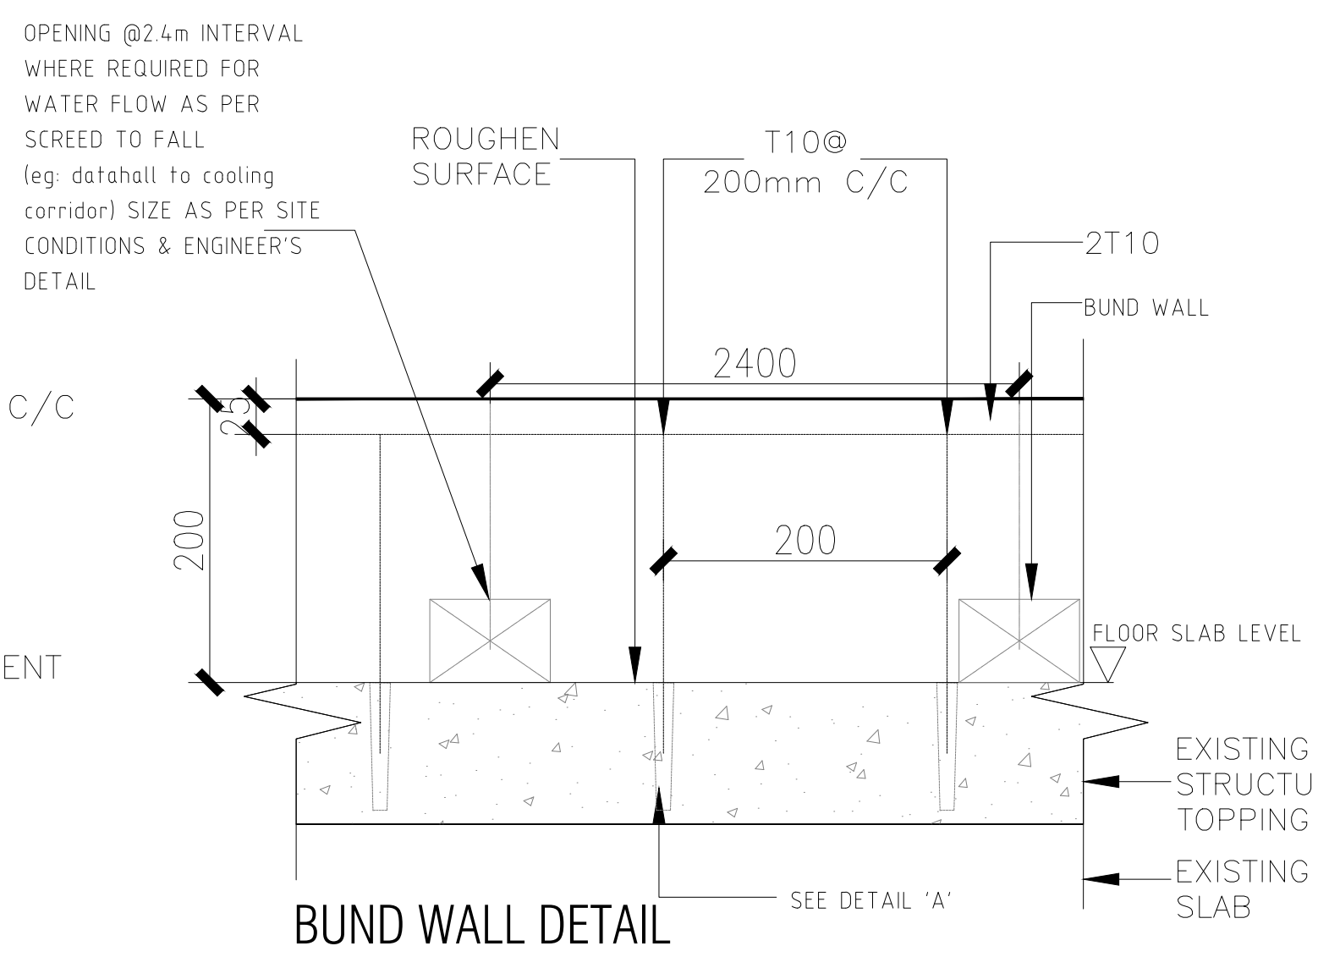
OPENING @2.4m INTERVAL WHERE REQUIRED FOR WATER FLOW AS PER SCREED TO FALL (eg: datahall to cooling corridor) SIZE AS PER SITE CONDITIONS & ENGINEER'S DETAIL
ROUGHEN SURFACE
T10@ 200mm C/C
2T10
BUND WALL
2400
25
200
200
FLOOR SLAB LEVEL
EXISTING STRUCTURAL TOPPING
EXISTING SLAB
SEE DETAIL 'A'

BUND WALL DETAIL
Scale 1:8

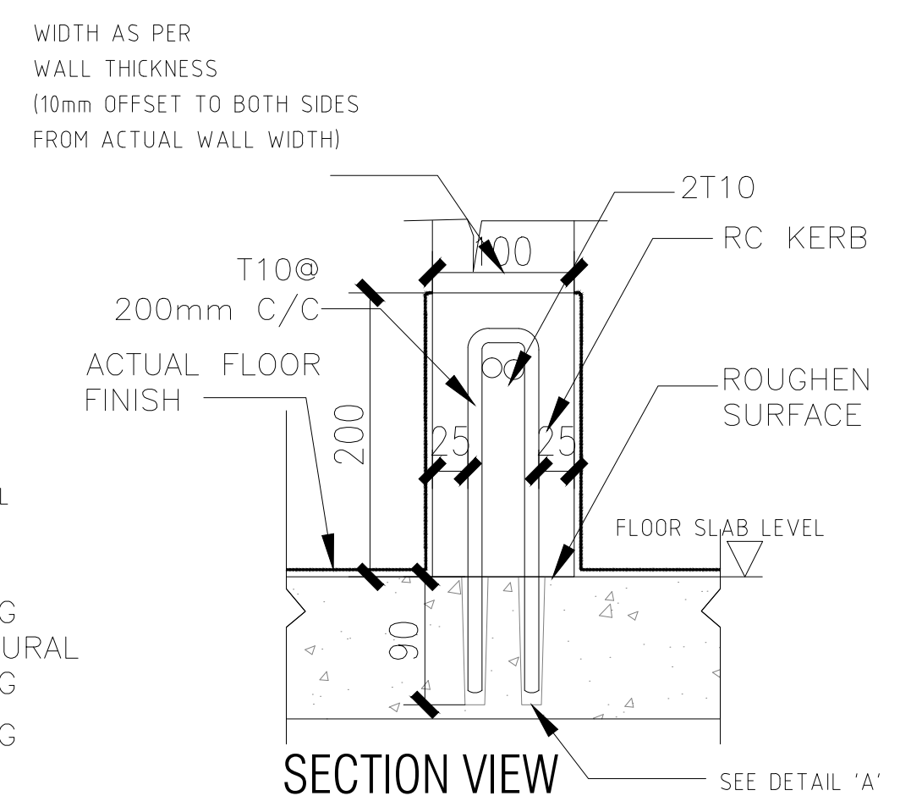
WIDTH AS PER WALL THICKNESS (10mm OFFSET TO BOTH SIDES FROM ACTUAL WALL WIDTH)
2T10
RC KERB
100
T10@ 200mm C/C
ACTUAL FLOOR FINISH
ROUGHEN SURFACE
200
25
25
FLOOR SLAB LEVEL
90
SEE DETAIL 'A'

SECTION VIEW
Scale 1:8

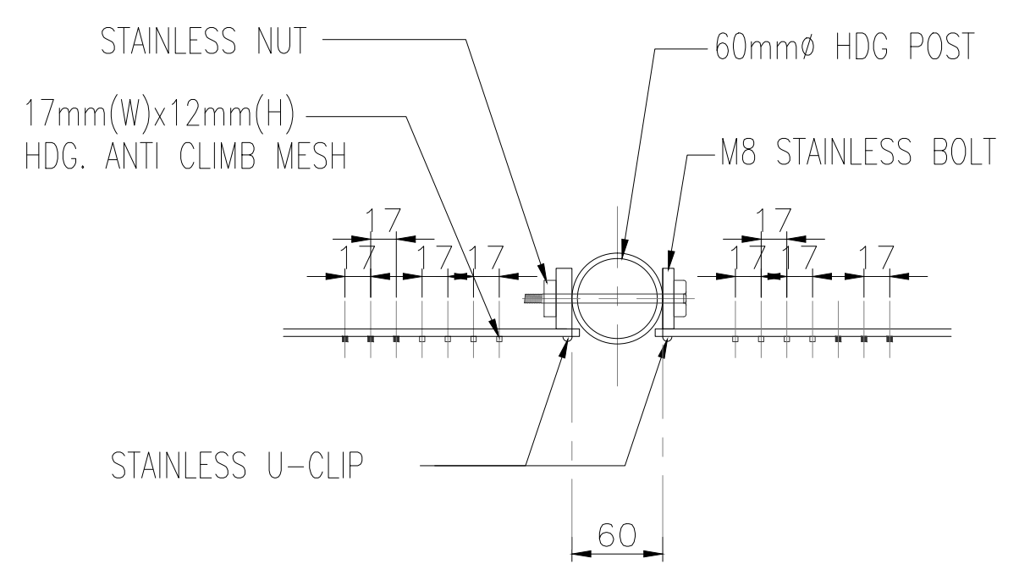
STAINLESS NUT
17mm(W)x12mm(H) HDG. ANTI CLIMB MESH
60mmø HDG POST
M8 STAINLESS BOLT
17
STAINLESS U-CLIP
60

DETAIL `D'
SCALE 1:20

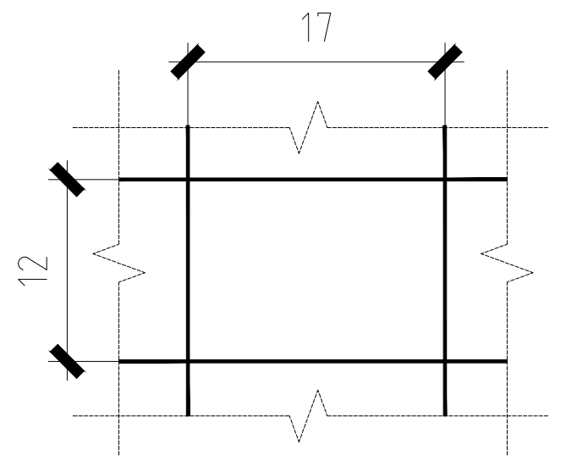

DETAIL `E'
SCALE : NTS

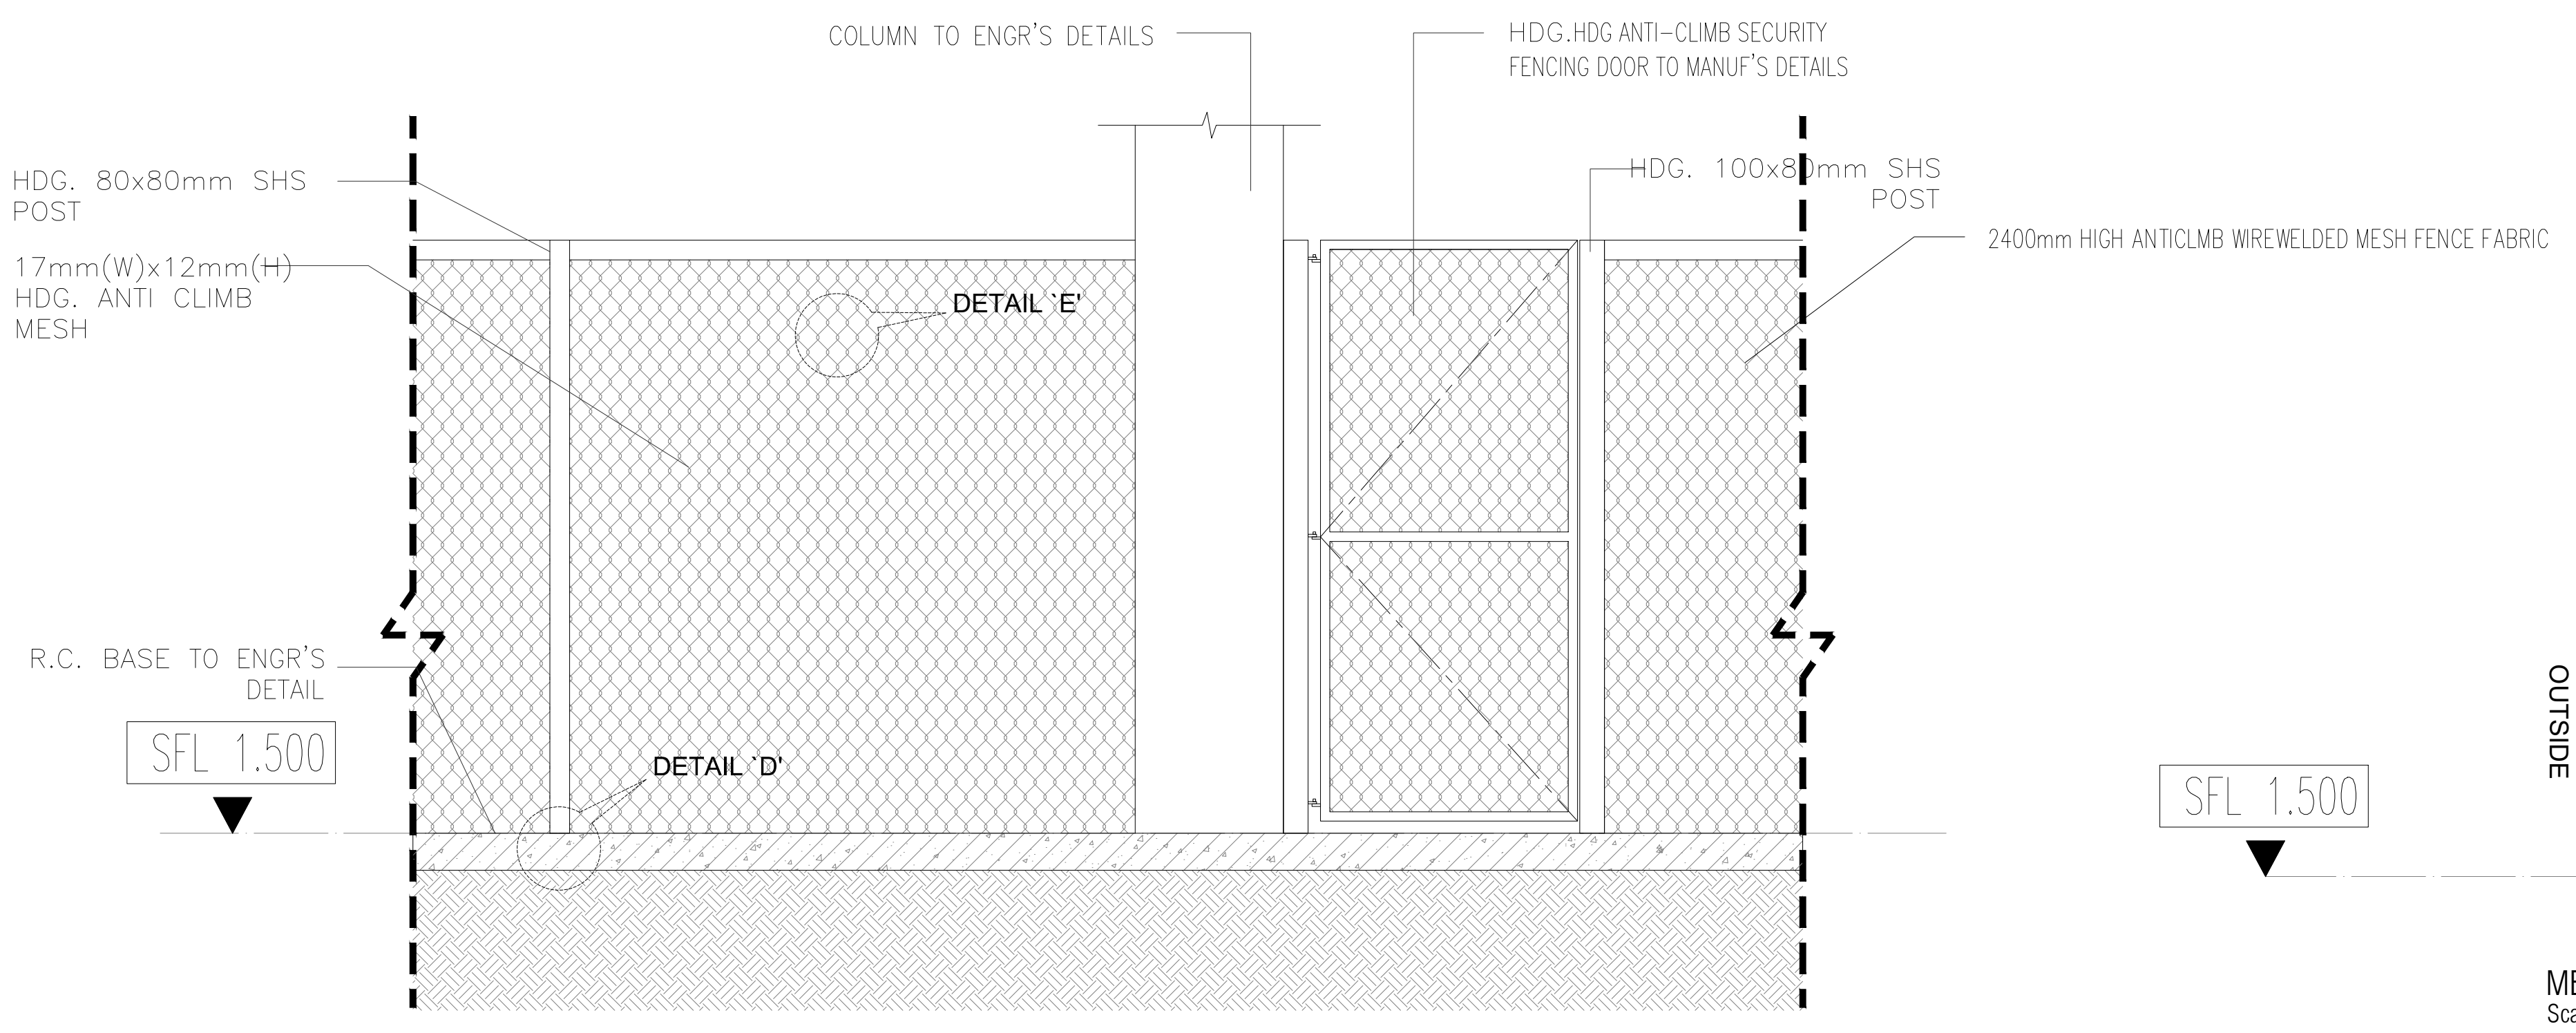
COLUMN TO ENGR'S DETAILS
HDG.HDG ANTI-CLIMB SECURITY FENCING DOOR TO MANUF'S DETAILS
HDG. 80x80mm SHS POST
HDG. 100x80mm SHS POST
17mm(W)x12mm(H) HDG. ANTI CLIMB MESH
2400mm HIGH ANTICLMB WIREWELDED MESH FENCE FABRIC
DETAIL `E'
R.C. BASE TO ENGR'S DETAIL
SFL 1.500
DETAIL `D'

MESH FENCE FABRIC ELEVATION VIEW
Scale 1:25

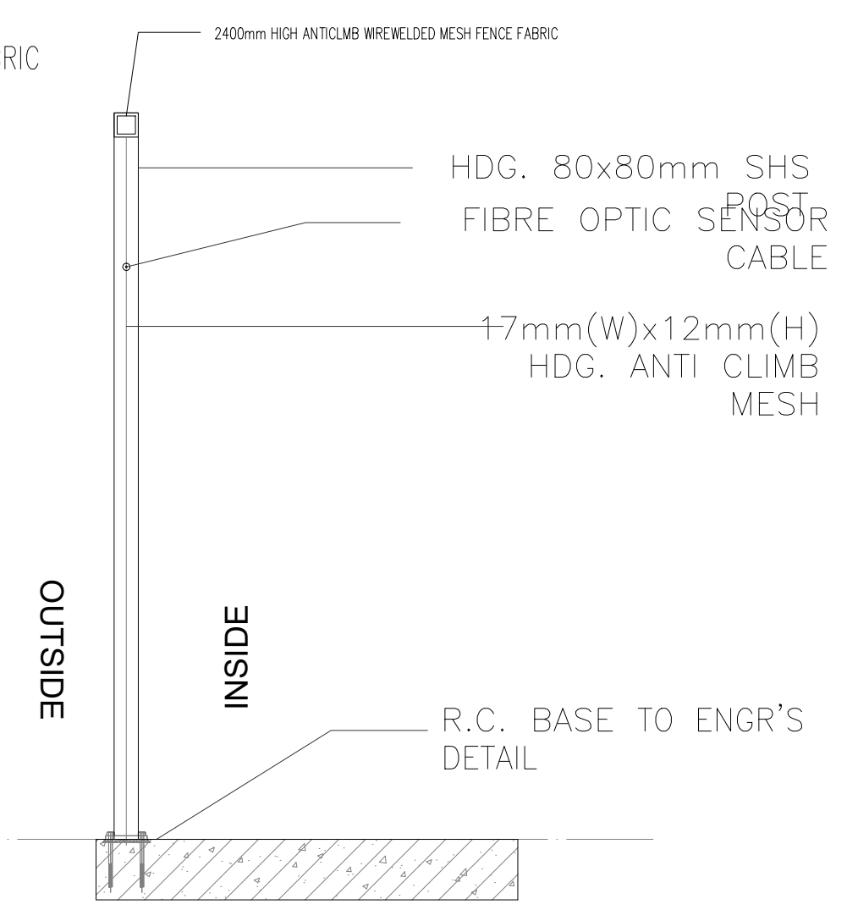
2400mm HIGH ANTICLMB WIREWELDED MESH FENCE FABRIC
HDG. 80x80mm SHS POST
FIBRE OPTIC SENSOR CABLE
17mm(W)x12mm(H) HDG. ANTI CLIMB MESH
OUTSIDE
INSIDE
R.C. BASE TO ENGR'S DETAIL
SFL 1.500

MESH FENCE FABRIC SECTION VIEW
Scale 1:25

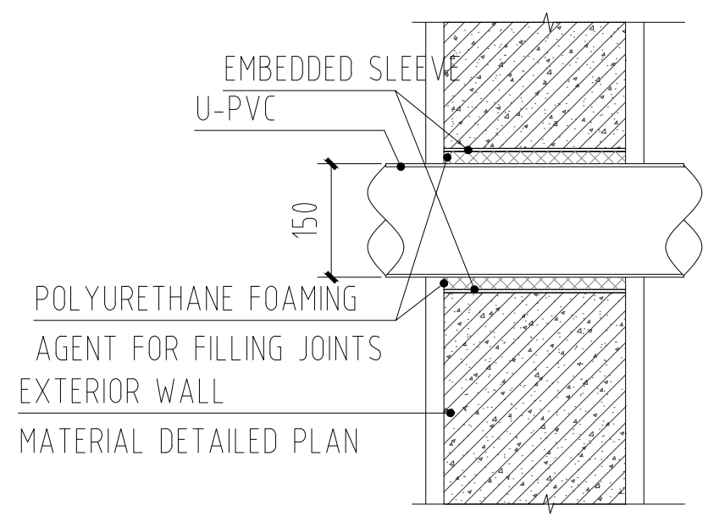
EMBEDDED SLEEVE
U-PVC
150
POLYURETHANE FOAMING AGENT FOR FILLING JOINTS
EXTERIOR WALL MATERIAL DETAILED PLAN

Pipe through wall DETAIL
Scale 1:10

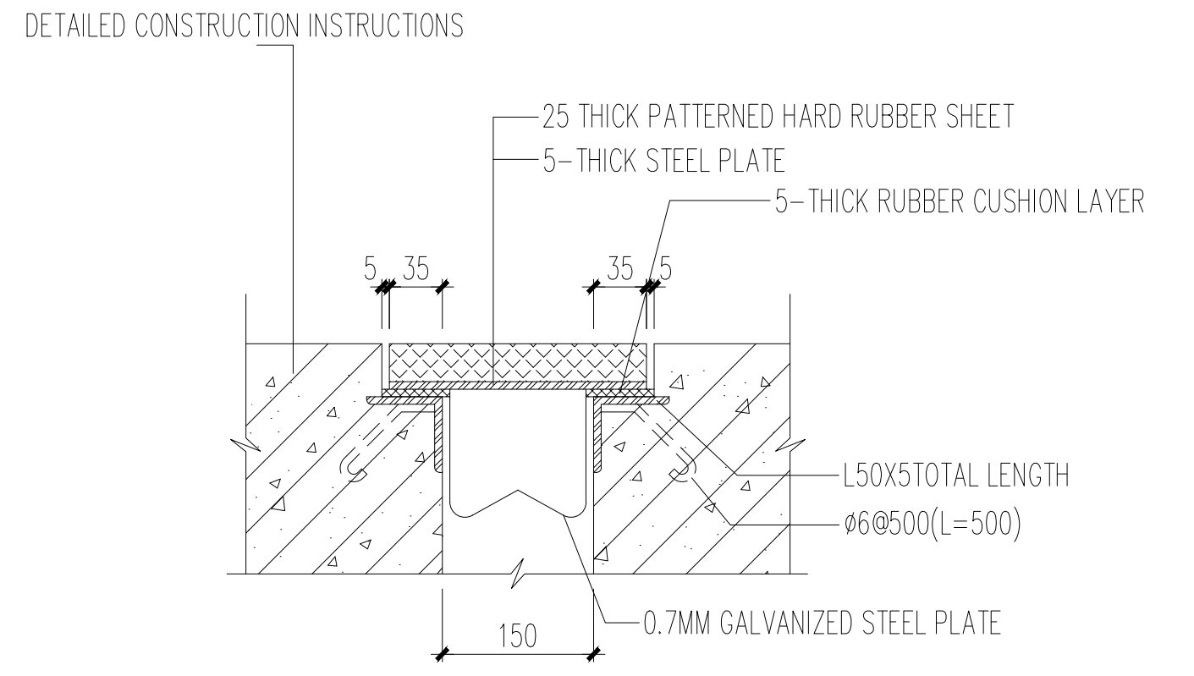
DETAILED CONSTRUCTION INSTRUCTIONS
25 THICK PATTERNED HARD RUBBER SHEET
5-THICK STEEL PLATE
5-THICK RUBBER CUSHION LAYER
5
35
35
5
L50X5TOTAL LENGTH
ø6@500(L=500)
150
0.7MM GALVANIZED STEEL PLATE

FLOOR DEFORMATION JOINT DETAIL-03
Scale 1:5

THE "SFL" MARKED IN THE DRAWING REFERS TO THE STRUCTURAL FLOOR LEVEL, WHILE THE FINISHED FLOOR LEVEL (FFL) IS DETERMINED BASED ON FLOOR FINISHES.

NOTE : THIS PRINT IS OF A CONFIDENTIAL NATURE, IT SHALL NOT BE TRACED,PHOTOGRAPHED,PHOTOSTATED OR REPRODUCED IN ANY MANER,NOR USED FOR ANY PURPOSE WHATSOEVER EXCEPT BY WRITTEN PERMISSION

CLIENT :
GULF EDGE DC 01
87 Wireless Road, M Thai Tower 11th. Floor, All Seasons Place, Lumpini,
Pathumwan, Bangkok 10330, Thailand

CONTRACTOR :
华西发展(泰国)有限公司
บริษัท หัวซือ ดีเวลลอปเม้นต์ (ประเทศไทย) จำกัด
HUASHI DEVELOPMENT CO.,LTD
No. 202, Room No. 1403, 14/F, Le Concorde Building,
Ratchadapisek Road, Huaykhwang Sub-District,
Huaykhwang District, Bangkok Metropolitan 10310.

CONSULTANT :
ARbay
บริษัท เอ อาร์ เบย์ จำกัด
ARbay Company Limited
31 st Floor Bangkok Insurance Building
25 South Sathorn road Thungmahamek
Sathorn Bangkok 10120 THAILAND
T +66 (0) 2286 8199
F +66 (0) 2286 2863
info@arbay.co.th

CONSULTANT :
Qbic Engineers & Architects Co.,Ltd.
8 Soi KALONG 4 SANAMBINNAM ROAD,
THASAI SUB-DISTRICT, MUANG NONTHABURI DISTRICT
, NONTHABURI.
Tel 662-950-4374
Fax 662-580-3231
E-Mail : qbic@qbic.co.th, www.qbic.co.th
QBIC ENGINEERS AND ARCHITECTS CO.,LTD.

CONSULTANT :
MITR
MITR TECHNICAL CONSULTANT CO.,LTD.
1168/8 12th FLOOR, LUMPINI TOWER BUILDING,
RAMA IV RD., THUNGMAHAMEK, SATHORN, BANGKOK 10120, THAILAND
TEL : 0-2679-9079-84
FAX : 0-2679-9085 E-mail: mitr_dd@mitr.com

Architect : SIGNATURE
ประกิต พนานุรัตน์ วสถ. 580
ที่อยู่
251/1 ถ.จารุเมือง แขวงรองเมือง เขตปทุมวัน
กรุงเทพมหานคร โทรศัพท์ 02-286-8199

Structural Engineer : SIGNATURE
วิศวกรผู้ออกแบบโครงสร้าง
ณัฐสม สงวนวงษ์ วย 1423
ที่อยู่
2/1 ซ.รามคำแหง 150 ถ.รามคำแหง
แขวง สะพานสูง เขต สะพานสูง กทม. 10240

Structural Inspector : SIGNATURE
วิศวกรผู้ตรวจสอบโครงสร้าง
โกมล จุฑาภัทร วย 964
ที่อยู่
24/18 ซ.นวมินทร์ 129 ถ. นวมินทร์
แขวง นวลจันทร์ เขต บึงกุ่ม กทม. 10230

Electrical Engineer : SIGNATURE
วิศวกรผู้ออกแบบระบบไฟฟ้ากำลัง
นายสุภัทร บูรณวิทย์ วฟก.1265
ที่อยู่
21 ซอยทานสัมฤทธิ์ 13
ตำบลท่าทราย อ.เมืองนนทบุรี จ.นนทบุรี 11000

Mechanical Engineer : SIGNATURE
วิศวกรผู้ออกแบบระบบเครื่องกลและปรับอากาศ
นายประสิทธิ์ เกียวสุนทร วก.1221
ประสิทธิ์
ที่อยู่
44/372 ซอยบางกระดี่ 35/1 แขวงแสมดำ
เขตบางขุนเทียน กทม. 10150

Sanitary Engineer : SIGNATURE
วิศวกรผู้ออกแบบระบบสุขาภิบาล และดับเพลิง
นายทศวรรษ สนั่นฤทธิ์ วส. 215
ทศวรรษ
ที่อยู่
บ้านเลขที่ 99/107 หมู่ที่ 3 ต.ศีรษะจรเข้น้อย
อ.บางเสาธง จ.สมุทรปราการ 10540

ISSUE/REVISION

REV.	DESCRIPTION	DATE
A	90% DEVELOPED	09/05/2026

PROJECT NAME :
GEDC 01
LOCATION:
Nikhom Phattana district, Rayong ,industrial estate,CPGC

BUILDING :
MAIN BUILDING

90% DEVELOPED

TITLE :
TYPICAL DETAILS A

JOB NO.	SCALE 1:50
DRAWN FLY	REF.
CHECKED LJC	DWG.NO. MPK01A-90-A-TD-001
APPROVED LXD	
DATE 2026.05.09	