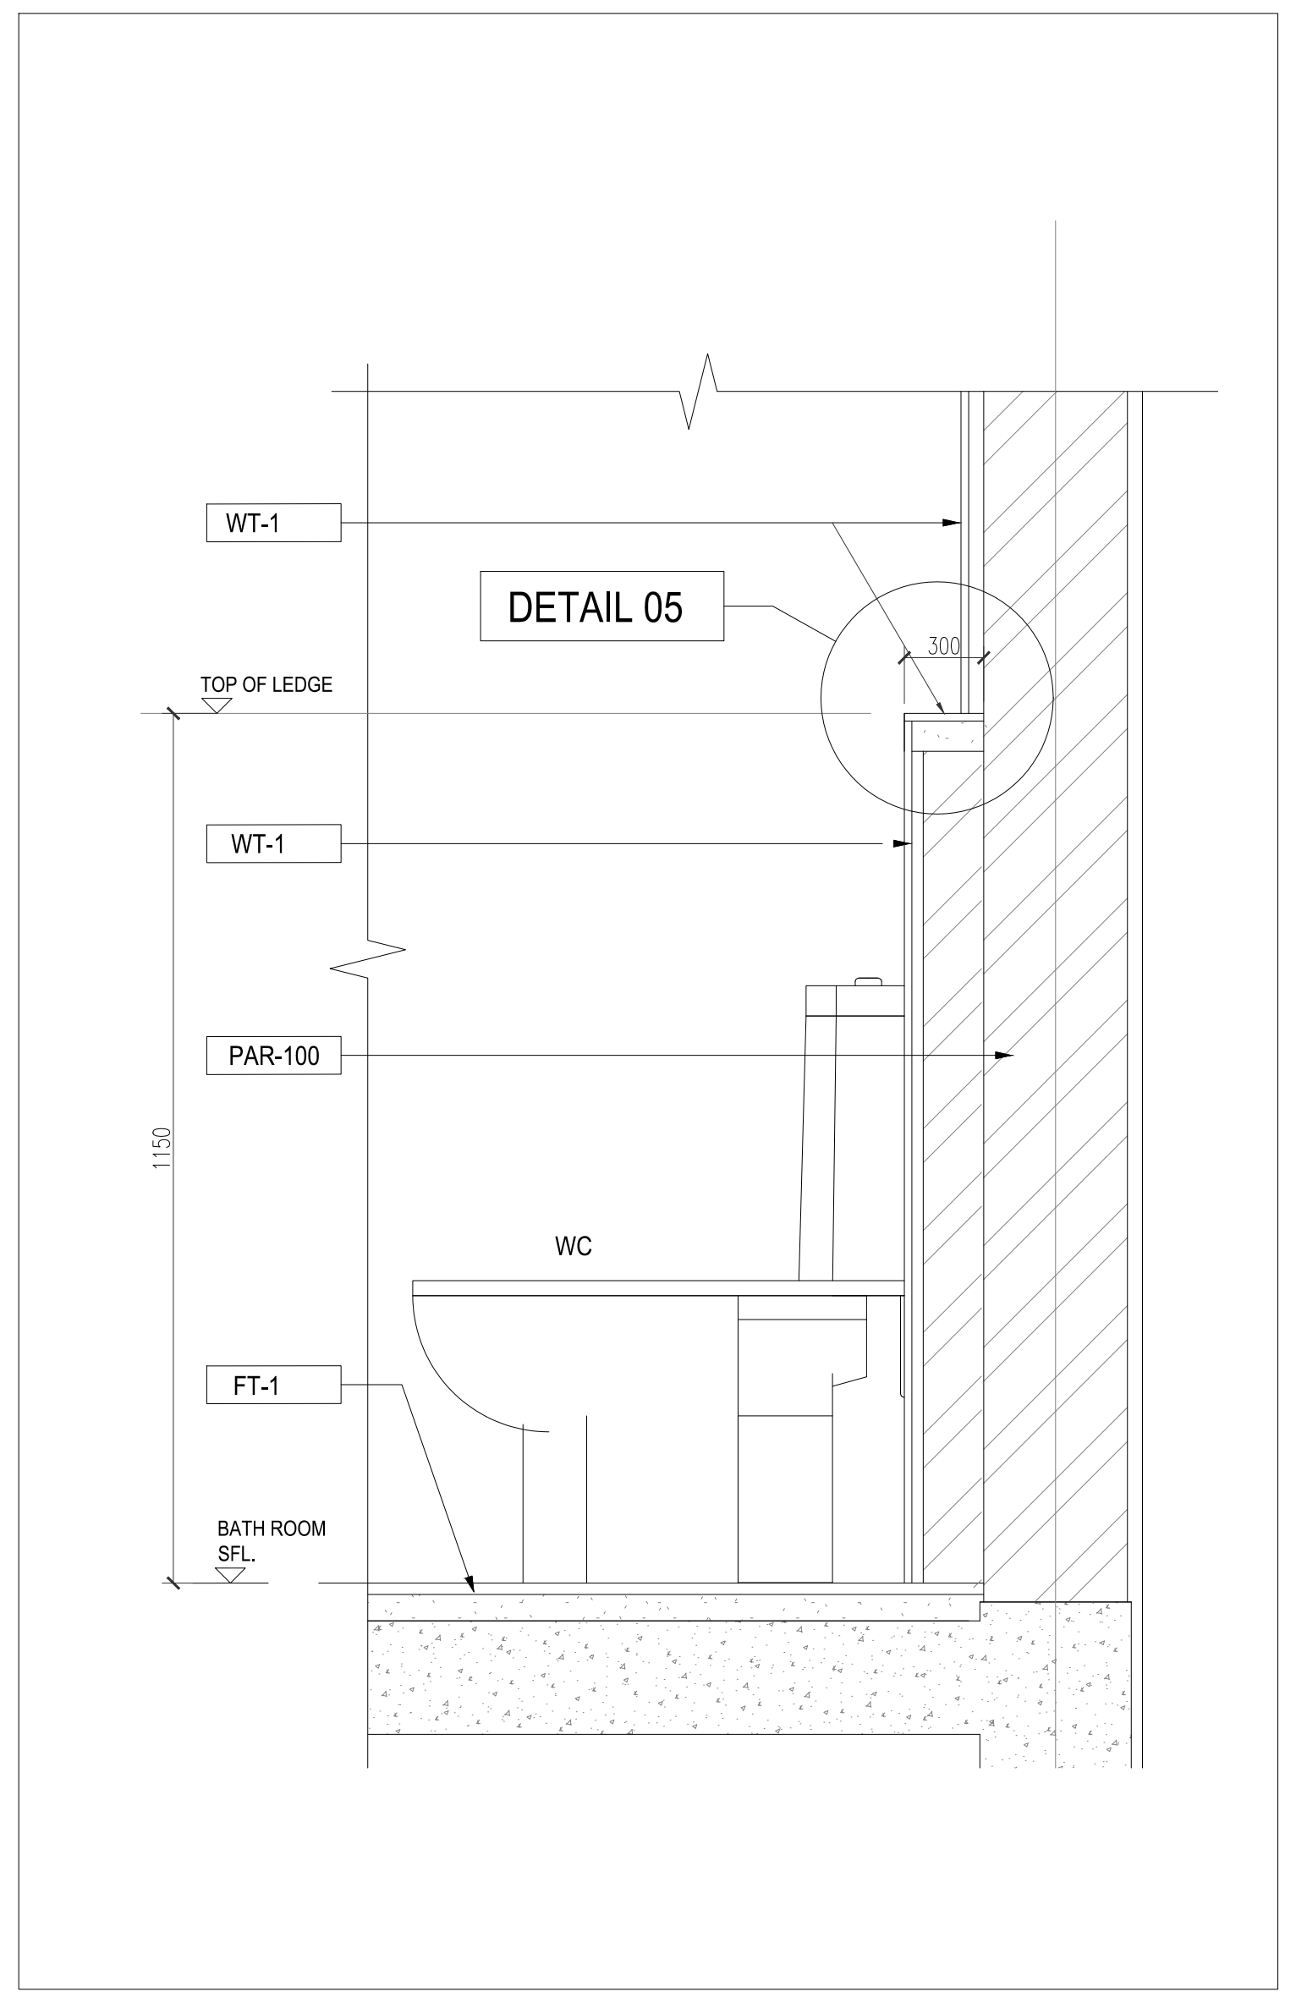

01 DETAIL
SCALE 1: 10

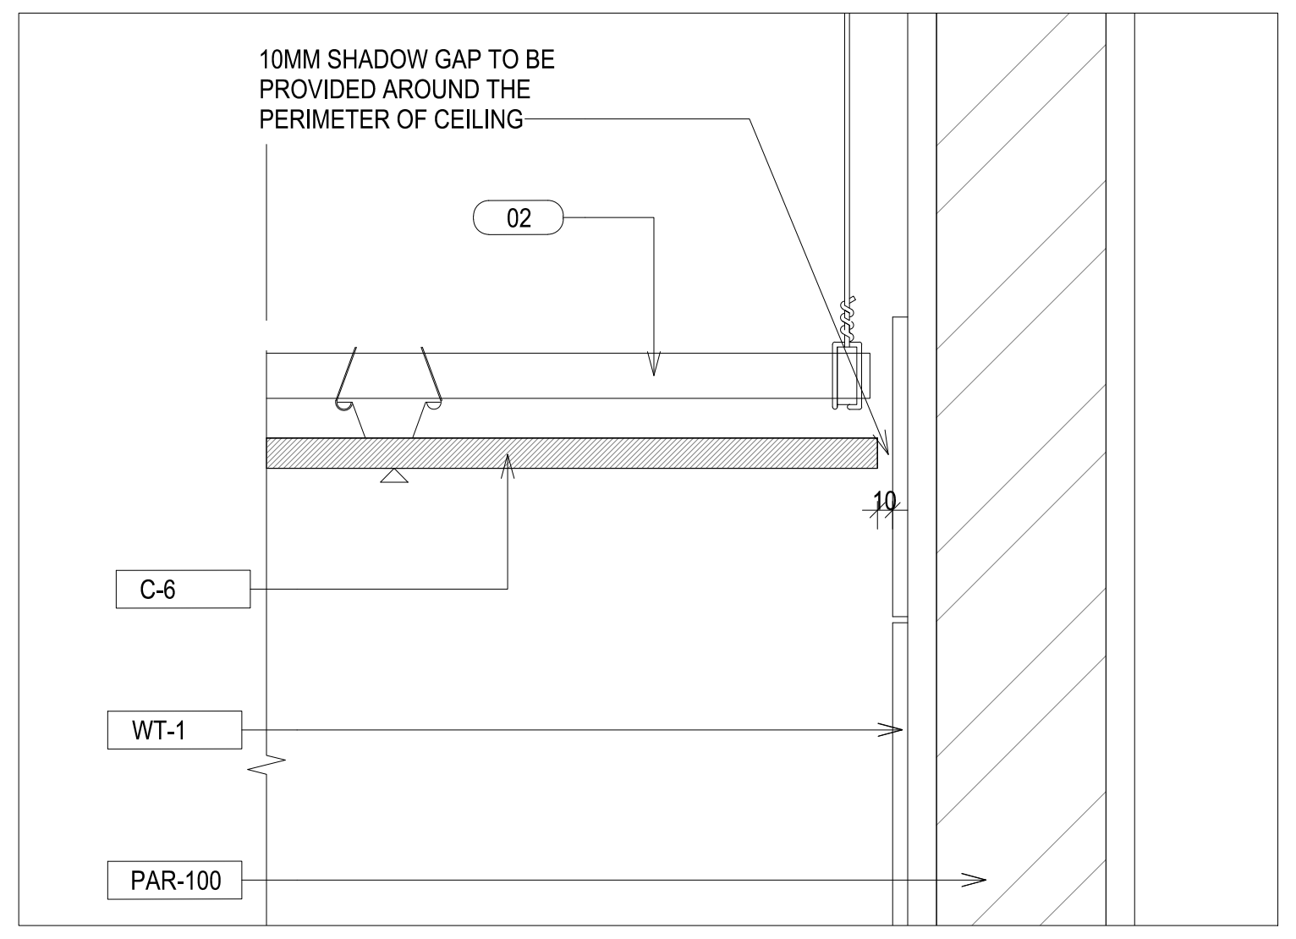
10MM SHADOW GAP TO BE PROVIDED AROUND THE PERIMETER OF CEILING
02
10
C-6
WT-1
PAR-100

02 DETAIL
SCALE 1: 5

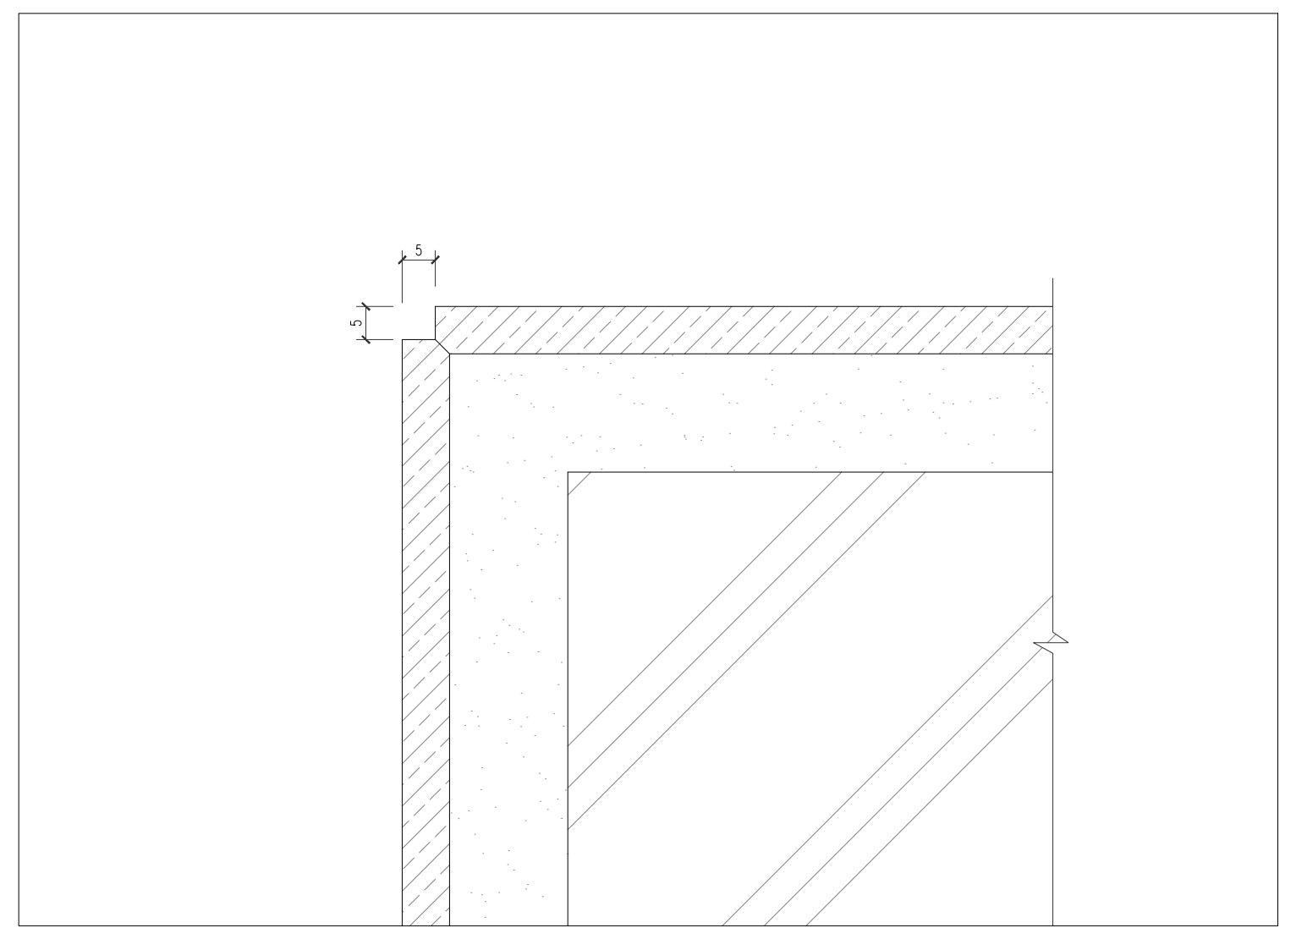

10 TYPICAL TILE JOINT DETAIL 'BRID-MOUTH'
SCALE 1: 1

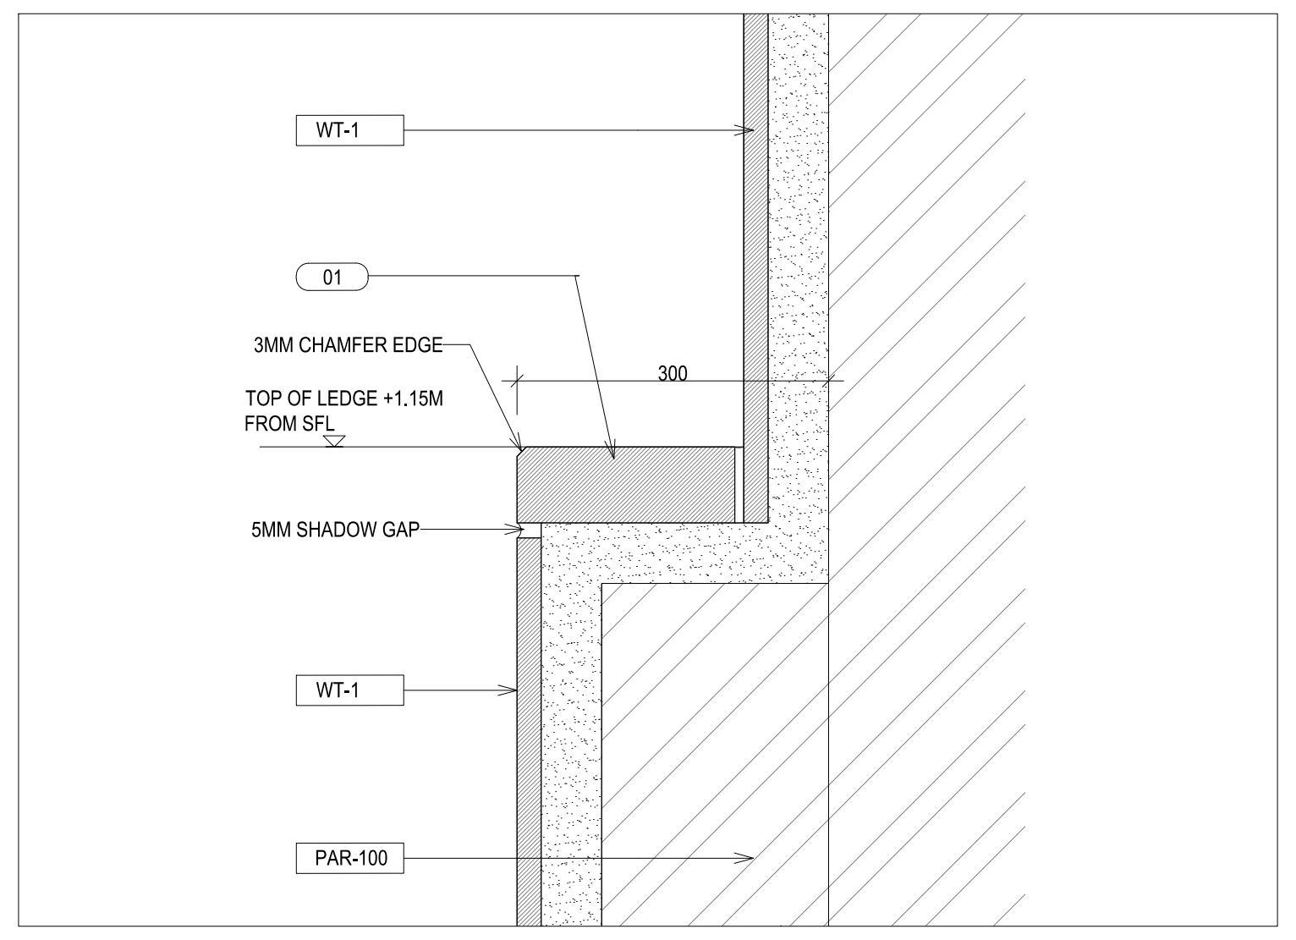

03 DETAIL
SCALE 1: 2.5

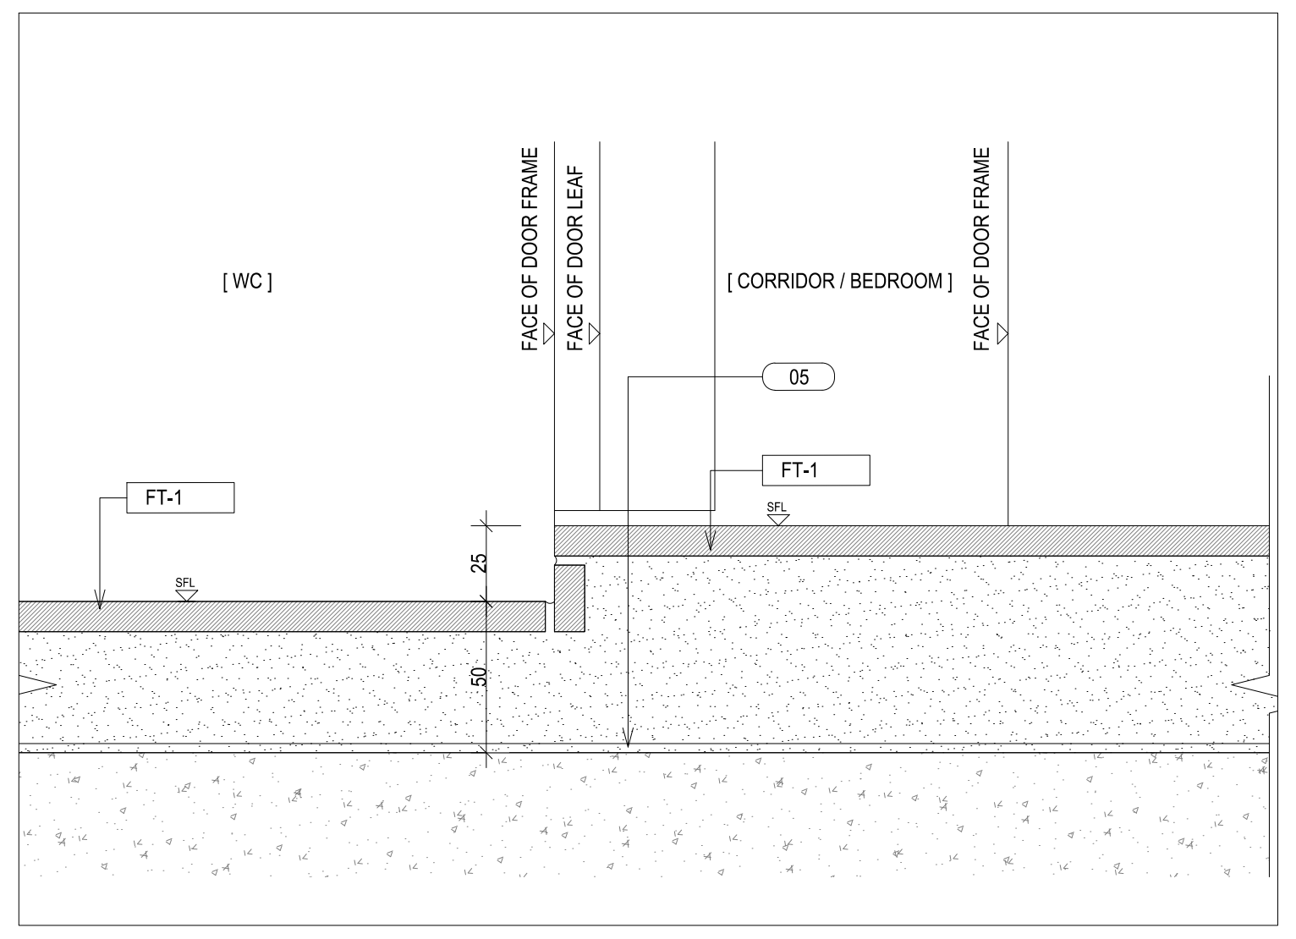

04 DETAIL
SCALE 1: 2.5

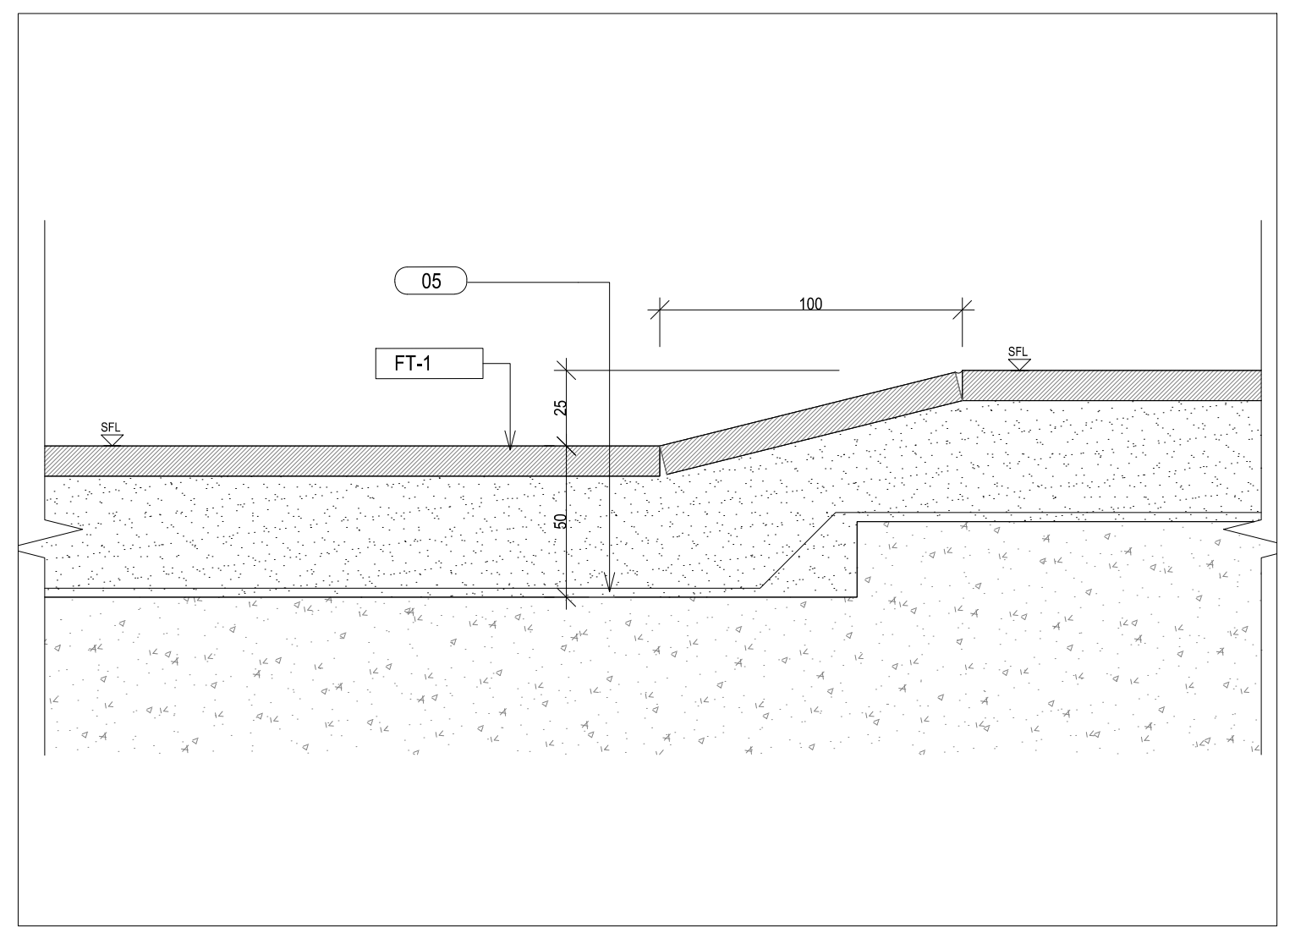

05 DETAIL
SCALE 1: 2.5

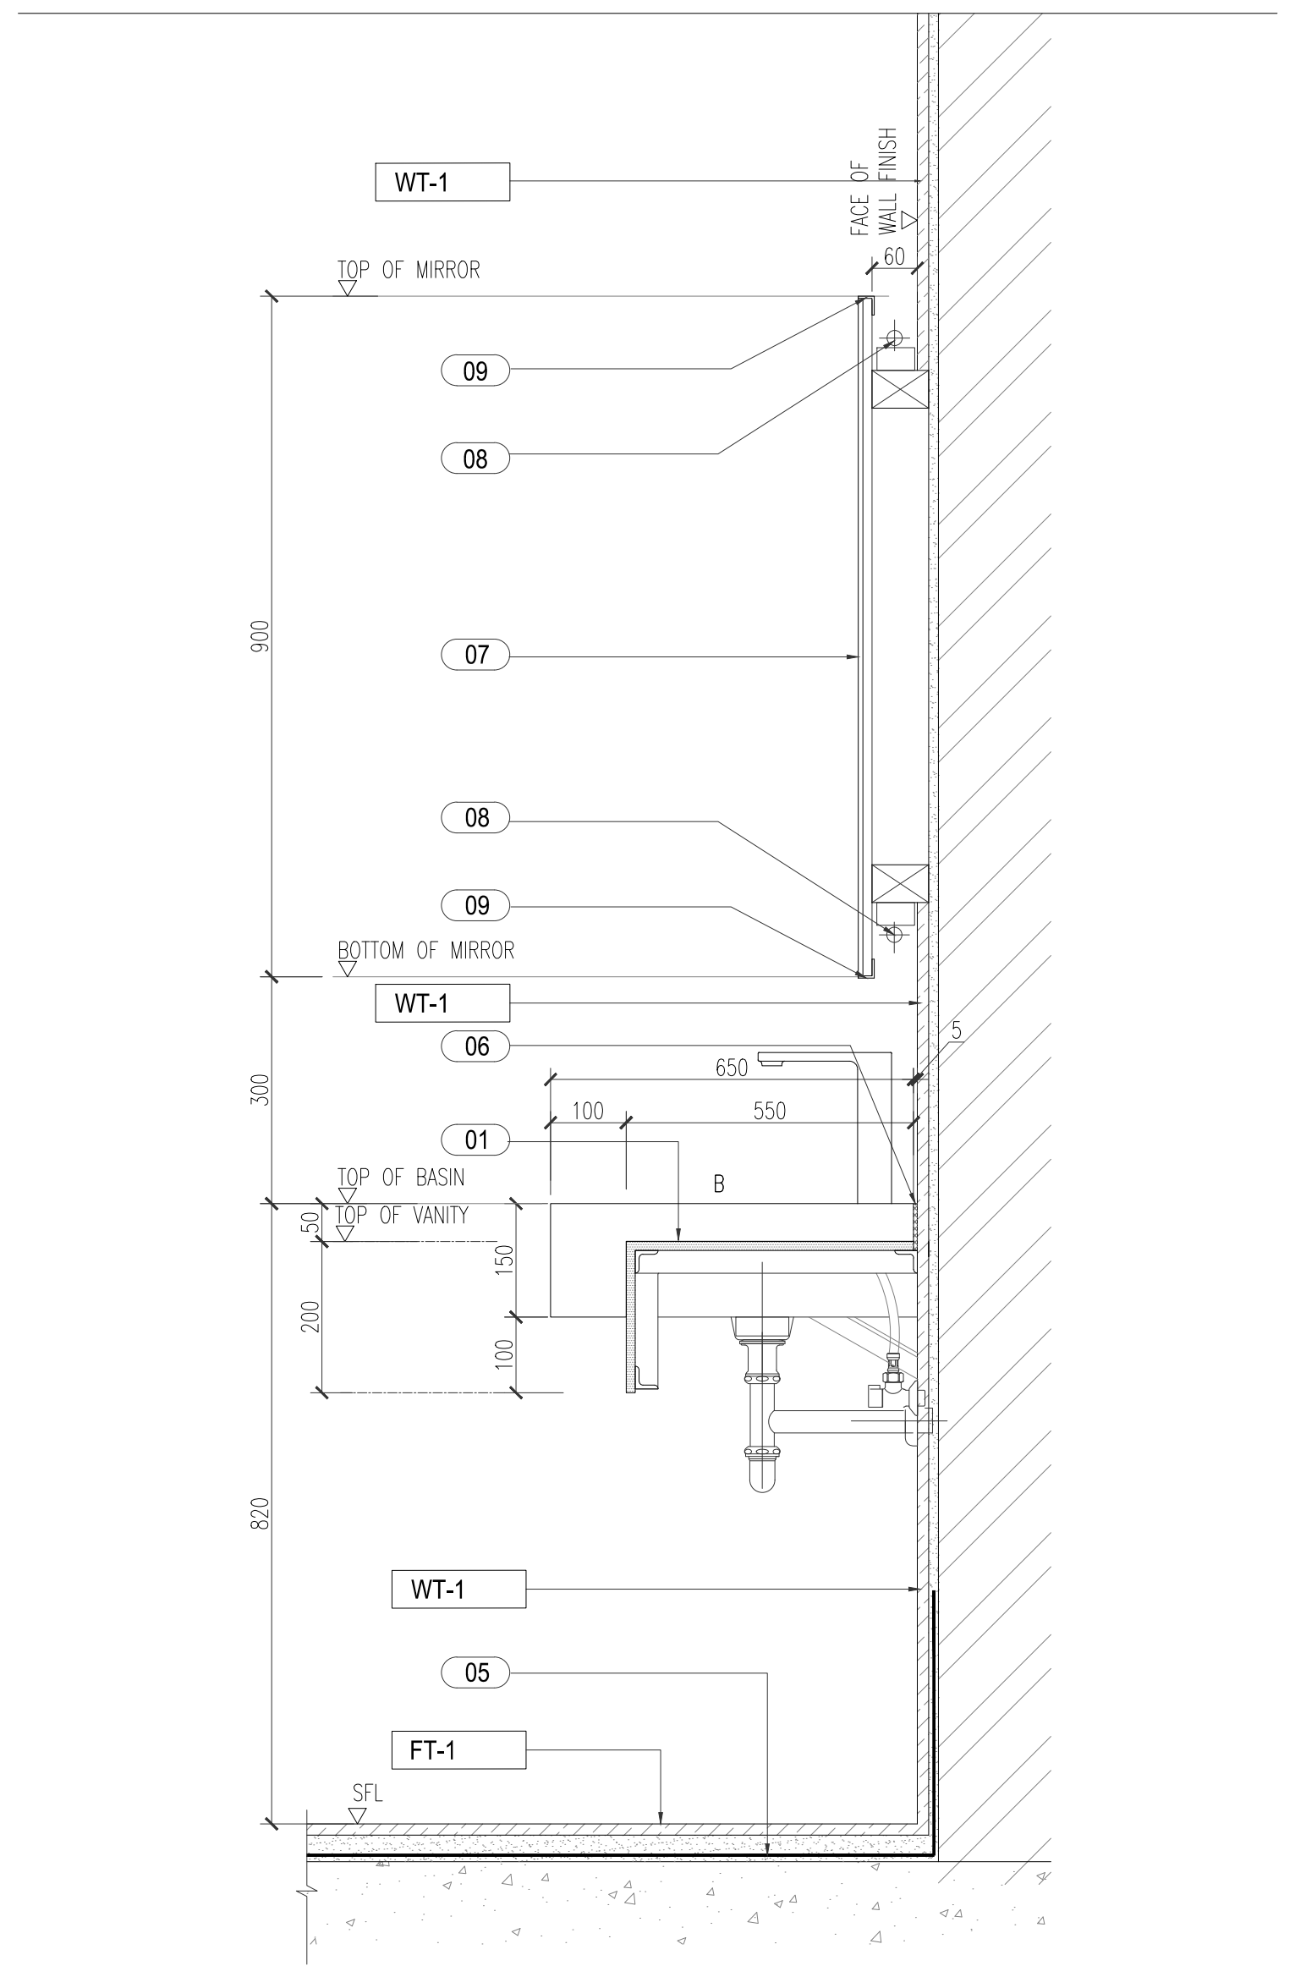

06 VANITY DETAIL (COMMON AREA)
SCALE 1: 10

TOILET DETAIL LEGEND :

REFERENCE	DESCRIPTION
C-6	600 X 600MM ALUMINIUM BUCKLE PLATE CEILING WITH UNISTRUTSTRUCTURALCEILING SYSTEM + ANTI-DUST PAINT SOFFIT
FT-1	12mm THK NON-SLIP HOMOGENOUS TILE (R10) ON WATERPROOF SCREED WITH WATERPROOFING SYSTEM
PAR-100	BRICK/RC WALL AS INDICATED IN PLAN
WT-1	300*600MM12MM THK WATERPROOF HOMOGENOUS TILE
01	25MM THK. SOLID SURFACE WITH STEEL BRACING
02	SUSPENDED CEILING SYSTEM, METAL FURRINGS
03	RC LINTEL TO ENGR.'S DETAIL
04	DOOR/WINDOW DETAIL REFER TO DOOR/WINDOW SCHEDULE
05	SELECTED CEMENTITIOUS WATERPROOFING COMPOUND ON SEMENT SCREED, 300MM HT. (MIN.) UPTURN TO WALL & 1200MM @ SHOWER AREA BEFORE TILING COMMENCE
06	CLEAR SEALANT
07	6MM THK. MIRROR WITH CHAMFERED EDGE ON 6MM THK. WATER RESISTANT MARINE PLYWOOD BACKING WITH PERIMETER ALUMINIUM TRIM EDGING
08	RECESSED WARM WHITE COLOR FLUORESCENT LIGHT
09	20 X 20MM S.S ANGLE AT MIRROR PERIMETER EDGE
B	BASIN
FT	FLOOR TRAP
TRH	TOILET ROLL HOLDER
WC	WATER CLOSET
HB	HAND BIDET
MR	MIRROR
UR	URINAL
SH	SHOWER HEAD
HDR	HAND DRYER
SD	SOAP DISPENSER
GB	S.S GRAB BAR
s.o.p	TILES SETTING OUT POINTS
⊠	450 X 450MM CEILING ACCESS PANEL

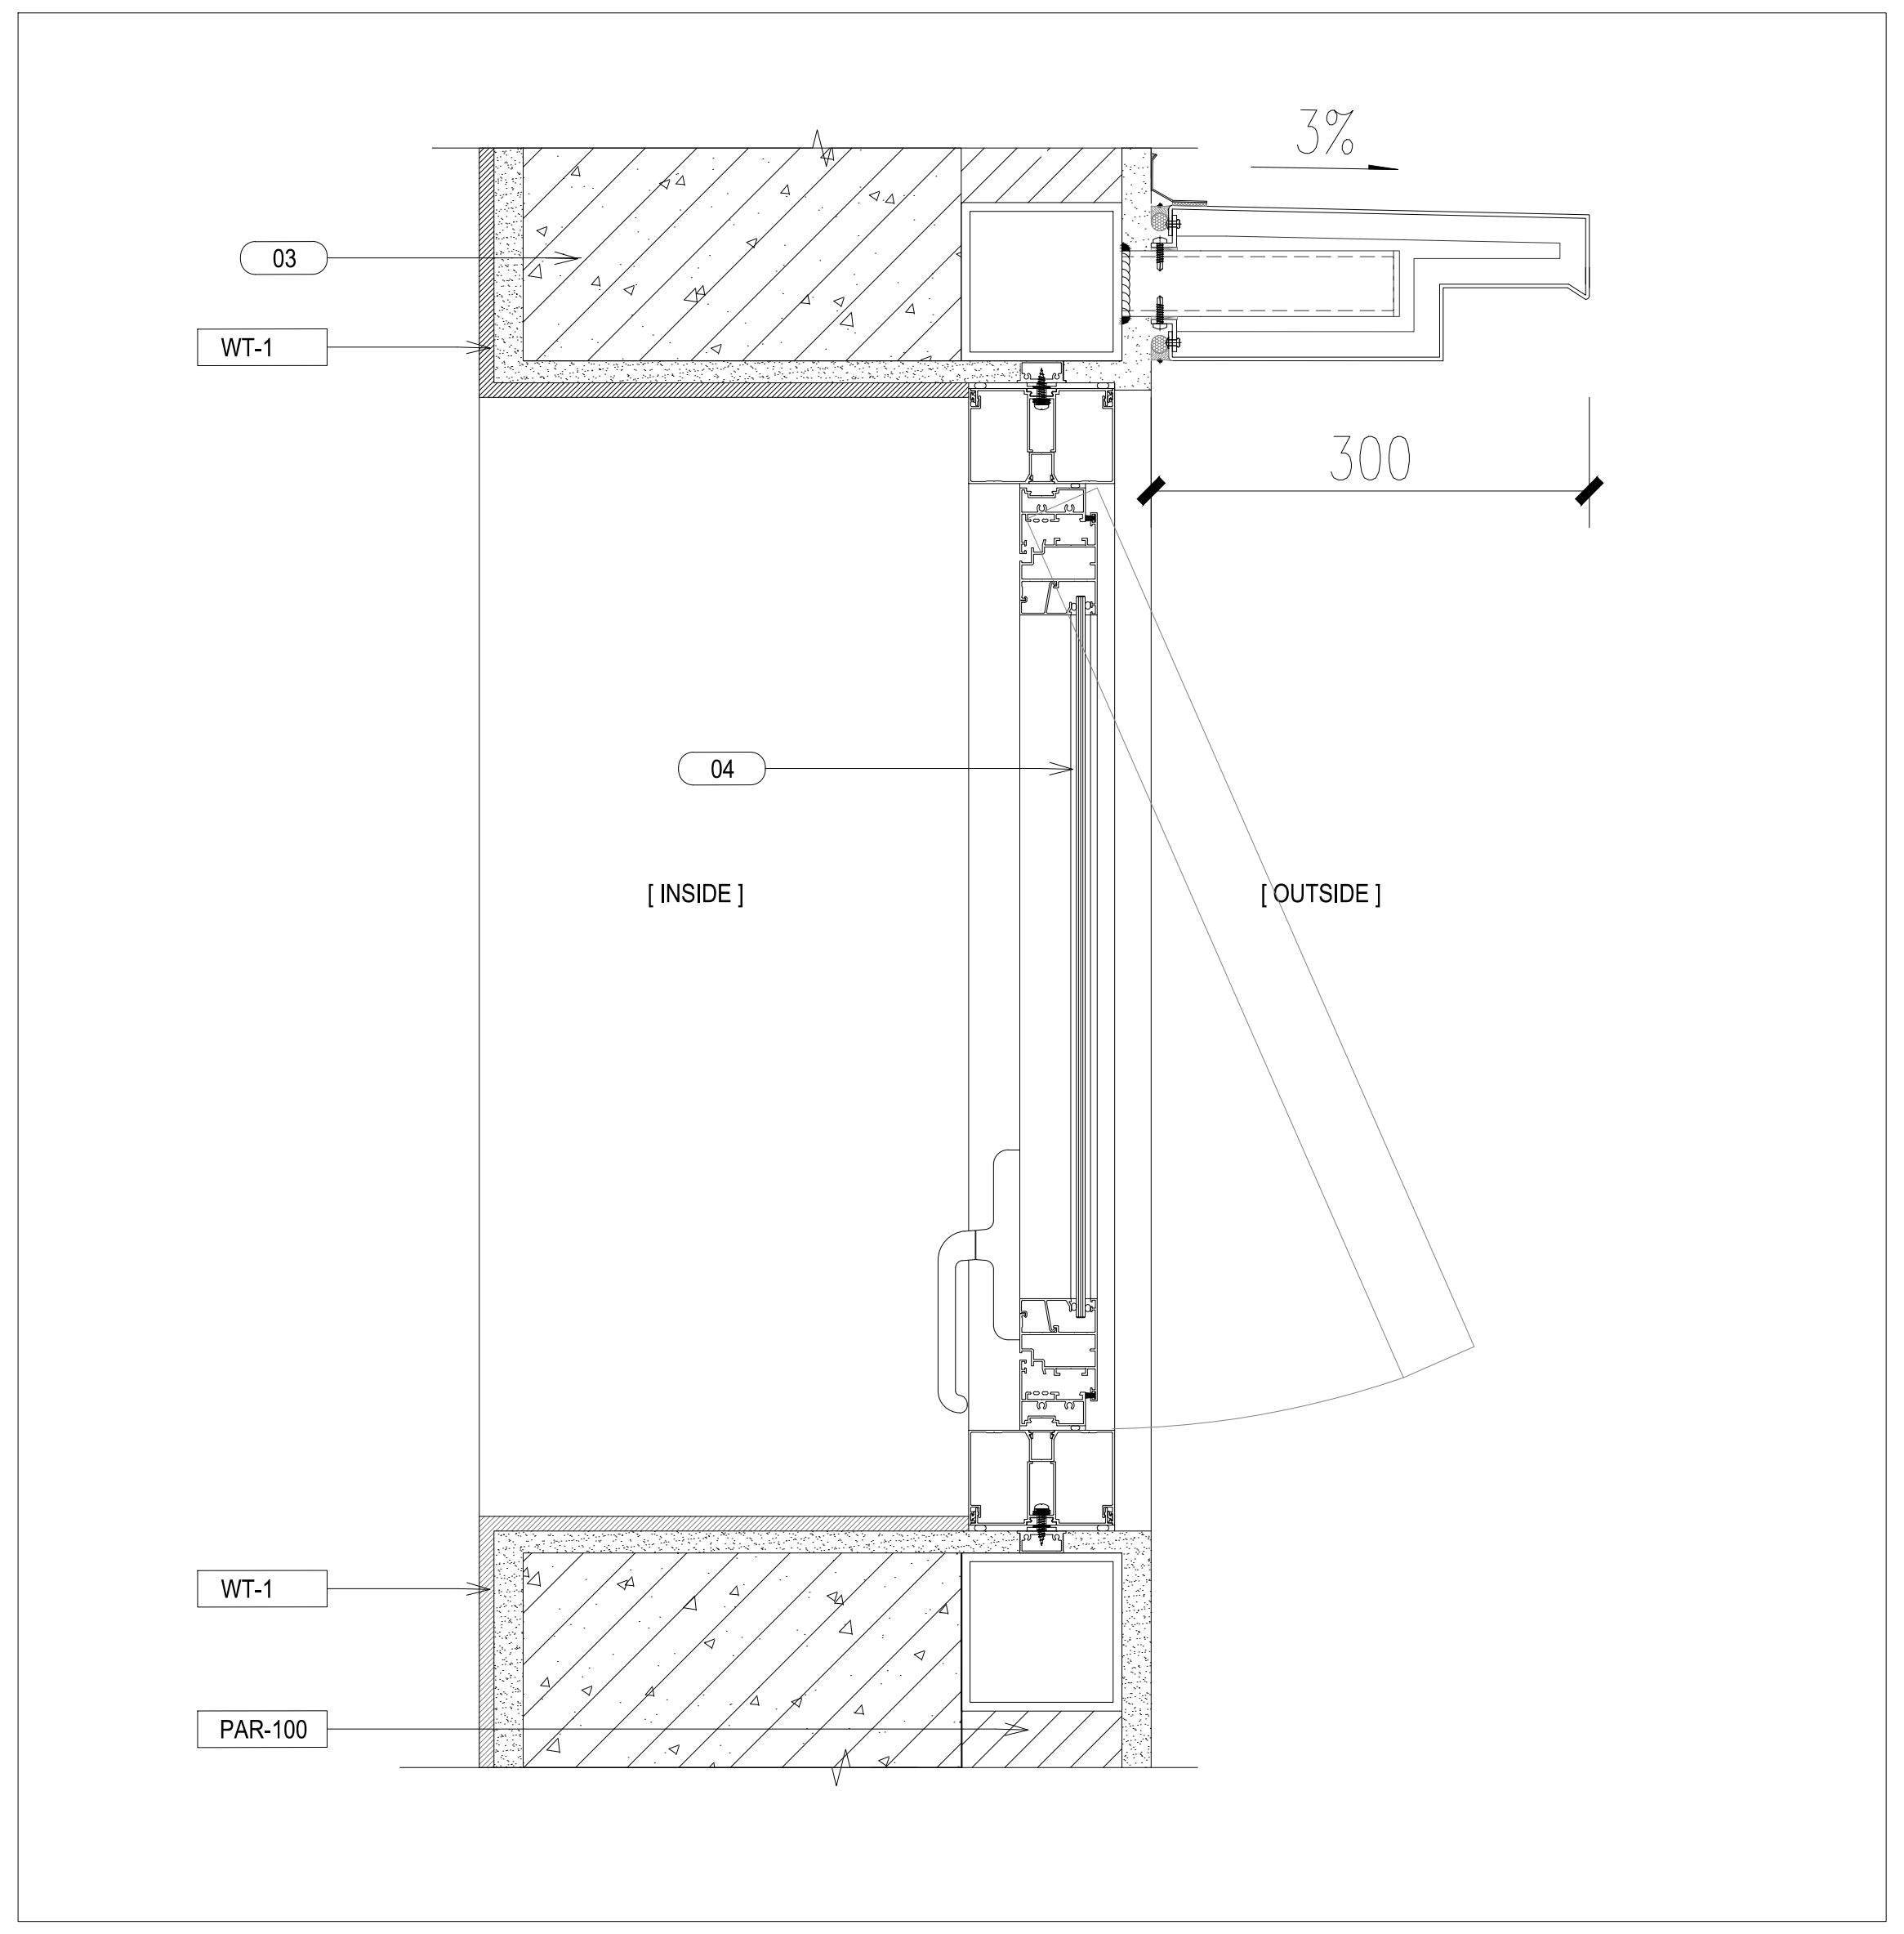

07 DETAIL
SCALE 1: 5

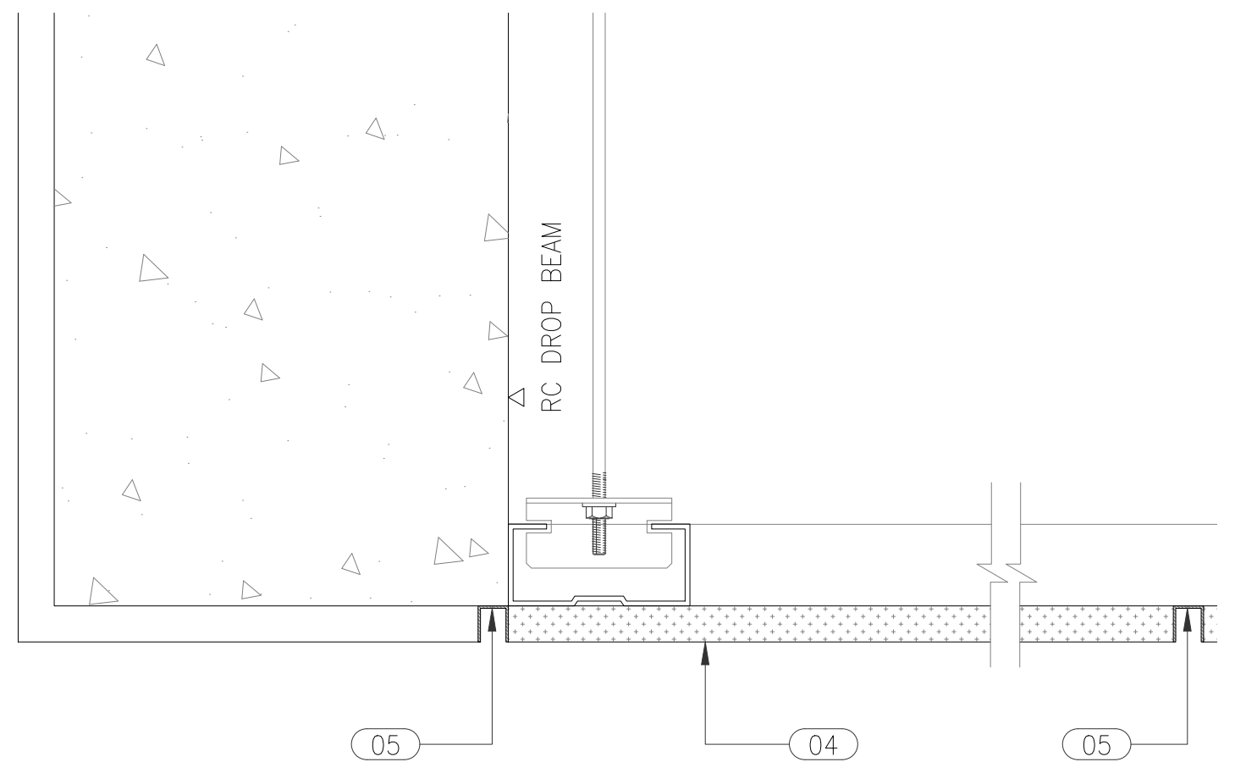

08 TYPICAL CEILING GROOVE DETAIL
SCALE 1 : 2.5

CEILING DETAIL LEGEND :

01	PROPRIETARY 10MM SHADOW GAP METAL BEAD(CONTINUOUS) WITH PAINTED FINISH
02	LED LIGHT (3000K)
03	PROPRIETARY UPVC EDGE BEADING
04	CALCIUM SILICATE BOARD WITH ANTI-DUST PAINT SOFFIT
05	10 X 10 S.S RECESSED GROOVE LINE, FLUSH WITH CEILING BOARD

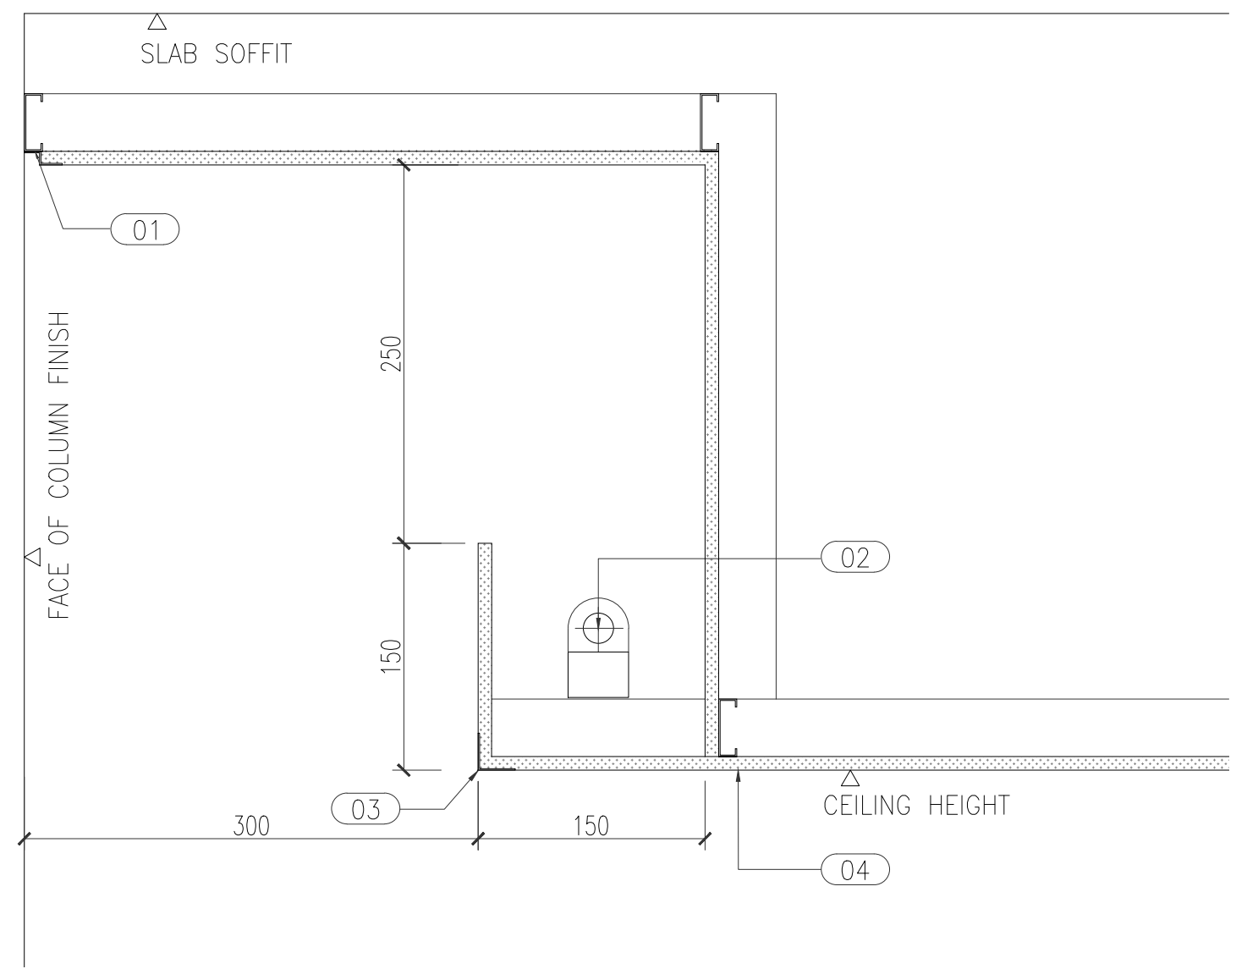

09 RECESS LIGHT TROUGH DETAIL - COLUMN
SCALE 1 : 5

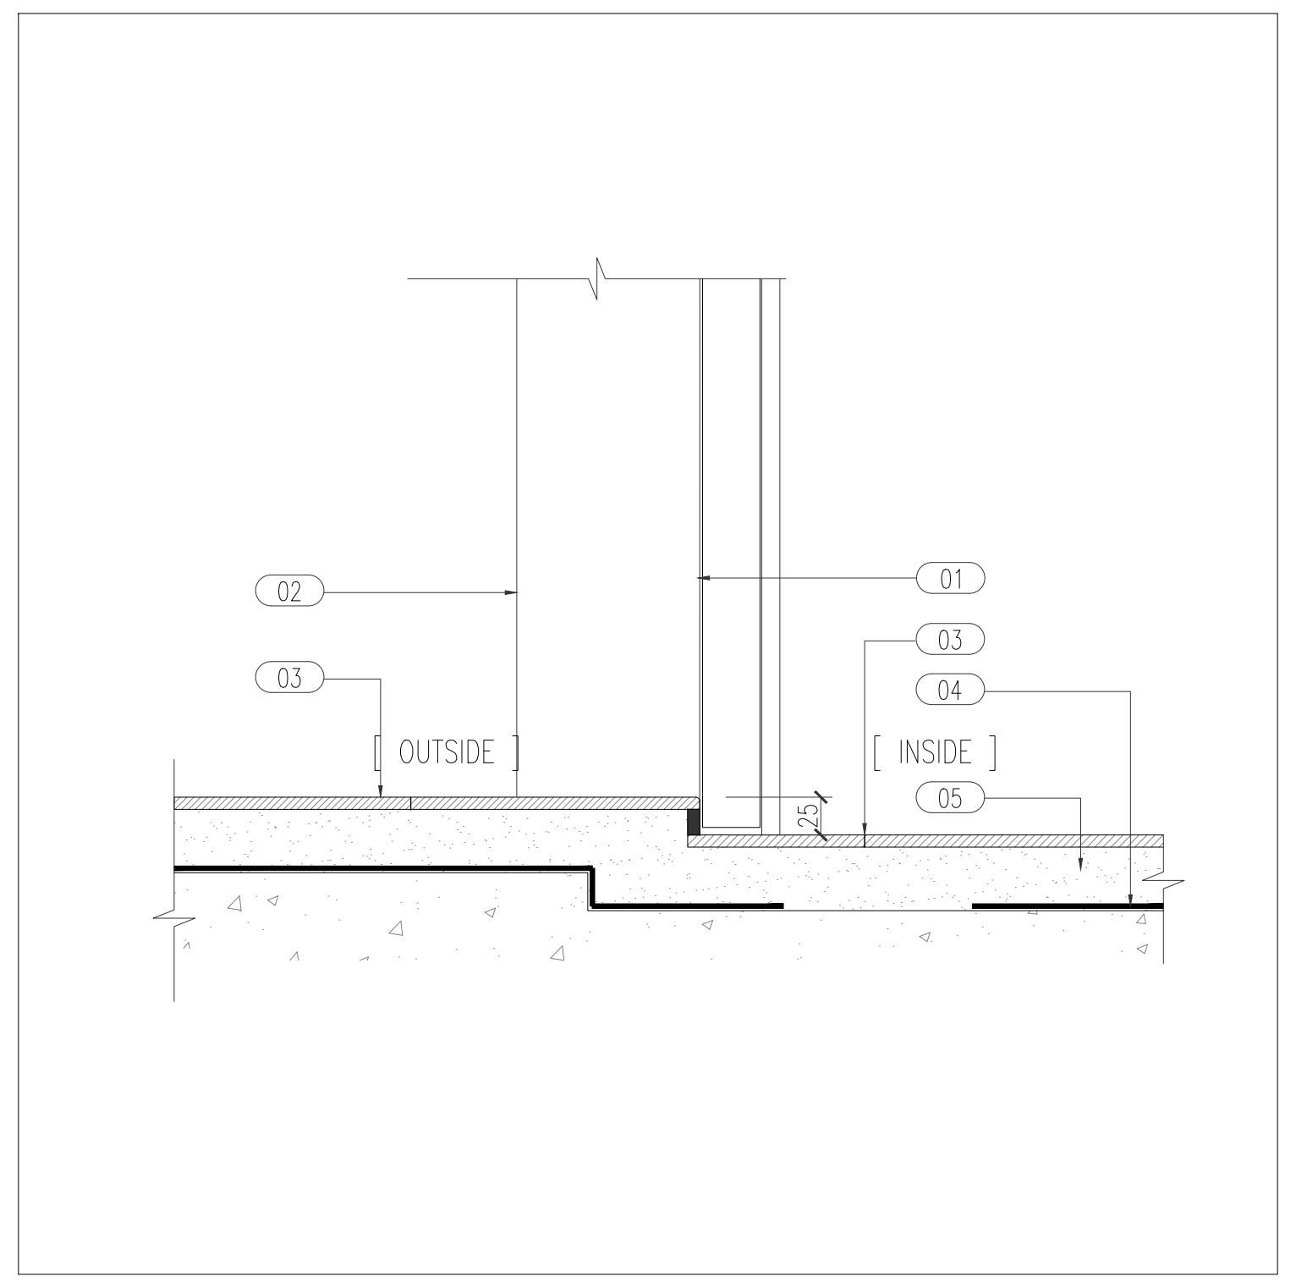

10 THRESHOLD @ TOILET / CHANGING ROOM
SCALE 1 : 5

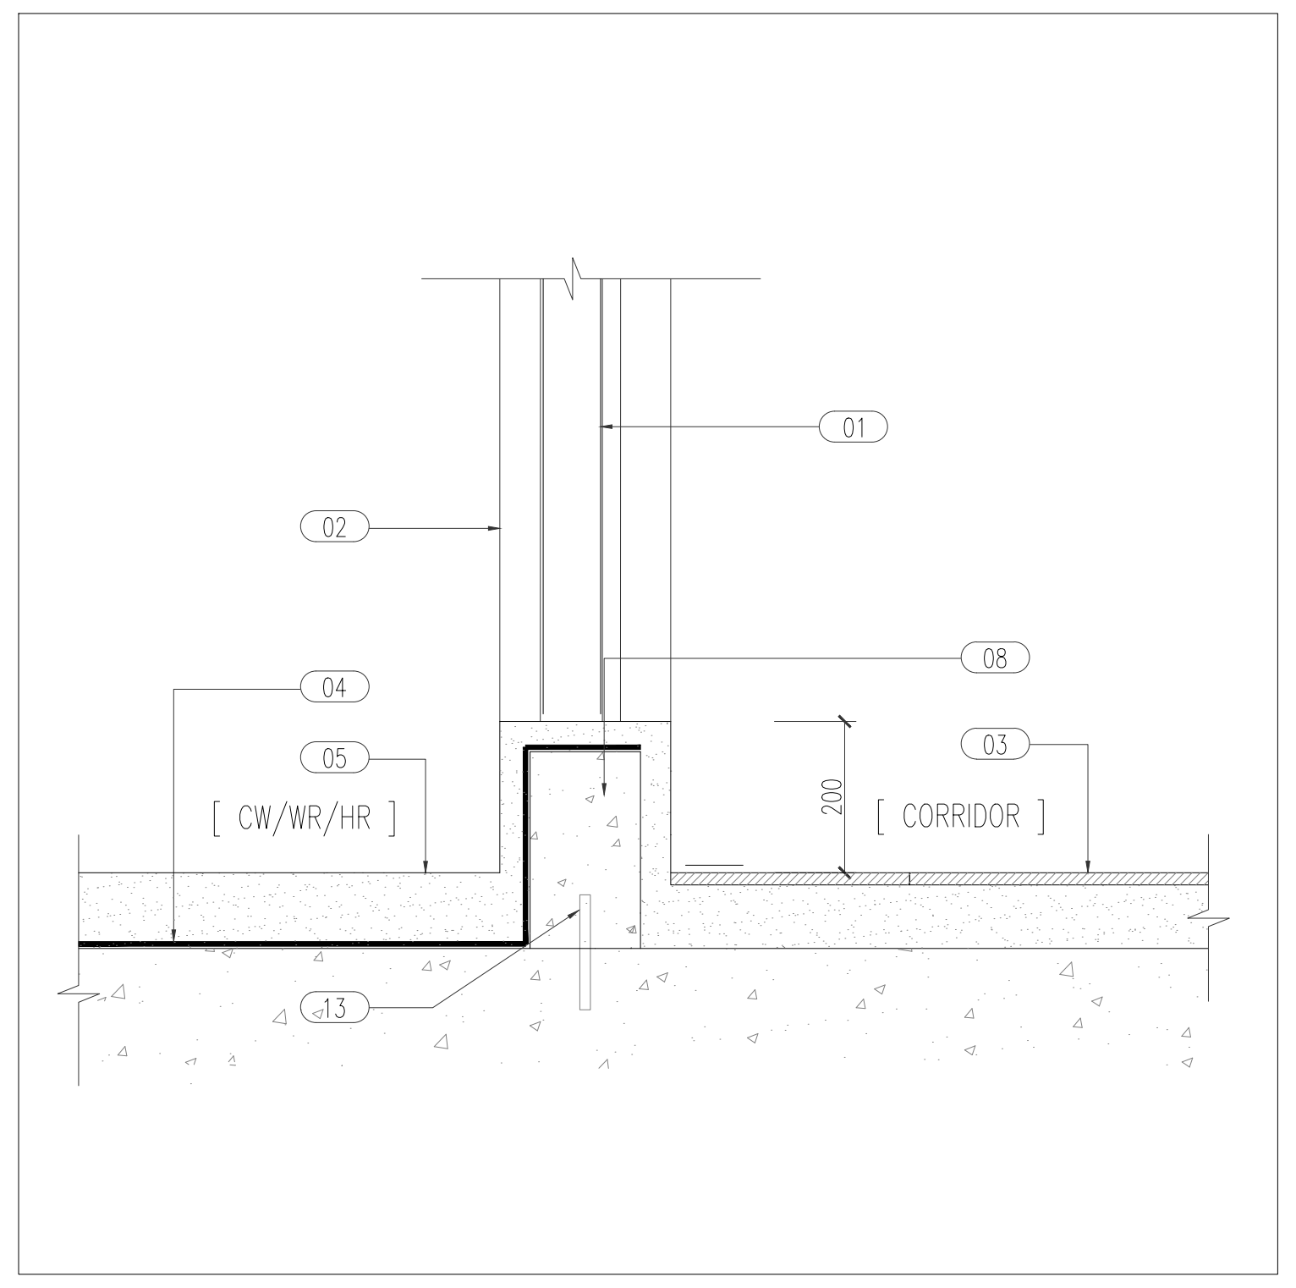

11 TYPICAL UPSTAND KERB DETAIL
SCALE 1 :5

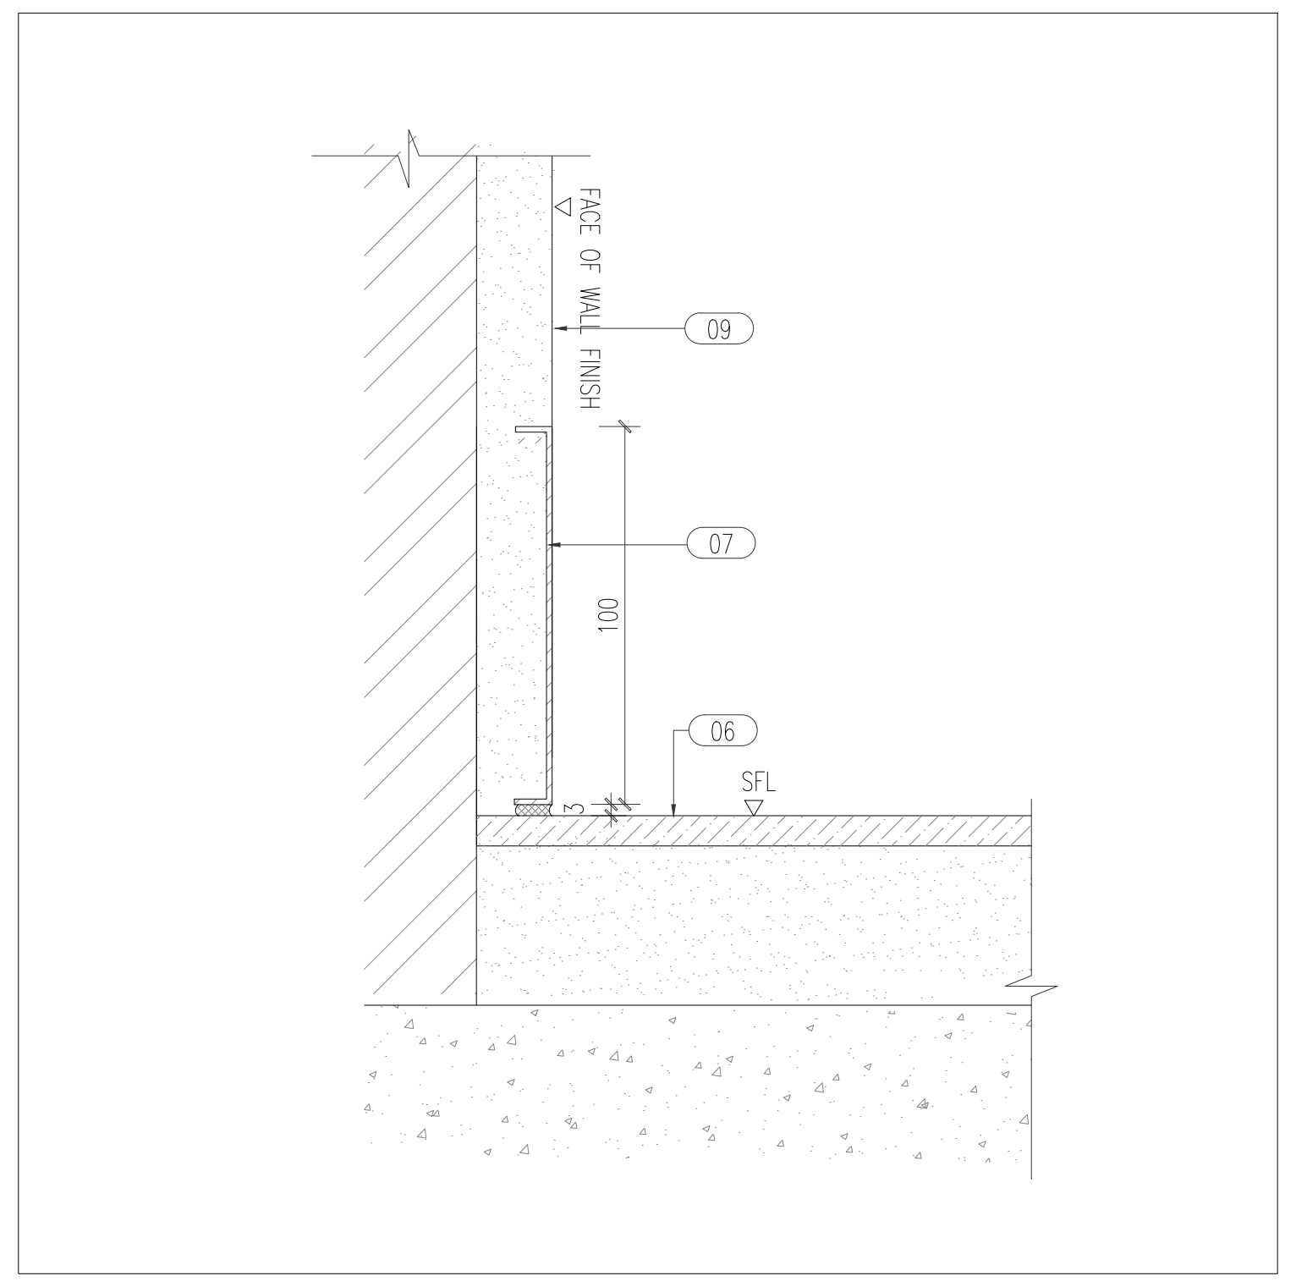

12 TYPICAL SKIRTING DETAIL
SCALE 1 : 2
(CORRESPONDING TO BASEBOARD FINISH -- B-2)

FLOOR DETAIL LEGEND :

01	DOTTED LINES INDICATE POSITION OF DOOR
02	DOOR JAMB TO DETAIL
03	SELECTED TILES REF. TO FINISHES SCHEDULE
04	SELECTED WATERPROOFING (REFER TO WATERPROOFING DETAILS & ARCHITECTURAL SPEC.S)
05	CEMENT RENDER/FLOOR HARDENER TO FLOOR FINISHES SCHEDULE
06	CONCRETE SCREED + EPOXY FLOORING
07	10mm THK STAINLESS STEEL
08	CONC. UPSTAND/KERB
09	PLASTER/SKIM COAT/SPRAY TILE FINISHED
10	100MM HIGH SKIRTING TO MATCH FLOOR TILE SELECTION

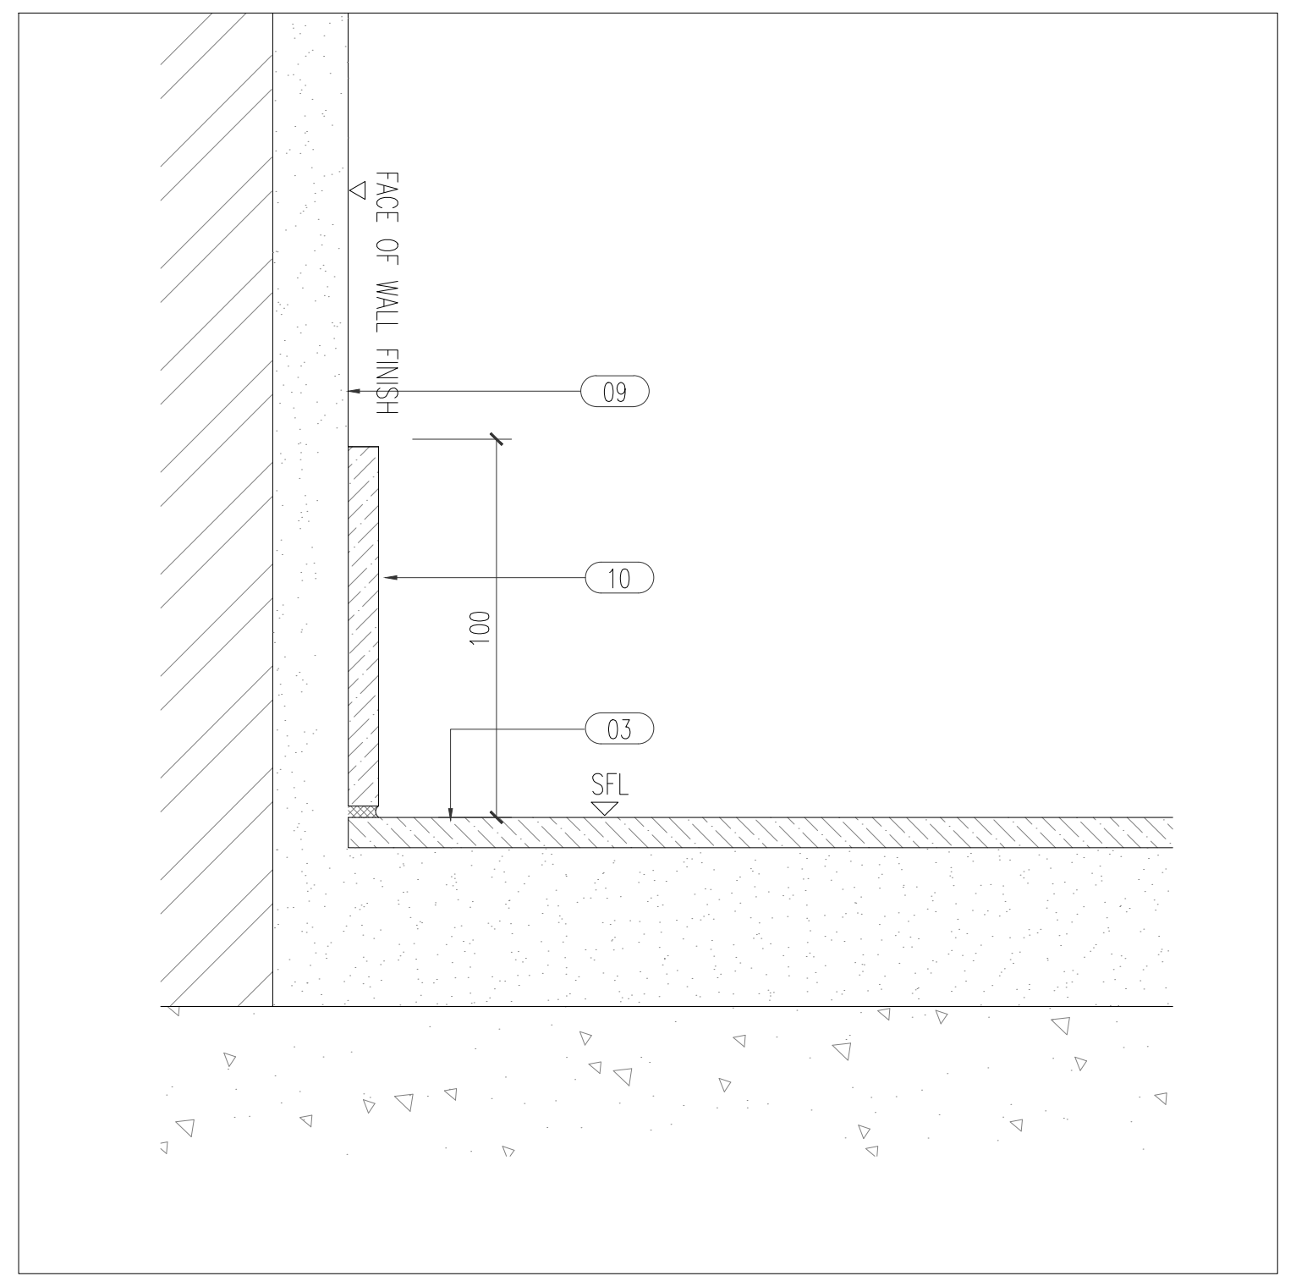

13 TYPICAL TILE SKIRTING DETAIL @ APARTMENT
SCALE 1 : 2
(CORRESPONDING TO BASEBOARD FINISH -- B-3)

CLIENT :

GULF EDGE DC 01

87 Wireless Road, M Thai Tower 11th. Floor, All Seasons Place, Lumpini,
Pathumwan, Bangkok 10330, Thailand

CONTRACTOR :

华西发展(泰国)有限公司
บริษัท หัวซือ ดีเวลลอปเม้นต์ (ประเทศไทย) จำกัด
HUASHI DEVELOPMENT CO.,LTD
No. 202, Room No. 1403, 14/F, Le Concorde Building,
Ratchadapisek Road, Huaykhwang Sub-District,
Huaykhwang District, Bangkok Metropolitan 10310.

CONSULTANT :

ARbay
บริษัท เอ อาร์ เบย์ จำกัด
ARbay Company Limited
31 st Floor Bangkok Insurance Building
25 South Sathorn road Thungmahamek
Sathorn Bangkok 10120 THAILAND
T +66 (0) 2286 8199
F +66 (0) 2286 2863
info@arbay.co.th

CONSULTANT :

Qbic Engineers & Architects Co.,Ltd.
8 Soi KALONG 4 SANAMBINNAM ROAD,
THASAI SUB-DISTRICT, MUANG NONTHABURI DISTRICT
, NONTHABURI.
Tel 662-950-4374
Fax 662-580-3231
E-Mail : qbic@qbic.co.th, www.qbic.co.th
QBIC ENGINEERS AND ARCHITECTS CO.,LTD.

CONSULTANT :

MITR
MITR TECHNICAL CONSULTANT CO.,LTD.
1168/8 12th FLOOR, LUMPINI TOWER BUILDING,
RAMA IV RD., THUNGMAHAMEK, SATHORN, BANGKOK 10120, THAILAND
TEL : 0-2679-9079-84
FAX : 0-2679-9085 E-mail: mitr_dd@mitr.com

Architect : SIGNATURE
ประกิต พนานุรัตน์ วสถ. 580
ที่อยู่
251/1 ถ.จารุเมือง แขวงรองเมือง เขตปทุมวัน
กรุงเทพมหานคร โทรศัพท์ 02-286-8199

Structural Engineer : SIGNATURE
วิศวกรผู้ออกแบบโครงสร้าง
ณัฐสม สงวนวงษ์ วย 1423
ที่อยู่
2/1 ซ.รามคำแหง 150 ถ.รามคำแหง
แขวง สะพานสูง เขต สะพานสูง กทม. 10240

Structural Inspector : SIGNATURE
วิศวกรผู้ตรวจสอบโครงสร้าง
โกมล จุฑาภัทร วย 964
ที่อยู่
24/18 ซ.นวมินทร์ 129 ถ. นวมินทร์
แขวง นวลจันทร์ เขต บึงกุ่ม กทม. 10230

Electrical Engineer : SIGNATURE
วิศวกรผู้ออกแบบระบบไฟฟ้ากำลัง
นายสุภัทร บูรณวิทย์ วฟก.1265
ที่อยู่
21 ซอยทานสัมฤทธิ์ 13
ตำบลท่าทราย อ.เมืองนนทบุรี จ.นนทบุรี 11000

Mechanical Engineer : SIGNATURE
วิศวกรผู้ออกแบบระบบเครื่องกลและปรับอากาศ
นายประสิทธิ์ โกยวสุนทร วก.1221
ประสิทธิ์
ที่อยู่
44/372 ซอยบางกระดี่ 35/1 แขวงแสมดำ
เขตบางขุนเทียน กทม. 10150

Sanitary Engineer : SIGNATURE
วิศวกรผู้ออกแบบระบบสุขาภิบาล และดับเพลิง
นายทศวรรษ สันนฤทธิ์ วส. 215
ทศวรรษ
ที่อยู่
บ้านเลขที่ 99/107 หมู่ที่ 3 ต.ศีรษะจรเข้น้อย
อ.บางเสาธง จ.สมุทรปราการ 10540

ISSUE/REVISION

REV.	DESCRIPTION	DATE
A	90% DEVELOPED	09/05/2026

PROJECT NAME :
GEDC 01
LOCATION:
Nikhom Phattana district, Rayong ,industrial estate,CPGC

BUILDING :
MAIN BUILDING

90% DEVELOPED

TITLE :
TYPICAL DETAILS B

JOB NO.	SCALE 1:50
DRAWN FLY	REF.
CHECKED LJC	DWG.NO. MPK01A-90-A-TD-002
APPROVED LXD	
DATE 2026.05.09	

NOTE : THIS PRINT IS OF A CONFIDENTIAL NATURE, IT SHALL NOT BE TRACED,PHOTOGRAPHED,PHOTOSTATED OR REPRODUCED IN ANY MANER,NOR USED FOR ANY PURPOSE WHATSOEVER EXCEPT BY WRITTEN PERMISSION