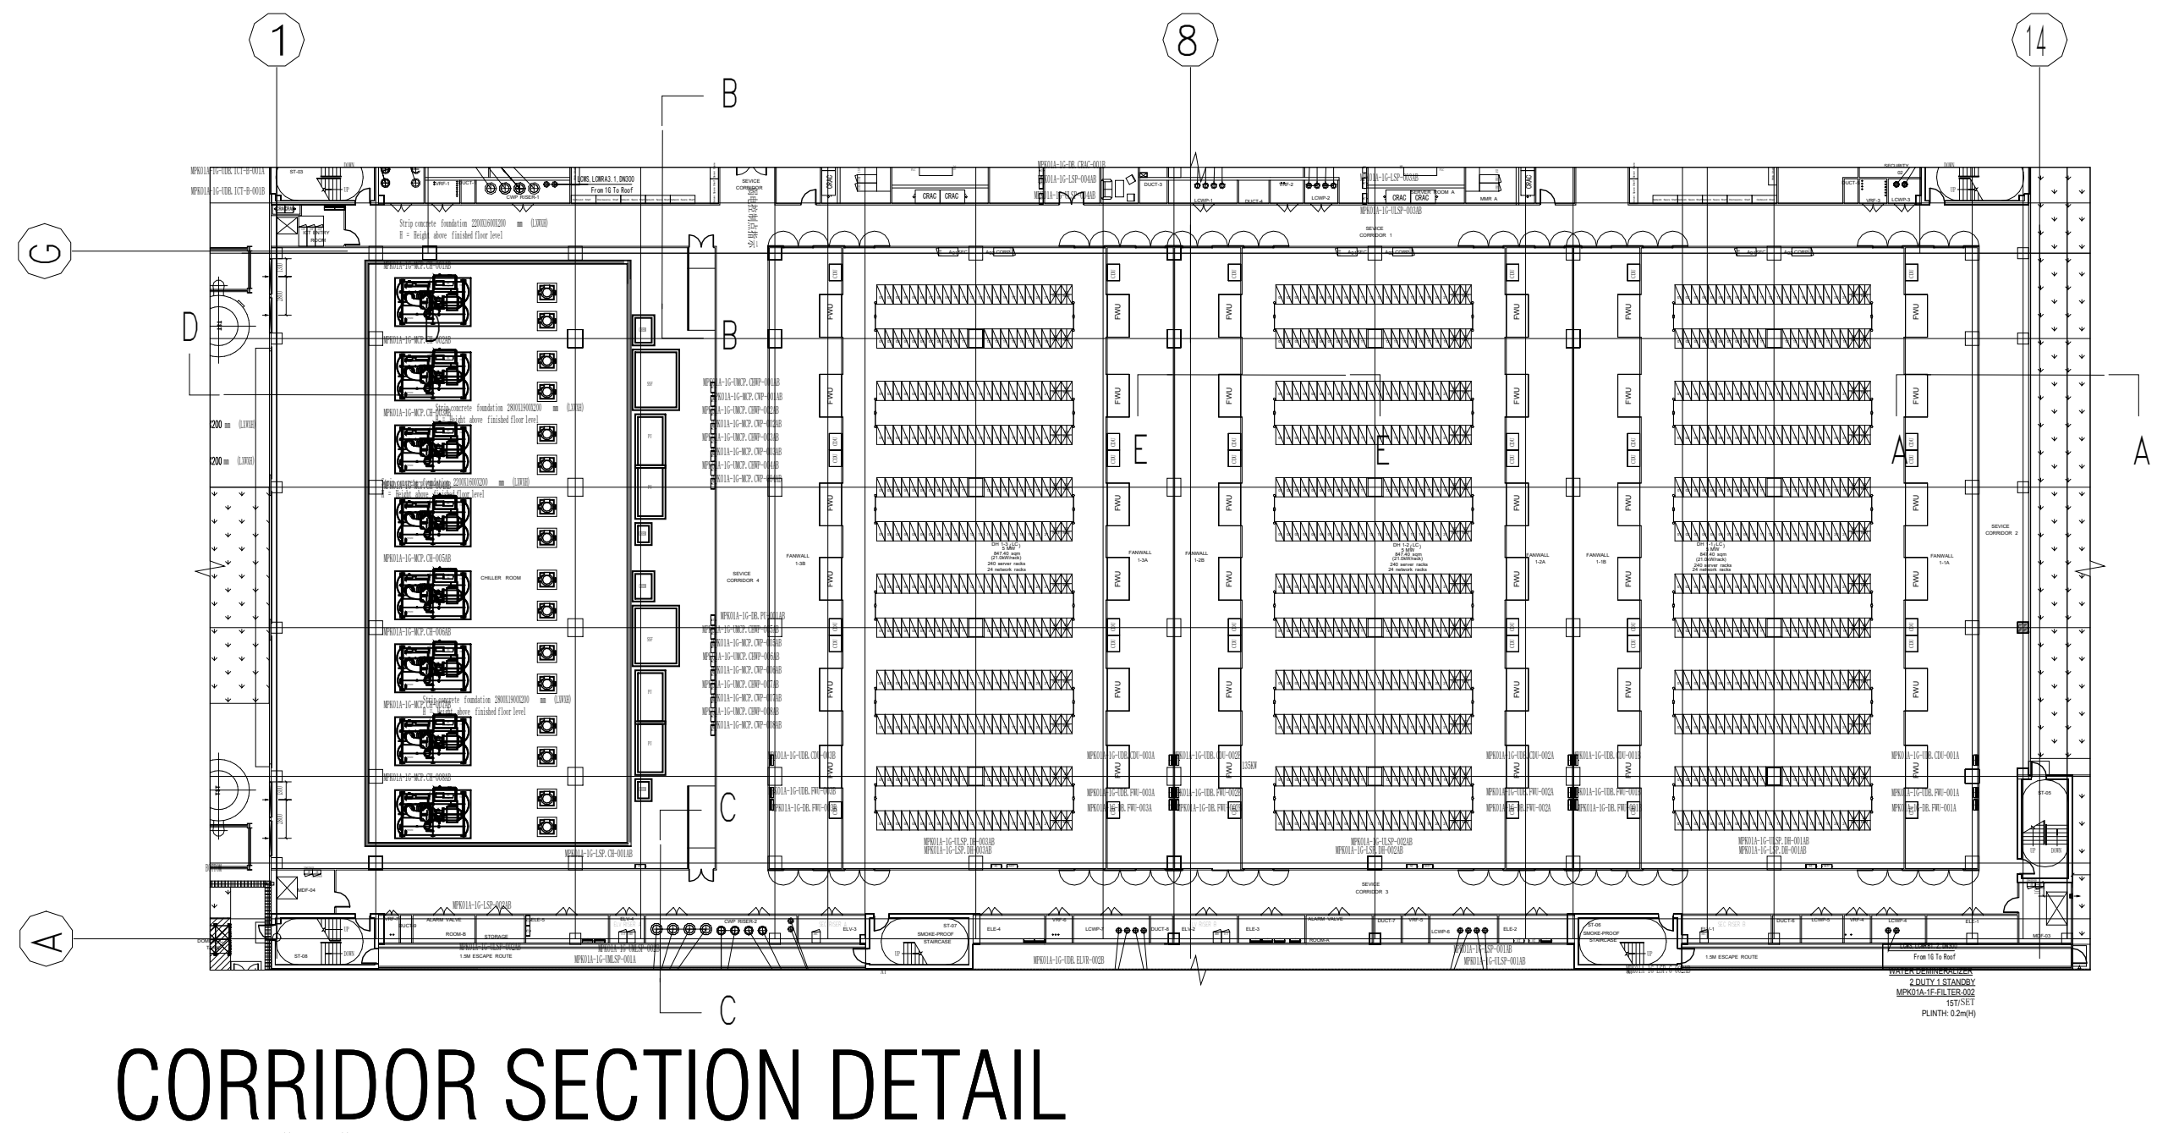

CORRIDOR SECTION DETAIL PLAN

Scale 1:75

THE "SFL" MARKED IN THE DRAWING REFERS TO THE STRUCTURAL FLOOR LEVEL, WHILE THE FINISHED FLOOR LEVEL (FFL) IS DETERMINED BASED ON FLOOR FINISHES.

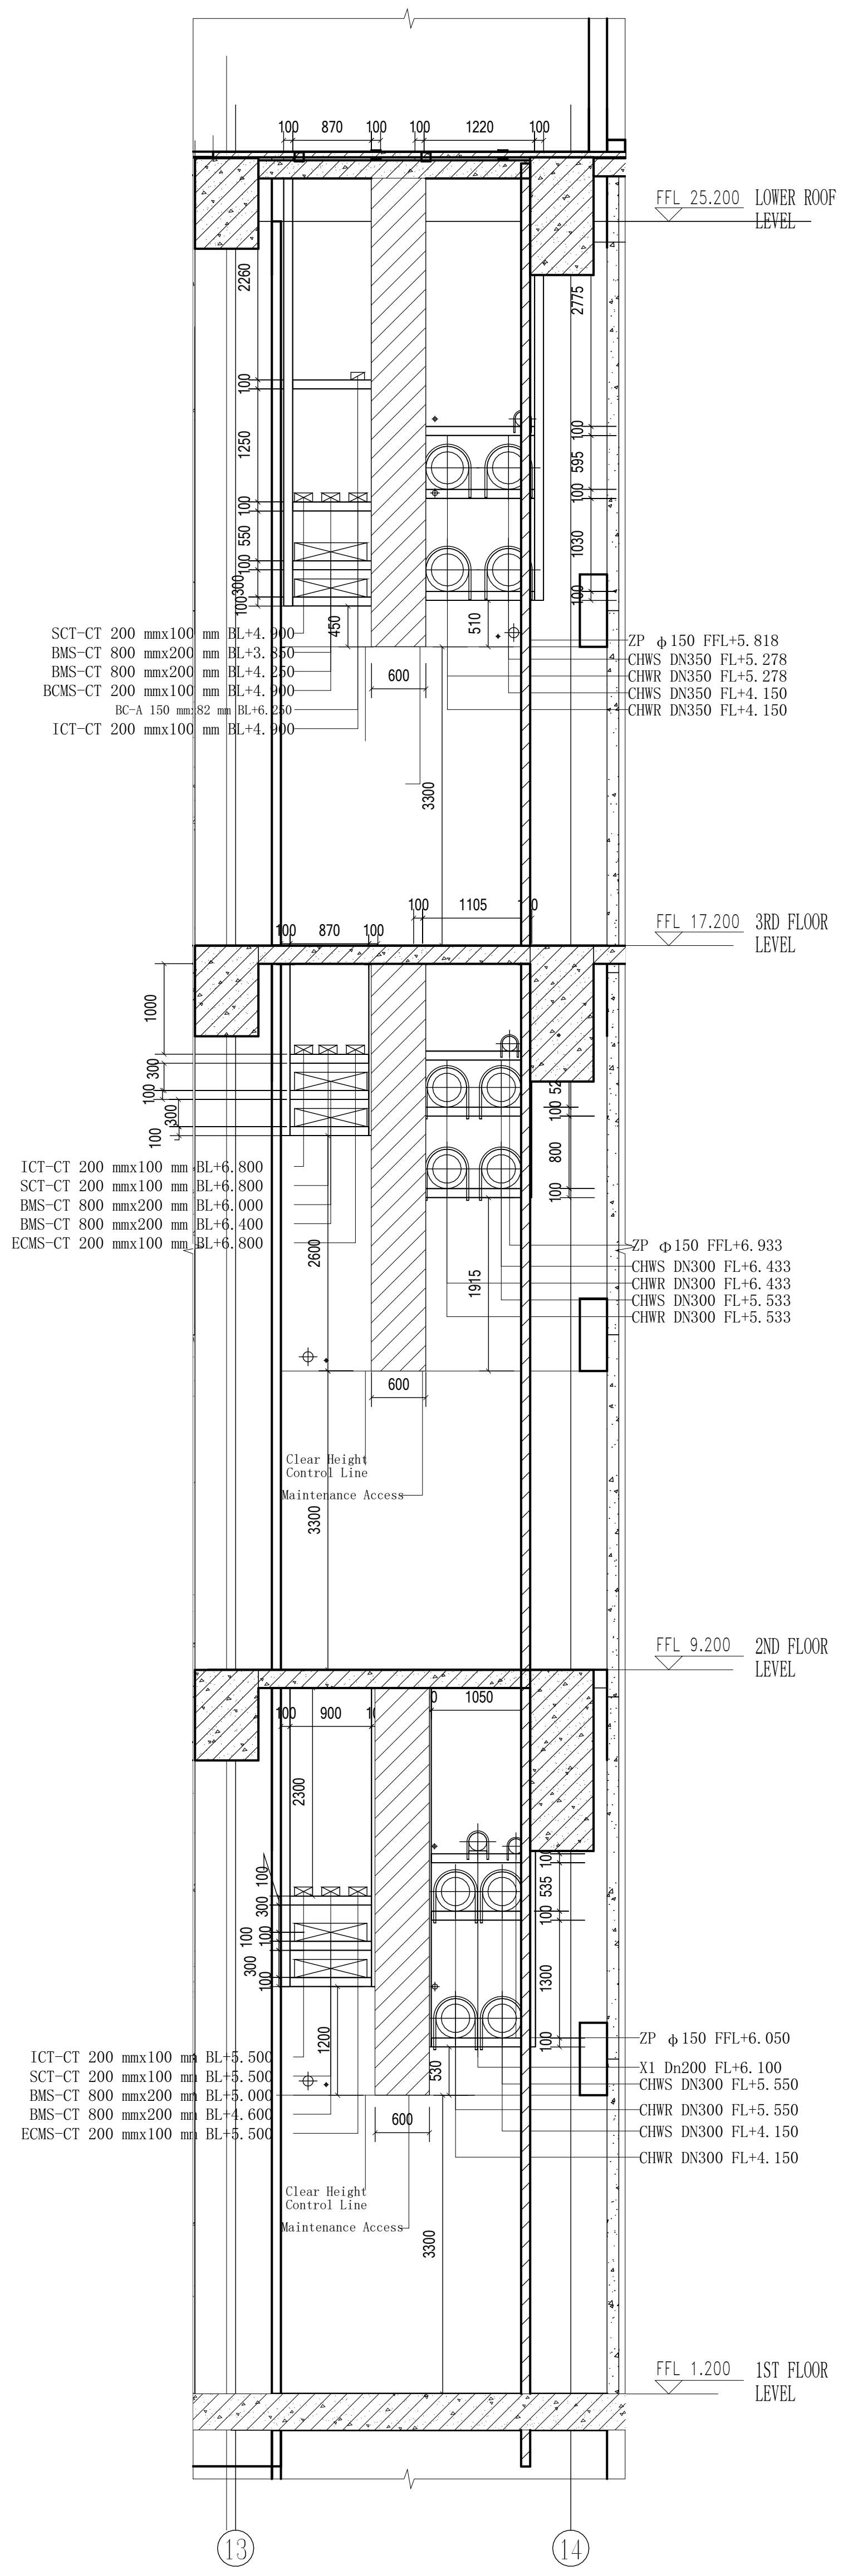
13
14
FFL 25.200 LOWER ROOF LEVEL
FFL 17.200 3RD FLOOR LEVEL
FFL 9.200 2ND FLOOR LEVEL
FFL 1.200 1ST FLOOR LEVEL
SCT-CT 200 mmx100 mm BL+4.900
BMS-CT 800 mmx200 mm BL+3.850
BMS-CT 800 mmx200 mm BL+4.250
BCMS-CT 200 mmx100 mm BL+4.900
BC-A 150 mmx82 mm BL+6.250
ICT-CT 200 mmx100 mm BL+4.900
ZP ϕ150 FFL+5.818
CHWS DN350 FL+5.278
CHWR DN350 FL+5.278
CHWS DN350 FL+4.150
CHWR DN350 FL+4.150
ICT-CT 200 mmx100 mm BL+6.800
SCT-CT 200 mmx100 mm BL+6.800
BMS-CT 800 mmx200 mm BL+6.000
BMS-CT 800 mmx200 mm BL+6.400
ECMS-CT 200 mmx100 mm BL+6.800
ZP Φ150 FFL+6.933
CHWS DN300 FL+6.433
CHWR DN300 FL+6.433
CHWS DN300 FL+5.533
CHWR DN300 FL+5.533
ICT-CT 200 mmx100 mm BL+5.500
SCT-CT 200 mmx100 mm BL+5.500
BMS-CT 800 mmx200 mm BL+5.000
BMS-CT 800 mmx200 mm BL+4.600
ECMS-CT 200 mmx100 mm BL+5.500
ZP ϕ150 FFL+6.050
X1 Dn200 FL+6.100
CHWS DN300 FL+5.550
CHWR DN300 FL+5.550
CHWS DN300 FL+4.150
CHWR DN300 FL+4.150
Clear Height Control Line
Maintenance Access
600
3300

SECTION A-A

Scale 1:50

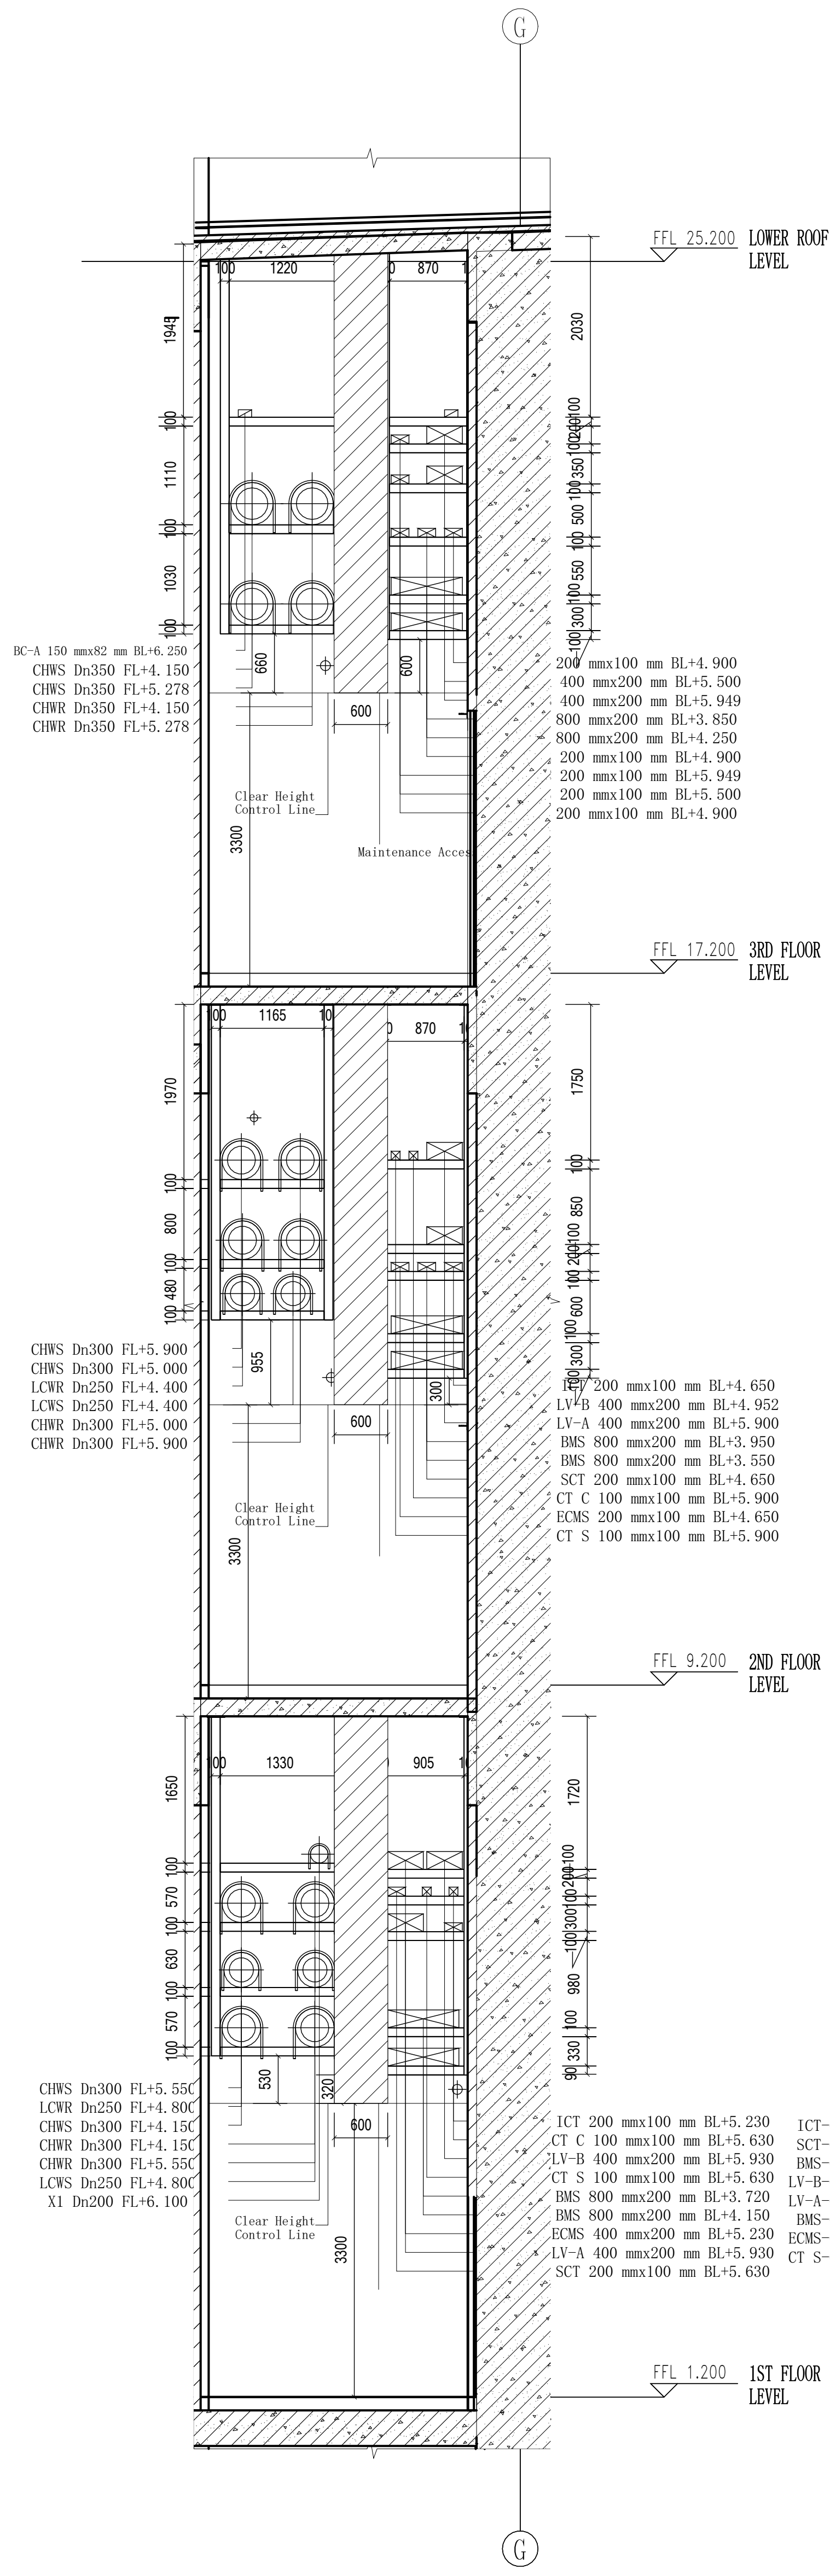
G
FFL 25.200 LOWER ROOF LEVEL
FFL 17.200 3RD FLOOR LEVEL
FFL 9.200 2ND FLOOR LEVEL
FFL 1.200 1ST FLOOR LEVEL
BC-A 150 mmx82 mm BL+6.250
CHWS Dn350 FL+4.150
CHWS Dn350 FL+5.278
CHWR Dn350 FL+4.150
CHWR Dn350 FL+5.278
200 mmx100 mm BL+4.900
400 mmx200 mm BL+5.500
400 mmx200 mm BL+5.949
800 mmx200 mm BL+3.850
800 mmx200 mm BL+4.250
200 mmx100 mm BL+4.900
200 mmx100 mm BL+5.949
200 mmx100 mm BL+5.500
200 mmx100 mm BL+4.900
CHWS Dn300 FL+5.900
CHWS Dn300 FL+5.000
LCWR Dn250 FL+4.400
LCWS Dn250 FL+4.400
CHWR Dn300 FL+5.000
CHWR Dn300 FL+5.900
ICT 200 mmx100 mm BL+4.650
LV-B 400 mmx200 mm BL+4.952
LV-A 400 mmx200 mm BL+5.900
BMS 800 mmx200 mm BL+3.950
BMS 800 mmx200 mm BL+3.550
SCT 200 mmx100 mm BL+4.650
CT C 100 mmx100 mm BL+5.900
ECMS 200 mmx100 mm BL+4.650
CT S 100 mmx100 mm BL+5.900
CHWS Dn300 FL+5.550
LCWR Dn250 FL+4.800
CHWS Dn300 FL+4.150
CHWR Dn300 FL+4.150
CHWR Dn300 FL+5.550
LCWS Dn250 FL+4.800
X1 Dn200 FL+6.100
ICT 200 mmx100 mm BL+5.230
CT C 100 mmx100 mm BL+5.630
LV-B 400 mmx200 mm BL+5.930
CT S 100 mmx100 mm BL+5.630
BMS 800 mmx200 mm BL+3.720
BMS 800 mmx200 mm BL+4.150
ECMS 400 mmx200 mm BL+5.230
LV-A 400 mmx200 mm BL+5.930
SCT 200 mmx100 mm BL+5.630
Clear Height Control Line
Maintenance Access
600
3300

SECTION B-B

Scale 1:50

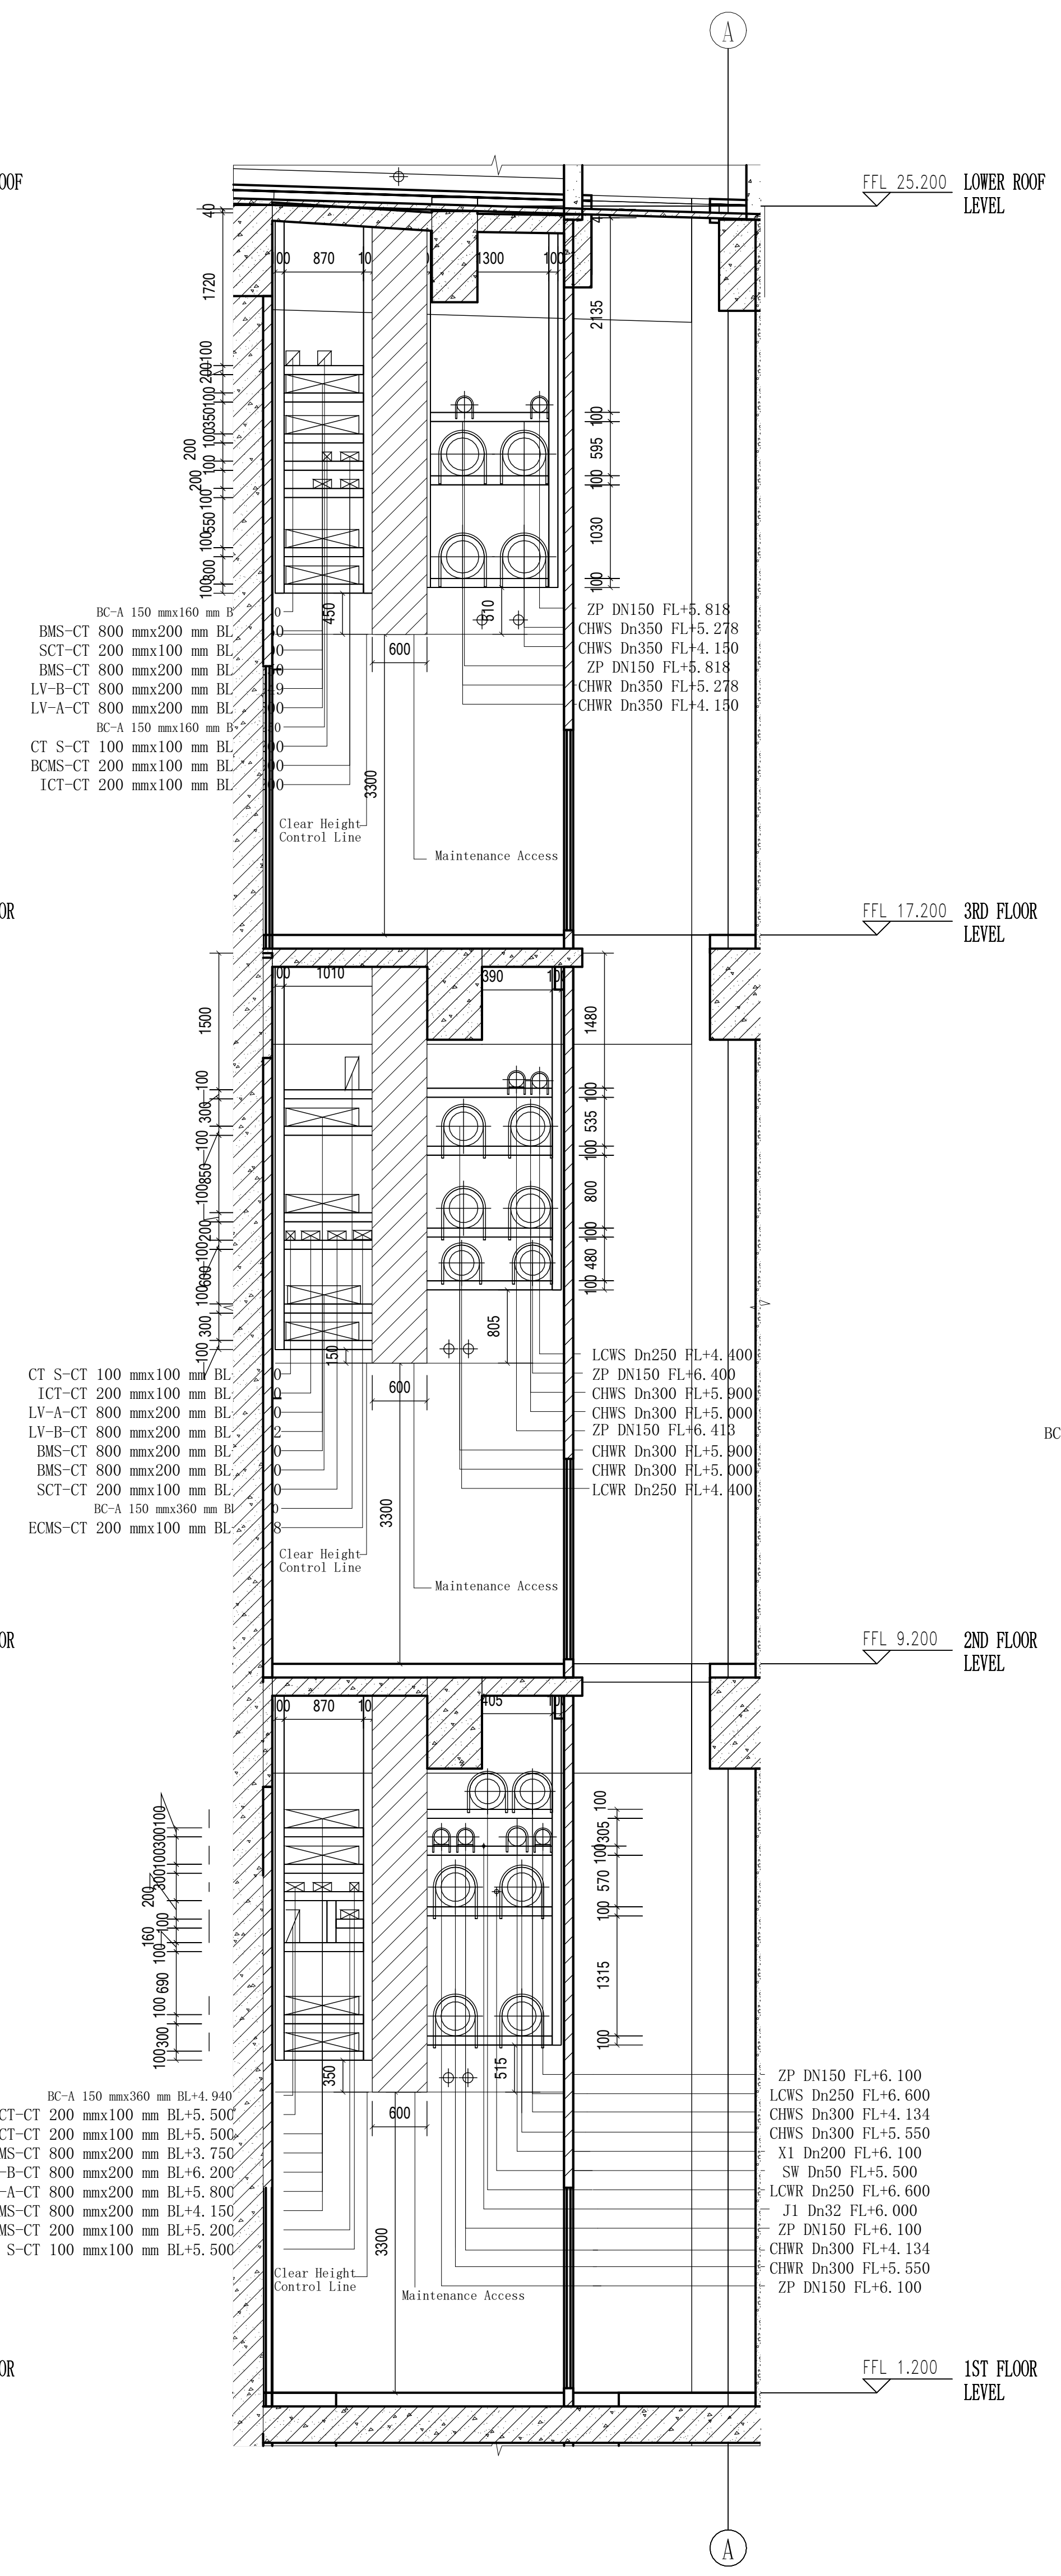

SECTION C-C

Scale 1:50

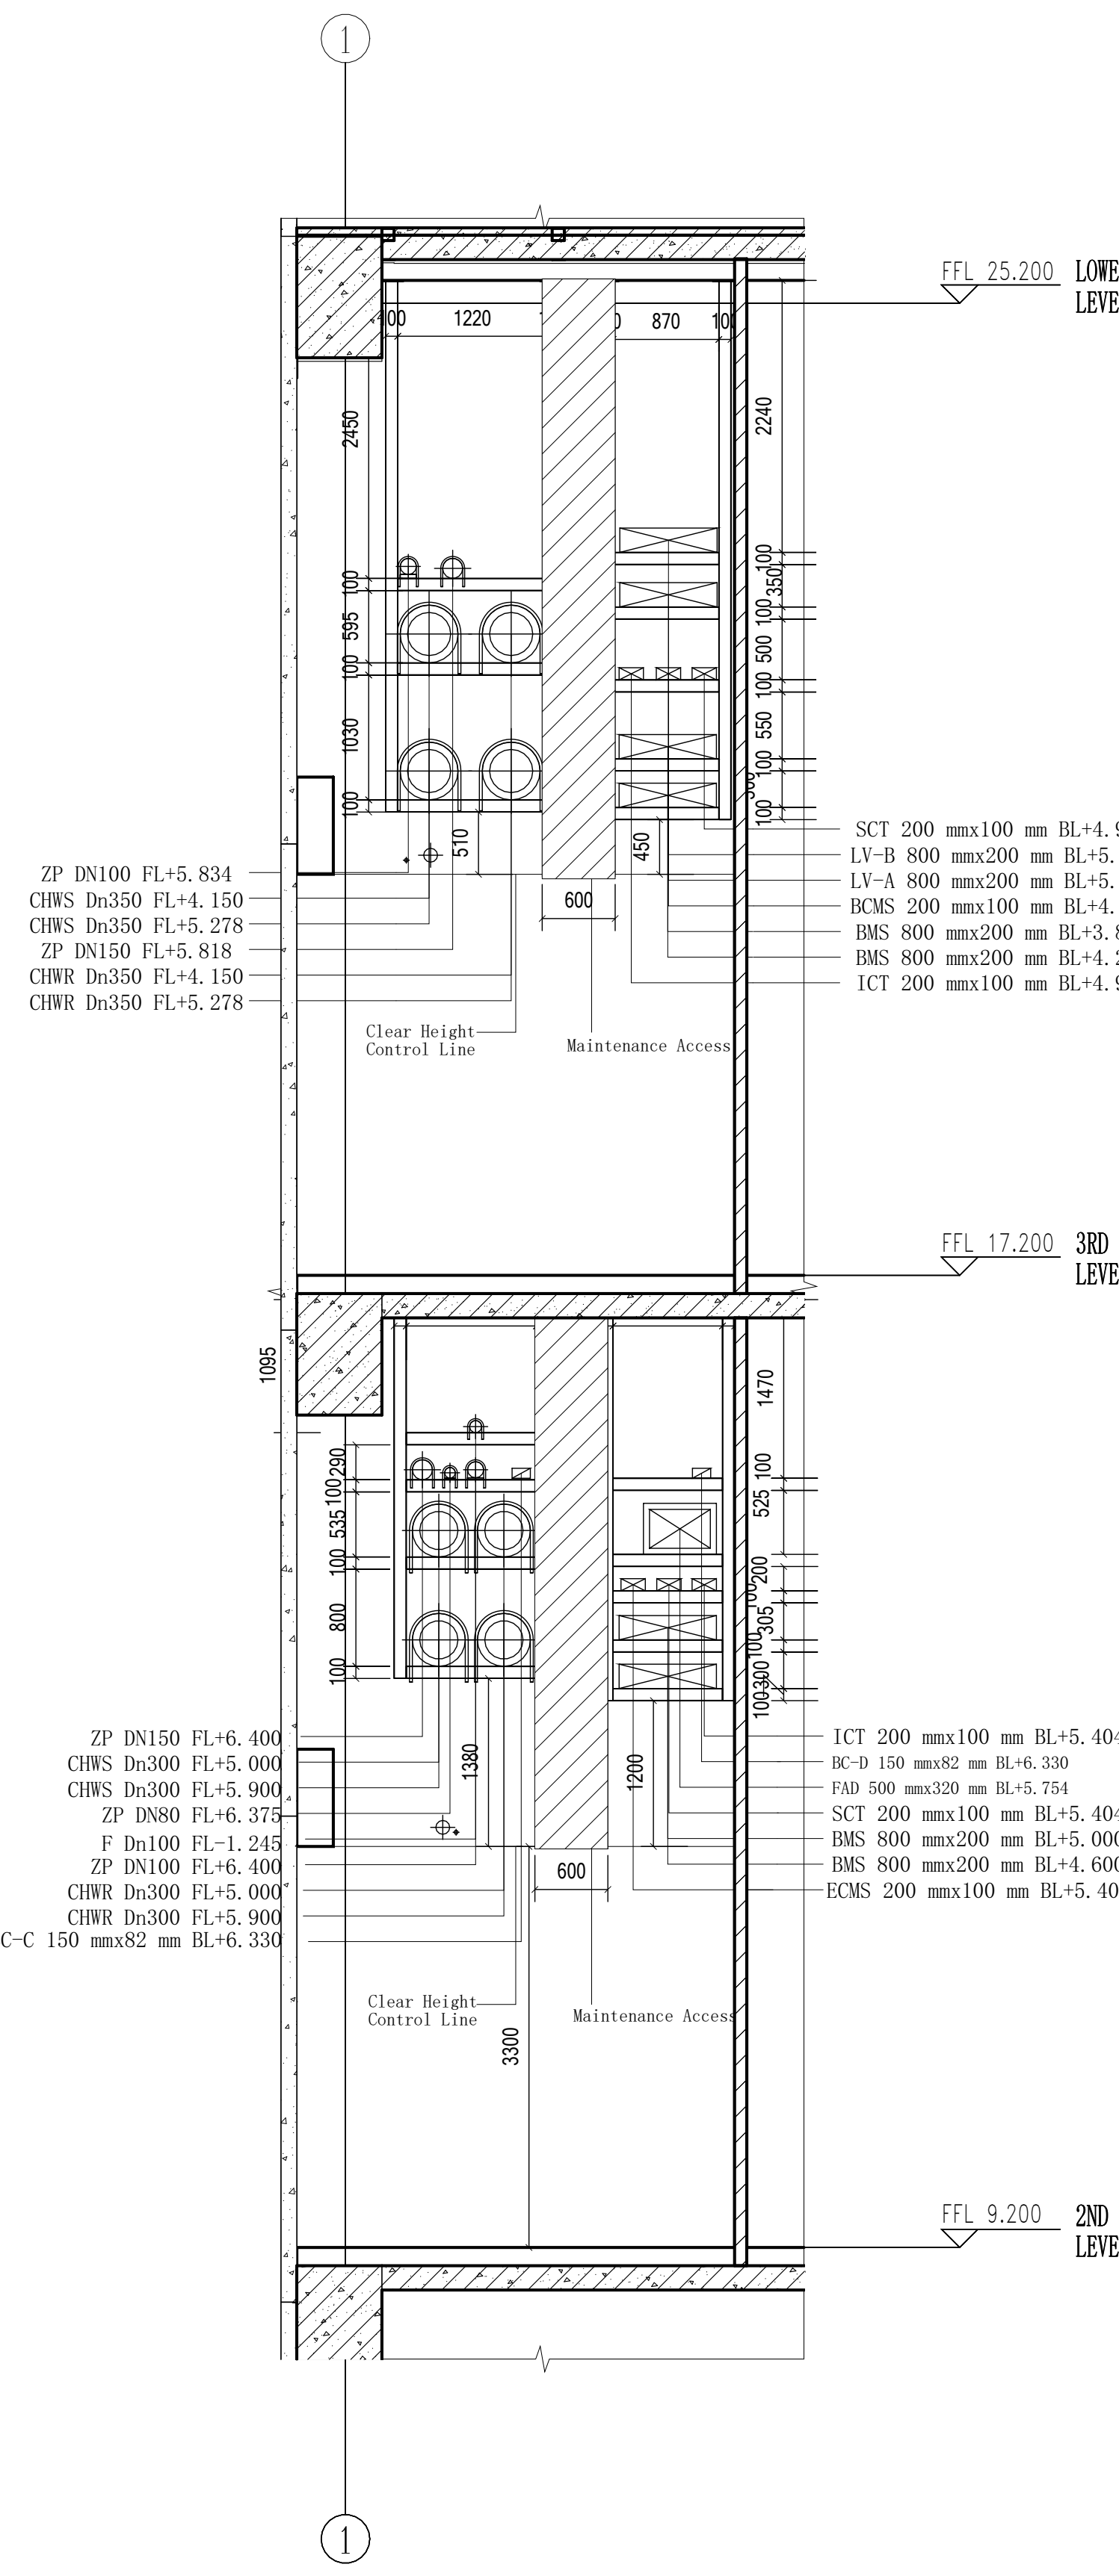
1
FFL 25.200 LOWER ROOF LEVEL
FFL 17.200 3RD FLOOR LEVEL
FFL 9.200 2ND FLOOR LEVEL
ZP DN100 FL+5.834
CHWS Dn350 FL+4.150
CHWS Dn350 FL+5.278
ZP DN150 FL+5.818
CHWR Dn350 FL+4.150
CHWR Dn350 FL+5.278
SCT 200 mmx100 mm BL+4.900
LV-B 800 mmx200 mm BL+5.949
LV-A 800 mmx200 mm BL+5.500
BCMS 200 mmx100 mm BL+4.900
BMS 800 mmx200 mm BL+3.850
BMS 800 mmx200 mm BL+4.250
ICT 200 mmx100 mm BL+4.900
ZP DN150 FL+6.400
CHWS Dn300 FL+5.000
CHWS Dn300 FL+5.900
ZP DN80 FL+6.375
F Dn100 FL-1.245
ZP DN100 FL+6.400
CHWR Dn300 FL+5.000
CHWR Dn300 FL+5.900
BC-C 150 mmx82 mm BL+6.330
ICT 200 mmx100 mm BL+5.404
BC-D 150 mmx82 mm BL+6.330
FAD 500 mmx320 mm BL+5.754
SCT 200 mmx100 mm BL+5.404
BMS 800 mmx200 mm BL+5.000
BMS 800 mmx200 mm BL+4.600
ECMS 200 mmx100 mm BL+5.404
Clear Height Control Line
Maintenance Access
600
3300

SECTION D-D

Scale 1:50

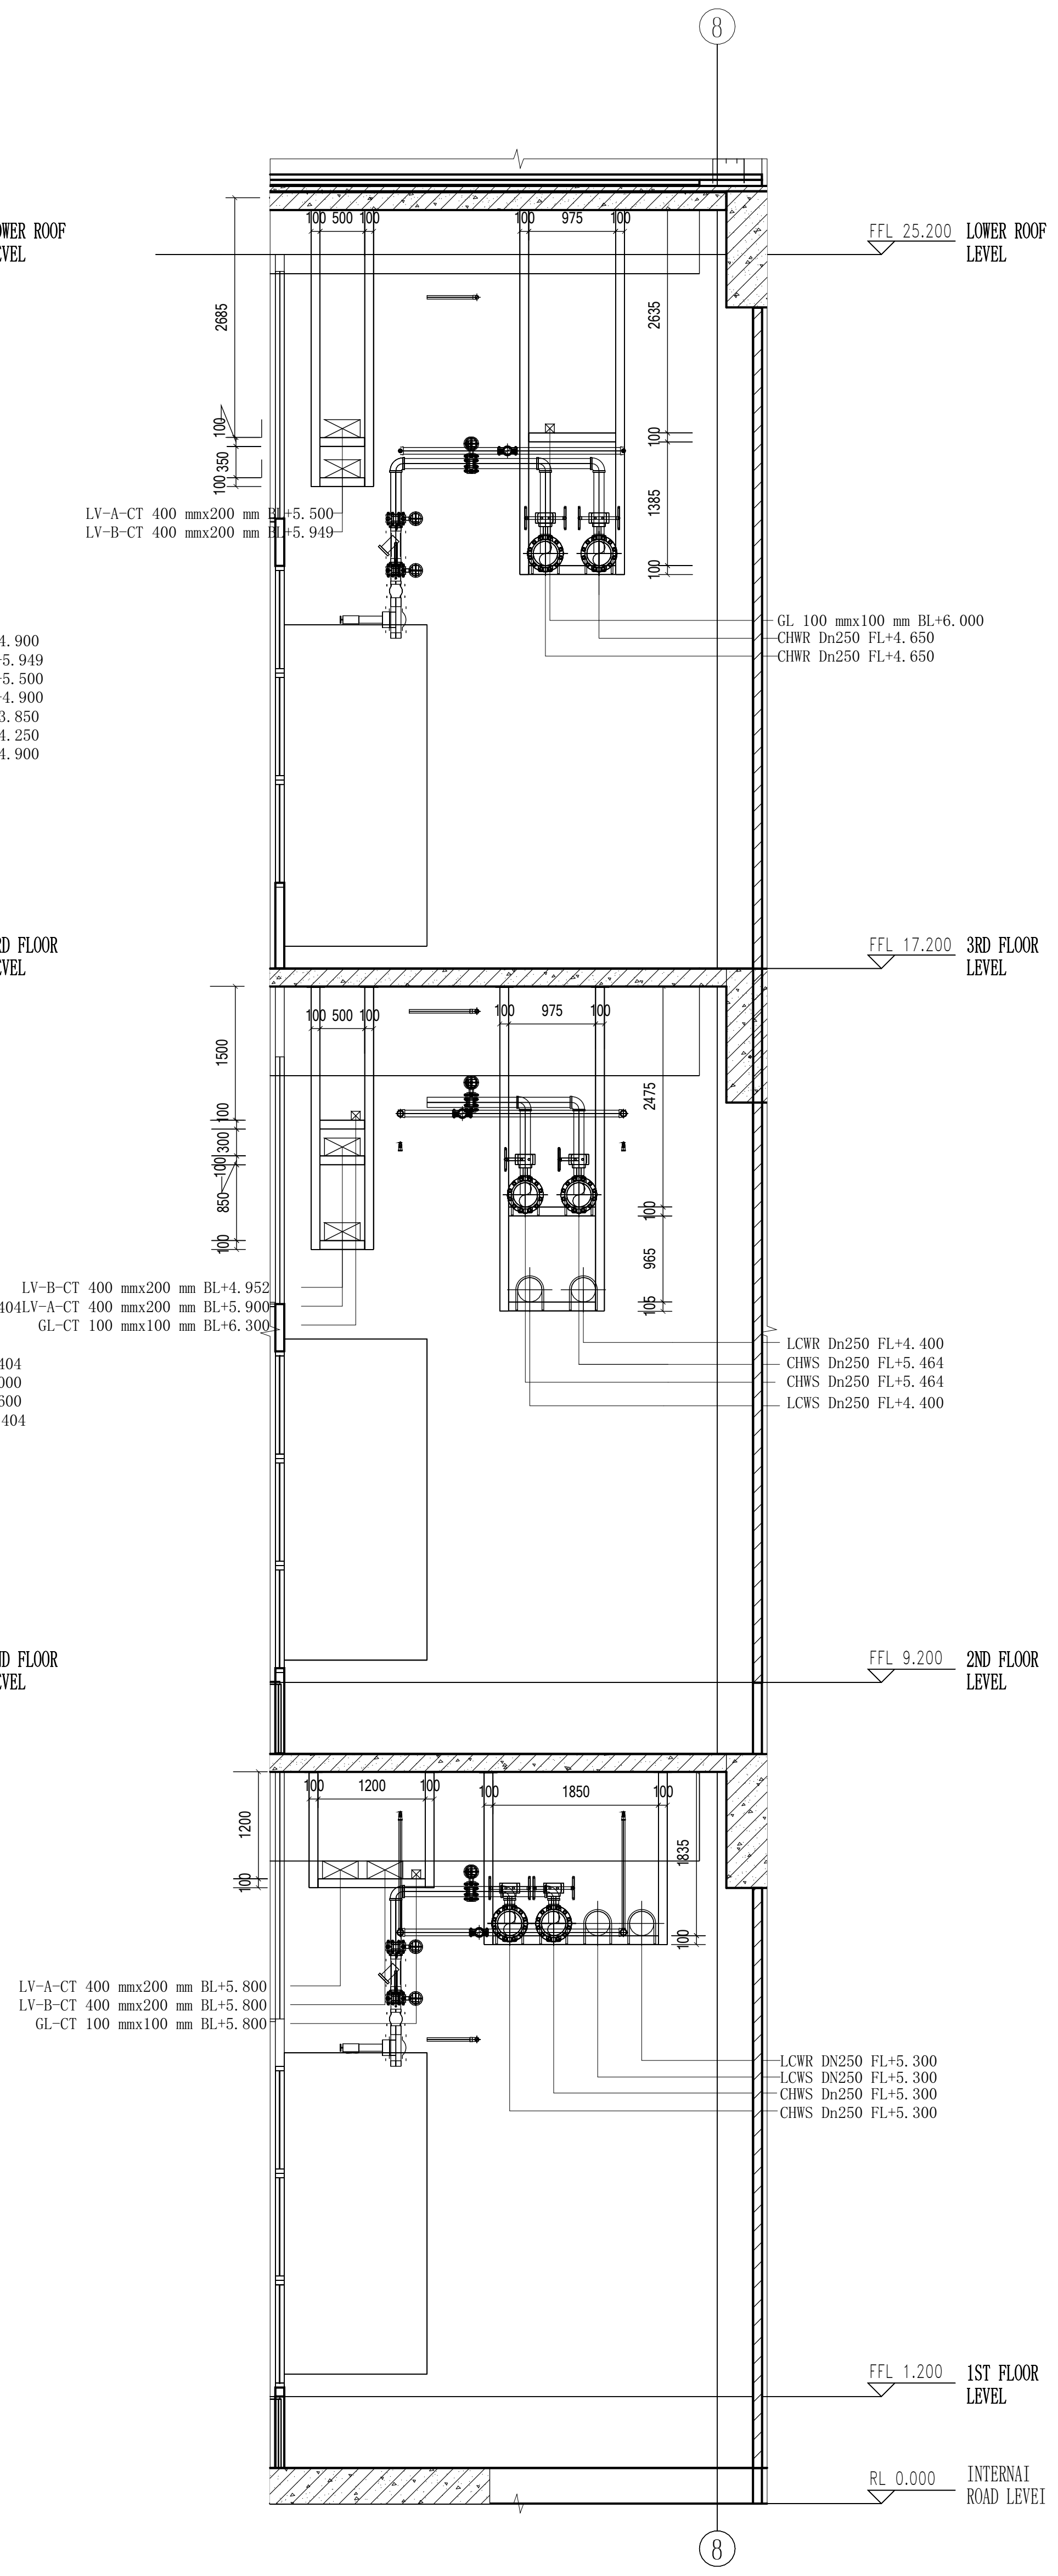
8
FFL 25.200 LOWER ROOF LEVEL
FFL 17.200 3RD FLOOR LEVEL
FFL 9.200 2ND FLOOR LEVEL
FFL 1.200 1ST FLOOR LEVEL
RL 0.000 INTERNAL ROAD LEVEL
LV-A-CT 400 mmx200 mm BL+5.500
LV-B-CT 400 mmx200 mm BL+5.949
GL 100 mmx100 mm BL+6.000
CHWR Dn250 FL+4.650
CHWR Dn250 FL+4.650
LV-B-CT 400 mmx200 mm BL+4.952
LV-A-CT 400 mmx200 mm BL+5.900
GL-CT 100 mmx100 mm BL+6.300
LCWR Dn250 FL+4.400
CHWS Dn250 FL+5.464
CHWS Dn250 FL+5.464
LCWS Dn250 FL+4.400
LV-A-CT 400 mmx200 mm BL+5.800
LV-B-CT 400 mmx200 mm BL+5.800
GL-CT 100 mmx100 mm BL+6.300
LCWR Dn250 FL+5.300
LCWS DN250 FL+5.300
CHWS Dn250 FL+5.300
CHWS Dn250 FL+5.300

SECTION E-E

Scale 1:50

NOTE :THIS PRINT IS OF A CONFIDENTIAL NATURE, IT SHALL NOT BE TRACED,PHOTOGRAPHED,PHOTOSTATED OR REPRODUCED IN ANY MANER,NOR USED FOR ANY PURPOSE WHATSOEVER EXCEPT BY WRITTEN PERMISSION

CLIENT :

GULF EDGE DC 01

87 Wireless Road, M Thai Tower 11th. Floor, All Seasons Place, Lumpini, Pathumwan, Bangkok 10330, Thailand

CONTRACTOR :

华西发展(泰国)有限公司
บริษัท หัวซือ ดีเวลลอปเม้นต์ (ประเทศไทย) จำกัด
HUASHI DEVELOPMENT CO.,LTD
No. 202, Room No. 1403, 14/F, Le Concorde Building,
Ratchadapisek Road, Huaykhwang Sub-District,
Huaykhwang District, Bangkok Metropolitan 10310.

CONSULTANT :

ARbay
บริษัท เอ อาร์ เบย์ จำกัด
ARbay Company Limited
31 st Floor Bangkok Insurance Building
25 South Sathorn road Thungmahamek
Sathorn Bangkok 10120 THAILAND
T +66 (0) 2286 8199
F +66 (0) 2286 2863
info@arbay.co.th

CONSULTANT :

Qbic Engineers & Architects Co.,Ltd.
8 Soi KALONG 4 SANAMBINNAM ROAD,
THASAI SUB-DISTRICT, MUANG NONTHABURI DISTRICT
, NONTHABURI.
Tel 662-950-4374
Fax 662-580-3231
E-Mail : qbic@qbic.co.th, www.qbic.co.th
QBIC ENGINEERS AND ARCHITECTS CO.,LTD.

CONSULTANT :

MITR
MITR TECHNICAL CONSULTANT CO.,LTD.
1168/8 12th FLOOR, LUMPINI TOWER BUILDING,
RAMA IV RD., THUNGMAHAMEK, SATHORN, BANGKOK 10120, THAILAND
TEL : 0-2679-9079-84
FAX : 0-2679-9085 E-mail: mitr_dd@mitr.com

Architect :	SIGNATURE
ประกิต พนานุรัตน์ วสถ. 580 ที่อยู่ 251/1 ถ.จารุเมือง แขวงรองเมือง เขตปทุมวัน กรุงเทพมหานคร โทรศัพท์ 02-286-8199	
Structural Engineer :	SIGNATURE
วิศวกรผู้ออกแบบโครงสร้าง	
ณัฐสม สงวนวงษ์ วย 1423 ที่อยู่ 2/1 ซ.รามคำแหง 150 ถ.รามคำแหง แขวง สะพานสูง เขต สะพานสูง กทม. 10240	ณัฐสม สงวนวงษ์
Structural Inspector :	SIGNATURE
วิศวกรผู้ตรวจสอบโครงสร้าง	
โกมล จุฑาภัทร วย 964 ที่อยู่ 24/18 ซ.นวมินทร์ 129 ถ. นวมินทร์ แขวง นวลจันทร์ เขต บึงกุ่ม กทม. 10230	
Electrical Engineer :	SIGNATURE
วิศวกรผู้ออกแบบระบบไฟฟ้ากำลัง	
นายสุภัทร บูรณวิทย์ วฟก.1265 ที่อยู่ 21 ซอยทานสัมฤทธิ 13 ตำบลท่าทราย อ.เมืองนนทบุรี จ.นนทบุรี 11000	
Mechanical Engineer :	SIGNATURE
วิศวกรผู้ออกแบบระบบเครื่องกลและปรับอากาศ	
นายประสิทธิ์ เกียวสุนทร วก.1221 ที่อยู่ 44/372 ซอยบางกระดี 35/1 แขวงแสมดำ เขตบางขุนเทียน กทม. 10150	ประสิทธิ์
Sanitary Engineer :	SIGNATURE
วิศวกรผู้ออกแบบระบบสุขาภิบาล และดับเพลิง	
นายทศวรรษ สนันฤทธิ์ วส. 215 ที่อยู่ บ้านเลขที่ 99/107 หมู่ที่ 3 ต.ศีรษะจรเข้น้อย อ.บางเสาธง จ.สมุทรปราการ 10540	ทศวรรษ

ISSUE/REVISION

REV.	DESCRIPTION	DATE
A	90% DEVELOPED	09/05/2026

PROJECT NAME :

GEDC 01

LOCATION:
Nikhom Phattana district, Rayong ,industrial estate,CPGC

BUILDING :

90% DEVELOPED

TITLE :

ROOMDETAIL-CORRIDOR SECTION DETAIL PLAN &SECTION

JOB NO.	SCALE 作为说明
DRAWN 作者	REF.
CHECKED 审图员	DWG. NO. MPK01-90-A-CSD-001
APPROVED 审核者	
DATE 2026.05.09	