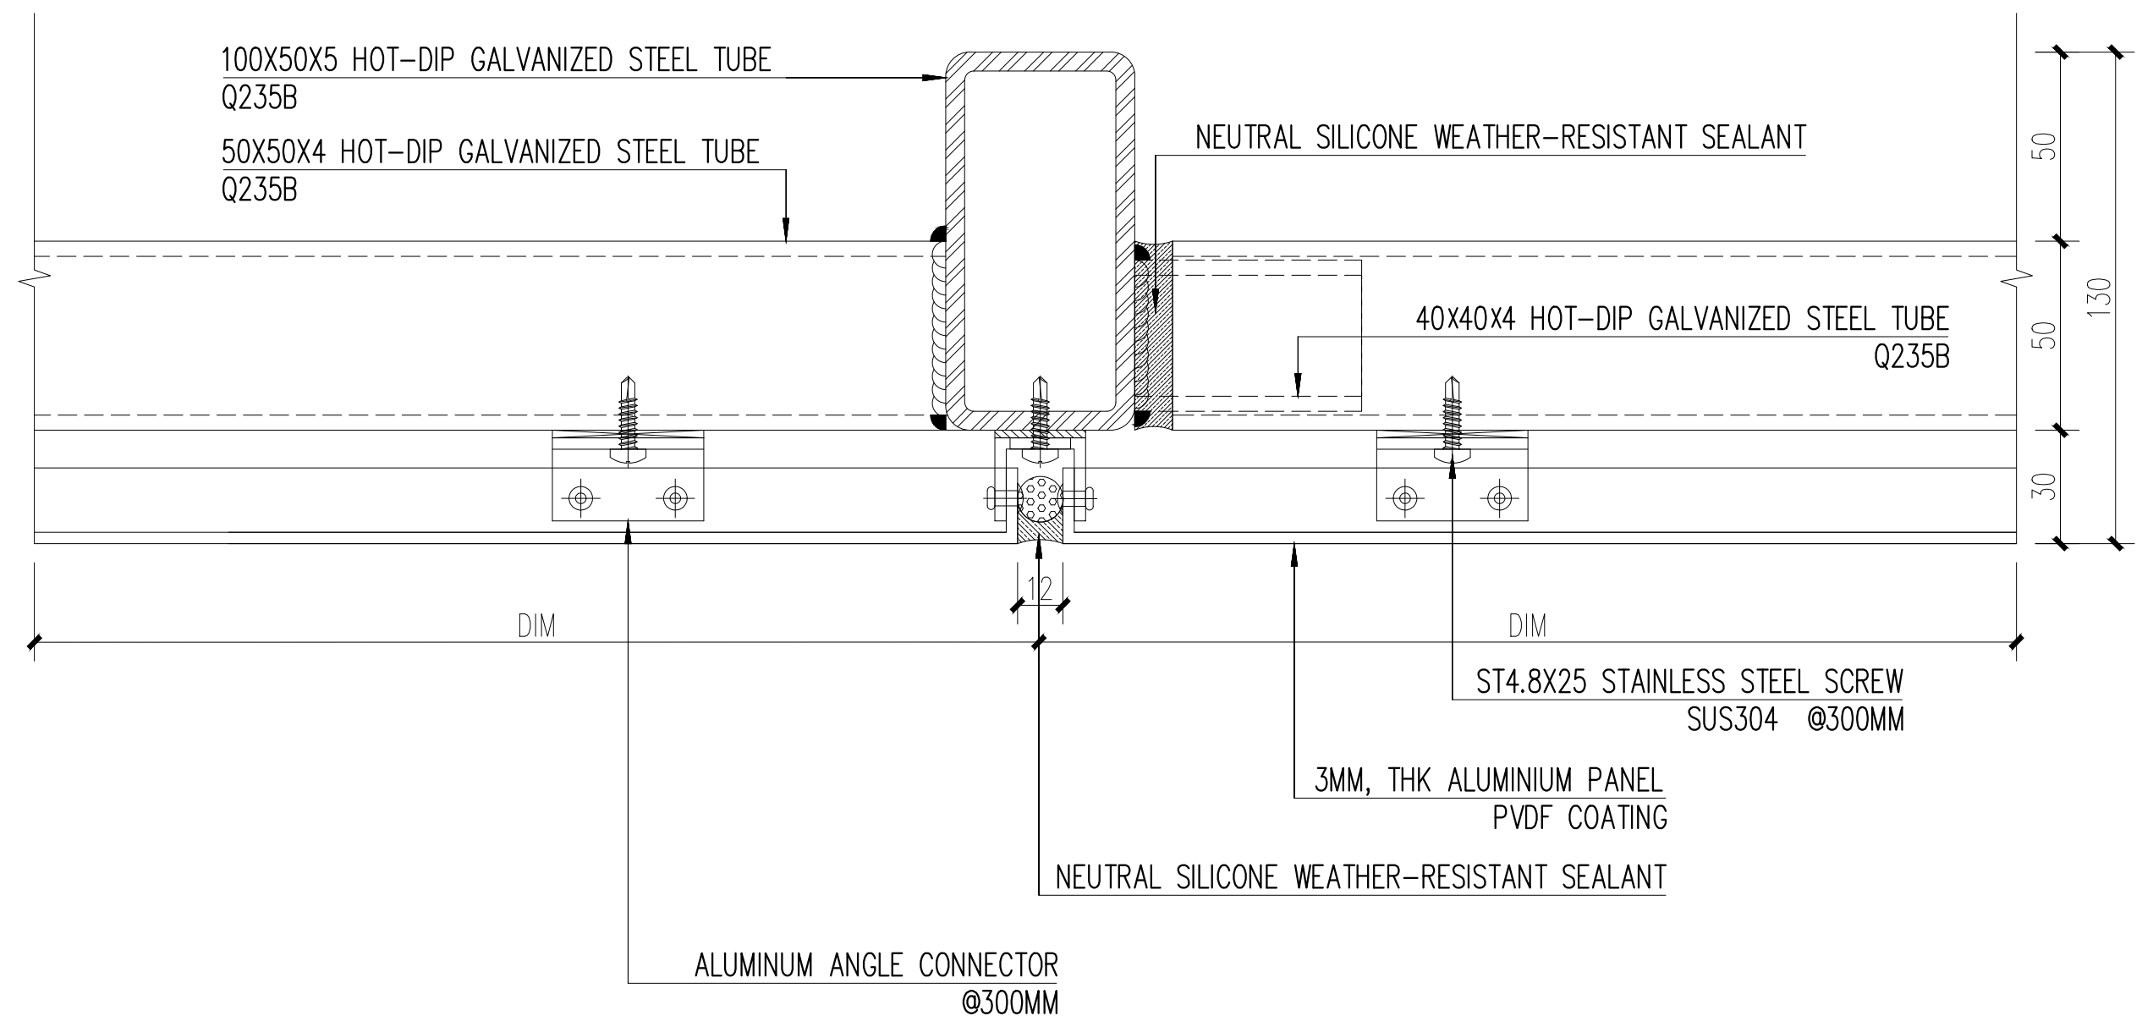
100X50X5 HOT-DIP GALVANIZED STEEL TUBE
Q235B
50X50X4 HOT-DIP GALVANIZED STEEL TUBE
Q235B
NEUTRAL SILICONE WEATHER-RESISTANT SEALANT
40X40X4 HOT-DIP GALVANIZED STEEL TUBE
Q235B
50
50
30
130
12
DIM
DIM
ST4.8X25 STAINLESS STEEL SCREW
SUS304 @300MM
3MM, THK ALUMINIUM PANEL
PVDF COATING
NEUTRAL SILICONE WEATHER-RESISTANT SEALANT
ALUMINUM ANGLE CONNECTOR
@300MM

①

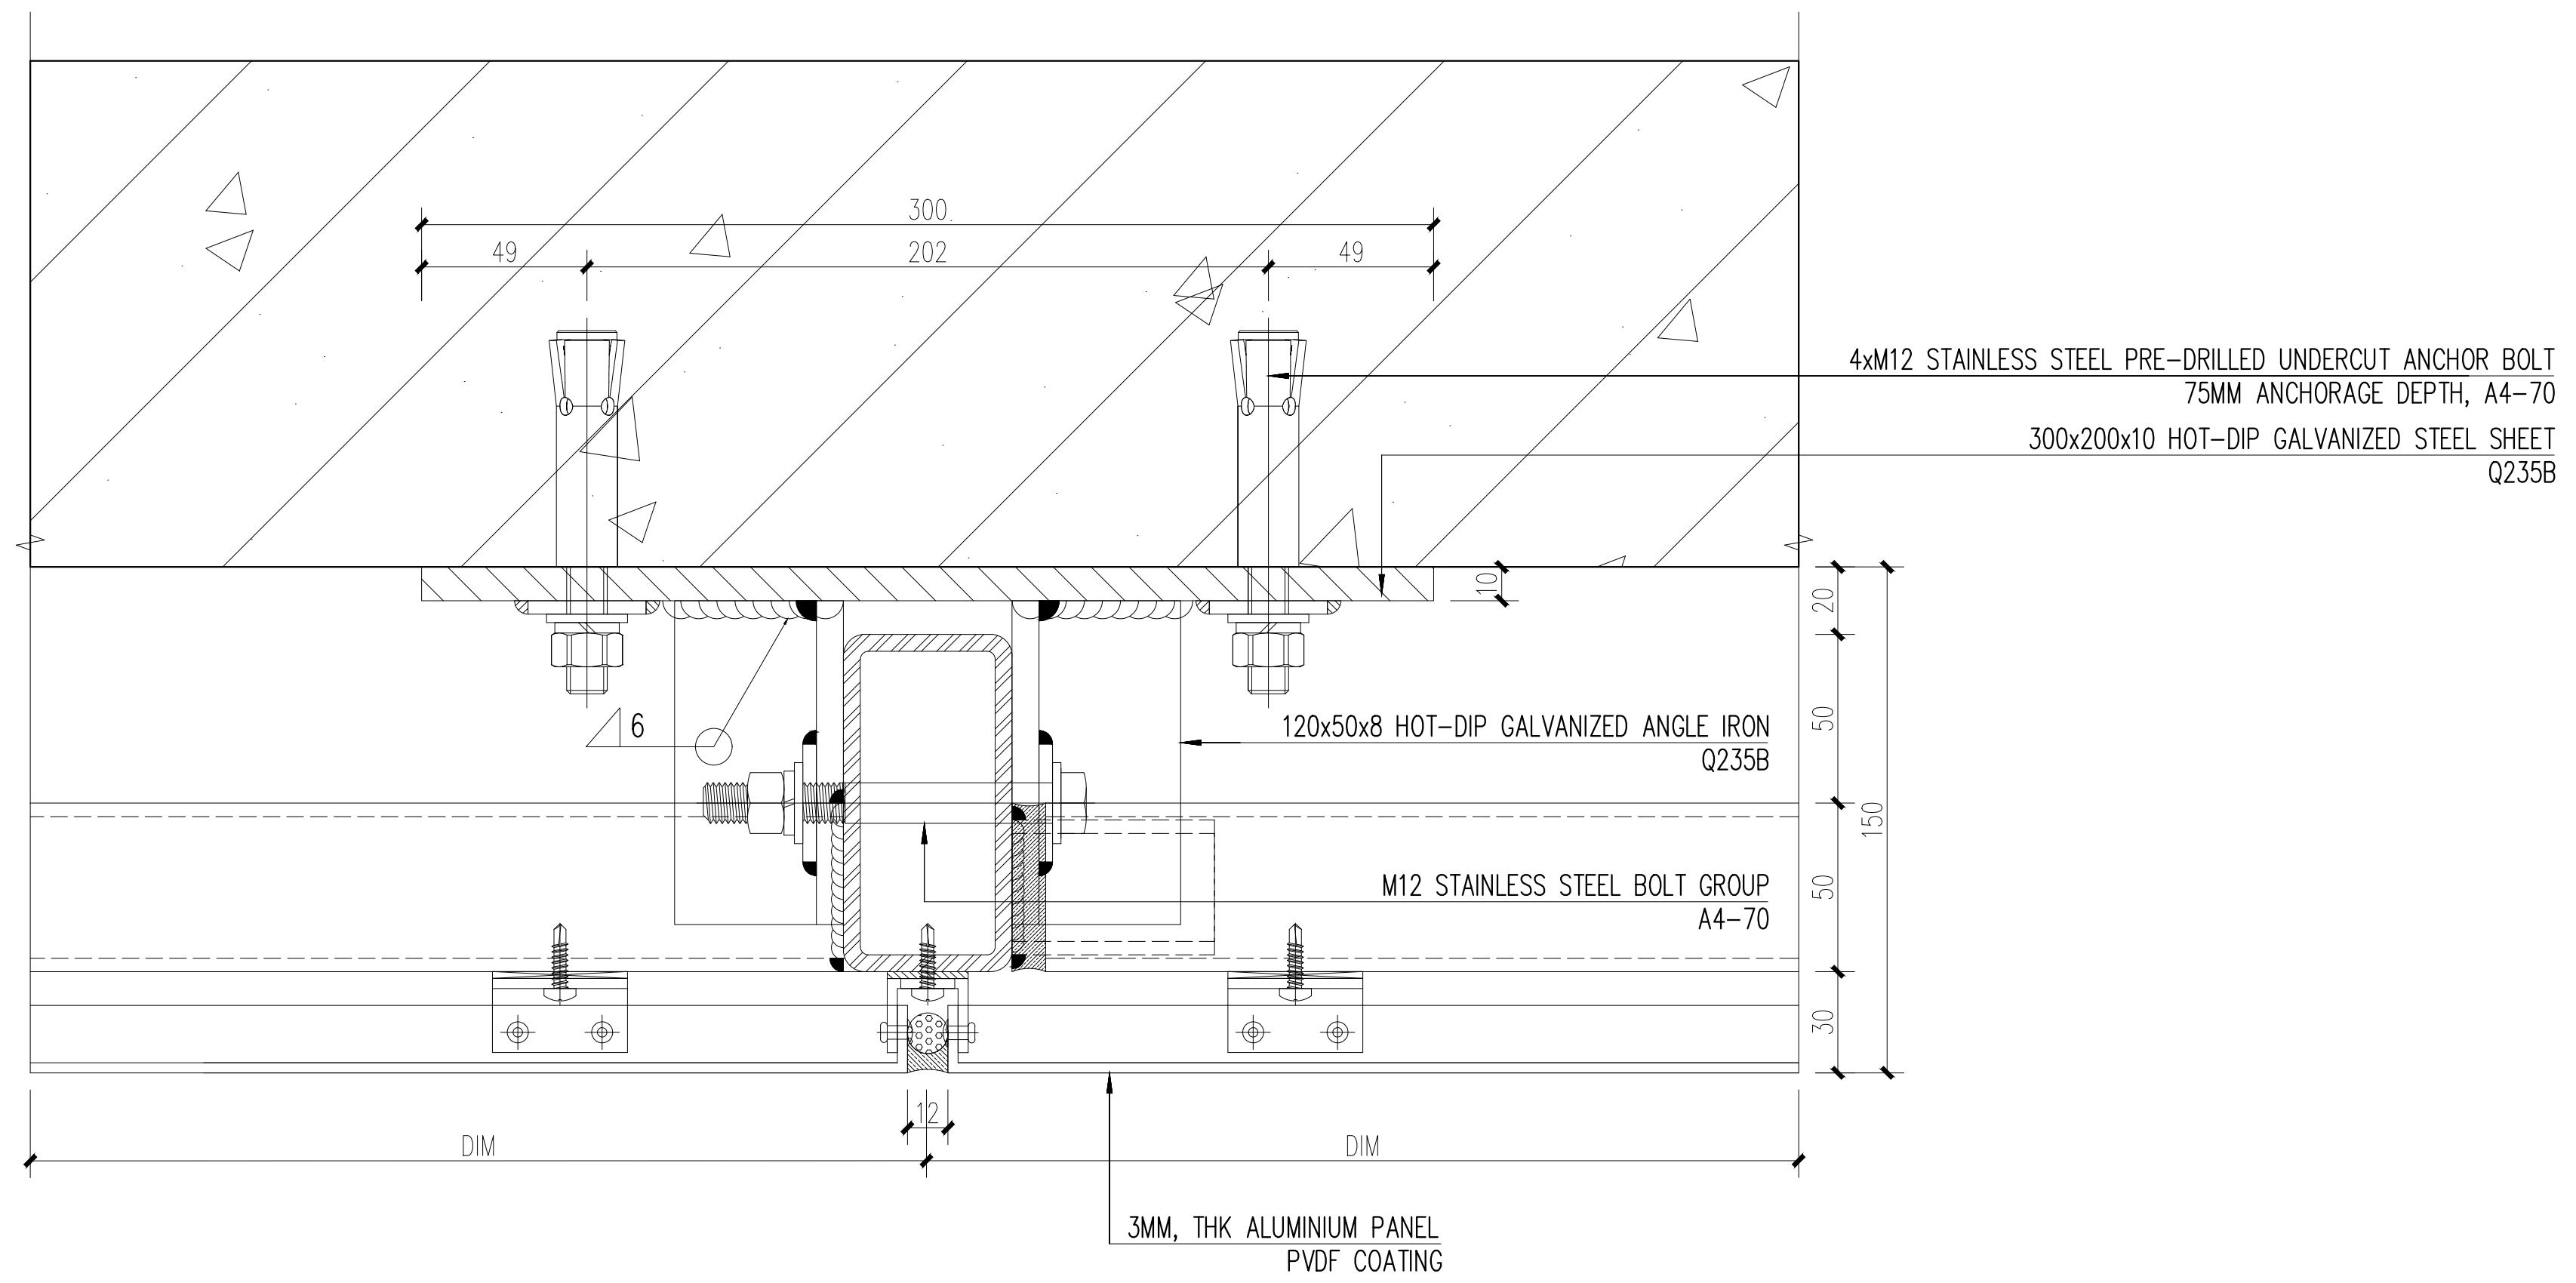
300
49
202
49
4xM12 STAINLESS STEEL PRE-DRILLED UNDERCUT ANCHOR BOLT
75MM ANCHORAGE DEPTH, A4-70
300x200x10 HOT-DIP GALVANIZED STEEL SHEET
Q235B
10
20
50
50
30
150
6
120x50x8 HOT-DIP GALVANIZED ANGLE IRON
Q235B
M12 STAINLESS STEEL BOLT GROUP
A4-70
12
DIM
DIM
3MM, THK ALUMINIUM PANEL
PVDF COATING

②

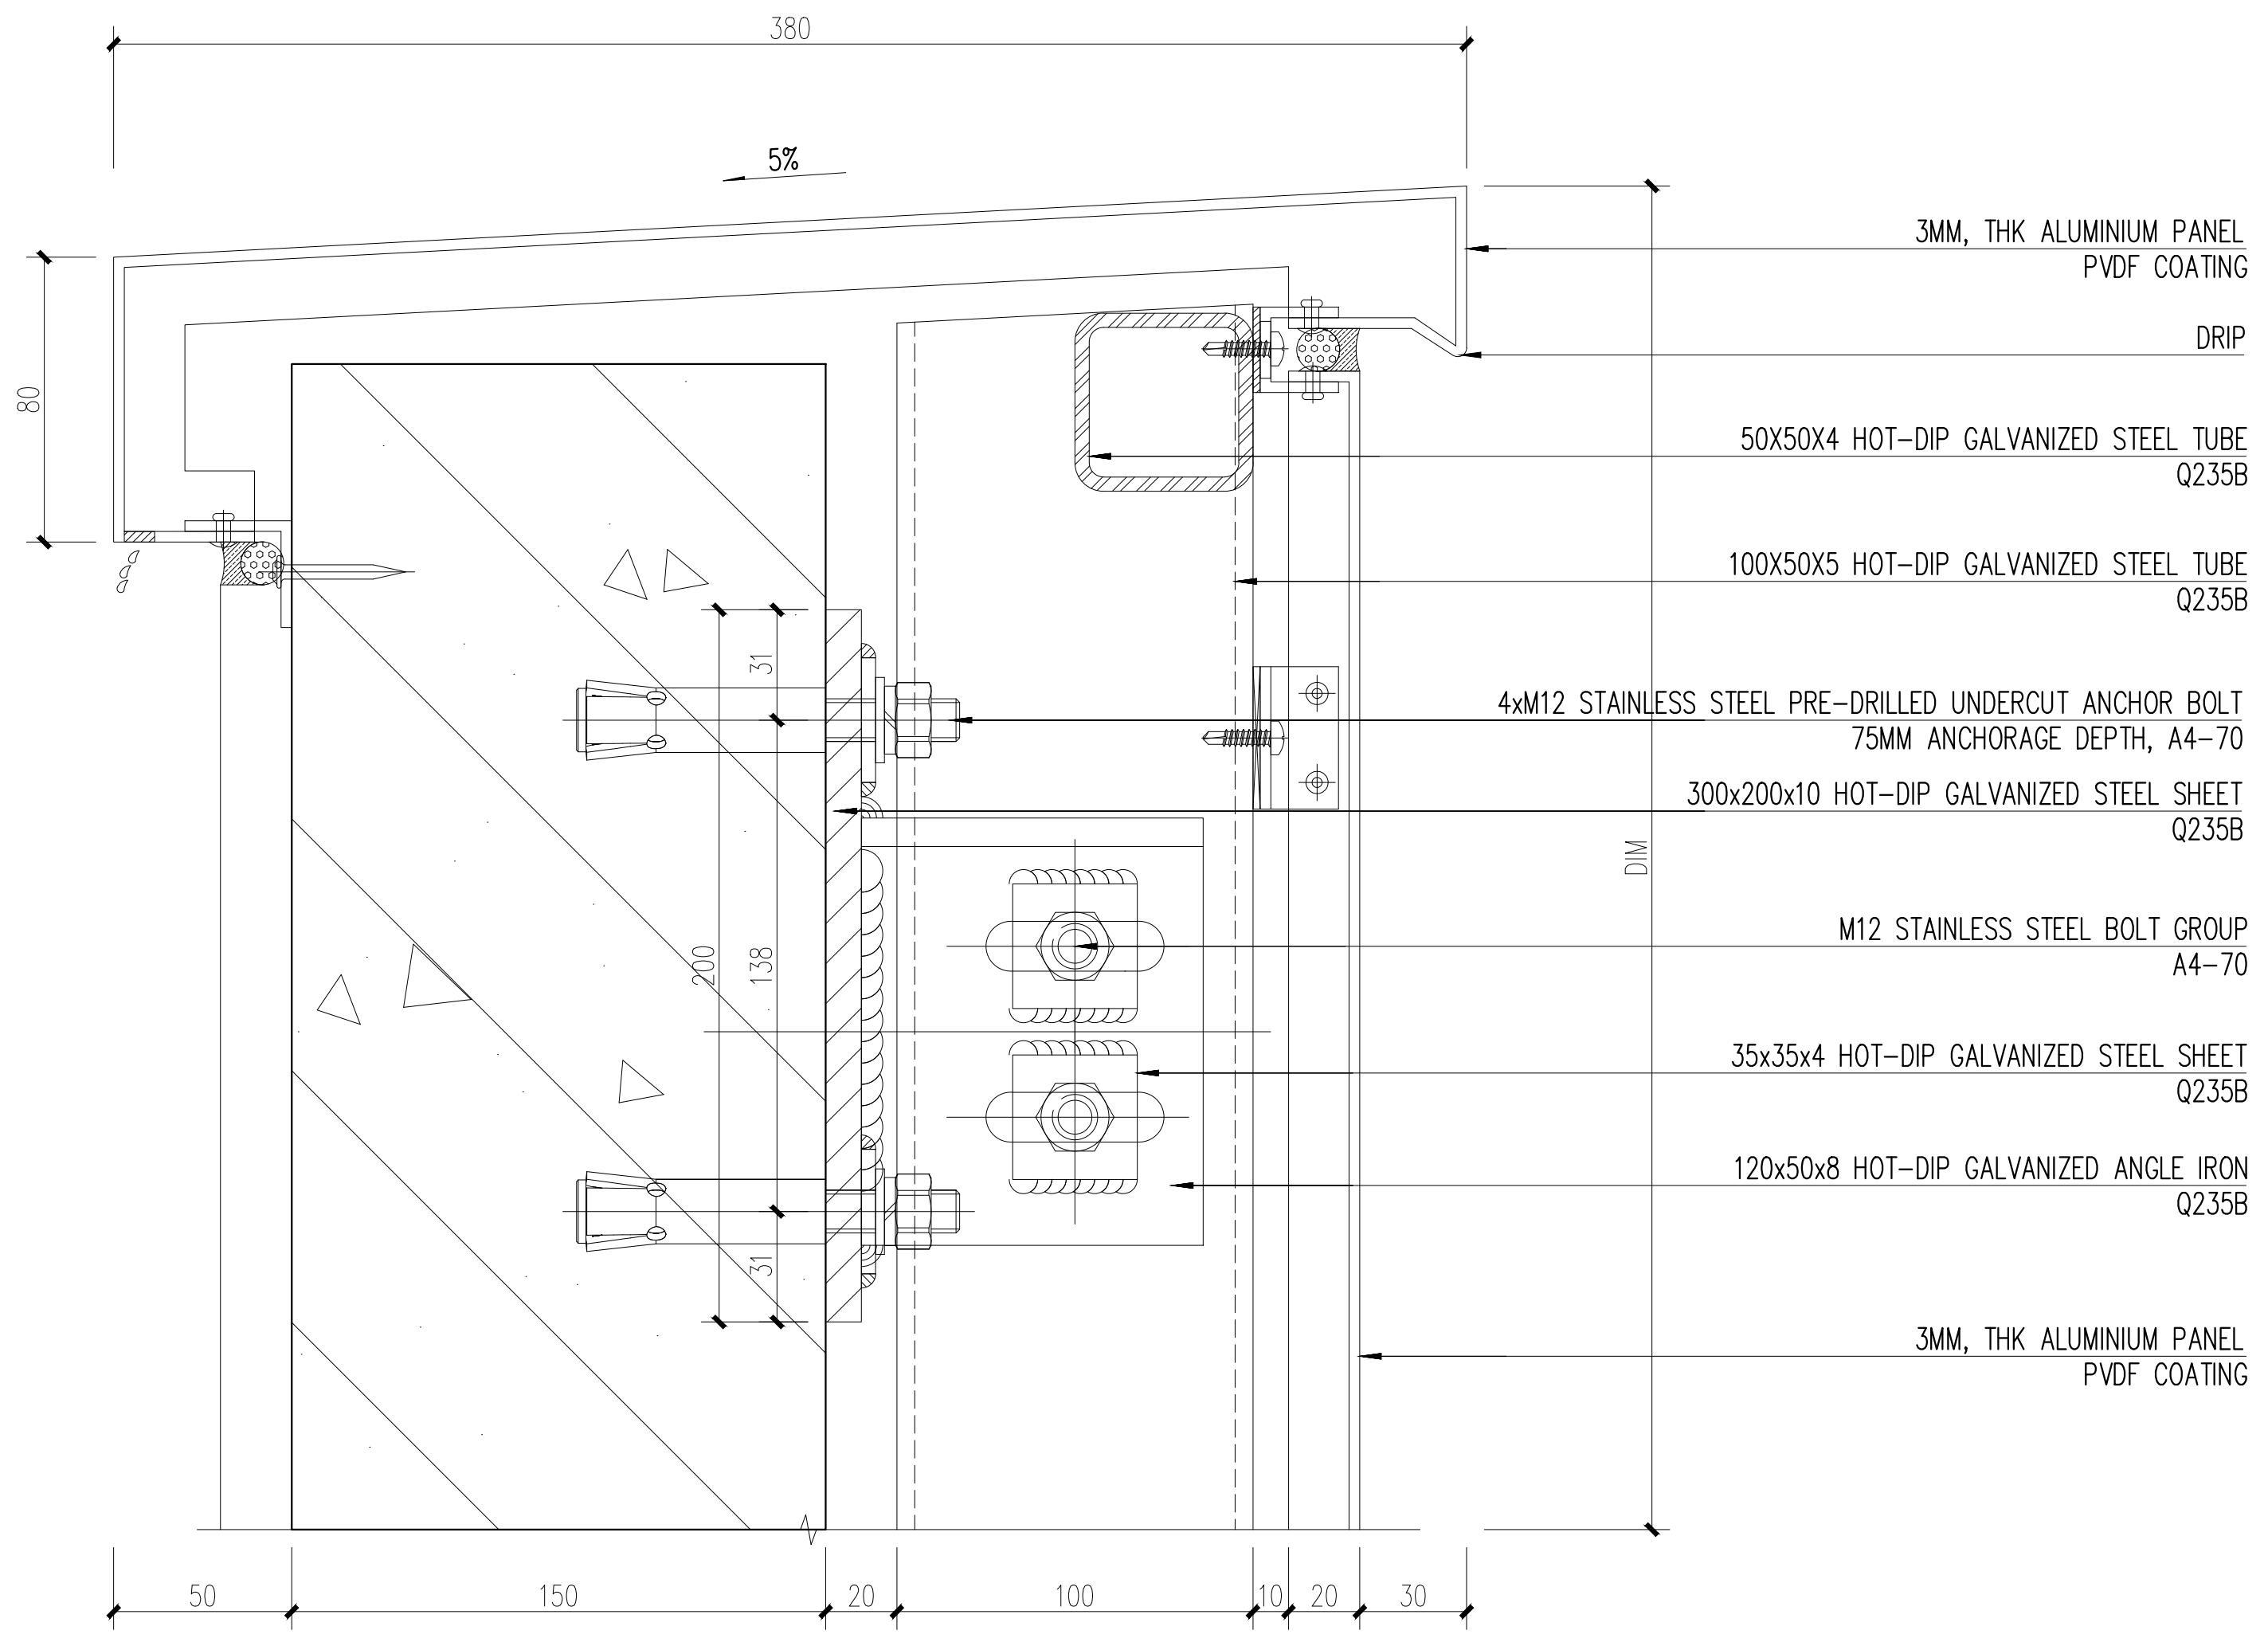
380
5%
80
3MM, THK ALUMINIUM PANEL
PVDF COATING
DRIP
50X50X4 HOT-DIP GALVANIZED STEEL TUBE
Q235B
100X50X5 HOT-DIP GALVANIZED STEEL TUBE
Q235B
4xM12 STAINLESS STEEL PRE-DRILLED UNDERCUT ANCHOR BOLT
75MM ANCHORAGE DEPTH, A4-70
300x200x10 HOT-DIP GALVANIZED STEEL SHEET
Q235B
M12 STAINLESS STEEL BOLT GROUP
A4-70
35x35x4 HOT-DIP GALVANIZED STEEL SHEET
Q235B
120x50x8 HOT-DIP GALVANIZED ANGLE IRON
Q235B
3MM, THK ALUMINIUM PANEL
PVDF COATING
31
200
138
31
DIM
50
150
20
100
10
20
30

③

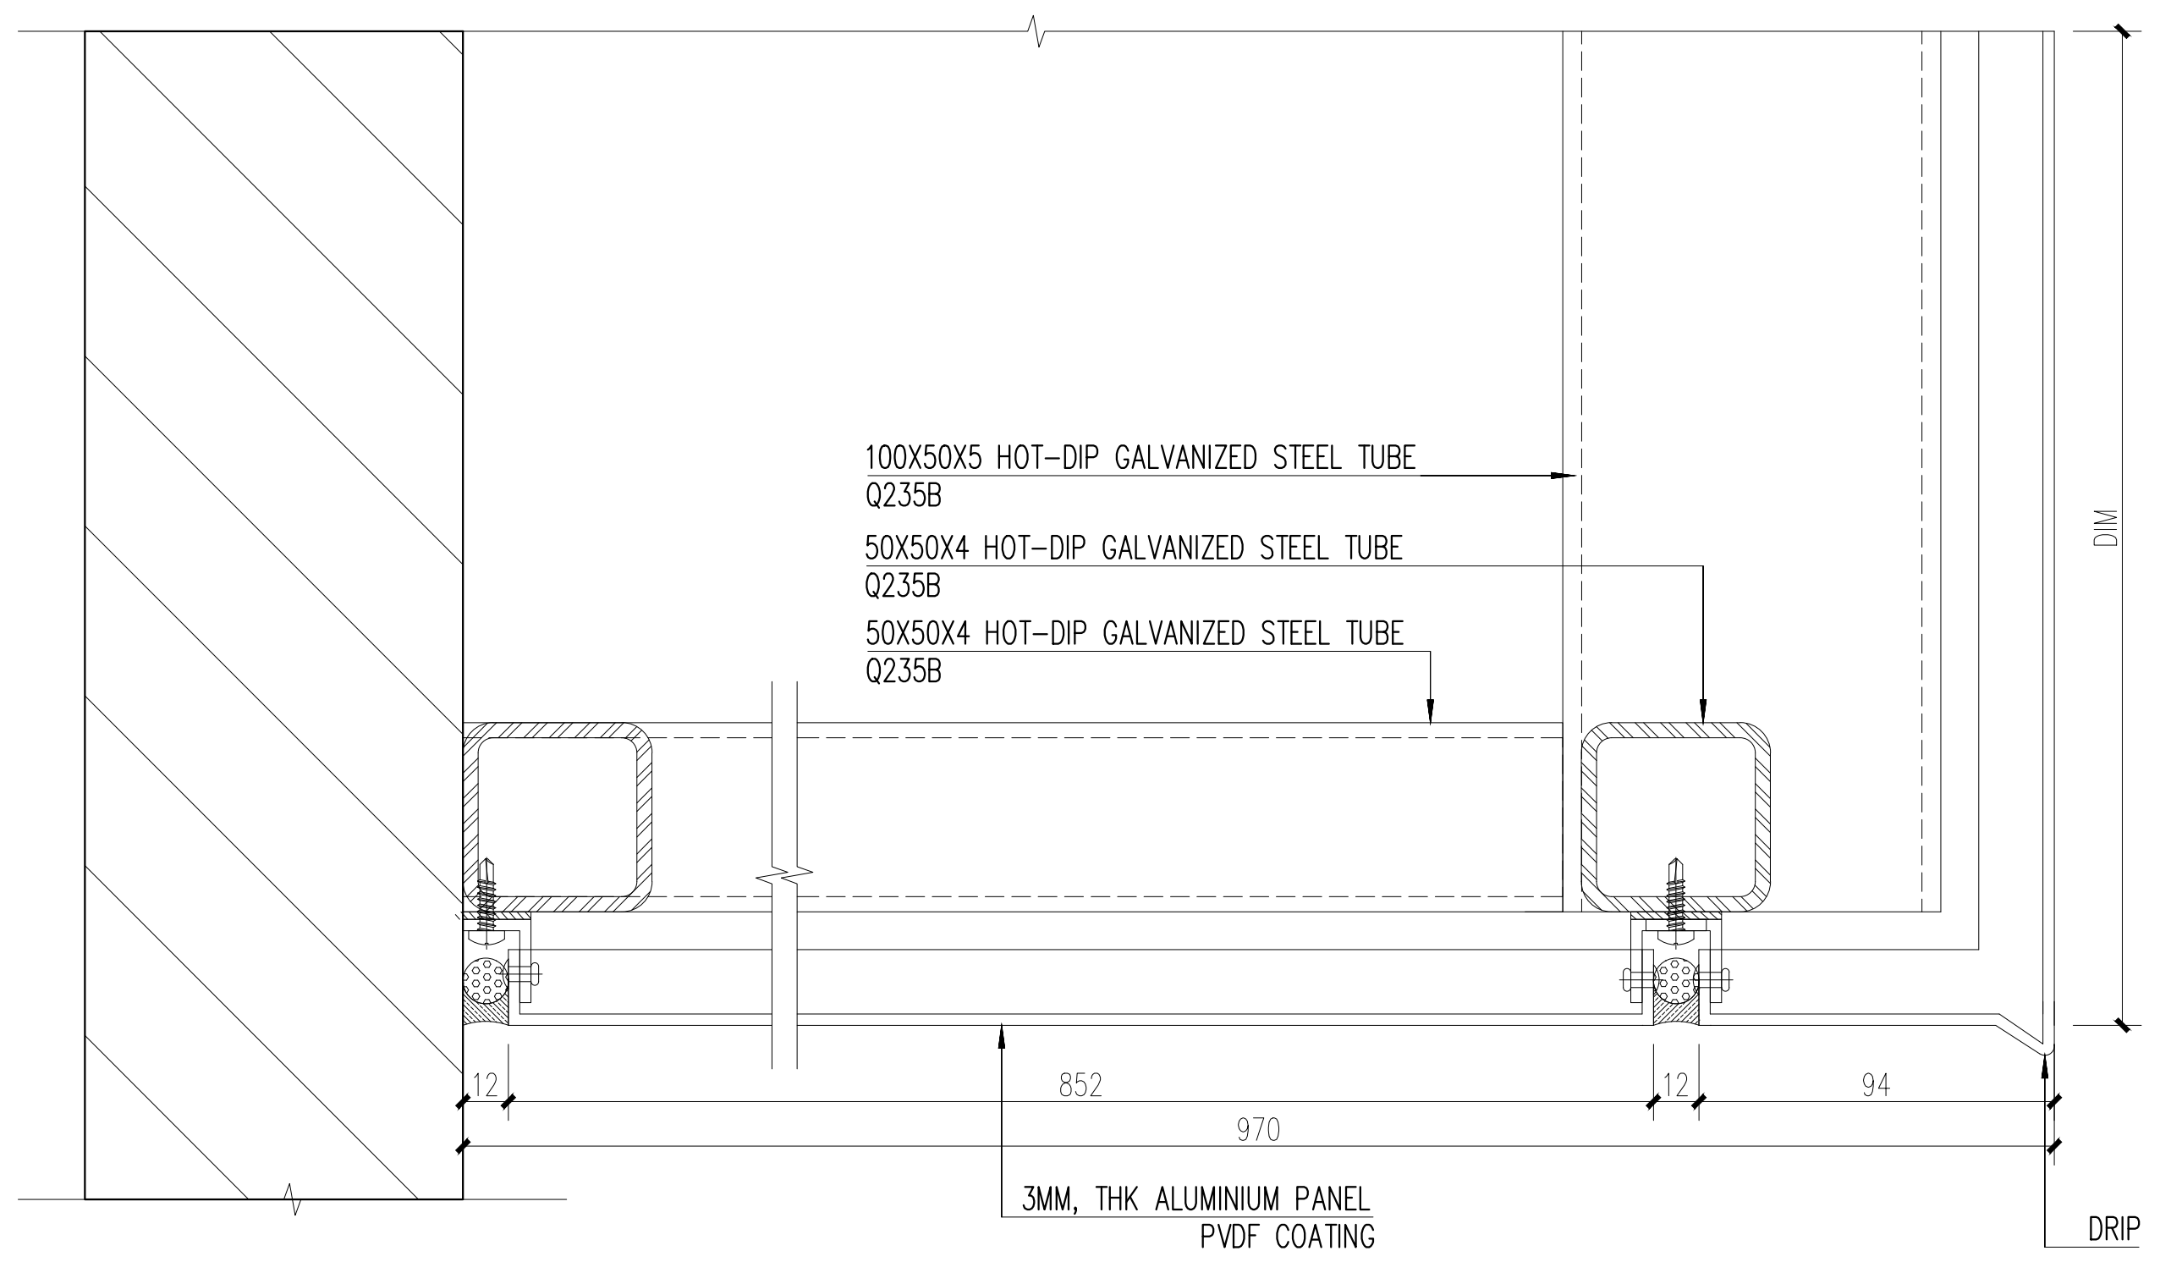
100X50X5 HOT-DIP GALVANIZED STEEL TUBE
Q235B
50X50X4 HOT-DIP GALVANIZED STEEL TUBE
Q235B
50X50X4 HOT-DIP GALVANIZED STEEL TUBE
Q235B
DIM
12
852
12
94
970
3MM, THK ALUMINIUM PANEL
PVDF COATING
DRIP

④

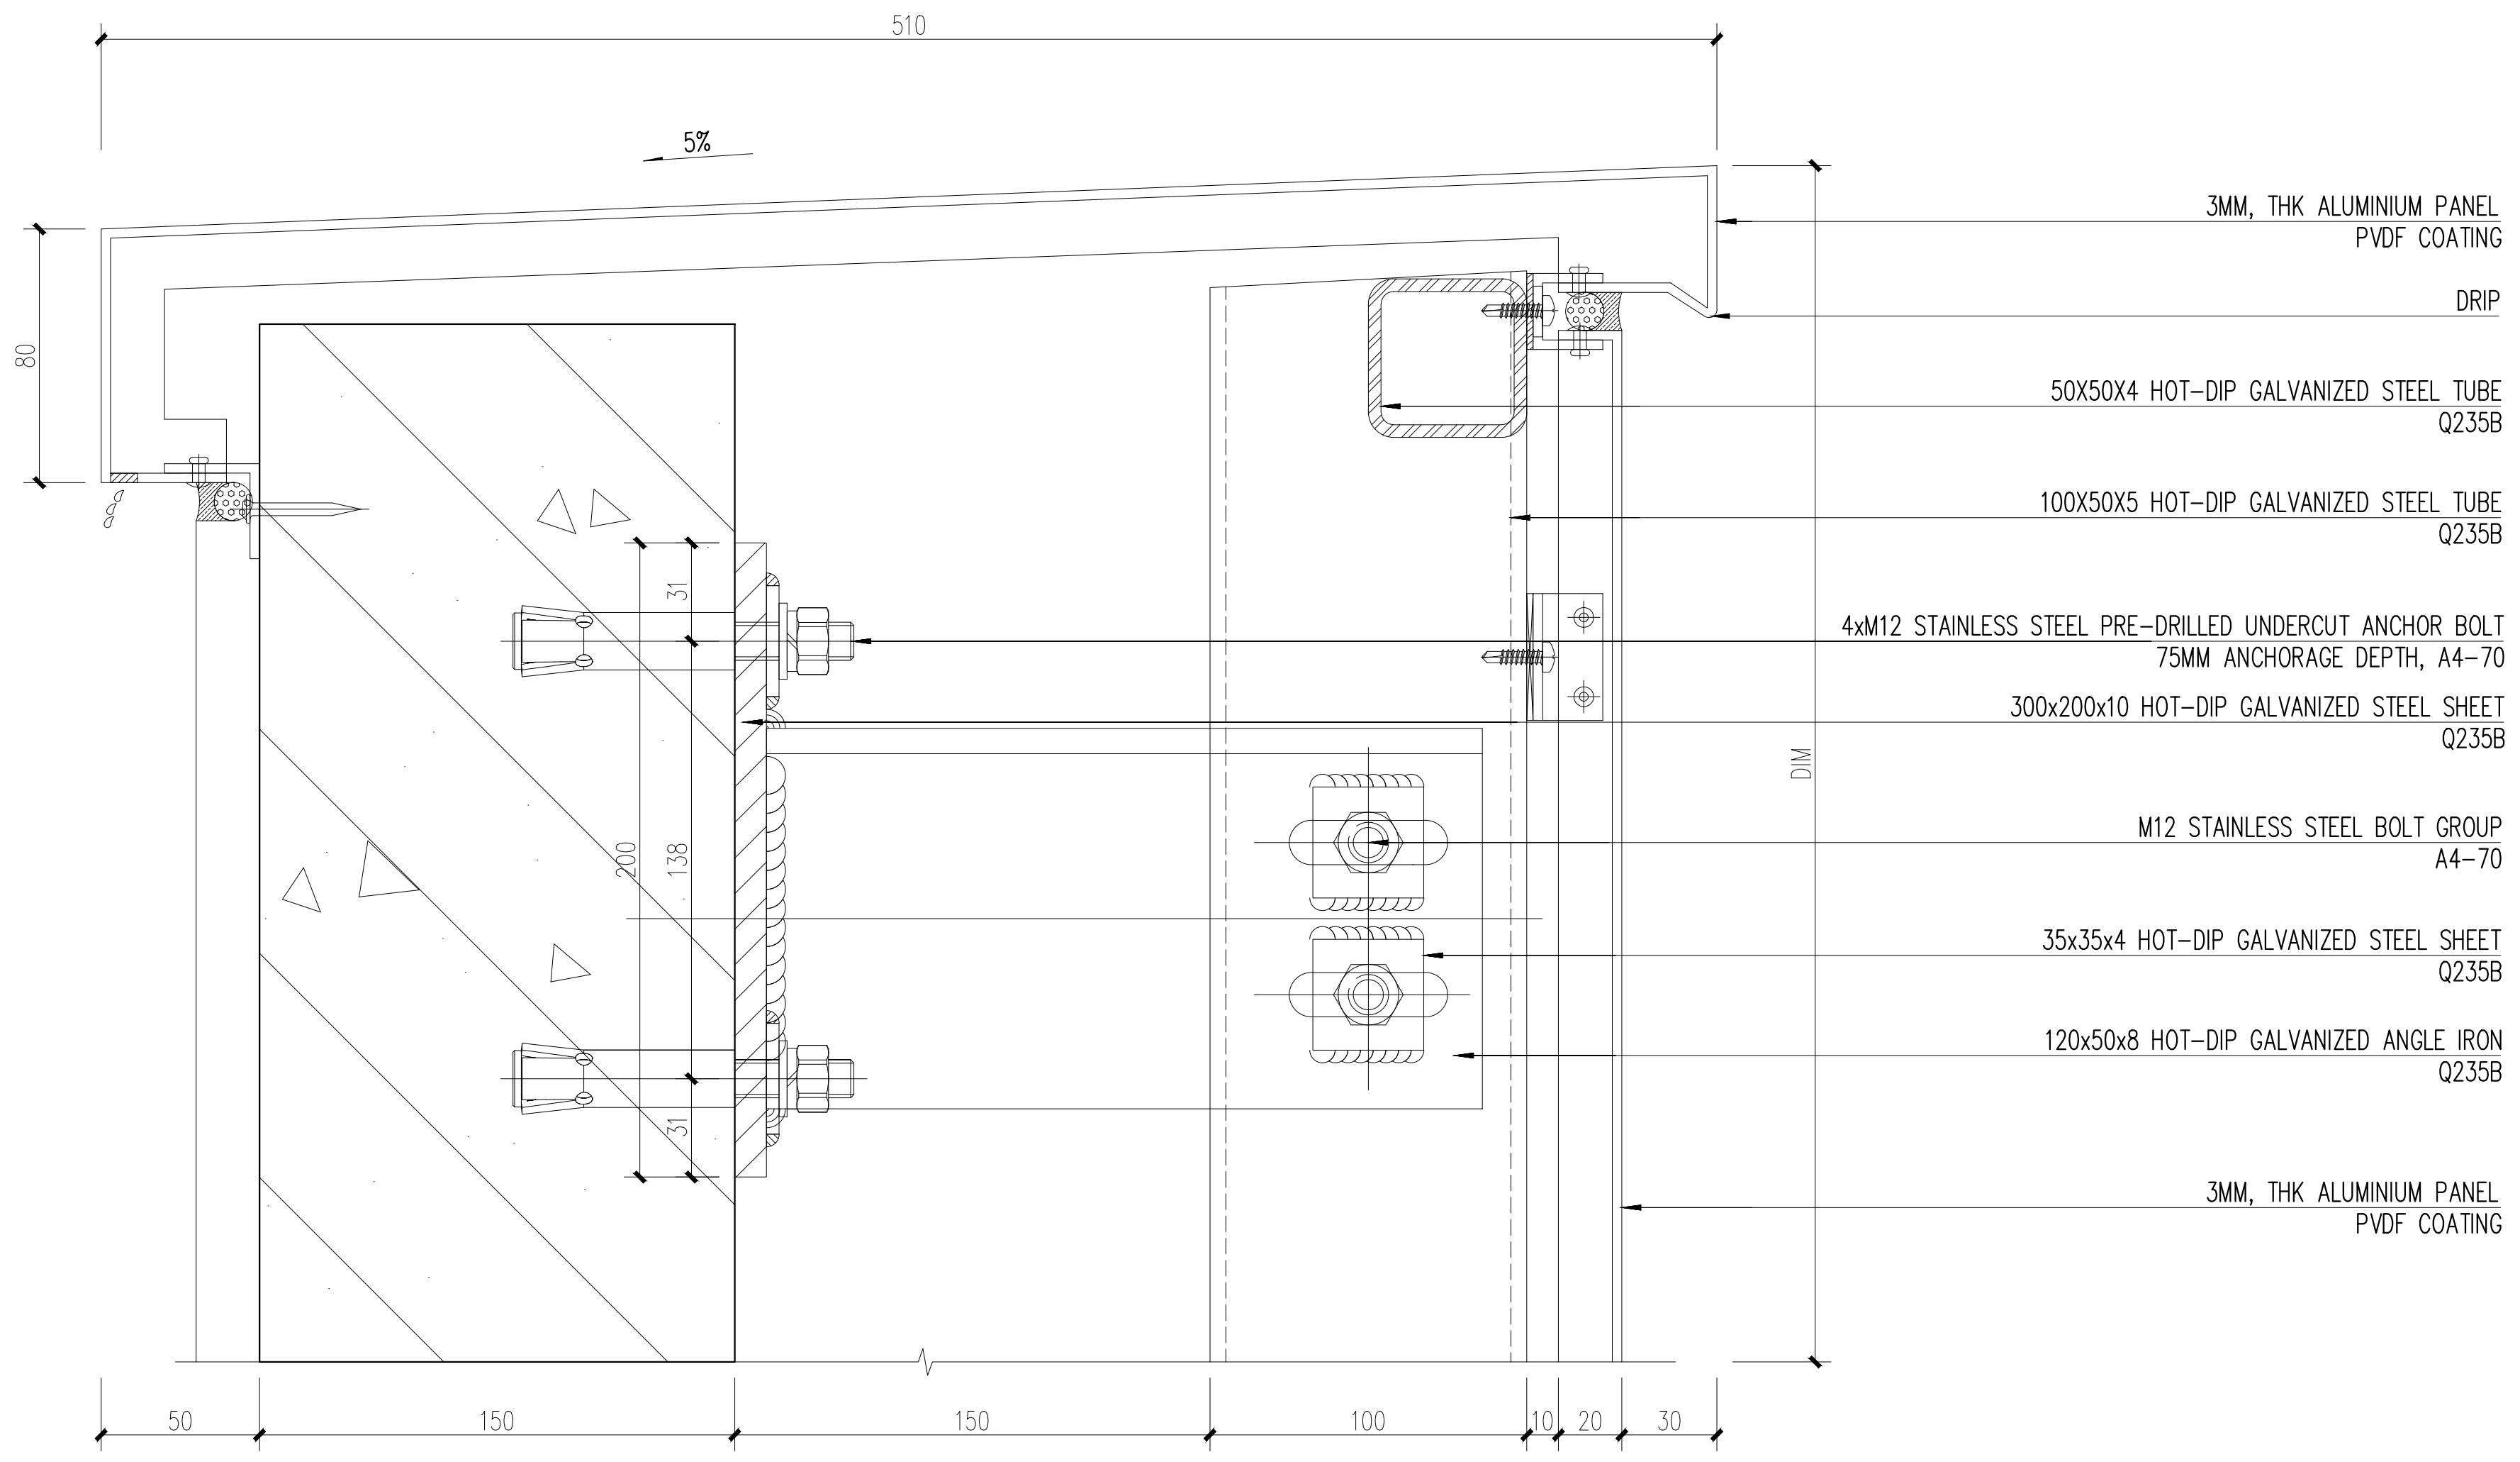
510
5%
80
3MM, THK ALUMINIUM PANEL
PVDF COATING
DRIP
50X50X4 HOT-DIP GALVANIZED STEEL TUBE
Q235B
100X50X5 HOT-DIP GALVANIZED STEEL TUBE
Q235B
4xM12 STAINLESS STEEL PRE-DRILLED UNDERCUT ANCHOR BOLT
75MM ANCHORAGE DEPTH, A4-70
300x200x10 HOT-DIP GALVANIZED STEEL SHEET
Q235B
M12 STAINLESS STEEL BOLT GROUP
A4-70
35x35x4 HOT-DIP GALVANIZED STEEL SHEET
Q235B
120x50x8 HOT-DIP GALVANIZED ANGLE IRON
Q235B
3MM, THK ALUMINIUM PANEL
PVDF COATING
31
200
138
31
DIM
50
150
150
100
10
20
30

⑤

CLIENT :

GULF EDGE DC 01

87 Wireless Road, M Thai Tower 11th. Floor, All Seasons Place, Lumpini,
Pathumwan, Bangkok 10330, Thailand

CONTRACTOR :

华西发展(泰国)有限公司
บริษัท หัวซือ ดีเวลลอปเม้นต์ (ประเทศไทย) จำกัด
HUASHI DEVELOPMENT CO.,LTD
No. 202, Room No. 1403, 14/F, Le Concorde Building,
Ratchadapisek Road, Huaykhwang Sub-District,
Huaykhwang District, Bangkok Metropolitan 10310.

CONSULTANT :

ARbay
บริษัท เอ อาร์ เบย์ จำกัด
ARbay Company Limited
31 st Floor Bangkok Insurance Building
25 South Sathorn road Thungmahamek
Sathorn Bangkok 10120 THAILAND
T +66 (0) 2286 8199
F +66 (0) 2286 2863
info@arbay.co.th

CONSULTANT :

Qbic Engineers & Architects Co.,Ltd.
8 Soi KALONG 4 SANAMBINNAM ROAD,
THASAI SUB-DISTRICT, MUANG NONTHABURI DISTRICT
, NONTHABURI.
Tel 662-950-4374
Fax 662-580-3231
E-Mail : qbic@qbic.co.th, www.qbic.co.th
QBIC ENGINEERS AND ARCHITECTS CO.,LTD.

CONSULTANT :

MITR
MITR TECHNICAL CONSULTANT CO.,LTD.
1168/8 12th FLOOR, LUMPINI TOWER BUILDING,
RAMA IV RD., THUNGMAHAMEK, SATHORN, BANGKOK 10120, THAILAND
TEL : 0-2679-9079-84
FAX : 0-2679-9085 E-mail: mitr_dd@mitr.com

Architect : SIGNATURE
ประกิด พนานุรัตน์ วสถ. 580
ที่อยู่
251/1 ถ.จารุเมือง แขวงรองเมือง เขตปทุมวัน
กรุงเทพมหานคร โทรศัพท์ 02-286-8199

Structural Engineer : SIGNATURE
วิศวกรผู้ออกแบบโครงสร้าง
ณัฐสม สงวนวงษ์ วย 1423
ที่อยู่
2/1 ซ.รามคำแหง 150 ถ.รามคำแหง
แขวง สะพานสูง เขต สะพานสูง กทม. 10240

Structural Inspector : SIGNATURE
วิศวกรผู้ตรวจสอบโครงสร้าง
โกมล จุฑาภัทร วย 964
ที่อยู่
24/18 ซ.นวมินทร์ 129 ถ. นวมินทร์
แขวง นวลจันทร์ เขต บึงกุ่ม กทม. 10230

Electrical Engineer : SIGNATURE
วิศวกรผู้ออกแบบระบบไฟฟ้ากำลัง
นายสุภัทร บูรณวิทย์ วฟก.1265
ที่อยู่
21 ซอยทานสัมฤทธิ 13
ตำบลท่าทราย อ.เมืองนนทบุรี จ.นนทบุรี 11000

Mechanical Engineer : SIGNATURE
วิศวกรผู้ออกแบบระบบเครื่องกลและปรับอากาศ
นายประสิทธิ เกียวสุนทร วก.1221
ประสิทธิ์
ที่อยู่
44/372 ซอยบางกระดี 35/1 แขวงแสมดำ
เขตบางขุนเทียน กทม. 10150

Sanitary Engineer : SIGNATURE
วิศวกรผู้ออกแบบระบบสุขาภิบาล และดับเพลิง
นายทศวรรษ สนันฤทธิ์ วส. 215
ทศวรรษ
ที่อยู่
บ้านเลขที 99/107 หมู่ที 3 ต.ศีรษะจรเข้น้อย
อ.บางเสาธง จ.สมุทรปราการ 10540

ISSUE/REVISION

REV.	DESCRIPTION	DATE
A	90% DEVELOPED	09/05/2026

PROJECT NAME :

GEDC 01

LOCATION:
Nikhom Phattana district, Rayong ,industrial estate,CPGC

BUILDING :

90% DEVELOPED

TITLE :

CURTAIN WALL DETAIL

JOB NO.	SCALE 1:2
DRAWN LXP	REF.
CHECKED LJC	DWG.NO. MPK01A-90-A-CWD-001
APPROVED LXD	
DATE 2026.05.09	

NOTE : THIS PRINT IS OF A CONFIDENTIAL NATURE, IT SHALL NOT BE TRACED,PHOTOGRAPHED,PHOTOSTATED OR REPRODUCED IN ANY MANER,NOR USED FOR ANY PURPOSE WHATSOEVER EXCEPT BY WRITTEN PERMISSION

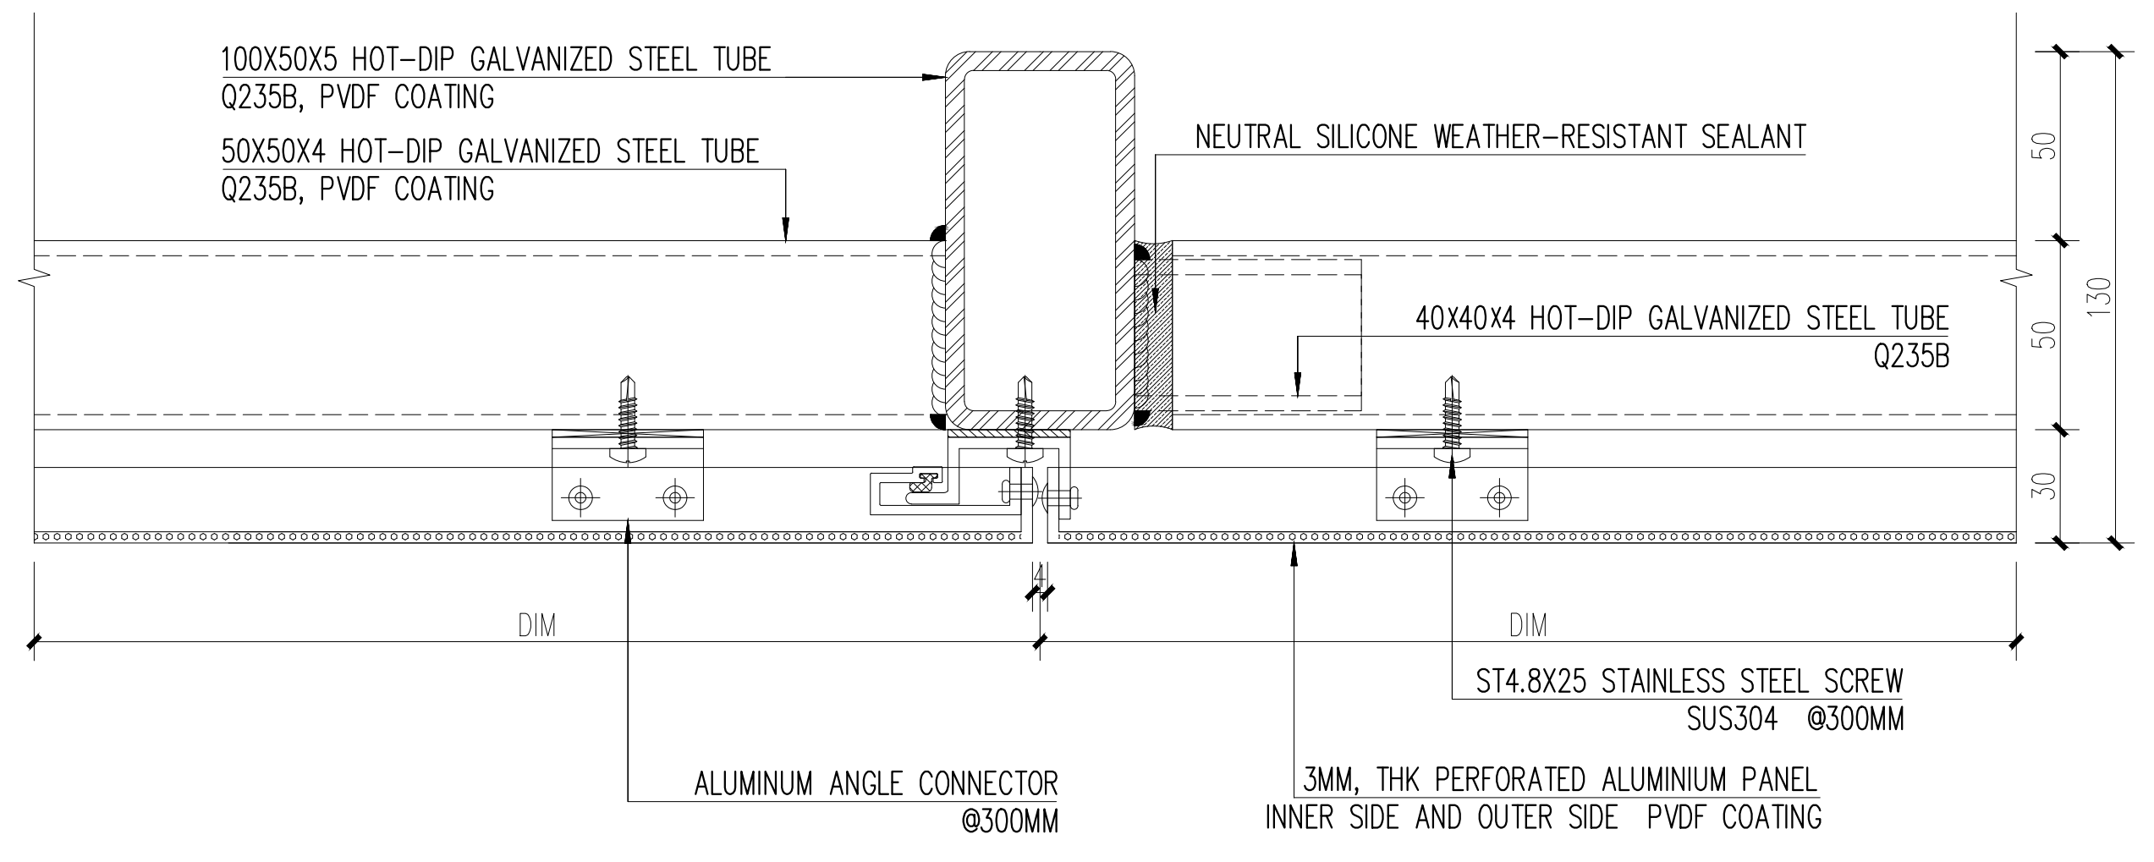
100X50X5 HOT-DIP GALVANIZED STEEL TUBE
Q235B, PVDF COATING
50X50X4 HOT-DIP GALVANIZED STEEL TUBE
Q235B, PVDF COATING
NEUTRAL SILICONE WEATHER-RESISTANT SEALANT
40x40x4 HOT-DIP GALVANIZED STEEL TUBE
Q235B
50
50
50
30
130
DIM
DIM
ALUMINUM ANGLE CONNECTOR
@300MM
ST4.8X25 STAINLESS STEEL SCREW
SUS304 @300MM
3MM, THK PERFORATED ALUMINIUM PANEL
INNER SIDE AND OUTER SIDE PVDF COATING

①

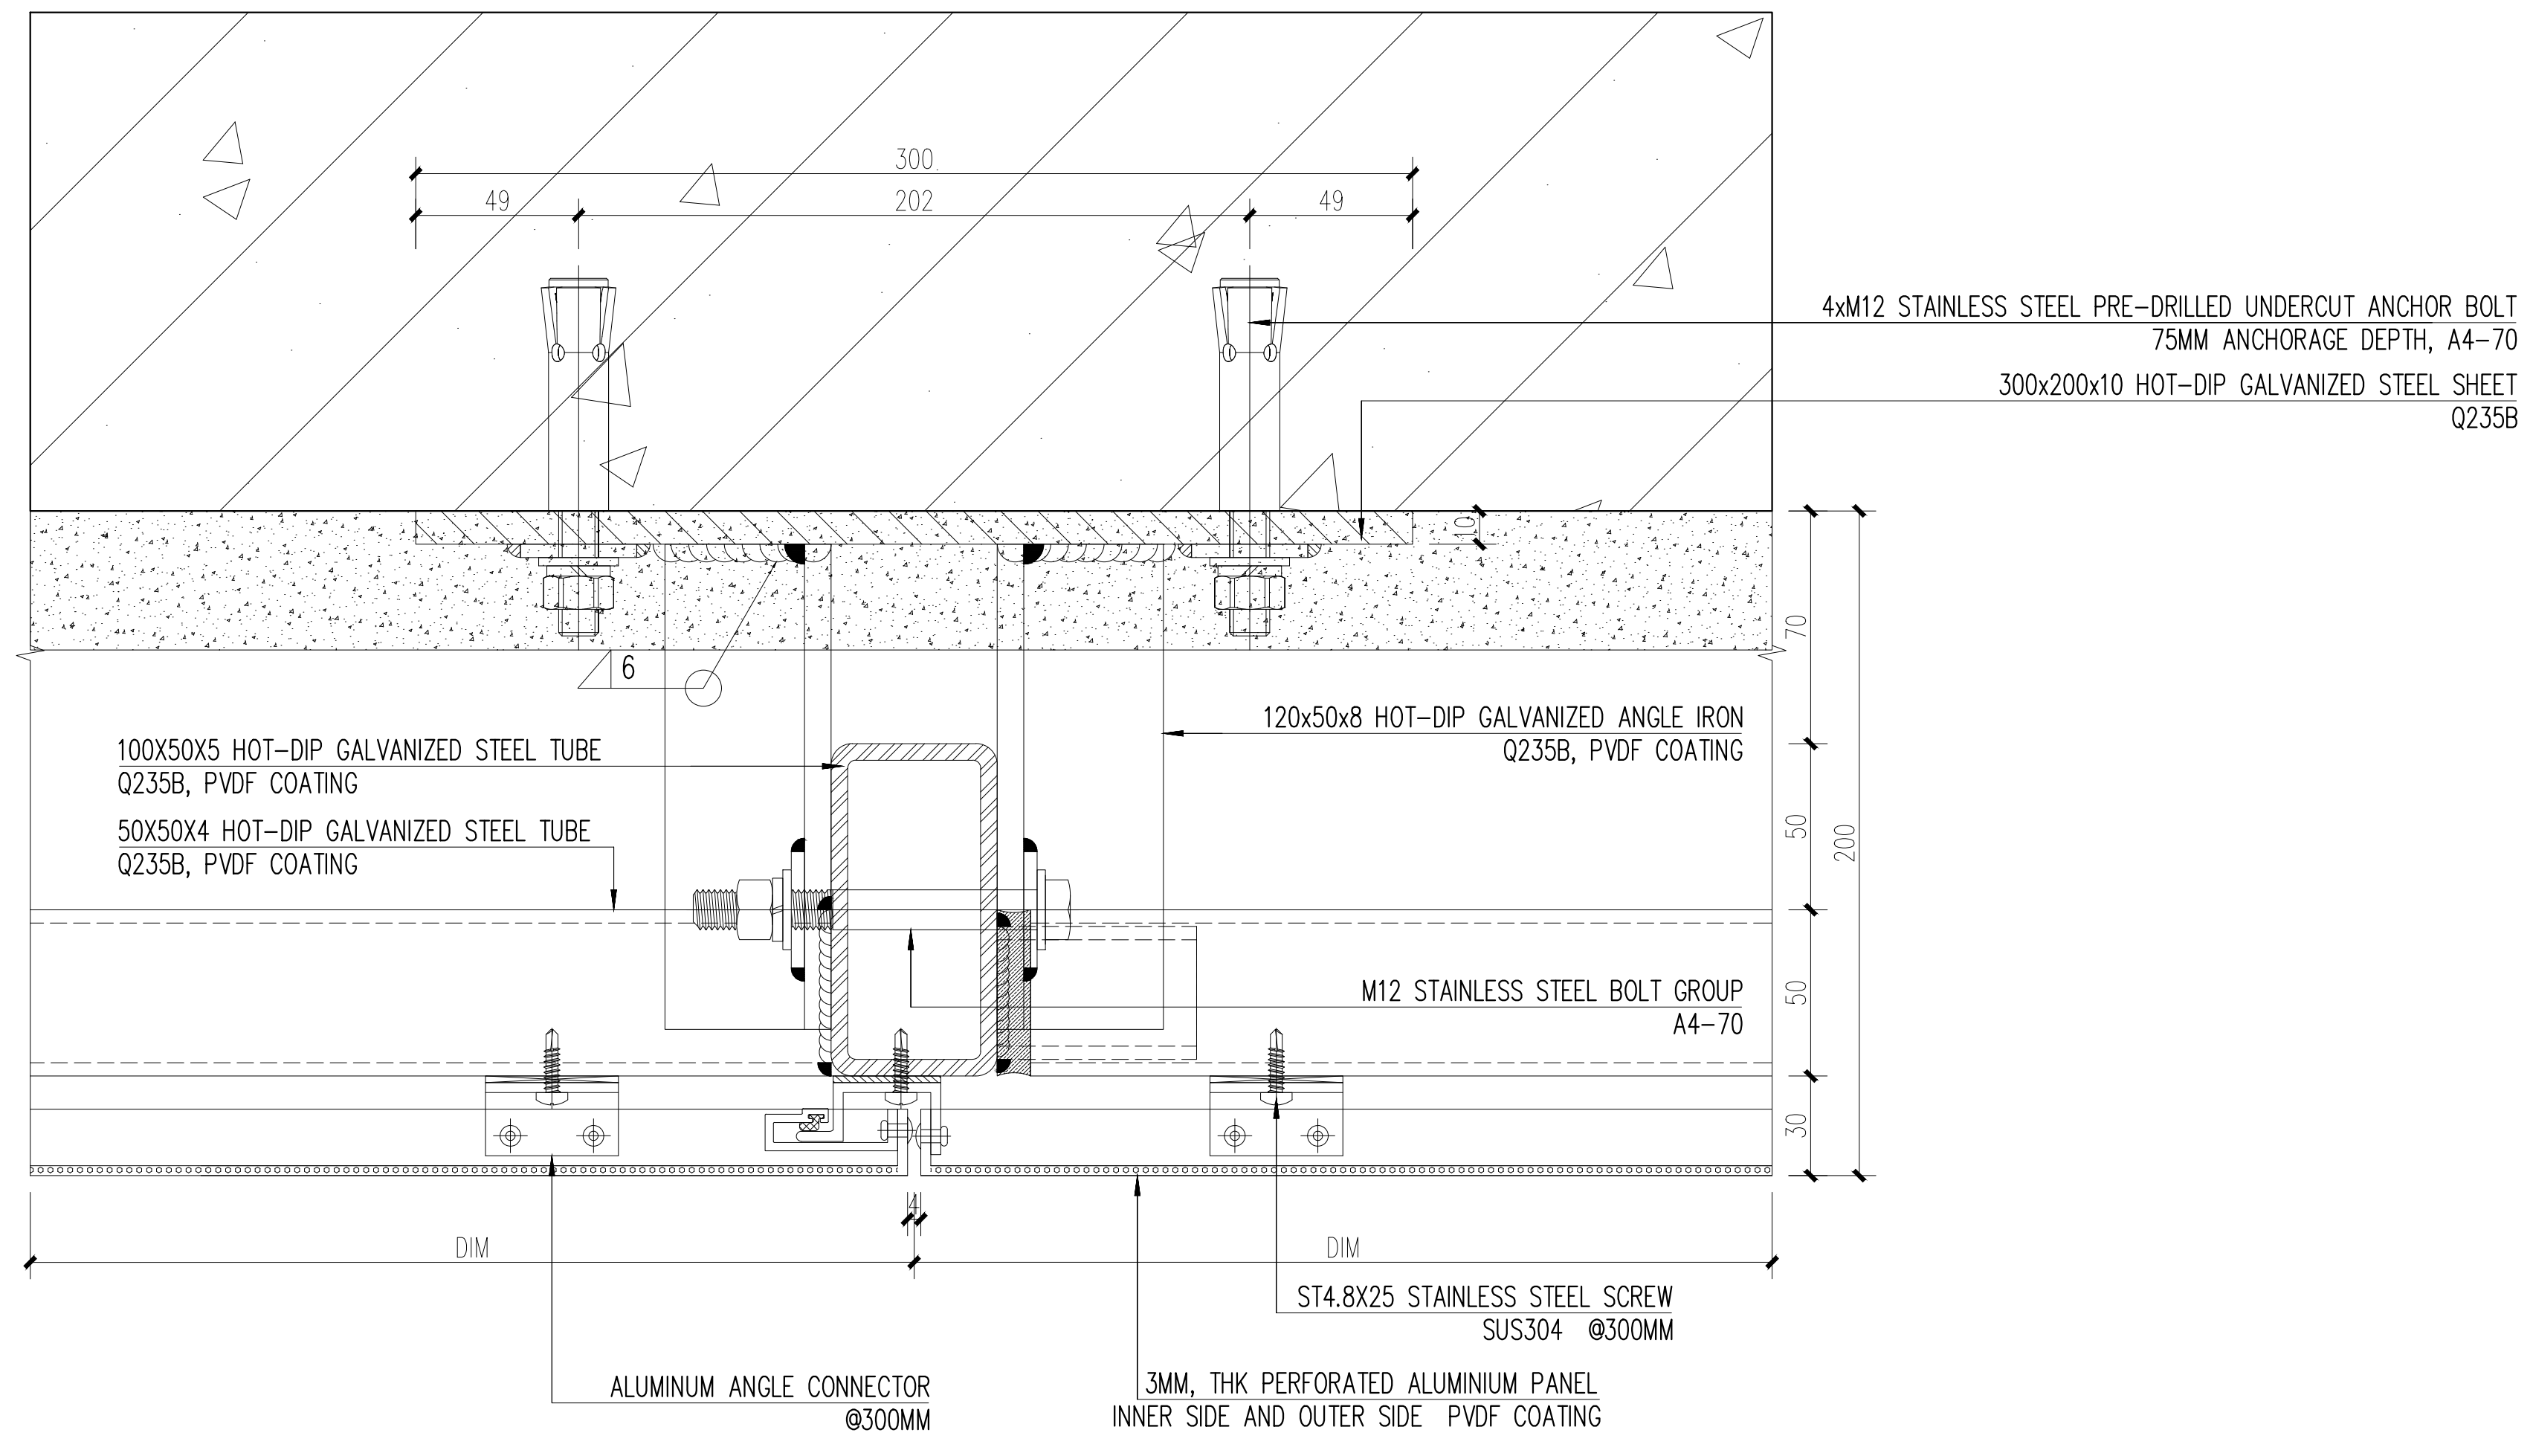
300
49
202
49
4xM12 STAINLESS STEEL PRE-DRILLED UNDERCUT ANCHOR BOLT
75MM ANCHORAGE DEPTH, A4-70
300x200x10 HOT-DIP GALVANIZED STEEL SHEET
Q235B
6
70
200
50
50
30
100X50X5 HOT-DIP GALVANIZED STEEL TUBE
Q235B, PVDF COATING
50X50X4 HOT-DIP GALVANIZED STEEL TUBE
Q235B, PVDF COATING
120x50x8 HOT-DIP GALVANIZED ANGLE IRON
Q235B, PVDF COATING
M12 STAINLESS STEEL BOLT GROUP
A4-70
DIM
DIM
ALUMINUM ANGLE CONNECTOR
@300MM
ST4.8X25 STAINLESS STEEL SCREW
SUS304 @300MM
3MM, THK PERFORATED ALUMINIUM PANEL
INNER SIDE AND OUTER SIDE PVDF COATING

②

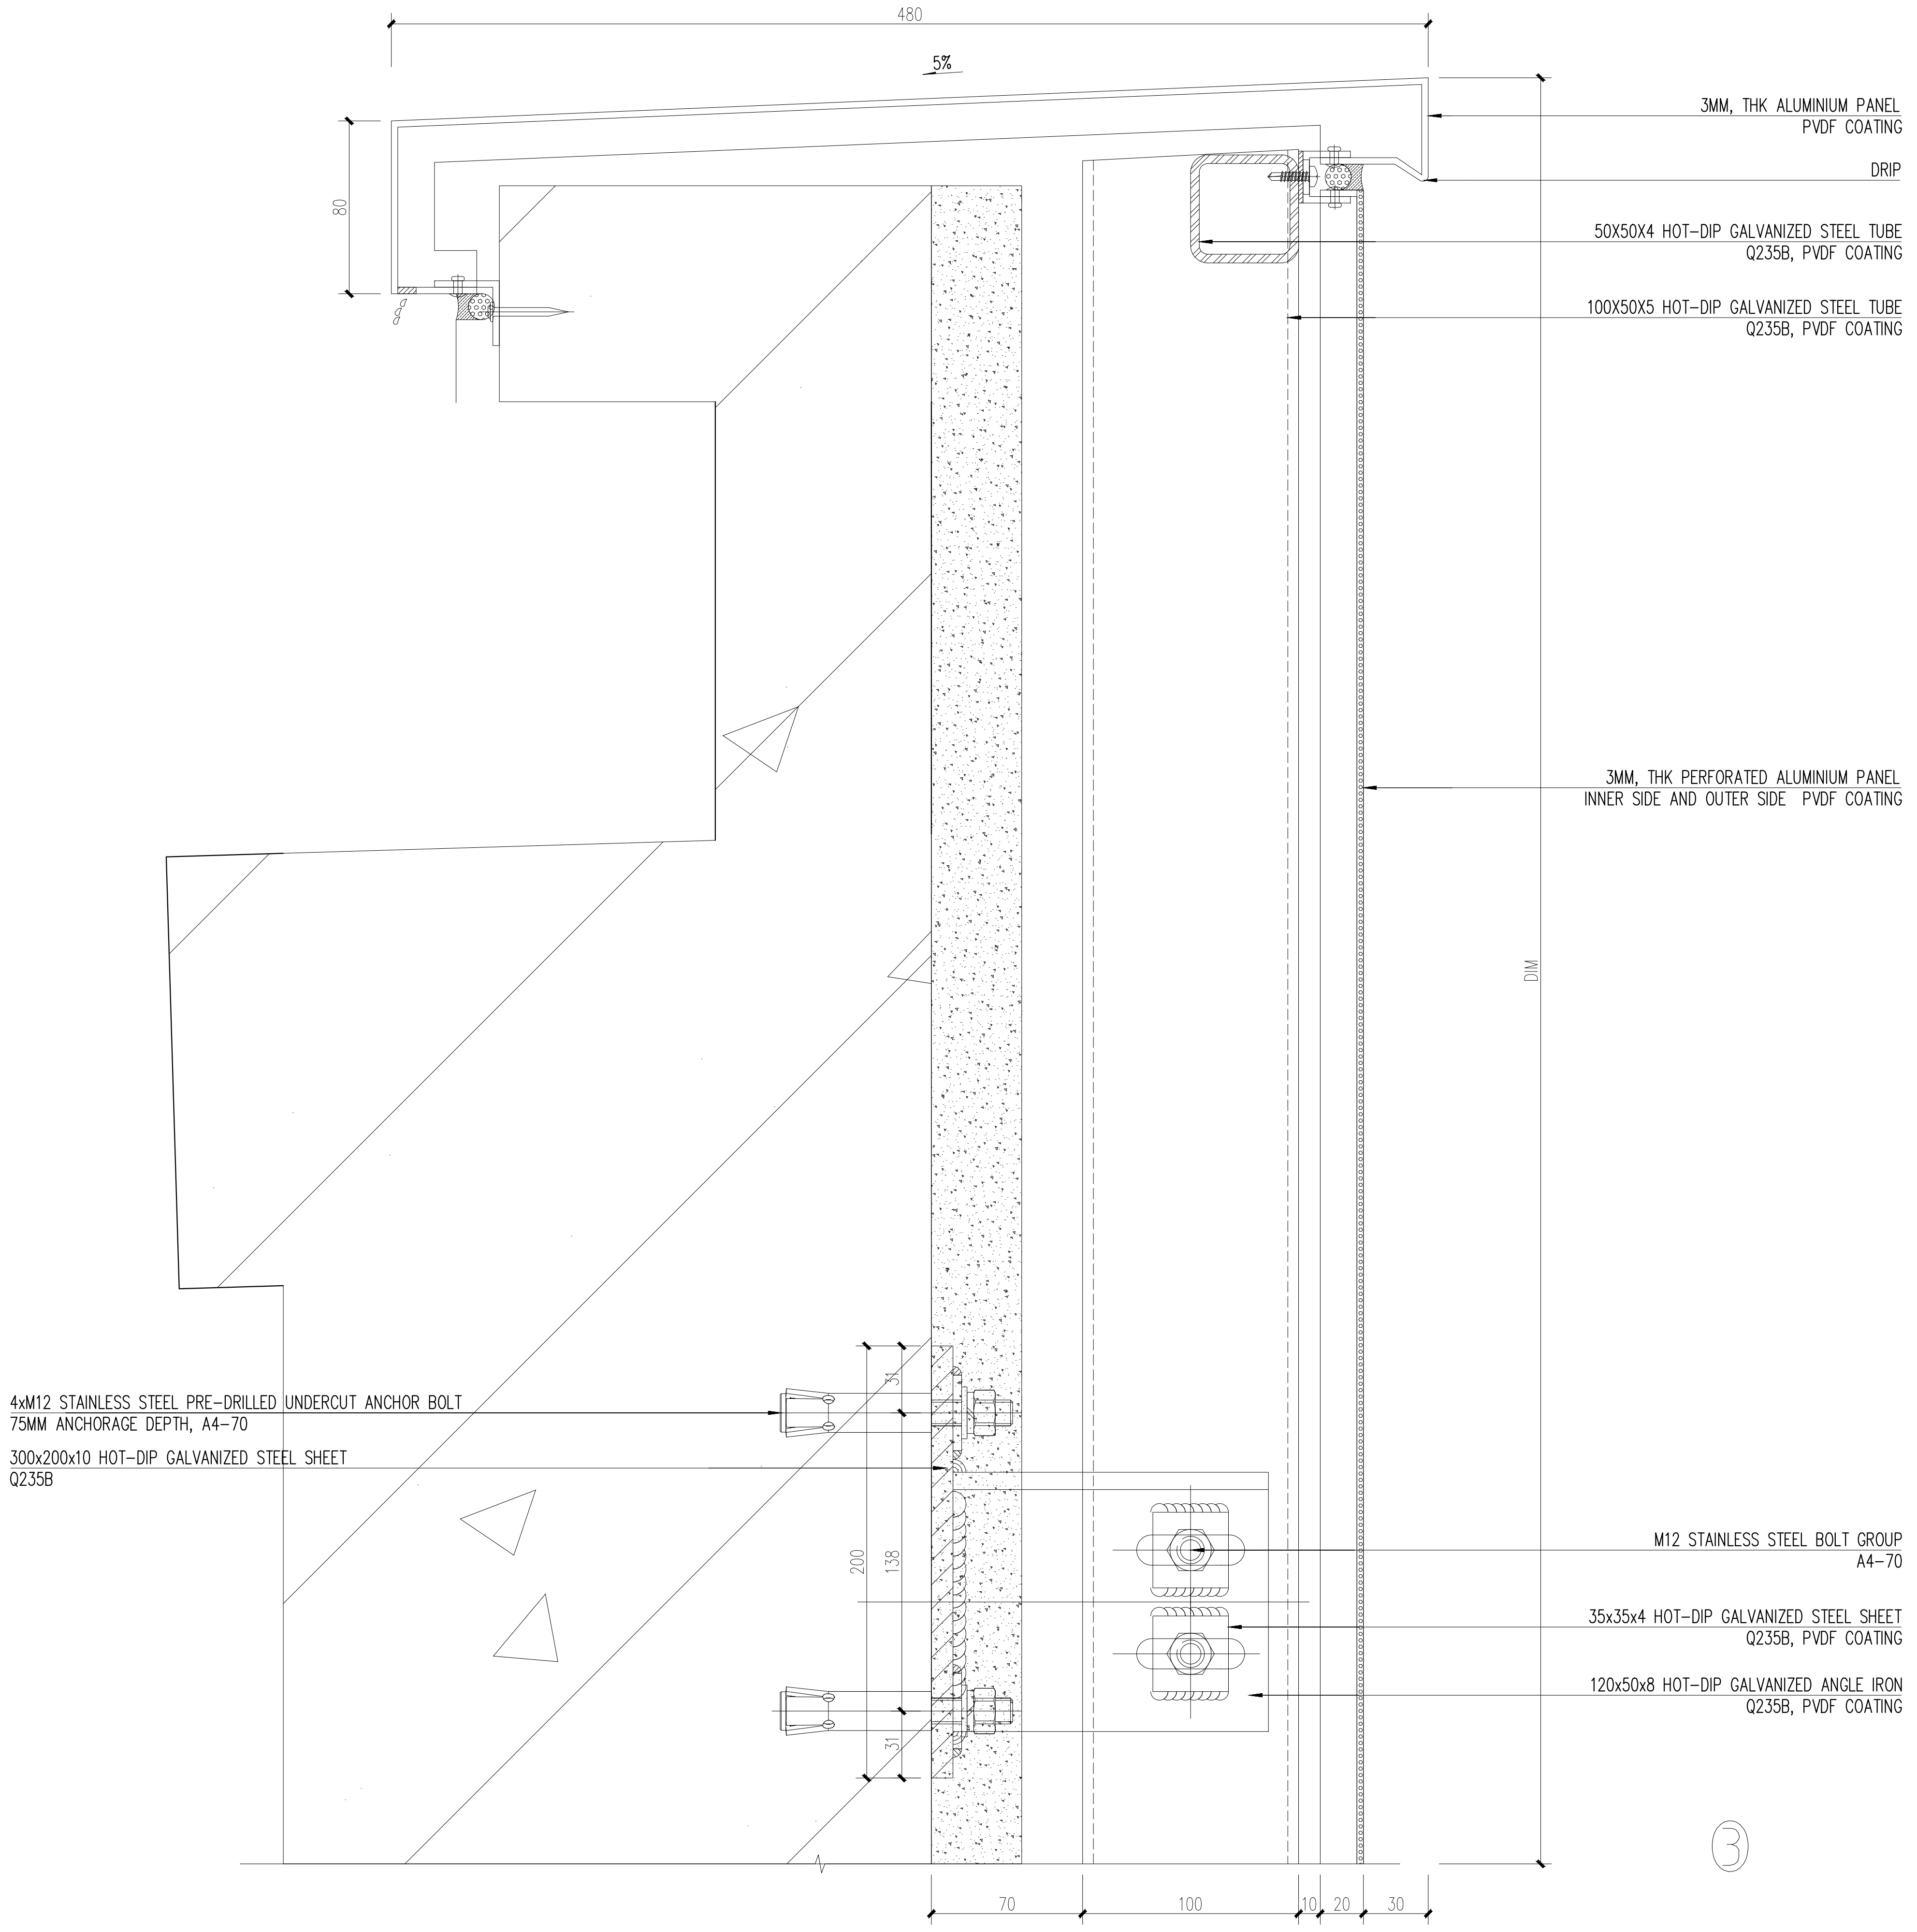
480
5%
80
3MM, THK ALUMINIUM PANEL
PVDF COATING
DRIP
50X50X4 HOT-DIP GALVANIZED STEEL TUBE
Q235B, PVDF COATING
100X50X5 HOT-DIP GALVANIZED STEEL TUBE
Q235B, PVDF COATING
3MM, THK PERFORATED ALUMINIUM PANEL
INNER SIDE AND OUTER SIDE PVDF COATING
DIM
4xM12 STAINLESS STEEL PRE-DRILLED UNDERCUT ANCHOR BOLT
75MM ANCHORAGE DEPTH, A4-70
300x200x10 HOT-DIP GALVANIZED STEEL SHEET
Q235B
M12 STAINLESS STEEL BOLT GROUP
A4-70
35x35x4 HOT-DIP GALVANIZED STEEL SHEET
Q235B, PVDF COATING
120x50x8 HOT-DIP GALVANIZED ANGLE IRON
Q235B, PVDF COATING
200
138
31
31
70
100
10
20
30

③

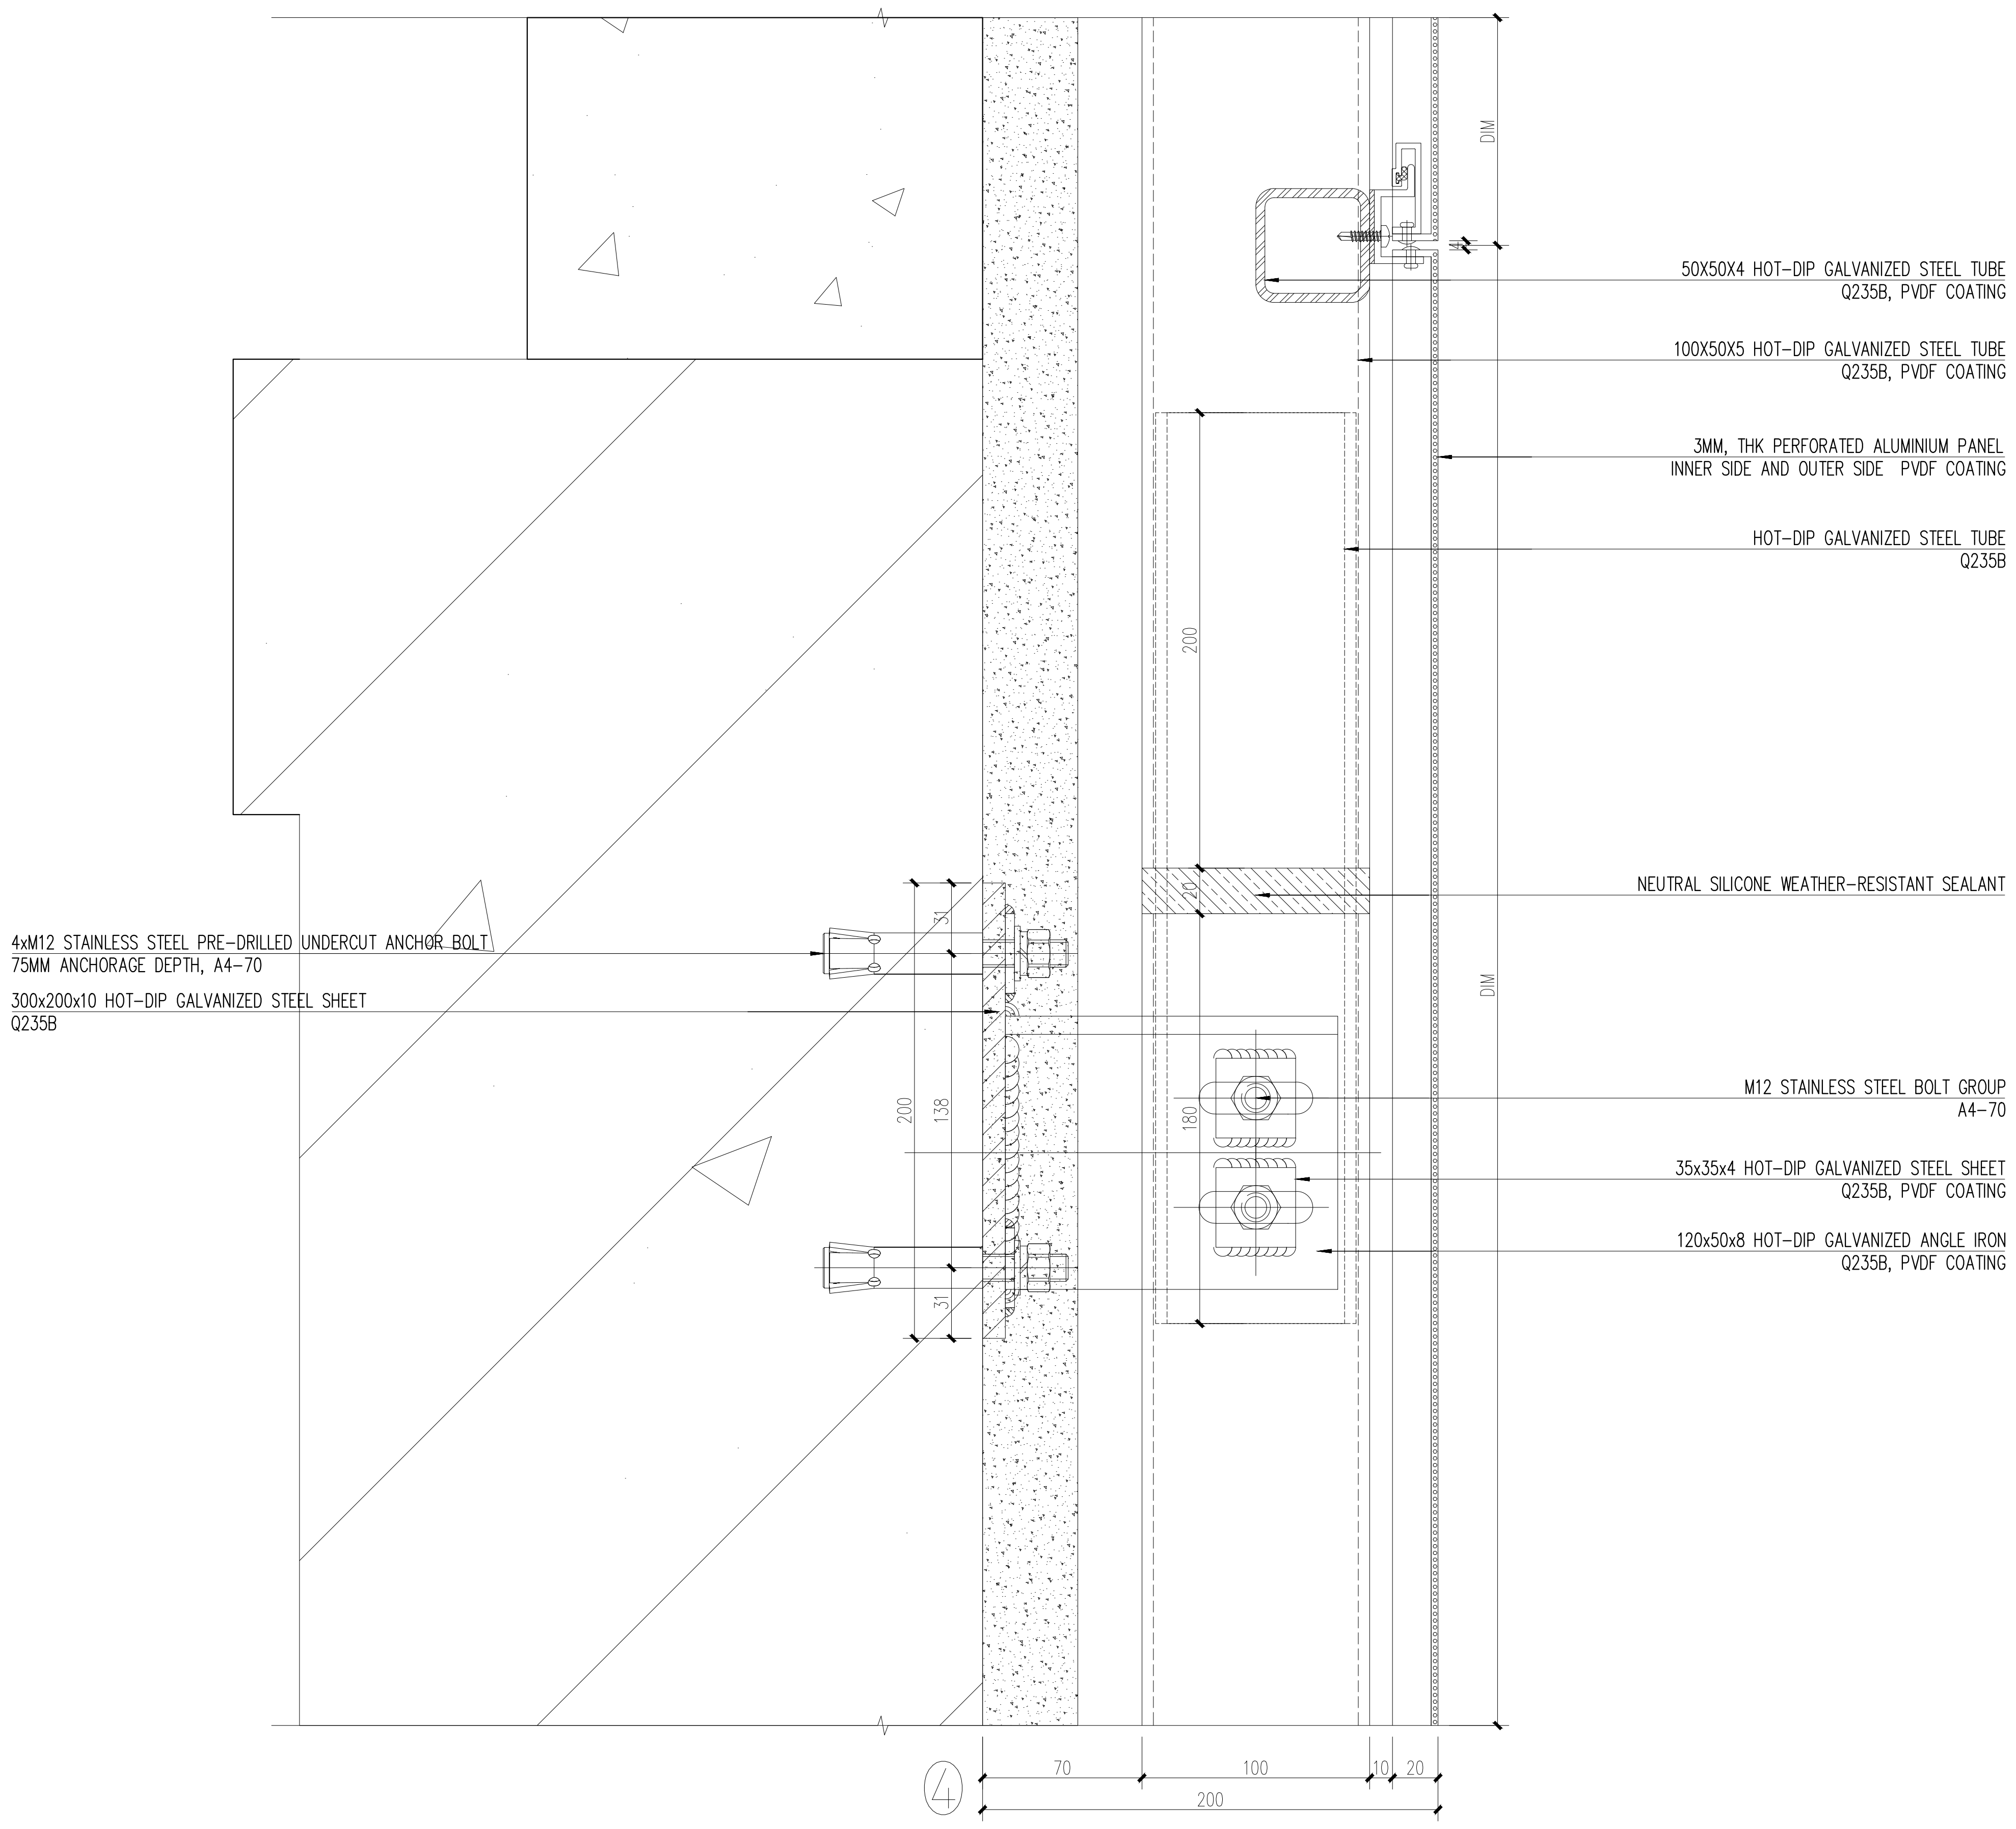
DIM
50X50X4 HOT-DIP GALVANIZED STEEL TUBE
Q235B, PVDF COATING
100X50X5 HOT-DIP GALVANIZED STEEL TUBE
Q235B, PVDF COATING
3MM, THK PERFORATED ALUMINIUM PANEL
INNER SIDE AND OUTER SIDE PVDF COATING
HOT-DIP GALVANIZED STEEL TUBE
Q235B
200
NEUTRAL SILICONE WEATHER-RESISTANT SEALANT
4xM12 STAINLESS STEEL PRE-DRILLED UNDERCUT ANCHOR BOLT
75MM ANCHORAGE DEPTH, A4-70
300x200x10 HOT-DIP GALVANIZED STEEL SHEET
Q235B
DIM
M12 STAINLESS STEEL BOLT GROUP
A4-70
35x35x4 HOT-DIP GALVANIZED STEEL SHEET
Q235B, PVDF COATING
120x50x8 HOT-DIP GALVANIZED ANGLE IRON
Q235B, PVDF COATING
31
200
138
180
31
70
100
10
20
200

④

NOTE : THIS PRINT IS OF A CONFIDENTIAL NATURE, IT SHALL NOT BE TRACED,PHOTOGRAPHED,PHOTOSTATED OR REPRODUCED IN ANY MANER,NOR USED FOR ANY PURPOSE WHATSOEVER EXCEPT BY WRITTEN PERMISSION

CLIENT :

GULF EDGE DC 01

87 Wireless Road, M Thai Tower 11th. Floor, All Seasons Place, Lumpini,
Pathumwan, Bangkok 10330, Thailand

CONTRACTOR :

华西发展(泰国)有限公司
บริษัท หัวซือ ดีเวลลอปเม้นต์ (ประเทศไทย) จำกัด
HUASHI DEVELOPMENT CO.,LTD
No. 202, Room No. 1403, 14/F, Le Concorde Building,
Ratchadapisek Road, Huaykhwang Sub-District,
Huaykhwang District, Bangkok Metropolitan 10310.

CONSULTANT :

ARbay
บริษัท เอ อาร์ เบย์ จำกัด
ARbay Company Limited
31 st Floor Bangkok Insurance Building
25 South Sathorn road Thungmahamek
Sathorn Bangkok 10120 THAILAND
T +66 (0) 2286 8199
F +66 (0) 2286 2863
info@arbay.co.th

CONSULTANT :

Qbic Engineers & Architects Co.,Ltd.
8 Soi KALONG 4 SANAMBINNAM ROAD,
THASAI SUB-DISTRICT, MUANG NONTHABURI DISTRICT
, NONTHABURI.
Tel 662-950-4374
Fax 662-580-3231
E-Mail : qbic@qbic.co.th, www.qbic.co.th
QBIC ENGINEERS AND ARCHITECTS CO.,LTD.

CONSULTANT :

MITR
MITR TECHNICAL CONSULTANT CO.,LTD.
1168/8 12th FLOOR, LUMPINI TOWER BUILDING,
RAMA IV RD., THUNGMAHAMEK, SATHORN, BANGKOK 10120, THAILAND
TEL : 0-2679-9079-84
FAX : 0-2679-9085 E-mail: mitr_dd@mitr.com

Architect :	SIGNATURE
ประกิต พนานุรัตน์ วสถ. 580 ที่อยู่ 251/1 ถ.จารุเมือง แขวงรองเมือง เขตปทุมวัน กรุงเทพมหานคร โทรศัพท์ 02-286-8199	

Structural Engineer :	SIGNATURE
วิศวกรผู้ออกแบบโครงสร้าง	
ณัฐสม สงวนวงษ์ วย 1423 ที่อยู่ 2/1 ซ.รามคำแหง 150 ถ.รามคำแหง แขวง สะพานสูง เขต สะพานสูง กทม. 10240	ณัฐสม สงวนวงษ์

Structural Inspector :	SIGNATURE
วิศวกรผู้ตรวจสอบโครงสร้าง	
โกมล จุฑาภัทร วย 964 ที่อยู่ 24/18 ซ.นวมินทร์ 129 ถ. นวมินทร์ แขวง นวลจันทร์ เขต บึงกุ่ม กทม. 10230	

Electrical Engineer :	SIGNATURE
วิศวกรผู้ออกแบบระบบไฟฟ้ากำลัง	
นายสุภัทร บูรณวิทย์ วฟก.1265 ที่อยู่ 21 ซอยทานสัมฤทธิ 13 ตำบลท่าทราย อ.เมืองนนทบุรี จ.นนทบุรี 11000	สุภัทร บูรณวิทย์

Mechanical Engineer :	SIGNATURE
วิศวกรผู้ออกแบบระบบเครื่องกลและปรับอากาศ	
นายประสิทธิ์ เกียวสุนทร วก.1221 ที่อยู่ 44/372 ซอยบางกระดี 35/1 แขวงแสมดำ เขตบางขุนเทียน กทม. 10150	ประสิทธิ์

Sanitary Engineer :	SIGNATURE
วิศวกรผู้ออกแบบระบบสุขาภิบาล และดับเพลิง	
นายทศวรรษ สนันฤทธิ์ วส. 215 ที่อยู่ บ้านเลขที 99/107 หมู่ที 3 ต.ศีรษะจรเข้น้อย อ.บางเสาธง จ.สมุทรปราการ 10540	ทศวรรษ

ISSUE/REVISION

REV.	DESCRIPTION	DATE
A	90% DEVELOPED	09/05/2026

PROJECT NAME :

GEDC 01

LOCATION:
Nikhom Phattana district, Rayong ,industrial estate,CPGC

BUILDING :

90% DEVELOPED

TITLE :

CURTAIN WALL DETAIL

JOB NO.	SCALE 1:2
DRAWN LXP	REF.
CHECKED LJC	DWG.NO.
APPROVED LXD	MPK01A-90-A-CWD-002
DATE 2026.05.09	