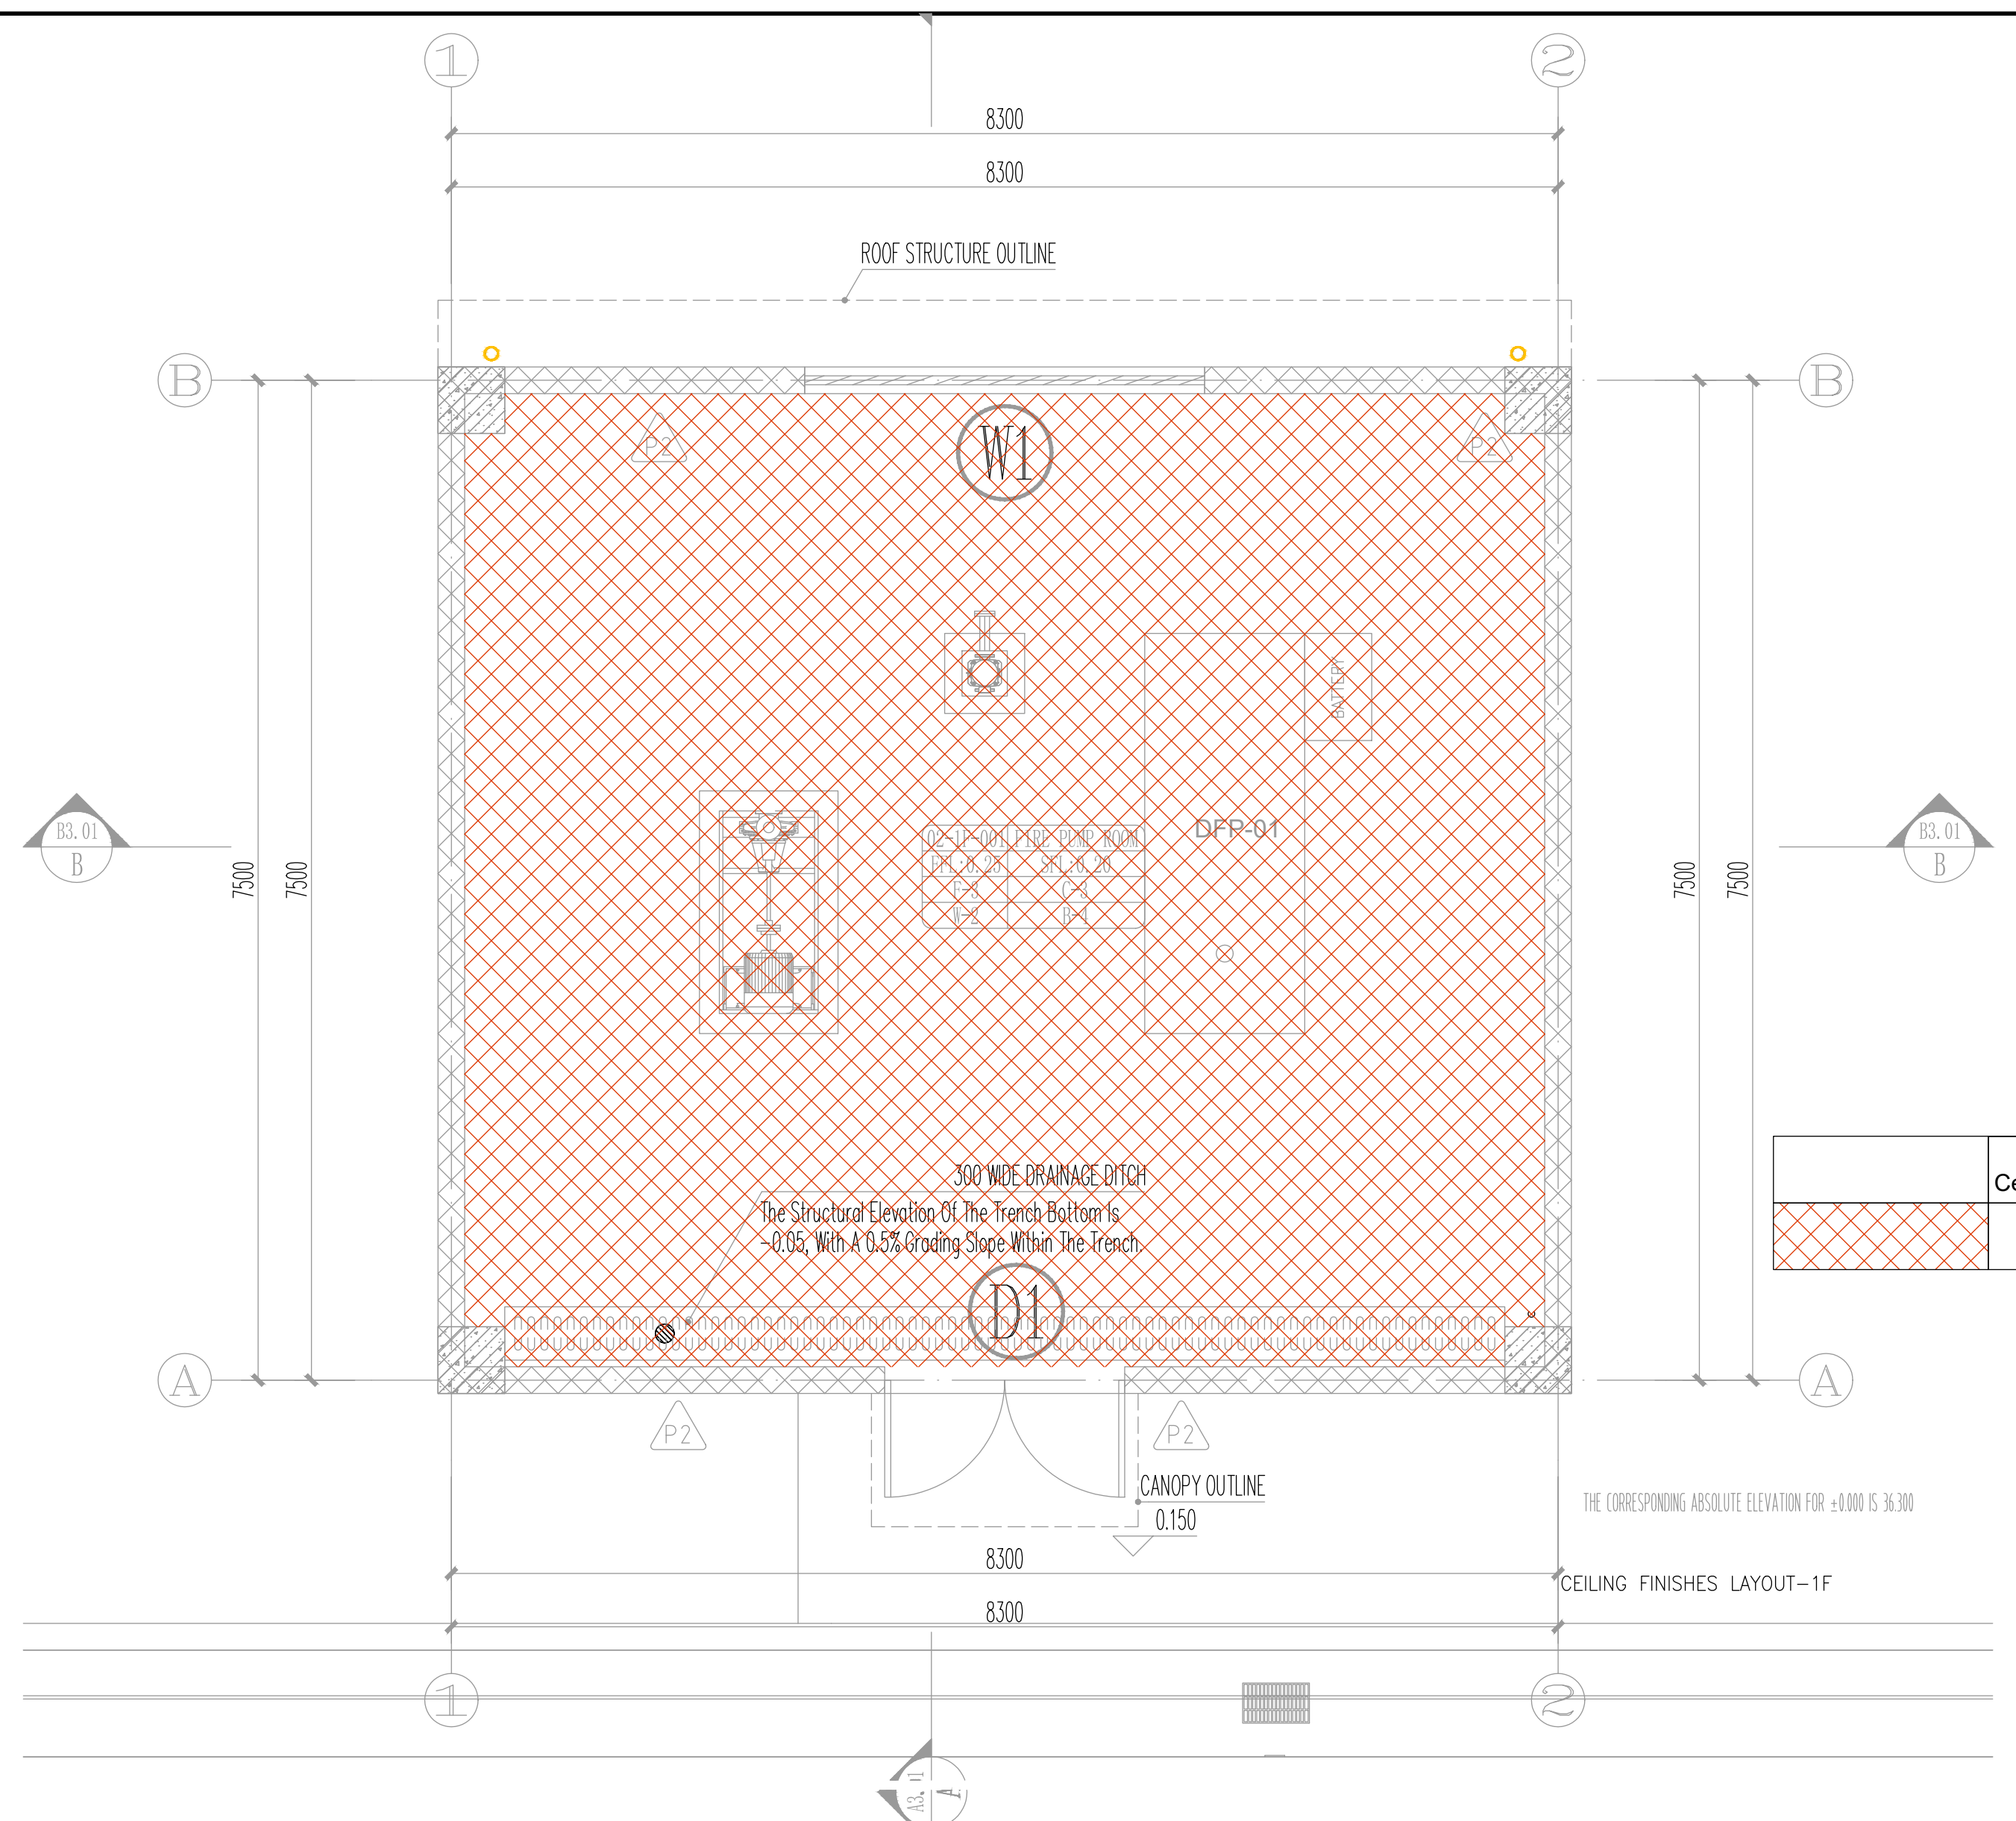
8300
8300
ROOF STRUCTURE OUTLINE
W1
DFP-01
7500
7500
300 WIDE DRAINAGE DITCH
The Structural Elevation Of The Trench Bottom Is
-0.05, With A 0.5% Grading Slope Within The Trench.
D1
P2
CANOPY OUTLINE
0.150
THE CORRESPONDING ABSOLUTE ELEVATION FOR ±0.000 IS 36.300
A
B
1
2

CEILING FINISHES LAYOUT-1F

	Ceiling No.	Description	Ceiling Material & Finish Specification	Vender
▨	C-3	MOISTURE-PROOF PAINT	MOISTURE-PROOF PAINT ON CONCRETE CEILING SLAB	

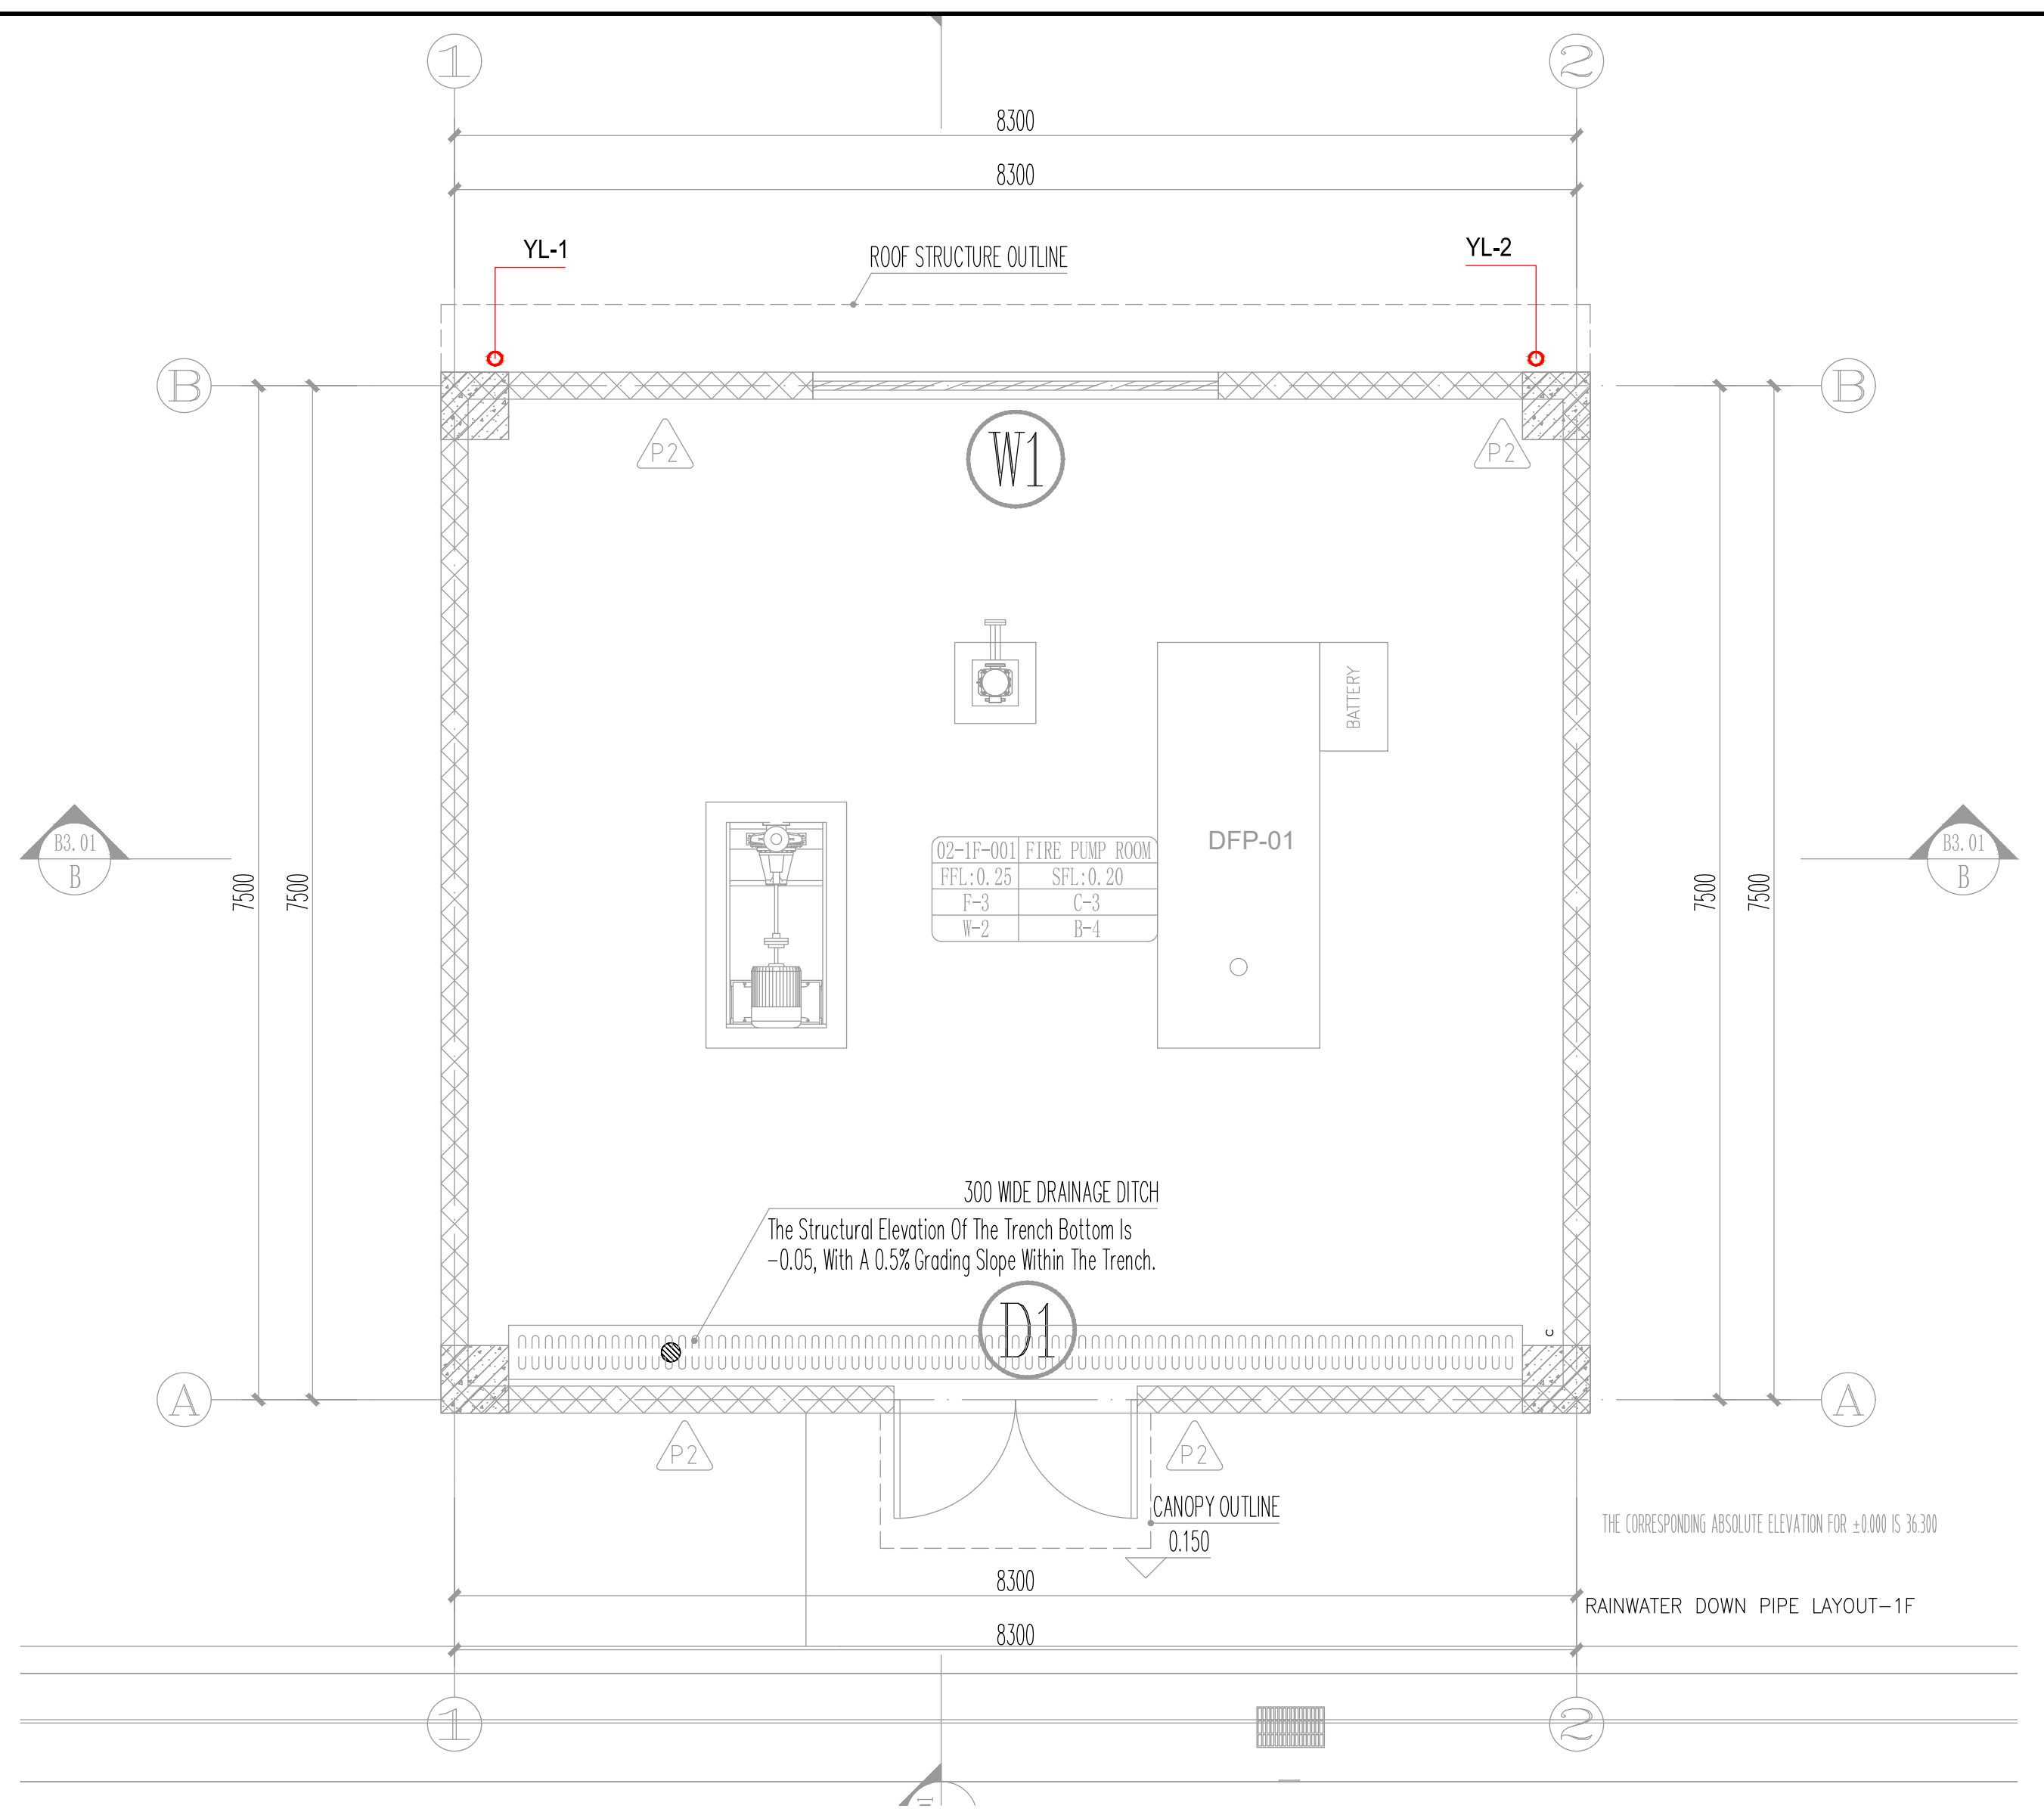
8300
8300
YL-1
ROOF STRUCTURE OUTLINE
YL-2
W1
DFP-01
7500
7500
300 WIDE DRAINAGE DITCH
The Structural Elevation Of The Trench Bottom Is
-0.05, With A 0.5% Grading Slope Within The Trench.
D1
P2
CANOPY OUTLINE
0.150
THE CORRESPONDING ABSOLUTE ELEVATION FOR ±0.000 IS 36.300
A
B
1
2

RAINWATER DOWN PIPE LAYOUT-1F

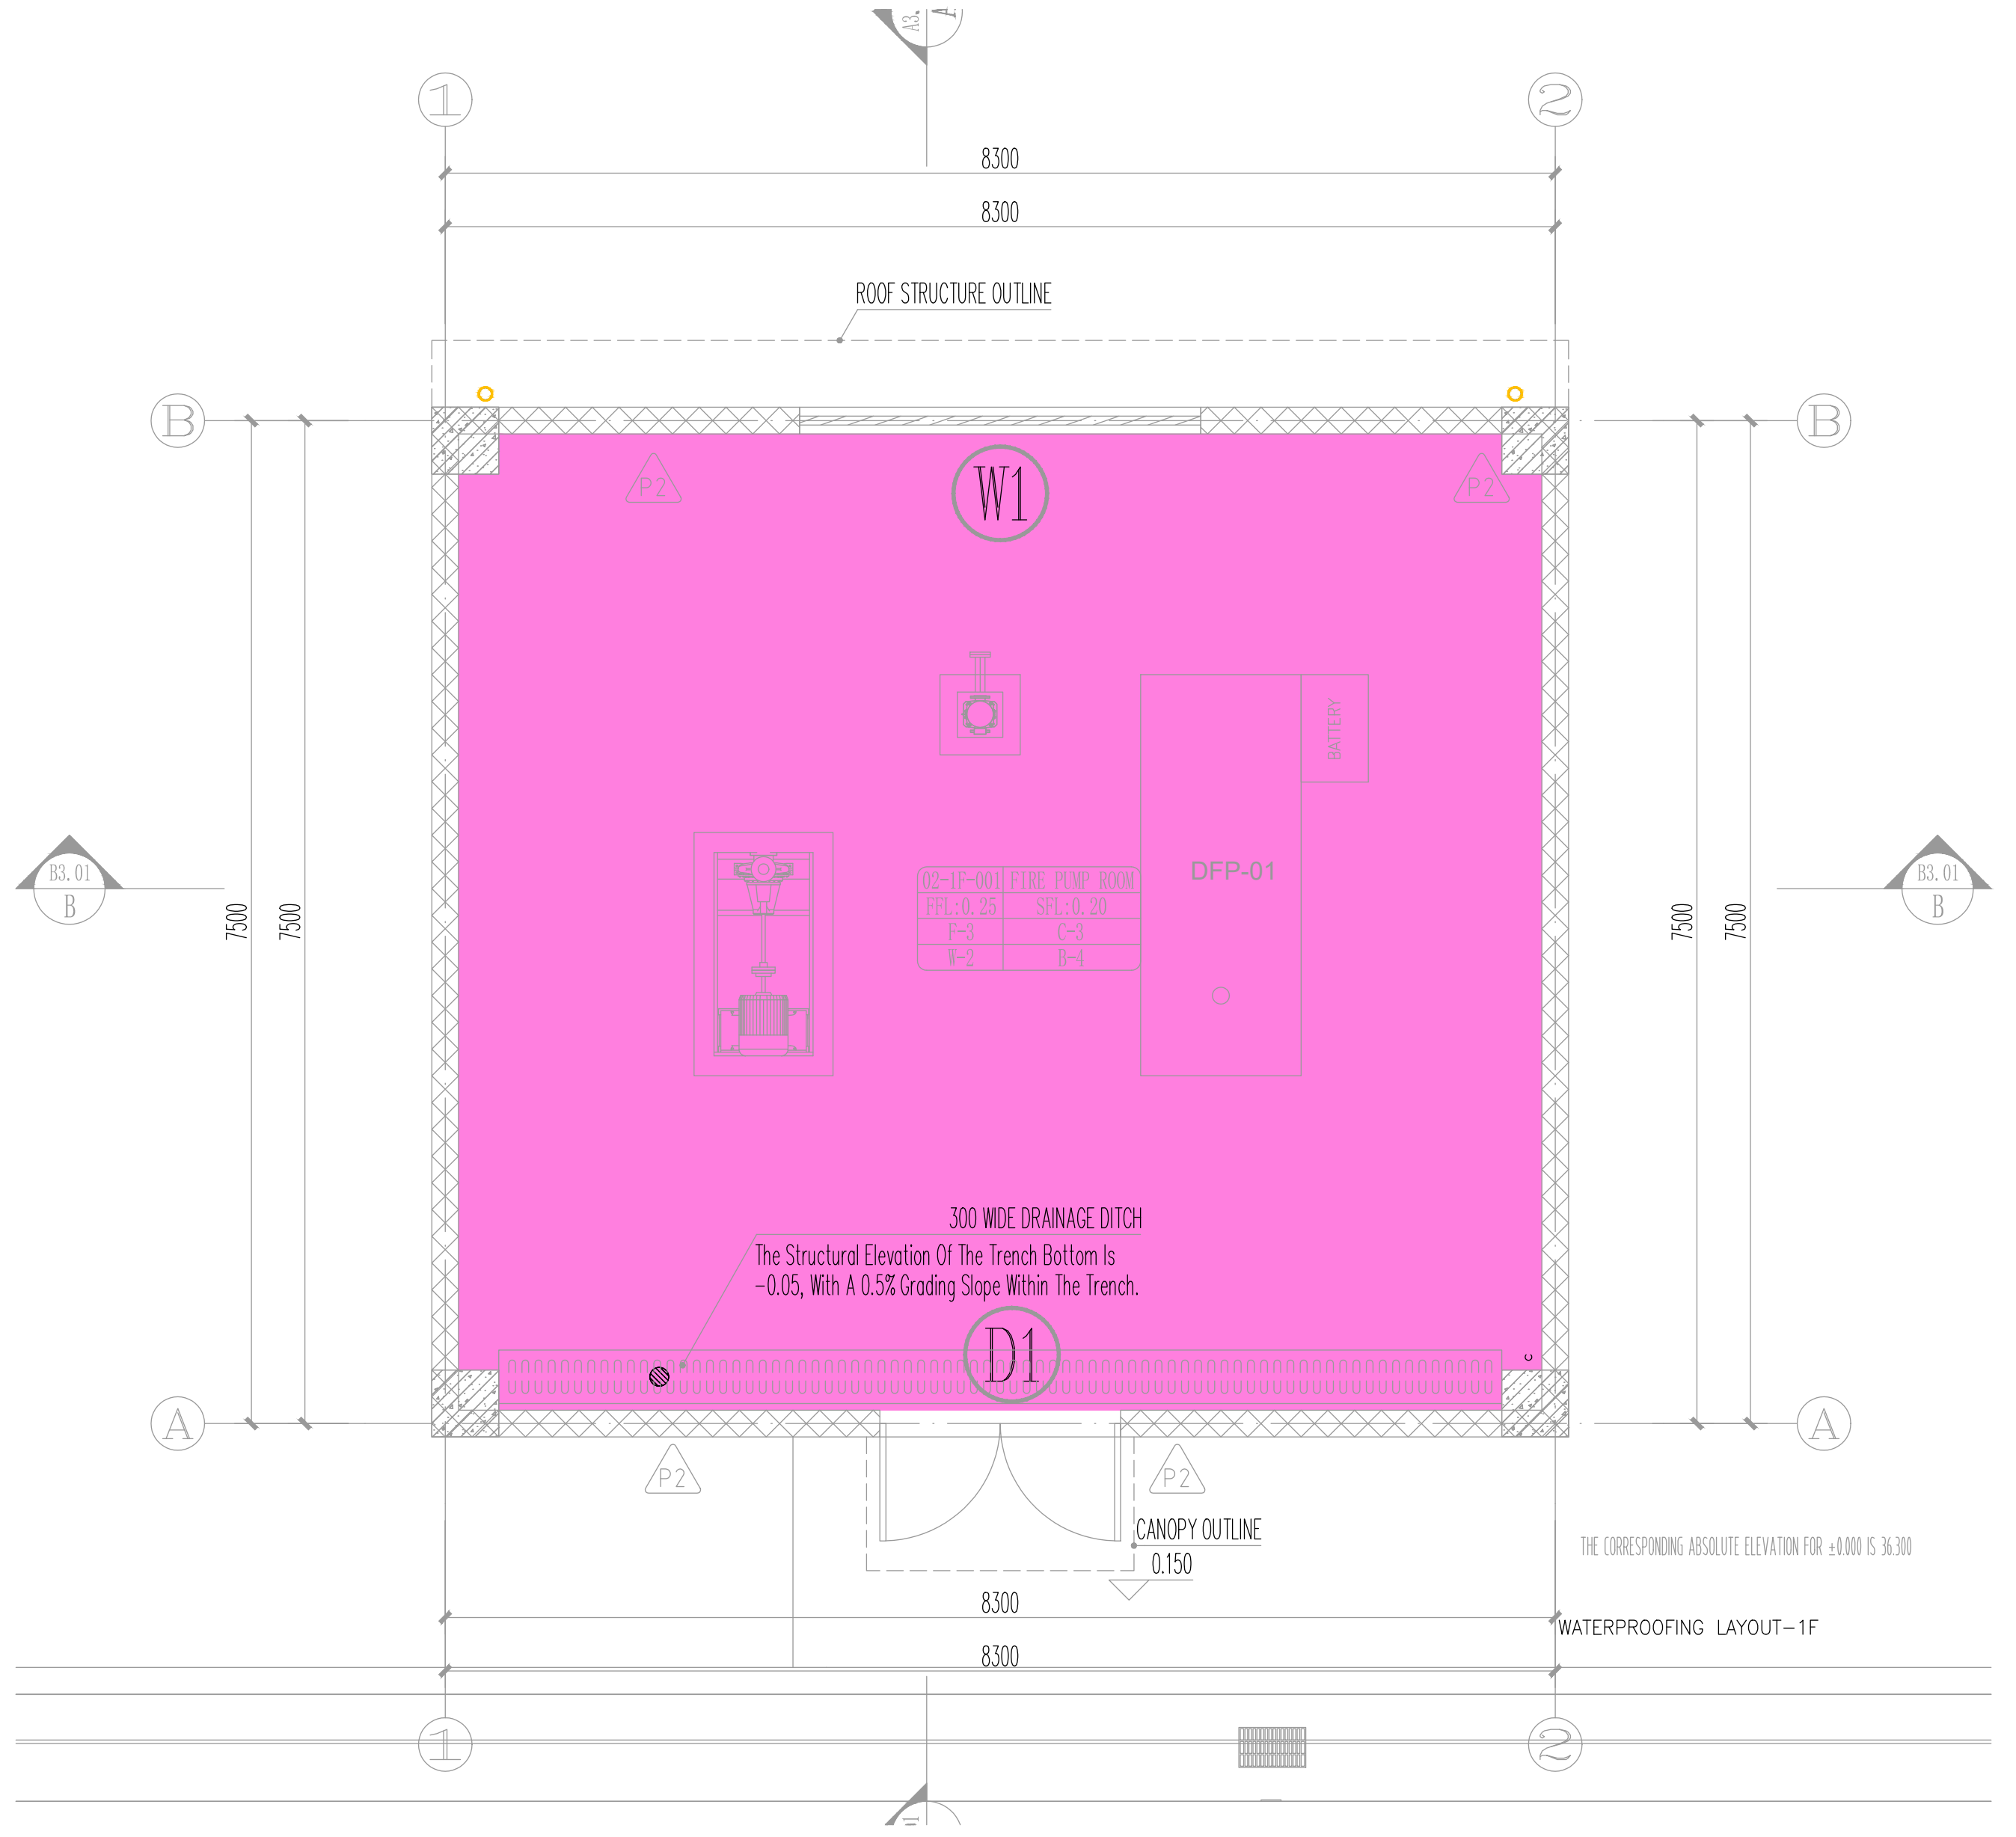
8300
8300
ROOF STRUCTURE OUTLINE
W1
DFP-01
7500
7500
300 WIDE DRAINAGE DITCH
The Structural Elevation Of The Trench Bottom Is
-0.05, With A 0.5% Grading Slope Within The Trench.
D1
P2
CANOPY OUTLINE
0.150
THE CORRESPONDING ABSOLUTE ELEVATION FOR ±0.000 IS 36.300
A
B
1
2

WATERPROOFING LAYOUT-1F

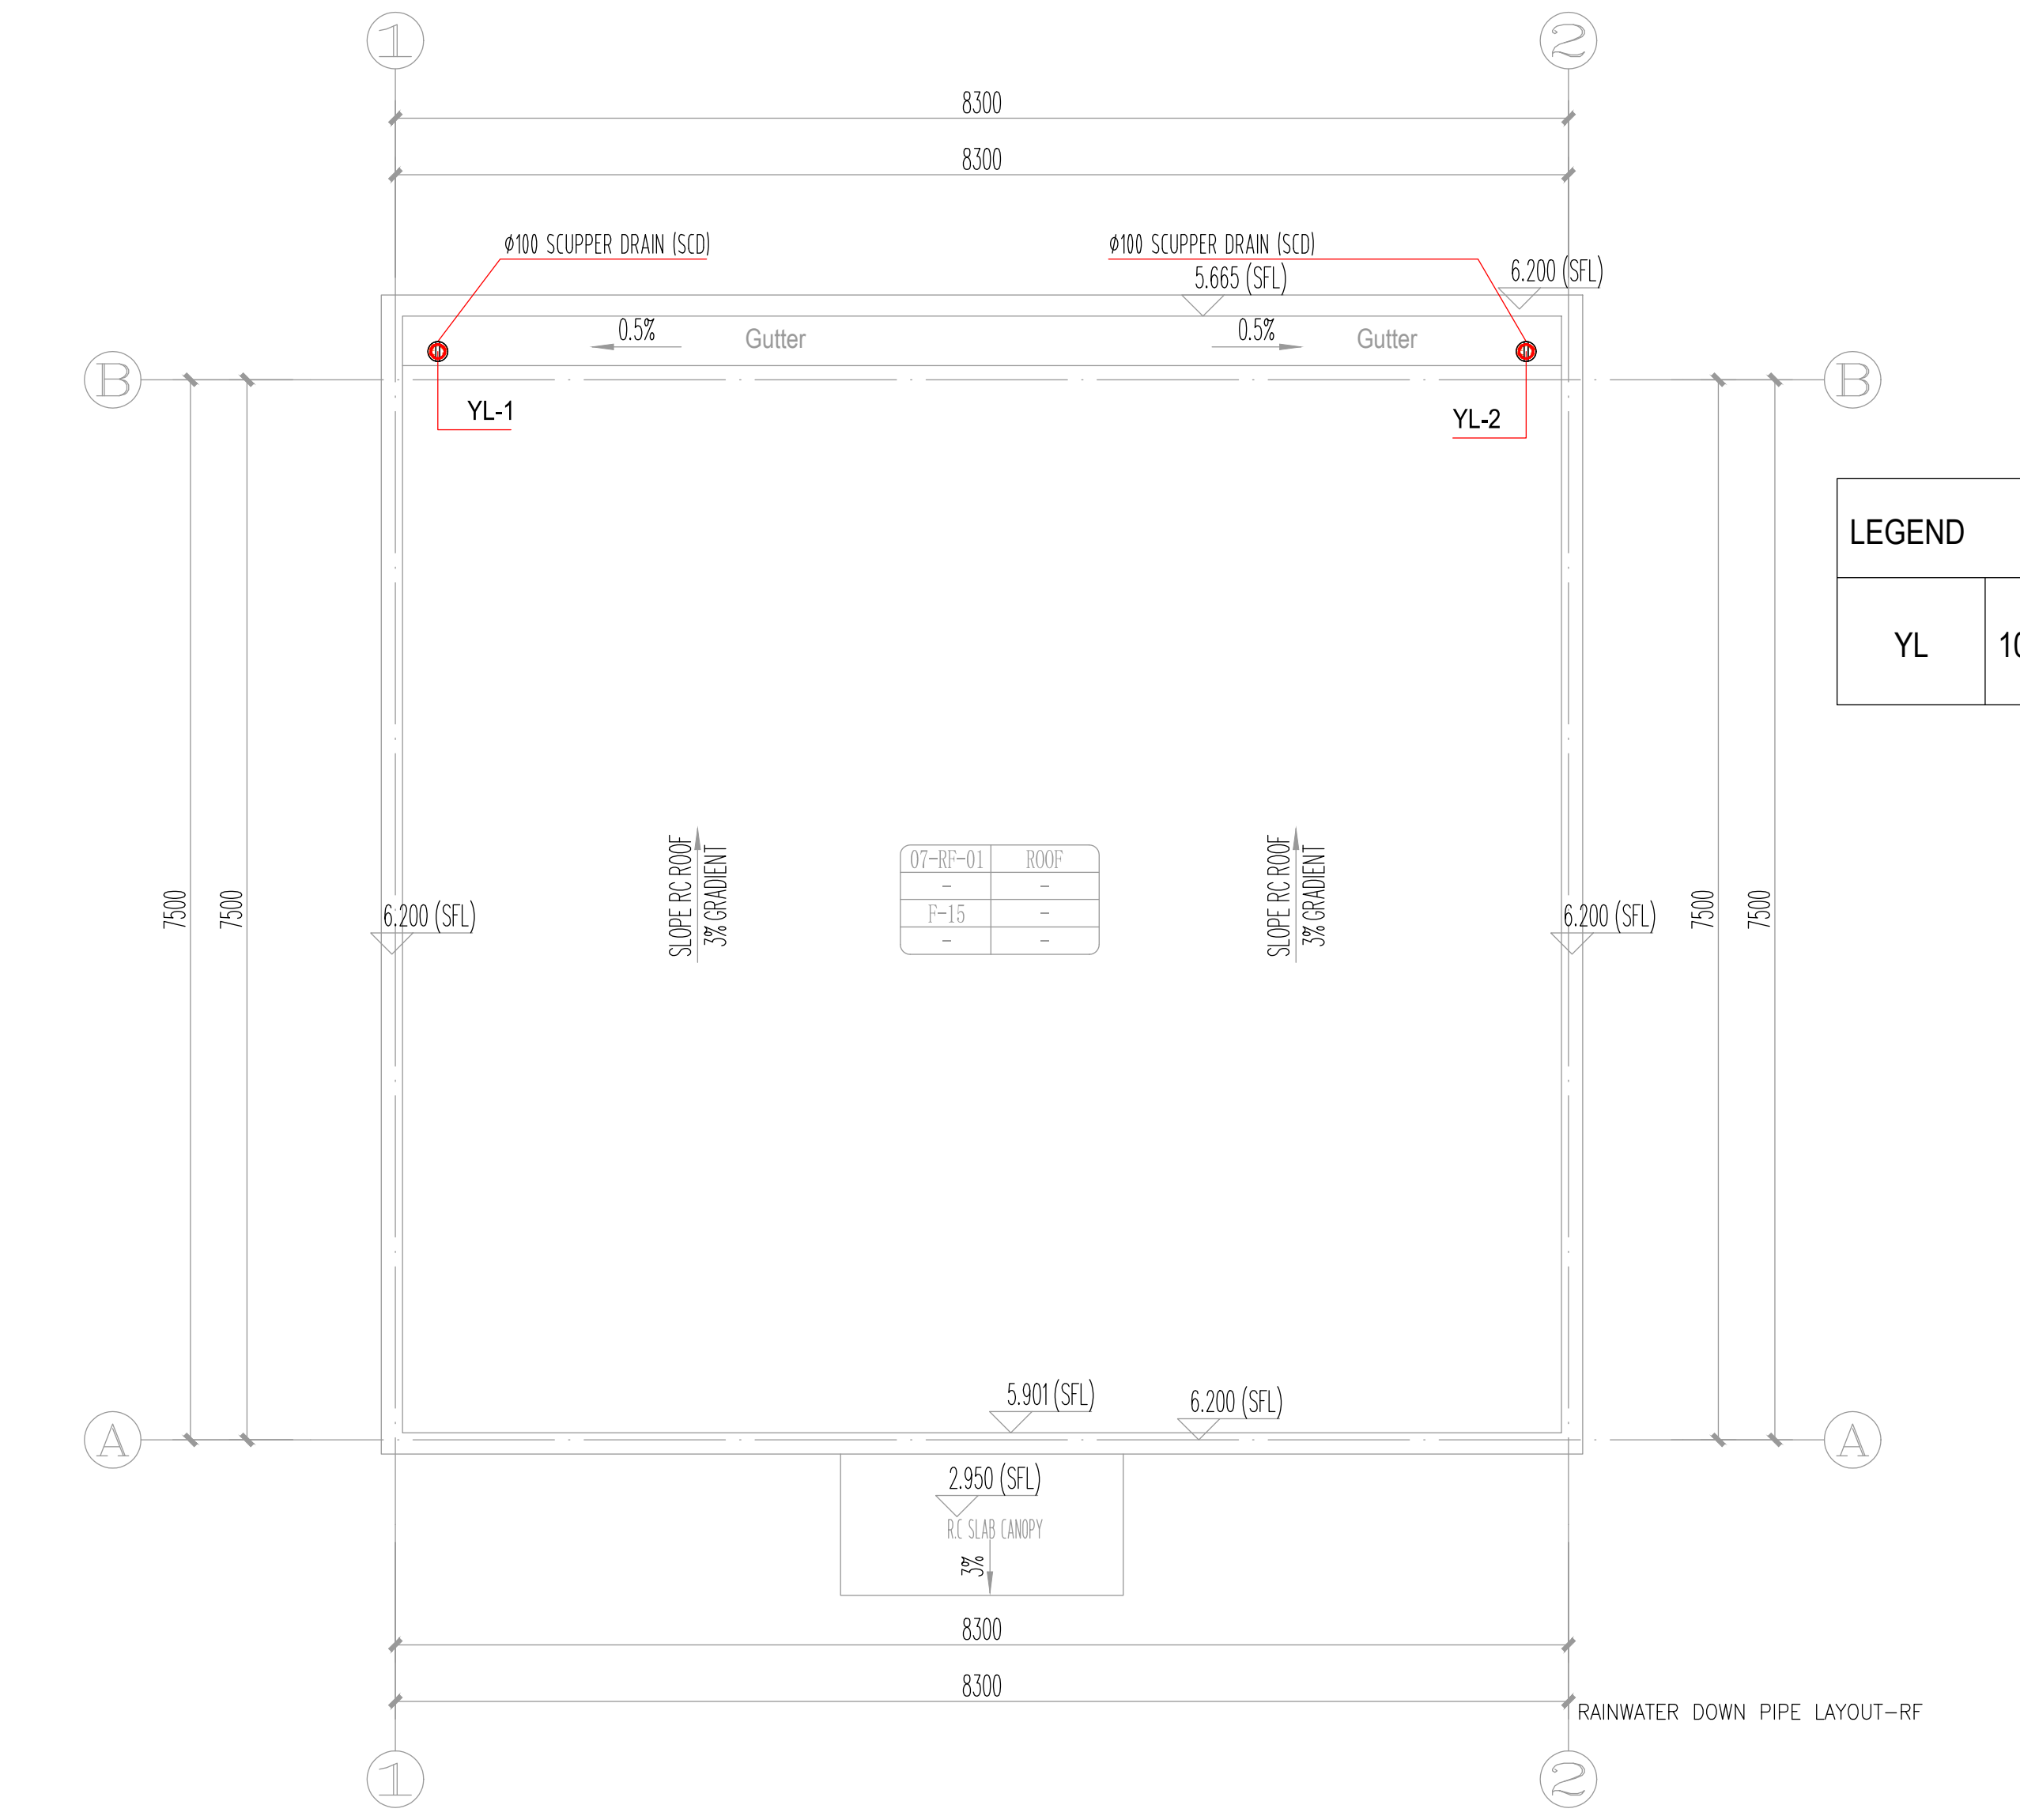

RAINWATER DOWN PIPE LAYOUT-RF

LEGEND	
YL	100MM HDPE

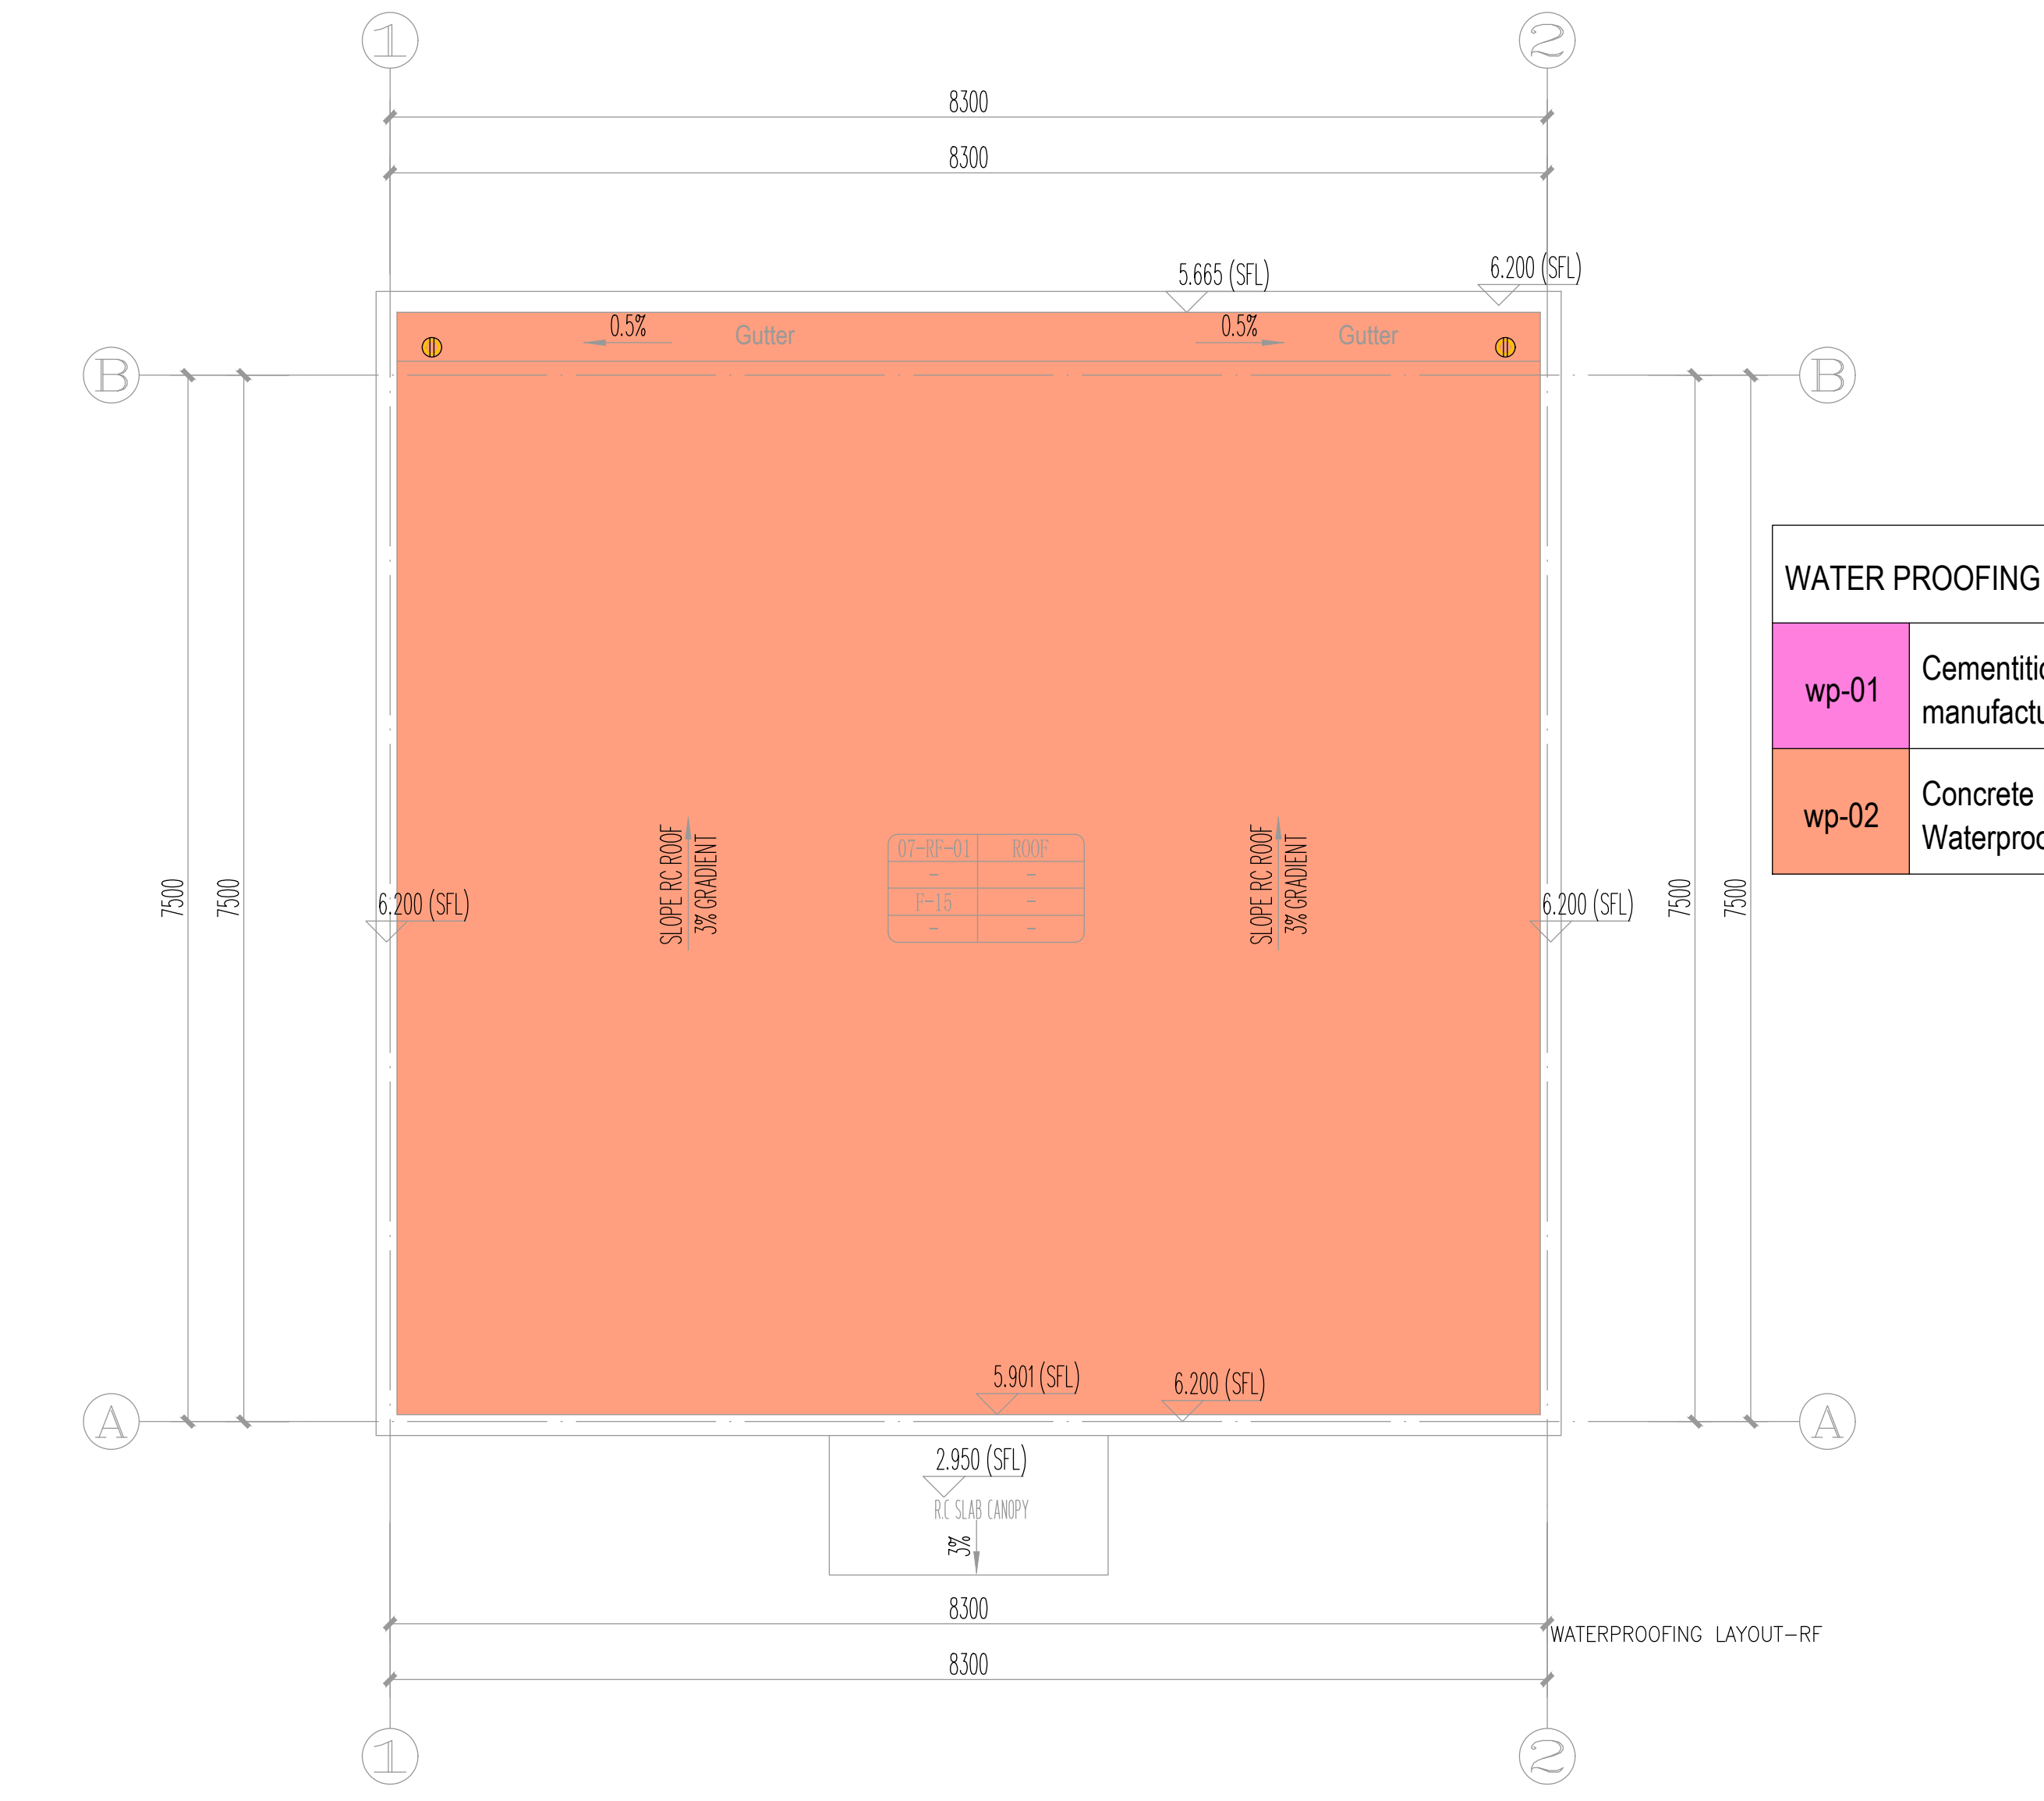

WATERPROOFING LAYOUT-RF

WATER PROOFING	
wp-01	Cementitious waterproofing(to manufacturer's detail)
wp-02	Concrete Roof + Curing Agent+ Waterproofing

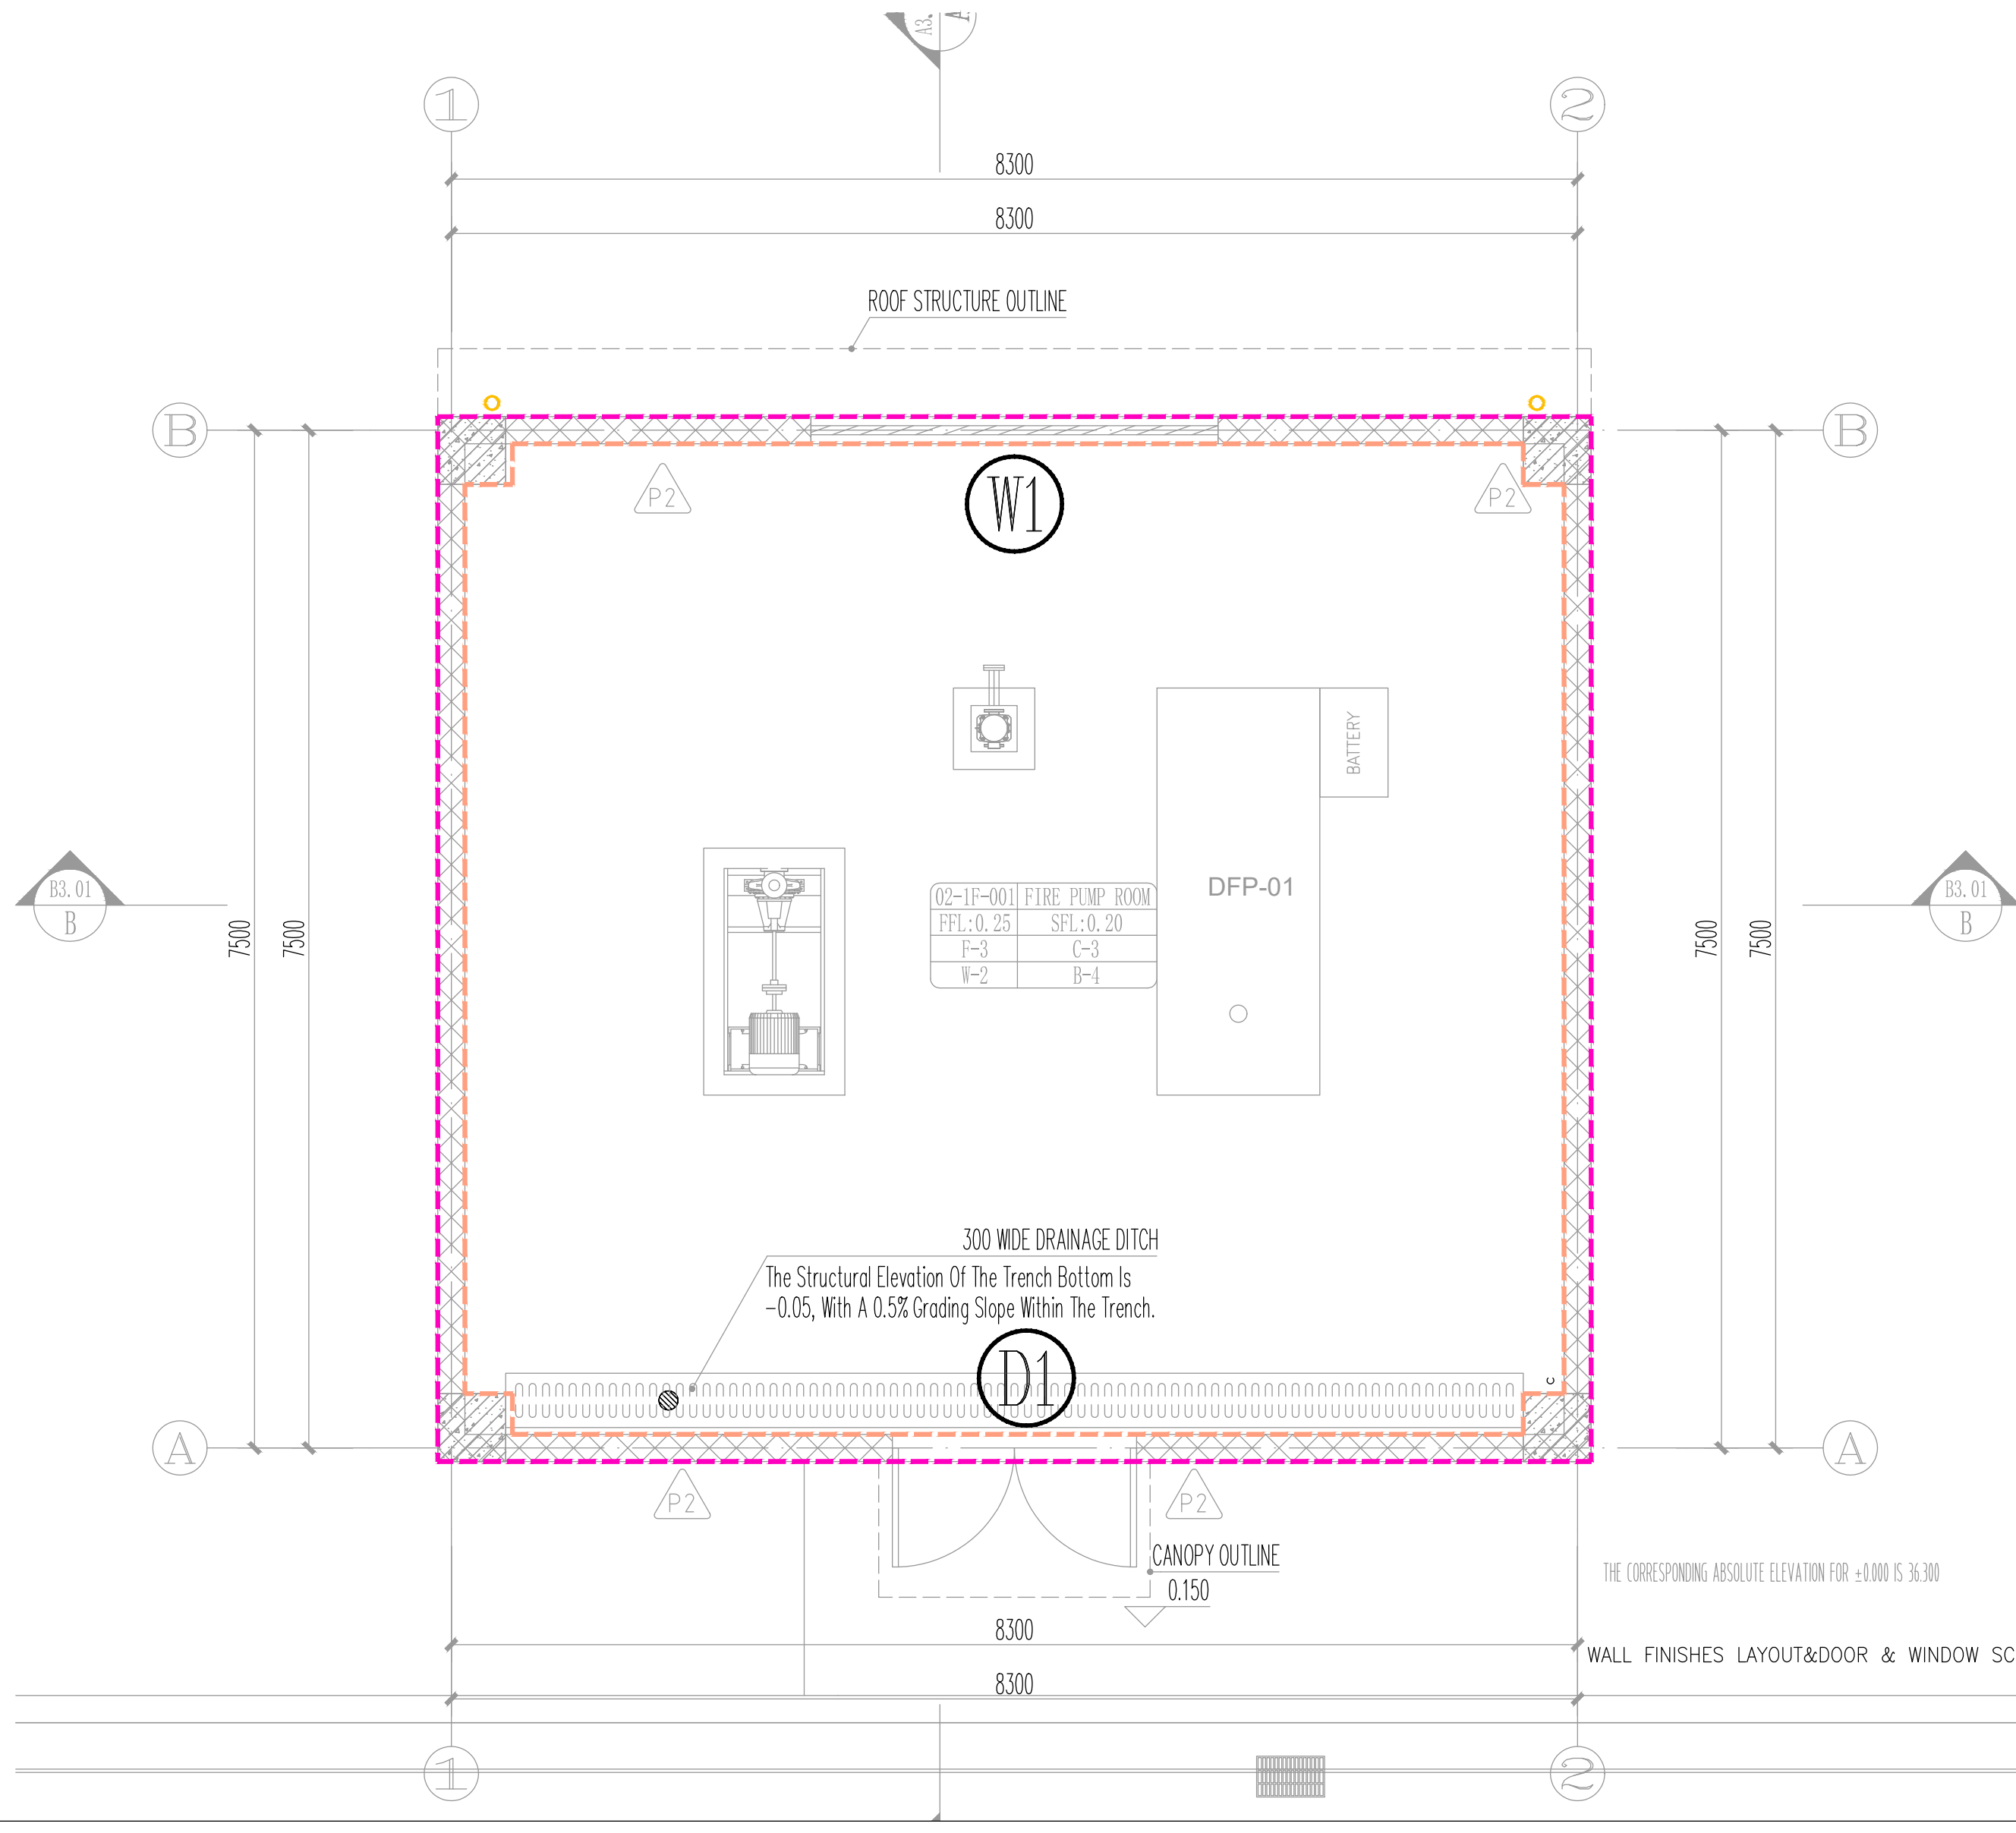
8300
8300
ROOF STRUCTURE OUTLINE
W1
DFP-01
7500
7500
300 WIDE DRAINAGE DITCH
The Structural Elevation Of The Trench Bottom Is
-0.05, With A 0.5% Grading Slope Within The Trench.
D1
P2
CANOPY OUTLINE
0.150
THE CORRESPONDING ABSOLUTE ELEVATION FOR ±0.000 IS 36.300
A
B
1
2

WALL FINISHES LAYOUT&DOOR & WINDOW SCHEDULE-1F

LEGEND	Wall No.	Description	TILE SIZE(MM) WIDTH X DEPTH
- - - -	W-2	Skim Coat With Scrub Resistant Paint	Scratch-resistant
- - - -	W-5	12mm Thk Waterproof Homogenous Tile	Waterproof

DOOR SCHEDULE

	DESCRIPTION	SISE(MM) WIDTH X HEIGHT
D1	G.I METAL FRAME DOUBLE LEAF 2 HOUR FIRE RATED SOLID STEEL DOOR PANEL	1800 X 2400
W1	1.4mm THK.POWDER COATED ALUMN. FRAME FIXED DETACHABLE LOUVERS TO MANUF'S DETAIL;THE INNER SIDE OF THE SHUTTERS SHOULD BE EQUIPPED WITH INSECT AND RODENT PROOF WIRE MESH；EXTERNAL LOUVRES SHALL BE DOUBLE BANK RAINPROOFED TO PREVENT WATER INGRESS.	3000 X 900

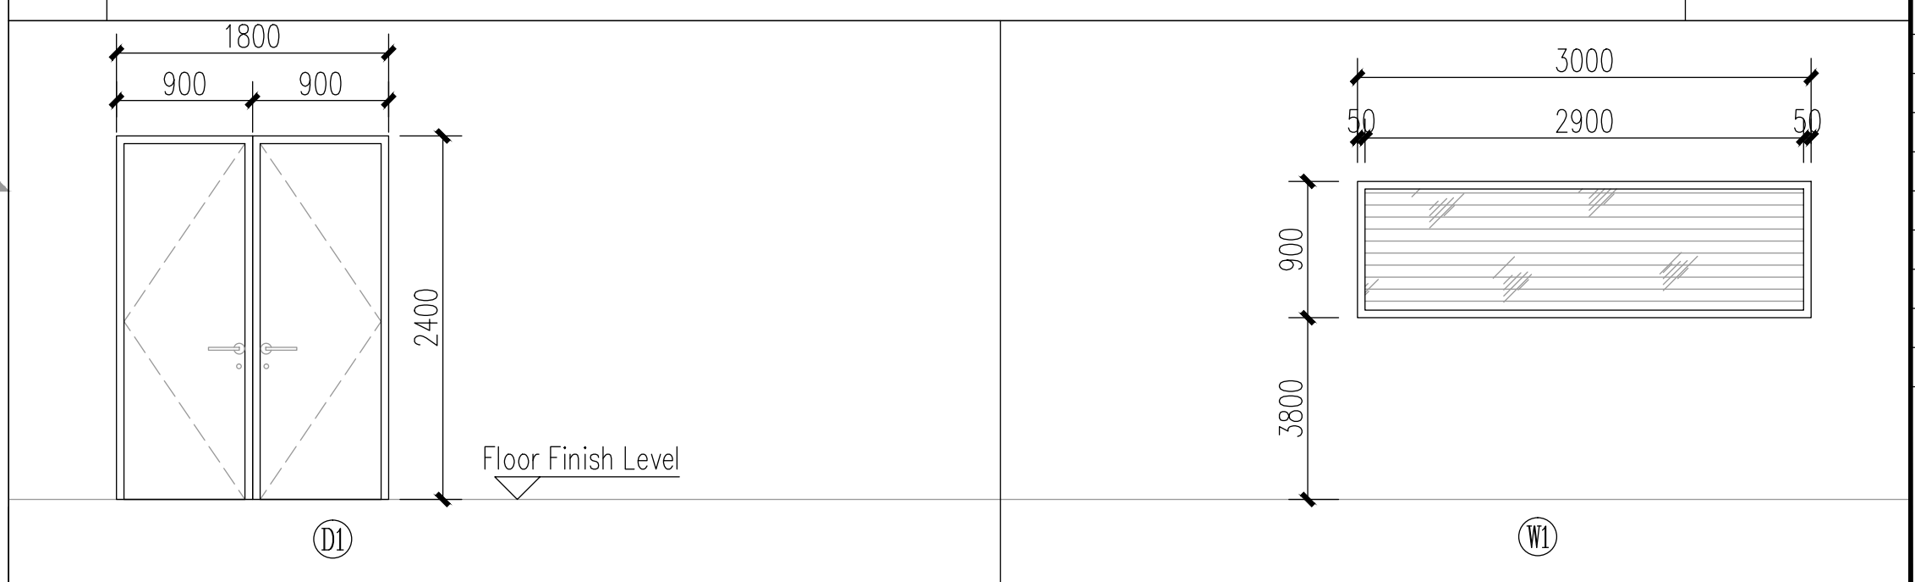

FUNCTON	FIRE PUMP ROOM、DOMESTIC PUMP ROOM(FOR FUTURE)	FUNCTON	FIRE PUMP ROOM、DOMESTIC PUMP ROOM(FOR FUTURE)
TYPE	STEEL SINGLE DOOR,2HRS FIRE RATED	TYPE	Aluminum Louvre Window
	SINGLE SWING	HARDWARE	
HARDWARE	DOOR CLOSER	Total	5
	DOOR STOPPER		
	HANDLE		
	KEY		
Total	2		

LEED: Remark for all door & window glazing
Exterior Glazing Performance:
SHGC=0.3 or better
U-value = 2.0 W/(m2K) or better'
Notes:
The specific specifications for doors, windows, and hardware will be provided during the IFC review stage.

CLIENT :

GULF EDGE DC 01

87 Wireless Road, M Thai Tower 11th. Floor, All Seasons Place, Lumpini,
Pathumwan, Bangkok 10330, Thailand

CONTRACTOR :

华西发展(泰国)有限公司
บริษัท หัวซือ ดีเวลลอปเม้นต์ (ประเทศไทย) จำกัด
HUASHI DEVELOPMENT CO.,LTD
No. 202, Room No. 1403, 14/F, Le Concorde Building,
Ratchadapisek Road, Huaykhwang Sub-District,
Huaykhwang District, Bangkok Metropolitan 10310.

CONSULTANT :

ARbay
บริษัท เอ อาร์ เบย์ จำกัด
ARbay Company Limited
31 st Floor Bangkok Insurance Building
25 South Sathorn road Thungmahamek
Sathorn Bangkok 10120 THAILAND
T +66 (0) 2286 8199
F +66 (0) 2286 2863
info@arbay.co.th

CONSULTANT :

Qbic Engineers & Architects Co.,Ltd.
8 Soi KALONG 4 SANAMBINNAM ROAD,
THASAI SUB-DISTRICT, MUANG NONTHABURI DISTRICT
, NONTHABURI.
Tel 662-950-4374
Fax 662-580-3231
E-Mail : qbic@qbic.co.th, www.qbic.co.th
QBIC ENGINEERS AND ARCHITECTS CO.,LTD.

CONSULTANT :

MITR
MITR TECHNICAL CONSULTANT CO.,LTD.
1168/8 12th FLOOR, LUMPINI TOWER BUILDING,
RAMA IV RD., THUNGMAHAMEK, SATHORN, BANGKOK 10120, THAILAND
TEL : 0-2679-9079-84
FAX : 0-2679-9085 E-mail: mitr_dd@mitr.com

Architect :	SIGNATURE
ประกิต พนานุรัตน์ วสถ. 580 ที่อยู่ 251/1 ถ.จารุเมือง แขวงรองเมือง เขตปทุมวัน กรุงเทพมหานคร โทรศัพท์ 02-286-8199	
Structural Engineer :	SIGNATURE
วิศวกรผู้ออกแบบโครงสร้าง	
ณัฐสม สงวนวงษ์ วย 1423 ที่อยู่ 2/1 ซ.รามคำแหง 150 ถ.รามคำแหง แขวง สะพานสูง เขต สะพานสูง กทม. 10240	
Structural Inspector :	SIGNATURE
วิศวกรผู้ตรวจสอบโครงสร้าง	
โกมล จุฑาภัทร วย 964 ที่อยู่ 24/18 ซ.นวมินทร์ 129 ถ. นวมินทร์ แขวง นวลจันทร์ เขต บึงกุ่ม กทม. 10230	
Electrical Engineer :	SIGNATURE
วิศวกรผู้ออกแบบระบบไฟฟ้ากำลัง	
นายสุภัทร บูรณวิทย์ วฟก.1265 ที่อยู่ 21 ซอยทานสัมฤทธิ์ 13 ตำบลท่าทราย อ.เมืองนนทบุรี จ.นนทบุรี 11000	
Mechanical Engineer :	SIGNATURE
วิศวกรผู้ออกแบบระบบเครื่องกลและปรับอากาศ	
นายประสิทธิ์ เกียวสุนทร วก.1221 ที่อยู่ 44/372 ซอยบางกระดี่ 35/1 แขวงแสมดำ เขตบางขุนเทียน กทม. 10150	ประสิทธิ์
Sanitary Engineer :	SIGNATURE
วิศวกรผู้ออกแบบระบบสุขาภิบาล และดับเพลิง	
นายทศวรรษ สนั่นฤทธิ์ วส. 215 ที่อยู่ บ้านเลขที่ 99/107 หมู่ที่ 3 ต.ศีรษะจรเข้น้อย อ.บางเสาธง จ.สมุทรปราการ 10540	ทศวรรษ

ISSUE/REVISION

REV.	DESCRIPTION	DATE
A	90% DEVELOPED	09/05/2026

PROJECT NAME :

GEDC 01

LOCATION:
Nikhom Phattana district, Rayong ,industrial estate,CPGC

BUILDING :
FIRE&DOMESTIC PUMP ROOM

90% DEVELOPED

TITLE :

CEILING FINISHES & WATERPROOFING RAINWATER DOWN PIPE & DOOR & WINDOW & WALL FINISHES LAYOUT

JOB NO.	SCALE
DRAWN LK	REF.
CHECKED LJC	DWG.NO.
APPROVED LXD	MPK02-60-A-CL&WP&RWDP&DW&WF-101
DATE 2026.05.09	

NOTE : THIS PRINT IS OF A CONFIDENTIAL NATURE, IT SHALL NOT BE TRACED,PHOTOGRAPHED,PHOTOSTATED OR REPRODUCED IN ANY MANER,NOR USED FOR ANY PURPOSE WHATSOEVER EXCEPT BY WRITTEN PERMISSION