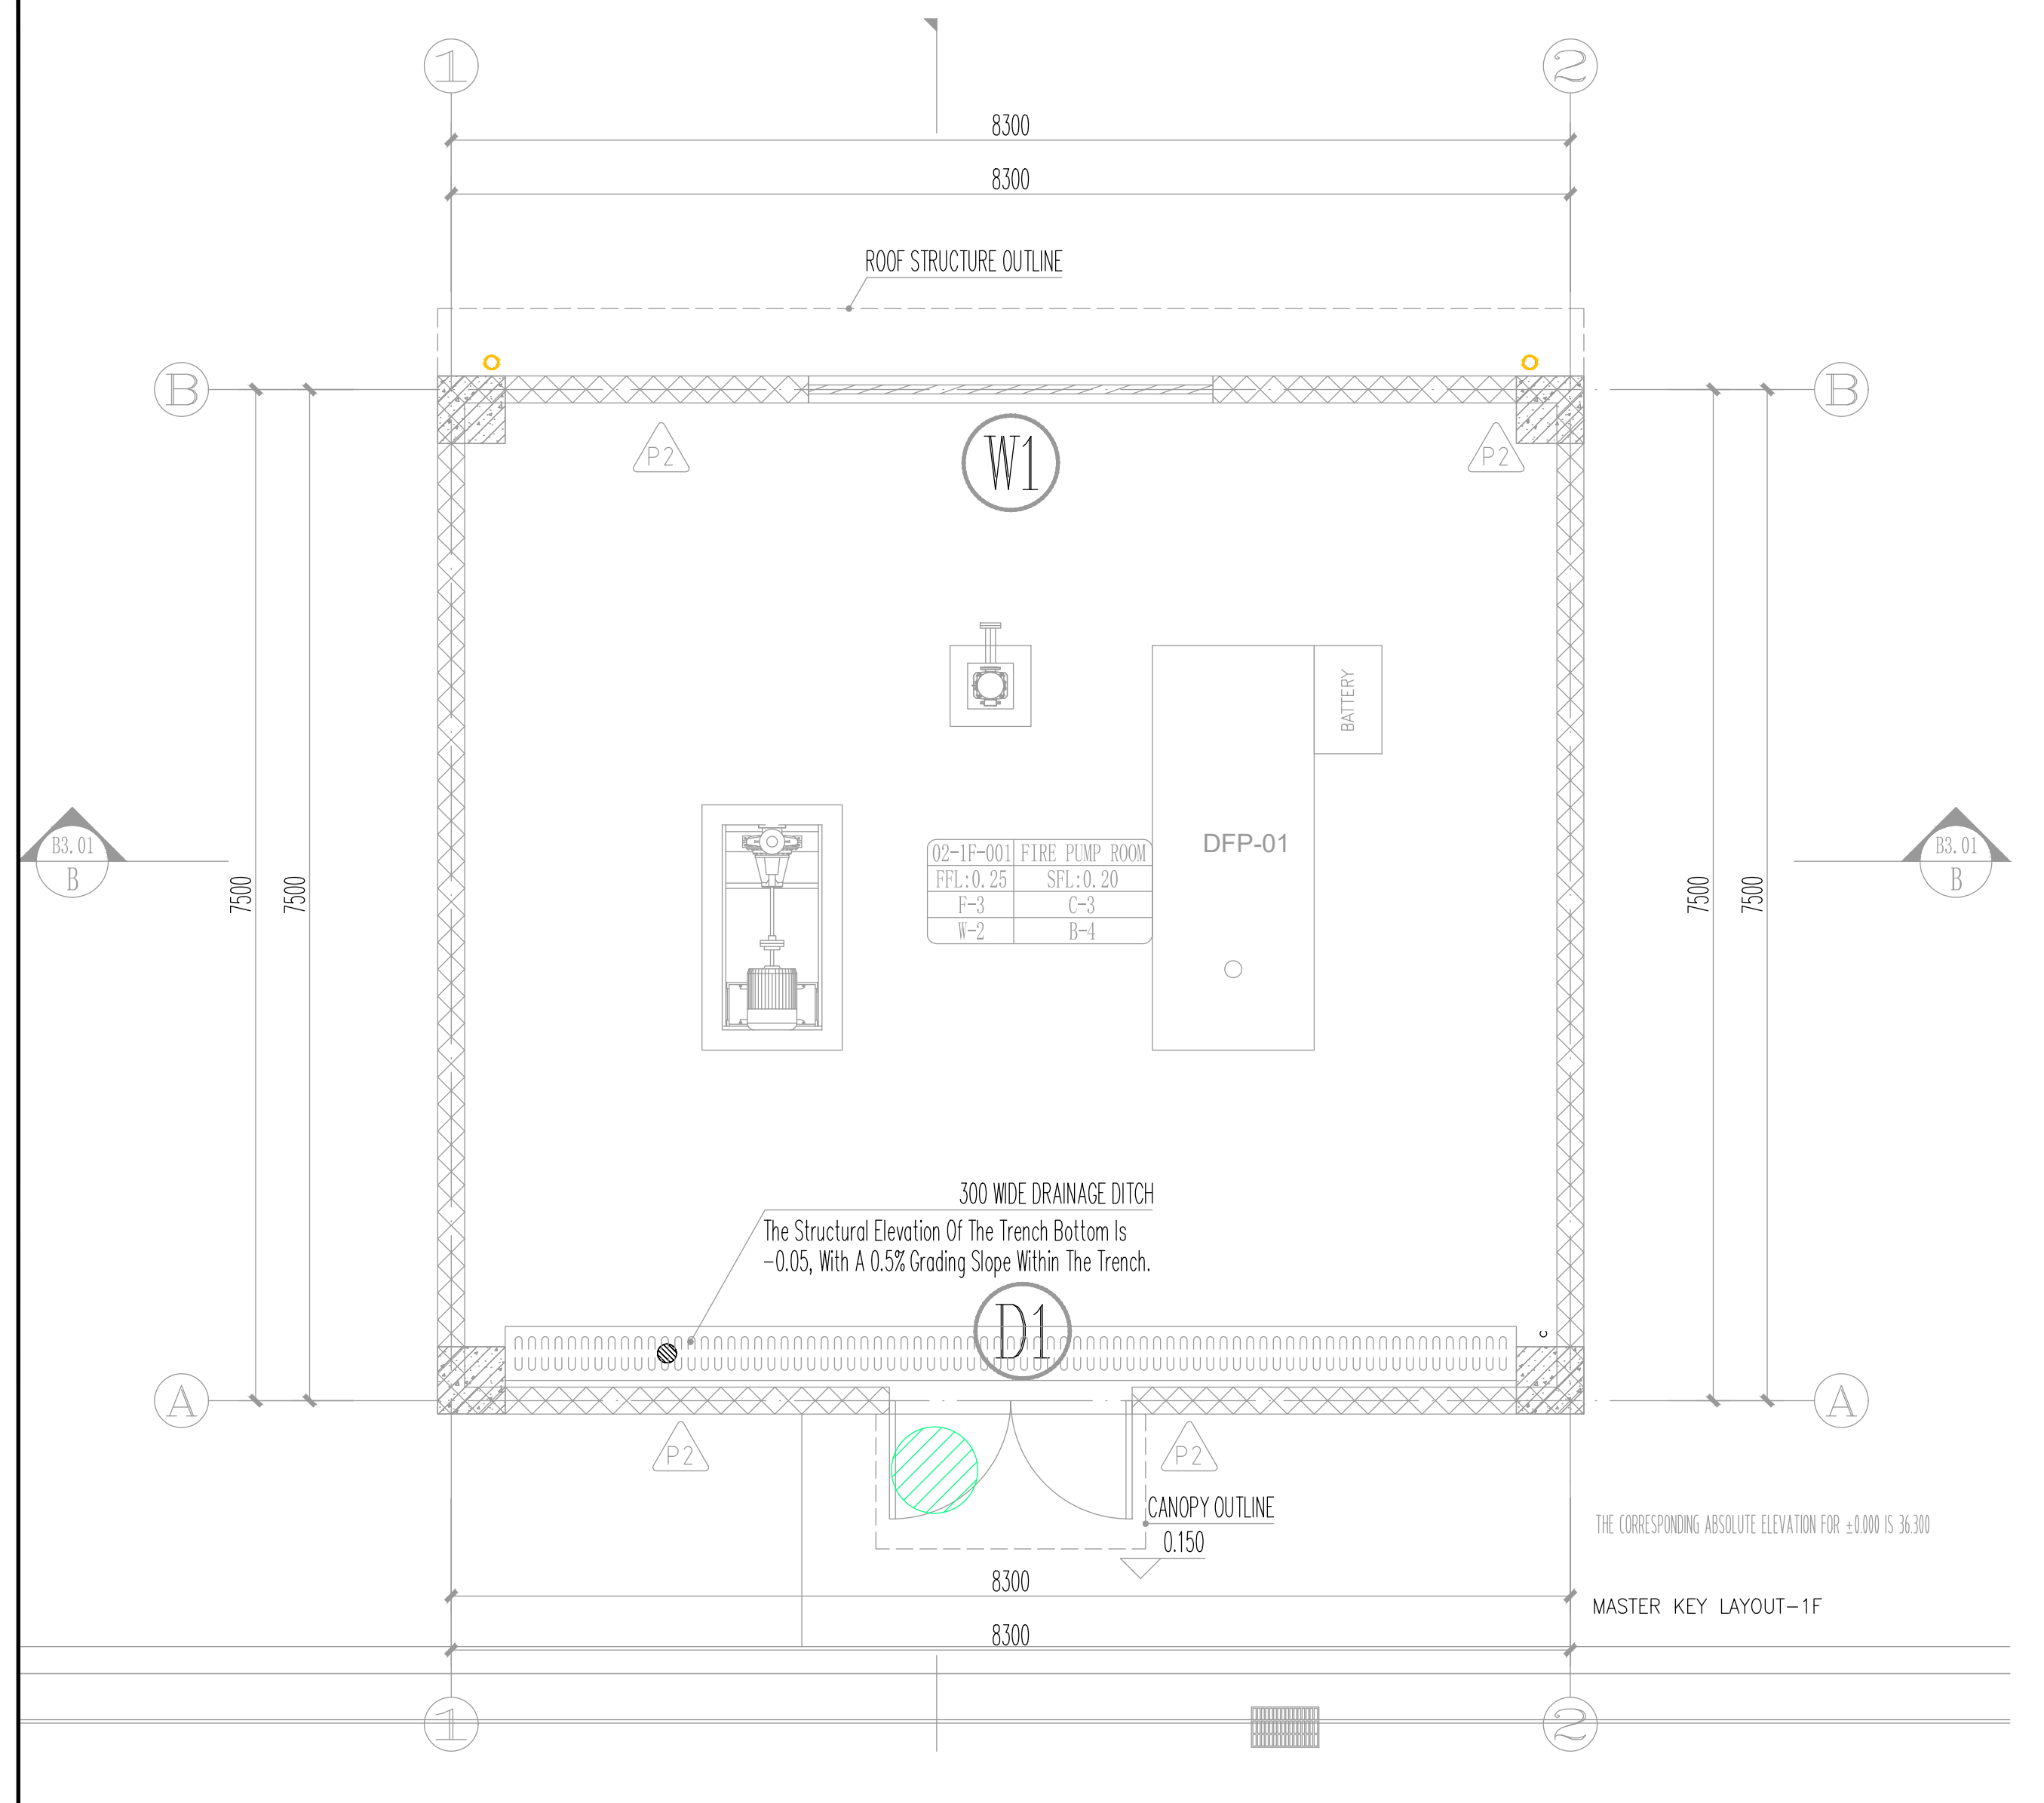
①
②
8300
8300
ROOF STRUCTURE OUTLINE
Ⓑ
Ⓐ
7500
7500
W1
P2
BATTERY
DFP-01
02-1F-001 FIRE PUMP ROOM
FFL:0.25 SFL:0.20
F-3 C-3
W-2 B-4
B3.01
B
300 WIDE DRAINAGE DITCH
The Structural Elevation Of The Trench Bottom Is -0.05, With A 0.5% Grading Slope Within The Trench.
D1
CANOPY OUTLINE
0.150
THE CORRESPONDING ABSOLUTE ELEVATION FOR ±0.000 IS 36.300

MASTER KEY LAYOUT-1F

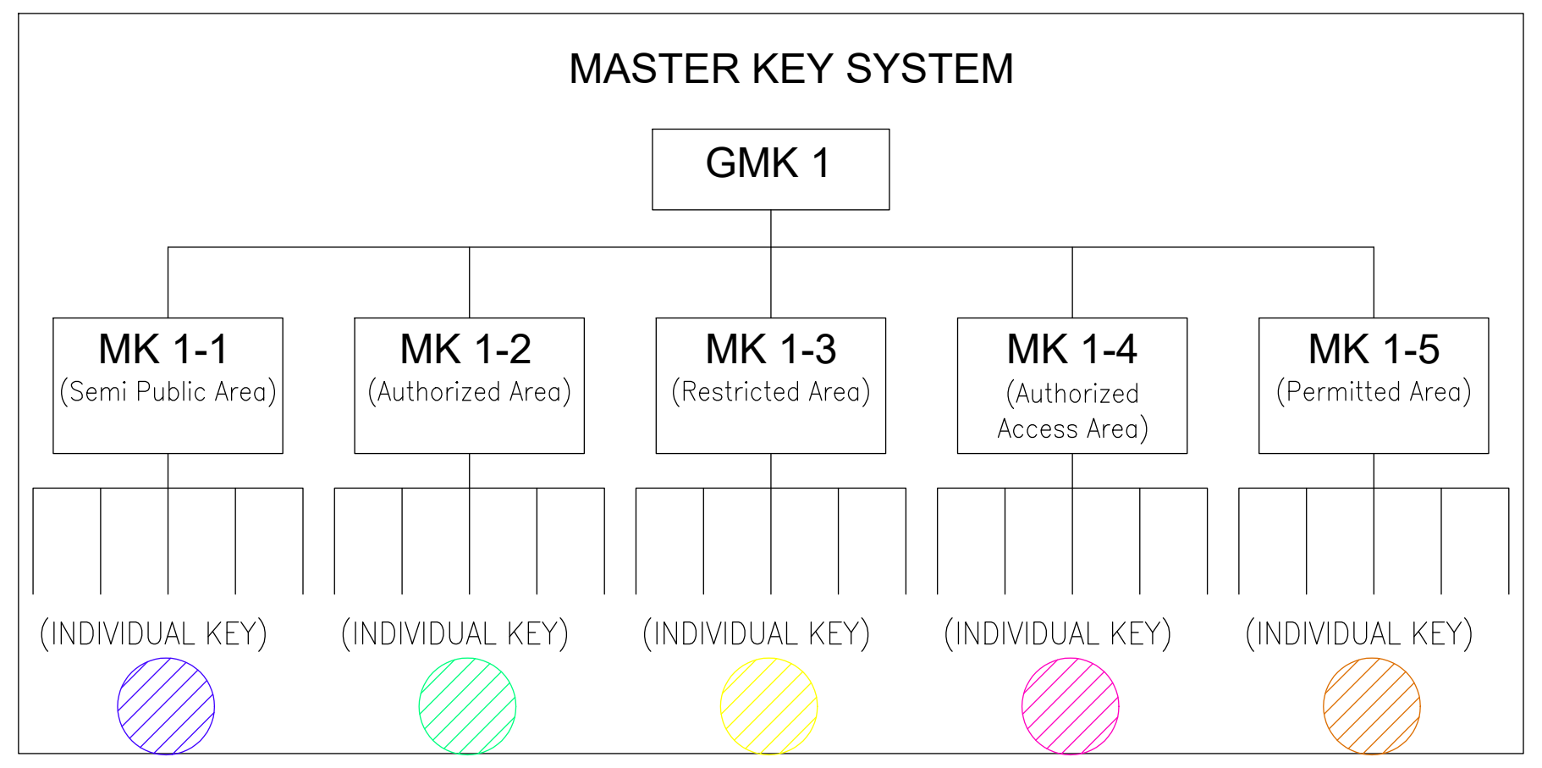

MASTER KEY SYSTEM

GMK 1

MK 1-1 (Semi Public Area)
MK 1-2 (Authorized Area)
MK 1-3 (Restricted Area)
MK 1-4 (Authorized Access Area)
MK 1-5 (Permitted Area)

(INDIVIDUAL KEY) (INDIVIDUAL KEY) (INDIVIDUAL KEY) (INDIVIDUAL KEY) (INDIVIDUAL KEY)

LEGEND:
GMK=GRAND MASTER KEY
MK1-0 ~ MK1-5= MASTER KEY
NOTE:
EACH DOOR HAS ITS OWN INDIVIDUAL MECHANICAL KEY; EACH SECURITY ZONE HAS A MASTER KEY WHICH CAN OPEN EVERY DOOR IN THAT ZONE.

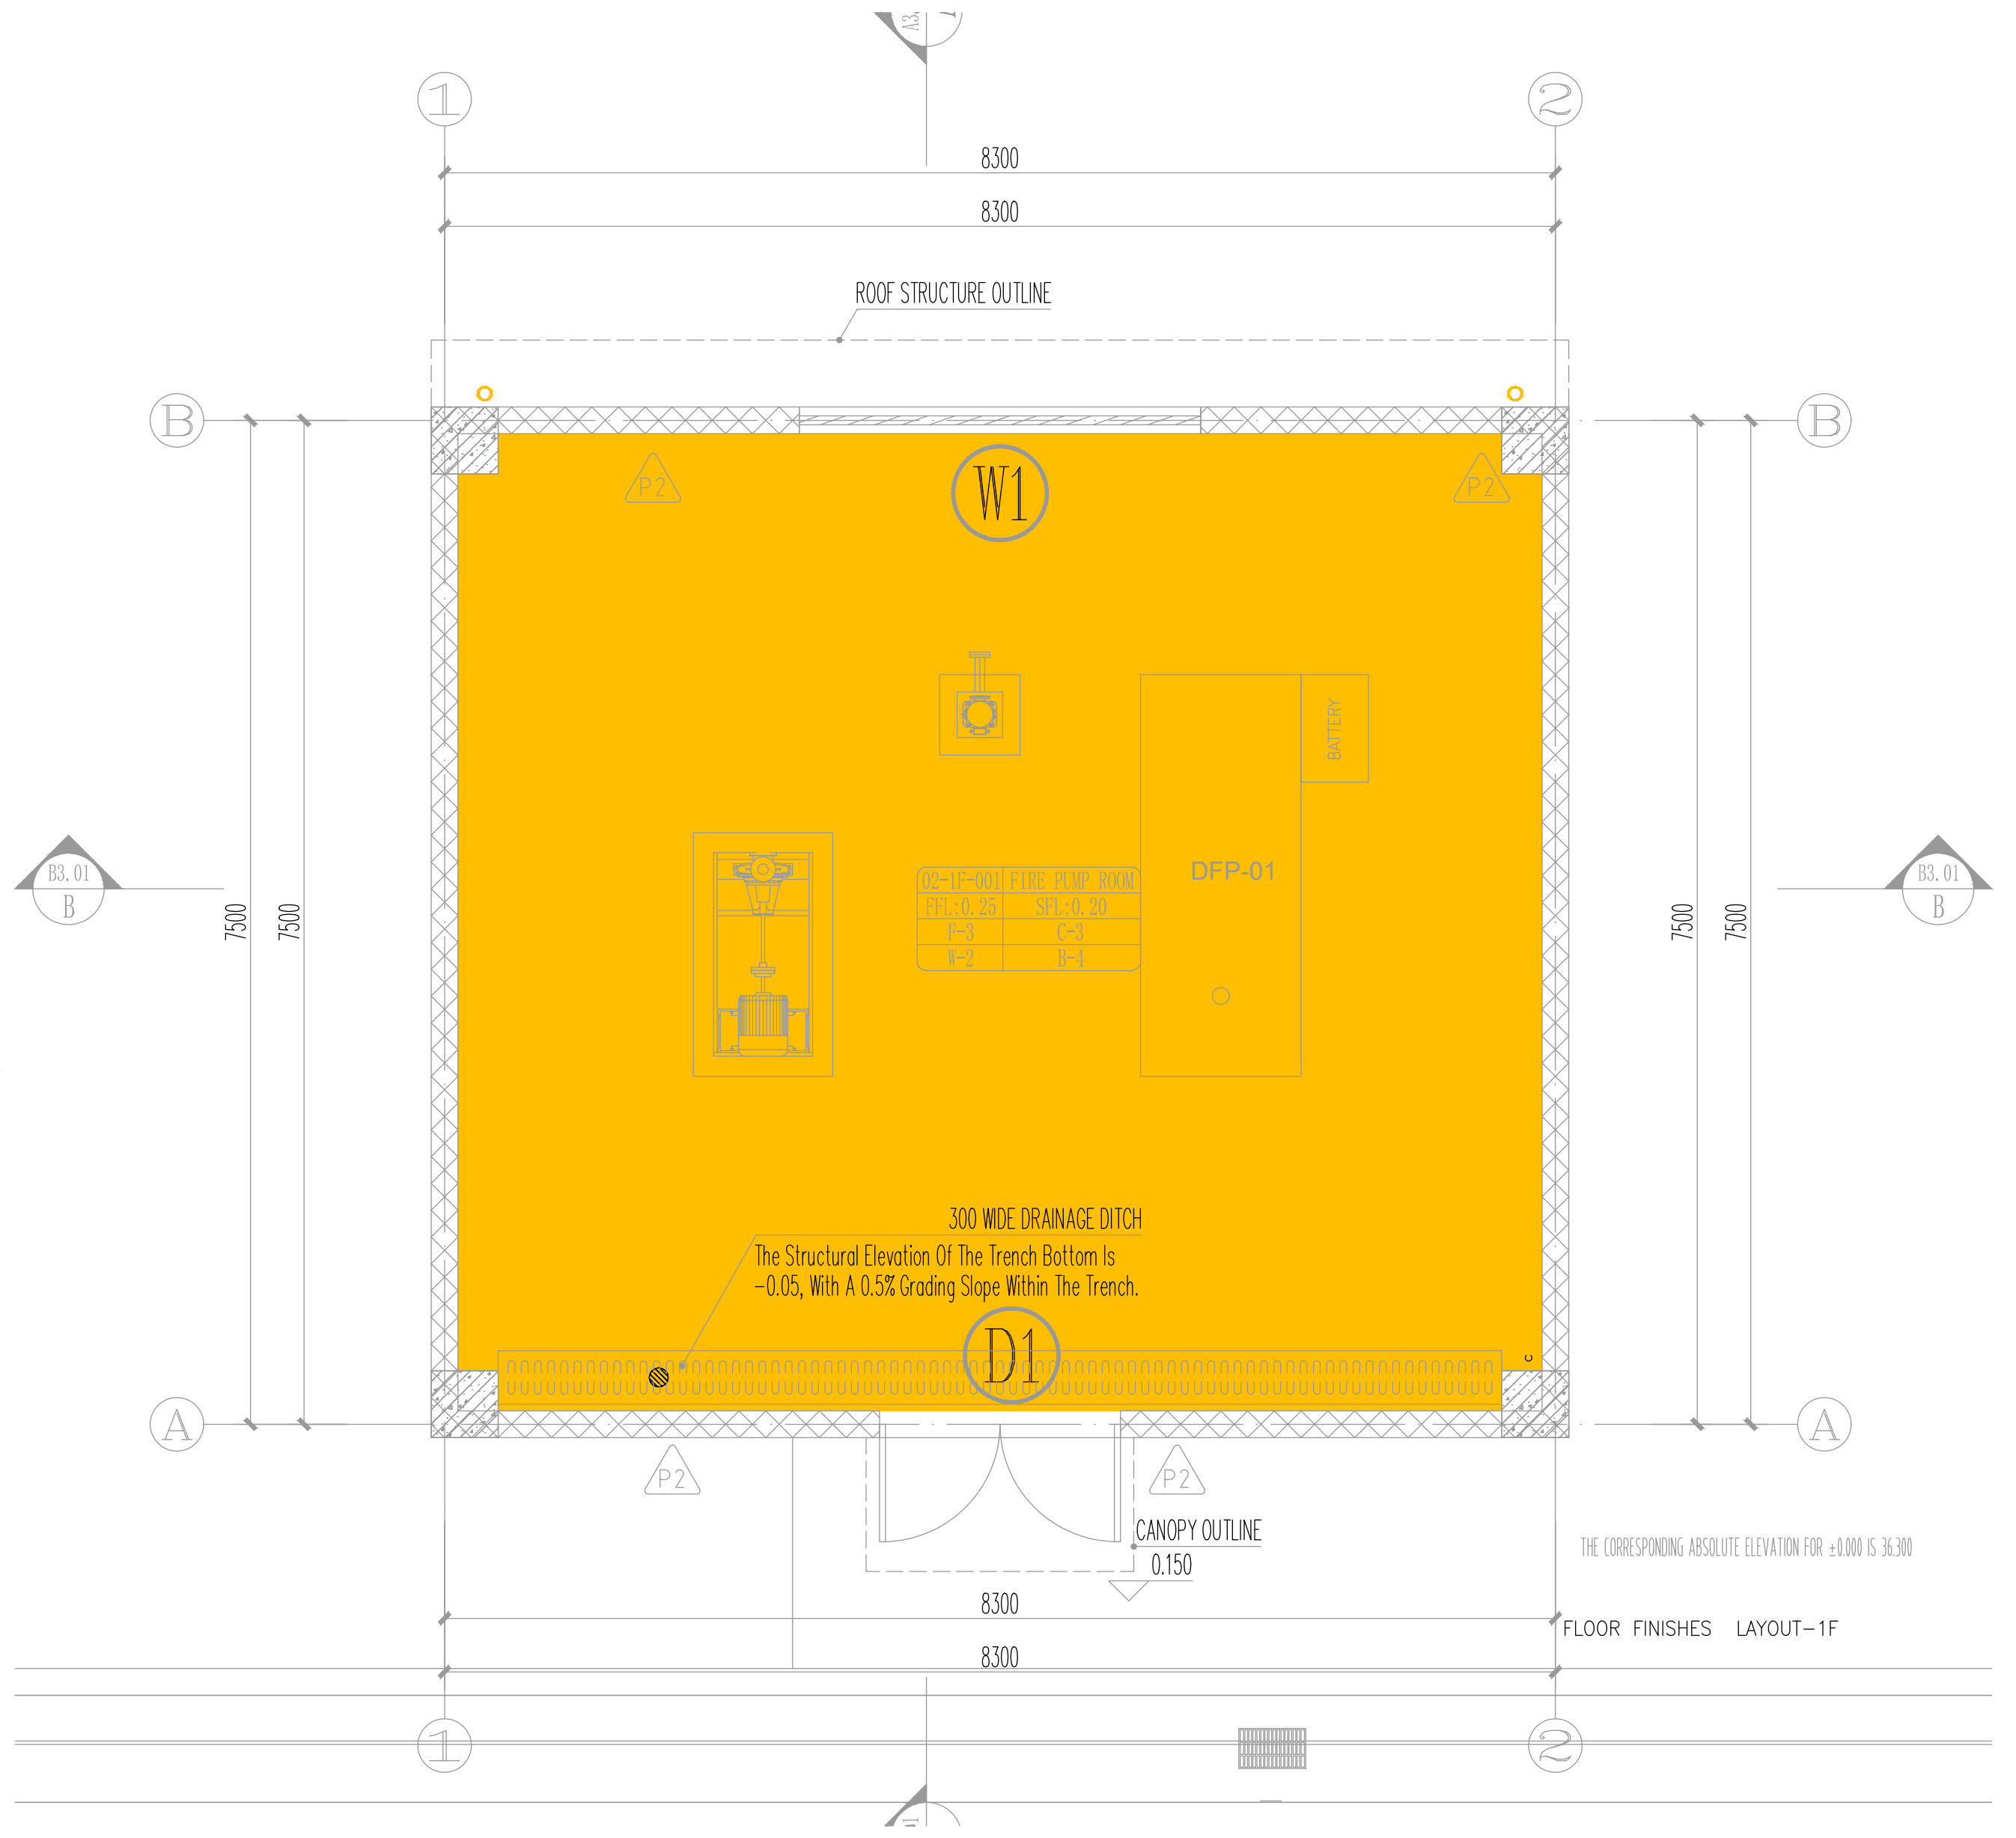
①
②
8300
8300
ROOF STRUCTURE OUTLINE
Ⓑ
Ⓐ
7500
7500
W1
DFP-01
300 WIDE DRAINAGE DITCH
The Structural Elevation Of The Trench Bottom Is -0.05, With A 0.5% Grading Slope Within The Trench.
D1
CANOPY OUTLINE
0.150
THE CORRESPONDING ABSOLUTE ELEVATION FOR ±0.000 IS 36.300

FLOOR FINISHES LAYOUT-1F

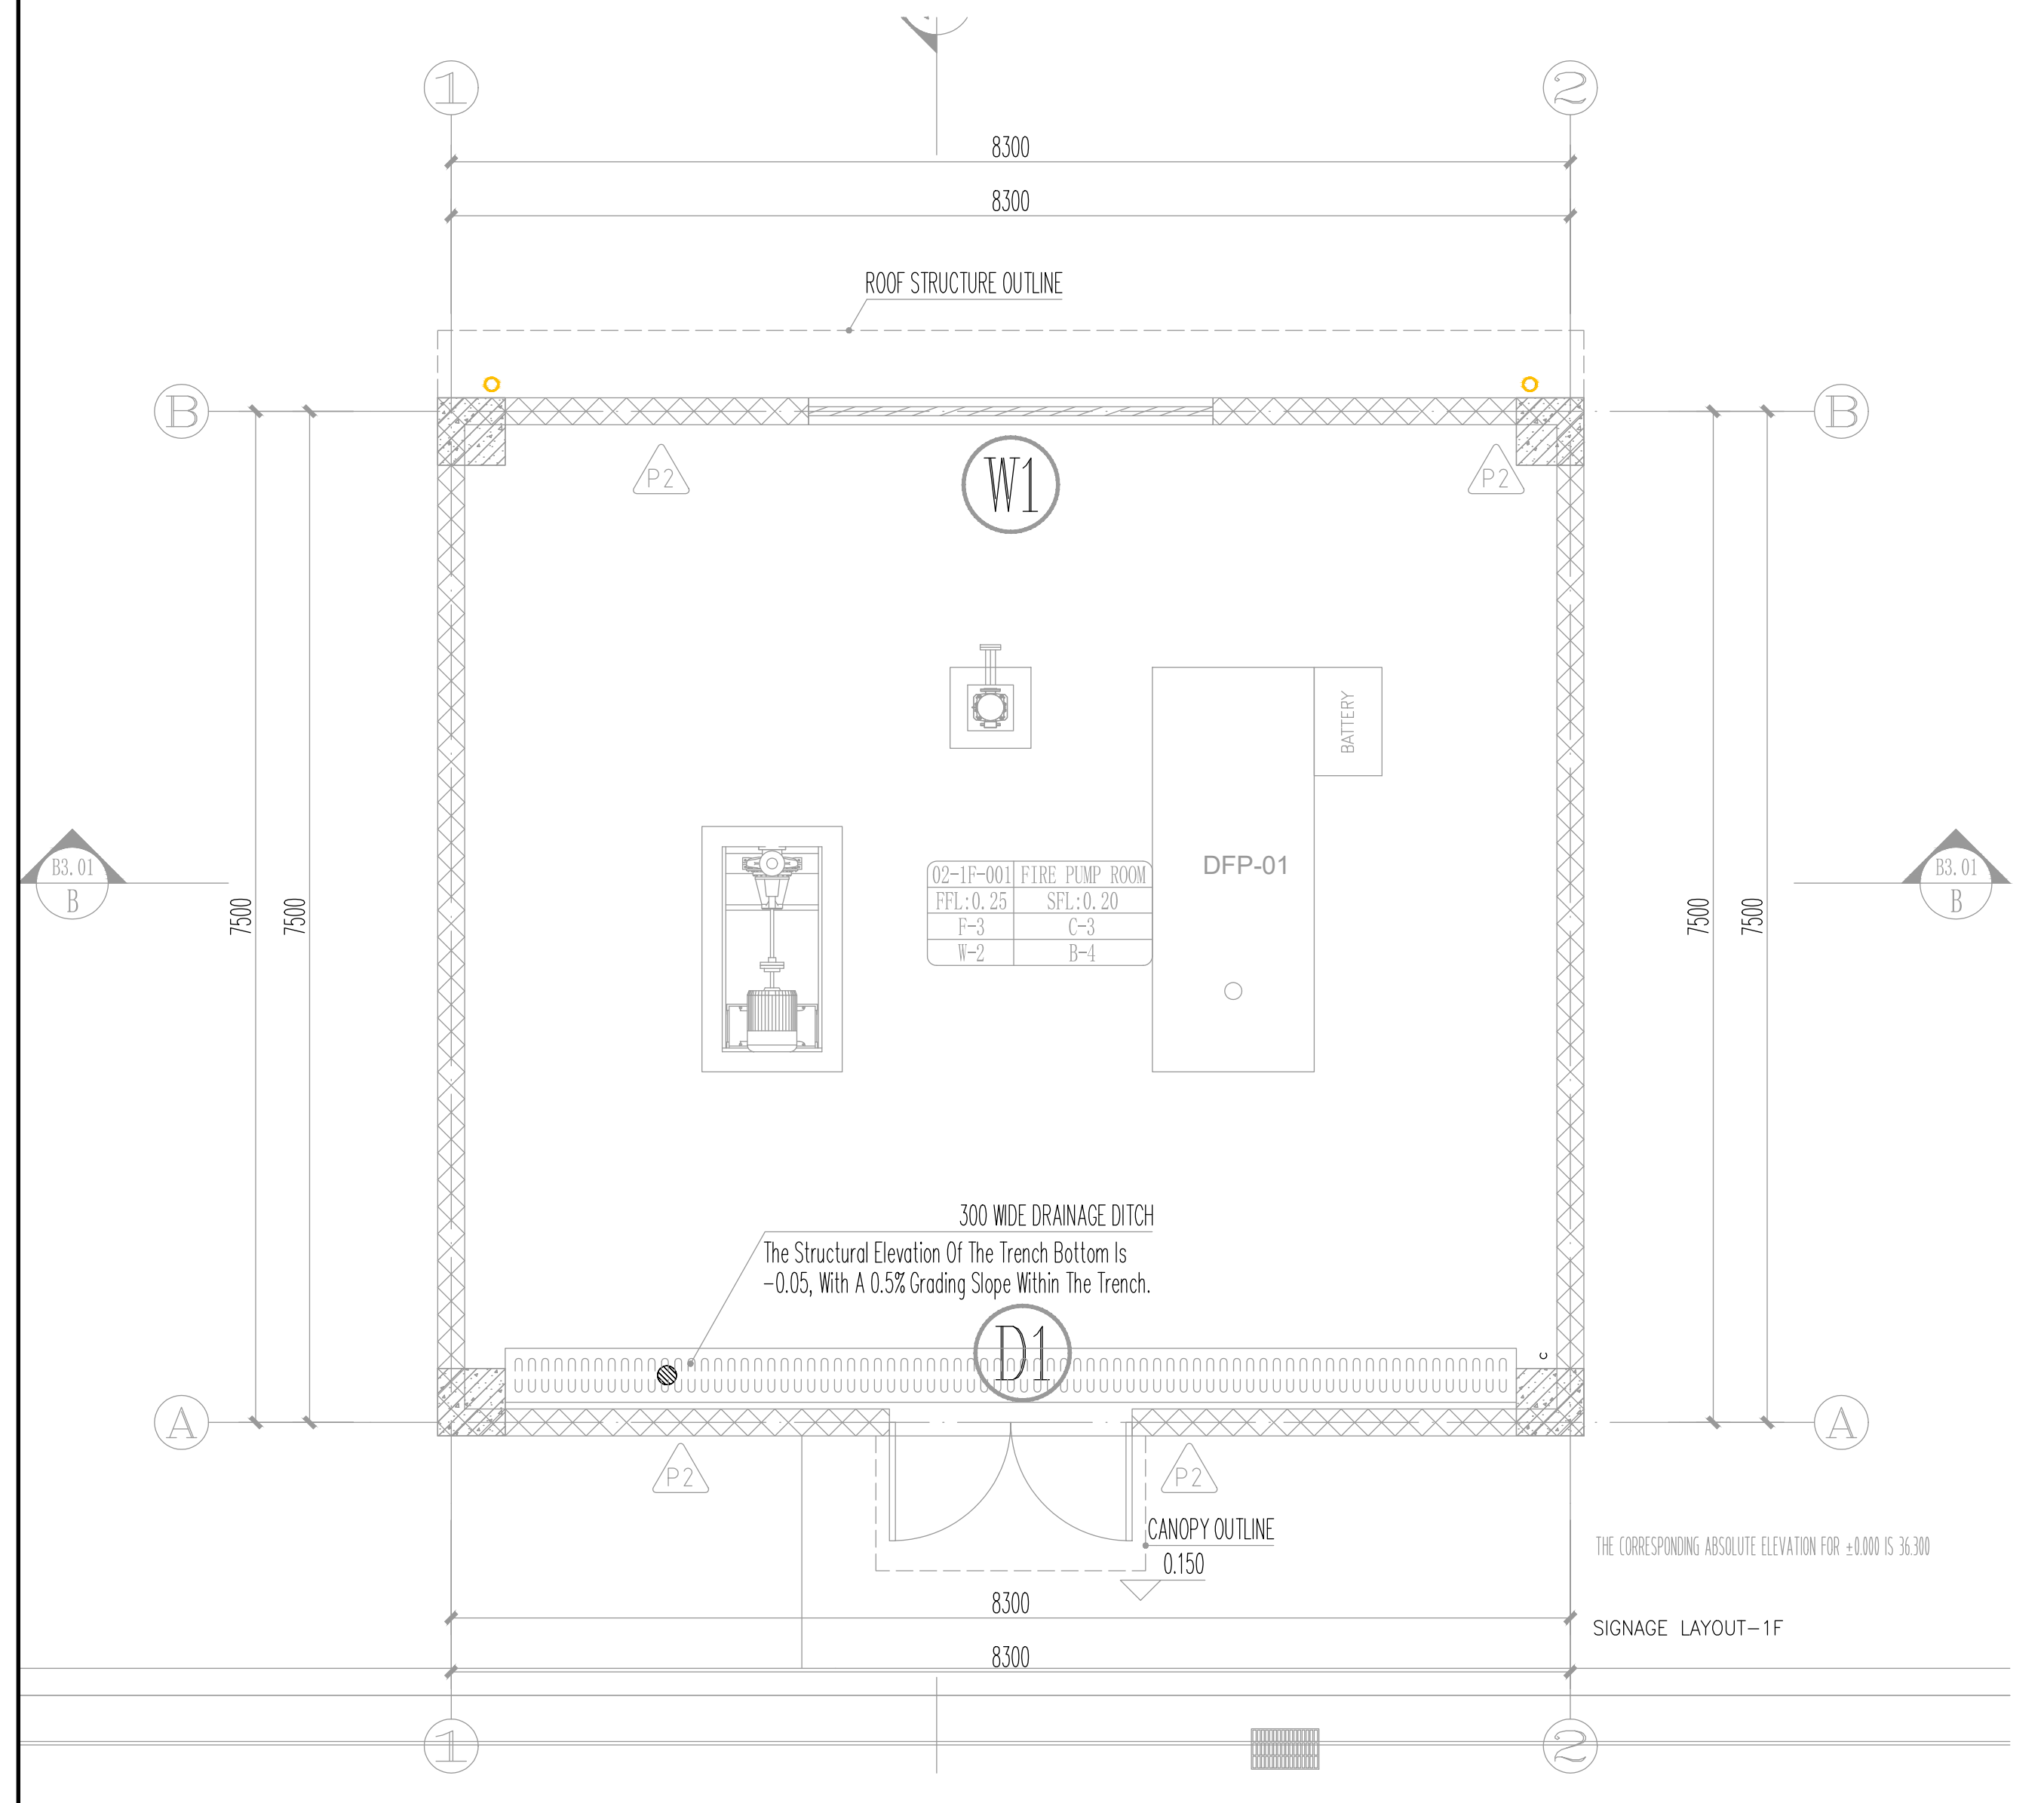
①
②
8300
8300
ROOF STRUCTURE OUTLINE
Ⓑ
Ⓐ
7500
7500
W1
P2
BATTERY
DFP-01
B3.01
B
300 WIDE DRAINAGE DITCH
The Structural Elevation Of The Trench Bottom Is -0.05, With A 0.5% Grading Slope Within The Trench.
D1
CANOPY OUTLINE
0.150
THE CORRESPONDING ABSOLUTE ELEVATION FOR ±0.000 IS 36.300

SIGNAGE LAYOUT-1F

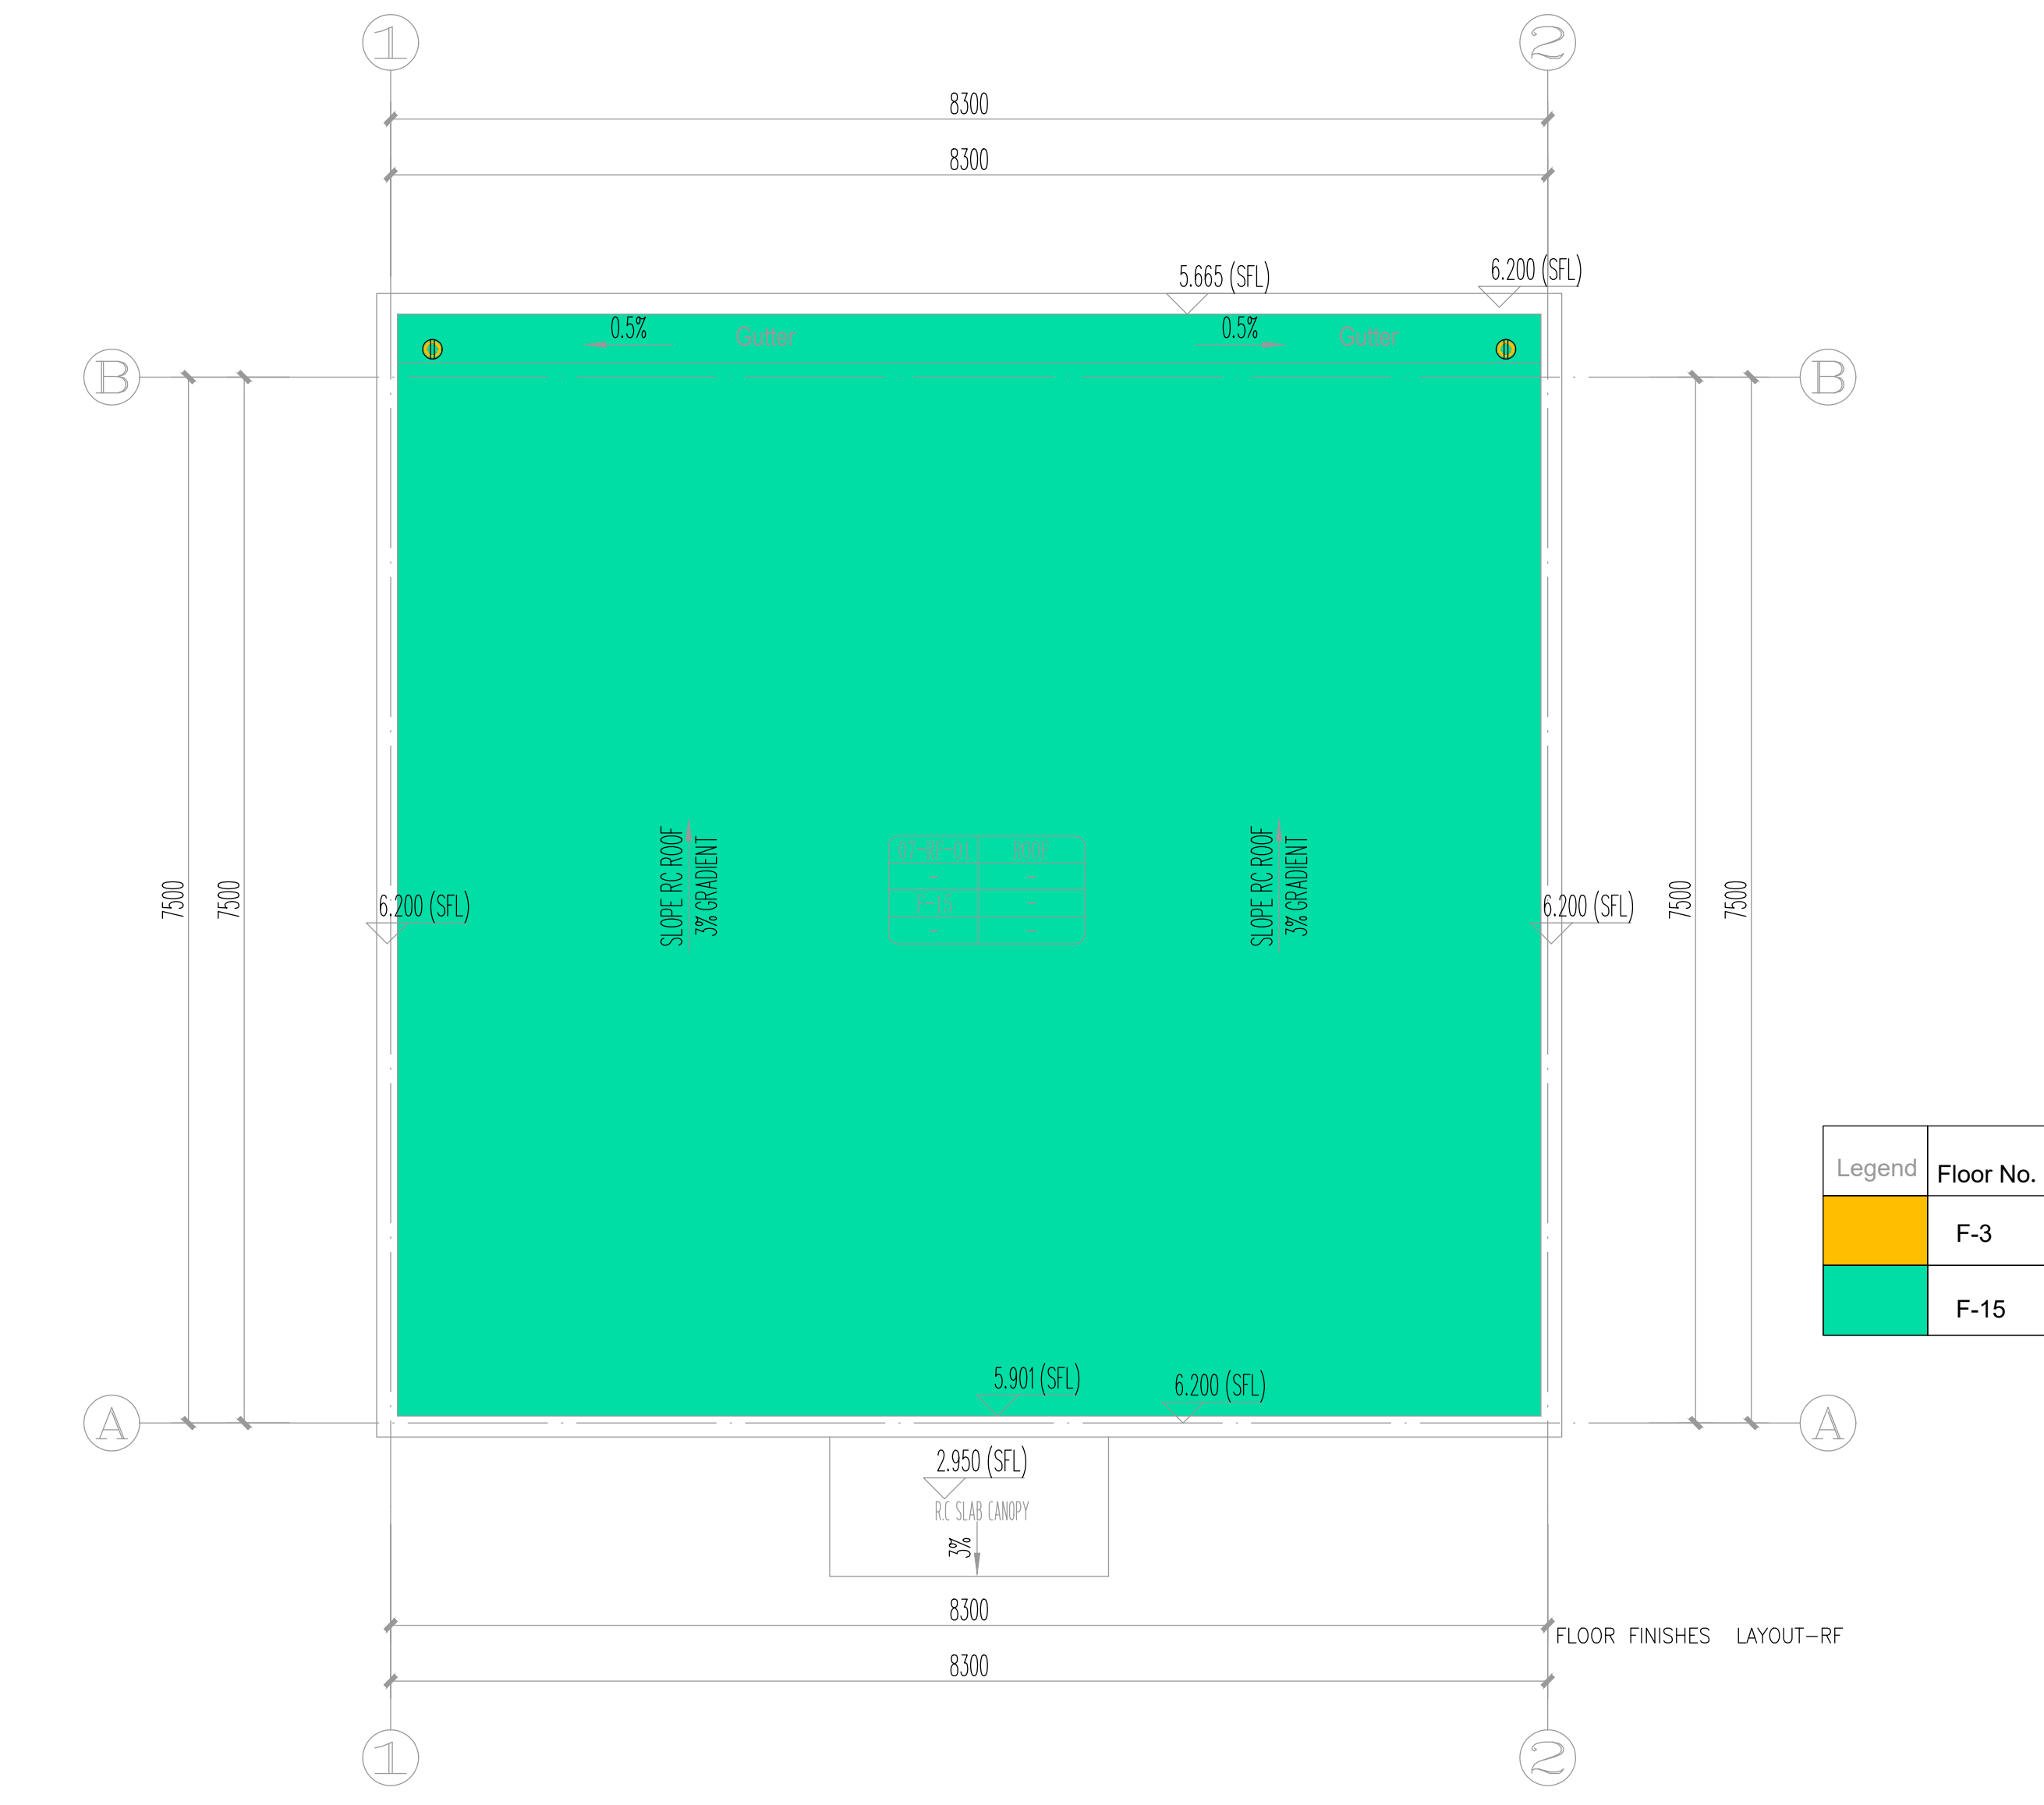
①
②
8300
8300
5.665 (SFL)
6.200 (SFL)
0.5%
Gutter
Ⓑ
Ⓐ
7500
7500
6.200 (SFL)
SLOPE RC ROOF 3% GRADIENT
5.901 (SFL)
2.950 (SFL)
R.C SLAB CANOPY
3%

FLOOR FINISHES LAYOUT-RF

Legend	Floor No.	Description	Floor Finish Specification
🟨	F-3	Concrete Steel Trowel Finish	Concrete Screed + Curing Agent+ Waterproofing
🟩	F-15	Concrete Roof+ Waterproofing	Concrete Roof + Curing Agent+ Waterproofing

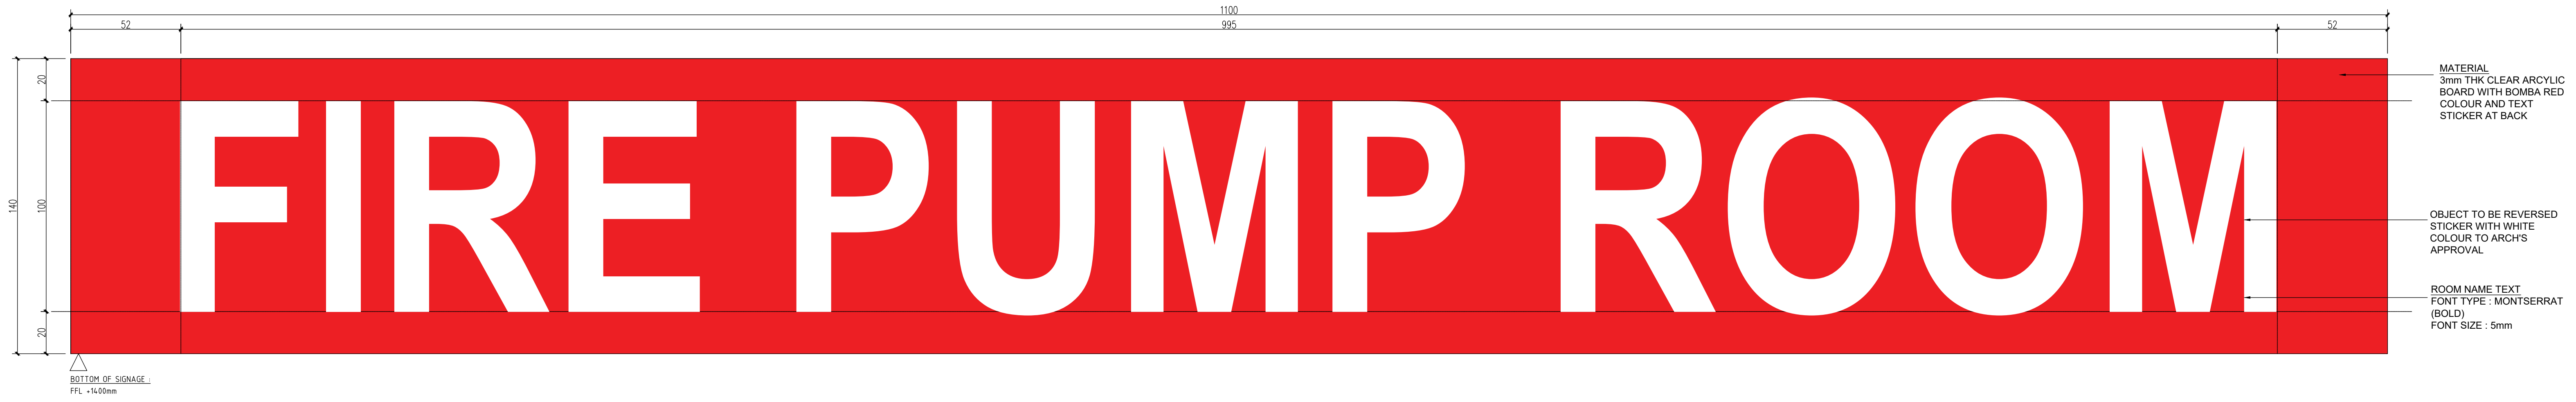
1100
52
995
52
140
20
100
20
FIRE PUMP ROOM

MATERIAL
3mm THK CLEAR ARCYLIC BOARD WITH BOMBA RED COLOUR AND TEXT STICKER AT BACK

OBJECT TO BE REVERSED STICKER WITH WHITE COLOUR TO ARCH'S APPROVAL

ROOM NAME TEXT
FONT TYPE : MONTSERRAT (BOLD)
FONT SIZE : 5mm

BOTTOM OF SIGNAGE :
FFL +1400mm

LOCATION	SIGNAGE B		QUANTITY	MATERIAL
	ENGLISH	MALAY		
GROUND FLOOR	DOMESTIC PUMP ROOM	-	1	3mm TRANSPARENT ACRYLIC 140mm X 240mm with HIGH RES UV PRINT STICKER TO MATCH PANTONE RED
	FIRE PUMP ROOM	-	1	

CLIENT :

GULF EDGE DC 01

87 Wireless Road, M Thai Tower 11th. Floor, All Seasons Place, Lumpini,
Pathumwan, Bangkok 10330, Thailand

CONTRACTOR :

华西发展(泰国)有限公司
บริษัท หัวซือ ดีเวลลอปเม้นต์ (ประเทศไทย) จำกัด
HUASHI DEVELOPMENT CO.,LTD
No. 202, Room No. 1403, 14/F, Le Concorde Building,
Ratchadapisek Road, Huaykhwang Sub-District,
Huaykhwang District, Bangkok Metropolitan 10310.

CONSULTANT :

ARbay
บริษัท เอ อาร์ เบย์ จำกัด
ARbay Company Limited
31 st Floor Bangkok Insurance Building
25 South Sathorn road Thungmahamek
Sathorn Bangkok 10120 THAILAND
T +66 (0) 2286 8199
F +66 (0) 2286 2863
info@arbay.co.th

CONSULTANT :

Qbic Engineers & Architects Co.,Ltd.
8 Soi KALONG 4 SANAMBINNAM ROAD,
THASAI SUB-DISTRICT, MUANG NONTHABURI DISTRICT
, NONTHABURI.
Tel 662-950-4374
Fax 662-580-3231
E-Mail : qbic@qbic.co.th, www.qbic.co.th
QBIC ENGINEERS AND ARCHITECTS CO.,LTD.

CONSULTANT :

MITR
MITR TECHNICAL CONSULTANT CO.,LTD.
1168/8 12th FLOOR, LUMPINI TOWER BUILDING,
RAMA IV RD., THUNGMAHAMEK, SATHORN, BANGKOK 10120, THAILAND
TEL : 0-2679-9079-84
FAX : 0-2679-9085 E-mail: mitr_dd@mitr.com

Architect : SIGNATURE
ประกิต พนานุรัตน์ วสถ. 580
ที่อยู่
251/1 ถ.จารุเมือง แขวงรองเมือง เขตปทุมวัน
กรุงเทพมหานคร โทรศัพท์ 02-286-8199

Structural Engineer : SIGNATURE
วิศวกรผู้ออกแบบโครงสร้าง
ณัฐสม สงวนวงษ์ วย 1423
ที่อยู่
2/1 ซ.รามคำแหง 150 ถ.รามคำแหง
แขวง สะพานสูง เขต สะพานสูง กทม. 10240

Structural Inspector : SIGNATURE
วิศวกรผู้ตรวจสอบโครงสร้าง
โกมล จุฑาภัทร วย 964
ที่อยู่
24/18 ซ.นวมินทร์ 129 ถ. นวมินทร์
แขวง นวลจันทร์ เขต บึงกุ่ม กทม. 10230

Electrical Engineer : SIGNATURE
วิศวกรผู้ออกแบบระบบไฟฟ้ากำลัง
นายสุภัทร บูรณวิทย์ วฟก.1265
ที่อยู่
21 ซอยทานสัมฤทธิ์ 13
ตำบลท่าทราย อ.เมืองนนทบุรี จ.นนทบุรี 11000

Mechanical Engineer : SIGNATURE
วิศวกรผู้ออกแบบระบบเครื่องกลและปรับอากาศ
นายประสิทธิ์ โกียวสุนทร วก.1221
ที่อยู่
44/372 ซอยบางกระดี่ 35/1 แขวงแสมดำ
เขตบางขุนเทียน กทม. 10150
ประสิทธิ์

Sanitary Engineer : SIGNATURE
วิศวกรผู้ออกแบบระบบสุขาภิบาล และดับเพลิง
นายทศวรรษ สันนฤทธิ์ วส. 215
ที่อยู่
บ้านเลขที่ 99/107 หมู่ที่ 3 ต.ศีรษะจรเข้น้อย
อ.บางเสาธง จ.สมุทรปราการ 10540
ทศวรรษ

ISSUE/REVISION

REV.	DESCRIPTION	DATE
A	90% DEVELOPED	09/05/2026

PROJECT NAME :
GEDC 01
LOCATION:
Nikhom Phattana district, Rayong ,industrial estate,CPGC

BUILDING :
FIRE&DOMESTIC PUMP ROOM

90% DEVELOPED

TITLE :
MASTER KEY & SIGNAGE &
FLOOR FINISHES LAYOUT

JOB NO.	SCALE 1:50
DRAWN LK	REF.
CHECKED LJC	DWG.NO.
APPROVED LXD	MPK02-60-A-MK&SN&FF-101
DATE 2026.05.09	

NOTE : THIS PRINT IS OF A CONFIDENTIAL NATURE, IT SHALL NOT BE TRACED,PHOTOGRAPHED,PHOTOSTATED OR REPRODUCED IN ANY MANER,NOR USED FOR ANY PURPOSE WHATSOEVER EXCEPT BY WRITTEN PERMISSION