Floor No.	Description	Floor Finish Specification	Vender
F-8	Porcelain Tile	600x600 12mm Thk Non-slip Homogenous Tile (r10) On Waterproofing,Low Voc Tile Adhesive And Grout	
F-15	Concrete Roof+ Waterproofing	SELF-ADHESIVE POLYMER-MODIFIED BITUMEN WATERPROOFING MEMBRANE(3+3mmTHK.)+NON-CURING RUBBER ASPHALT WATERPROOF COATING(2mmTHK.)+XPS INSULATION BOARD(75mmTHK R-12(12 BTU/(h·°F·ft2)(2.12(K·m2)/W))Or Better)+REINFORCED CONCRETE COVER(50mm THK For Roof Slab Top Coat With TOA Heatshield Paint SRI≥82）（XPS insulation board density ≥ 30 kg/m³, compressive strength ≥ 250 kPa）	

Wall No.	Description	Wall Material & Structure Specification	Vender
P2	200MM THK. BRICKWALLWITH PLASTERED(U-value < 0.5 W/(m²·K)		Local
P3	Uac Precast Wall	100mm.Thk Autoclaved Aerated Concrete Wall Panel,2hr.Fire Rated Low Voc Content & Emission Insulation,Low Voc Content & Emission Silicone Sealant	

Ceiling No.	Description	Ceiling Material & Finish Specification	Vender
C-3	MOISTURE-PROOF PAINT	MOISTURE-PROOF PAINT ON CONCRETE CEILING SLAB	

Wall No.	Description	TILE SIZE(MM) WIDTH X DEPTH
W-5	12mm Thk Waterproof Homogenous Tile	Waterproof(For wall height 1.5m and below)
W-2	Skim Coat With Scrub Resistant Paint	Scratch-resistant(For wall height above 1.5m)
WF-1	EXTERIOR WALL PAINT	

BASEBOARD (SKIRTING) FINISHES

CODE	Finish	HEIGHT(MM)
B-3	Non-slip Homogenous Tile (R10)	

Note On Levels- All Levels Shown Are Absolute Elevation

SD	SURFACE MOUNTED SMOKE DETECTOR, PHOTOELECTRIC TYPE
L1	- CEILING MOUNTED LOUDSPEAKER 6W TYPE L1
B	SELF-CONTAINED SEALED LEAD ACID BATTERY EMERGENCY LIGHT 2x9W LED LAMPS WITH 2-HOURS BACK UP TIME,BUILT-IN ADDRESSABLE MODULE THE LIGHTING FIXTURE COMES WITH A BATTERY MONITORING SYSTEM
	LED EXIT SIGN LUMINAIRE, WALL OR SUSPENDED MOUNTED (SINGLE SIDE) WITH 2-HOURS BACK UP TIME,BUILT-IN ADDRESSABLE MODULE,THE LIGHTING FIXTURE COMES WITH A BATTERY MONITORING SYSTEM
▨	REINFORCED CONCRETE STRUCTURAL COLUMN
	DRAINAGE DITCH，DEPTH REFERENCE PLANE
▽	TELEPHONE OUTLET, RJ 11 TYPE
RANN	REMOTE GRAPHIC ANNUNCIATOR BOARD
FATB	FIRE ALARM TERMINAL BOX

ANTI-TERMITE TREATMENT :
ANTI TERMITE TREATMENT SHALL BE EXECUTED BY APPROVED APPLICATOITHE CONTRACTOR SHALL ALLOW FOR :
1. WORKING IN 4-STAGES
2.PROVSIONOFA FIVE (5L VEARS ONT UARANIEE BY MANUJACLER AND APPICAOR COMMENCING FROMTHE DALE OF CERFICALE OF PRACICAL COMPEION ON QUALLY OF MAIERALS AND STANDARD OF WOKMANSHIL
3. PROVISION OF TREATMENT AGAINST TERMITE ATTACK DURING THE QUARANTEE PERIOD FREE OF CHARGE TO THE EMPLOYER THE TERMITICIDE TO BE USED IS "HEXTAR" OR APPROVED EQUIVALENT LMIDACLOPNID: AT A DILUTION RATE OF 1:800: TO COMPLY WITH THE SPECIALIST REQUIREMENTS
TREATMENT METHOD:POWER SPRAY THE COMPACTED SOIL SURFACE AT THE RATE OF 5 LITRES/M2 OF TERMICIDE AT THE CORRECT CONCENTRAION FOR EVERY SQUARE METER
POWER SPRAY THE COMPACTED SOILSURFACE FOR PILE CAP, GROUND BEAM, GROUND FOOR, AND APRON AT THE RATE OF 5 ITRESLM2 OF TEMITICIDE FOR EVERY SOUARE METER
LEED Note:
1 All adhesives, sealants, paints, primers, and coatings shall be low-VOC content and low-VOC emissions materials.
2 All ceiling boards shall be low-VOC emissions materials.
3 Used at least 20 EPD products from 5 manufacturers.
4 All materials shall comply with LEED TOR.

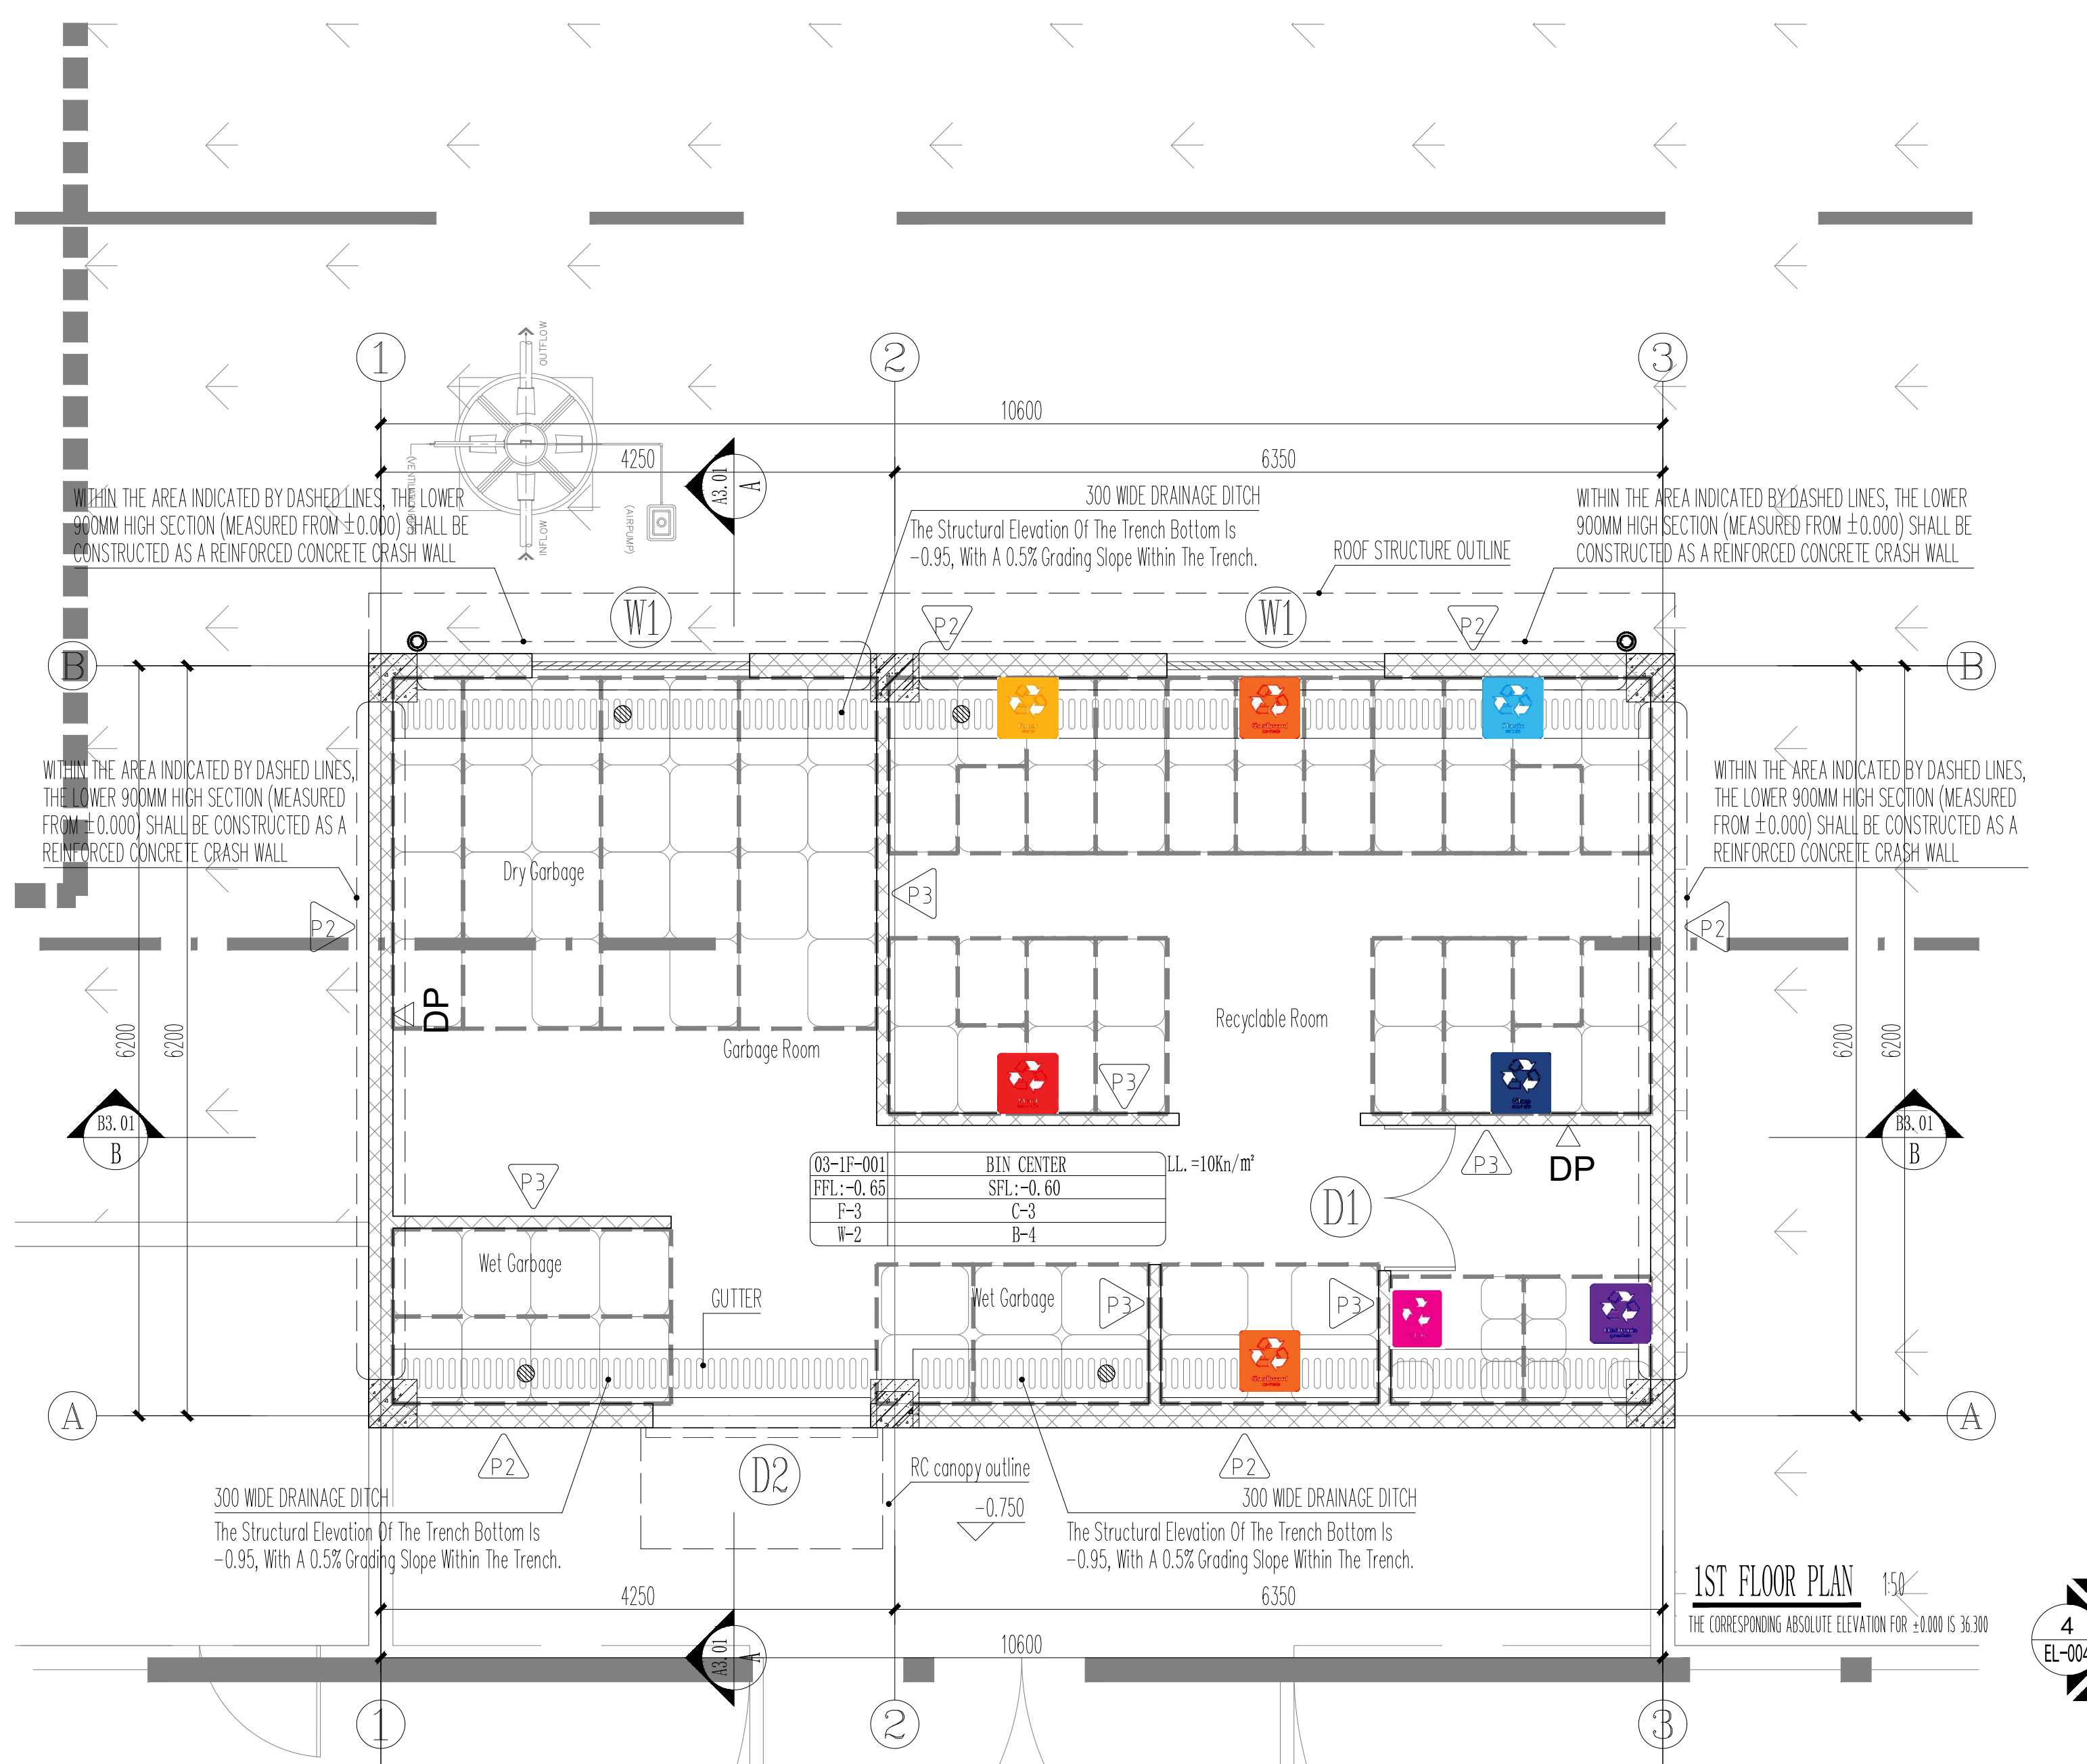
WITHIN THE AREA INDICATED BY DASHED LINES, THE LOWER 900MM HIGH SECTION (MEASURED FROM ±0.000) SHALL BE CONSTRUCTED AS A REINFORCED CONCRETE CRASH WALL
300 WIDE DRAINAGE DITCH
The Structural Elevation Of The Trench Bottom Is −0.95, With A 0.5% Grading Slope Within The Trench.
ROOF STRUCTURE OUTLINE
Dry Garbage
Garbage Room
Recyclable Room
Wet Garbage
GUTTER
RC canopy outline
03-1F-001 BIN CENTER
FFL:-0.65 SFL:-0.60
F-3 C-3
W-2 B-4
LL. =10Kn/m²
DP
W1
D1
D2
P2
P3
10600
6350
4250
6200
−0.750
1ST FLOOR PLAN 1:50
THE CORRESPONDING ABSOLUTE ELEVATION FOR ±0.000 IS 36.300
EL-001
EL-002
EL-003
EL-004

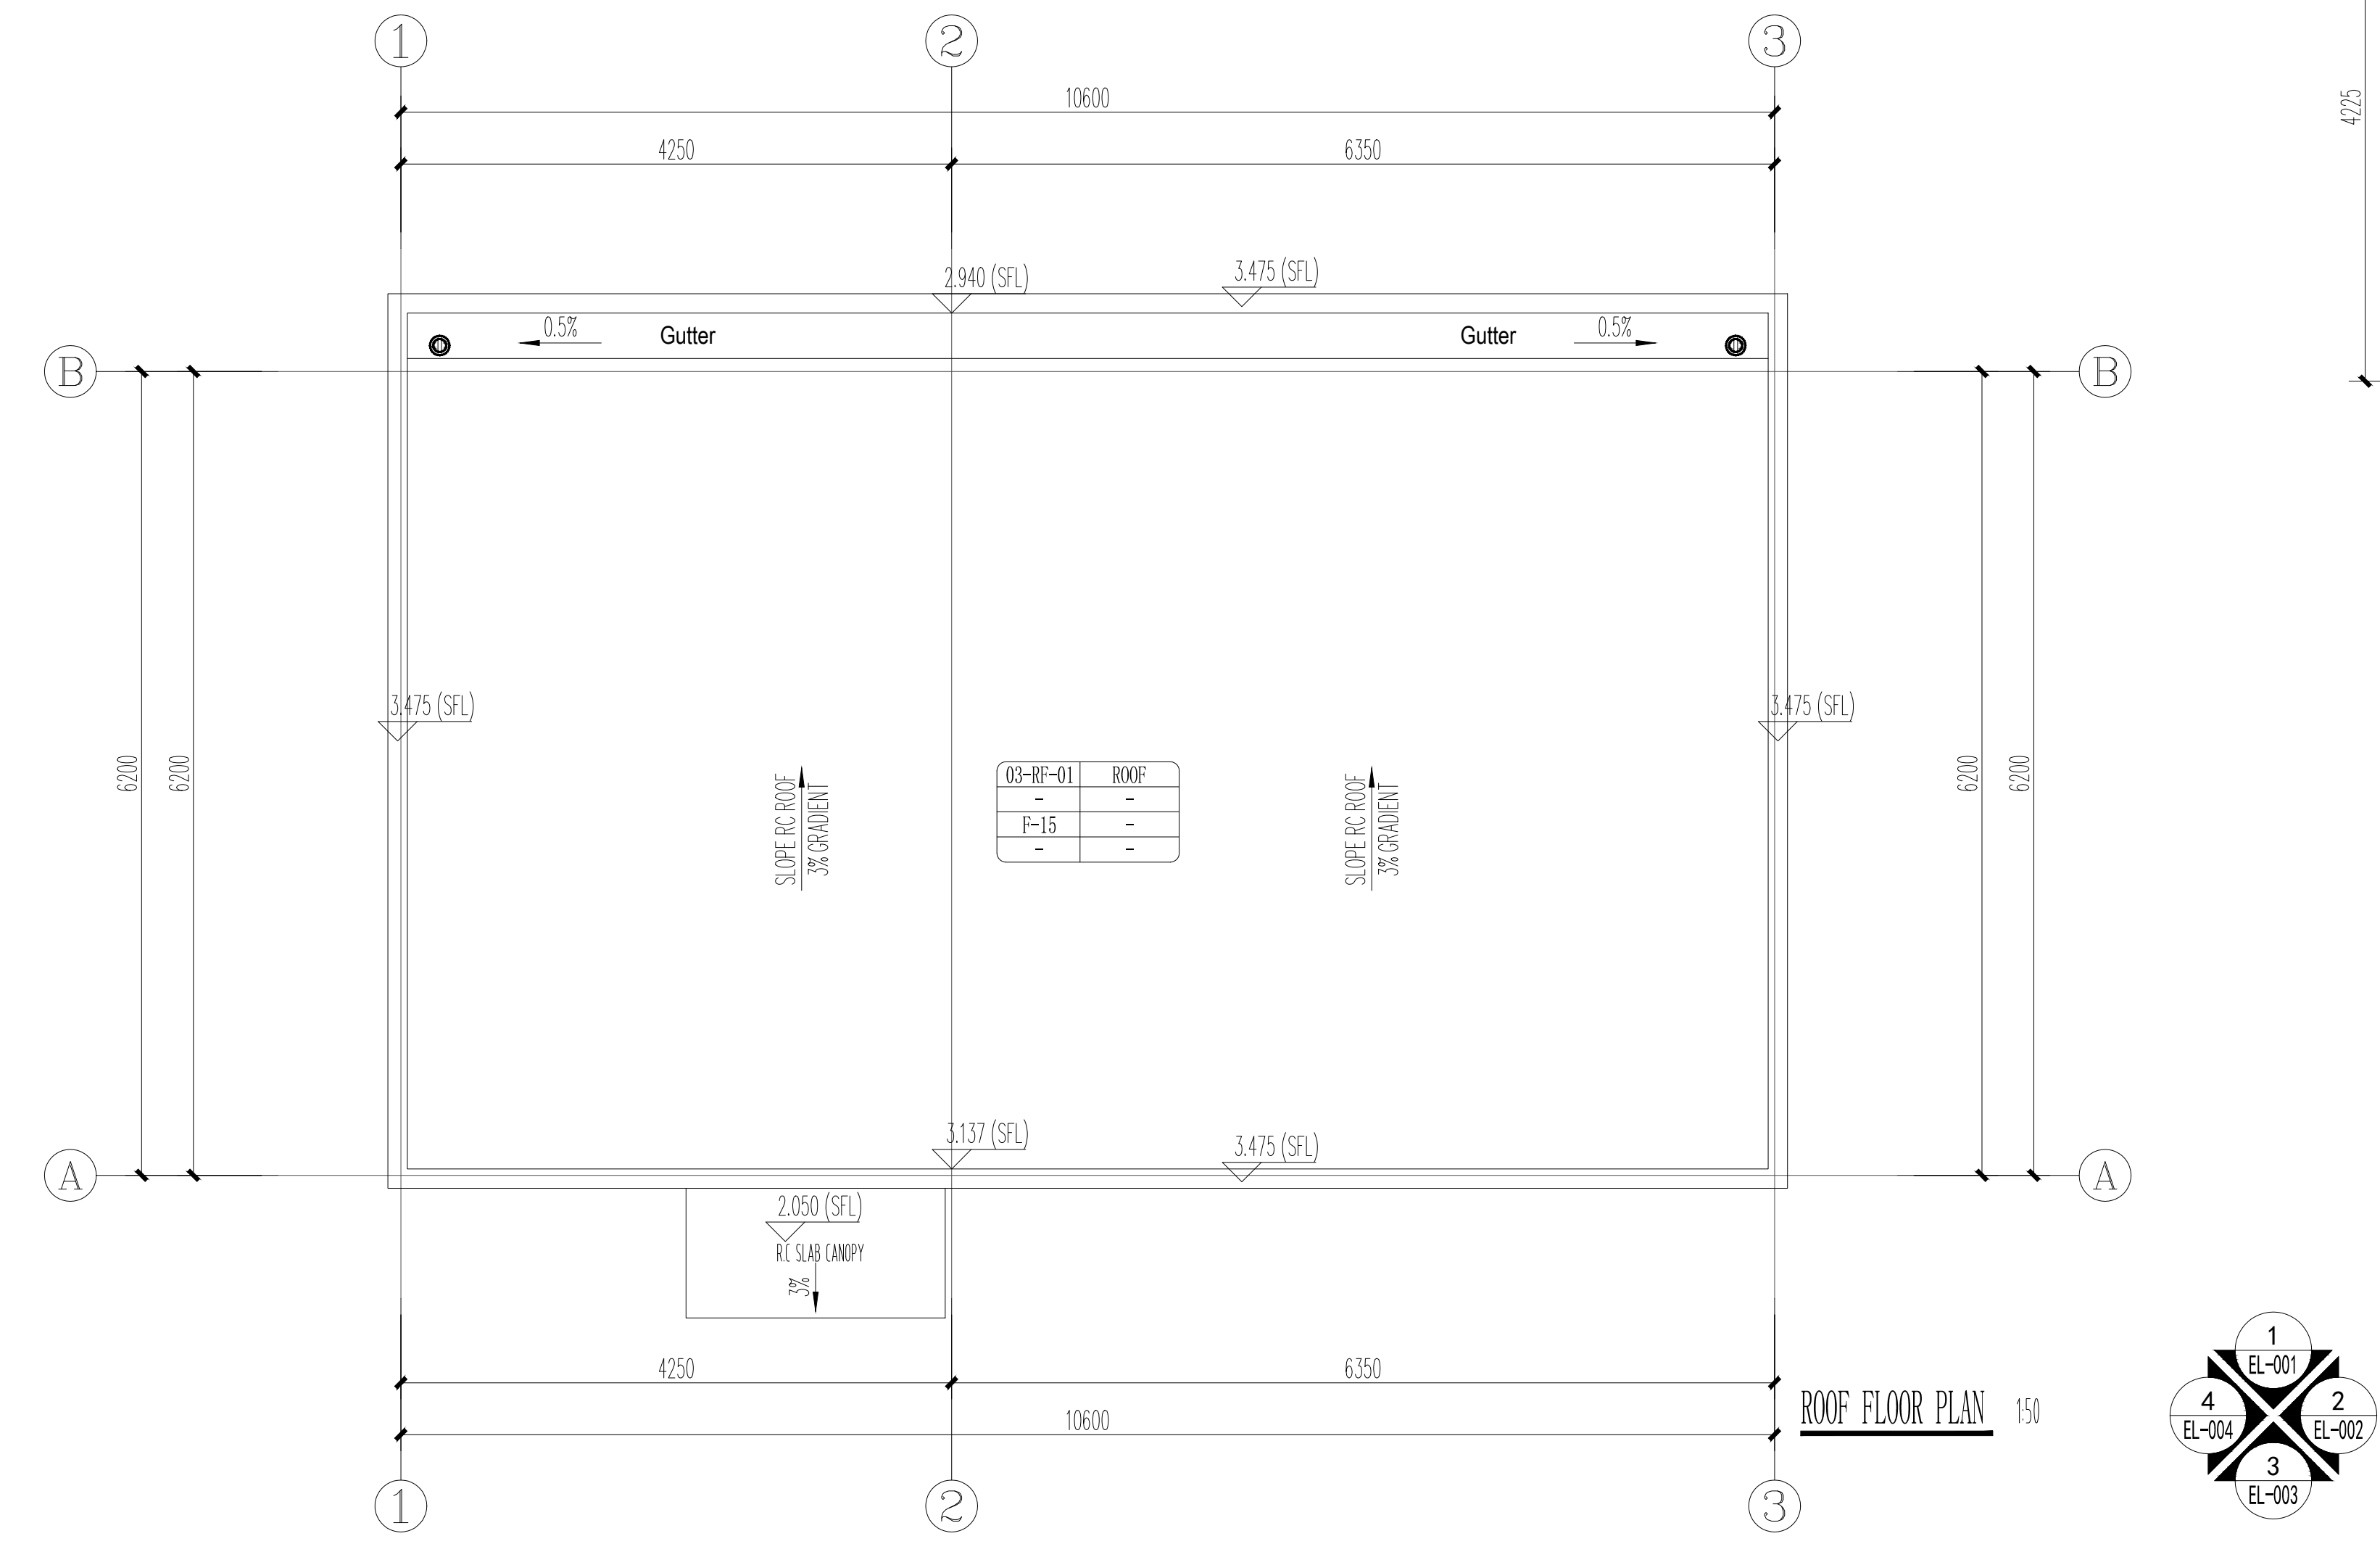

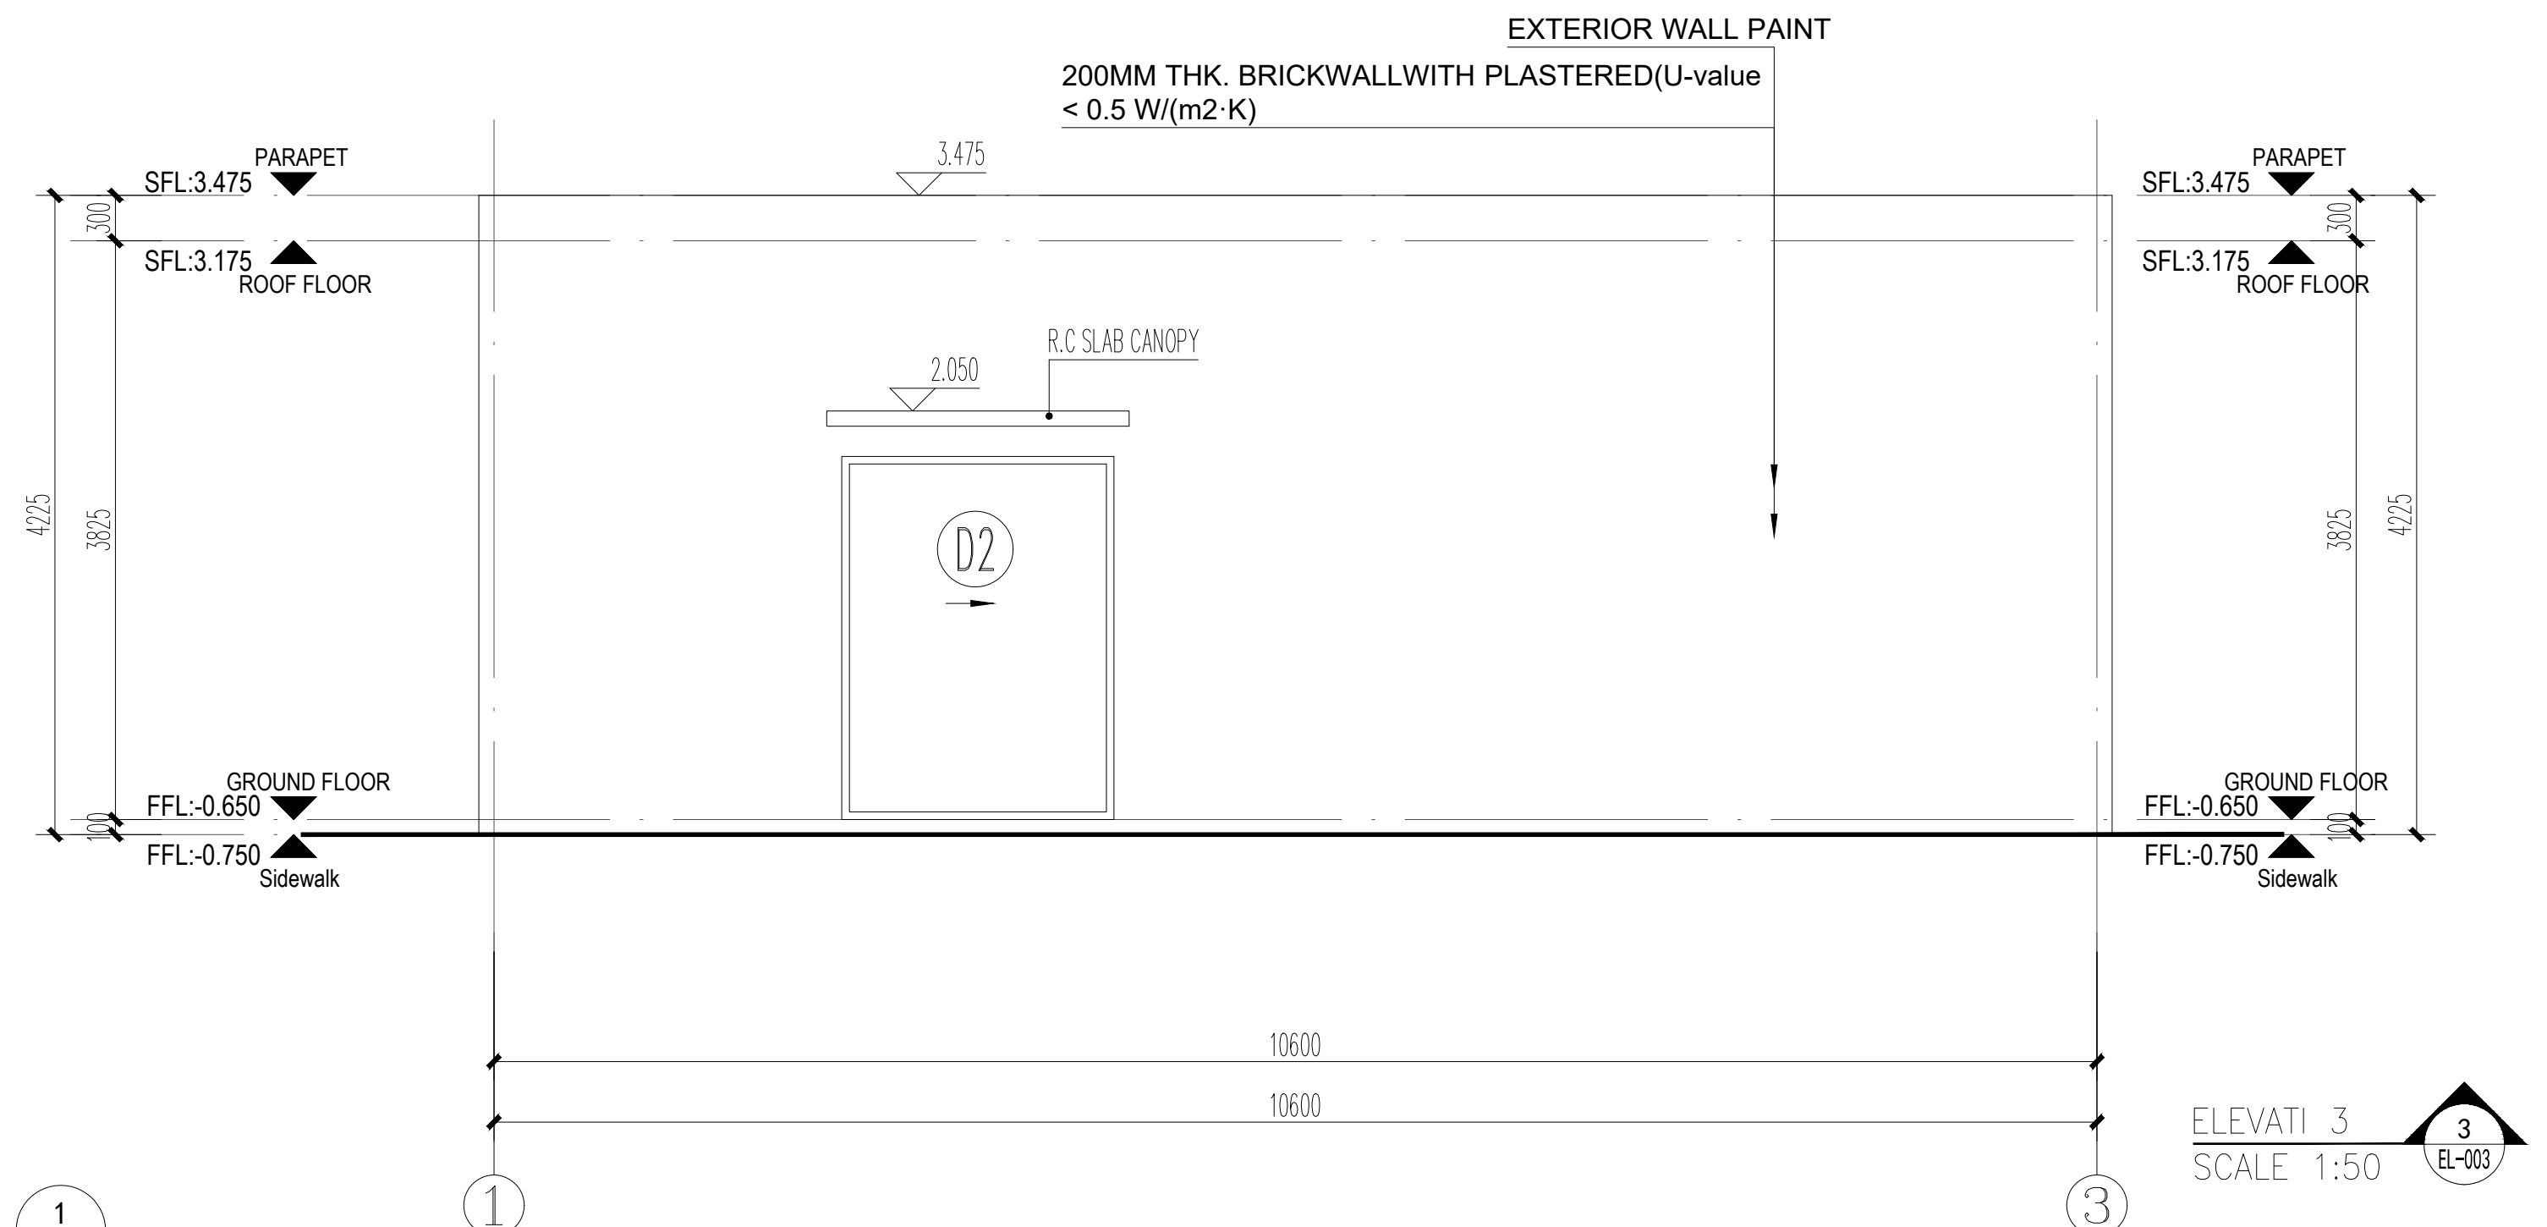

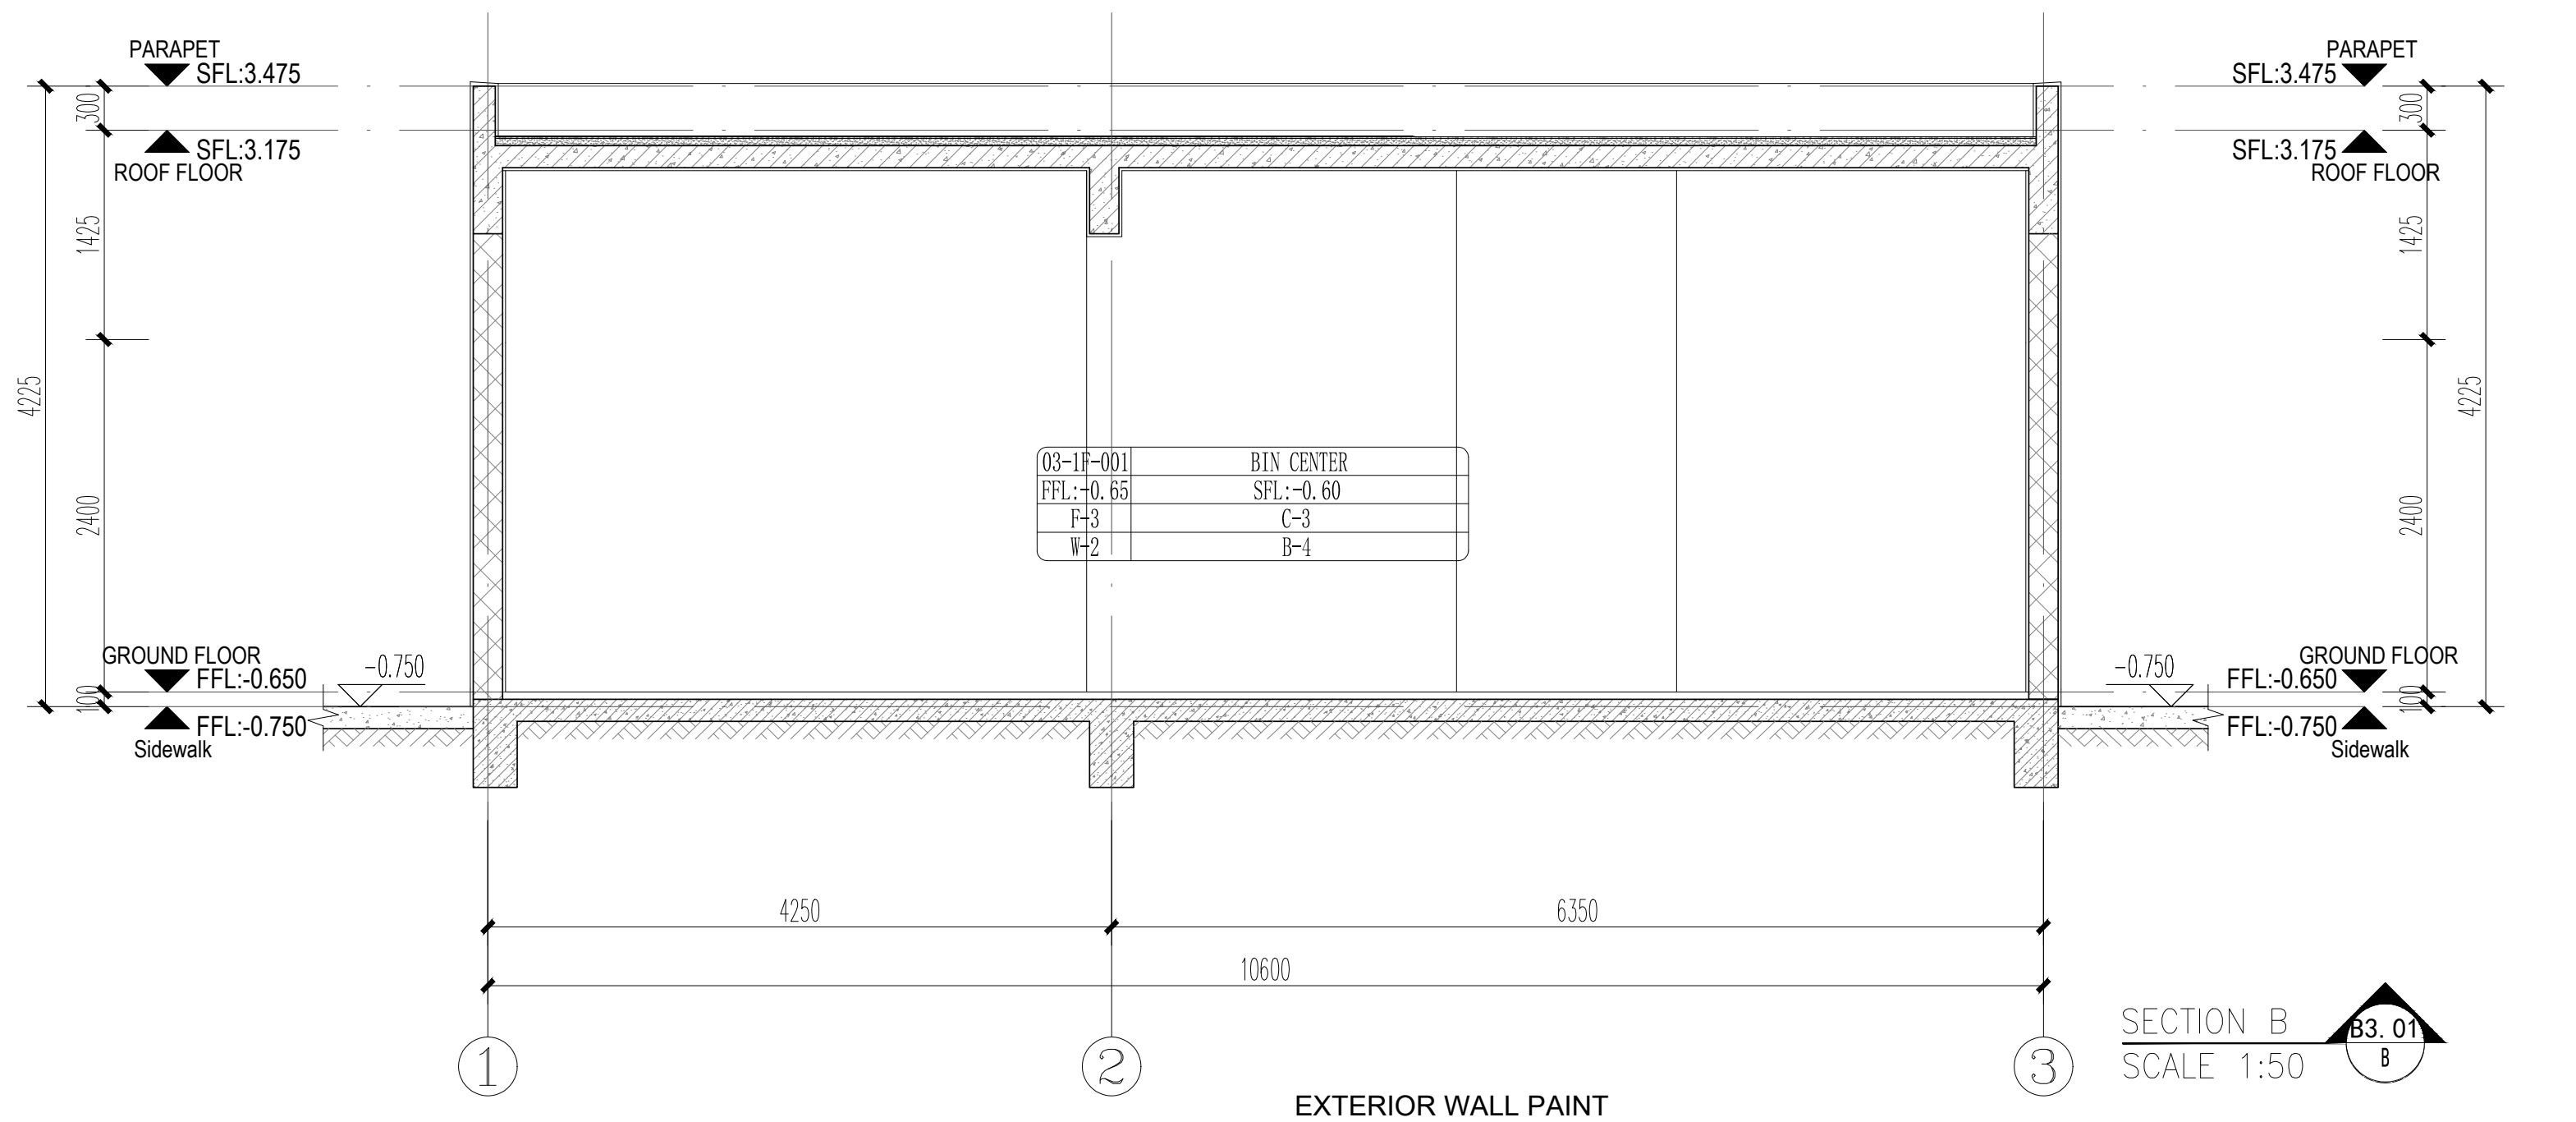

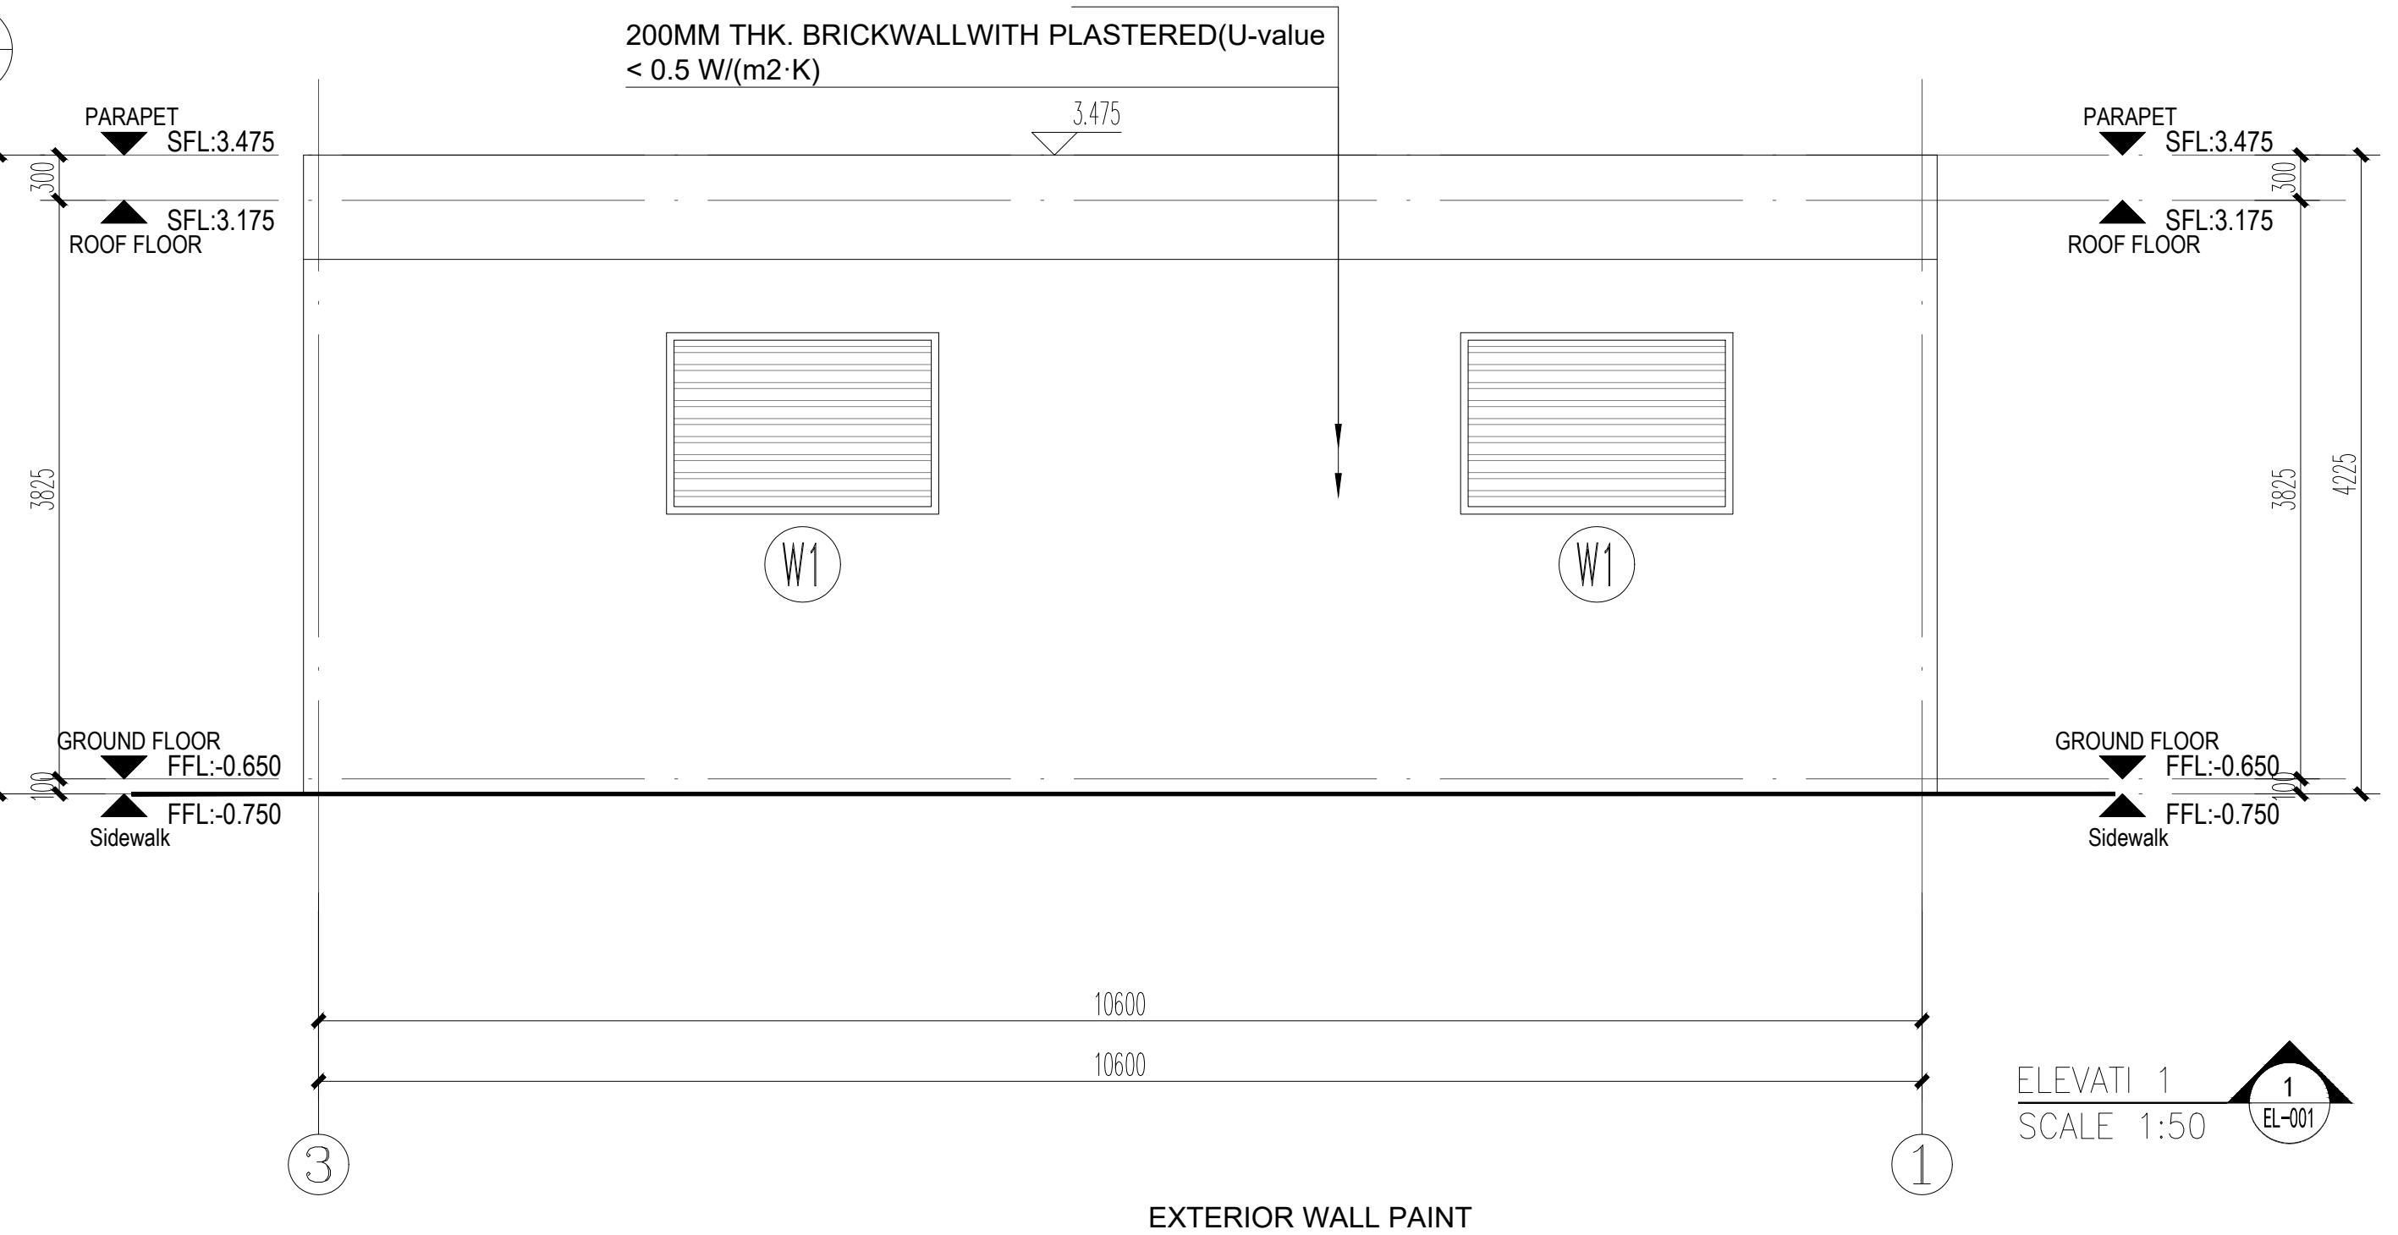

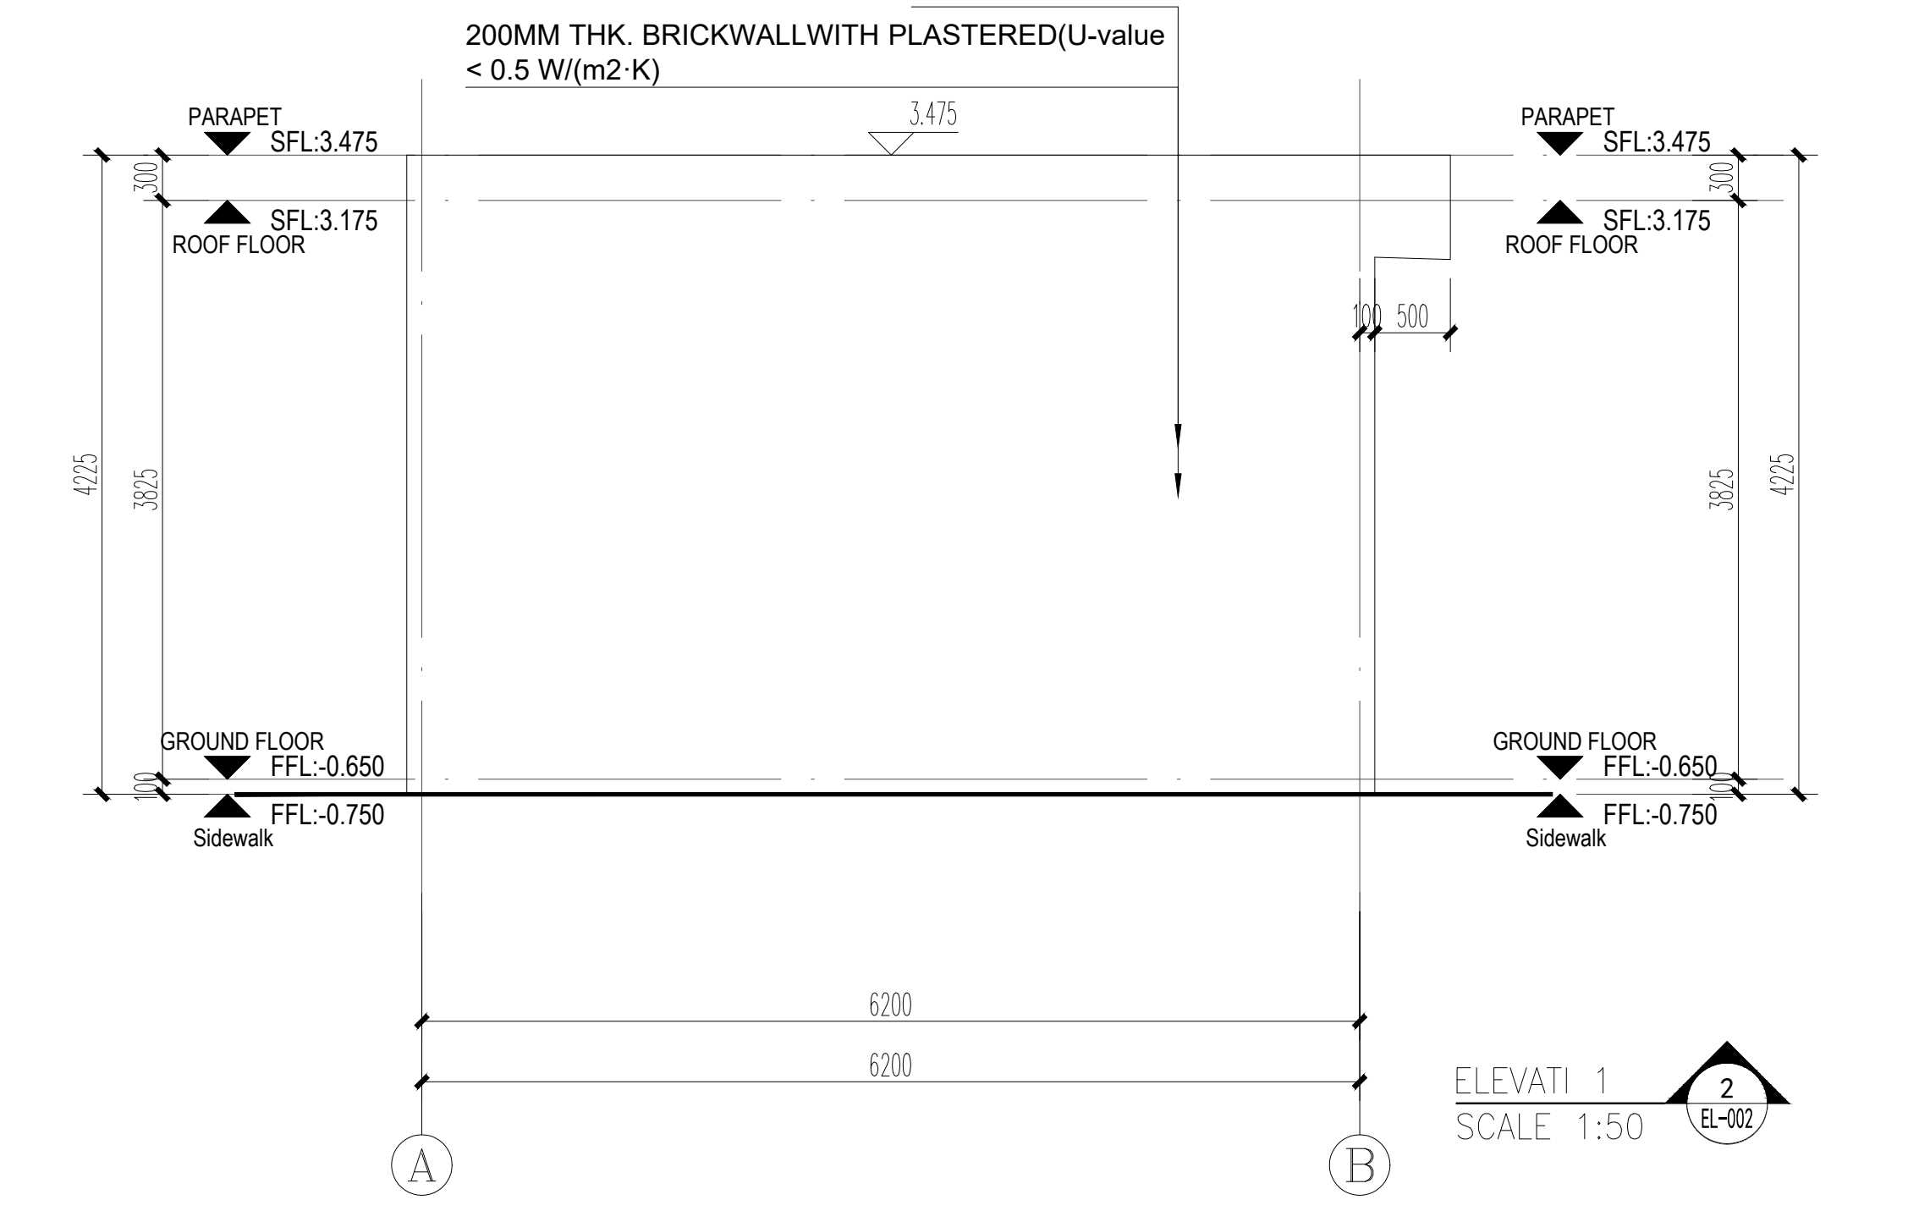

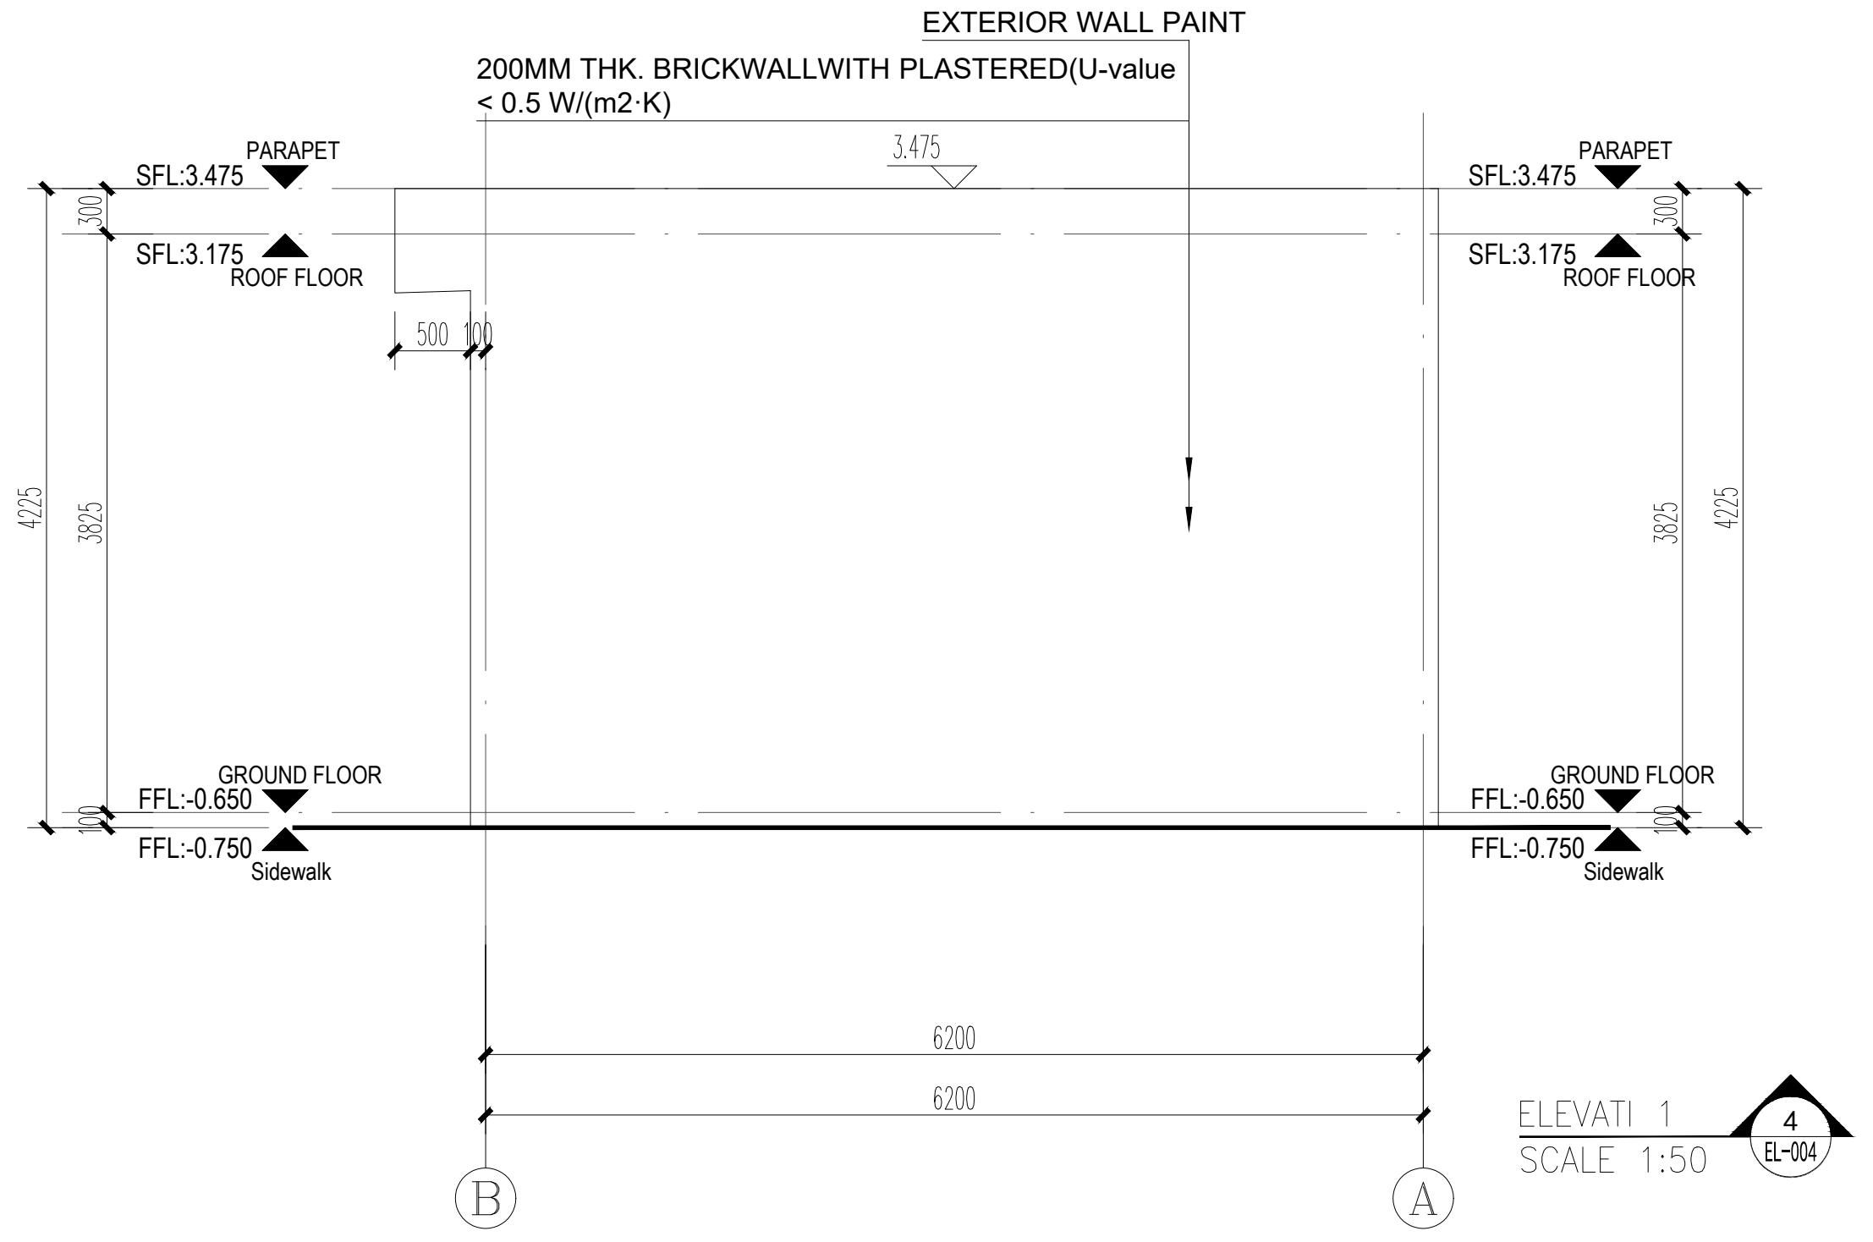

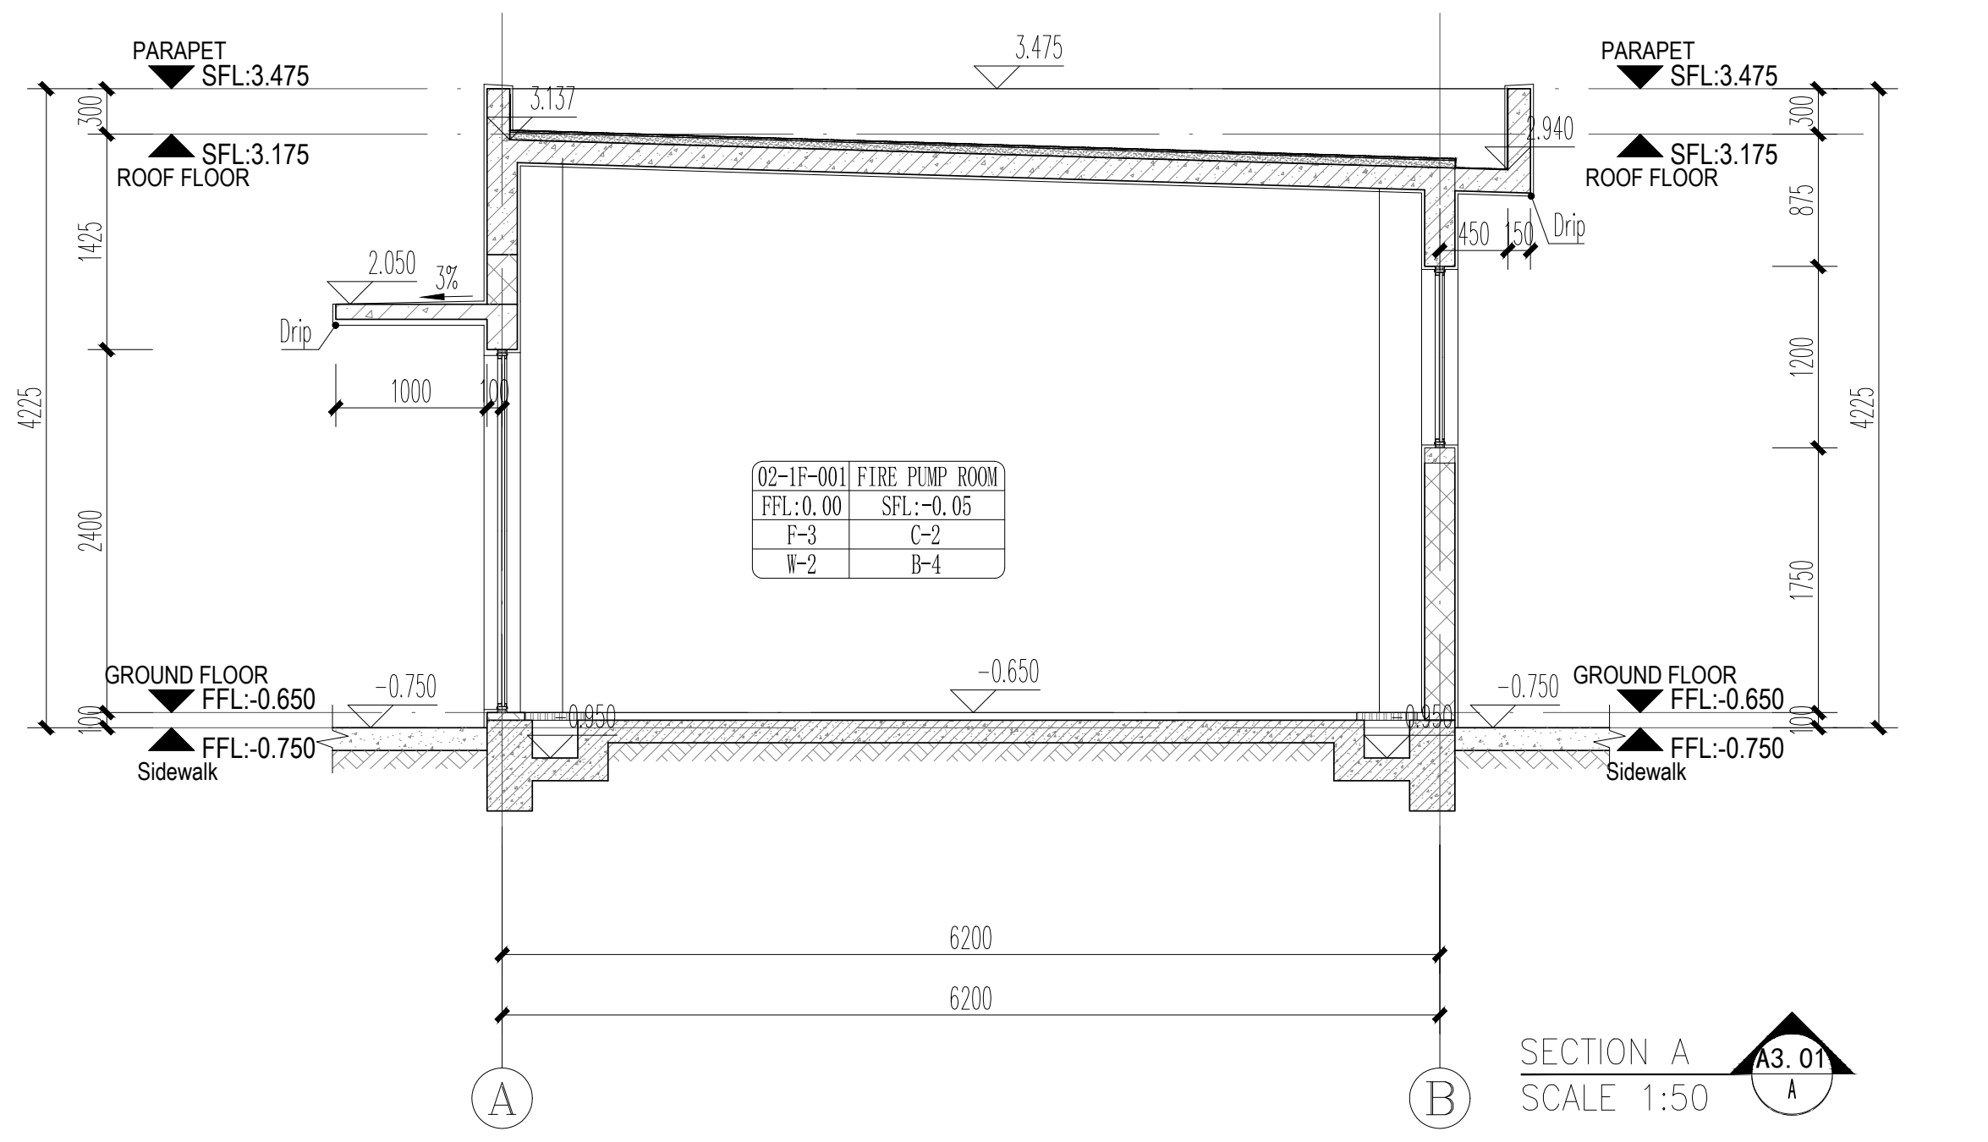

CLIENT :

GULF EDGE DC 01

87 Wireless Road, M Thai Tower 11th. Floor, All Seasons Place, Lumpini,
Pathumwan, Bangkok 10330, Thailand

CONTRACTOR :

华西发展(泰国)有限公司
บริษัท หัวซือ ดีเวลลอปเม้นต์ (ประเทศไทย) จำกัด
HUASHI DEVELOPMENT CO.,LTD
No. 202, Room No. 1403, 14/F, Le Concorde Building,
Ratchadapisek Road, Huaykhwang Sub-District,
Huaykhwang District, Bangkok Metropolitan 10310.

CONSULTANT :

ARbay
บริษัท เอ อาร์ เบย์ จำกัด
ARbay Company Limited
31 st Floor Bangkok Insurance Building
25 South Sathorn road Thungmahamek
Sathorn Bangkok 10120 THAILAND
T +66 (0) 2286 8199
F +66 (0) 2286 2863
info@arbay.co.th

CONSULTANT :

Qbic Engineers & Architects Co.,Ltd.
8 Soi KALONG 4 SANAMBINNAM ROAD,
THASAI SUB-DISTRICT, MUANG NONTHABURI DISTRICT
, NONTHABURI.
Tel 662-950-4374
Fax 662-580-3231
E-Mail : qbic@qbic.co.th, www.qbic.co.th
QBIC ENGINEERS AND ARCHITECTS CO.,LTD.

CONSULTANT :

MITR
MITR TECHNICAL CONSULTANT CO.,LTD.
1168/8 12th FLOOR, LUMPINI TOWER BUILDING,
RAMA IV RD., THUNGMAHAMEK, SATHORN, BANGKOK 10120, THAILAND
TEL : 0-2679-9079-84
FAX : 0-2679-9085 E-mail: mitr_dd@mitr.com

Architect : SIGNATURE
ประกิต พนานุรัตน์ วสถ. 580
ที่อยู่
251/1 ถ.จารุเมือง แขวงรองเมือง เขตปทุมวัน
กรุงเทพมหานคร โทรศัพท์ 02-286-8199

Structural Engineer : SIGNATURE
วิศวกรผู้ออกแบบโครงสร้าง
ณัฐสม สงวนวงษ์ วย 1423
ที่อยู่
2/1 ซ.รามคำแหง 150 ถ.รามคำแหง
แขวง สะพานสูง เขต สะพานสูง กทม. 10240

Structural Inspector : SIGNATURE
วิศวกรผู้ตรวจสอบโครงสร้าง
โกมล จุฑาภัทร วย 964
ที่อยู่
24/18 ซ.นวมินทร์ 129 ถ. นวมินทร์
แขวง นวลจันทร์ เขต บึงกุ่ม กทม. 10230

Electrical Engineer : SIGNATURE
วิศวกรผู้ออกแบบระบบไฟฟ้ากำลัง
นายสุภัทร บูรณวิทย์ วฟก.1265
ที่อยู่
21 ซอยทานสัมฤทธิ์ 13
ตำบลท่าทราย อ.เมืองนนทบุรี จ.นนทบุรี 11000

Mechanical Engineer : SIGNATURE
วิศวกรผู้ออกแบบระบบเครื่องกลและปรับอากาศ
นายประสิทธิ์ เกียวสุนทร วก.1221
ที่อยู่
44/372 ซอยบางกระดี่ 35/1 แขวงแสมดำ
เขตบางขุนเทียน กทม. 10150
ประสิทธิ์

Sanitary Engineer : SIGNATURE
วิศวกรผู้ออกแบบระบบสุขาภิบาล และดับเพลิง
นายทศวรรษ สนันฤทธิ์ วส. 215
ที่อยู่
บ้านเลขที่ 99/107 หมู่ที่ 3 ต.ศีรษะจรเข้น้อย
อ.บางเสาธง จ.สมุทรปราการ 10540
ทศวรรษ

ISSUE/REVISION

REV.	DESCRIPTION	DATE
A	90% DEVELOPED	09/05/2026

PROJECT NAME :
GEDC 01

LOCATION:
Nikhom Phattana district, Rayong ,industrial estate,CPGC

BUILDING :
BIN CENTER

90% DEVELOPED

TITLE :
BIN CENTER PLAN & SECTION & ELEVATION

JOB NO.	SCALE 1:50
DRAWN LK	REF.
CHECKED LJC	DWG.NO.
APPROVED LXD	MPK03-60-A-P&EL&SE-101
DATE 2026.05.09	

NOTE : THIS PRINT IS OF A CONFIDENTIAL NATURE, IT SHALL NOT BE TRACED,PHOTOGRAPHED,PHOTOSTATED OR REPRODUCED IN ANY MANER,NOR USED FOR ANY PURPOSE WHATSOEVER EXCEPT BY WRITTEN PERMISSION