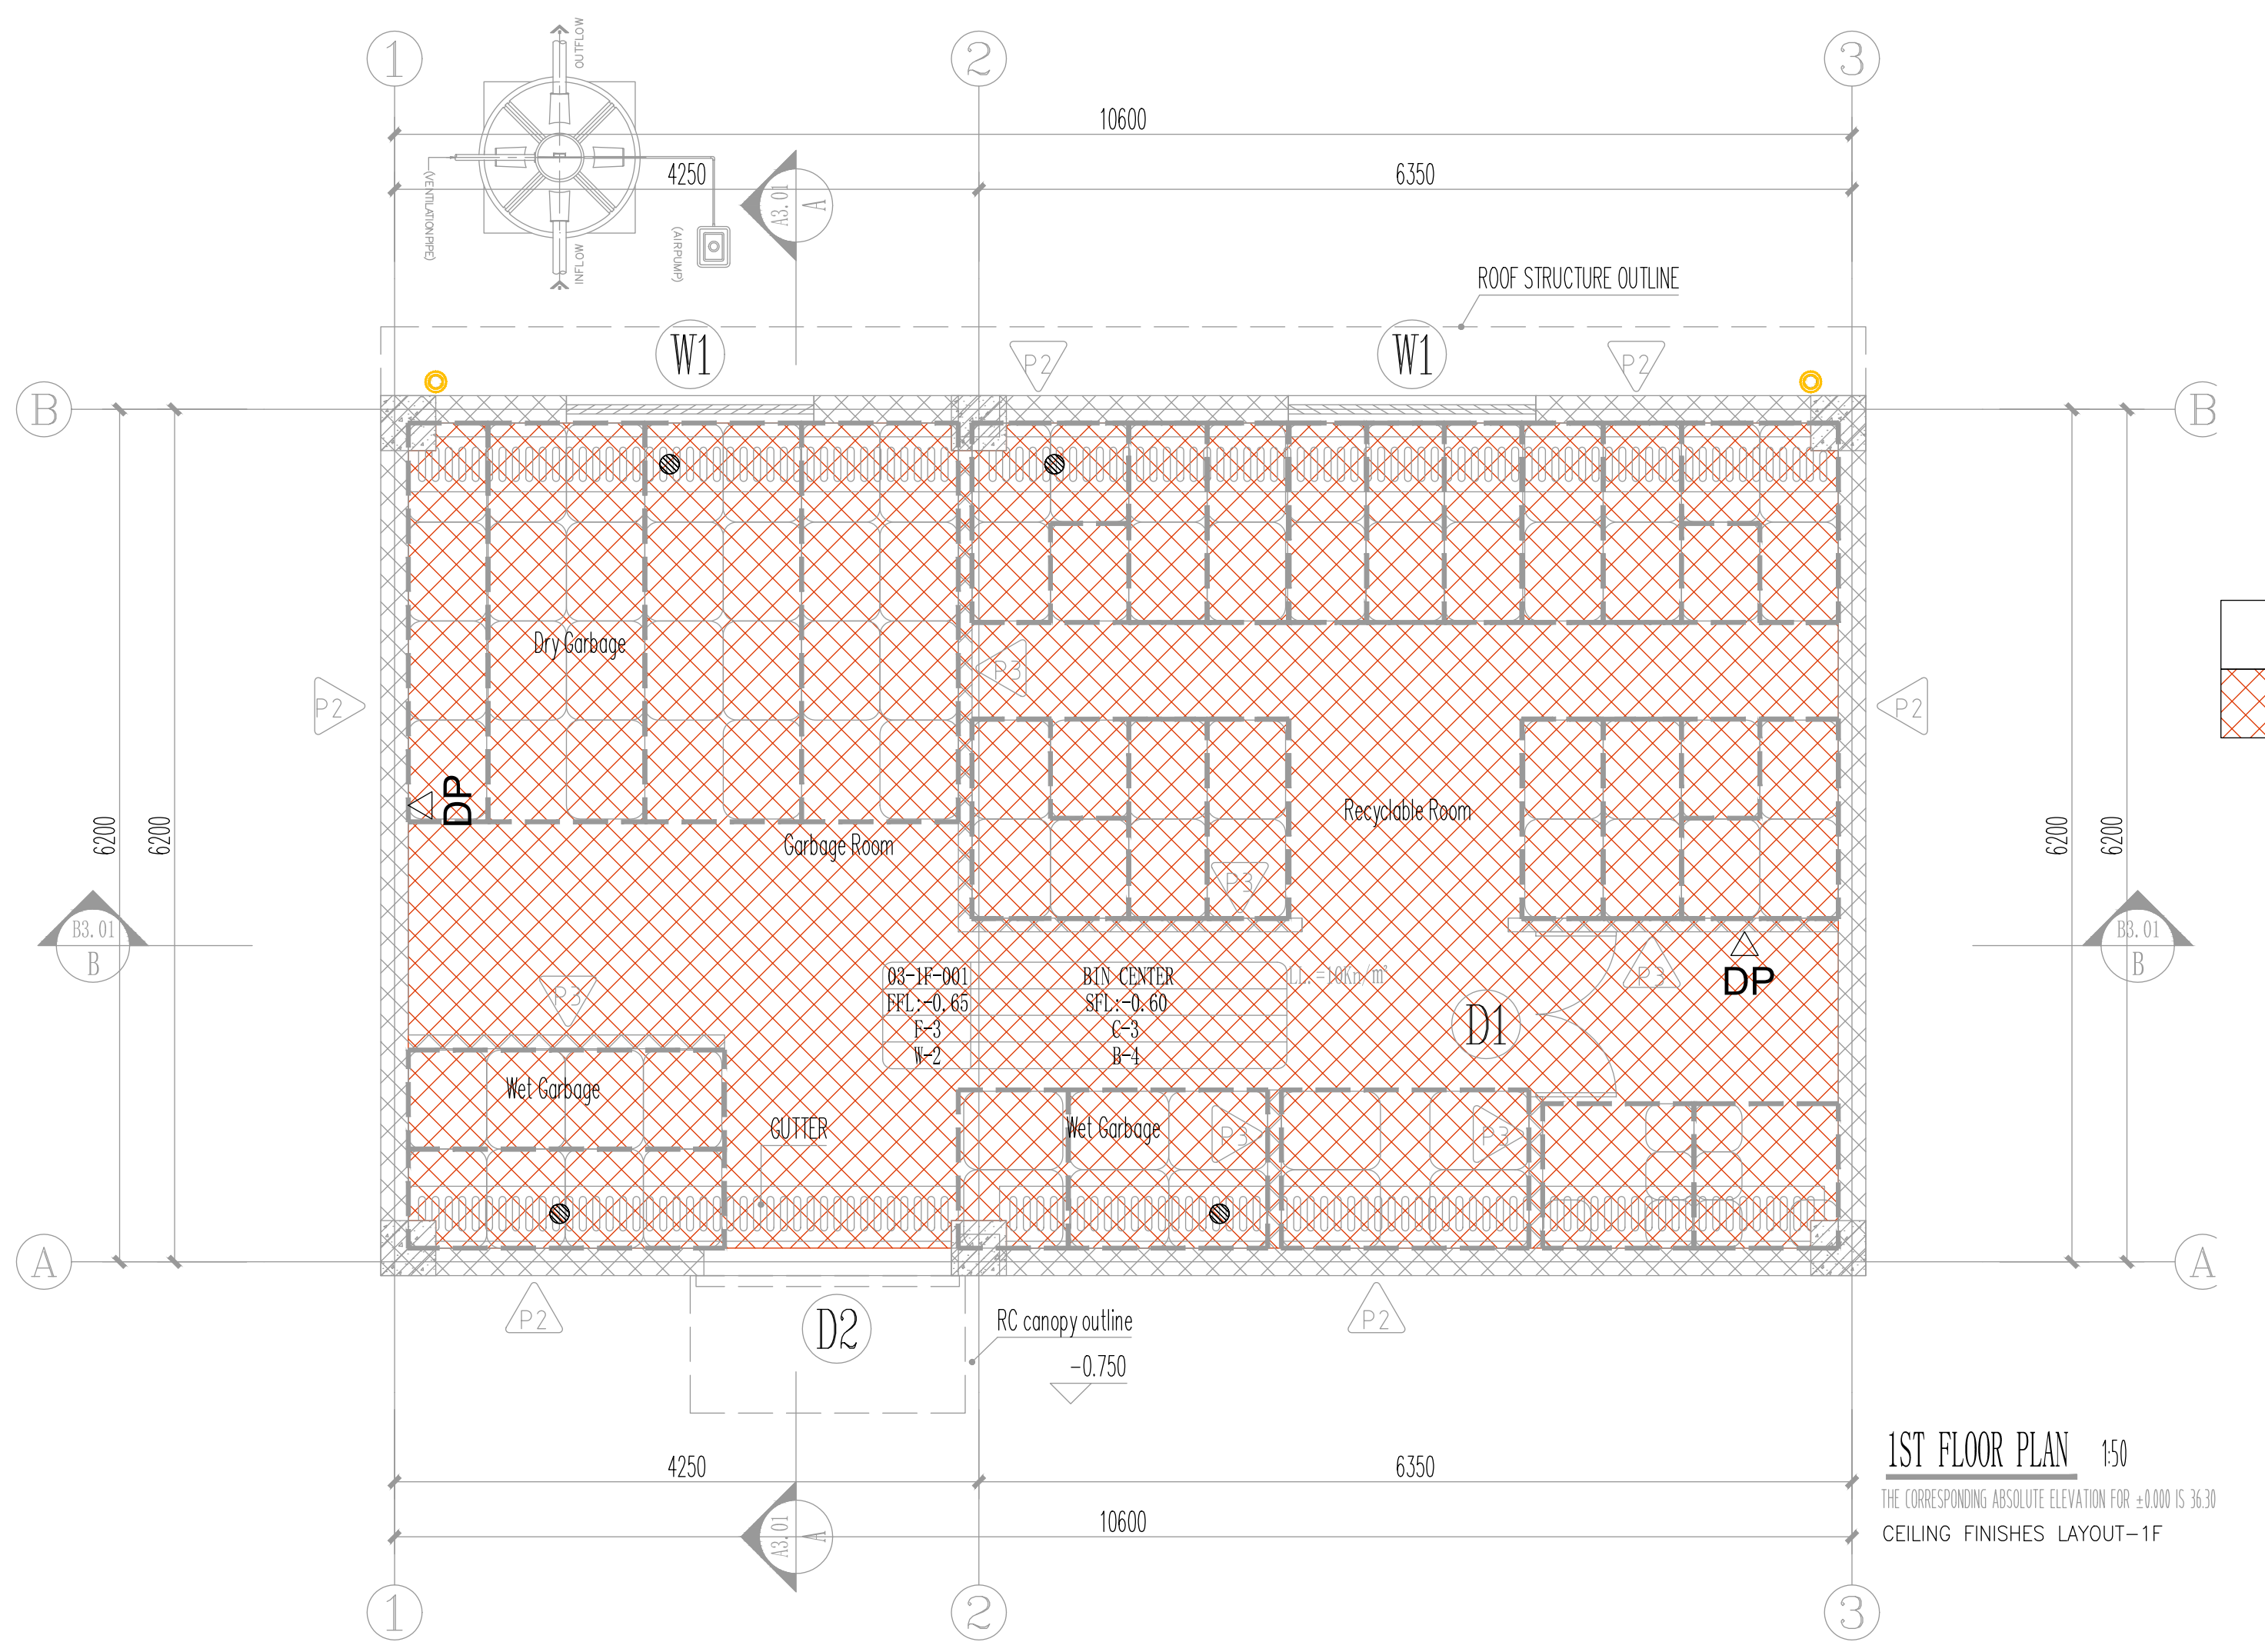

1ST FLOOR PLAN 1:50
THE CORRESPONDING ABSOLUTE ELEVATION FOR ±0.000 IS 36.30
CEILING FINISHES LAYOUT-1F

	Ceiling No.	Description	Ceiling Material & Finish Specification	Vender
▨	C-3	MOISTURE-PROOF PAINT	MOISTURE-PROOF PAINT ON CONCRETE CEILING SLAB	

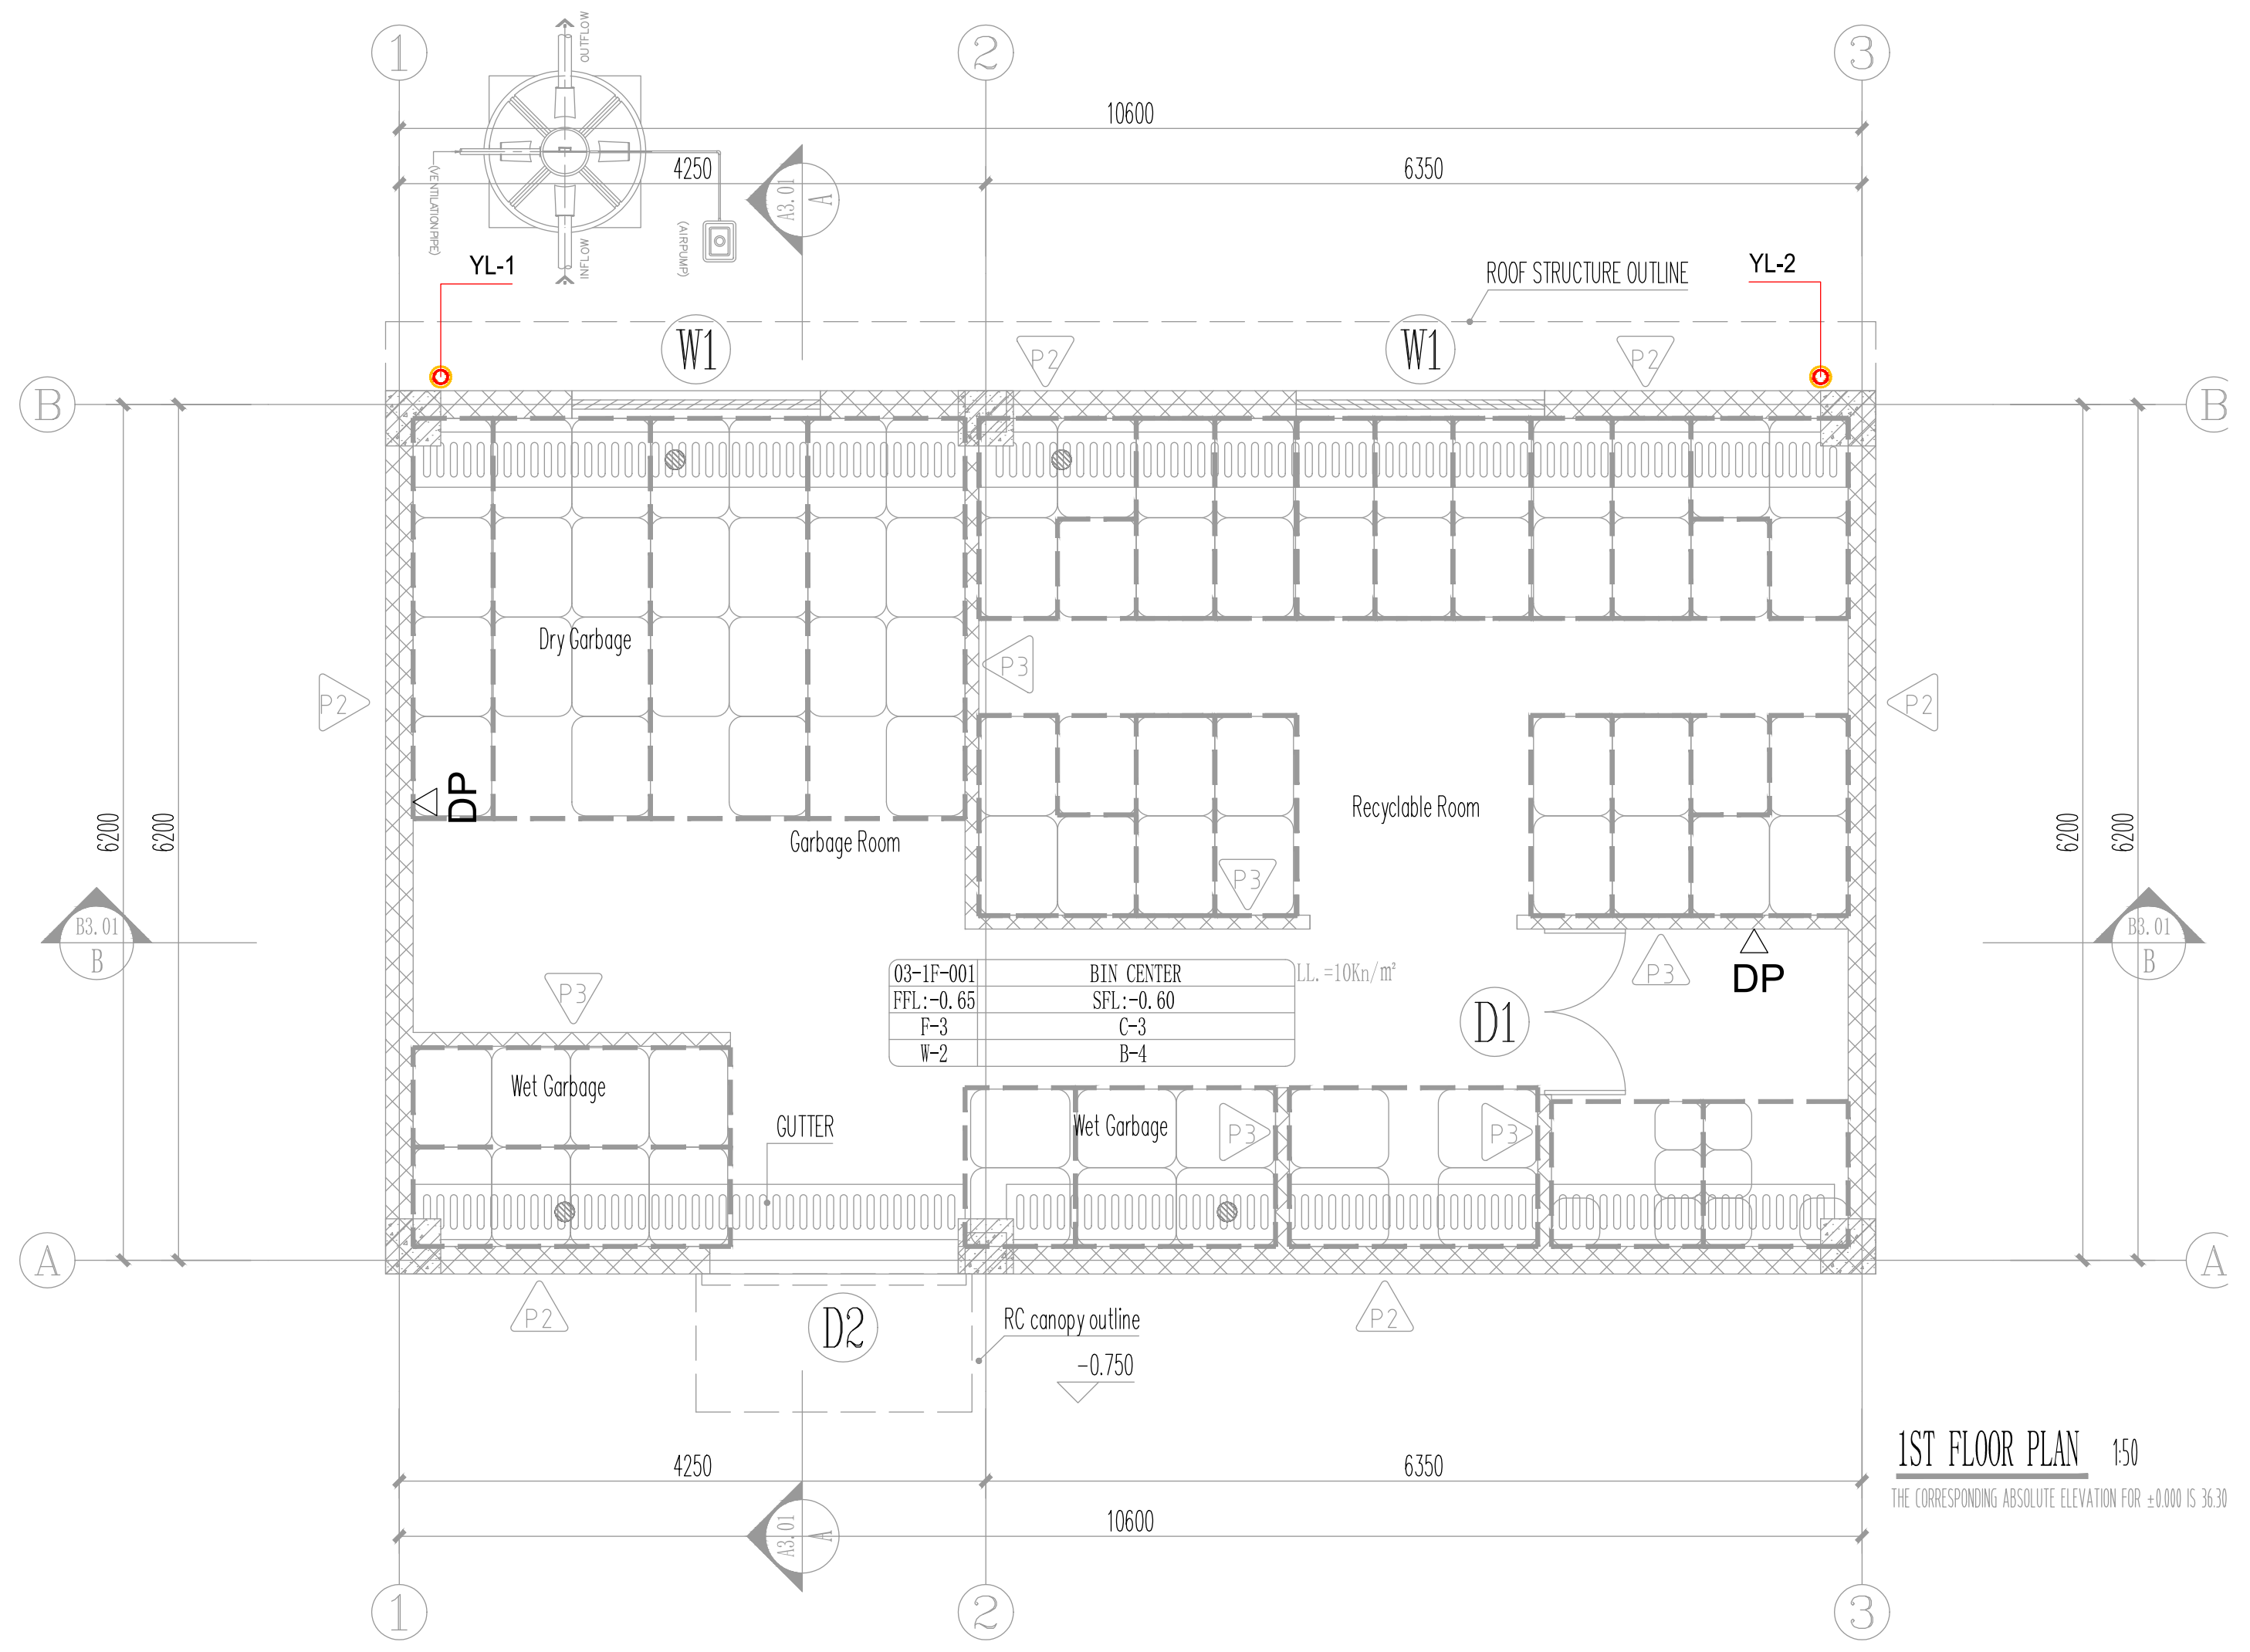

1ST FLOOR PLAN 1:50
THE CORRESPONDING ABSOLUTE ELEVATION FOR ±0.000 IS 36.30

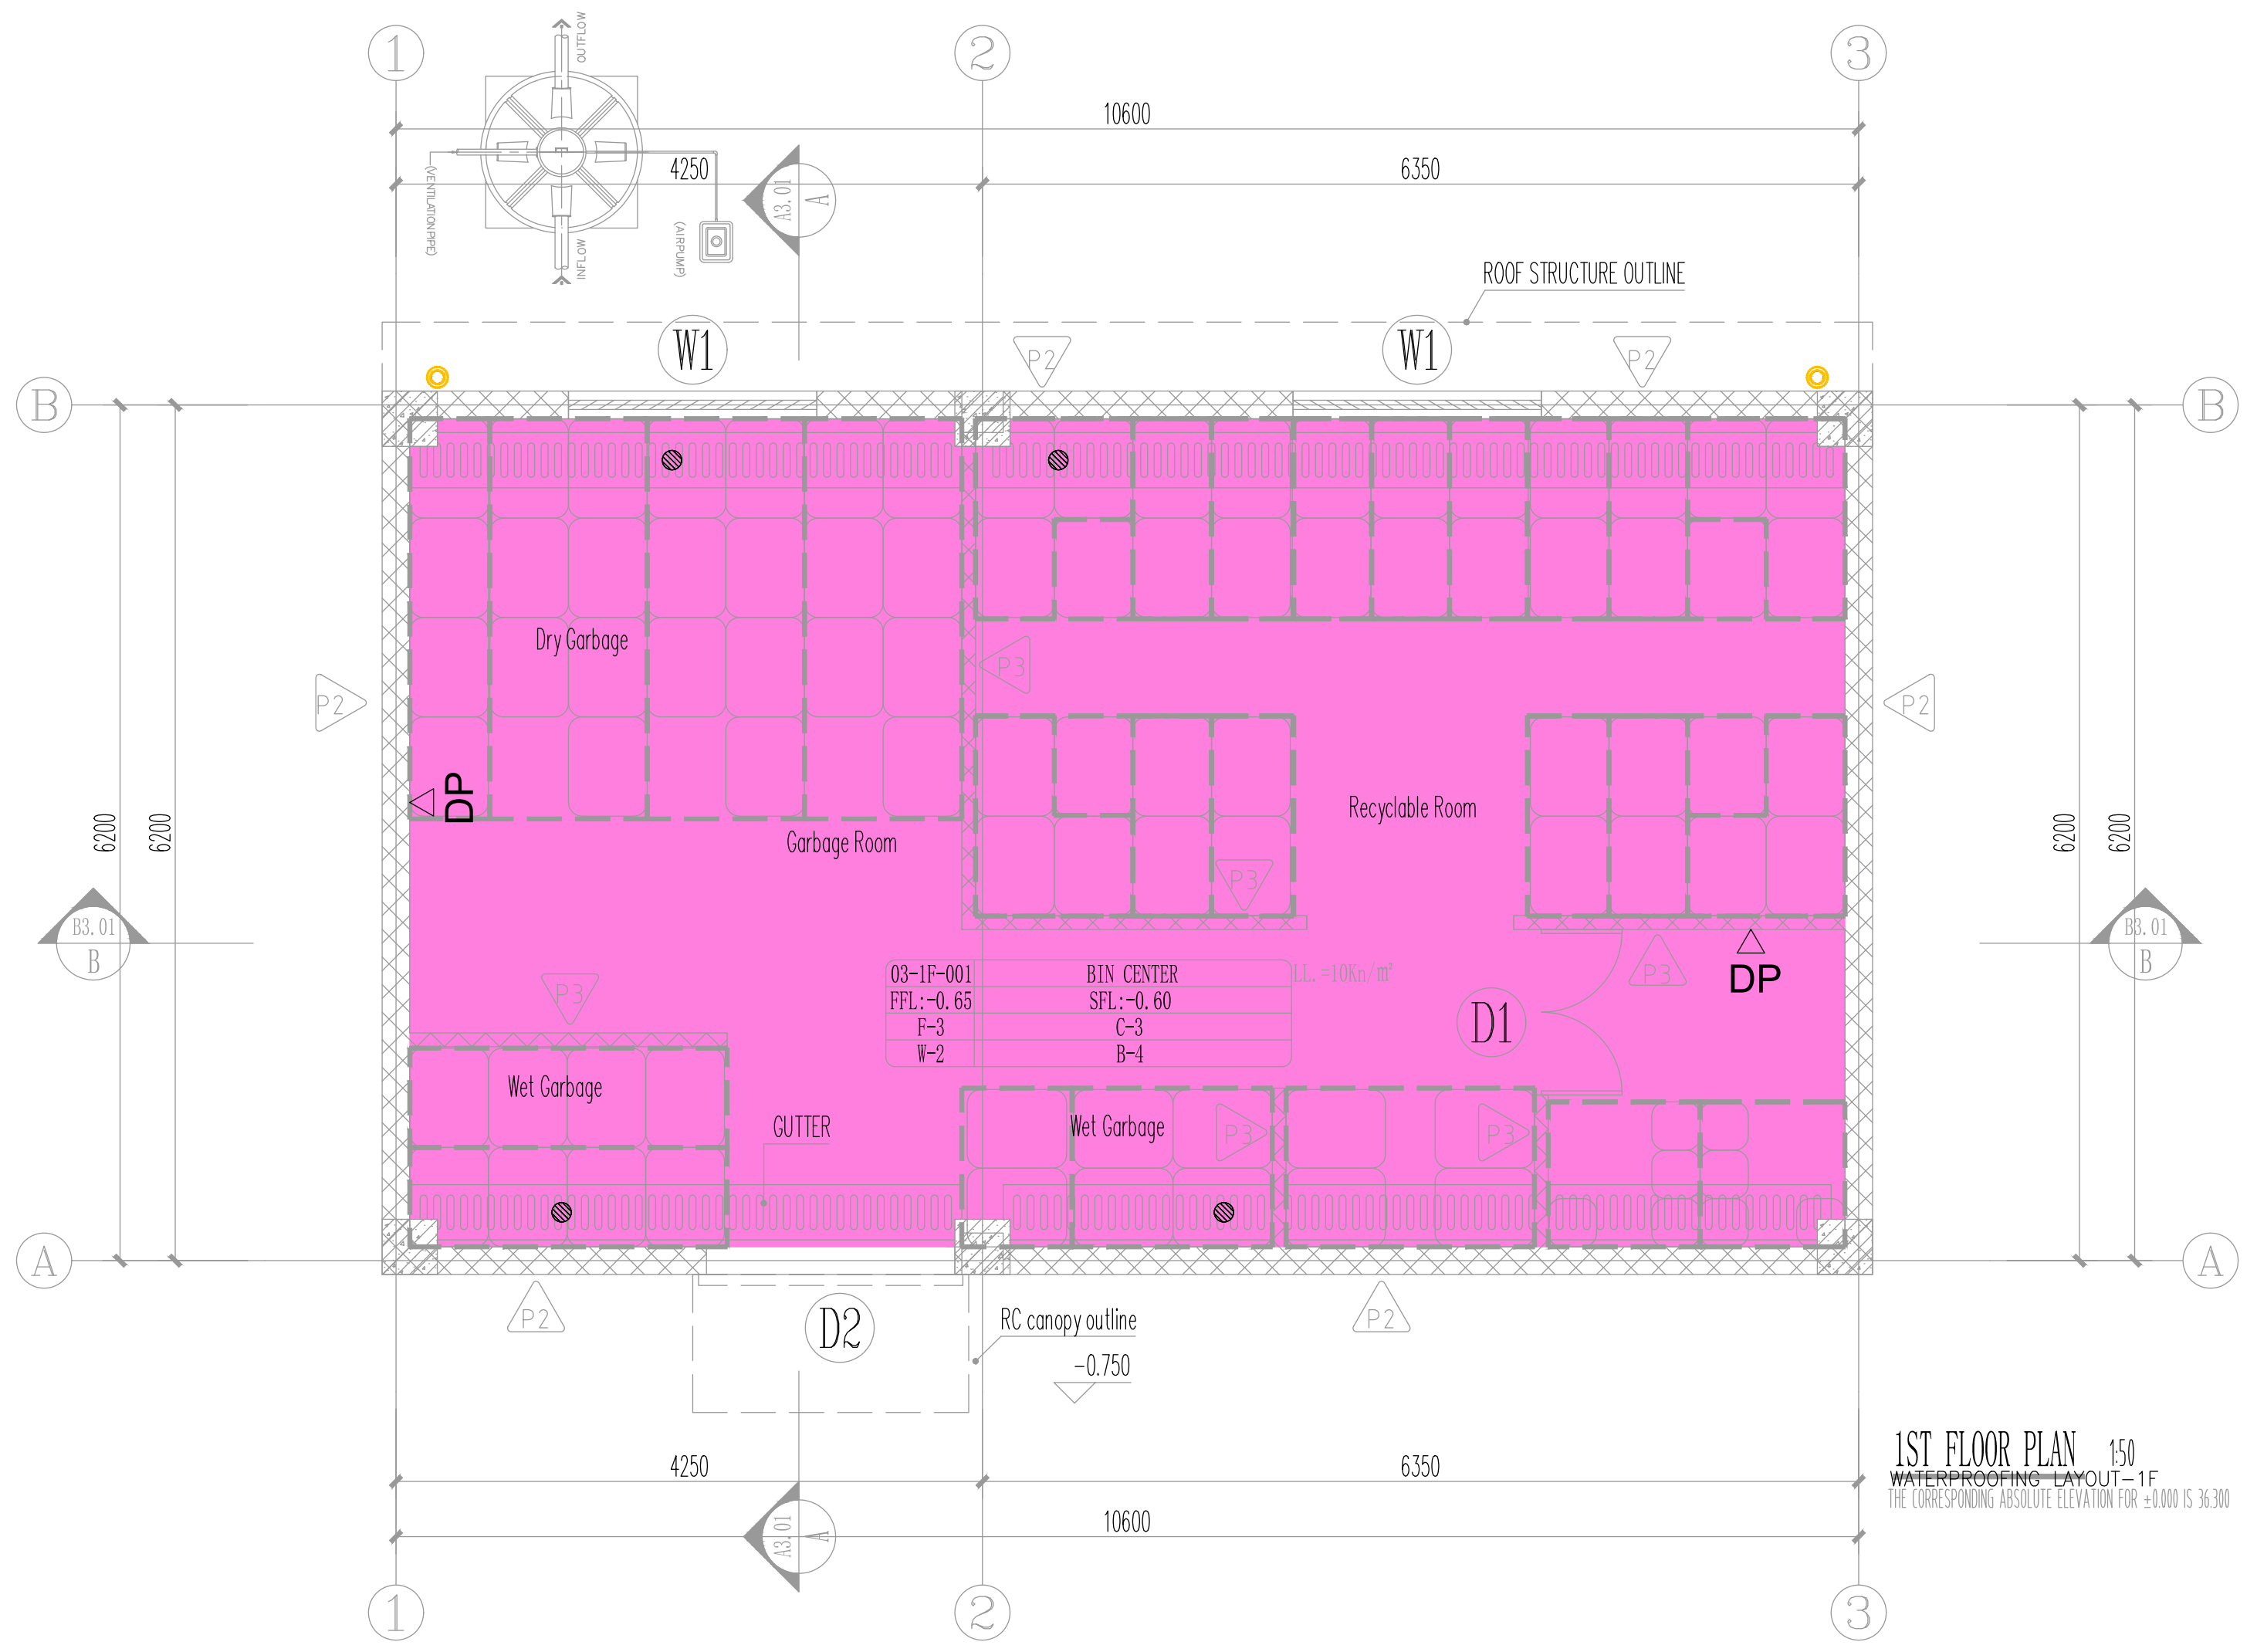

1ST FLOOR PLAN 1:50
WATERPROOFING LAYOUT-1F
THE CORRESPONDING ABSOLUTE ELEVATION FOR ±0.000 IS 36.300

WATER PROOFING	
wp-01	Cementitious waterproofing(to manufacturer's detail)
wp-02	Concrete Roof + Curing Agent+ Waterproofing

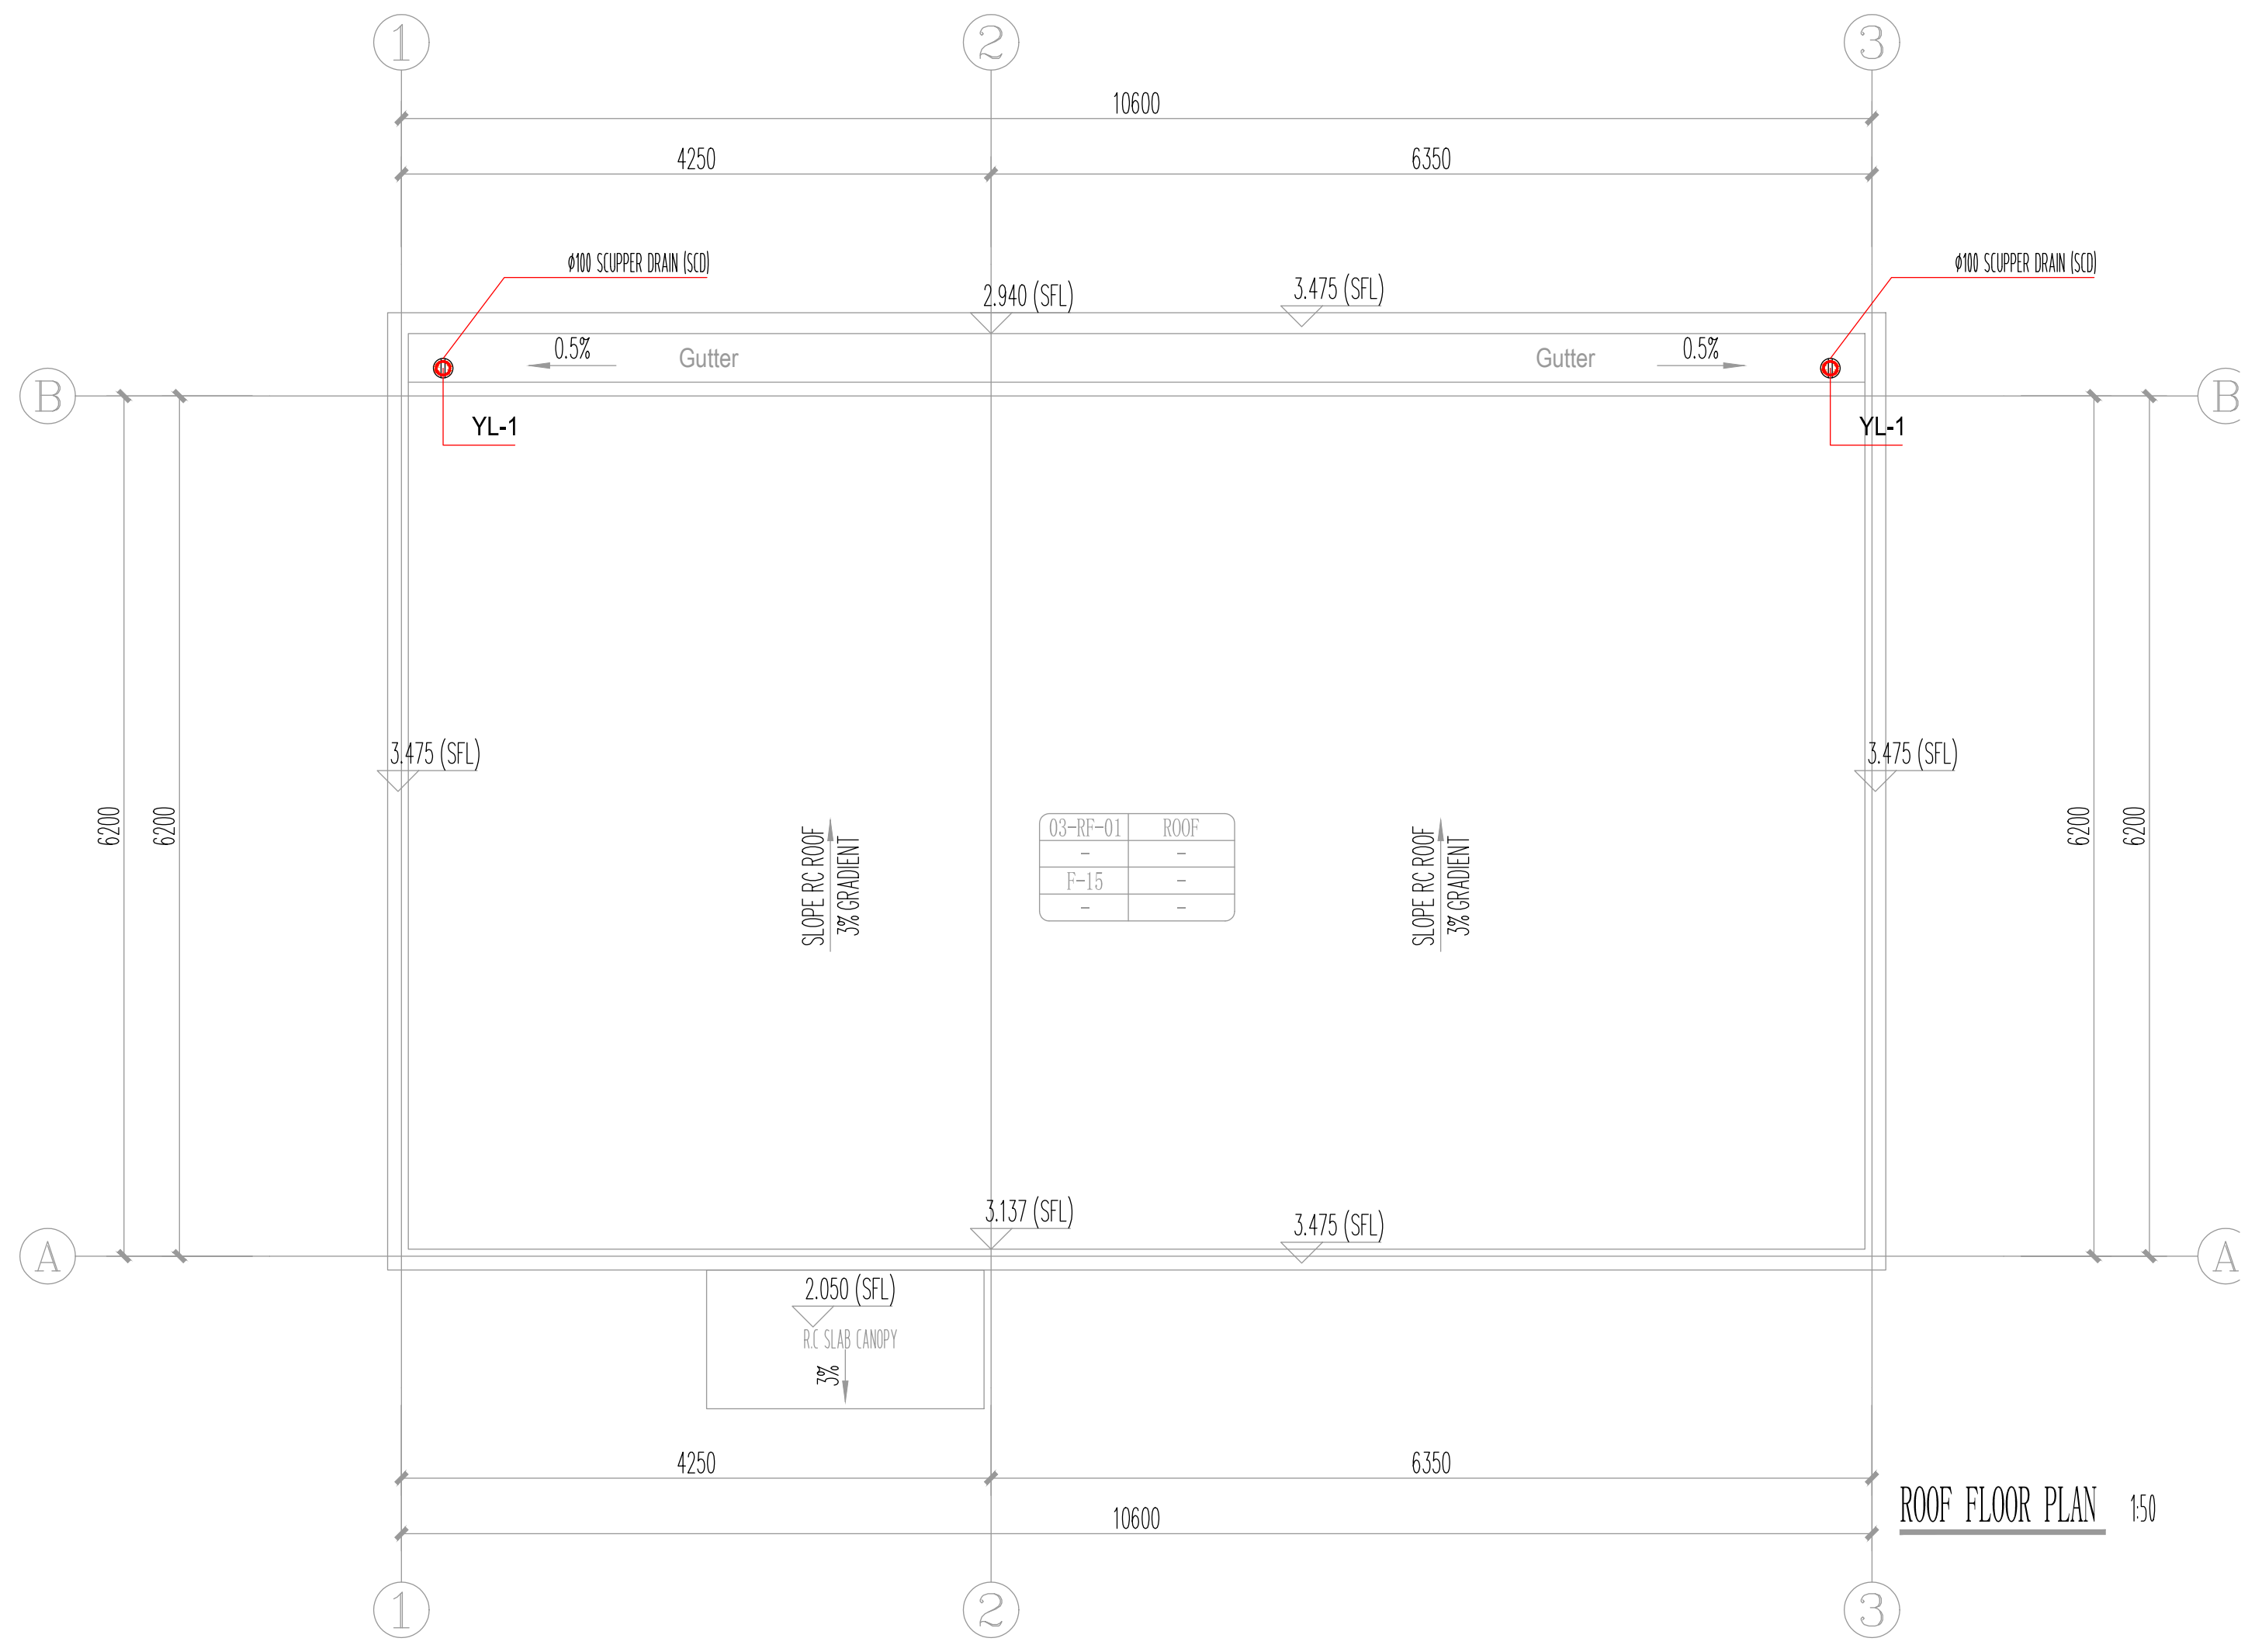

ROOF FLOOR PLAN 1:50

LEGEND	
YL	100MM HDPE

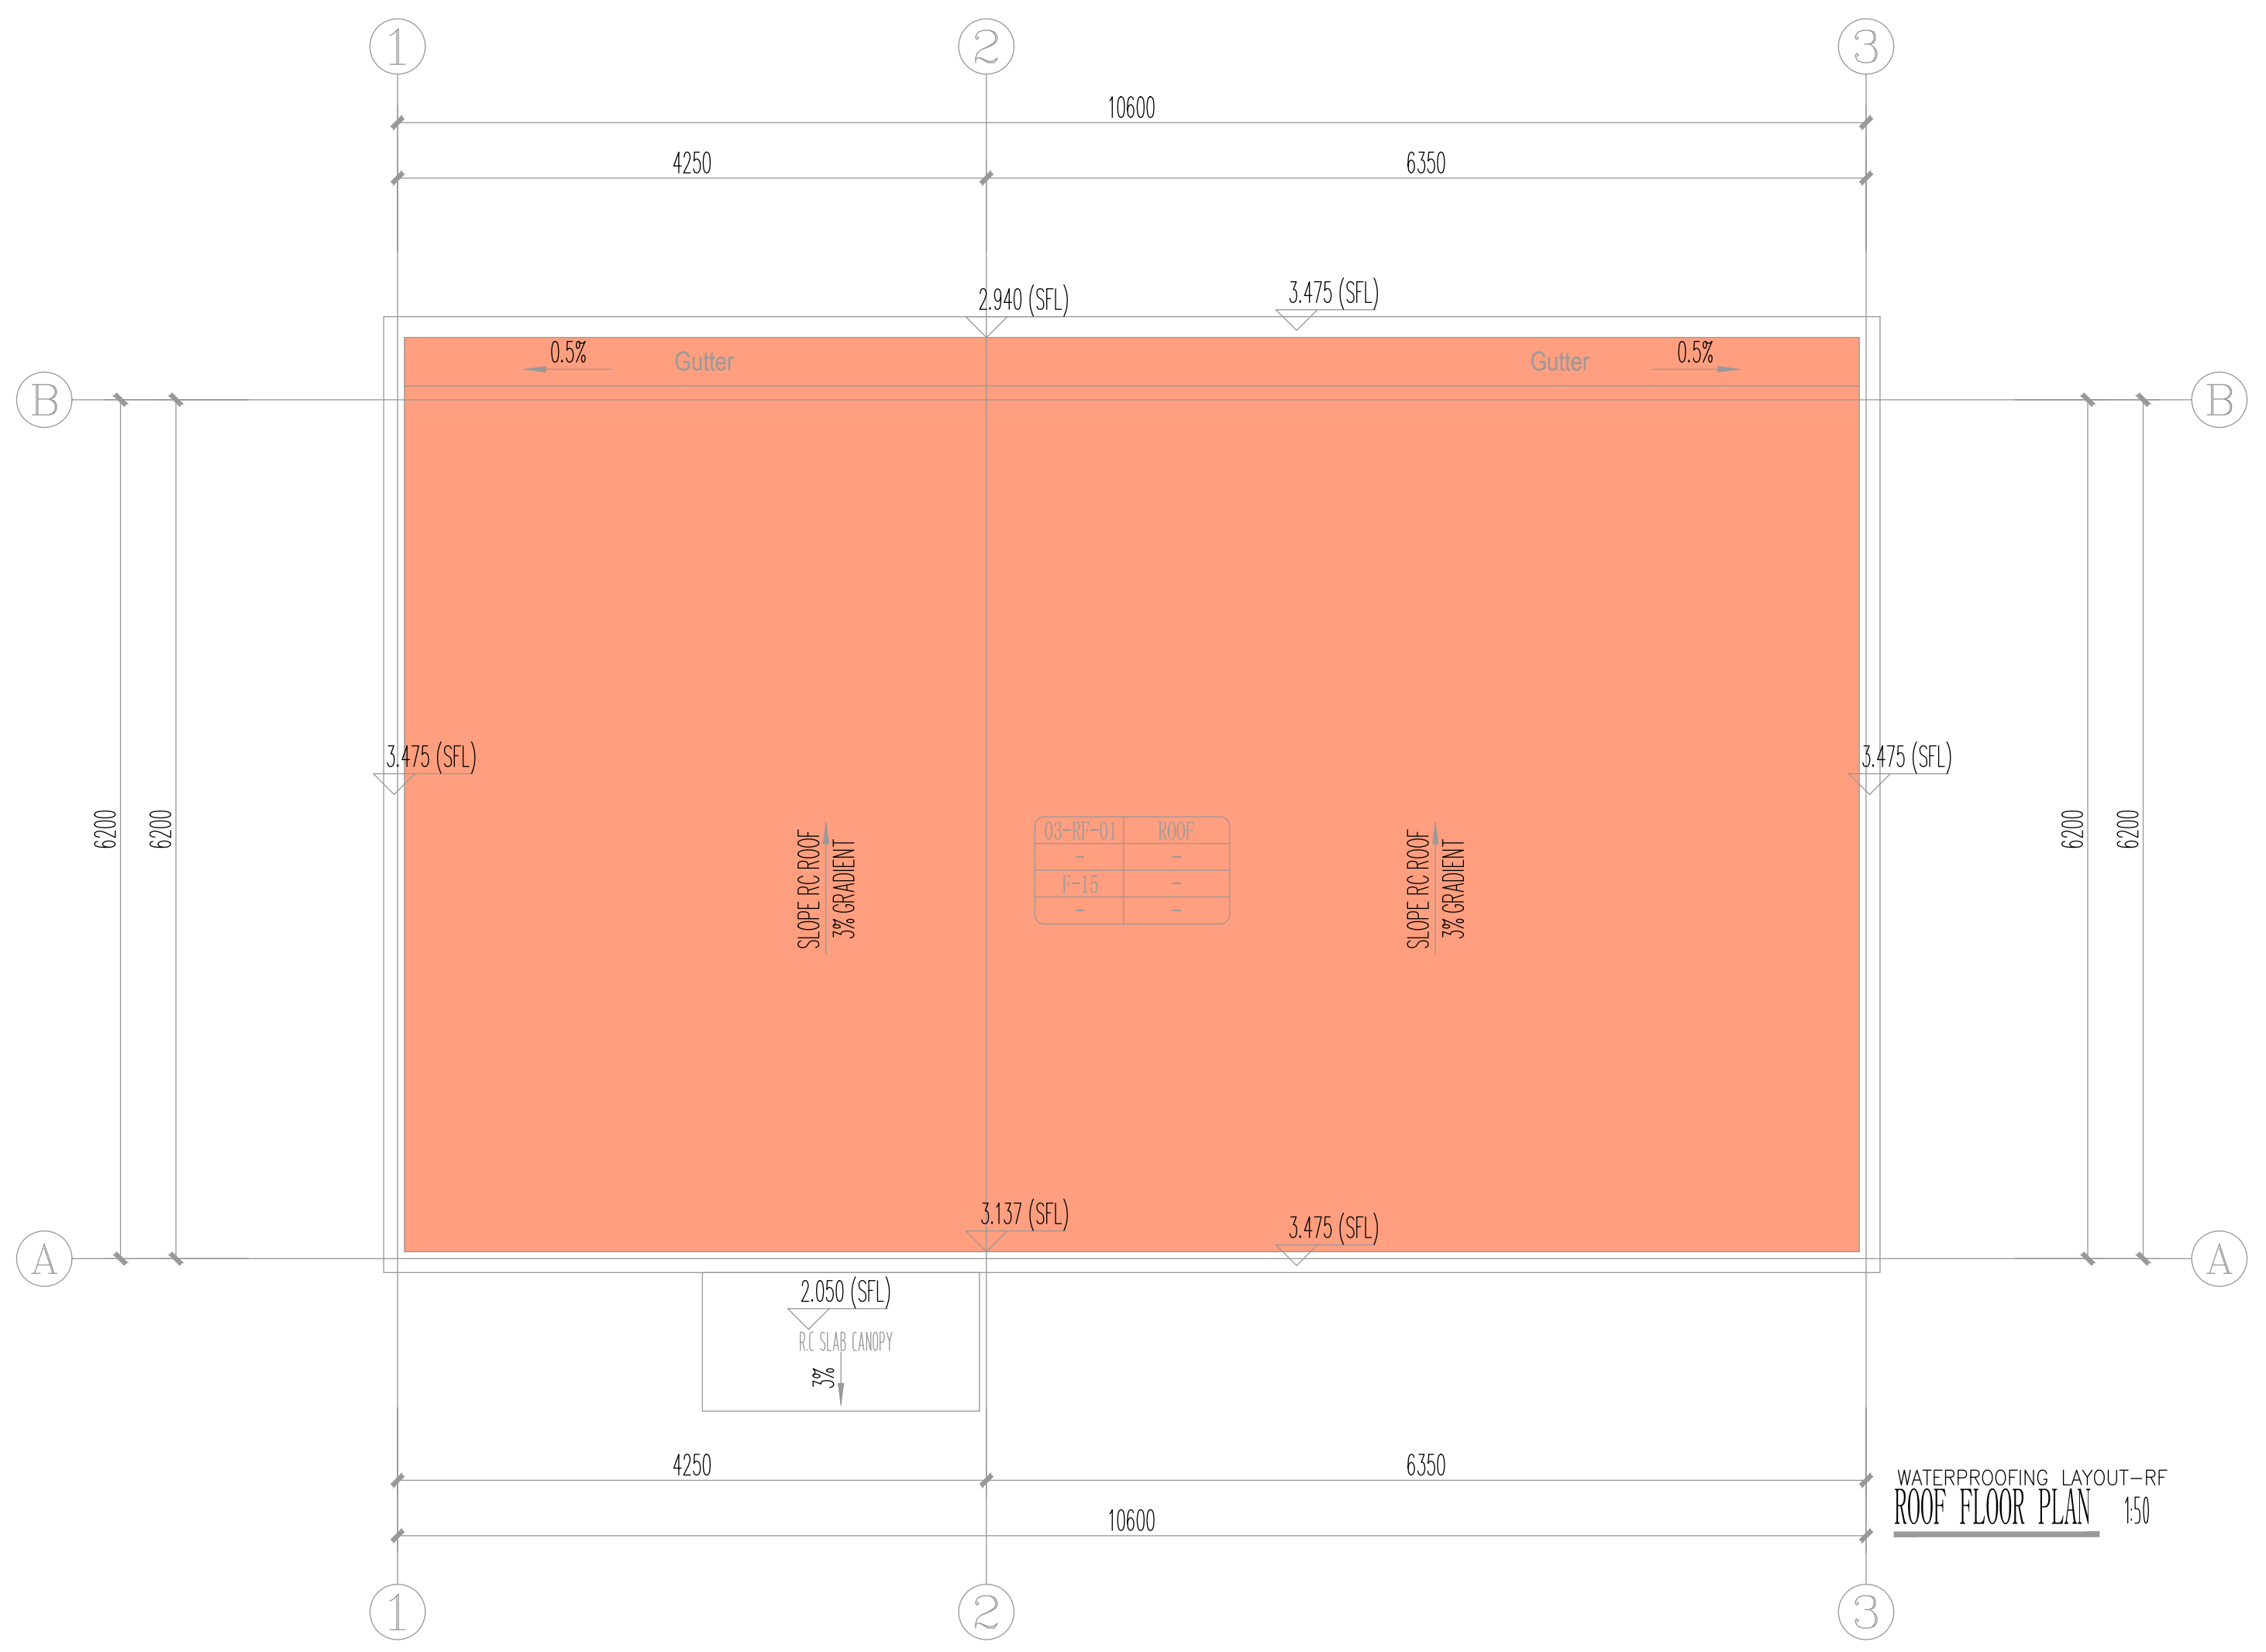

WATERPROOFING LAYOUT-RF
ROOF FLOOR PLAN 1:50

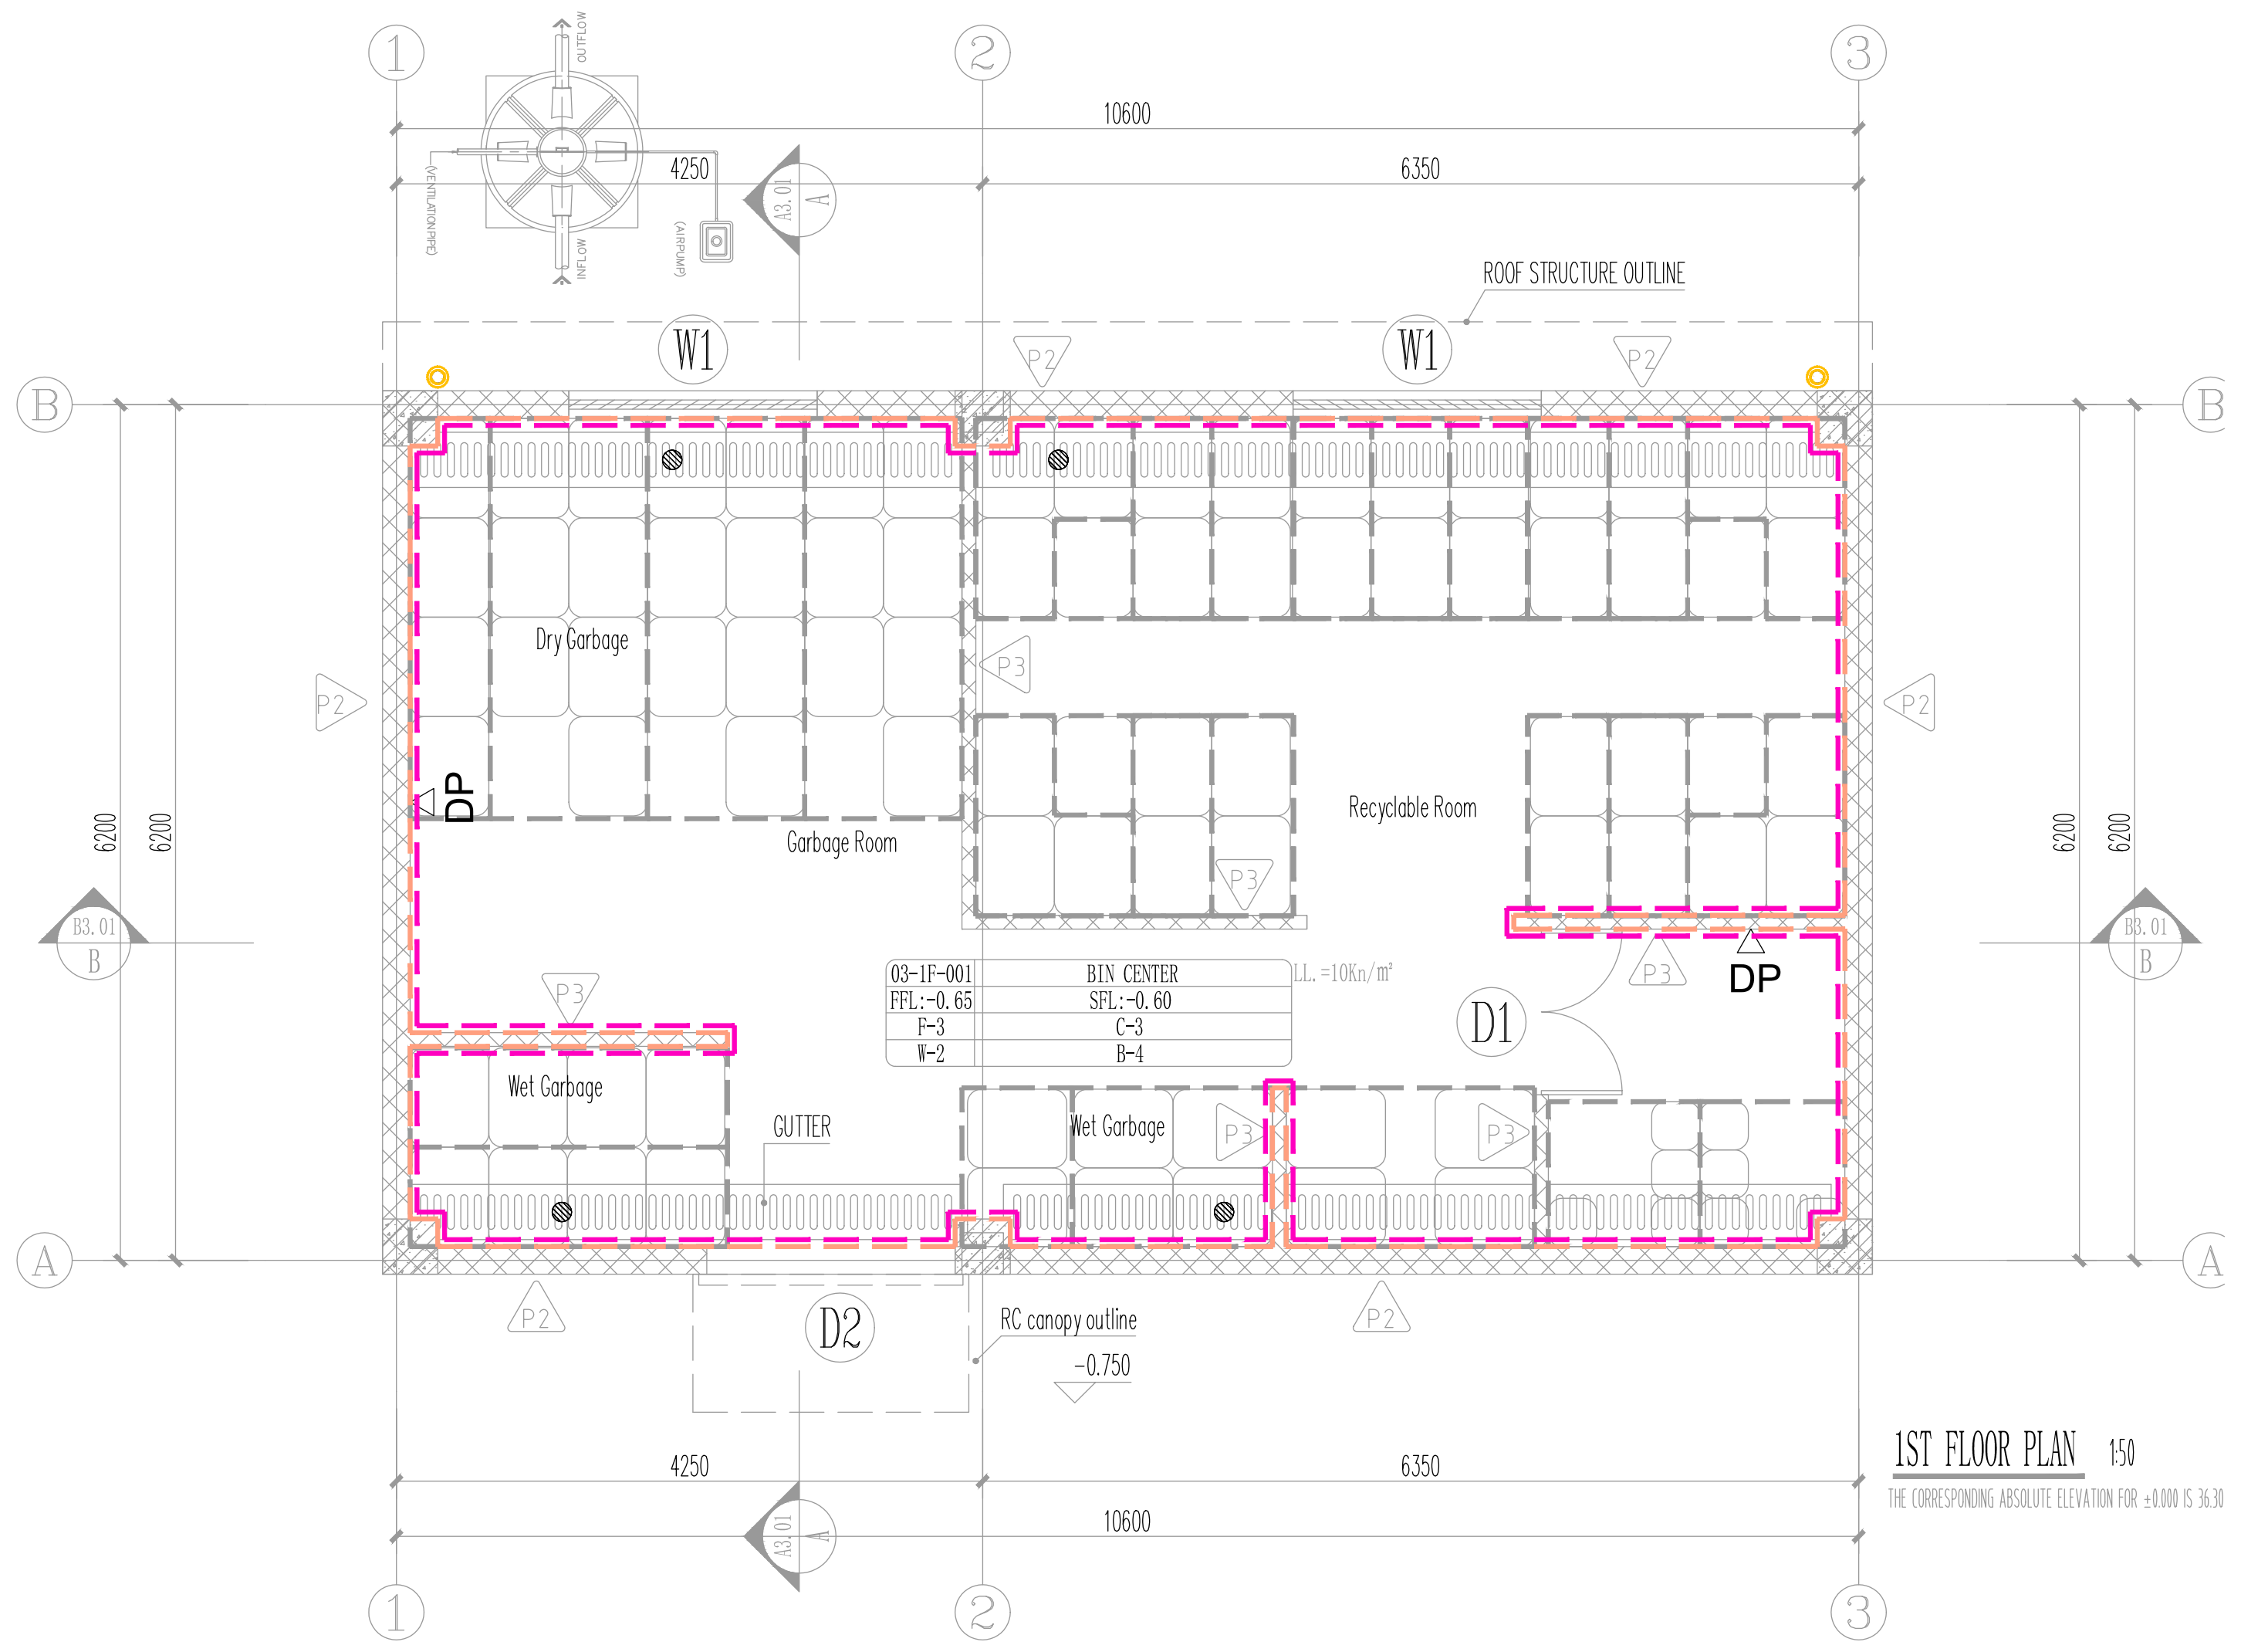

1ST FLOOR PLAN 1:50
THE CORRESPONDING ABSOLUTE ELEVATION FOR ±0.000 IS 36.30

LEGEND	Wall No.	Description	TILE SIZE(MM) WIDTH X DEPTH
‐ ‐ ‐	W-5	12mm Thk Waterproof Homogenous Tile	Waterproof(For wall height 1.5m and below)
‐ ‐ ‐	W-2	Skim Coat With Scrub Resistant Paint	Scratch-resistant(For wall height above 1.5m)

DOOR SCHEDULE

	DESCRIPTION	SISE(MM) WIDTH X HEIGHT
D1	G.I METAL FRAME DOOR TO MANUF'S DETAIL	1800 X 2400
W1	1.4mm THK.POWDER COATED ALUMN. FRAME FIXED DETACHABLE LOUVERS TO MANUF'S DETAIL;THE INNER SIDE OF THE SHUTTERS SHOULD BE EQUIPPED WITH INSECT AND RODENT PROOF WIRE MESH；EXTERNAL LOUVRES SHALL BE DOUBLE BANK RAINPROOFED TO PREVENT WATER INGRESS.	1800 X 1200

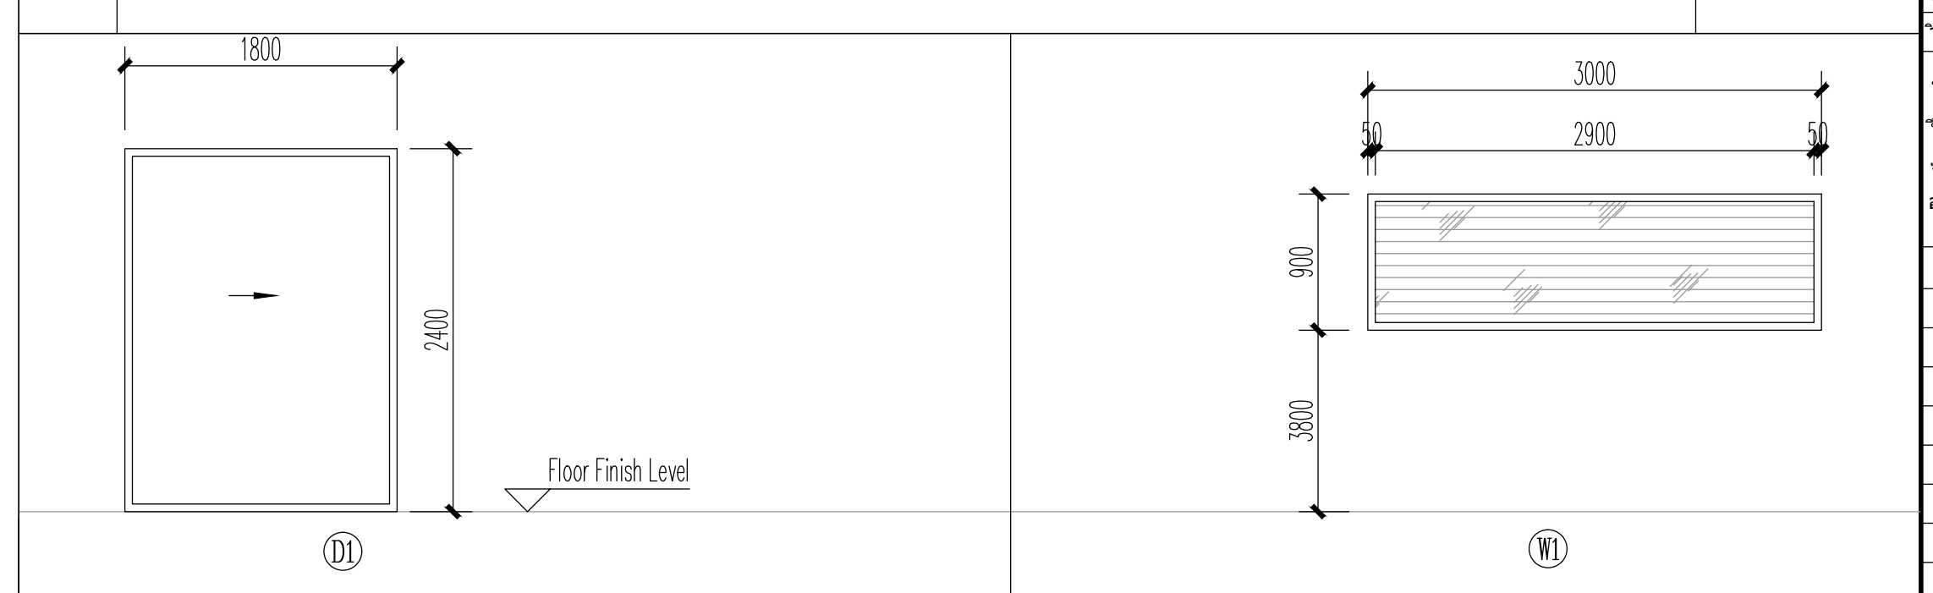

FUNCTON	BIN CENTER	FUNCTON	BIN CENTER
TYPE	G.I METAL FRAME SLIDING DOOR	TYPE	Aluminum Louvre Window
	SINGLE SWING	HARDWARE	
HARDWARE	DOOR STOPPER	Total	2
	HANDLE		
	KEY		
Total	1		

LEED: Remark for all door & window glazing
Exterior Glazing Performance:
SHGC=0.3 or better
U-value = 2.0 W/(m2K) or better'
Notes:
The specific specifications for doors, windows, and hardware will be provided during the IFC review stage.

CLIENT :

GULF EDGE DC 01

87 Wireless Road, M Thai Tower 11th. Floor, All Seasons Place, Lumpini,
Pathumwan, Bangkok 10330, Thailand

CONTRACTOR :

华西发展(泰国)有限公司
บริษัท หัวซือ ดีเวลลอปเม้นต์ (ประเทศไทย) จำกัด
HUASHI DEVELOPMENT CO.,LTD
No. 202, Room No. 1403, 14/F, Le Concorde Building,
Ratchadapisek Road, Huaykhwang Sub-District,
Huaykhwang District, Bangkok Metropolitan 10310.

CONSULTANT :

ARbay
บริษัท เอ อาร์ เบย์ จำกัด
ARbay Company Limited
31 st Floor Bangkok Insurance Building
25 South Sathorn road Thungmahamek
Sathorn Bangkok 10120 THAILAND
T +66 (0) 2286 8199
F +66 (0) 2286 2863
info@arbay.co.th

CONSULTANT :

Qbic Engineers & Architects Co.,Ltd.
8 Soi KALONG 4 SANAMBINNAM ROAD,
THASAI SUB-DISTRICT, MUANG NONTHABURI DISTRICT
, NONTHABURI.
Tel 662-950-4374
Fax 662-580-3231
E-Mail : qbic@qbic.co.th, www.qbic.co.th
QBIC ENGINEERS AND ARCHITECTS CO.,LTD.

CONSULTANT :

MITR
MITR TECHNICAL CONSULTANT CO.,LTD.
1168/8 12th FLOOR, LUMPINI TOWER BUILDING,
RAMA IV RD., THUNGMAHAMEK, SATHORN, BANGKOK 10120, THAILAND
TEL : 0-2679-9079-84
FAX : 0-2679-9085 E-mail: mitr_dd@mitr.com

Architect :	SIGNATURE
ประกิต พนานุรัตน์ วสถ. 580 ที่อยู่ 251/1 ถ.จารุเมือง แขวงรองเมือง เขตปทุมวัน กรุงเทพมหานคร โทรศัพท์ 02-286-8199	
Structural Engineer :	SIGNATURE
วิศวกรผู้ออกแบบโครงสร้าง	
ณัฐสม สงวนวงษ์ วย 1423 ที่อยู่ 2/1 ซ.รามคำแหง 150 ถ.รามคำแหง แขวง สะพานสูง เขต สะพานสูง กทม. 10240	ณัฐสม สงวนวงษ์
Structural Inspector :	SIGNATURE
วิศวกรผู้ตรวจสอบโครงสร้าง	
โกมล จุฑาภัทร วย 964 ที่อยู่ 24/18 ซ.นวมินทร์ 129 ถ. นวมินทร์ แขวง นวลจันทร์ เขต บึงกุ่ม กทม. 10230	
Electrical Engineer :	SIGNATURE
วิศวกรผู้ออกแบบระบบไฟฟ้ากำลัง	
นายสุภัทร บูรณวิทย์ วฟก.1265 ที่อยู่ 21 ซอยทานสัมฤทธิ์ 13 ตำบลท่าทราย อ.เมืองนนทบุรี จ.นนทบุรี 11000	สุภัทร
Mechanical Engineer :	SIGNATURE
วิศวกรผู้ออกแบบระบบเครื่องกลและปรับอากาศ	
นายประสิทธิ์ เกียวสุนทร วก.1221 ที่อยู่ 44/372 ซอยบางกระดี่ 35/1 แขวงแสมดำ เขตบางขุนเทียน กทม. 10150	ประสิทธิ์
Sanitary Engineer :	SIGNATURE
วิศวกรผู้ออกแบบระบบสุขาภิบาล และดับเพลิง	
นายทศวรรษ สนันฤทธิ์ วส. 215 ที่อยู่ บ้านเลขที่ 99/107 หมู่ที่ 3 ต.ศีรษะจรเข้น้อย อ.บางเสาธง จ.สมุทรปราการ 10540	ทศวรรษ

ISSUE/REVISION

REV.	DESCRIPTION	DATE
A	90% DEVELOPED	09/05/2026

PROJECT NAME :

GEDC 01

LOCATION:
Nikhom Phattana district, Rayong ,industrial estate,CPGC

BUILDING :

BIN CENTER

90% DEVELOPED

TITLE :

CEILING FINISHES & WATERPROOFING RAINWATER DOWN PIPE & DOOR & WINDOW & WALL FINISHES LAYOUT

JOB NO.	SCALE
DRAWN LK	REF.
CHECKED LJC	DWG.NO. MPK03-60-A-CL&WP&RWDP&DW&WF-101
APPROVED LXD	
DATE 2026.05.09	

NOTE : THIS PRINT IS OF A CONFIDENTIAL NATURE, IT SHALL NOT BE TRACED,PHOTOGRAPHED,PHOTOSTATED OR REPRODUCED IN ANY MANER,NOR USED FOR ANY PURPOSE WHATSOEVER EXCEPT BY WRITTEN PERMISSION