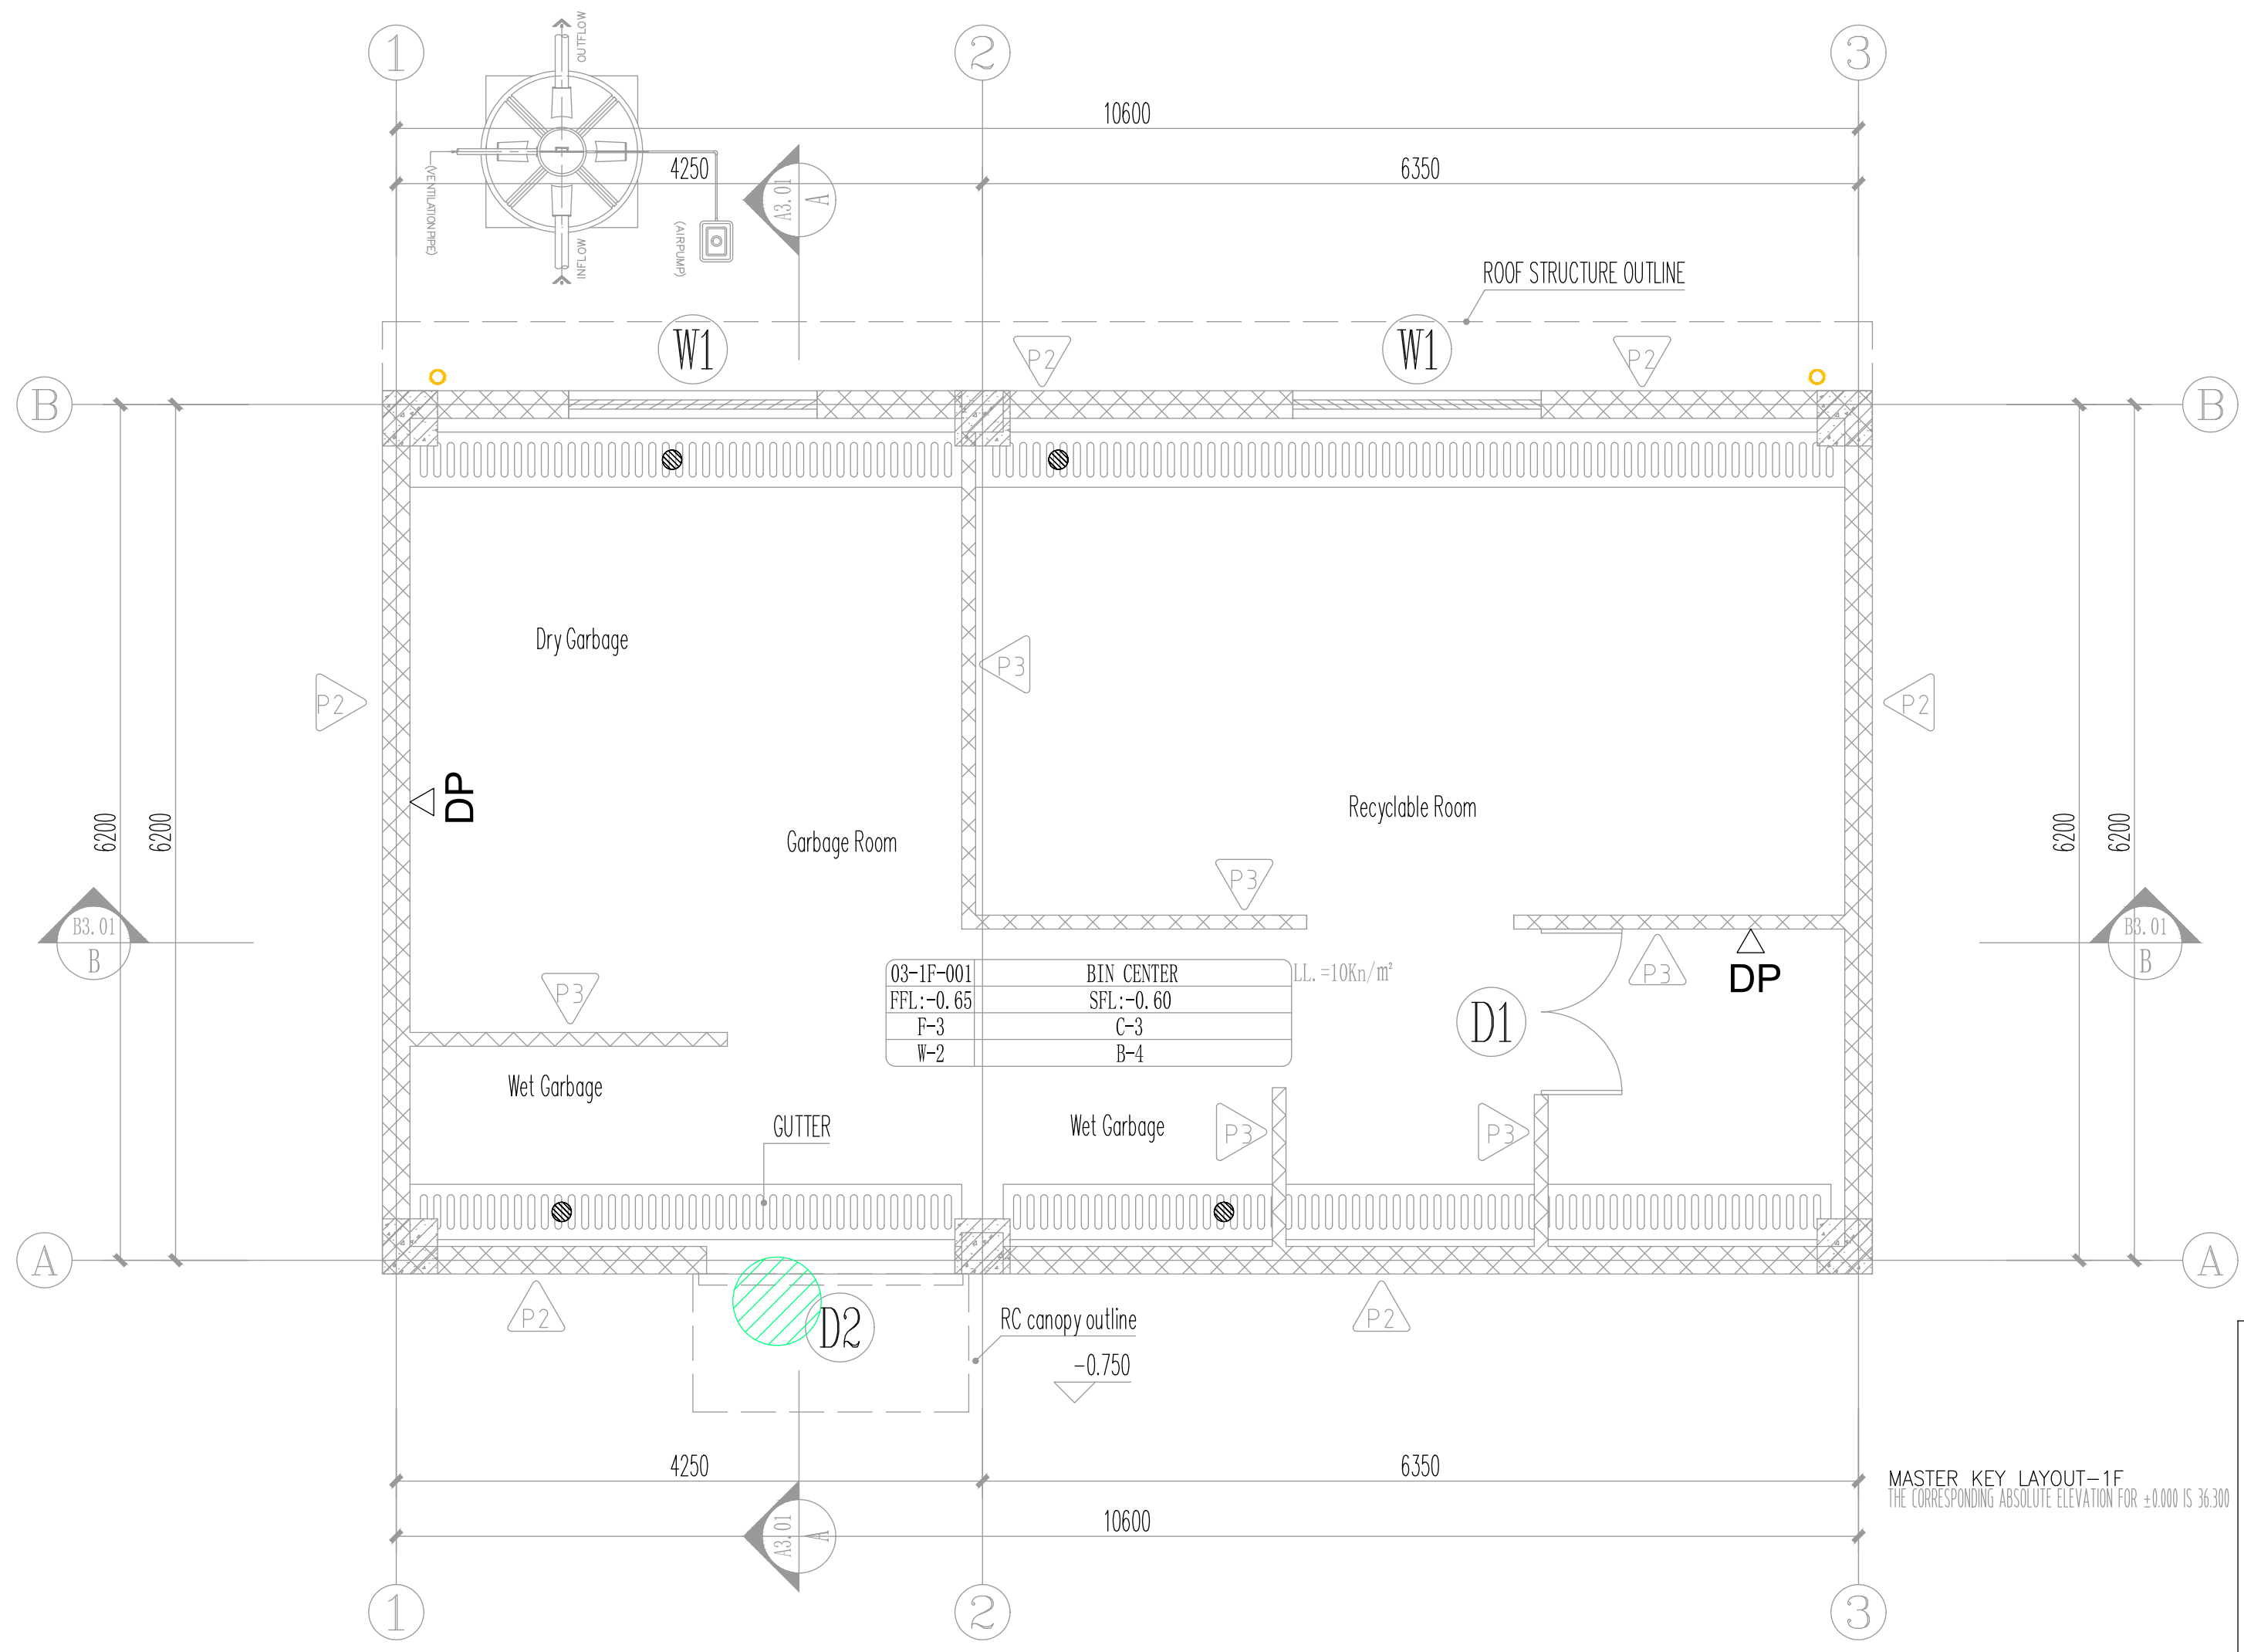

MASTER KEY LAYOUT-1F
THE CORRESPONDING ABSOLUTE ELEVATION FOR ±0.000 IS 36.300

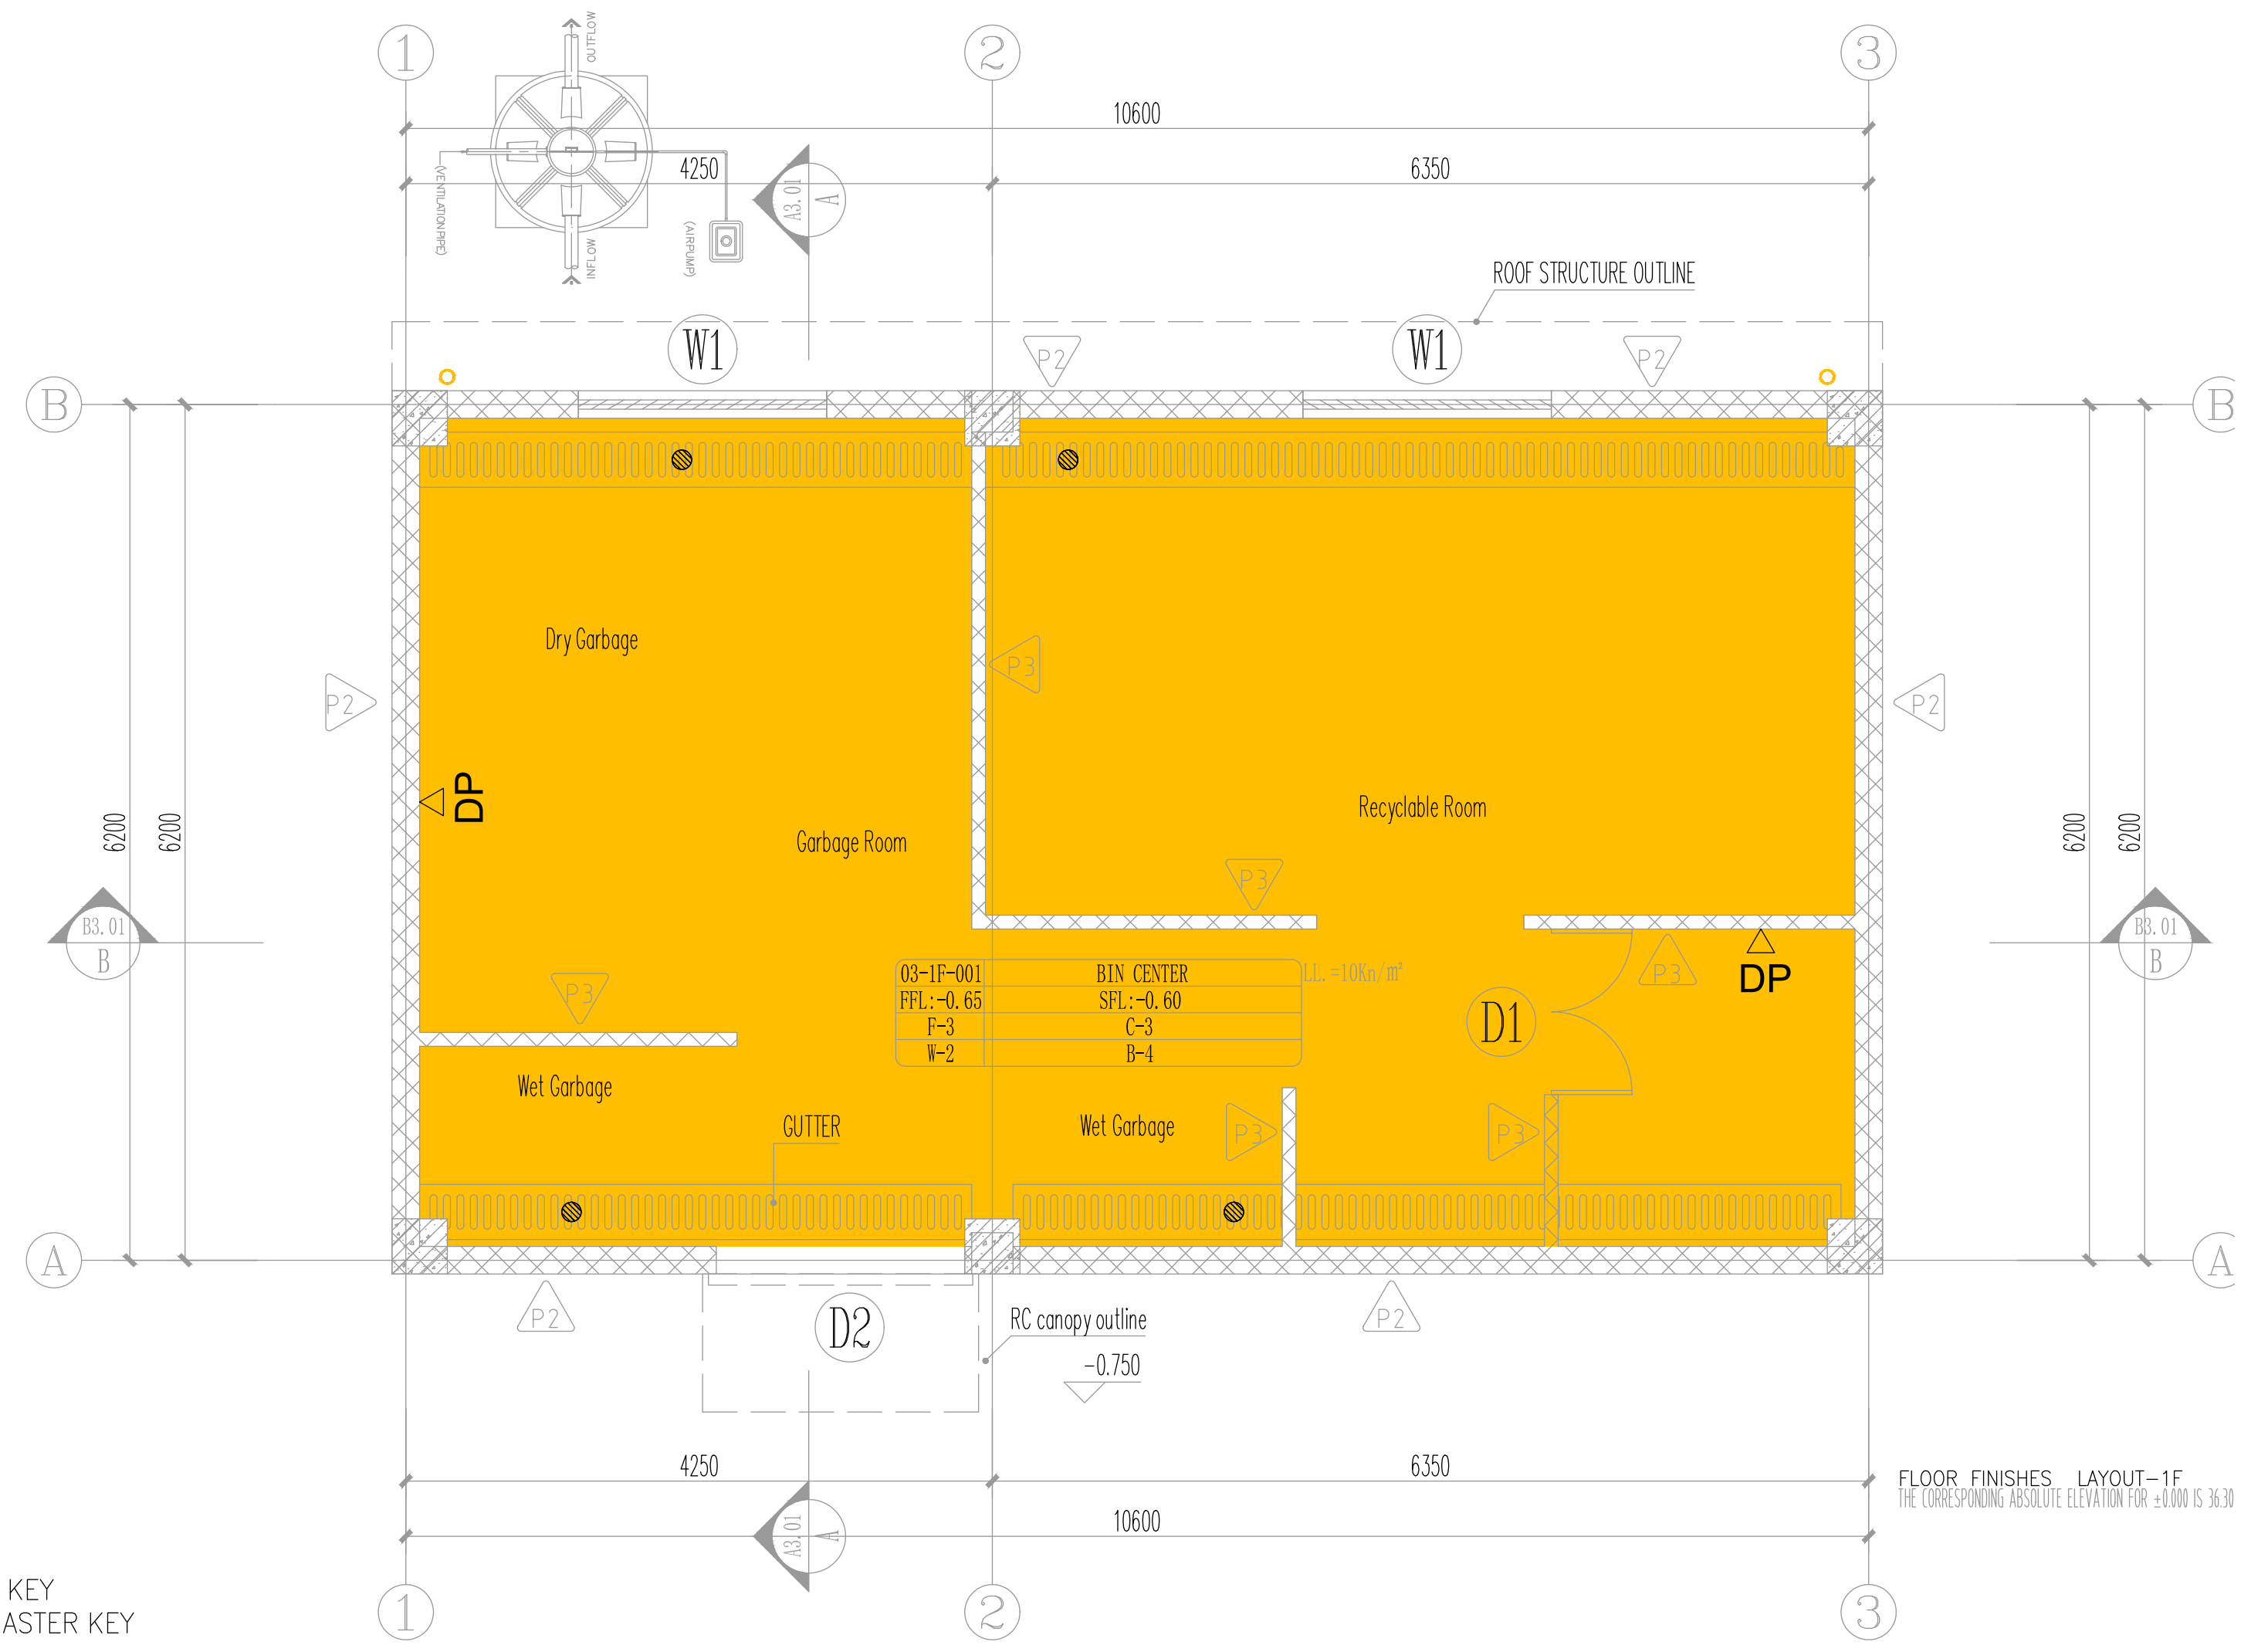

FLOOR FINISHES LAYOUT-1F
THE CORRESPONDING ABSOLUTE ELEVATION FOR ±0.000 IS 36.300

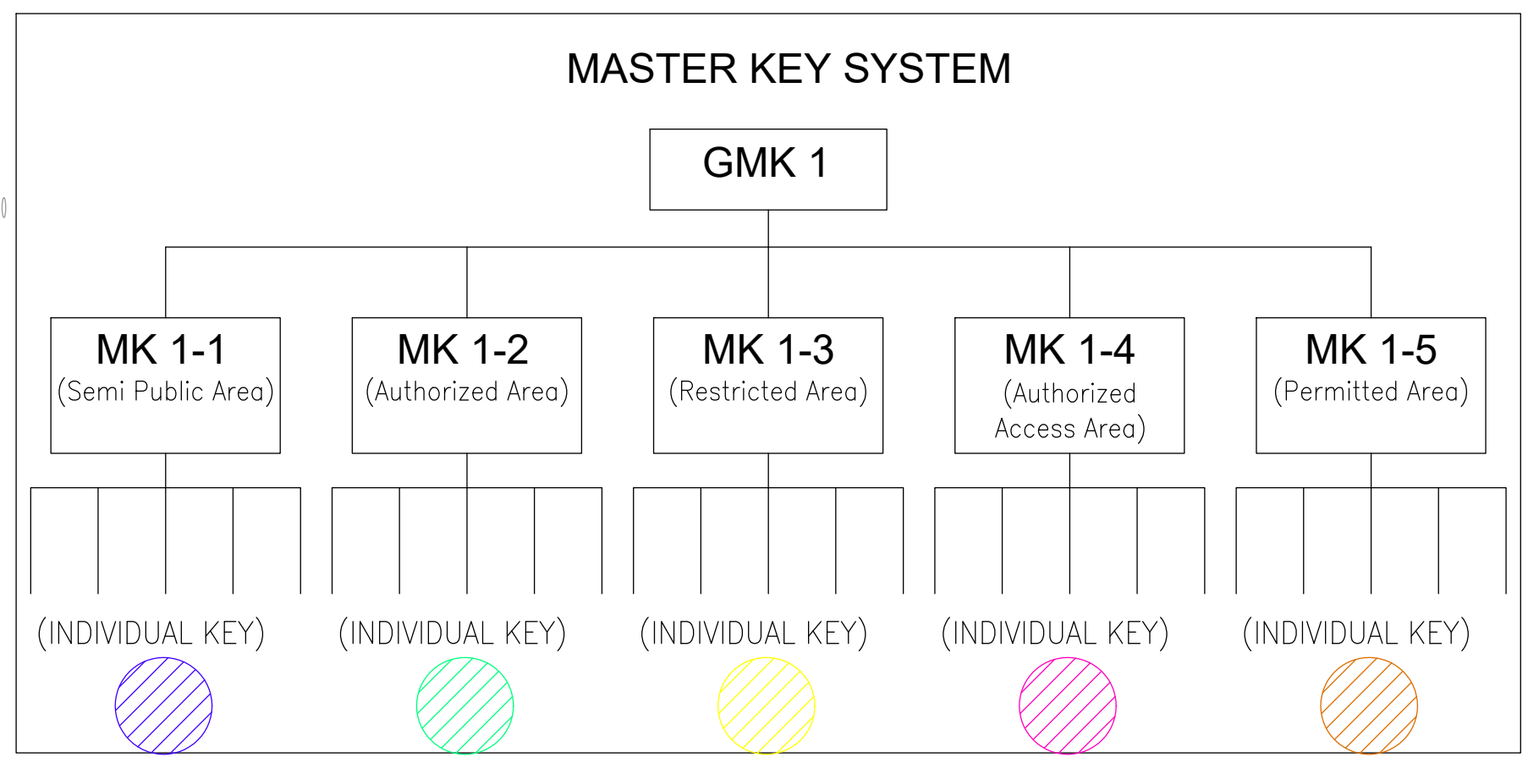

MASTER KEY SYSTEM

GMK 1

MK 1-1 (Semi Public Area)
MK 1-2 (Authorized Area)
MK 1-3 (Restricted Area)
MK 1-4 (Authorized Access Area)
MK 1-5 (Permitted Area)

(INDIVIDUAL KEY)
(INDIVIDUAL KEY)
(INDIVIDUAL KEY)
(INDIVIDUAL KEY)
(INDIVIDUAL KEY)

LEGEND:
GMK=GRAND MASTER KEY
MK1-0 ~ MK1-5= MASTER KEY
NOTE:
EACH DOOR HAS ITS OWN INDIVIDUAL MECHANICAL KEY; EACH SECURITY ZONE HAS A MASTER KEY WHICH CAN OPEN EVERY DOOR IN THAT ZONE.

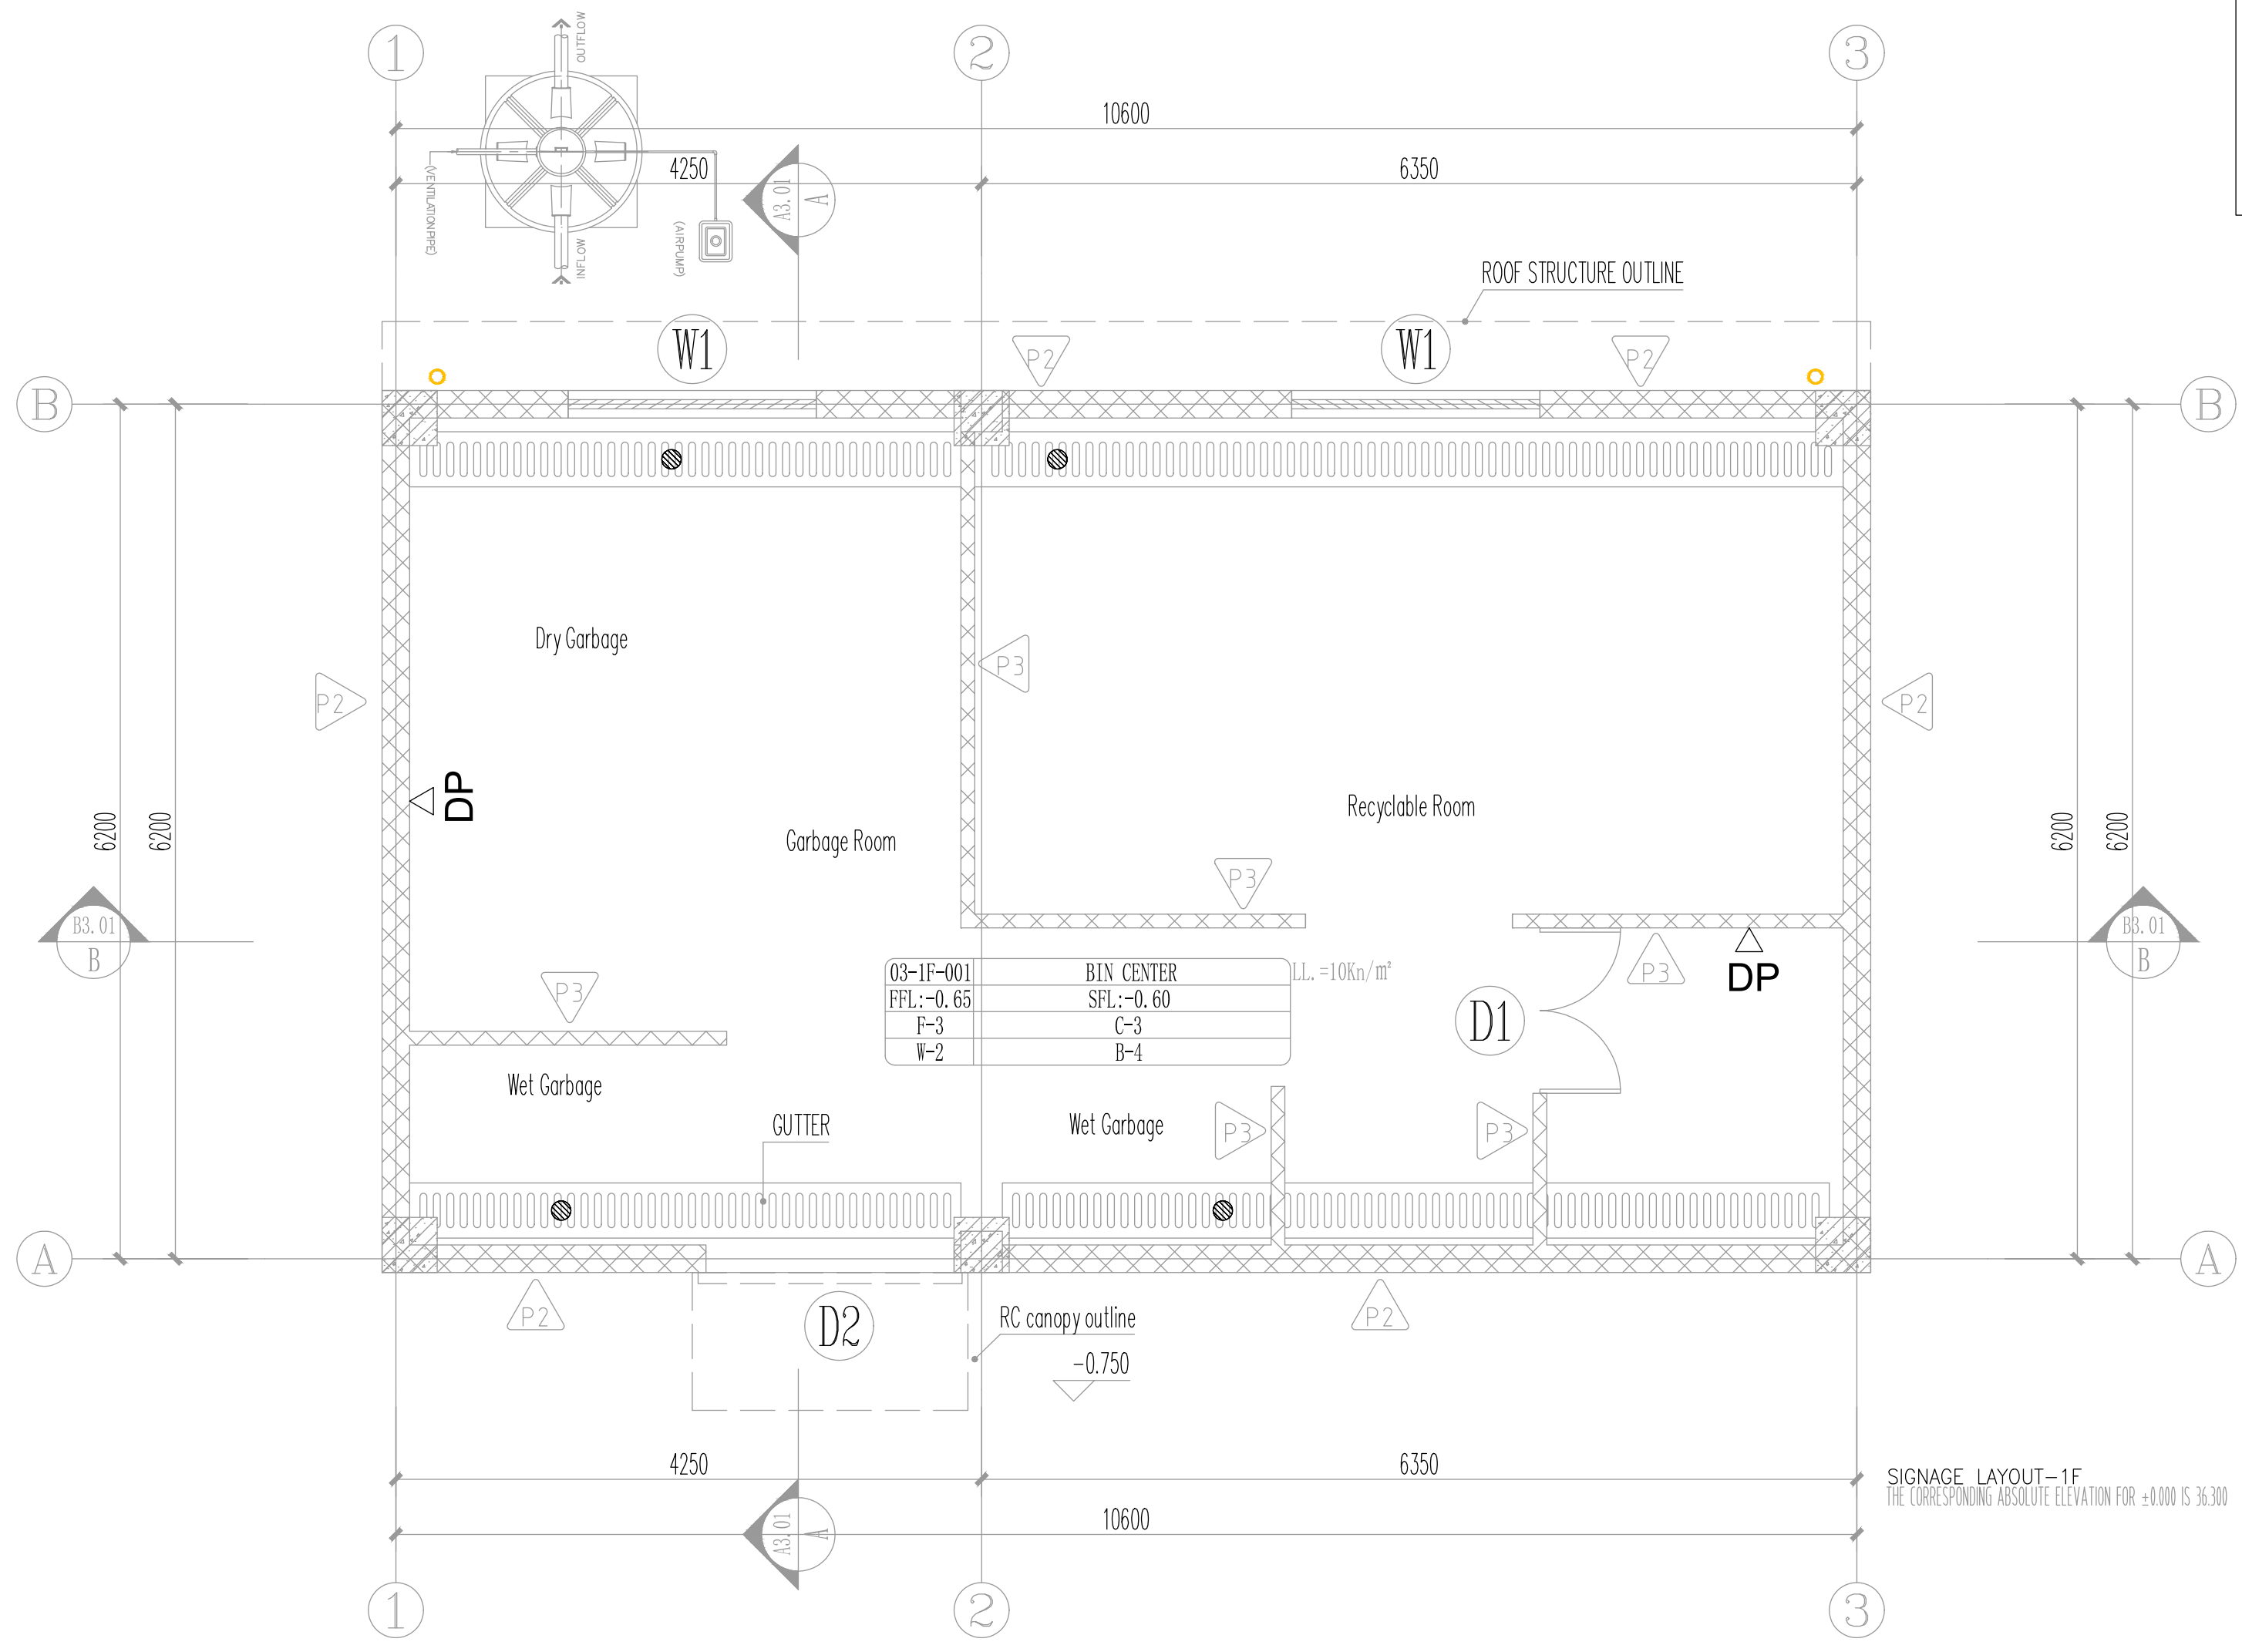

SIGNAGE LAYOUT-1F
THE CORRESPONDING ABSOLUTE ELEVATION FOR ±0.000 IS 36.300

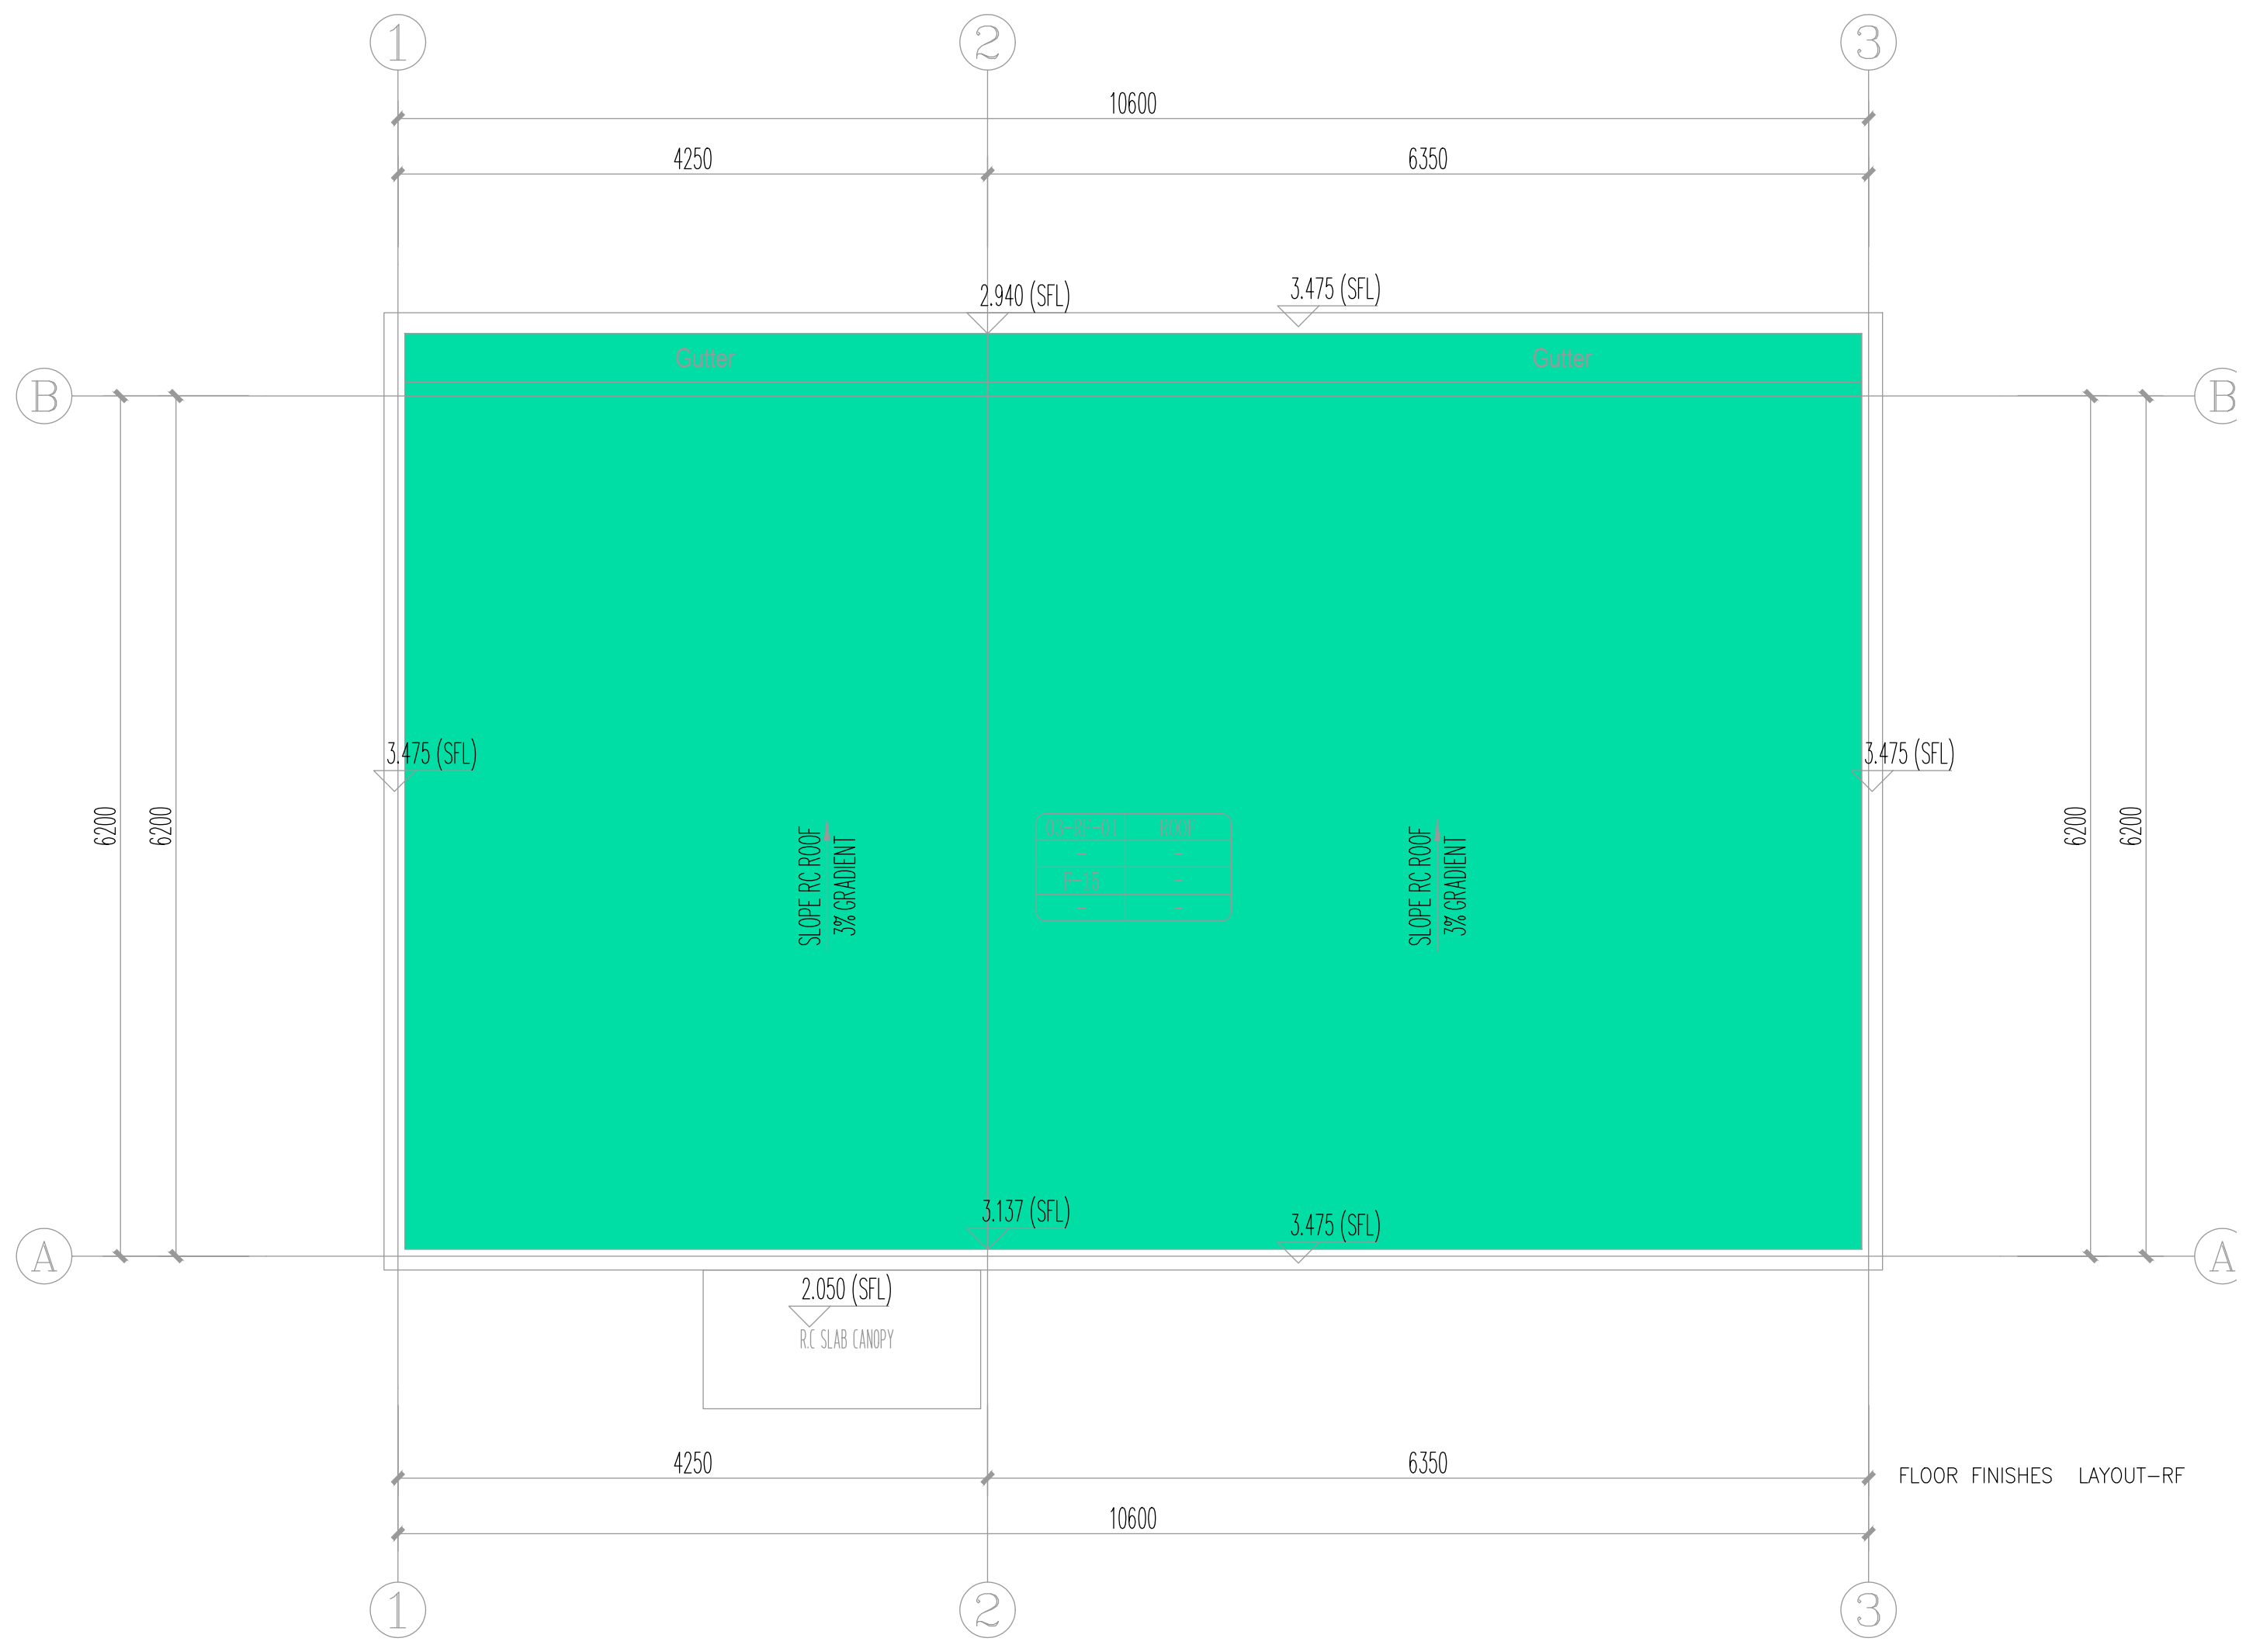

FLOOR FINISHES LAYOUT-RF

Legend	Floor No.	Description	Floor Finish Specification
🟧	F-3	Concrete Steel Trowel Finish	Concrete Screed + Curing Agent+ Waterproofing
🟩	F-15	Concrete Roof+ Waterproofing	Concrete Roof + Curing Agent+ Waterproofing

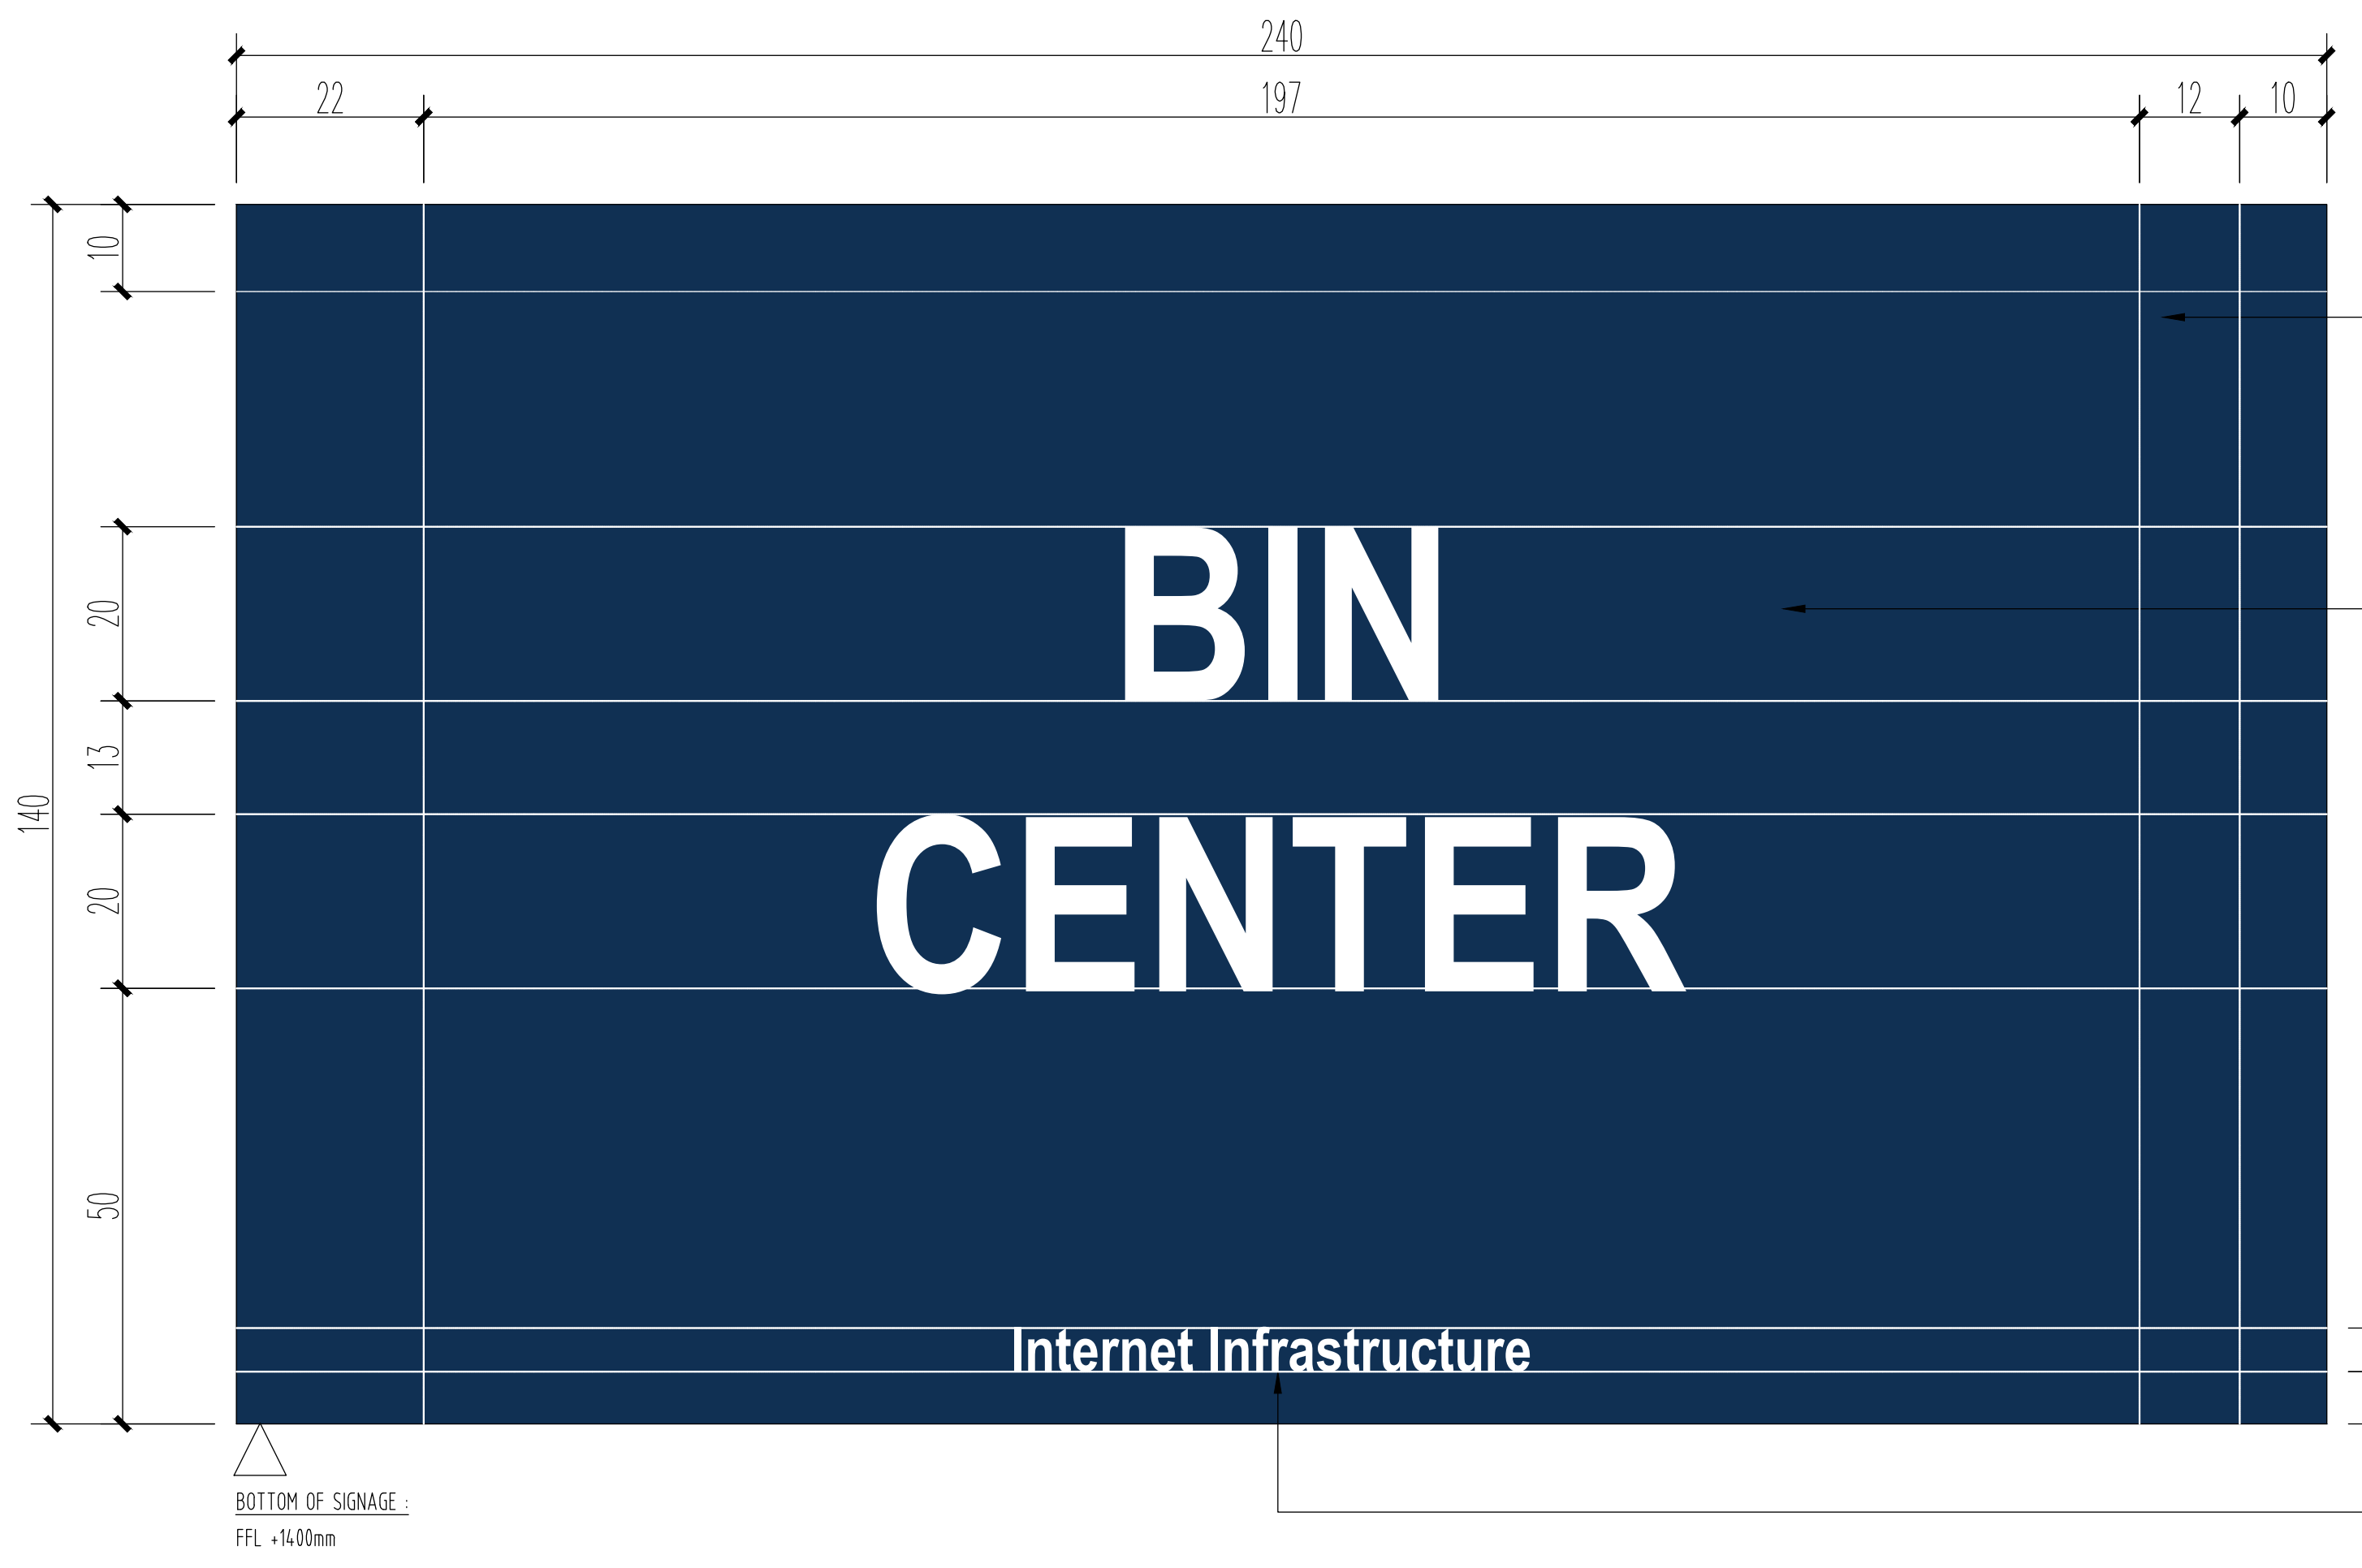

MATERIAL
3mm THK CLEAR ARCYLIC BOARD WITH DARK BLUE COLOUR AND TEXT STICKER AT BACK

ROOM NAME TEXT
FONT TYPE : MONTSERRAT
FONT SIZE : 20mm

ROOM NAME TEXT
FONT TYPE : MONTSERRAT (BOLD)
FONT SIZE : 6mm

LOCATION	SIGNAGE A		QUANTITY	MATERIAL
	ENGLISH	LOCATION CODE		
1ST FLOOR PLAN	BIN CENTER	-	1	3mmTRANSPARENTACRYLIC 140mmX 240mm withHIGH RES UVPRINT STICKERTO MATCHPANTONE NAVYBLUE

NOTE : THIS PRINT IS OF A CONFIDENTIAL NATURE, IT SHALL NOT BE TRACED,PHOTOGRAPHED,PHOTOSTATED OR REPRODUCED IN ANY MANER,NOR USED FOR ANY PURPOSE WHATSOEVER EXCEPT BY WRITTEN PERMISSION

CLIENT :
GULF EDGE DC 01
87 Wireless Road, M Thai Tower 11th. Floor, All Seasons Place, Lumpini,
Pathumwan, Bangkok 10330, Thailand

CONTRACTOR :
华西发展(泰国)有限公司
บริษัท หัวซือ ดีเวลลอปเม้นต์ (ประเทศไทย) จำกัด
HUASHI DEVELOPMENT CO.,LTD
No. 202, Room No. 1403, 14/F, Le Concorde Building,
Ratchadapisek Road, Huaykhwang Sub-District,
Huaykhwang District, Bangkok Metropolitan 10310.

CONSULTANT :
ARbay
บริษัท เอ อาร์ เบย์ จำกัด
ARbay Company Limited
31 st Floor Bangkok Insurance Building
25 South Sathorn road Thungmahamek
Sathorn Bangkok 10120 THAILAND
T +66 (0) 2286 8199
F +66 (0) 2286 2863
info@arbay.co.th

CONSULTANT :
Qbic Engineers & Architects Co.,Ltd.
8 Soi KALONG 4 SANAMBINNAM ROAD,
THASAI SUB-DISTRICT, MUANG NONTHABURI DISTRICT
, NONTHABURI.
Tel 662-950-4374
Fax 662-580-3231
E-Mail : qbic@qbic.co.th, www.qbic.co.th
QBIC ENGINEERS AND ARCHITECTS CO.,LTD.

CONSULTANT :
MITR
MITR TECHNICAL CONSULTANT CO.,LTD.
1168/8 12th FLOOR, LUMPINI TOWER BUILDING,
RAMA IV RD., THUNGMAHAMEK, SATHORN, BANGKOK 10120, THAILAND
TEL : 0-2679-9079-84
FAX : 0-2679-9085 E-mail: mitr_dd@mitr.com

Architect :	SIGNATURE
ประกิต พนานุรัตน์ วสถ. 580 ที่อยู่ 251/1 ถ.จารุเมือง แขวงรองเมือง เขตปทุมวัน กรุงเทพมหานคร โทรศัพท์ 02-286-8199	
Structural Engineer :	SIGNATURE
วิศวกรผู้ออกแบบโครงสร้าง	
ณัฐสม สงวนวงษ์ วย 1423 ที่อยู่ 2/1 ซ.รามคำแหง 150 ถ.รามคำแหง แขวง สะพานสูง เขต สะพานสูง กทม. 10240	ณัฐสม สงวนวงษ์
Structural Inspector :	SIGNATURE
วิศวกรผู้ตรวจสอบโครงสร้าง	
โกมล จุฑาภัทร วย 964 ที่อยู่ 24/18 ซ.นวมินทร์ 129 ถ. นวมินทร์ แขวง นวลจันทร์ เขต บึงกุ่ม กทม. 10230	
Electrical Engineer :	SIGNATURE
วิศวกรผู้ออกแบบระบบไฟฟ้ากำลัง	
นายสุภัทร บูรณวิทย์ วฟก.1265 ที่อยู่ 21 ซอยทานสัมฤทธิ์ 13 ตำบลท่าทราย อ.เมืองนนทบุรี จ.นนทบุรี 11000	
Mechanical Engineer :	SIGNATURE
วิศวกรผู้ออกแบบระบบเครื่องกลและปรับอากาศ	
นายประสิทธิ์ เกียวสุนทร วก.1221 ที่อยู่ 44/372 ซอยบางกระดี่ 35/1 แขวงแสมดำ เขตบางขุนเทียน กทม. 10150	ประสิทธิ์
Sanitary Engineer :	SIGNATURE
วิศวกรผู้ออกแบบระบบสุขาภิบาล และดับเพลิง	
นายทศวรรษ สนันฤทธิ์ วส. 215 ที่อยู่ บ้านเลขที่ 99/107 หมู่ที่ 3 ต.ศีรษะจรเข้น้อย อ.บางเสาธง จ.สมุทรปราการ 10540	ทศวรรษ

ISSUE/REVISION

REV.	DESCRIPTION	DATE
A	90% DEVELOPED	09/05/2026

PROJECT NAME :
GEDC 01

LOCATION:
Nikhom Phattana district, Rayong ,industrial estate,CPGC

BUILDING :
BIN CENTER

90% DEVELOPED

TITLE :
MASTER KEY & SIGNAGE &
FLOOR FINISHES LAYOUT

JOB NO.	SCALE 1:50
DRAWN LK	REF.
CHECKED LJC	DWG.NO. MPK03-60-A-MK&SN&FF-101
APPROVED LXD	
DATE 2026.05.09	