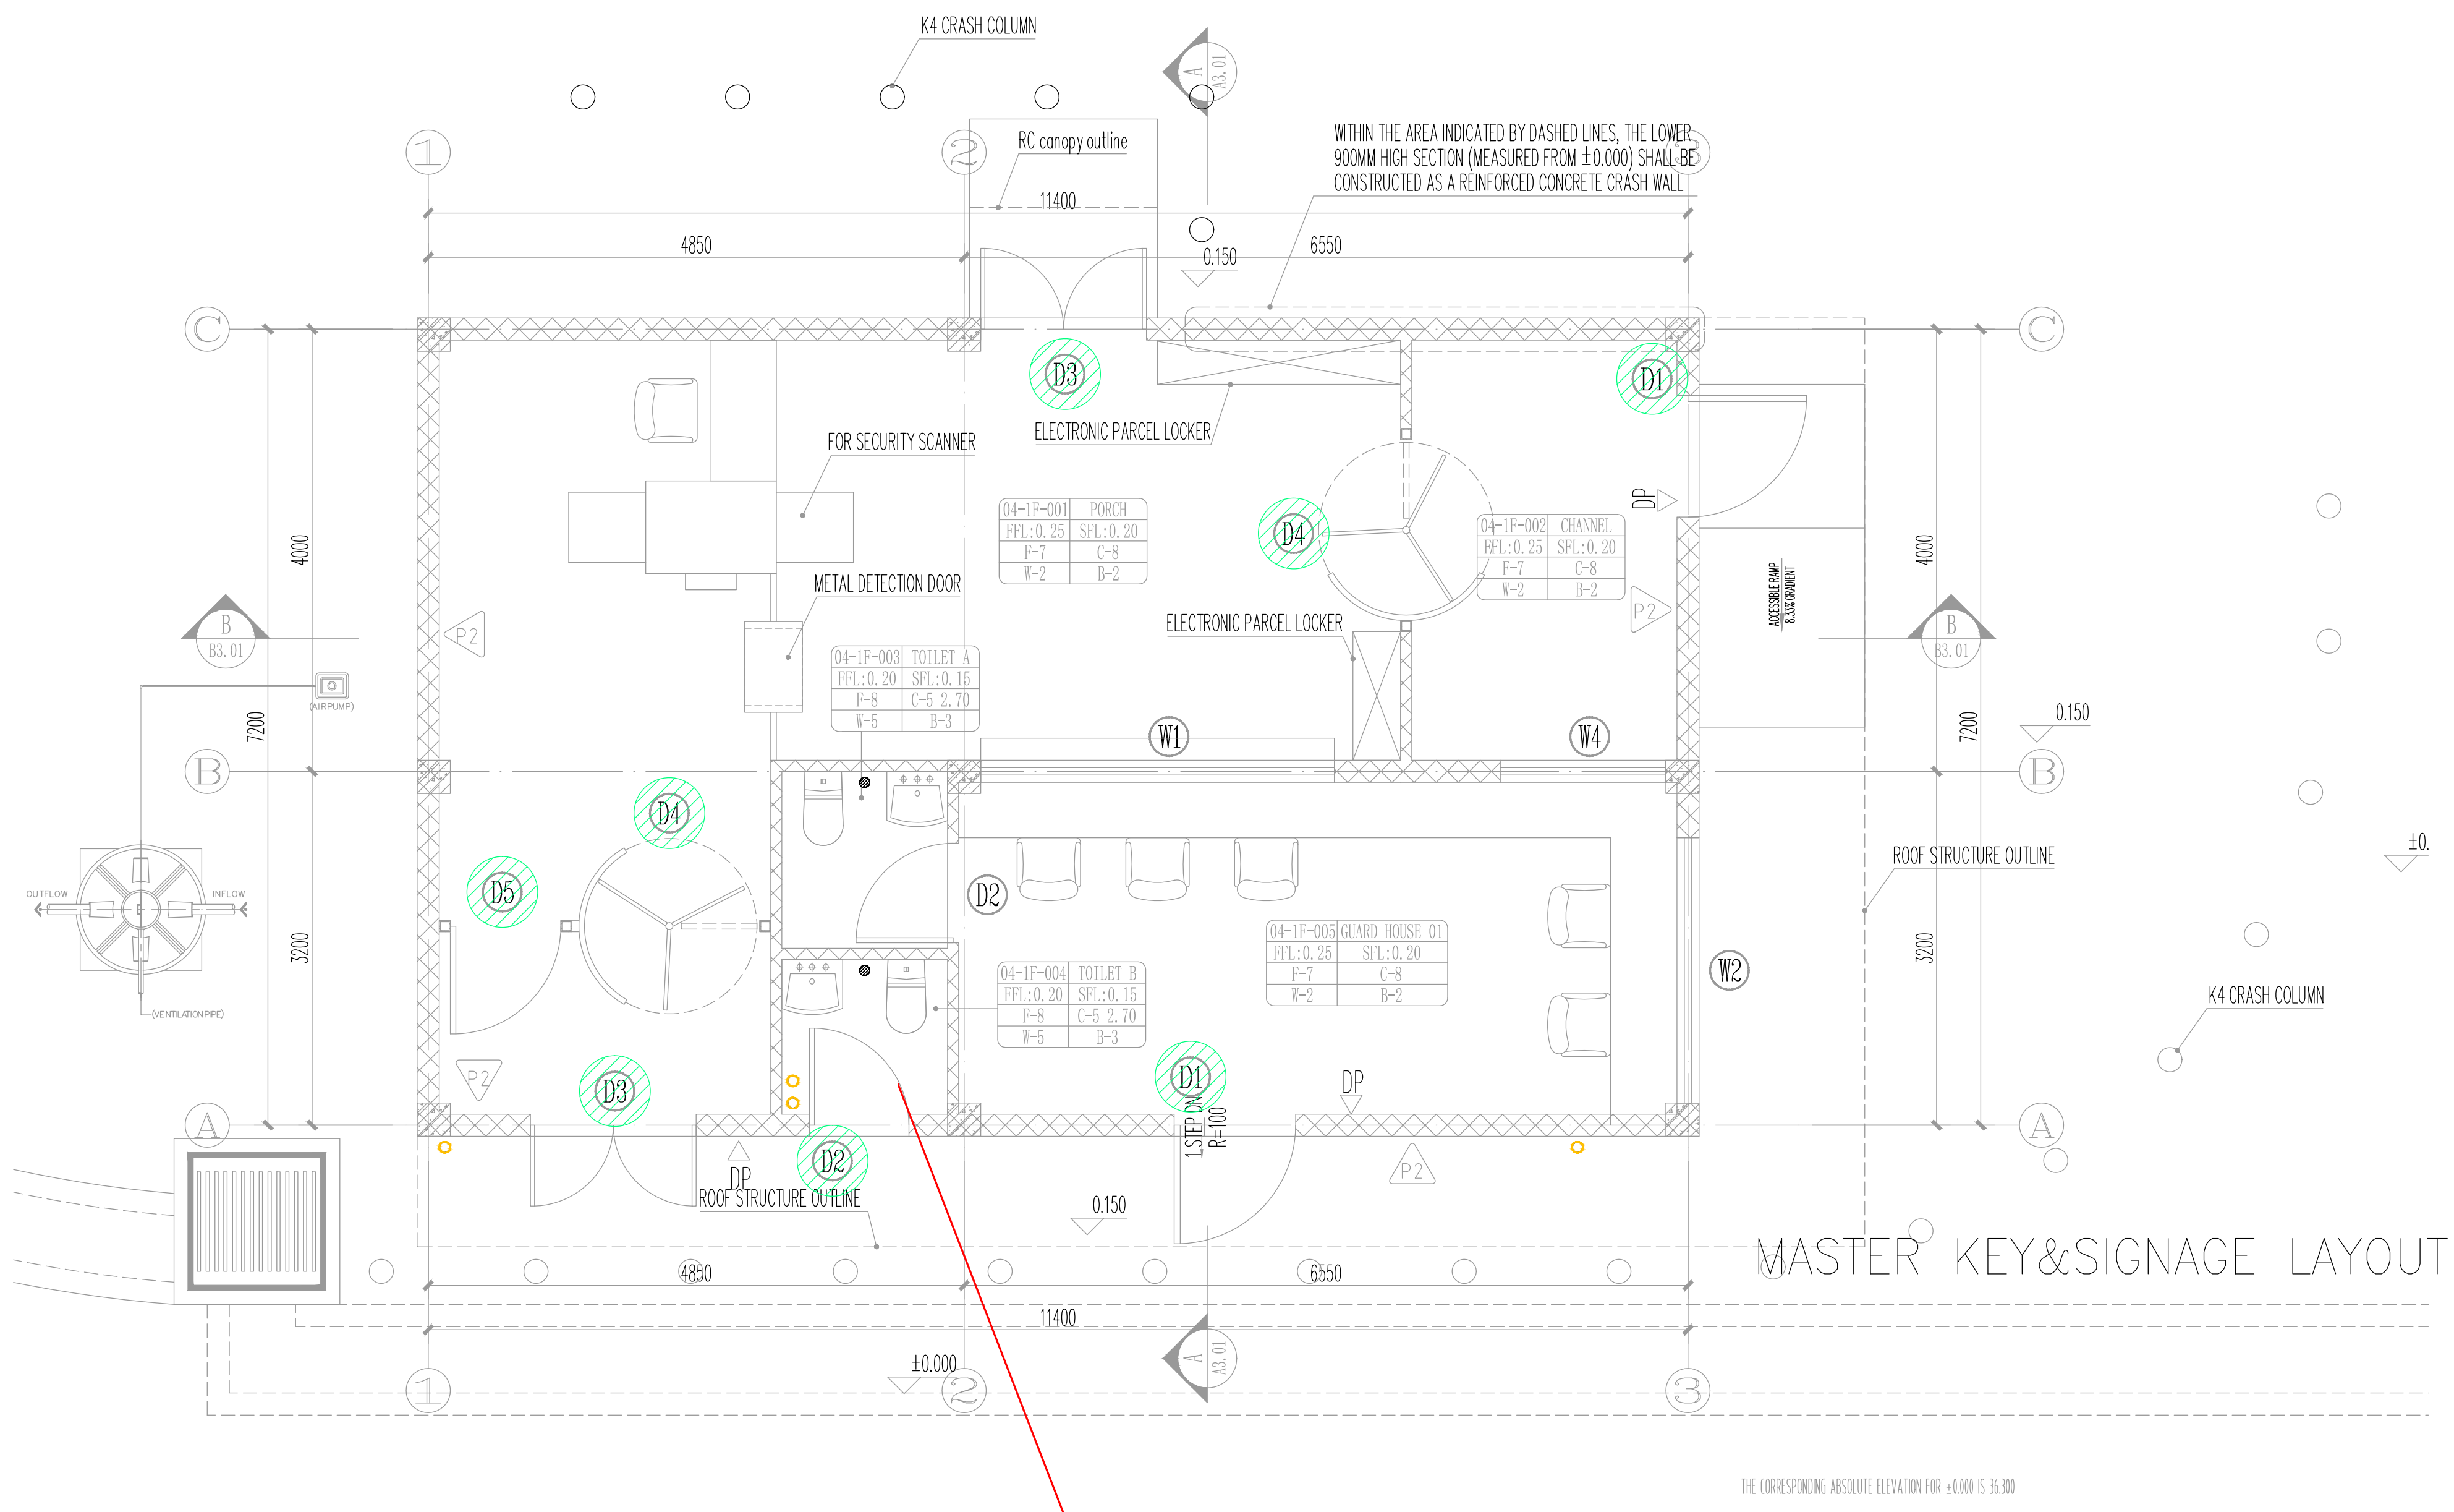
K4 CRASH COLUMN
RC canopy outline
WITHIN THE AREA INDICATED BY DASHED LINES, THE LOWER 900MM HIGH SECTION (MEASURED FROM ±0.000) SHALL BE CONSTRUCTED AS A REINFORCED CONCRETE CRASH WALL
11400
4850
6550
0.150
FOR SECURITY SCANNER
ELECTRONIC PARCEL LOCKER
METAL DETECTION DOOR
04-1F-001 PORCH FFL:0.25 SFL:0.20 F-7 C-8 W-2 B-2
04-1F-002 CHANNEL FFL:0.25 SFL:0.20 F-7 C-8 W-2 B-2
04-1F-003 TOILET A FFL:0.20 SFL:0.15 F-8 C-5 2.70 W-5 B-3
04-1F-004 TOILET B FFL:0.20 SFL:0.15 F-8 C-5 2.70 W-5 B-3
04-1F-005 GUARD HOUSE 01 FFL:0.25 SFL:0.20 F-7 C-8 W-2 B-2
D1
D2
D3
D4
D5
W1
W2
W4
P2
DP
4000
7200
3200
ROOF STRUCTURE OUTLINE
1.STEP DN R=100
ACCESSIBLE RAMP 8.33% GRADIENT
AIRPUMP
OUTFLOW
INFLOW
VENTILATION PIPE
±0.000
±0.
A3.01
B3.01
THE CORRESPONDING ABSOLUTE ELEVATION FOR ±0.000 IS 36.300

MASTER KEY&SIGNAGE LAYOUT–1F

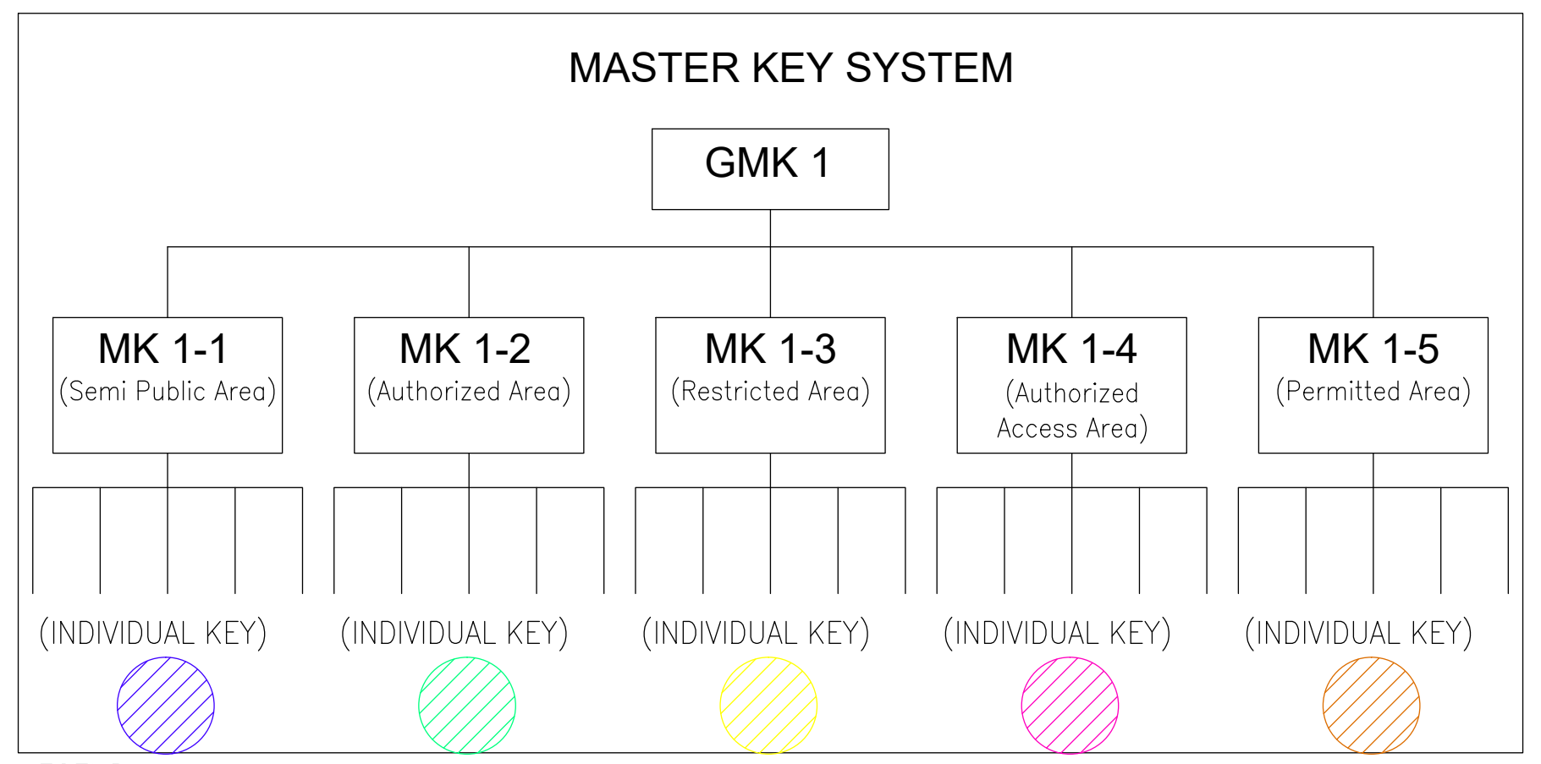
MASTER KEY SYSTEM
GMK 1
MK 1-1 (Semi Public Area)
MK 1-2 (Authorized Area)
MK 1-3 (Restricted Area)
MK 1-4 (Authorized Access Area)
MK 1-5 (Permitted Area)
(INDIVIDUAL KEY)
(INDIVIDUAL KEY)
(INDIVIDUAL KEY)
(INDIVIDUAL KEY)
(INDIVIDUAL KEY)

LEGEND:
GMK=GRAND MASTER KEY
MK1–0 ~ MK1–5= MASTER KEY
NOTE:
EACH DOOR HAS ITS OWN INDIVIDUAL MECHANICAL KEY; EACH SECURITY ZONE HAS A MASTER KEY WHICH CAN OPEN EVERY DOOR IN THAT ZONE.

Modified according to the review comments (ACM_GSA03_DesignReview_SD60_Rev B - Arch)

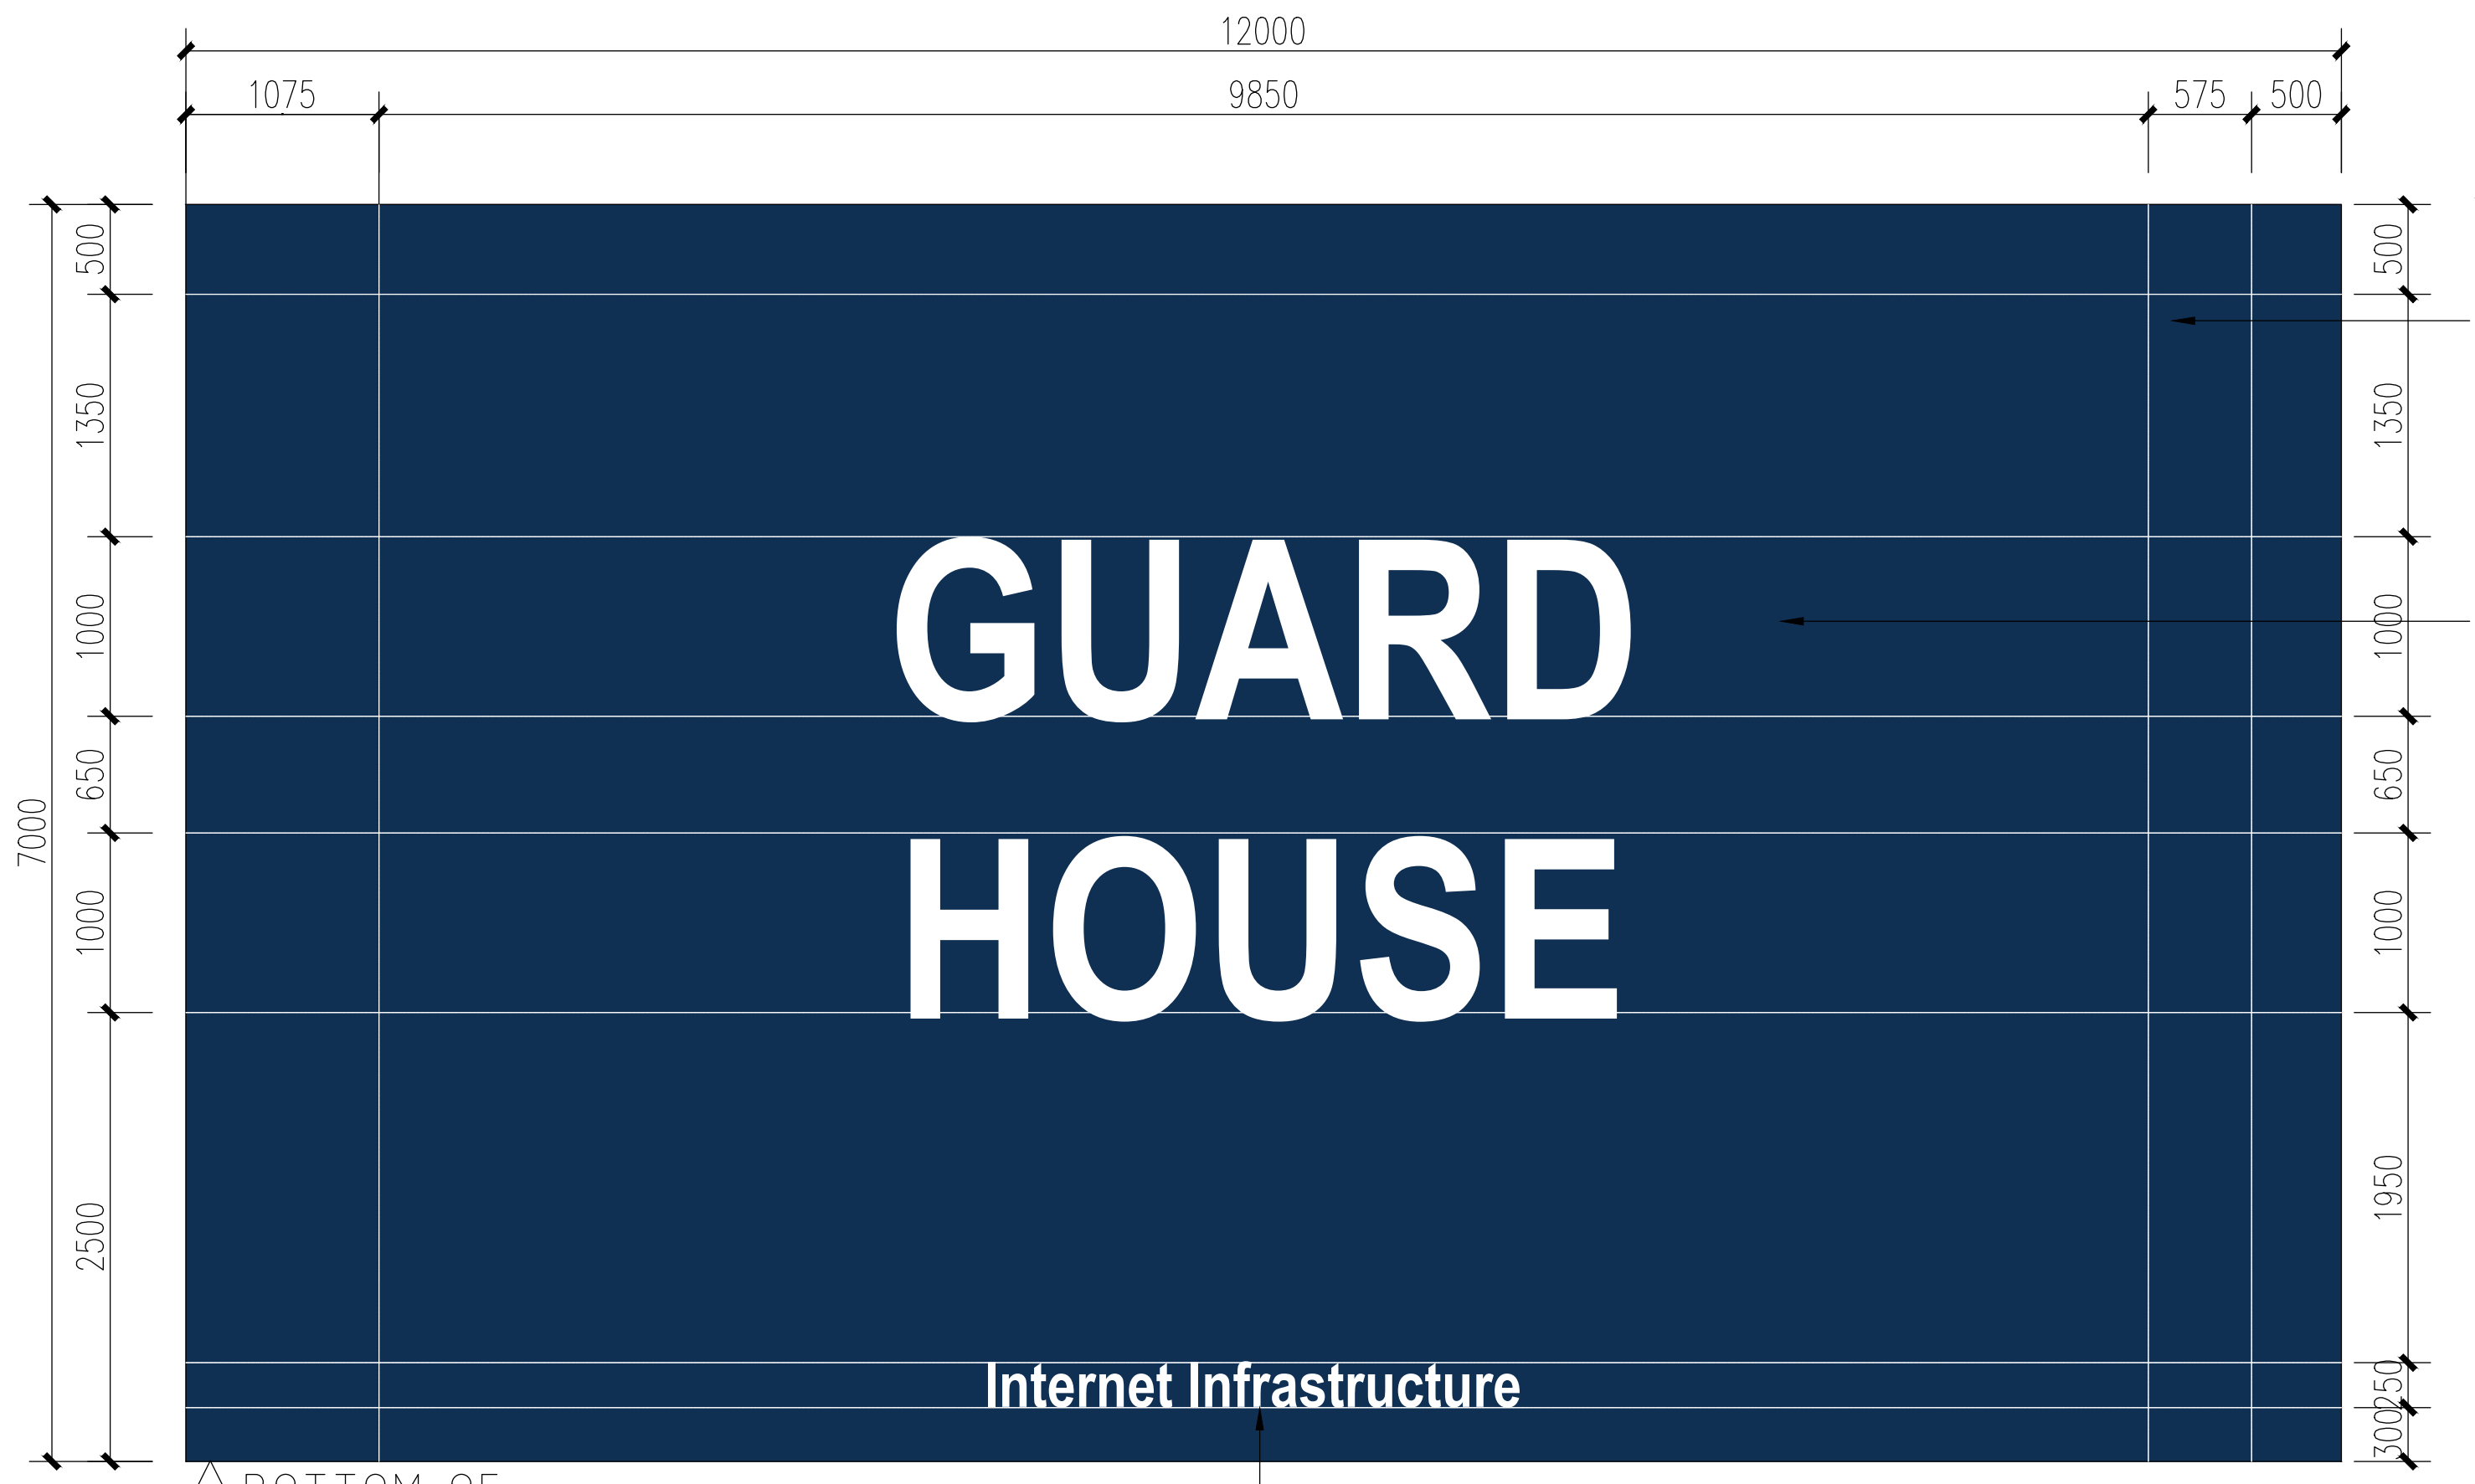
12000
1075
9850
575
500
7000
500
1350
1000
650
1000
2500
1950
250
300
GUARD HOUSE
Internet Infrastructure

MATERIAL
3mm THK CLEAR ARCYLIC BOARD WITH DARK BLUE COLOUR AND TEXT STICKER AT BACK

ROOM NAME TEXT
FONT TYPE : MONTSERRAT
FONT SIZE : 20mm

ROOM NAME TEXT
FONT TYPE : MONTSERRAT (BOLD)
FONT SIZE : 6mm

BOTTOM OF SIGNAGE :
FFL +1400mm

LOCATION	SIGNAGE A		QUANTITY	MATERIAL
	ENGLISH	MALAY		
GROUND FLOOR	GUARD HOUSE	-	1	3mm TRANSPARENT ACRYLIC 140mm X 240mm with HIGH RES UV PRINT STICKER TO MATCH PANTONE NAVY BLUE

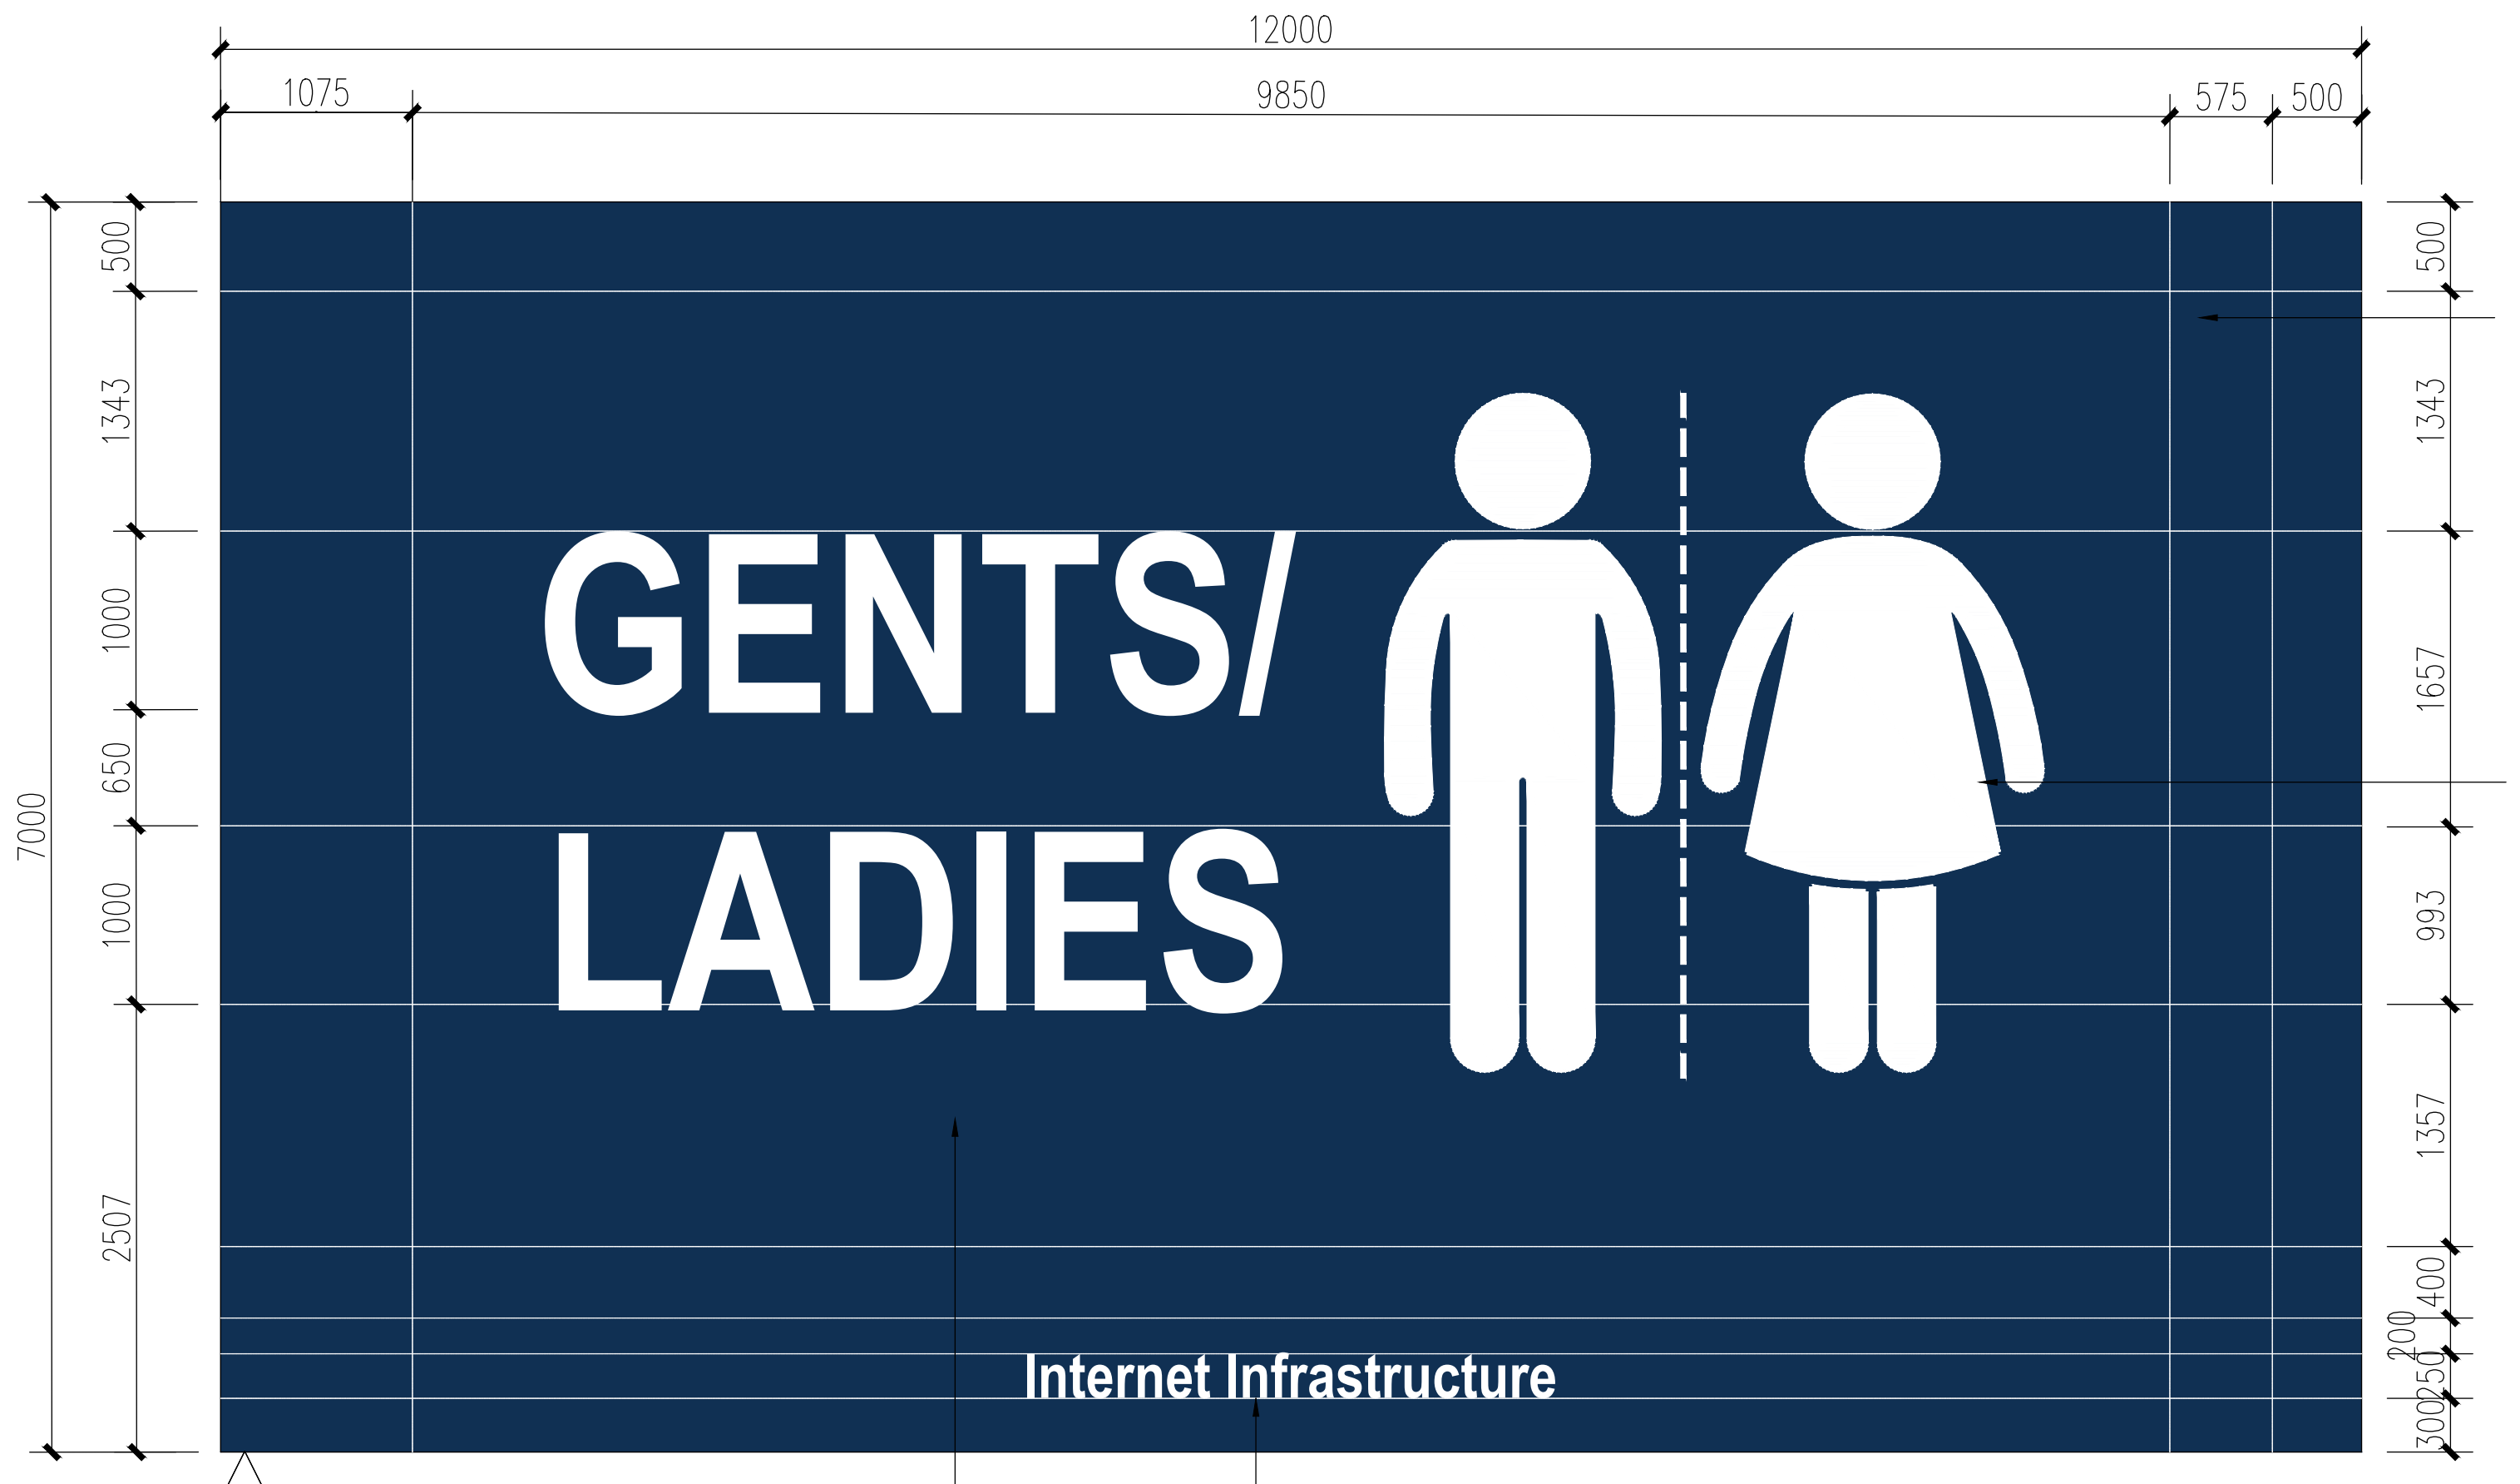
12000
1075
9850
575
500
7000
500
1343
1000
650
1000
2507
1657
993
1357
400
200
250
300
GENTS/ LADIES
Internet Infrastructure

MATERIAL
3mm THK CLEAR ARCYLIC BOARD WITH DARK BLUE COLOUR AND TEXT STICKER AT BACK
OBJECT TO BE REVERSED STICKER WITH WHITE COLOUR TO ARCH'S APPROVAL

ROOM NAME TEXT
FONT TYPE : MONTSERRAT (BOLD)
FONT SIZE : 5mm

ROOM NAME TEXT
FONT TYPE : MONTSERRAT
FONT SIZE :20mm

BOTTOM OF SIGNAGE :
FFL +1400mm

LOCATION	SIGNAGE A		QUANTITY	MATERIAL
	ENGLISH	MALAY		
GROUND FLOOR	TOILET	-	1	3mm TRANSPARENT ACRYLIC 140mm X 240mm with HIGH RES UV PRINT STICKER TO MATCH PANTONE NAVY BLUE

CLIENT :
GULF EDGE DC 01
87 Wireless Road, M Thai Tower 11th. Floor, All Seasons Place, Lumpini,
Pathumwan, Bangkok 10330, Thailand

CONTRACTOR :
华西发展(泰国)有限公司
บริษัท หัวซือ ดีเวลลอปเม้นต์ (ประเทศไทย) จำกัด
HUASHI DEVELOPMENT CO.,LTD
No. 202, Room No. 1403, 14/F, Le Concorde Building,
Ratchadapisek Road, Huaykhwang Sub–District,
Huaykhwang District, Bangkok Metropolitan 10310.

CONSULTANT :
ARbay
บริษัท เอ อาร์ เบย์ จำกัด
ARbay Company Limited
31 st Floor Bangkok Insurance Building
25 South Sathorn road Thungmahamek
Sathorn Bangkok 10120 THAILAND
T +66 (0) 2286 8199
F +66 (0) 2286 2863
info@arbay.co.th

CONSULTANT :
Qbic Engineers & Architects Co.,Ltd.
8 Soi KALONG 4 SANAMBINNAM ROAD,
THASAI SUB–DISTRICT, MUANG NONTHABURI DISTRICT
, NONTHABURI.
Tel 662–950–4374
Fax 662–580–3231
E–Mail : qbic@qbic.co.th, www.qbic.co.th
QBIC ENGINEERS AND ARCHITECTS CO.,LTD.

CONSULTANT :
MITR
MITR TECHNICAL CONSULTANT CO.,LTD.
1168/8 12th FLOOR, LUMPINI TOWER BUILDING,
RAMA IV RD., THUNGMAHAMEK, SATHORN, BANGKOK 10120, THAILAND
TEL : 0–2679–9079–84
FAX : 0–2679–9085 E–mail: mitr_dd@mitr.com

Architect :	SIGNATURE
ประกิต พนานุรัตน์ วสถ. 580 ที่อยู่ 251/1 ถ.จารุเมือง แขวงรองเมือง เขตปทุมวัน กรุงเทพมหานคร โทรศัพท์ 02-286-8199	
Structural Engineer :	SIGNATURE
วิศวกรผู้ออกแบบโครงสร้าง	
ณัฐสม สงวนวงษ์ วย 1423 ที่อยู่ 2/1 ซ.รามคำแหง 150 ถ.รามคำแหง แขวง สะพานสูง เขต สะพานสูง กทม. 10240	
Structural Inspector :	SIGNATURE
วิศวกรผู้ตรวจสอบโครงสร้าง	
โกมล จุฑาภัทร วย 964 ที่อยู่ 24/18 ซ.นวมินทร์ 129 ถ. นวมินทร์ แขวง นวลจันทร์ เขต บึงกุ่ม กทม. 10230	
Electrical Engineer :	SIGNATURE
วิศวกรผู้ออกแบบระบบไฟฟ้ากำลัง	
นายสุภัทร บูรณวิทย์ วฟก.1265 ที่อยู่ 21 ซอยทานสัมฤทธิ์ 13 ตำบลท่าทราย อ.เมืองนนทบุรี จ.นนทบุรี 11000	
Mechanical Engineer :	SIGNATURE
วิศวกรผู้ออกแบบระบบเครื่องกลและปรับอากาศ	
นายประสิทธิ์ เกียวสุนทร วก.1221 ที่อยู่ 44/372 ซอยบางกระดี่ 35/1 แขวงแสมดำ เขตบางขุนเทียน กทม. 10150	ประสิทธิ์
Sanitary Engineer :	SIGNATURE
วิศวกรผู้ออกแบบระบบสุขาภิบาล และดับเพลิง	
นายทศวรรษ สันนฤทธิ์ วส. 215 ที่อยู่ บ้านเลขที่ 99/107 หมู่ที่ 3 ต.ศีรษะจรเข้น้อย อ.บางเสาธง จ.สมุทรปราการ 10540	ทศวรรษ

ISSUE/REVISION

REV.	DESCRIPTION	DATE
A	90% DEVELOPED	09/05/2026

PROJECT NAME :
GEDC 01
LOCATION:
Nikhom Phattana district, Rayong ,industrial estate,CPGC

BUILDING :
GUARD HOUSE A

90% DEVELOPED

TITLE :
MASTER KEY & SIGNAGE LAYOUT

JOB NO.	SCALE 1:50
DRAWN LK	REF.
CHECKED LJC	DWG.NO. MPK04–60–A–MS&SN–101
APPROVED LXD	
DATE 2026.05.09	

NOTE : THIS PRINT IS OF A CONFIDENTIAL NATURE, IT SHALL NOT BE TRACED,PHOTOGRAPHED,PHOTOSTATED OR REPRODUCED IN ANY MANER,NOR USED FOR ANY PURPOSE WHATSOEVER EXCEPT BY WRITTEN PERMISSION