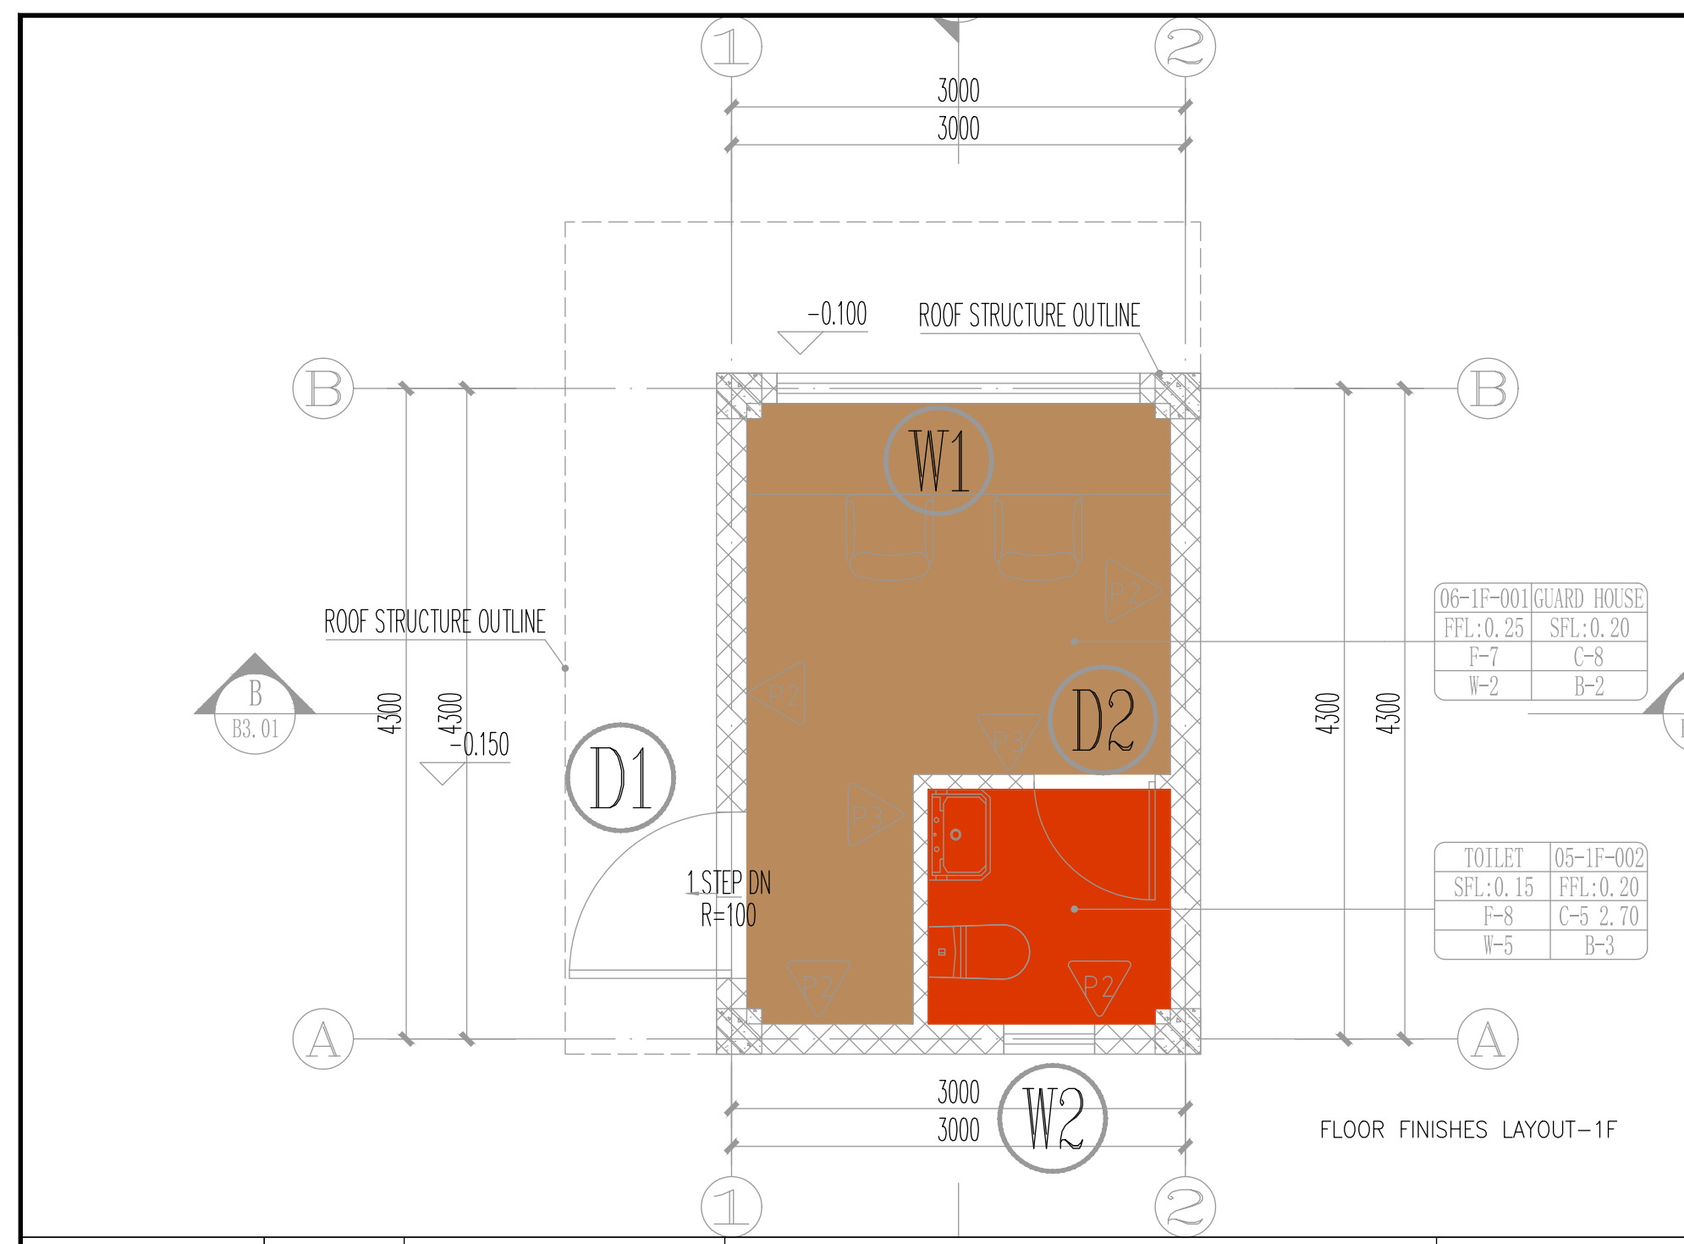

FLOOR FINISHES LAYOUT-1F

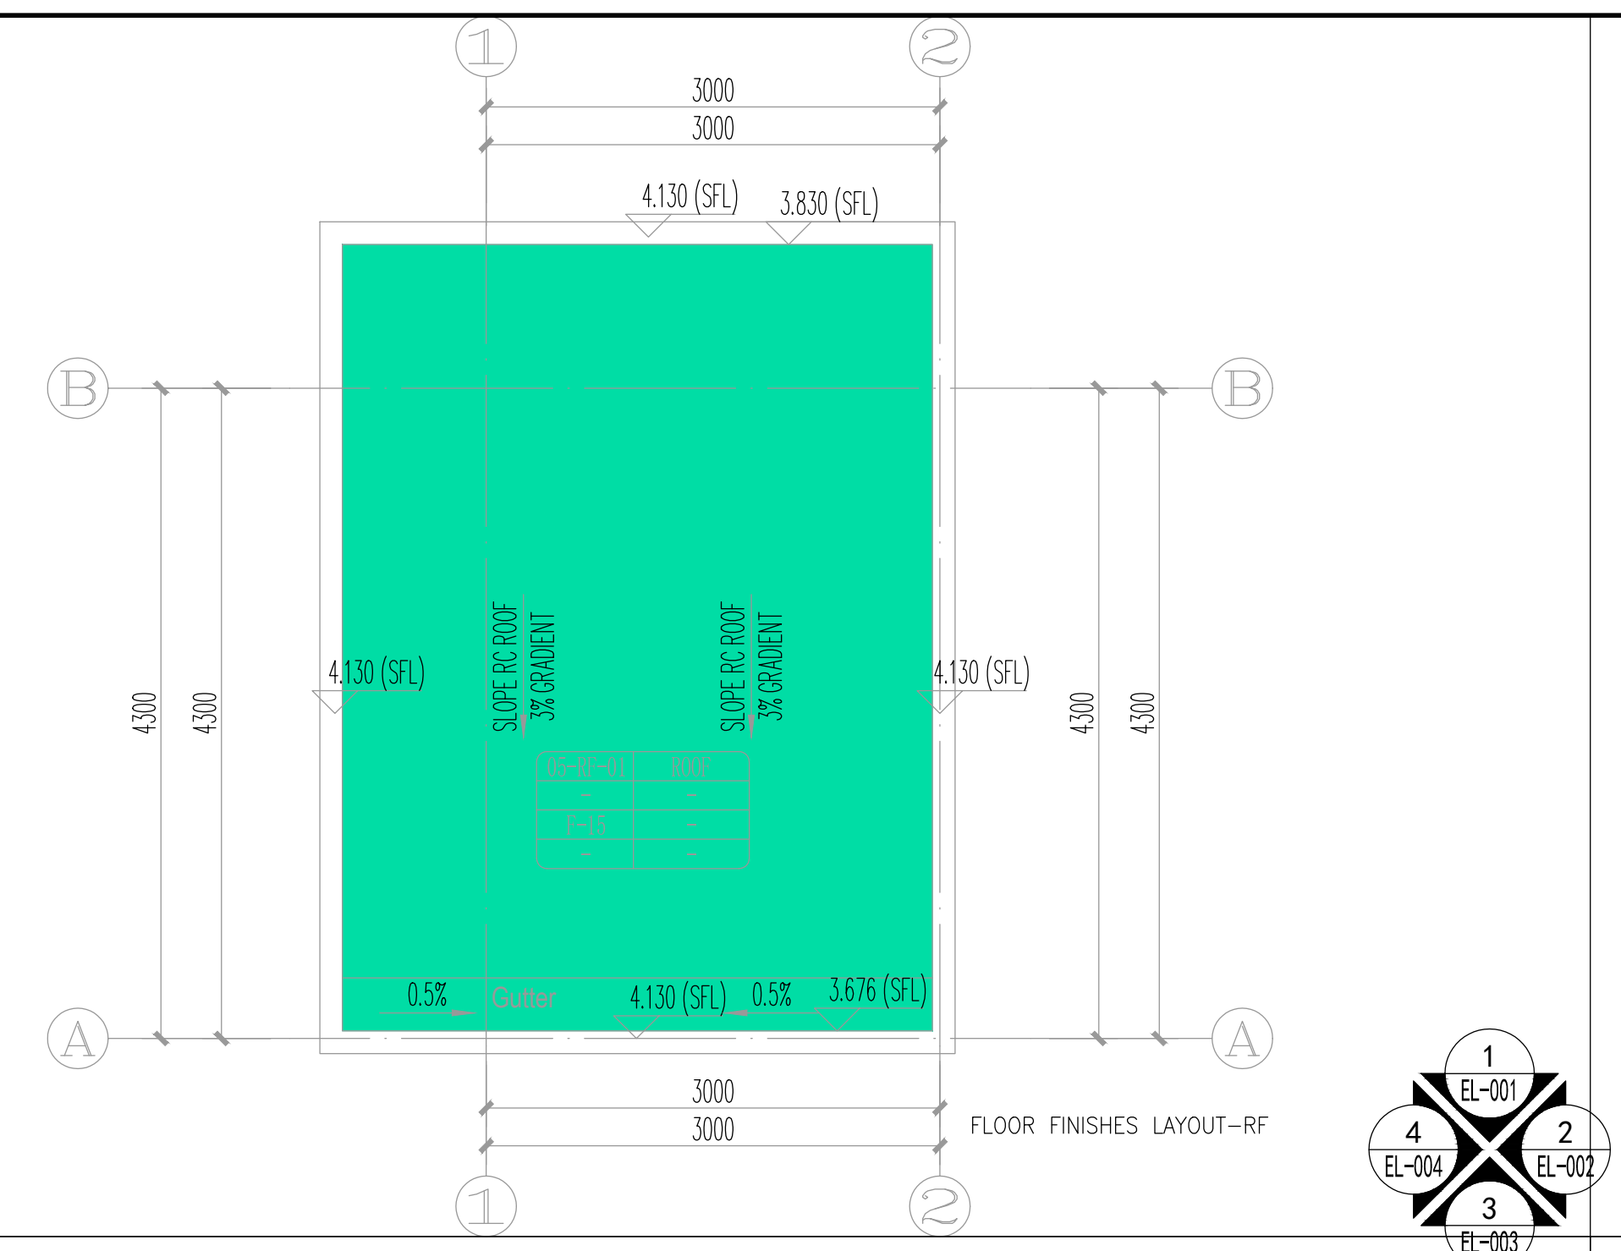

FLOOR FINISHES LAYOUT-RF

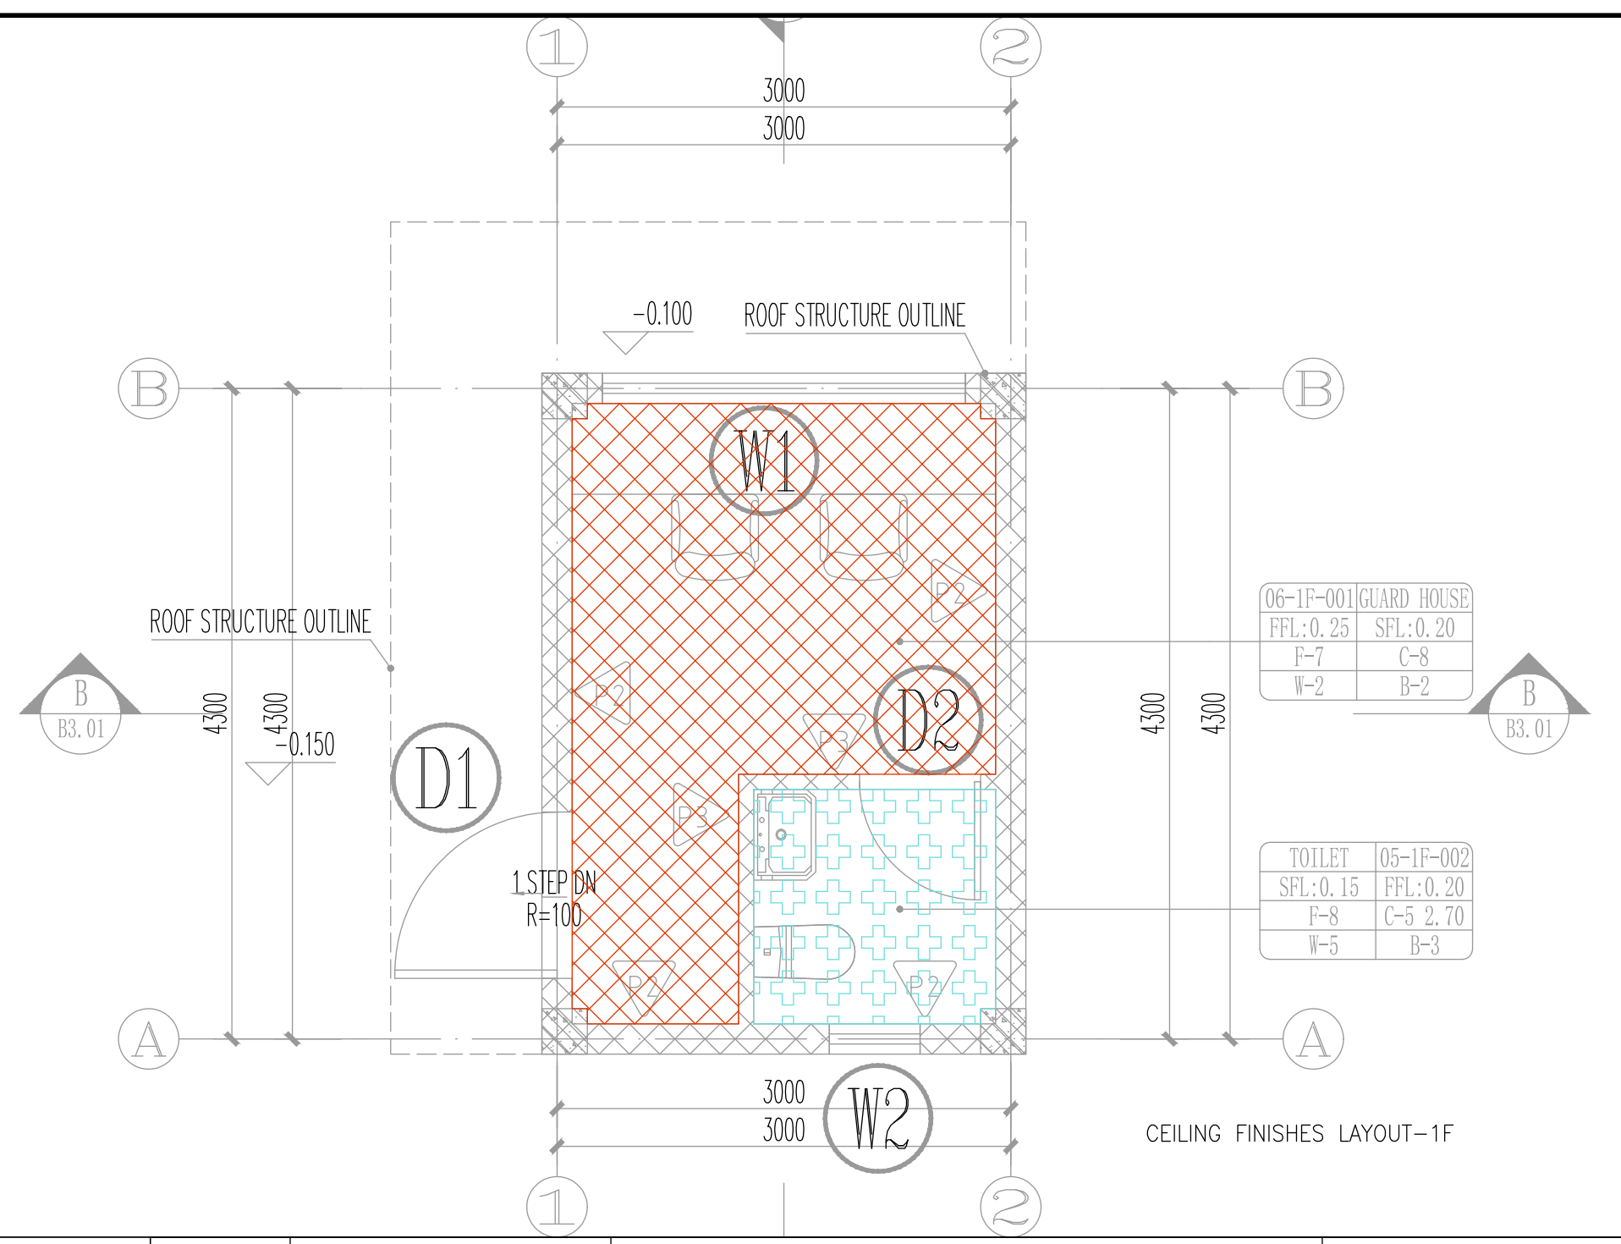

CEILING FINISHES LAYOUT-1F

	Floor No.	Description	Floor Finish Specification	Vender
🟫	F-7	Ceramic Tile	600x600 Ceramic Tile On Concrete Steel Trowel Finish; Low Voc Content & Emission Adhesive	
🟥	F-8	Porcelain Tile	600x600 12mm Thk Non-slip Homogenous Tile (r10) On Waterproofing,Low Voc Tile Adhesive And Grout	
🟩	F-15	Concrete Roof+ Waterproofing	Concrete Roof + Curing Agent+ Waterproofing	

	Ceiling No.	Description	Ceiling Material & Finish Specification	Vender
▨	C-3	MOISTURE-PROOF PAINT	MOISTURE-PROOF PAINT ON CONCRETE CEILING SLAB	
▨	C-5	ALUMINIUM BUCKLE PLATE CEILING	MOISTURE PROOF ALUMINIUM BUCKLE PLATE CEILING + ANTI-DUST PAINT SOFFIT	

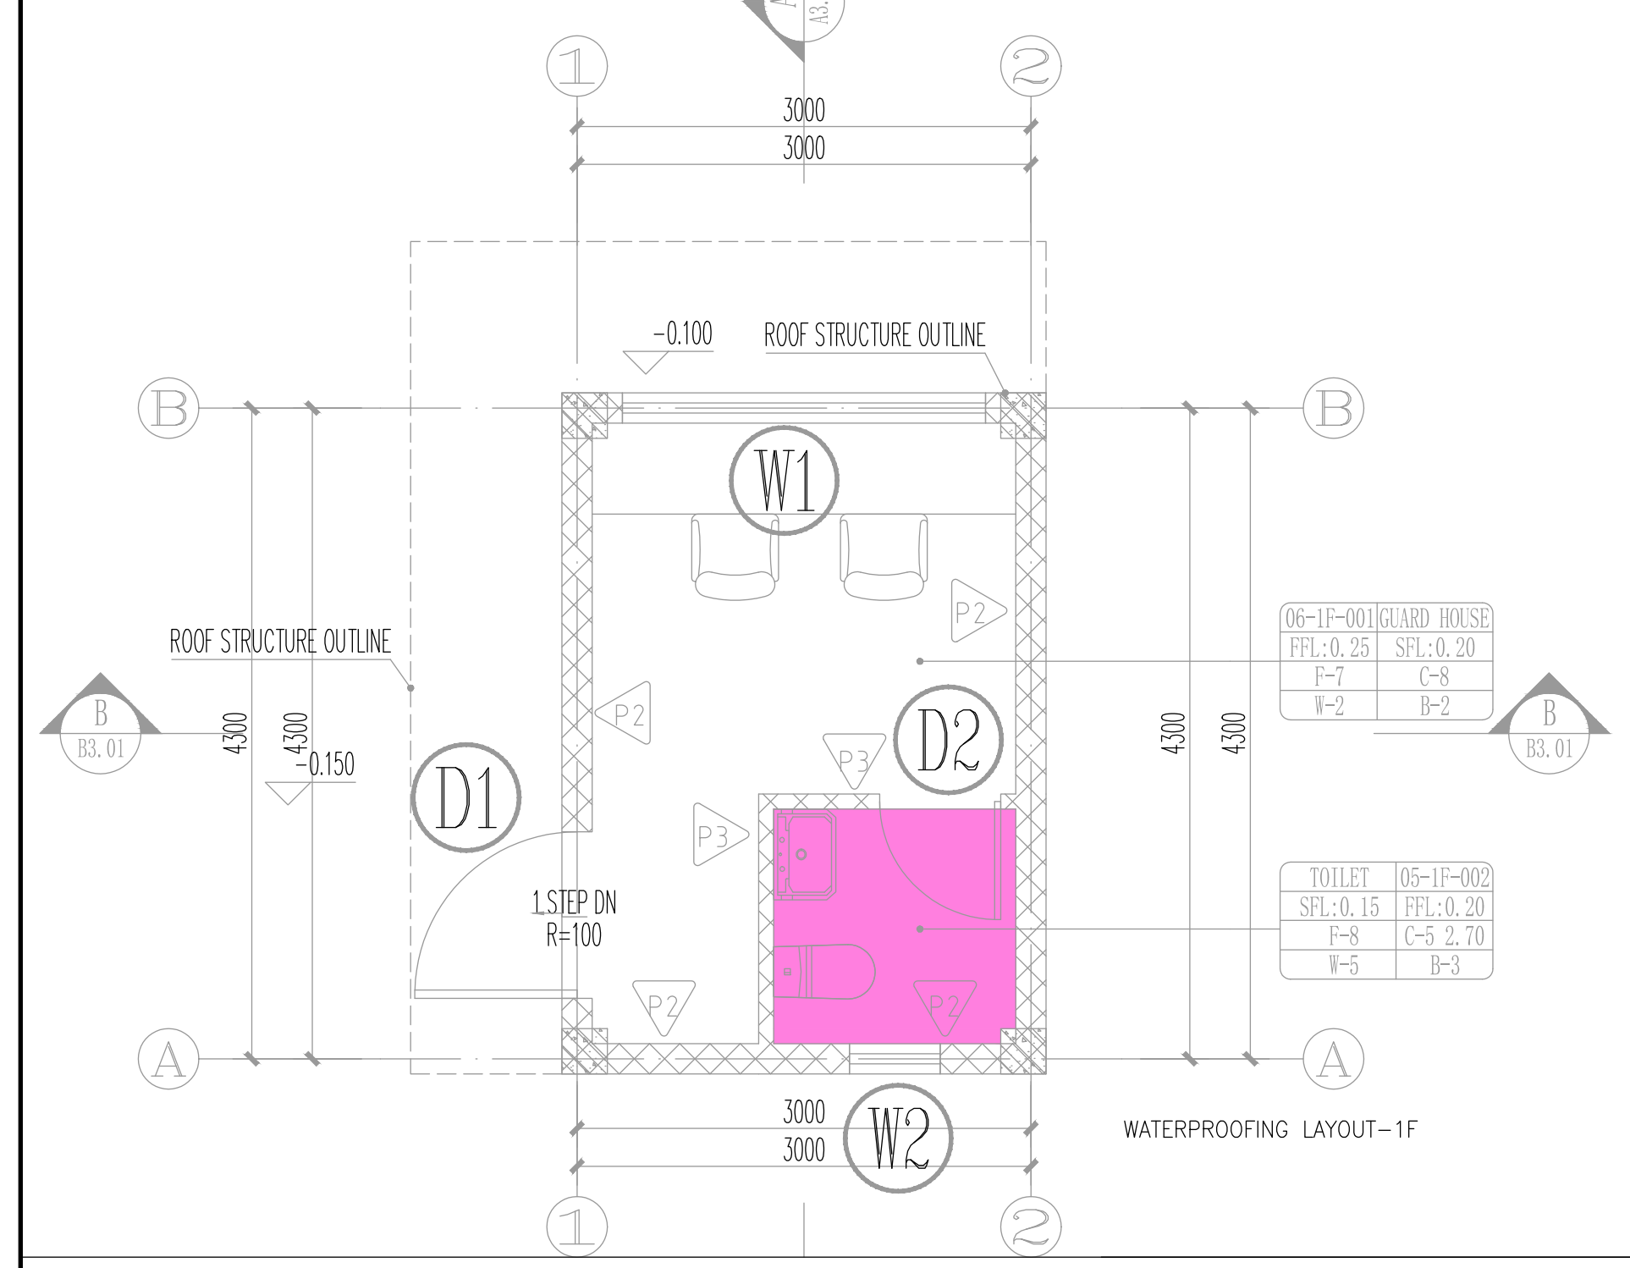

WATERPROOFING LAYOUT-1F

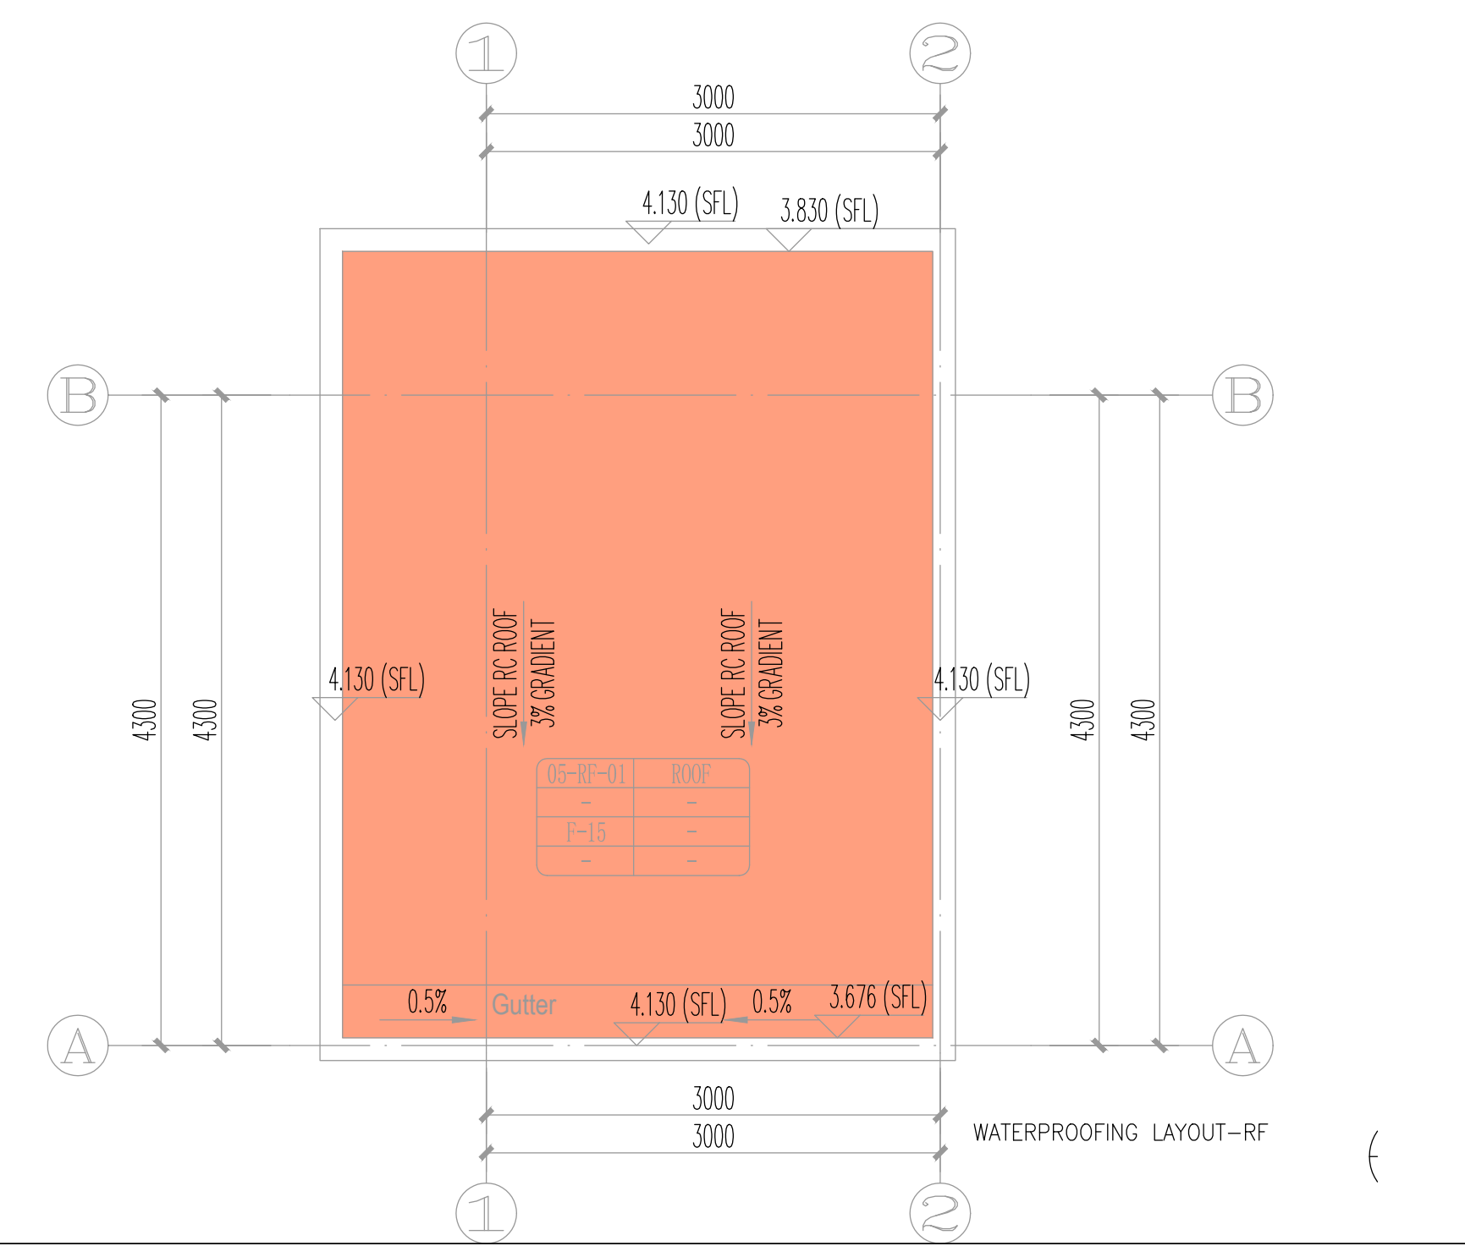

WATERPROOFING LAYOUT-RF

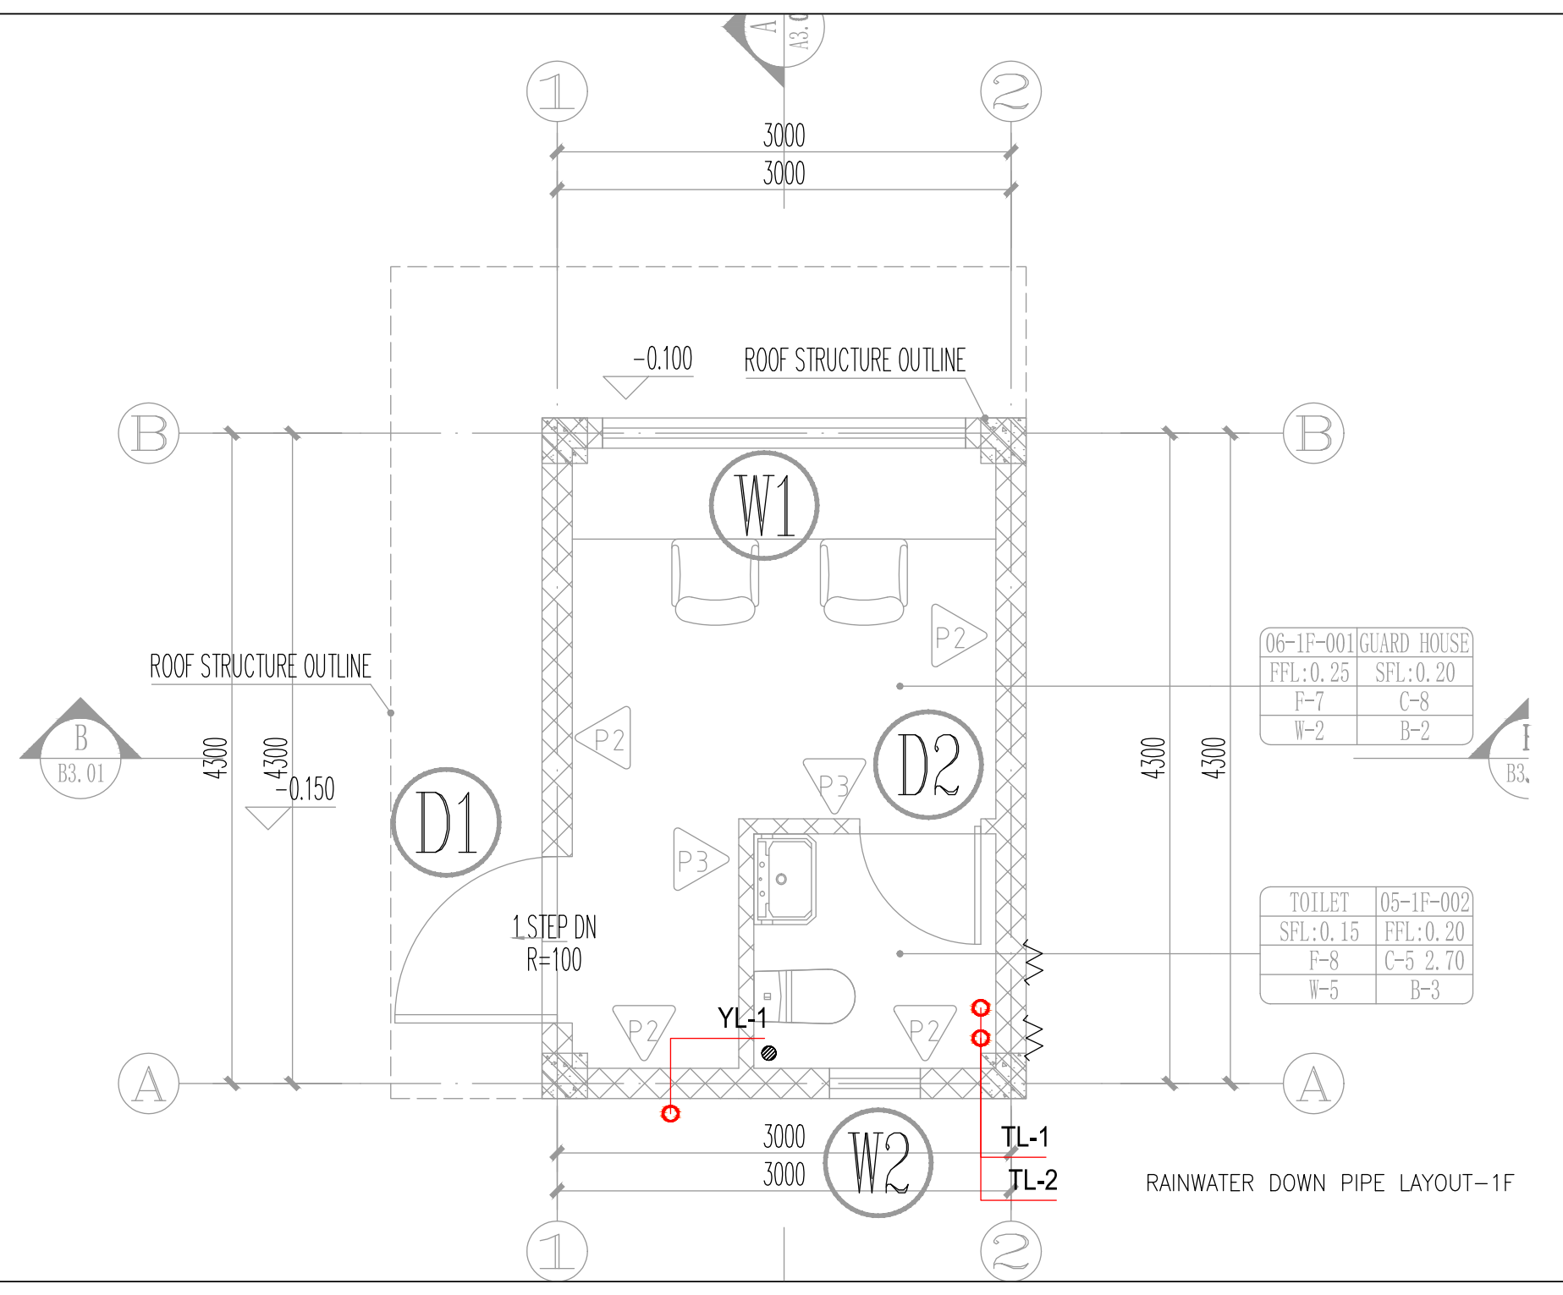

RAINWATER DOWN PIPE LAYOUT-1F

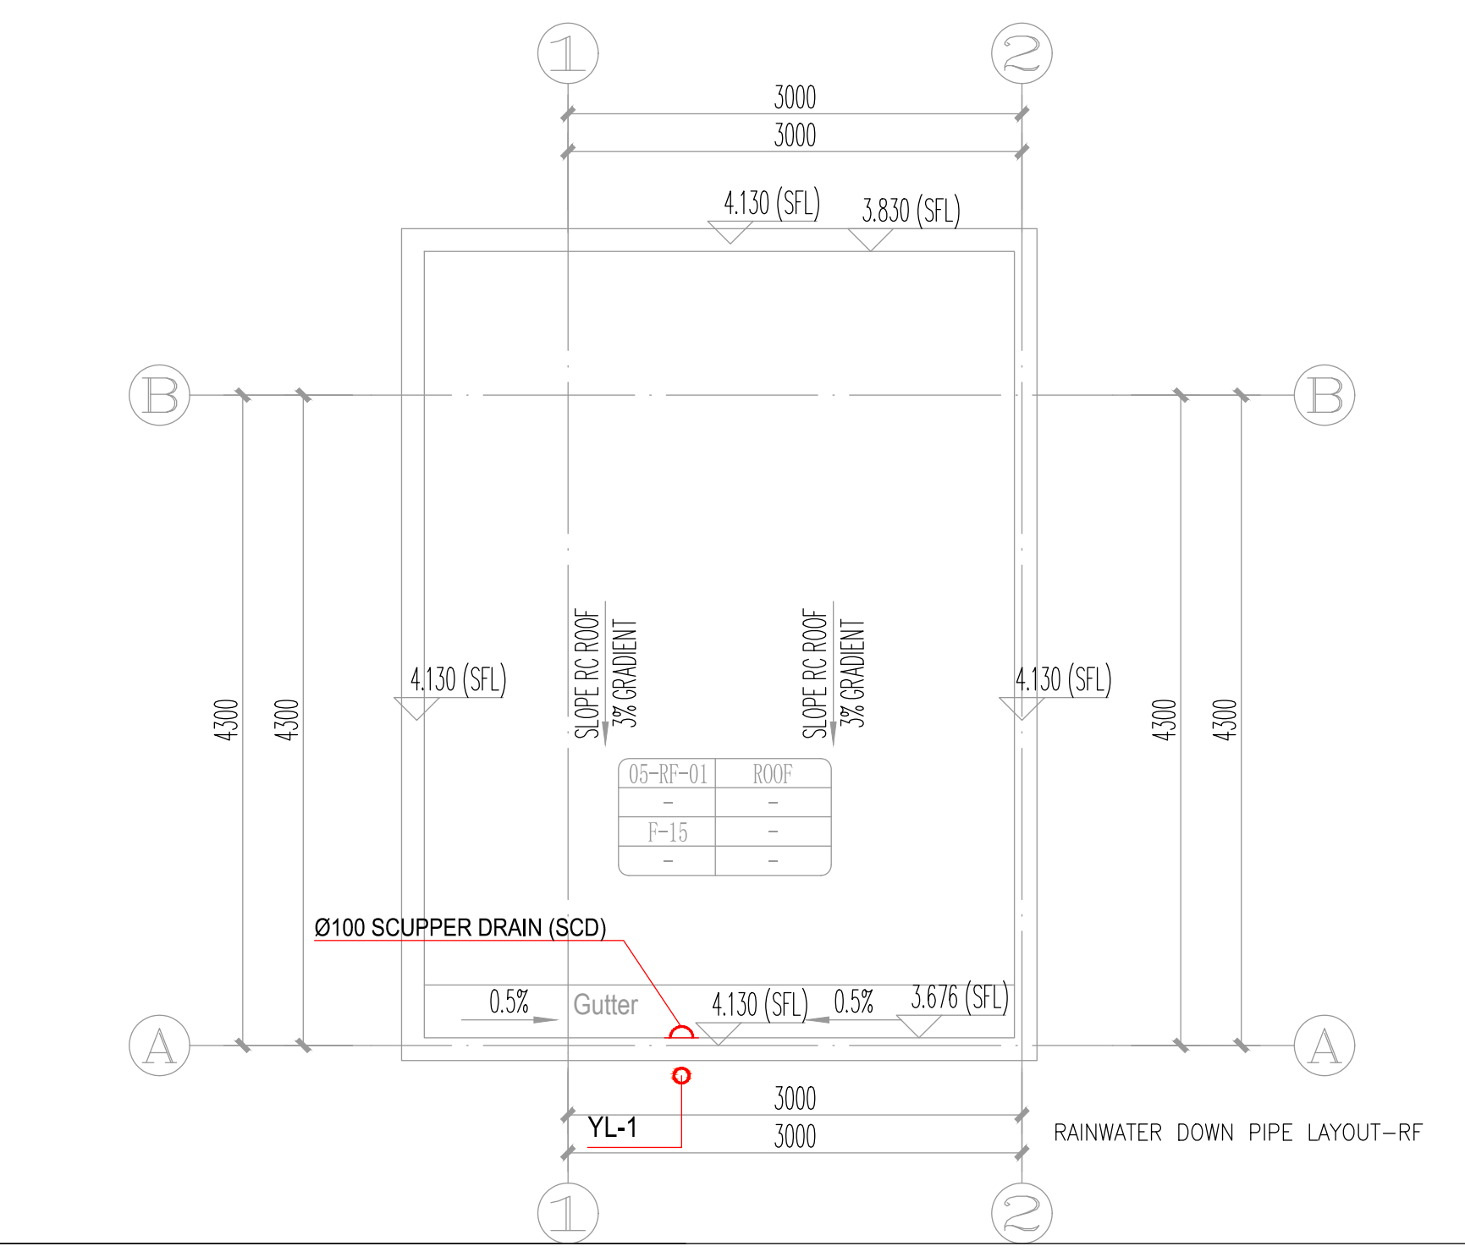

RAINWATER DOWN PIPE LAYOUT-RF

WATER PROOFING

wp-01	Cementitious waterproofing(to manufacturer's detail)
wp-02	Concrete Roof + Curing Agent+ Waterproofing

LEGEND

YTL	100MM HDPE
TL	100MM PVC

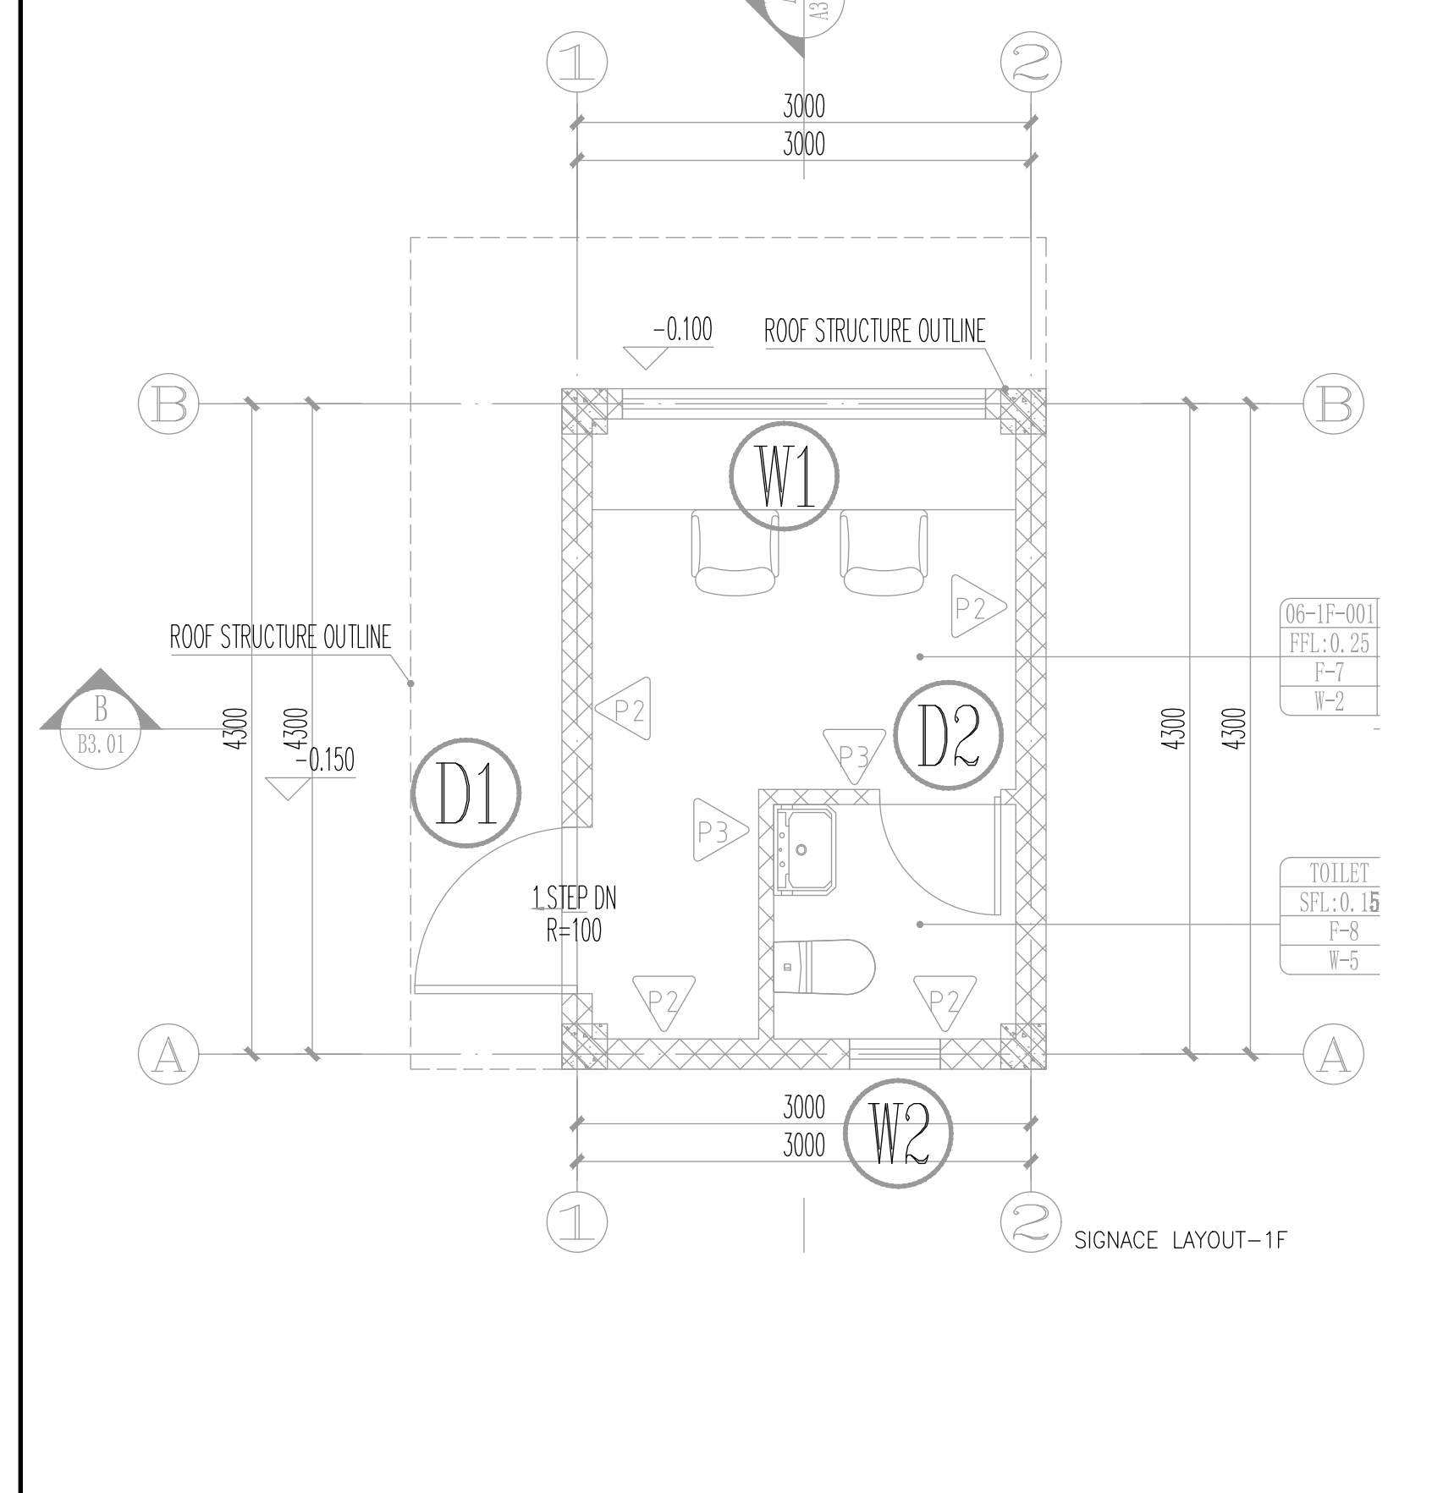

SIGNAGE LAYOUT-1F

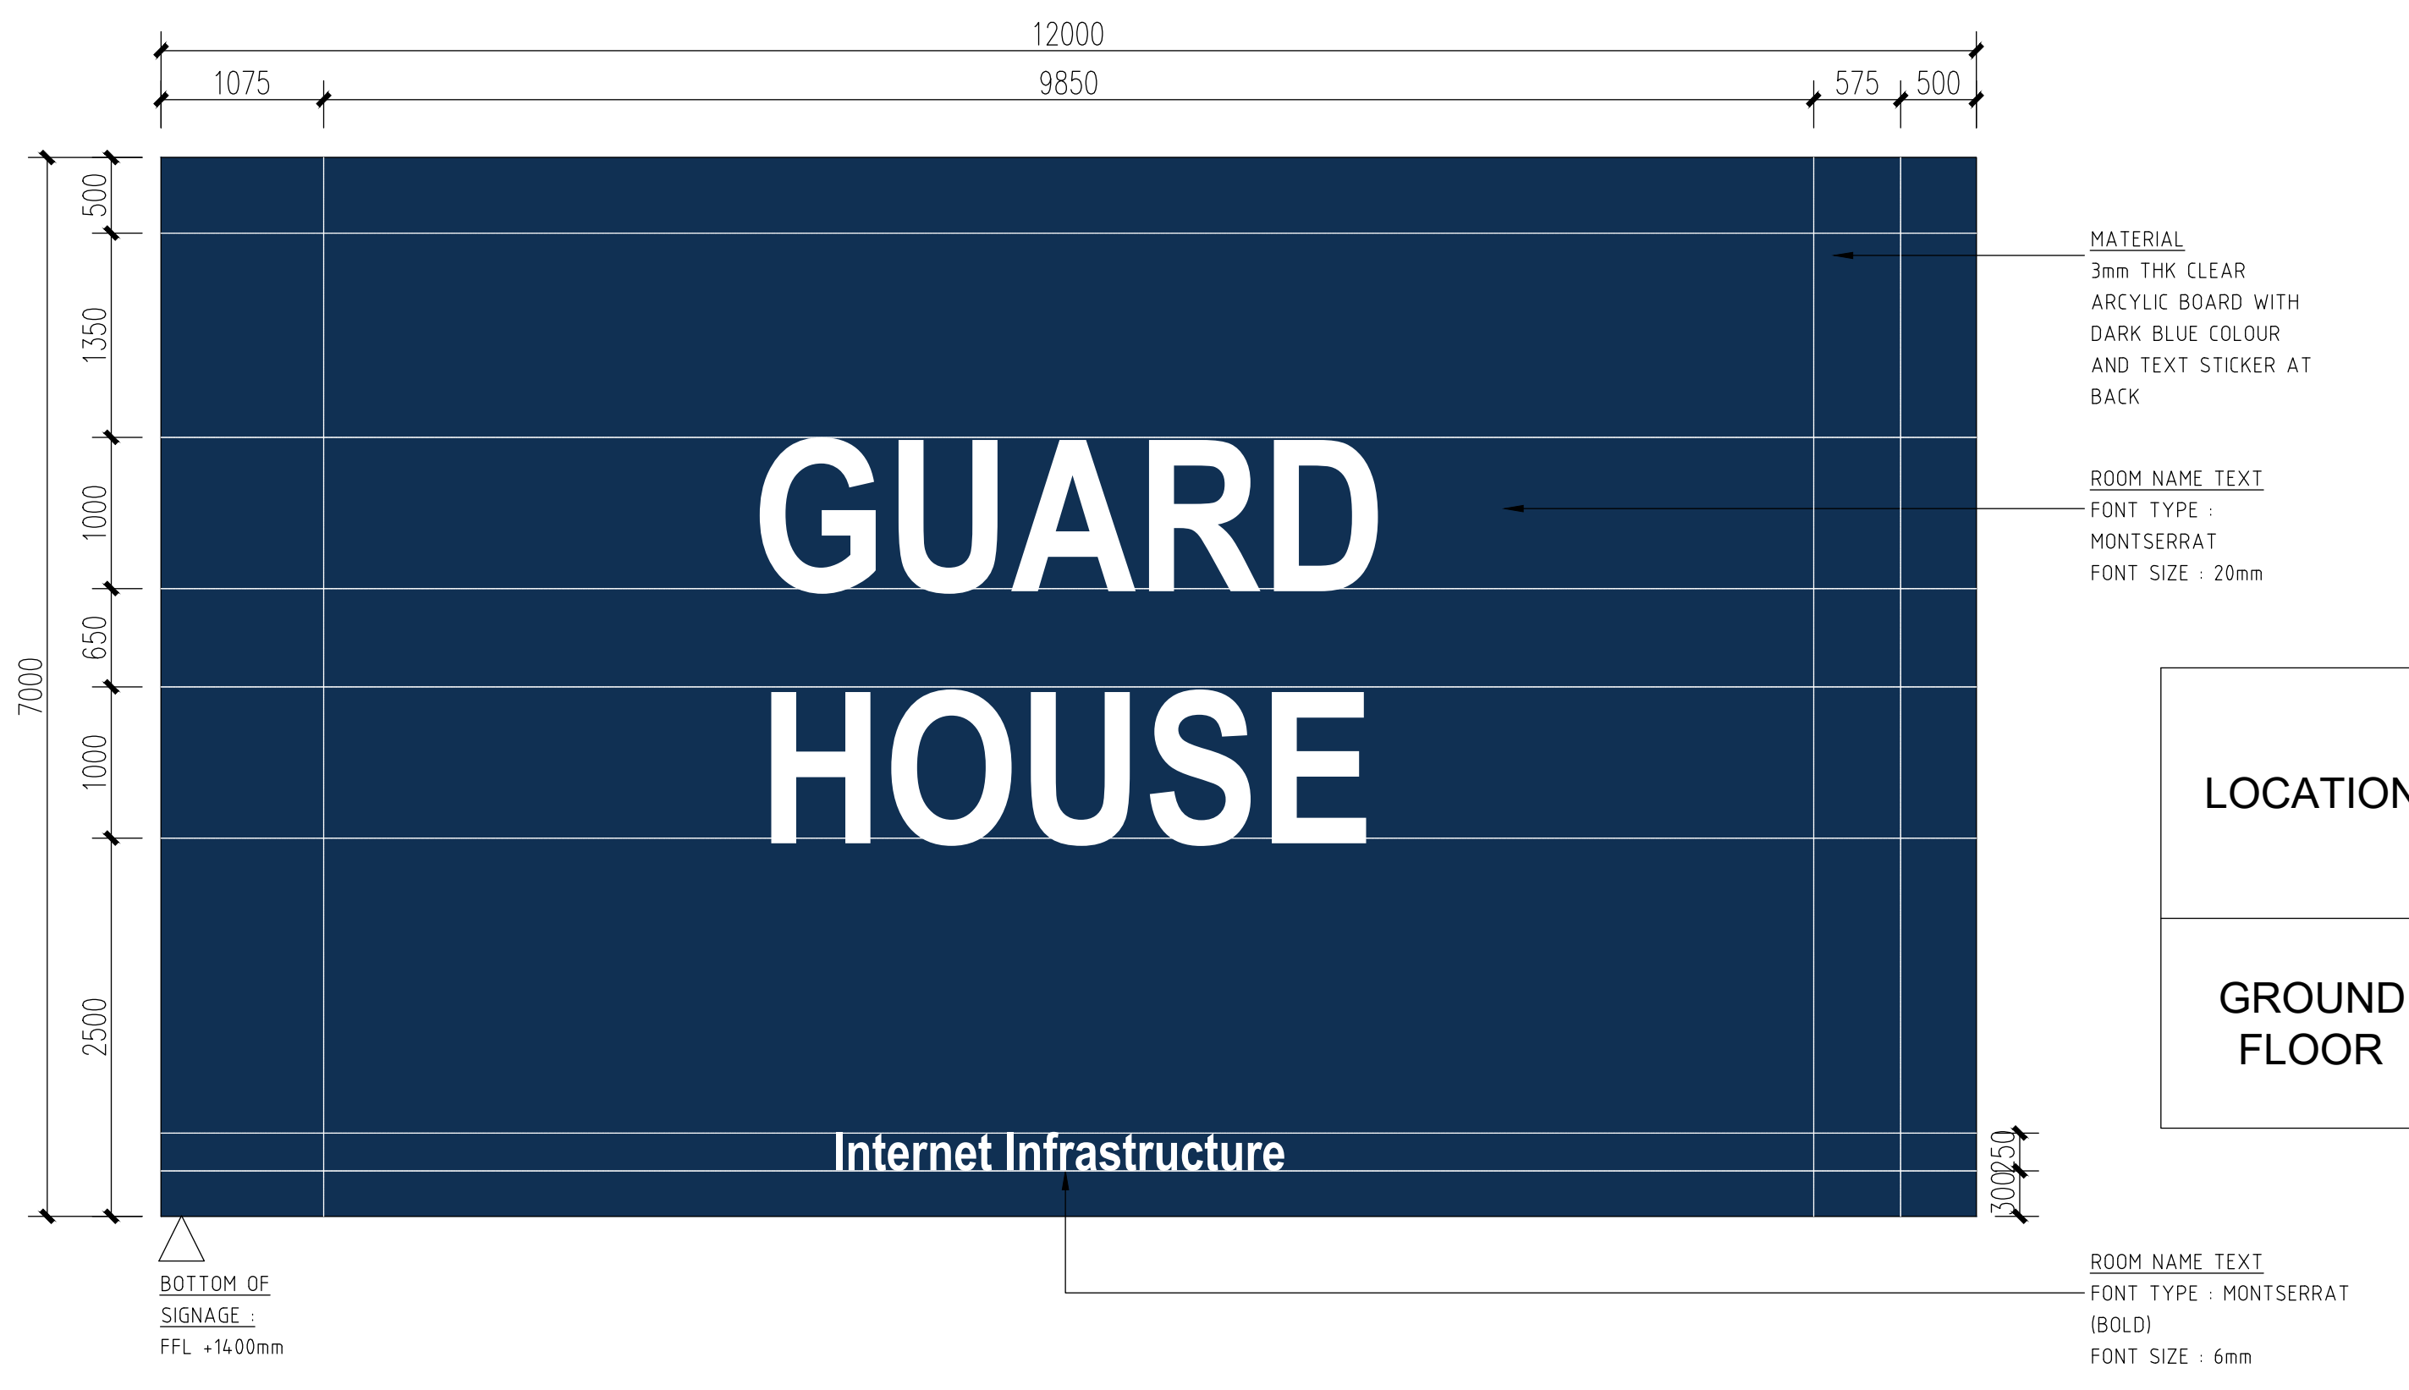

MATERIAL
3mm THK CLEAR
ARCYLIC BOARD WITH
DARK BLUE COLOUR
AND TEXT STICKER AT
BACK

ROOM NAME TEXT
FONT TYPE :
MONTSERRAT
FONT SIZE : 20mm

BOTTOM OF
SIGNAGE :
FFL +1400mm

ROOM NAME TEXT
FONT TYPE : MONTSERRAT
(BOLD)
FONT SIZE : 6mm

LOCATION	SIGNAGE A		QUANTITY	MATERIAL
	ENGLISH	MALAY		
GROUND FLOOR	GUARD HOUSE	-	1	3mm TRANSPARENT ACRYLIC 140mm X 240mm with HIGH RES UV PRINT STICKER TO MATCH PANTONE NAVY BLUE

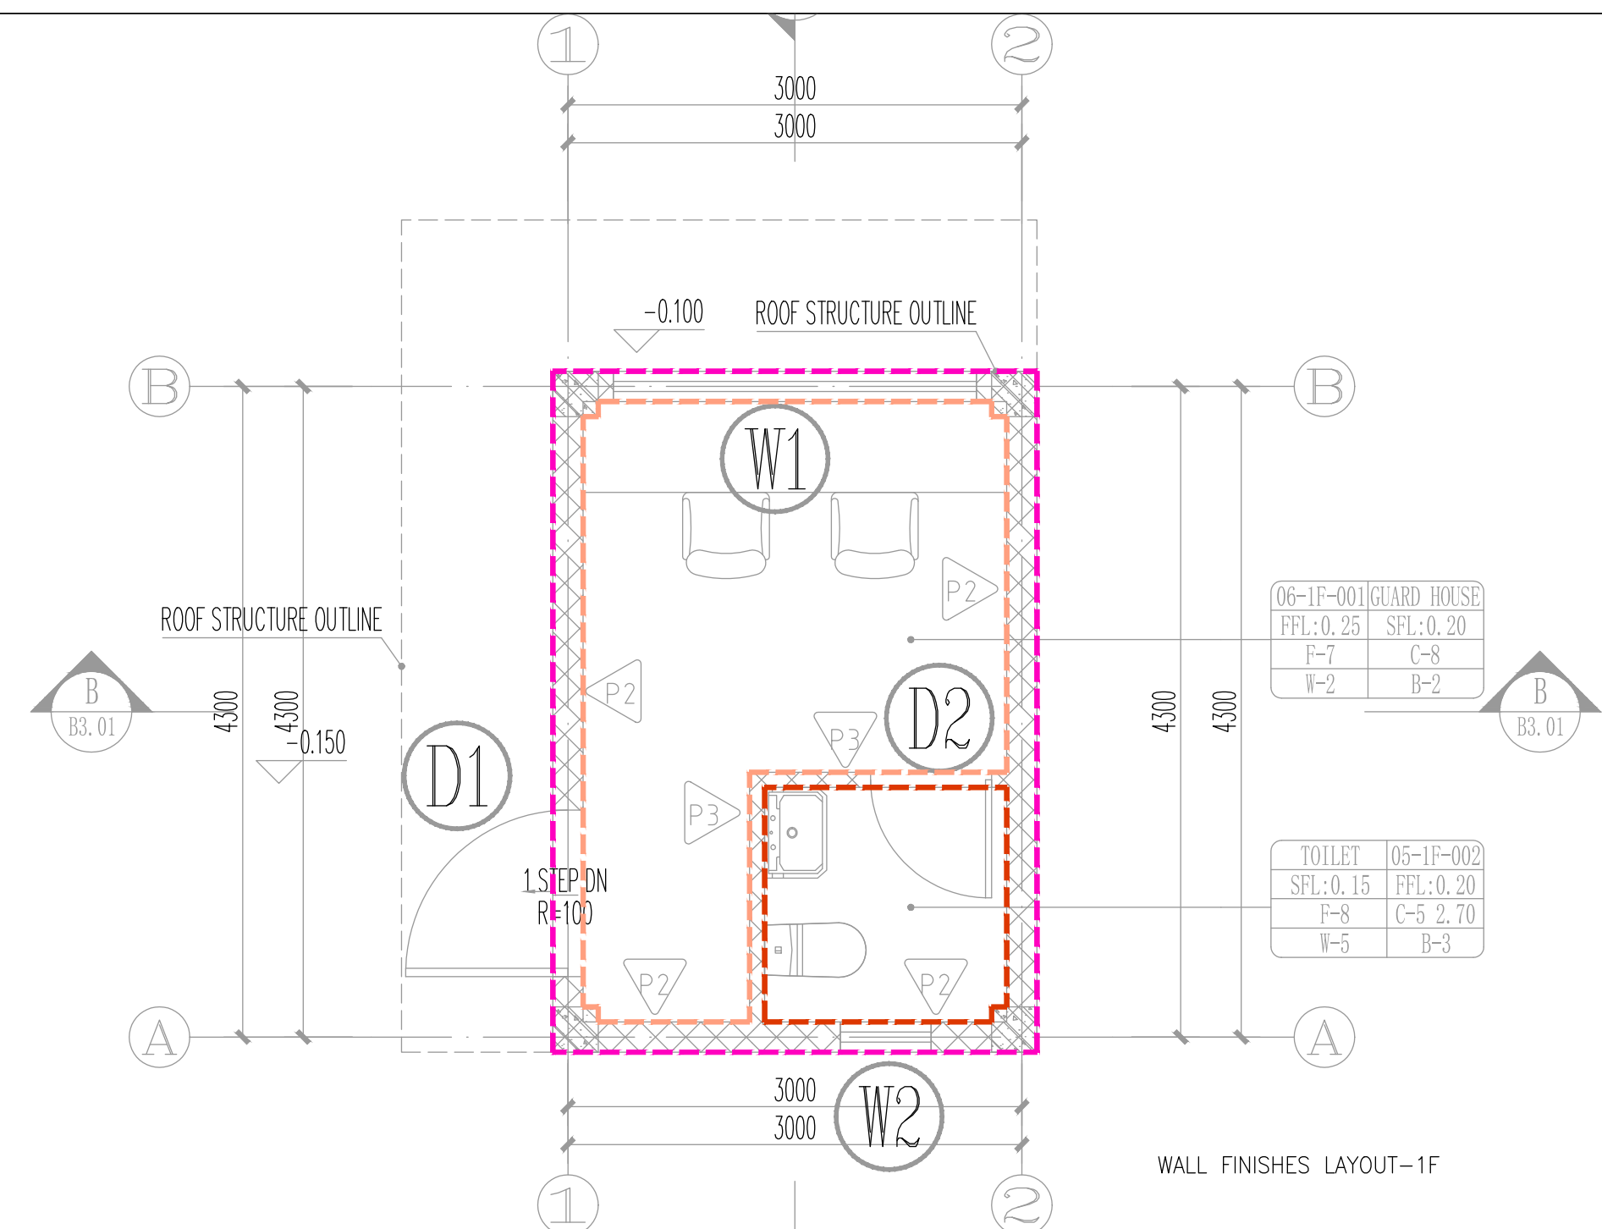

WALL FINISHES LAYOUT-1F

LEGEND	Wall No.	Description	TILE SIZE(MM) WIDTH X DEPTH
- - -	W-2	Skim Coat With Scrub Resistant Paint	Scratch-resistant
- - -	W-5	12mm Thk Waterproof Homogenous Tile	Waterproof
- - -	WF-1	EXTERIOR WALL PAINT	

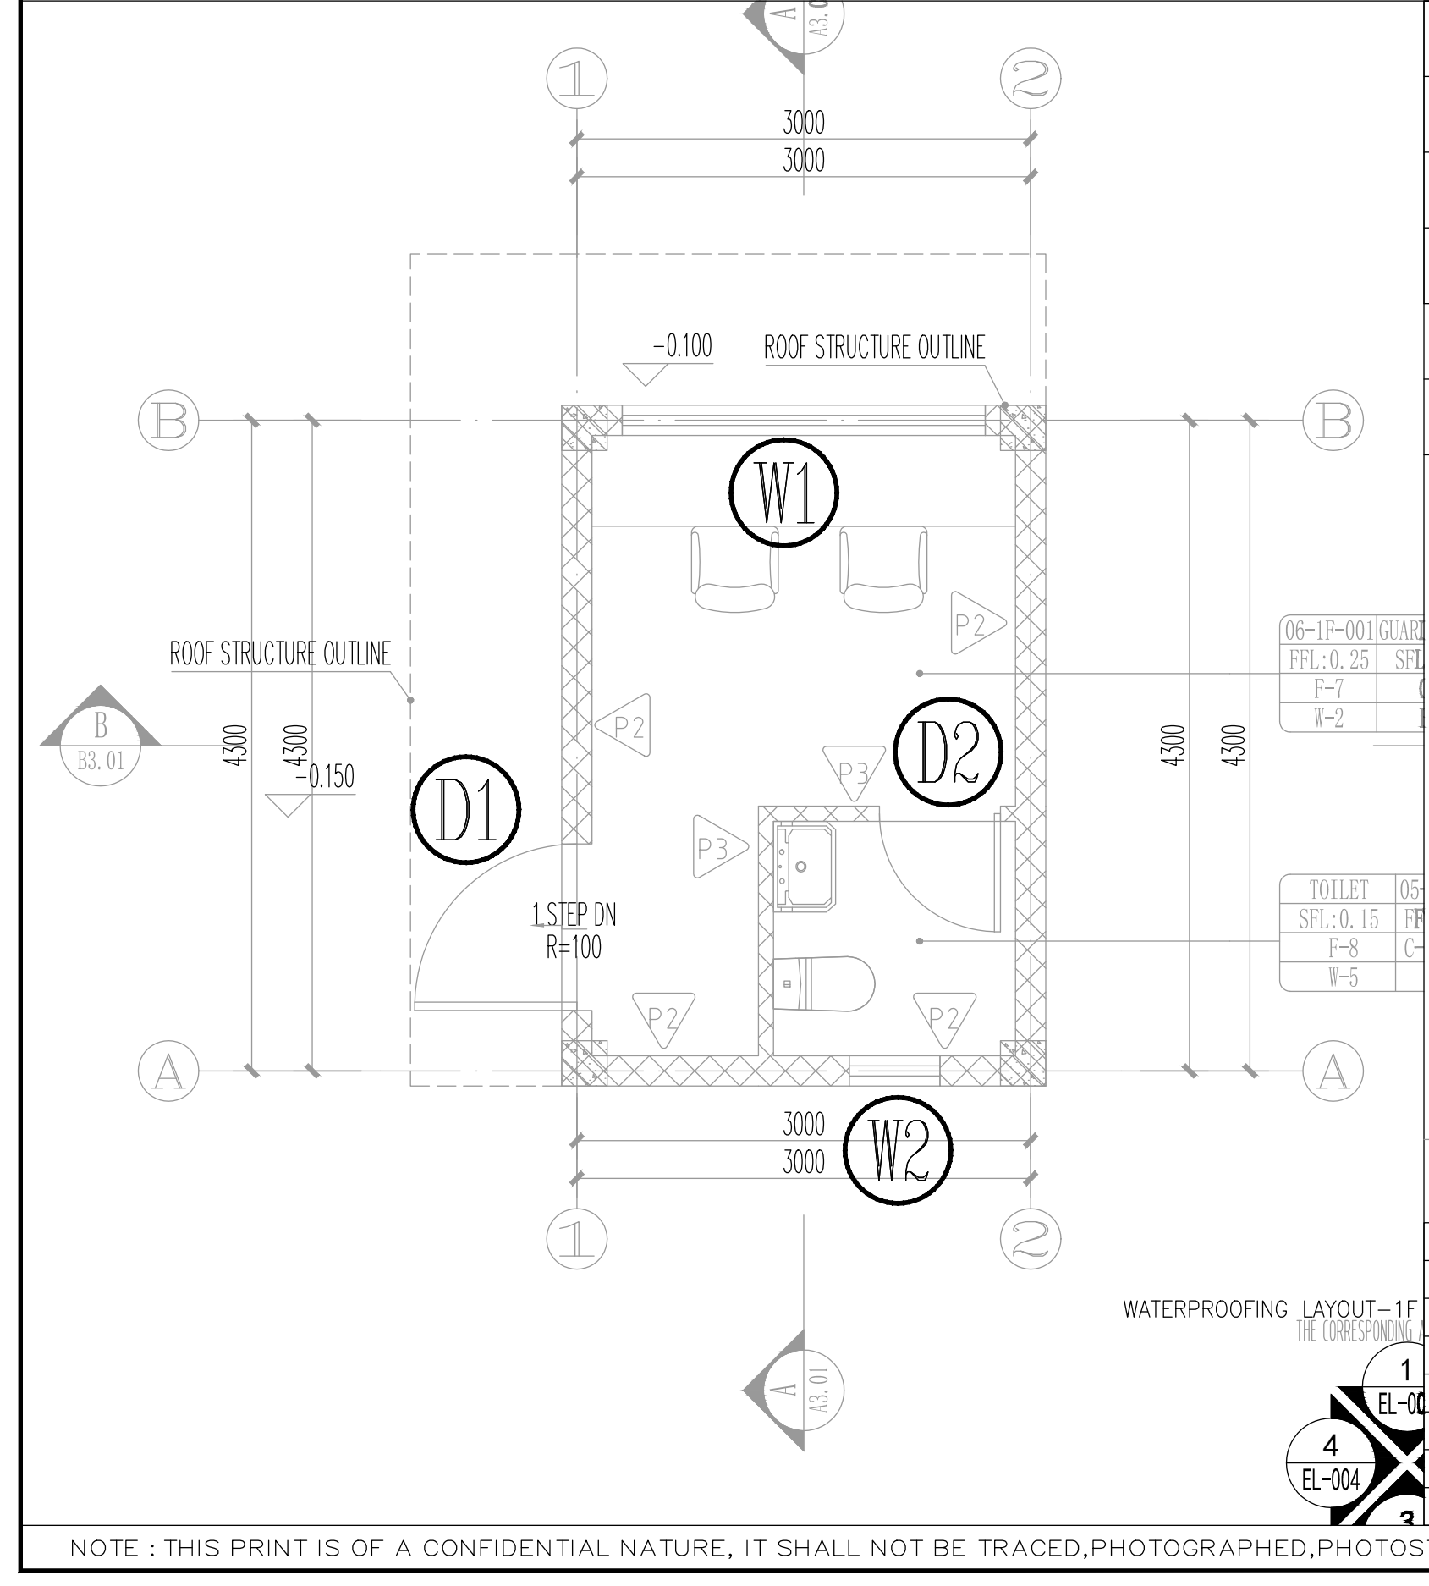

WATERPROOFING LAYOUT-1F

DOOR SCHEDULE

	DESCRIPTION	SISE(MM) WIDTH X HEIGHT
Ⓓ1	G.I METAL FRAME SINGLE LEAF SOLID STEEL DOOR PANEL	1100 X2400
Ⓓ2	METAL FRAME WATER RESISTANT TMBERFLUSH DOOR TO MANUF'S DETAIL	900 X2200
Ⓦ1	FORCED-ENTRY CLASS WNDOW TO MANUF'SDETAIL	2400 X 1000
Ⓦ2	ALUMINUM CASENENT WNDOW	600 X 900

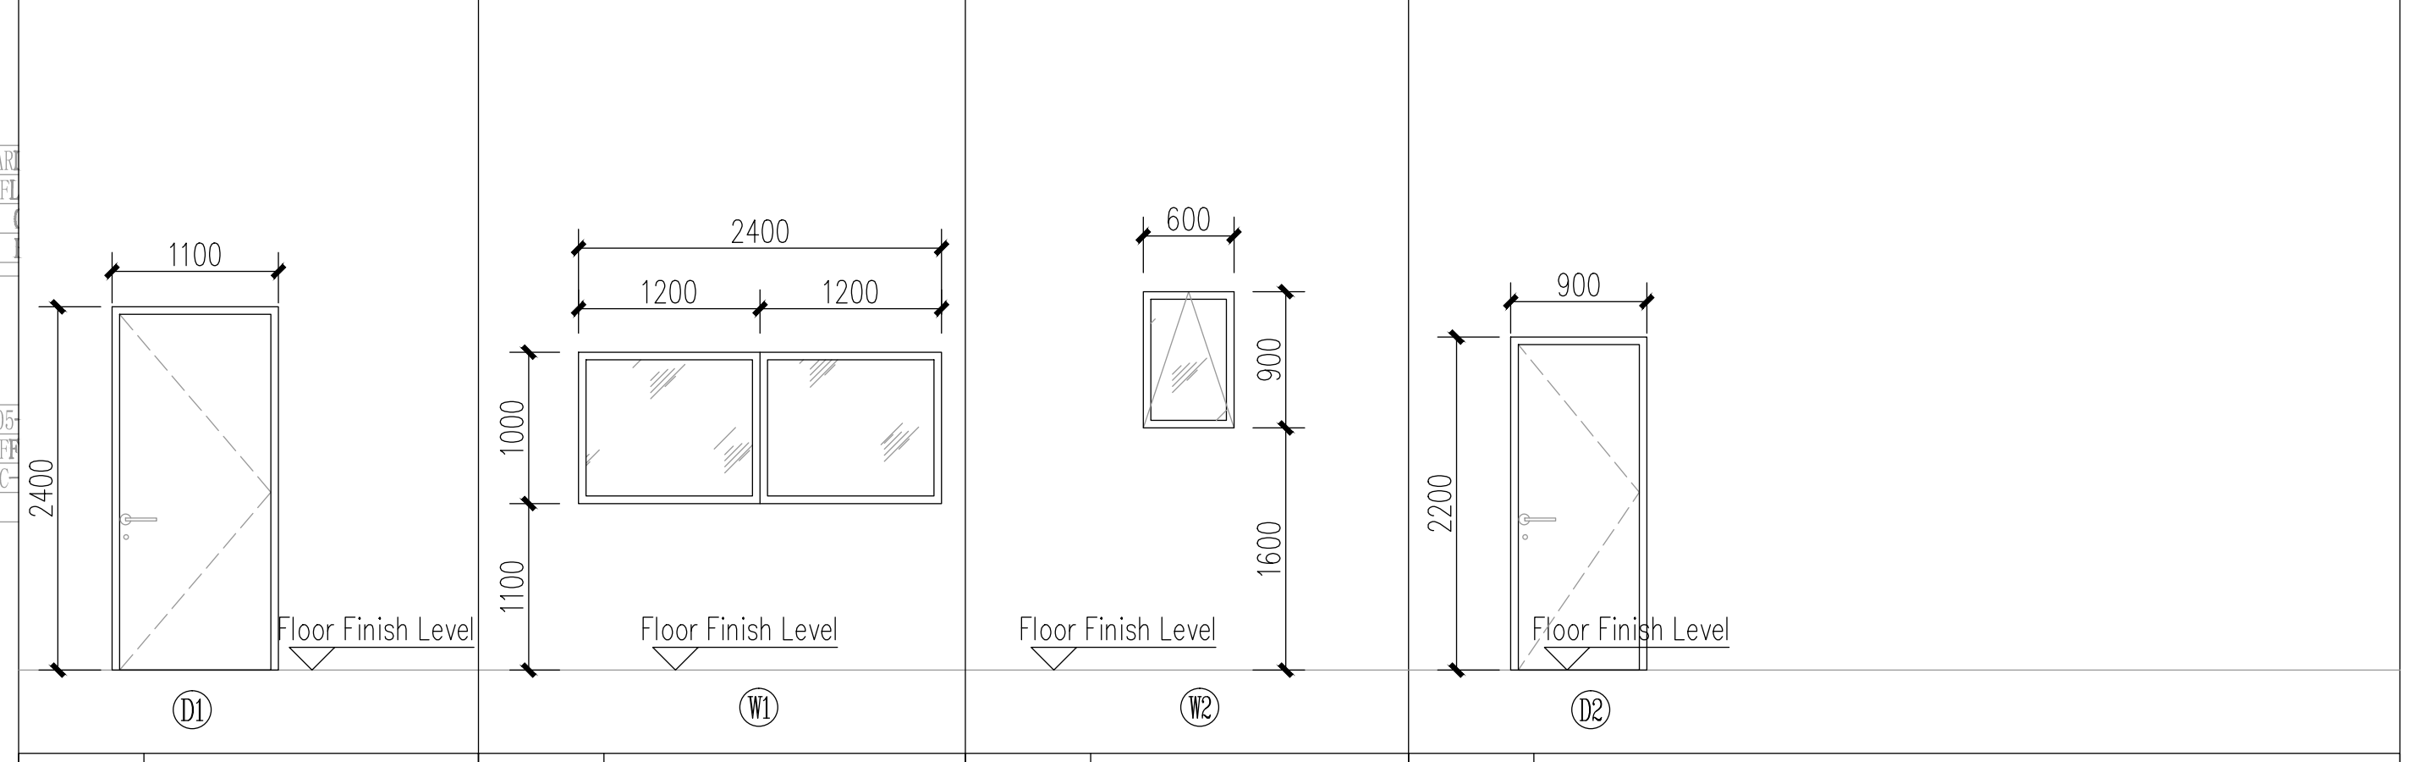

FUNCTON	GUARD HOUSE	FUNCTON	GUARD HOUSE	FUNCTON	GUARD HOUSE	FUNCTON	TOILET
TYPE	STEEL SINGLE DOOR,	TYPE	ALUMINUM CASENENT WNDOW	TYPE	ALUMINUM CASENENT WNDOW	TYPE	METAL FRAME WATER RESISTANT TMBERFLUSH DOOR
	SINGLE SWING	HARDWARE		HARDWARE			SINGLE SWING
HARDWARE	DOOR CLOSER	Total		Total		HARDWARE	DOOR CLOSER
	DOOR STOPPER						DOOR STOPPER
	HANDLE						HANDLE
	KEY						KEY
Total	1					Total	2

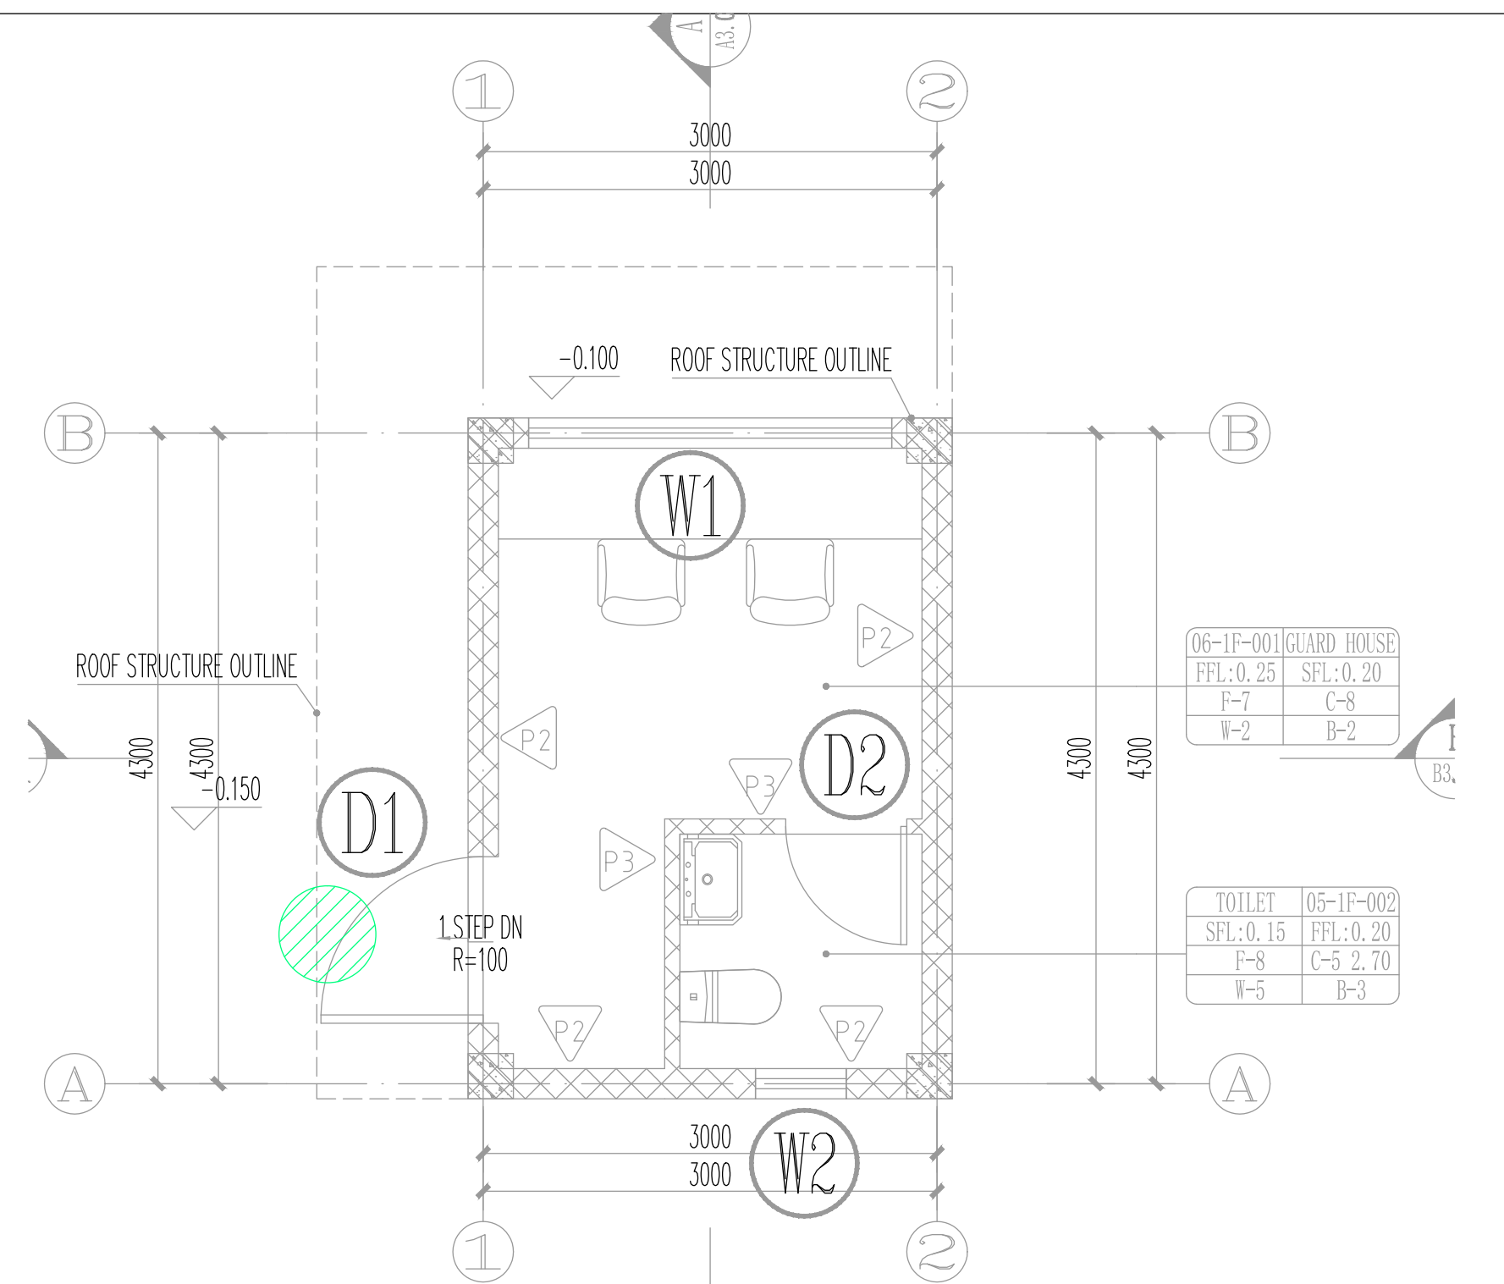

LEED: Remark for all door & window glazing
Exterior Glazing Performance:
SHGC=0.3 or better
U-value = 2.0 W/(m2K) or better'
Notes:
The specific specifications for doors, windows, and hardware will be provided during the IFC review stage.

MASTER KEY LAYOUT-1F
THE CORRESPONDING ABSOLUTE ELEVATION

MASTER KEY SYSTEM

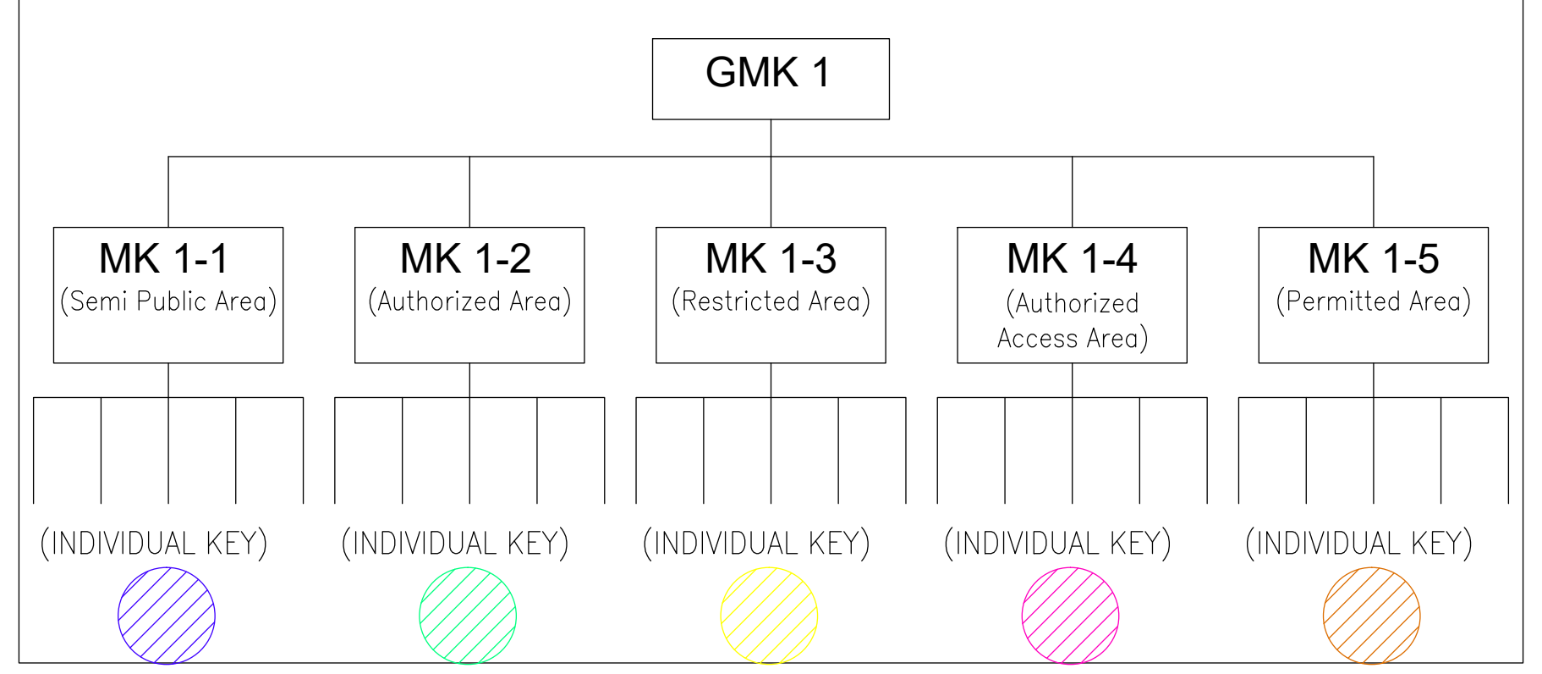

LEGEND:
GMK=GRAND MASTER KEY
MK1-0 ~ MK1-5= MASTER KEY
NOTE:
EACH DOOR HAS ITS OWN INDIVIDUAL MECHANICAL KEY; EACH SECURITY ZONE HAS A MASTER KEY WHICH CAN OPEN EVERY DOOR IN THAT ZONE.

NOTE : THIS PRINT IS OF A CONFIDENTIAL NATURE, IT SHALL NOT BE TRACED,PHOTOGRAPHED,PHOTOSTATED OR REPRODUCED IN ANY MANER,NOR USED FOR ANY PURPOSE WHATSOEVER EXCEPT BY WRITTEN PERMISSION

CLIENT :
GULF EDGE DC 01
87 Wireless Road, M Thai Tower 11th. Floor, All Seasons Place, Lumpini,
Pathumwan, Bangkok 10330, Thailand

CONTRACTOR :
华西发展(泰国)有限公司
บริษัท หัวซือ ดีเวลลอปเม้นต์ (ประเทศไทย) จำกัด
HUASHI DEVELOPMENT CO.,LTD
No. 202, Room No. 1403, 14/F, Le Concorde Building,
Ratchadapisek Road, Huaykhwang Sub-District,
Huaykhwang District, Bangkok Metropolitan 10310.

CONSULTANT :
ARbay
บริษัท เอ อาร์ เบย์ จำกัด
ARbay Company Limited
31 st Floor Bangkok Insurance Building
25 South Sathorn road Thungmahamek
Sathorn Bangkok 10120 THAILAND
T +66 (0) 2286 8199
F +66 (0) 2286 2863
info@arbay.co.th

CONSULTANT :
Qbic Engineers & Architects Co.,Ltd.
8 Soi KALONG 4 SANAMBINNAM ROAD,
THASAI SUB-DISTRICT, MUANG NONTHABURI DISTRICT
, NONTHABURI.
Tel 662-950-4374
Fax 662-580-3231
E-Mail : qbic@qbic.co.th, www.qbic.co.th
QBIC ENGINEERS AND ARCHITECTS CO.,LTD.

CONSULTANT :
MITR
MITR TECHNICAL CONSULTANT CO.,LTD.
1168/8 12th FLOOR, LUMPINI TOWER BUILDING,
RAMA IV RD., THUNGMAHAMEK, SATHORN, BANGKOK 10120, THAILAND
TEL : 0-2679-9079-84
FAX : 0-2679-9085 E-mail: mitr_dd@mitr.com

Architect :	SIGNATURE
ประกิต พนานุรัตน์ วสถ. 580 ที่อยู่ 251/1 ถ.จารุเมือง แขวงรองเมือง เขตปทุมวัน กรุงเทพมหานคร โทรศัพท์ 02-286-8199	

Structural Engineer :	SIGNATURE
วิศวกรผู้ออกแบบโครงสร้าง	
ณัฐสม สงวนวงษ์ วย 1423 ที่อยู่ 2/1 ซ.รามคำแหง 150 ถ.รามคำแหง แขวง สะพานสูง เขต สะพานสูง กทม. 10240	ณัฐสม สงวนวงษ์

Structural Inspector :	SIGNATURE
วิศวกรผู้ตรวจสอบโครงสร้าง	
โกมล จุฑาภัทร วย 964 ที่อยู่ 24/18 ซ.นวมินทร์ 129 ถ. นวมินทร์ แขวง นวลจันทร์ เขต บึงกุ่ม กทม. 10230	

Electrical Engineer :	SIGNATURE
วิศวกรผู้ออกแบบระบบไฟฟ้ากำลัง	
นายสุภัทร บูรณวิทย์ วฟก.1265 ที่อยู่ 21 ซอยทานสัมฤทธิ์ 13 ตำบลท่าทราย อ.เมืองนนทบุรี จ.นนทบุรี 11000	สุภัทร

Mechanical Engineer :	SIGNATURE
วิศวกรผู้ออกแบบระบบเครื่องกลและปรับอากาศ	
นายประสิทธิ์ ถ้ยวสุนทร วก.1221 ที่อยู่ 44/372 ซอยบางกระดี่ 35/1 แขวงแสมดำ เขตบางขุนเทียน กทม. 10150	ประสิทธิ์

Sanitary Engineer :	SIGNATURE
วิศวกรผู้ออกแบบระบบสุขาภิบาล และดับเพลิง	
นายทศวรรษ สันนฤทธิ์ วส. 215 ที่อยู่ บ้านเลขที่ 99/107 หมู่ที่ 3 ต.ศีรษะจรเข้น้อย อ.บางเสาธง จ.สมุทรปราการ 10540	ทศวรรษ

ISSUE/REVISION

REV.	DESCRIPTION	DATE
A	90% DEVELOPED	09/05/2026

PROJECT NAME :
GEDC 01
LOCATION:
Nikhom Phattana district, Rayong ,industrial estate,CPGC

BUILDING :
GUARD HOUSE B

90% DEVELOPED

TITLE :
FLOOR FINISHES&CEILING&WATERPROOFING &RAINWATER DOWN PIPE& SIGNAGE & WALL FINISHES &DOOR&WINDOW & MASTER KEY LAYOUT LAYOUT

JOB NO.	SCALE 1:50
DRAWN LK	REF.
CHECKED LJC	DWG.NO.
APPROVED LXD	MPK05-60-FF&CL&WR&RDP&SN&WL&DW&MK-101
DATE 2026.05.09	