DIMENSIONAL REQUIREMENTS	SHAFT SIZE(MMW X MMD)PER LFT (REFER TO DRAWINGS)	4450WX4800D	2350WX2200D	4450WX4800D
	SHAFT SIZE(MMWXMMD)PER GROUP(REFER TO DRAWINGS)	4450WX 4800D （PER GROUP)	2350WX 2200D （PER GROUP)	4450WX 4800D （PER GROUP)
	CARINTERNAL CLEAR SIZE(MMWX MMDWALLFINISHES TO WALLFINISHES EXCLUDEHANDRALS,NOTICE BOARD,LED,BUMPERS	2500W X 3500D	1600W X 1400D	2500W X 3500D
	CAR INTERNAL CLEAR CEILING HEIGHT (MMH)	3000H	2300H	3000H
	STRUCTURAL CAR HEIGHT(MMH)	3300H	2600H	3300H
	TYPE OF DOOR (MINIMUM 2 HOURS FIRE RATING LANDING DOOR)	POWER OPERATED 2-PANELS CENTRE-OPENING	POWER OPERATED 2-PANELS CENTRE-OPENING	POWER OPERATED 2-PANELS CENTRE-OPENING
	DOOR SIZE(MMWX MMH)	2000WX 3000H	1100WX 2100H	2000WX 3000H
	VENT HOLE PER LIFT (C/W WEATHER PROOF ALUMINUM LOUVERS GIVING A NET FREE AREA OF 40% OF 0.3M SQ/0.45MSQ PER LIFT	NET AREA 0.3M²	NET AREA 0.3M²	NET AREA 0.3M²
	PIT DEPTH(MM)(REFER TO DRAWINGS)	2400	2400	2400
	SUMP PIT SIZE(MMW X MML X MMD)PER LIFT (BY MAIN CONTRACTOR)	NIL	NIL	NIL
OTHER FEATURES	PRIMARY LIFT HOMING FLOOR	L1	L1	L1
	ALLOWABLE CAGE FINISHES WEIGHT (KG PER LIFT)	300KG	300KG	300KG
	HANDICAP COMPLIANCE	NO	YES	NO
	VENTILATION MODE	MV	AIRCON	MV
	FIREMEN SWITCH	1	NIL	NIL

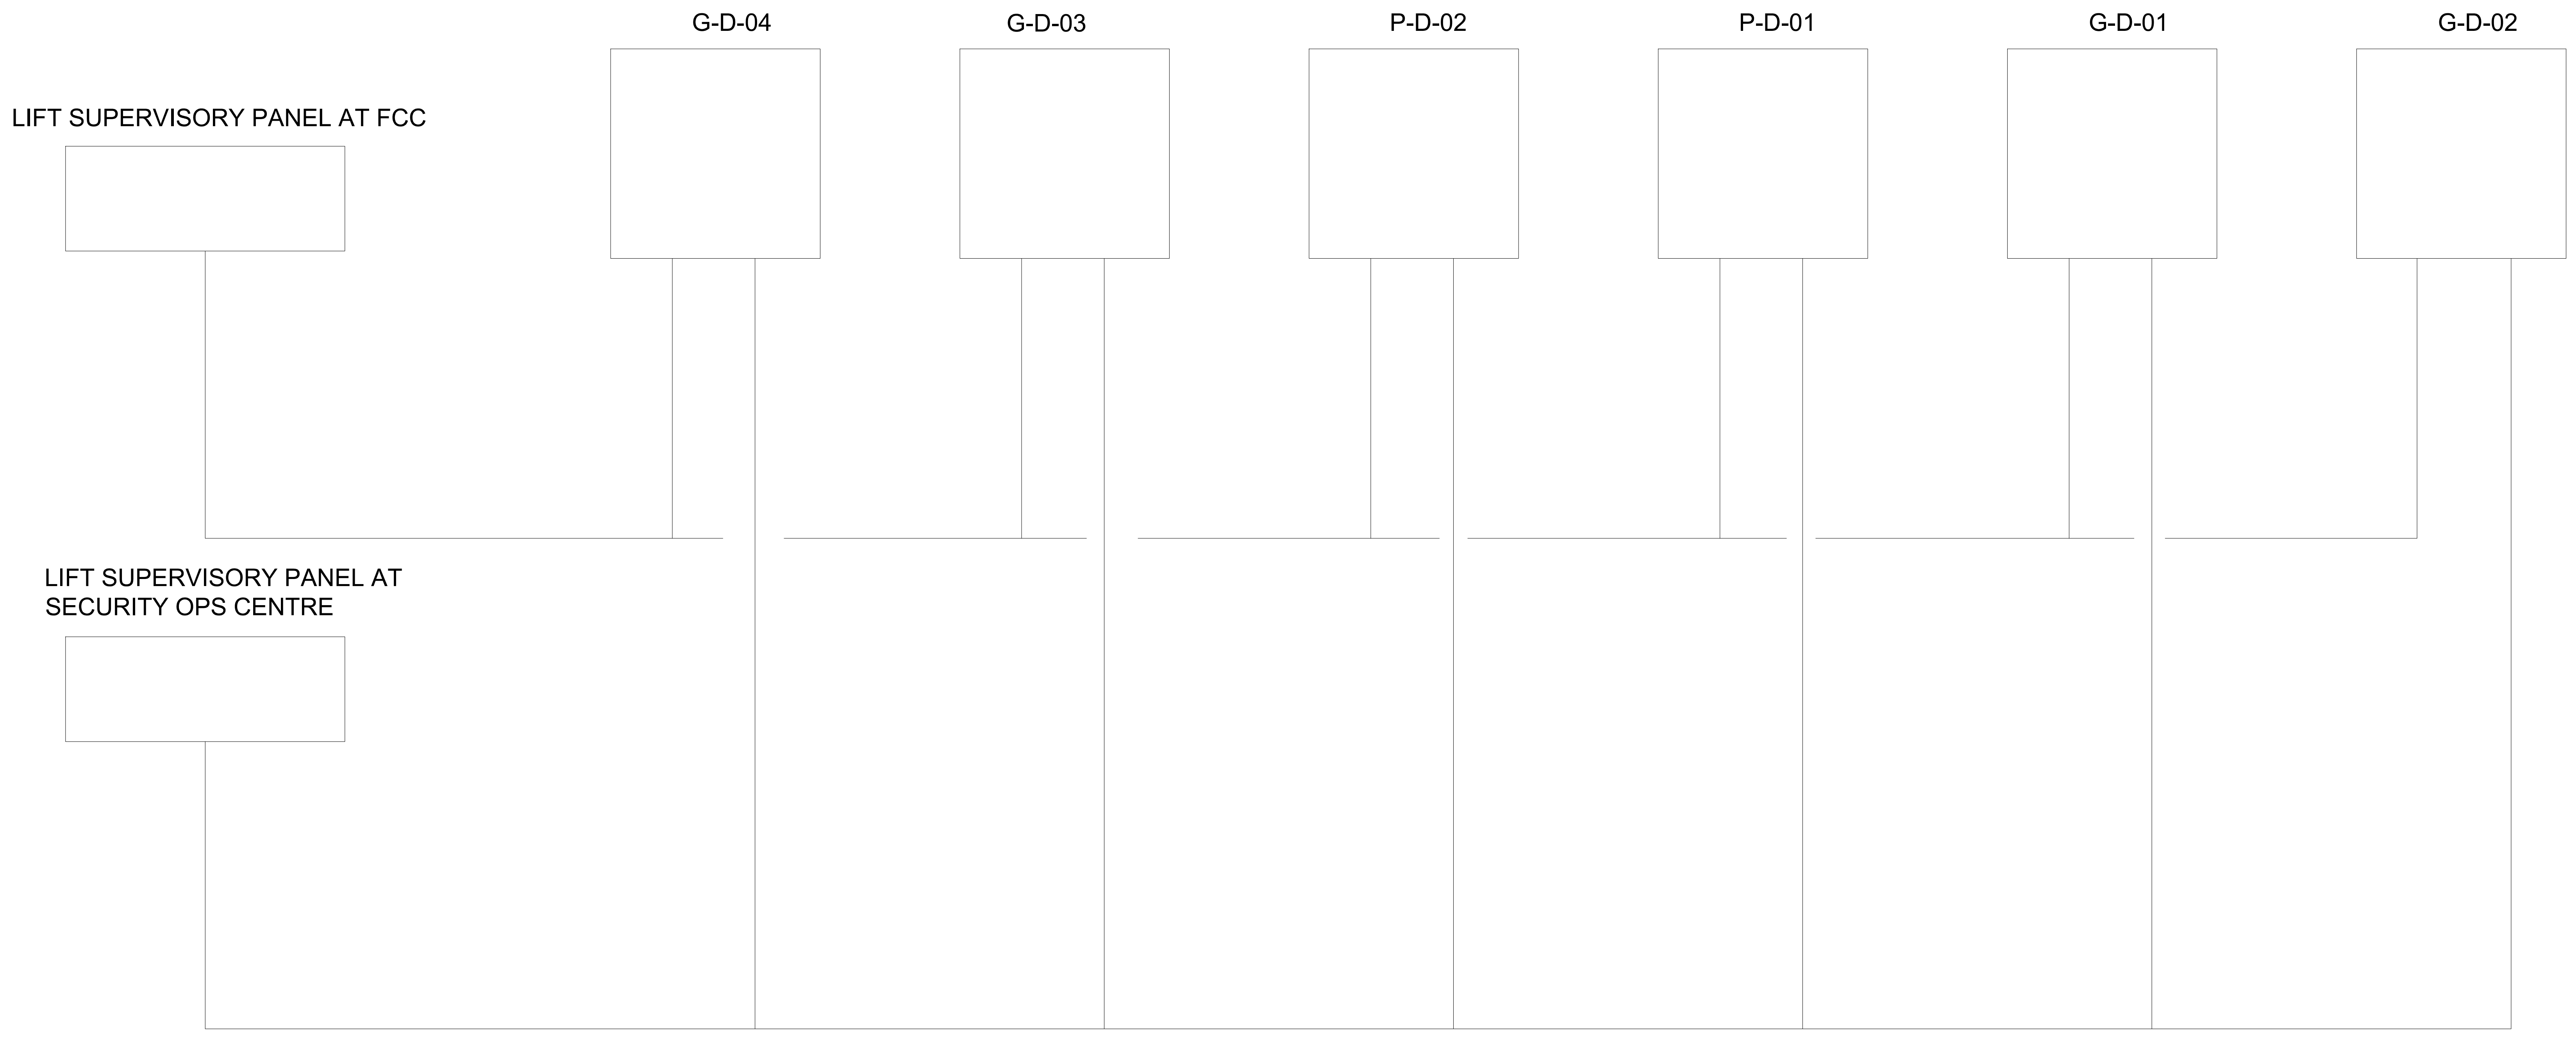

NOTE : THIS PRINT IS OF A CONFIDENTIAL NATURE, IT SHALL NOT BE TRACED,PHOTOGRAPHED,PHOTOSTATED OR REPRODUCED IN ANY MANER,NOR USED FOR ANY PURPOSE WHATSOEVER EXCEPT BY WRITTEN PERMISSION

CLIENT :

GULF EDGE DC 01

87 Wireless Road, M Thai Tower 11th. Floor, All Seasons Place, Lumpini,
Pathumwan, Bangkok 10330, Thailand

CONTRACTOR :

华西发展(泰国)有限公司
บริษัท หัวซือ ดีเวลลอปเม้นต์ (ประเทศไทย) จำกัด
HUASHI DEVELOPMENT CO.,LTD
No. 202, Room No. 1403, 14/F, Le Concorde Building,
Ratchadapisek Road, Huaykhwang Sub-District,
Huaykhwang District, Bangkok Metropolitan 10310.

CONSULTANT :

ARbay
บริษัท เอ อาร์ เบย์ จำกัด
ARbay Company Limited
31 st Floor Bangkok Insurance Building
25 South Sathorn road Thungmahamek
Sathorn Bangkok 10120 THAILAND
T +66 (0) 2286 8199
F +66 (0) 2286 2863
info@arbay.co.th

CONSULTANT :

Qbic Engineers & Architects Co.,Ltd.
8 Soi KALONG 4 SANAMBINNAM ROAD,
THASAI SUB-DISTRICT, MUANG NONTHABURI DISTRICT
, NONTHABURI.
Tel 662-950-4374
Fax 662-580-3231
E-Mail : qbic@qbic.co.th, www.qbic.co.th
QBIC ENGINEERS AND ARCHITECTS CO.,LTD.

CONSULTANT :

MITR
MITR TECHNICAL CONSULTANT CO.,LTD.
1168/8 12th FLOOR, LUMPINI TOWER BUILDING,
RAMA IV RD., THUNGMAHAMEK, SATHORN, BANGKOK 10120, THAILAND
TEL : 0-2679-9079-84
FAX : 0-2679-9085 E-mail: mitr_dd@mitr.com

Architect : SIGNATURE
ประกิต พนานุรัตน์ วสถ. 580
ที่อยู่
251/1 ถ.จารุเมือง แขวงรองเมือง เขตปทุมวัน
กรุงเทพมหานคร โทรศัพท์ 02-286-8199

Structural Engineer : SIGNATURE
วิศวกรผู้ออกแบบโครงสร้าง
ณัฐสม สงวนวงษ์ วย 1423
ที่อยู่
2/1 ซ.รามคำแหง 150 ถ.รามคำแหง
แขวง สะพานสูง เขต สะพานสูง กทม. 10240

Structural Inspector : SIGNATURE
วิศวกรผู้ตรวจสอบโครงสร้าง
โกมล จุฑาภัทร วย 964
ที่อยู่
24/18 ซ.นวมินทร์ 129 ถ. นวมินทร์
แขวง นวลจันทร์ เขต บึงกุ่ม กทม. 10230

Electrical Engineer : SIGNATURE
วิศวกรผู้ออกแบบระบบไฟฟ้ากำลัง
นายสุภัทร บูรณวิทย์ วฟก.1265
ที่อยู่
21 ซอยทานสัมฤทธิ์ 13
ตำบลท่าทราย อ.เมืองนนทบุรี จ.นนทบุรี 11000

Mechanical Engineer : SIGNATURE
วิศวกรผู้ออกแบบระบบเครื่องกลและปรับอากาศ
นายประสิทธิ์ โกยวสุนทร วก.1221
ที่อยู่
44/372 ซอยบางกระดี่ 35/1 แขวงแสมดำ
เขตบางขุนเทียน กทม. 10150
ประสิทธิ์

Sanitary Engineer : SIGNATURE
วิศวกรผู้ออกแบบระบบสุขาภิบาล และดับเพลิง
นายทศวรรษ สนันฤทธิ์ วส. 215
ที่อยู่
บ้านเลขที่ 99/107 หมู่ที่ 3 ต.ศีรษะจรเข้น้อย
อ.บางเสาธง จ.สมุทรปราการ 10540
ทศวรรษ

ISSUE/REVISION

REV.	DESCRIPTION	DATE
A	90% DEVELOPED	09/05/2026

PROJECT NAME :

GEDC 01

LOCATION:
Nikhom Phattana district, Rayong ,industrial estate,CPGC

BUILDING :

90% DEVELOPED

TITLE :

VERTICAL TRANSPORTATION SYSTEM SCHEMATIC

JOB NO.	SCALE 1:50
DRAWN LW	REF.
CHECKED LJC	DWG.NO.
APPROVED LXD	MPK00-90-VT-SC-002
DATE 2026.05.09	