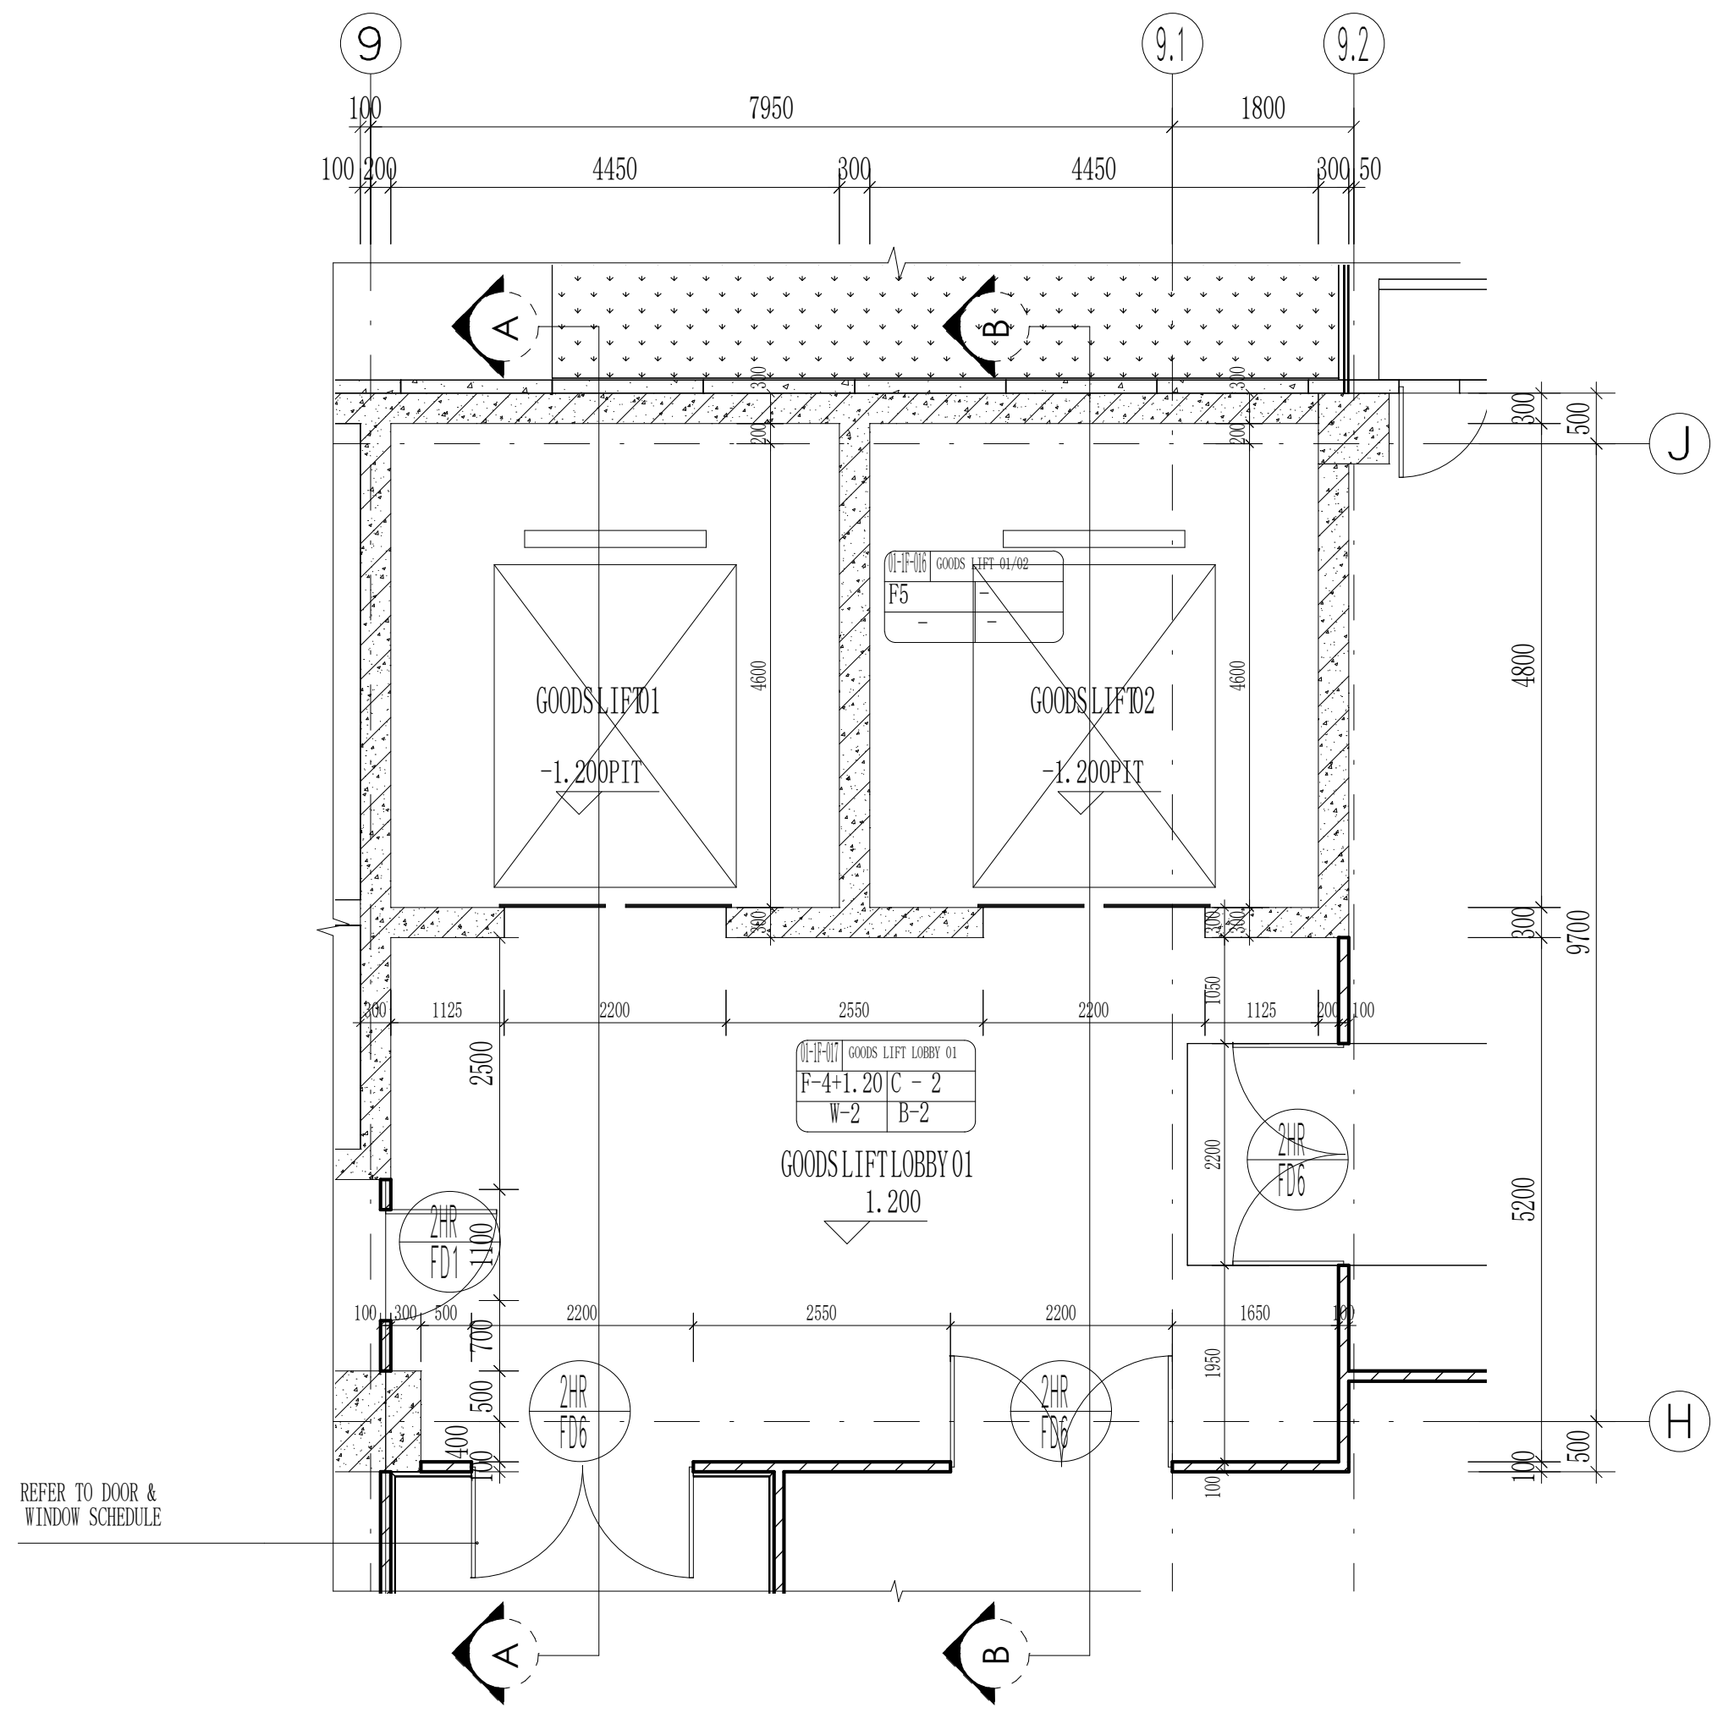

GOODS LIFT 01-02
GROUND FL
SCALE 1:75

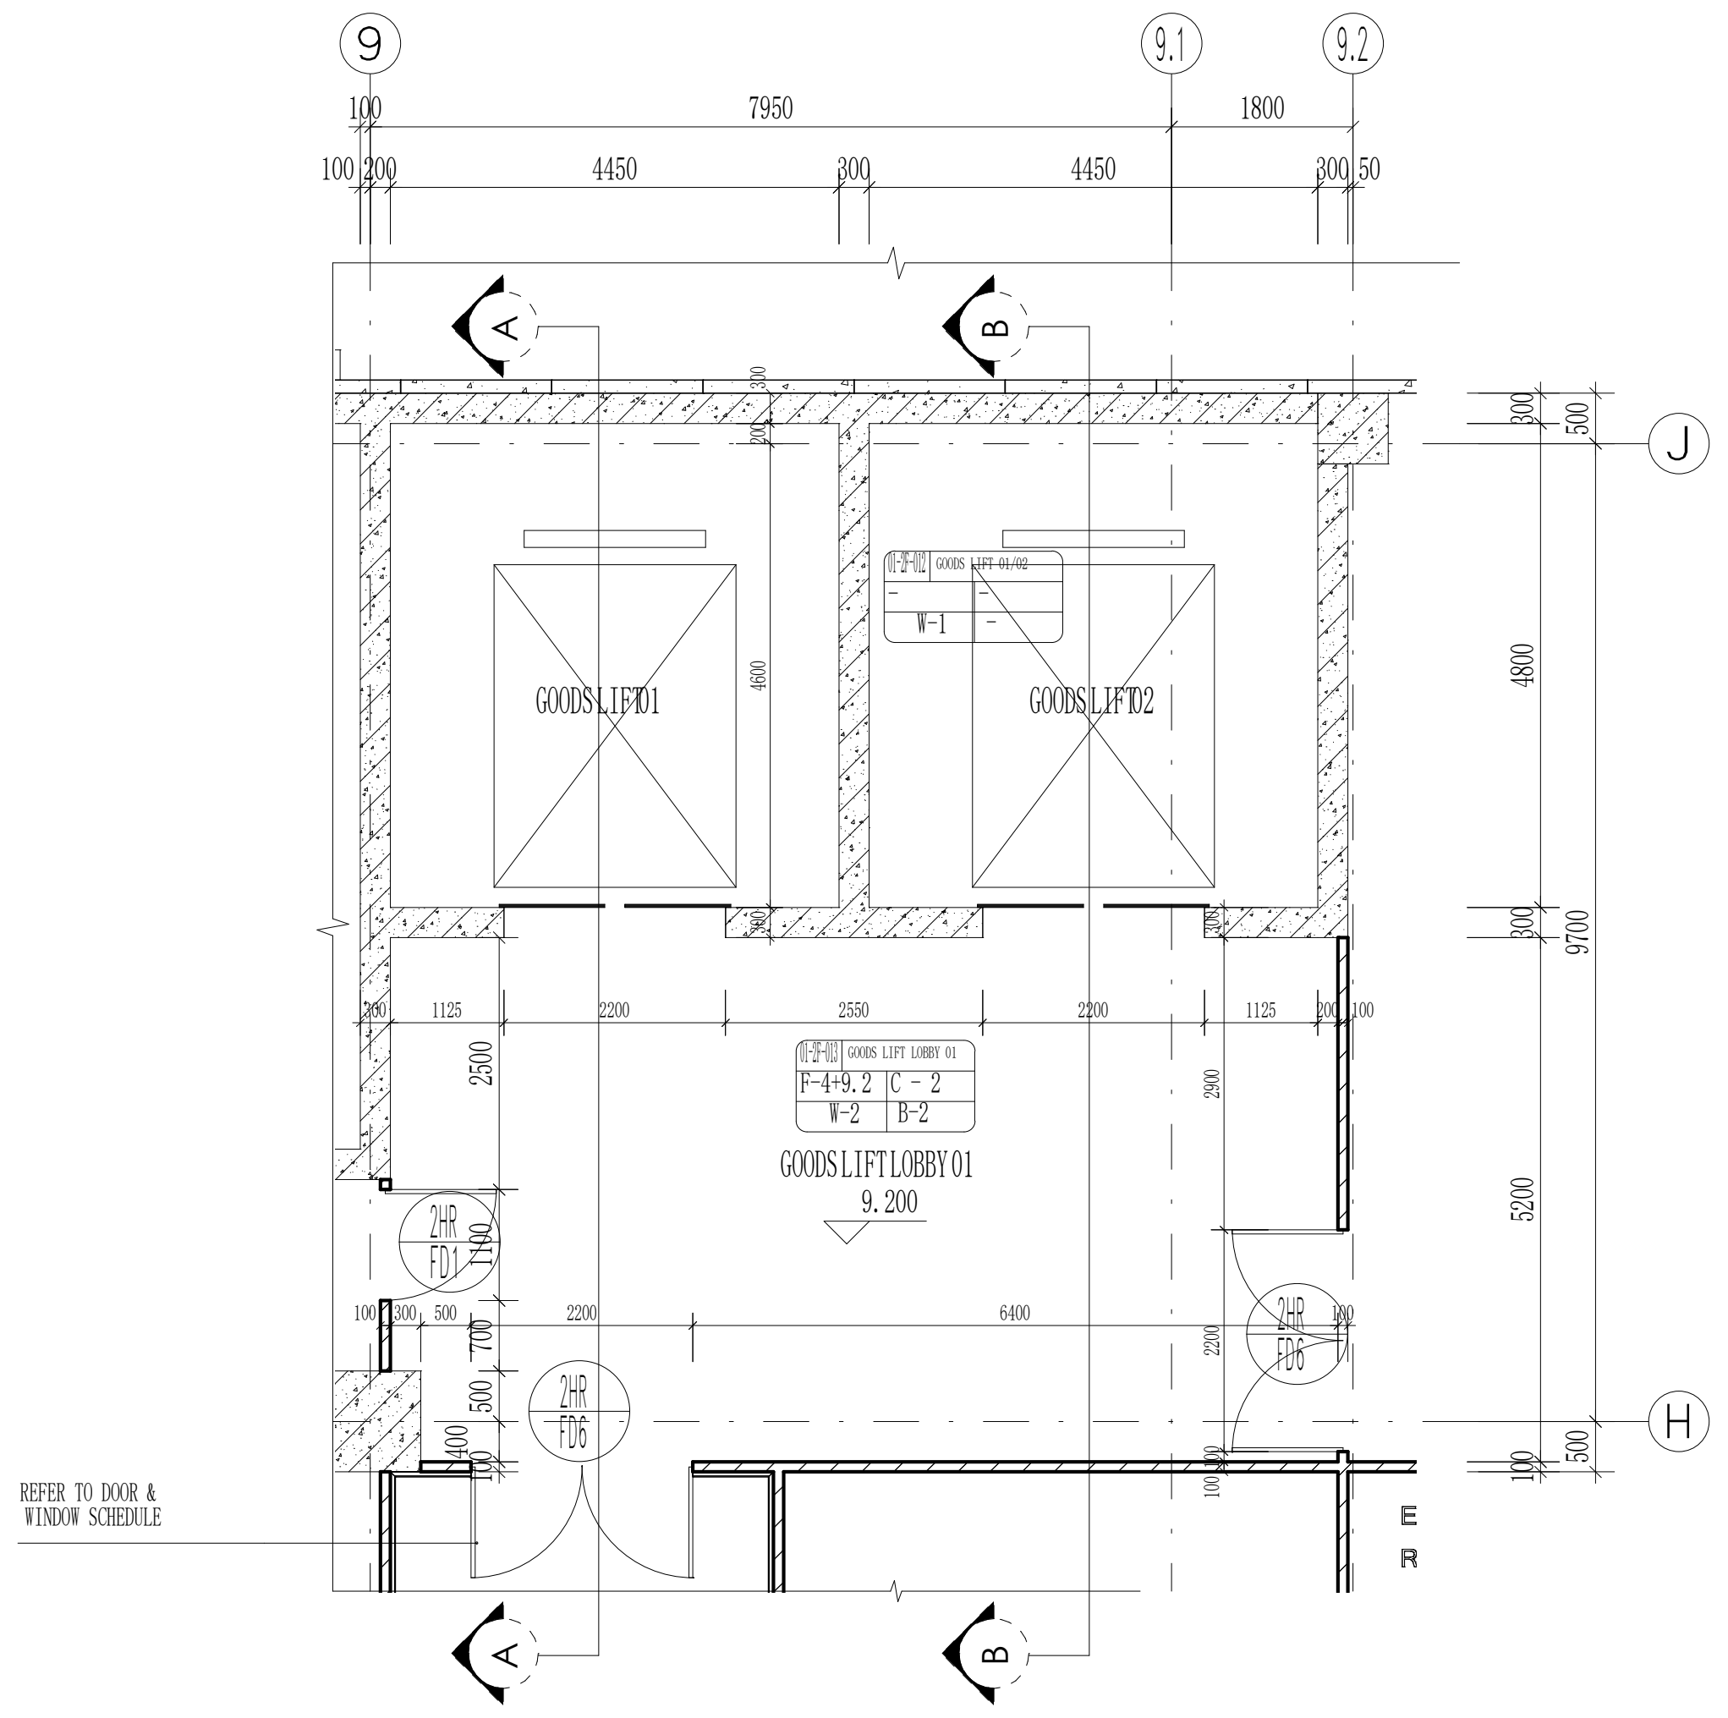

GOODS LIFT 01-02 2ND
FL
SCALE 1:75

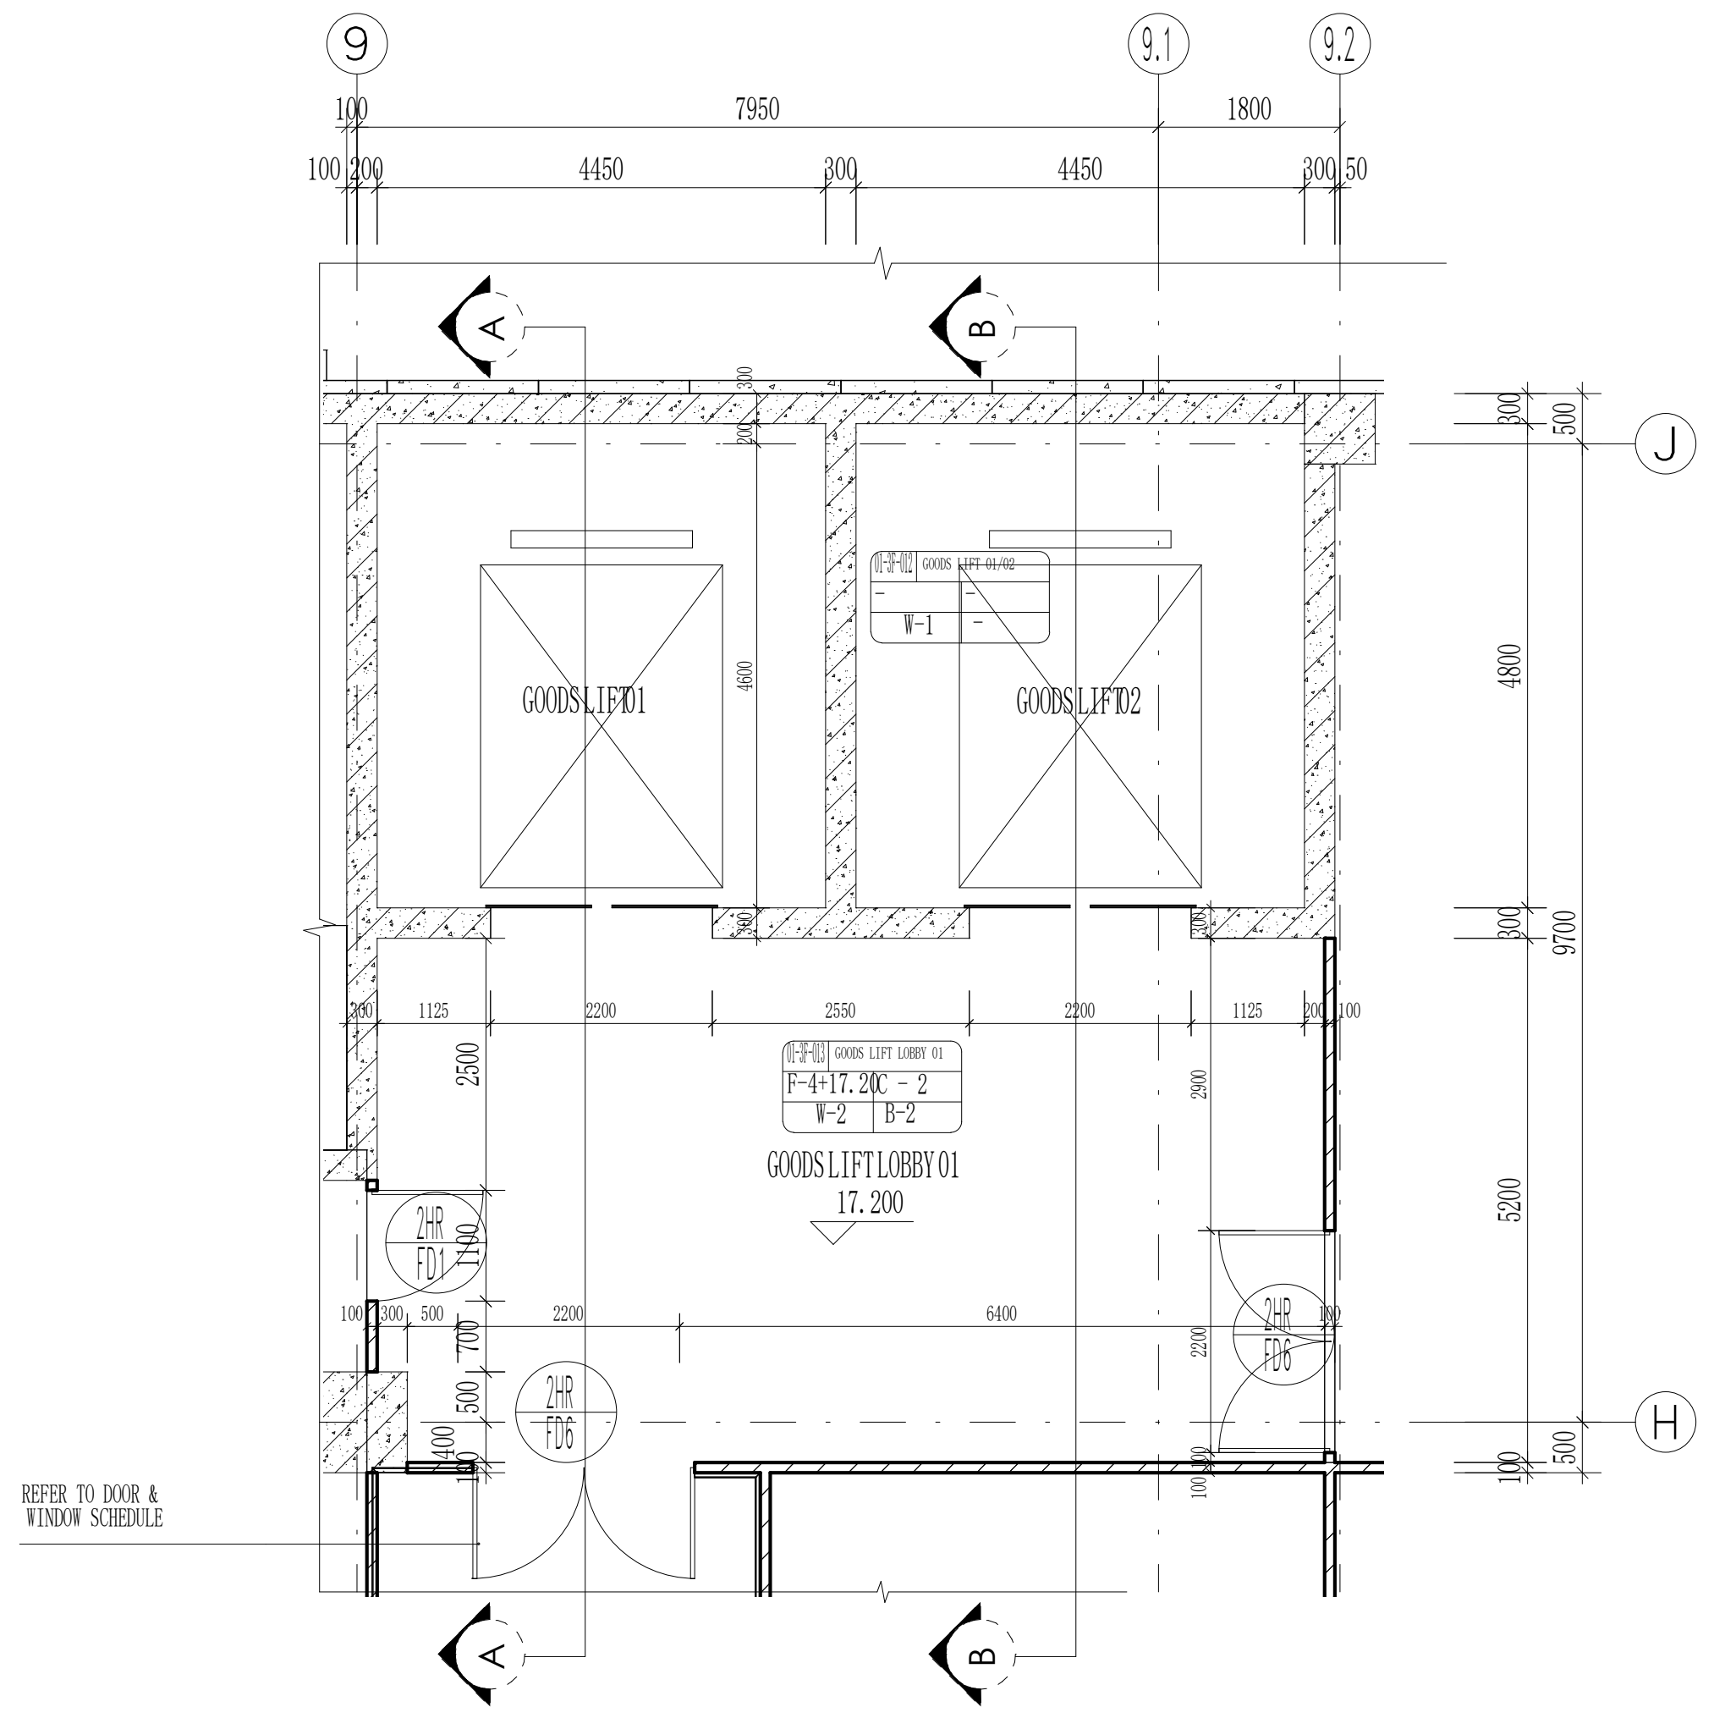

GOODS LIFT 01-02 3RD
FL
SCALE 1:75

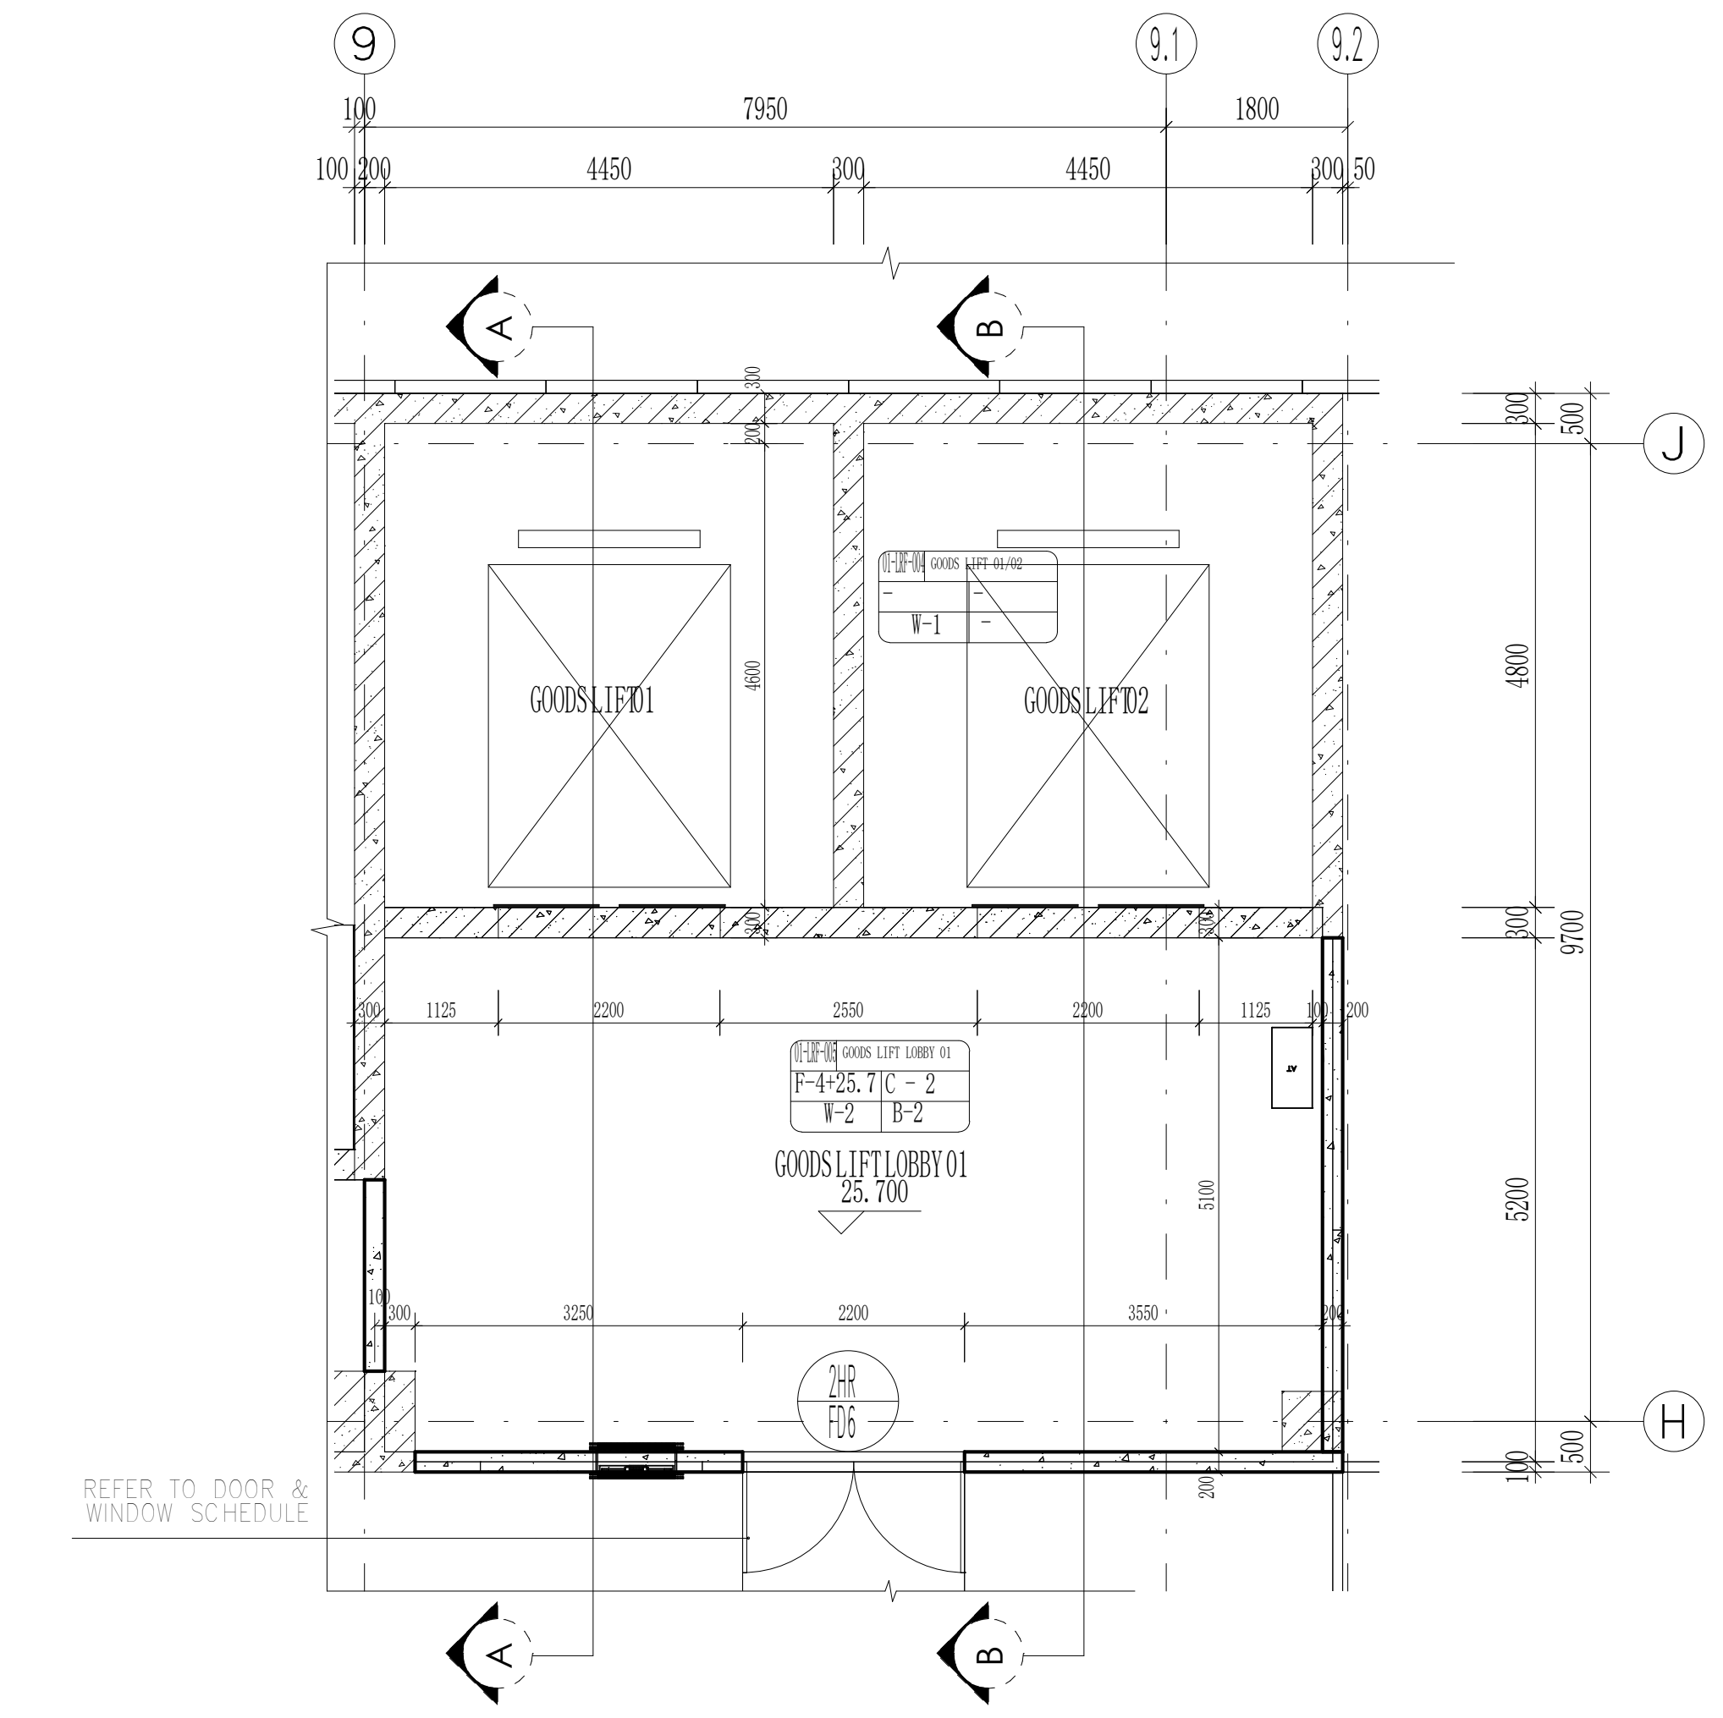

GOODS LIFT 01-02 ROOF
FL
SCALE 1:75

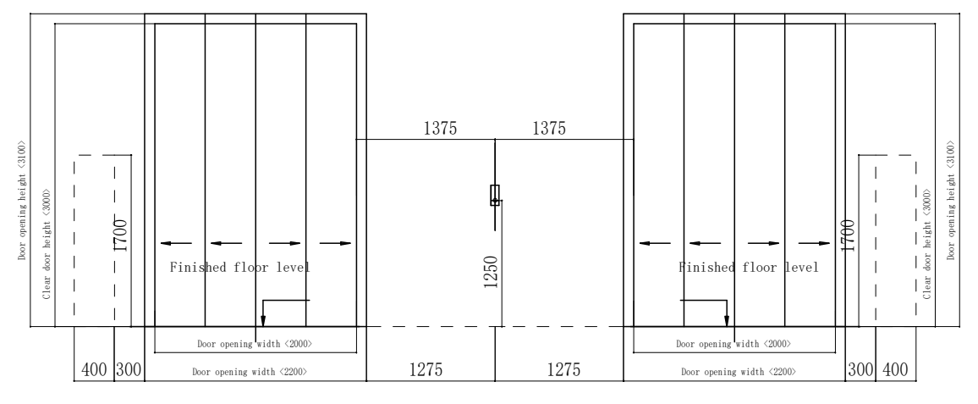
1375
1375
1700
1250
Finished floor level
Door opening height <3100>
Clear door height <3000>
Door opening width <2000>
Door opening width <2200>
400
300
1275
1275

FOR LANDING
CALL Scale 1:75

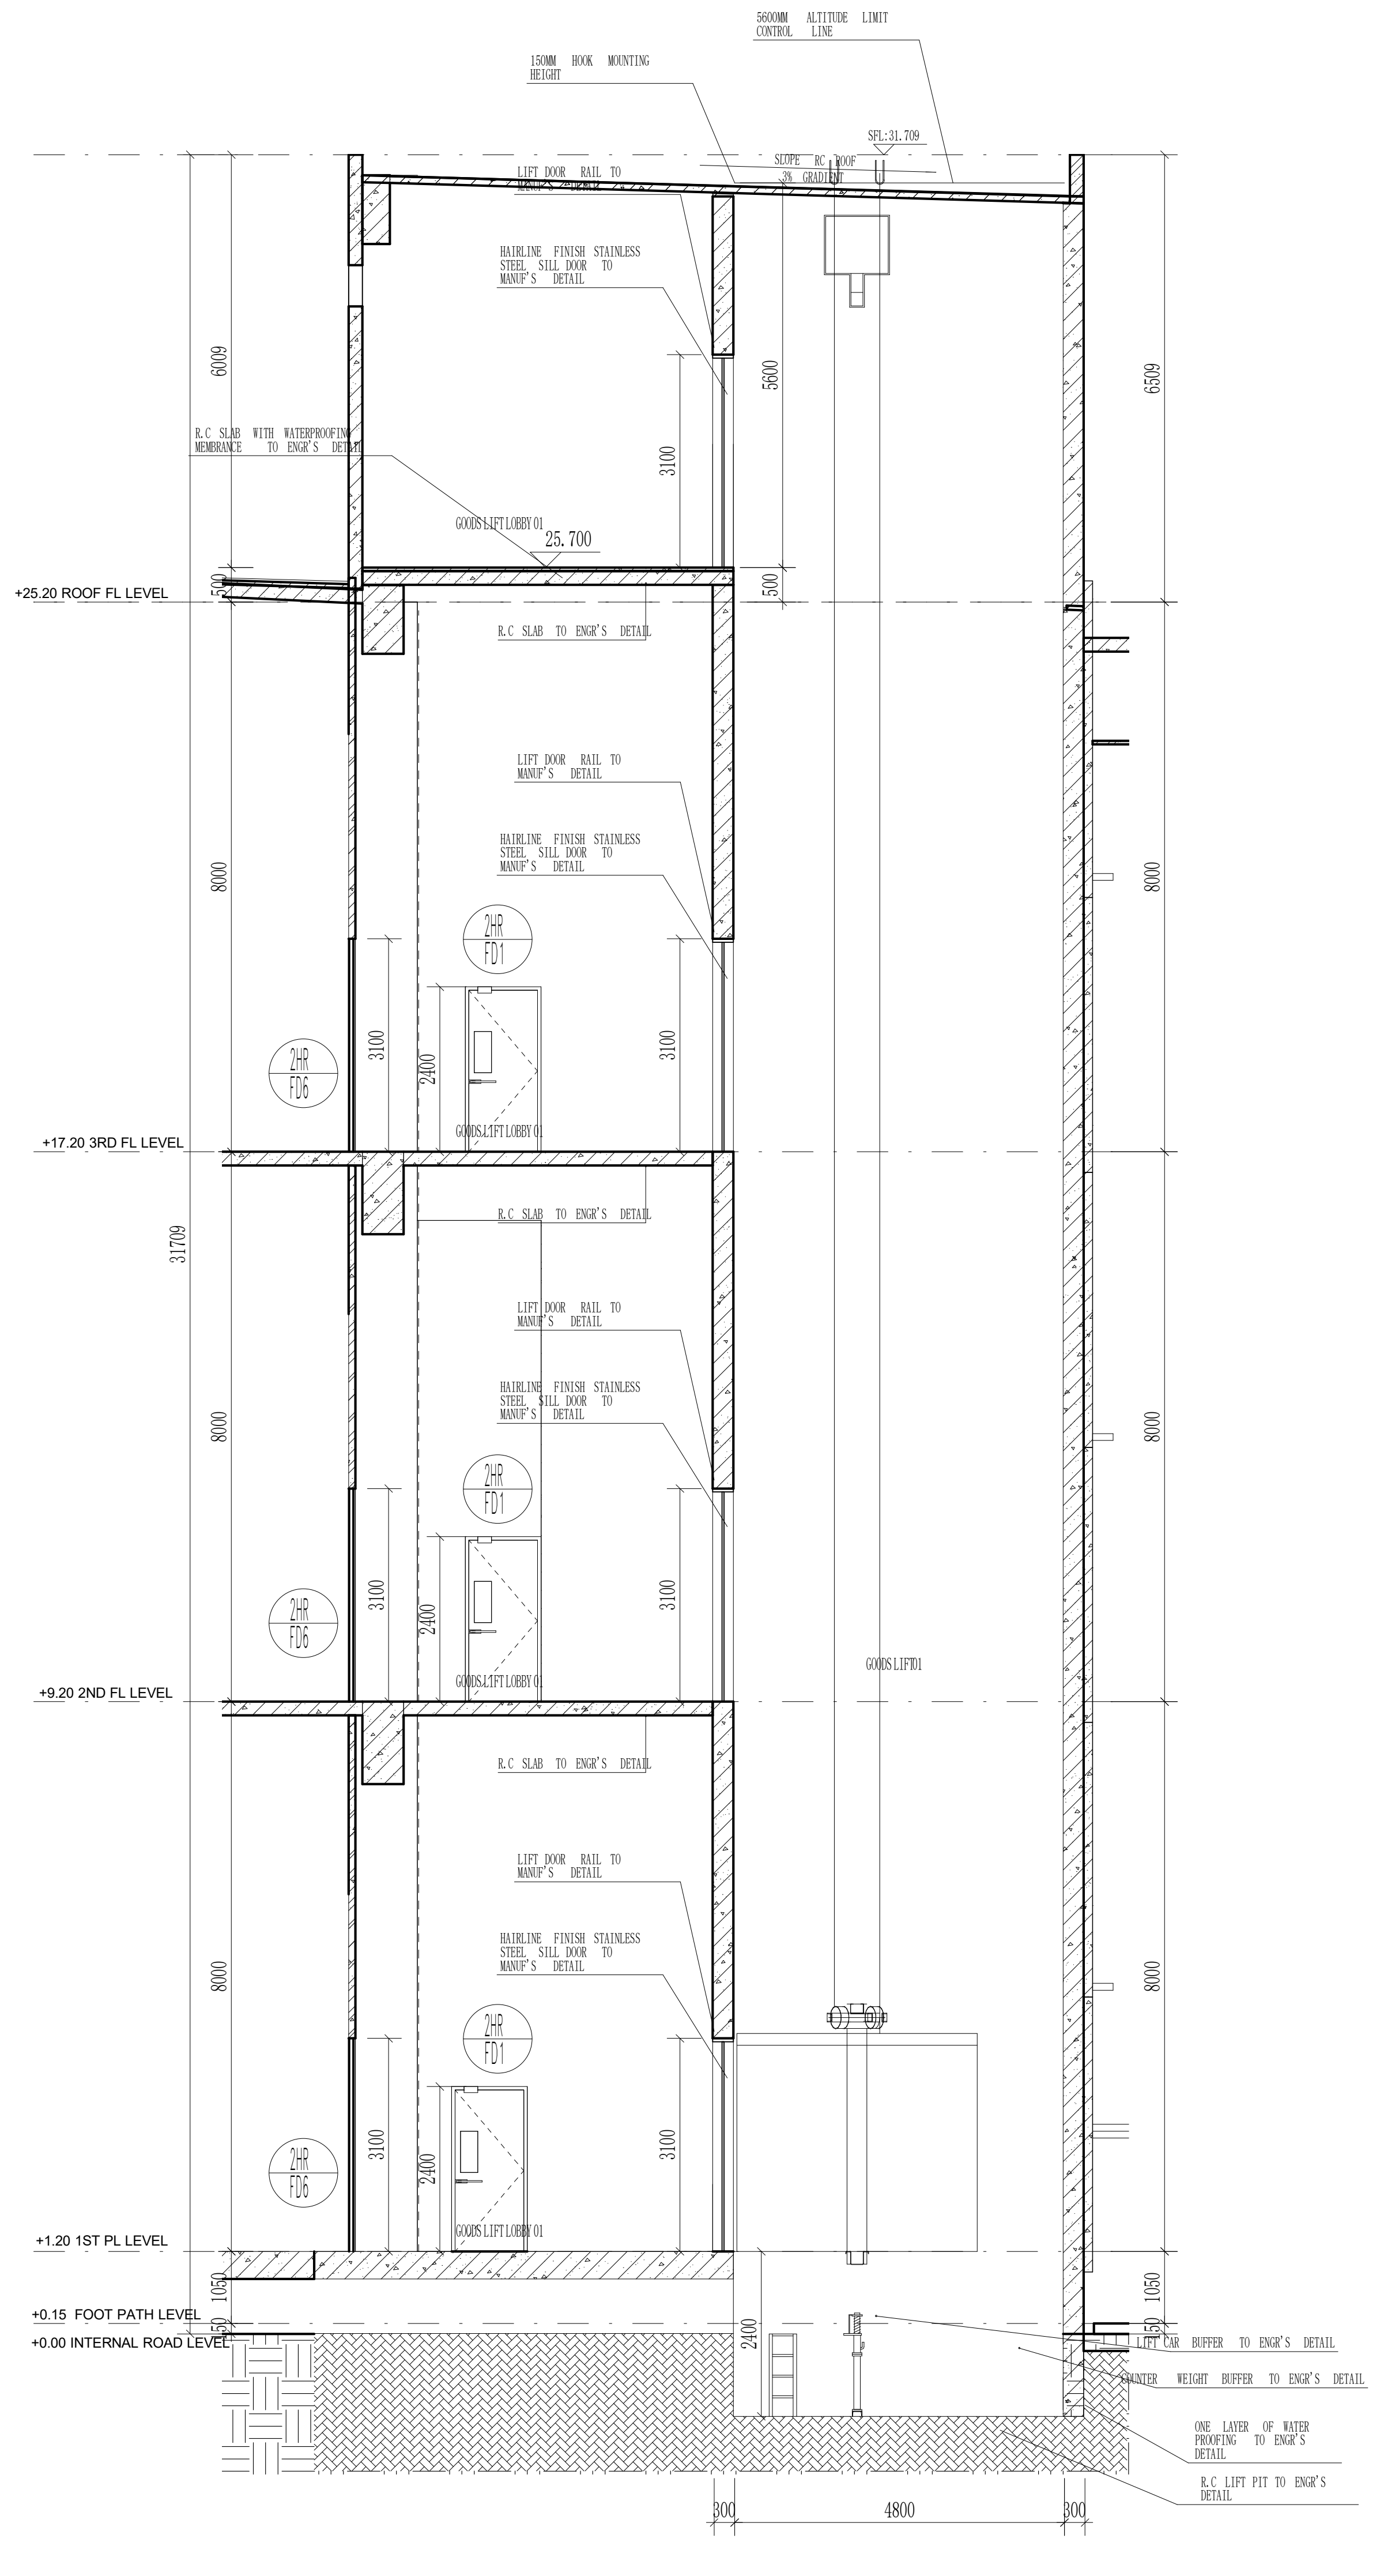
5600MM ALTITUDE LIMIT CONTROL LINE
150MM HOOK MOUNTING HEIGHT
SFL:31.709
SLOPE RC ROOF 3% GRADIENT
LIFT DOOR RAIL TO MANUF'S DETAIL
HAIRLINE FINISH STAINLESS STEEL SILL DOOR TO MANUF'S DETAIL
R.C SLAB WITH WATERPROOFING MEMBRANCE TO ENGR'S DETAIL
GOODS LIFT LOBBY 01
25.700
R.C SLAB TO ENGR'S DETAIL
2HR FD1
2HR FD6
GOODS LIFT 01
+25.20 ROOF FL LEVEL
+17.20 3RD FL LEVEL
+9.20 2ND FL LEVEL
+1.20 1ST PL LEVEL
+0.15 FOOT PATH LEVEL
+0.00 INTERNAL ROAD LEVEL
LIFT CAR BUFFER TO ENGR'S DETAIL
COUNTER WEIGHT BUFFER TO ENGR'S DETAIL
ONE LAYER OF WATER PROOFING TO ENGR'S DETAIL
R.C LIFT PIT TO ENGR'S DETAIL
6009
6509
5600
3100
2400
500
8000
31709
1050
150
300
4800
J
H

Section A
SCALE 1:75

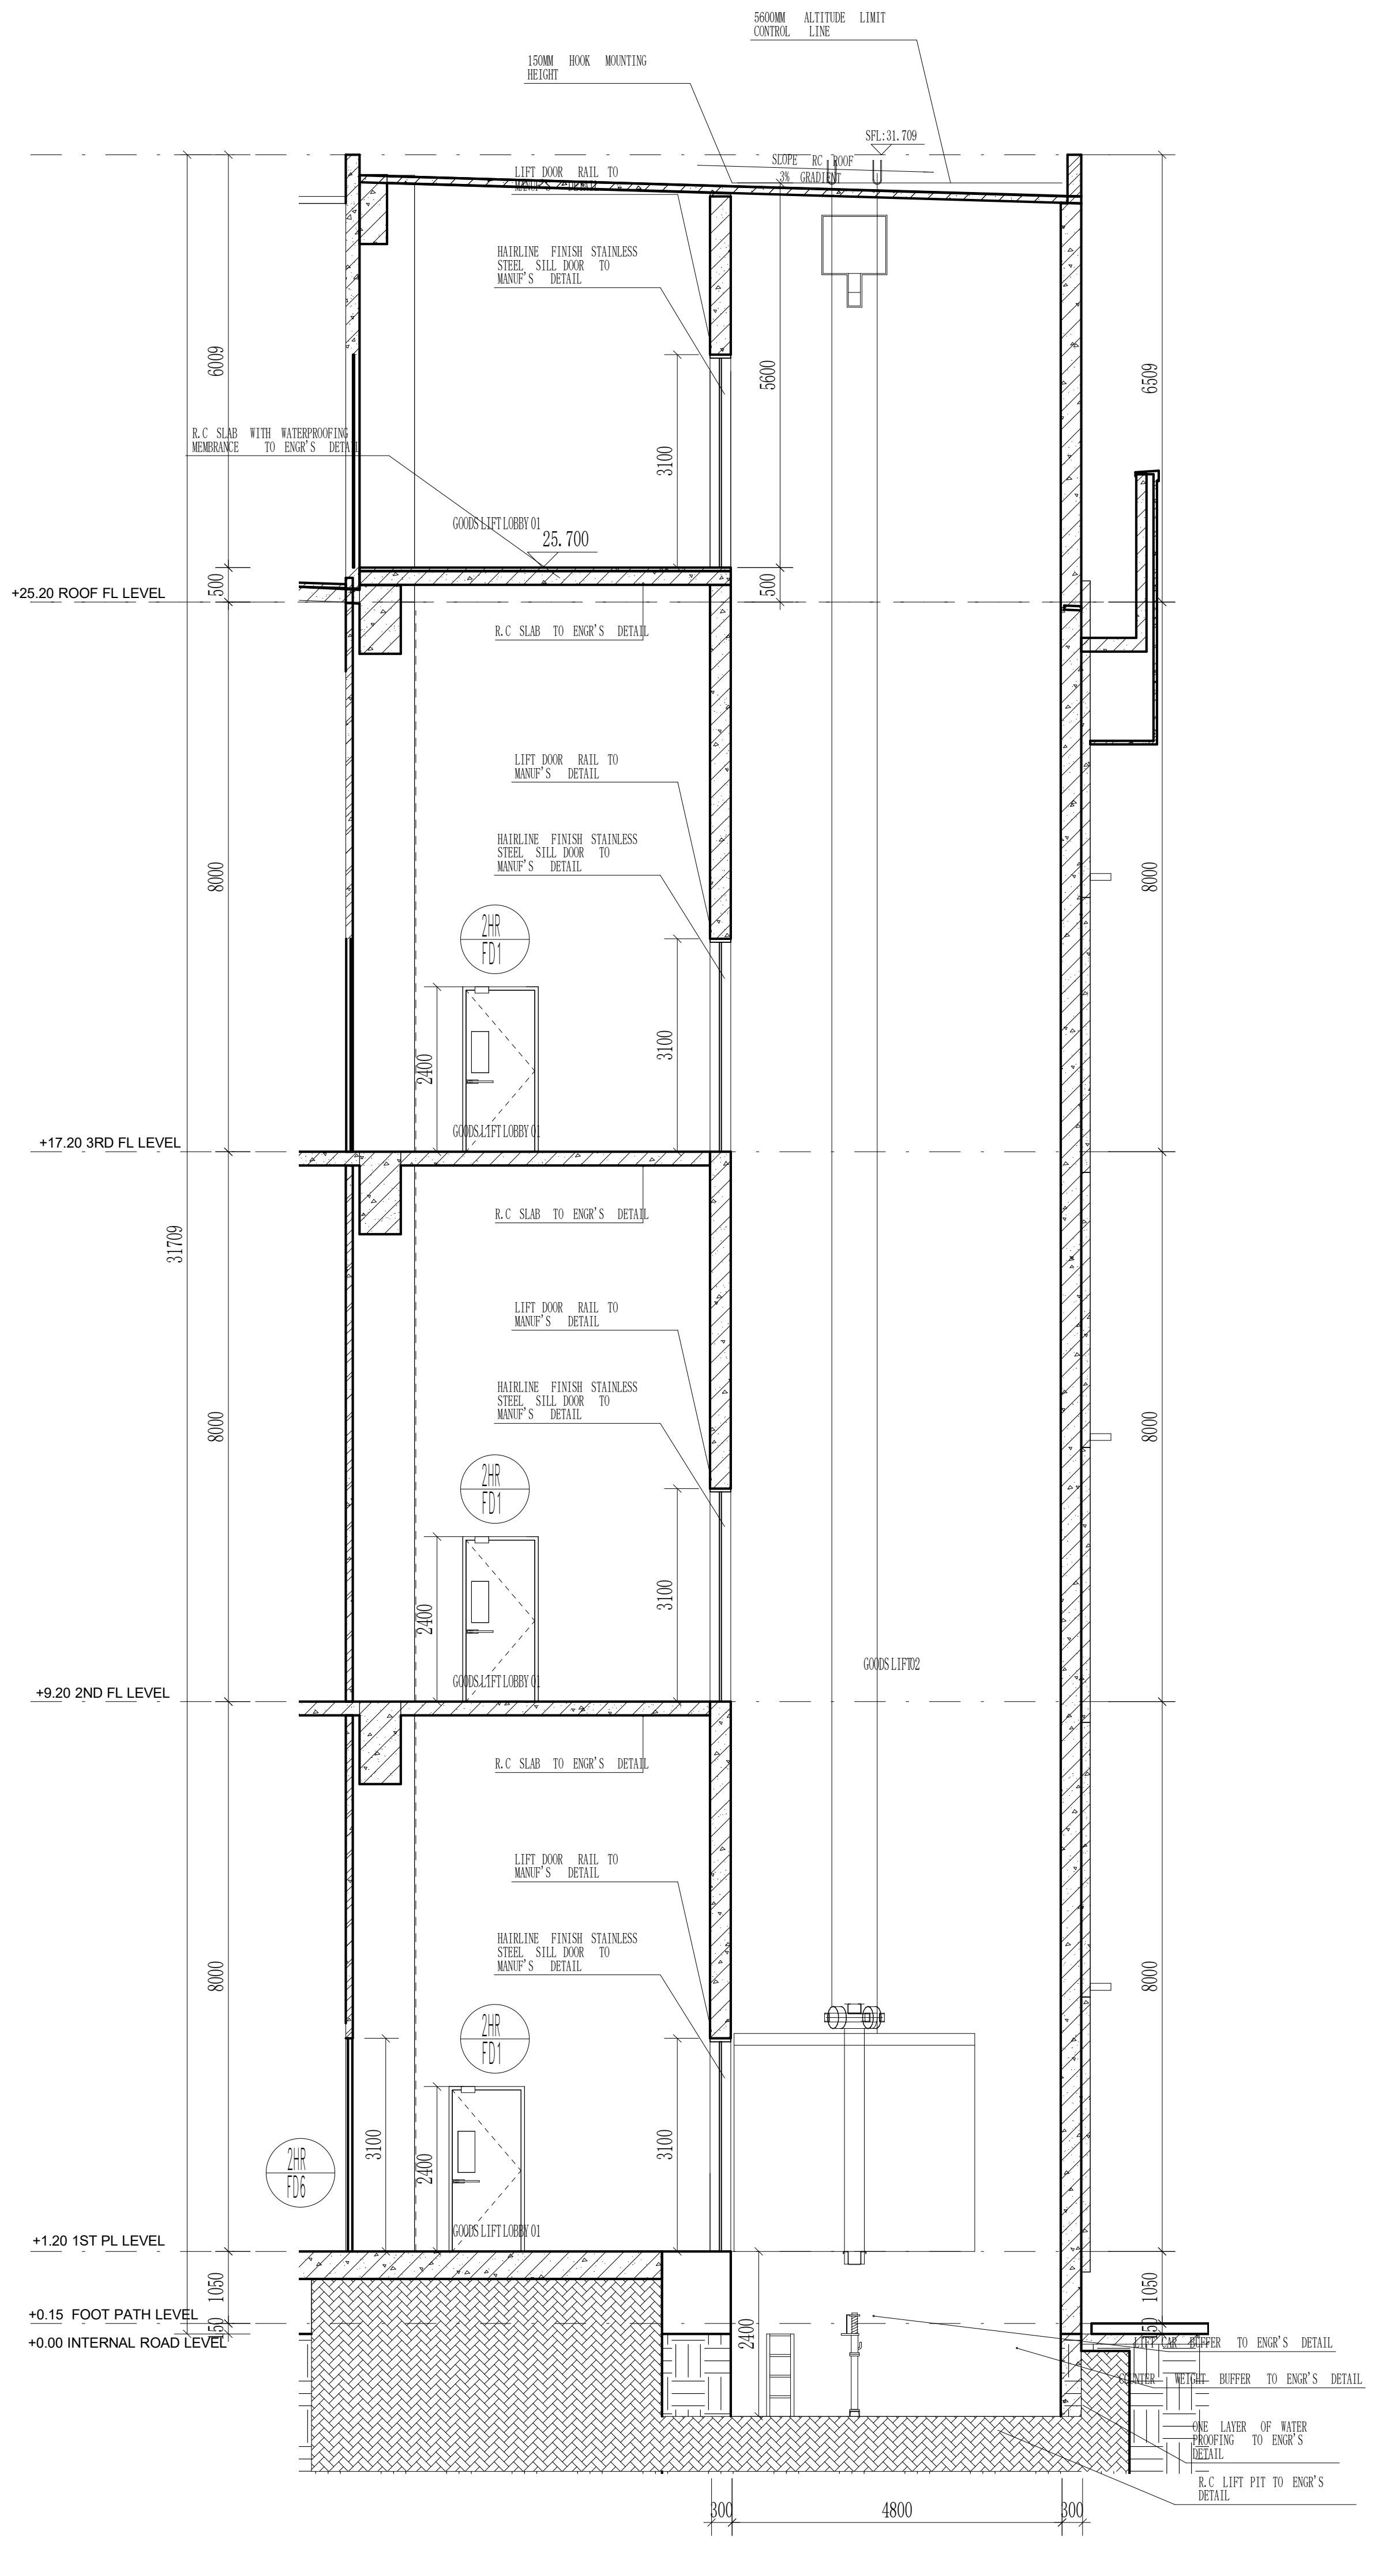
5600MM ALTITUDE LIMIT CONTROL LINE
150MM HOOK MOUNTING HEIGHT
SFL:31.709
LIFT DOOR RAIL TO MANUF'S DETAIL
HAIRLINE FINISH STAINLESS STEEL SILL DOOR TO MANUF'S DETAIL
R.C SLAB WITH WATERPROOFING MEMBRANCE TO ENGR'S DETAIL
GOODS LIFT LOBBY 01
25.700
R.C SLAB TO ENGR'S DETAIL
GOODS LIFT 02
+25.20 ROOF FL LEVEL
+17.20 3RD FL LEVEL
+9.20 2ND FL LEVEL
+1.20 1ST PL LEVEL
+0.15 FOOT PATH LEVEL
+0.00 INTERNAL ROAD LEVEL
LIFT CAR BUFFER TO ENGR'S DETAIL
COUNTER WEIGHT BUFFER TO ENGR'S DETAIL
ONE LAYER OF WATER PROOFING TO ENGR'S DETAIL
R.C LIFT PIT TO ENGR'S DETAIL
6009
6509
8000
31709
300
4800

Section B
SCALE 1:75

CLIENT :

GULF EDGE DC 01

87 Wireless Road, M Thai Tower 11th. Floor, All Seasons Place, Lumpini,
Pathumwan, Bangkok 10330, Thailand

CONTRACTOR :

华西发展(泰国)有限公司
บริษัท หัวซือ ดีเวลลอปเม้นต์ (ประเทศไทย) จำกัด
HUASHI DEVELOPMENT CO.,LTD
No. 202, Room No. 1403, 14/F, Le Concorde Building,
Ratchadapisek Road, Huaykhwang Sub-District,
Huaykhwang District, Bangkok Metropolitan 10310.

CONSULTANT :

ARbay
บริษัท เอ อาร์ เบย์ จำกัด
ARbay Company Limited
31 st Floor Bangkok Insurance Building
25 South Sathorn road Thungmahamek
Sathorn Bangkok 10120 THAILAND
T +66 (0) 2286 8199
F +66 (0) 2286 2863
info@arbay.co.th

CONSULTANT :

Qbic Engineers & Architects Co.,Ltd.
8 Soi KALONG 4 SANAMBINNAM ROAD,
THASAI SUB-DISTRICT, MUANG NONTHABURI DISTRICT
, NONTHABURI.
Tel 662-950-4374
Fax 662-580-3231
E-Mail : qbic@qbic.co.th, www.qbic.co.th
QBIC ENGINEERS AND ARCHITECTS CO.,LTD.

CONSULTANT :

MITR
MITR TECHNICAL CONSULTANT CO.,LTD.
1168/8 12th FLOOR, LUMPINI TOWER BUILDING,
RAMA IV RD., THUNGMAHAMEK, SATHORN, BANGKOK 10120, THAILAND
TEL : 0-2679-9079-84
FAX : 0-2679-9085 E-mail: mitr_dd@mitr.com

Architect : SIGNATURE
ประกิต พนานุรัตน์ วสถ. 580
ที่อยู่
251/1 ถ.จารุเมือง แขวงรองเมือง เขตปทุมวัน
กรุงเทพมหานคร โทรศัพท์ 02-286-8199

Structural Engineer : SIGNATURE
วิศวกรผู้ออกแบบโครงสร้าง
ณัฐสม สงวนวงษ์ วย 1423
ที่อยู่
2/1 ซ.รามคำแหง 150 ถ.รามคำแหง
แขวง สะพานสูง เขต สะพานสูง กทม. 10240
ณัฐสม สงวนวงษ์

Structural Inspector : SIGNATURE
วิศวกรผู้ตรวจสอบโครงสร้าง
โกมล จุฑาภัทร วย 964
ที่อยู่
24/18 ซ.นวมินทร์ 129 ถ. นวมินทร์
แขวง นวลจันทร์ เขต บึงกุ่ม กทม. 10230

Electrical Engineer : SIGNATURE
วิศวกรผู้ออกแบบระบบไฟฟ้ากำลัง
นายสุภัทร บูรณวิทย์ วฟก.1265
ที่อยู่
21 ซอยทานสัมฤทธิ์ 13
ตำบลท่าทราย อ.เมืองนนทบุรี จ.นนทบุรี 11000

Mechanical Engineer : SIGNATURE
วิศวกรผู้ออกแบบระบบเครื่องกลและปรับอากาศ
นายประสิทธิ์ เกี้ยวสุนทร วก.1221
ที่อยู่
44/372 ซอยบางกระดี่ 35/1 แขวงแสมดำ
เขตบางขุนเทียน กทม. 10150
ประสิทธิ์

Sanitary Engineer : SIGNATURE
วิศวกรผู้ออกแบบระบบสุขาภิบาล และดับเพลิง
นายทศวรรษ สนั่นฤทธิ์ วส. 215
ที่อยู่
บ้านเลขที่ 99/107 หมู่ที่ 3 ต.ศีรษะจรเข้น้อย
อ.บางเสาธง จ.สมุทรปราการ 10540
ทศวรรษ

ISSUE/REVISION

REV.	DESCRIPTION	DATE
A	90% DEVELOPED	09/05/2026

PROJECT NAME :
GEDC 01
LOCATION:
Nikhom Phattana district, Rayong ,industrial estate,CPGC

BUILDING :
MAIN BUILDING

90% DEVELOPED

TITLE :
GOODS LIFT 01-02

JOB NO.
SCALE 1 : 75
DRAWN LW
REF.
CHECKED LJC
DWG. NO. MPK01A-90-VT-LT-001
APPROVED LXD
DATE 2026.05.09

NOTE :THIS PRINT IS OF A CONFIDENTIAL NATURE, IT SHALL NOT BE TRACED,PHOTOGRAPHED,PHOTOSTATED OR REPRODUCED IN ANY MANER,NOR USED FOR ANY PURPOSE WHATSOEVER EXCEPT BY WRITTEN PERMISSION