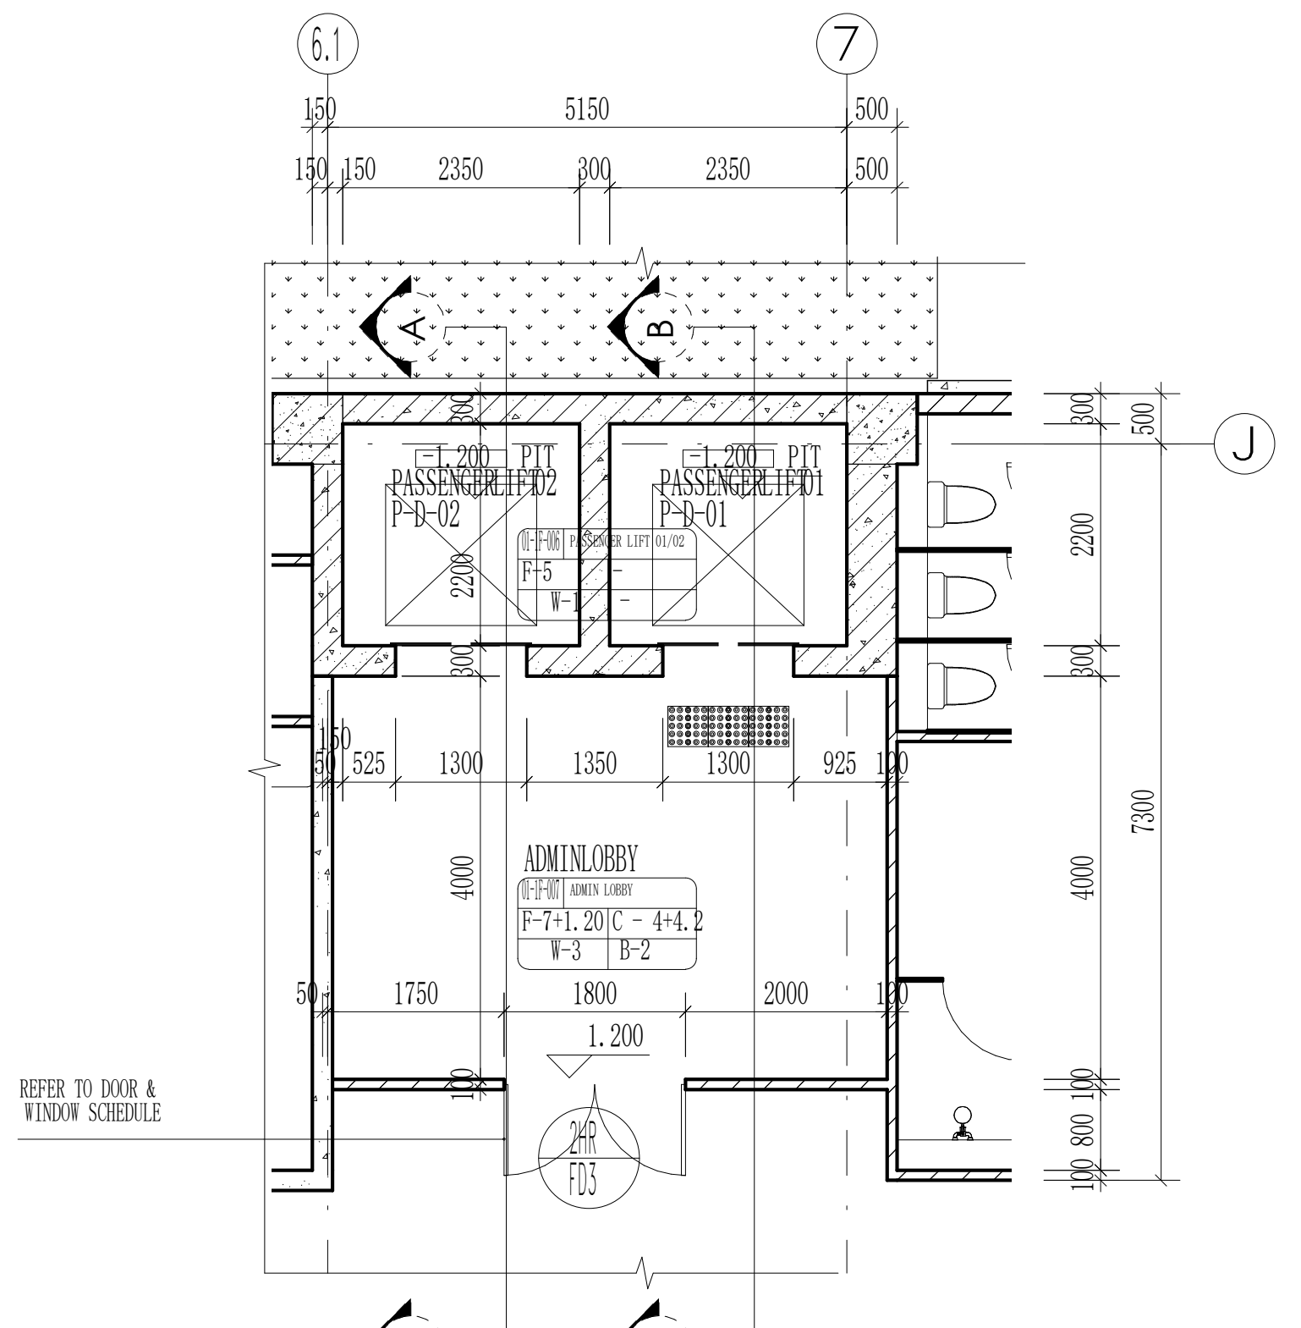

PASSAGER LIFT GROUND FL

SCALE 1:75

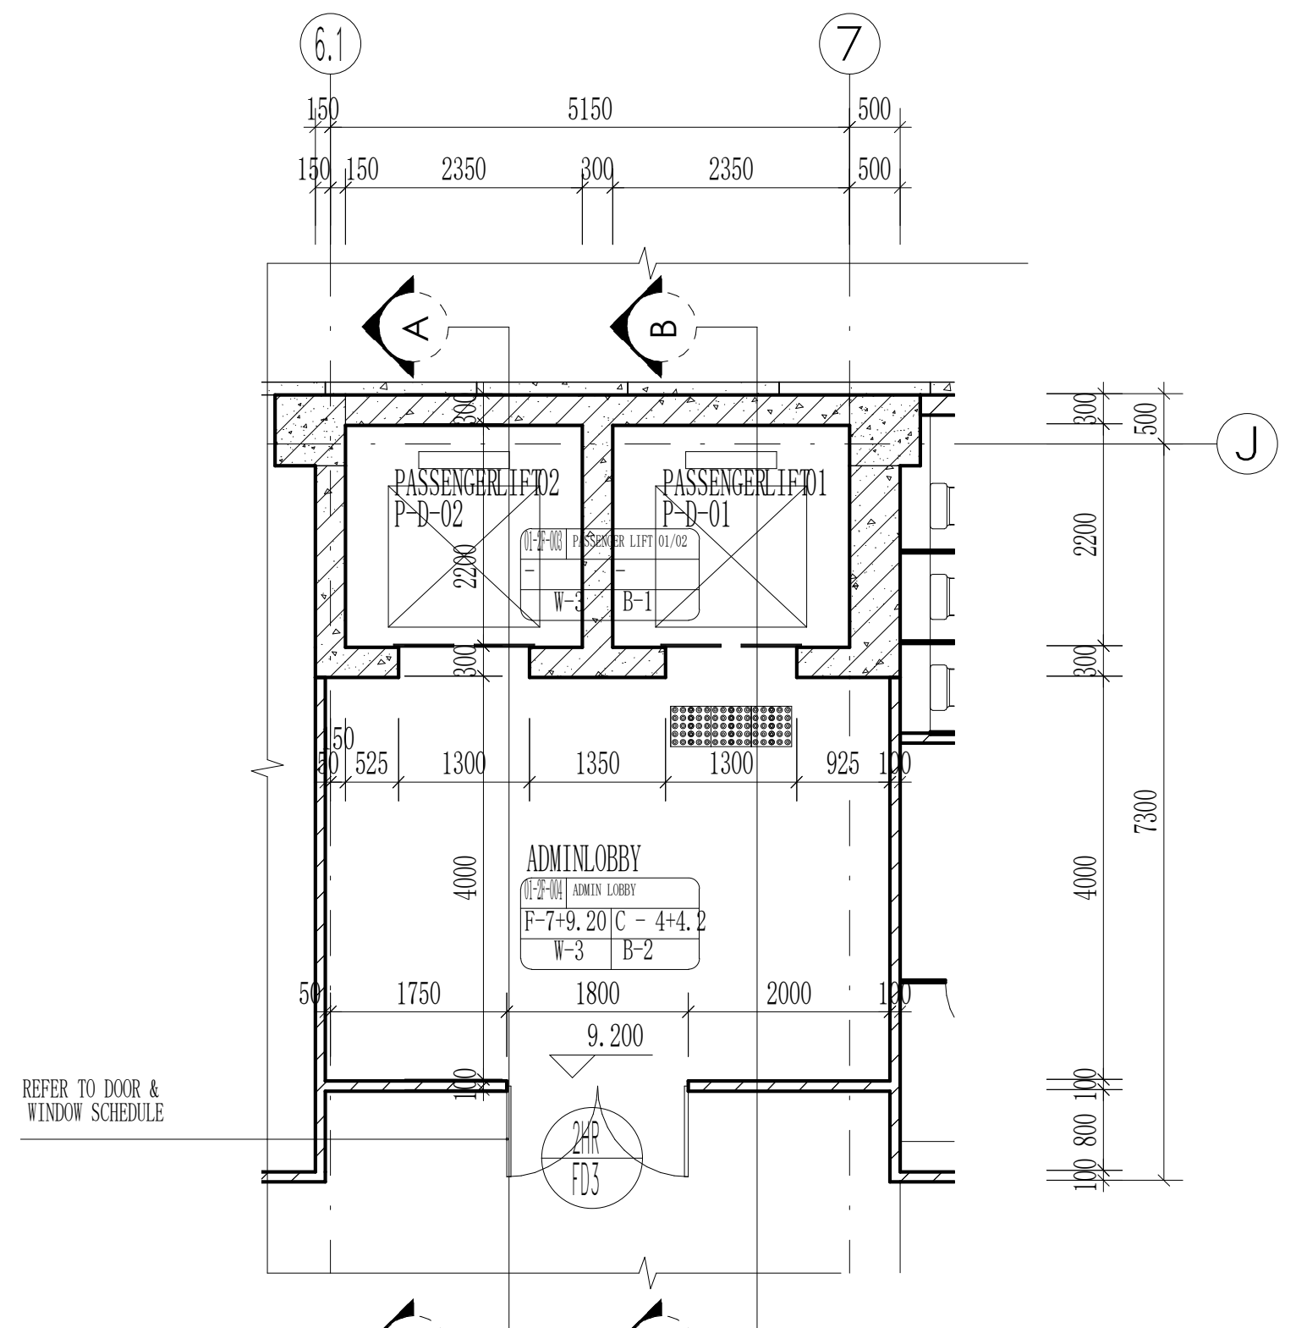

PASSAGER LIFT 2ND FL

SCALE 1:75

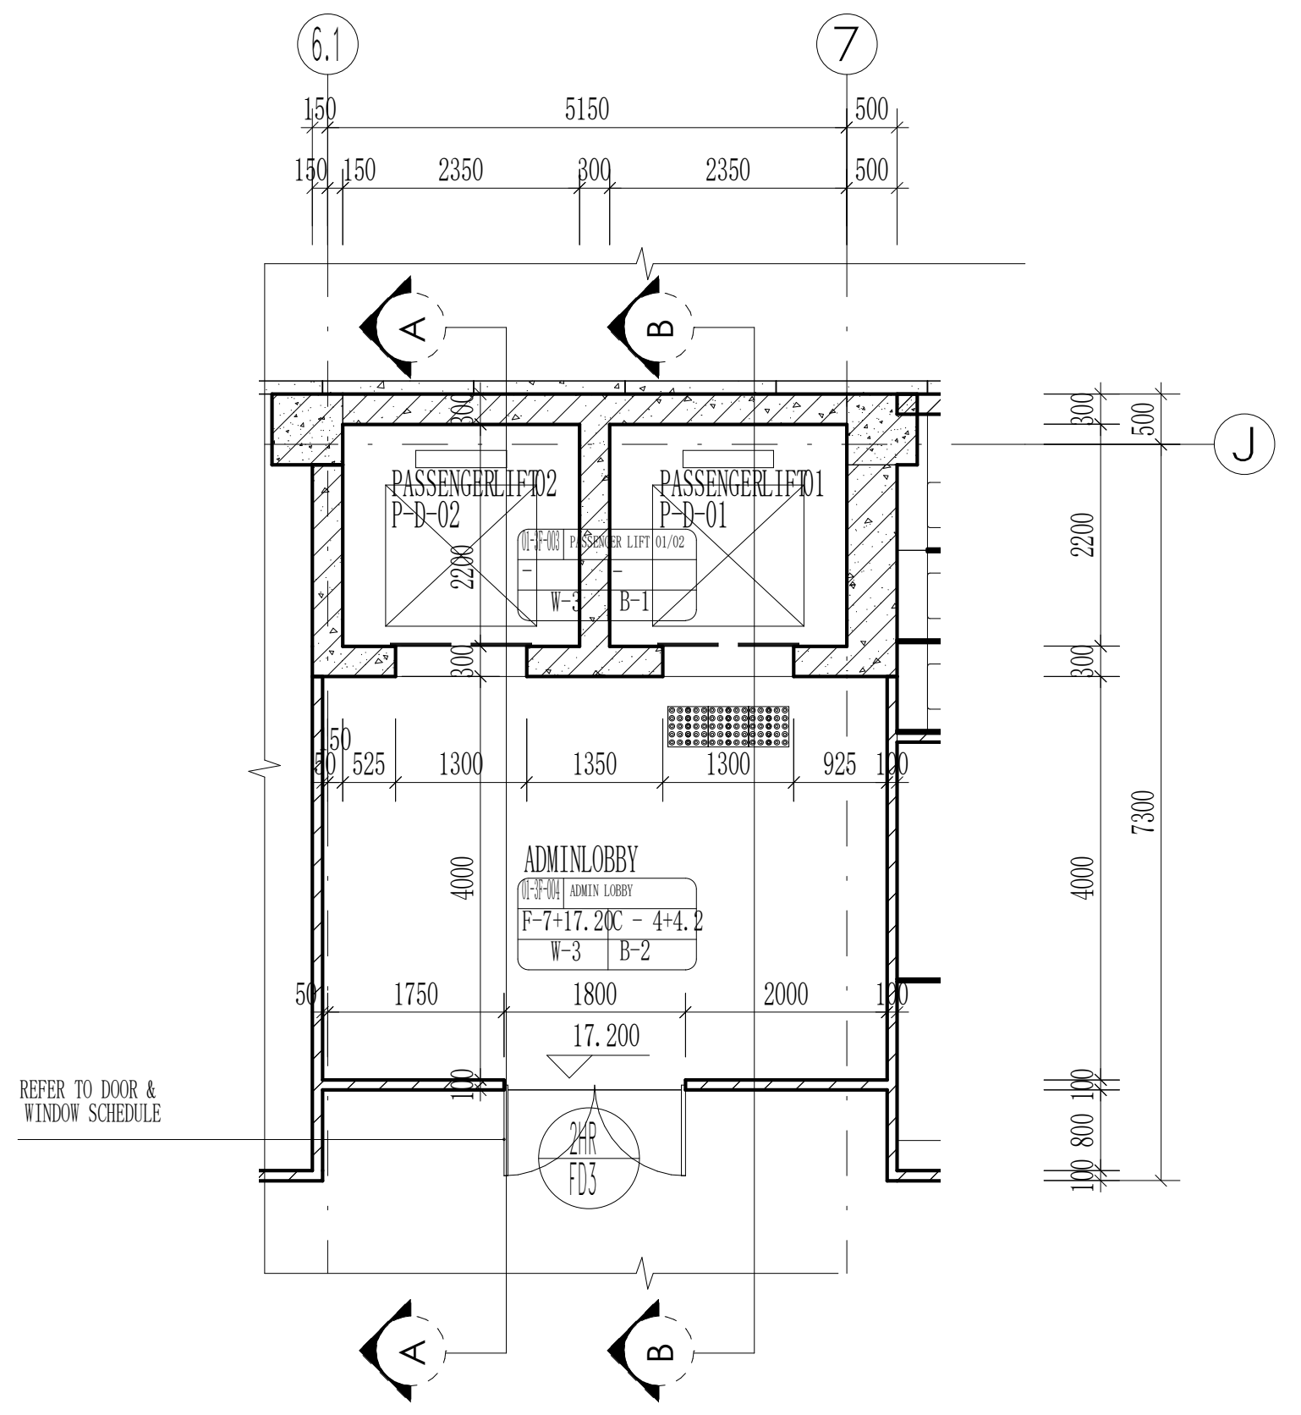

PASSAGER LIFT 3RD FL

SCALE 1:75

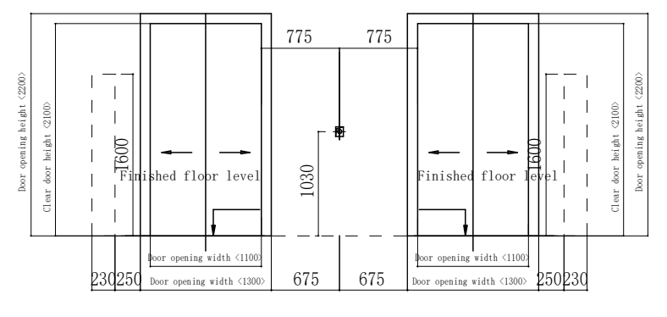
775
775
Door opening height <2200>
Clear door height <2100>
1600
Finished floor level
1030
Door opening width <1100>
Door opening width <1300>
230
250
675
675
250
230

FOR LANDING CALL

Scale 1:75

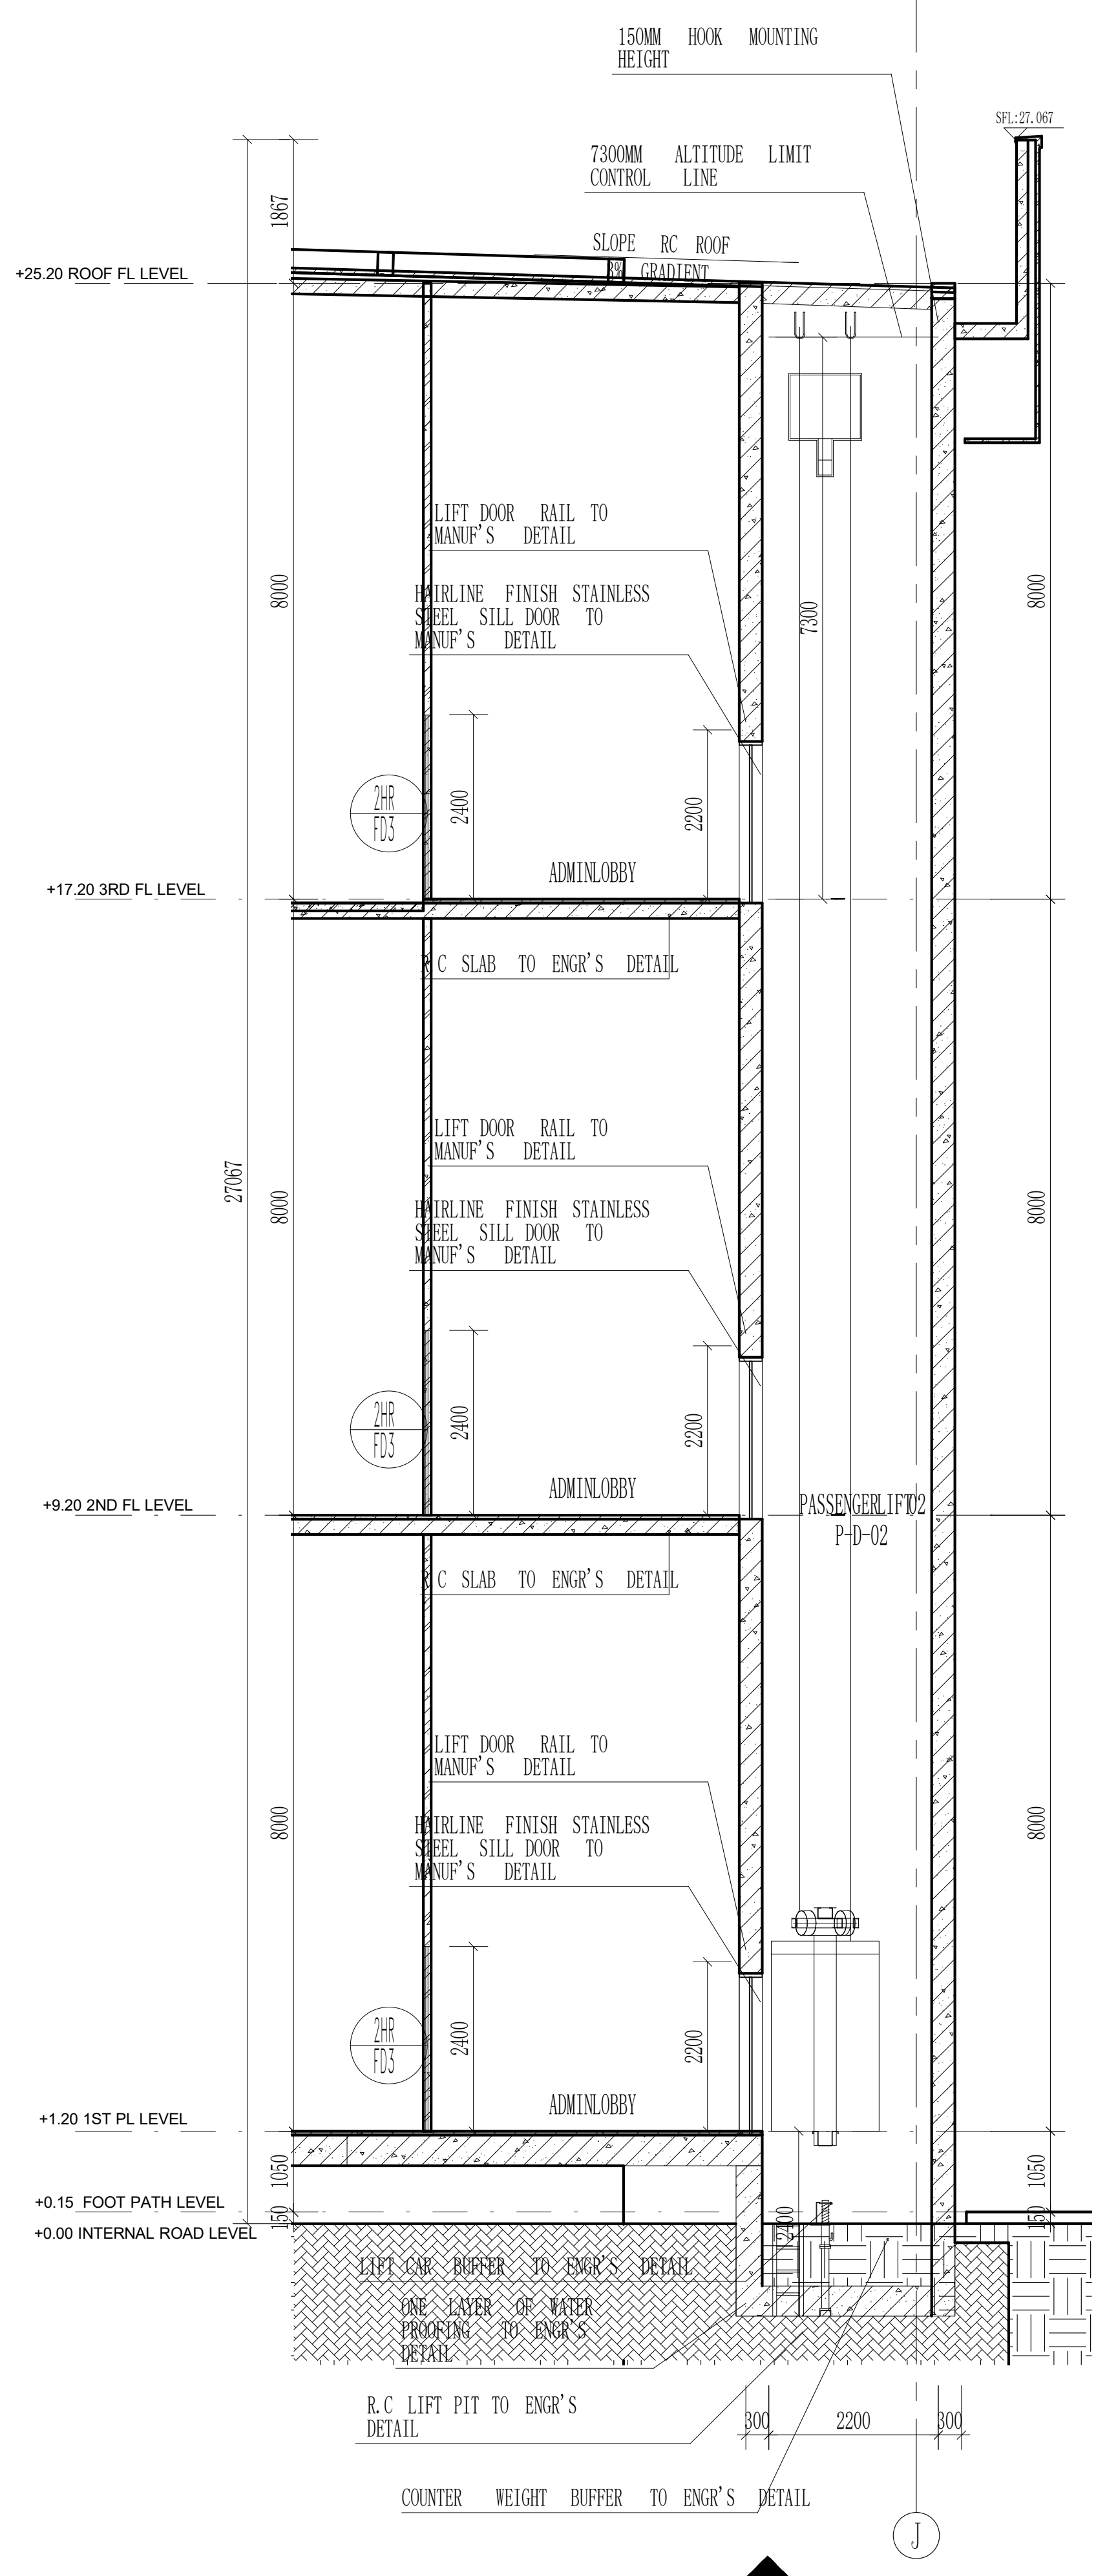
150MM HOOK MOUNTING HEIGHT
7300MM ALTITUDE LIMIT CONTROL LINE
SFL:27.067
SLOPE RC ROOF
3% GRADIENT
+25.20 ROOF FL LEVEL
1867
8000
7300
LIFT DOOR RAIL TO MANUF'S DETAIL
HAIRLINE FINISH STAINLESS STEEL SILL DOOR TO MANUF'S DETAIL
2HR
FD3
2400
2200
ADMINLOBBY
+17.20 3RD FL LEVEL
R.C SLAB TO ENGR'S DETAIL
27067
+9.20 2ND FL LEVEL
PASSENGERLIFT02
P-D-02
+1.20 1ST PL LEVEL
1050
150
+0.15 FOOT PATH LEVEL
+0.00 INTERNAL ROAD LEVEL
LIFT CAR BUFFER TO ENGR'S DETAIL
ONE LAYER OF WATER PROOFING TO ENGR'S DETAIL
R.C LIFT PIT TO ENGR'S DETAIL
300
2200
300
COUNTER WEIGHT BUFFER TO ENGR'S DETAIL
J

Section A

SCALE 1:75

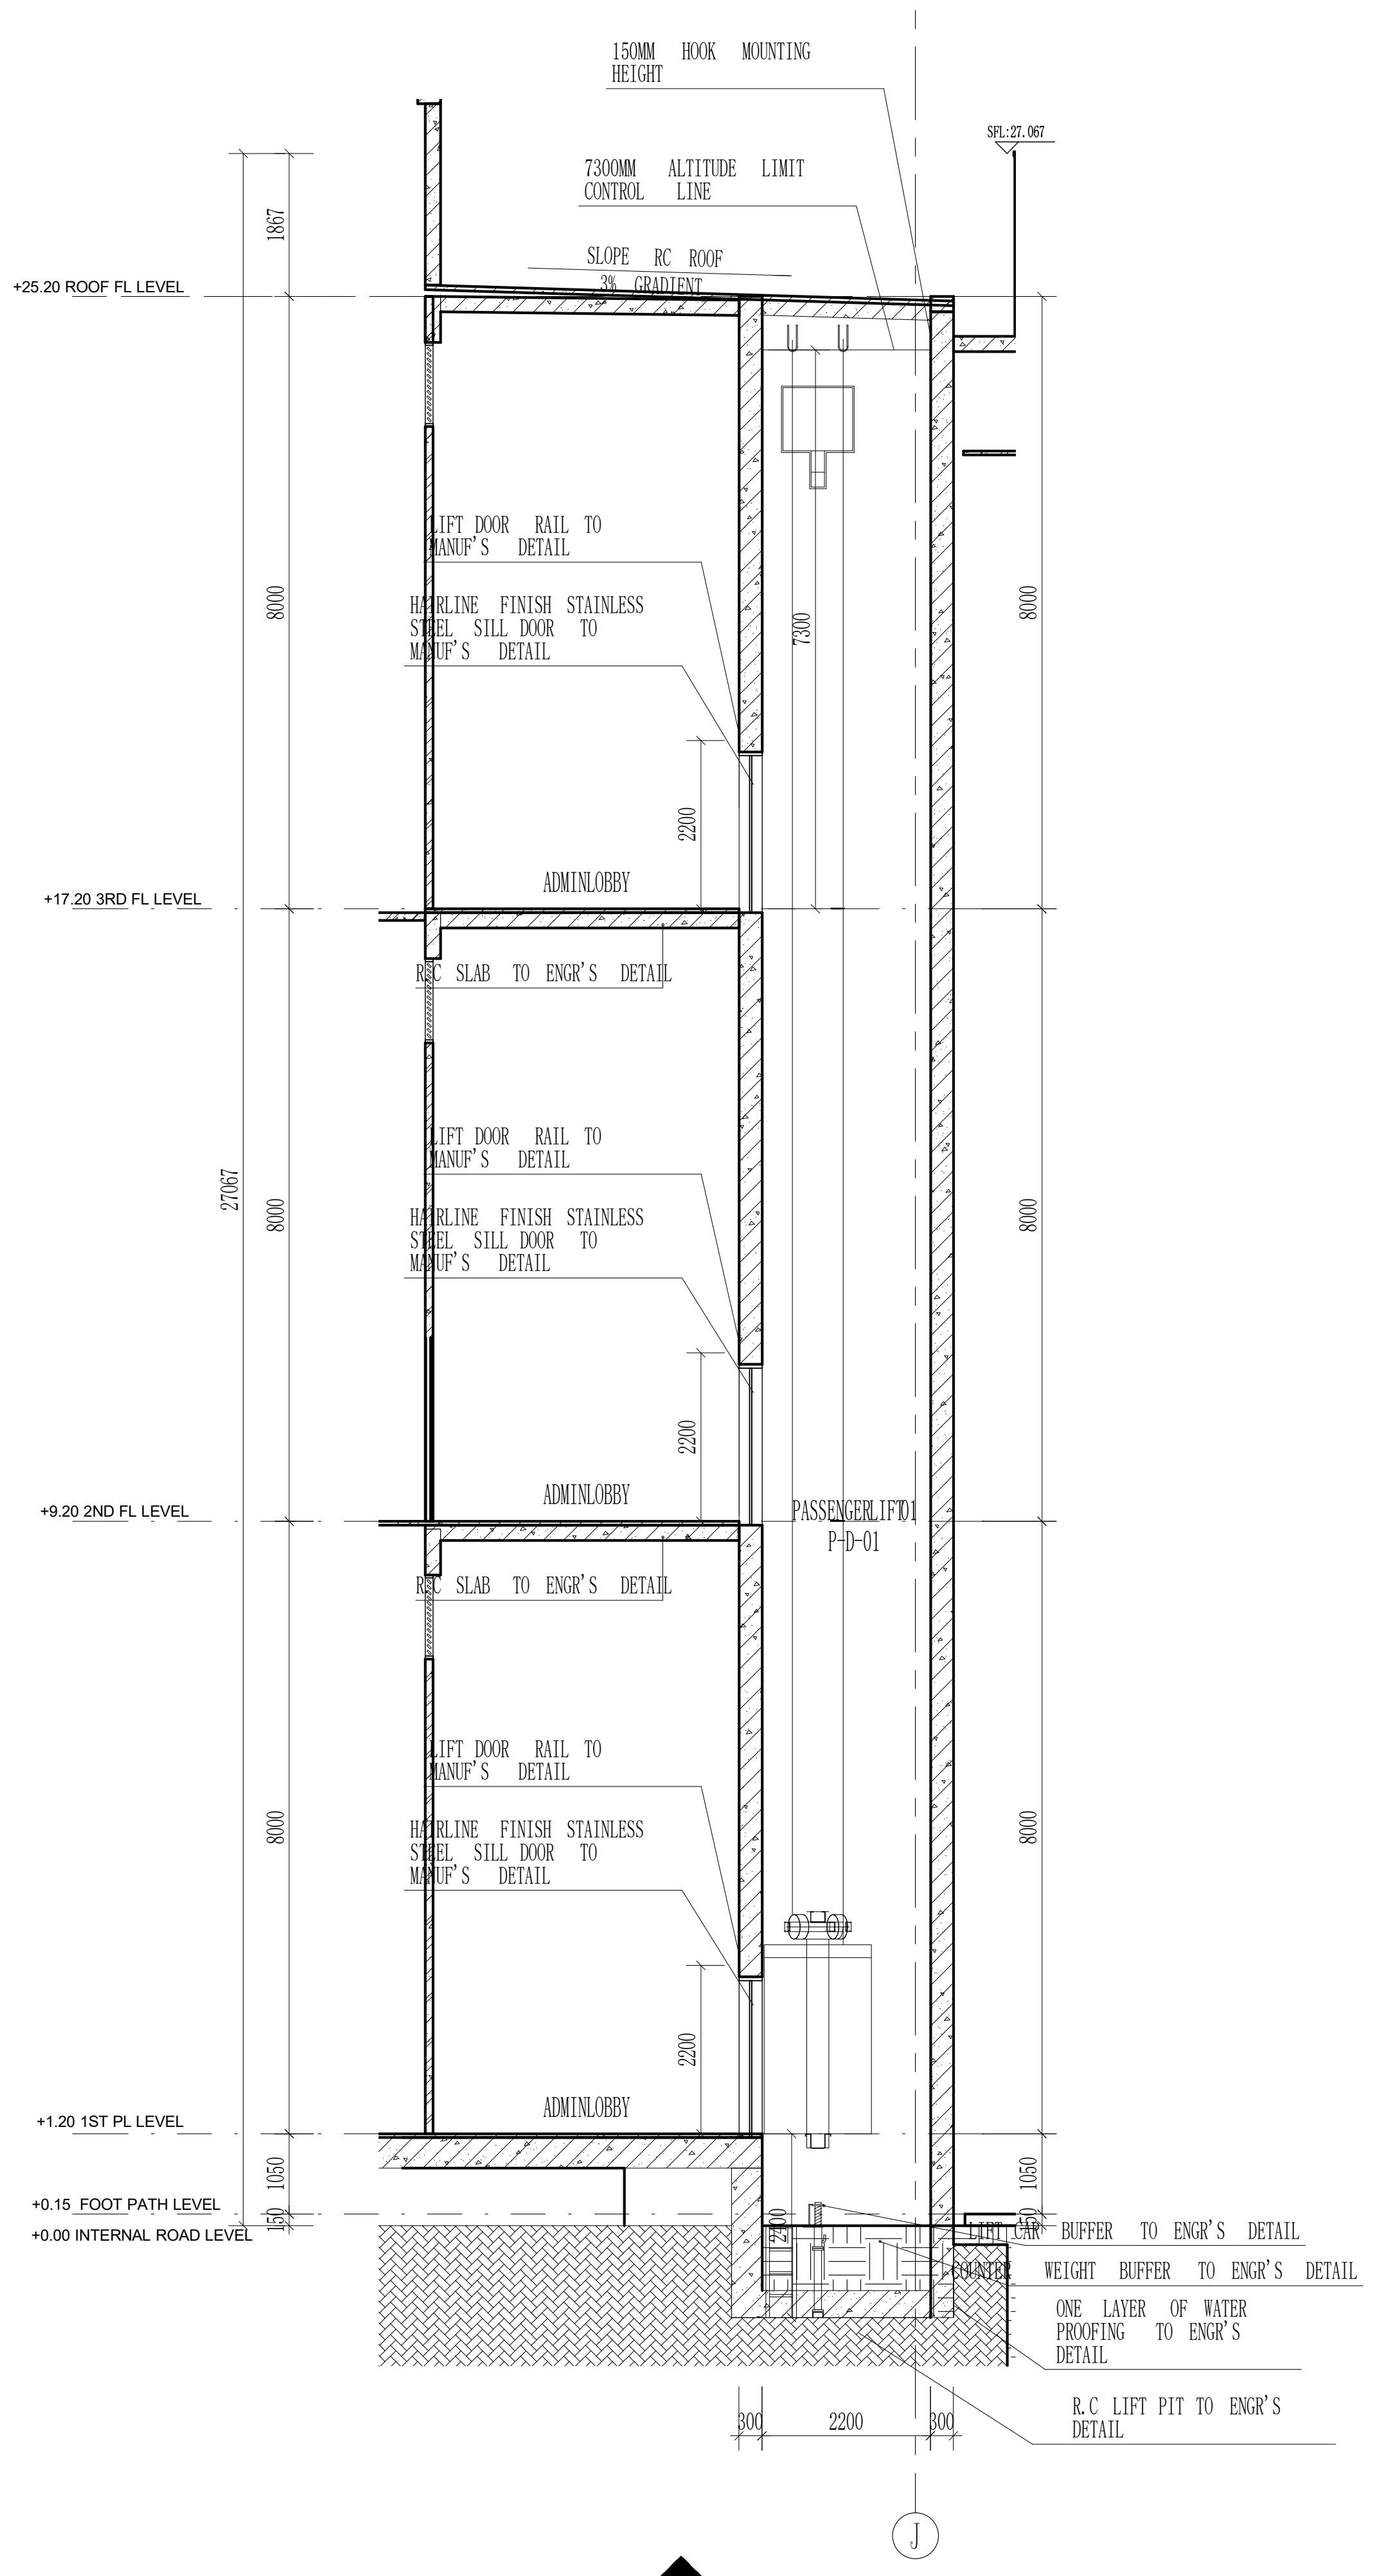
150MM HOOK MOUNTING HEIGHT
7300MM ALTITUDE LIMIT CONTROL LINE
SFL:27.067
SLOPE RC ROOF
3% GRADIENT
+25.20 ROOF FL LEVEL
1867
8000
7300
LIFT DOOR RAIL TO MANUF'S DETAIL
HAIRLINE FINISH STAINLESS STEEL SILL DOOR TO MANUF'S DETAIL
2200
ADMINLOBBY
+17.20 3RD FL LEVEL
R.C SLAB TO ENGR'S DETAIL
27067
+9.20 2ND FL LEVEL
PASSENGERLIFT01
P-D-01
+1.20 1ST PL LEVEL
1050
150
+0.15 FOOT PATH LEVEL
+0.00 INTERNAL ROAD LEVEL
LIFT CAR BUFFER TO ENGR'S DETAIL
WEIGHT BUFFER TO ENGR'S DETAIL
ONE LAYER OF WATER PROOFING TO ENGR'S DETAIL
R.C LIFT PIT TO ENGR'S DETAIL
300
2200
300
J

Section B

SCALE 1:75

CLIENT :

GULF EDGE DC 01

87 Wireless Road, M Thai Tower 11th. Floor, All Seasons Place, Lumpini,
Pathumwan, Bangkok 10330, Thailand

CONTRACTOR :

华西发展(泰国)有限公司
บริษัท หัวซือ ดีเวลลอปเม้นต์ (ประเทศไทย) จำกัด
HUASHI DEVELOPMENT CO.,LTD
No. 202, Room No. 1403, 14/F, Le Concorde Building,
Ratchadapisek Road, Huaykhwang Sub-District,
Huaykhwang District, Bangkok Metropolitan 10310.

CONSULTANT :

ARbay
บริษัท เอ อาร์ เบย์ จำกัด
ARbay Company Limited
31 st Floor Bangkok Insurance Building
25 South Sathorn road Thungmahamek
Sathorn Bangkok 10120 THAILAND
T +66 (0) 2286 8199
F +66 (0) 2286 2863
info@arbay.co.th

CONSULTANT :

Qbic Engineers & Architects Co.,Ltd.
8 Soi KALONG 4 SANAMBINNAM ROAD,
THASAI SUB-DISTRICT, MUANG NONTHABURI DISTRICT
, NONTHABURI.
Tel 662-950-4374
Fax 662-580-3231
E-Mail : qbic@qbic.co.th, www.qbic.co.th
QBIC ENGINEERS AND ARCHITECTS CO.,LTD.

CONSULTANT :

MITR
MITR TECHNICAL CONSULTANT CO.,LTD.
1168/8 12th FLOOR, LUMPINI TOWER BUILDING,
RAMA IV RD., THUNGMAHAMEK, SATHORN, BANGKOK 10120, THAILAND
TEL : 0-2679-9079-84
FAX : 0-2679-9085 E-mail: mitr_dd@mitr.com

Architect :	SIGNATURE
ประกิต พนานุรัตน์ วสถ. 580 ที่อยู่ 251/1 ถ.จารุเมือง แขวงรองเมือง เขตปทุมวัน กรุงเทพมหานคร โทรศัพท์ 02-286-8199	

Structural Engineer :	SIGNATURE
วิศวกรผู้ออกแบบโครงสร้าง	
ณัฐสม สงวนวงษ์ วย 1423 ที่อยู่ 2/1 ซ.รามคำแหง 150 ถ.รามคำแหง แขวง สะพานสูง เขต สะพานสูง กทม. 10240	ณัฐสม สงวนวงษ์

Structural Inspector :	SIGNATURE
วิศวกรผู้ตรวจสอบโครงสร้าง	
โกมล จุฑาภัทร วย 964 ที่อยู่ 24/18 ซ.นวมินทร์ 129 ถ. นวมินทร์ แขวง นวลจันทร์ เขต บึงกุ่ม กทม. 10230	

Electrical Engineer :	SIGNATURE
วิศวกรผู้ออกแบบระบบไฟฟ้ากำลัง	
นายสุภัทร บูรณวิทย์ วฟก.1265 ที่อยู่ 21 ซอยทานสัมฤทธิ์ 13 ตำบลท่าทราย อ.เมืองนนทบุรี จ.นนทบุรี 11000	สุภัทร บูรณวิทย์

Mechanical Engineer :	SIGNATURE
วิศวกรผู้ออกแบบระบบเครื่องกลและปรับอากาศ	
นายประสิทธิ์ เกี้ยวสุนทร วก.1221 ที่อยู่ 44/372 ซอยบางกระดี่ 35/1 แขวงแสมดำ เขตบางขุนเทียน กทม. 10150	ประสิทธิ์

Sanitary Engineer :	SIGNATURE
วิศวกรผู้ออกแบบระบบสุขาภิบาล และดับเพลิง	
นายทศวรรษ สนั่นฤทธิ์ วส. 215 ที่อยู่ บ้านเลขที่ 99/107 หมู่ที่ 3 ต.ศีรษะจรเข้น้อย อ.บางเสาธง จ.สมุทรปราการ 10540	ทศวรรษ

ISSUE/REVISION

REV.	DESCRIPTION	DATE
A	90% DEVELOPED	09/05/2026

PROJECT NAME :

GEDC 01

LOCATION:
Nikhom Phattana district, Rayong ,industrial estate,CPGC

BUILDING :
MAIN BUILDING

90% DEVELOPED

TITLE :

PASSAGER LIFT

JOB NO.		SCALE	1 : 75
DRAWN	LW	REF.	
CHECKED	LJC	DWG. NO.	MPK01A-90-VT-LT1-003
APPROVED	LXD		
DATE	2026.05.09		

NOTE :THIS PRINT IS OF A CONFIDENTIAL NATURE, IT SHALL NOT BE TRACED,PHOTOGRAPHED,PHOTOSTATED OR REPRODUCED IN ANY MANER,NOR USED FOR ANY PURPOSE WHATSOEVER EXCEPT BY WRITTEN PERMISSION